

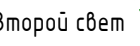
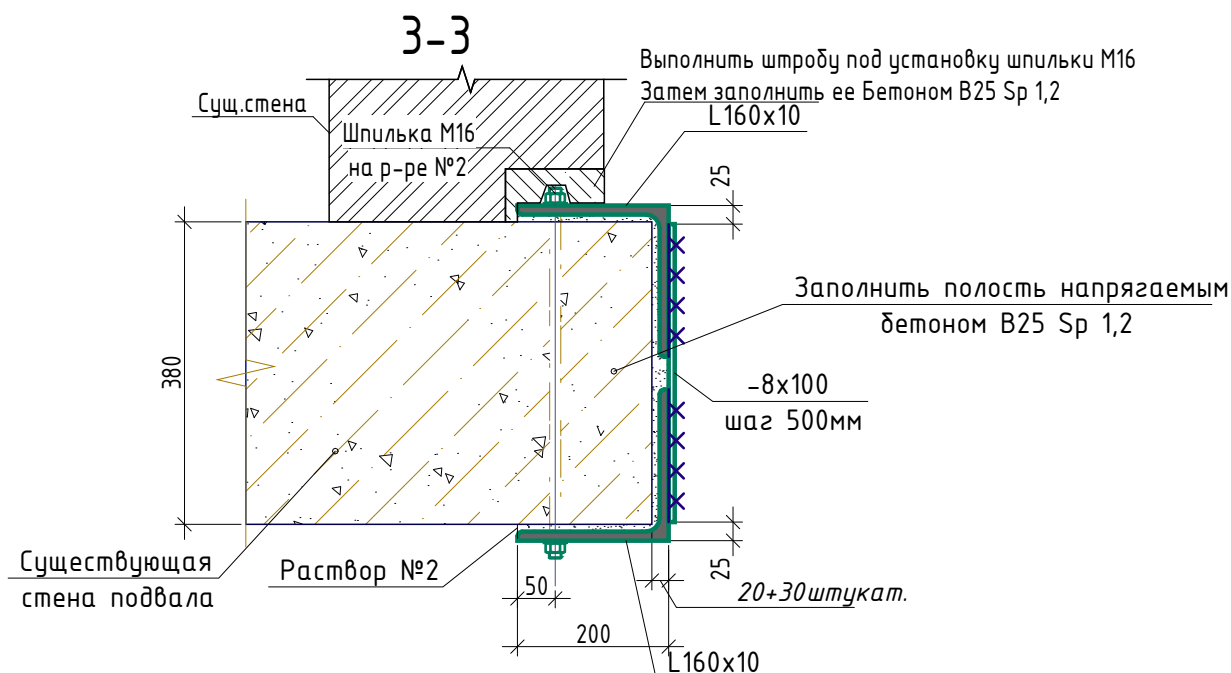
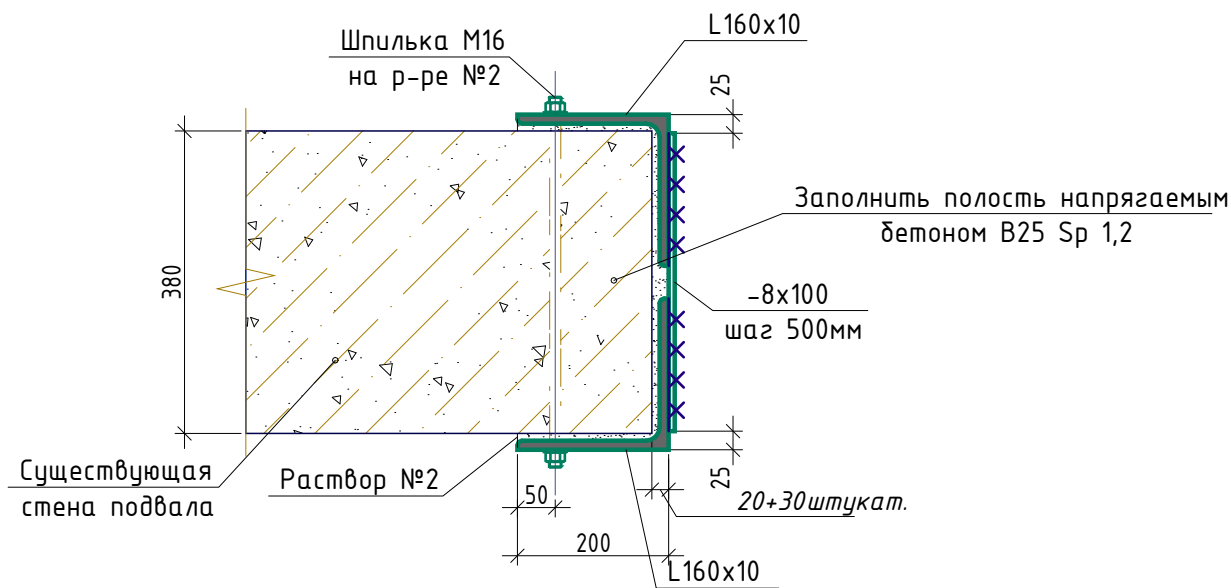


M1:100

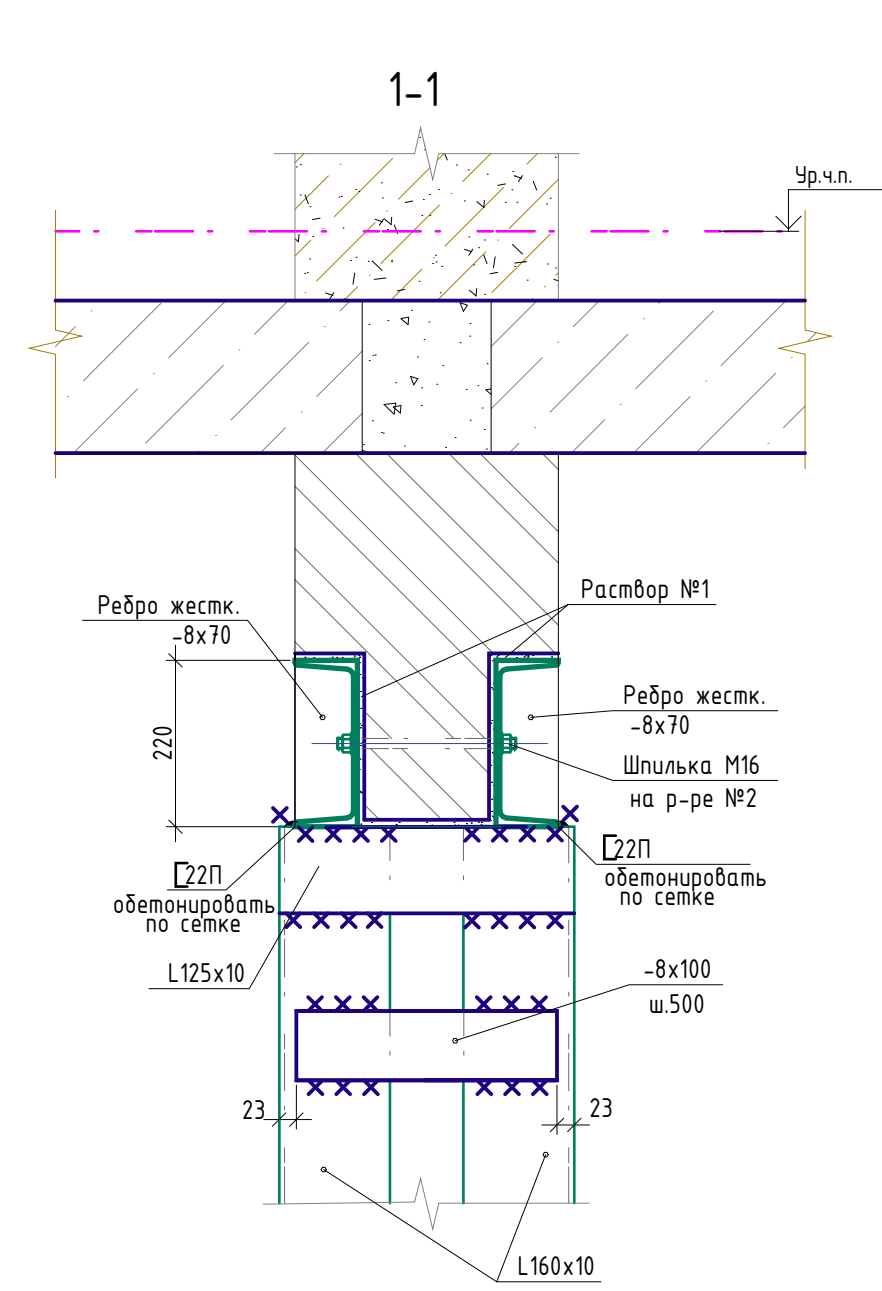

Формат A1A

Рама Рм-4 2200x1030мм

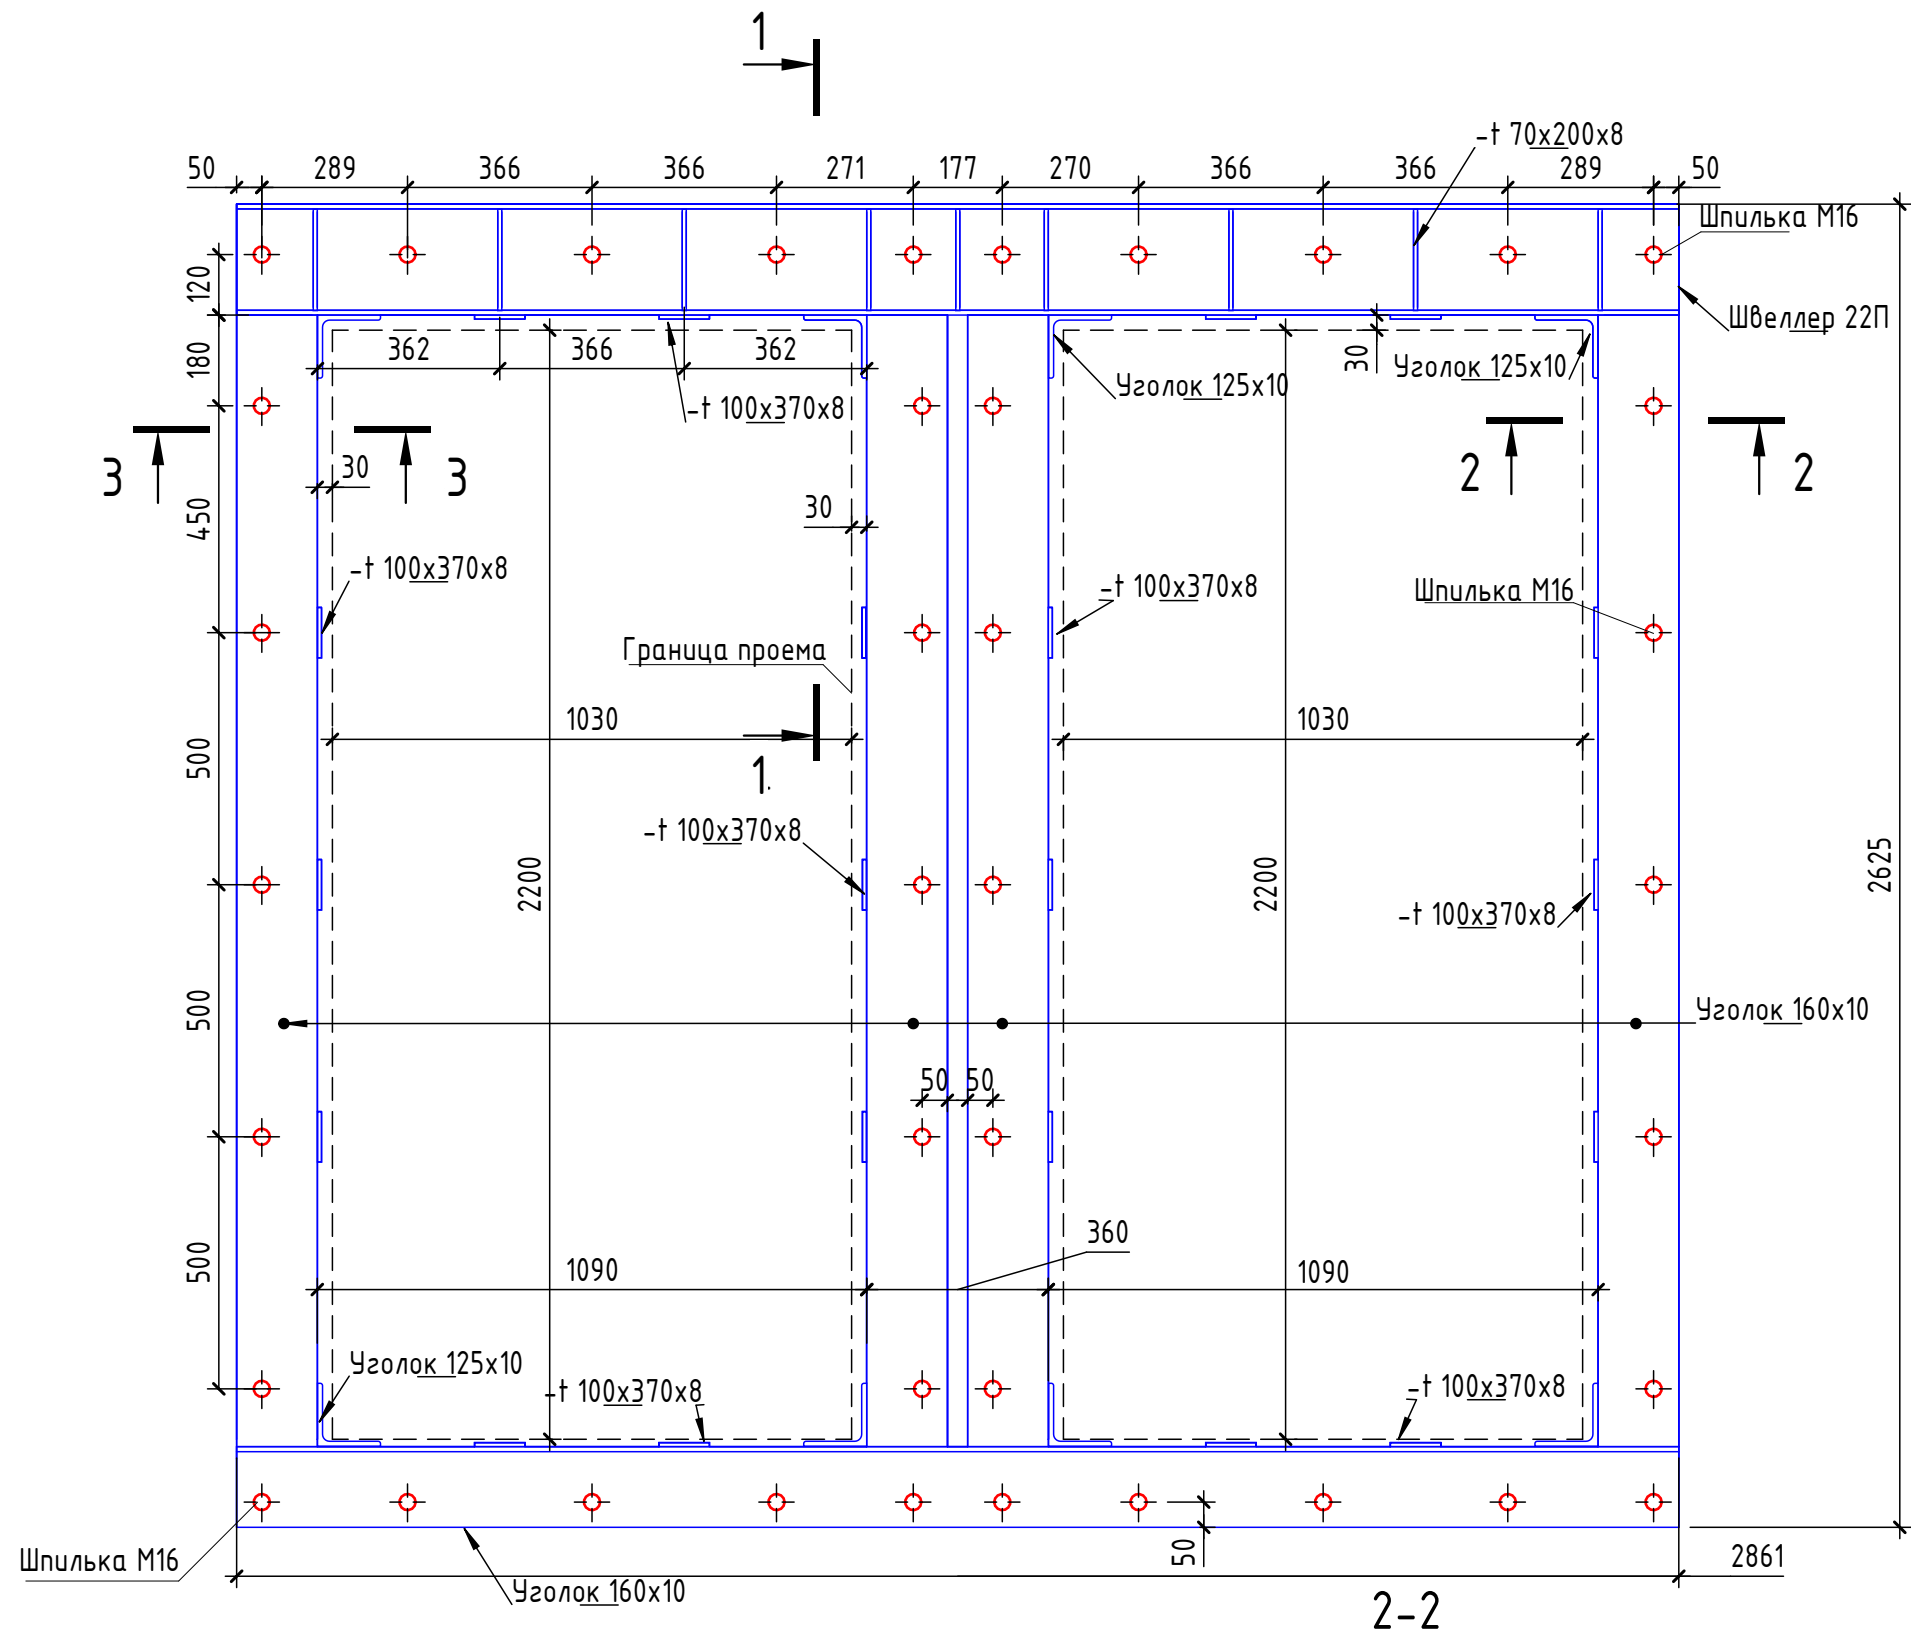

Общая ведомость материалов на раму Рм-4

№ П.п	Обозначение	Наименование	Общая длинна(п.м)	Кол-во(шт.)	Примечание
		-т 70х200х8		18	
		-т 100х370х8		20	
	ГОСТ8509-93	Уголок 125х10	3,6		
	ГОСТ8509-93	Уголок 160х10	23,7		
	ГОСТ 8240-97	Швеллер 22П	5,7		
		Шпилька М16 1000.56.016 шт.	20		
		Шайба С.16.01.08кп.016 шт.		80	
		Гайка М16 56.016 шт.		80	
		Штукатурка			0.14м³
		Сетка 12х2.0 оц.			2.6м²

- Перед производством работ выполнить вскрытие отделочного слоя проемов и уточнить все размеры.
- Методика производства работ.
- Установку деталей крепления стен над пробиваемым проемом в существующей стене произвести в следующем порядке:
 - До начала производства работ следует произвести установку временных опор в количестве 4 шт., L=по месту мм.
 - На плоскости стены разметить контуры проема и горизонтальных штраб.
 - Разбивку отверстий в стене и перемычке для пропуска болтов произвести в соответствии с разбивкой отверстий в стальной перемычке. Отверстия пробить шлямбуром диаметром 40 мм.
 - Прорезать горизонтальную штрабу с одной стороны, с другой стороны по центру шлямбурных отверстий прорезать гнездо размером 100х100 мм, очистить от пыли и грязи, на поверхности штрабы нанести слой раствором №1 толщиной 10–20 мм, завести швеллер и предварительно стянуть со стеной болтами для плотного впрессовывания в штрабу.
 - Установку швеллера с другой стороны стены повторить.
 - Швеллеры окончательно стянуть между собой шпилькой.
 - Произвести вырезание проема методом алмазной резки под перемычкой согласно схеме.
 - После разборки проема снизу к стальной перемычке приварить накладки и оштукатурить по сетке.
 - Металлические элементы выполнить из стали С245 ГОСТ 27772-2015.
 - Обварить все элементы по контуру сопрягаемых элементов. Катет сварных швов принимать по наименьшей толщине свариваемых элементов. Сварку производить по ГОСТ 5264–80 (ручная дуговая). Сварку производить электродами Э-46 по ГОСТ 9467–75.
 - Элементы усиления устанавливать на раствор №2, толщиной не менее 10 мм.
 - Все металлические изделия окрасить грунтовкой ГФ-021 ГОСТ 25129-2020.
 - После монтажа и закрепления элементов металлических конструкций оштукатурить их по сетке.
 - Под все гайки установить пружинные шайбы для предотвращения раскручивания.

Типы растворов применяемых для установки стальных конструкций и их применение.

- Раствор №1 на напрягаемом цементе, массовый состав: цемент ЦЦ-20 М500 (ТУ 5734–072–46854090–98, ТУ 21-20-18-80) – 1 часть, песок – 1,1 части, суперпластификатор С-3 (ТУ 5745-004-43184789-05) – 0,002--0,007 части, В/Ц= 0,4--0,45.
 - Раствор №2 безусадочный, массовый состав: цемент ЦЦ-10 М400 (ТУ 5734–072–46854090–98, ТУ 21-20-48-82) – 1 часть, песок – 2 части, суперпластификатор С-3 (ТУ 5745-004-43184789-05) – 0,002--0,007 части, В/Ц=0,4--0,45.
- Указания по приготовлению растворов №1 и №2: компоненты смеси должны быть тщательно перемешаны в сухом состоянии, после чего к ним добавляется чистая вода комнатной температуры с растворенным в ней суперпластификатором. Песок средний или крупный должен соответствовать ГОСТ 8736-93 и иметь не более 5% примесей, рекомендуется использовать промытый и просушенный песок. Вода должна удовлетворять требованиям ГОСТ 23732. Поверхность нанесения должна быть предварительно очищена от механических и химических частиц загрязнения и увлажнена, следует избегать подтеков воды непосредственно перед нанесением. Стальные поверхности увлажнять не следует.
- Для обеспечения условий, необходимых для расширения материала требуется тщательное его увлажнение в течение 24 часов любым доступным способом.

Общие указания

- До начала работ проверить наличие всех видов разводов (электро-и слаботочных), попадающих в зону устройства проема;
- Перед началом производства работ все размеры уточнить по месту путем фактического измерения;
- Все работы вести по специально разработанному ППР, разработанному подрядной организацией и согласованному с техническим надзором.

						696/П-24-АНО - КР			
						Капитальный ремонт Государственного бюджетного общеобразовательного учреждения города Москвы Школа №1282 Сокольники по адресу: г. Москва, ул. Барболина, д.1, корп.1			
Изм.	Кол.уч.	Лист	№ док.	Подп.	Дата	Капитальный ремонт	Стадия	Лист	Листов
Разработал	Васясин А.А						Р	2	
Проверил	Головина					Рама Рм-4 2200х1030мм			
ГАП	Гулько								
Норм.контр.	Выходова								