


Пластина опорная 720x500 под площадки

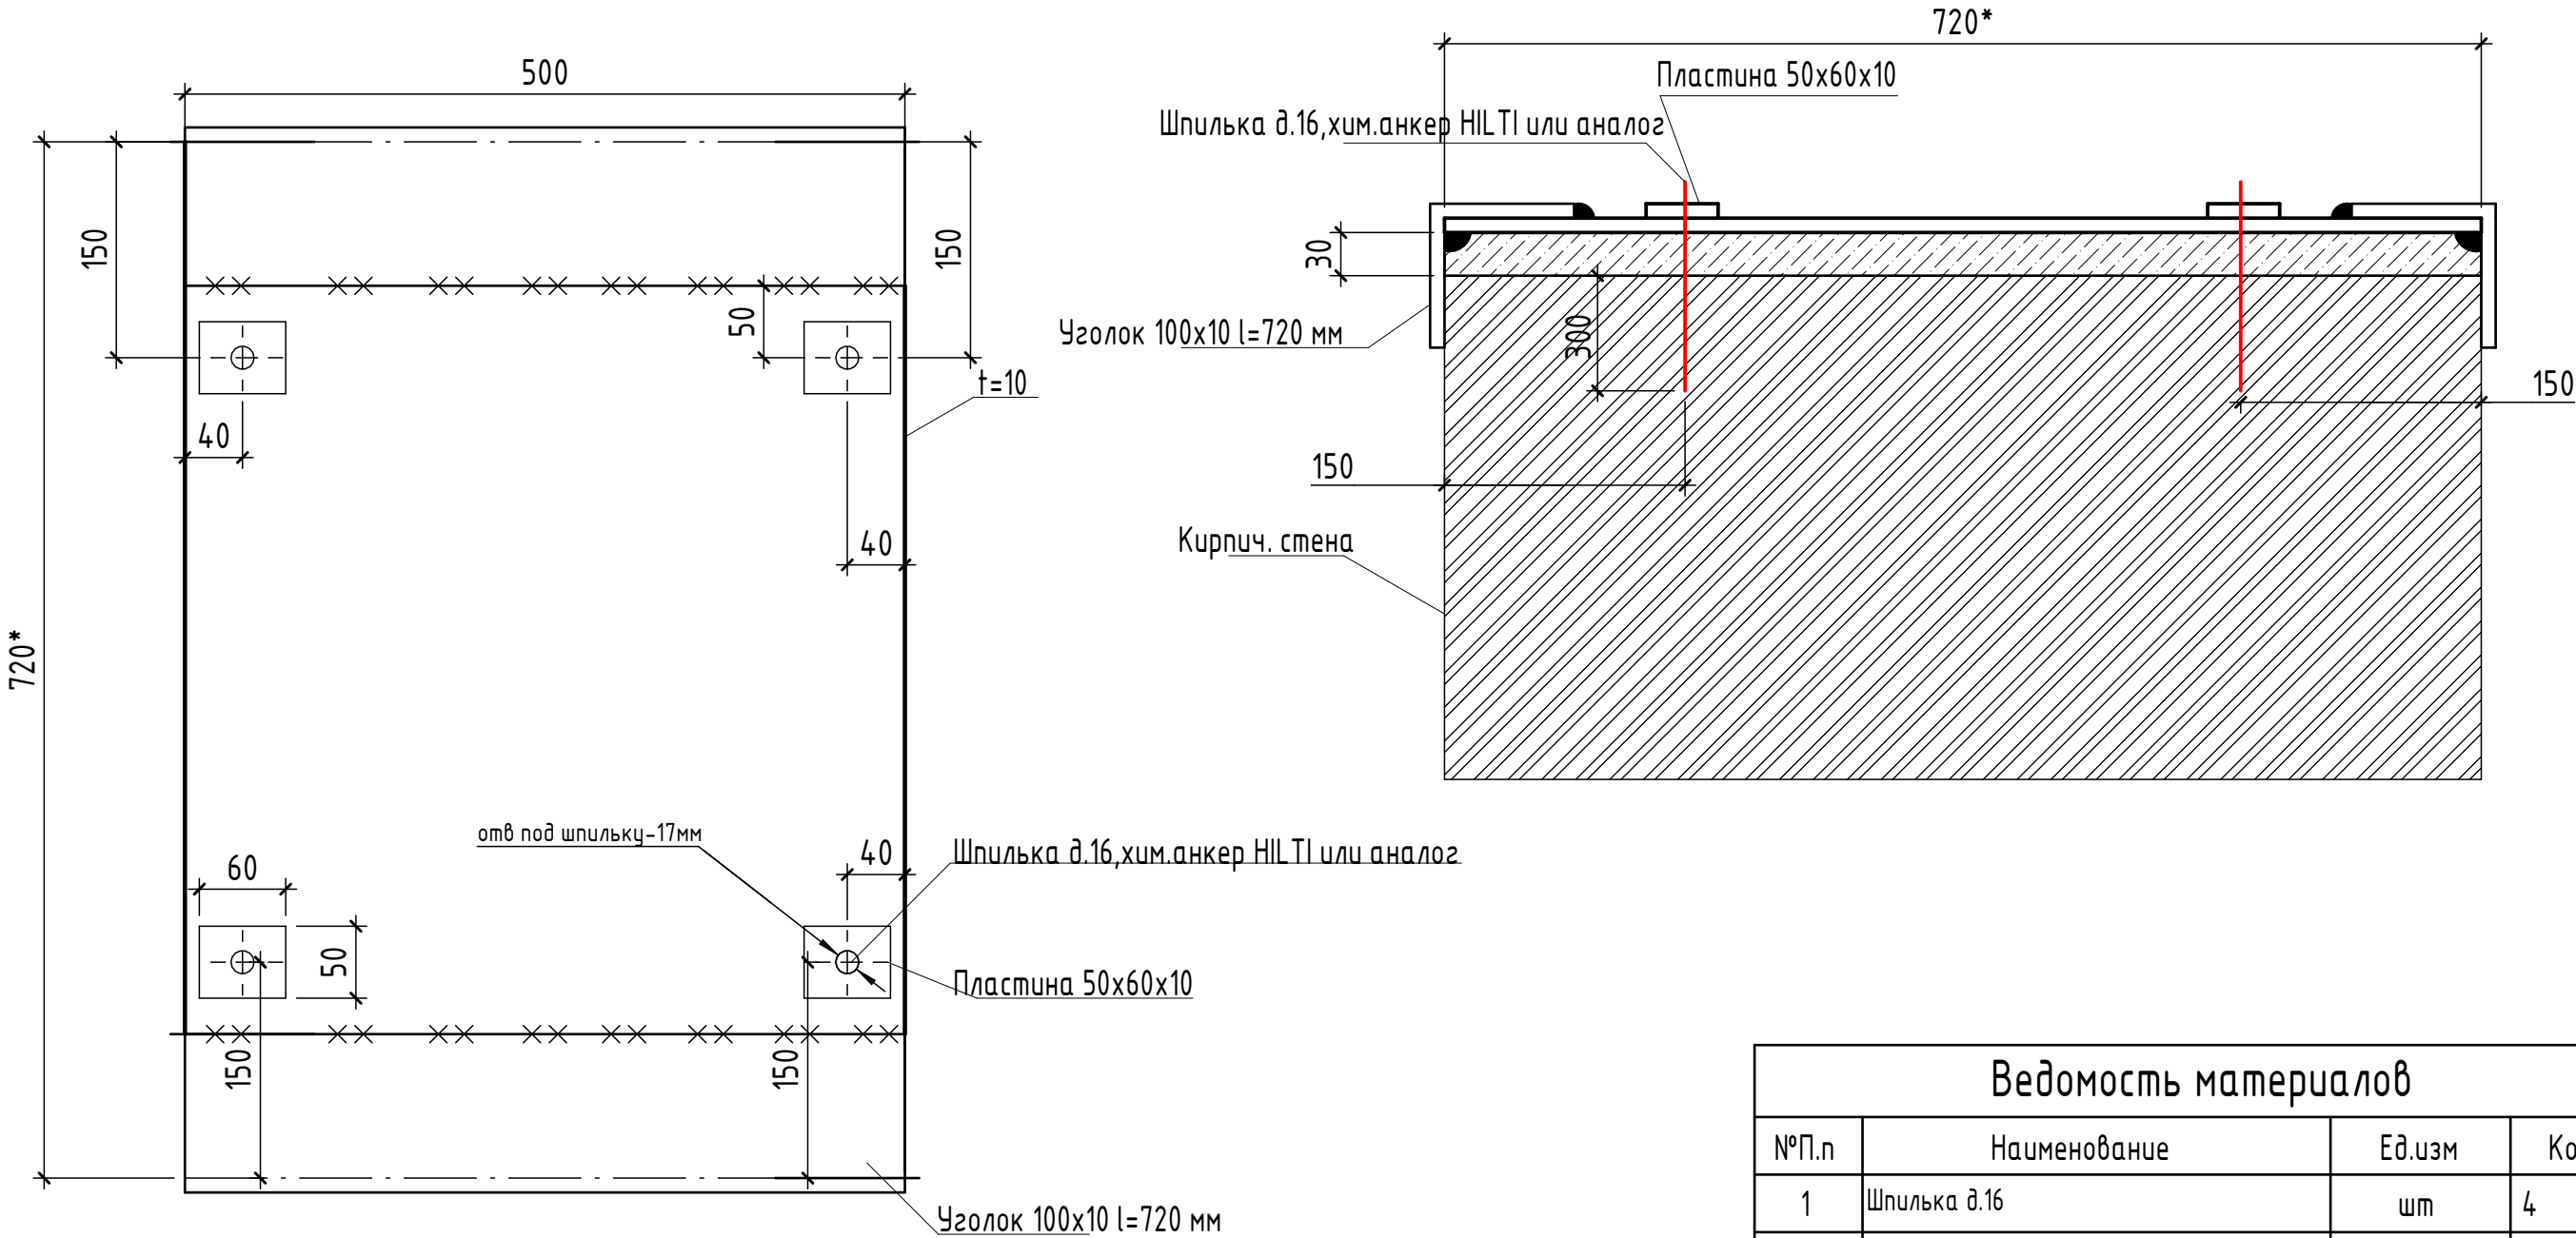


Ведомость материалов			
№П.п	Наименование	Ед.изм	Кол-во
1	Шпилька д.16	шт	4
2	Пластина 50x60x10	шт	4
3	Уголок 100x10	пз.м	1.5
4	- 720x500x10	шт	1
5	-300x300x10	шт	1
6	Гайка М16	шт	4
7	Шайба.усил М16	шт	4

						696/П-24-АНО-Р - КР			
						Капитальный ремонт Государственного бюджетного общеобразовательного учреждения города Москвы Школа №1282 Сокольники по адресу: г. Москва, ул Барболина, д.1, корп.1			
Изм.	Кол.уч.	Лист	№ док.	Подп.	Дата	Капитальный ремонт	Стадия	Лист	Листов
Разработал			Васясин А.А				Р	52	
ГИП			Гулько А.Н			Пластины опорные под площадки			
Н.контроль			Выходова Н.А						

*Размер справочный уточнить по месту

Узел крепления стоек площадок оборудования (1 : 10)

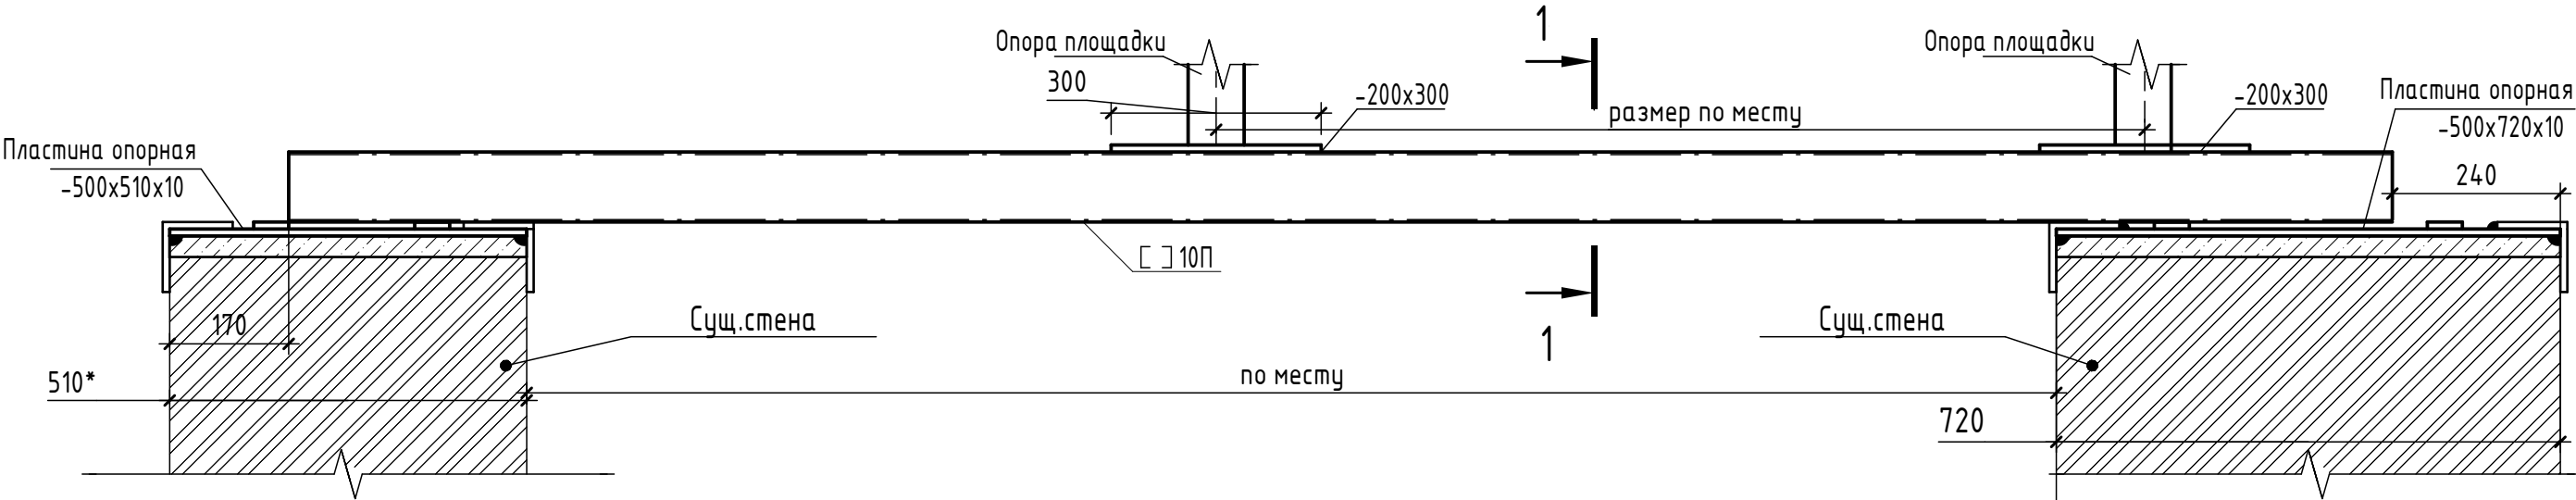


Ведомость материалов узел на крепление стоек при ширине 3м			
№П.п	Наименование	Ед.изм	Кол-во
1	Шпилька д.16	Пз.м	4
2	Пластина 50x60x10	шт	8
3	Уголок 100x10	пз.м	3
4	- 720x500x10	шт	1
5	-510x500x10	шт	1
6	Гайка М16	шт	8
7	Шайба.усил М16	шт	8
8	-160x70x5	шт	20
9	-200x300x10	шт	2
10	Швеллер 10П	пз.м	7


*Размер справочный уточнить по месту

						696/П-24-АНО-Р - КР			
						Капитальный ремонт Государственного бюджетного общеобразовательного учреждения города Москвы Школа №1282 Сокольники по адресу: г. Москва, ул Барболина, д.1, корп.1			
Изм.	Кол.уч.	Лист	№ док.	Подп.	Дата	Капитальный ремонт	Стадия	Лист	Листов
Разработал	Васясин А.А						Р	53	
ГИП	Гулько А.Н								
						Узел крепления стоек площадок оборудования			
Н.контроль	Выходова Н.А								

Узел крепления стоек площадок оборудования (1 : 10)

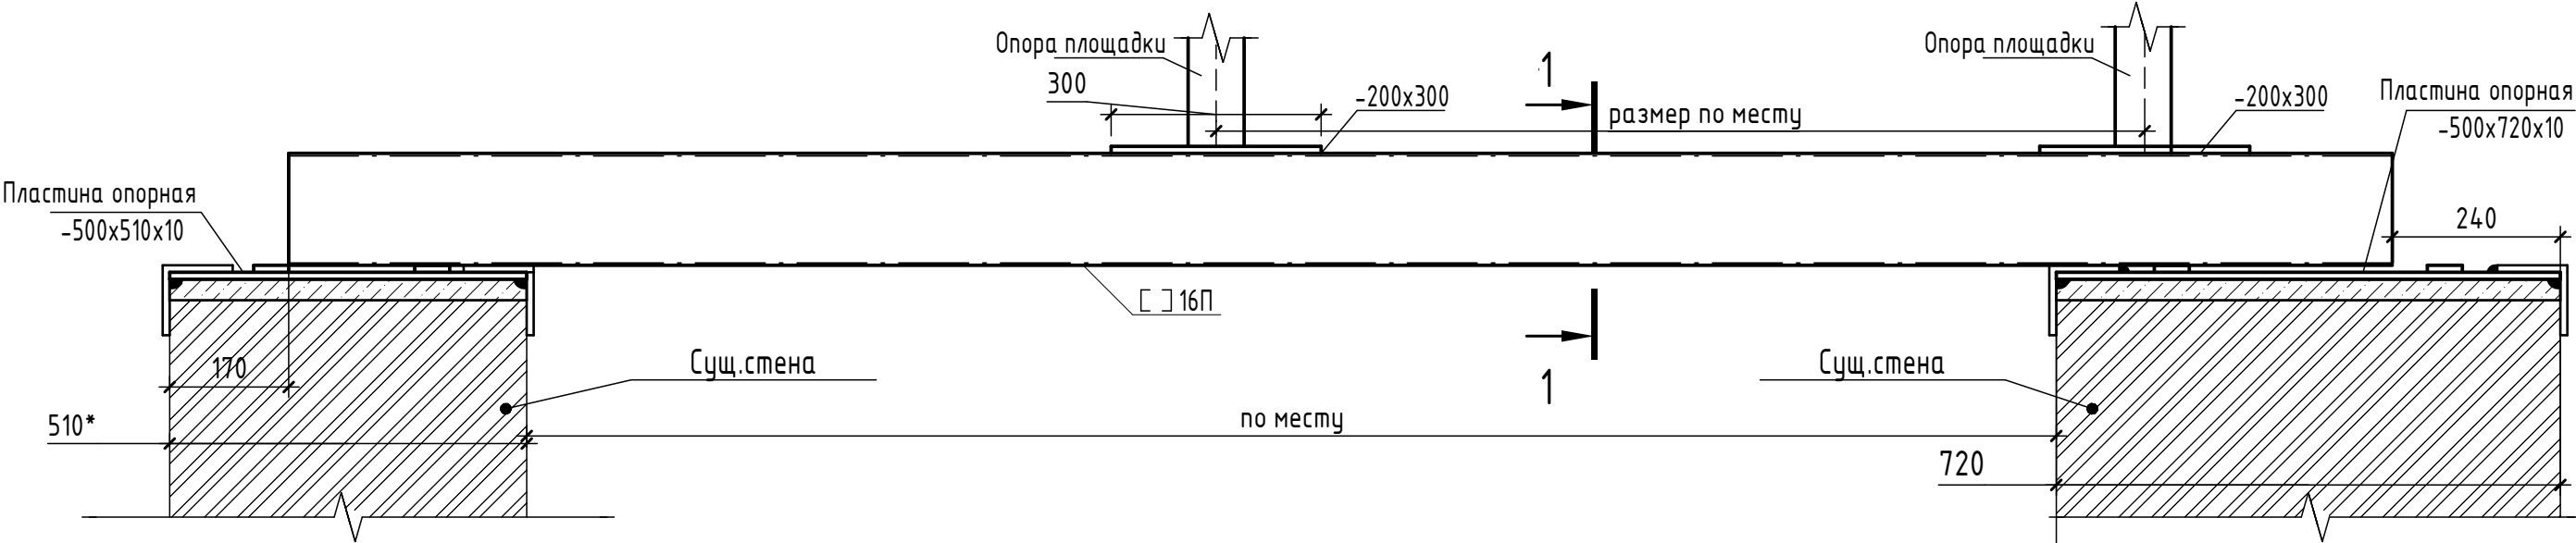

1-1.. (1 : 5)

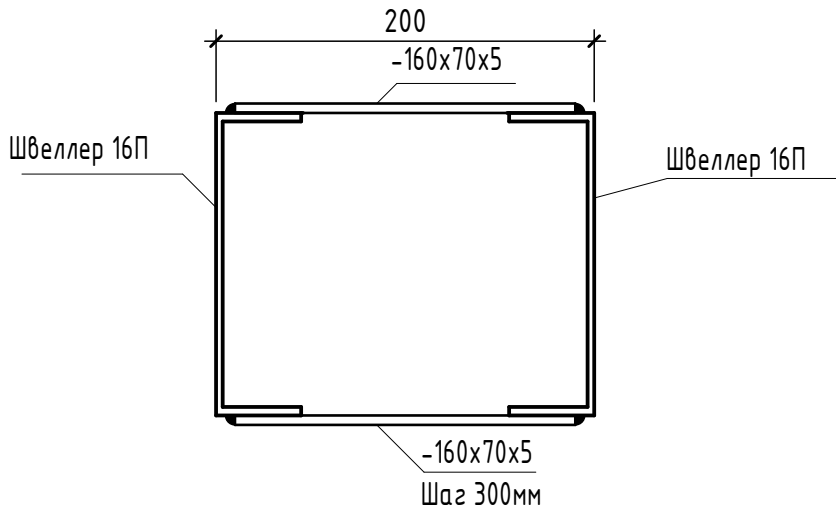


Ведомость материалов узел на крепление стоек при ширине 3м			
№П.п	Наименование	Ед.изм	Кол-во
1	Шпилька д.16	Пз.м	4
2	Пластина 50x60x10	шт	8
3	Уголок 100x10	пз.м	3
4	- 720x500x10	шт	1
5	-510x500x10	шт	1
6	Гайка М16	шт	8
7	Шайба.усил М16	шт	8
8	-160x70x5	шт	20
9	-200x300x10	шт	2
10	Швеллер 16П	пз.м	7


*Размер справочный уточнить по месту

						696/П-24-АНО-Р - КР				
						Капитальный ремонт Государственного бюджетного общеобразовательного учреждения города Москвы Школа №1282 Сокольники по адресу: г. Москва, ул Барболина, д.1, корп.1				
Изм.	Кол.уч.	Лист	№ док.	Подп.	Дата					
Разработал	Васясин.А.А					Капитальный ремонт		Стадия	Лист	Листов
Проверил	Головина							Р	54	
ГАП		Гулько				Узел крепления стоек площадок оборудования				
Норм.контроль		Выходова								



Узел крепления стоек площадок оборудования вариант 3 (1 : 20)

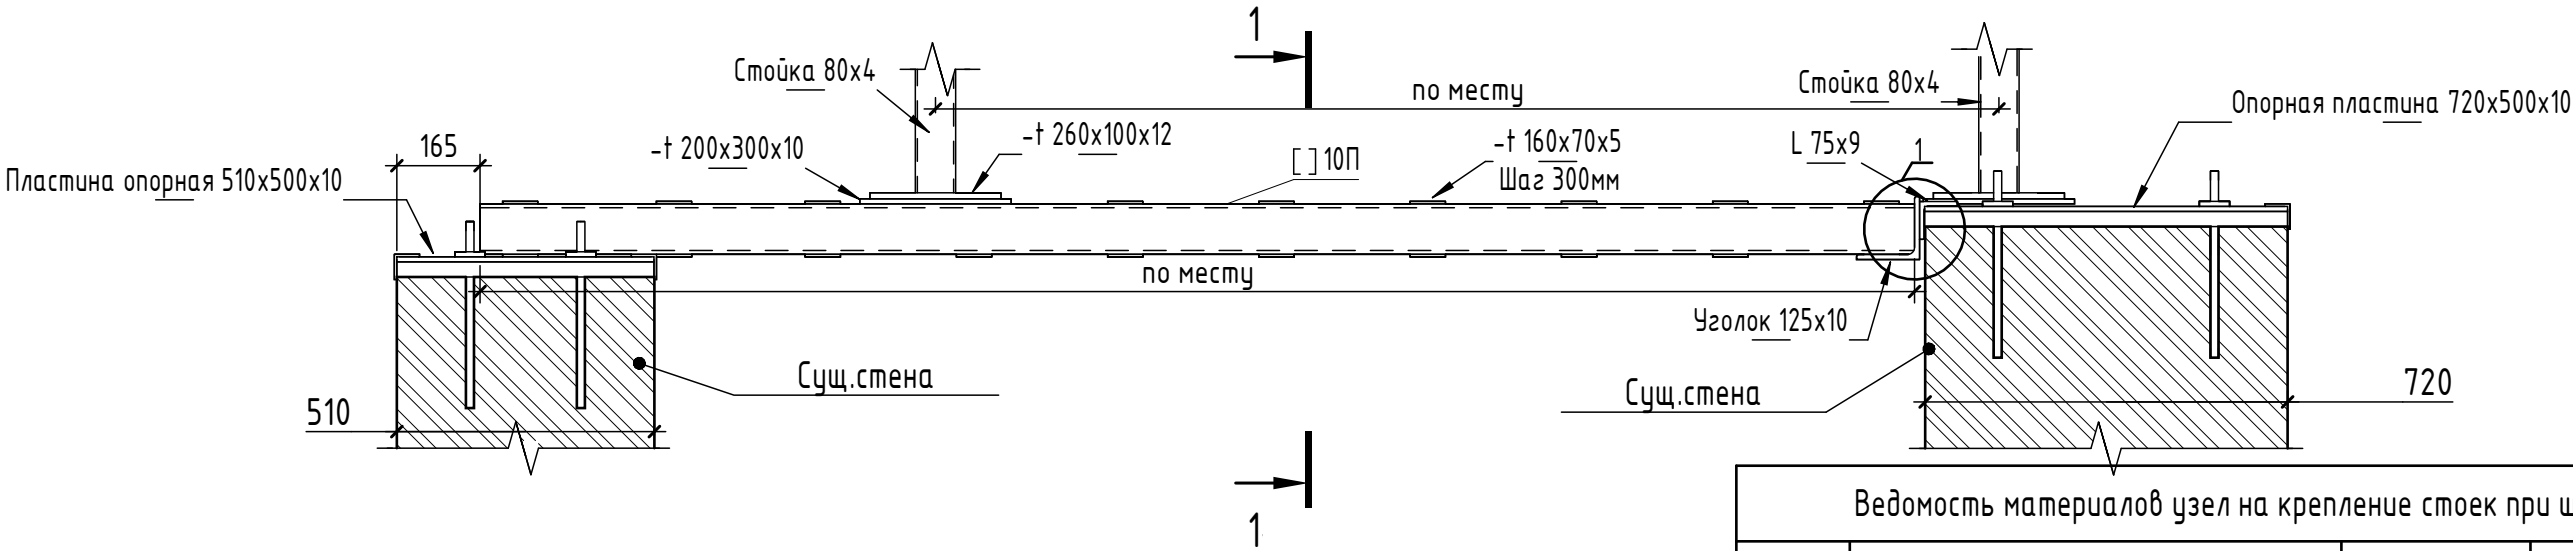

1-1.. (1 : 5)

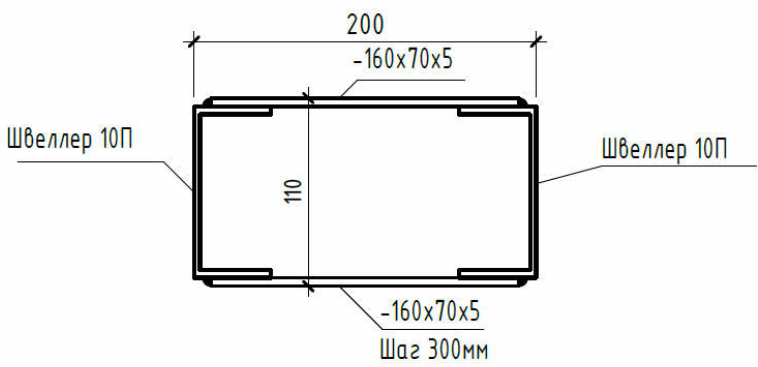

Узел 1 (1 : 5)

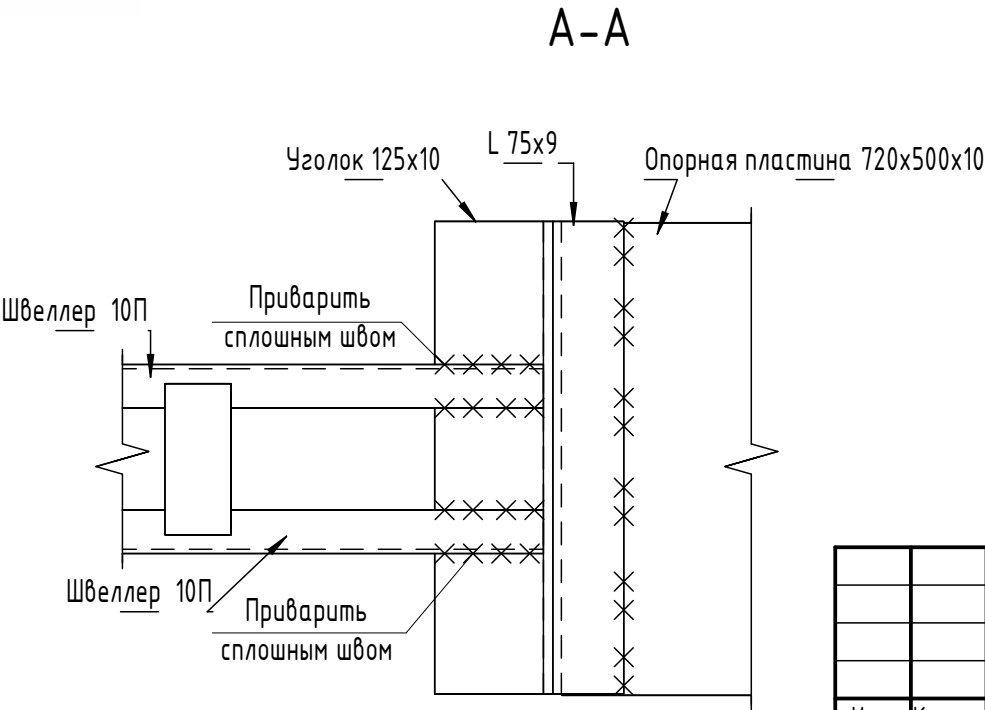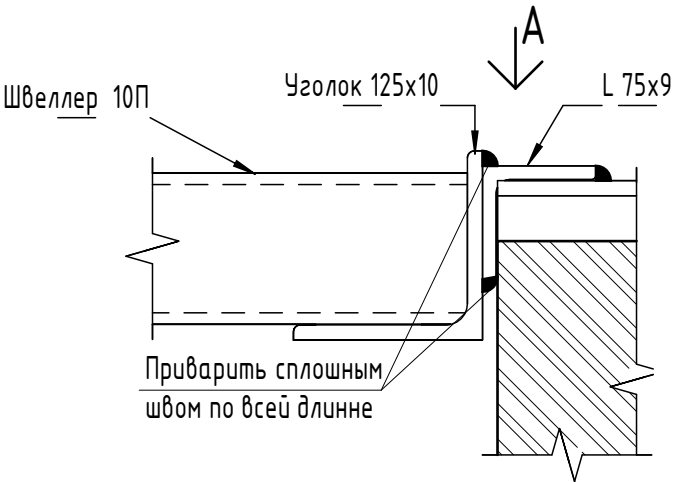

Ведомость материалов узел на крепление стоек при ширине 3м			
№П.п	Наименование	Ед.изм	Кол-во
1	Шпилька д.16	Пз.м	4
2	Пластина 50х60х10	шт	8
3	Уголок 50х5	пз.м	1.5
4	- 720х500х10	шт	1
5	-510х500х10	шт	1
6	Гайка М16	шт	8
7	Шайба.усил М16	шт	8
8	-160х70х5	шт	20
9	-200х300х10	шт	2
10	Швеллер 10П	пз.м	7
11	Уголок 125х10	пз.м	0.5
12	Уголок 75х9	пз.м	0.5


Прим:
1)Сварочные работы выполнять электродом Э42.
Катет принять по минимальной толщине свариваемой детали.
*Размер справочный уточнить по месту

Согласовано					
Взам. инв. №					
Подп. и дата					
Инв. № подл.					


						696/П-24-АНО-Р - КР			
						Капитальный ремонт Государственного бюджетного общеобразовательного учреждения города Москвы Школа №1282 Сокольники по адресу: г. Москва, ул Барболина, д.1, корп.1			
Изм.	Кол.уч.	Лист	№ док.	Подп.	Дата	Капитальный ремонт	Стадия	Лист	Листов
Разработал	Васясин.А.А						Р	55	
Проверил	Головина								
ГАП	Гулько					Узел крепления стоек площадок оборудования вариант 3			
Норм.контроль	Выходова								

Создано	
Внесено	
Подп.	
Изм. № подл.	


План опорных пластин и стоек под площадку Пл-1 (1 : 20)

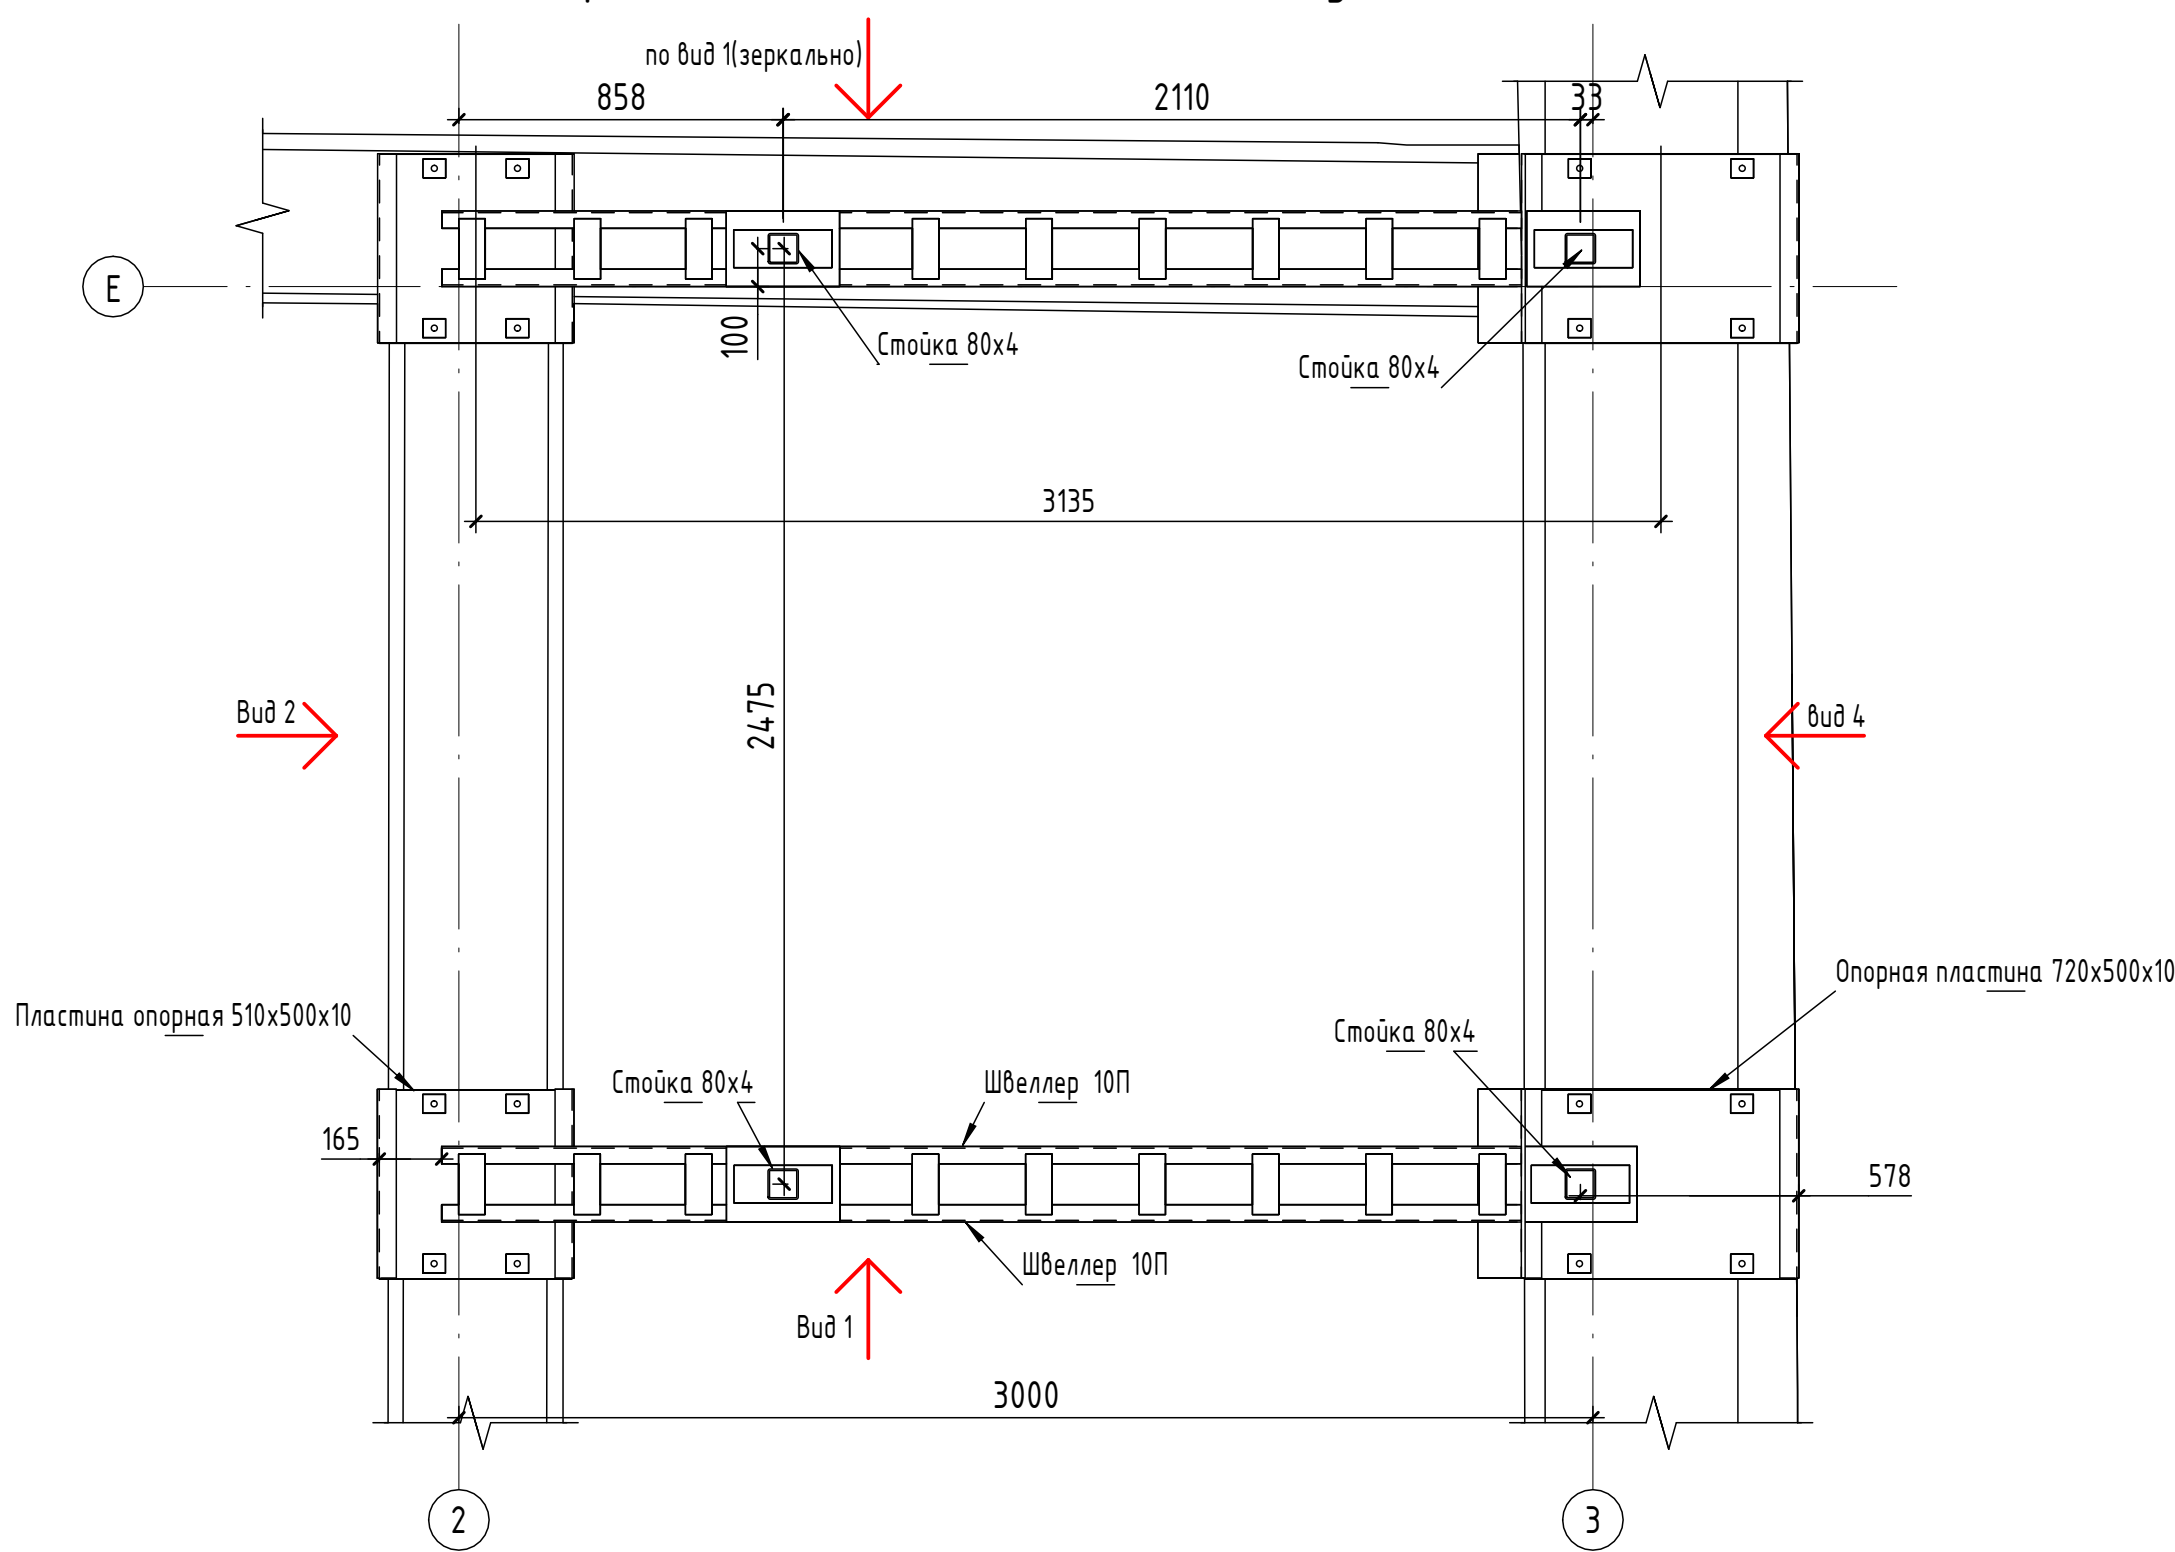


Вид 3(Площадка под настил) (1 : 20)

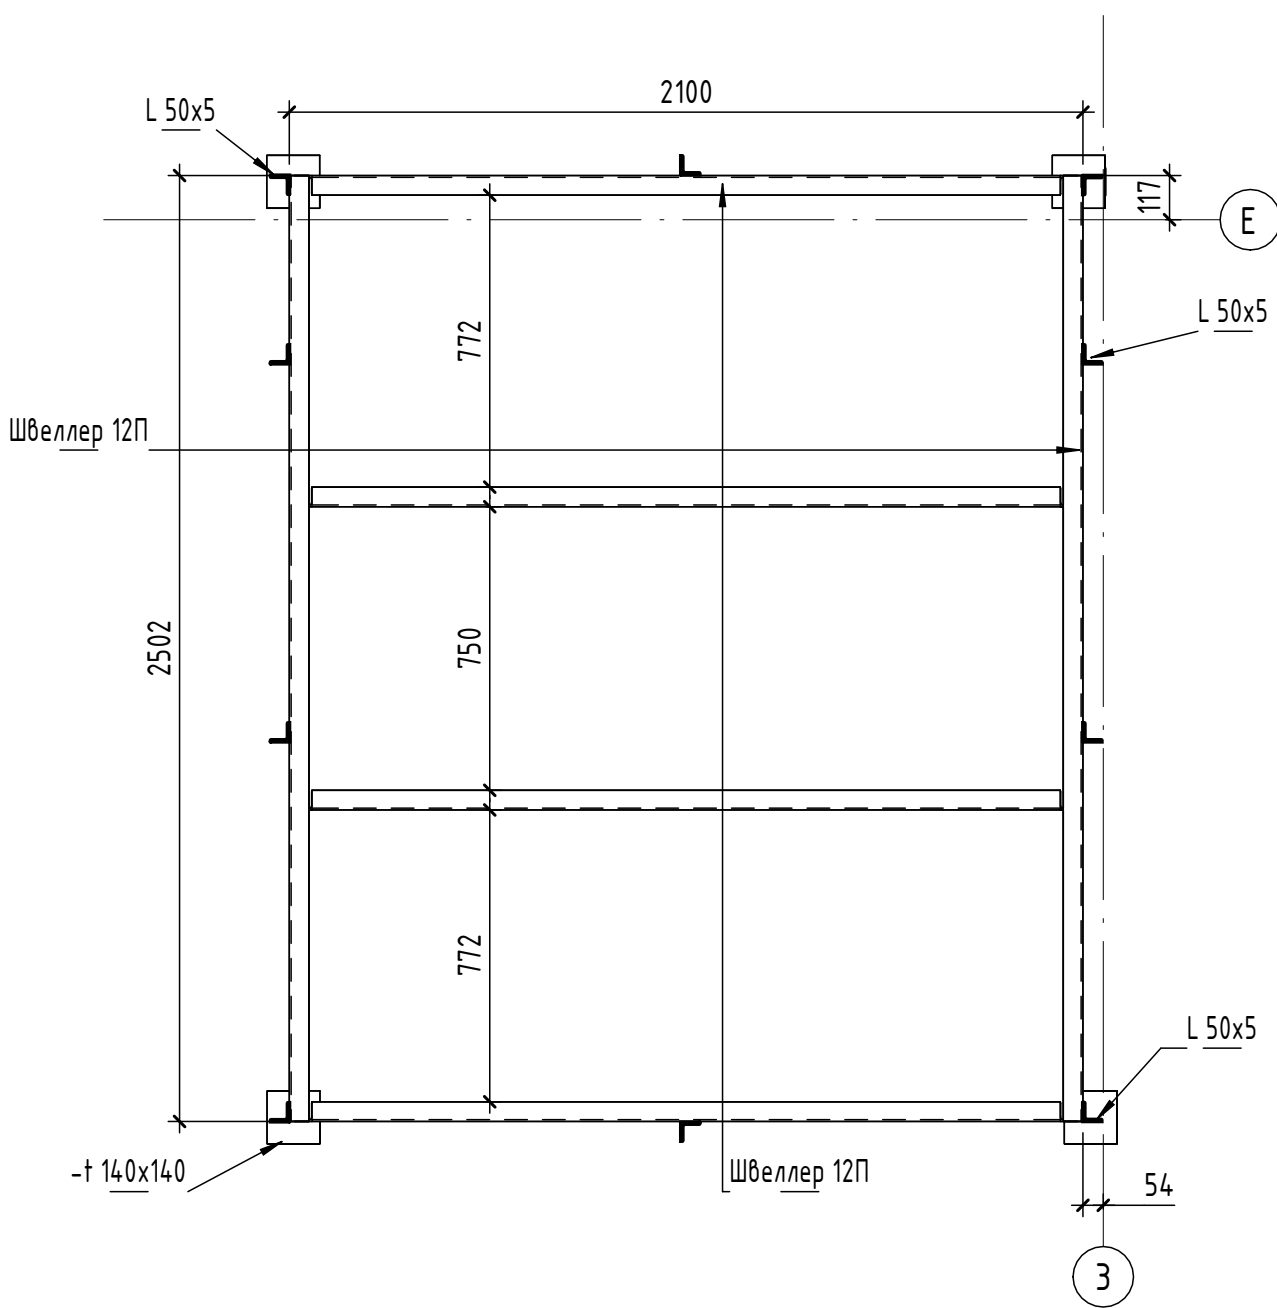


Вид 1 (1 : 20)

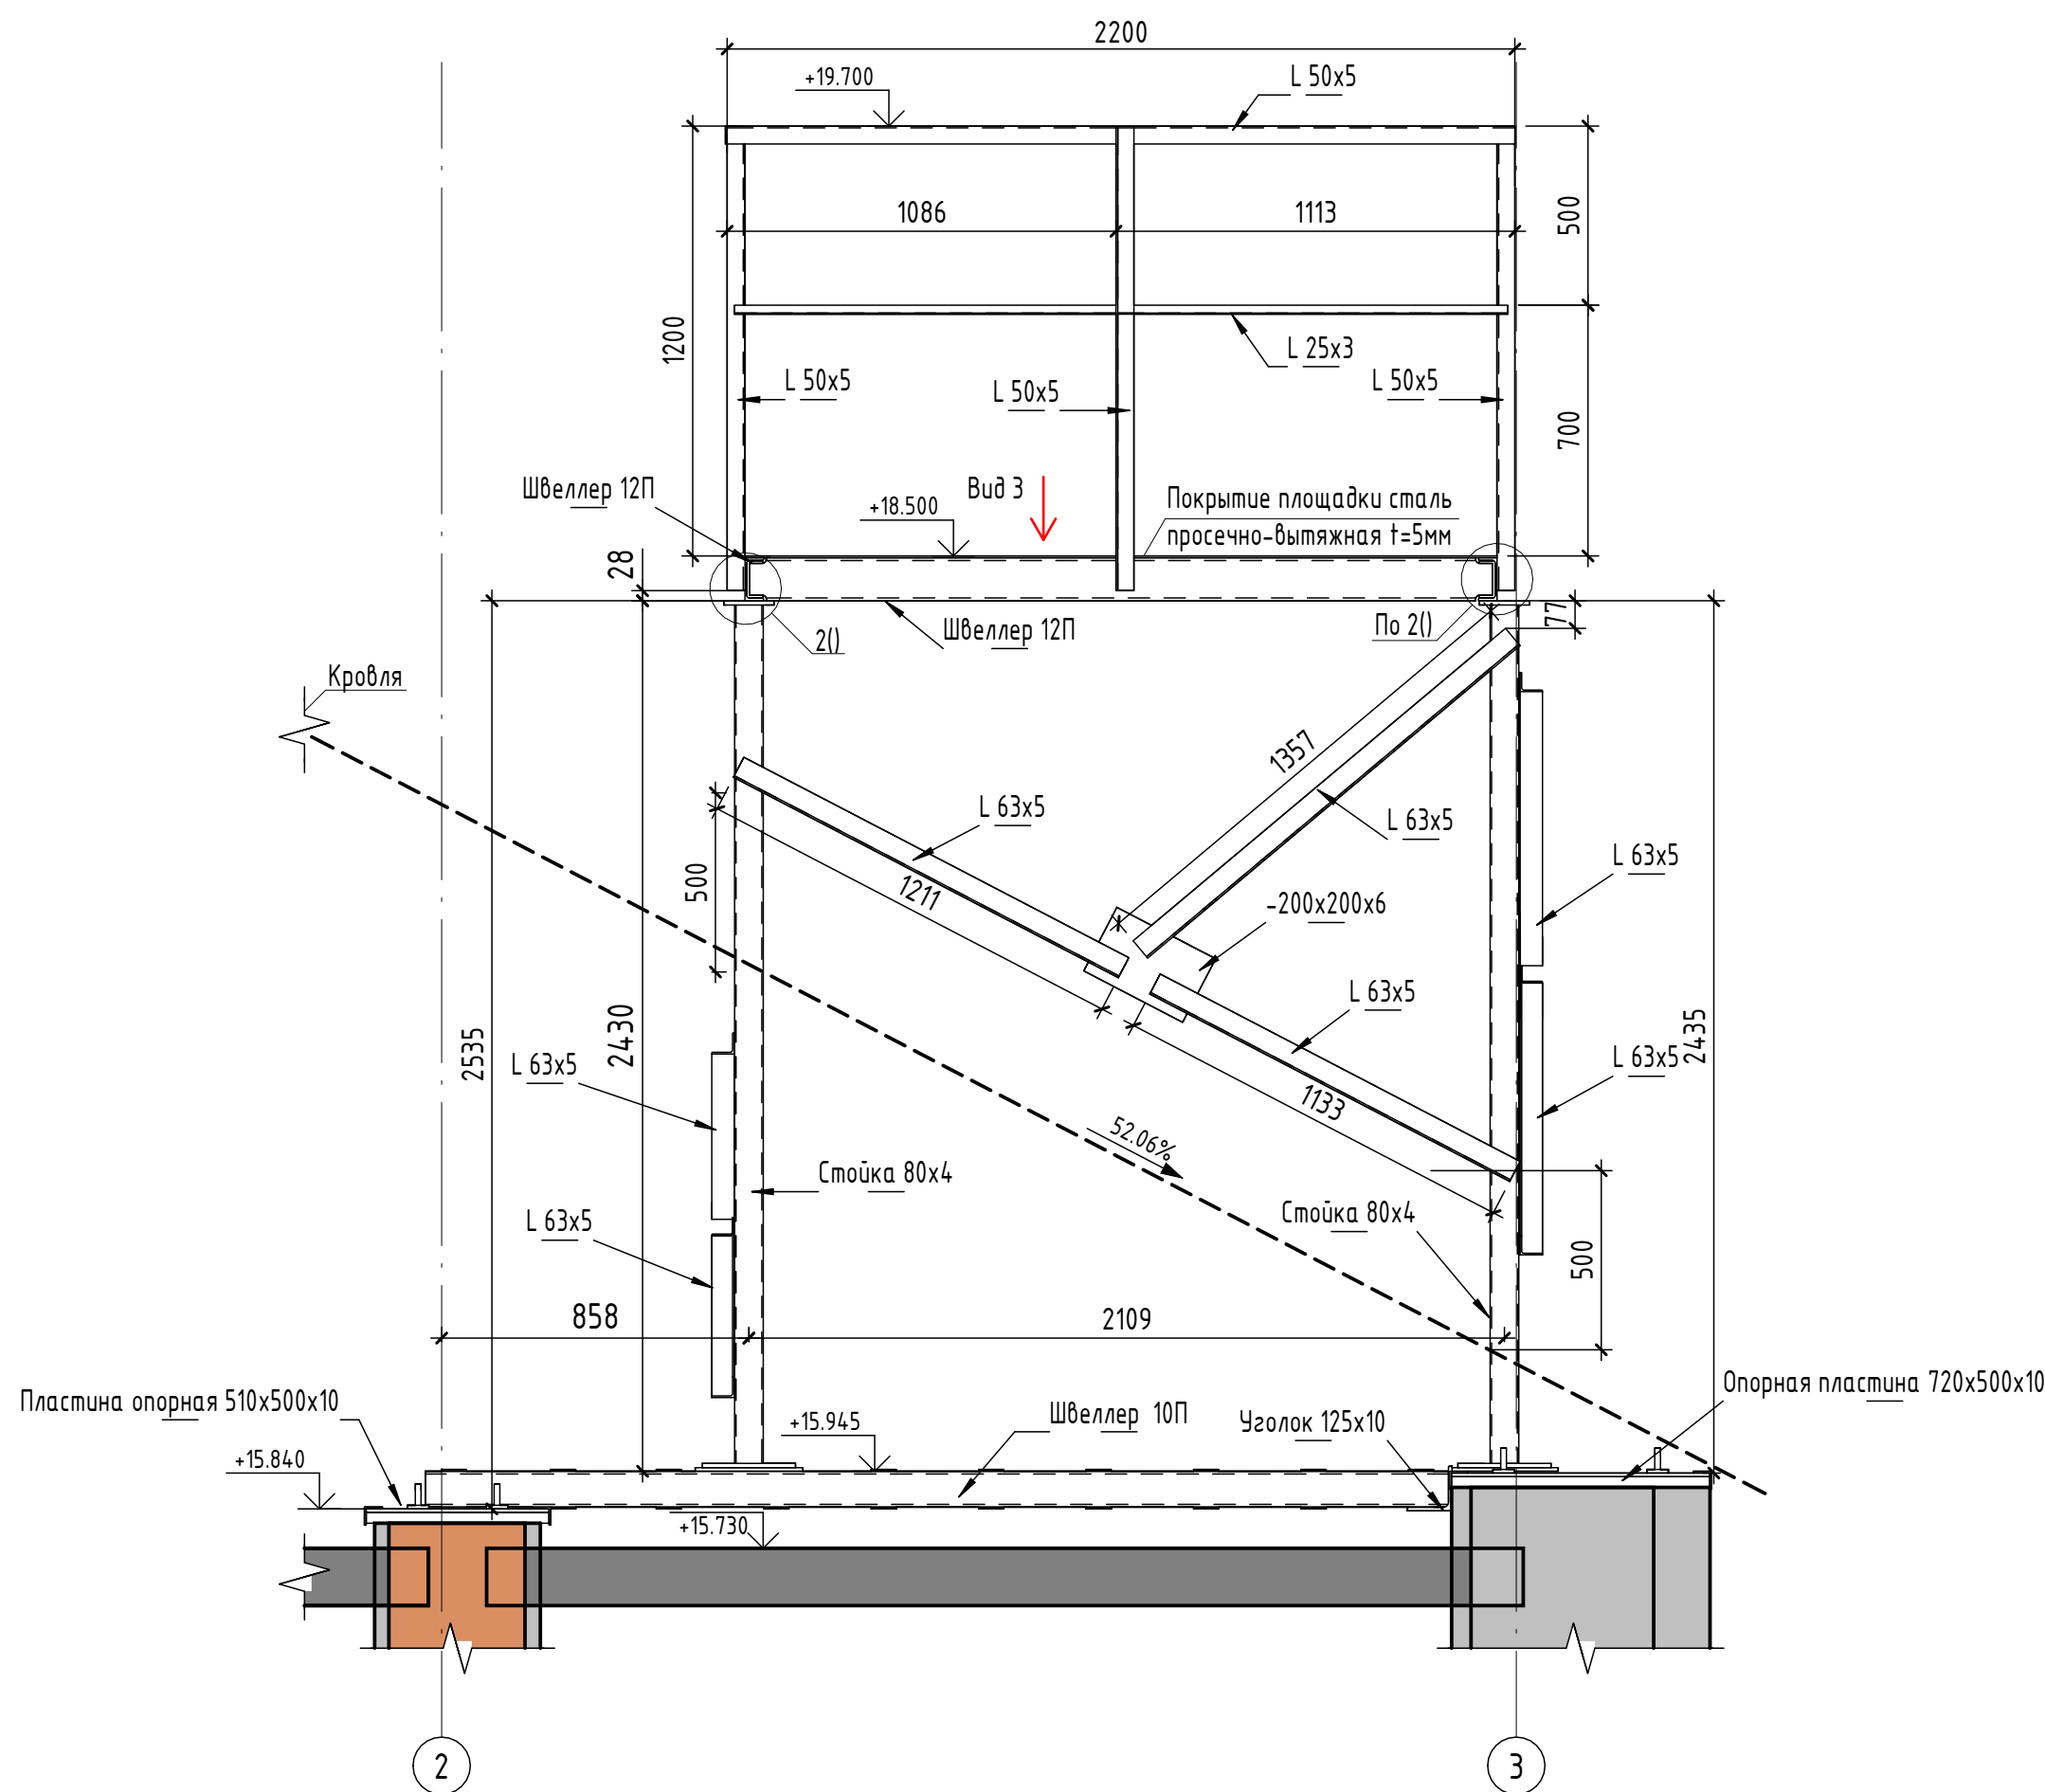

Вид 2 (1 : 20)

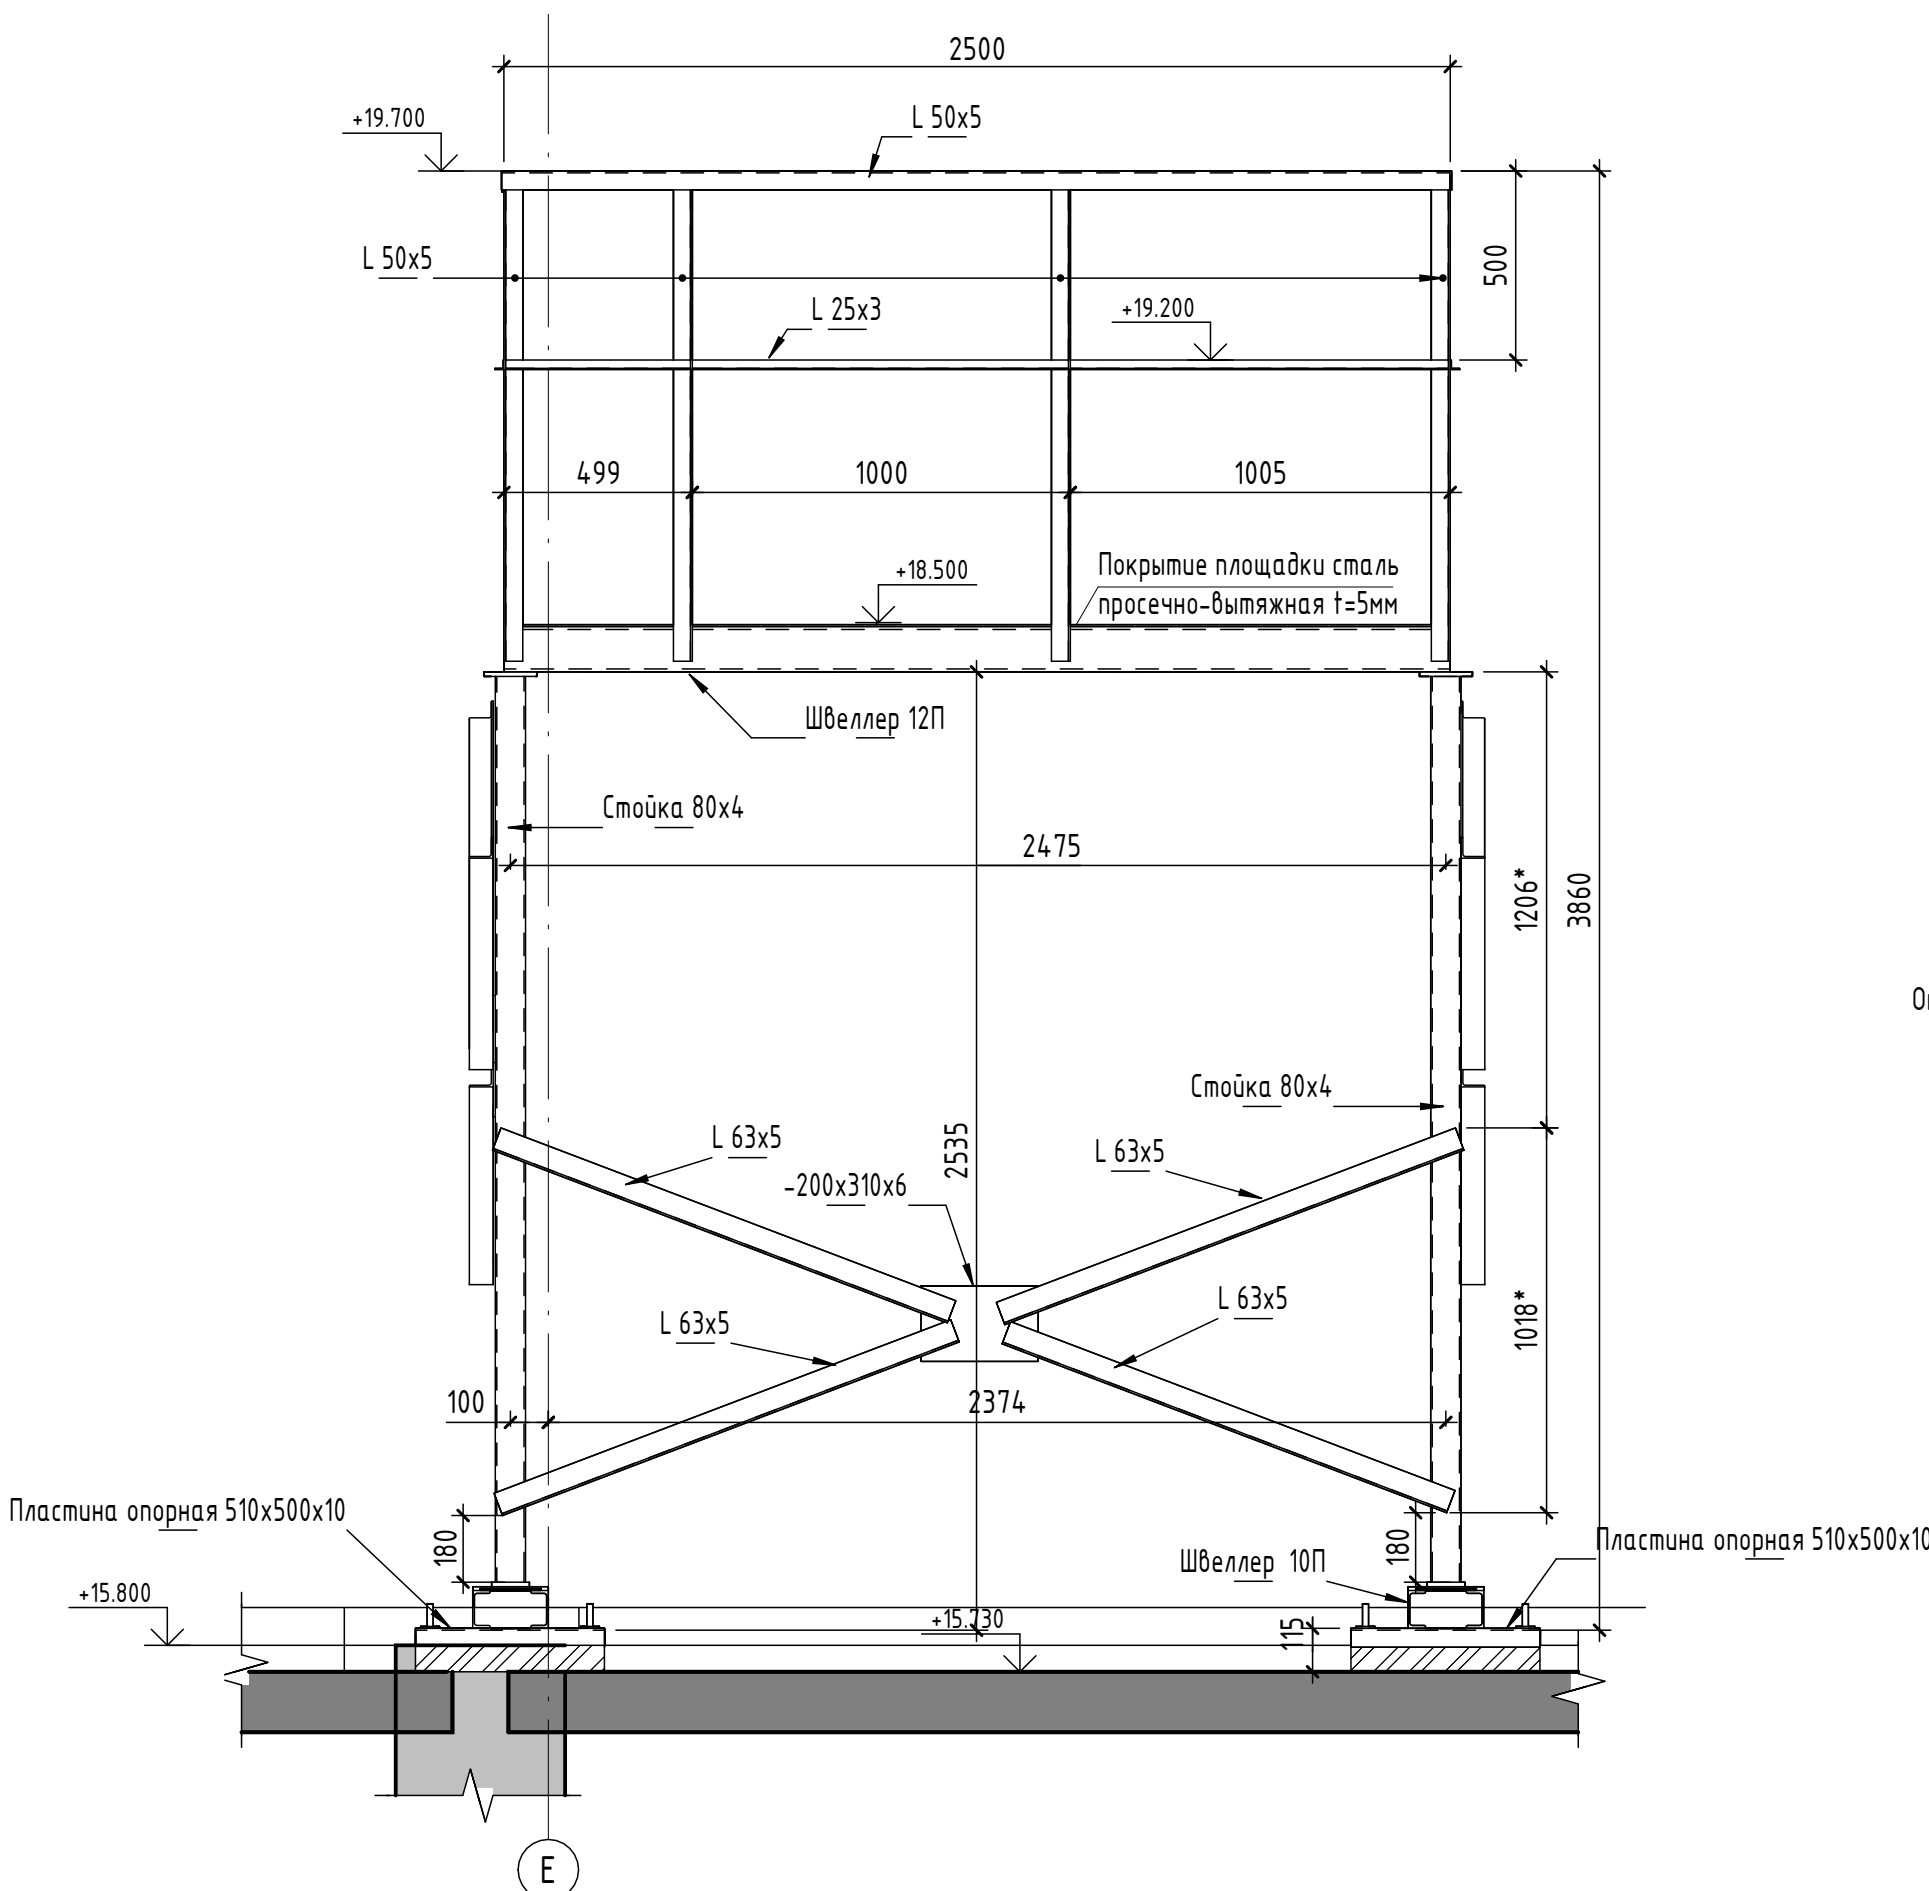

Вид 4 (1 : 20)

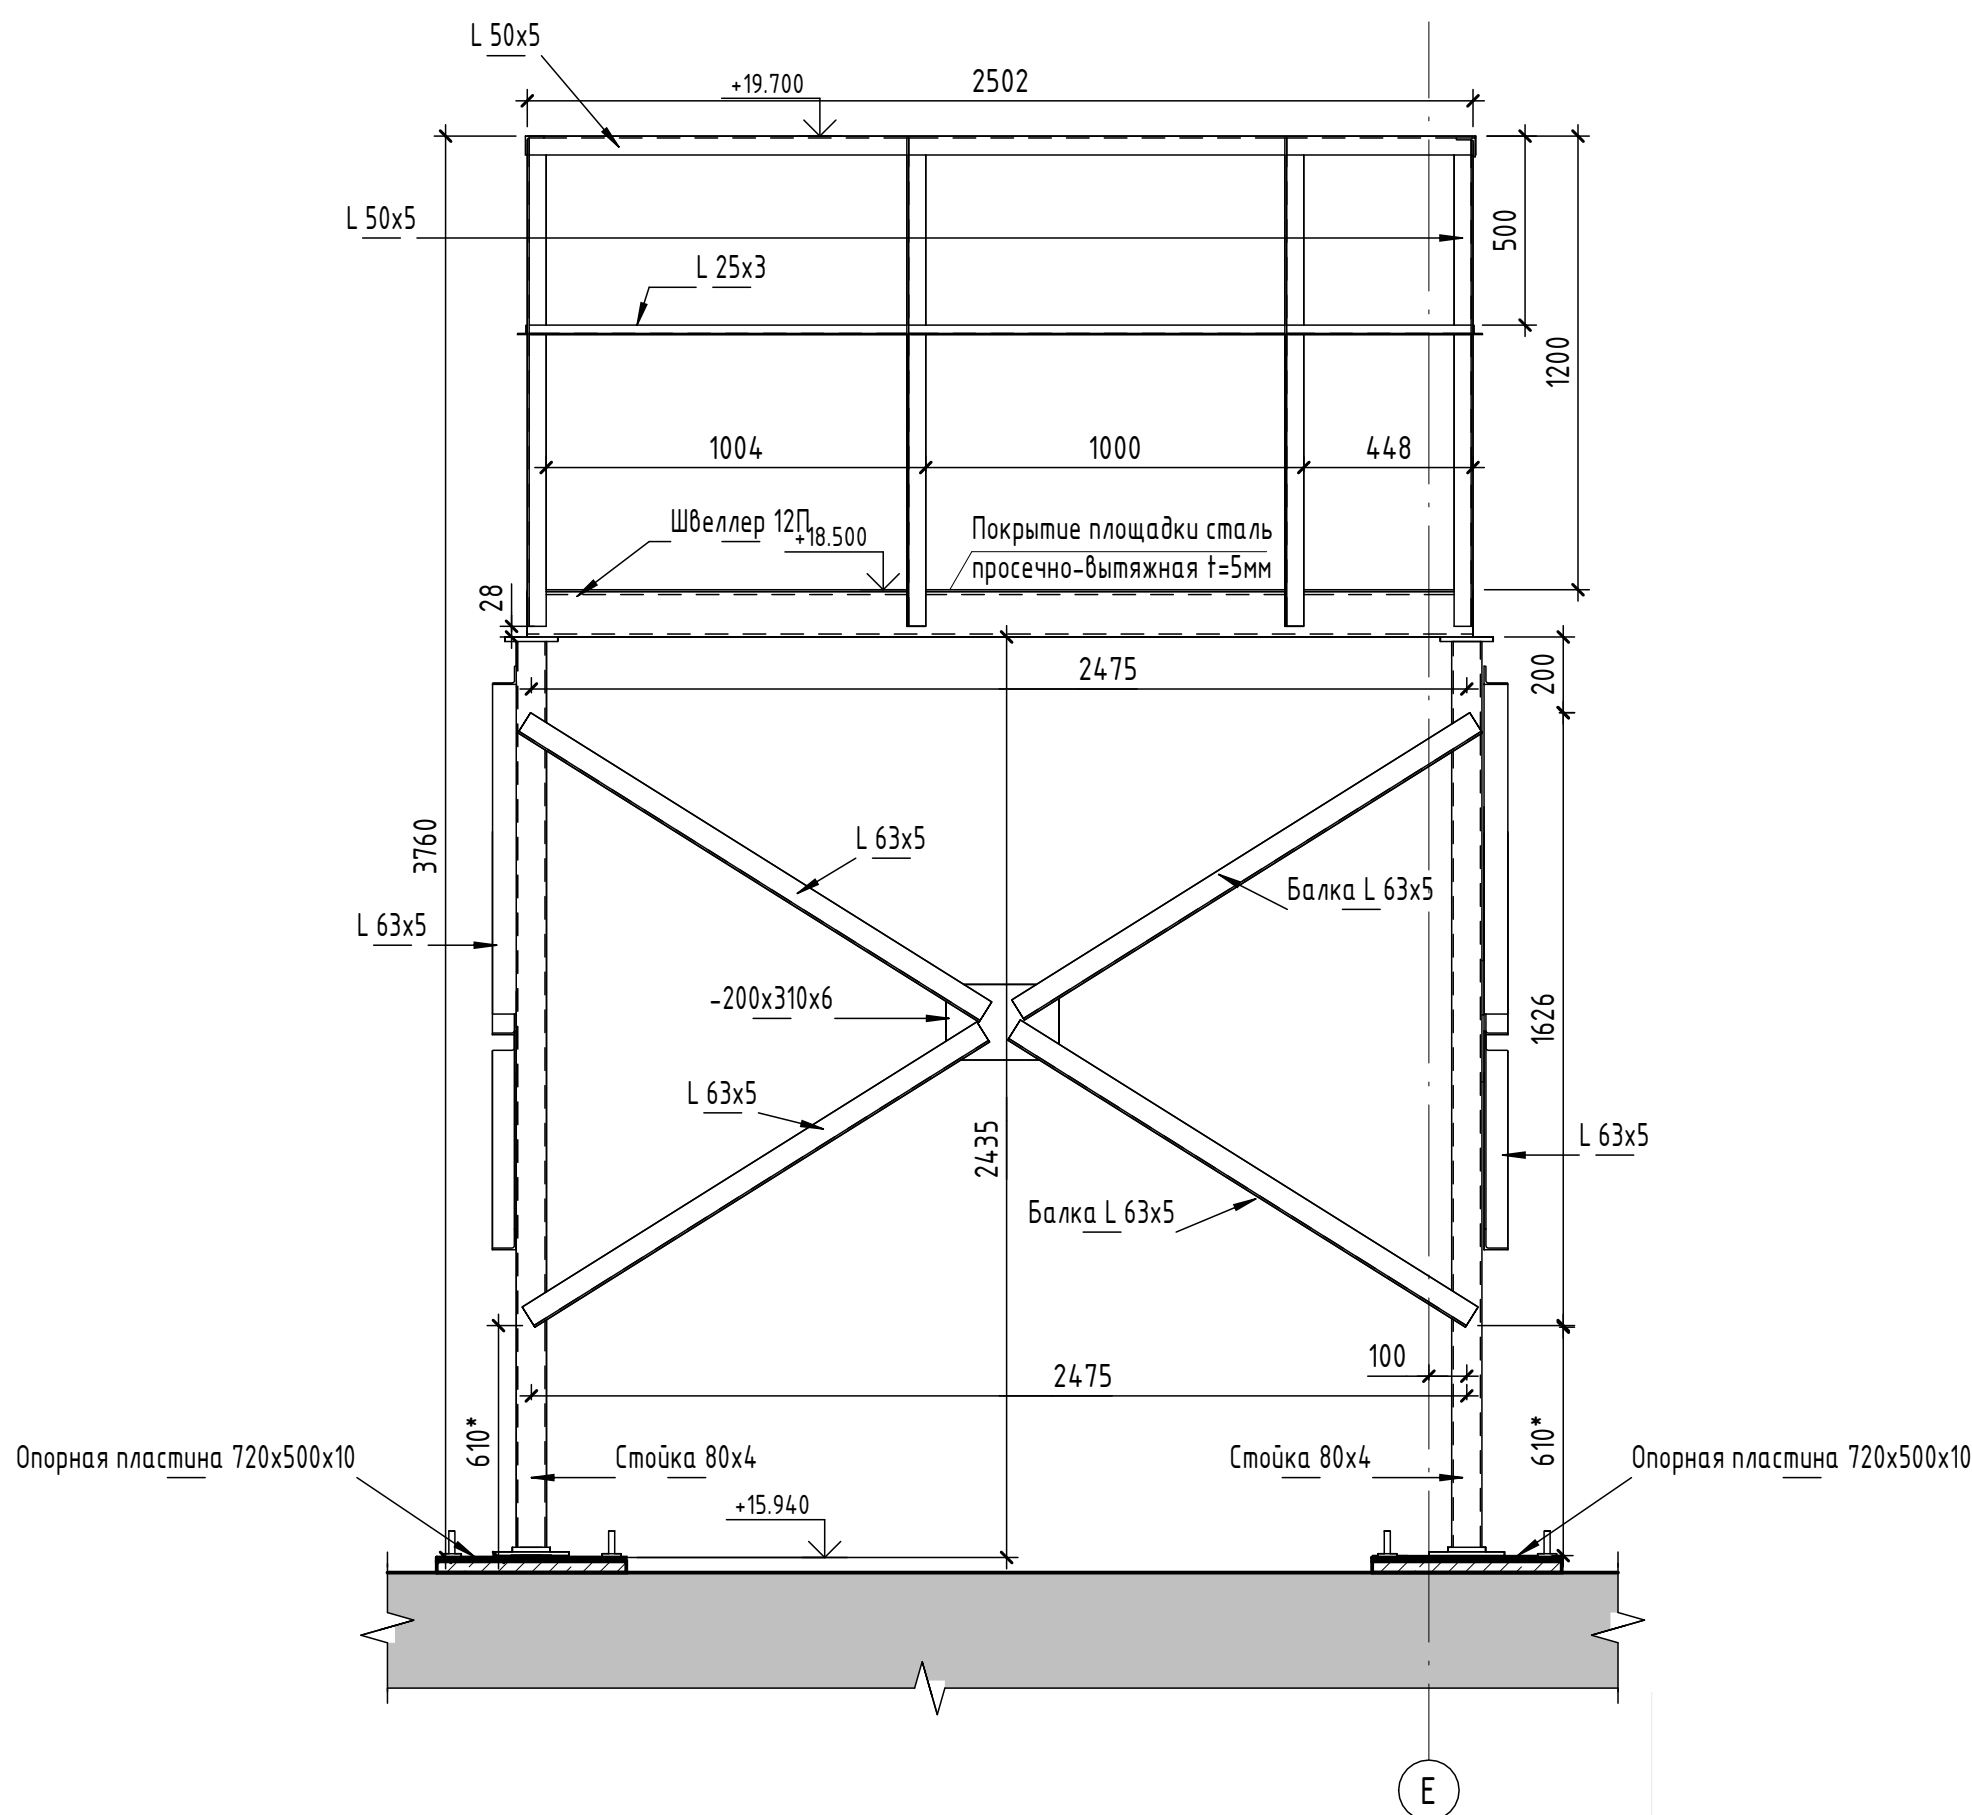


Прим:
1)В спецификацию не входят площадки.
Площадки показаны условно.
2)Размеры раскосов уточнять по месту. Они не должны пересекаться с кровельным пирогом.
*Размеры уточнить по месту


						696/П-24-АНО-Р - КР
						Капитальный ремонт Государственного бюджетного общеобразовательного учреждения города Москвы Школа №1282 Сокольники по адресу: г. Москва, ул Барболина, д.1, корп.1
Изм.	Жолч.	Лист	№ док.	Подп.	Дата	
Разработал	Василин А.А					
Проверил	Головина					
ГАП	Гулько					
Норм. контроль	Выходова					
						Капитальный ремонт
						Металконстр под площадку Пл-1
						ООО "ПРОЕКТ+"
						Формат А1А

Ведомость материалов на площадку Пл-1


№п.п	Обозначение	Наименование	Общая длина(п.м)	Кол-во	Примечание
	ГОСТ 19903-2015	-200x200x6	0.6	2	
	ГОСТ 19903-2015	-200x310x6	0.6	2	
	ГОСТ 19903-2015	-t 50x60x10	0.7	14	
	ГОСТ 19903-2015	-t 140x140	0.6	4	
	ГОСТ 19903-2015	-t 160x70x5	5.9	37	
	ГОСТ 19903-2015	-t 200x300x10	0.8	4	
	ГОСТ 19903-2015	-t 260x100x12	0.4	4	
	ГОСТ 19903-2015	-t 510x500x10	1	2	
	ГОСТ 19903-2015	-t 720x500x10	1	2	
	Труба ГОСТ 8639-82	80x80x4	9.6	4	
	ГОСТ8509-93	L 50x5	10	20	
	ГОСТ8509-93	L 63x5	18.3	14	
	ГОСТ8509-93	Уголок 125x10	1	2	
	ГОСТ 8240-97	Швеллер 10П	11.4	4	
	ГОСТ 22042-76	Шпилька М16	5.2	14	

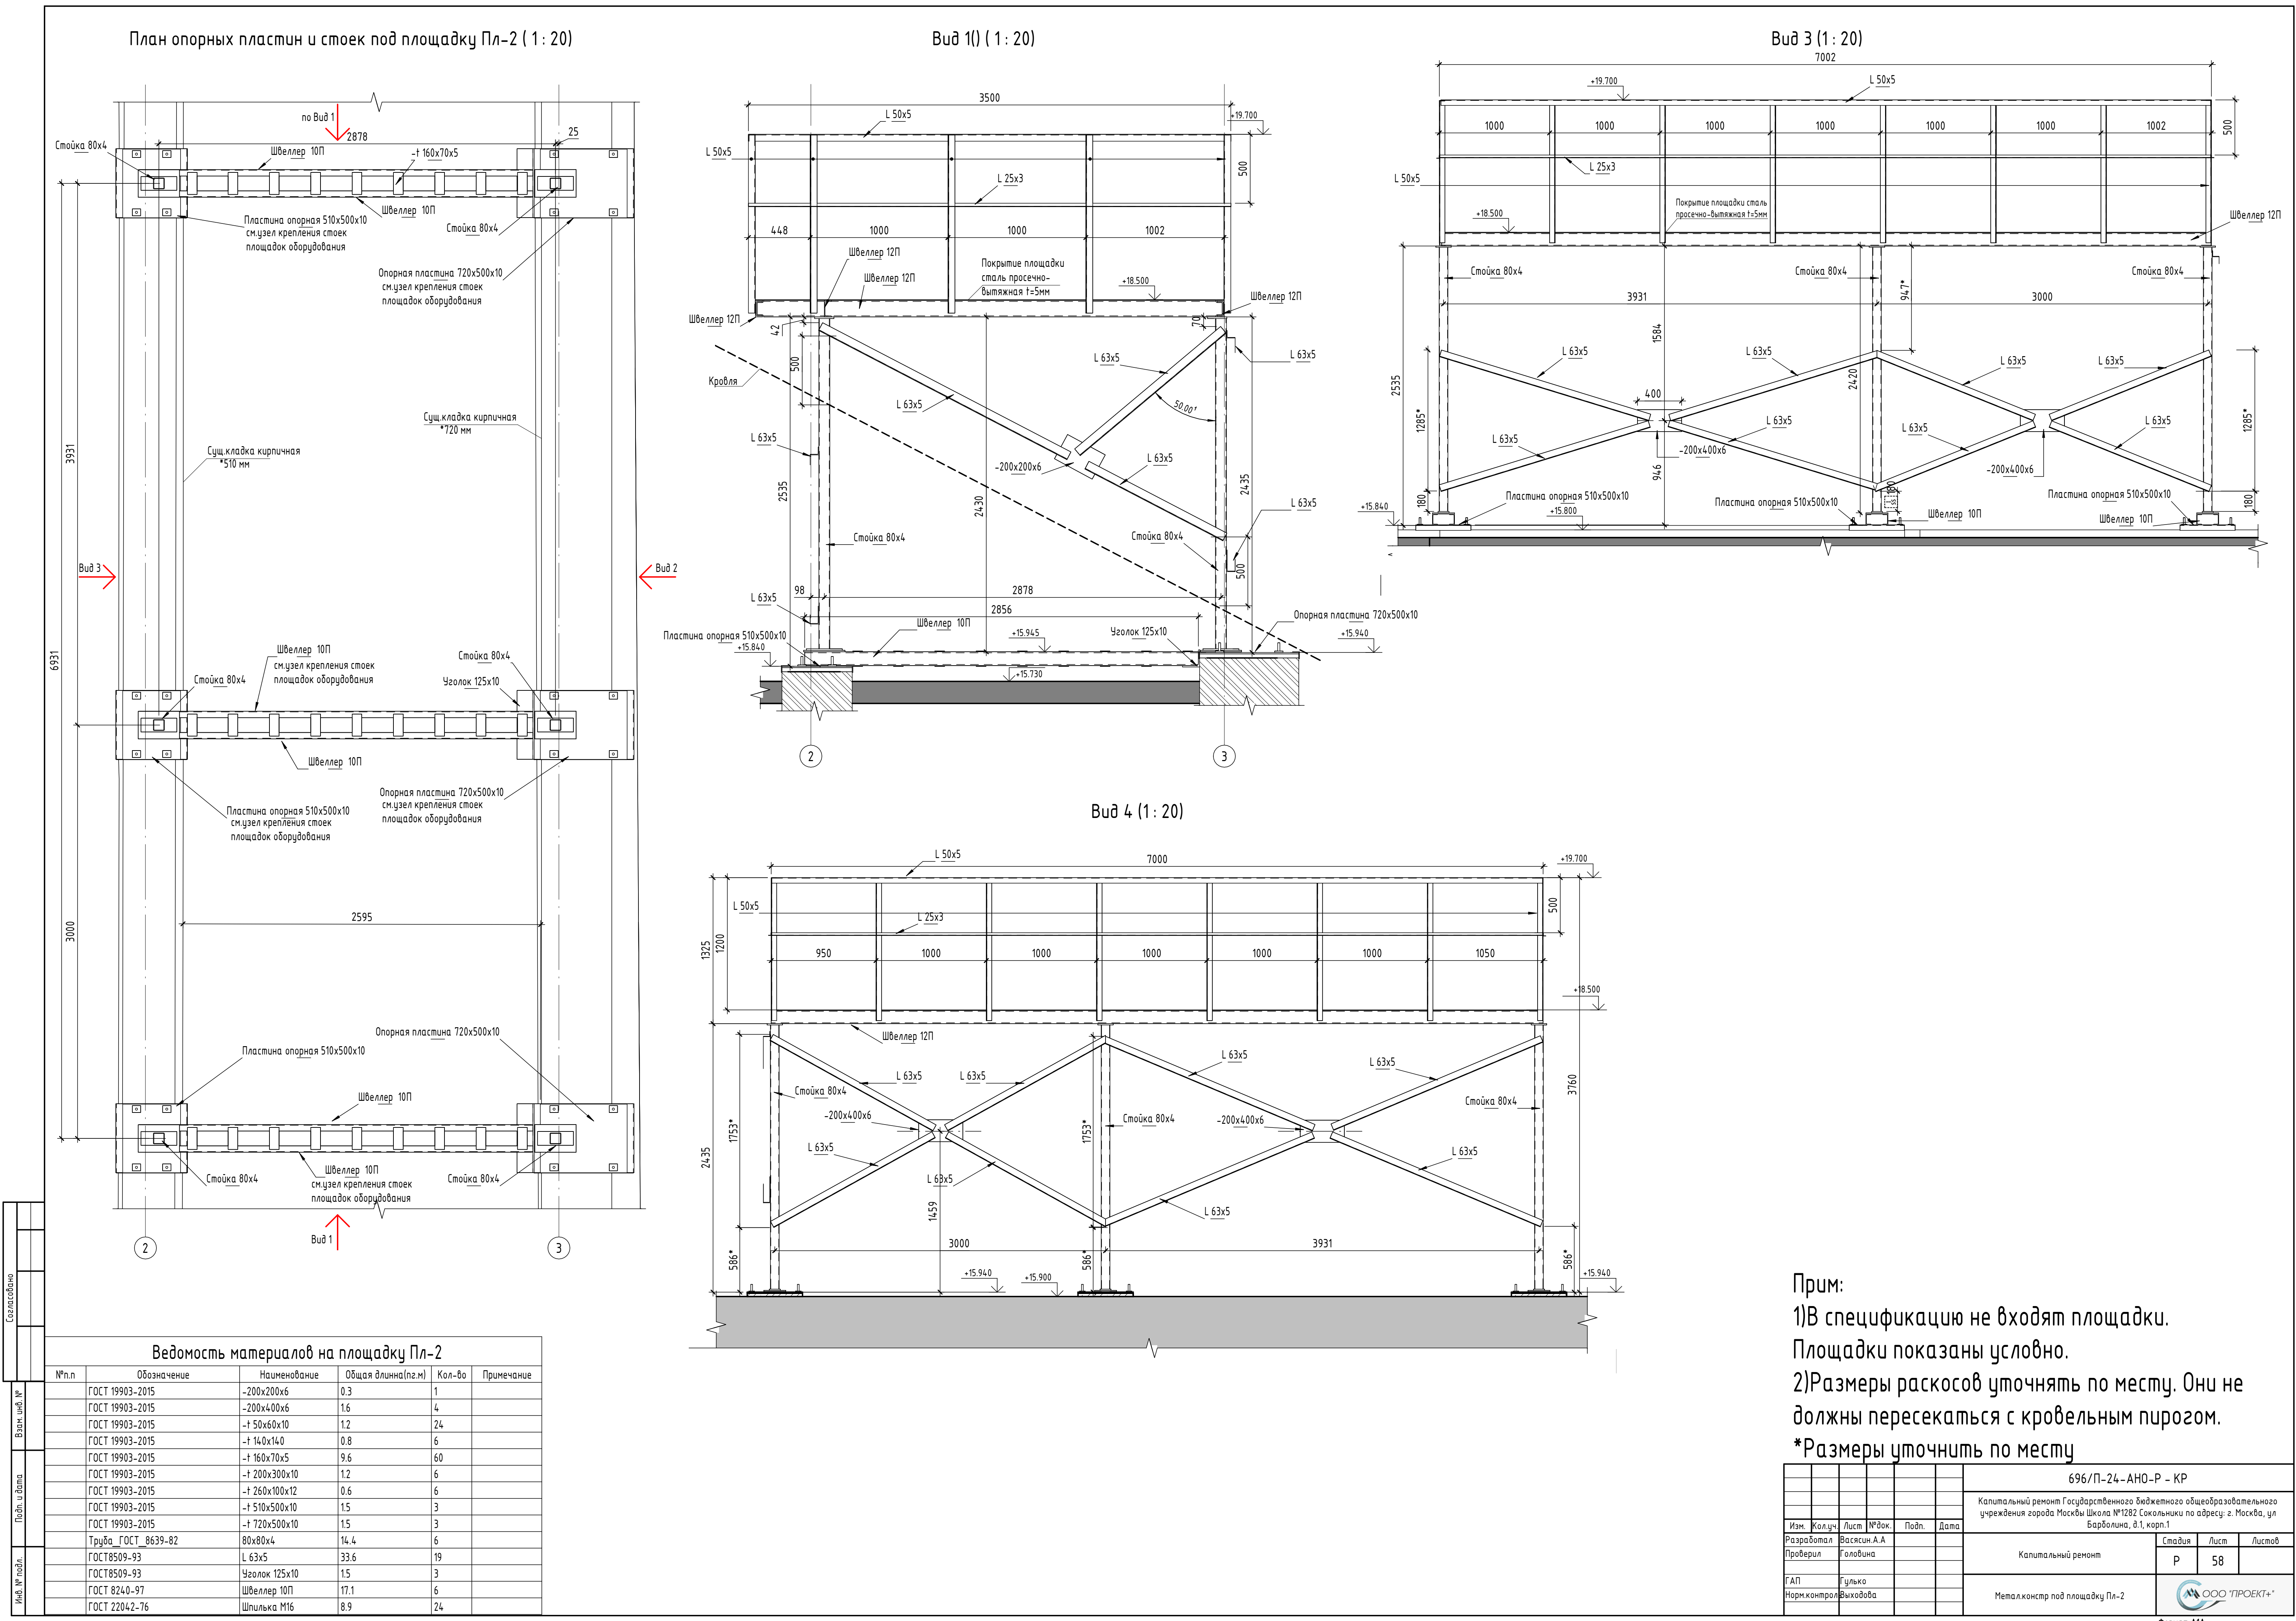


План опорных пластин и стоек под площадку Пл-7 (1 : 20)

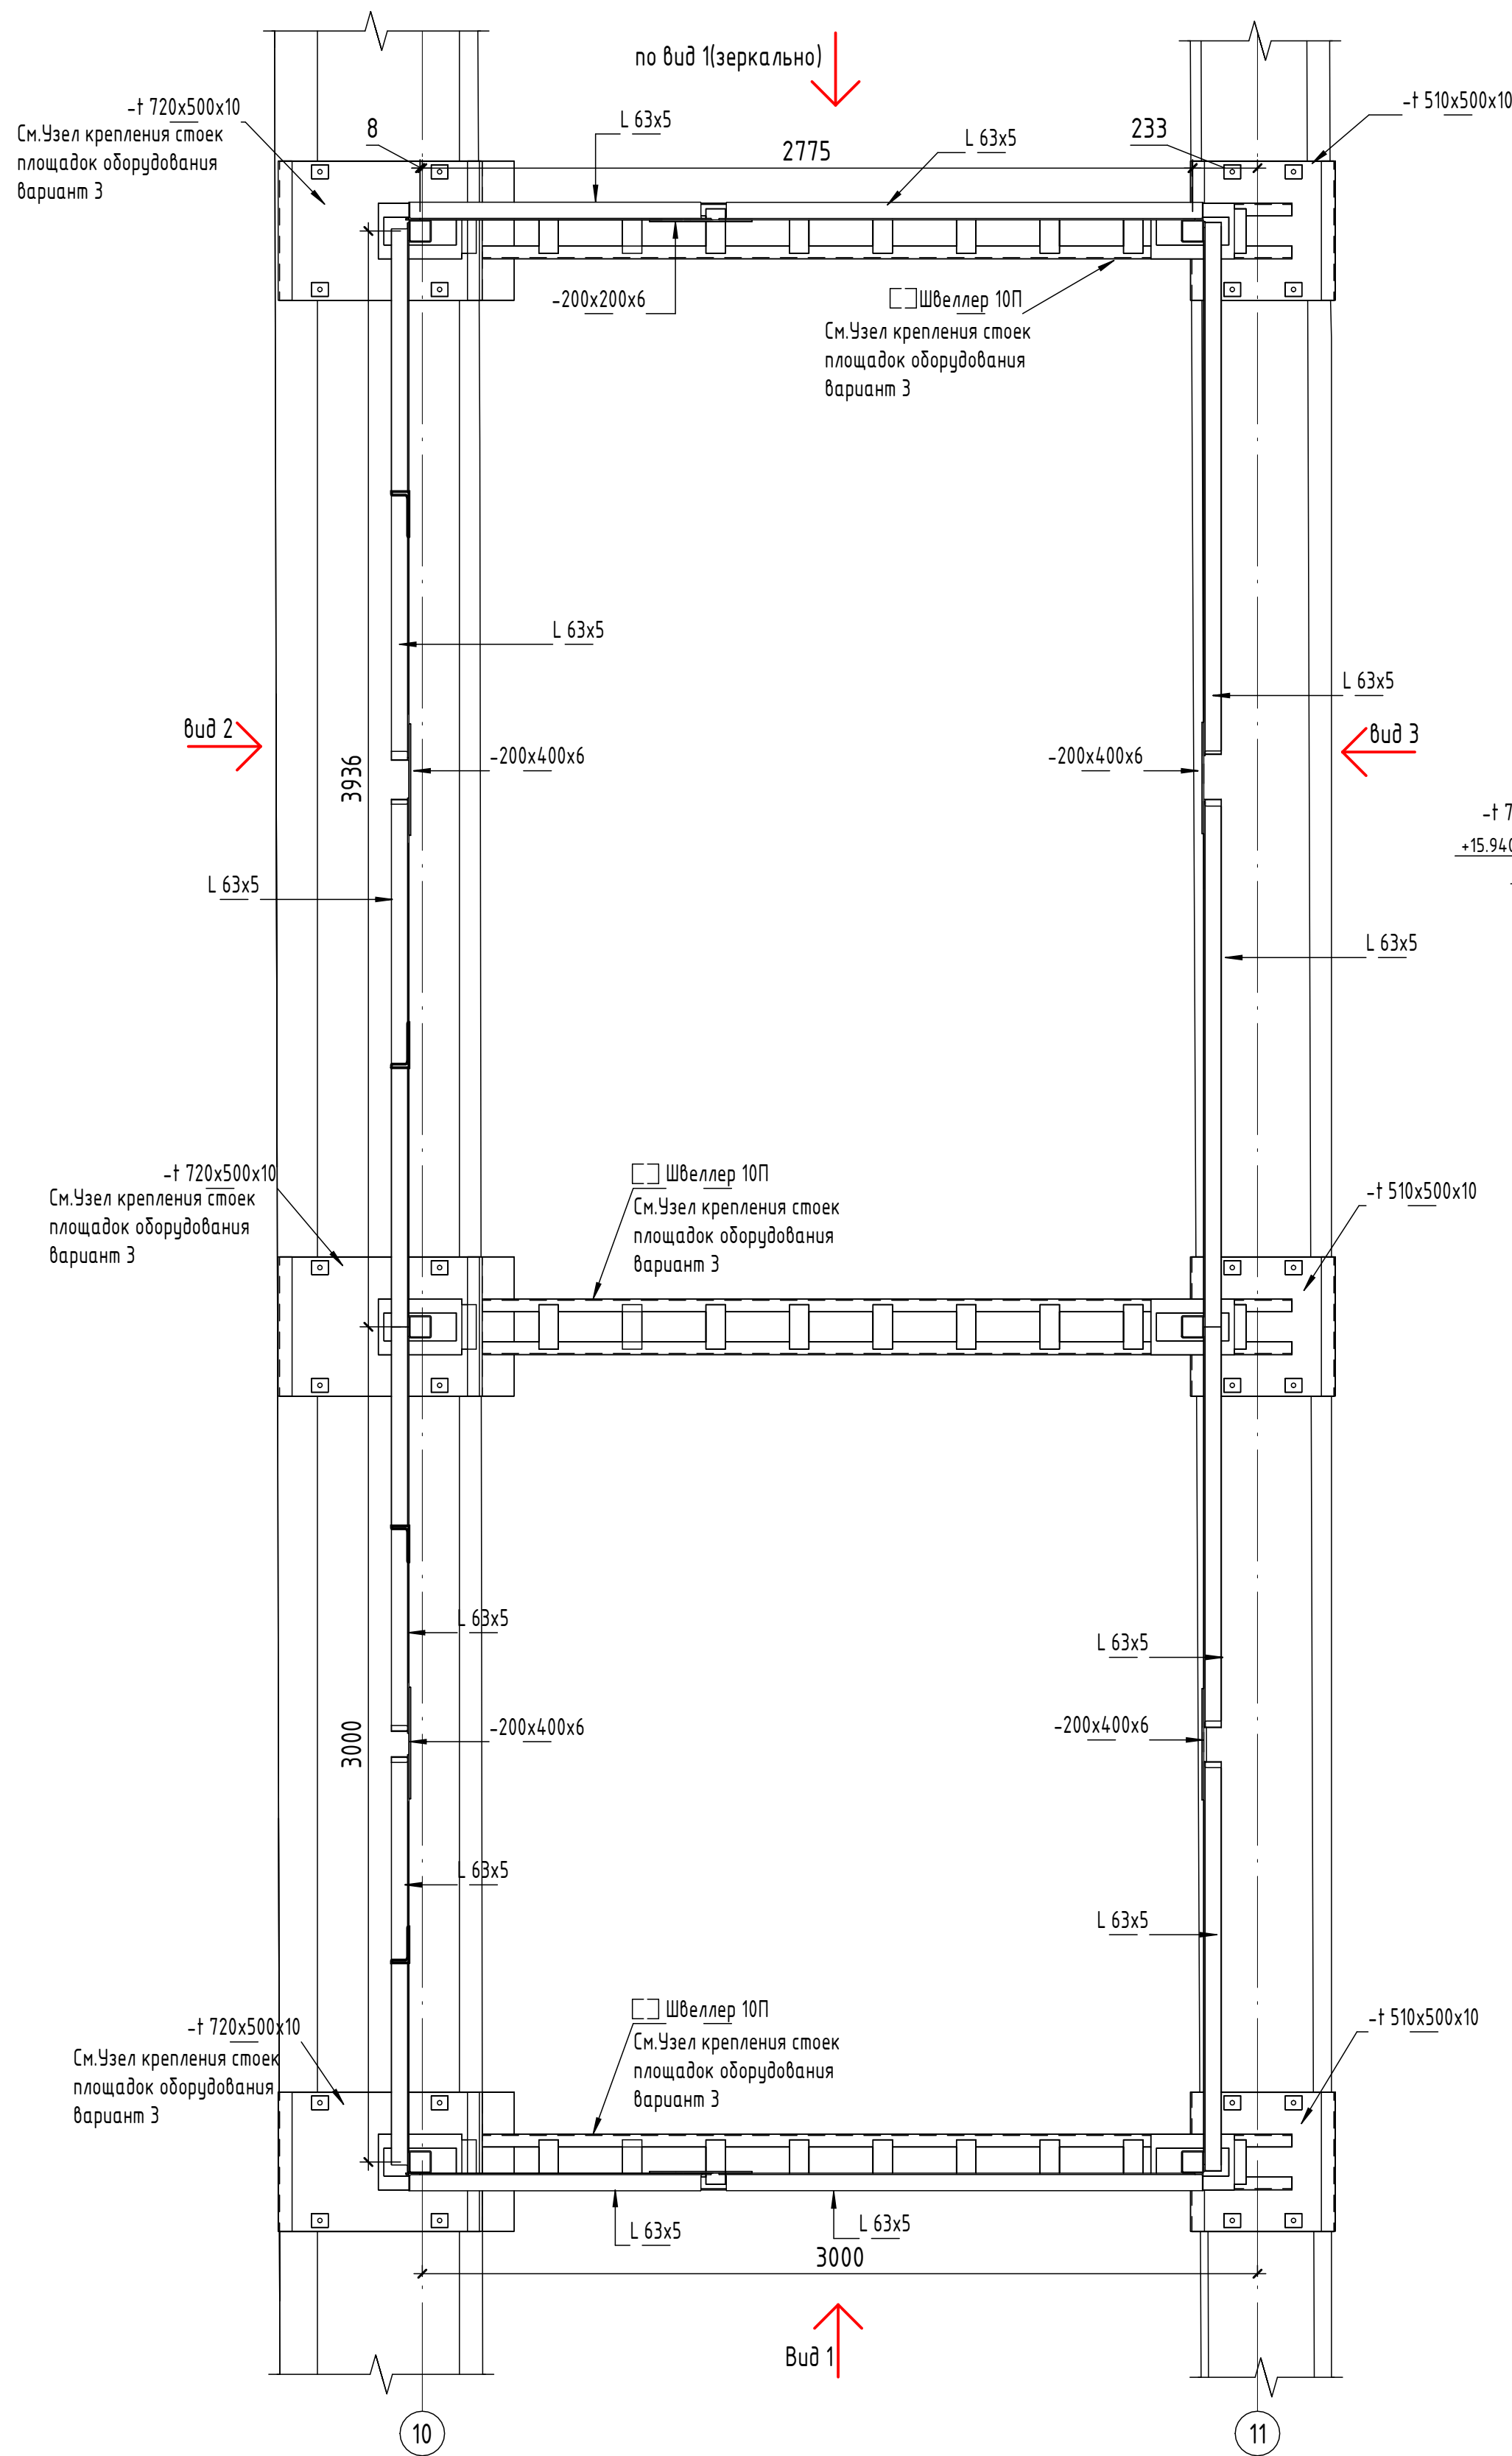


Вид 1 (1 : 20)

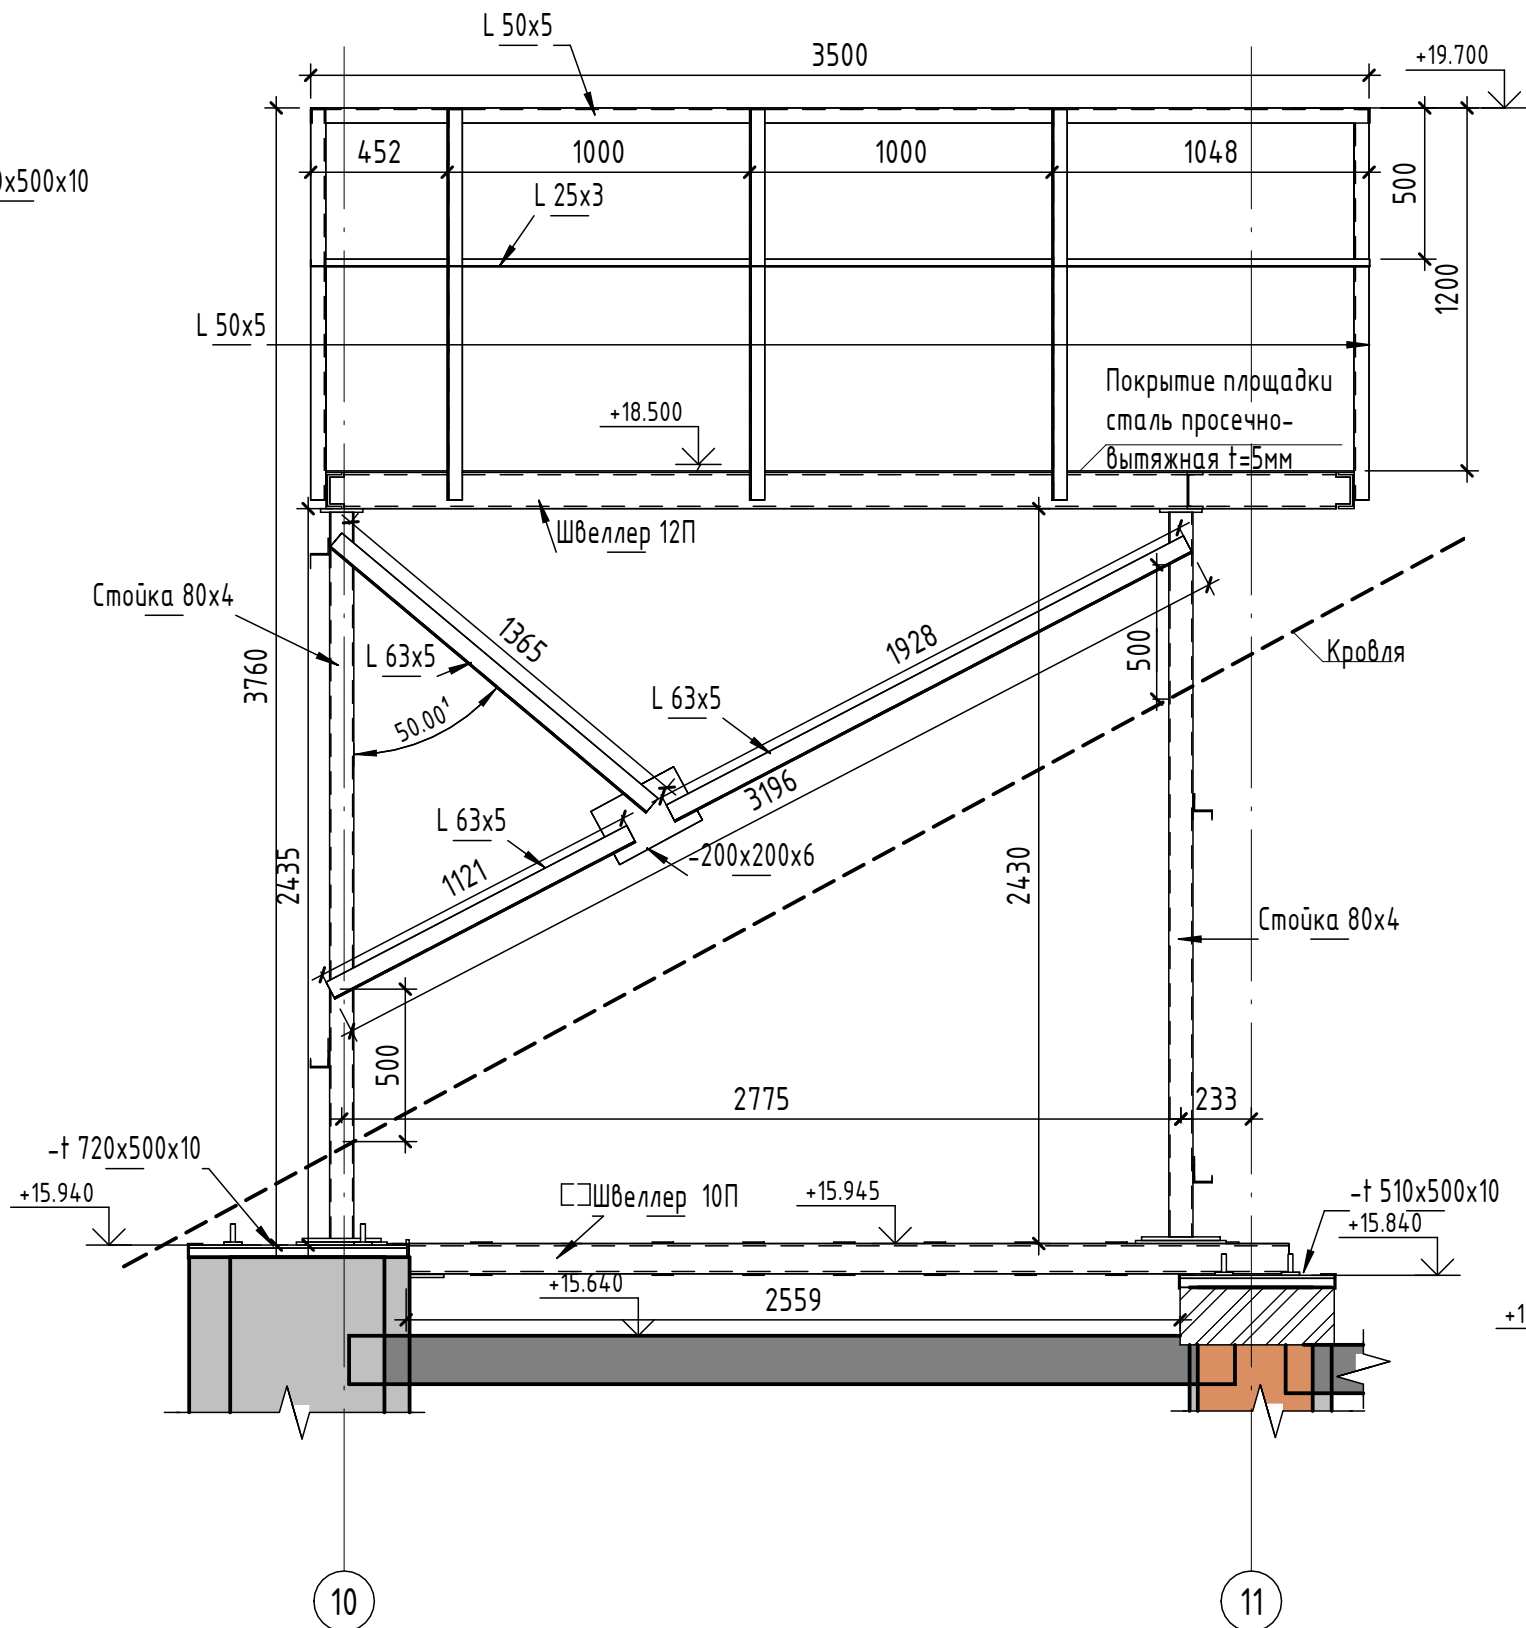

Вид 2 (1 : 20)

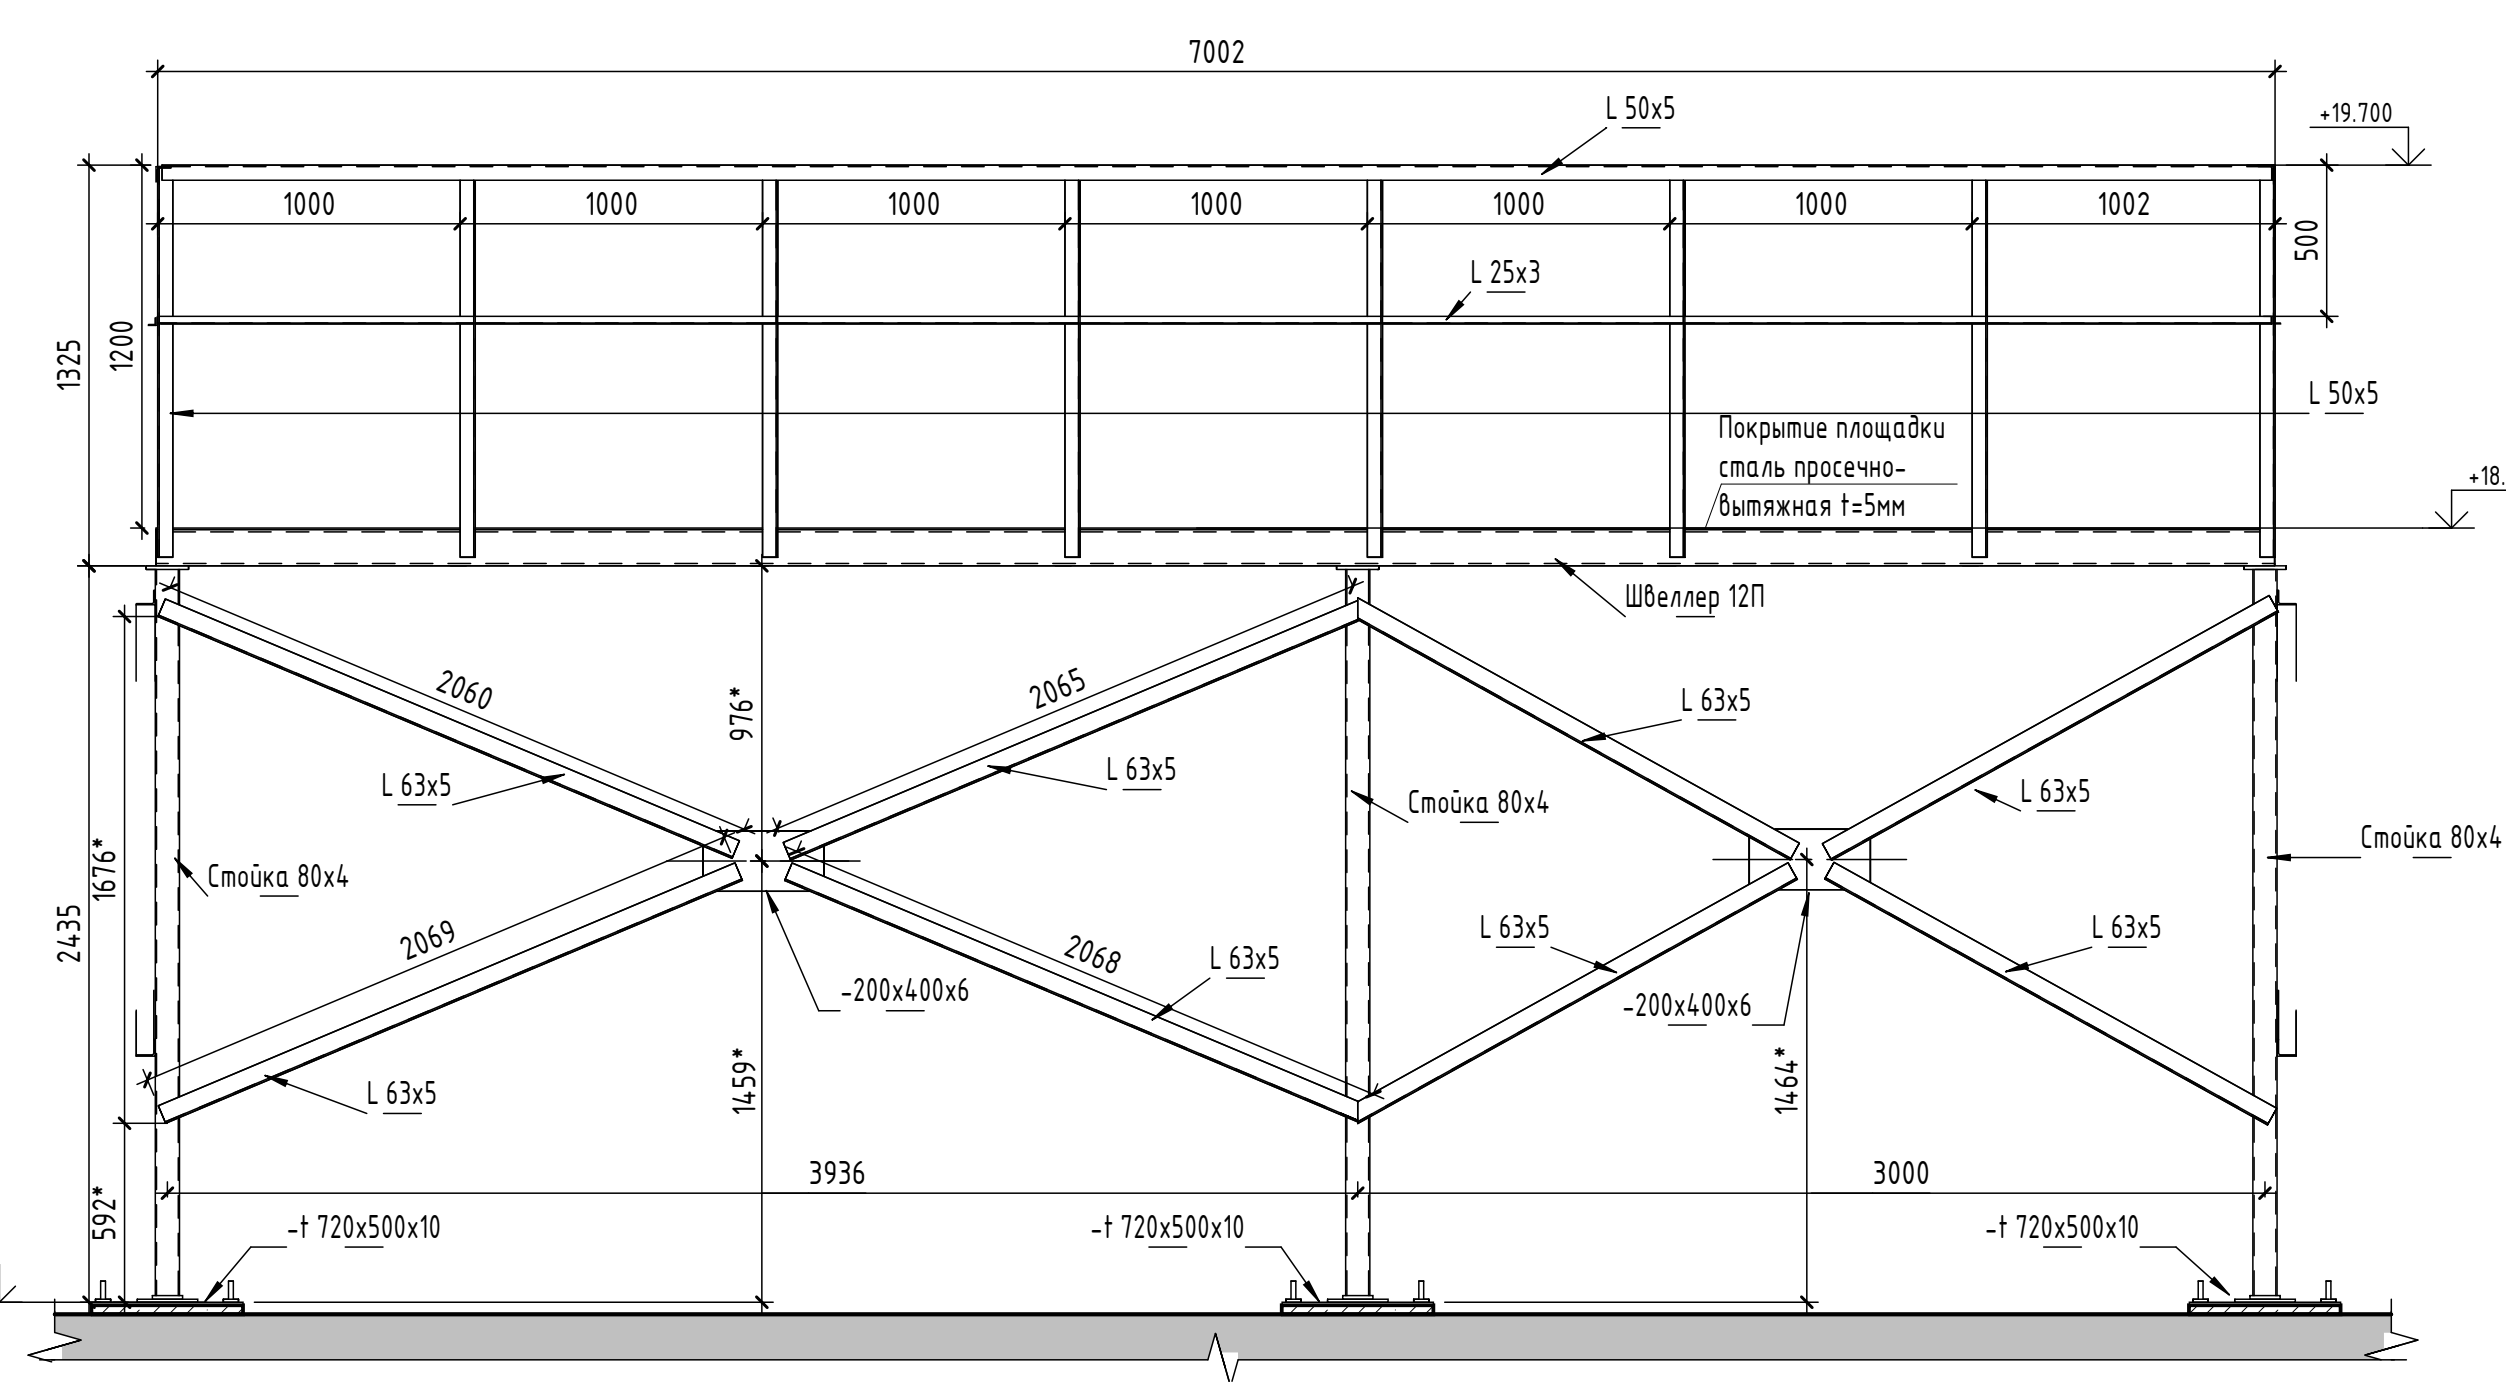

Вид 3 (1 : 20)

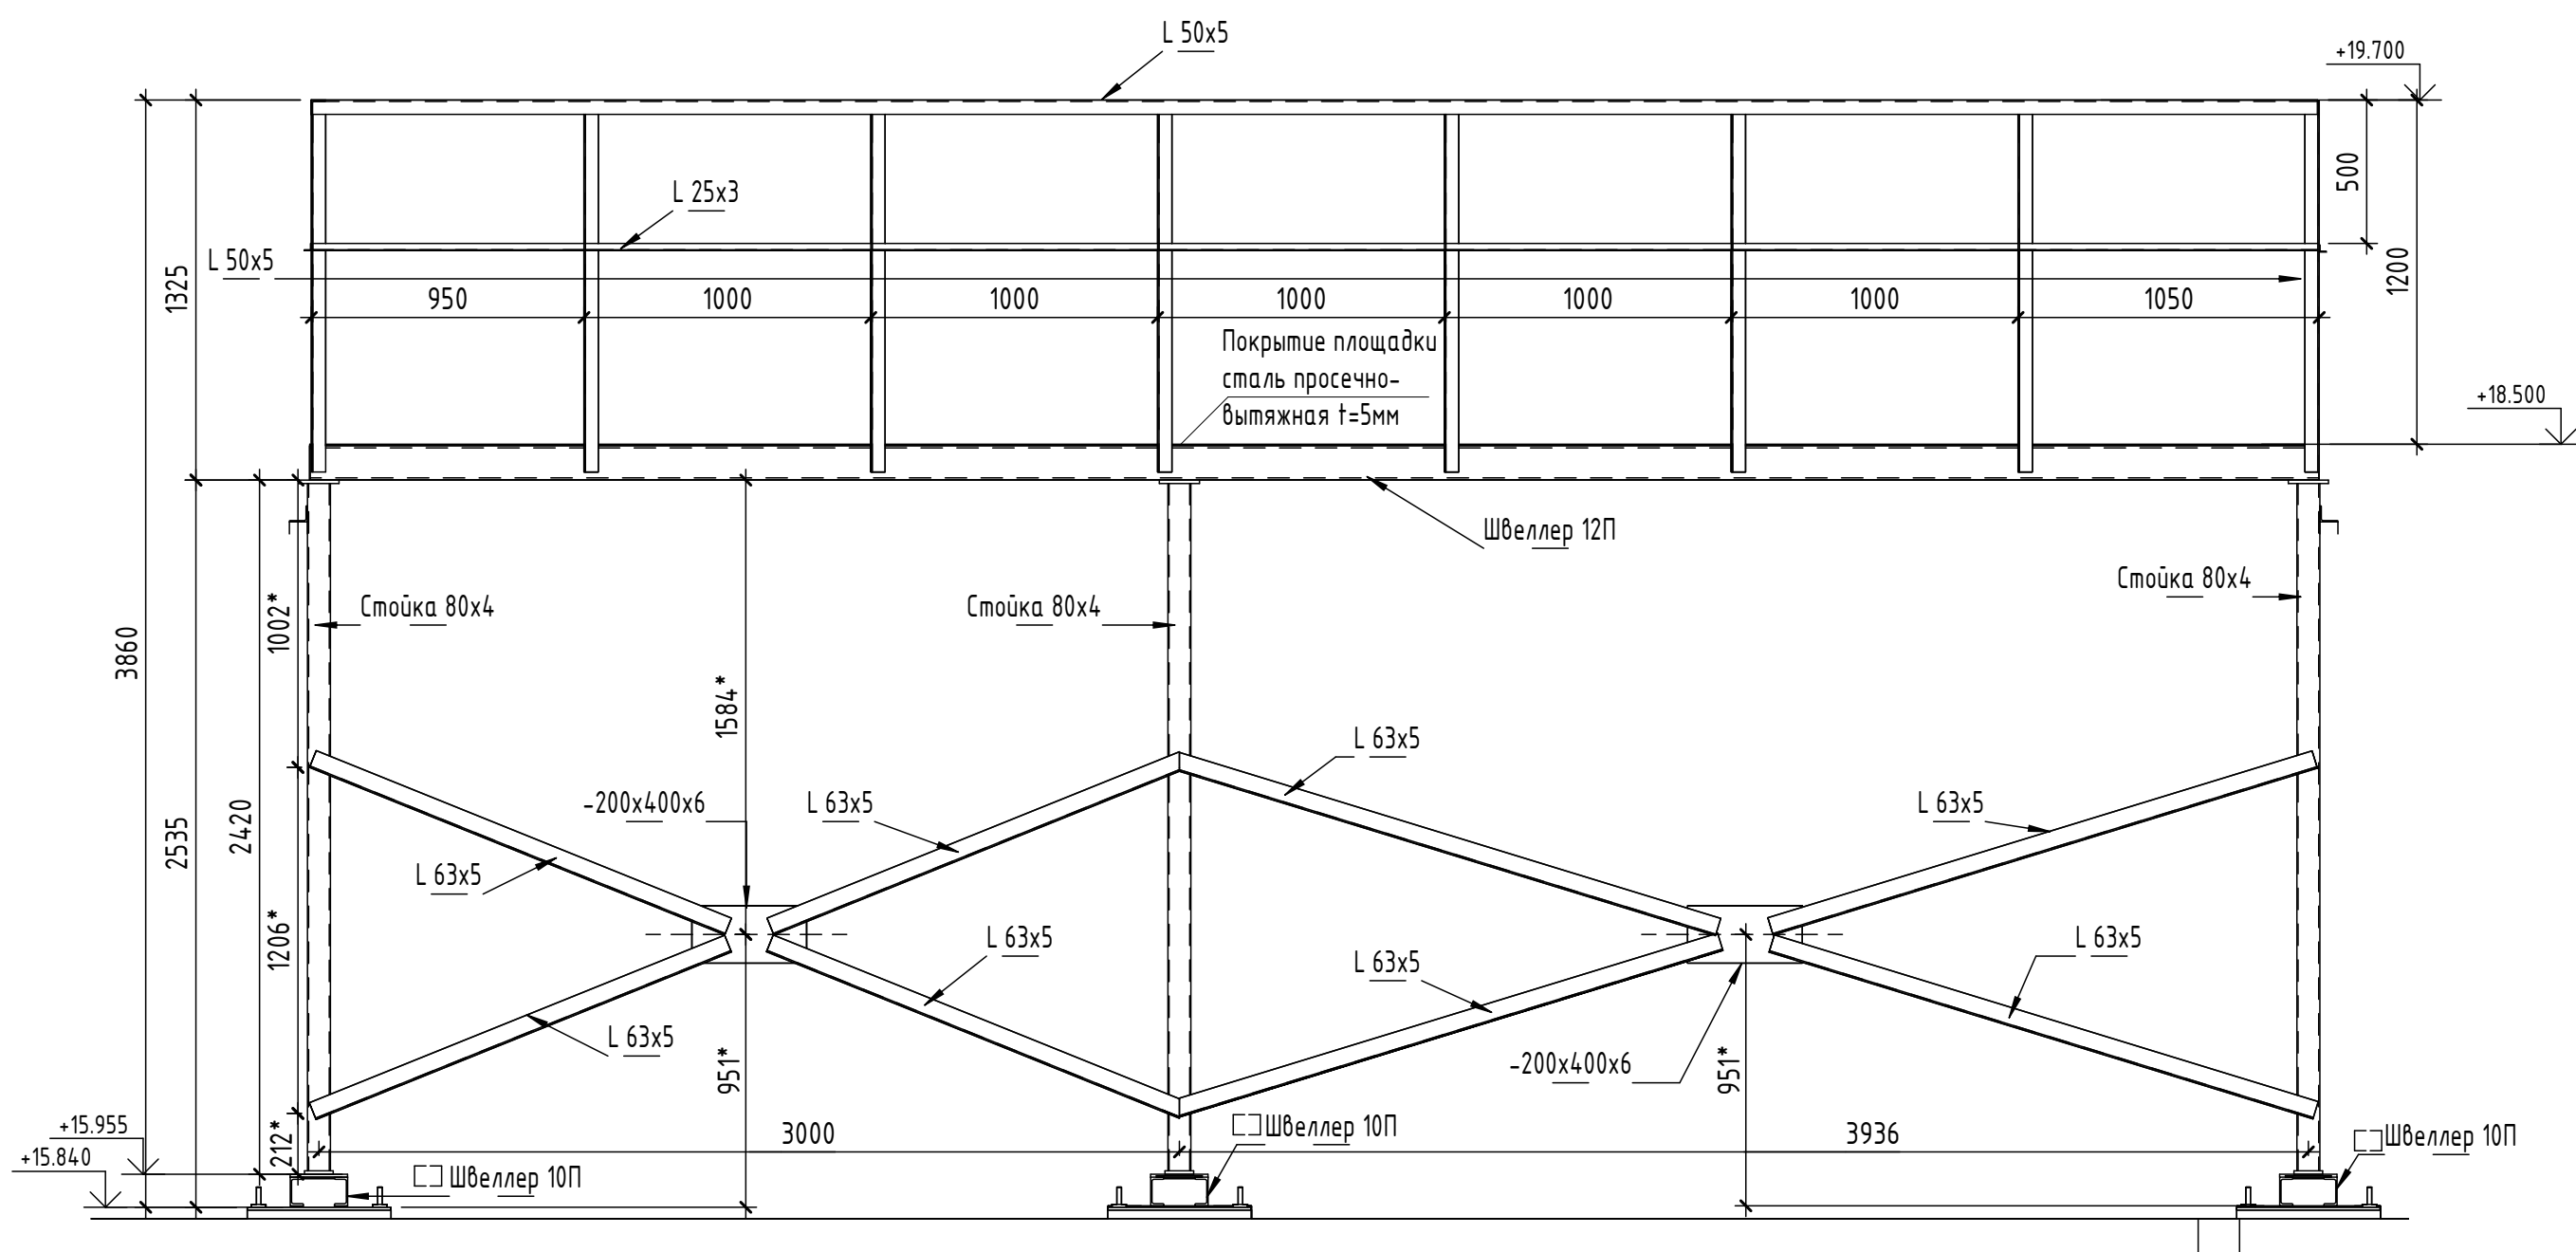


Прим:
1)В спецификацию не входят площадки.
Площадки показаны условно.
2)Размеры раскосов уточнять по месту. Они не
должны пересекаться с кровельным пирогом.
*Размеры уточнить по месту

						696/П-24-АНО-Р - КР		
						Капитальный ремонт Государственного бюджетного общеобразовательного учреждения города Москвы Школа №1282 Сокольники по адресу: г. Москва, ул. Барболина, д.1, корп.1		
Изм.	Жел.ч.	Лист	№ док.	Подп.	Дата	Капитальный ремонт	Стадия	Лист
Разработал	Василин А.А.						Р	60
Проверил	Головина							
ГАП	Гулько					Металконстр под площадку Пл-7		
Норм.контроль	Выходова							


Ведомость материалов на площадку Пл-7

№п.п	Обозначение	Наименование	Общая длина(п.м)	Кол-во	Примечание
	ГОСТ 19903-2015	-200x200x6	0.6	2	
	ГОСТ 19903-2015	-200x400x6	1.6	4	
	ГОСТ 19903-2015	-1 50x60x10	1.1	21	
	ГОСТ 19903-2015	-1 140x140	0.8	6	
	ГОСТ 19903-2015	-1 160x70x5	8.6	54	
	ГОСТ 19903-2015	-1 200x300x10	1.2	6	
	ГОСТ 19903-2015	-1 260x120x12	0.6	6	
	ГОСТ 19903-2015	-1 510x500x10	1.5	3	
	ГОСТ 19903-2015	-1 720x500x10	1.5	3	
	Труба ГОСТ 8639-82	80x80x4	14.5	6	
	ГОСТ8509-93	L 50x5	6	12	
	ГОСТ8509-93	L 63x5	37.9	22	
	ГОСТ8509-93	Узелок 125x10	1.5	3	
	ГОСТ 8240-97	Швеллер 10П	17.5	6	
	ГОСТ 22042-76	Шпилька М16	7.8	21	


План опорных пластин и стоек под площадку Пл-9 (1 : 20)

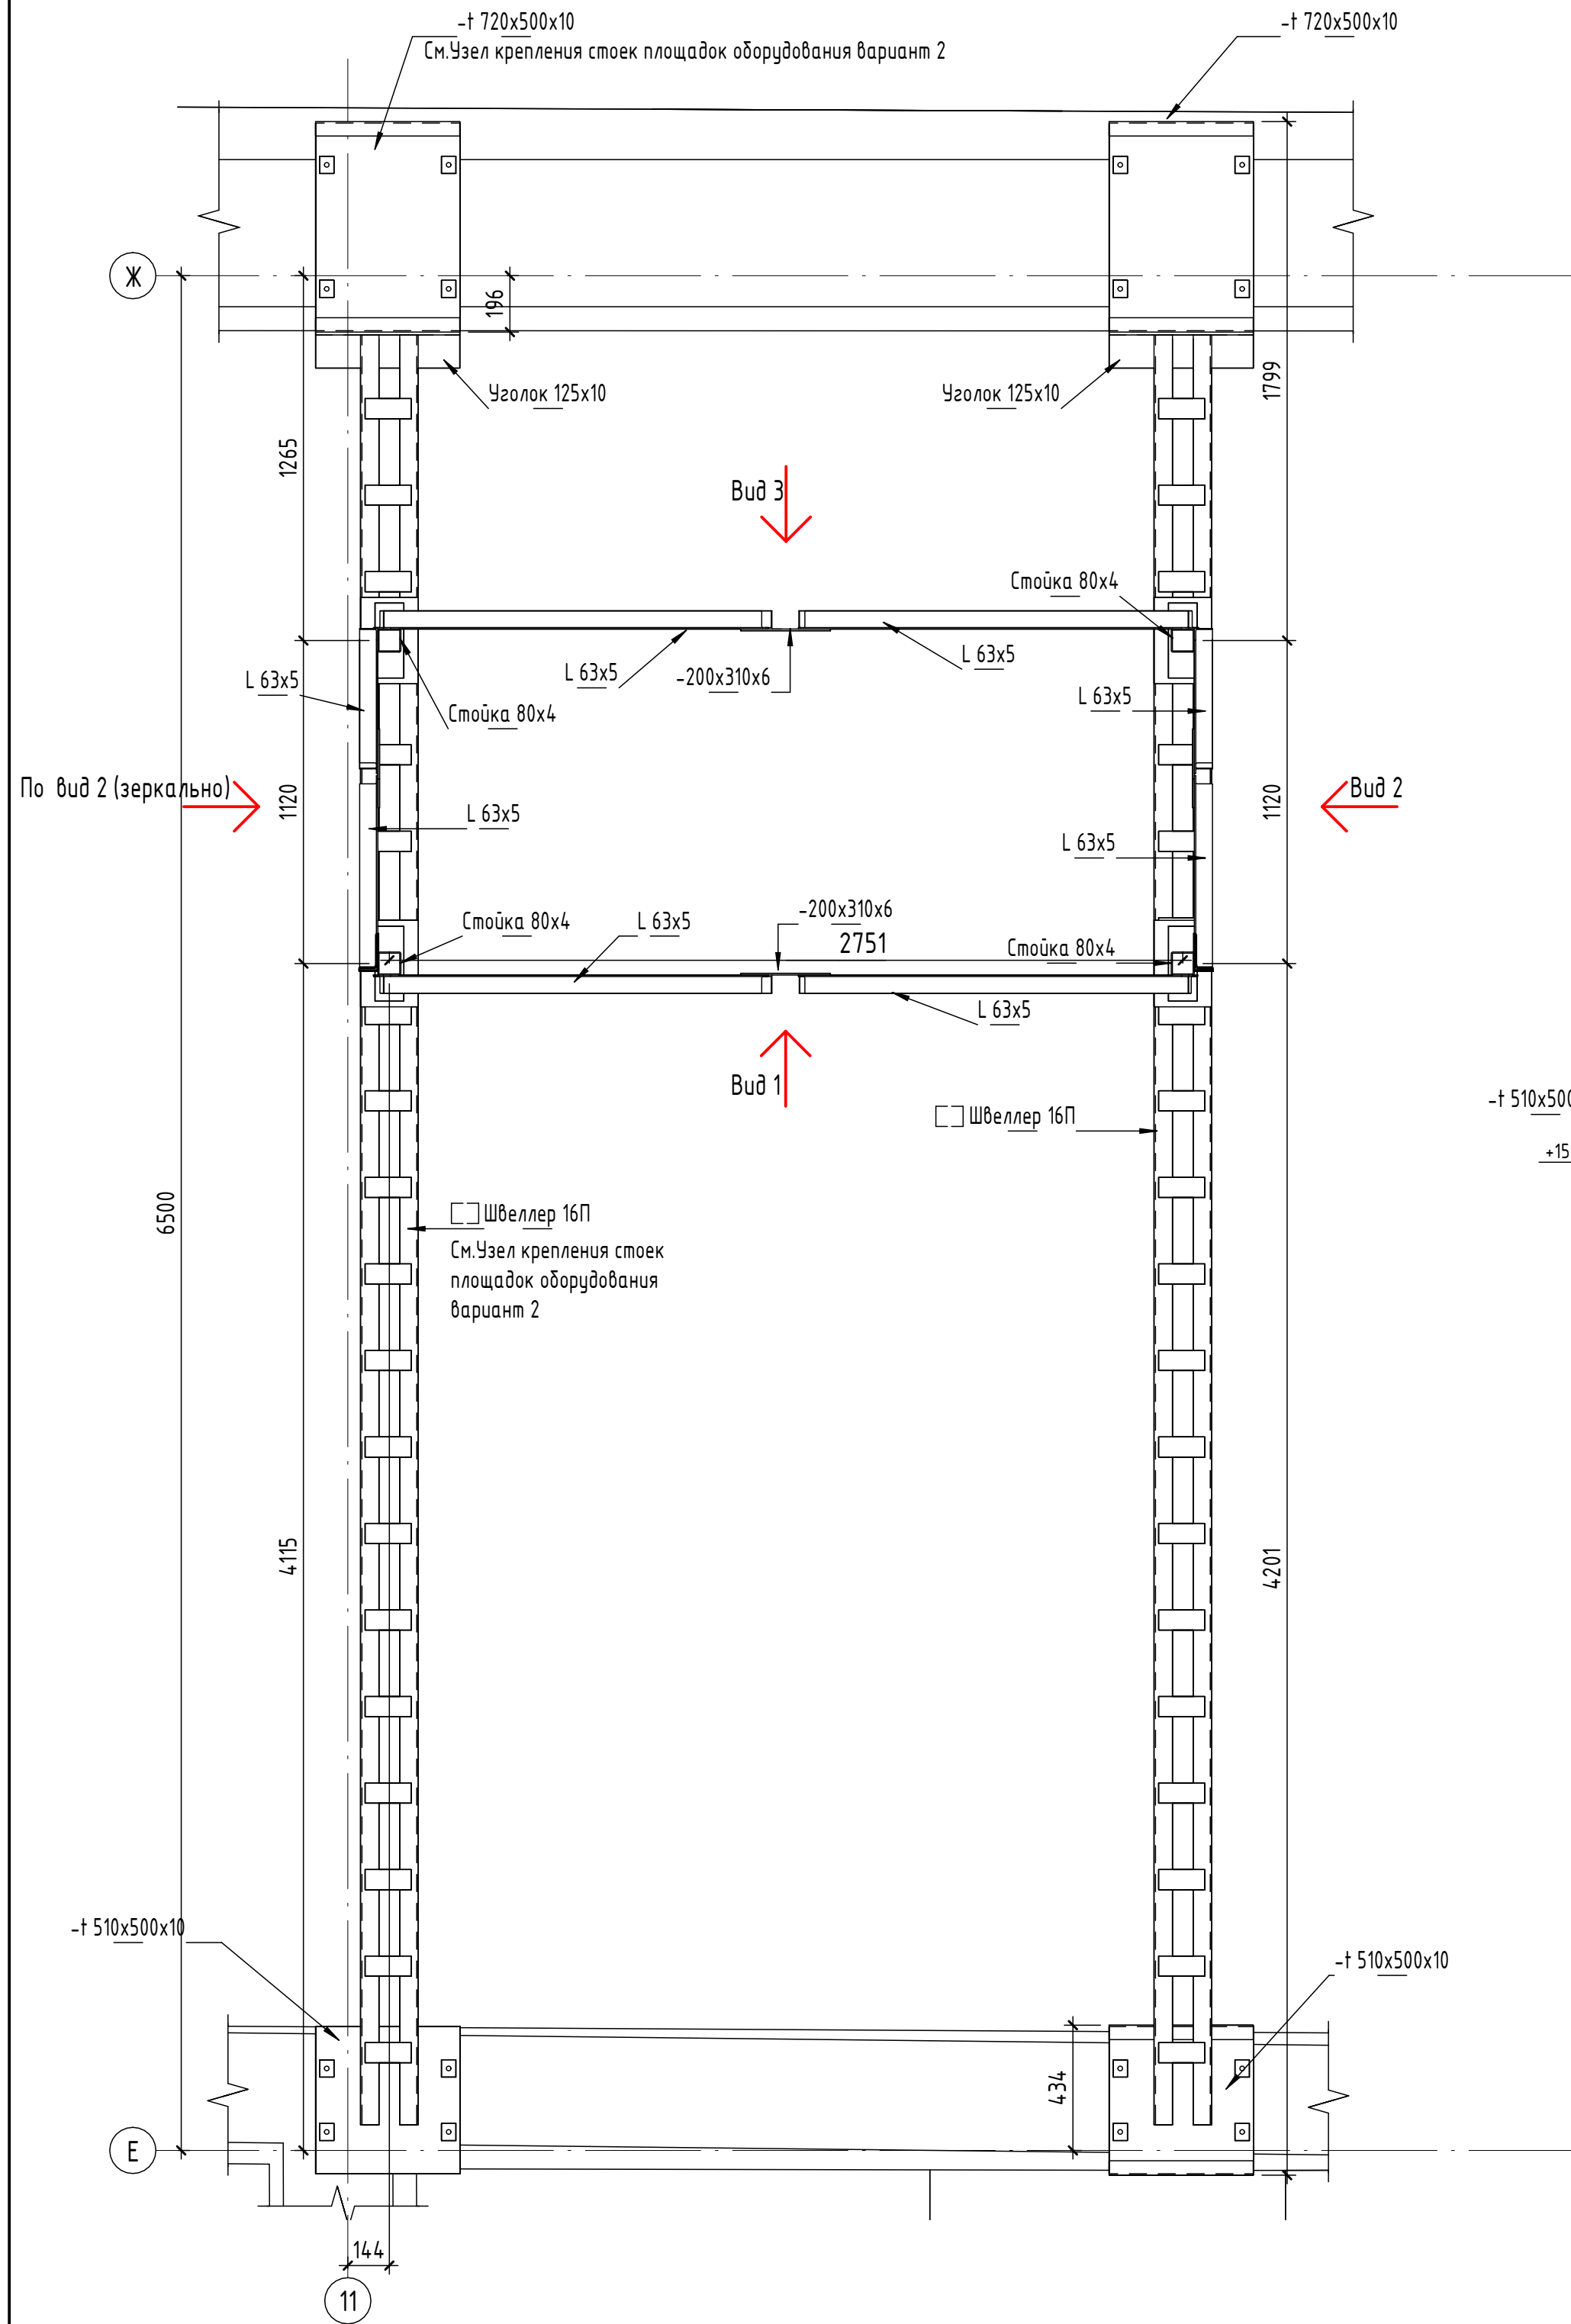


Вид 2 (1 : 20)

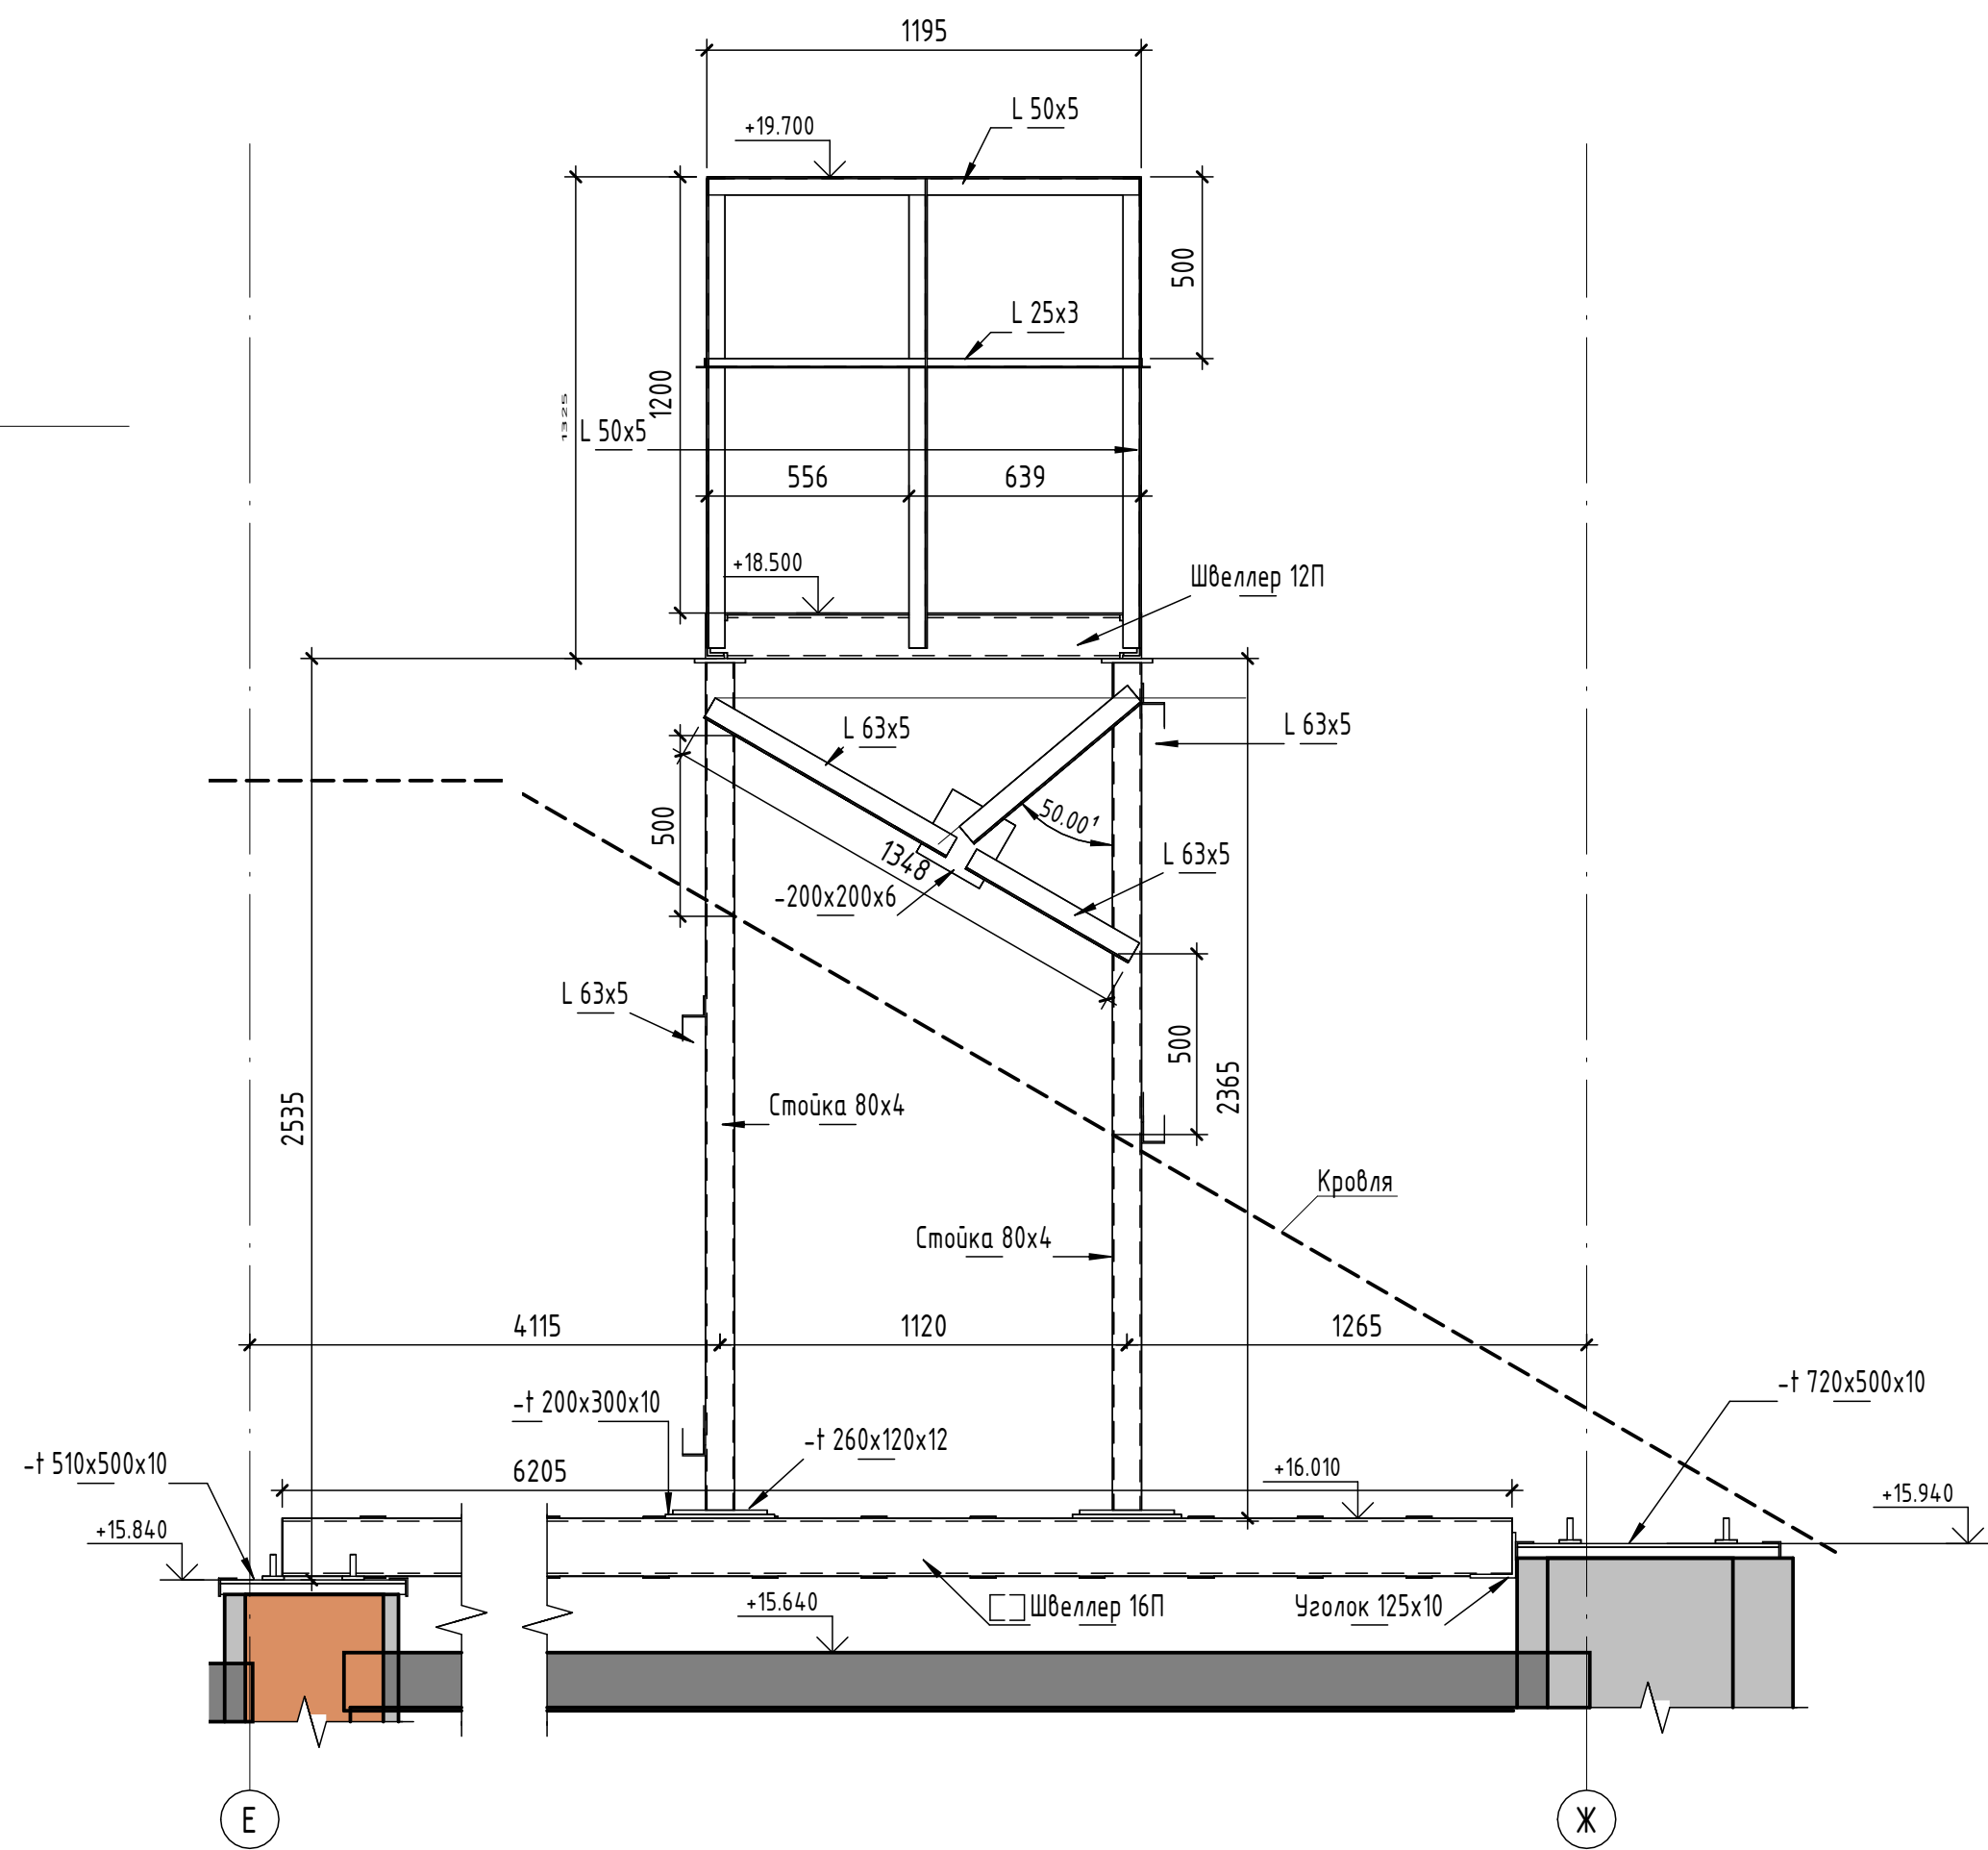

Вид 1 (1 : 20)

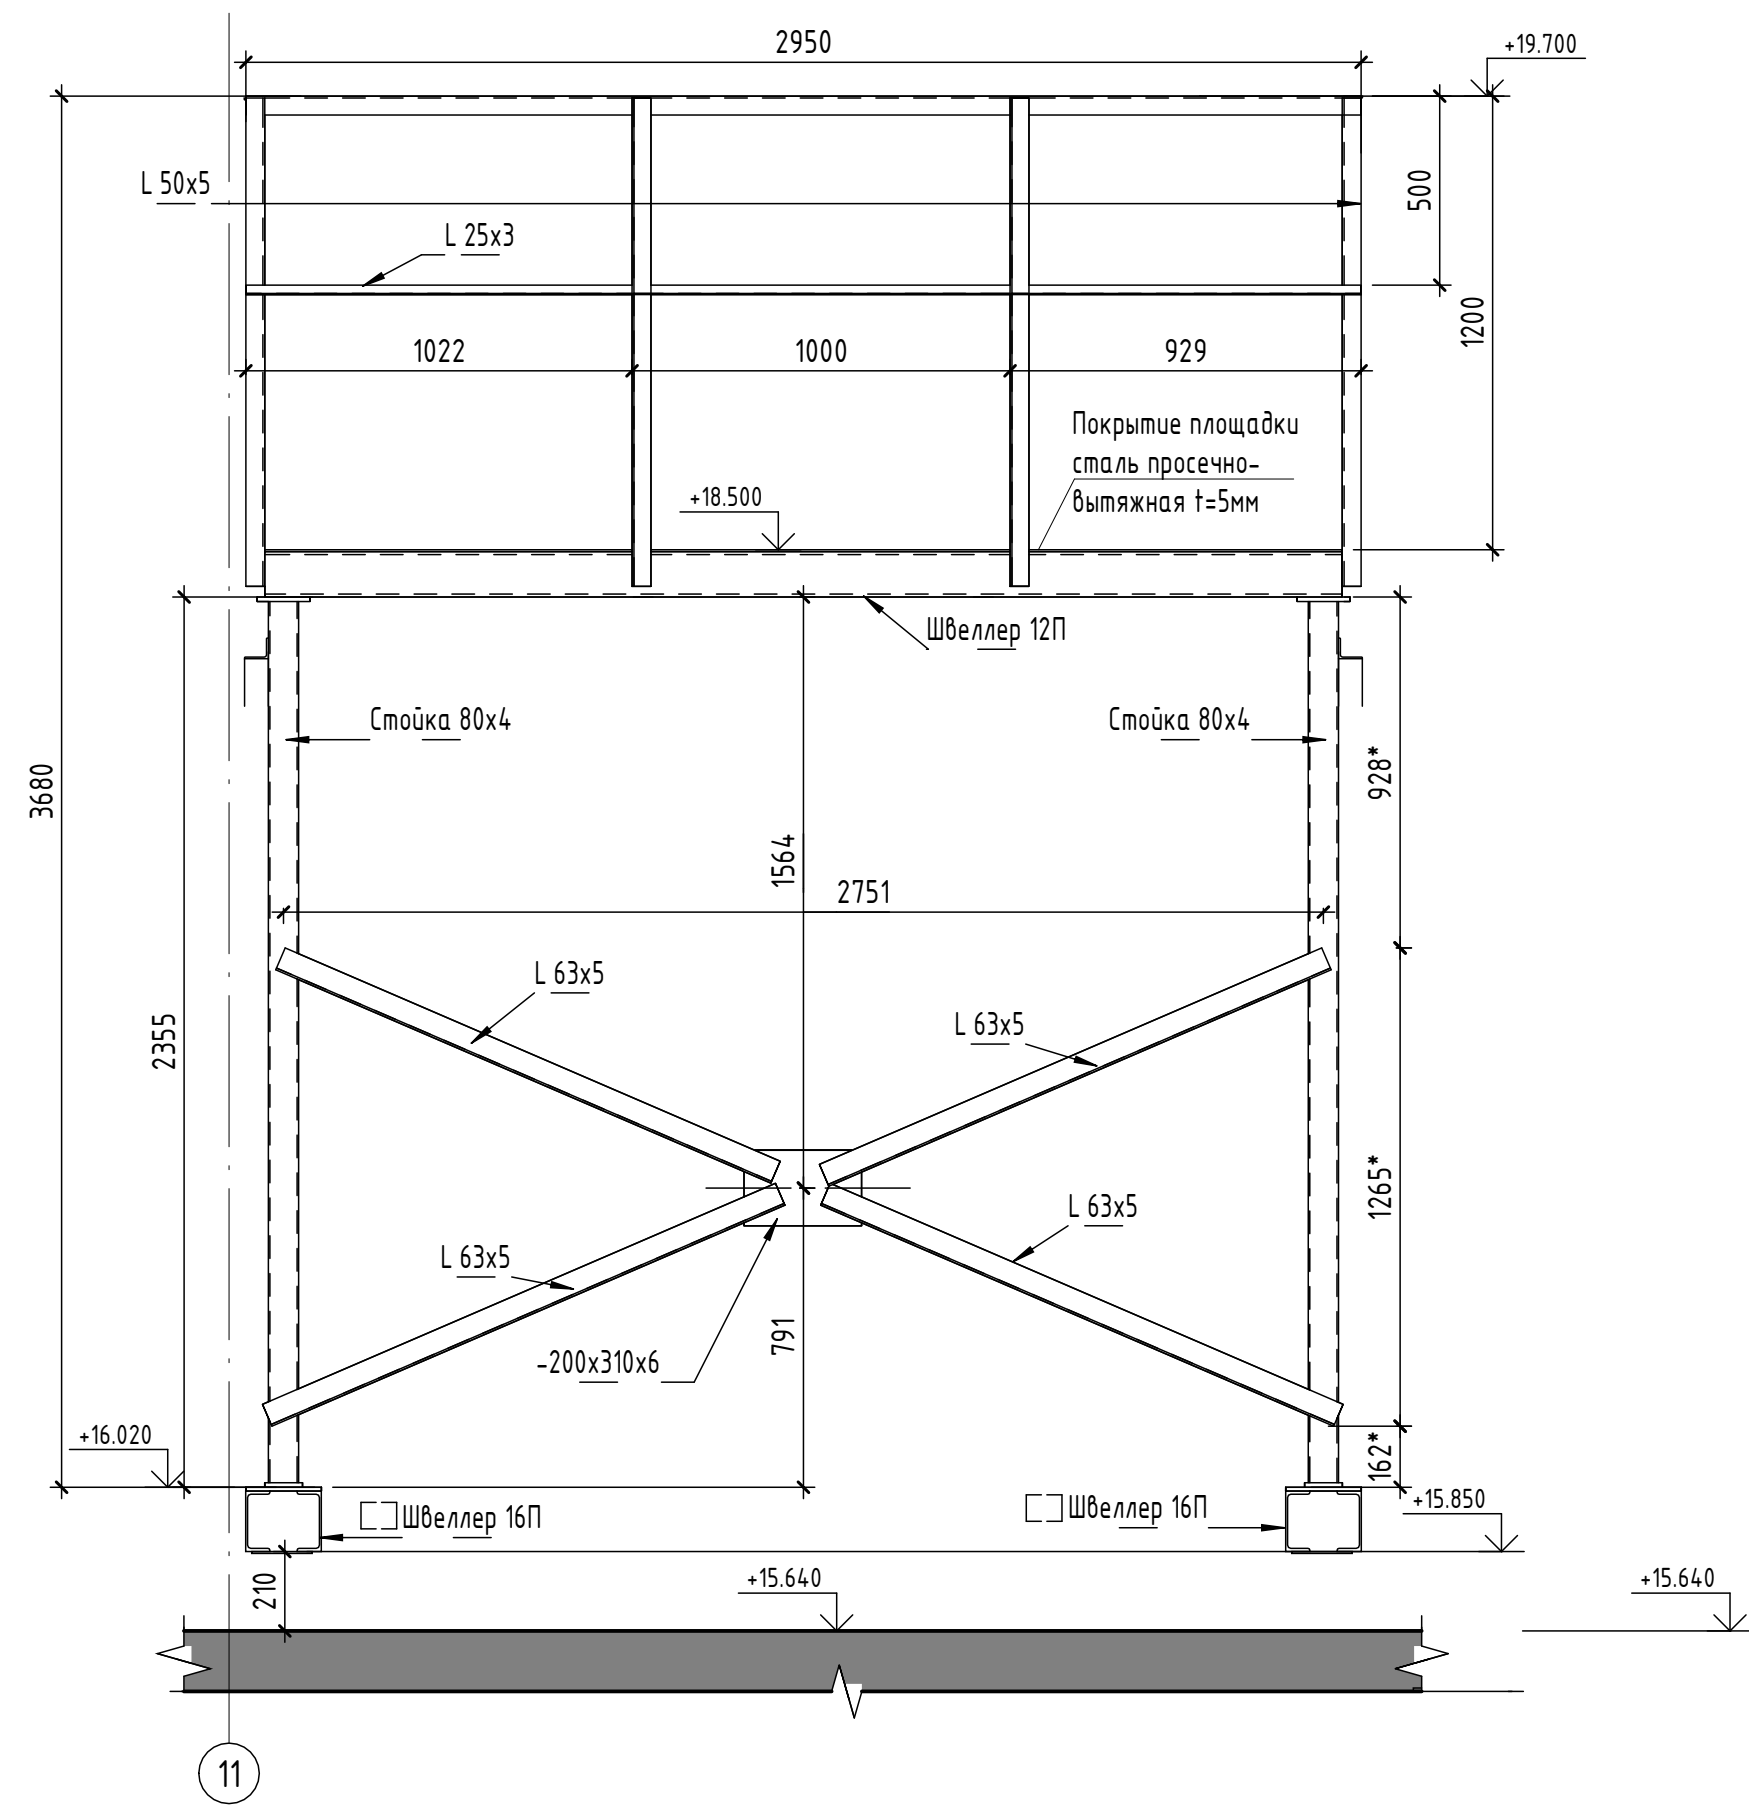

Вид 3 (1 : 20)

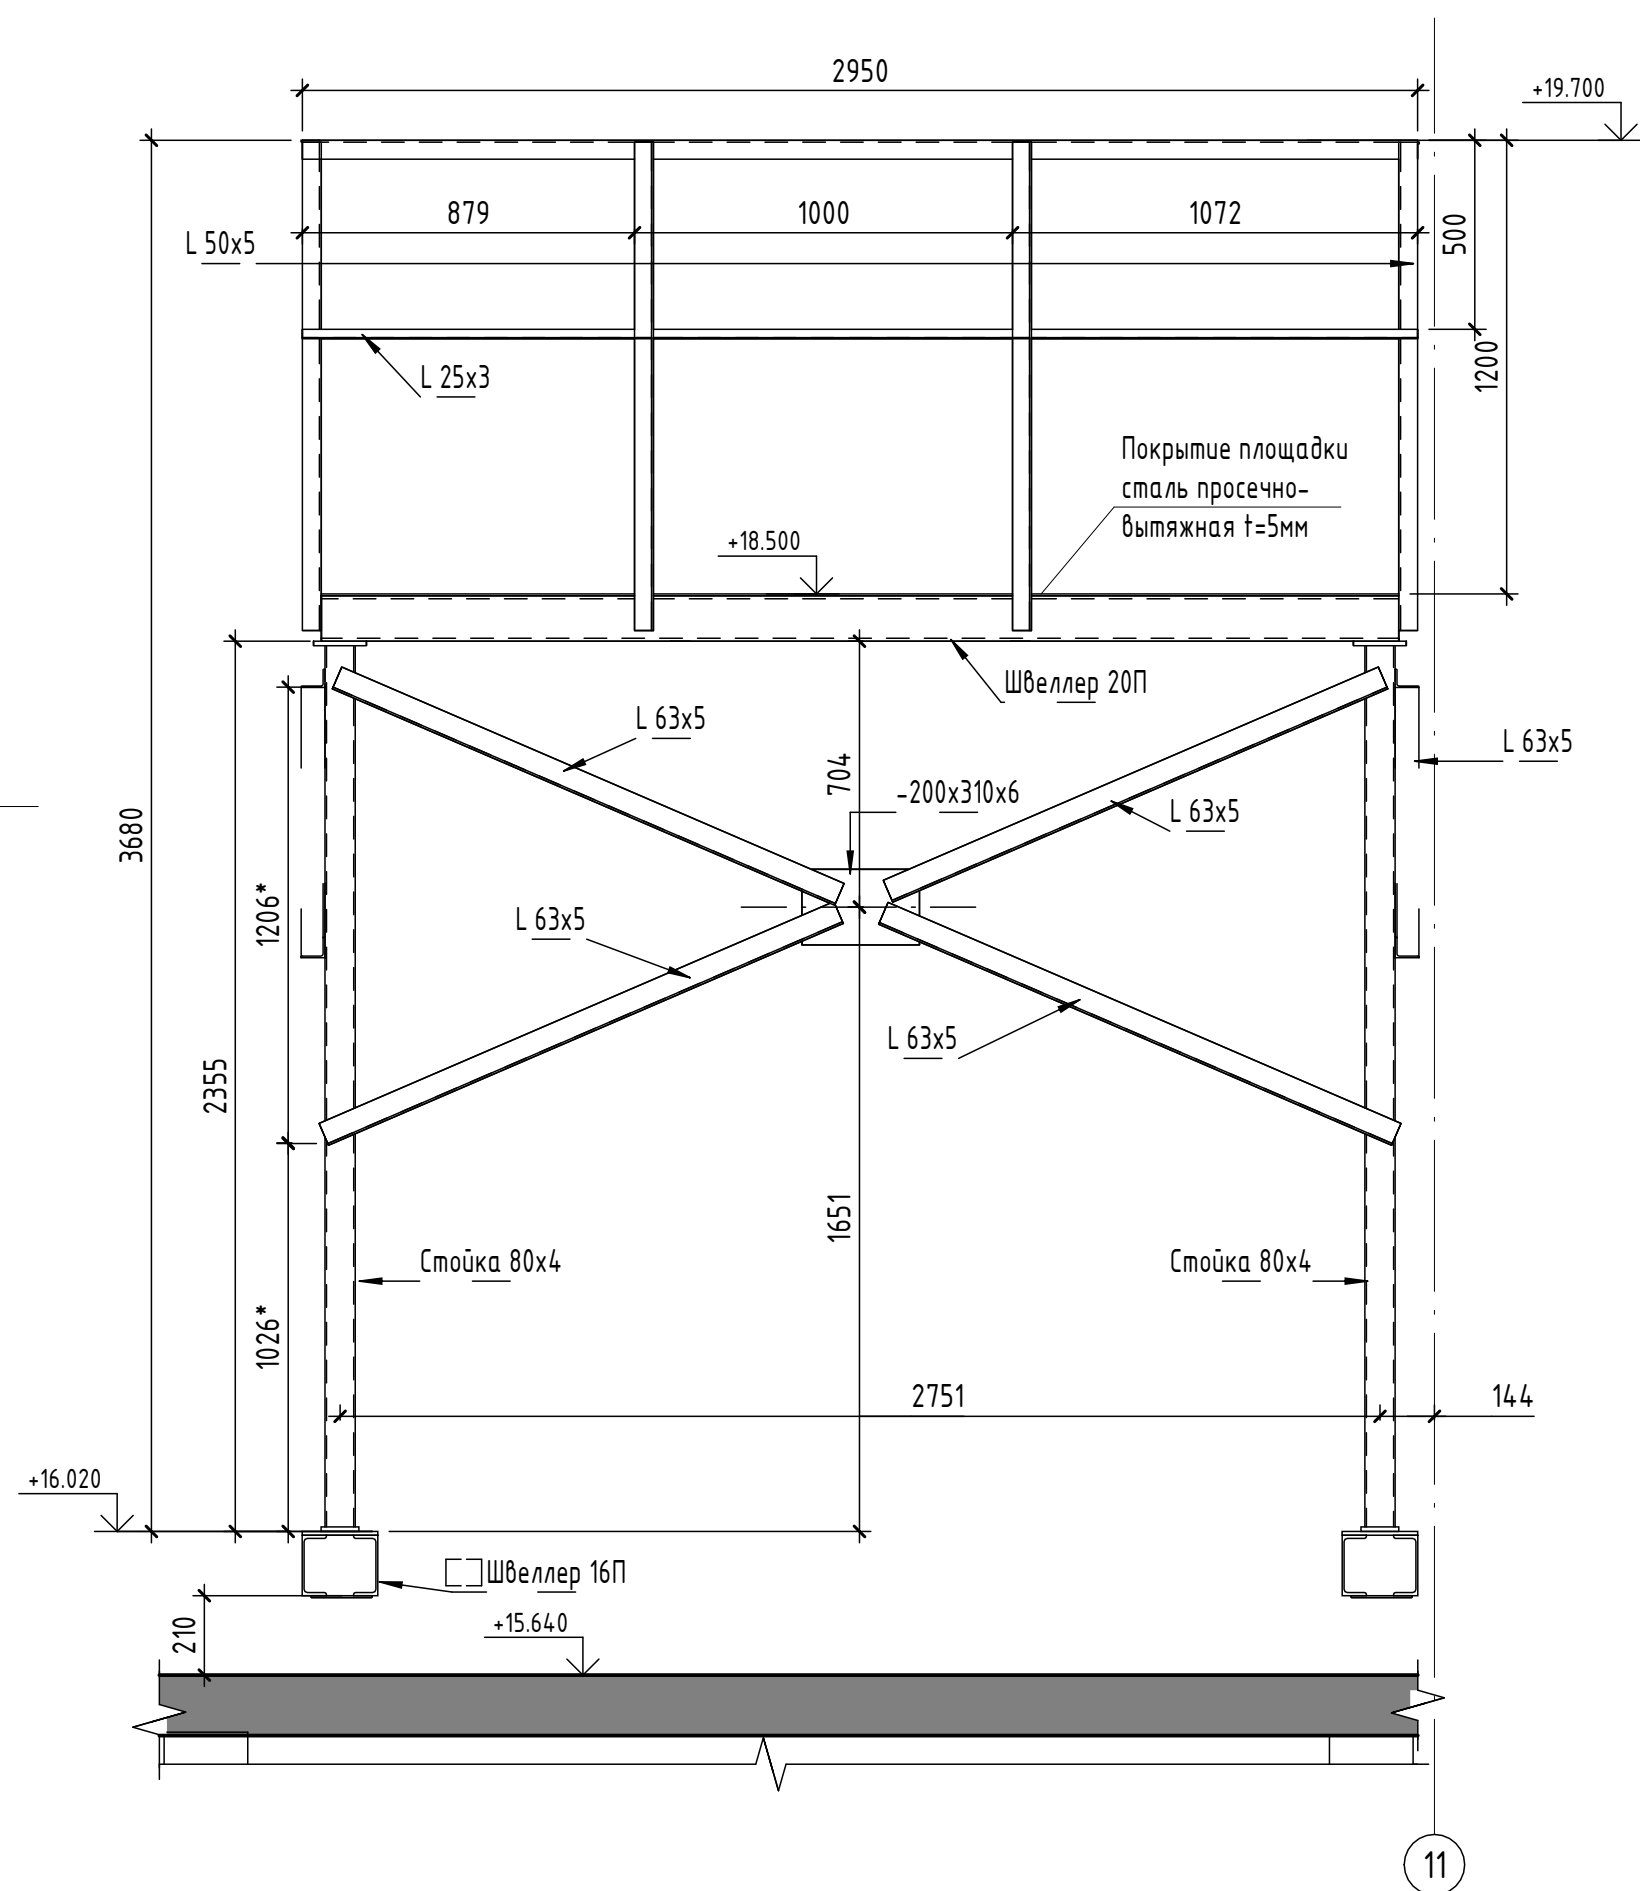

Ведомость материалов на площадку Пл-9

№п.п	Обозначение	Наименование	Общая длина(п.м)	Кол-во	Примечание
1	ГОСТ 19903-2015	-200х200х6	0.4	2	
2	ГОСТ 19903-2015	-200х310х6	0.6	2	
3	ГОСТ 19903-2015	-1 50х60х10	0.8	16	
4	ГОСТ 19903-2015	-1 140х140	0.6	4	
5	ГОСТ 19903-2015	-1 160х70х5	12.3	77	
6	ГОСТ 19903-2015	-1 200х300х10	0.8	4	
7	ГОСТ 19903-2015	-1 260х120х12	0.4	4	
8	ГОСТ 19903-2015	-1 510х500х10	1	2	
9	ГОСТ 19903-2015	-1 720х500х10	1	2	
10	Труба ГОСТ 8639-82	80х80х4	9.3	4	
11	ГОСТ8509-93	L 50х5	2	4	
12	ГОСТ8509-93	L 63х5	15.4	14	
13	ГОСТ 8240-97	Балка 16П	24.8	4	
14	ГОСТ8509-93	Уголок 125х10	1	2	
15	ГОСТ 22042-76	Шпилька М16	5.9	16	

Прим:

1)В спецификацию не входят площадки.



Площадки показаны условно.

2)Размеры раскосов уточнять по месту. Они не должны пересекаться с кровельным пирогом.

*Размеры уточнить по месту

696/П-24-АНО-Р - КР					
Капитальный ремонт Государственного бюджетного общеобразовательного учреждения города Москвы Школа №1282 Сокольники по адресу: г. Москва, ул. Барболова, д.1, корп.1					
Изм.	Жол.ч.	Лист	№доп.	Подп.	Дата
Разработал	Васясин А.А.				
Проверил	Головина				
ГАП	Гулько				
Норм.контроль	Выходова				
Капитальный ремонт				Стадия	Лист
Метал.контр. под площадку Пл-9				Р	61
ООО "ПРОЕКТ+"				Листов	

Инв. № подл.	Подп. и дата	Взам. инв. №	Согласовано	

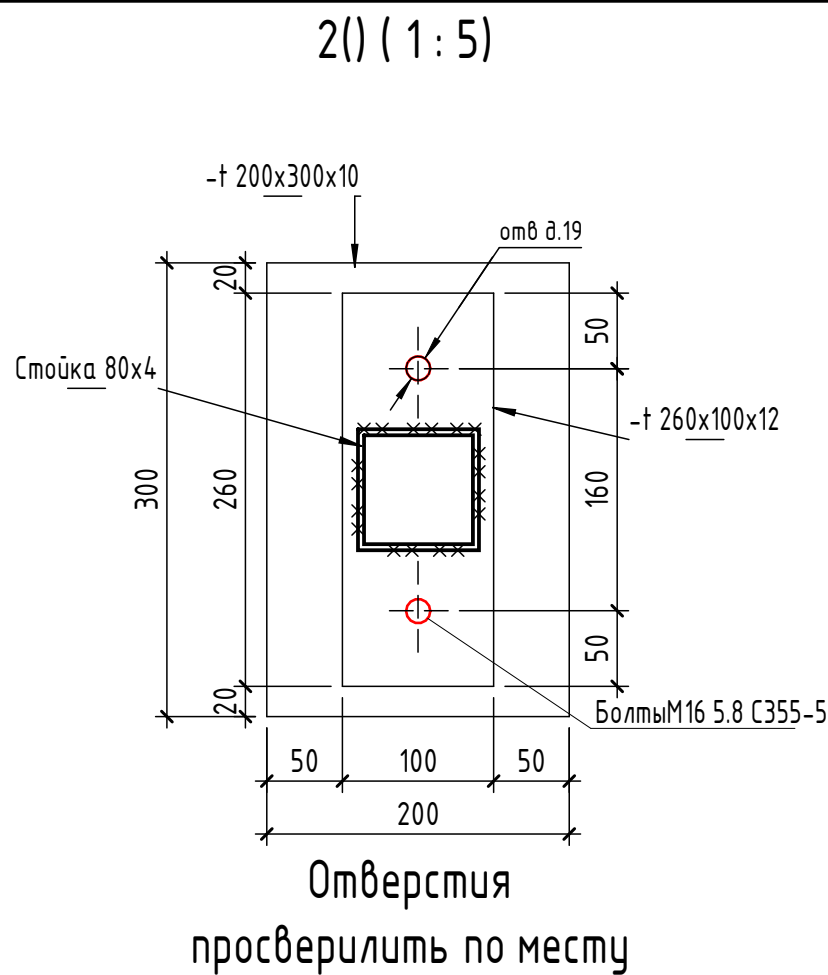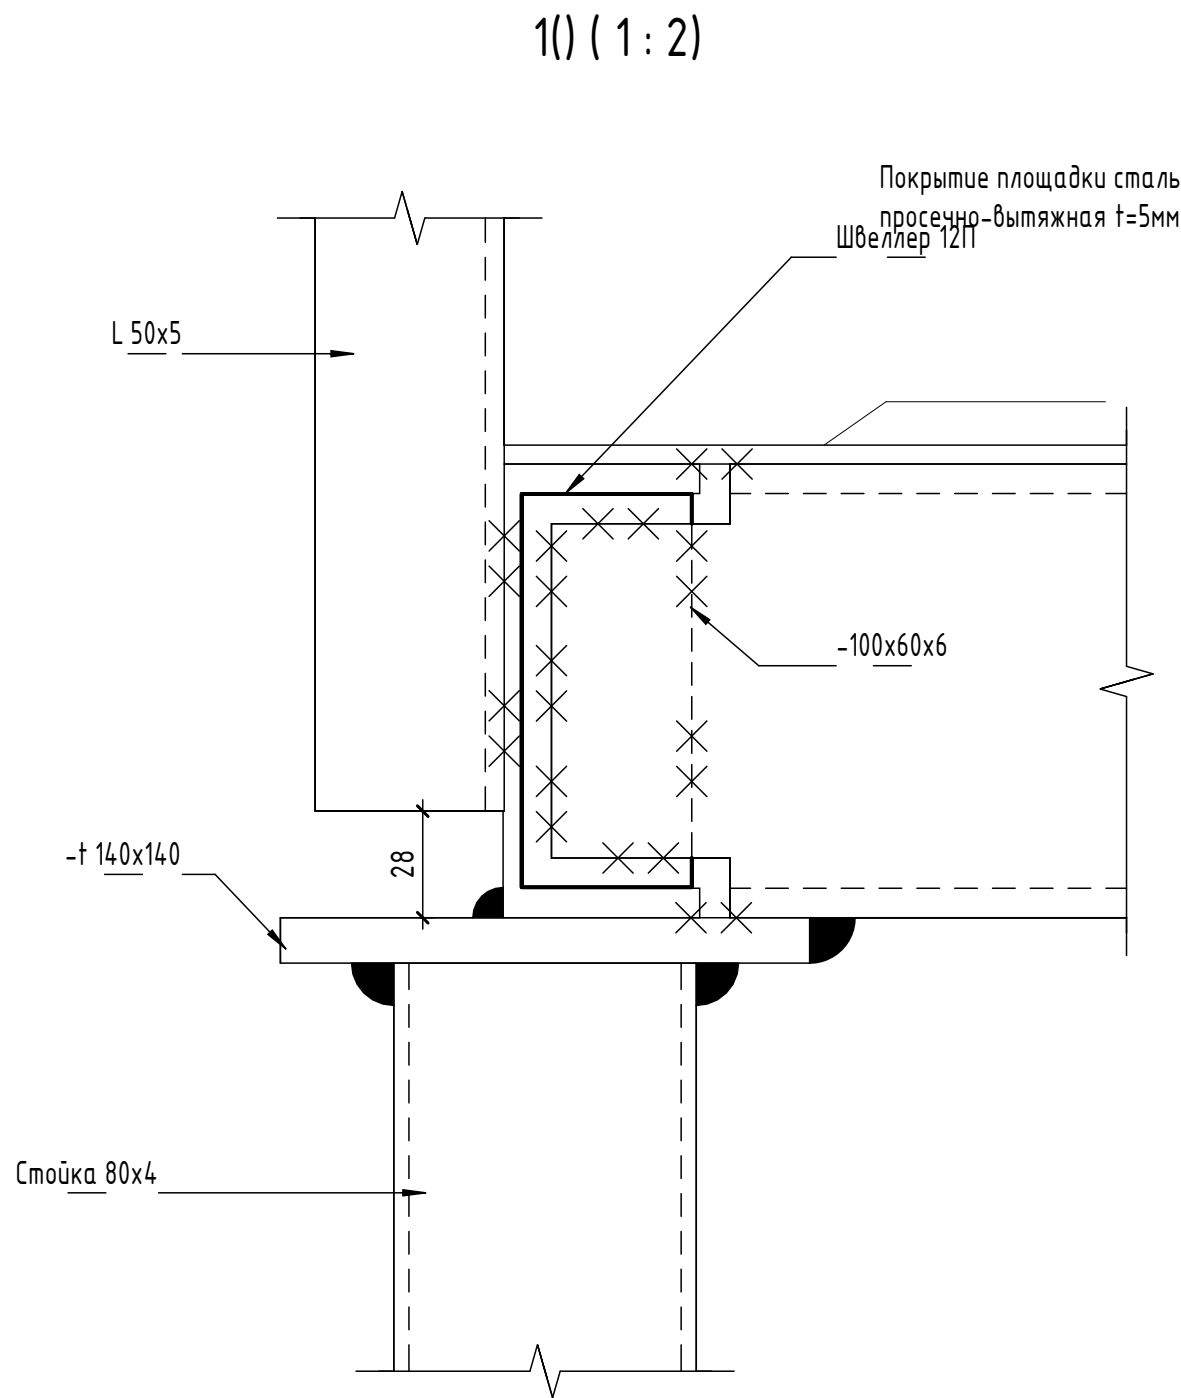

						696/П-24-АНО-Р - КР			
						Капитальный ремонт Государственного бюджетного общеобразовательного учреждения города Москвы Школа №1282 Сокольники по адресу: г. Москва, ул Барболина, д.1, корп.1			
Изм.	Кол.уч.	Лист	№ док.	Подп.	Дата	Капитальный ремонт	Стадия	Лист	Листов
Разработал	Васясин.А.А						Р	62	
Проверил	Головина								
ГАП	Гулько					Узлы	 ООО "ПРОЕКТ+" Формат А2А		
Норм.контроль	Выходова								