


Узел ремонта местных повреждения фундамента дутового
(1 : 5)

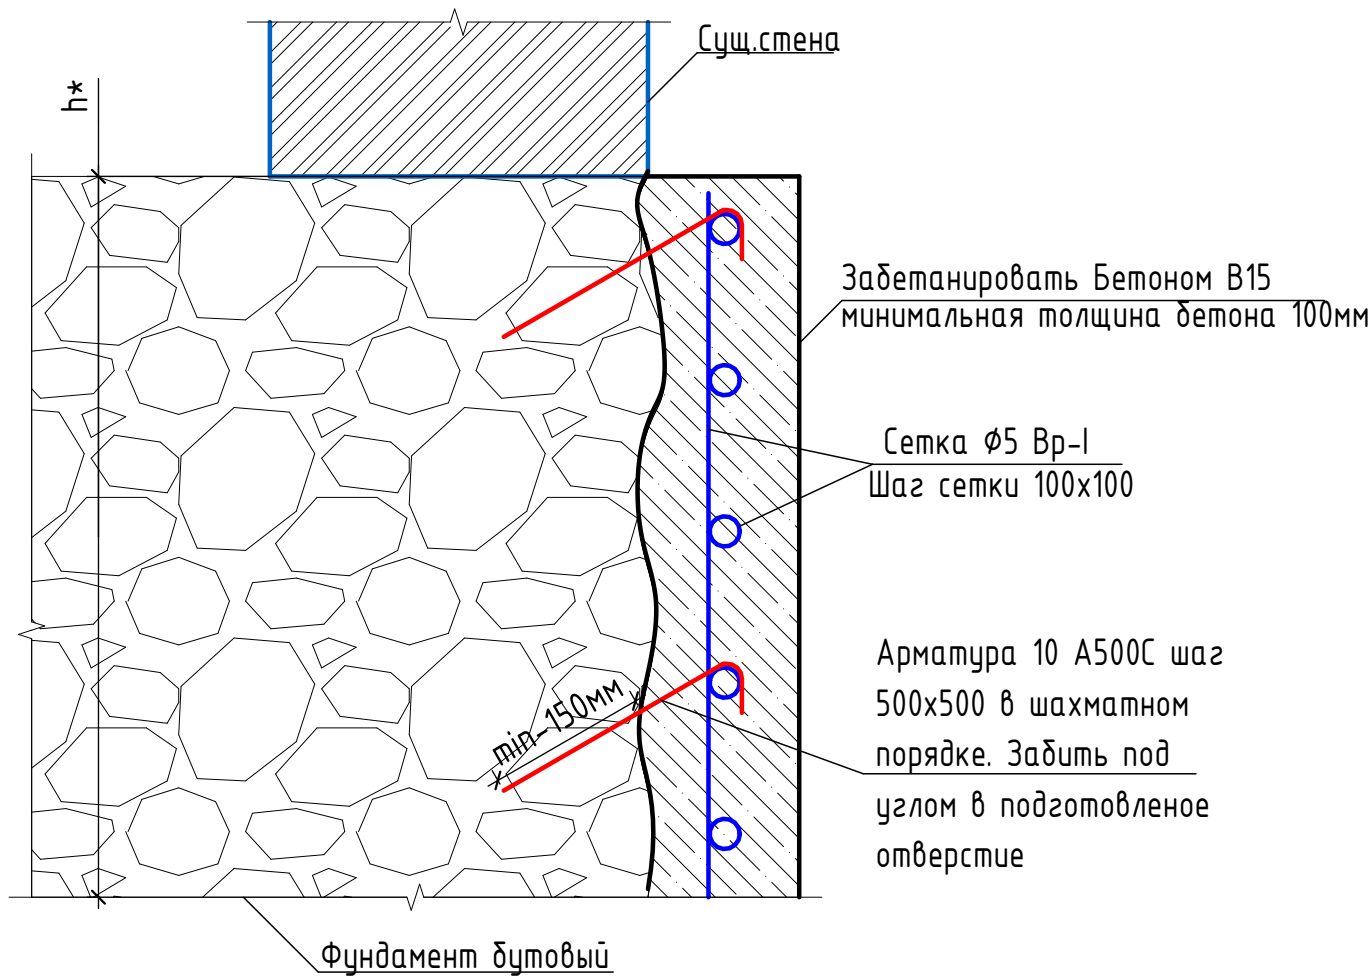

Кол-во материалов на 1м ²			
№п.п	Наименование	Ед.изм.	Кол-во
1	Бетон В15 М200	м ³	0.12
2	Сетка 5 ВР-I	Кг	3.08
3	Арматура 10А500С	Пг.м	1.5

Согласовано		Взам. инв. №	Подп. и дата	Инв. № подл.

						000 -			
Изм.	Кол.уч.	Лист	№ док.	Подпись	Дата				
							Стадия	Лист	Листов
							Р	2	
						Ремонт местных повреждения фундамента бутового			