
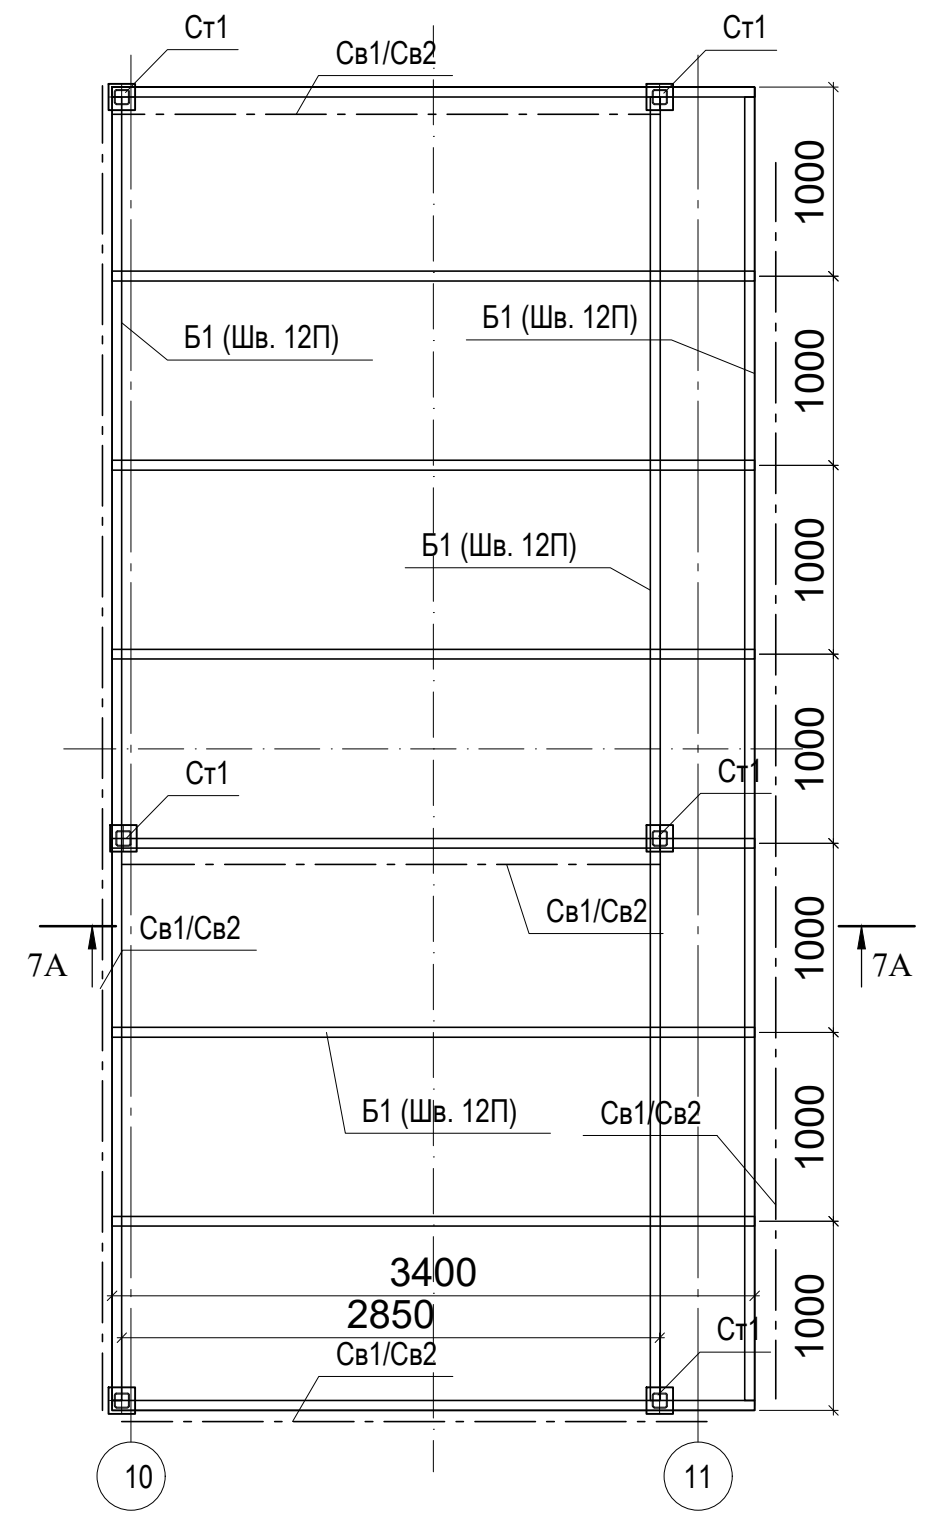
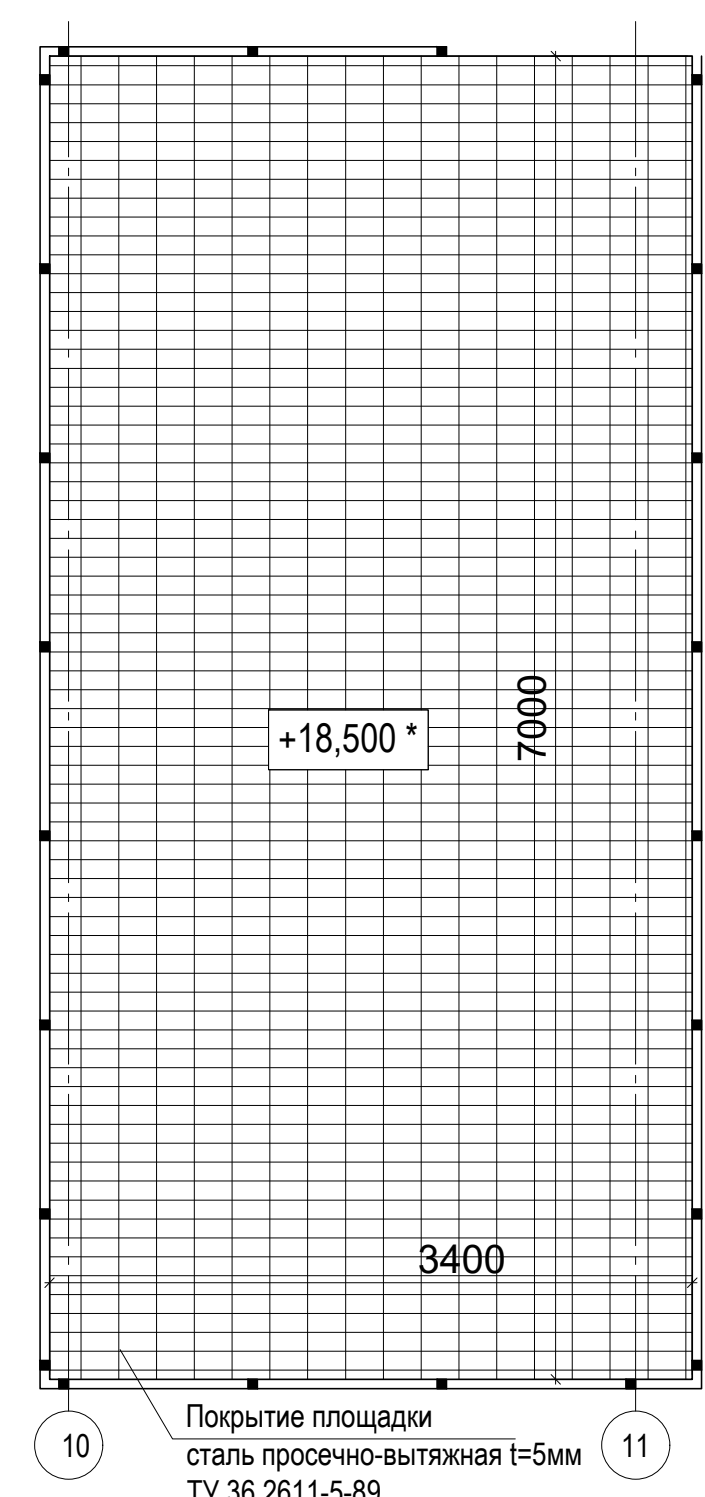


Инв. № подл.	Подп. и дата	Взам. инв. №

						696/П-24- АНО-КР
						Капитальный ремонт Государственного бюджетного общеобразовательного учреждения города Москвы Школа № Сокольники по адресу: г. Москва, ул. Барболина, д.1, корп.
Изм	Колуч	Лист	№ док	Подпись	Дата	
Разработал		Шопиничова			06.26	Конструктивные решения
Н. Контр.		Гулько			06.26	
Нач. Упр.					06.26	Площадки обслуживания оборудования на кровле Пл-1-Пл-4. Узлы
						000 "Проект +"

Площадка Пл-8

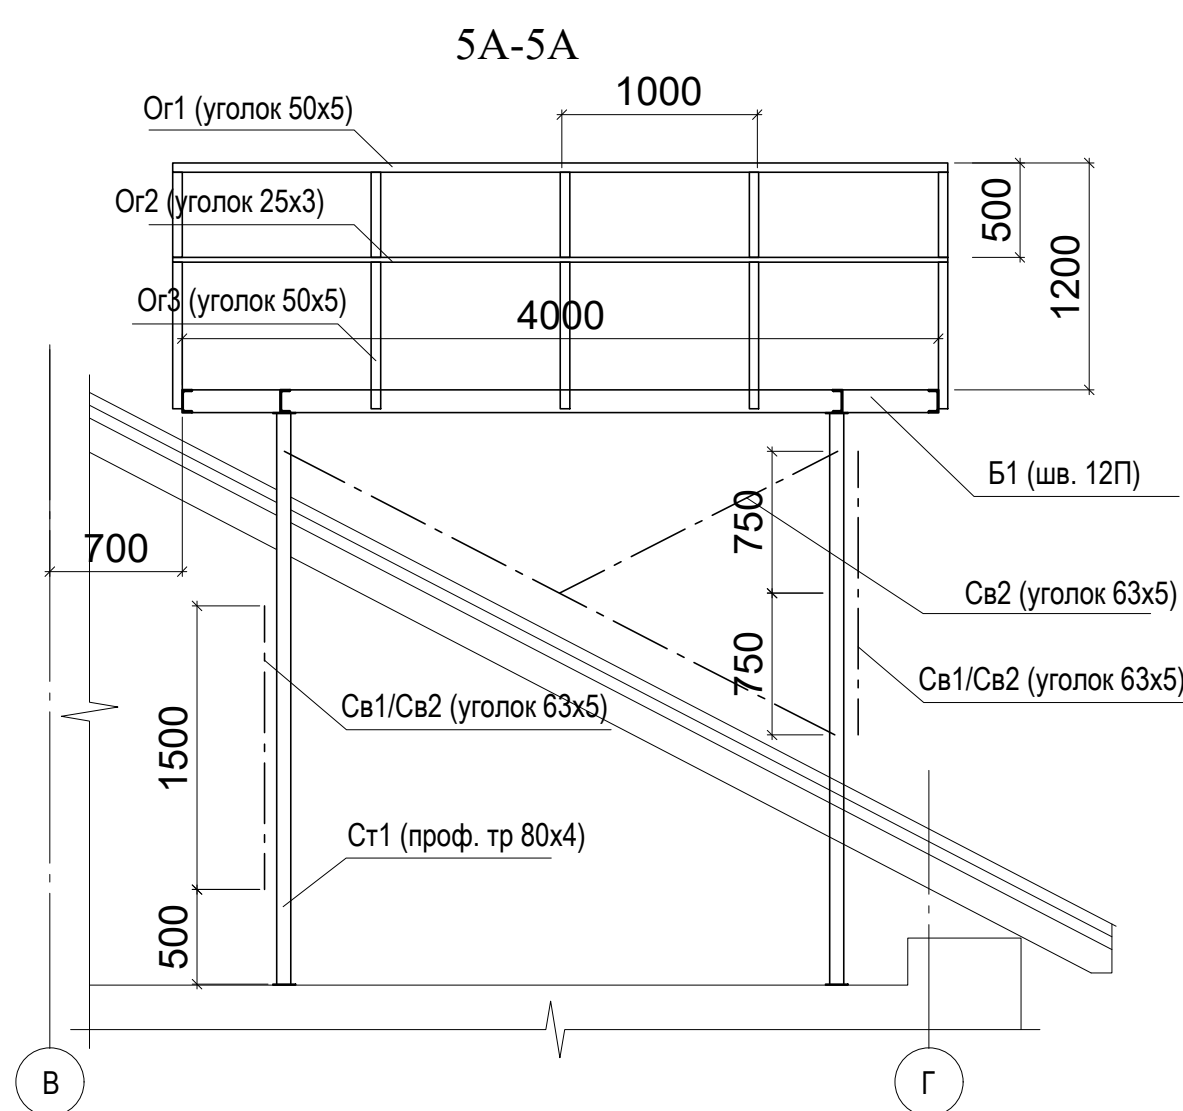

Спецификация элементов площадки Пл-5						
Поз.	Обозначение	Наименование	ед. изм.	Кол.	Масса ед. изм.	Примечание
1	ГОСТ 8240-97	Швеллер № 12П L п.м.	гм	124	10,44	1294,56
2	ГОСТ 8639-82	Труба 80х80х4 L=3000	шт	10	27,66	276,60
3	ГОСТ 8509-93	Уголок L63х5 L= п.м	м	76	4,81	365,71
4	ГОСТ 8510-86	Уголок L50х5 L=1300	шт	36	4,90	176,44
5	ГОСТ 8568--77	Уголок L50х5 L=п.м.	м	38	3,77	143,18
6	ТУ 36.2611-5-89	Лист просечно-вытяжной t=5мм	м ²	60	16,40	984,00
7	ГОСТ 19903-2015	Листовая сталь t=10мм	м ²	0,5	78,50	39,25
7	ГОСТ 19903-2015	Листовая сталь t=6мм	м ²	0,5	47,10	23,55
8	ГОСТ 8509-93	Уголок L25х3 L= п. м.	м	38	1,12	42,67

Спецификация элементов площадки Пл-6

Поз.	Обозначение	Наименование	ед. изм.	Кол.	Масса ед., кг	Примечание
1	ГОСТ 8240-97	Швеллер № 12П L = п.м.	пм	9	10,44	93,96
2	ГОСТ 8639-92	Труба 80х80х4 L = 3000	шт	4	27,61	110,64
3	ГОСТ 8509-93	Уголок L63x5 L = п.м.	м	18	4,86	86,62
4	ТУ 36.26111-5-89	Лист прокатно-выкатной t=5мм	м ²	5	16,40	82,00
5	ГОСТ 19003-2015	Листовая сталь t=10мм	м ²	0,2	78,50	15,70
	ГОСТ 19003-2015	Листовая сталь t=6мм	м ²	0,1	47,10	4,71

Спецификация элементов площадки Пл-7

Поз.	Обозначение	Наименование	ед. изм.	Кол.	Масса ед. изм.	Примечание
1	ГОСТ 8240-97	Швеллер № 12П Л.п.м.	пм	48	10,44	501.12
2	ГОСТ 8639-82	Труба 80х804 L=3000	шт	6	27,66	165.96
3	ГОСТ 8509-93	Уголок Л5х5 L = п.м	м	37	4,81	178.04
4	ГОСТ 8510-86	Уголок Л50х5 L=1300	шт	24	4,90	117.62
5	ГОСТ 8568-77	Уголок Л50х5 L=п.м.	м	21	3,77	79.13
6	ТУ 36.20115-89	Лист прокатно-выкатный t=5мм	м ²	24	16,40	393.60
7	ГОСТ 19903-2015	Листовая сталь t=10мм	м ²	0.35	78,50	27.48
7	ГОСТ 19903-2015	Листовая сталь t=6мм	м ²	0,2	47,10	9.42
8	ГОСТ 8509-93	Уголок Л25х3 L = п.м.	м	21	1,12	23.58




Спецификация элементов площадки Пл-8

Поз.	Обозначение	Наименование	ед. изм.	Кол.	Масса ед., кг	Примечание
1	ГОСТ 8240-97	Швеллер № 12П Л.п.м.	пм	32	10,44	334,08
2	ГОСТ 8639-82	Труба 80х80х4 L=3000	шт	4	27,66	110,64
3	ГОСТ 8509-93	Уголок Л5х5 L = п.м.	м	23	4,81	110,68
4	ГОСТ 8510-86	Уголок Л50х5 L=1300	шт	16	4,90	78,42
5	ГОСТ 8568-77	Уголок Л50х5 L=п.м.	м	15	3,77	56,52
6	ТУ 36.2011-5-89	Лист проечно-выжигный t=5мм	м²	13,5	16,40	221,40
7	ГОСТ 19903-2015	Листовая сталь t=10мм	м²	0,2	78,50	15,70
7	ГОСТ 19903-2015	Листовая сталь t=6мм	м²	0,15	47,10	7,06
8	ГОСТ 8509-93	Уголок Л25х3 L = п.м.	м	15	1,12	16,85




Спецификация элементов площадки Пл-9

Поз.	Обозначение	Наименование	ед. изм.	Кол.	Масса ед., кг	Приме- чание
1	ГОСТ 8240-97	Швеллер № 12П п.п.м.	пм	9	10,44	93,96
2	ГОСТ 8639-92	Уголок 80х80х4 L=3000	шт	4	27,61	110,64
3	ГОСТ 8509-93	Труба L63х5 L=п.м.	м	14	48,67	67,37
4	ТУ 36.26115-89	Лист прокатно-вытесной t=5мм	м²	3,5	16,40	57,40
5	ГОСТ 19903-2015	Листовая сталь t=10мм	м²	2	28,50	15,70
	ГОСТ 19903-2015	Листовая сталь t=6мм.	м²	0,2	47,10	9,42

1. Все соединения элементов в опорах сварные. Сварку элементов бестип электродными 3424 по ГОСТ 9467-75.
2. Камен сланцевый должен принимать по наименьшей из толщин свариваемых элементов, но не менее 4 мм.
3. Стальные конструкции оцинковывать грунтовым цинком Г-021 ГОСТ 25129-82 в два слоя с последующей окраской эмалью ПФ-115 ГОСТ 6465-76 в два слоя
4. Марка стали по прочности принята для всех металлических элементов С245 по ГОСТ 27772-2009.
5. Окисляющие материалы клон с сварки элементов производиться по месту, после получения и уточнения размеров.
6. Оборудование устанавливается с использованием виброзащиты для предотвращения динамических нагрузок на конструкции здания.

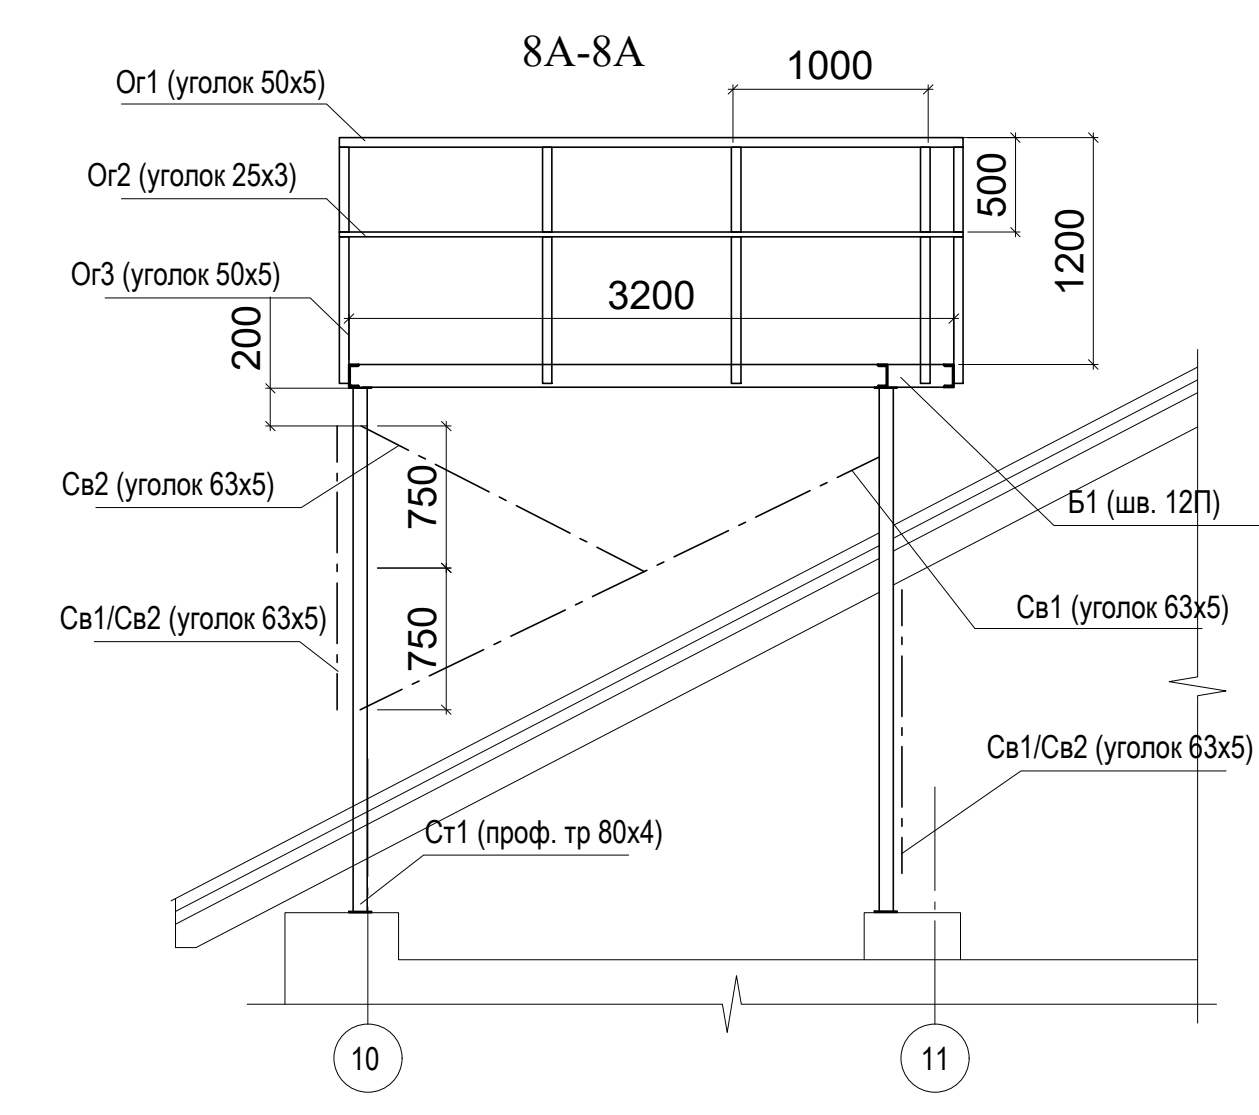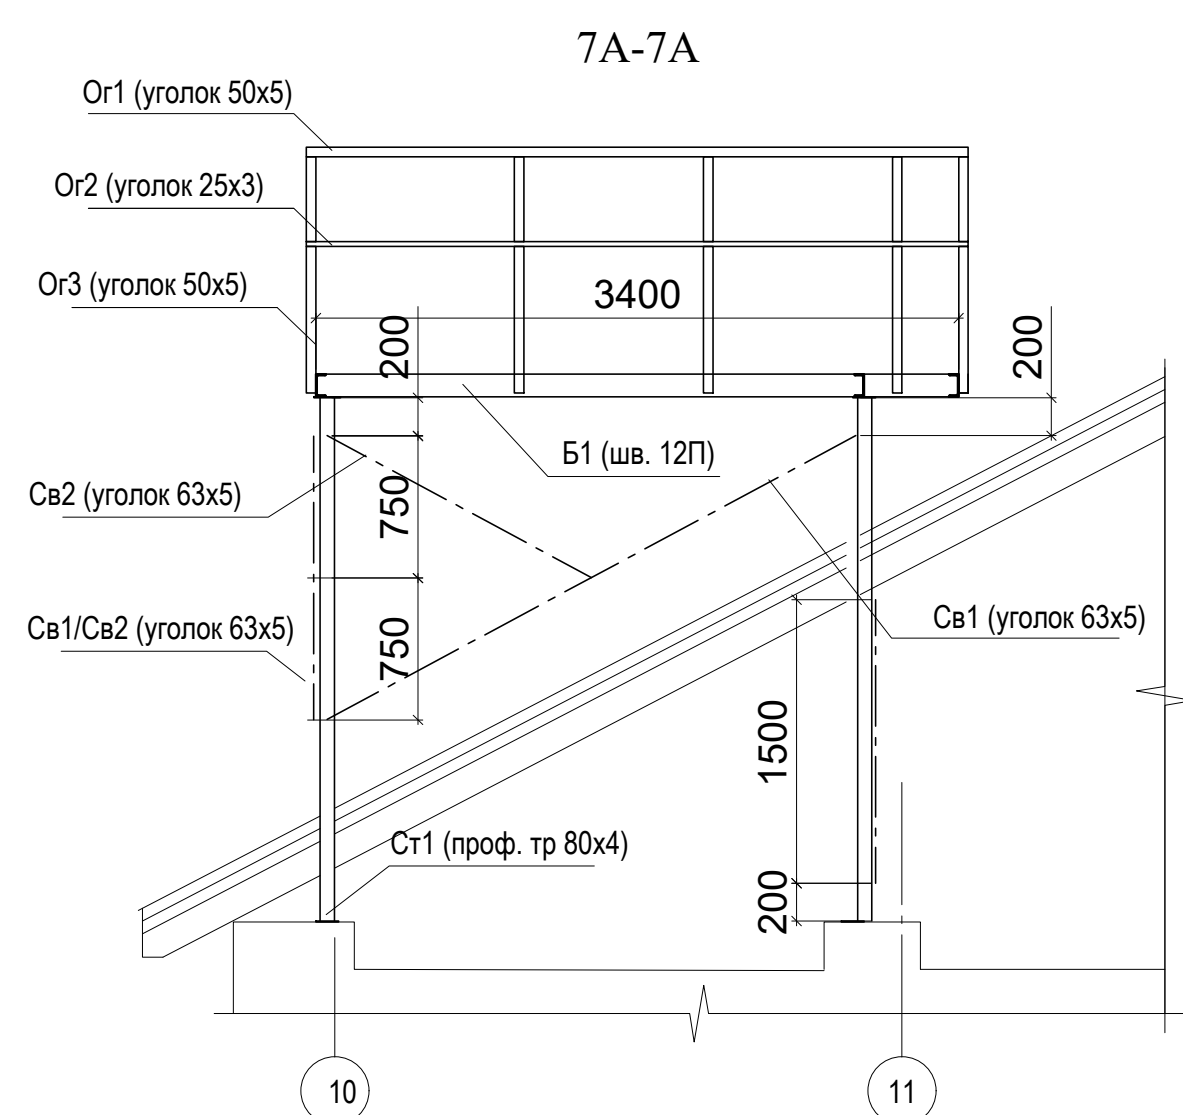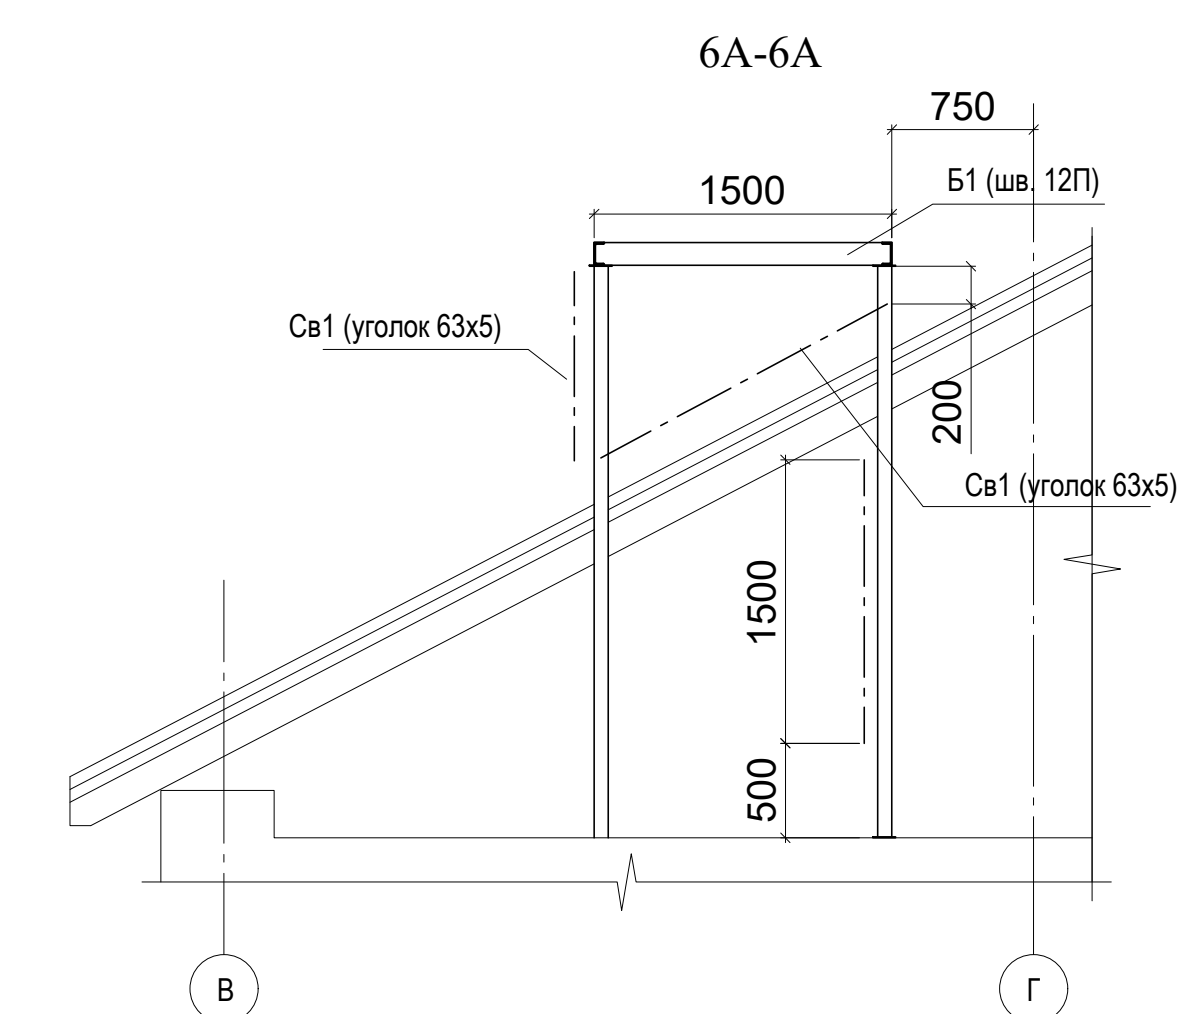

Площадка Пл-9

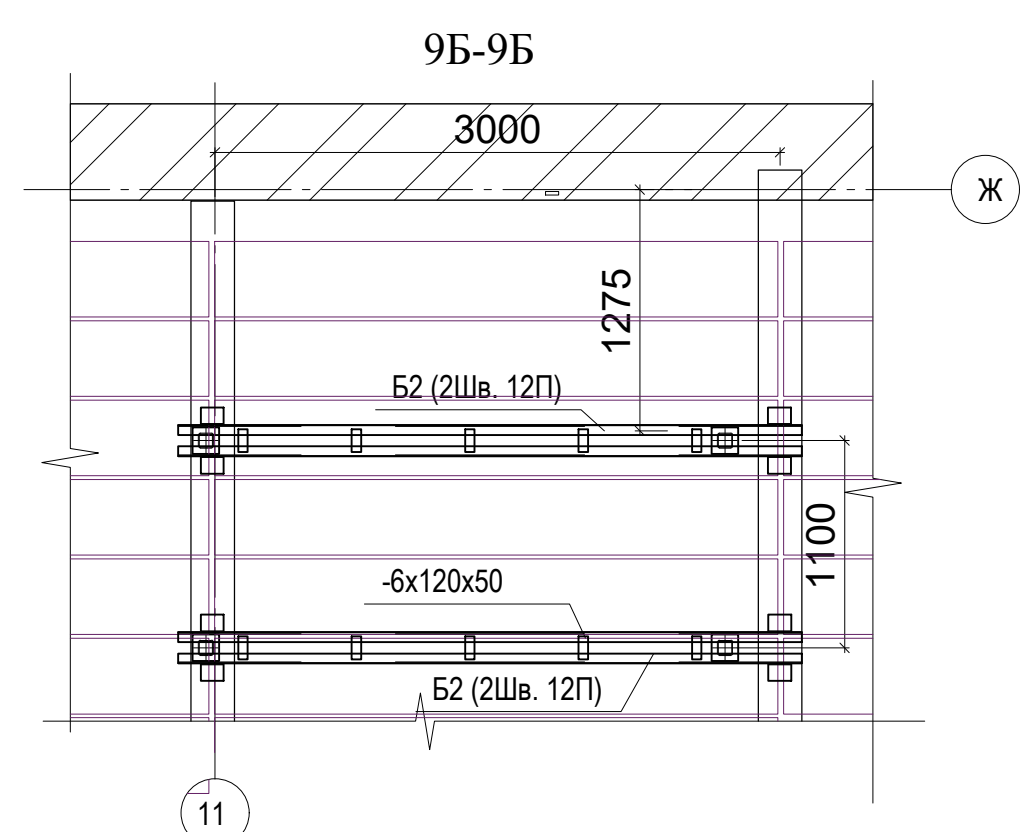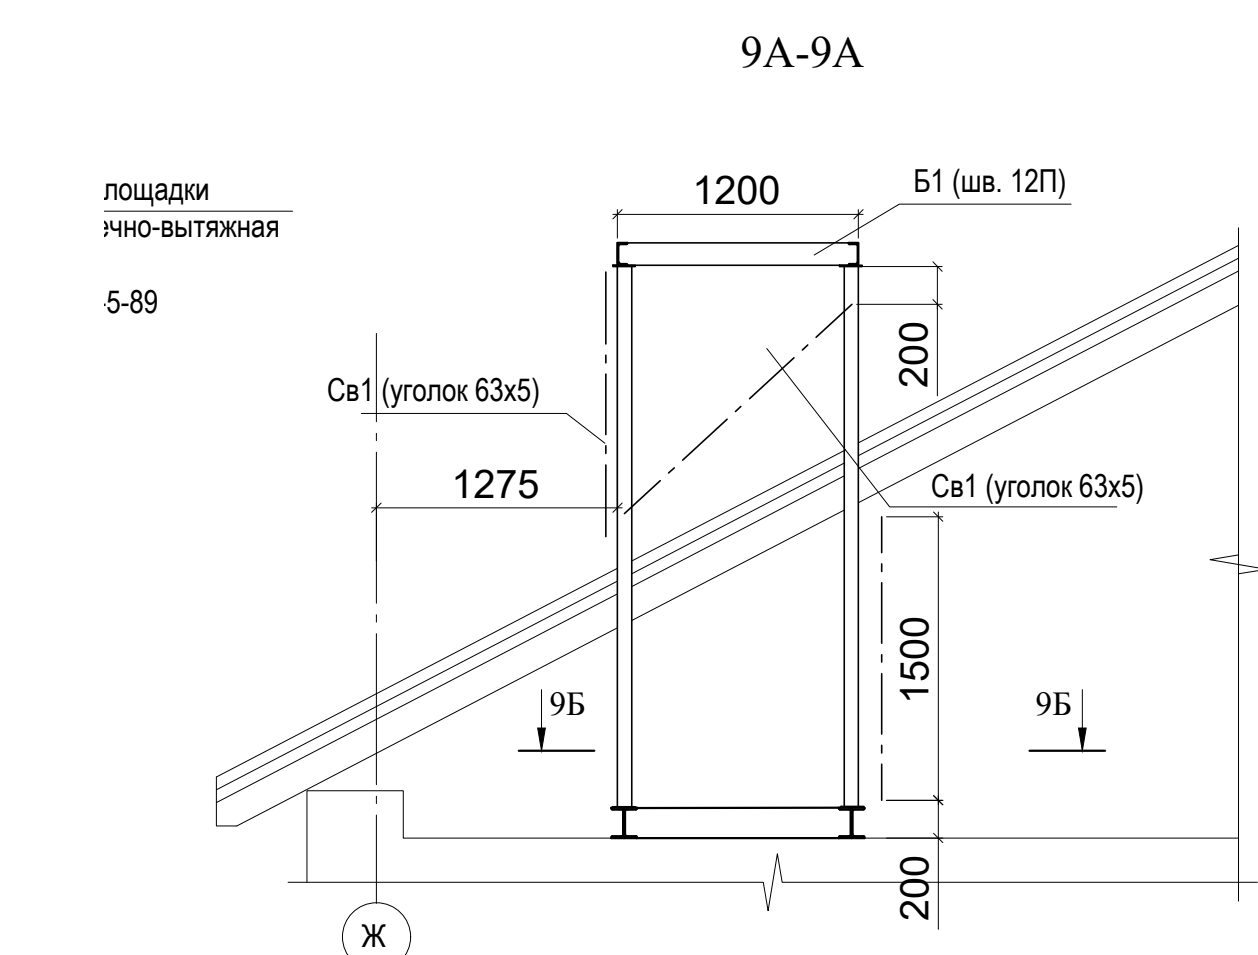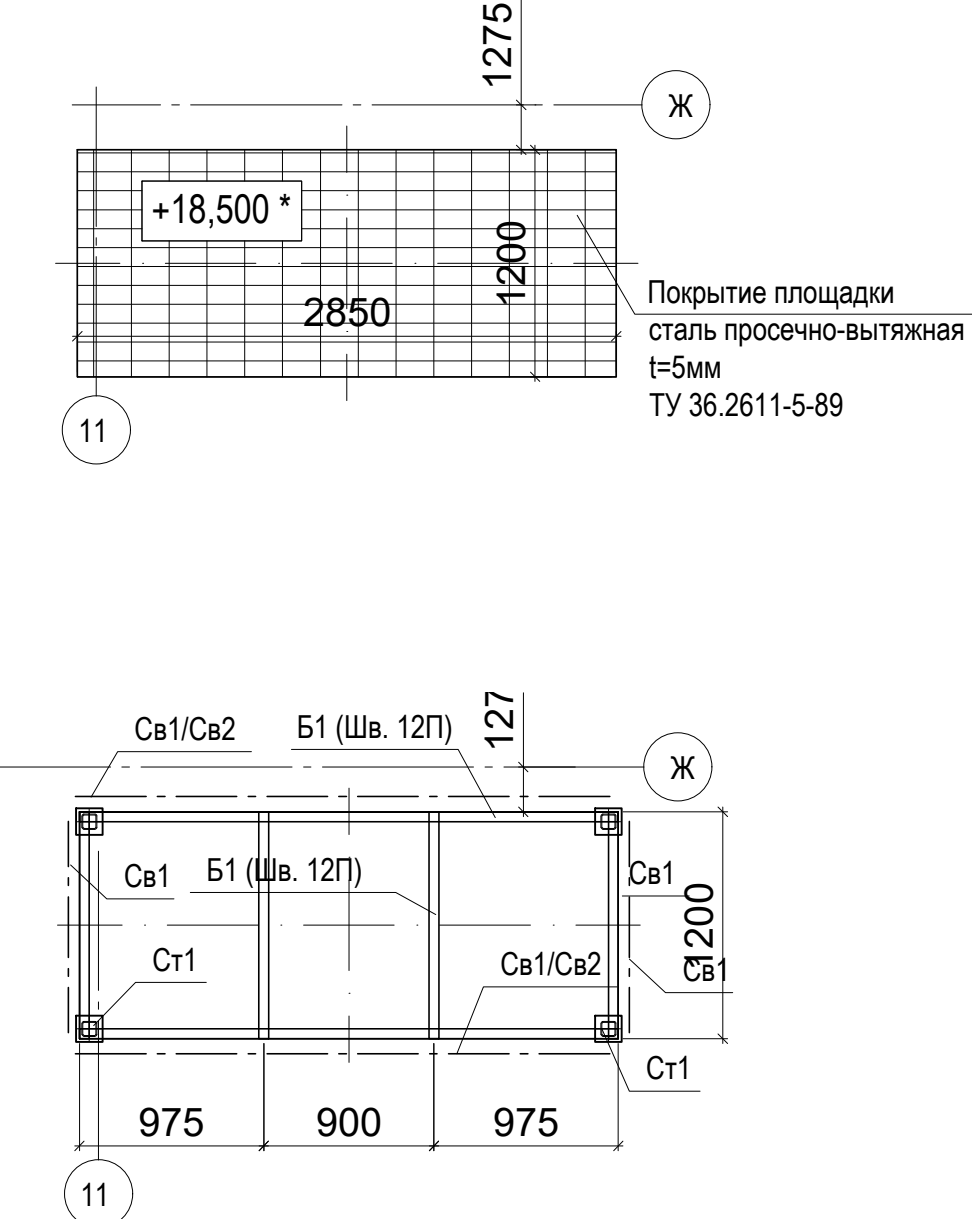

						696/П-24. АНО-КР				
						Капитальный ремонт Государственного бюджетного общеобразовательного учреждения города Москвы Школа №182 Сокольники по адресу: г. Москва, ул. Барбарина, д/п, корп.1				
Изм.	Колуч	Лист	№ док	Подпись	Дата					
Разработал:					06.26	Стандия				
Н. Контр.					06.26	Р				
Нач. Упр.					06.26	2				
						Листов				
						Конструктивные решения				
						Площади обслуживания объектов на кровле Пл-5-Пл-9, Узлы				
						000 "Проект - "				