



Узел примыкания отмостки и цоколя

Отделка фасада стеклофибробетонные рифленые панели RAL 1013 - 20 мм  
Крепежная система по типу вентилируемый фасад с вент зазором - 50 мм  
Плиты теплоизоляционные минераловатные ТЕХНОНИКОЛЬ РОКЛАЙТ - 150 мм  
Существующие стены

Отделка цоколя - натуральный камень (гранит) - 300x600x20 мм - вертикальная поверхность  
Подсистема для крепления отделки цоколя  
Плиты теплоизоляционные минераловатные ТЕХНОНИКОЛЬ РОКЛАЙТ - 150 мм  
Двухслойная гидроизоляция ТЕХНОЭЛАСТ  
Праймер битумный ТЕХНОНИКОЛЬ  
Существующие фундаментные блоки

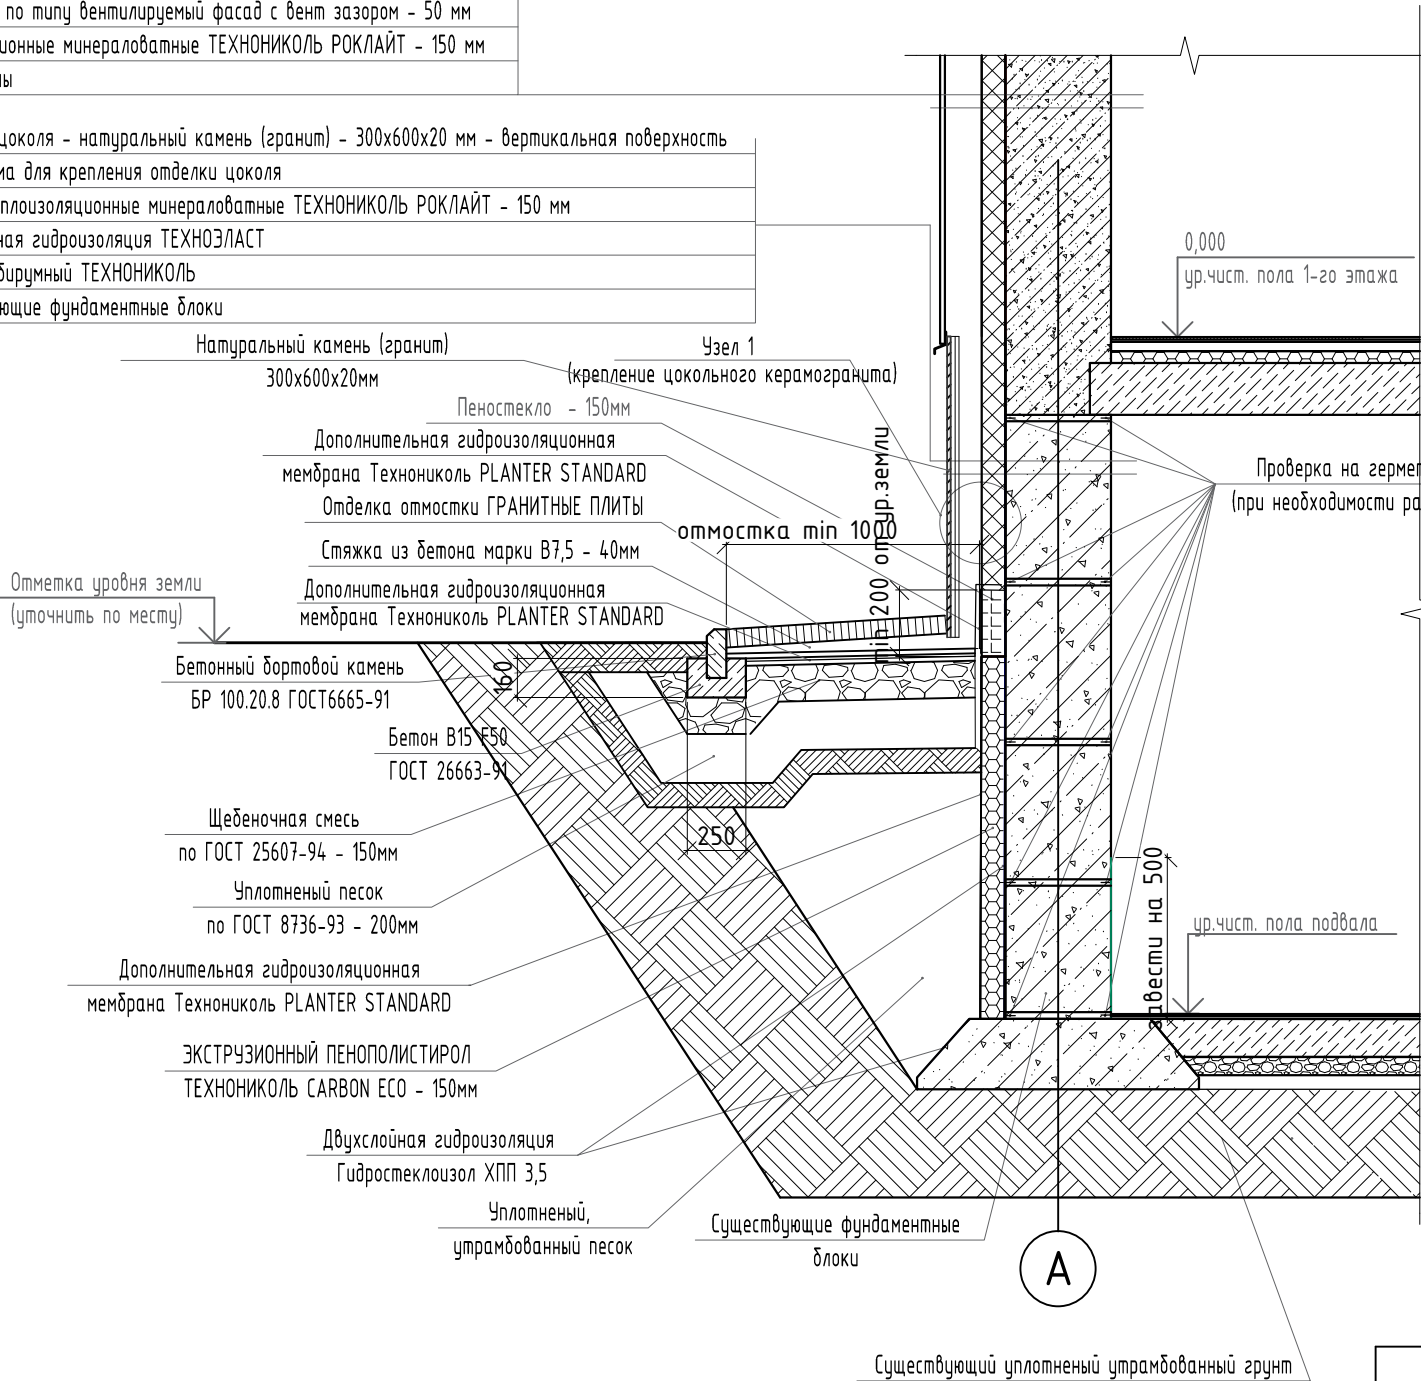

Узел 2  
(крепление цокольного керамогранита)

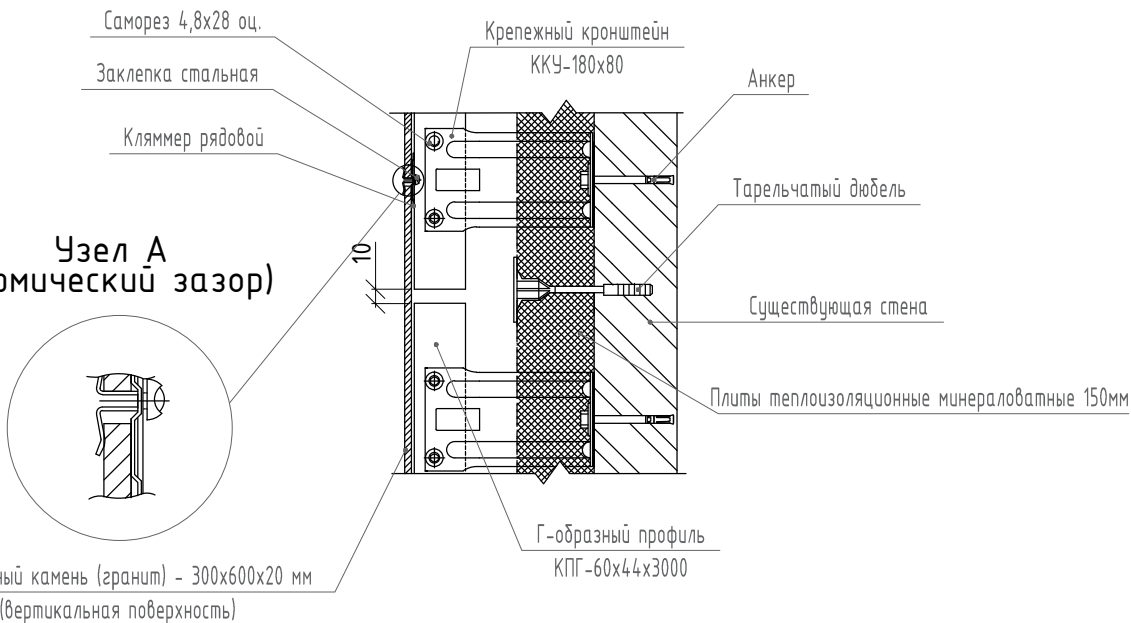

|            |          |               |        |       |       |                                               |        |      |        |
|------------|----------|---------------|--------|-------|-------|-----------------------------------------------|--------|------|--------|
|            |          |               |        |       |       | Капитальный ремонт здания                     |        |      |        |
| Изм.       | Кол. уч. | Лист          | № док. | Подп. | Дата  | Объемно-планировочные и архитектурные решения | Стадия | Лист | Листов |
| Разработал |          | Головина В.Н. |        |       | 04.25 |                                               |        |      |        |
| Проверил   |          | Набокова М.А. |        |       | 04.25 |                                               |        |      |        |
| ГИП        |          | Гулько А.Н.   |        |       | 04.25 | Узел примыкания отмостки и цоколя             |        |      |        |
| Н.контроль |          | Выходова Н.А. |        |       | 04.25 |                                               |        |      |        |