
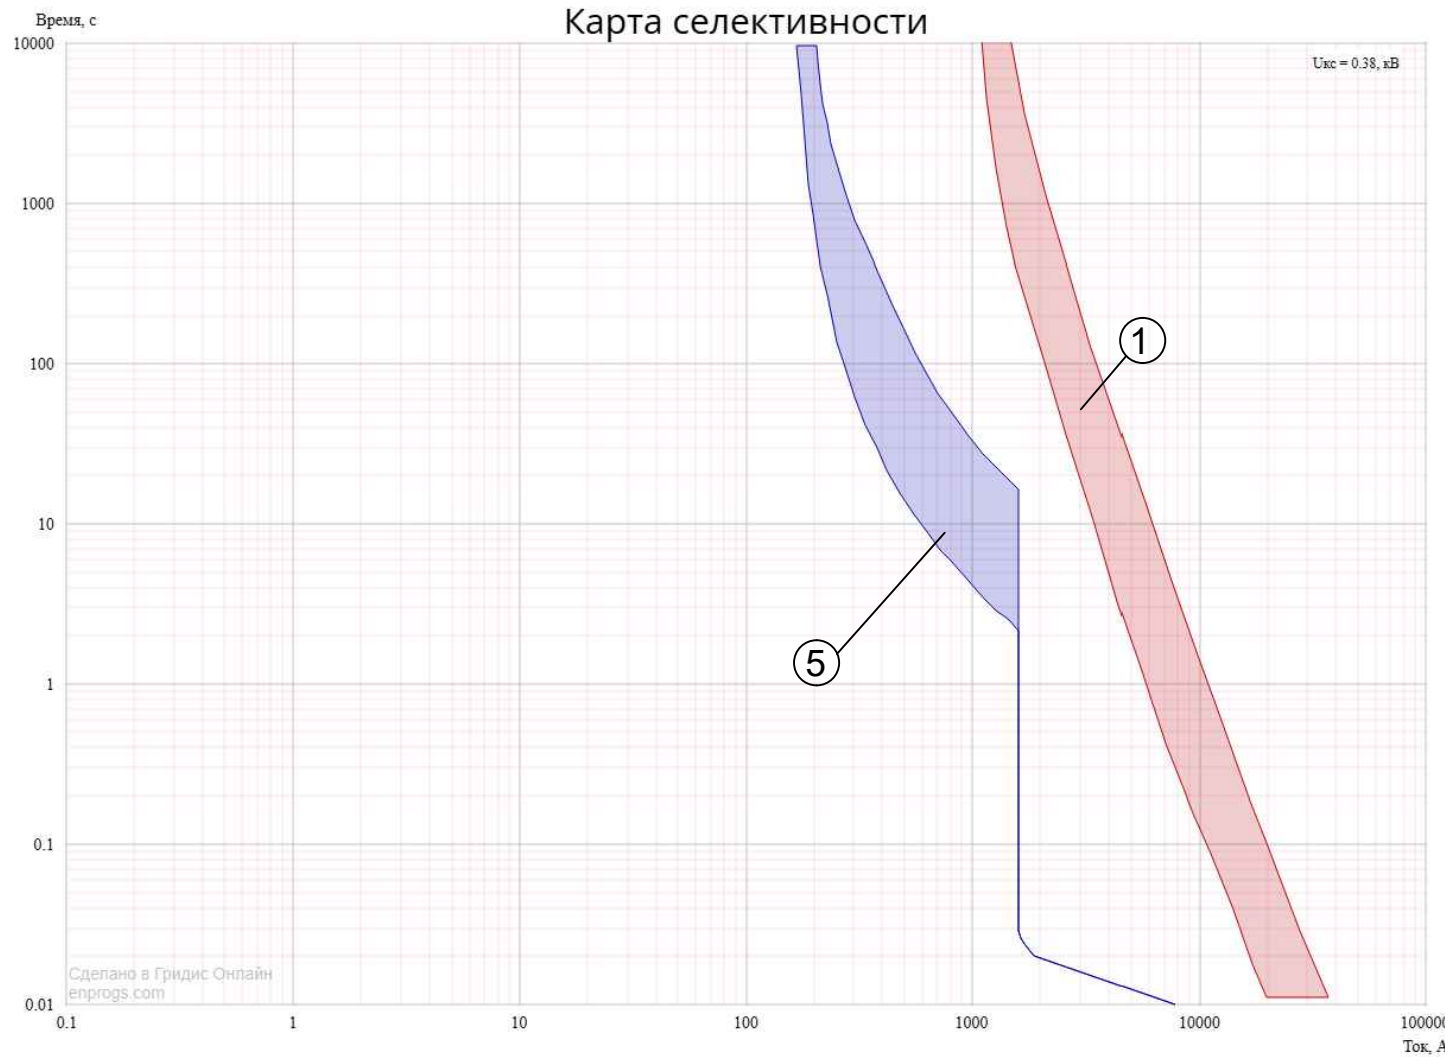
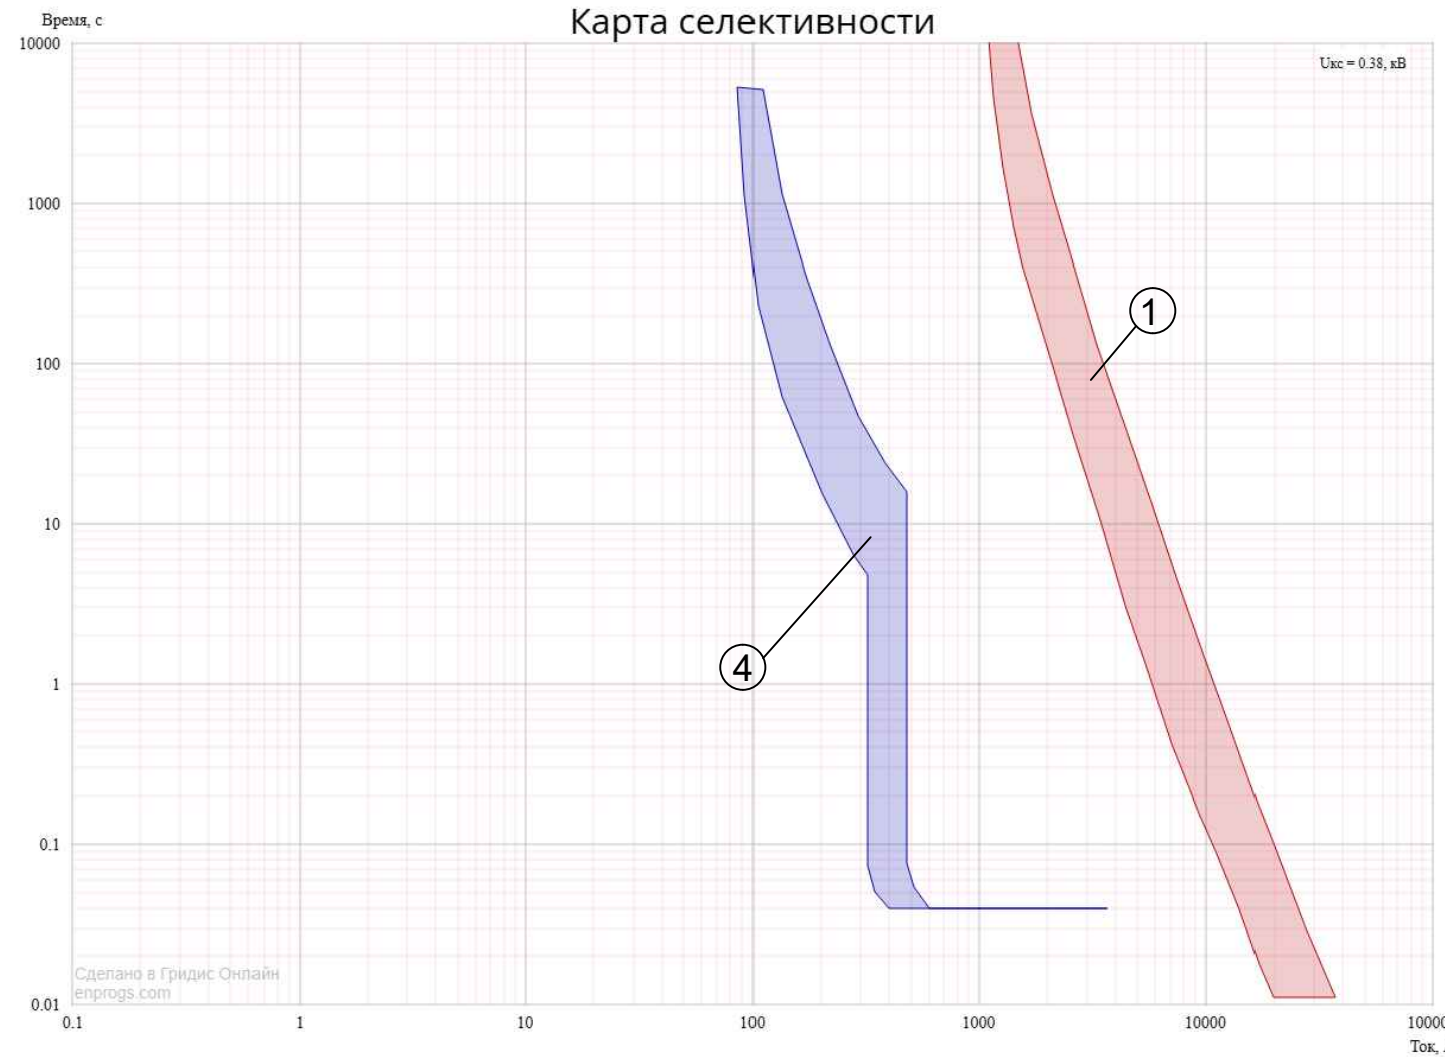
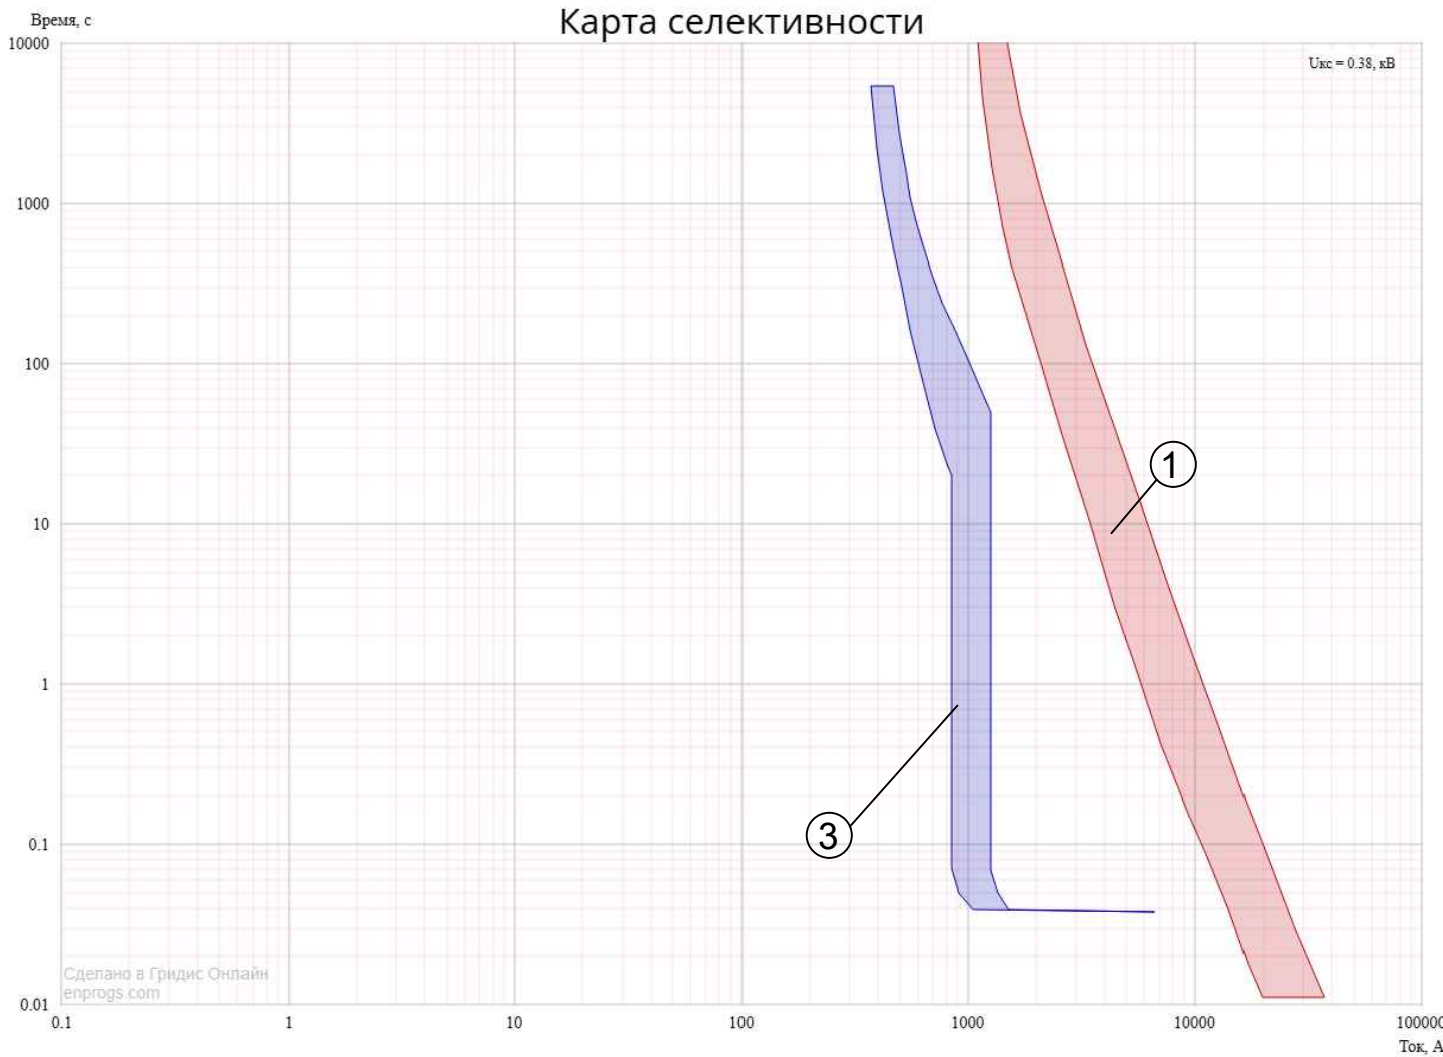


Согласовано		
Взам. инв. №		
Подпись и дата		
Инв. № подл.		

ПАО "Россети Московский регион": РУ-0,4 кВ ТП Н Нов.	Абонент ВРУ	Абонент ВРУ	Абонент (РПЗ)	Абонент ВРУ ФОК (ПЭСПЗ)
1. Предохранитель Тип gL/gG In=800A	② Автоматический выключатель AV-POWER-3/3 (10F) Тип расцепителя - термомagnetный In=400A кривая C (5-10In)	③ Автоматический выключатель AV-POWER-3/3 (20F) Тип расцепителя - термомagnetный In=315A кривая C (5-10In)	③ Автоматический выключатель Dekraft ABP-302 (QF5-1, QF5-2) Тип расцепителя - термомagnetный In=80A кривая C (5-10In)	④ Автоматический выключатель Dekraft ABP-300 (QF6-1, QF6-2) Тип расцепителя - термомagnetный In=160A кривая C (5-10In)

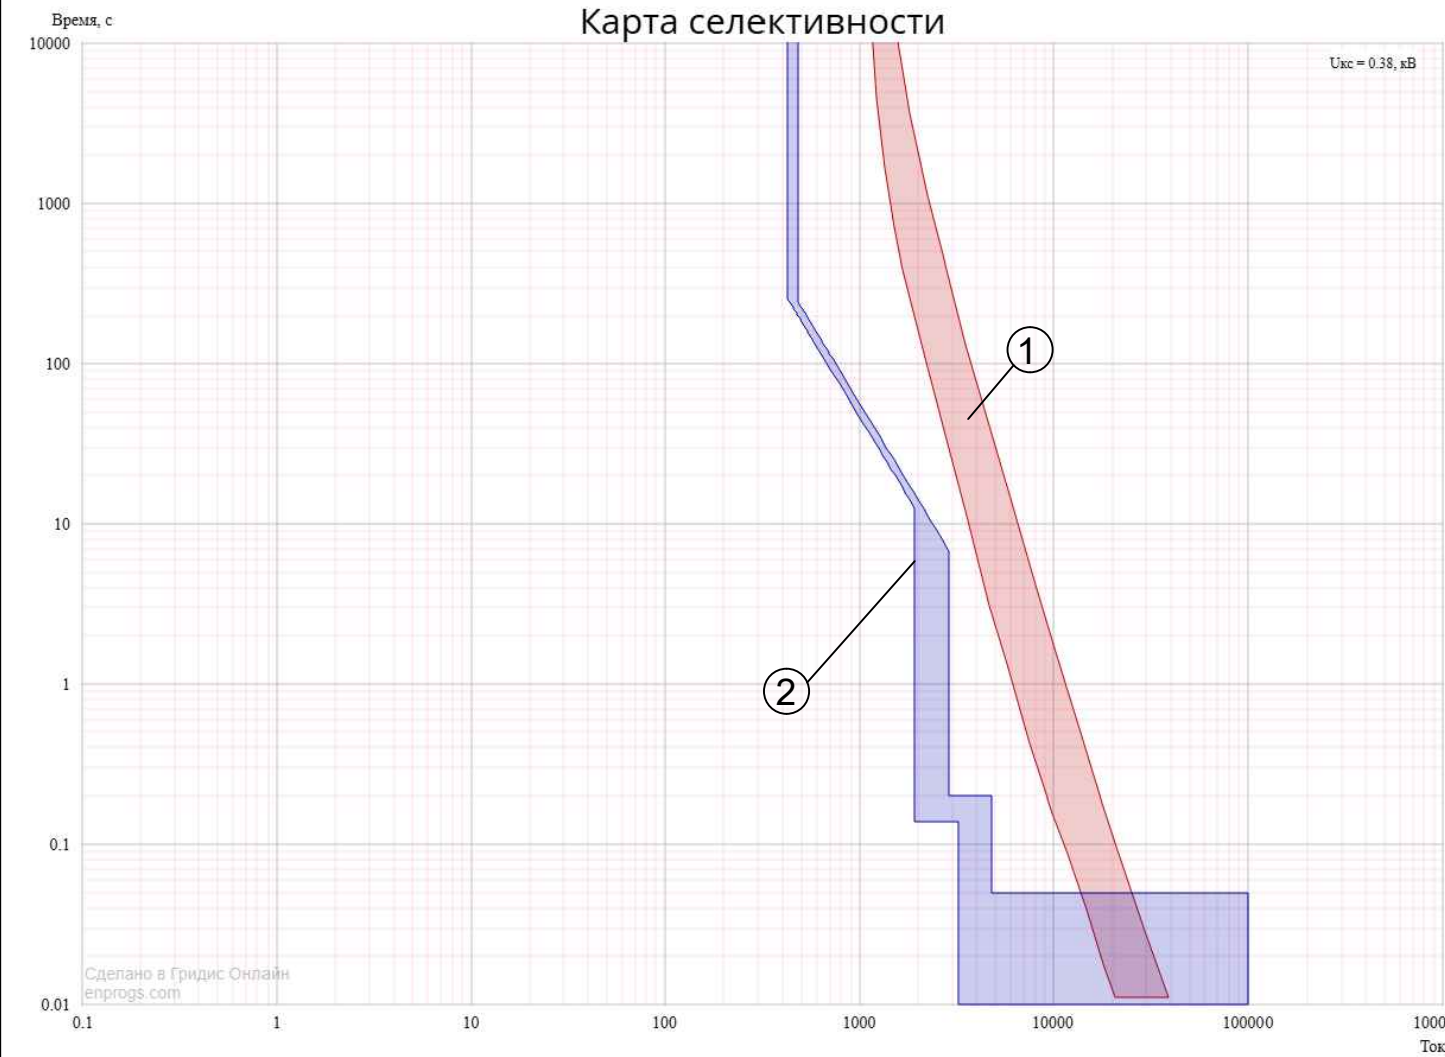

						696/П-25-АНО-Р-30М
						Здание по адресу: г. Москва, ул. Барболина, д.1, корп.1
Изм.	Кол.уч.	Лист	№ док.	Подп.	Дата	Капитальный ремонт Государственного бюджетного общеобразовательного учреждения города Москвы Школа №1282
Разраб.	Никитин				07.26	
ГИП	Гулько				07.26	Карта селективности ГРЩ -1282
Н. контр.	Гулько				07.26	ООО "ПРОЕКТ+"
						Формат