
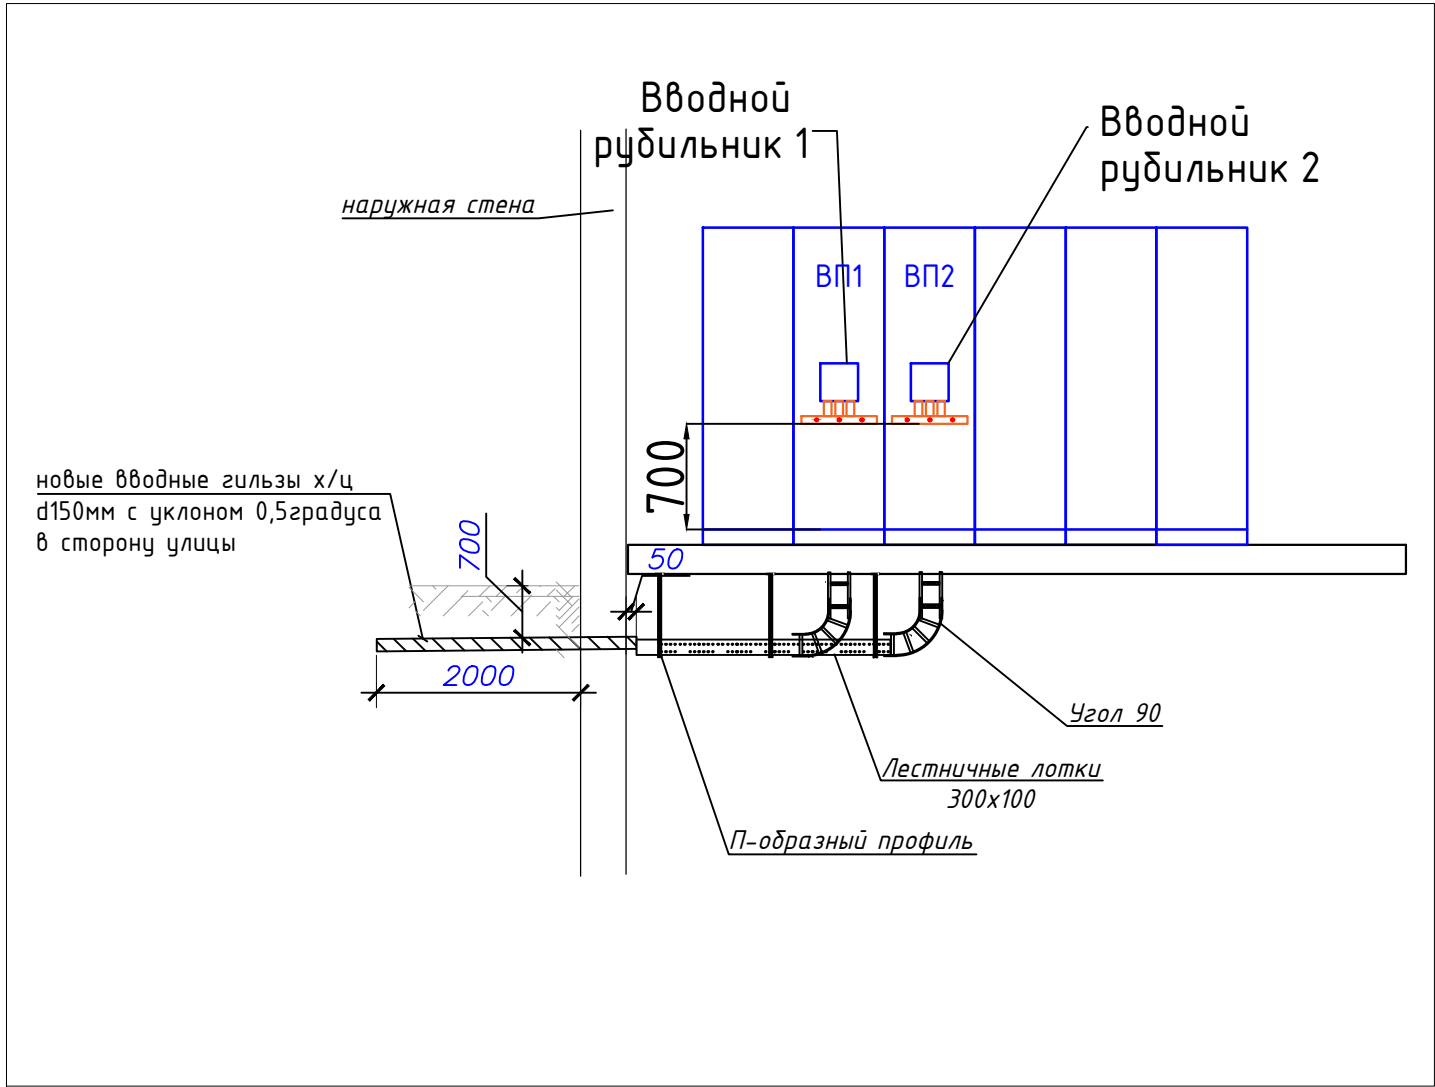
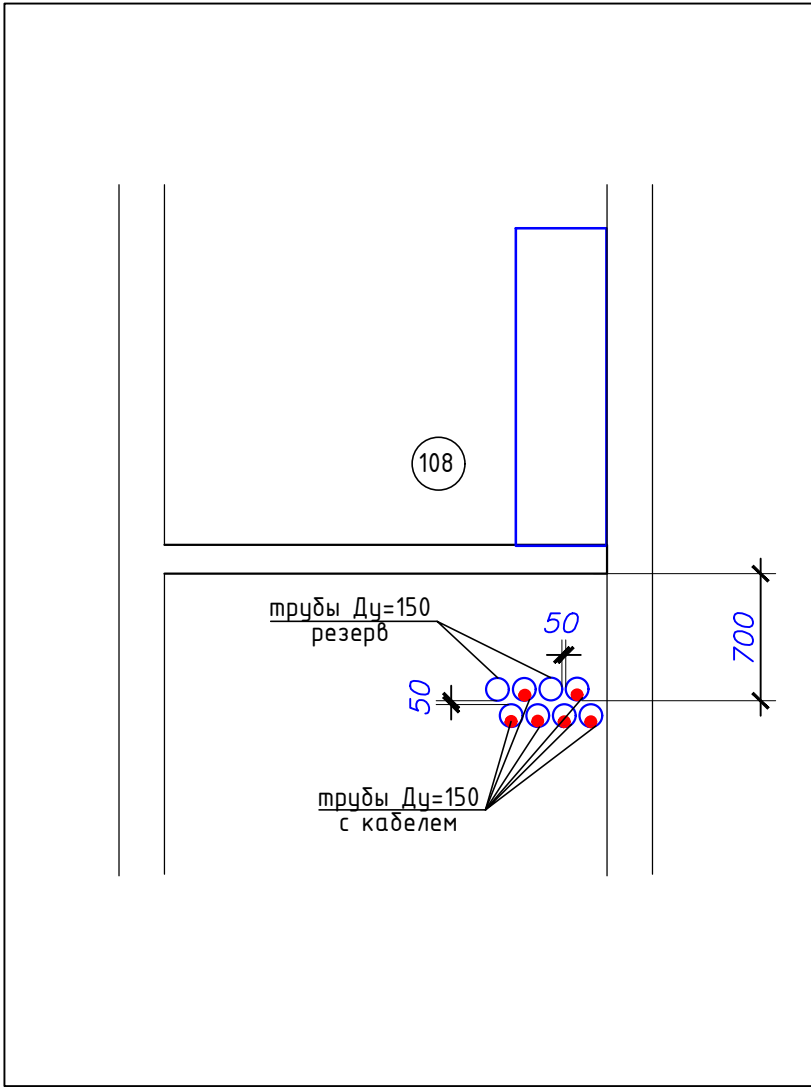


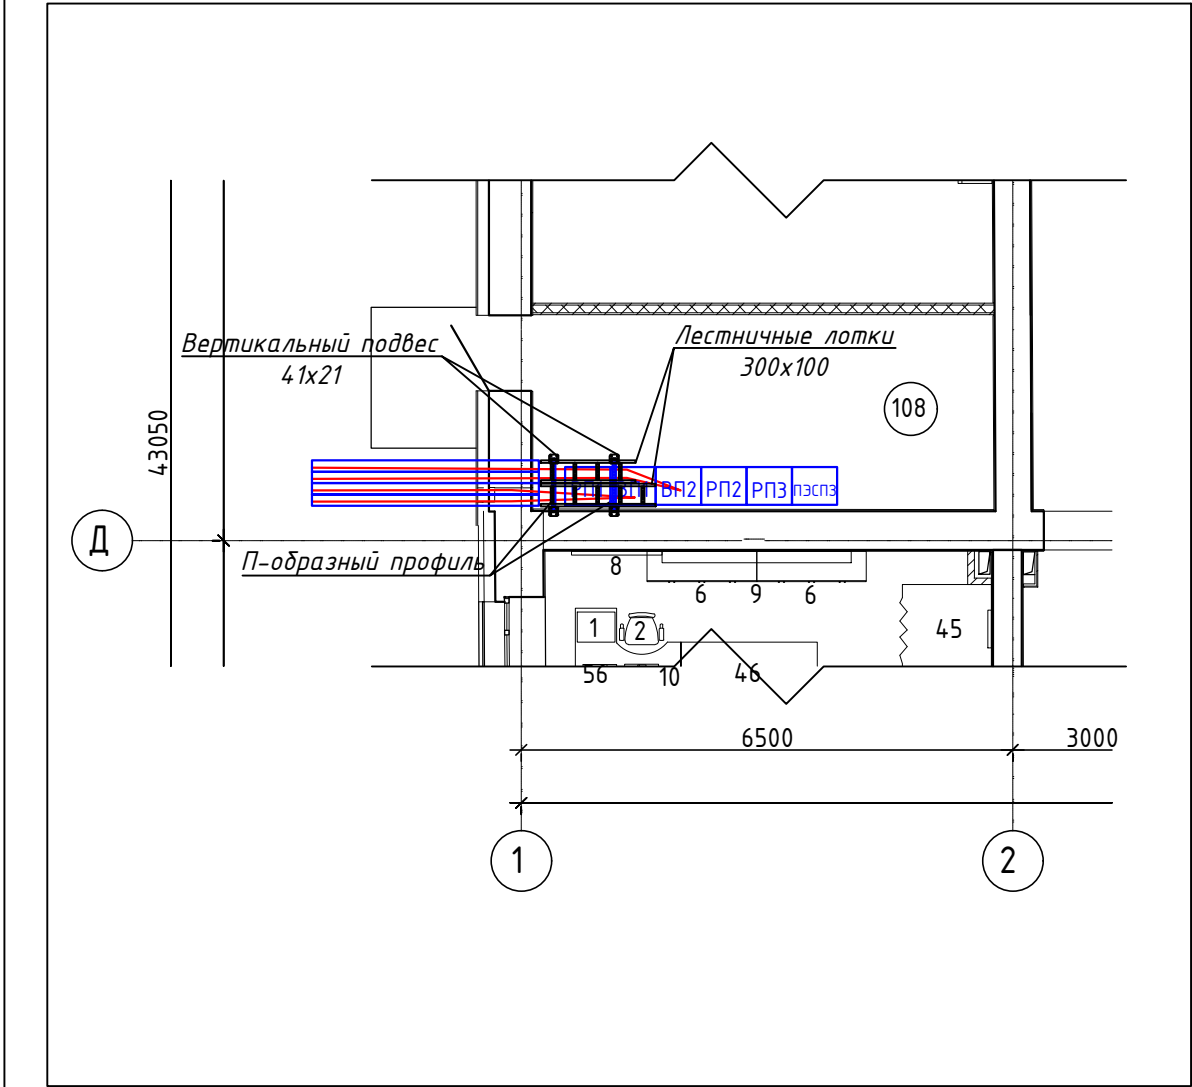

Условные обозначения

- | | |
|--|--------------------------------|
| | лоток лестничный 300x100мм |
| | Угол 90 градусов 300x100 |
| | П-образный профиль PSL |
| | Вертикальный подвес 41x21 L700 |
| | Труба х/ц d150мм |

						696/П-25-АНО-Р-30М			
						Здание по адресу: г. Москва, ул. Барболина, д.1, корп.1			
Изм.	Кол.уч	Лист	№ док.	Подп.	Дата	Капитальный ремонт Государственного бюджетного общеобразовательного учреждения города Москвы Школа №1282	Стадия	Лист	Листов
Разраб.			Никитин		07.26		Р	54	
ГИП			Гулько		07.26				
						Ввод кабельных линий 0,4 кВ в здание			
Н. контр.			Гулько		07.26				