

109548, г. Москва, Муниципальный Округ Печатники, ул. Шоссейная, д. 19, к. 1,
кв.117 e-mail PROEKTplus-work@yandex.ru

Свидетельство № СРО- П-110-009723217107-0532

**Капитальный ремонт Государственного Бюджетного
Общеобразовательного Учреждения города Москвы
«Школа № 1282 «Сокольники»
по адресу: г. Москва, ул. Барболина, д. 1, корп. 1
1 этап**

РАБОЧАЯ ДОКУМЕНТАЦИЯ

Система электроснабжения

696/П-24-АНО-Р-ЭОМ

Генеральный директор

Главный инженер проекта




Н.А. Выходова

А.Н. Гулько

2026


Име. № подл.	Подп. И дата	Взам. инв. №

План 1 этажа

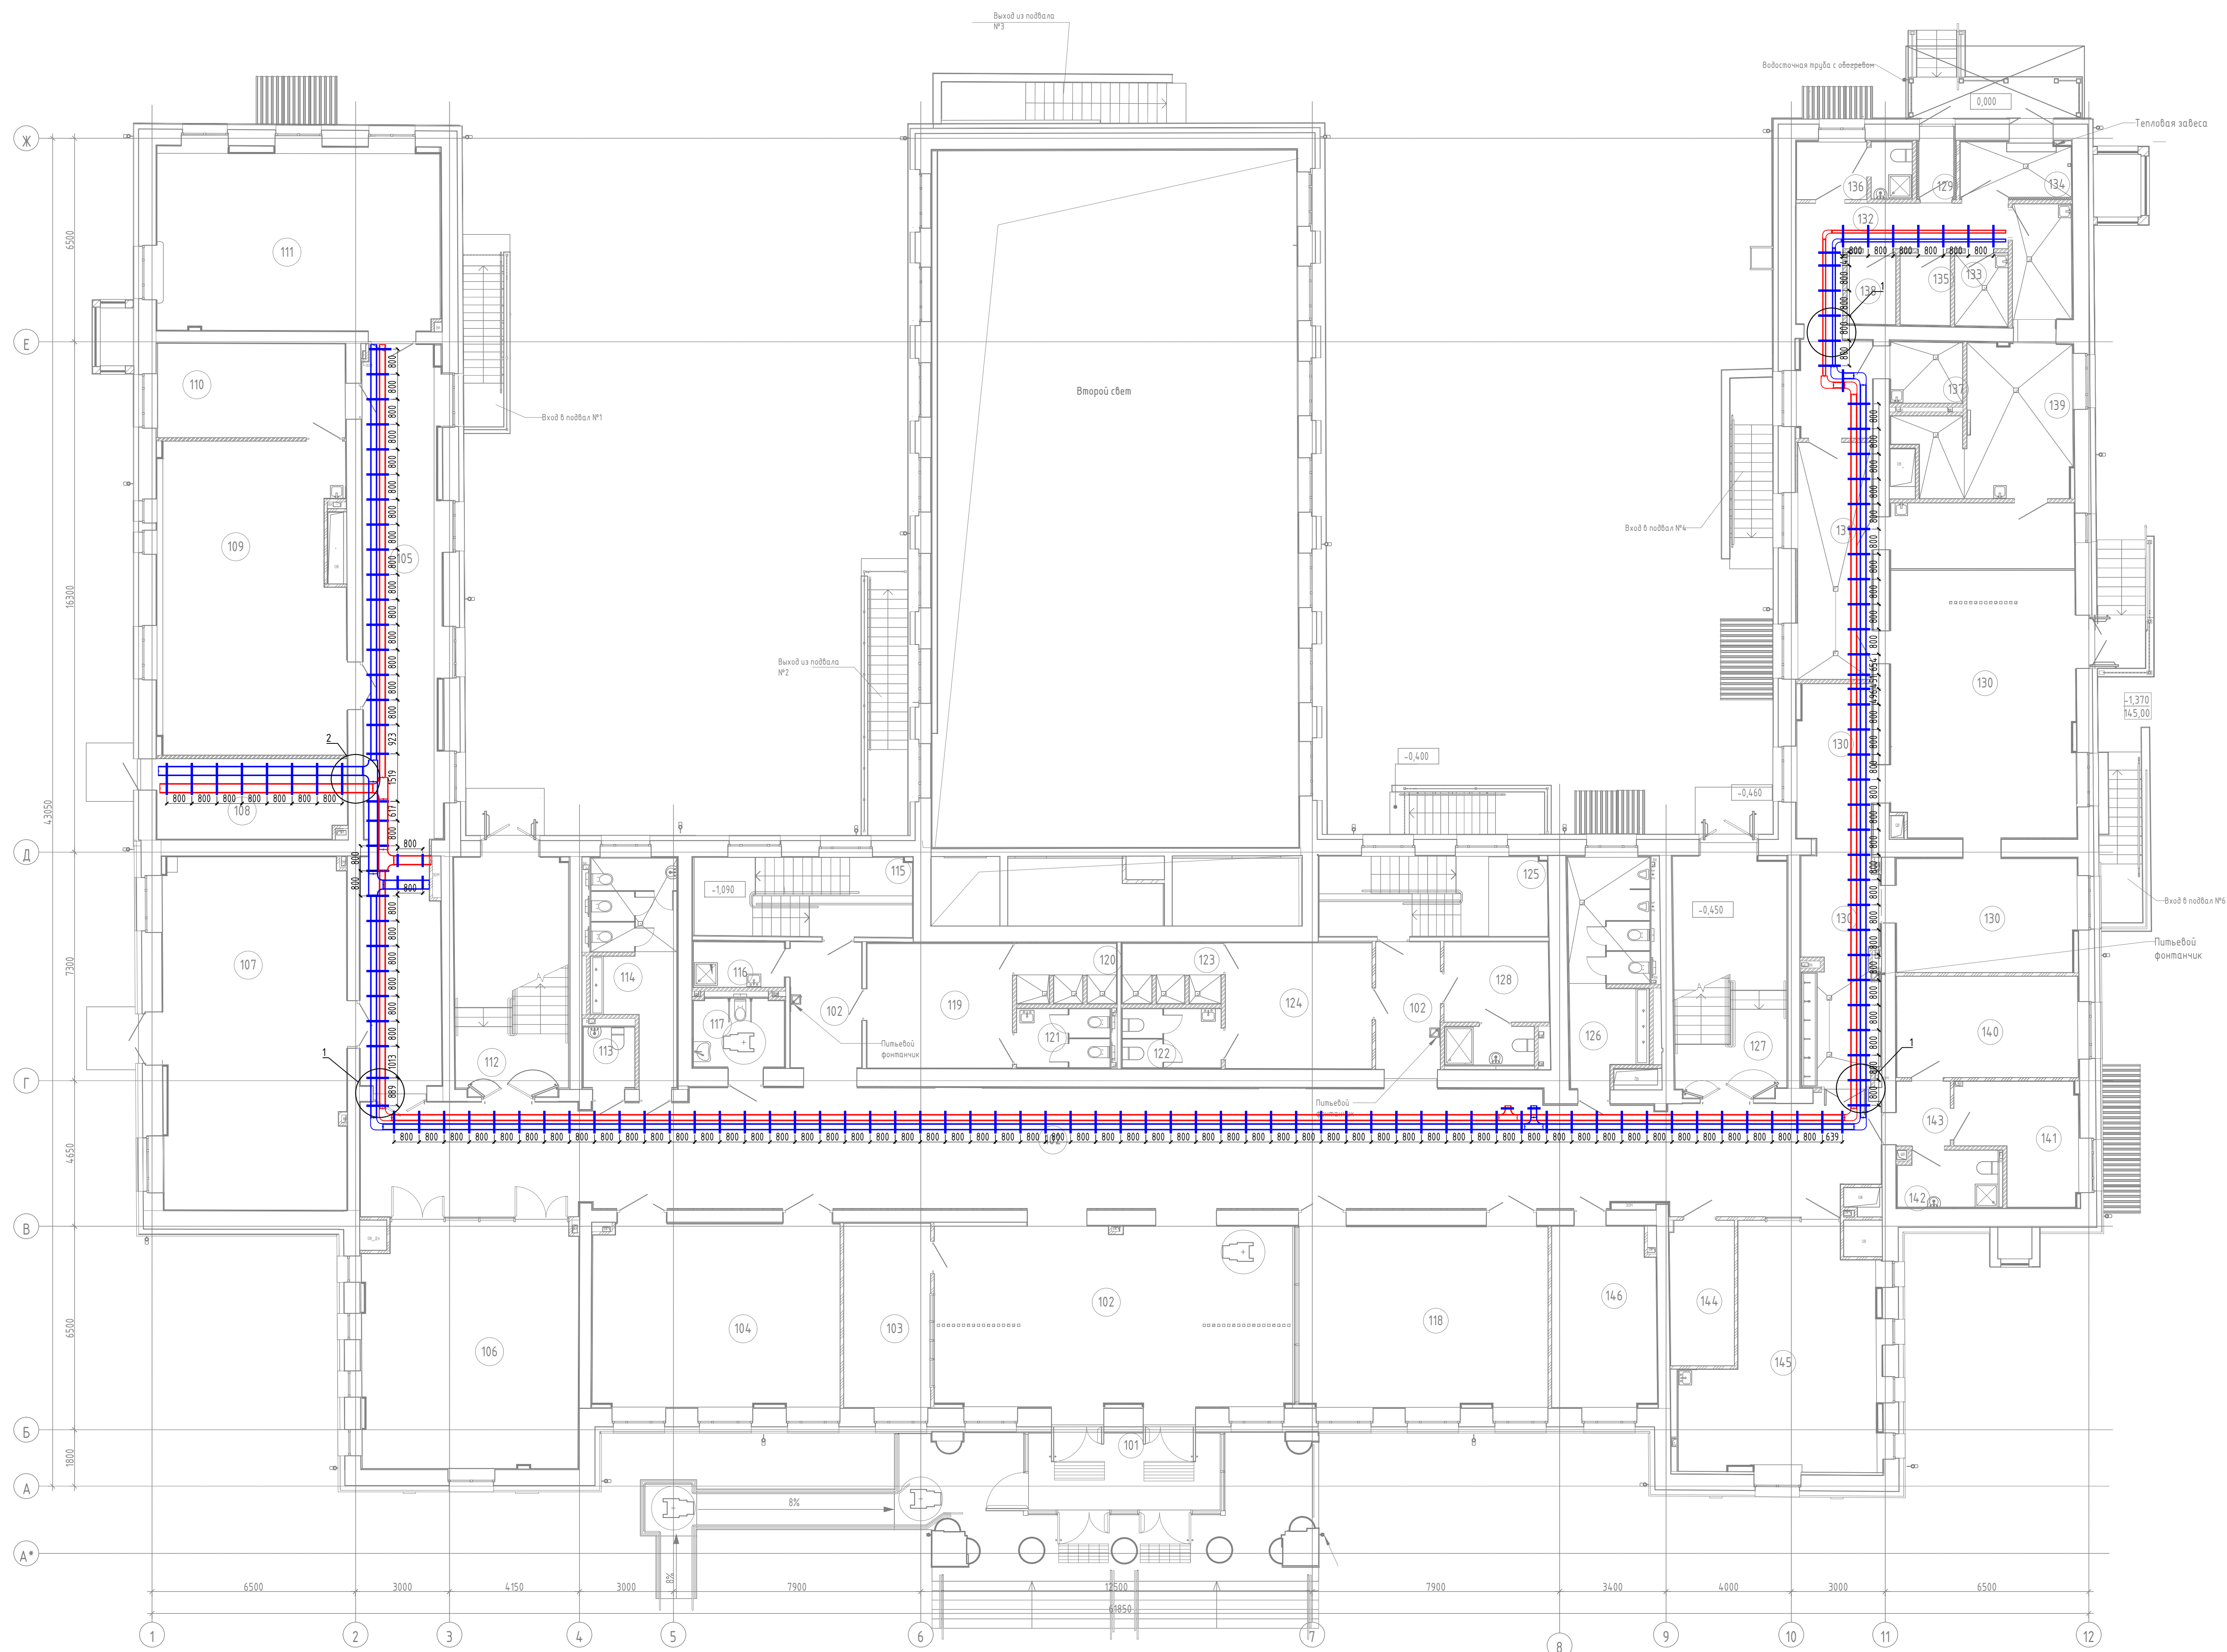

Экспликация помещений 1-го этажа			
Номер помещения	Наименование	Площадь, м²	Кот. помещения
101	Гамбур	12,5	
102	Вестибиль	287,7	
103	Комната охраны (с диспетчерским пунктом)	18,2	
104	Гардероб для обучающихся	46,2	
105	Коридор	59,9	
106	Гардероб для обучающихся	53,7	
107	Учебный кабинет (Тип 1)	66,1	
108	Электрощитовая	15,5	Б3
109	Учебный кабинет (Тип 2)	58,5	
110	Кладовая	18,0	Б3
111	Учебный кабинет (металлтика)	53,3	
112	Лестничная клетка (Тип А1)	27,8	
113	Туалет для персонала	3,3	
114	Ванная для девочек	17,0	
115	Технологическая лестница	17,8	
116	ПМ	4,6	Б4
117	Экспериментальная уборная для МГН	6,6	
118	Гардероб для обучающихся	46,4	
119	Раздевальня Тип 1	18,7	
120	Душевая	6,3	
121	Ванная	5,7	
122	Ванная	6,1	
123	Душевая	6,2	
124	Раздевальня Тип 1	18,8	
125	Технологическая лестница	18,9	
126	Ванная для мальчиков	18,4	
127	Лестничная клетка (Тип А1)	27,8	
128	Тренировочная с санузлом	12,1	
129	Гамбур	2,2	
130	Обеденный зал	114,5	
131	Мачеха для столовой посуды	18,4	Б4
132	Коридор	21,2	
133	Кладовая и мясная оборотной тары	4,0	Б4
134	Загрузочный цех	6,6	Б4
135	Кладовая сухих продуктов	3,7	Б4
136	Помещение персонала с санузлом	6,0	
137	Помещение для временного хранения пищевых отходов	4,8	Б4
138	ПМ	3,5	Б4
139	Помещение подготовки блюд к реализации с участком мойки кухонной посуды	29,2	Б4
140	Кабинет врача	18,7	
141	Процедурный (прибавочный) кабинет	12,9	
142	Помещение для хранения уборочного инвентаря, приготовления дезинфицирующих растворов	5,5	Б4
143	Офисная медбокс	3,4	
144	Помещение СС	9,5	Б4
145	Кабинет с рабочим пространством для учителей. Тип 1	41,5	
146	Гардероб для учителей	19,1	
Итого:		1254,5	


Огнестойкая проходка через стену.

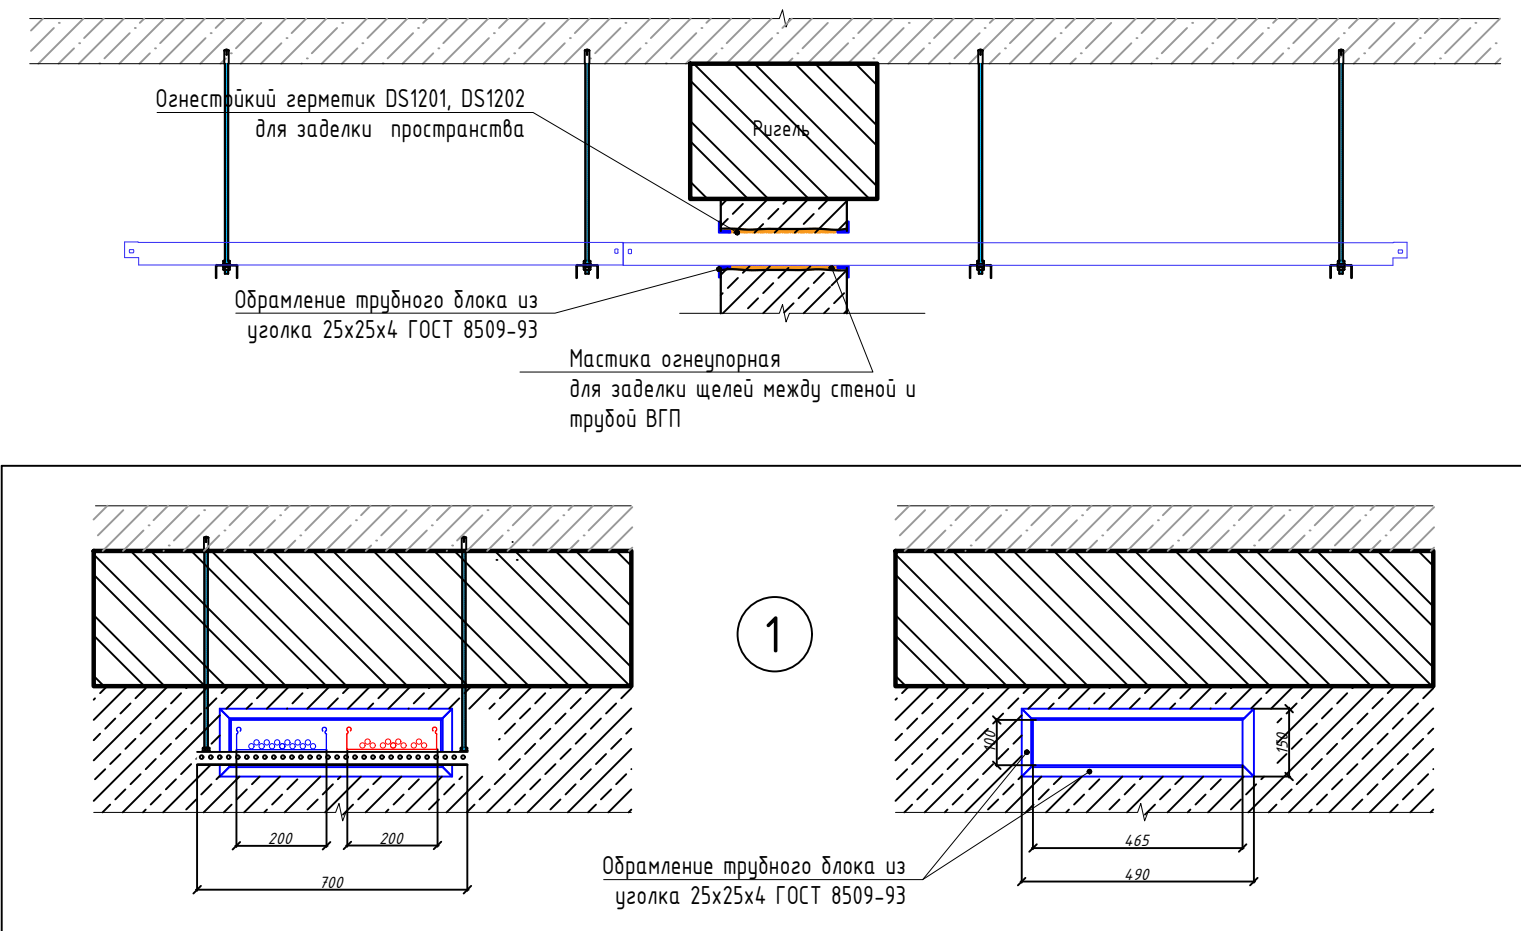


Узел крепления кабельной трассы

№	Обозначение	Наименование
1	СН4.08030	Анкер заливной М8
2	СН4.08032	Шпилька резьбовая М8
3	ВРЛ290*	Профиль PSL
4	СН10800	Гайка М8
5	СН10800	Шайба 8

Размер и марки профиля отмечены знаком "*" уточнить при монтаже

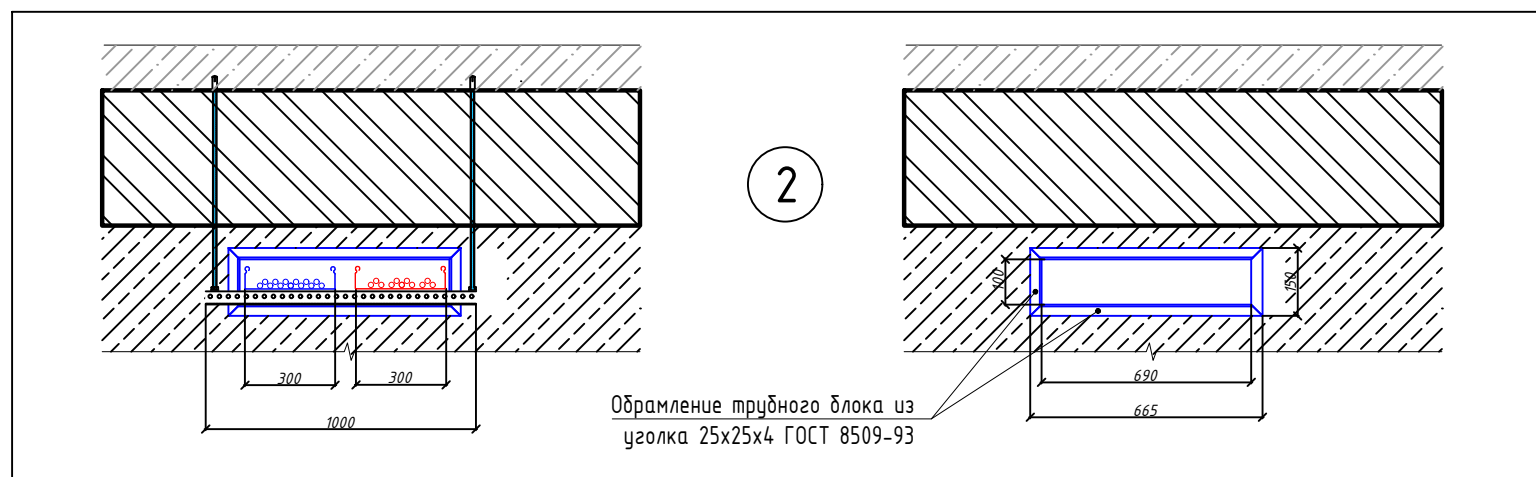

Огнестойкая проходка через перекрытие М 120

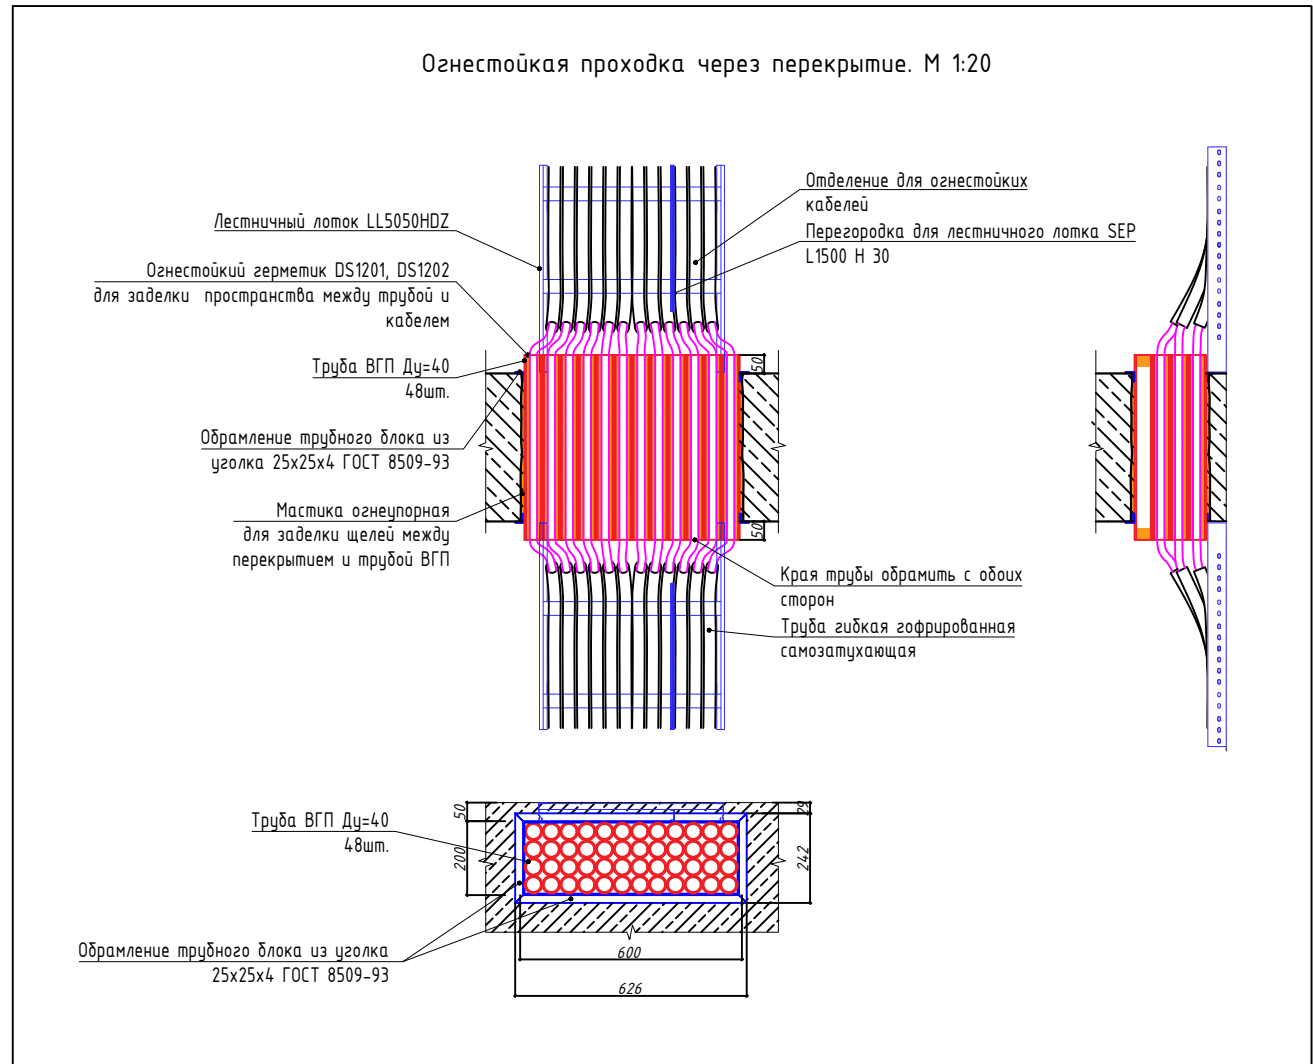

- Примечания:
1. Электропроектировщик РАЗРЕШАЕТ трассы прокладки кабельных трасс - корректировать самостоятельно по месту, исходя из структуры потолка и наличия инженерных систем.
 2. Проект проектировщик 120/101 кабельные конструкции для систем вынужденного электроснабжения.
 3. Кабели на разрезах кабельных трасс показаны условно.
 4. Расстояние между точками крепления кабельных трасс принять не более 800мм, при невозможности обеспечения такого расстояния допускается увеличение до 1000мм.
 5. Крышки лотков на разрезах кабельных конструкций не показаны.


696/П-25-АНО-Р-30М

Здание по адресу: г. Москва, ул. Барвиха, д.1, корп.1

Имя	Вол	Лист	№ док	Подп	Дата	Контент	Статус	Лист	Листов
Разработ	Гуляка	Иванов	07.26		07.26	Капитальный ремонт Государственного бюджетного общеобразовательного учреждения города Москвы Школа №1282	Р	1	
Н. контр.	Гуляка	Иванов	07.26		07.26	План кабельных конструкций сетей вынужденного электроснабжения 1 этажа			


Формат

План 2 этажа

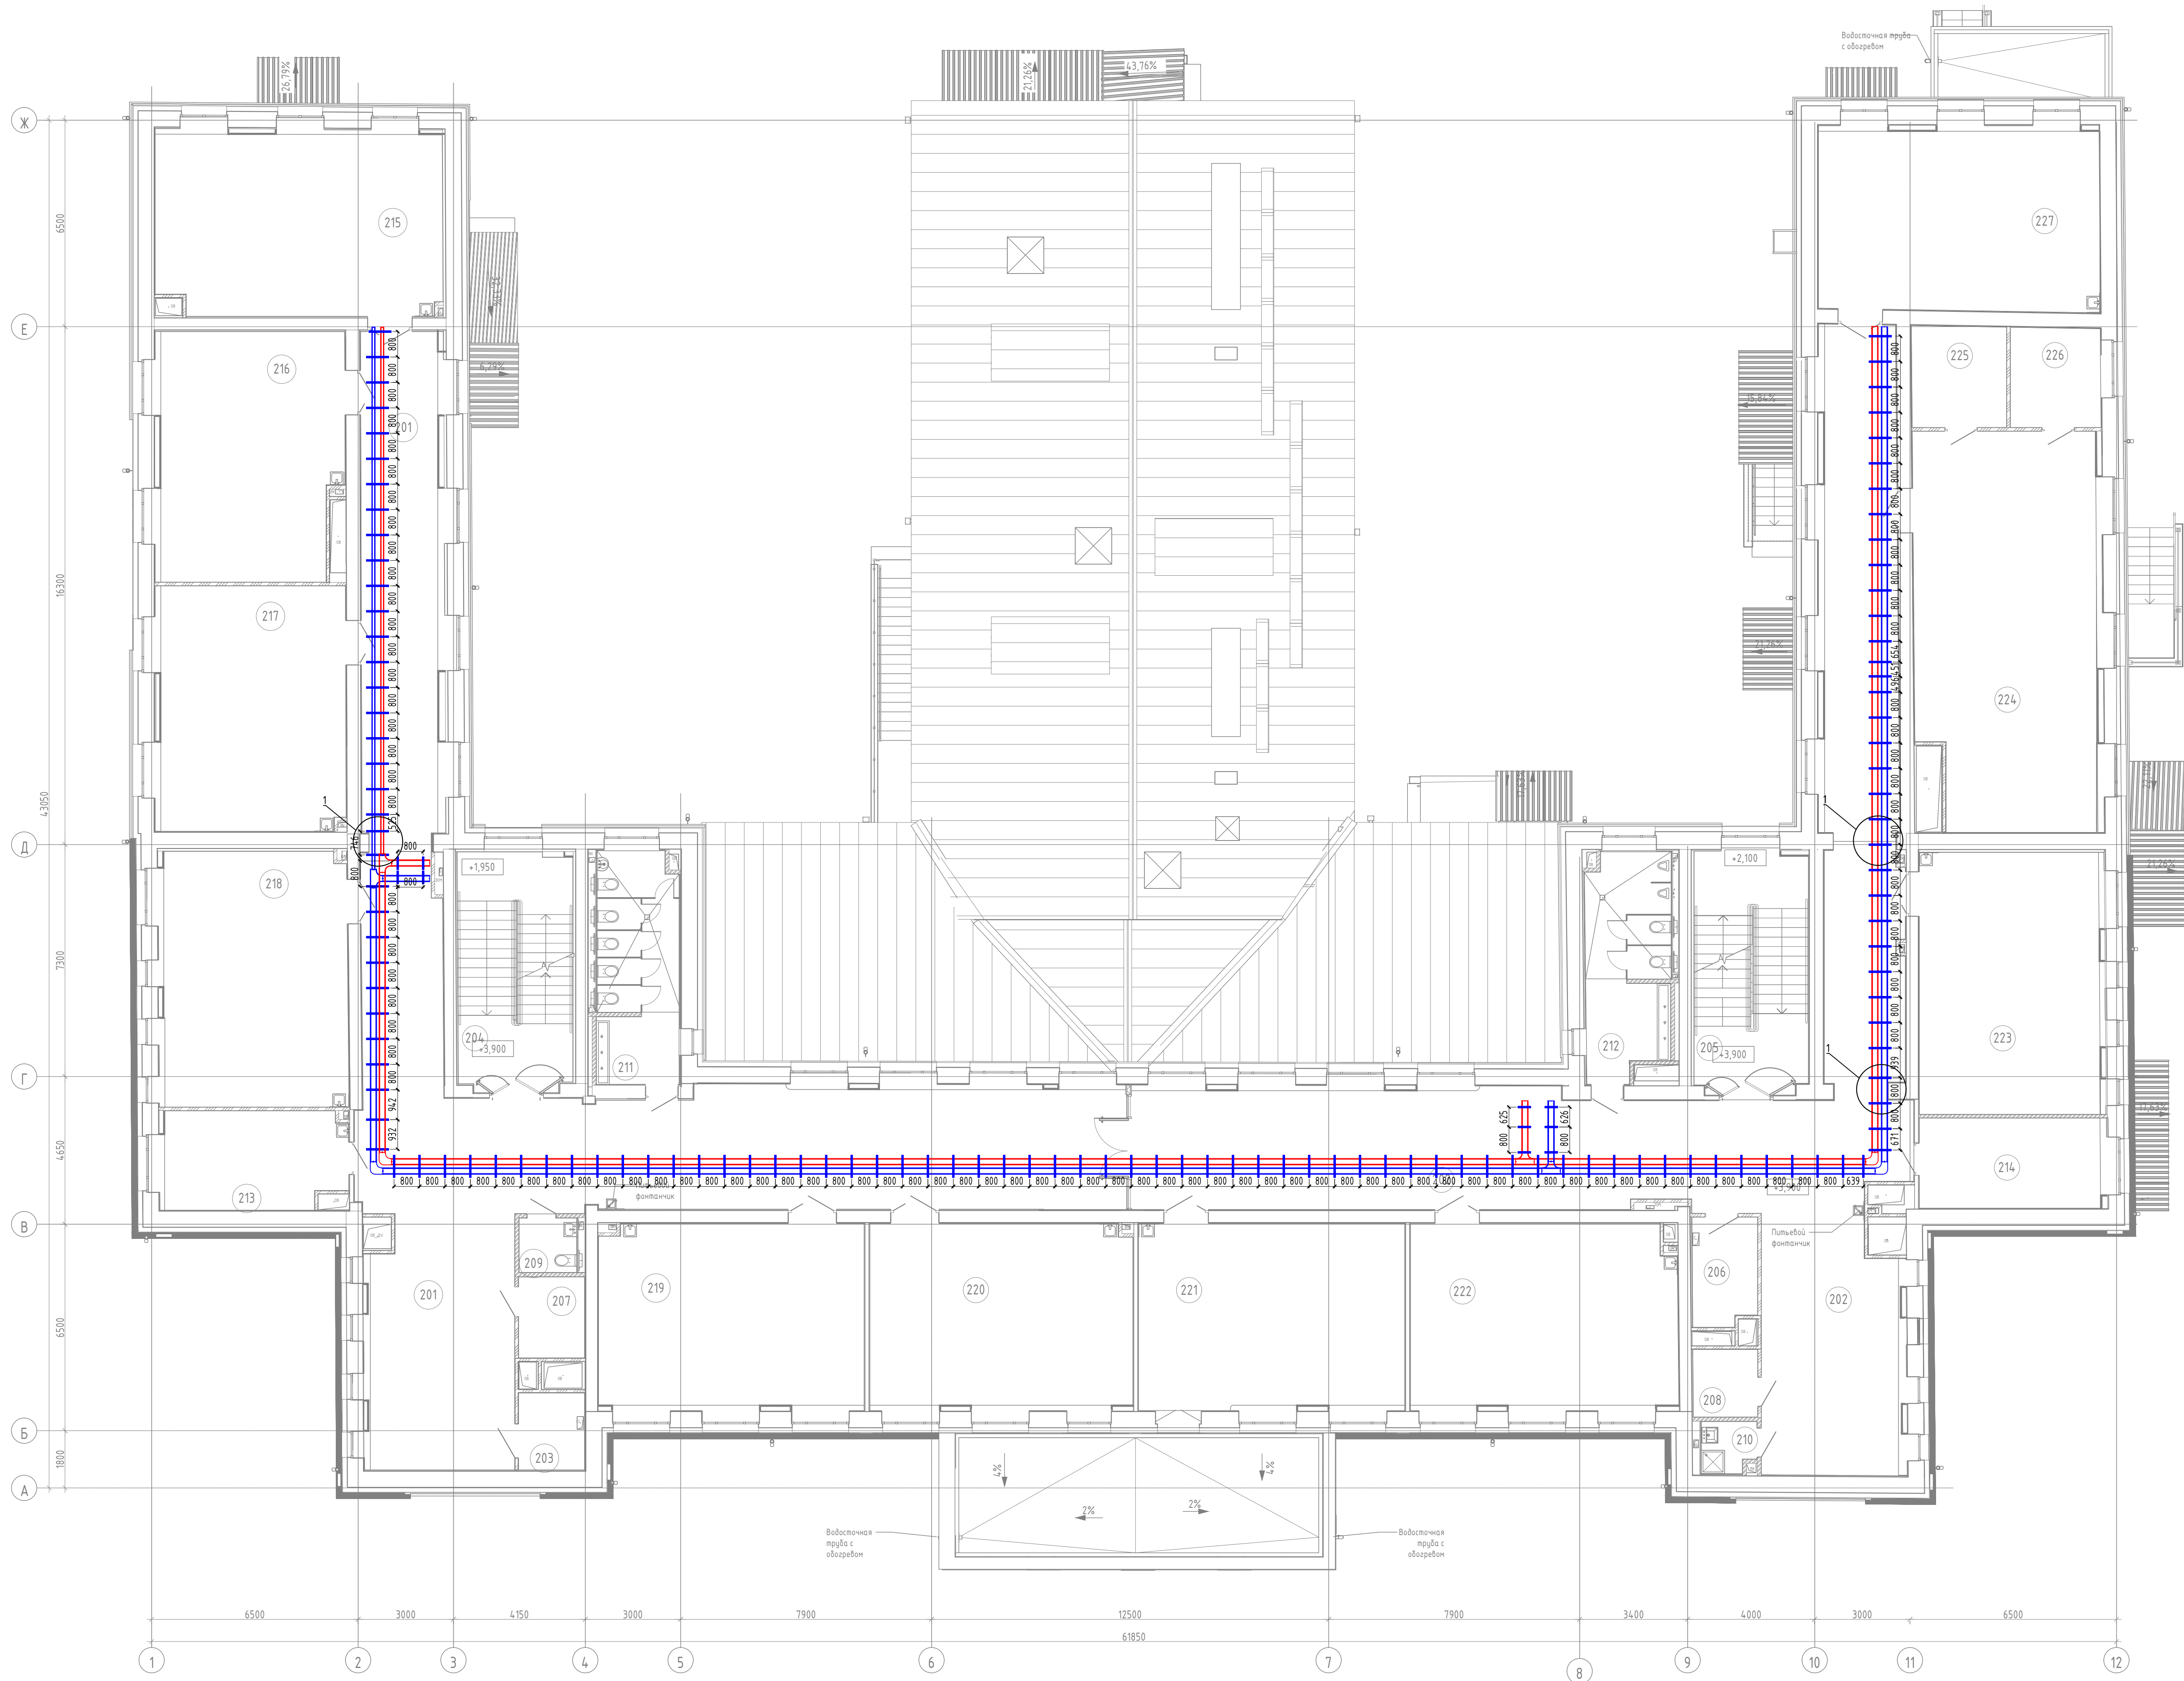


Экспликация помещений 2-го этажа			
Номер помеще-ния	Наименование	Площадь, м²	Кол. помеще-ния
201	Коридор с рекреацией	191,5	
202	Коридор с рекреацией	187,2	
203	Помещение СС	5,1	В4
204	Лестничная клетка (Тип А1)	27,4	
205	Лестничная клетка (Тип А1)	27,6	
206	Помещение СС	6,7	В4
207	Подсобное помещение	5,3	В4
208	Подсобное помещение	4,3	В4
209	Туалет для персонала	3,1	
210	ПМ	2,2	В4
211	Зеркала для девочек	19,1	
212	Зеркала для мальчиков	19,8	
213	Кабинет для индивидуальных занятий, в т.ч. учитель-наставник	18,1	
214	Административный кабинет, Тип 1	16,9	
215	Учебный кабинет	52,7	
216	Учебный кабинет	45,6	
217	Учебный кабинет	46,2	
218	Учебный кабинет	46,4	
219	Учебный кабинет	49,3	
220	Учебный кабинет	48,9	
221	Учебный кабинет	49,6	
222	Учебный кабинет	49,3	
223	Учебный кабинет	47,9	
224	Гимнастический зал	72,6	
225	Раздевальня Тип 1	9,5	
226	Раздевальня Тип 1	8,9	
227	Учебный кабинет	51,7	
		1111,7	

Огнестойкая проходка через стену.

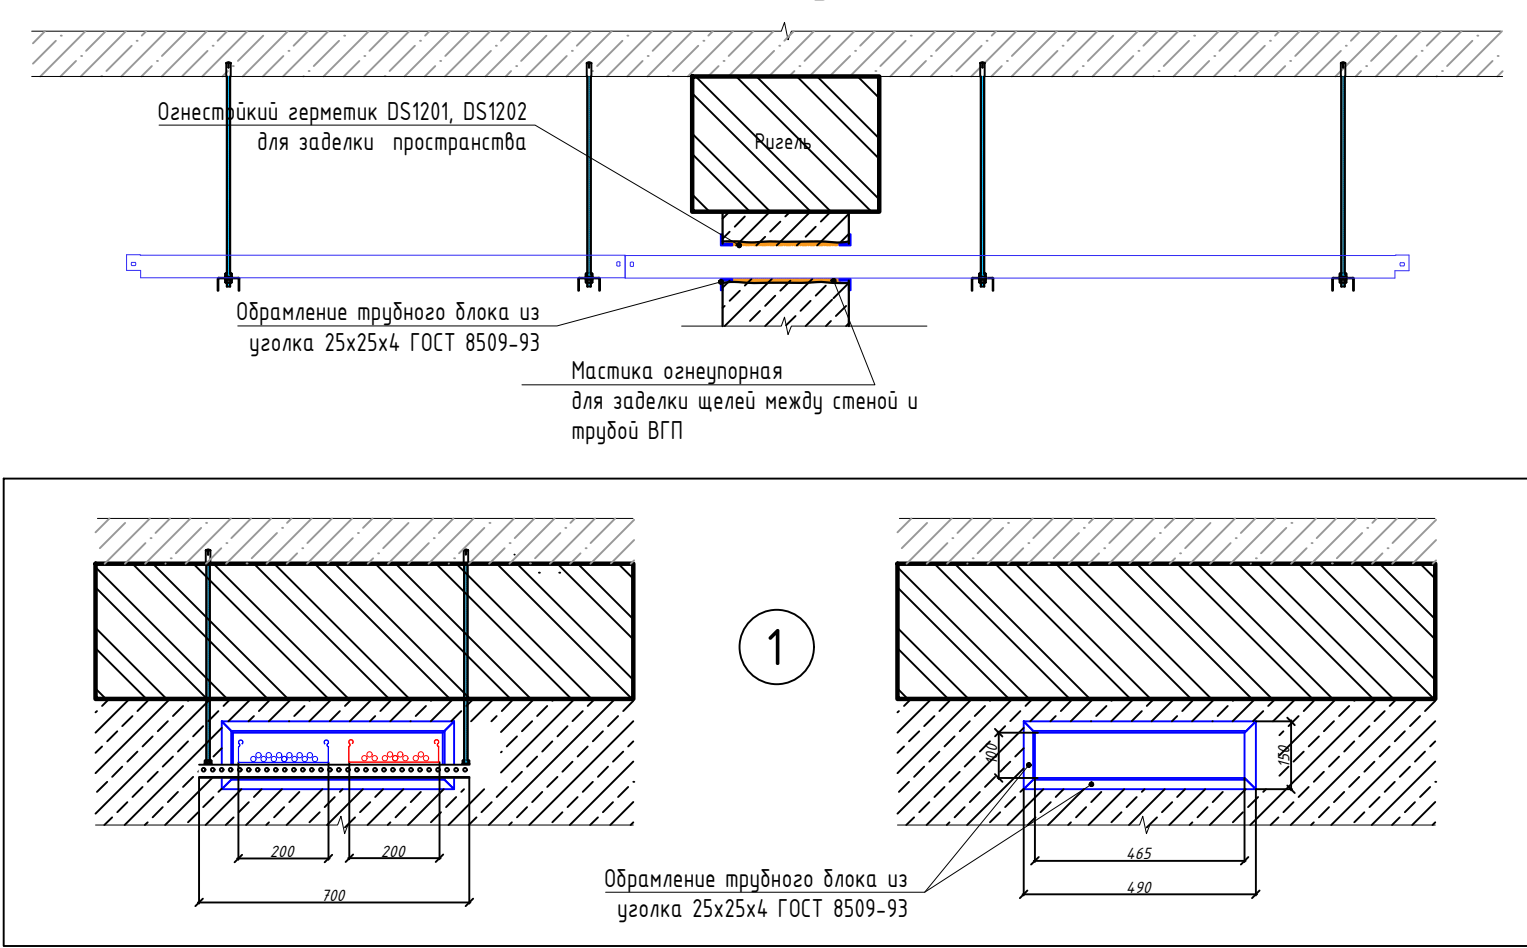

Огнестойкая проходка через перекрытие. М 1:20

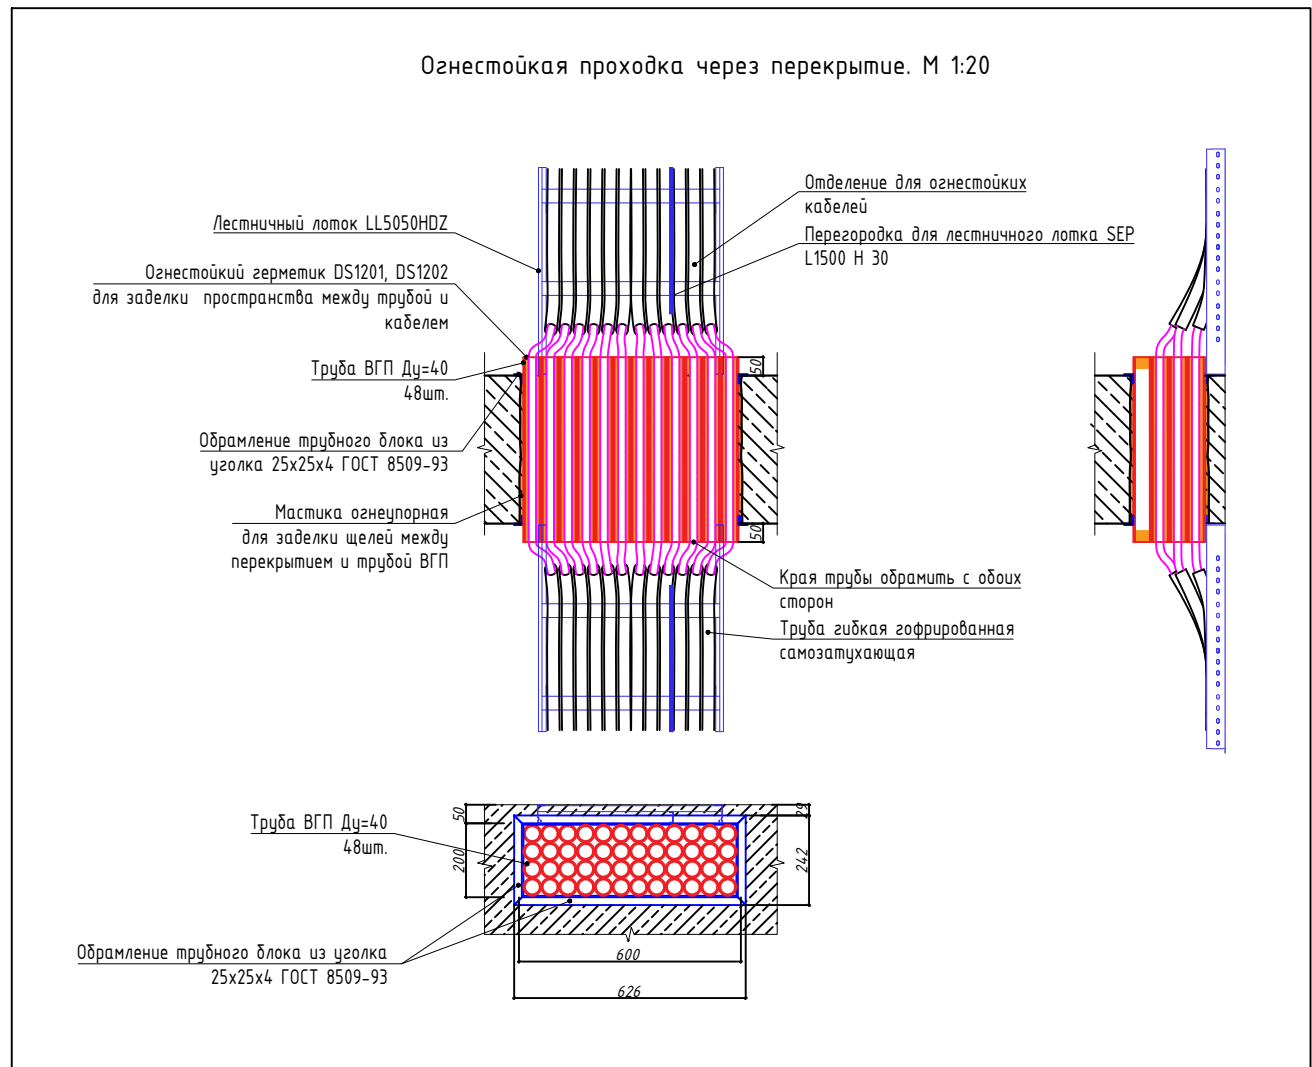

Условные обозначения:
— Лоток
— Лоток для кабелей ПЭС/ПЗ
— Профиль монтажный для кабельных конструкций с указанием типоразмера.

Узел крепления кабельной трассы

№	Обозначение	Наименование
1	СМ20802	Анкер заливочный МВ
2	СМ20802	Шпилька резьбовая МВ
3	ВР1290+	Профиль PSL
4	СМ10800	Гайка МВ
5	СМ20800	Шайба В

Размер и марки профиля отмечены знаком "х" условно при монтаже

- Примечания:
1. Электронная организация РАЗРЕШАЕТся прокладки кабельных трасс – корректировать составленные по месту, исходя из структуры потолка и наличия инженерных систем.
2. Прокладка кабельных конструкций для систем внутреннего электроснабжения.
3. Кабели на разрезе кабельных трасс показаны условно.
4. Расстояние между точками крепления кабельных трасс принять не более 800мм, при необходимости обеспечения такого расстояния возможно увеличение до 1000мм.
5. Крышки лотков на разрезе кабельных конструкций не показаны.


696/П-25-АНО-Р-30М

Здание по адресу: г. Москва, ул. Барвиха, д.1, корп.1

Имя	Кол.	Лист	№ докум.	Дата	Контрагент	Статус	Лист	Листов
Разработчик	Иванов	07.26	07.26	07.26	Капитальный ремонт Государственного бюджетного образовательного учреждения города Москвы Школа №1282	Р	2	Листов
Н.контр.	Гуляев	07.26	07.26	07.26	План кабельных конструкций сетей выделенного электроснабжения 2 этажа			


Формат

План 3 этажа

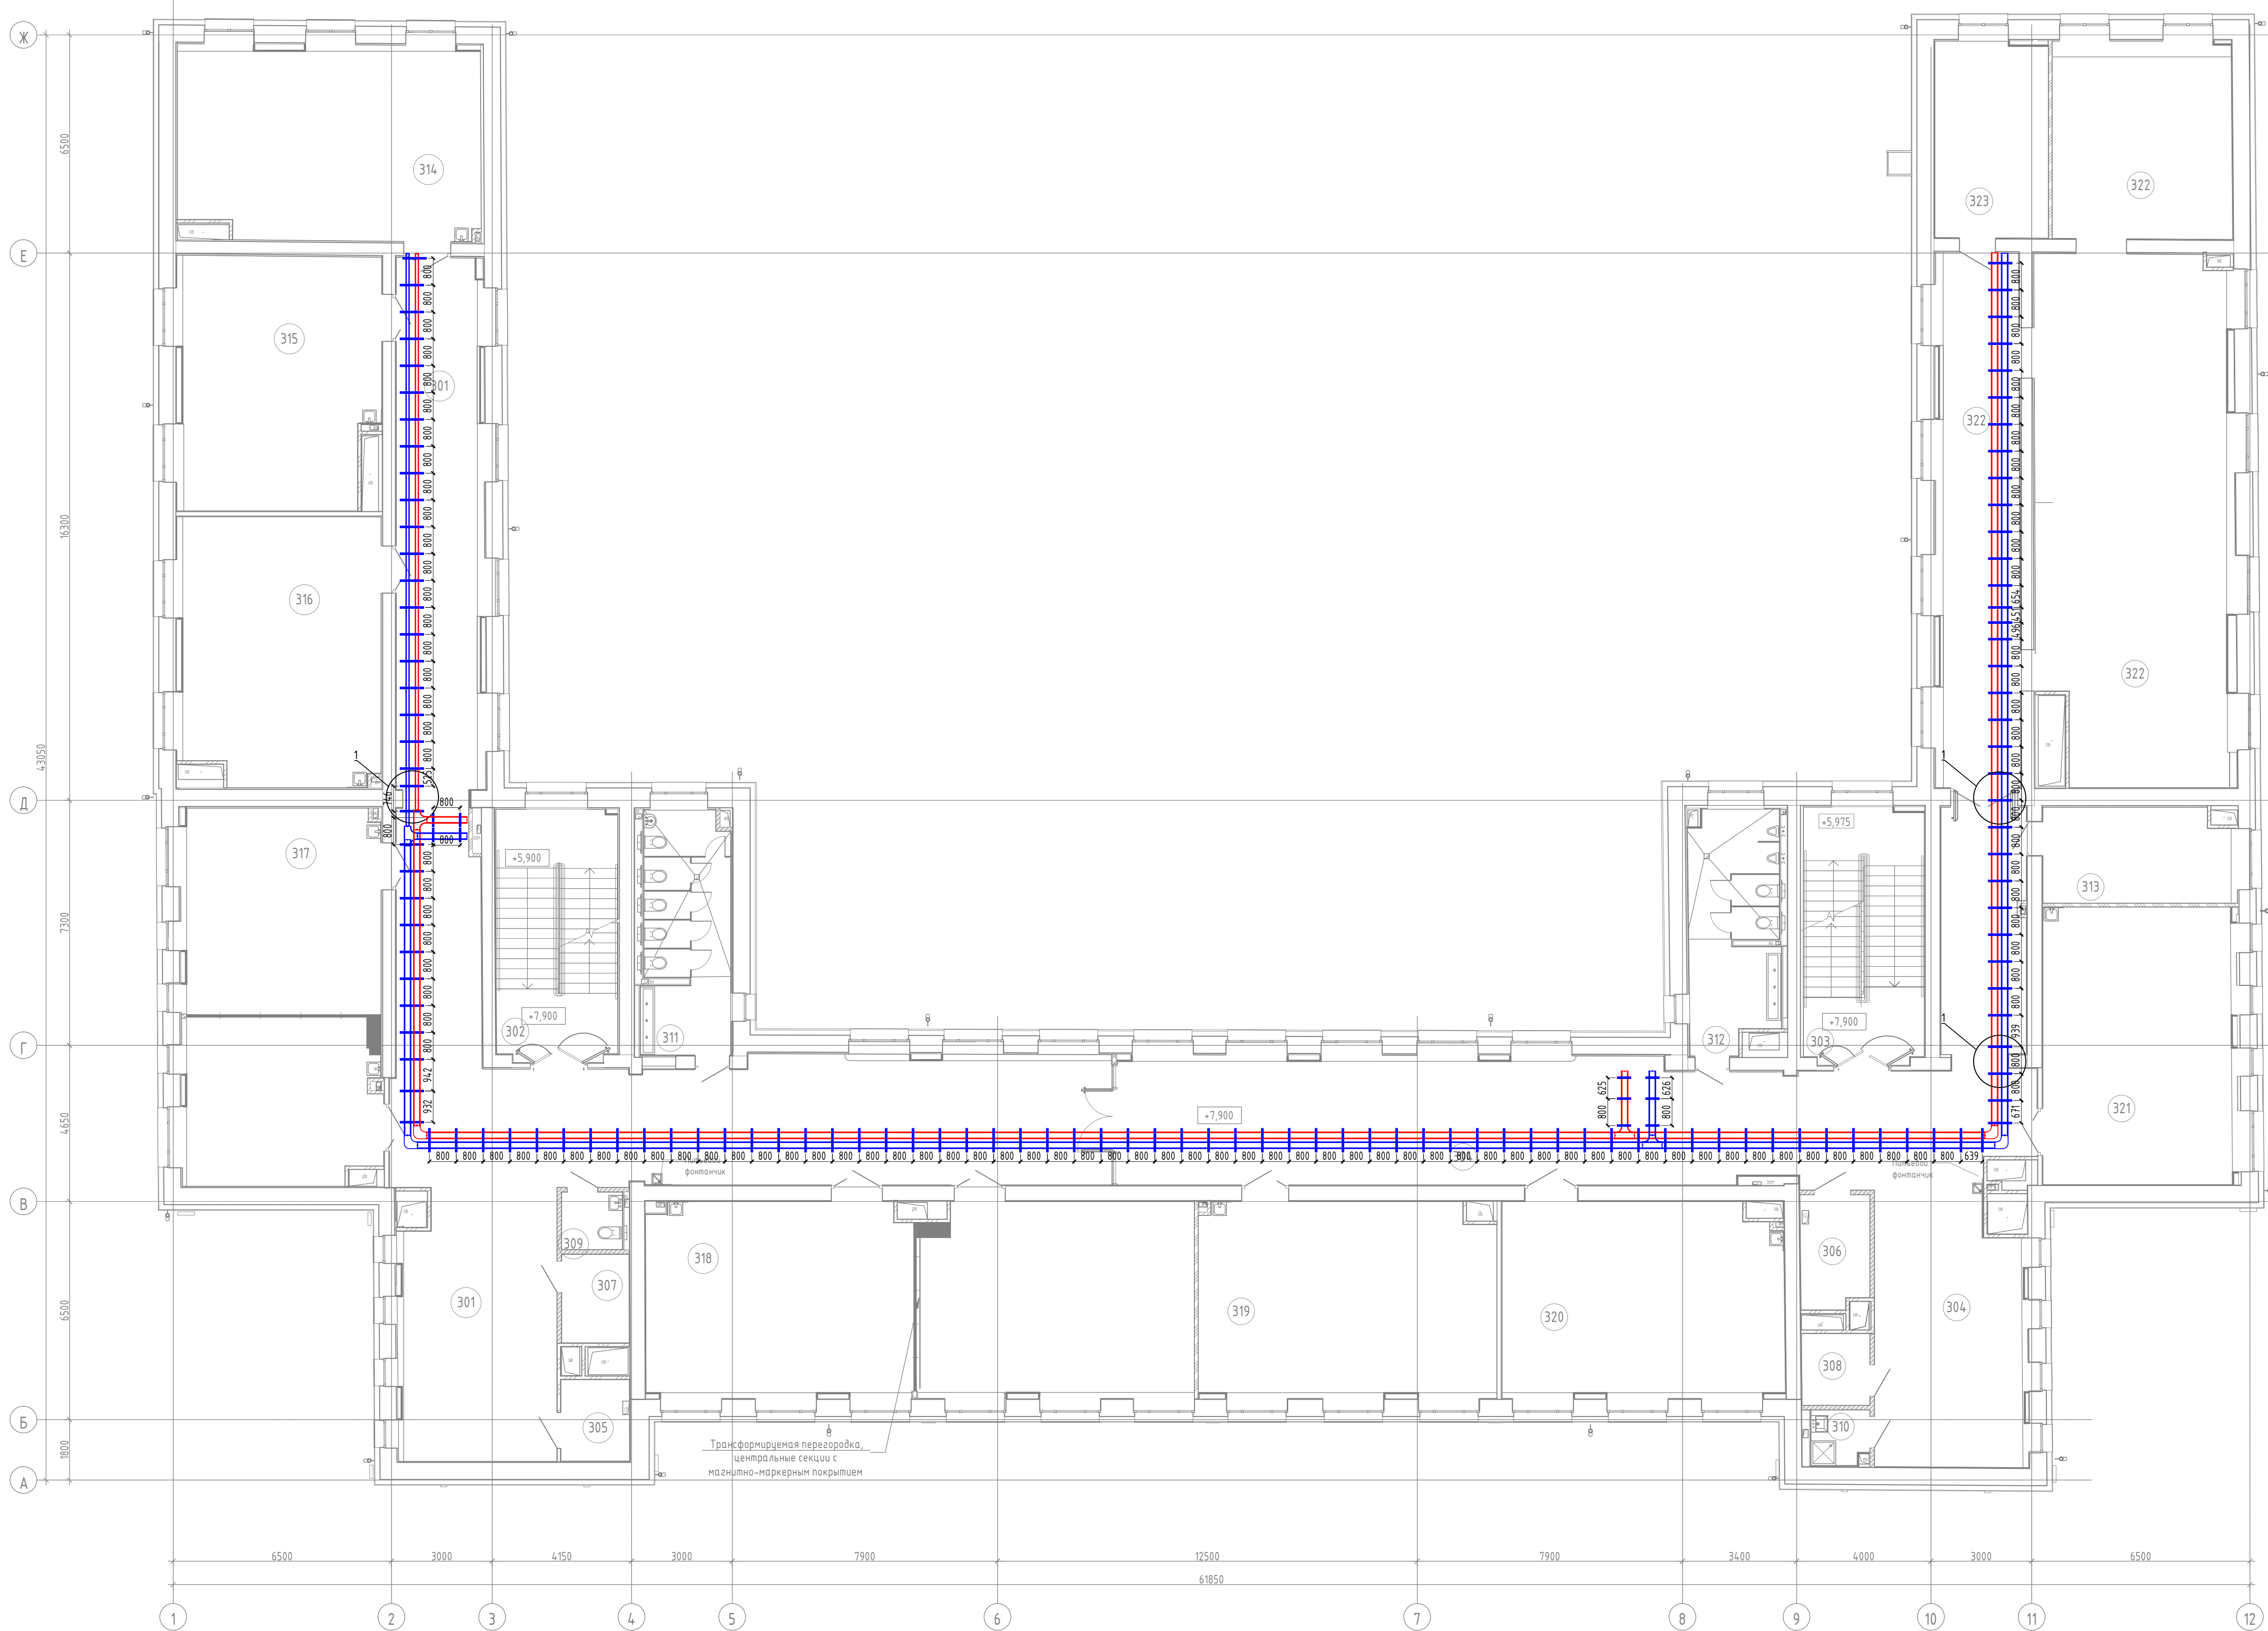


Экспликация помещений 3-го этажа			
Номер помеще-ния	Наименование	Площадь, м²	Кот. помеще-ния
301	Коридор с рекреацией	179,8	
302	Лестничная клетка (Тип А)	27,3	
303	Лестничная клетка (Тип А)	27,7	
304	Коридор с рекреацией	155,8	
305	Помещение СС	5,1	В4
306	Помещение СС	6,8	В4
307	Подсобное помещение	5,3	В4
308	Подсобное помещение	4,3	В4
309	Туалет для персонала	3,1	
310	ПМ	2,3	В4
311	Зубная для девочек	19,0	
312	Зубная для мальчиков	18,9	
313	Кабинет для индивидуальных занятий, 6	16,0	
314	Учебный кабинет	51,9	
315	Учебный кабинет	44,6	
316	Учебный кабинет	47,9	
317	Кабинет иностранного языка с возможностью деления/трансформированной перегородкой на два помещения	66,5	
318	Персональная аудитория с возможностью деления/трансформированной перегородкой на два помещения	94,7	
319	Учебный кабинет	51,4	
320	Учебный кабинет	48,7	
321	Учебный кабинет	47,9	
322	Многофункциональный информационный выделенный центр с ресурсами для индивидуальных и групповых занятий, учебный центр детских учреждений	163,4	
323	Многофункциональный информационный выделенный центр (хранение (закрытый фонд) и выдача книг)	119,8	В3
		1108,1	

Огнестойкая проходка через стену.

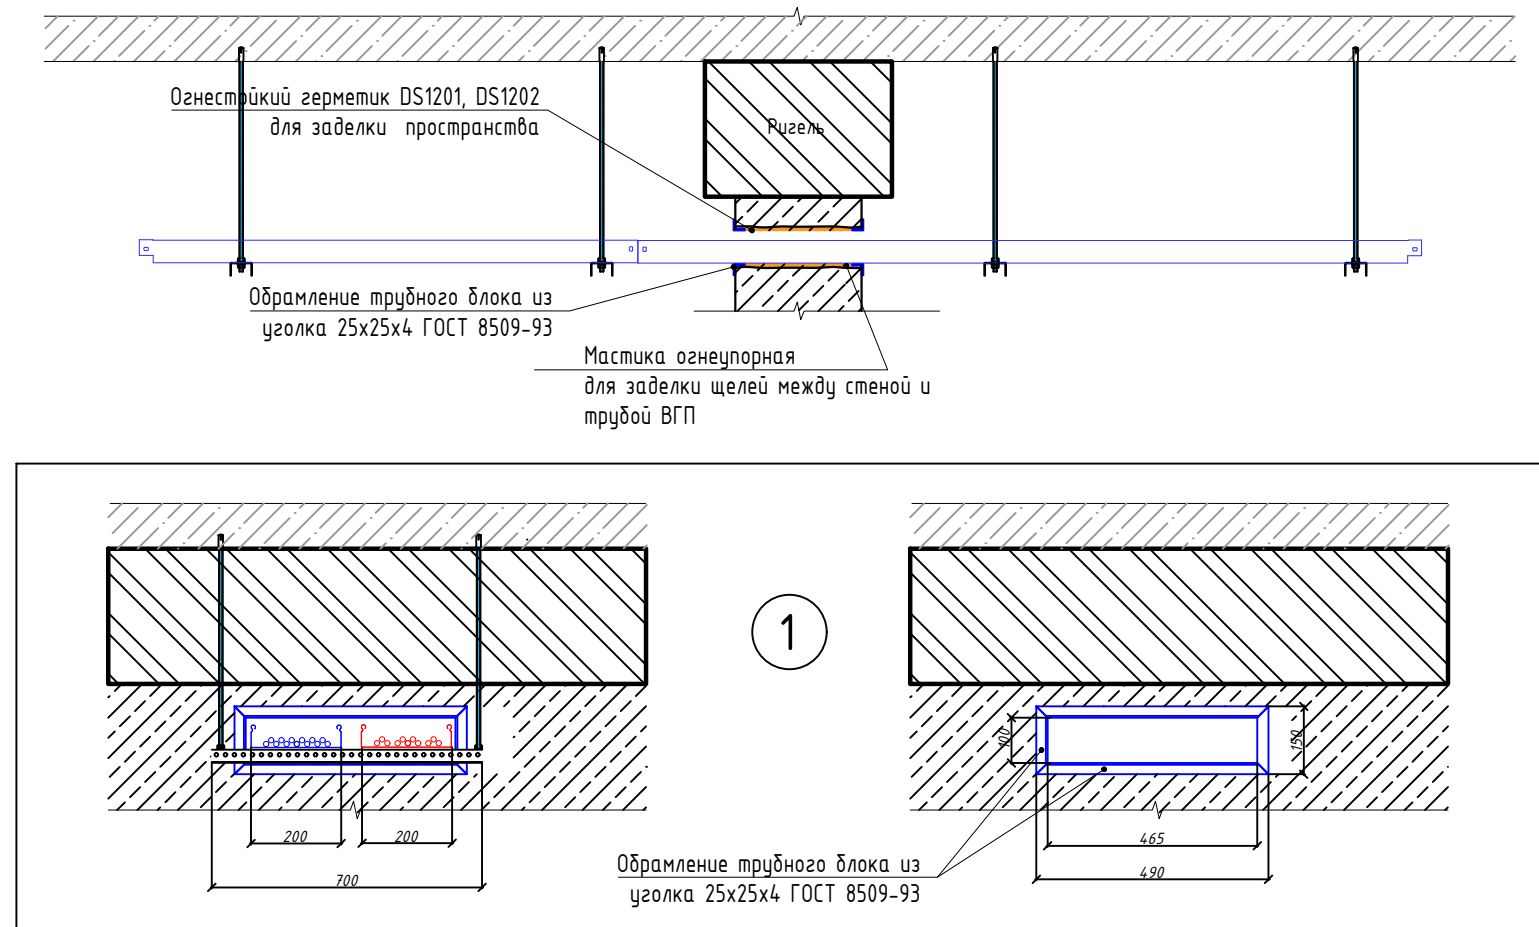

Огнестойкая проходка через перекрытие. М 120

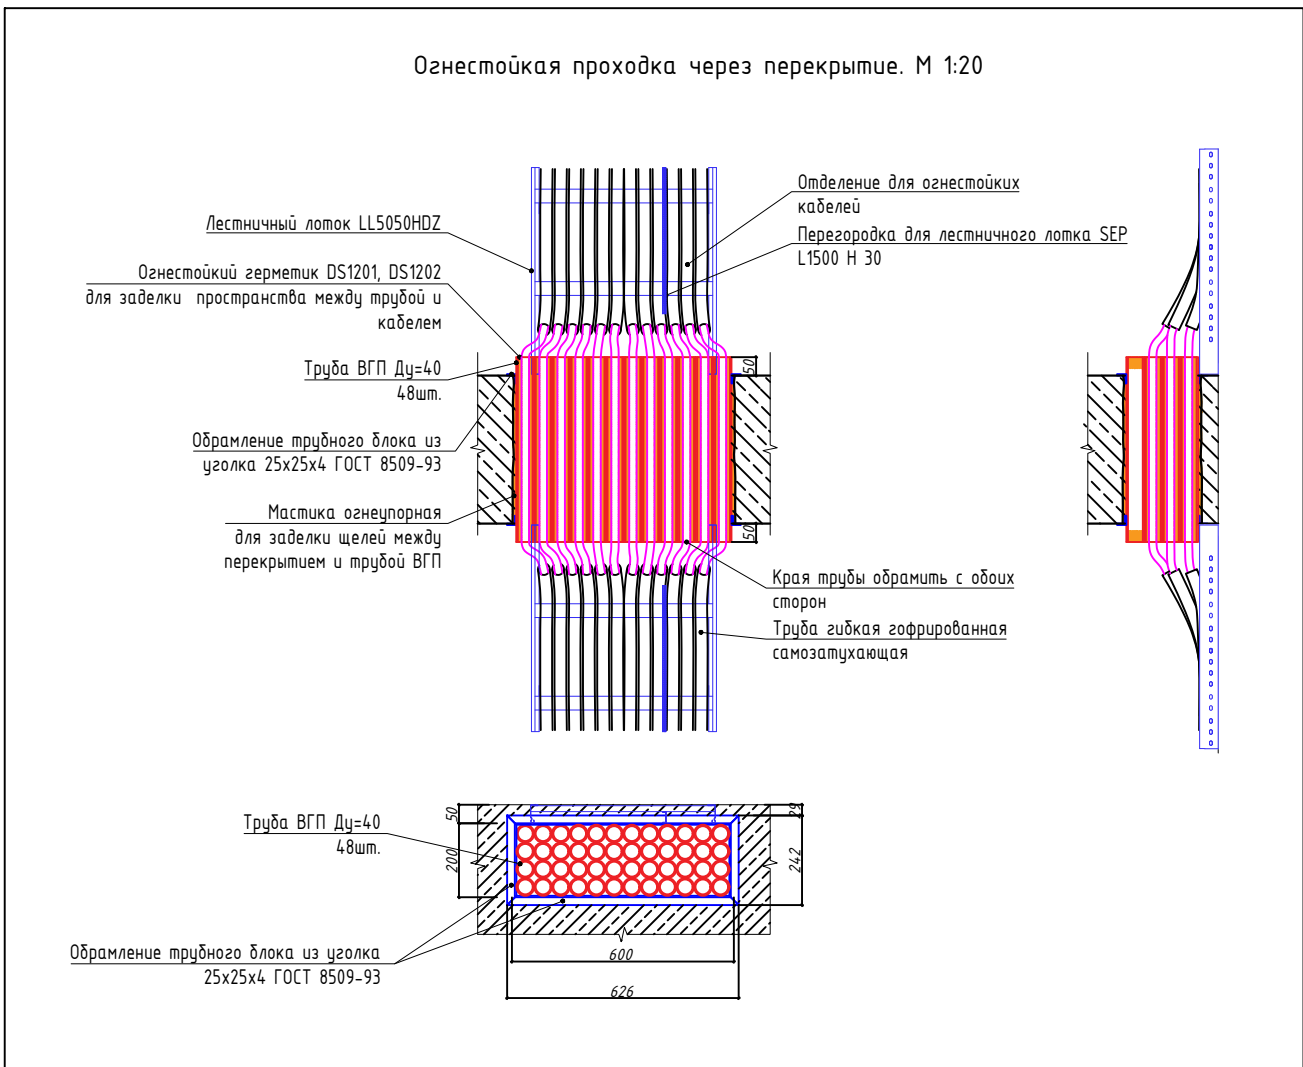

Условные обозначения.

- Лоток
- Лоток для кабелей ПЗСПЗ
- Профиль монтажный для кабельных конструкций с указанием типоразмера.


Узел крепления кабельной трассы

Поз.	Обозначение	Наименование
1	СМ1.00830	Анкер заливной МВ
2	СМ2.00802	Шпилька резьбовая МВ
3	ВР1.250	Профиль ПСЛ
4	СМ10.0800	Гайка М8
5	СМ12.0800	Шайба 8

Размер и марки профиля отмечены знаком "+" уточнить при монтаже


- Примечания:
- Эксплуатационная организация РАЗРЕШАЕТ прокладку кабельных трасс - корректировать самостоятельно по месту, исходя из структуры потолка и наличия инженерных систем;
 - Проектант предусматривает ГОРЮЮ кабельные конструкции для систем внутреннего электроснабжения;
 - Кабели на разрезе кабельных трасс показаны условно;
 - Расстояние между точками крепления кабельных трасс принять не более 800мм, при необходимости обеспечения такого расстояния возможно увеличение до 1000мм;
 - Крышки лотков на разрезе кабельных конструкций не показаны.

План 4 этажа

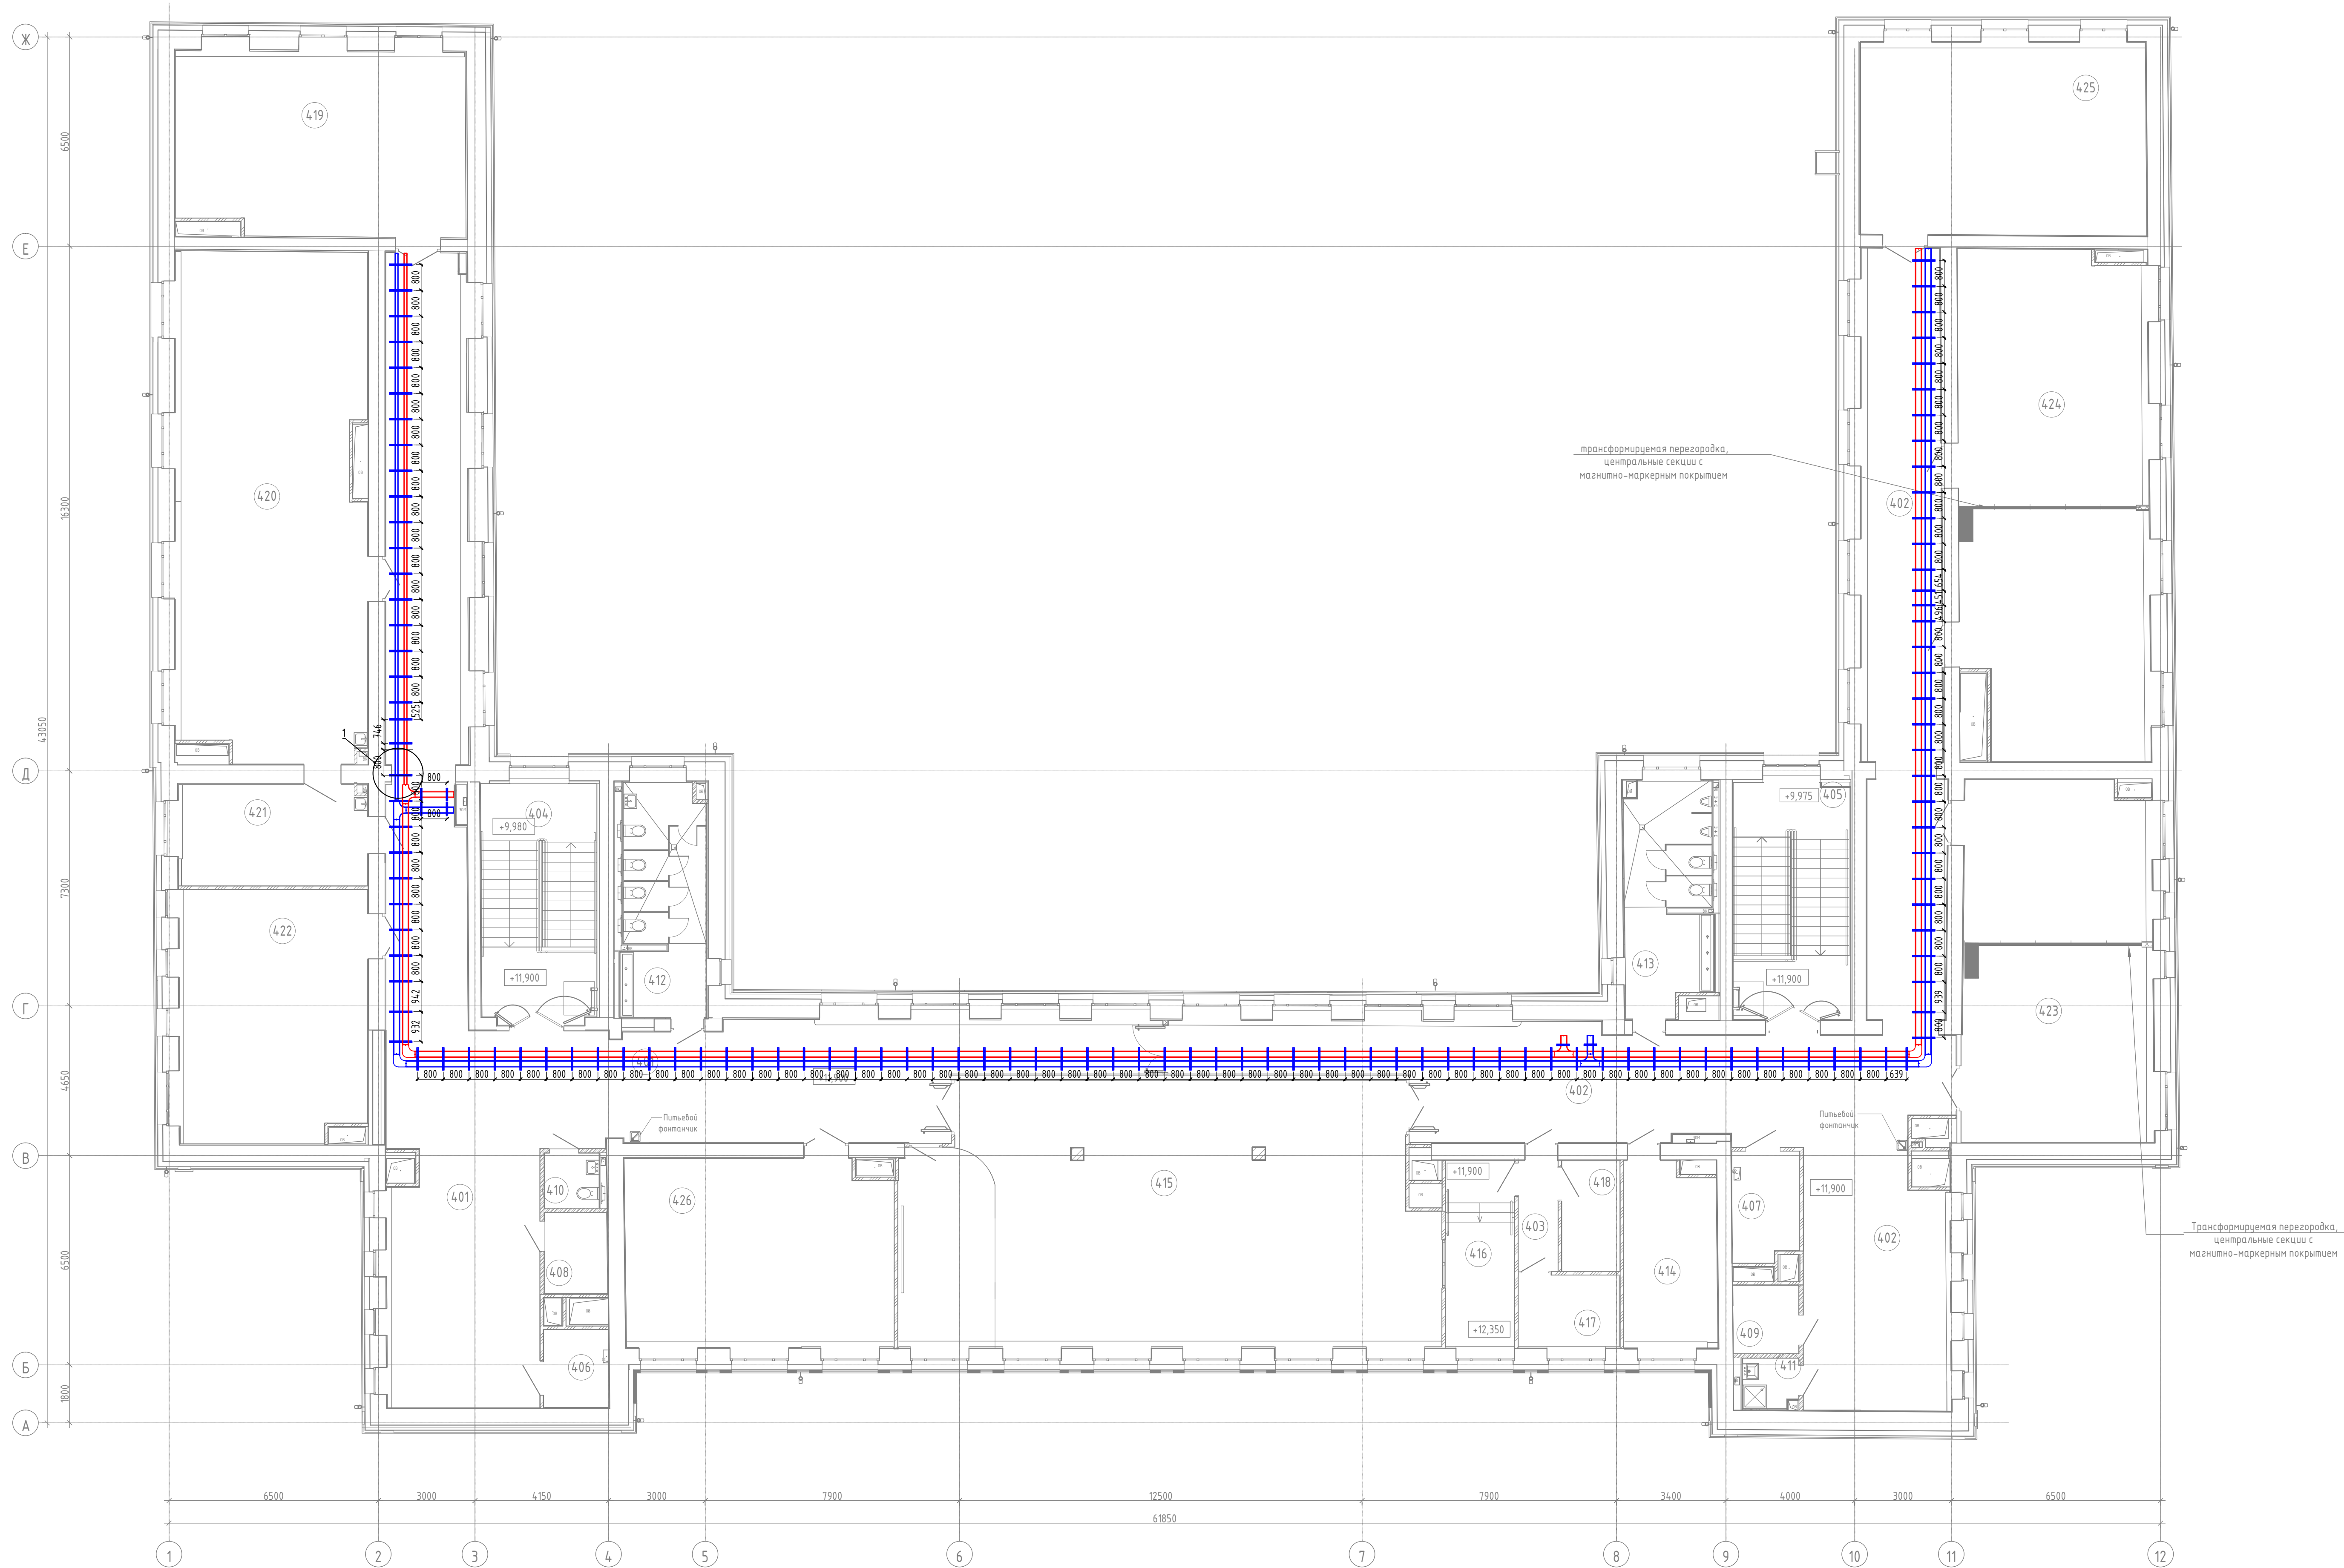

Экспликация помещений 4-го этажа			
Номер помещения	Назначение	Площадь, м²	Кол. помещ.
401	Коридор с рекреацией	173,6	
402	Коридор с рекреацией	166,2	
403	Танц-зал	4,1	
404	Автоматическая клетка (Туп А1)	26,9	
405	Автоматическая клетка (Туп А1)	26,8	
406	Помещение СС	5,0	В4
407	Помещение СС	6,8	В4
408	Подсобное помещение	5,0	В4
409	Подсобное помещение	4,3	В4
410	Туалет для персонала	2,9	
411	ПМ	2,1	В4
412	Уборная для девочек	19,0	
413	Уборная для мальчиков	19,1	
414	Кабинет для индивидуальных занятий, 8 п.ч. специализация-психологом	16,2	
415	Актовый зал (с эстрадой в цокольном этаже)	131,1	
416	Технический центр	12,4	В3
417	Арт-студия	6,9	
418	Кабинет инвентаря	6,1	В4
419	Кабинет математики	50,8	
420	Учебный кабинет (для изучения естественных наук/географии Туп 2)	92,4	
421	Лаборатория биологии	18,3	В3
422	Учебный кабинет (история)	45,0	
423	Кабинет иностранного языка с возможностью децентрализованной перегородкой на два помещения	65,9	
424	Учебный кабинет информатики с возможностью децентрализованной перегородкой на два помещения	90,5	
425	Кабинет русского языка и литературы	53,4	
426	Кабинет русского языка и литературы	48,1	
		1098,5	

Огнестойкая проходка через стену.

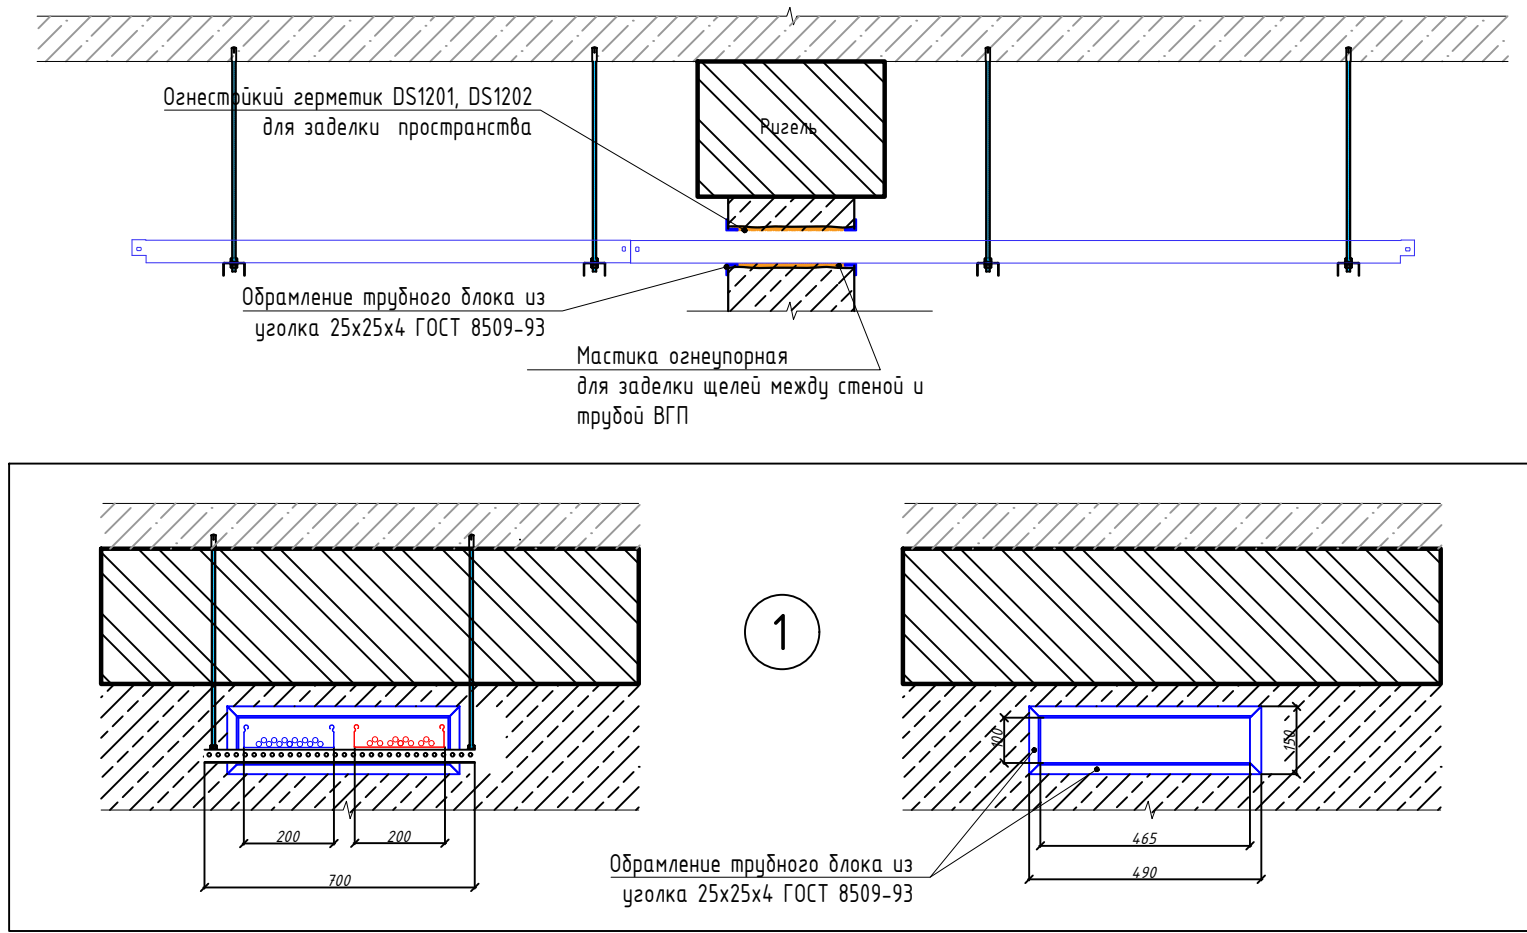


Условные обозначения:
— Лоток
— Лоток для кабелей ПЭСПЗ
— Профиль монтажный для кабельных конструкций с указанием типоразмера.

Узел крепления кабельной трассы

Поз.	Обозначение	Назначение
1	СМ400830	Анкер резьбовой М8
2	СМ200802	Шпилька резьбовая М8
3	ВР1294	Профиль ПСЛ
4	СМ10800	Головка М8
5	СМ120800	Шайба 8

Размер и номер профиля обозначены знаком "4" уточнить при монтаже

Огнестойкая проходка через перекрытие. М 1:20

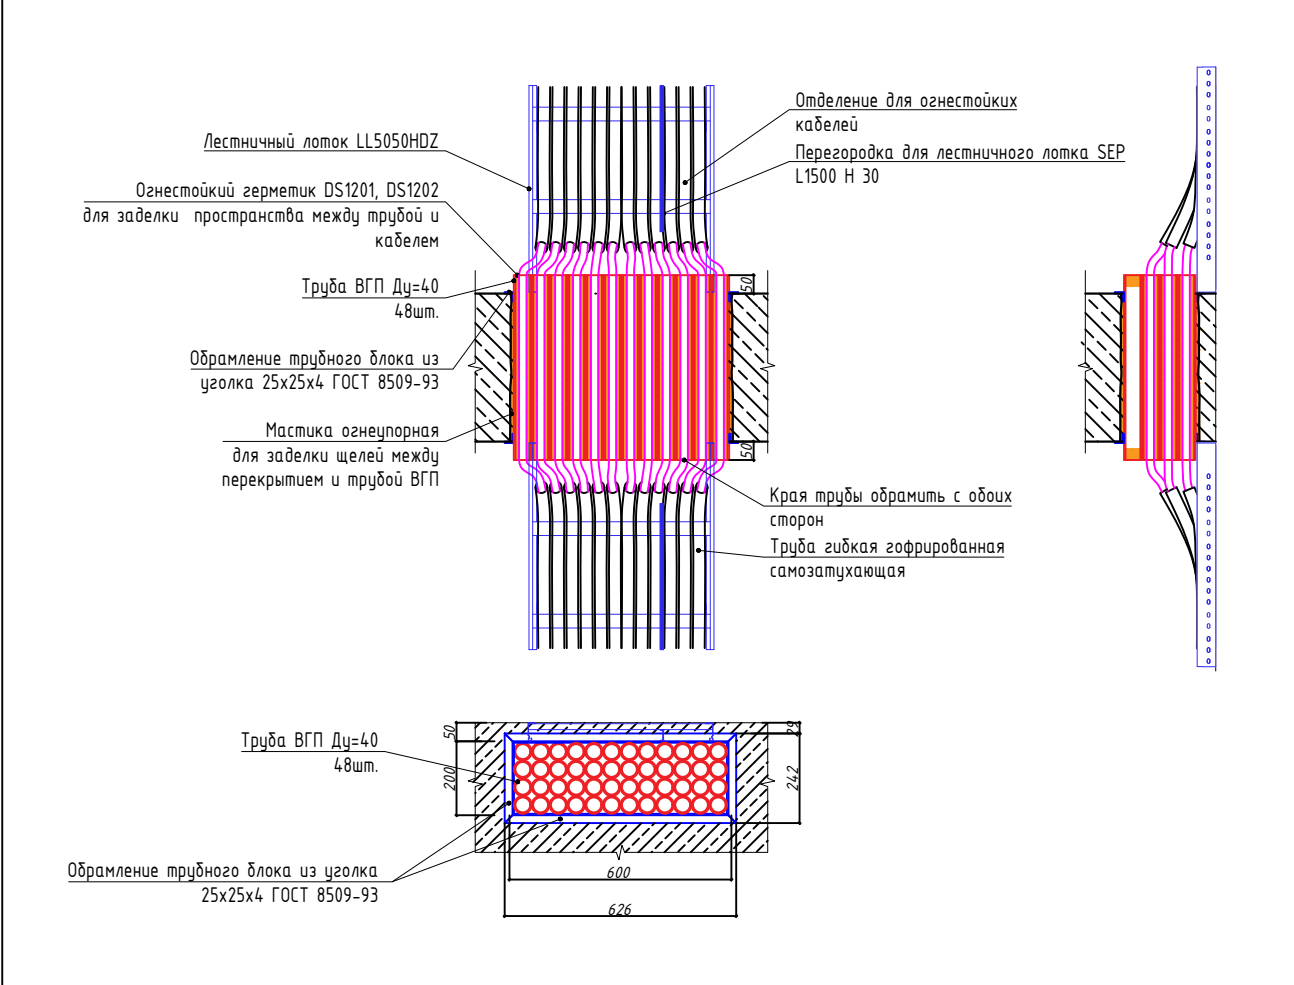

- Примечания:
1. Электротехнической организацией РАЗРЕШАЕТСЯ прокладка кабельных трасс - корректировать самостоятельно по месту, исходя из структуры потолка и наличия инженерных систем;
2. Проектом предусмотрены ГОРЯЧИЕ кабельные конструкции для систем внутреннего электроснабжения;
3. Кабели на разрезе кабельных трасс показаны условно;
4. Расстояние между точками крепления кабельных трасс принять не более 800мм, при необходимости обеспечения такого расстояния возможно увеличение до 1000мм;
5. Крышки лотков на разрезе кабельных конструкций не показаны.

696/П-25-АНО-Р-30М

Здание по адресу: г. Москва, ул. Барвиха, д.1, корп.1

Имя	Кол.	Лист	№ док.	Подп.	Дата	Классификация	Статус	Лист	Листов
Разработчик	Иванов	07.26	07.26	07.26	07.26	Капитальный ремонт Государственного бюджетного общеобразовательного учреждения города Москвы Школа №1282	Р	4	Листов
Н. контр.	Гуляко	07.26	07.26	07.26	07.26	План кабельных конструкций сетей внутреннего электроснабжения 4 этажа			

Формат

[illegible]