

109548, г. Москва, Муниципальный Округ Печатники, ул. Шоссейная, д. 19, к. 1,
кв.117 e-mail PROEKTplus-work@yandex.ru

Свидетельство № СРО- П-110-009723217107-0532

**Капитальный ремонт Государственного Бюджетного
Общеобразовательного Учреждения города Москвы
«Школа № 1282 «Сокольники»
по адресу: г. Москва, ул. Барболина, д. 1, корп. 1
1 этап**

РАБОЧАЯ ДОКУМЕНТАЦИЯ

Система электроснабжения

696/П-24-АНО-Р-ЭОМ

Генеральный директор

Главный инженер проекта




Н.А. Выходова

А.Н. Гулько

2026


Име. № подл.	Подп. И дата	Взам. инв. №

План 1 этажа

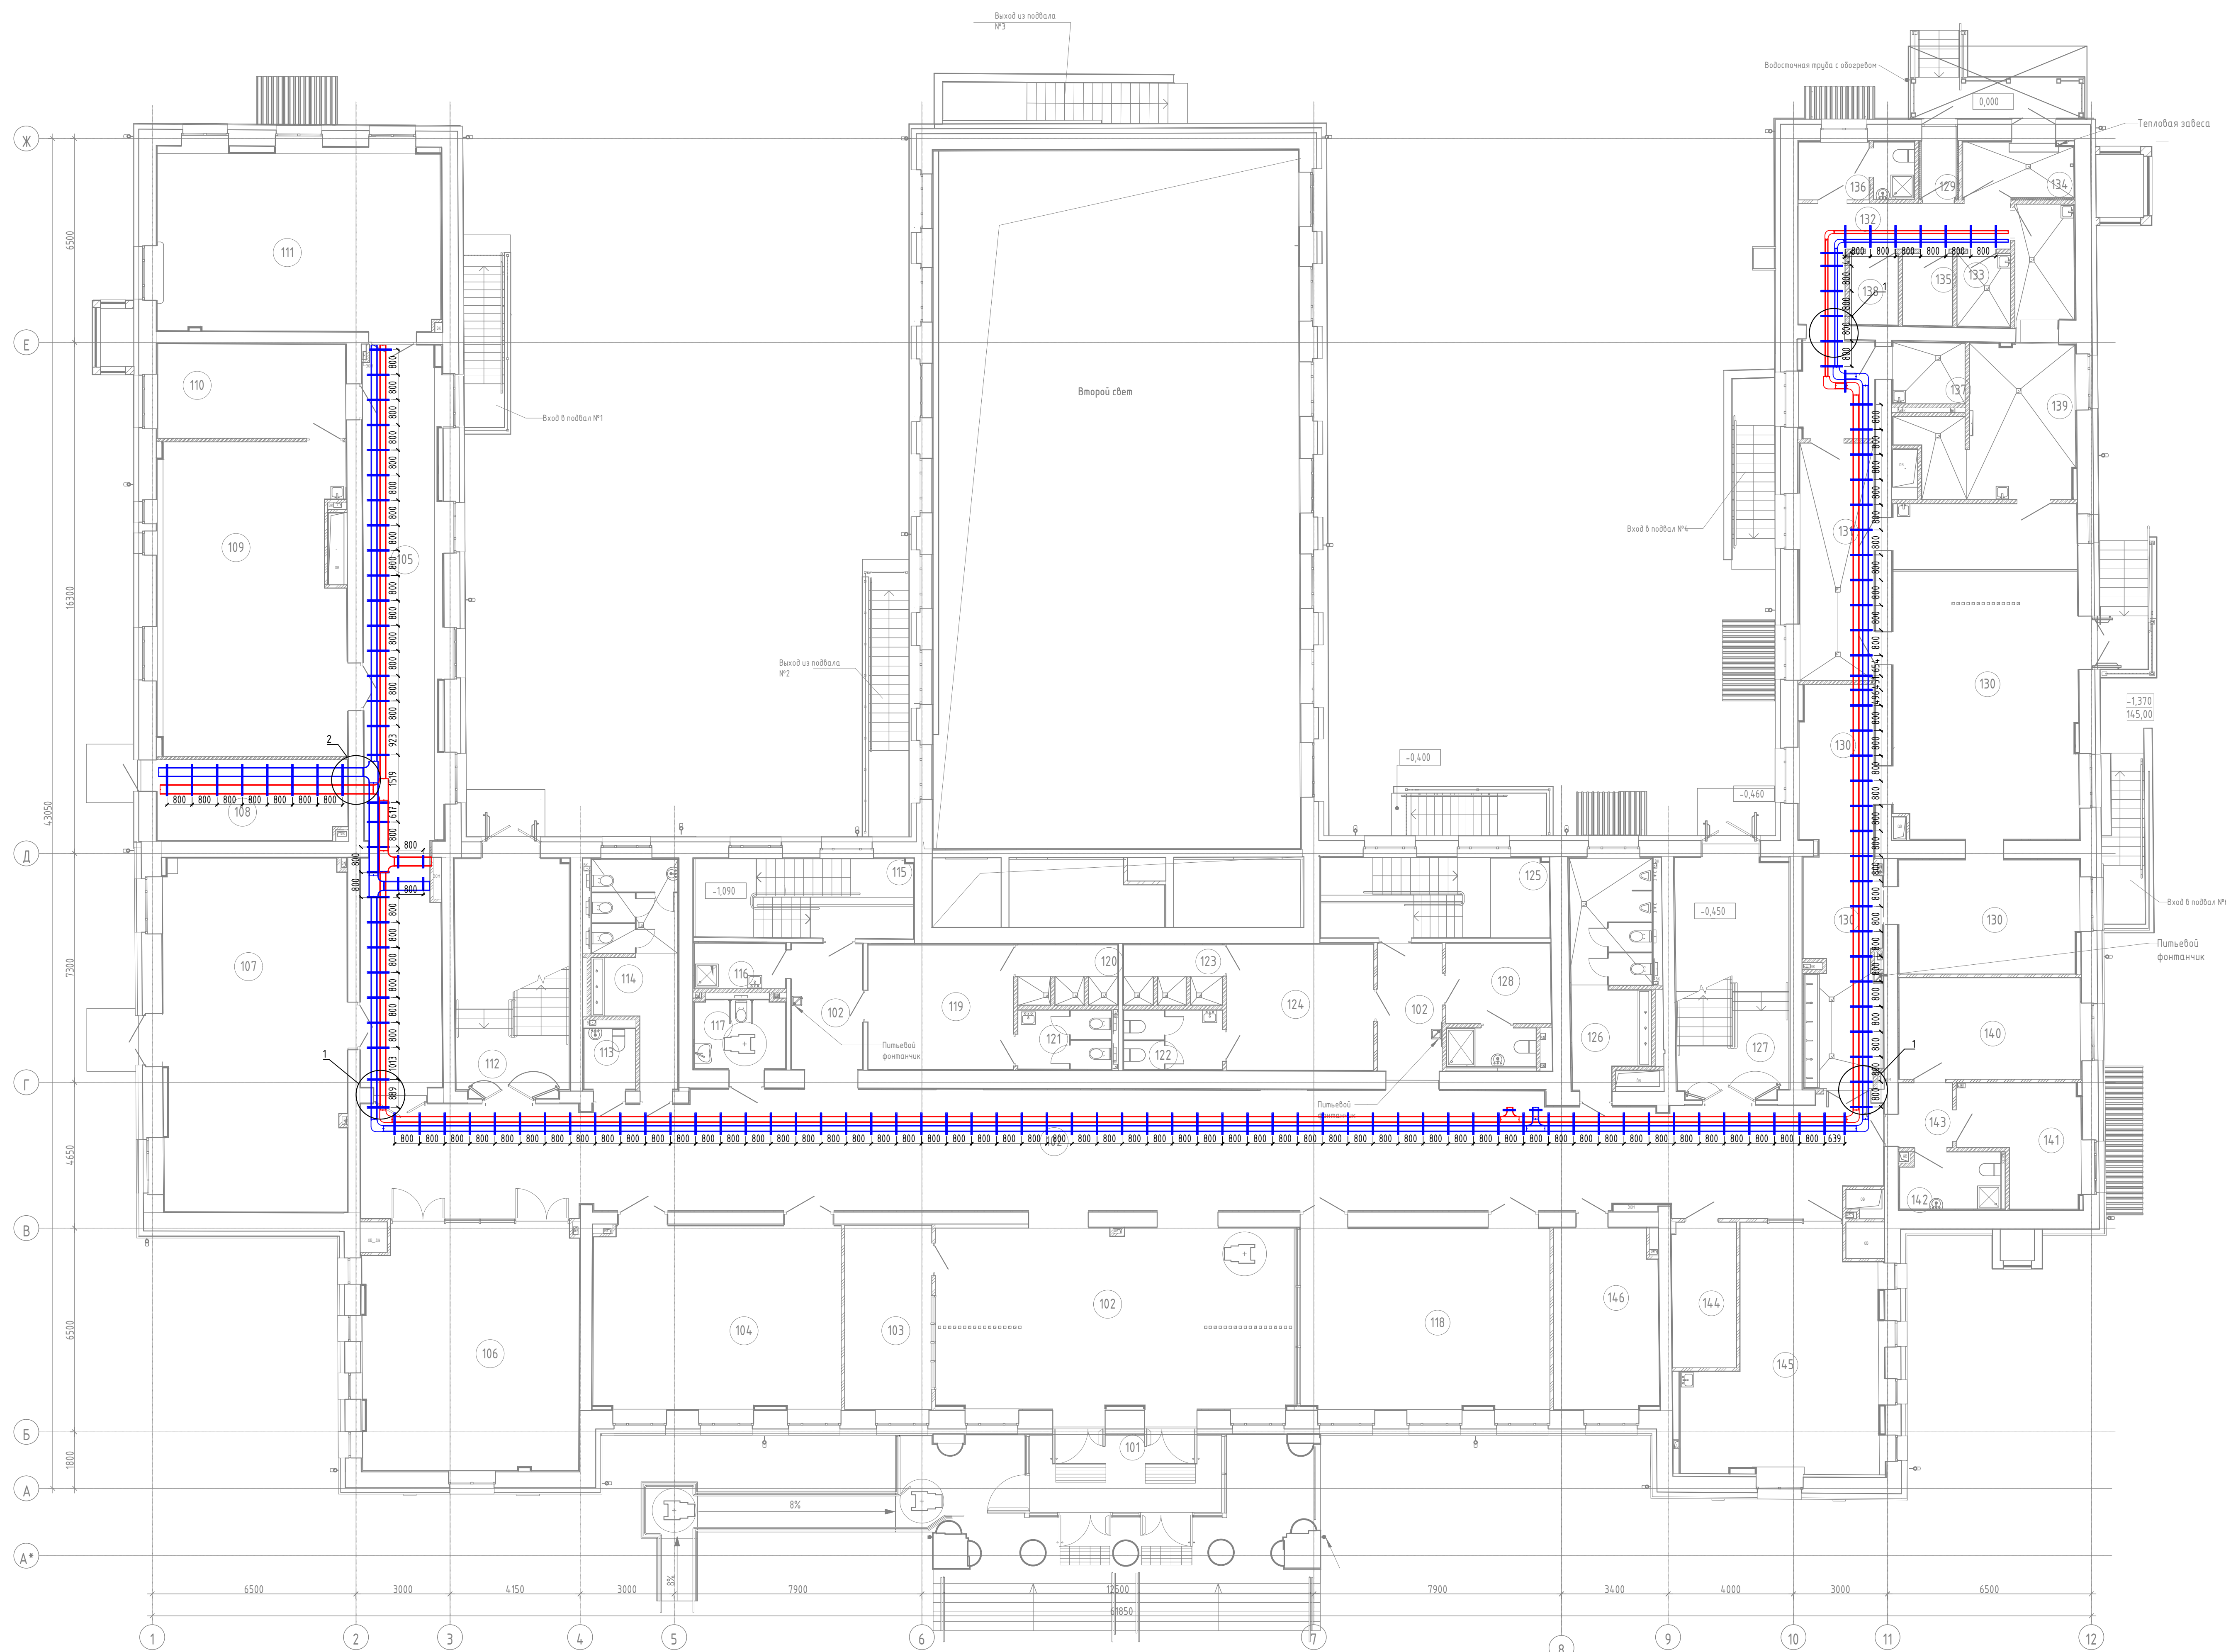

Экспликация помещений 1-го этажа			
Номер помеще-ния	Наименование	Площадь, м²	Кот. помеще-ния
101	Гамбур	12,5	
102	Вестибиль	287,7	
103	Комната охраны (с диспетчерским пунктом)	18,2	
104	Гардероб для обучающихся	46,2	
105	Коридор	59,9	
106	Гардероб для обучающихся	53,7	
107	Учебный кабинет (Тип 1)	66,1	
108	Электрощитовая	15,5	Б3
109	Учебный кабинет (Тип 2)	58,5	
110	Кладовая	18,0	Б3
111	Учебный кабинет (металлтика)	53,3	
112	Лестничная клетка (Тип А1)	27,8	
113	Туалет для персонала	3,3	
114	Ванная для девочек	17,0	
115	Технологическая лестница	17,8	
116	ПМ	4,6	Б4
117	Экспериментальная уборная для МН	6,6	
118	Гардероб для обучающихся	46,4	
119	Раздевальня Тип 1	18,7	
120	Душевая	6,3	
121	Ванная	5,7	
122	Ванная	6,1	
123	Душевая	6,2	
124	Раздевальня Тип 1	18,8	
125	Технологическая лестница	18,9	
126	Ванная для мальчиков	18,4	
127	Лестничная клетка (Тип А1)	27,8	
128	Тренажерная с санузлом	12,1	
129	Гамбур	2,2	
130	Обеденный зал	114,5	
131	Меченая для столовой посуды	18,4	Б4
132	Коридор	21,2	
133	Кладовая и мясная оборотной тары	4,0	Б4
134	Загрузочный цех	6,6	Б4
135	Кладовая сухих продуктов	3,7	Б4
136	Помещение персонала с санузлом	6,0	
137	Помещение для временного хранения пищевых отходов	4,8	Б4
138	ПМ	3,5	Б4
139	Помещение подготовки блюд к реализации с участком мойки кухонной посуды	29,2	Б4
140	Кабинет врача	18,7	
141	Процедурный (прибавочный) кабинет	12,9	
142	Помещение для хранения уборочного инвентаря, приготовления дезинфицирующих растворов	5,5	Б4
143	Окислительная медбюка	3,4	
144	Помещение СС	9,5	Б4
145	Кабинет с рабочим пространством для учителей. Тип 1	41,5	
146	Гардероб для учителей	19,1	
Итого:		1254,5	


Огнестойкая проходка через стену.

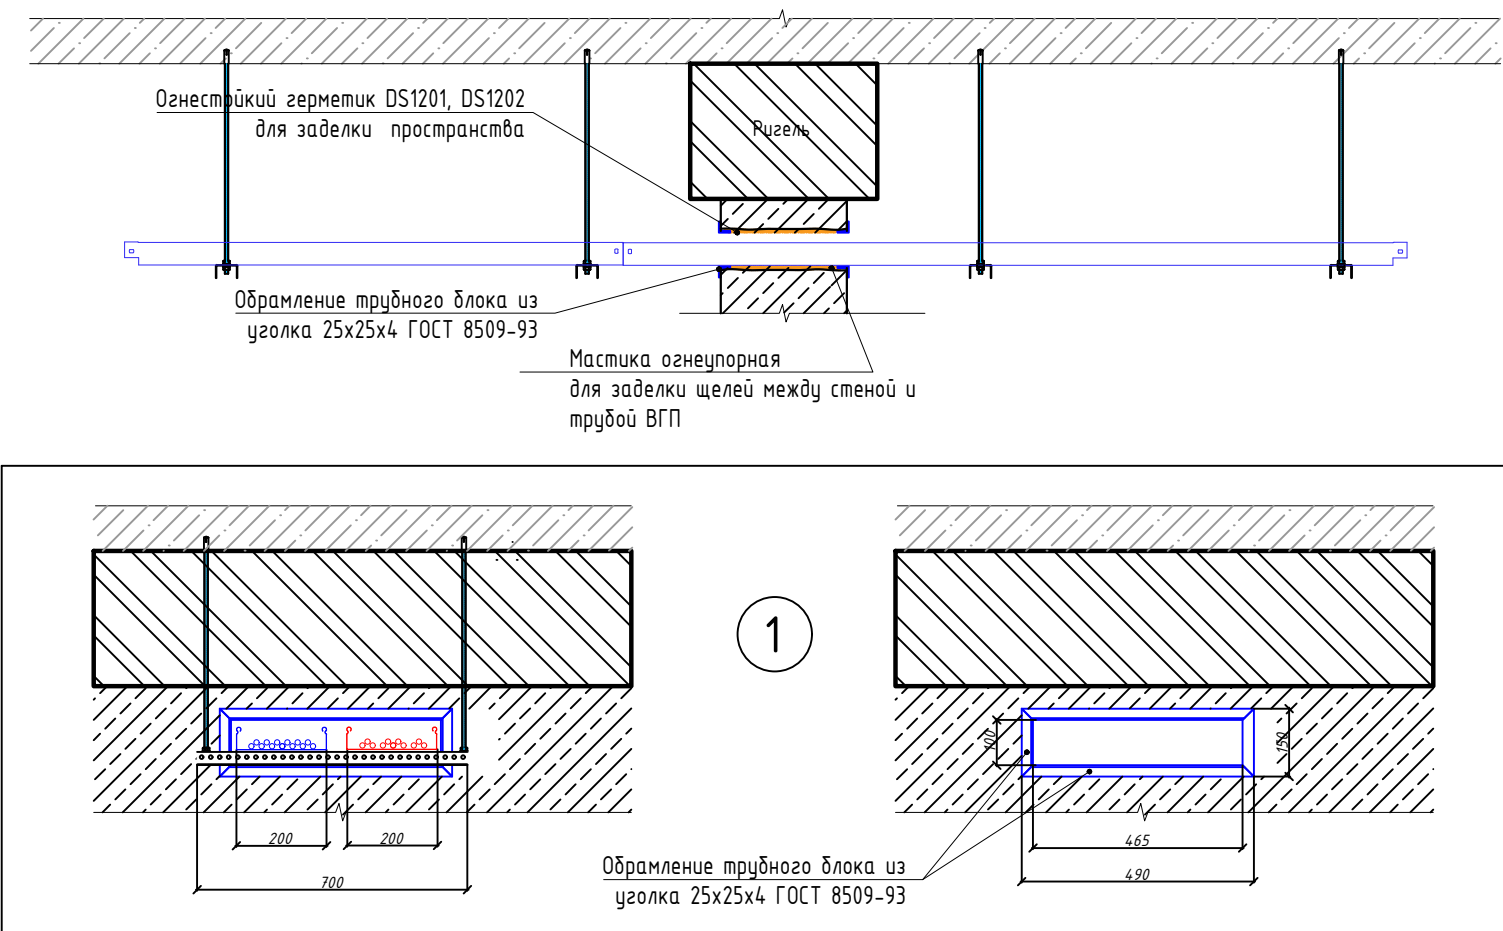


Узел крепления кабельной трассы

№	Обозначение	Наименование
1	СН408030	Анкер заливной М8
2	СН408032	Шпилька резьбовая М8
3	ВРЛ290*	Профиль PSL
4	СН108080	Гайка М8
5	СН120800	Шайба 8

Размер и марки профиля отмечены знаком "*" уточнить при монтаже

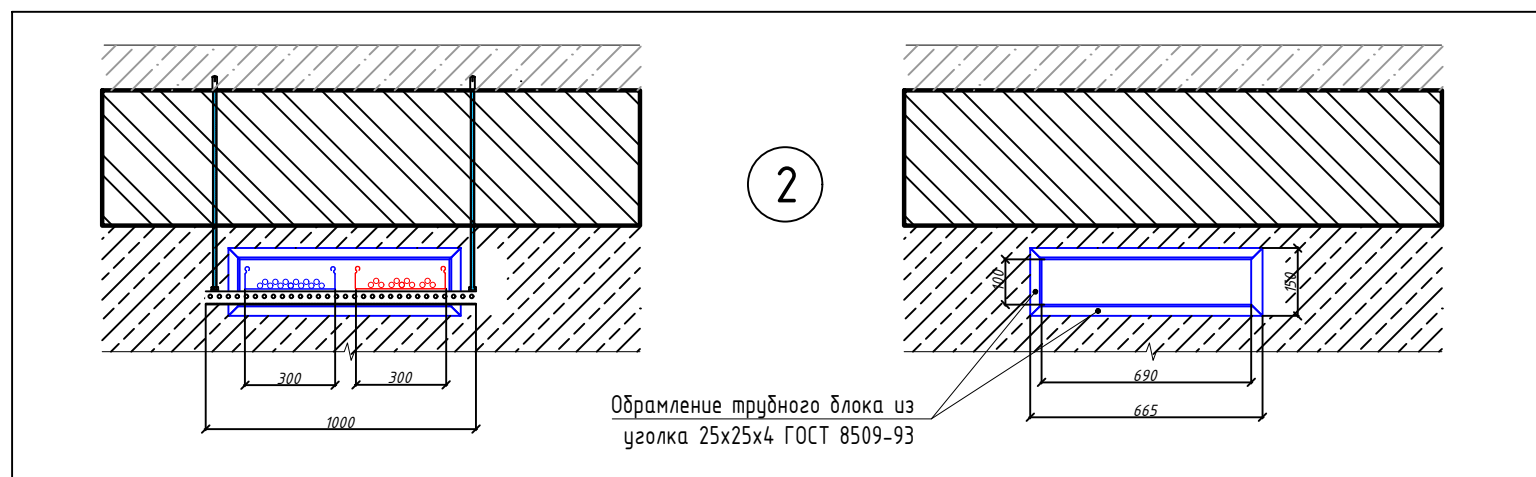

Огнестойкая проходка через перекрытие М 120

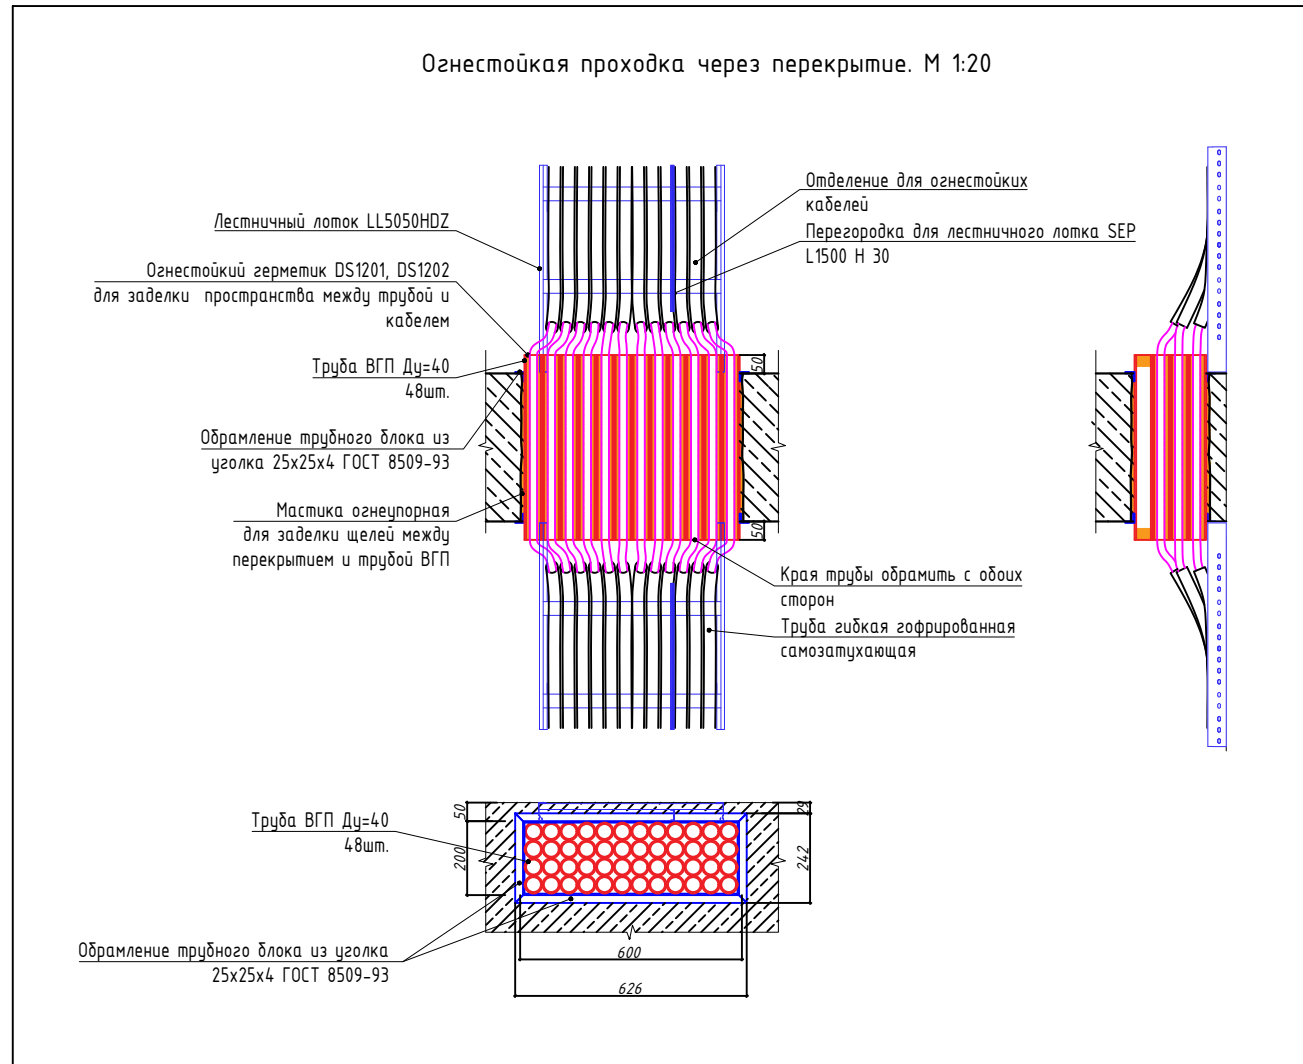

- Примечания:
1. Электропроектная организация РАЗРЕШАЕТ трассы прокладки кабельных трасс - корректировать самостоятельно по месту, исходя из структуры потолка и наличия инженерных систем.
 2. Проект предусматривает 100% кабельные конструкции для систем вынужденного электроснабжения.
 3. Кабели на разрезах кабельных трасс показаны условно.
 4. Расстояние между точками крепления кабельных трасс принять не более 800мм, при невозможности обеспечения такого расстояния допускается увеличение до 1000мм.
 5. Крышки лотков на разрезах кабельных конструкций не показаны.


696/П-25-АНО-Р-30М

Здание по адресу: г. Москва, ул. Барвиха, д.1, корп.1

Имя	Вол	Лист	№ док	Подп	Дата	Копировать	Статус	Лист	Листов
Разработчик	Гуляев	Иванов	07.26	07.26	07.26	Копировать	Р	1	Листов
Генеральный директор	Гуляев	Иванов	07.26	07.26	07.26	Копировать	Р	1	Листов
Н.контр.	Гуляев	Иванов	07.26	07.26	07.26	Копировать	Р	1	Листов


ООО "ПРОЕКТИ"

План 2 этажа

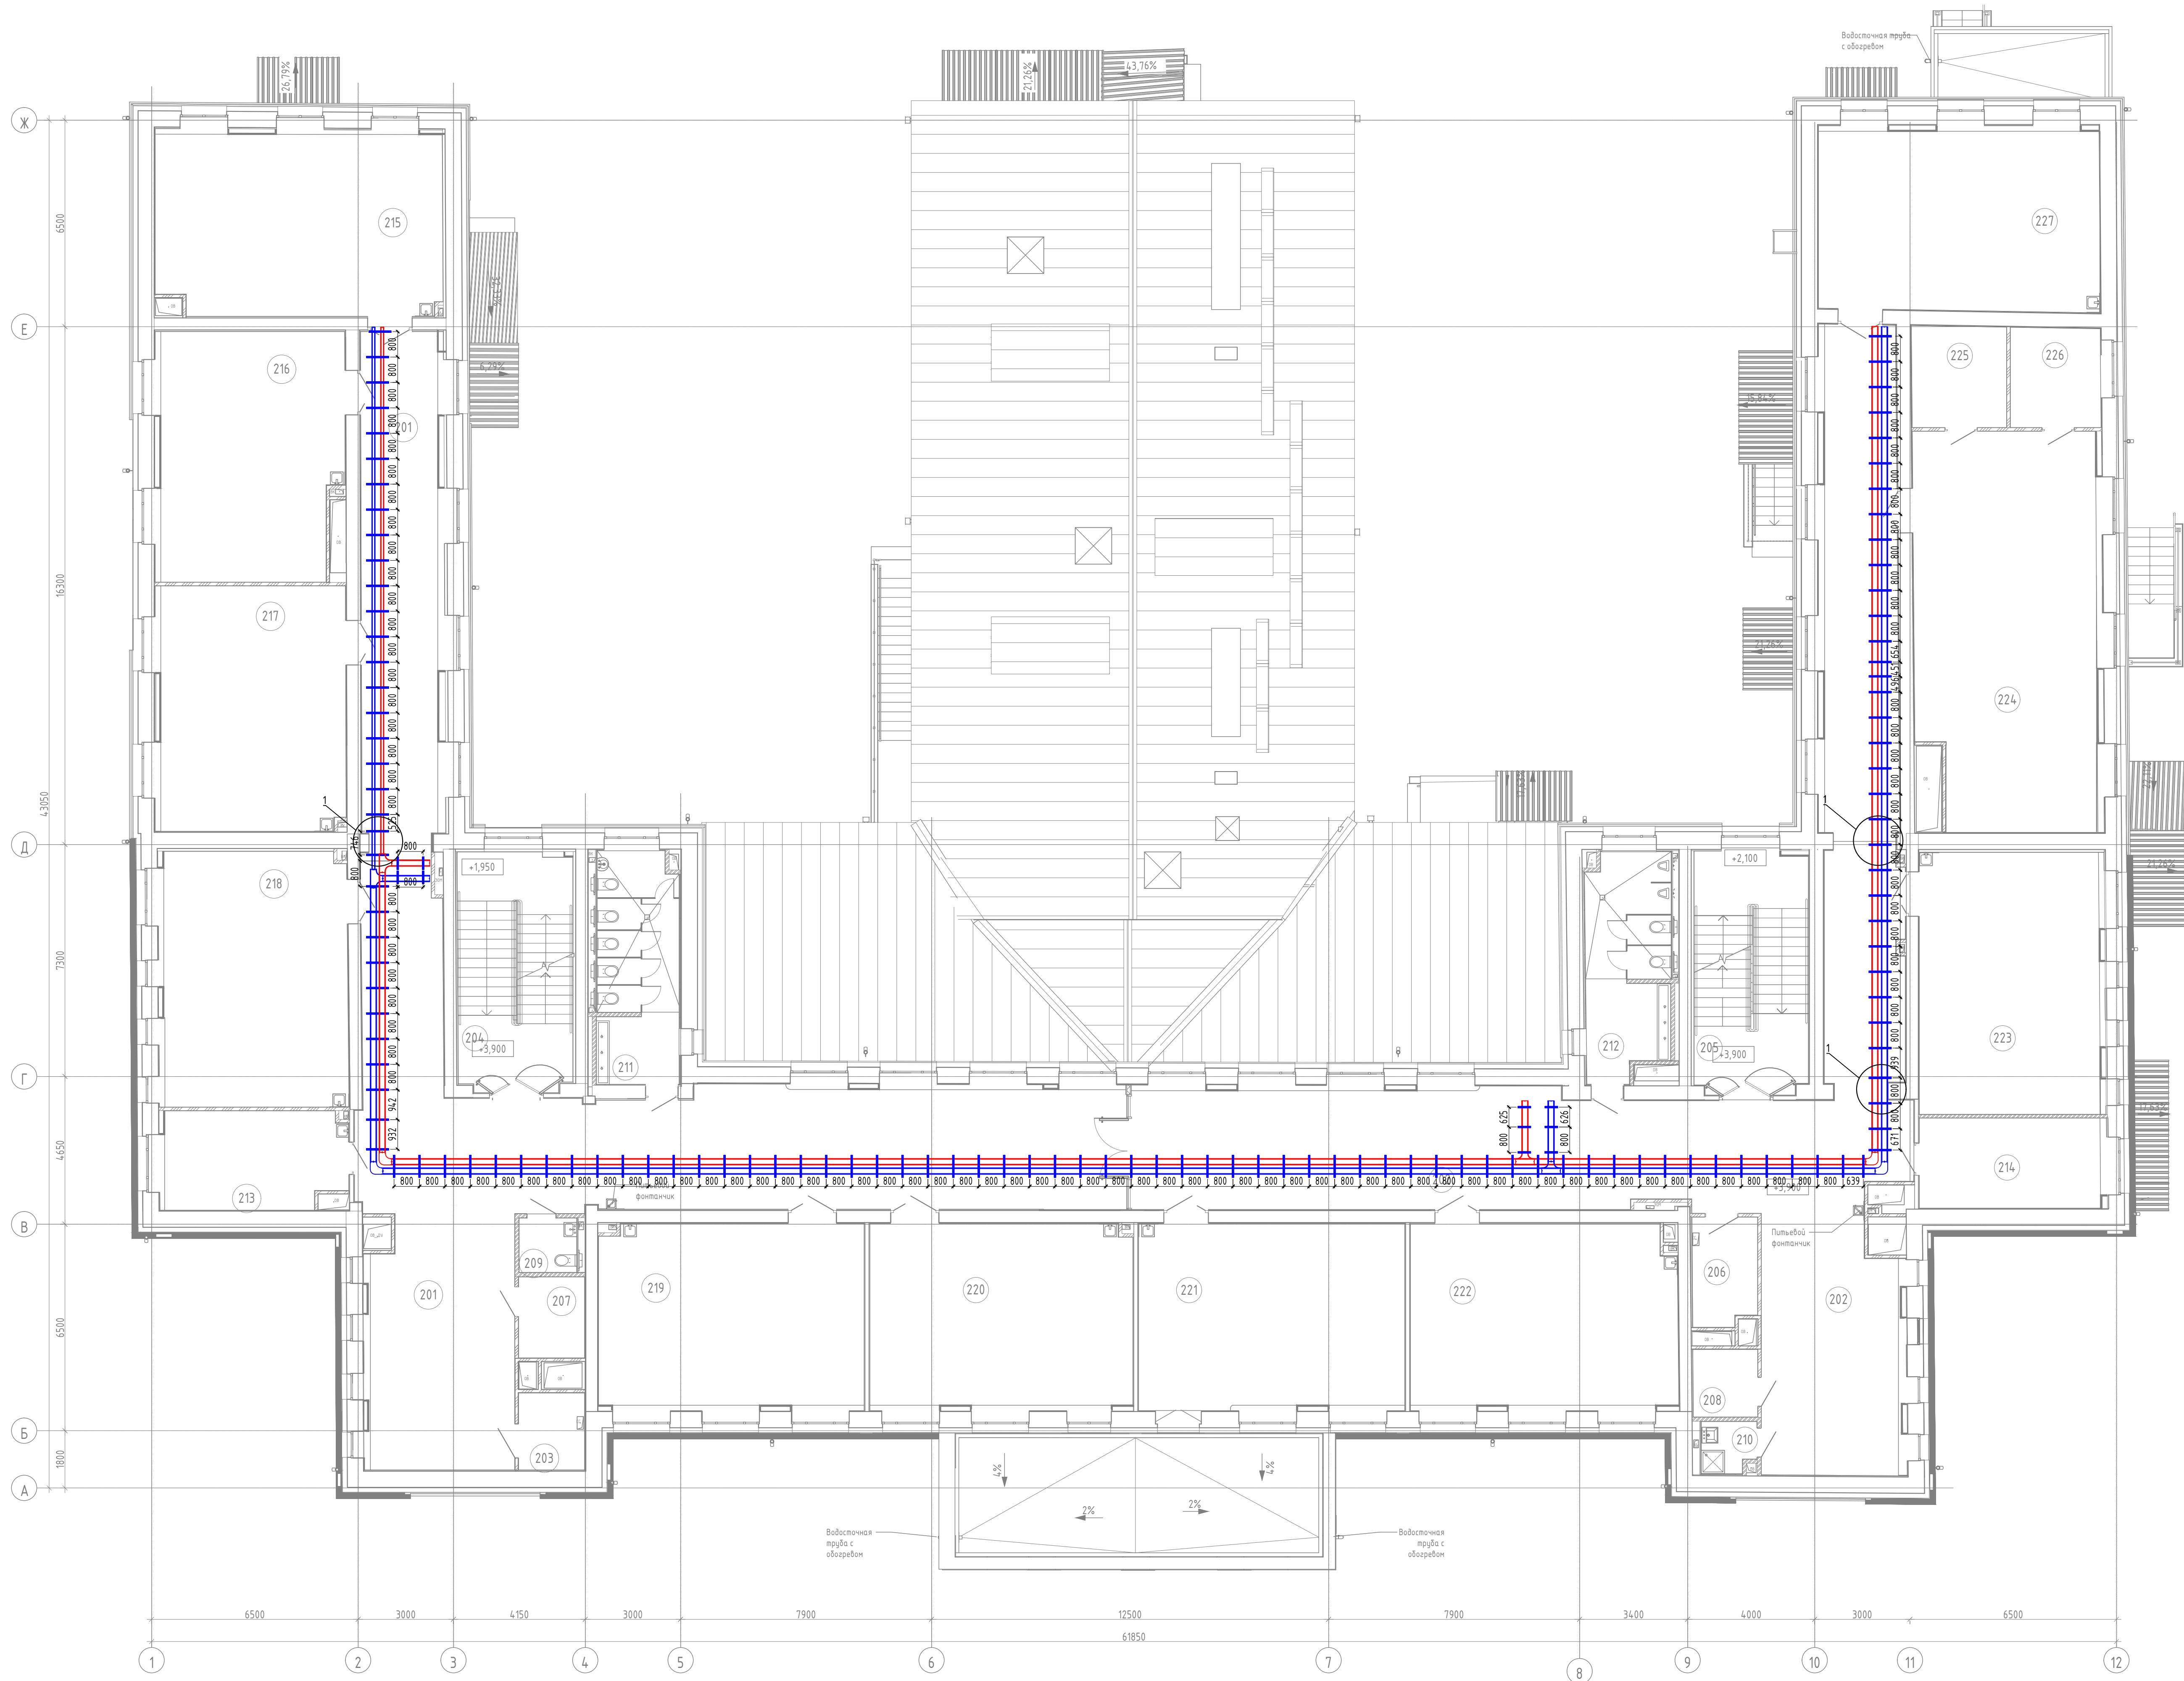


Экспликация помещений 2-го этажа			
Номер помеще-ния	Наименование	Площадь, м²	Кол. помеще-ния
201	Коридор с рекреацией	191,5	
202	Коридор с рекреацией	187,2	
203	Помещение СС	5,1	В4
204	Лестничная клетка (Тип А1)	27,4	
205	Лестничная клетка (Тип А1)	27,6	
206	Помещение СС	6,7	В4
207	Подсобное помещение	5,3	В4
208	Подсобное помещение	4,3	В4
209	Тублен для персонала	3,1	
210	ПМ	2,2	В4
211	Зеркала для девочек	19,1	
212	Зеркала для мальчиков	19,8	
213	Кабинет для индивидуальных занятий, в т.ч. учитель-наставник	18,1	
214	Административный кабинет, Тип 1	16,9	
215	Учебный кабинет	52,7	
216	Учебный кабинет	45,6	
217	Учебный кабинет	46,2	
218	Учебный кабинет	46,4	
219	Учебный кабинет	49,3	
220	Учебный кабинет	48,9	
221	Учебный кабинет	49,6	
222	Учебный кабинет	49,3	
223	Учебный кабинет	47,9	
224	Гимнастический зал	72,6	
225	Раздевальня Тип 1	9,5	
226	Раздевальня Тип 1	8,9	
227	Учебный кабинет	51,7	
		1111,7	

Огнестойкая проходка через стену.

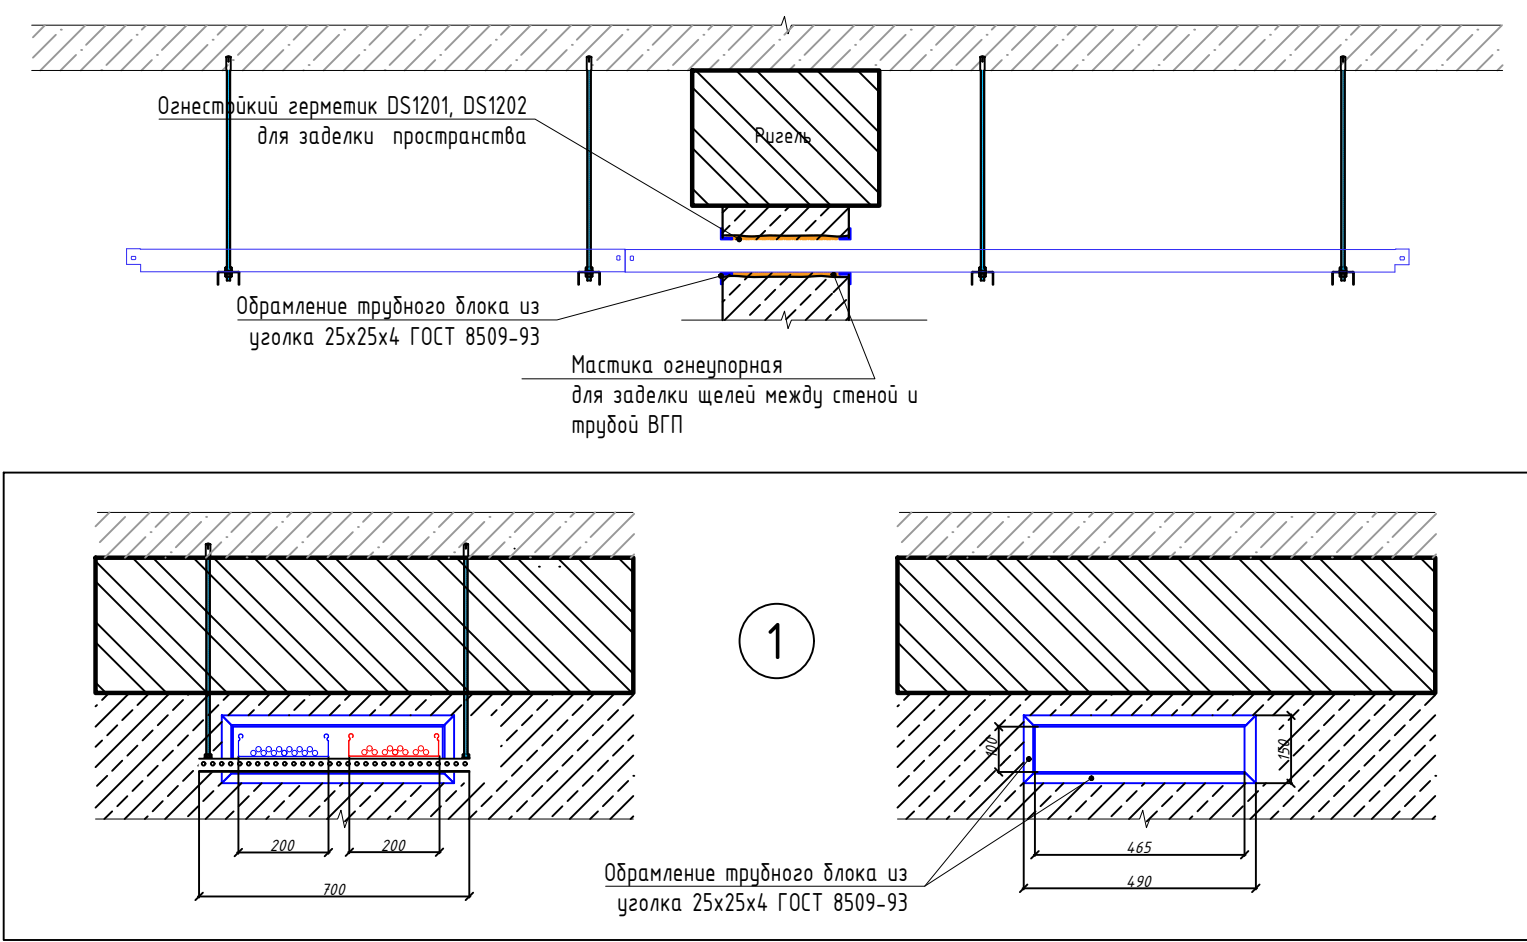

Огнестойкая проходка через перекрытие. М 1:20

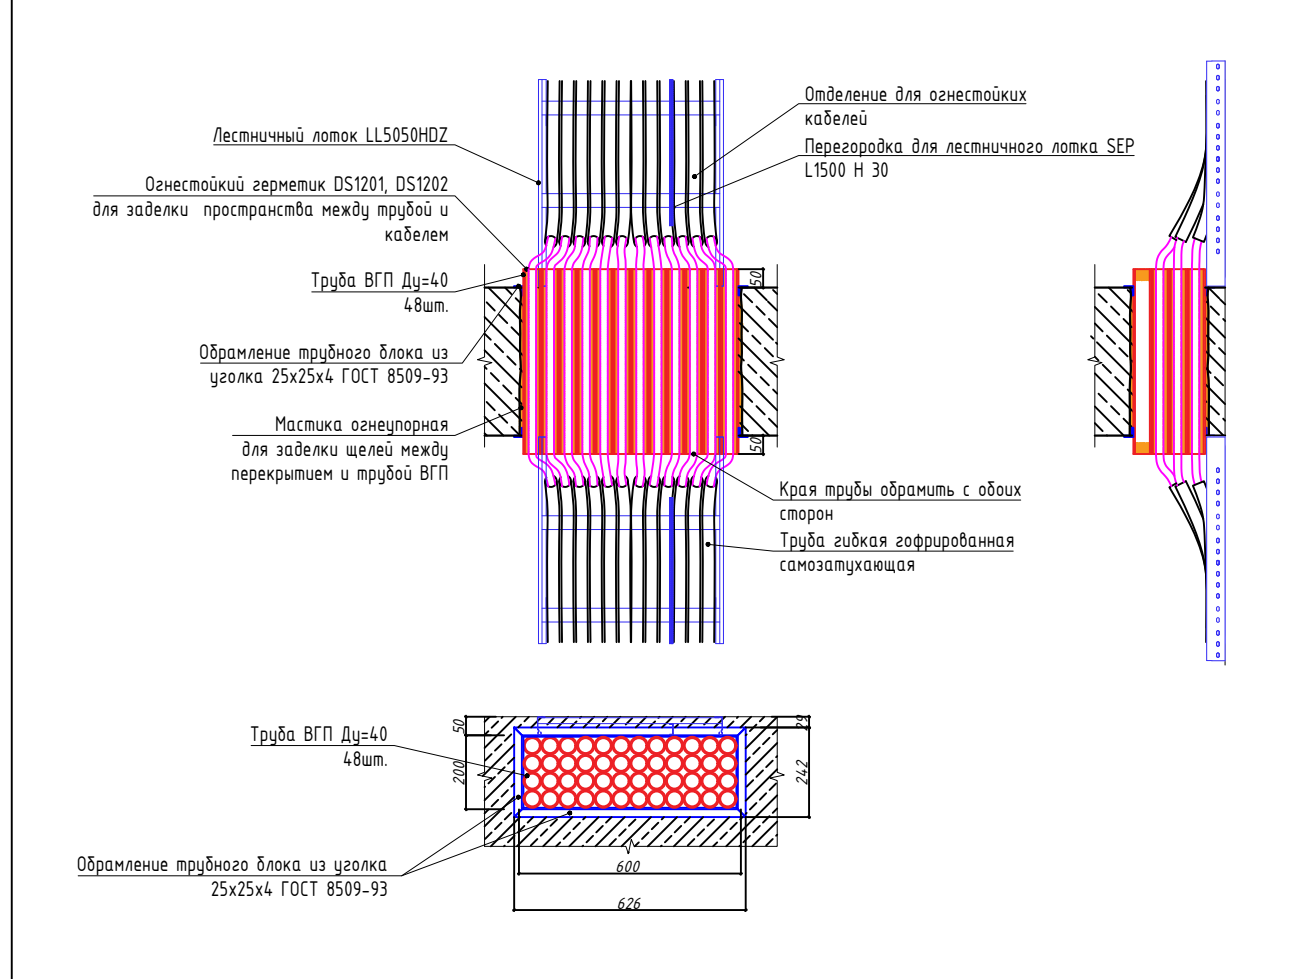

Условные обозначения:

- Лоток
- Лоток для кабелей ПЭС/ПЗ
- Профиль монтажный для кабельных конструкций с указанием типоразмера.

Узел крепления кабельной трассы

№	Обозначение	Наименование
1	СМ20802	Анкер заливочный МВ
2	СМ20802	Шпилька резьбовая МВ
3	ВР1290+	Профиль PSL
4	СМ10800	Гайка МВ
5	СМ20800	Шайба В

Размер и марки профиля отмечены знаком "х" условно при монтаже

- Примечания:
1. Электронная организация РАЗРЕШАЕТся прокладки кабельных трасс – корректировать составленные по месту, исходя из структуры потолка и наличия инженерных систем.
 2. Прокладка кабельных конструкций для систем внутреннего электроснабжения.
 3. Кабели на разрезе кабельных трасс показаны условно.
 4. Расстояние между точками крепления кабельных трасс принять не более 800мм, при необходимости обеспечения такого расстояния возможно увеличение до 1000мм.
 5. Крышки лотков на разрезе кабельных конструкций не показаны.


696/П-25-АНО-Р-30М

Данные по адресу: г. Москва, ул. Барвиха, д.1, корп.1

Имя	Кол.	Лист	№ док.	Подп.	Дата	Копированный проект Государственного бюджетного образовательного учреждения города Москвы Школа №1282	Статус	Лист	Листов
Разработчик	Гуляко	07.26	07.26				Р	2	
Н.контр.	Гуляко	07.26				План кабельных конструкций сетей выделенного электроснабжения 2 этажа			



Формат

План 3 этажа

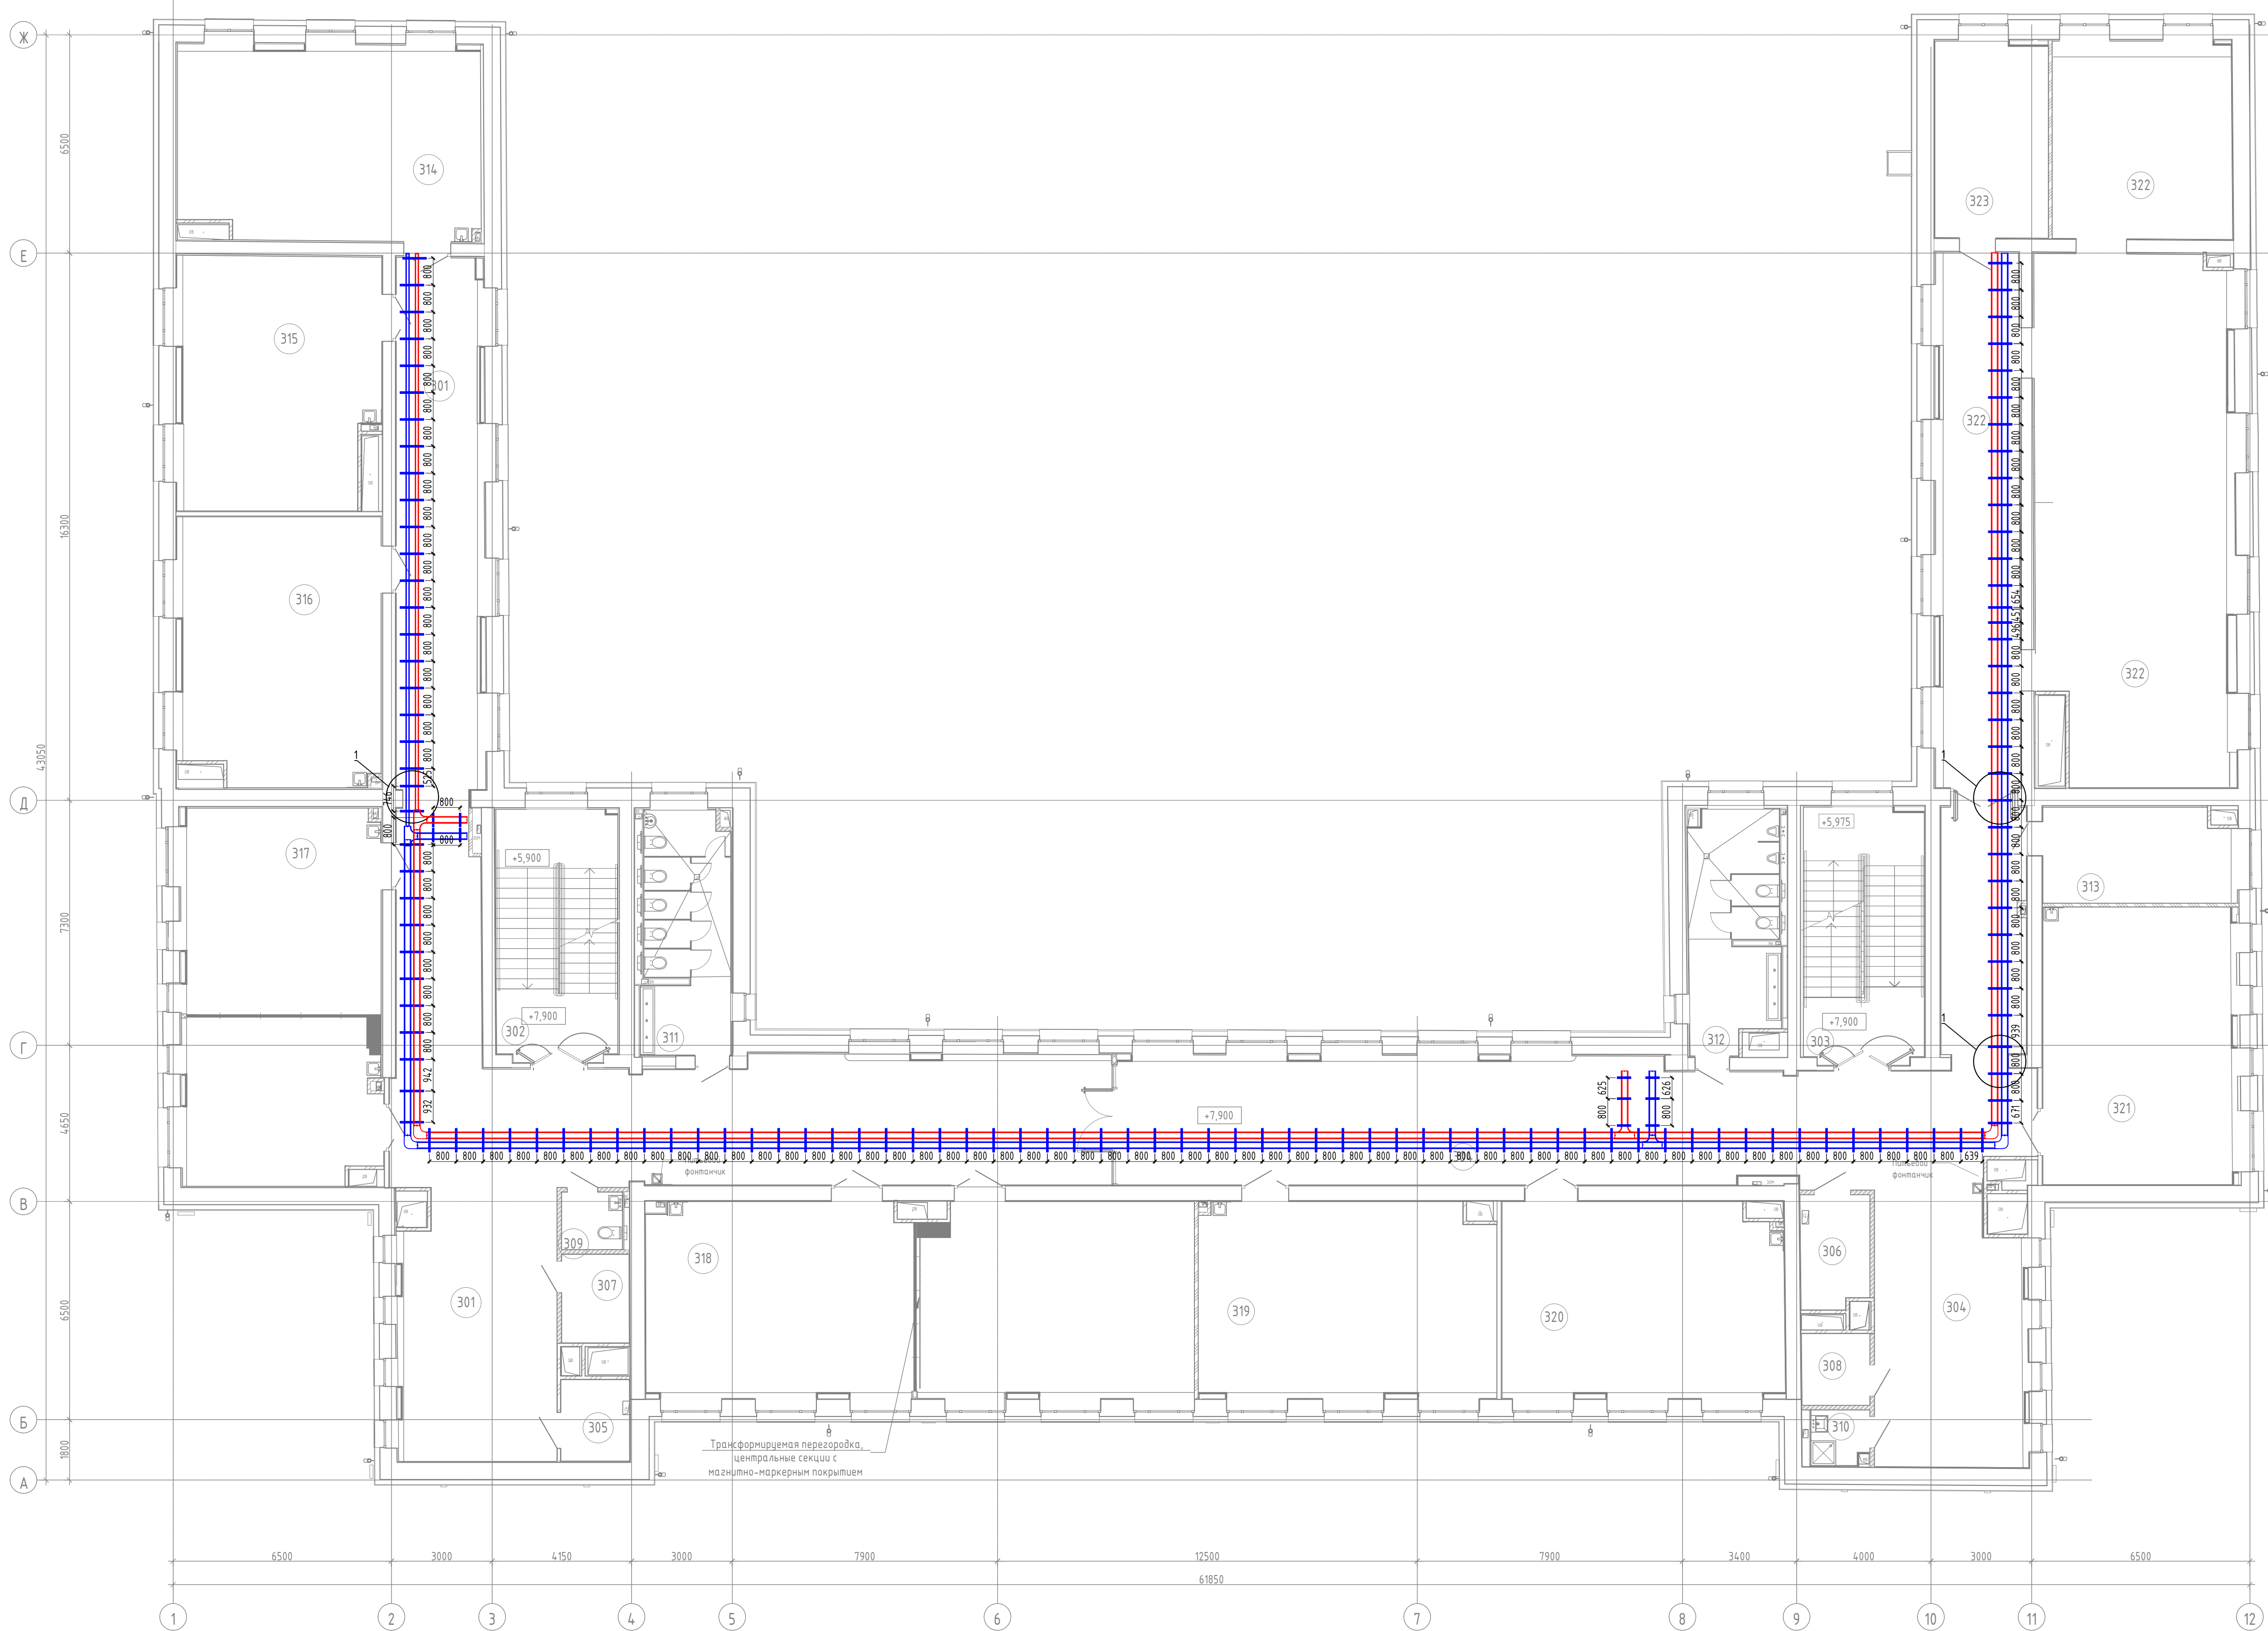

Экспликация помещений 3-го этажа			
Номер помеще-ния	Наименование	Площадь, м²	Кот.-помеще-ний
301	Коридор с рекреацией	179,8	
302	Лестничная клетка (Тип А)	27,3	
303	Лестничная клетка (Тип А)	27,7	
304	Коридор с рекреацией	155,8	
305	Помещение СС	5,1	В4
306	Помещение СС	6,8	В4
307	Подсобное помещение	5,3	В4
308	Подсобное помещение	4,3	В4
309	Туалет для персонала	3,1	
310	ПМ	2,3	В4
311	Зубная для девочек	19,0	
312	Зубная для мальчиков	18,9	
313	Кабинет для индивидуальных занятий, 6	16,0	
314	Учебный кабинет	51,9	
315	Учебный кабинет	44,6	
316	Учебный кабинет	47,9	
317	Кабинет иностранного языка с возможностью деления/трансформированной перегородкой на два помещения	66,5	
318	Персональная аудитория с возможностью деления/трансформированной перегородкой на два помещения	94,7	
319	Учебный кабинет	51,4	
320	Учебный кабинет	48,7	
321	Учебный кабинет	47,9	
322	Мультифункциональный информационный выделенный центр с ресурсами для индивидуальных и групповых занятий, учебный центр детских учреждений	163,4	
323	Мультифункциональный информационный выделенный центр (хранение (закрытый фонд) и выдача книг)	119,8	В3
		1108,1	

Огнестойкая проходка через стену.

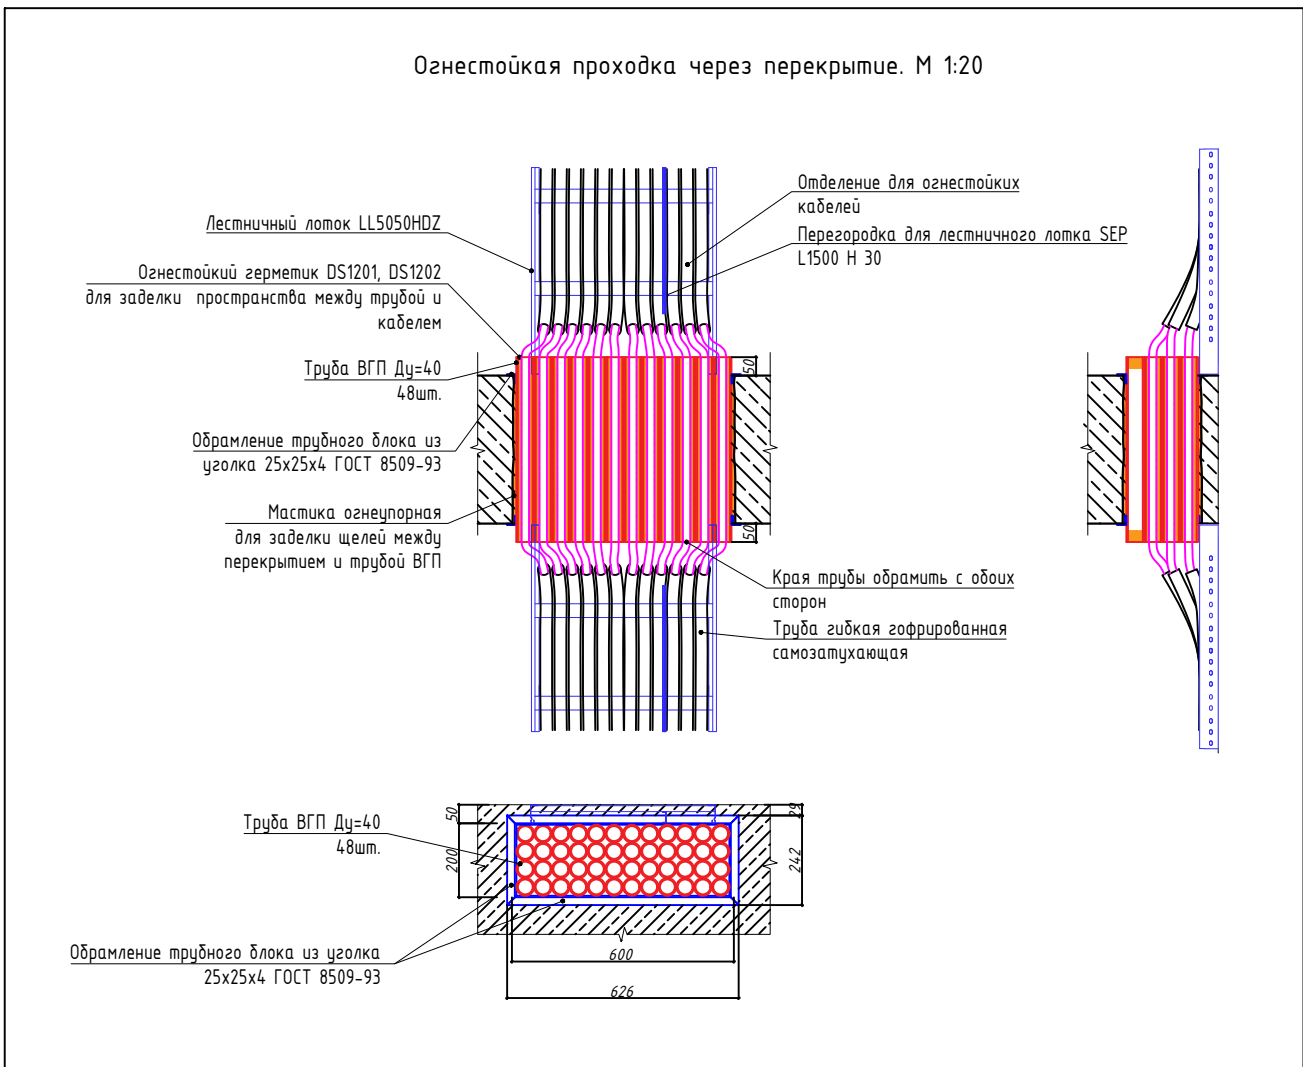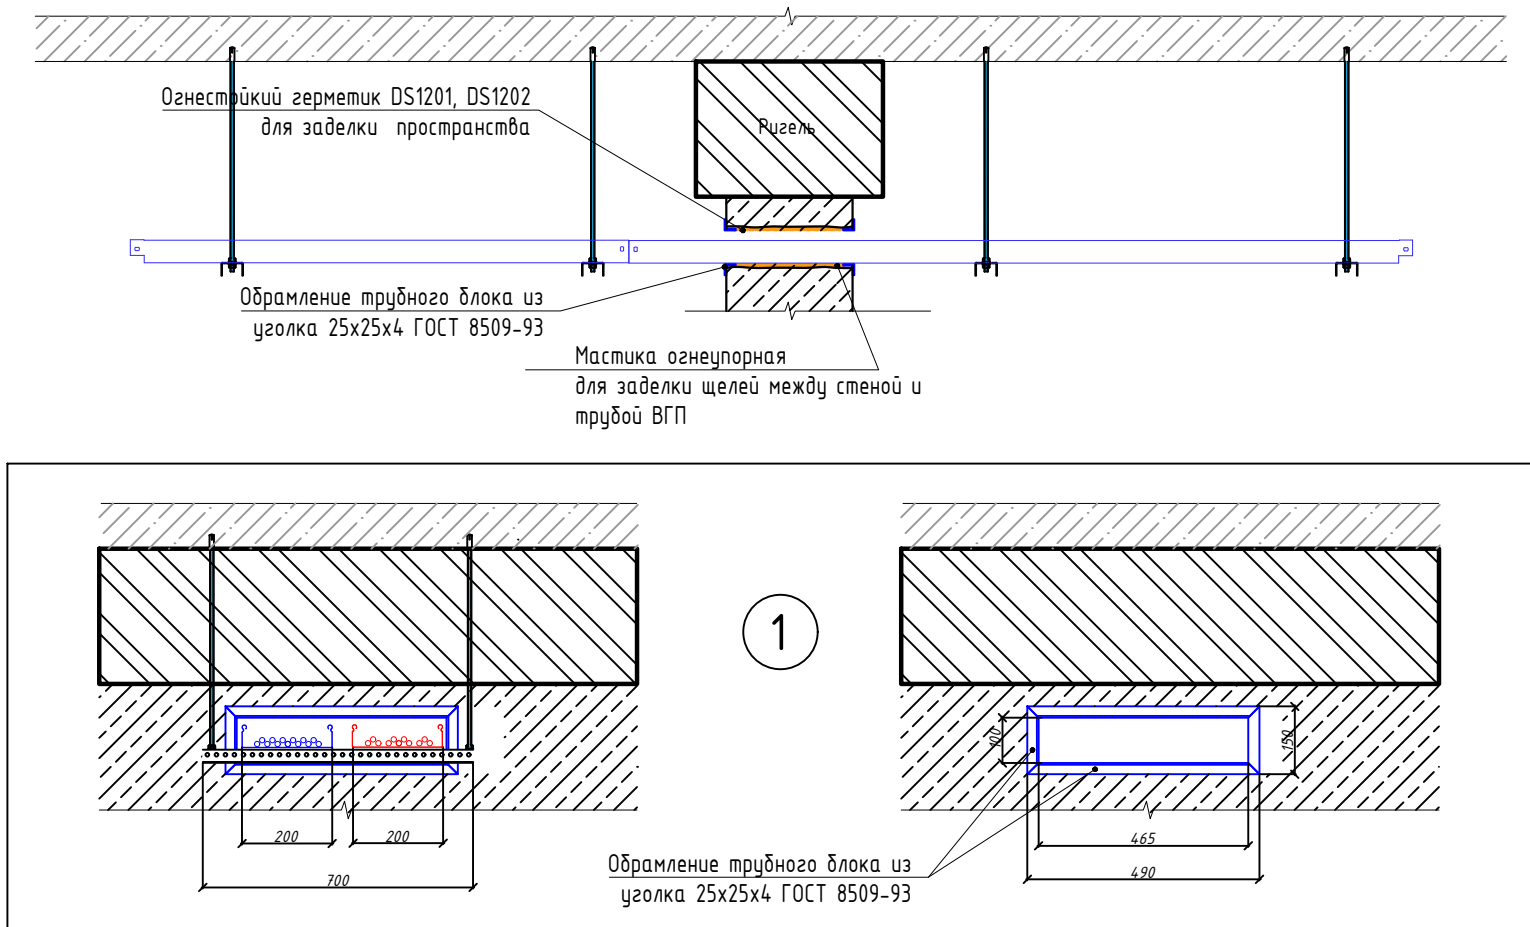

Условные обозначения:


- Лоток
- Лоток для кабелей ПЗСПЗ
- Профиль монтажный для кабельных конструкций с указанием типоразмера.

Поз.	Обозначение	Наименование
1	СМ100830	Анкер заливной МВ
2	СМ200802	Шпилька резьбовая МВ
3	ВР1250	Профиль ПСЛ
4	СМ100800	Гайка МВ
5	СМ200800	Шайба МВ

Размер и марки профиля отмечены знаком "+" указать при монтаже


- Примечания:
- Экспликация помещений 3-го этажа РАЗРАБАТЫВАЕТСЯ проектом кабельных трасс - корректировать самостоятельно по месту, исходя из структуры потолка и наличия инженерных систем;
 - Проект предусматривает ГОРЮЩИЕ кабельные конструкции для систем внутреннего электроснабжения;
 - Кабели на разрыве кабельных трасс показаны условно;
 - Расстояние между точками крепления кабельных трасс принять не более 800мм, при необходимости обеспечения такого расстояния возможно увеличение до 1000мм;
 - Крышки лотков на разрыве кабельных конструкций не показаны.

План 4 этажа

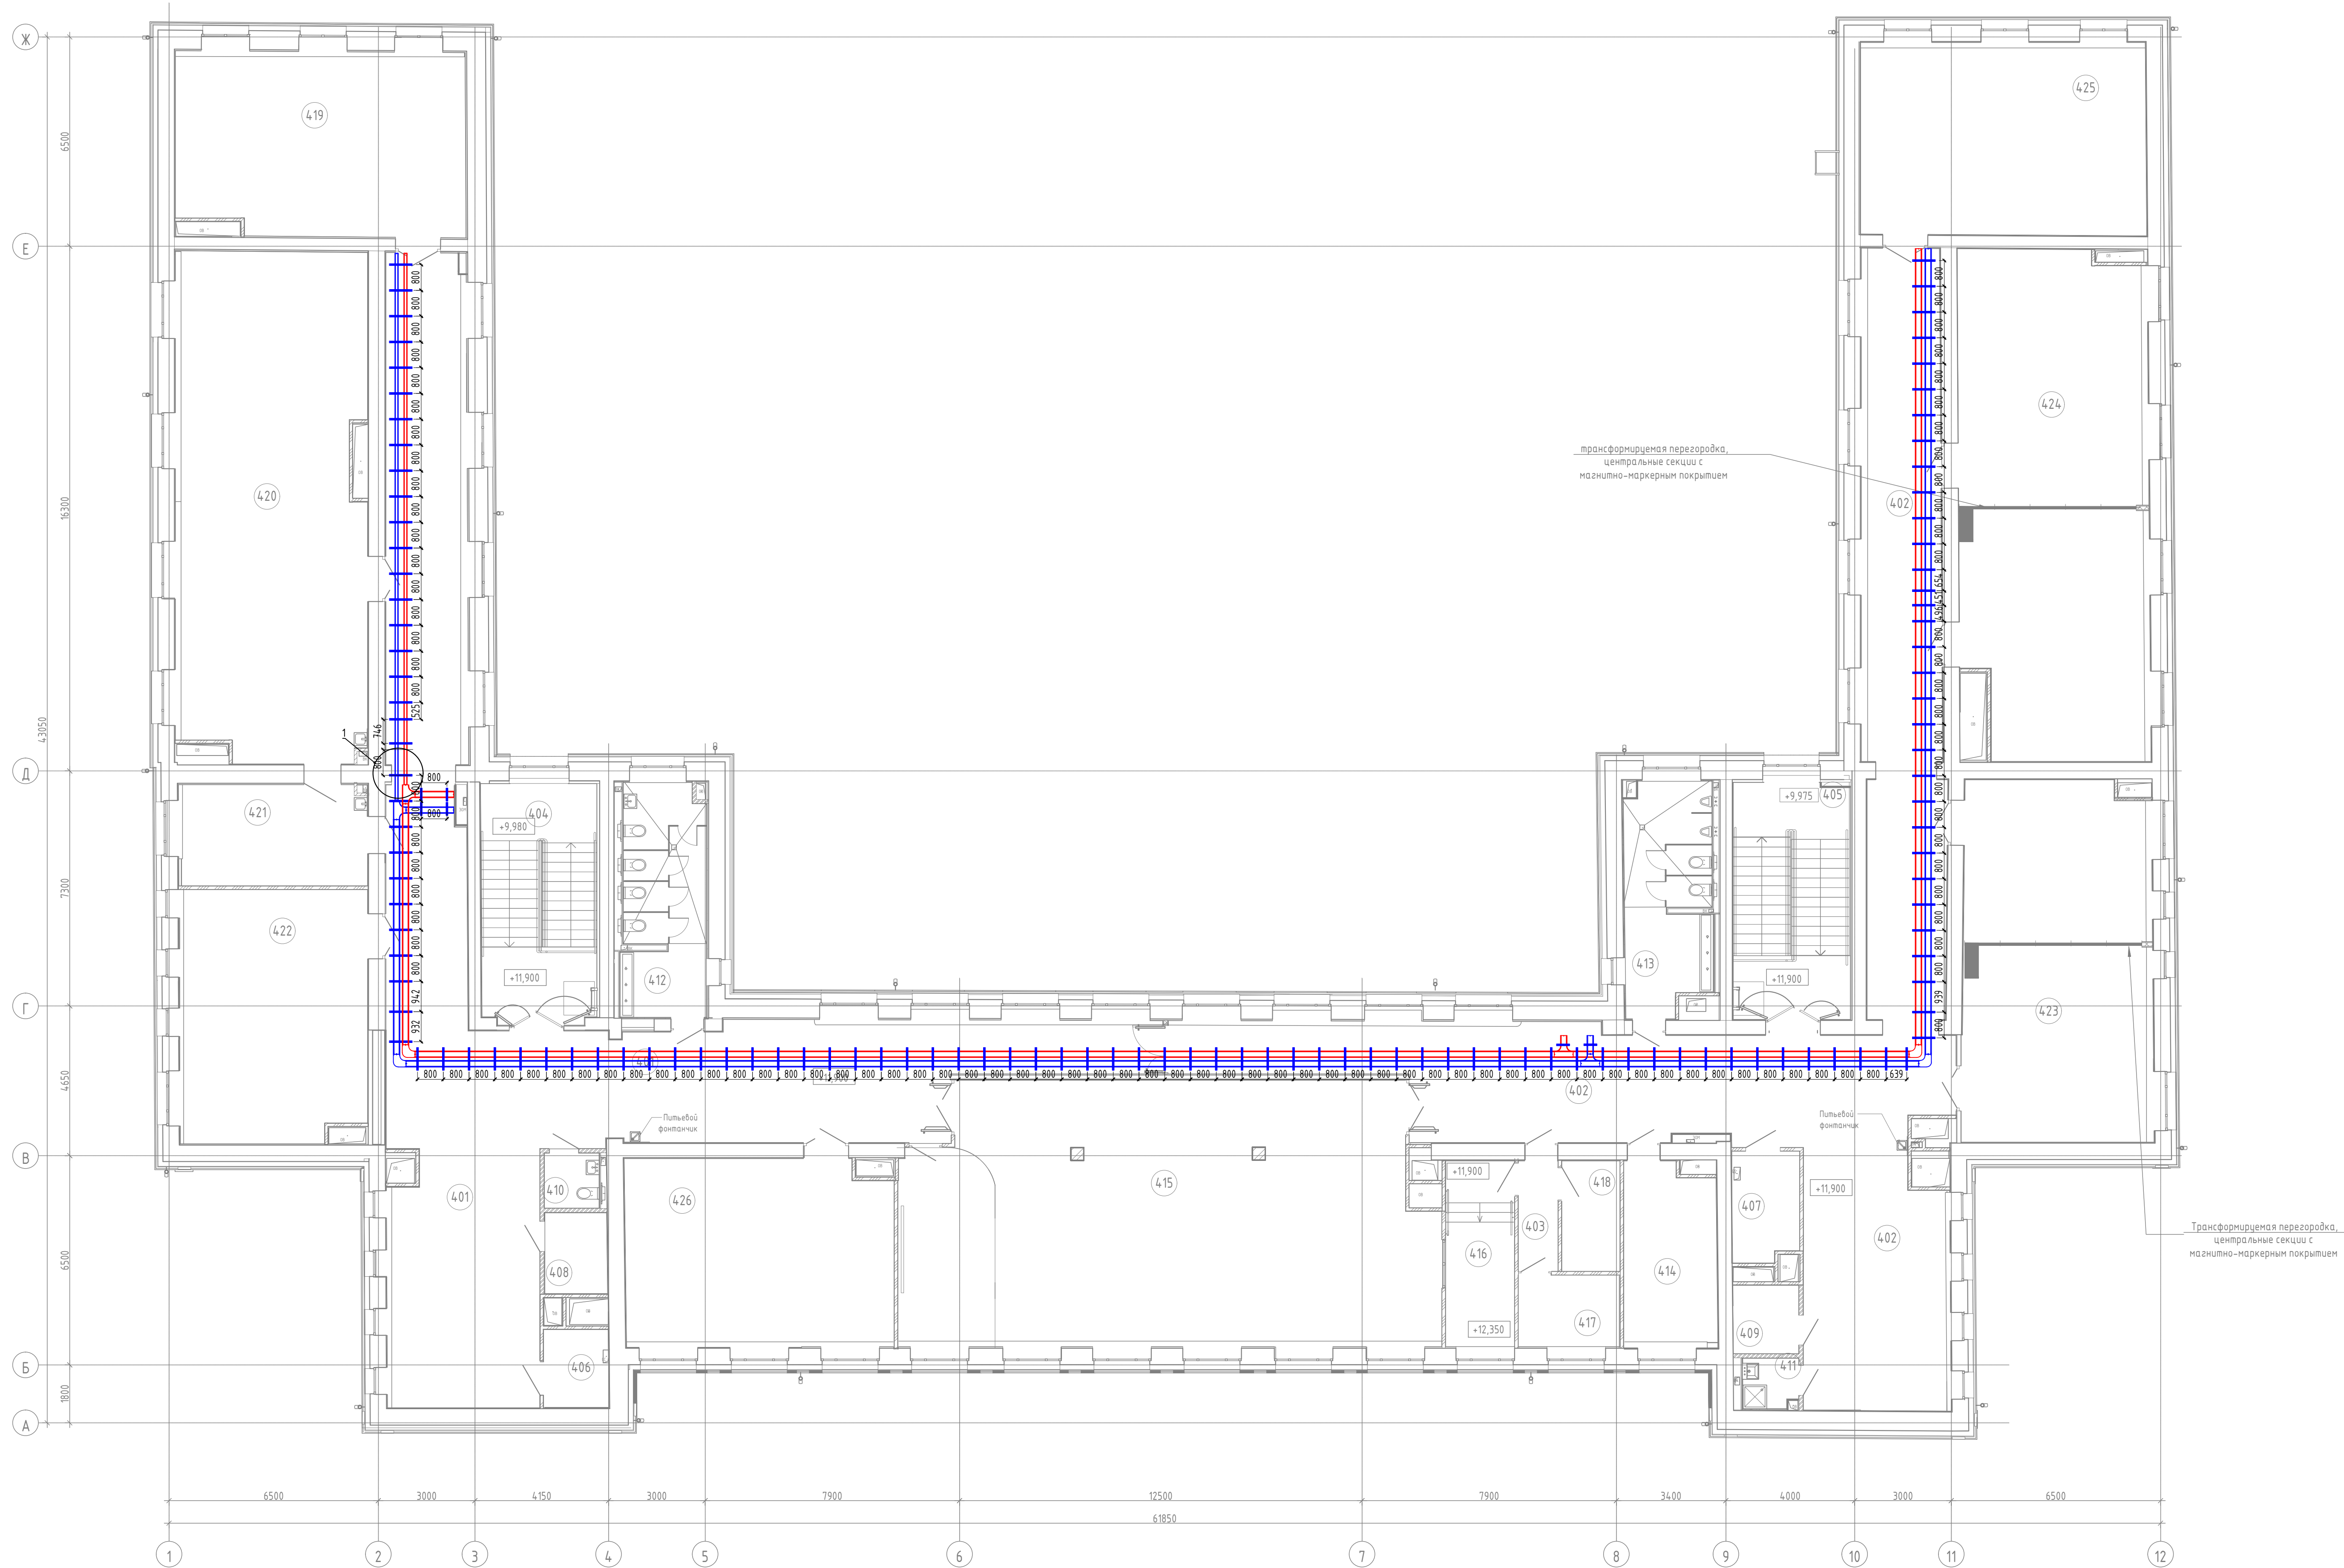

Экспликация помещений 4-го этажа			
Номер помещения	Назначение	Площадь, м²	Кол. помещ.
401	Коридор с рекреацией	173,6	
402	Коридор с рекреацией	166,2	
403	Танц-зал	4,1	
404	Автоматическая клетка (Тан АП)	26,9	
405	Автоматическая клетка (Тан АП)	26,8	
406	Помещение СС	5,0	В4
407	Помещение СС	6,8	В4
408	Подсобное помещение	5,0	В4
409	Подсобное помещение	4,3	В4
410	Туалет для персонала	2,9	
411	ПМ	2,1	В4
412	Уборная для девочек	19,0	
413	Уборная для мальчиков	19,1	
414	Кабинет для индивидуальных занятий, 8 п.ч. специализированным	16,2	
415	Актовый зал (с эстрадой в цокольном этаже)	131,1	
416	Технический центр	12,4	В3
417	Артистическая	6,9	
418	Кабинет инвентаря	6,1	В4
419	Кабинет математики	50,8	
420	Учебный кабинет (для изучения естественных наук/географии Тип 2)	92,4	
421	Лаборатория биологии	18,3	В3
422	Учебный кабинет (история)	45,0	
423	Кабинет иностранного языка с возможностью децентрализованной перегородкой на два помещения	65,9	
424	Учебный кабинет информатики с возможностью децентрализованной перегородкой на два помещения	90,5	
425	Кабинет русского языка и литературы	53,4	
426	Кабинет русского языка и литературы	48,1	
		1098,5	

Огнестойкая проходка через стену.

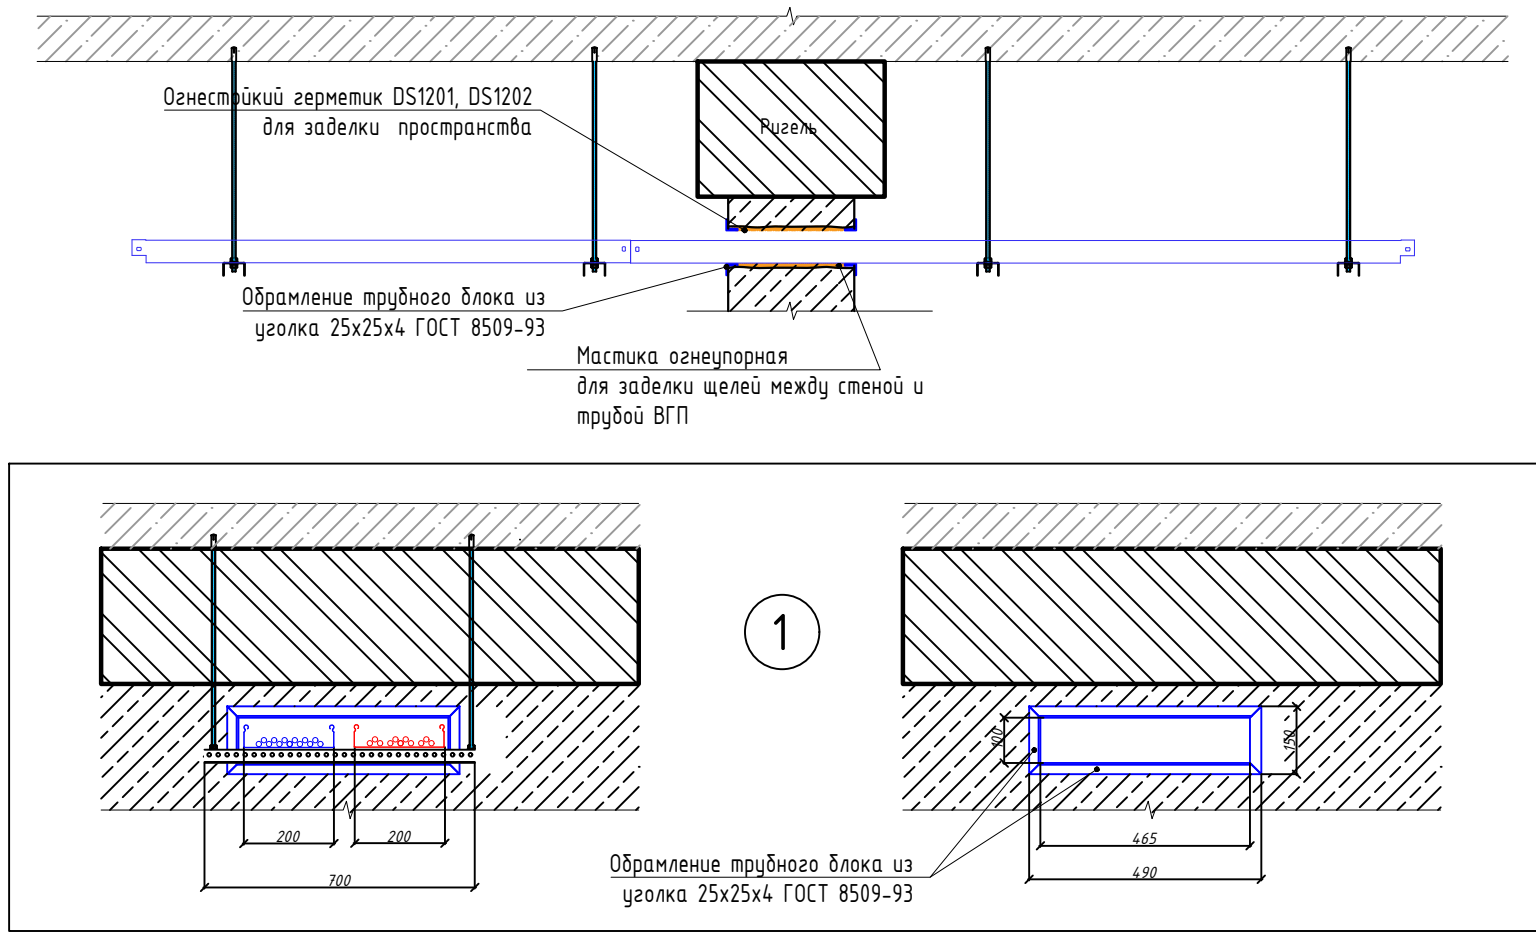


Условные обозначения:
— Лоток
— Лоток для кабелей ПЭСПЗ
— Профиль монтажный для кабельных конструкций с указанием типоразмера.

Узел крепления кабельной трассы

Поз.	Обозначение	Назначение
1	СМ400830	Анкер резьбовой М8
2	СМ200802	Штырь резьбовой М8
3	ВР1294	Профиль ПСЛ
4	СМ10800	Головка М8
5	СМ120800	Шайба 8

Размер и номер профиля обозначены знаком "4" уточнить при монтаже

Огнестойкая проходка через перекрытие. М 1:20

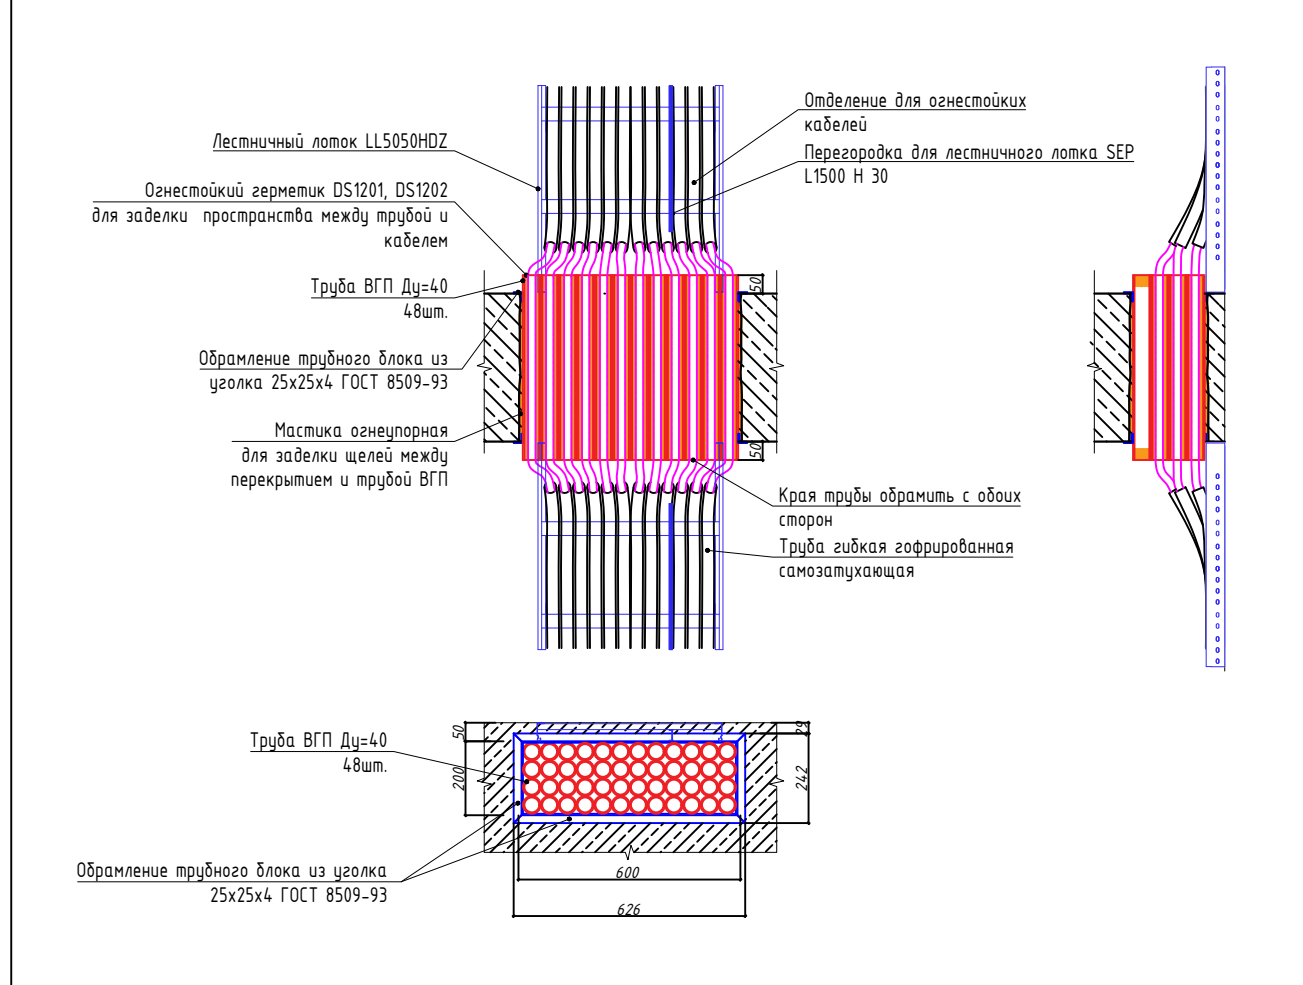

- Примечания:
- Экспликация помещений 4-го этажа: РАЗРЕШАЕТСЯ прокладка кабельных трасс - корректировать самостоятельно по месту, исходя из структуры потолка и наличия инженерных систем;
 - Проектные предельные значения кабельных конструкций для систем внутреннего электроснабжения;
 - Кабели на разрезе кабельных трасс показаны условно;
 - Расстояние между точками крепления кабельных трасс принять не более 800мм, при необходимости обеспечения такого расстояния возможно увеличение до 1000мм;
 - Крышки лотков на разрезе кабельных конструкций не показаны.

696/П-25-АНО-Р-30М

Здание по адресу: г. Москва, ул. Бардовская, д.1, корп.1

Имя	Кол.	Лист	№ док.	Подп.	Дата	Кол.	Лист	№ док.	Подп.	Дата	Кол.	Лист	№ док.	Подп.	Дата
Разработчик	Гуляко	Николаев	07.26	07.26	07.26	07.26	07.26	07.26	07.26	07.26	07.26	07.26	07.26	07.26	07.26
Генеральный директор	Гуляко	Гуляко	07.26	07.26	07.26	07.26	07.26	07.26	07.26	07.26	07.26	07.26	07.26	07.26	07.26
Н.контр.	Гуляко	Гуляко	07.26	07.26	07.26	07.26	07.26	07.26	07.26	07.26	07.26	07.26	07.26	07.26	07.26


Капитальный ремонт Государственного бюджетного общеобразовательного учреждения города Москвы Школа №1282

План кабельных конструкций сетей внутреннего электроснабжения 4 этажа

ООО УПРОЕКТ

Формат

План кровли

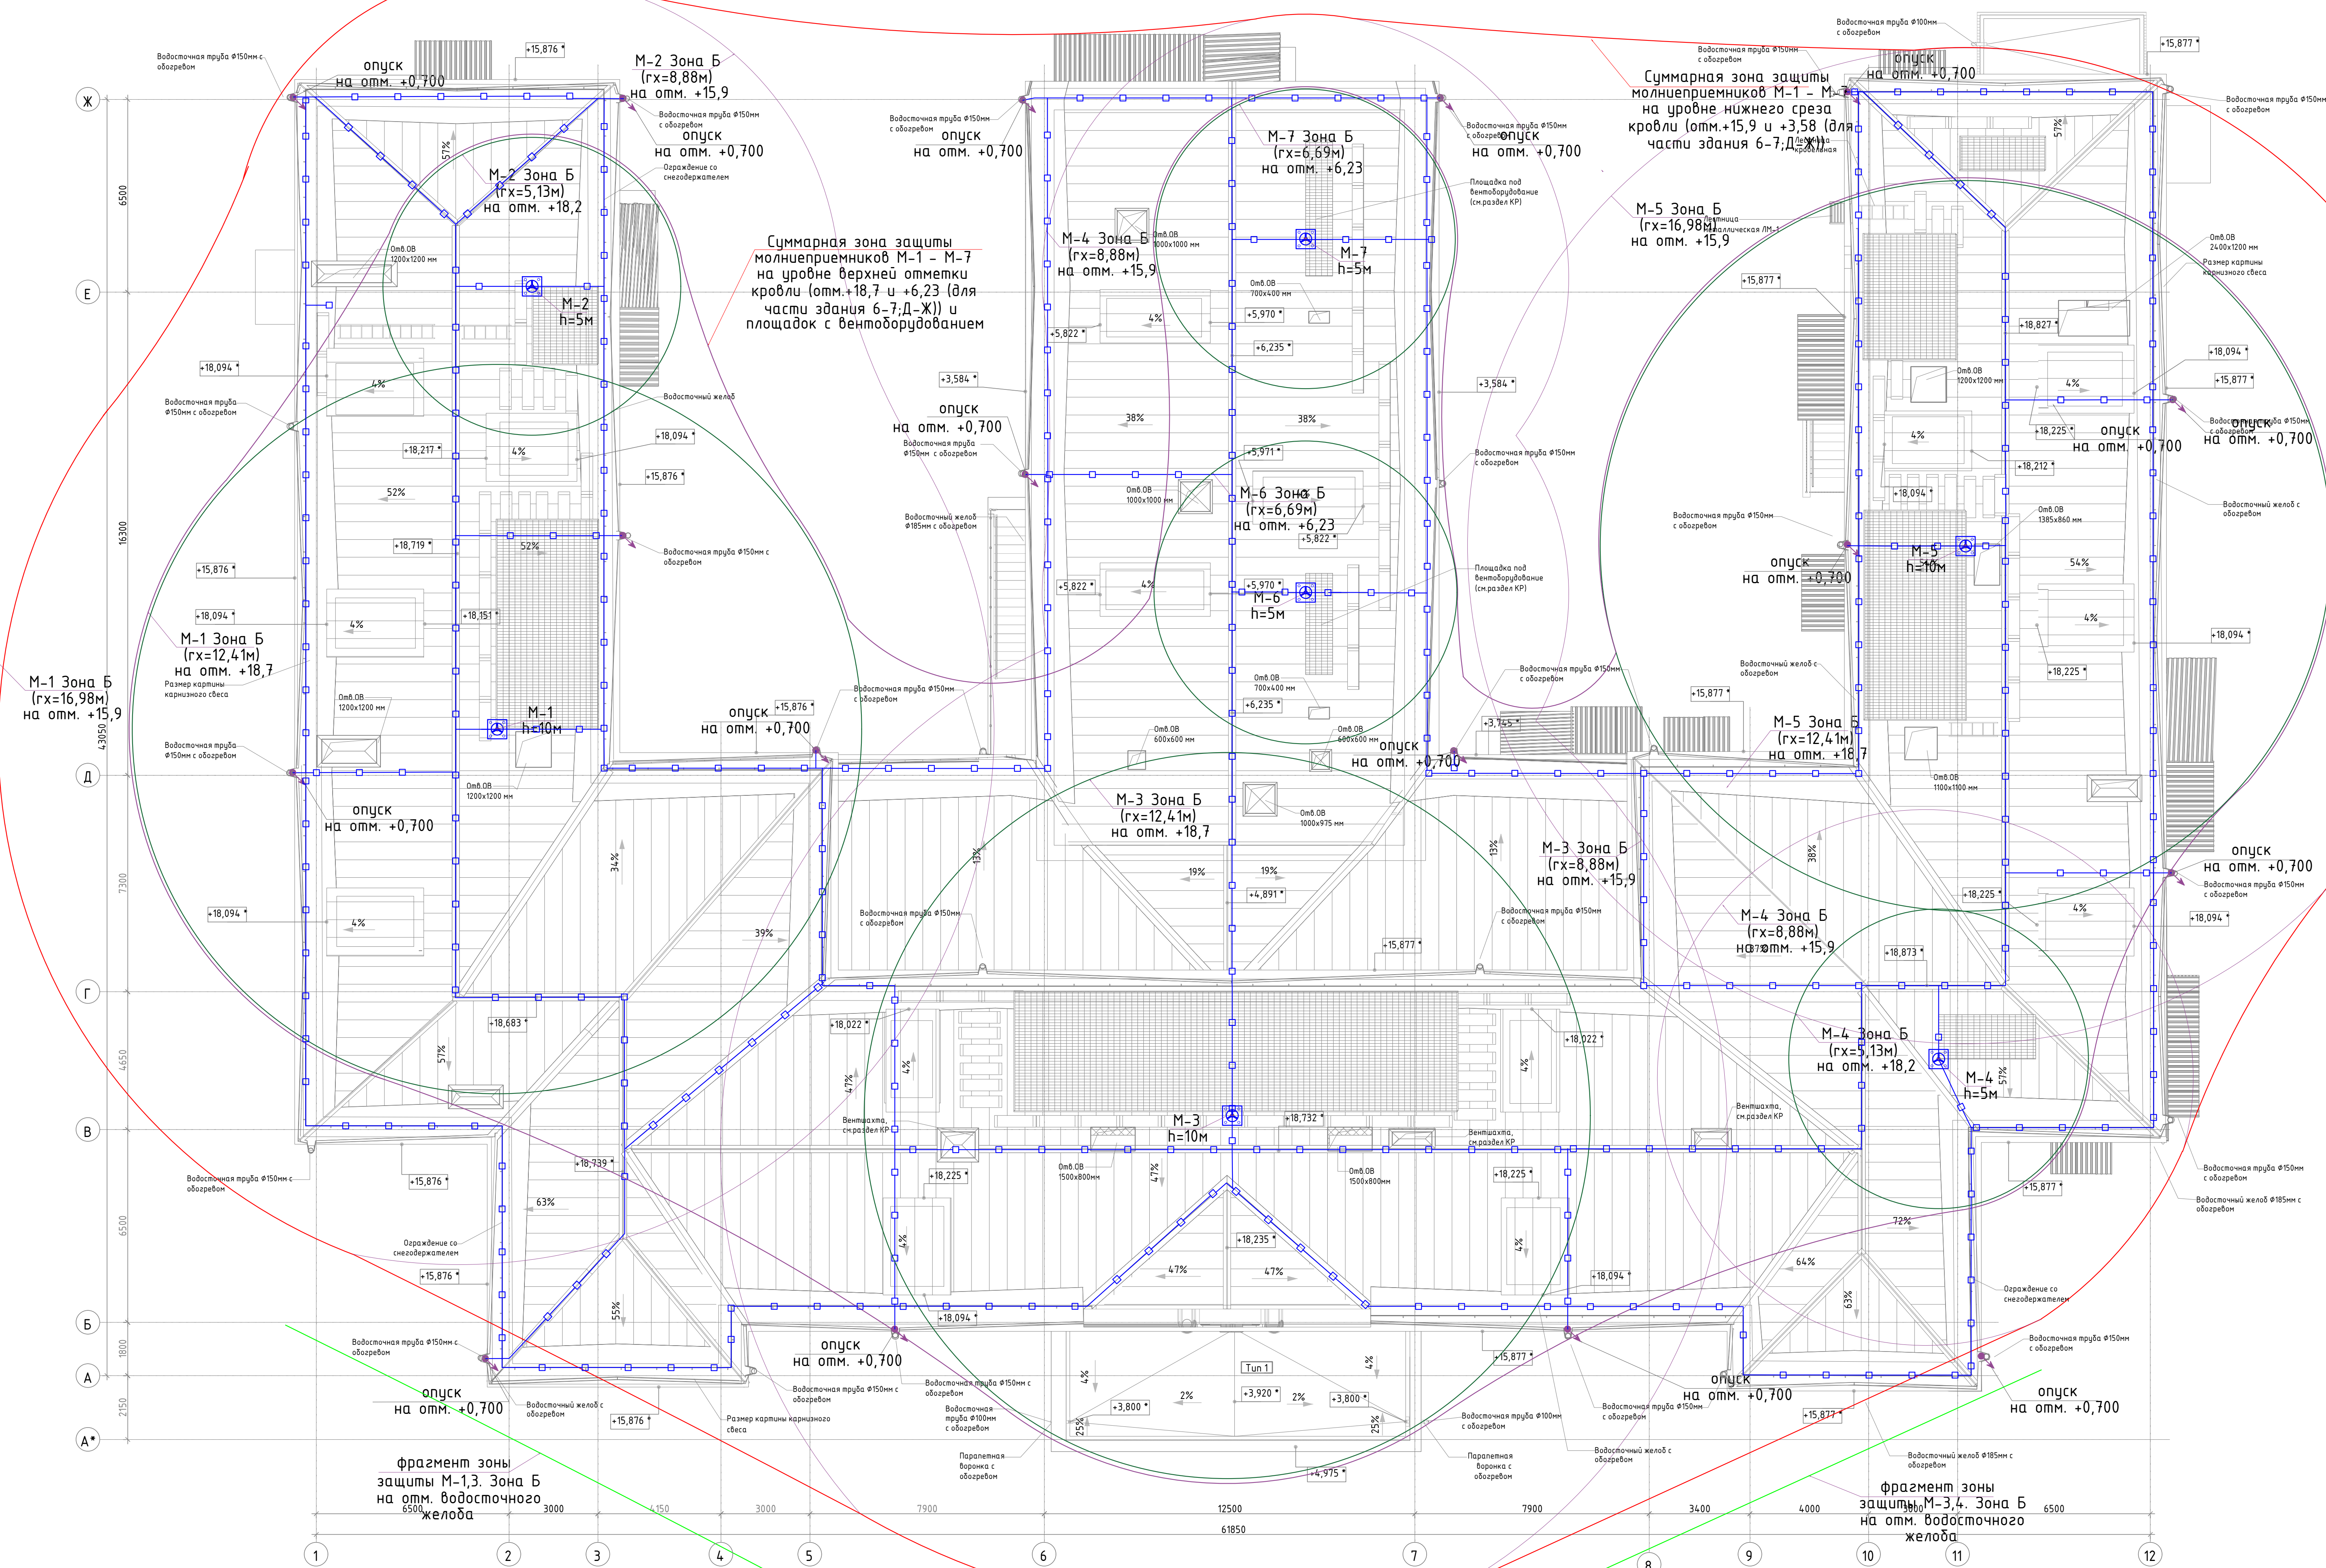

Мероприятия выполнены в соответствии с ПУЭ 7-е изд. Глава 1.7, СО 153-34.21.122-2003 «Инструкция по устройству молниезащиты зданий, сооружений и промышленных коммуникаций» (далее СО) и РД 34.21.122-87 «Инструкция по устройству молниезащиты зданий и сооружений» (далее РД).

Защита здания от разрядов молнии осуществляется с помощью стержневых молниеприемников:

- высотой 10 метров: М-1, М-3 и М-5 модель МС-14К-10000-0,3ГЦ;
- высотой 5 метров: М-2, М-4, М-6 и М-7 модель МС-12К-5000-0,3ГЦ.

Предварительный выбор количества и высот молниеприемников выполнена по методике пункта 1 приложения 3 РД для одиночных молниеприемников и сведен в таблицу 1. Конечные вычисления с учетом взаимного влияния зон защиты выполнены в соответствии с методикой пункта 2 и 3 приложения 3 РД. Результаты финальных расчетов нанесены на чертеж плана кровли в виде двух зон:

- суммарная зона защиты молниеприемников М-1 - М-7 на уровне верхней отметки кровли (отм.+18,7 и +6,23 (для части здания 6-7,Д-Ж)) и площадок с вентоборудованием;
- суммарная зона защиты молниеприемников М-1 - М-7 на уровне нижнего среза кровли (отм.+15,9 и +3,58 (для части здания 6-7,Д-Ж)).

Покрытие зон обеспечивает защиту от ПУМ как саму поверхность кровли, так и всех выступающих элементов.

Стержневые молниеприемники крепятся к вертикальным элементам конструкций площадок для вентилирования оборудования посредством комплексов крепежей К-1,2К (для молниеприемников 5 метров) и К-1,4К (для молниеприемников 10 метров).

Все стержневые молниеприемники соединить между собой стальной проволокой диаметром 8 мм (далее - магистраль).

От магистрали выполнить отпуски токоотводов стальной проволокой диаметром 8 мм по периметру кровли со средним шагом - 20 метров.


Все горизонтальные участки прокладки стальной проволоки производить посредством фальцевых зажимов ЗФ-8,2ГЦ (или аналог) к фальцу кровли с шагом 1 метр, без сверления поверхности кровли. Соединение стальной проволоки.

Крепление, соединение и отведение токоотводов к поверхности кровли производится с использованием фальцевых зажимов ЗФ-8,2ГЦ (или аналог) (см. узел 2).



Вертикальные участки токоотводов выполнять за трубами наружного водосточка посредством крепежей водосточных труб КВТ-8,2ГЦ (или аналог) с шагом установки 1 метр (см. узел №1) до отметки +0,700 метров.

Контур заземления - существующий. По результатам обследования контур удовлетворяет требованиям СО и РД.


В местах отпусков токоотводов выполнять монтаж стальных участков полос 40х4 с соединением, с одной стороны с контуром заземления посредством зажимов соединительных ЗС-2Н (или аналог) (см. узел 4), с другой стороны с токоотводом на фасаде (на отм.+0,700) посредством держателя проводника универсального ДПУ-4ГЦ (или аналог), см. узел №4.

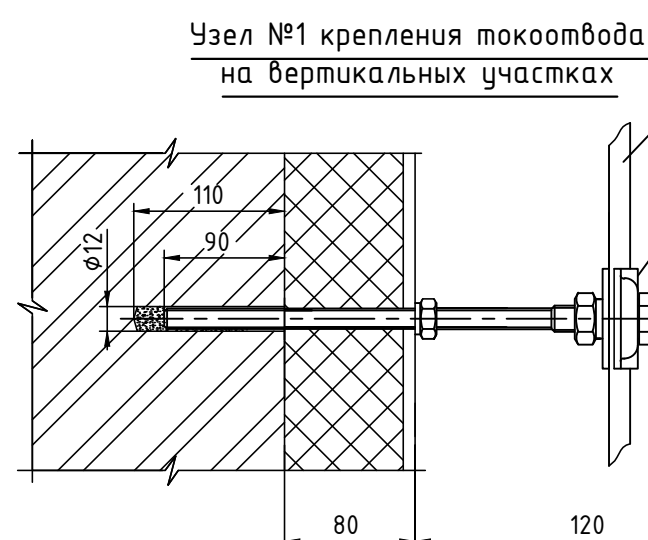

Узел №2 крепления токоотвода на вертикальных участках (кровля)

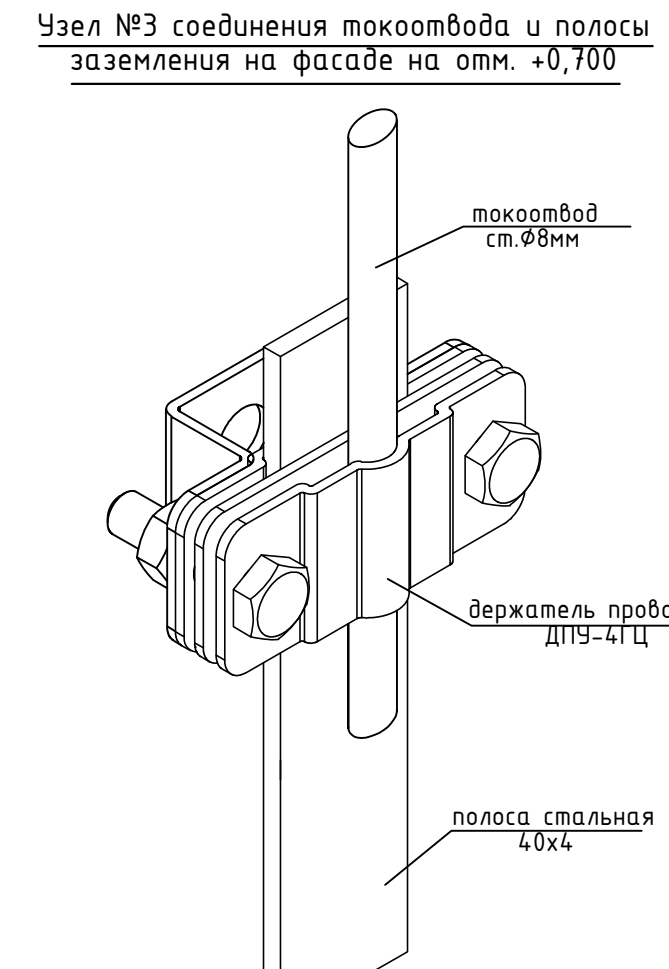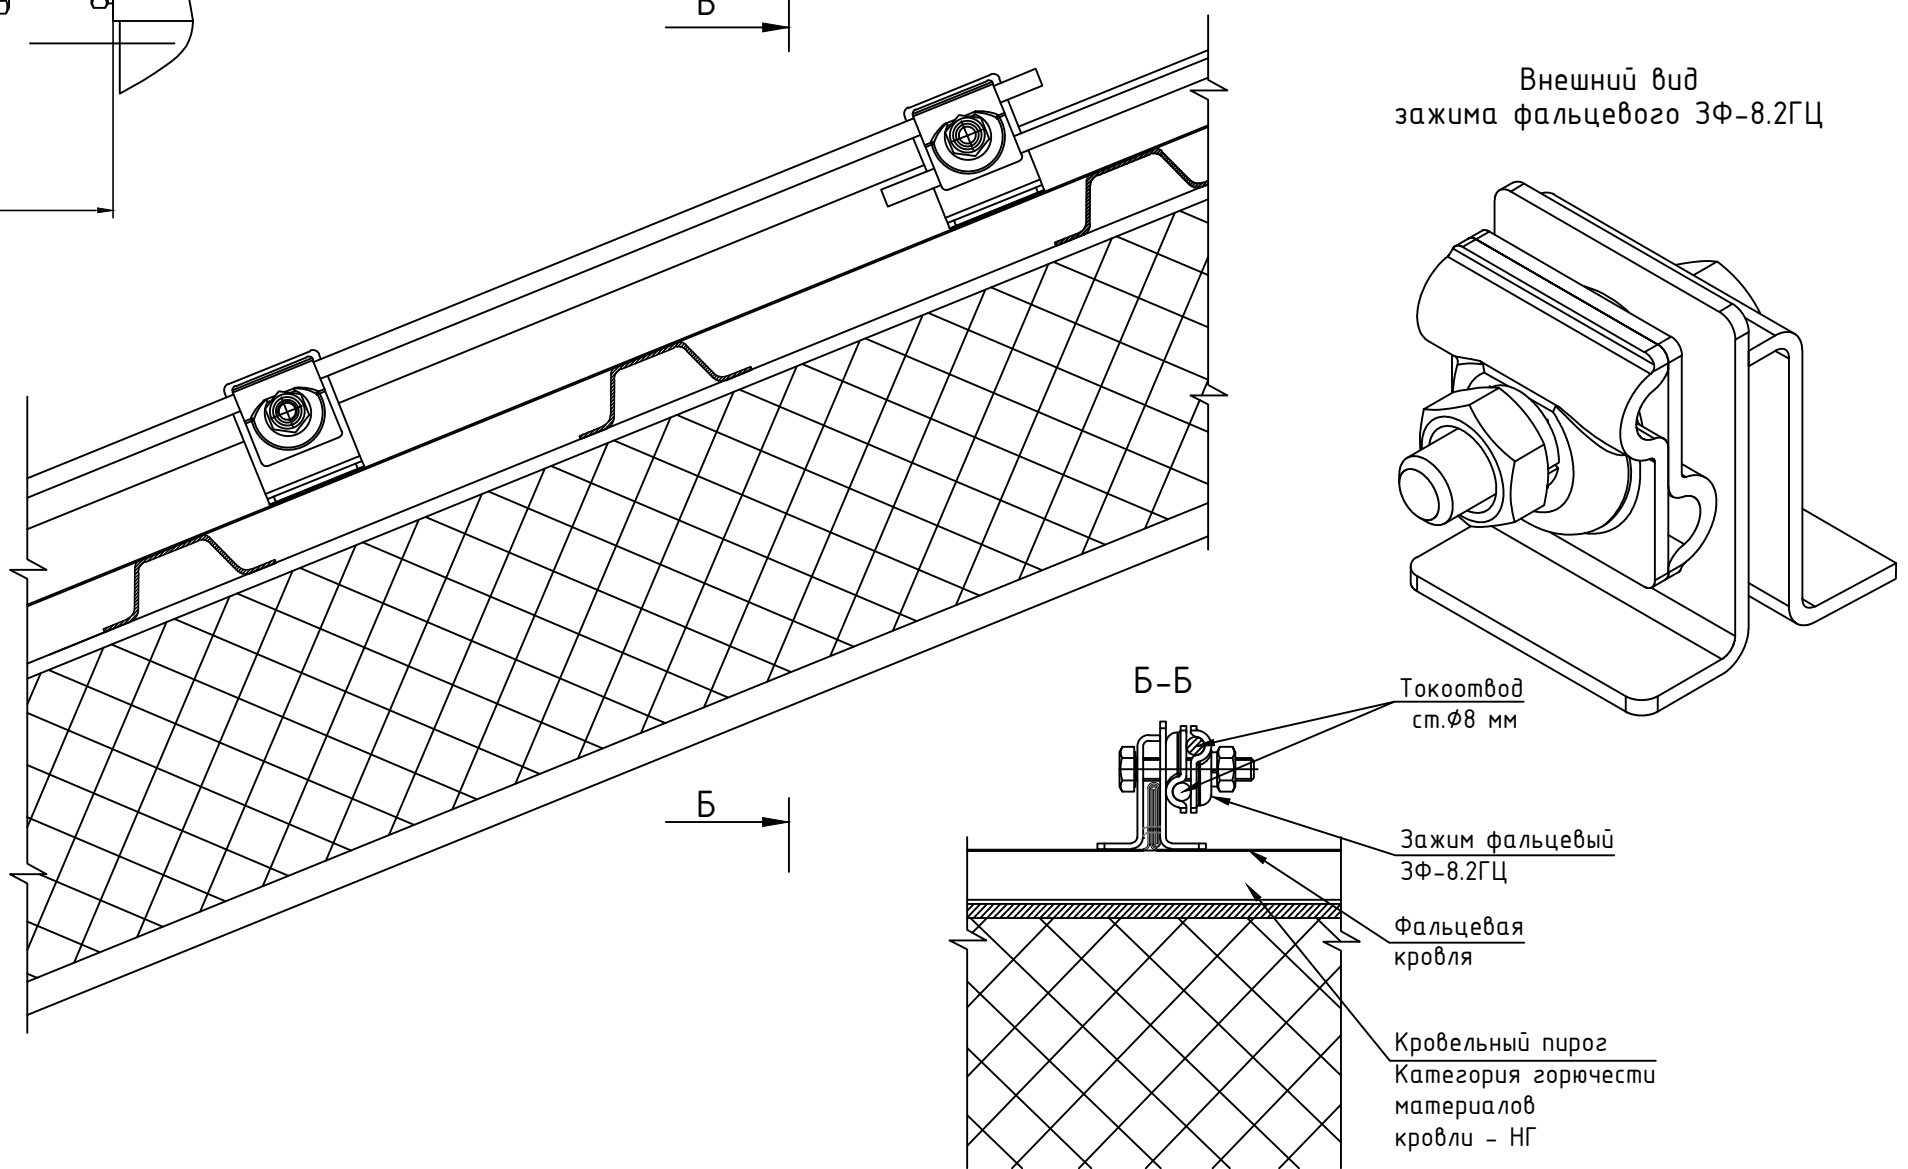

Узел №4 соединения токоотвода и полосы заземления в земле на отм.-0,700

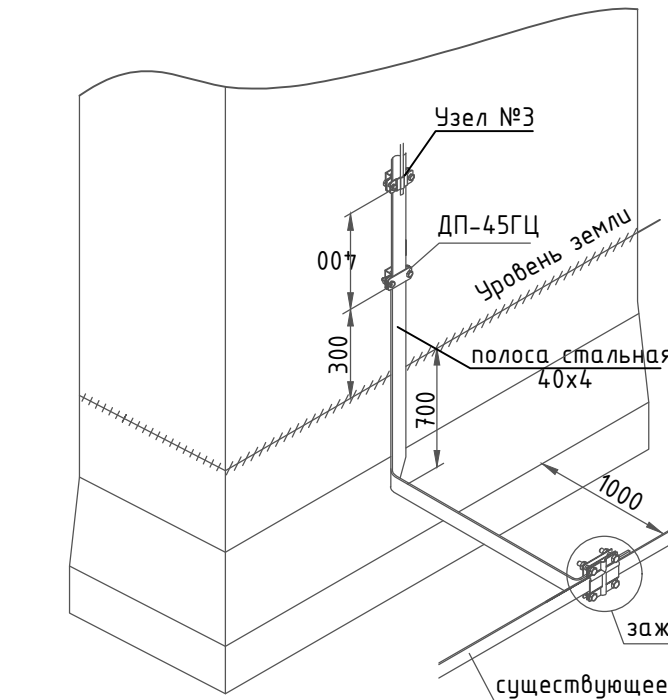

Условные обозначения

- - стержневой молниеприемник
- — — — — круглый стальной оцинкованный проводник (проволока) d=8 мм

696/П-25-АНО-Р-30М					
Здание по адресу: г. Москва, ул. Барбарина, д.1, корп.1					
Изм.	Кол. изм.	Лист	№ док.	Подп.	Дата
Разработ.	Никитин	07.26			
Генпр.	Гуляка	07.26			
Н. контр.	Гуляка	07.26			
Капитальный ремонт Государственного			Стадия		
учреждения города Москвы Школа №1282			Р		
Молниезащита			Листов		
			6		
			ООО ТИРОКТИ		
			Формат		

[illegible]

[illegible]