
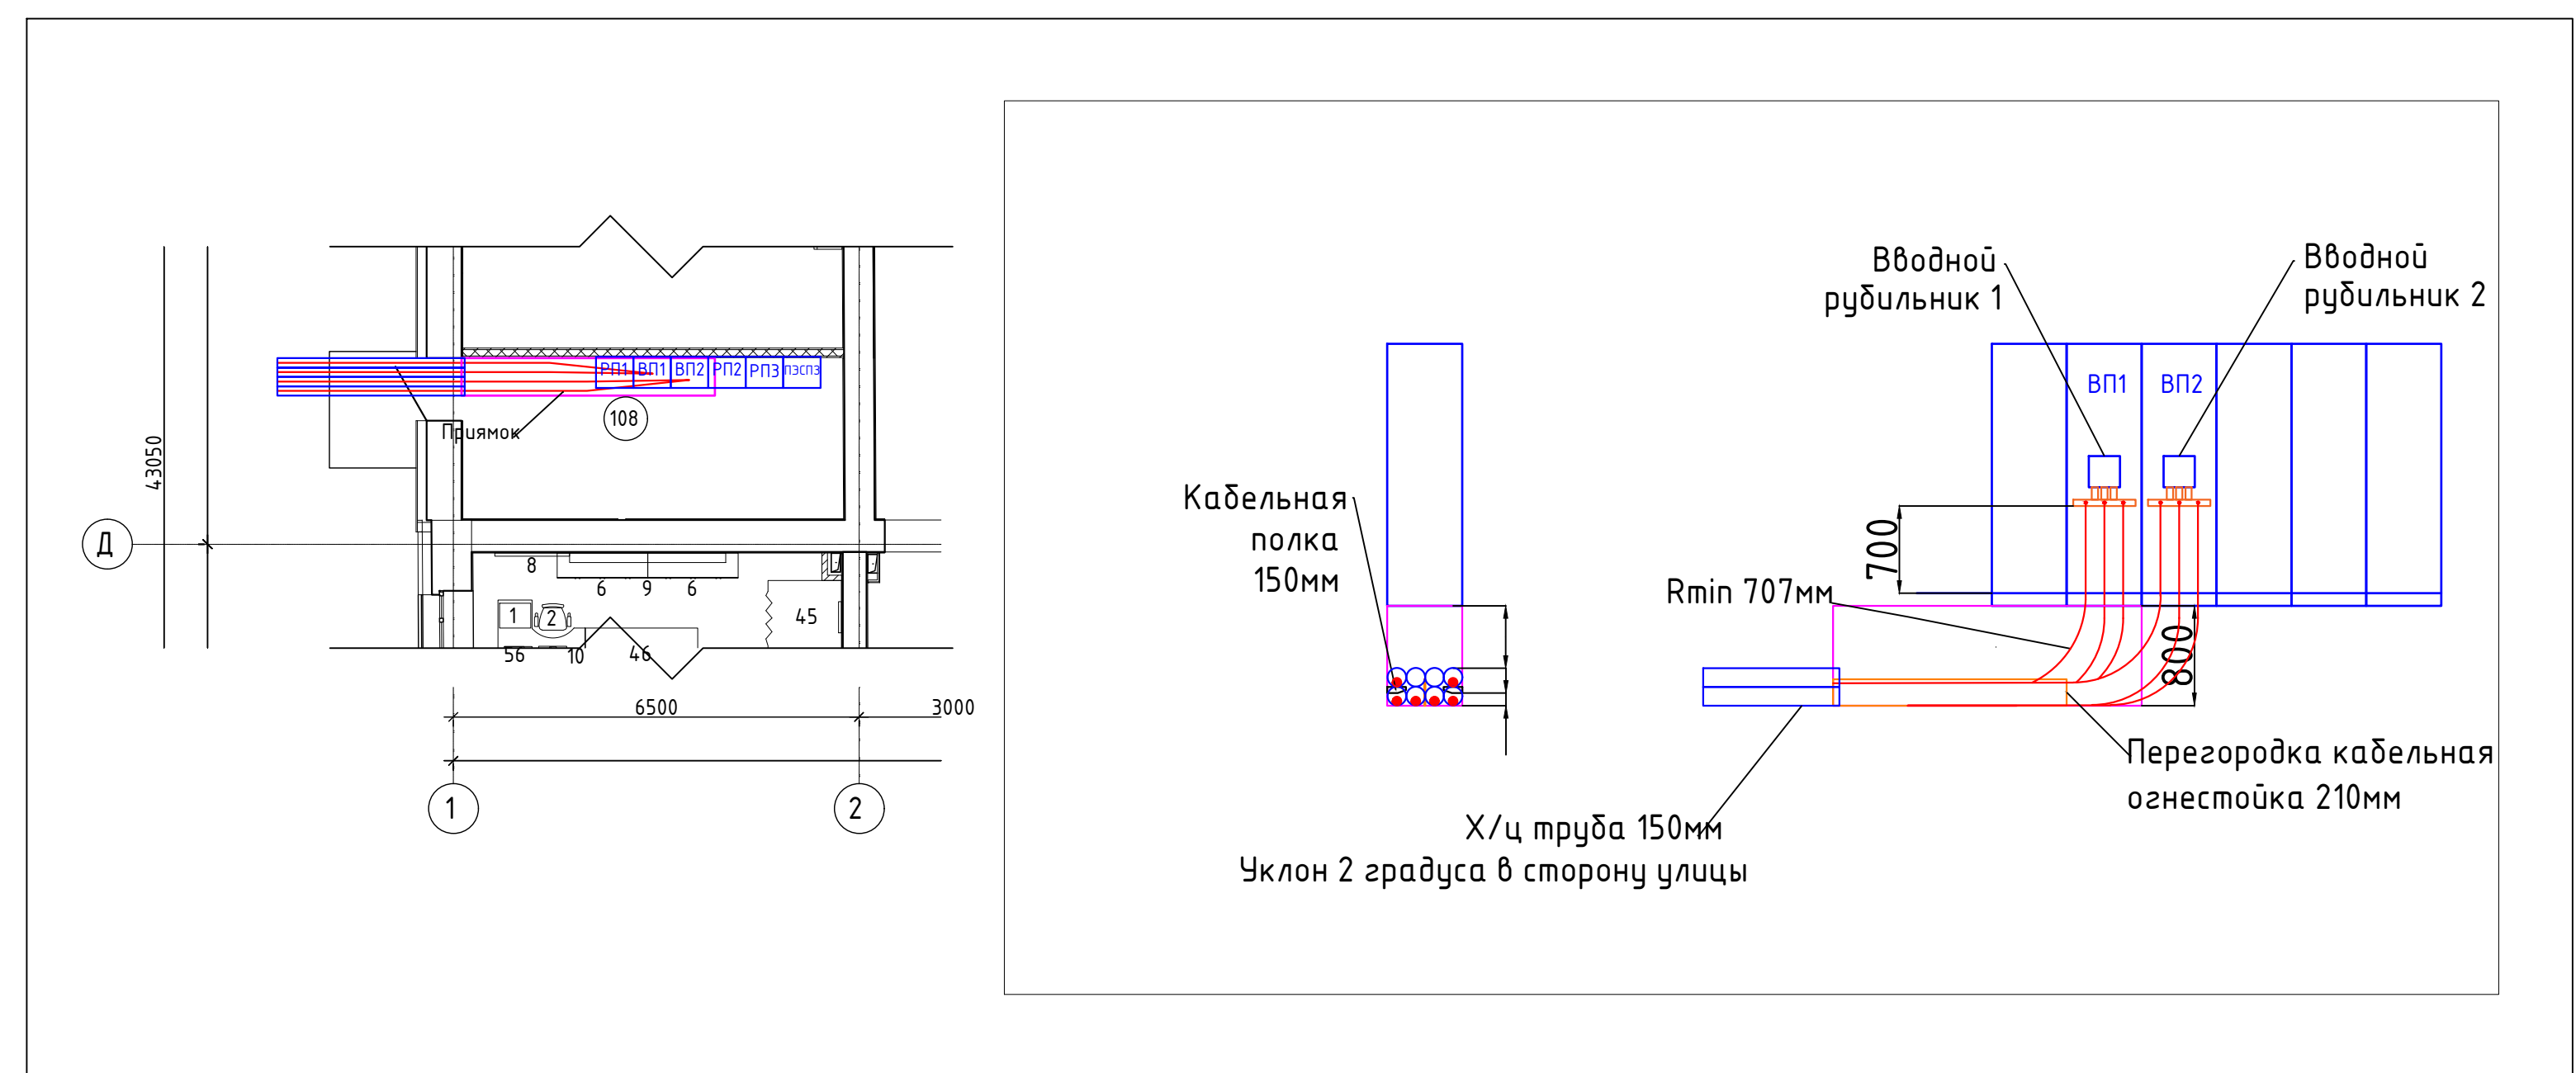
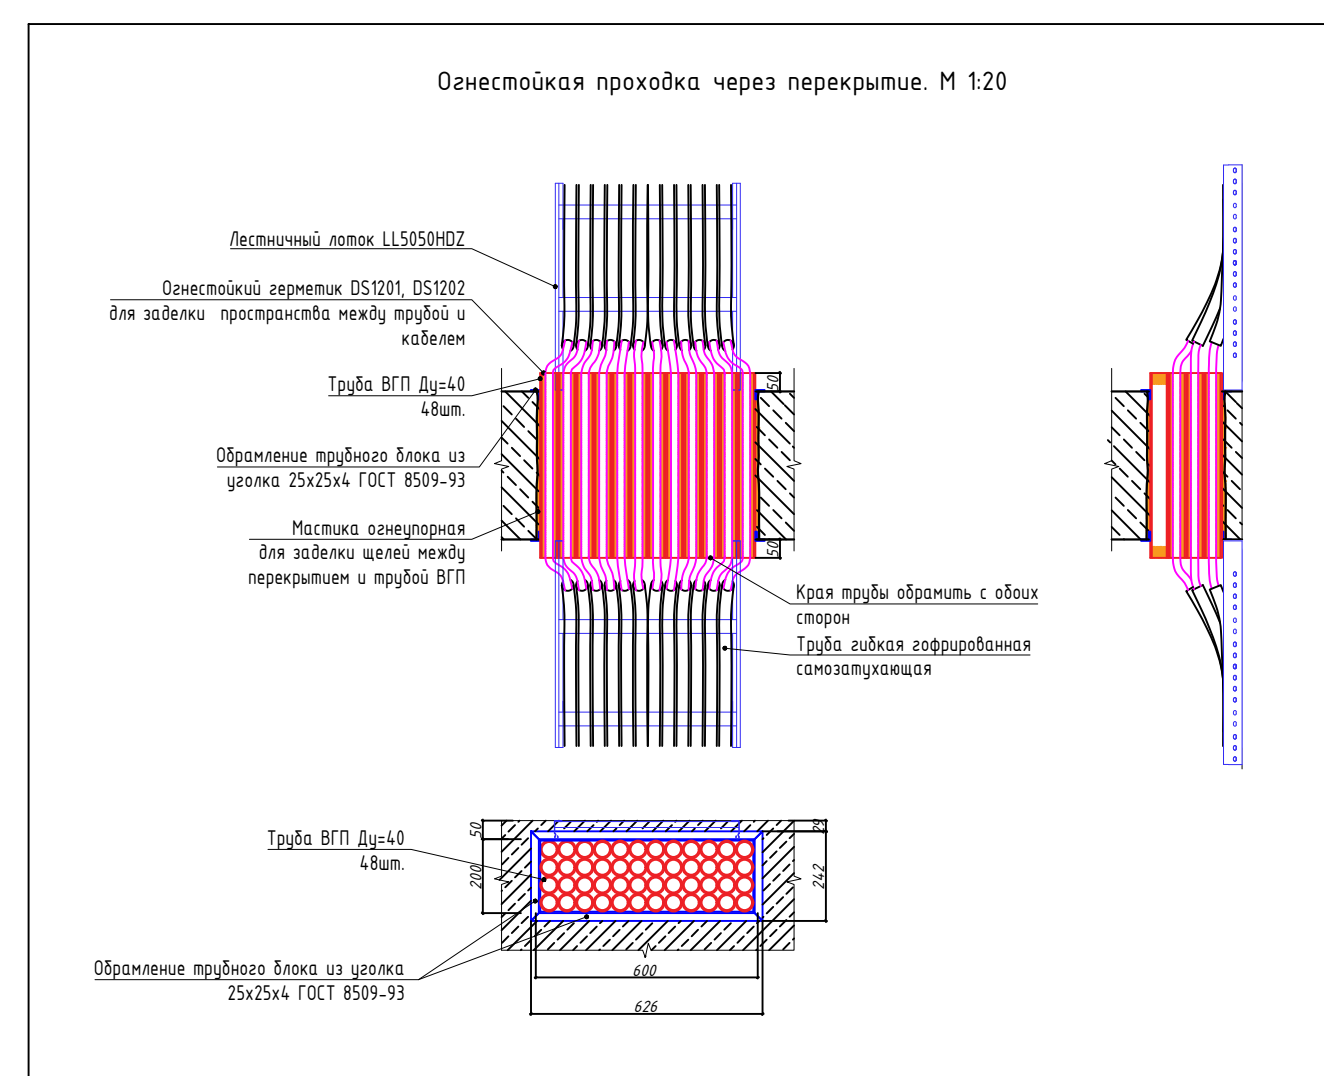


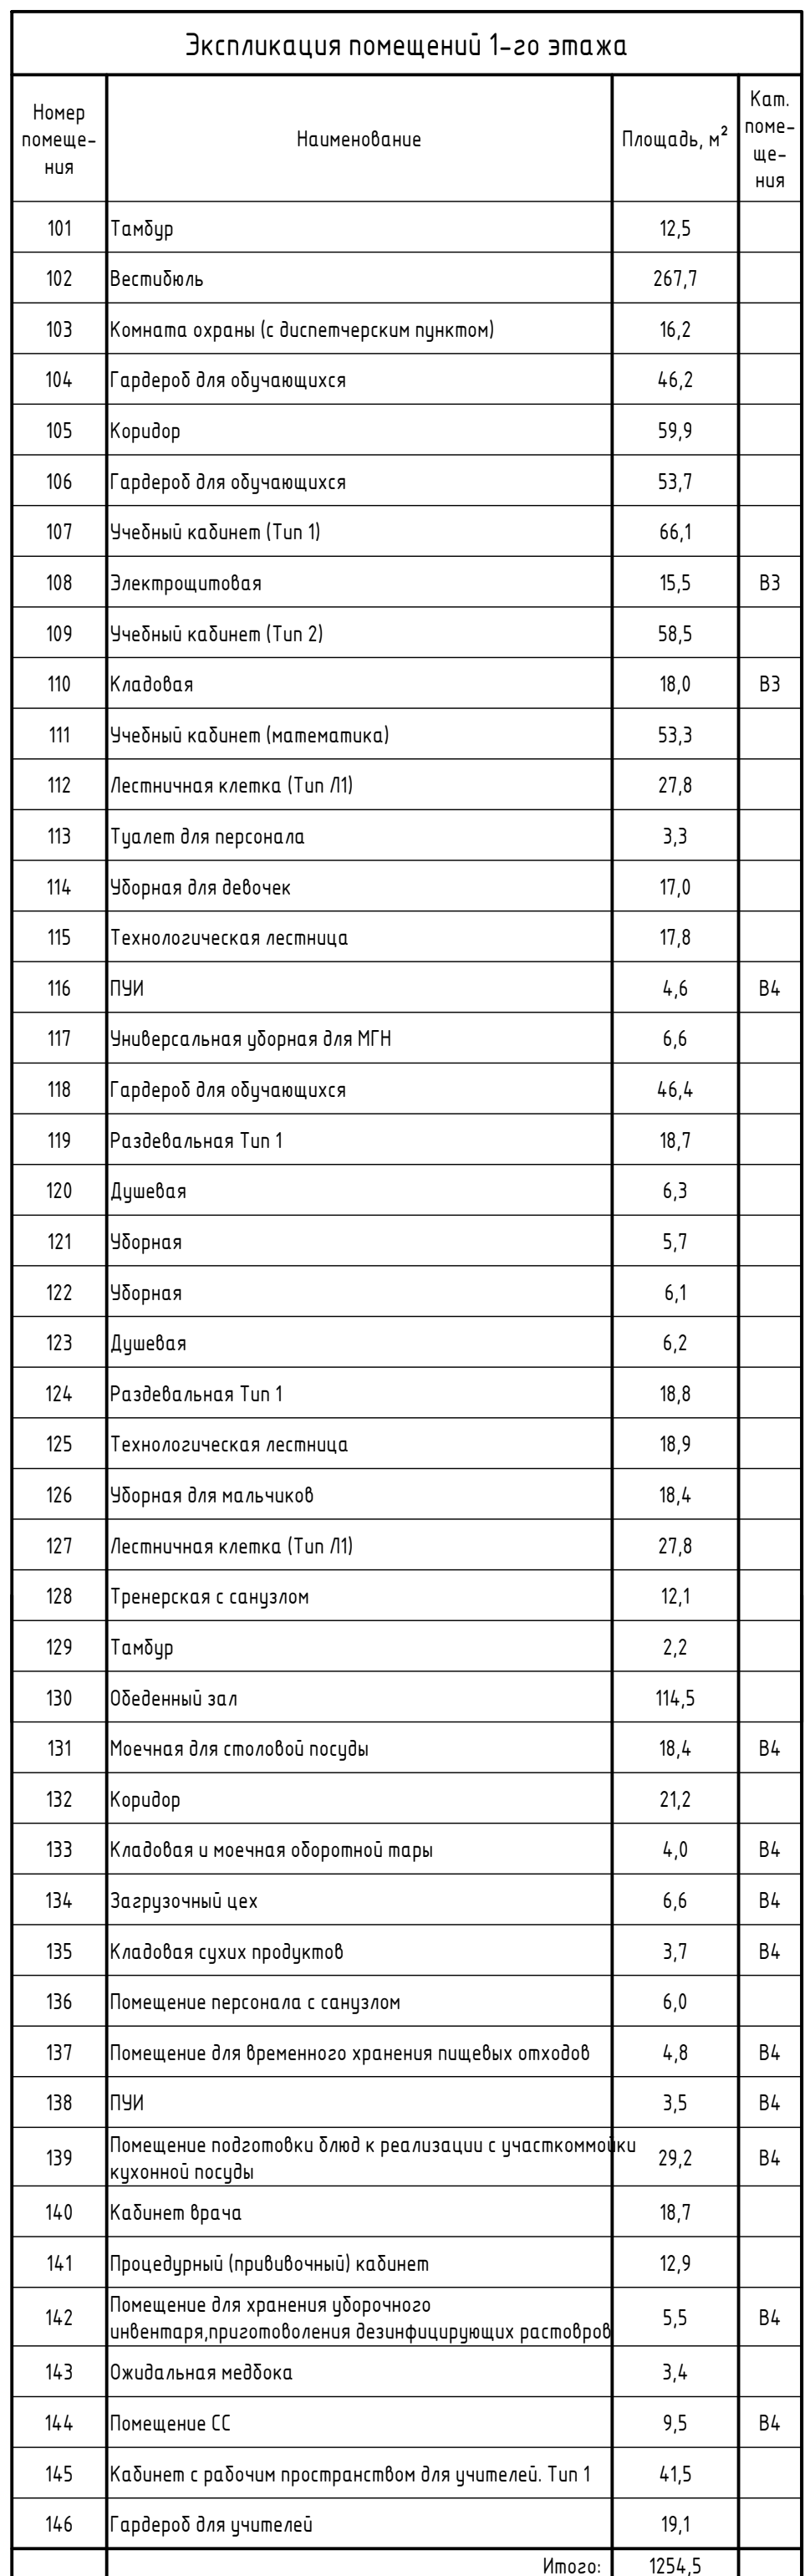

Примечания:

1. Электромонтажной организации РАЗРЕШАЕТСЯ прокладки кабельных трасс – корректировать самостоятельно по месту, исходя из структуры потолка и наличия инженерных систем;
2. Проект предусматривает 100% кабельные конструкции для систем внутреннего электроприсоединения;
3. Кабели на разрезах кабельных трасс показаны условно;
4. Расстояние между точками крепления кабельных трасс принять не более 800мм, при необходимости обеспечения такого расстояния возможно увеличение до 1000мм;
5. Крышки лотков на разрезах кабельных конструкций не показаны.

					696/П-25-АНО-Р-30М		
					Данные по адресу: г. Москва, ул. Барбарина, д/п, корп.1		
Изм.	Кол. экз.	Лист	№ док.	Подп.	Дата		
Разраб		Никитин		<i>[подпись]</i>	07.26	Капитальный ремонт Государственного бюджетного общеобразовательного учреждения города Москвы школы №1282	Страниц
ИИИ		Гулько		<i>[подпись]</i>	07.26		Лист
							Листов
						Р	4
И. н. комп.		Гулько		<i>[подпись]</i>	07.26	План кабельных конструкций сетей вытупного электрооборудования 1 этажа	
						 ООО "ПРОЕКТ"	