




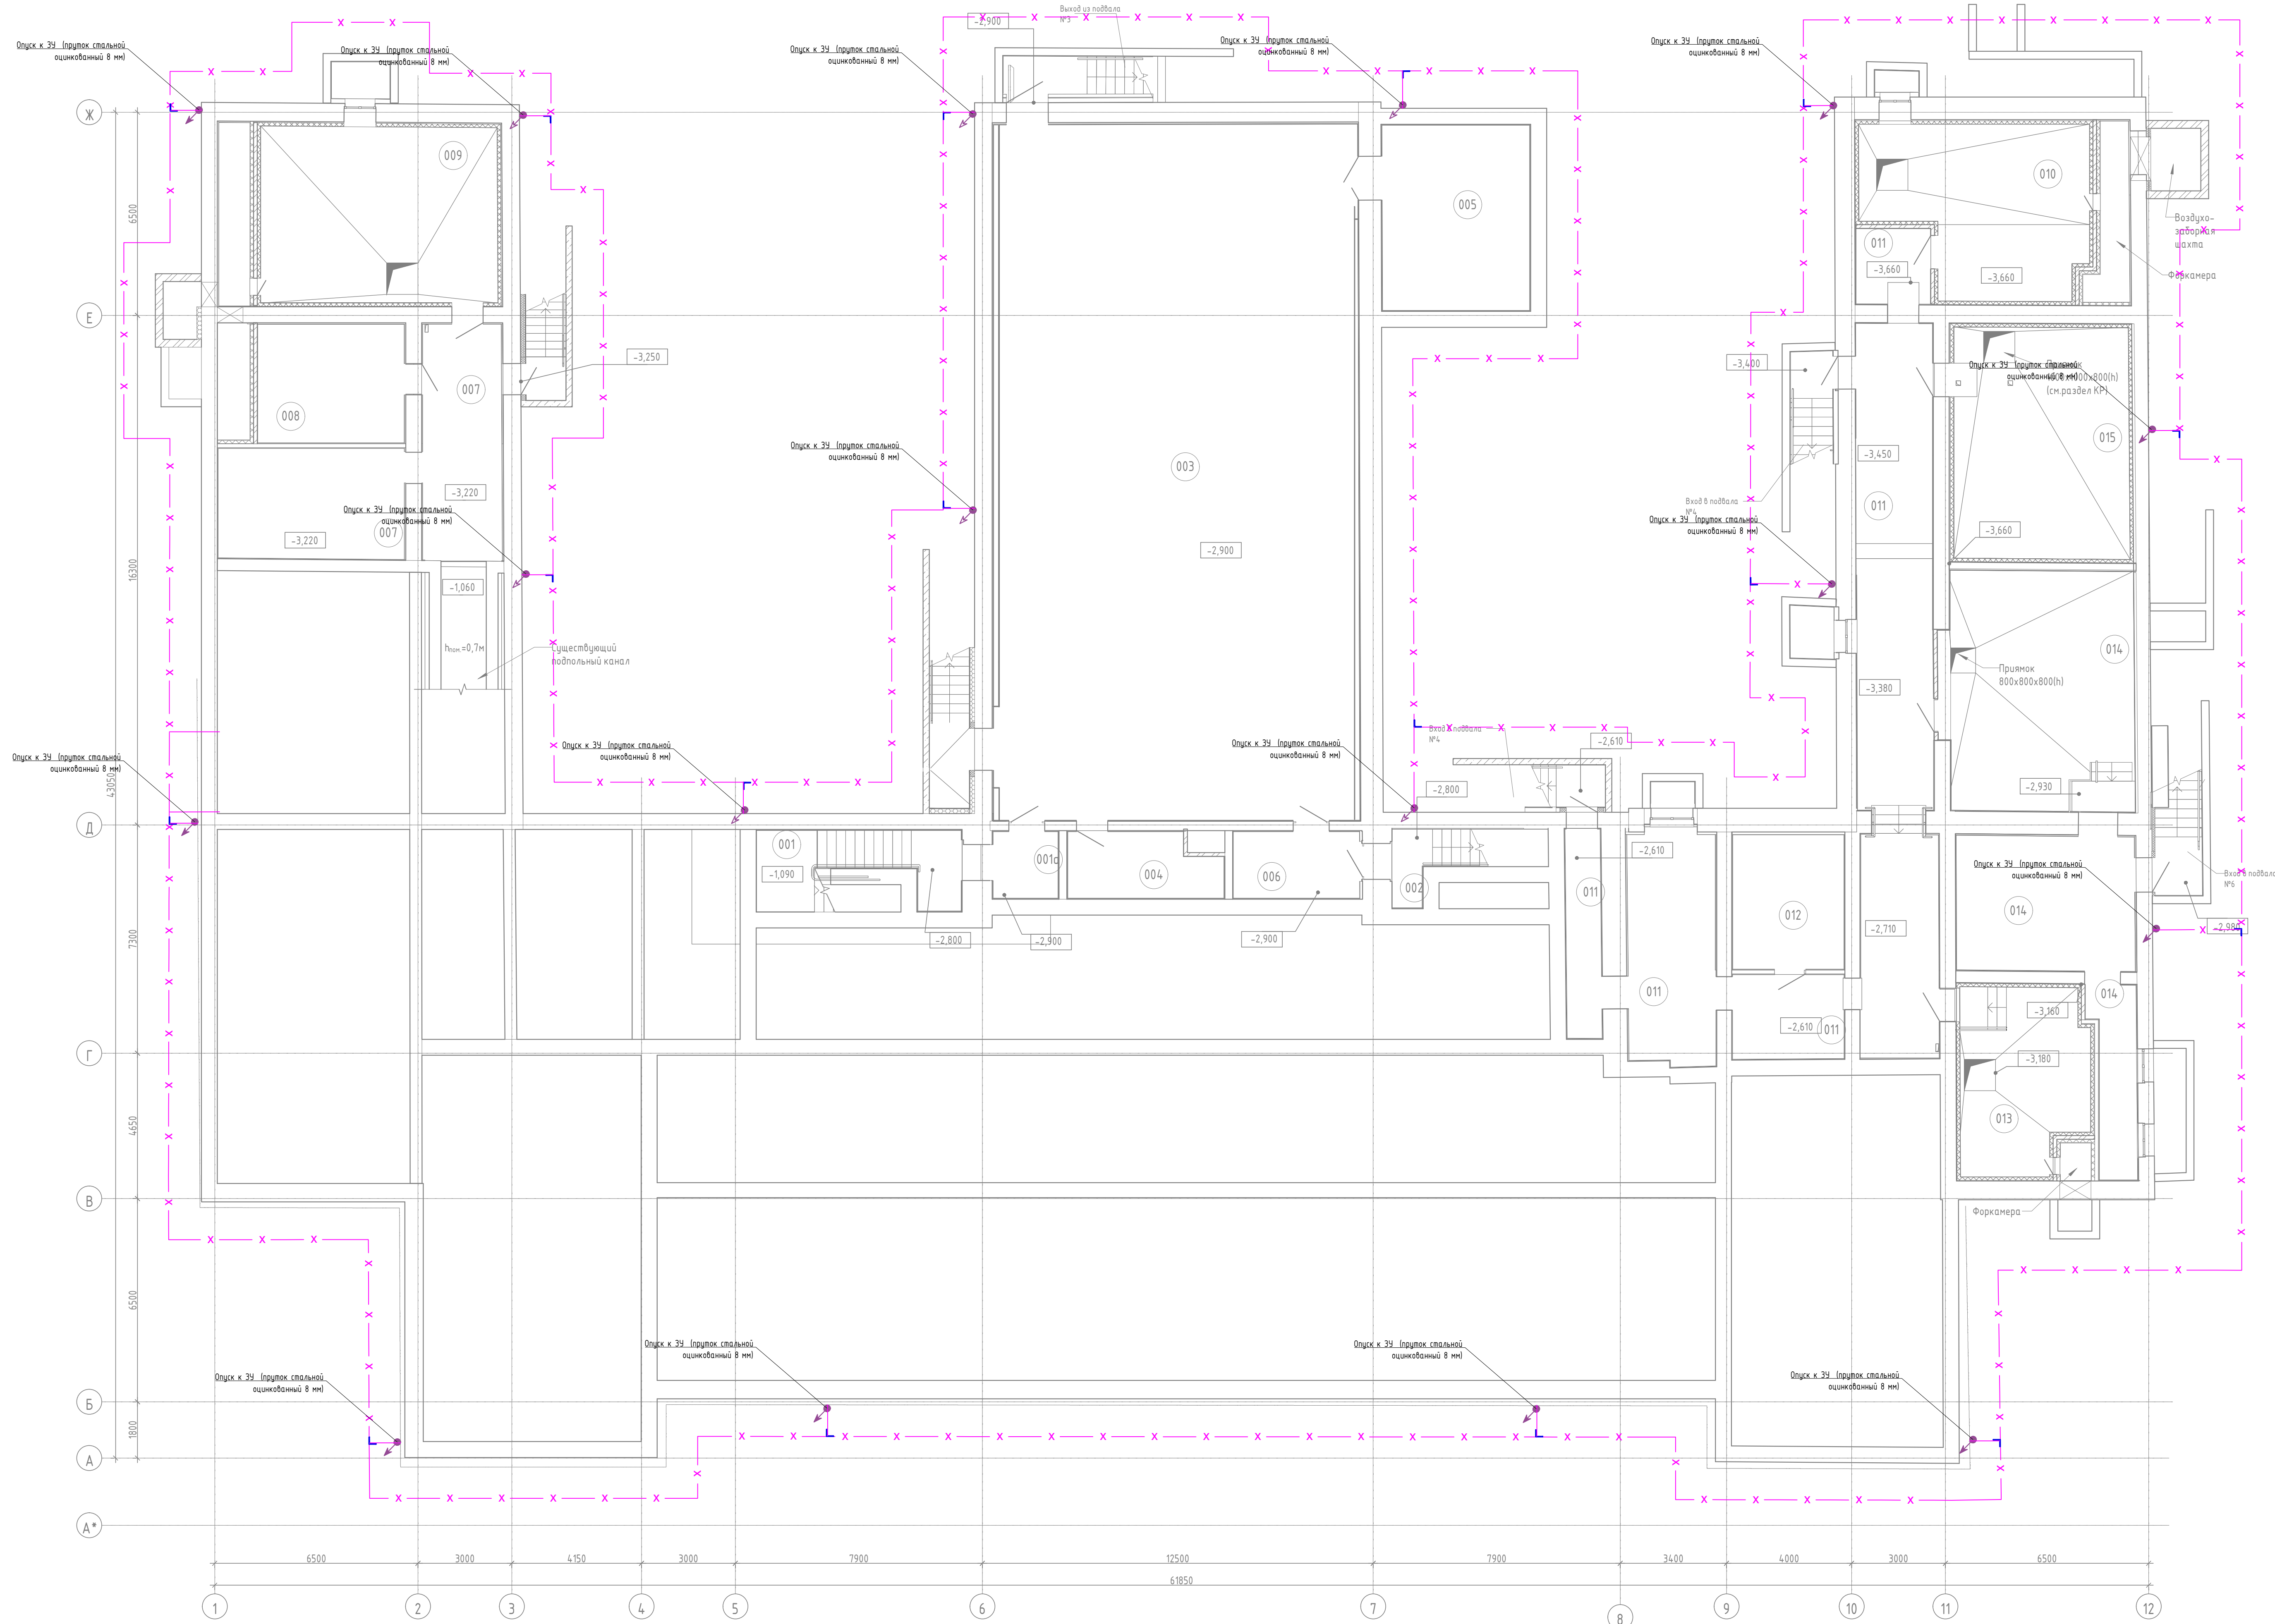

Узел соединения токопровода и полосы заземления на фасаде на отм. +0,700

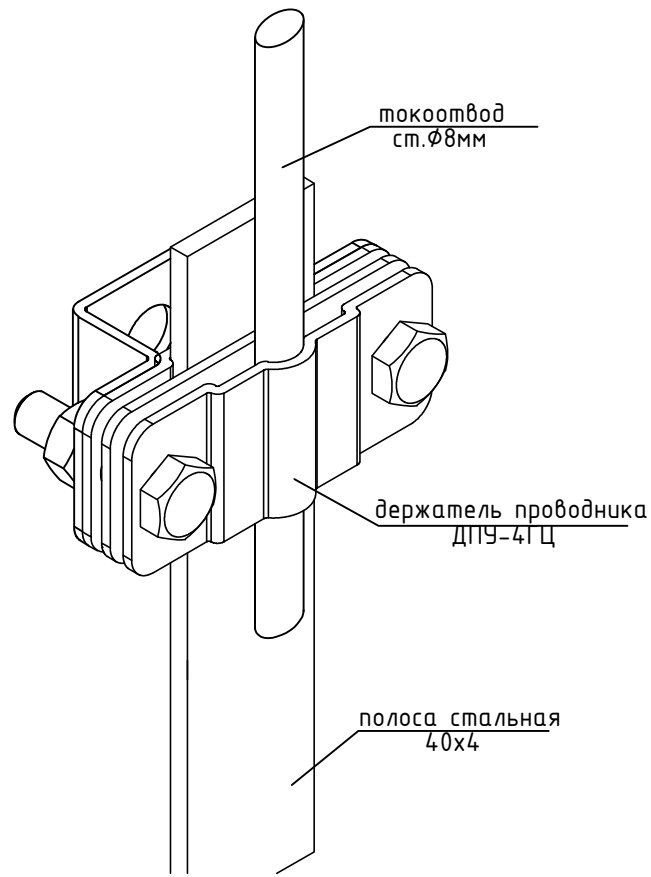

Узел соединения токопровода и полосы заземления в земле на отм. -0,700

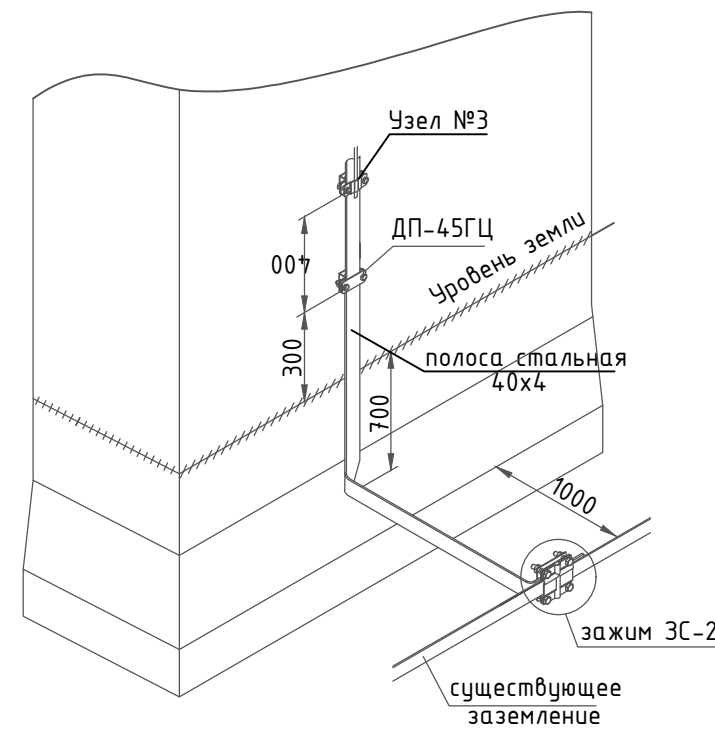


Условные обозначения

| N | Обозначение | Наименование                            |
|---|-------------|-----------------------------------------|
| 1 |             | Сталь полосовая горячеоцинкованная 40х4 |
| 2 |             | Вертикальный заземлитель                |

Примечание:  
Согласно п.4.5.2 ПЗ типового альбома А7-2010 и инструкции И1.03-08 по устройству защитного заземления расстояние от горизонтального заземлителя до параллельно проложенных трубопроводов должно составлять не менее 0,3м.

Траншея Т-3

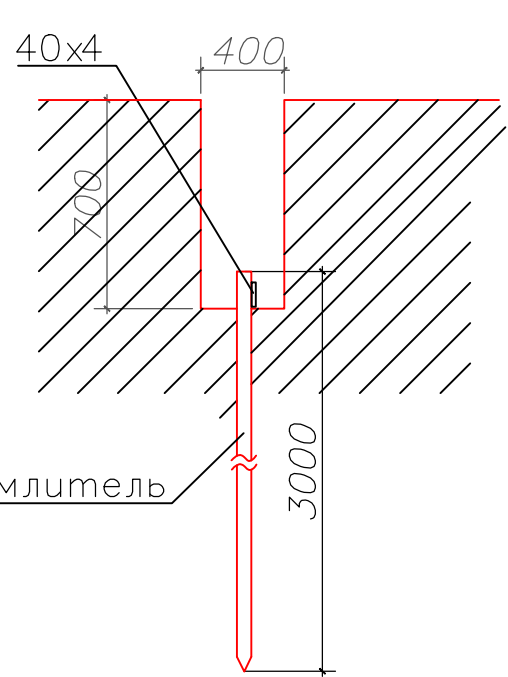

Вертикальный заземлитель

