

109548, г. Москва, Муниципальный Округ Печатники, ул. Шоссейная, д. 19, к. 1,
кв.117 e-mail PROEKTplus-work@yandex.ru

Свидетельство № СРО- П-110-009723217107-0532

СОГЛАСОВАНО:
Главный инженер
АО «МосводоканалСтройТрест»

_____ А.А. Вешкин

«__» _____ 2026г

**Капитальный ремонт Государственного Бюджетного
Общеобразовательного Учреждения города Москвы
«Школа № 1282 «Сокольники»
по адресу: г. Москва, ул. Барболина, д. 1, корп. 1
1 этап**

РАБОЧАЯ ДОКУМЕНТАЦИЯ

Основной комплект рабочих чертежей

Система водоснабжения и

канализации.

696/П-24-АНО-Р-ВК

Генеральный директор

Главный инженер проекта



Н.А. Выходова

А.Н. Гулько

2026

Име. № подл.	Подп. И дата	Взам. инв. №

Экспликация помещений подвала

Номер помеще-ния	Наименование	Площадь, м ²	Кат. поме-ще-ния
001	Техническая лестница	13,7	
001а	Тамбур-шлюз 1-го типа	4,9	
002	Техническая лестница	9,8	
002а	Тамбур-шлюз 1-го типа	5,0	
003	Спортивный зал	262,5	
004	Снарядная	10,1	B3
005	ПУИ	3,5	
006	Снарядная	28,0	B3
007	Коридор	21,0	
008	Коридор	17,9	
009	Кладовая	21,4	B3
010	Венткамера	Не окружено	B4
011	Форкамера	Не окружено	B4
012	Форкамера	3,8	B4
013	Венткамера	37,5	B4
014	Коридор	63,3	
015	Коридор	9,8	
016	Коридор	19,3	
017	Коридор	8,3	
018	Насосная	14,8	B4
019	Венткамера	19,3	B4
020	Форкамера	5,2	B4
021	ИТП	75,6	Д
022	Венткамера	4,1	B4
ИТОГО:		695,8	


Условные обозначения

- В1

Проектируемый хозяйственно-питьевой водопровод
- Т3

Поданный трубопровод горячего водоснабжения
- Т4

Циркуляционный трубопровод горячего водоснабжения

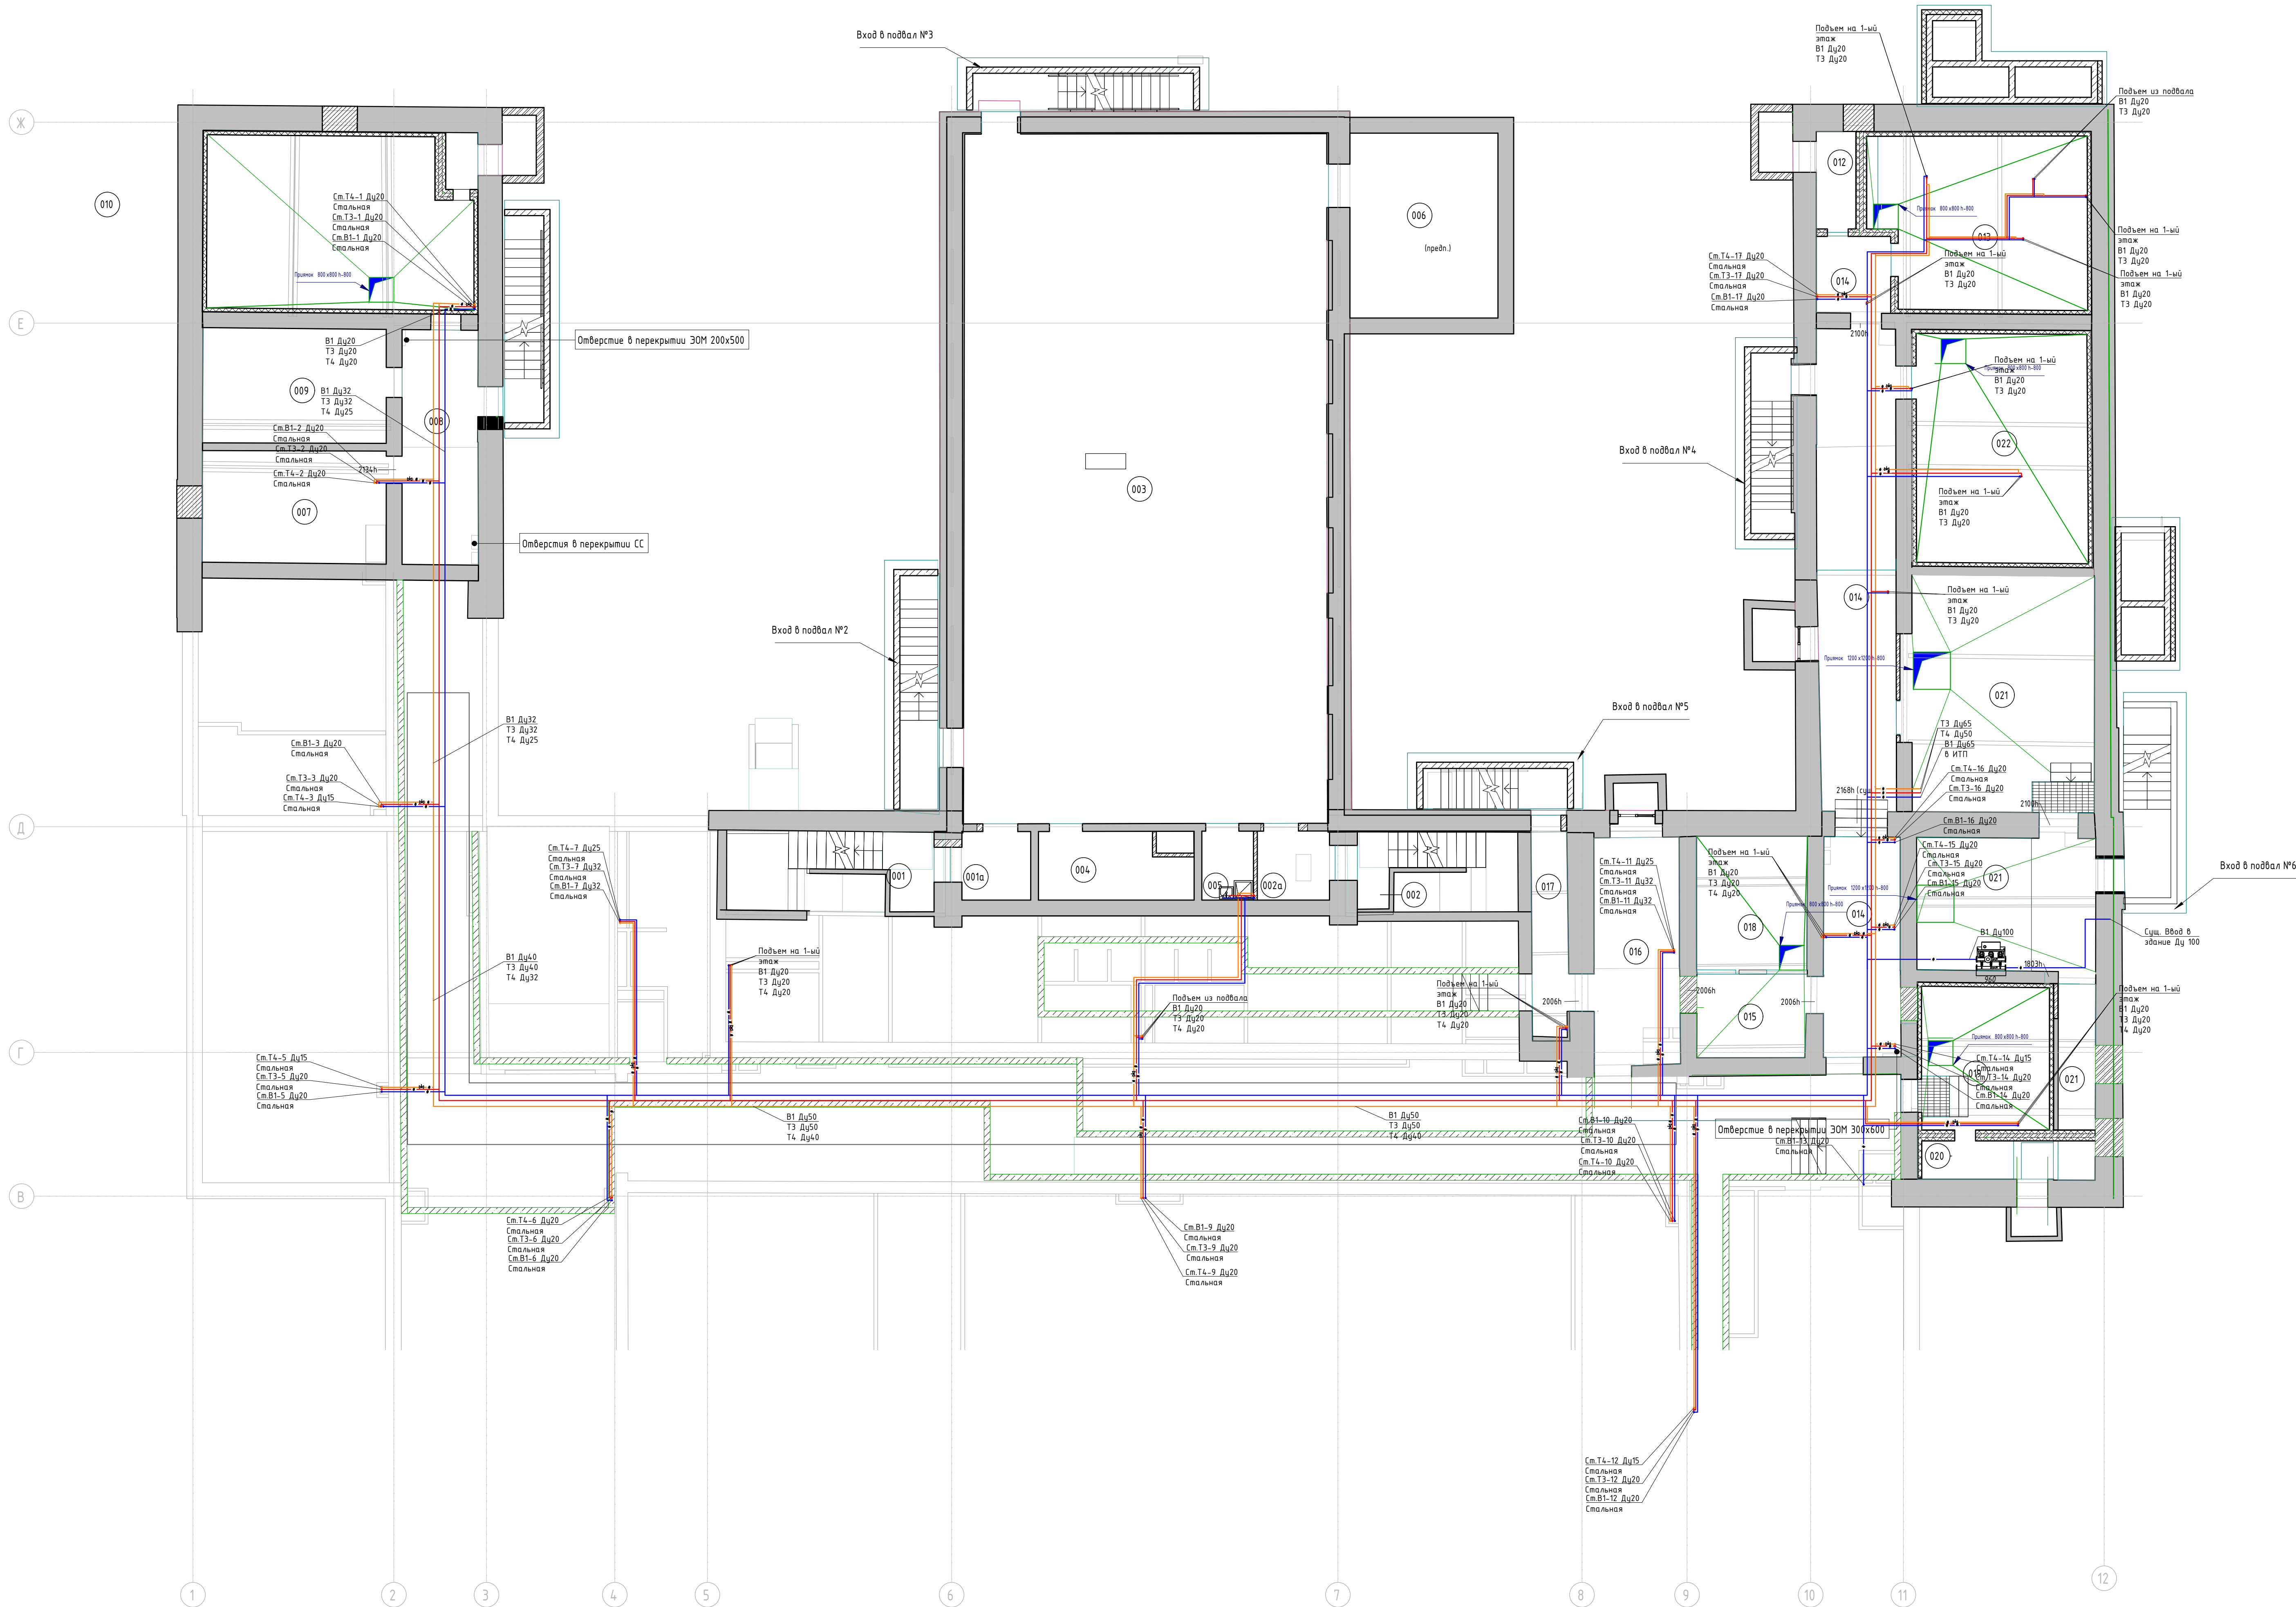

Экспликация помещений 1-го этажа

Номер помеще-ния	Наименование	Площадь, м²	Кат. поме-ще-ния
101	Тамбур	17,0	
102	Вестибиль	66,7	
103	Комната охраны (с диспетчерским пунктом)	16,0	
104	Гардероб для обучающихся	47,2	
105	Коридор	62,9	
106	Гардероб для обучающихся	54,2	
107	Учебный кабинет (Тип 1)	67,4	
108	Электрощитовая	15,5	ВЗ
109	Учебный кабинет (Тип 2)	57,3	
110	Кладовая	18,0	ВЗ
111	Учебный кабинет (математика)	52,3	
112	Лестничная клетка (Тип Л1)	27,6	
113	Туалет для персонала	2,8	
114	Уборная для девочек	15,9	
115	Техническая лестница	18,0	
116	ПУИ	4,0	В4
117	Универсальная уборная для МГН	6,5	
118	Коридор	194,5	
119	Раздевальная Тип 1	19,0	
120	Душевая	6,5	
121	Уборная	5,3	
122	Уборная	5,3	
123	Душевая	6,5	
124	Раздевальная Тип 1	18,4	
125	Техническая лестница	18,8	
126	Уборная для мальчиков	18,0	
127	Лестничная клетка (Тип Л1)	27,6	
128	Тренировочная с санузлом	8,7	
129	Умывальная	10,1	
130	Обеденный зал	108,3	
131	Моечная для столовой посуды	17,3	В4
132	Коридор	13,1	
133	Кладовая и моечная оборотной тары	4,0	В4
134	Загрузочный цех	6,2	В4
135	Кладовая сухих продуктов	3,7	В4
136	Помещение персонала с санузлом	4,2	
137	Пом. для временного хранения пищевых отходов	4,4	В4
138	ПУИ	3,6	В4
139	Пом. подготовки блюд к реализации с участком мойки кухонной посуды	30,5	В4
140	Кабинет врача	18,9	
141	Процедурный (прибывочный) кабинет	13,2	
142	Пом. для хранения уборочного инвентаря, приготовления дезинфицирующих растворов	5,9	В4
143	Ожидающая медблока	3,5	
144	Помещение СС	9,4	В4
145	Кабинет с рабочим пространством для учителей (Тип 1)	42,0	
146	Гардероб для учителей	19,4	
147	Гардероб для обучающихся	49,0	
148	Тамбур	2,0	
149	Венткамера	9,1	?
150	Венткамера	15,5	
ИТОГО:		1271,4	

Условные обозначения

- В1

Т3

Т4
- Проектируемый хозяйственно-питьевой водопровод

Подающий трубопровод горячего водоснабжения

Циркуляционный трубопровод горячего водоснабжения

				696/П-25-АНО-Р-ВК			
				Капитальный ремонт Государственного бюджетного общеобразовательного Учреждения города Москвы "Школа №1282 "Солнечный" по адресу: г. Москва, ул. Бардымова, д. 1, корп. 1			
Изм.	Кол.	Лист	М.В.И.	Подпись	Дата	Стенд	Лист
Разработал	Д.А.С.				06.26	Р	3
Ген.пр.	Г.И.С.				06.26		
Исполнил	Н.А.С.				06.26		
И.О.И.	Н.А.С.				06.26		
				Капитальный ремонт. Система водоснабжения			
				План 1-го этажа водоснабжения			
				Копировал			
				Формат А0			

Экспликация помещений 2-го этажа			
Номер помеще-ния	Наименование	Площадь, м²	Кот. помеще-ния
201	Коридор с рекреацией	191,5	
202	Коридор с рекреацией	197,2	
203	Помещение СС	5,1	В4
204	Лестничная клетка I тип ЛП	27,4	
205	Лестничная клетка I тип ЛП	27,6	
206	Помещение СС	6,7	В4
207	Подсобное помещение	5,3	В4
208	Подсобное помещение	4,3	В4
209	Туалет для персонала	3,1	
210	Или	2,2	В4
211	Забора для девочек	19,1	
212	Забора для мальчиков	18,8	
213	Кабинет для индивидуальных занятий, в т.ч. с учителем-логопедом	18,1	
214	Административный кабинет. Тип 1	16,9	
215	Учебный кабинет	52,7	
216	Учебный кабинет	45,6	
217	Учебный кабинет	46,2	
218	Учебный кабинет	46,4	
219	Учебный кабинет	49,3	
220	Учебный кабинет	48,9	
221	Учебный кабинет	49,6	
222	Учебный кабинет	49,3	
223	Учебный кабинет	47,9	
224	Гимнастический зал	72,6	
225	Раздевальня Тип 1	9,5	
226	Раздевальня Тип 1	8,9	
227	Учебный кабинет	51,7	

Условные обозначения


- В1

Проектируемый хозяйственно-питьевой водопровод
- Т3

Подающий трубопровод горячего водоснабжения
- Т4

Циркуляционный трубопровод горячего водоснабжения

					696/П-25-АНО-Р-ВК				
					Капитальный ремонт Государственного бюджетного общеобразовательного учреждения города Москвы "Школа №1282 "Солнышко" по адресу: г. Москва, ул. Бардымова, д. 1, корп. 1				
Испол.	Волгарь	Датум	10.06.2025	Подпись	Д.С.С.				
Разработал	Волгарь	Дата	06.25						
Тип	Генеральный	Генеральный	06.25						
					Капитальный ремонт Система водоотведения				
					План 2-го этажа водоснабжение				
Испол.	Волгарь	Датум	06.25	Подпись	Д.С.С.				
					Копирован				
					Формат А0				

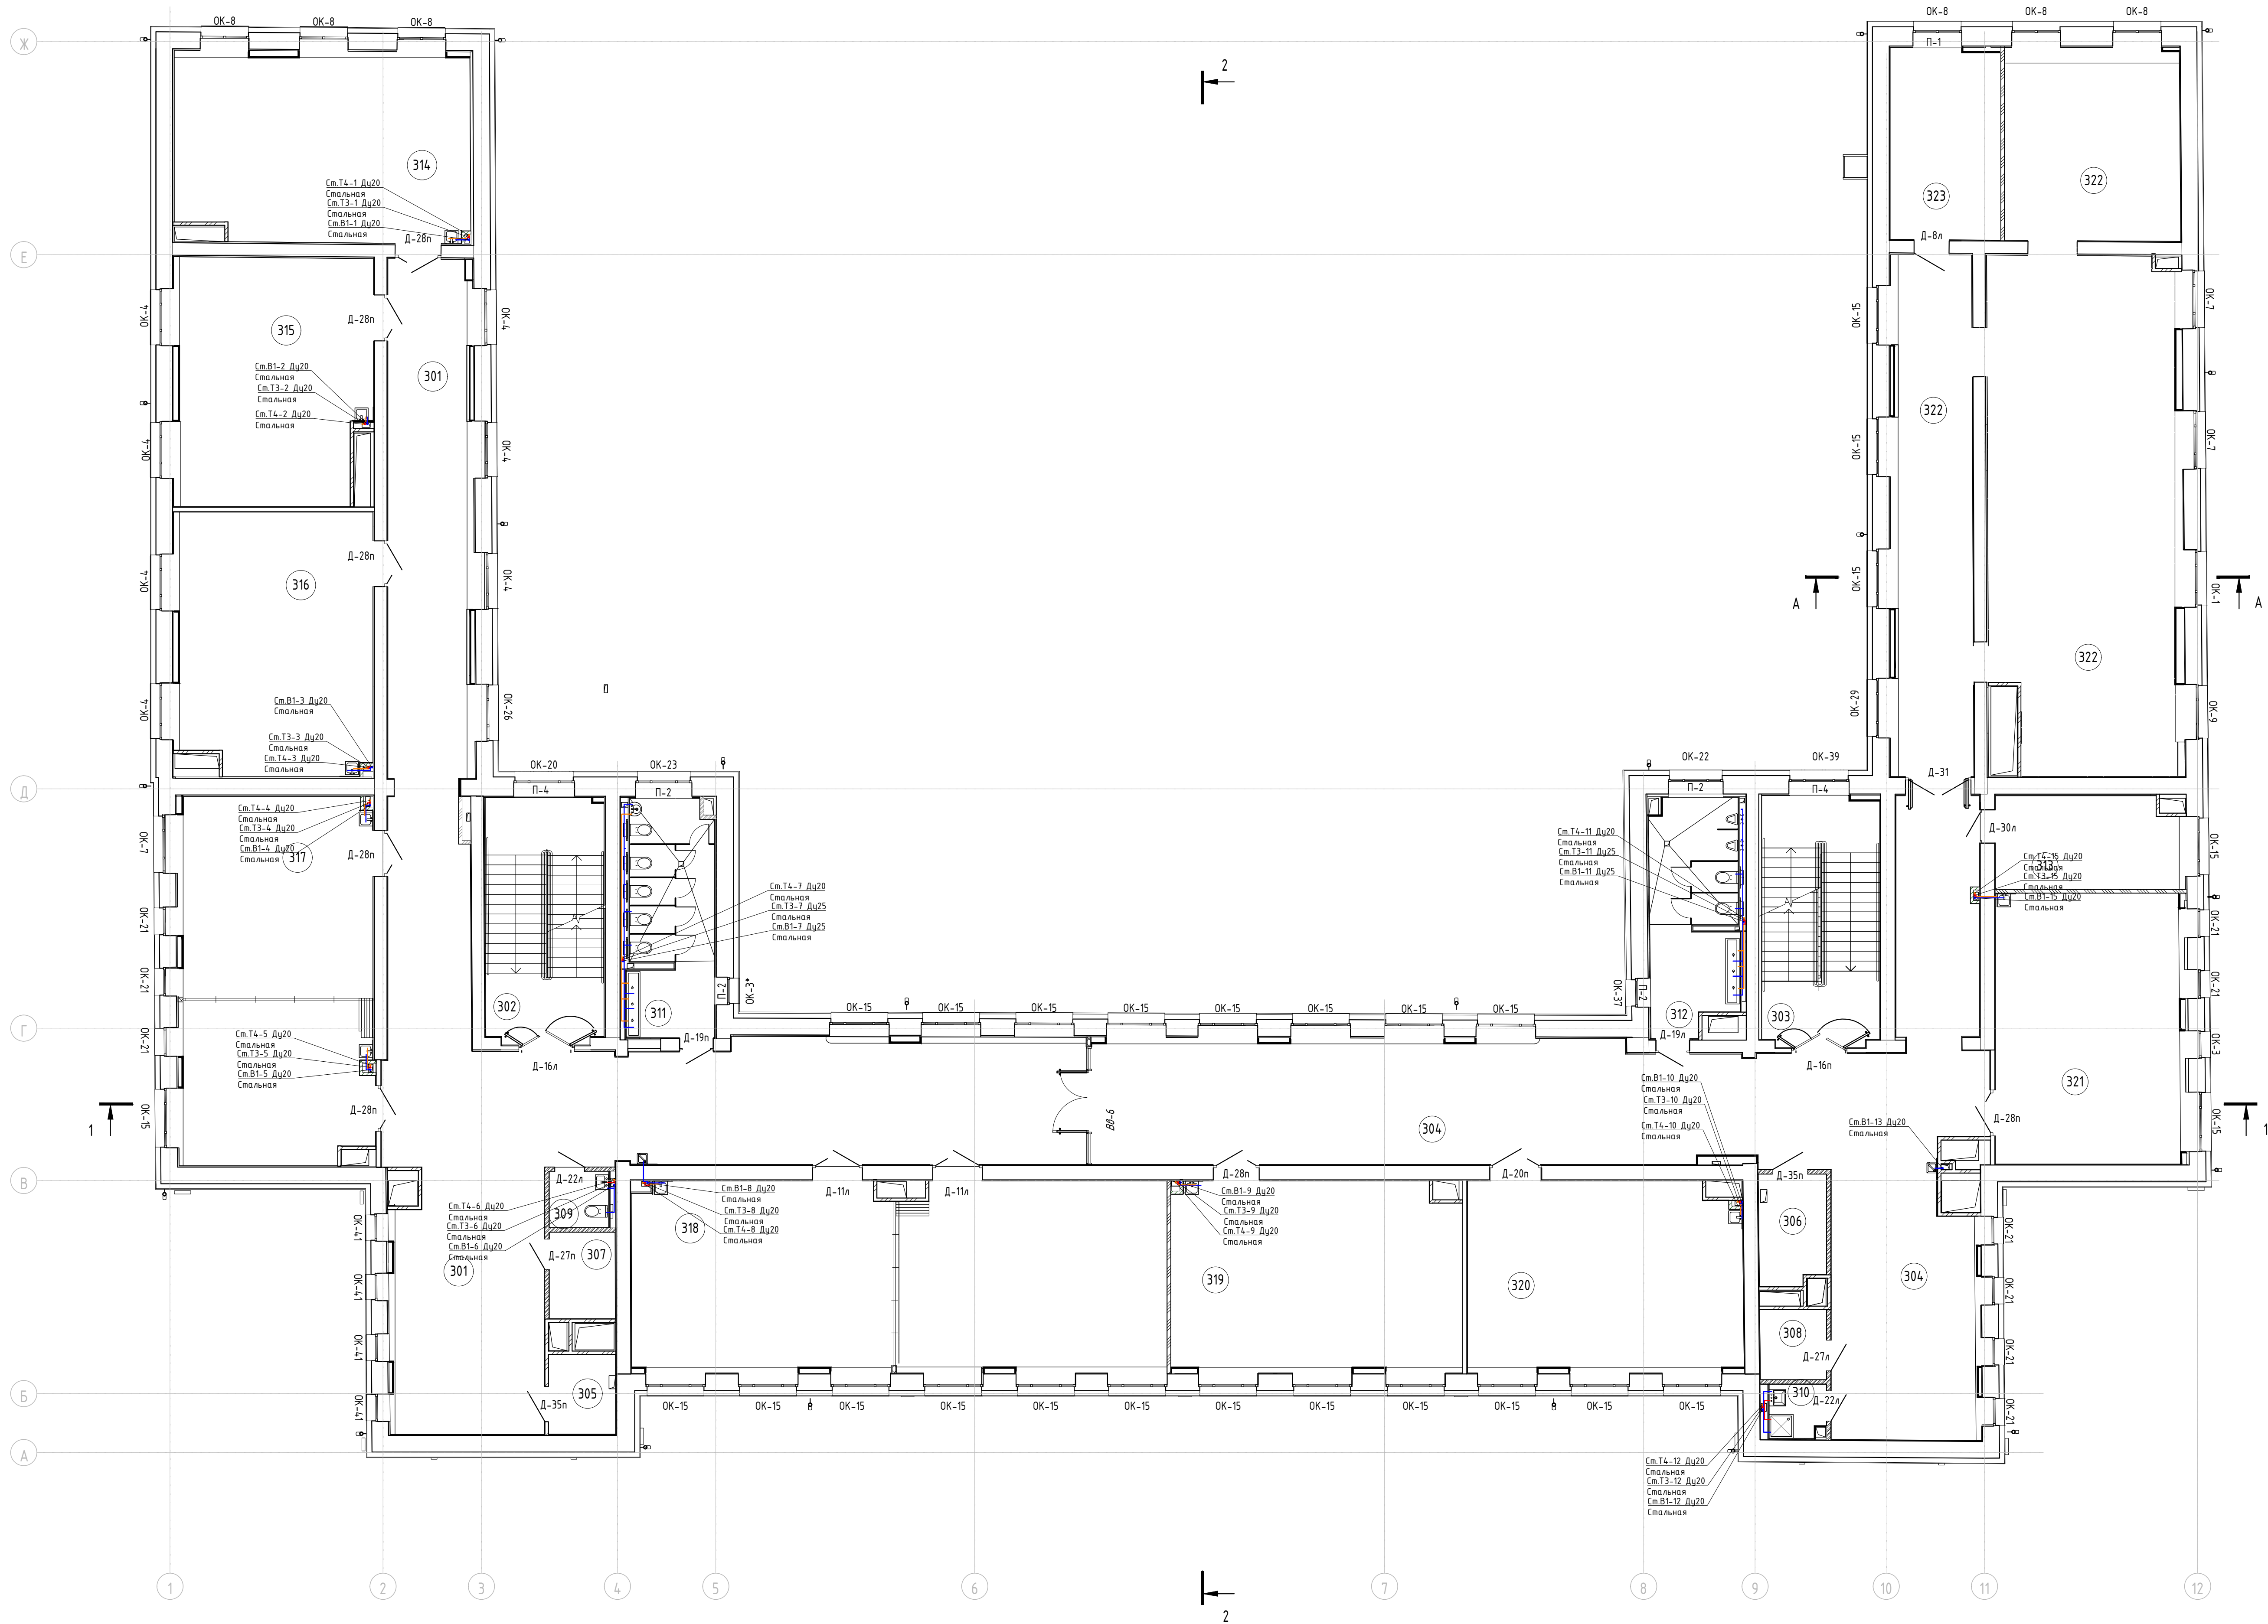

Экспликация помещений 3-го этажа			
Номер помеще-ния	Наименование	Площадь, м²	Кол-во помеще-ния
301	Коридор с рекреацией	179,8	
302	Лестничная клетка (Туп. П1)	27,3	
303	Лестничная клетка (Туп. П1)	27,7	
304	Коридор с рекреацией	155,8	
305	Помещение СС	5,1	В4
306	Помещение СС	6,8	В4
307	Подсобное помещение	5,3	В4
308	Подсобное помещение	4,3	В4
309	Туалет для персонала	3,1	
310	ПМ	2,3	В4
311	Зубная для девочек	19,0	
312	Зубная для мальчиков	18,9	
313	Кабинет для индивидуальных занятий, 6 аккордеонистов педагогов	16,0	
314	Учебный кабинет	51,9	
315	Учебный кабинет	44,6	
316	Учебный кабинет	47,9	
317	Кабинет иностранного языка с возможностью ведения трансформированной перегородкой на 800 помещений	66,5	
318	Музыкальная студия с возможностью ведения трансформированной перегородкой на 800 помещений	94,7	
319	Учебный кабинет	51,4	
320	Учебный кабинет	48,7	
321	Учебный кабинет	47,9	
322	Мультифункциональный информационный библиотечный центр, зона для индивидуальных и групповых занятий, медиатека, центра детских инициатив	163,4	
323	Мультифункциональный информационный библиотечный центр. Хранилище (закрытый фонд) и выдача книг	19,8	В3
		1108,1	

Условные обозначения

- В1 —

Проектируемый хозяйственно-питьевой водопровод
- Т3 —

Подающий трубопровод горячего водоснабжения
- Т4 —

Циркуляционный трубопровод горячего водоснабжения

696/П-25-АНО-Р-ВК					
Капитальный ремонт Государственного бюджетного общеобразовательного учреждения города Москвы "Школа №1282 "Солнышки" по адресу: г. Москва, ул. Бардымова, д. 1, корп. 1					
Исполнитель	Дмитрий	Дмитрий	Дмитрий	Дмитрий	Дмитрий
Разработчик	Борискин	Борискин	Борискин	Борискин	Борискин
Тип	Генеральный	Генеральный	Генеральный	Генеральный	Генеральный
Капитальный ремонт Система водоснабжения				Стенда	Лист
План 3-го этажа водоснабжение				Р	5
Исполнитель	Генеральный	Генеральный	Генеральный	Генеральный	Генеральный
Копировал					
Формат А0					

Экспликация помещений 4-го этажа			
Номер помеще-ния	Наименование	Площадь, м²	Кот. помеще-ния
401	Коридор с рекреацией	173,6	
402	Коридор с рекреацией	166,2	
403	Танбур	4,1	
404	Лестничная клетка (Тип Л1)	26,9	
405	Лестничная клетка (Тип Л1)	26,8	
406	Помещение СС	5,0	В4
407	Помещение СС	6,8	В4
408	Подсобное помещение	5,0	В4
409	Подсобное помещение	4,3	В4
410	Туалет для персонала	2,9	
411	РЗН	2,1	В4
412	Зубная для девочек	19,0	
413	Зубная для мальчиков	19,1	
414	Кабинет для индивидуальных занятий, в т.ч. логопедом-психологом	16,2	
415	Актовый зал (с эстрадой в рабочем положении)	131,1	
416	Технический центр	12,4	В3
417	Артистическая	6,9	
418	Кладовая инвентаря	6,1	В4
419	Кабинет математики	50,8	
420	Учебный кабинет (для изучения естественных биологических наук) Тип 2	92,4	
421	Лаборантская биологии	18,3	В3
422	Учебный кабинет (история)	45,0	
423	Кабинет иностранного языка с возможностью деления трансформируемой перегородкой на два помещения	65,9	
424	Учебный кабинет информатики с возможностью деления трансформируемой перегородкой на два помещения	90,5	
425	Кабинет русского языка и литературы	53,4	
426	Кабинет русского языка и литературы	48,1	
		1098,9	

Условные обозначения



- В1


Проектируемый хозяйственно-питьевой водопровод
- Т3

Подающий трубопровод горячего водоснабжения
- Т4

Циркуляционный трубопровод горячего водоснабжения


						696/П-25-АНО-Р-ВК					
						Капитальный ремонт Государственного бюджетного общеобразовательного учреждения города Москвы "Школа №1282 "Семьинки" по адресу: г. Москва, ул. Бардымова, д. 1 корп. 1					
Испол.	Волгарь	Дата	18.08.2025	Подпись	Догод	Разработал	Борискин	06.26	06.26	06.26	06.26
Тип	Гуляко					Капитальный ремонт Система водоотведения					
						План 4-го этажа водоснабжение	Р	Лист	6	Листов	
И.контр.	Гуляко					Копировал					

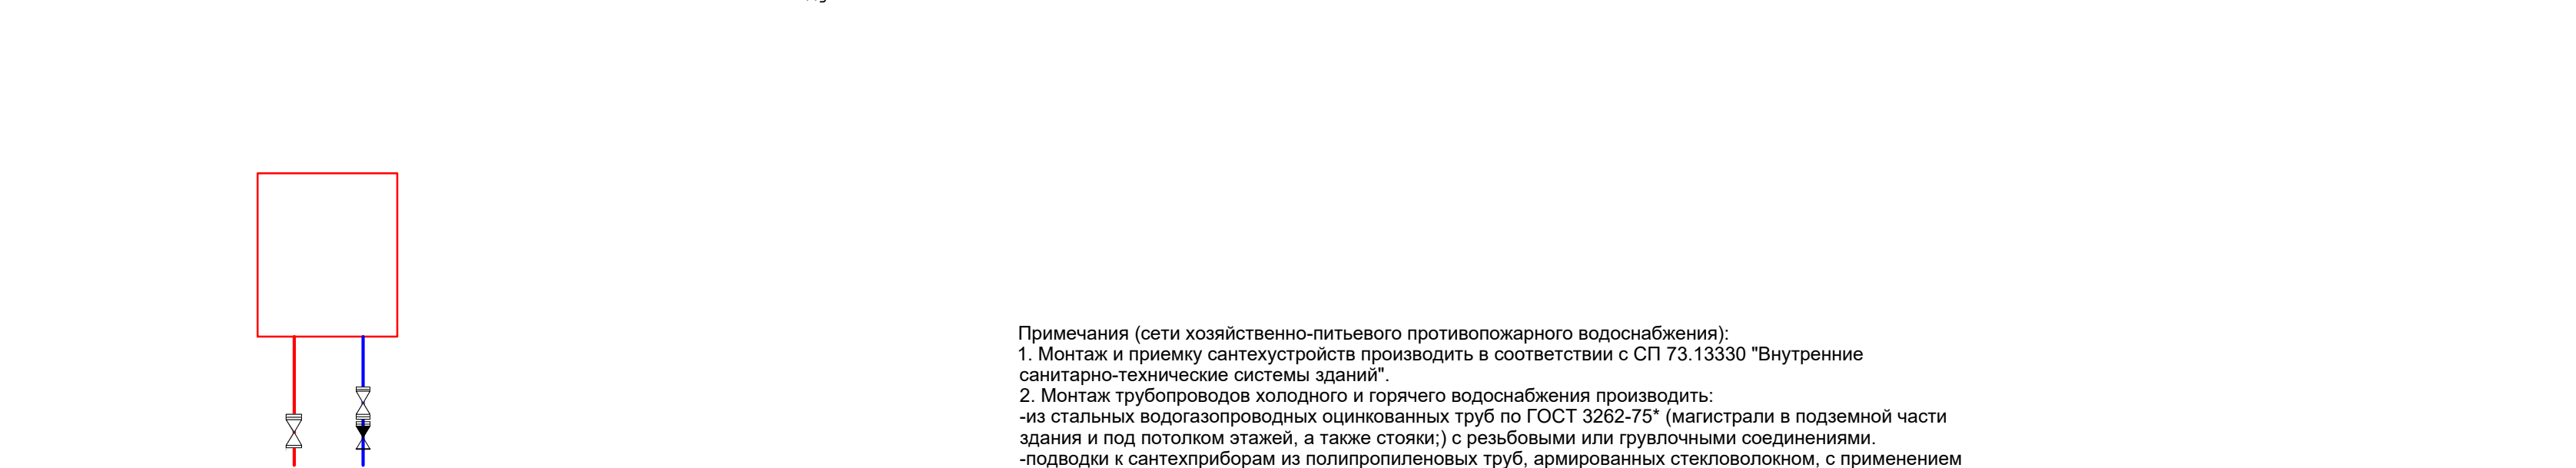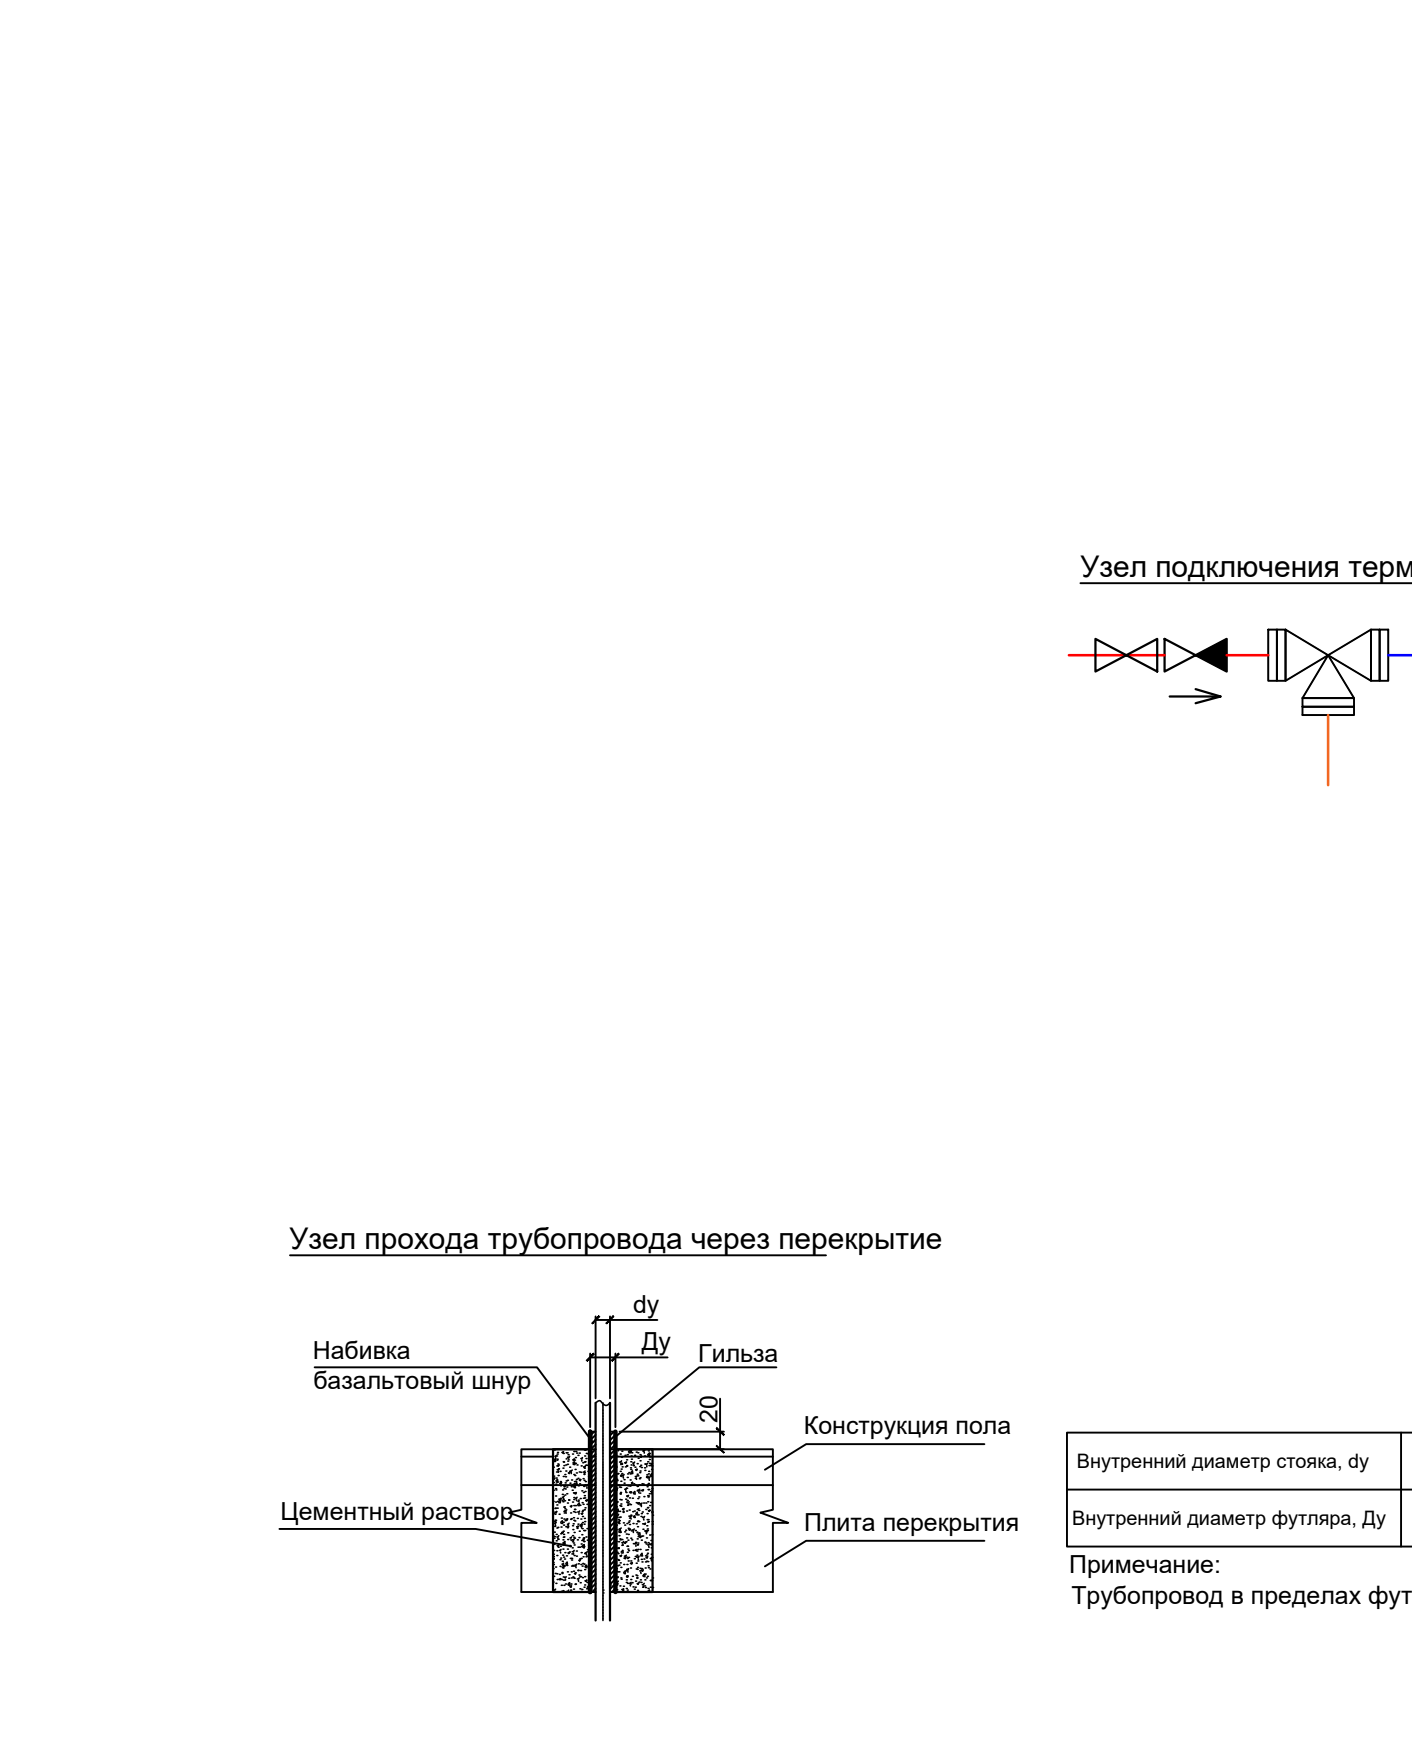

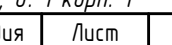
						696/П-25-АНО-Р-ВК			
						Государственный бюджетный Общественный бюджетный город Москвы Цикла МП22 Состояния по адресу: с Москва ул. Барбарина, д.1 корп.1			
Изм.	Колуч	Лист	№ док.	Подпись	Дата		Листов	Листов	
Разработка		Джамнов			09.25	Капитальный ремонт. Система водоснабжения	1	7	
Гип		Улько			09.25		Р	7	
Н.контроль	Надокова				09.25	Схема сети водоснабжения 			

Узлы крепления труб


Подвеска трубопровода к перекрытию

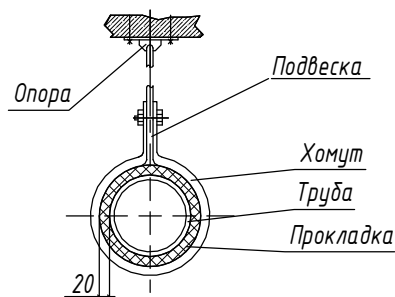


Вертикальная прокладка в стене

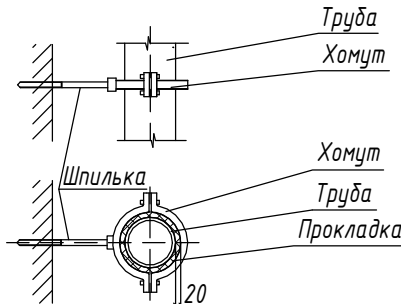


Крепеж трубы к полу

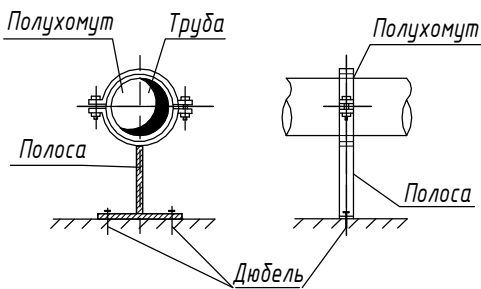

Вариант крепления подвески для нескольких труб

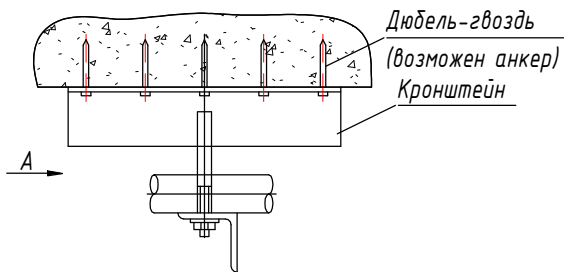

Вид А

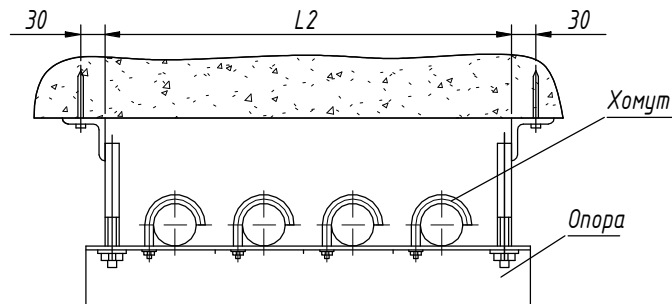

Примечания:

На чертеже показан один из вариантов крепления, на строительном объекте возможны и иные способы и варианты креплений

Наибольшее расстояние между средствами крепления стальных трубопроводов

Диаметр условного прохода трубы, мм	Наибольшее расстояние между средствами крепления трубопроводов, м	
	неизолированных	изолированных
15	2,5	1,5
20	3,0	2,0
25	3,5	2,0
32	4,0	2,5
150	4,5	3,0
50	5,0	3,0
70, 80	6,0	4,0
100	6,0	4,5
125	7,0	5,0
150	8,0	6,0

Согласовано		Взам. инв. №	Подп. и дата	Инв. № подл.

						696/П-25-АНО-Р-ВК			
						Капитальный ремонт Государственного Бюджетного Общеобразовательного Учреждения города Москвы "Школа №1282 "Сокольники" по адресу: г. Москва ул. Барболина, д. 1 корп. 1			
Изм.	Кол.уч.	Лист	№ док.	Подпись	Дата	Капитальный ремонт. Система водоотведения	Стадия	Лист	Листов
Разработал	Брусникин				06.26		Р	8	
ГИП	Гулько				06.26				
						Узлы крепления труб			
Н.контроль	Гулько				06.26				

Экспликация помещений подвала

Номер помеще-ния	Наименование	Площадь, м²	Кат. поме-ще-ния
001	Техническая лестница	13,7	
001a	Тамбур-шлюз 1-го типа	4,9	
002	Техническая лестница	9,8	
002a	Тамбур-шлюз 1-го типа	5,0	
003	Спортивный зал	262,5	
004	Снарядная	10,1	B3
005	ПУИ	3,5	
006	Снарядная	28,0	B3
007	Коридор	21,0	
008	Коридор	17,9	
009	Кладовая	21,4	B3
010	Венткамера	Не окружено	B4
011	Форкамера	Не окружено	B4
012	Форкамера	3,8	B4
013	Венткамера	37,5	B4
014	Коридор	63,3	
015	Коридор	9,8	
016	Коридор	19,3	
017	Коридор	8,3	
018	Насосная	14,8	B4
019	Венткамера	19,3	B4
020	Форкамера	5,2	B4
021	ИТП	75,6	Д
022	Венткамера	41,1	B4
ИТОГО:		695,8	

УСЛОВНЫЕ ОБОЗНАЧЕНИЯ

- K1

Хозяйственно-бытовая канализация
- KдН


Напорная дренажная канализация
- K3

Производственная канализация

Номер помещения	Наименование	Площадь, м ²	Кат. помещения
101	Тамбур	17,0	
102	Вестиболь	66,7	
103	Комната охраны (с диспетчерским пунктом)	16,0	
104	Гардероб для обучающихся	47,2	
105	Коридор	62,9	
106	Гардероб для обучающихся	54,2	
107	Учебный кабинет (Тип 1)	67,4	
108	Электрощитовая	15,5	ВЗ
109	Учебный кабинет (Тип 2)	57,3	
110	Кладовая	18,0	ВЗ
111	Учебный кабинет (математика)	52,3	
112	Лестничная клетка (Тип Л1)	27,6	
113	Туалет для персонала	2,8	
114	Уборная для девочек	15,9	
115	Техническая лестница	18,0	
116	ПУИ	4,0	В4
117	Универсальная уборная для МГН	6,5	
118	Коридор	194,5	
119	Раздевальная Тип 1	19,0	
120	Душевая	6,5	
121	Уборная	5,3	
122	Уборная	5,3	
123	Душевая	6,5	
124	Раздевальная Тип 1	18,4	
125	Техническая лестница	18,8	
126	Уборная для мальчиков	18,0	
127	Лестничная клетка (Тип Л1)	27,6	
128	Тренинговая с санузлом	8,7	
129	Умывальная	10,1	
130	Обеденный зал	108,3	
131	Моечная для столовой посуды	17,3	В4
132	Коридор	13,1	
133	Кладовая и моечная оборотной тары	4,0	В4
134	Загрузочный цех	6,2	В4
135	Кладовая сухих продуктов	3,7	В4
136	Помещение персонала с санузлом	4,2	
137	Пом. для временного хранения пищевых отходов	4,4	В4
138	ПУИ	3,6	В4
139	Пом. подготовки блюд к реализации с участком мойки кухонной посуды	30,5	В4
140	Кабинет врача	18,9	
141	Процедурный (прибавочный) кабинет	13,2	
142	Пом. для хранения уборочного инвентаря, приготовления дезинфицирующих растворов	5,9	В4
143	Ожидательная медблока	3,5	
144	Помещение СС	9,4	В4
145	Кабинет с рабочим пространством для учителей (Тип 1)	42,0	
146	Гардероб для учителей	19,4	
147	Гардероб для обучающихся	49,0	
148	Тамбур	2,0	
149	Венткамера	9,1	?
150	Венткамера	15,5	
ИТОГО:		1271,4	


— K1 —	Хозяйственно-бытовая канализация
— KдН —	Напорная дренажная канализация
— K3 —	Производственная канализация

[illegible]

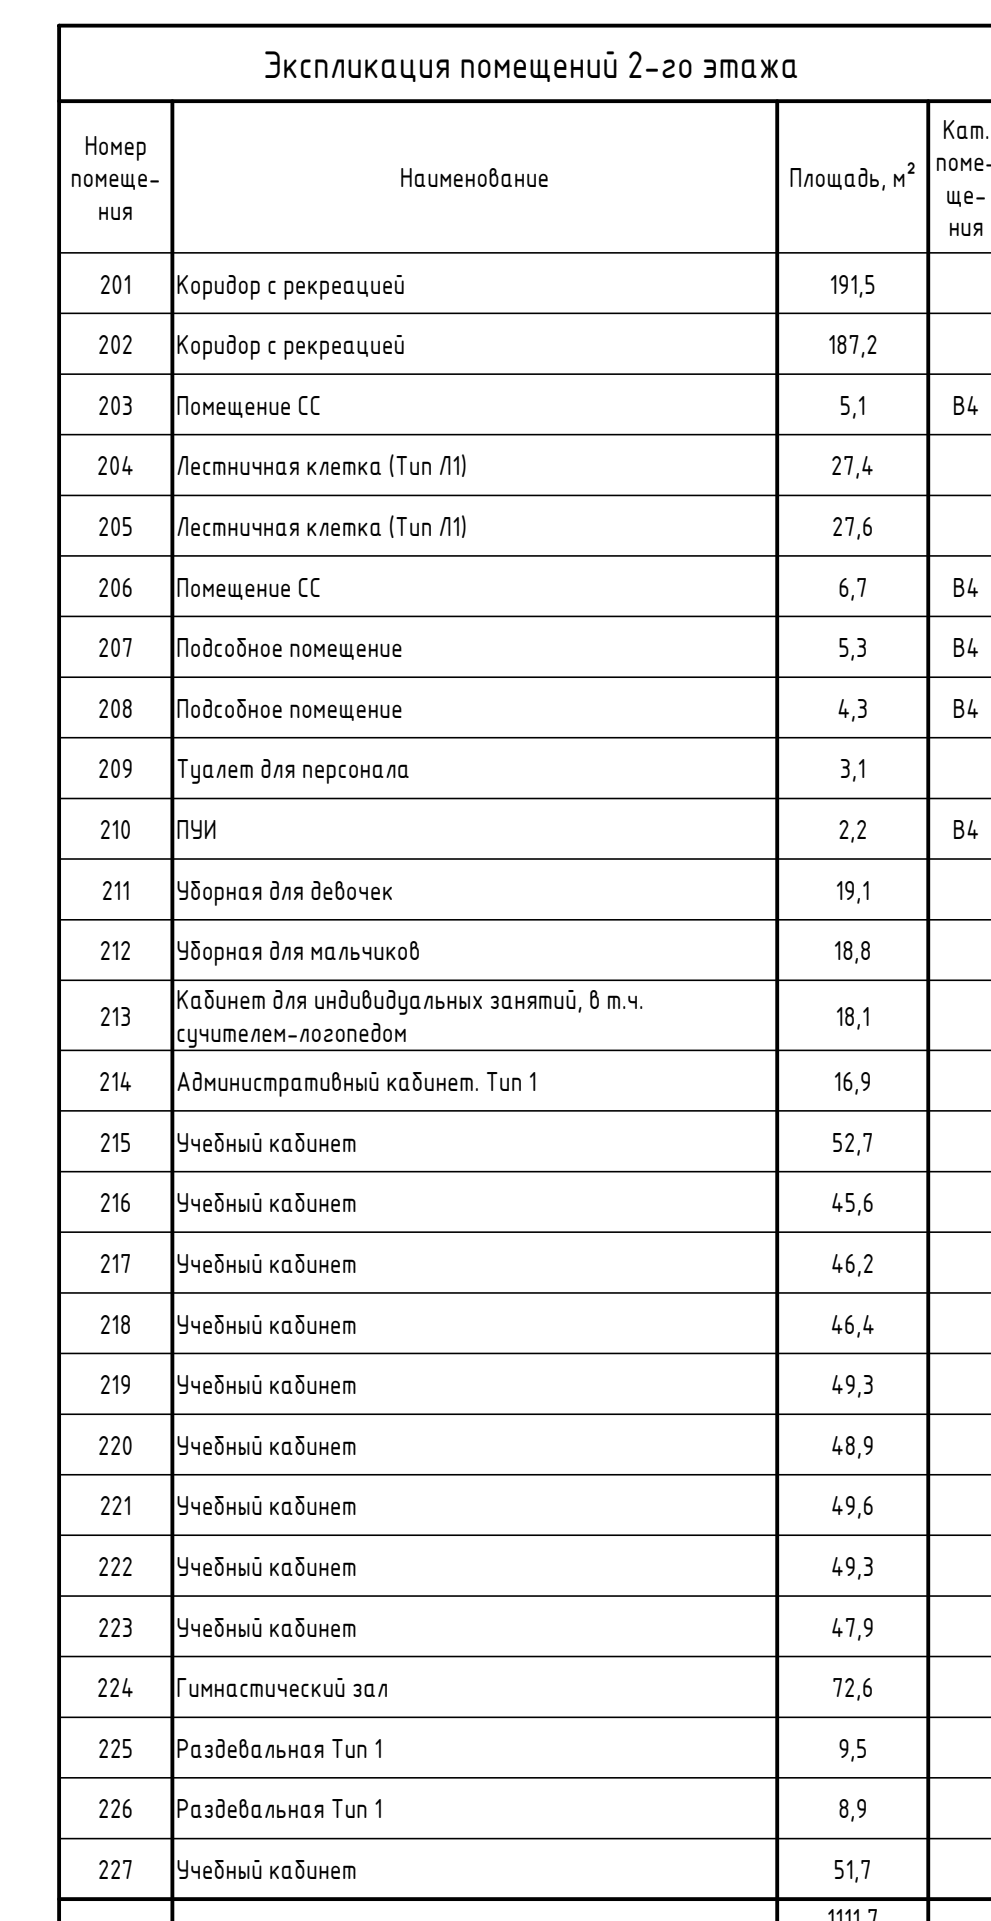

— K1 —	Хозяйственно-бытовая канализация
— КДН —	Напорная дренажная канализация
— КЗ —	Производственная канализация

Копировал	Формат А
-----------	----------

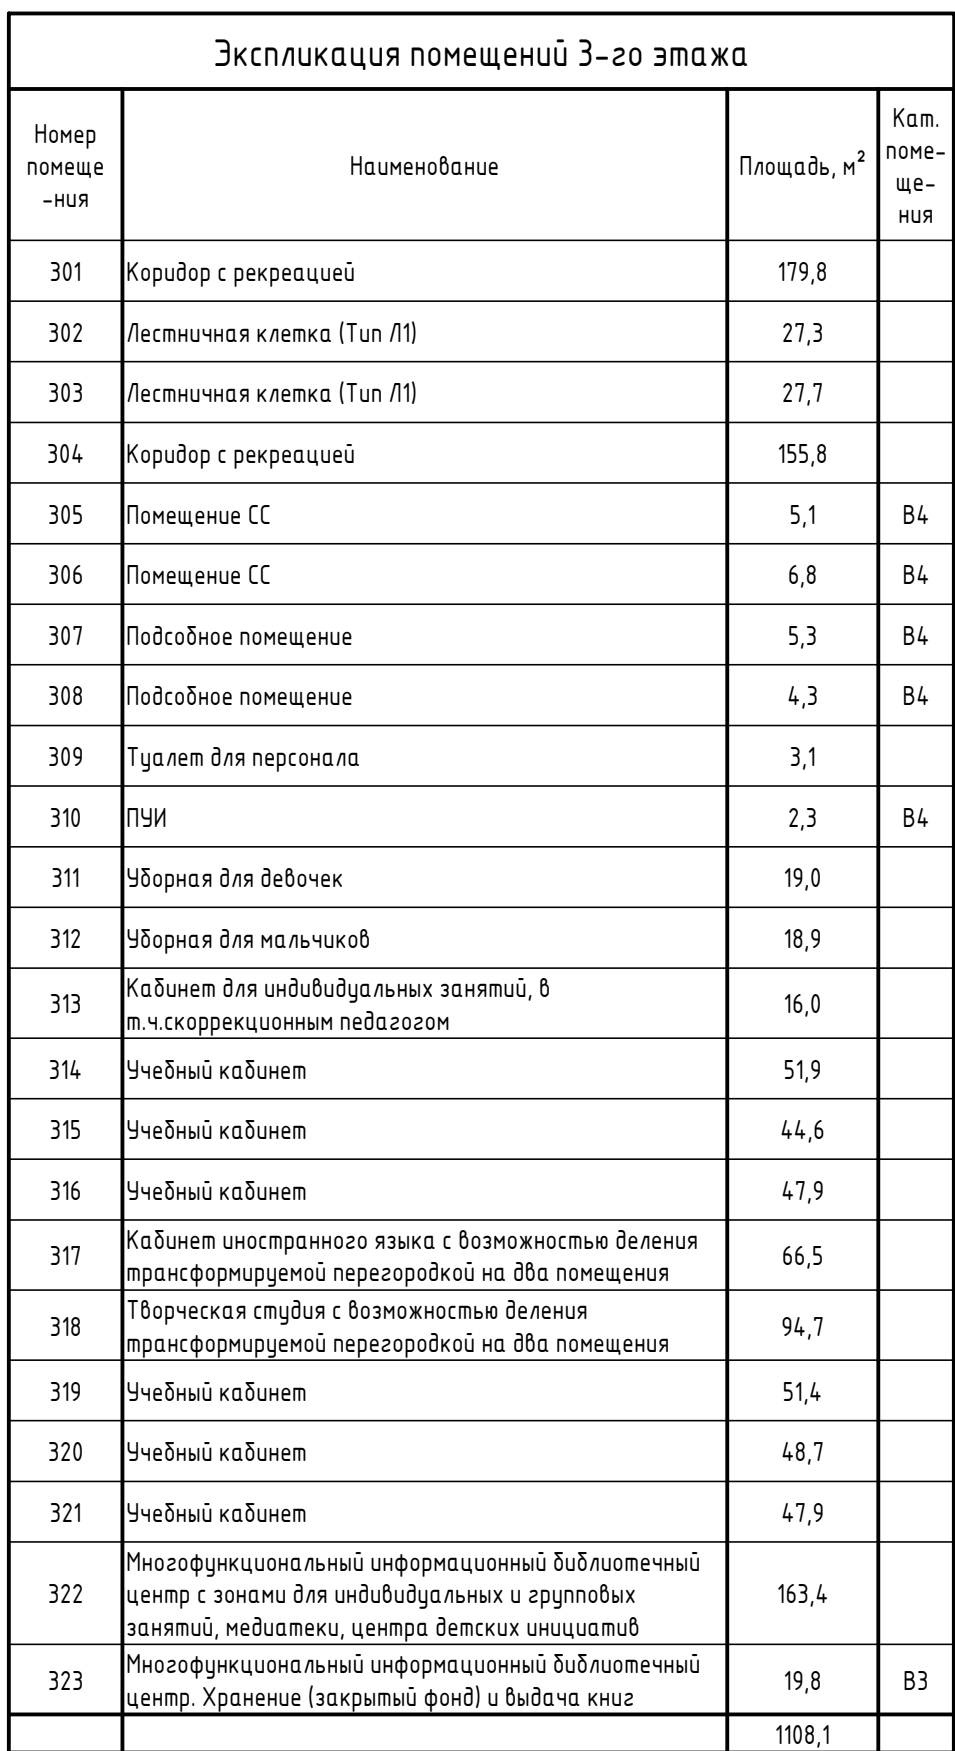


К1	Хозяйственно-бытовая канализация
КдН	Напорная дренажная канализация
КЗ	Производственная канализация



— K1 —	Хозяйственно-бытовая канализация
— КдН —	Напорная дренажная канализация
— КЗ —	Производственная канализация


[illegible]

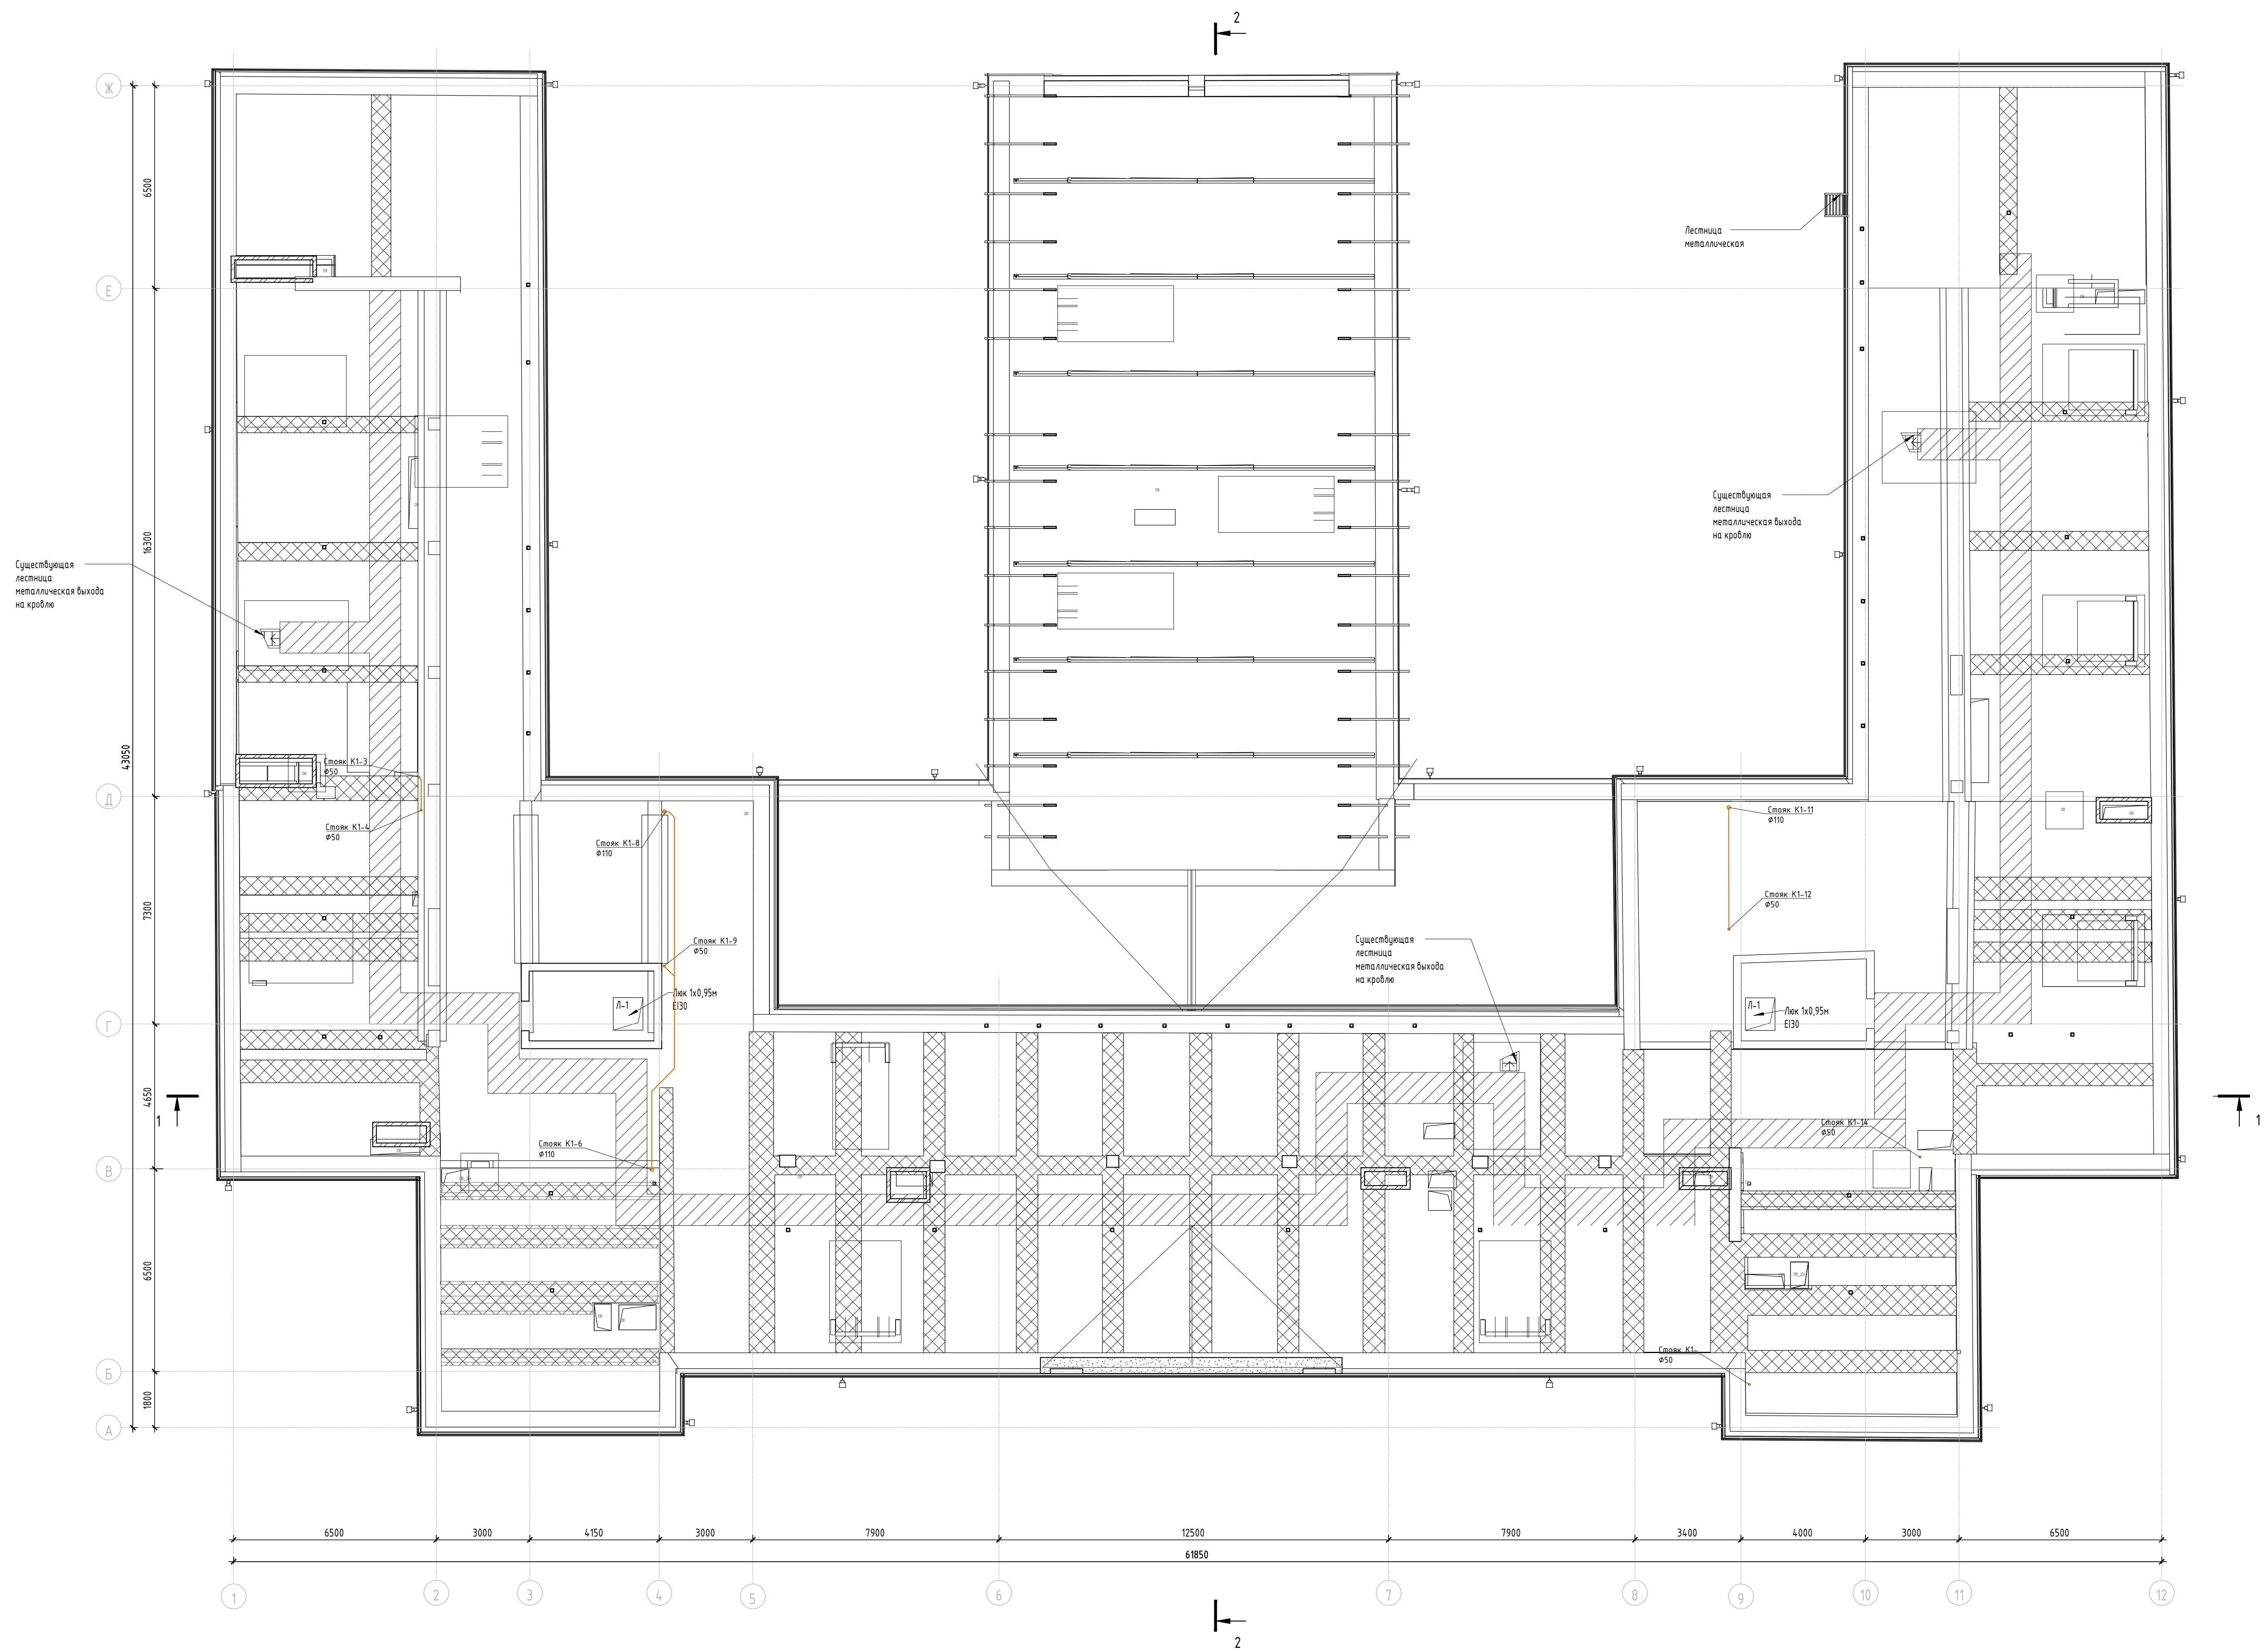

УСЛОВНЫЕ ОБОЗНАЧЕНИЯ

- K1 — Хозяйственно-бытовая канализация
- KДН — Напорная дренажная канализация
- KЗ — Производственная канализация

696/П-25-АНО-Р-ВК						Капитальный ремонт Государственного бюджетного общеобразовательного Учреждения города Москвы "Школа №1282 "Семьимини" по адресу: г. Москва, ул. Бардымова, д. 1 корп. 1			Стенда	Лист	Листов
Испол.	Молочко	Диз. 1х1	Диз. 1х1	Диз. 1х1	Диз. 1х1	Разработчик	Борискин	06.25	Капитальный ремонт Система водоотведения		
ТИП	Гилья	06.25	06.25	06.25	06.25	План чердака с сетями канализация			Копировал		
И.контр.	Гилья	06.25	06.25	06.25	06.25	Формат А0					

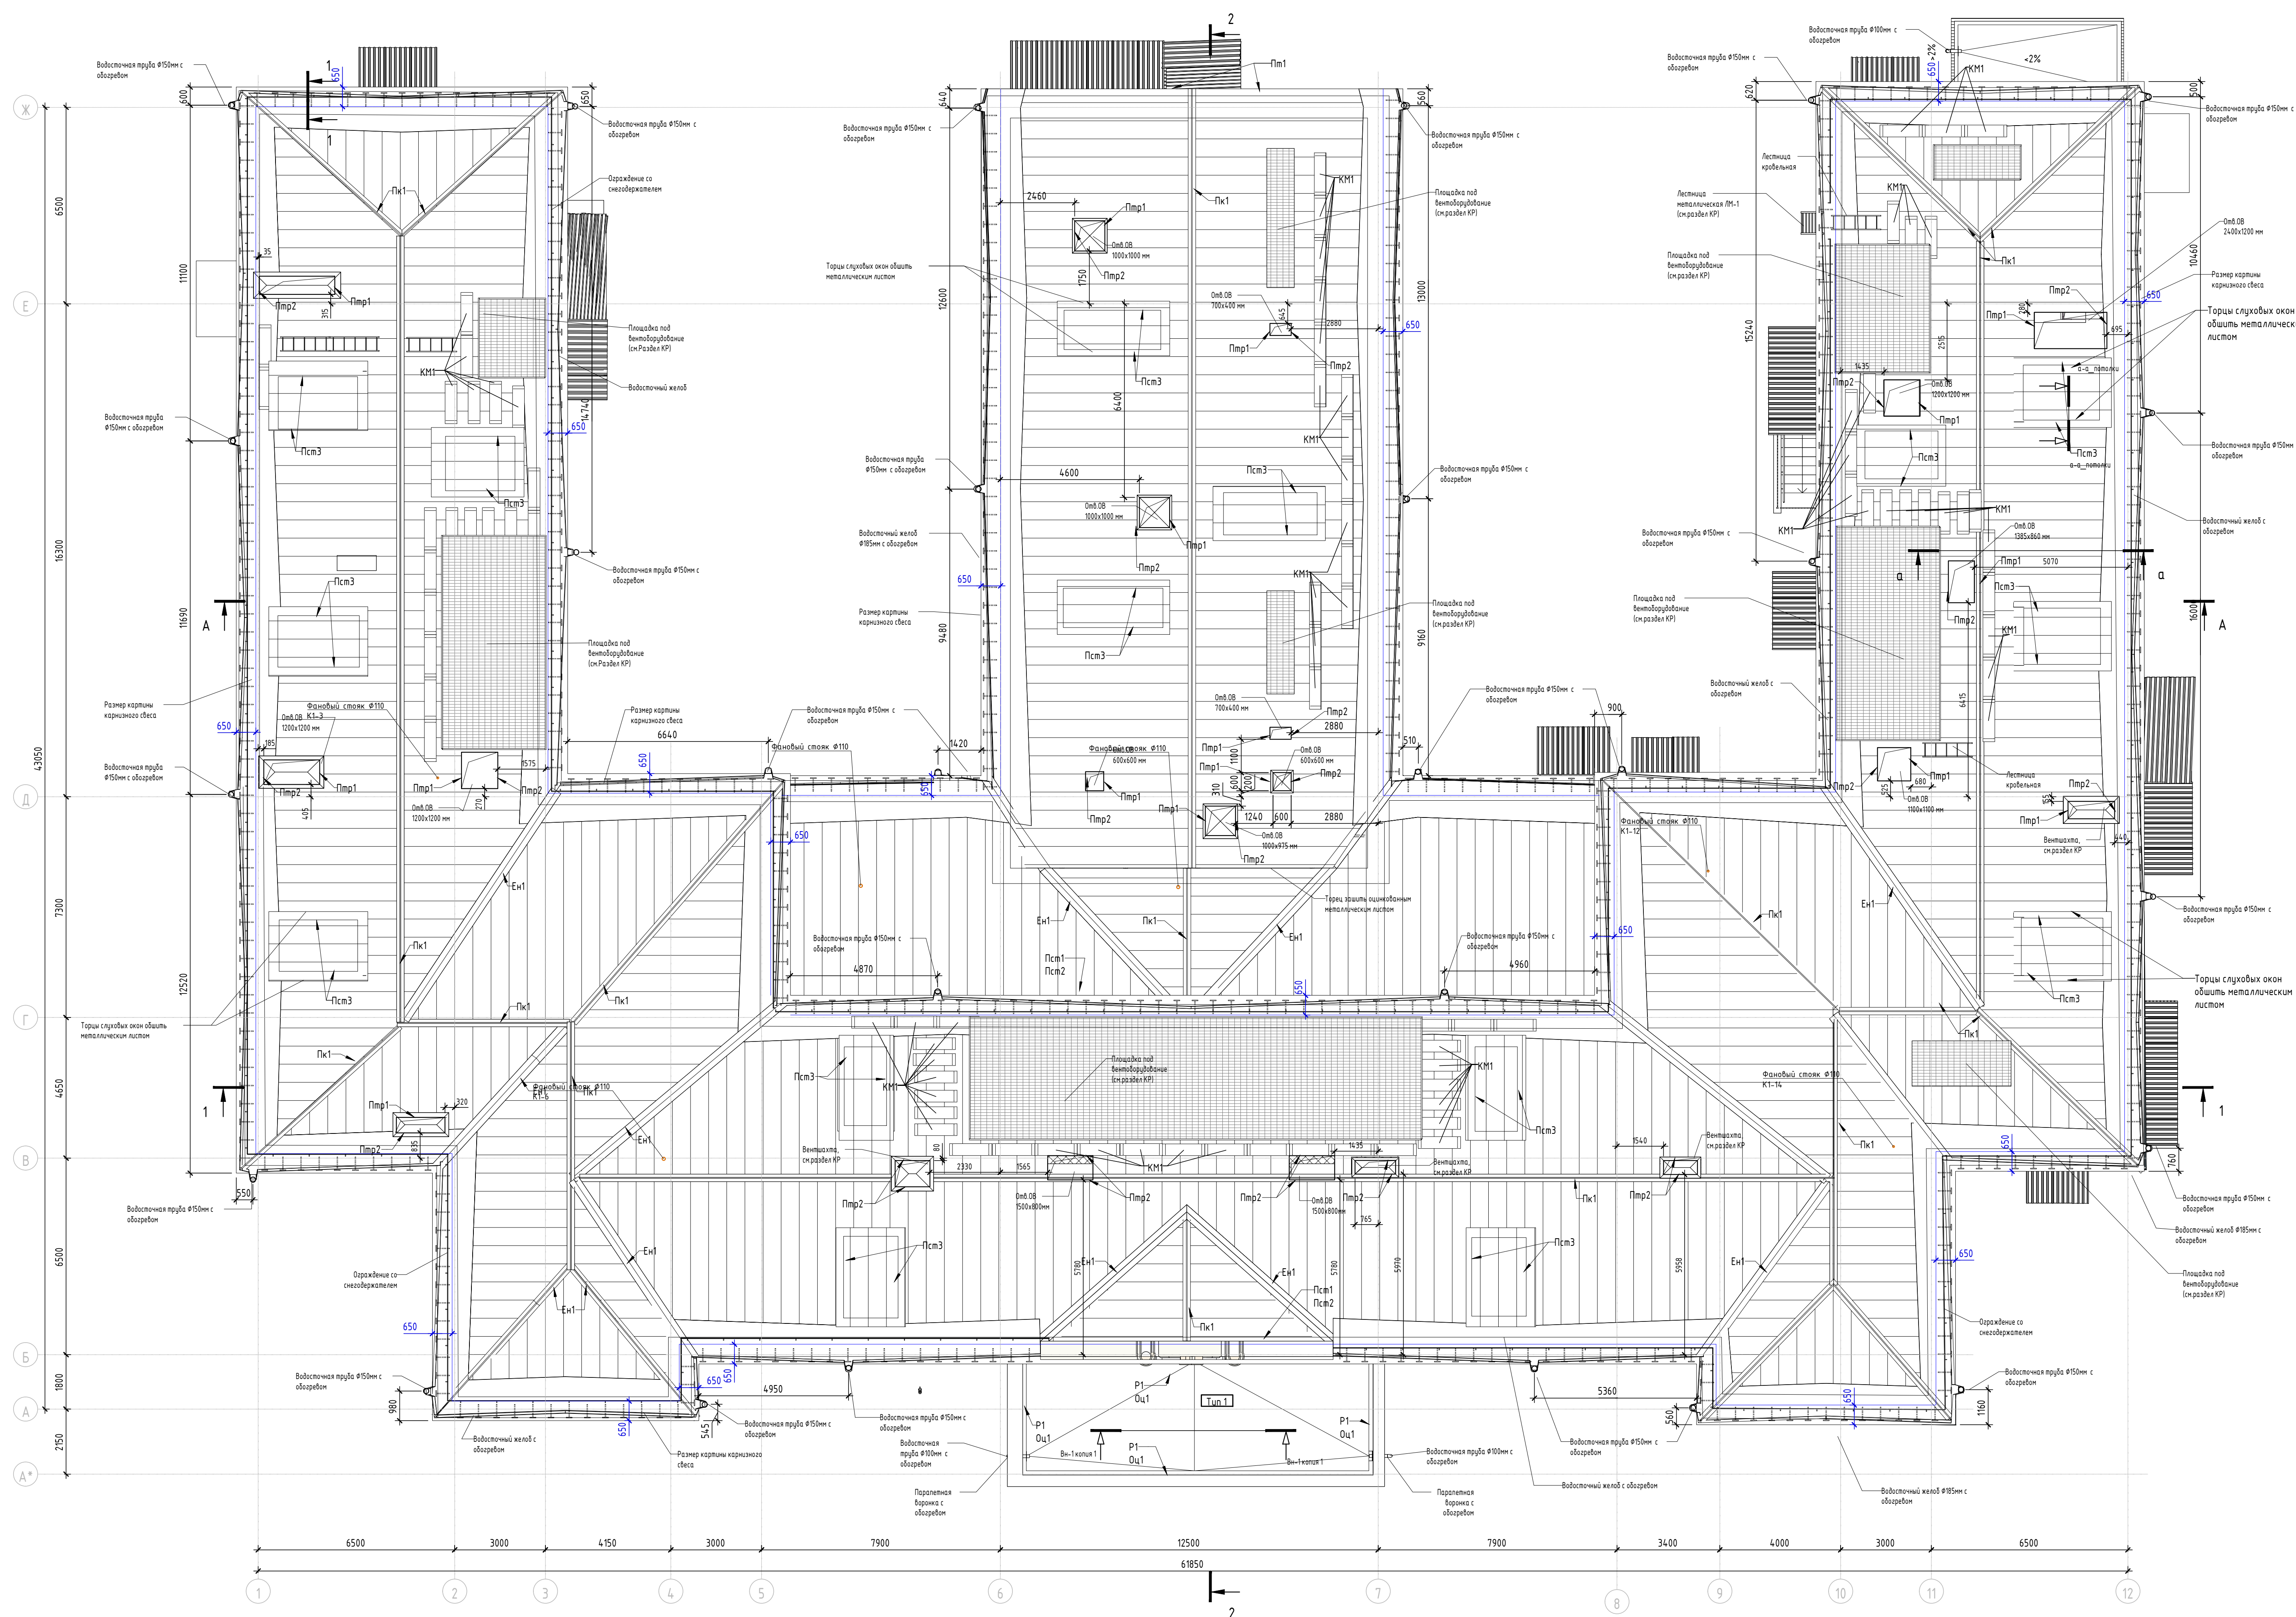



Условные обозначения:

- К1 - хозяйственно-бытовая канализация
- КdH - напорная дренажная канализация
- К3 - производственная канализация

УСЛОВНЫЕ ОБОЗНАЧЕНИЯ



- К1 — Хозяйственно-бытовая канализация
- КdH — Напорная дренажная канализация
- К3 — Производственная канализация

696/П-25-АНО-Р-ВК					
Капитальный ремонт Государственного бюджетного общеобразовательного учреждения «Школа №1282 "Солнечный"» по адресу: г. Москва, ул. Бардымова, д. 1, корп. 1					
Исполн.	Дизайн	Деталь	Дата	Стенда	Лист
И.В. Волков	В.И. Волков	В.И. Волков	06.25	Р	5
Тип	Генеральный	Система водоотведения	06.25	План кровли с сетями канализации	
И.В. Волков	В.И. Волков	В.И. Волков	06.25	Копирован	

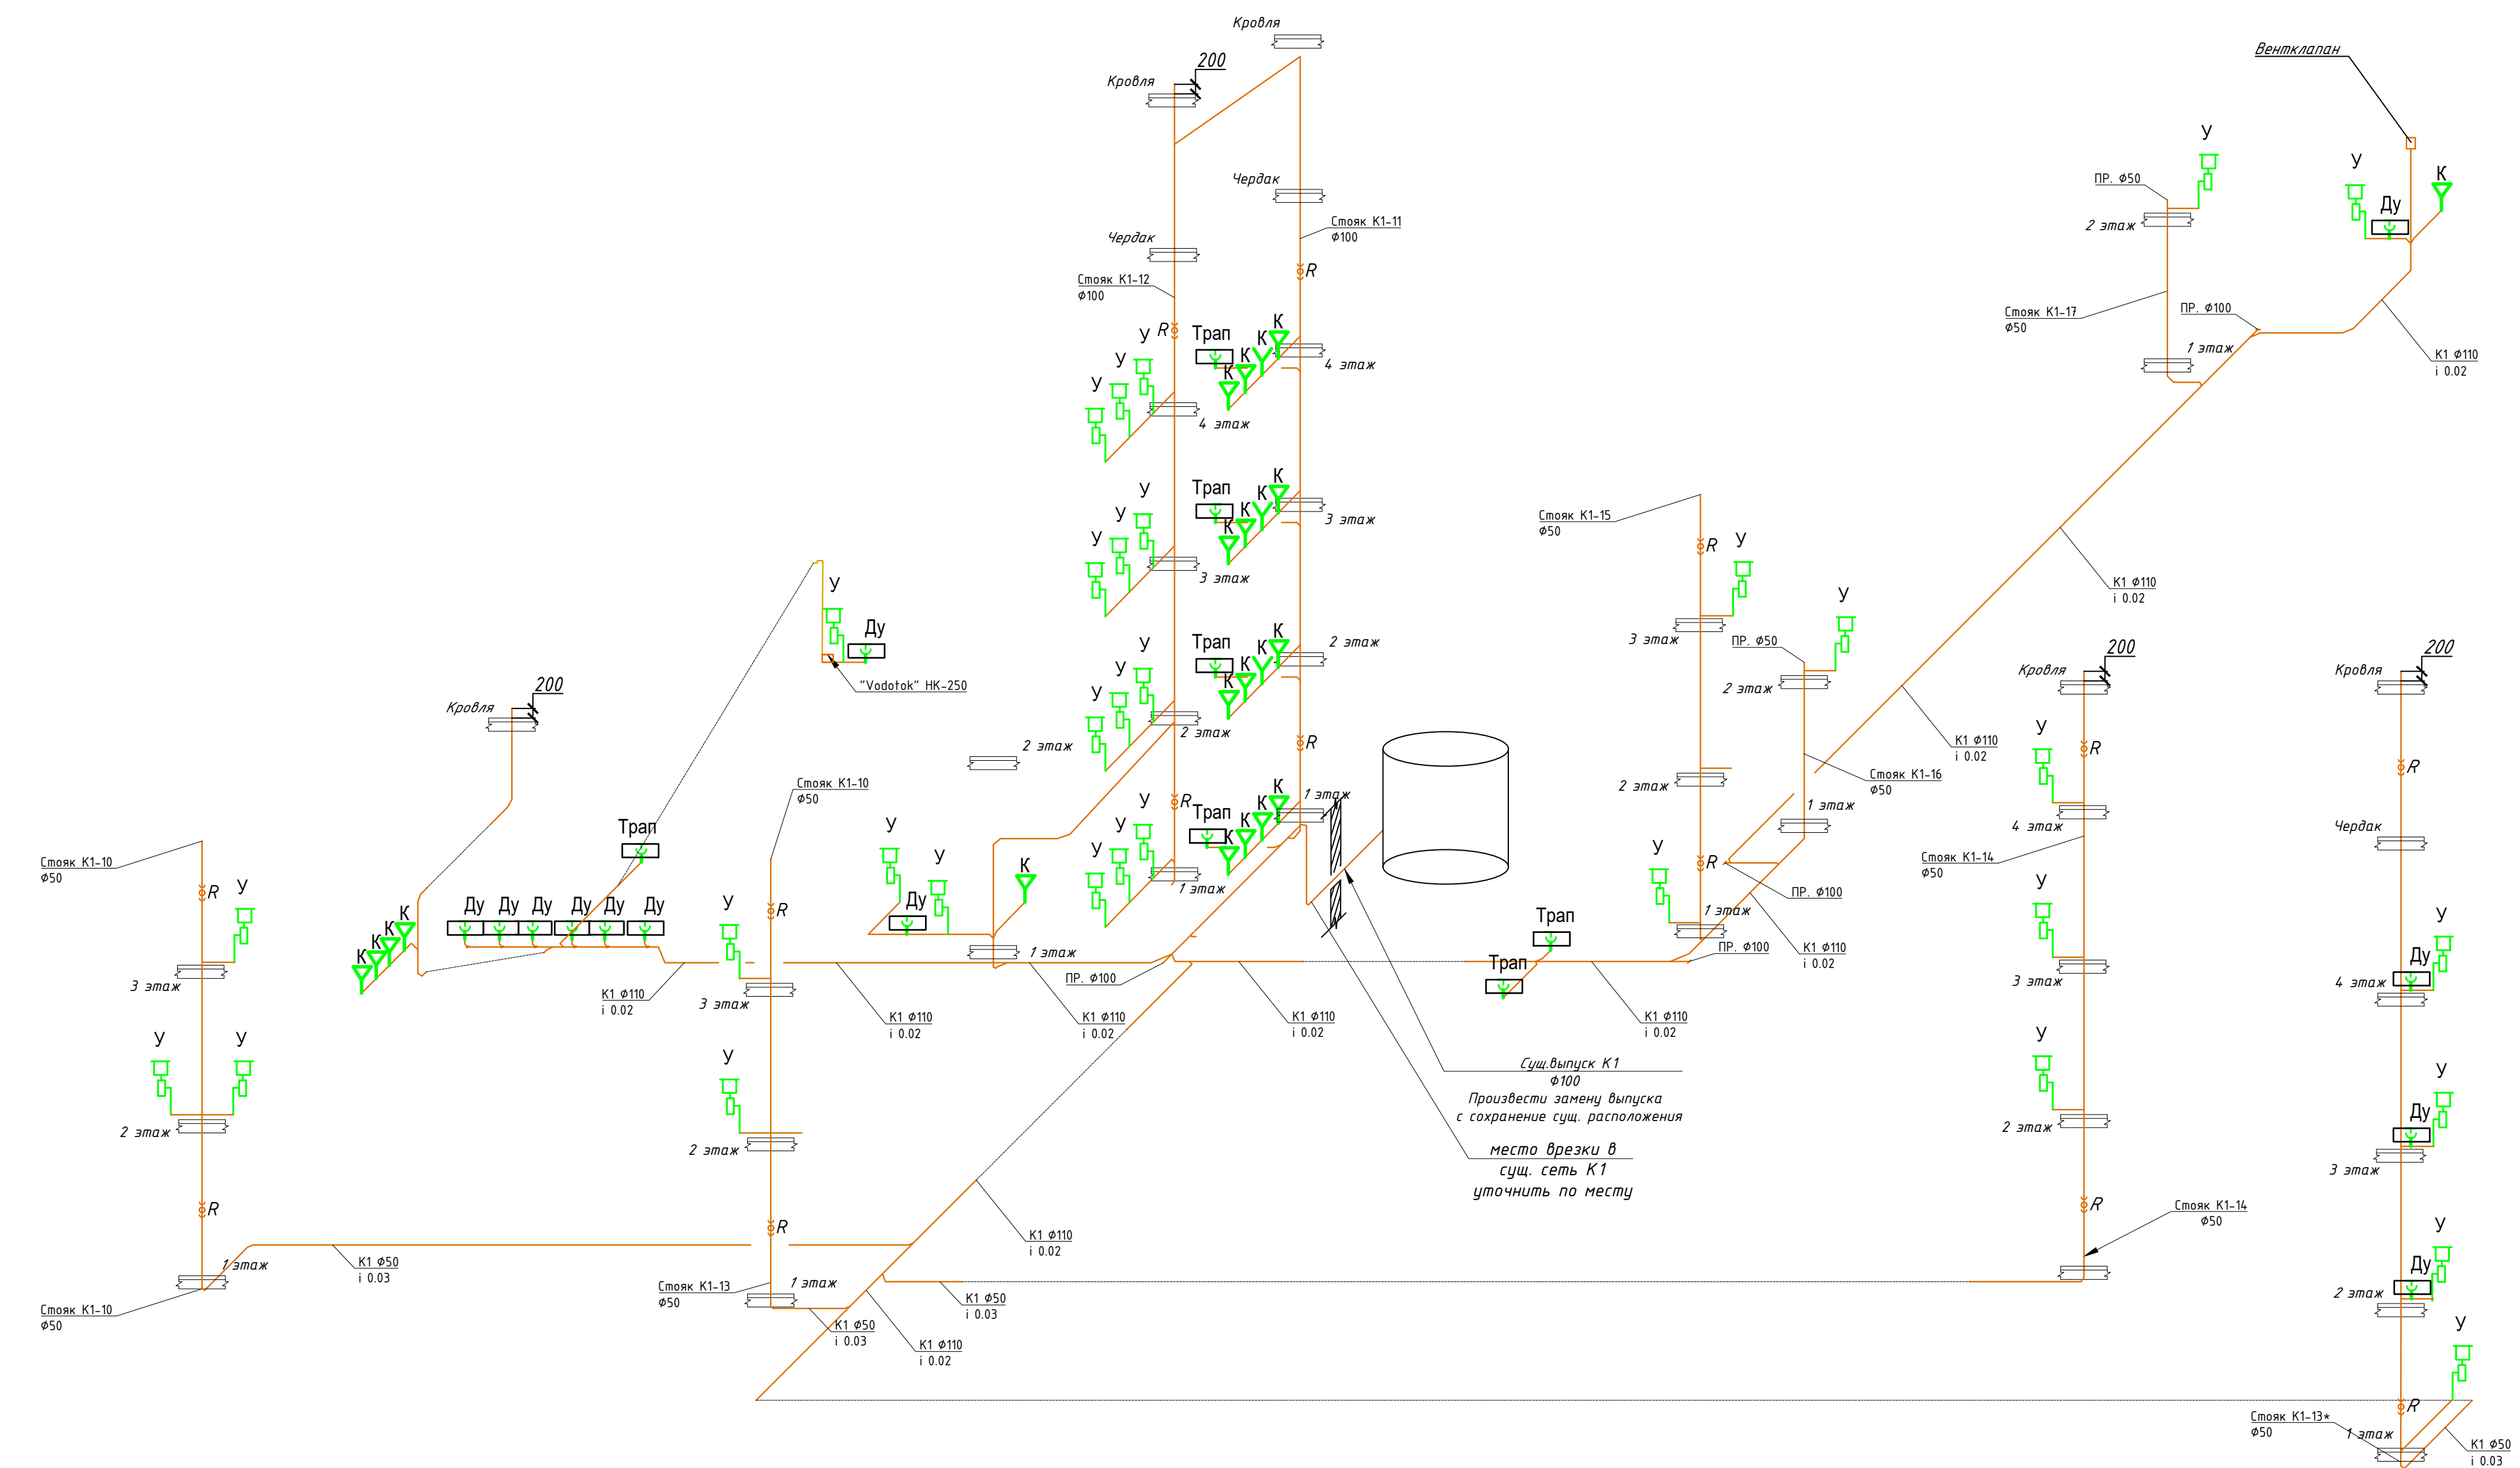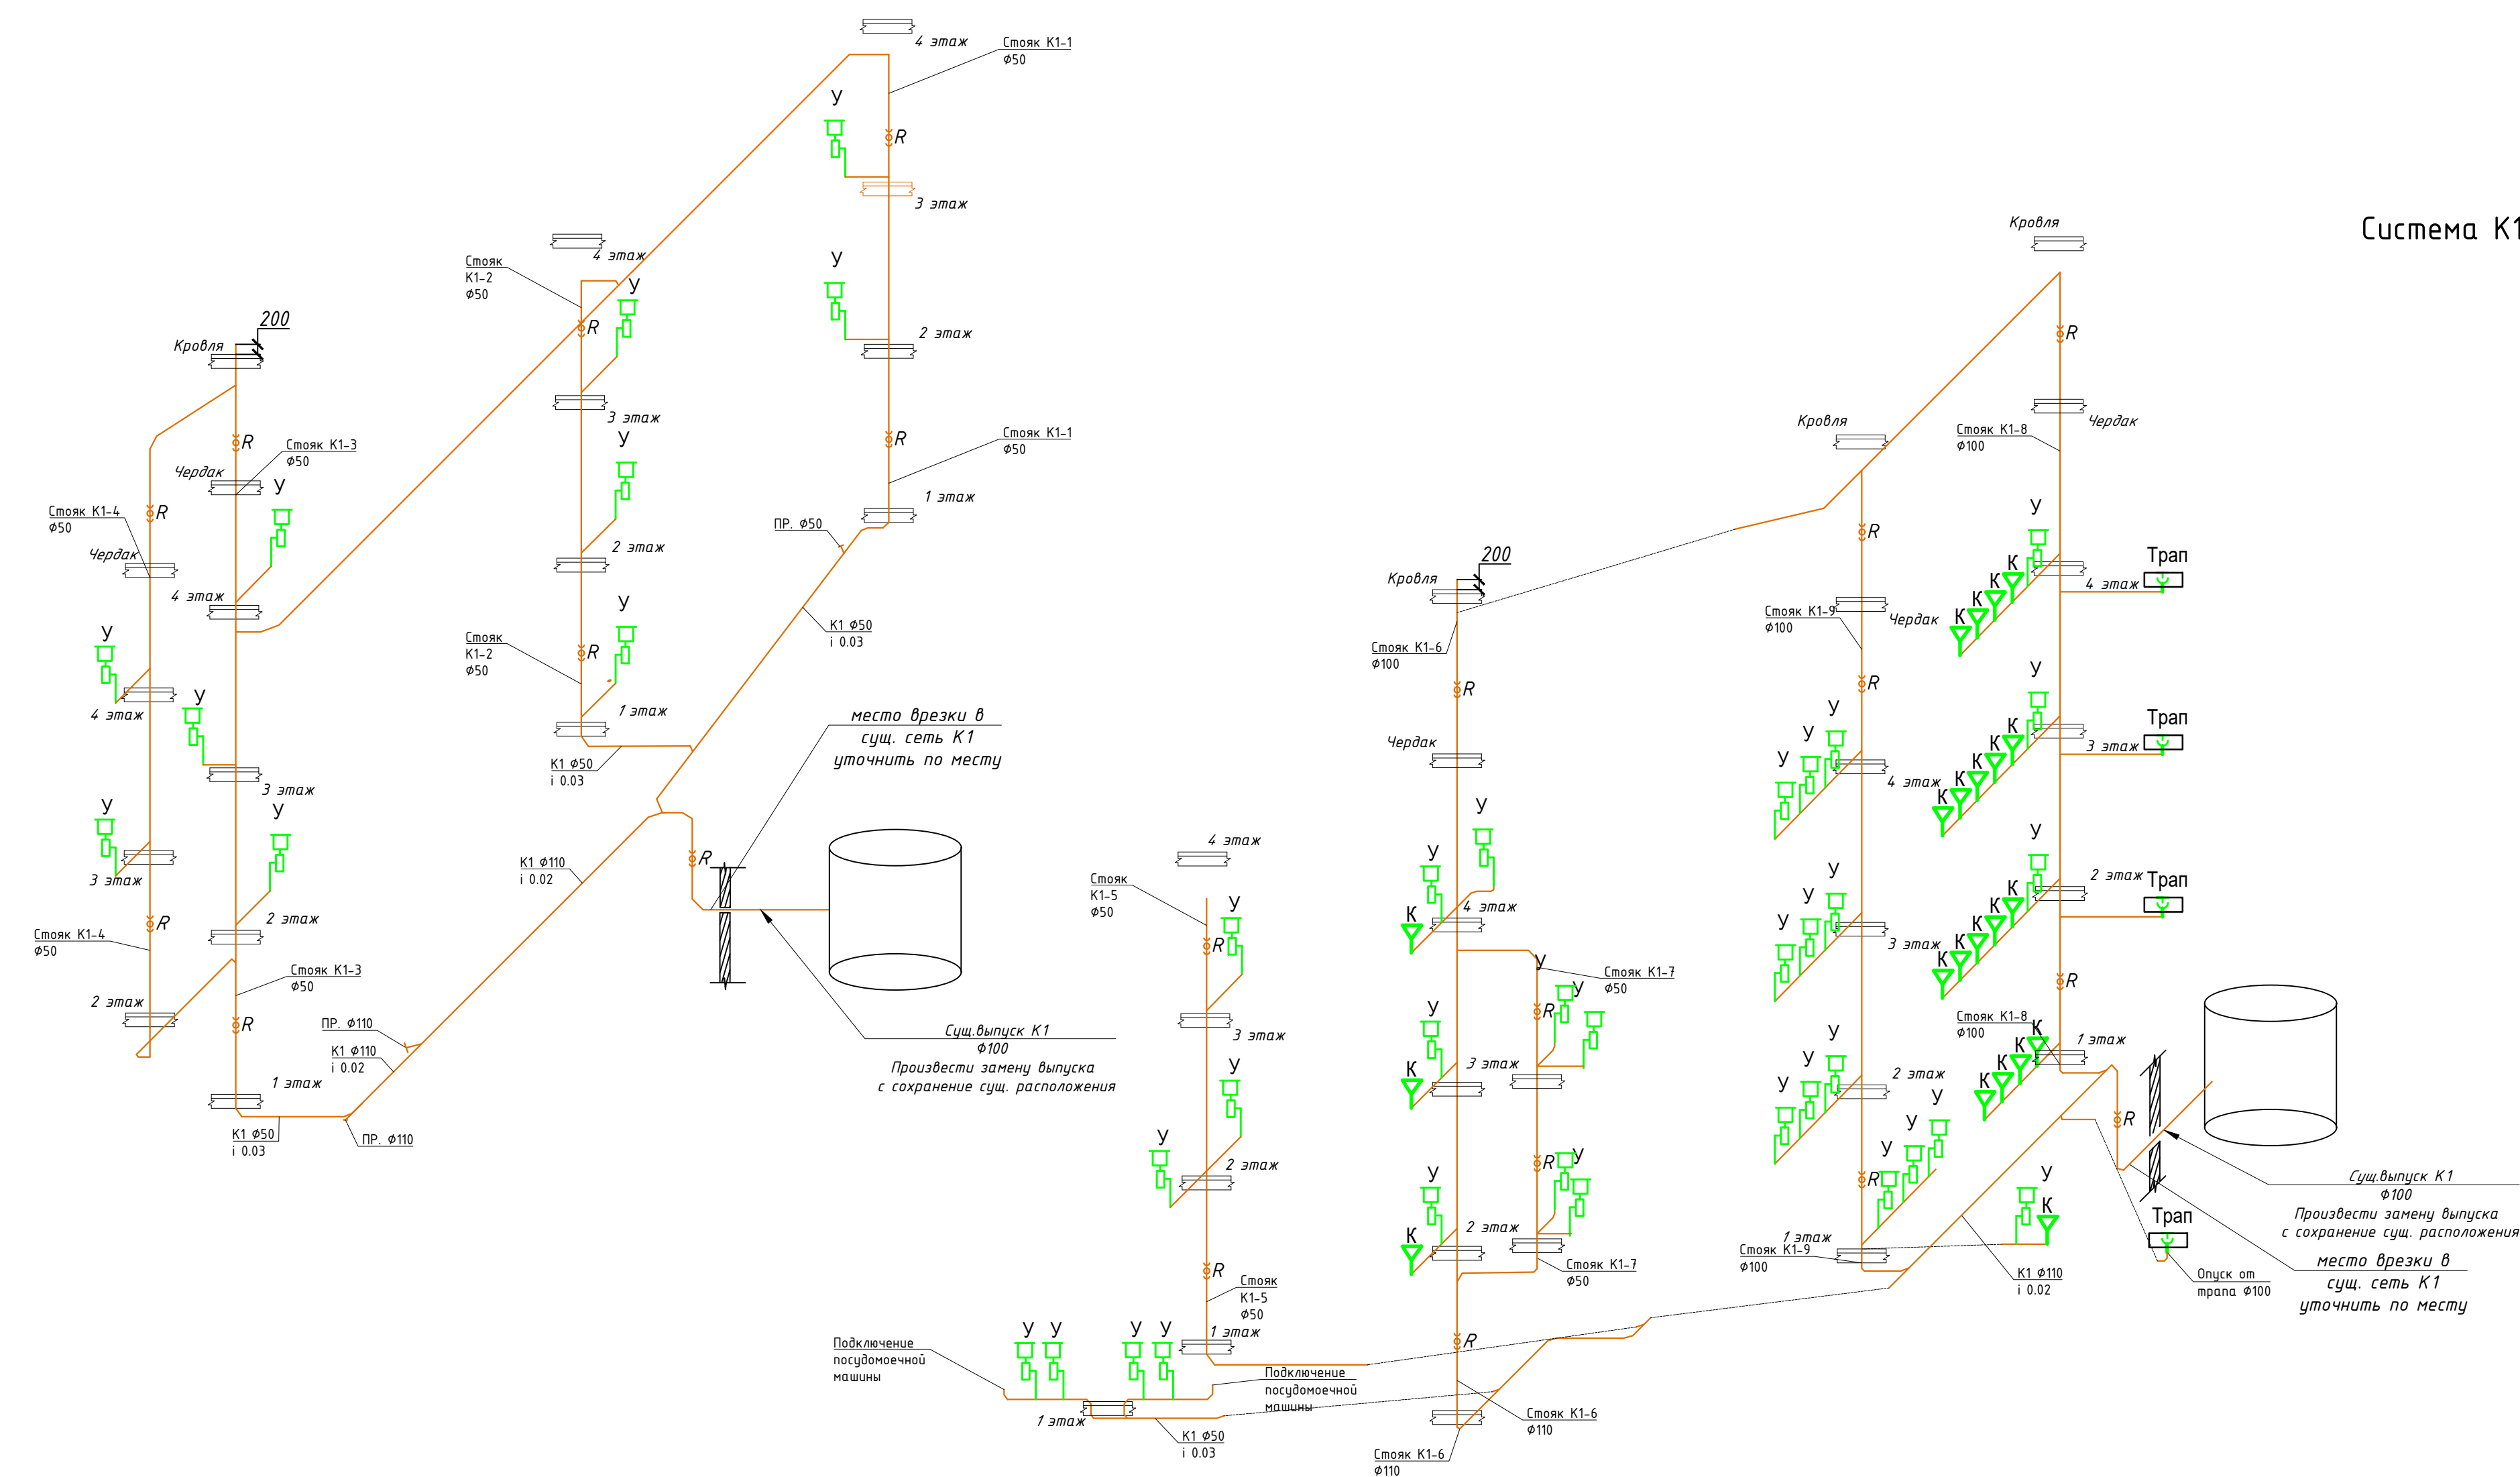


Система К4н


Система К3

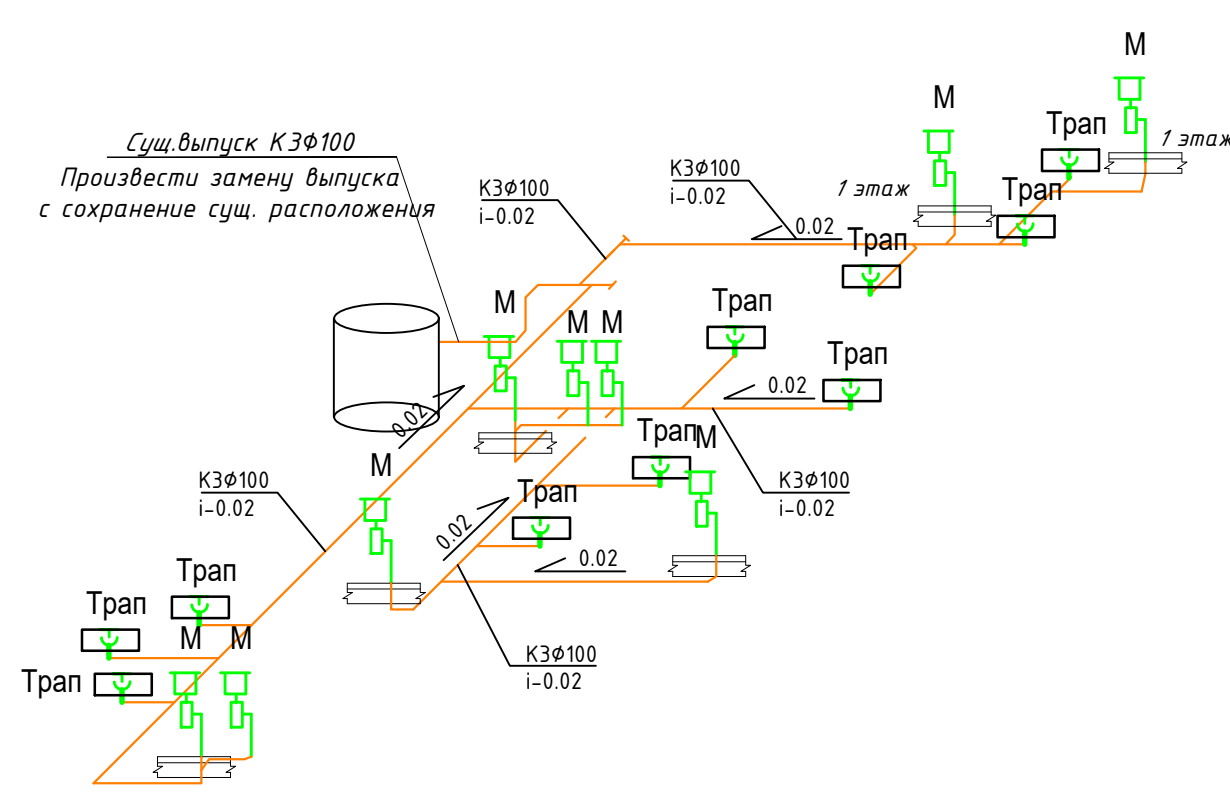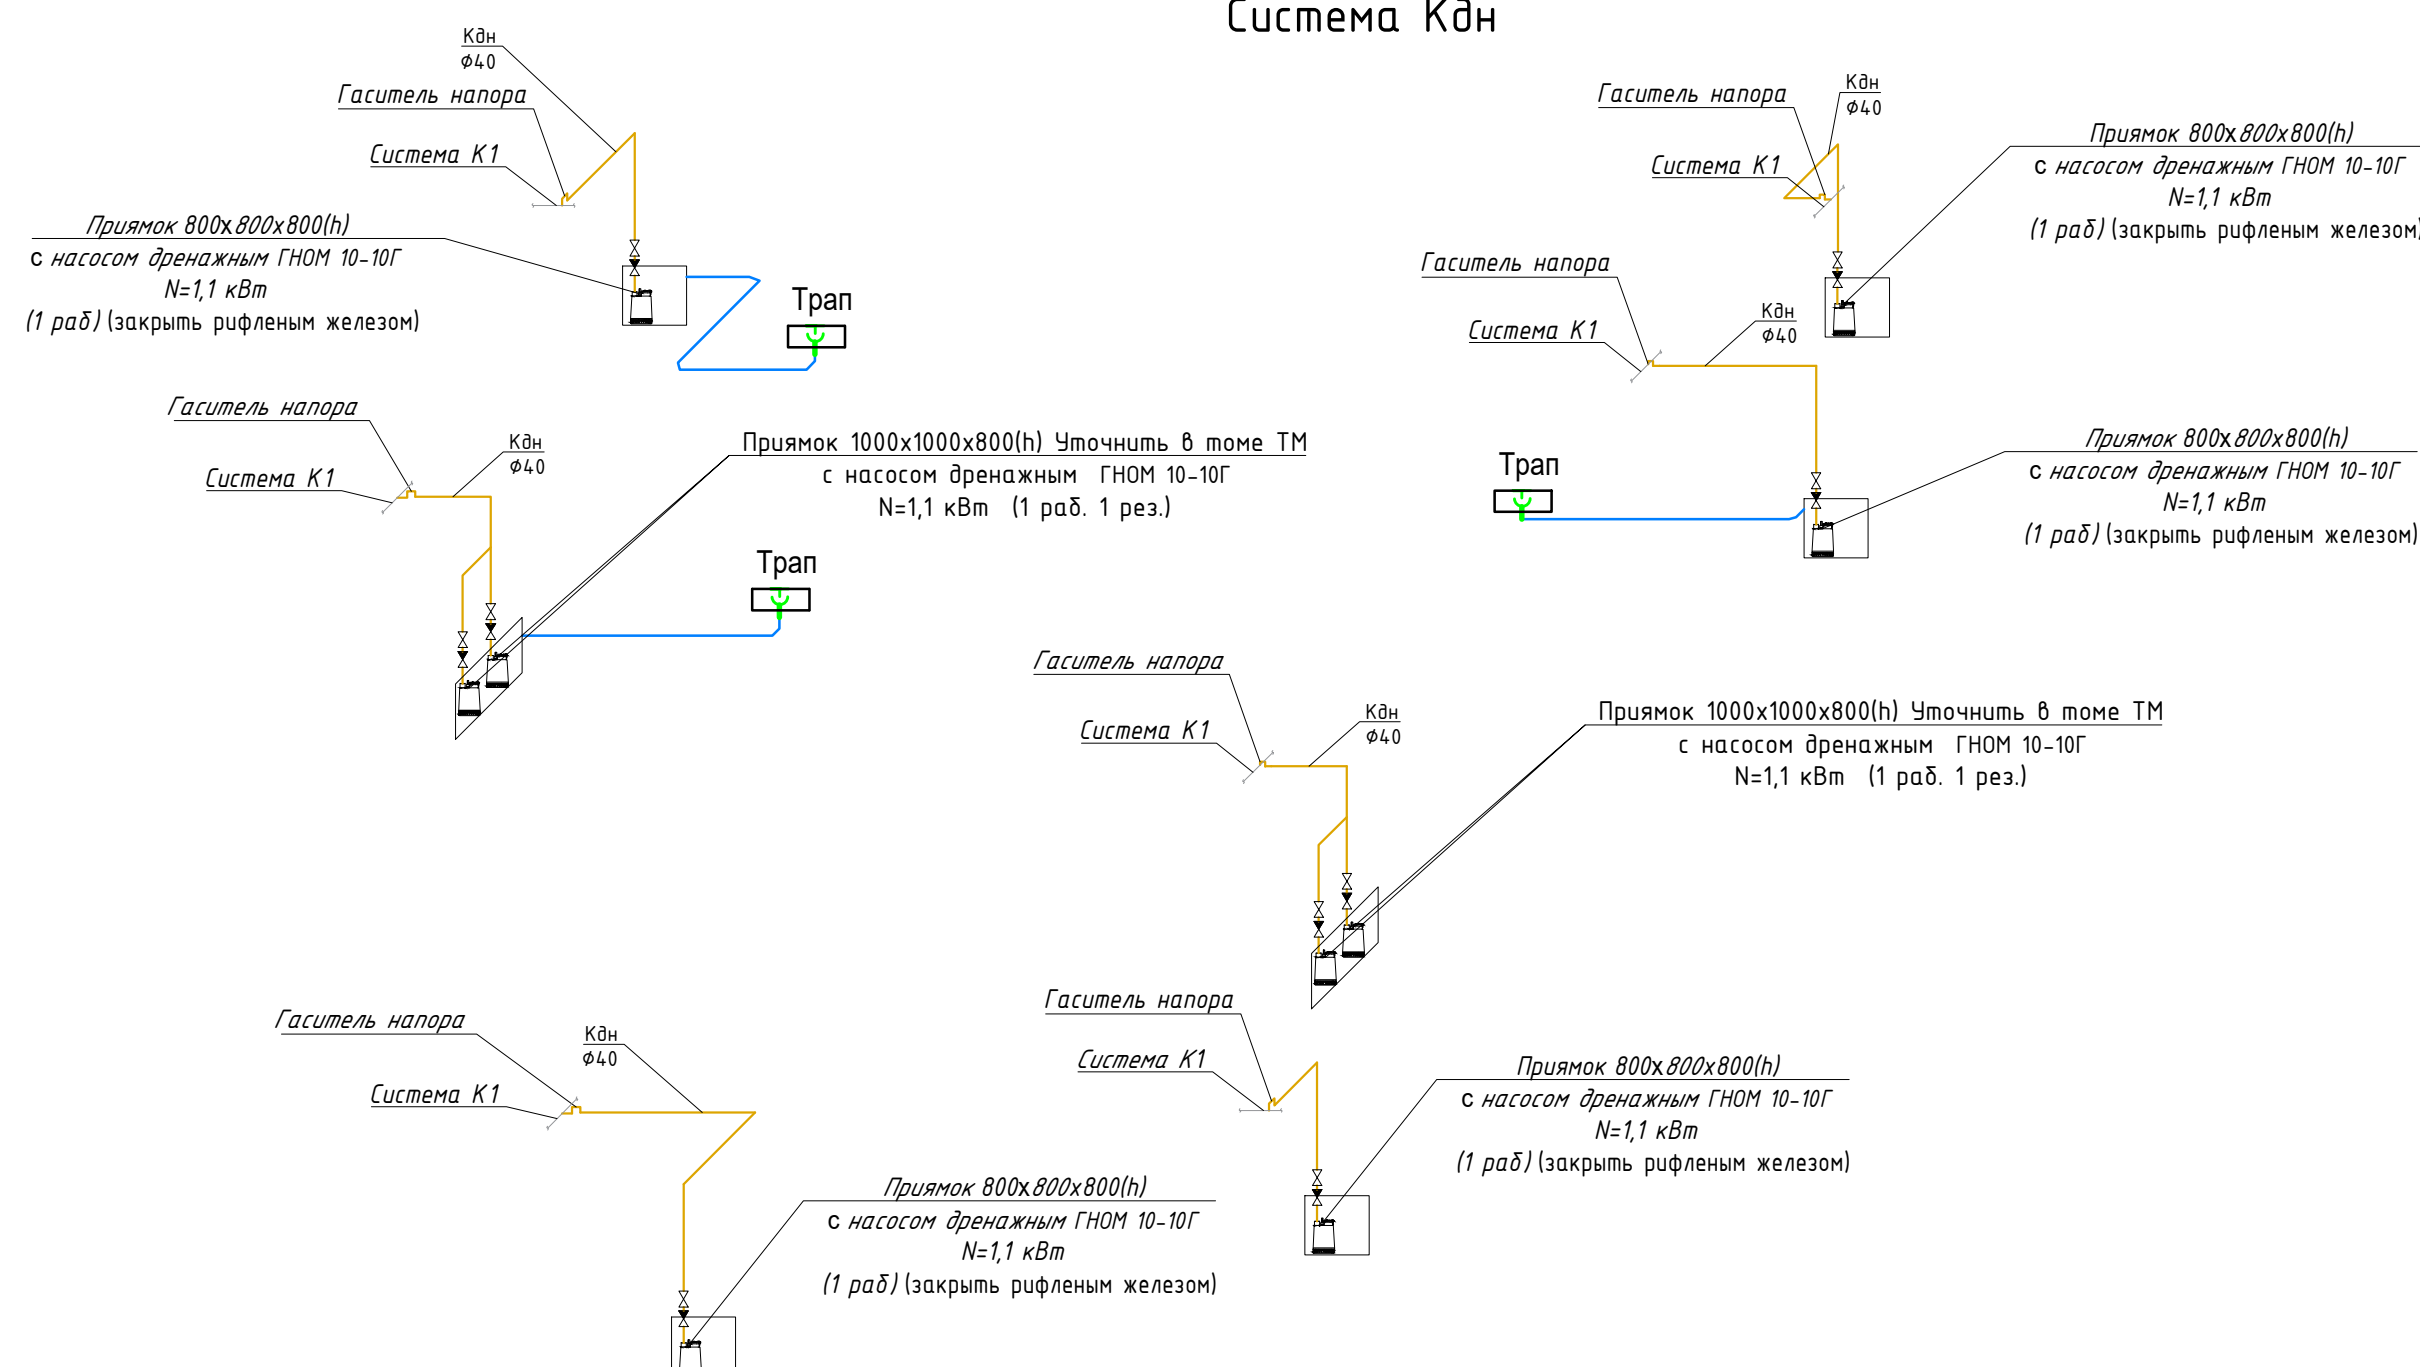

Типовой узел прохода трубопровода через перекрытие

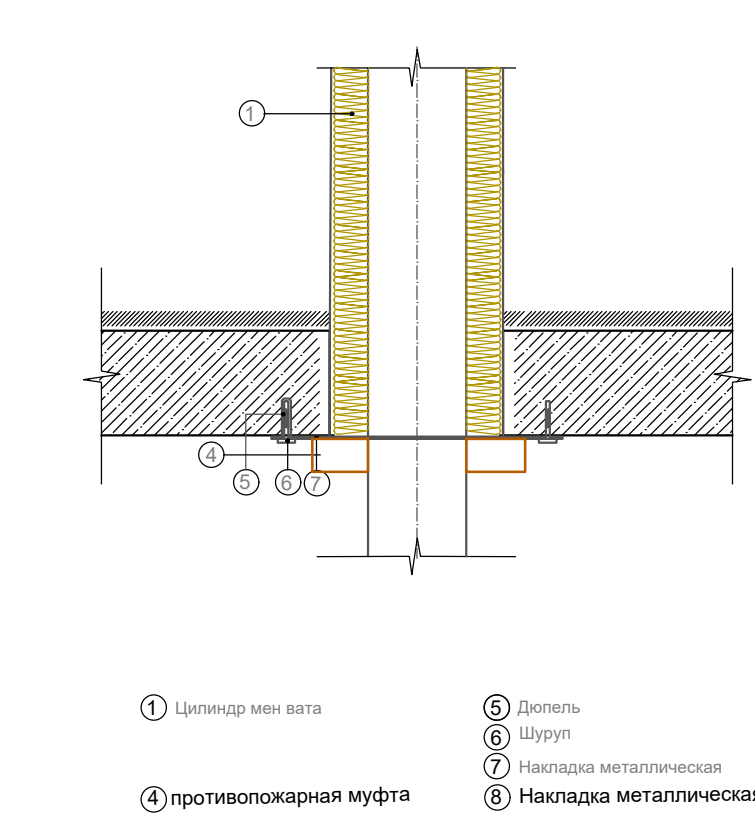


Типовой узел прохода трубопровода через стены

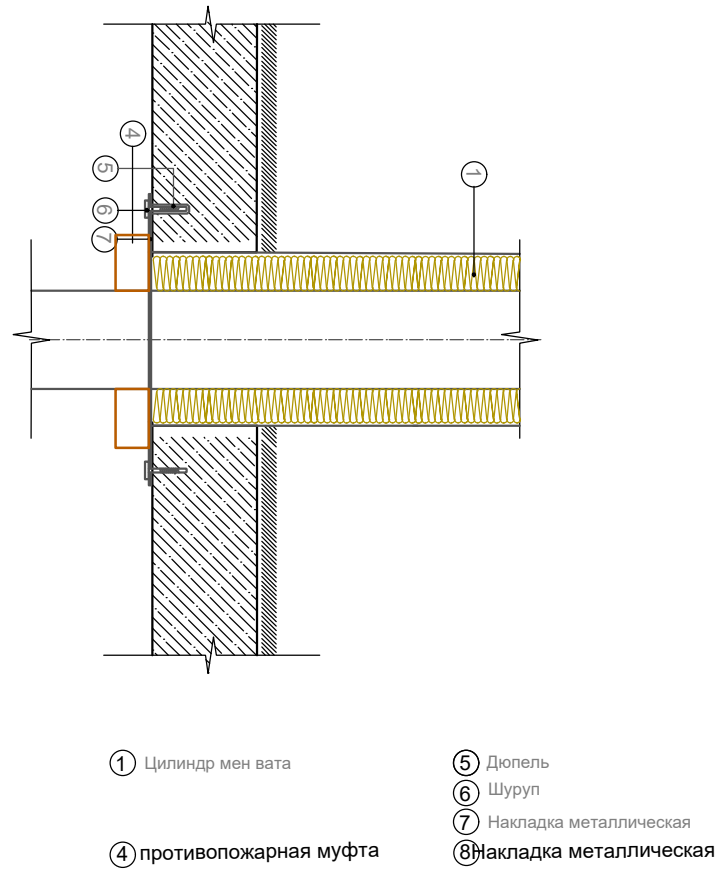


696/П-25-АНО-Р-ВК									
Капитальный ремонт государственного бюджетного общеобразовательного учреждения «Школа №1082 "Сокольники" по адресу: г. Москва, ул. Бардымова, д. 1, корп. 1									
Изм.	Кол.	Вкл.	М.В.В.	Подпись	Дата	Капитальный ремонт. Система водоотведения			
Разработчик	Д.А.М.	Г.И.П.	Г.И.П.	Г.И.П.	06.26	Схема системы канализации			
Исполнитель	Н.А.В.	И.И.И.	И.И.И.	И.И.И.	06.26	Формат А0			

Крепление трубопровода к стене

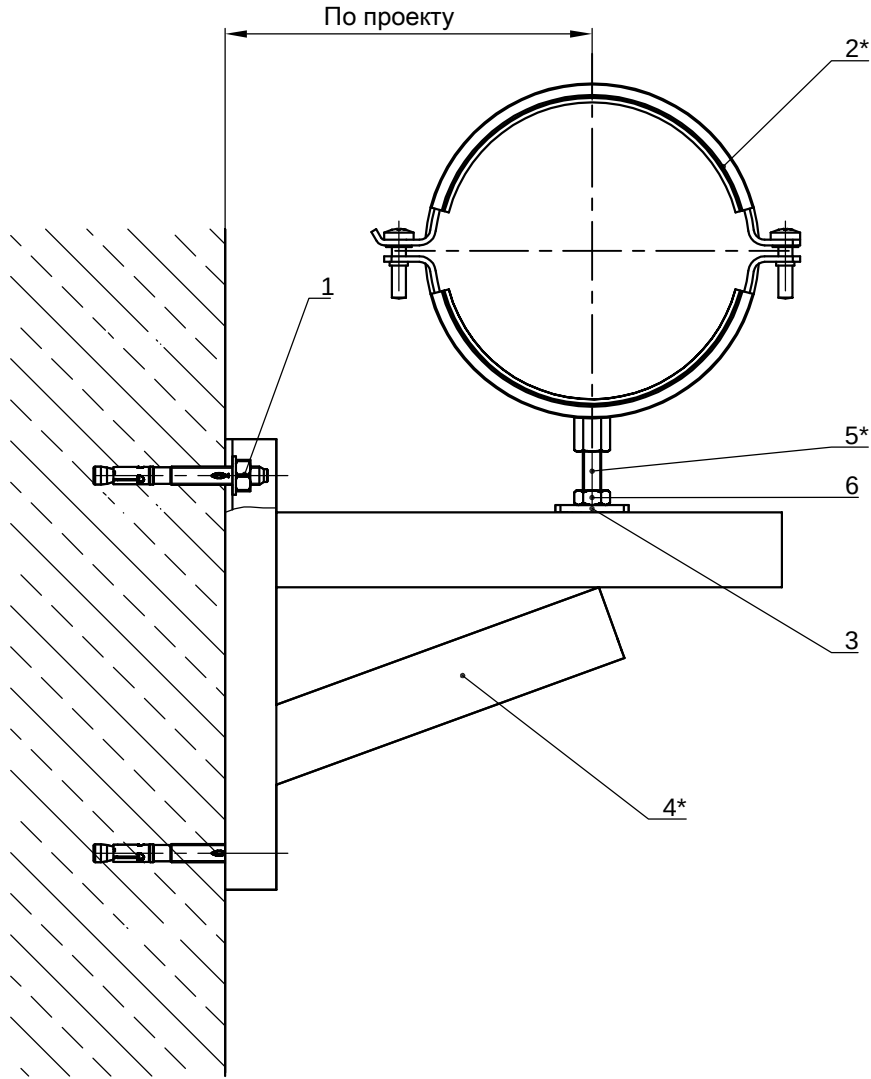

Крепление трубопровода к перекрытию

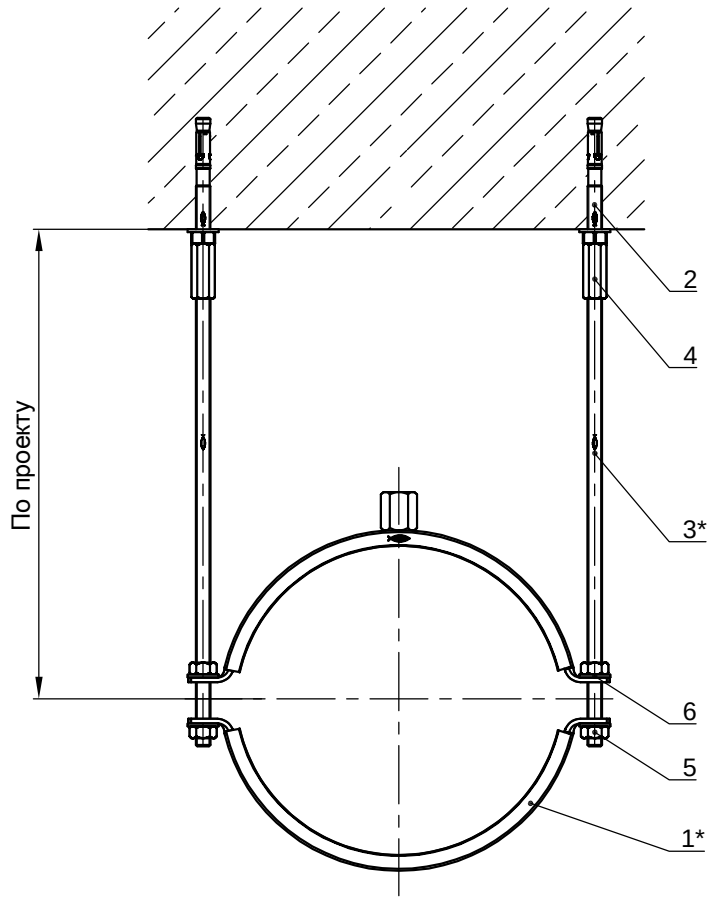

Согласовано			
Взам. инв. №			
Подп. и дата			
Инв. № подл.			

Поз.	Артикул	Наименование	Кол-во, шт
1	94981	Анкерный болт fischer FAZ II 10/10	2
2*		Хомут для трубопроводов fischer FRSM	1
3	504346	Гайка FCN Clix M 10	1
4*		Консоль fischer FCAM	1
5*		Шпилька резьбовая fischer G 10	1
6	79735	Гайка шестигранная fischer MU M10	1

Поз.	Артикул	Наименование	Кол-во, шт
1*		Хомут для трубопровода fischer FRSM	1
2	94871	Анкерный болт fischer FAZ II 8/10	2
3*		Шпилька fischer G8	2
4	79690	Муфта соединительная fischer VM M8	2
5	79734	Гайка шестигранная fischer MU M8	4
6	91477	Шайба fischer U 8x17	4

						696/П-25-АНО-Р-ВК			
						Капитальный ремонт Государственного бюджетного общеобразовательного учреждения города Москвы "Школа №1282 "Сокольники" по адресу: г. Москва, ул. Барболина, д.1, корп.1			
Изм.	Кол.уч.	Лист	№ док.	Подпись	Дата	Капитальный ремонт	Стадия	Лист	Листов
Разработал		Брусникин			06.26		Р	17	
ГИП		Гулько			06.26				
						Схема крепления труб канализации			
Н.контроль		Гулько			06.26				

Схема установки умывальника
Тип 1



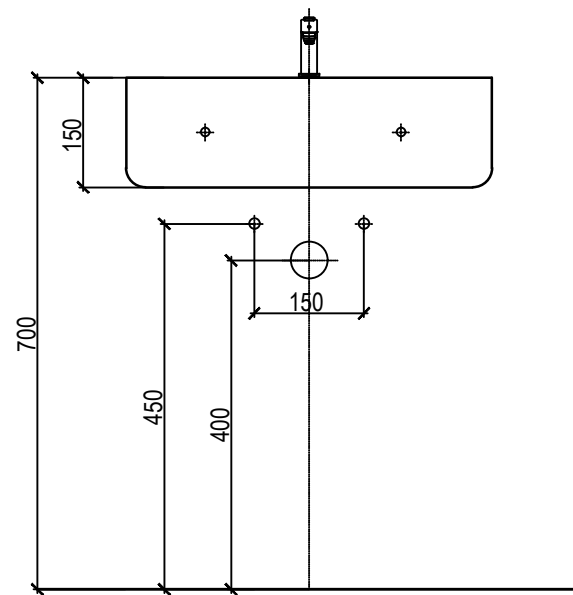


Схема установки умывальника
Тип 2

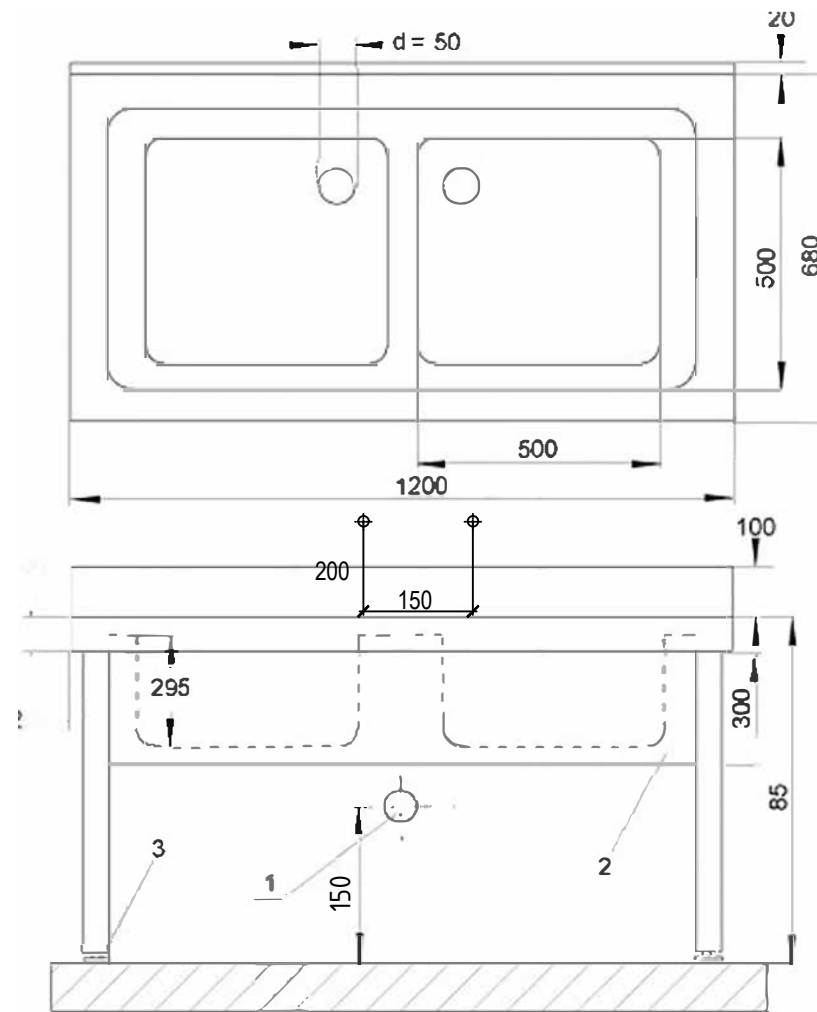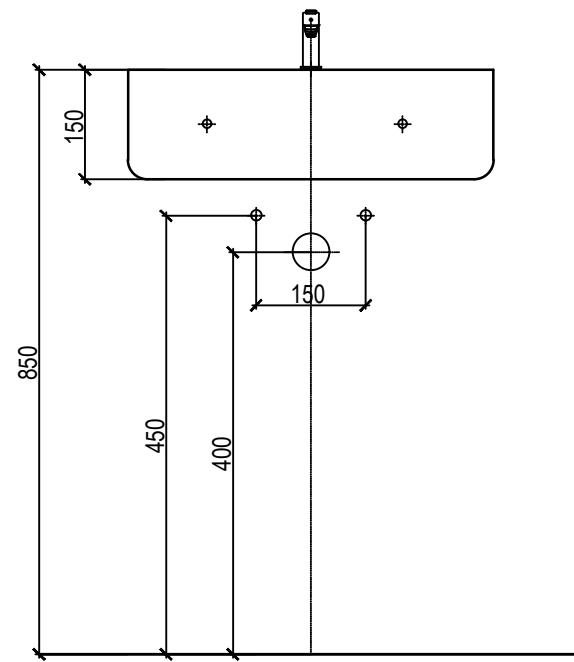

- 1 - отток
- 2 - облицование
- 3 - регулировочные винты



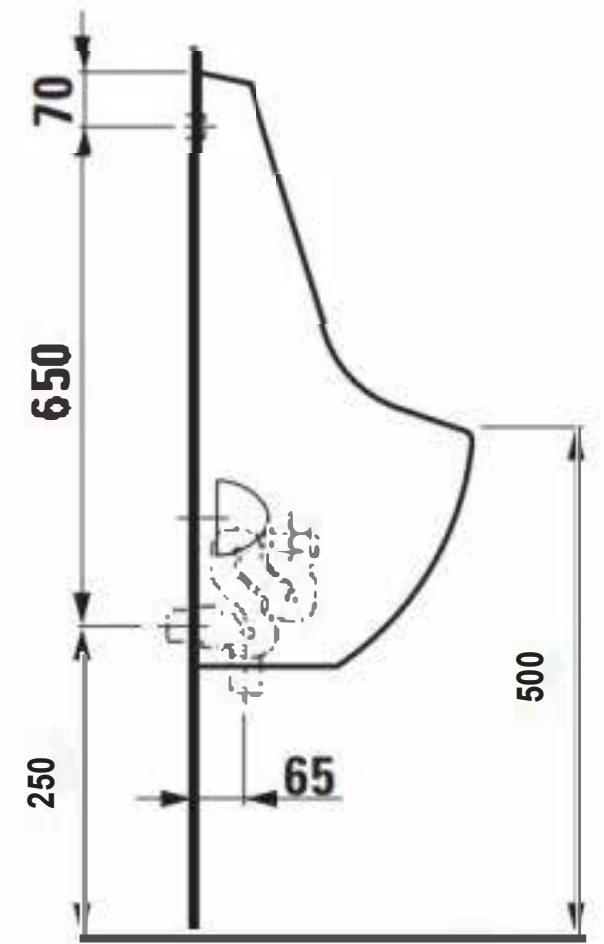


Схема установки Раковина
индивидуального изготовления
искусственный камень
Тип 3

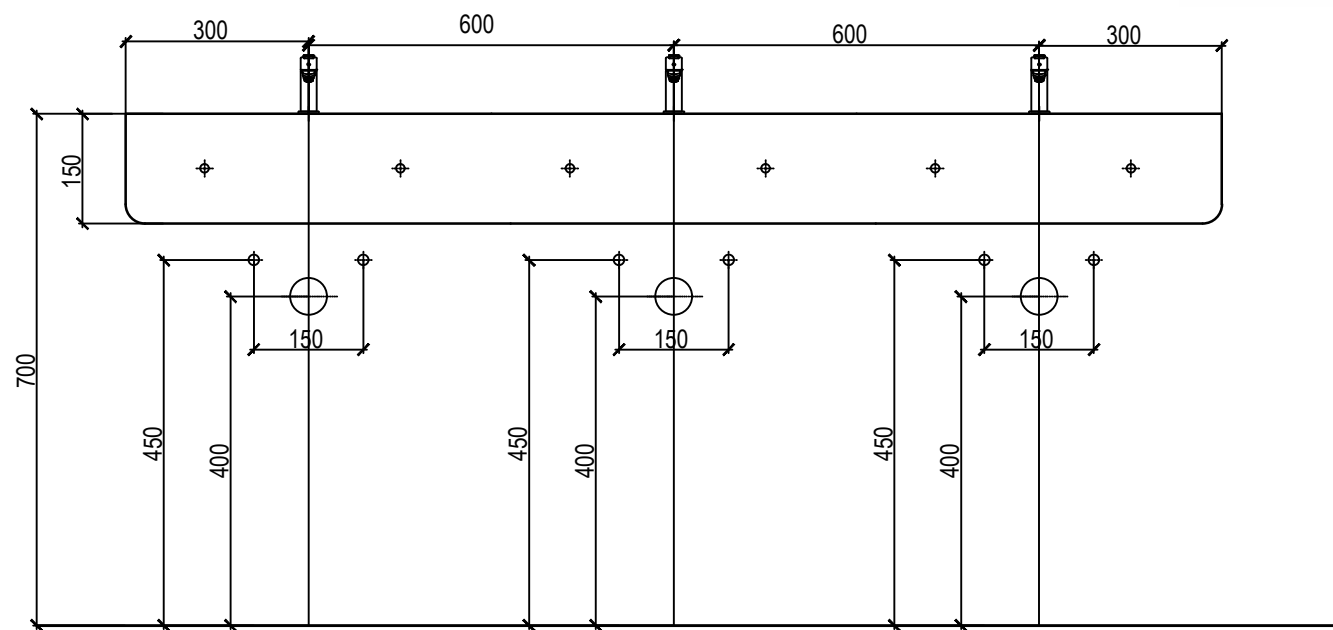

Подключения для Модуля кухонного

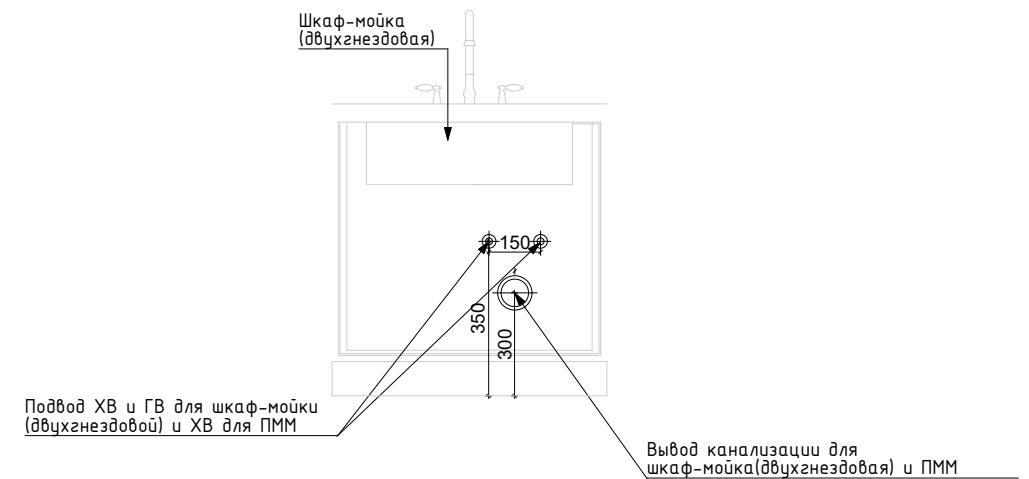


Примечание:

- 1. Душевой смеситель ставится на высоте 1500 мм
- 2. Унитаз на высоте 380 мм до кромки унитаза
- Высоту сантехприборов применять согласно "СП 73.13330.2016. СНиП 3.05.01-85. Свод правил. Внутренние санитарно-технические системы зданий"


Изм.	Кол.уч.	Лист	№	Подп.	Дата

696/П-25-АНО-Р-ВК

План

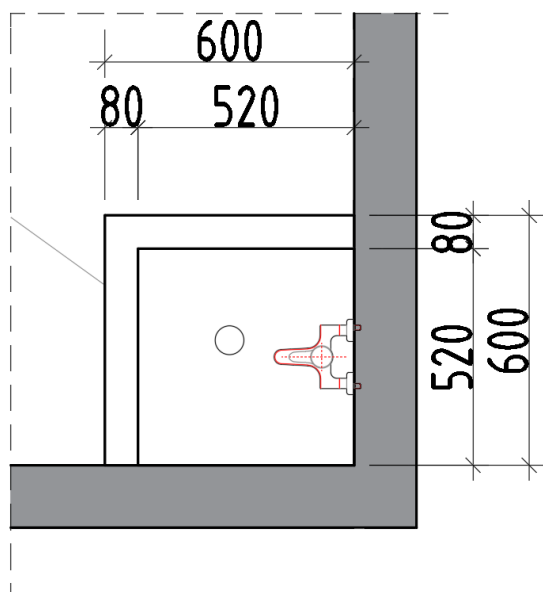

Вид сбоку

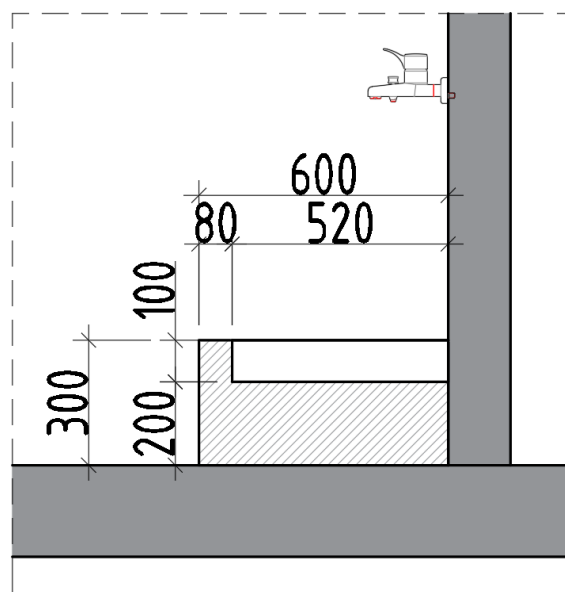

Поз.	Наименование и техническая характеристика	Тип, марка, обозначение документа, опросного листа	Код продукции	Поставщик	Единица измерения	Кол.	Масса 1 ед., кг	Примечание
	Хозяйственно-питьевой водопровод В1							
	Трубопроводная арматура							
	Кран шаровый латунный полнопроходной ВР/ВР: 1/2" (Ø15)	11Б27п Ду15		VALFEX (Россия)	шт.	129		
	Кран шаровый латунный полнопроходной ВР/ВР: 3/4" (Ø20)	11Б27п Ду20		VALFEX (Россия)	шт.	30		
	Кран шаровой латунный полнопроходный ВР/ВР: 1" (Ø25)	11Б27п Ду25		VALFEX (Россия)	шт.	2		
	Кран шаровой латунный полнопроходный ВР/ВР: (Ø32)	11Б27п Ду32		VALFEX (Россия)	шт.	4		
	Кран шаровой латунный полнопроходный ВР/ВР: (Ø50)	11Б27п Ду50		VALFEX (Россия)	шт.	1		
	Подводка для воды (гайка-гайка 1/2; 100 см;(к унитазу и писсуару)	04806		AQUALINE	шт.	44		
	Кран поливочный со штуцером для присоединения шланга, Ø25	BVR-VR Ду25		Ридан	шт.	4		
	Клапан обратный латунный 1/2"	VF.161.N.012		VALFEX (Россия)	шт.	18		
	Клапан обратный латунный 3/4"	VF.161.N.034		VALFEX (Россия)	шт.	78		
	Автоматический воздухоотводчик Ду15	VF.502.NV.04		VALFEX (Россия)	шт.	17		
	Трубопроводы							
	Трубы стальные водогазопроводные оцинкованные обыкновенные Ду20	ГОСТ 3262-75			м.п.	200		
	Трубы стальные водогазопроводные оцинкованные обыкновенные Ду25	ГОСТ 3262-75			м.п.	36		
	Трубы стальные водогазопроводные оцинкованные обыкновенные Ду32	ГОСТ 3262-75			м.п.	110		

Примечание:

						696/П-25-АНО-Р-ВК.СО			
						Капитальный ремонт Государственного бюджетного общеобразовательного учреждения города Москвы "Школа №1282 "Сокольники" по адресу: г. Москва, ул. Барболина, д.1, корп.1			
Изм.	Кол.уч	Лист	№ док	Подп.	Дата				
Разработал	Брицникин				06.26	Стадия		Лист	Листов
ГИП		Гулько			06.26	Р		1	4
Н.контроль	Гулько				06.26	Спецификация оборудования, изделий и материалов			

Согласовано	Взам. Инв. №	Подп. и дата	Инв. № Подл.	Поз.	Наименование и техническая характеристика	Тип, марка, обозначение документа, опросного листа	Код продукции	Поставщик	Единица измерения	Кол.	Масса 1 ед., кг	31 Примечание			
					Трубы стальные водогазопроводные оцинкованные обыкновенные Ду40	ГОСТ 3262-75			м.п.	23					
					Трубы стальные водогазопроводные оцинкованные обыкновенные Ду50	ГОСТ 3262-75			м.п.	56					
					Трубопровод из полипропилена, армированный стекловолокном PP-R SDR7,4 (PN20) Ø 20x2,8	ГОСТ 32415-2013		VALFEX (Россия)	м.п.	210		включая фасонные части			
					Трубопровод из полипропилена, армированный стекловолокном PP-R SDR7,4 (PN20) Ø 25x2,5	ГОСТ 32415-2013		VALFEX (Россия)	м.п.	88		включая фасонные части			
					Трубопровод из полипропилена, армированный стекловолокном PP-R SDR7,4 (PN20) Ø 32x4,4	ГОСТ 32415-2013		VALFEX (Россия)	м.п.	10		включая фасонные части			
					Трубы стальные водогазопроводные оцинкованные обыкновенные Ду65	ГОСТ 3262-75			м.п.	8					
					Трубы стальные водогазопроводные оцинкованные обыкновенные Ду100	ГОСТ 3262-75			м.п.	15					
					Трубопроводная теплоизоляция, δ=9 мм, для труб Ду20	K-flex ST 09x020	K-flex-трубка	«K-flex»	м.п.	200					
					Трубопроводная теплоизоляция δ=9 мм, для труб Ду25	K-flex ST 09x025	K-flex-трубка	«K-flex»	м.п.	36					
					Трубопроводная теплоизоляция δ=9 мм, для труб Ду32	K-flex ST 09x032	K-flex-трубка	«K-flex»	м.п.	110					
					Трубопроводная теплоизоляция δ=9 мм, для труб Ду40	K-flex ST 09x040	K-flex-трубка	«K-flex»	м.п.	23					
					Трубопроводная теплоизоляция δ=9 мм, для труб Ду50	K-flex ST 09x050	K-flex-трубка	«K-flex»	м.п.	56					
					Трубопроводная теплоизоляция δ=9 мм, для труб Ду65	K-flex ST 09x050	K-flex-трубка	«K-flex»	м.п.	8					
					Трубопроводная теплоизоляция δ=9 мм, для труб Ду100	K-flex ST 09x050	K-flex-трубка	«K-flex»	м.п.	15					
					Шаровый кран с электроприводом ду 20				шт.	2					
					Водопровод горячей воды с циркуляцией – Т3, Т4										
					Трубопроводная арматура										
					Кран шаровый латунный полнопроходной ВР/ВР: 1/2" (Ø15)	11Б27п Ду15		VALFEX (Россия)	шт.	71					
					Кран шаровой латунный полнопроходный ВР/ВР: 3/4" (Ø20)	11Б27п Ду20		VALFEX (Россия)	шт.	45					
					Кран шаровой латунный полнопроходный ВР/ВР: 1" (Ø25)	11Б27п Ду25		VALFEX (Россия)	шт.	7					
					Кран шаровой латунный полнопроходный ВР/ВР: 1 1/4" (Ø32)	11Б27п Ду32		VALFEX (Россия)	шт.	4					
					Клапан балансировочный, ручной Ду20	MSV-BD Ду20		Ридан	шт.	10					
					Клапан балансировочный, ручной Ду25	MSV-BD Ду25		Ридан	шт.	4					
					Термостатический смесительный клапан/смеситель 1/2"	TMV811-02		TIM	шт.	30					
	Термостатический смесительный клапан/смеситель 3/4"	TMV811-03		Zeissler	шт.	10									
	Клапан обратный латунный 1/2"	VF.161.N.012		VALFEX (Россия)	шт.	78									
	Клапан обратный латунный 3/4"	VF.161.N.034		VALFEX (Россия)	шт.	18									
							Изм.	Кол.уч	Лист	№	Подп.	Дата	696/П-25-АНО-Р-ВК.СО	Лист	
															2

Согласовано	Взам. Инв. №	Подп. и дата	Инв. № Подл.	Поз.	Наименование и техническая характеристика	Тип, марка, обозначение документа, опросного листа	Код продукции	Поставщик	Единица измерения	Кол.	Масса 1 ед., кг	Примечание		
					Автоматический воздухоотводчик Ду15	VF.502.NV.04		VALFEX (Россия)	шт.	34				
					Трубопроводы									
					Трубы стальные водогазопроводные оцинкованные обыкновенные Ду20	ГОСТ 3262-75			м.п.	246				
					Трубы стальные водогазопроводные оцинкованные обыкновенные Ду25	ГОСТ 3262-75			м.п.	154				
					Трубы стальные водогазопроводные оцинкованные обыкновенные Ду32	ГОСТ 3262-75			м.п.	189				
					Трубы стальные водогазопроводные оцинкованные обыкновенные Ду50	ГОСТ 3262-75			м.п.	80				
					Трубопровод из полипропилена, армированный стекловолокном PP-R SDR7,4 (PN20) Ø 20x3,4	ГОСТ 32415-2013		VALFEX (Россия)	м.п.	180		включая фасонные части		
					Трубопровод из полипропилена, армированный стекловолокном PP-R SDR7,4 (PN20) Ø 25x4,2	ГОСТ 32415-2013		VALFEX (Россия)	м.п.	68		включая фасонные части		
					Трубопровод из полипропилена, армированный стекловолокном PP-R SDR7,4 (PN20) Ø 32x4,4	ГОСТ 32415-2013		VALFEX (Россия)	м.п.	10		включая фасонные части		
					Материалы									
					Трубопроводная теплоизоляция, δ=13 мм для труб Ду20	K-flex ST 13x020	K-flex-трубка	«K-flex»	м.п.	478				
					Трубопроводная теплоизоляция δ=13 мм для труб Ду25	K-flex ST 13x025	K-flex-трубка	«K-flex»	м.п.	163				
					Трубопроводная теплоизоляция δ=13 мм для труб Ду32	K-flex ST 13x032	K-flex-трубка	«K-flex»	м.п.	189				
					Трубопроводная теплоизоляция δ=13 мм для труб Ду50	K-flex ST 13x050	K-flex-трубка	«K-flex»	м.п.	80				
					Крепления									
					Металлоконструкции для крепления стальных трубопроводов				кг	190				
					Комплект крепления для полипропиленовых труб									
					Ø20x2,8	9000000020		Политэк	шт.	210				
					Ø25x3,5	9000000025		Политэк	шт.	110				
					Ø32x4,4	9000000032		Политэк	шт.	10				
					Санитарно-техническое оборудование									
					Душевая стойка для подачи воды, хром глянec, комплектно с монтажная часть ole для душевого гарнитура, хром и встроенный однорычажный смеситель для душа с переключателем на два потока, хром глянec	69356KM.21.018 2299KM.21.018 69370KM.21.018		Керама Марацци (Россия)	шт	6		или аналог		
							Изм.	Кол.уч	Лист	№	Подп.	Дата	696/П-25-АНО-Р-ВК.СО	Лист
														3

[illegible]

Поз.	Наименование и техническая характеристика	Тип, марка, обозначение документа, опросного листа	Код продукции	Поставщик	Единица измерения	Кол.	Масса 1 ед., кг	Примечание
	<u>Канализация бытовая К1, К1Н</u>							
	<u>Сантехническое оборудование</u>							
29.	Унитаз подвесной	PLAZA MODERN		Kerama Marazzi	шт.	35		
30.	Инсталляция для подвесного унитаза, с кнопкой управления для скрытых систем инсталляции, хром-глянец	M101\1120KM+M571KMERN		Kerama Marazzi	шт.	36		
31.	Унитаз подвесной для МГН				шт.	1		
32.	Писсуар подвесной с крепежом, белый глянцевый, комплектно с системой смыва и инсталляцией	PROC.ur.02		Kerama Marazzi	шт.	8		
33.	Инсталляция для подвесного писсуара,с кнопкой смыва				компл.	8		или аналог
34.	Душевой поддон в строительном исполнении	APZ10-750KM		Kerama Marazzi	шт.	12		Закупка ДИОМ
35.	кухонный гарнитур				шт.	3		Закупка ДИОМ
36.	Тумба с раковиной в комплекте с локтевым смесителем				шт.	2		Закупка ДИОМ
37.	Ванна котломоечная двухсекционная					2		Закупка ДИОМ
38.	Ванна моечная односекционная тип 1				шт.	1		Закупка ДИОМ
39.	Ванна моечная двухсекционная тип 1				шт.	1		Закупка ДИОМ
40.	Ванна моечная трехсекционная тип 2				шт.	1		Закупка ДИОМ
41.	Тумба медицинская с двойной мойкой в комплекте с локтевым смесителем				шт.	1		Закупка ДИОМ
42.	Двойная мойка в кабинет врача				шт.	1		Закупка ДИОМ
	Раковина индивидуального изготовления искусственный камень				шт.	9		
	Тумба с раковиной				шт.	25		Закупка ДИОМ
	Рукомойник				шт.	6		
	Раковина мебельная\подвесная 50, белая глянцевая	PRO.WB.50		Kerama Marazzi	шт.	16		
	Раковина для МГН	5289B003-0001		Vitra	шт.	1		

696/П-25-АНО-Р-ВК.СО

Лист

3

Согласовано	
-------------	--	--	

Согласовано	Взам. Инв. №	Подп. и дата	Инв. № Подл.	Поз.	Наименование и техническая характеристика	Тип, марка, обозначение документа, опросного листа	Код продукции	Поставщик	Единица измерения	Кол.	Масса 1 ед., кг	39 Примечание		
					Оборудование									
					Тумба с раковиной			Керама Марацци	шт.	29		Закупка департамента		
					Кухонный гарнитур				шт.	1		Закупка департамента		
					Тумба с раковиной в комплекте с локтевым смесителем				шт.	2		Закупка департамента		
					Тумба медицинская с двойной мойкой в комплекте с локтевым смесителем				шт.	1		Закупка департамента		
					Питьевой фонтанчик				шт.	8		Закупка департамента		
					Двойная мойка в кабинет врача				шт.	1		Закупка департамента		
					Ванна котломоечная двухсекционная				шт.	2		Закупка департамента		
					Ванна моечная односекционная тип 1				шт.	2		Закупка департамента		
					Ванна котломоечная двухсекционная				шт	1		Закупка департамента		
					Ванна моечная двухсекционная тип 1				шт	1		Закупка департамента		
					Ванна моечная трехсекционная тип 2				м.п.	1		Закупка департамента		
					Рукомойник				шт	7		Закупка департамента		
					Смеситель с душирующим устройством				шт	10		Закупка департамента		
					Смеситель для рукомойника				шт	7		Закупка департамента		

						696/П-25-АНО-Р-ВК.СО				Лист
						696/П-25-АНО-Р-ВК.СО				6
Изм.	Кол.уч	Лист	№	Подп.	Дата					

[illegible]


[illegible]

[illegible]

[illegible]

ЛИСТ ПОДБОРА

Насосная установка повышения
давления **ANTARUS X 2**
MLV6-2/01

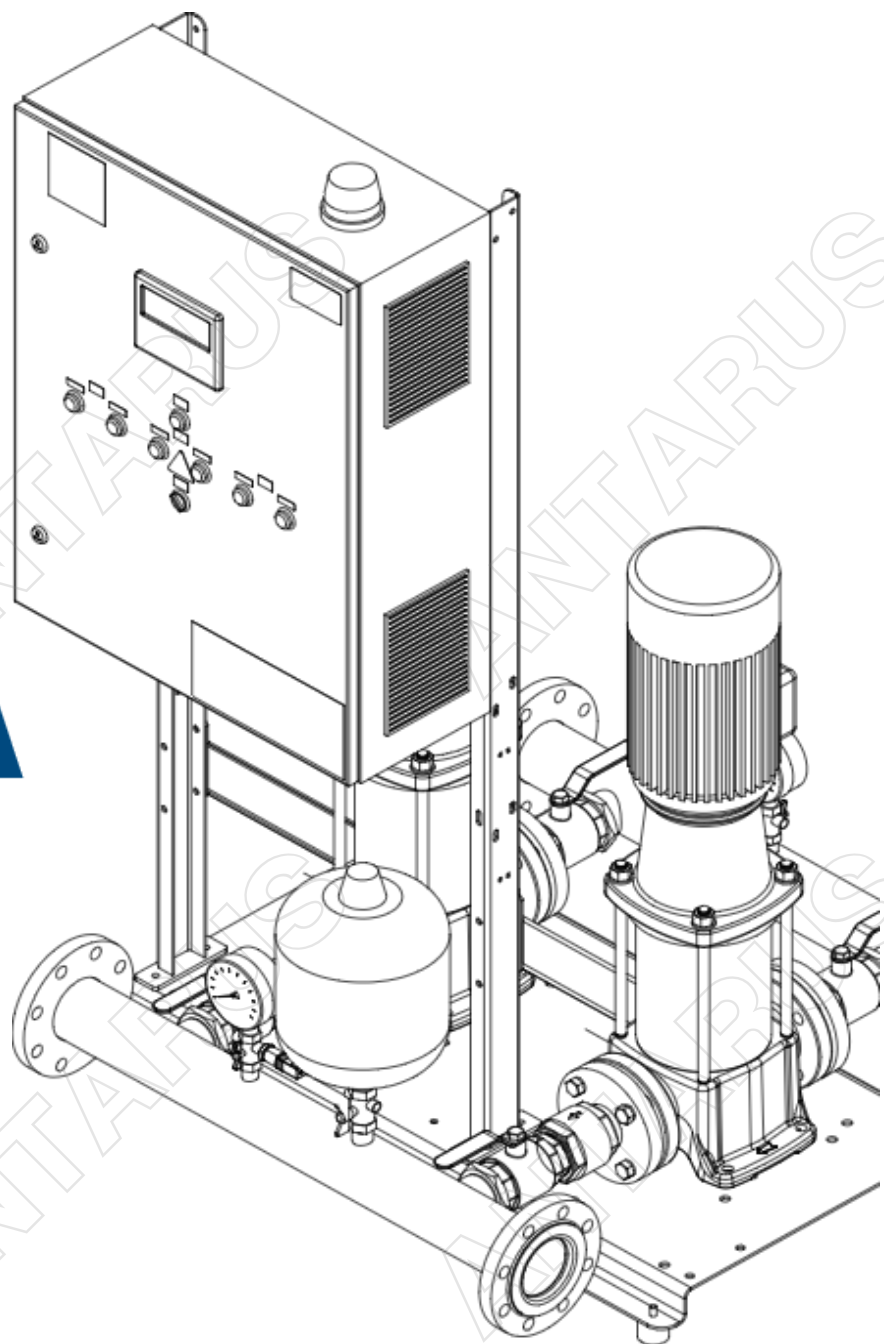

Артикул установки
660416




Онлайн-подбор
установки
по параметрам
за 30 секунд




Гарантия 5 лет
на установки
на насосах
ANTARUS



Производство
стандартных
моделей
2-3 недели

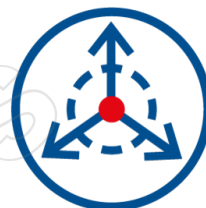

Онлайн-доступ
к BIM-моделям
всех продуктов
ANTARUS

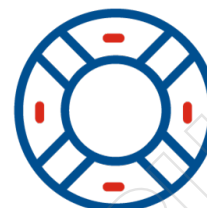



Сервисная
поддержка
по всей
России

*на изображении условно отображена линейка 2.0, чертеж вашей установки см. ниже

Насосная установка повышения давления **ANTARUS X 2 MLV6-2/01**



Артикул: 660416

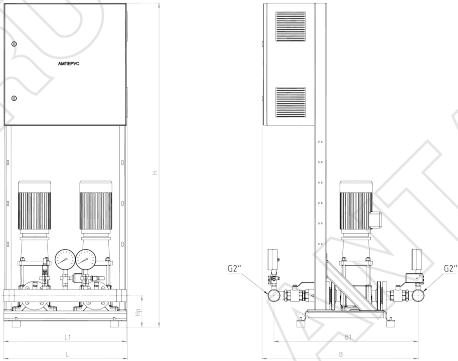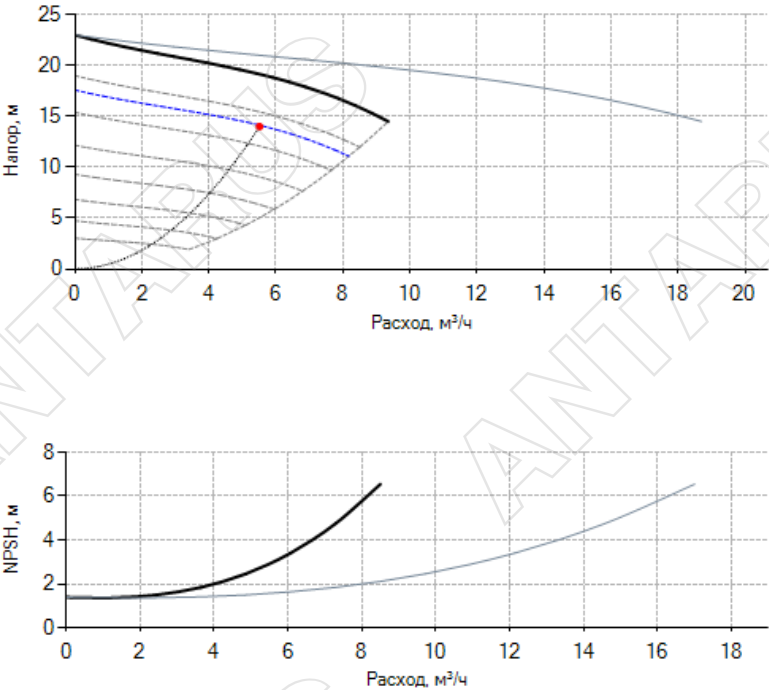

Запрашиваемые параметры:

Расход	5,51 м³/ч
Напор	14 м
Температура воды	0-70 °С

Фактические параметры:

Расход	5,51 м³/ч
Напор	14 м
Частота вращ. э/д	2 789 об/мин
Мощность на валу	0,29 кВт
Макс. уровень шума	53 дБа
Макс. раб. давление	16 бар
NPSH треб.	4,22 м
КПД насоса, %	65,6

Данные электродвигателя (одного):

Ном. мощность	0,55 кВт
Ном.напряжение	3х380 В, 50 гц
Ном. ток	1,24 А

Данные станции:

Вес	111 кг
Подключение	G 2"

Габариты установки:

L	600 мм
L1	600 мм
H	1 590 мм
Hn	154 мм
B	777 мм
B1	659 мм
B2	30 мм

Внимание! Фактические размеры и внешний вид установки могут незначительно отличаться от представленных.

Дополнительно:

№ п/п	Наименование	Количество	Ед. изм.
1	Основной насос ANTARUS MLV6-2/01-14	1	шт.
2	Резервный насос ANTARUS MLV6-2/01-14	1	шт.
3	Датчик давления	1	шт.
4	Манометр	2	шт.
5	Шаровой кран DN 32	4	шт.
6	Клапан обратный DN 32	2	шт.
7	Всасывающий коллектор из нерж. стали AISI 304 G 2"	1	шт.
8	Напорный коллектор из нерж. стали AISI 304 G 2"	1	шт.
9	Комплект виброопор	1	компл.
10	Шкаф управления	1	шт.

Описание

Готовая к подключению установка повышения давления. Комплект поставки:


- многоступенчатые насосы;
- всасывающий и напорный коллекторы из нержавеющей стали;
- рама-основание на регулируемых по высоте виброопорах;
- комплект запорной арматуры на всасывающих и напорных патрубках насосов, обратные клапаны на напорных патрубках;
- манометры, датчик давления, реле давления на всасывающем трубопроводе с диапазоном до 0,8МПа
- защита от «сухого» хода;

Автоматизация насосной станции ANTARUS X. Основные функции

1. Управление в автоматическом режиме 2-6 насосами
2. Поддержание давления при помощи преобразователей частоты и каскадного подключения/отключения насосов с использованием датчика давления
3. Выравнивание моторесурса насосов (ротация)
4. Защита насосов от сухого хода
5. Защита двигателей от перегрева, от перегрузки по току, от некачественного входного напряжения
6. Подключение резервных насосов при аварии основных
7. Удаленная диспетчеризация при помощи стандарта RS-485 по протоколу ModBus RTU



Схема внешних подключений

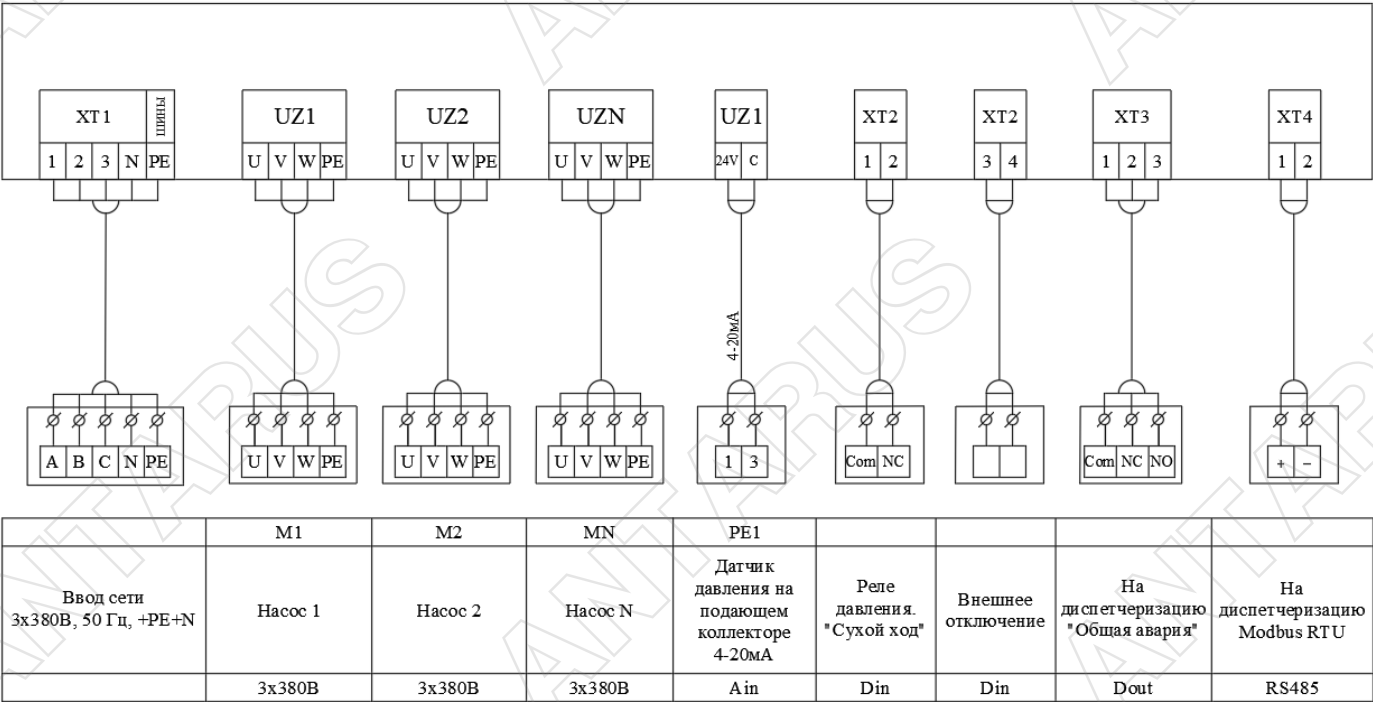



Online подбор за 30 секунд

Программа подбора насосных установок
ANTARUS SEARCH
search.antarus.su



Программа «Умная вода»

Программа для проектирования систем
внутреннего водопровода и канализации зданий
smartwater.su



Online библиотека

Документация, чертежи и модели по всем
продуктам ANTARUS
search.antarus.su/library

**Для консультаций и заказа обращайтесь в ближайшее
к Вам отделение компании «Элита»**

Москва
(495) 725-09-52

Екатеринбург
(343) 287-05-90

Омск
(3812) 50-21-48

Тюмень
(3452) 50-01-77

Санкт-Петербург
(812) 702-42-42

Иркутск
(914) 910-17-03

Пермь
(342) 254-55-76

Уфа
(347) 287-81-89

Архангельск
(911) 270-63-74

Казань
(843) 570-54-54

Ростов-на-Дону
(863) 206-16-26

Хабаровск
(4212) 75-50-95

Барнаул
(3852) 28-38-01

Краснодар
(861) 277-46-99

Самара
(846) 372-38-83

Челябинск
(351) 268-92-05

Владивосток
(4232) 79-00-79

Красноярск
(391) 274-60-02

Саратов
(8452) 57-69-83

Ярославль
(4852) 58-30-51

Волгоград
(8442) 26-00-01

Нижний Новгород
(831) 220-24-33

Сургут
(3462) 28-11-71

Воронеж
(473) 258-95-17

Новосибирск
(383) 354-05-34

Тверь
(4822) 65-50-19