

109548, г. Москва, Муниципальный Округ Печатники, ул. Шоссейная, д. 19, к. 1,
кв.117 e-mail PROEKTplus-work@yandex.ru

Свидетельство № СРО- П-110-009723217107-0532

СОГЛАСОВАНО:
Главный инженер
АО «МосводоканалСтройТрест»

_____ А.А. Вешкин

«__» _____ 2026г

**Капитальный ремонт Государственного Бюджетного
Общеобразовательного Учреждения города Москвы
«Школа № 1282 «Сокольники»
по адресу: г. Москва, ул. Барболина, д. 1, корп. 1
1 этап**

РАБОЧАЯ ДОКУМЕНТАЦИЯ

Основной комплект рабочих чертежей

Система водоснабжения и
канализации.

696/П-24-АНО-Р-ВК

Генеральный директор

Главный инженер проекта



Н.А. Выходова

А.Н. Гулько

2026

Име. № подл.	
Подп. И дата	
Взам. инв. №	

Экспликация помещений подвала

Номер помеще-ния	Наименование	Площадь, м ²	Кат. поме-ще-ния
001	Техническая лестница	13,7	
001а	Тамбур-шлюз 1-го типа	4,9	
002	Техническая лестница	9,8	
002а	Тамбур-шлюз 1-го типа	5,0	
003	Спортивный зал	262,5	
004	Снарядная	10,1	B3
005	ПУИ	3,5	
006	Снарядная	28,0	B3
007	Коридор	21,0	
008	Коридор	17,9	
009	Кладовая	21,4	B3
010	Венткамера	Не окружено	B4
011	Форкамера	Не окружено	B4
012	Форкамера	3,8	B4
013	Венткамера	37,5	B4
014	Коридор	63,3	
015	Коридор	9,8	
016	Коридор	19,3	
017	Коридор	8,3	
018	Насосная	14,8	B4
019	Венткамера	19,3	B4
020	Форкамера	5,2	B4
021	ИТП	75,6	Д
022	Венткамера	4,1	B4
ИТОГО:		695,8	


Условные обозначения

- В1

Проектируемый хозяйственно-питьевой водопровод
- Т3

Поданный трубопровод горячего водоснабжения
- Т4

Циркуляционный трубопровод горячего водоснабжения

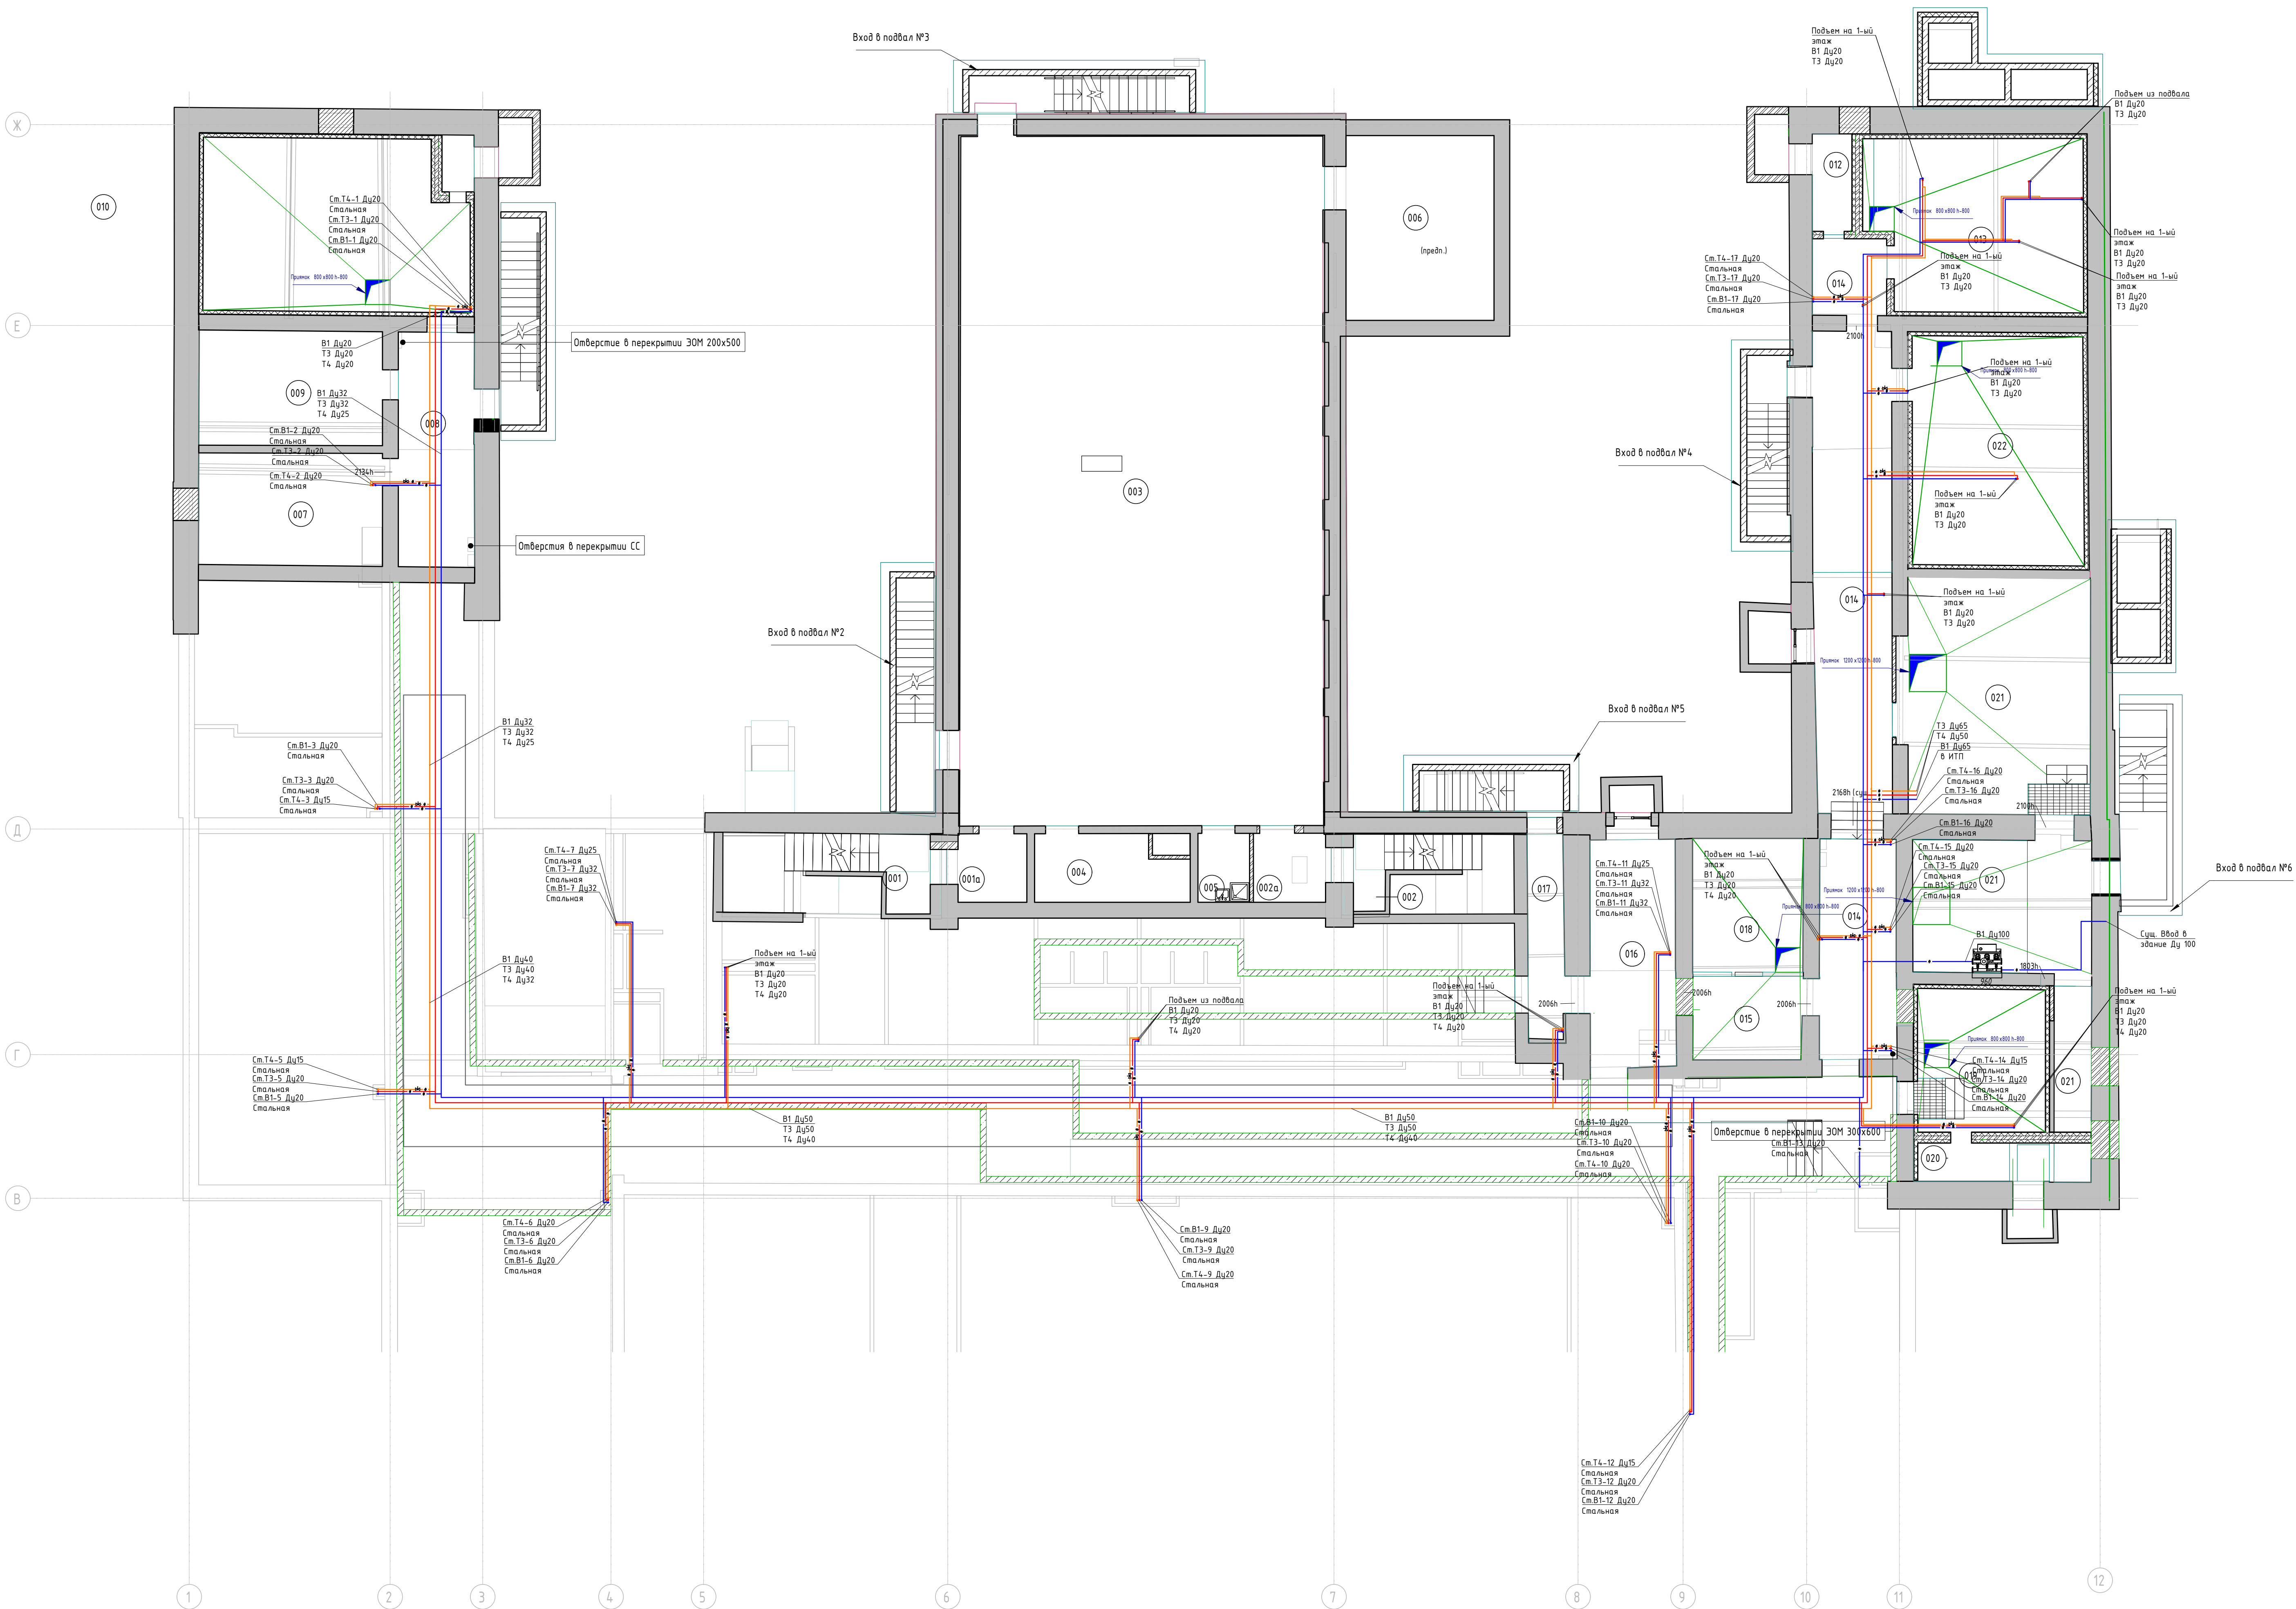

Номер помеще-ния	Наименование	Площадь, м ²	Кат. помеще-ния
101	Тамбур	17,0	
102	Вестибюль	66,7	
103	Комната охраны (с диспетчерским пунктом)	16,0	
104	Гардероб для обучающихся	47,2	
105	Коридор	62,9	
106	Гардероб для обучающихся	54,2	
107	Учебный кабинет (Тип 1)	67,4	
108	Электрощитовая	15,5	В3
109	Учебный кабинет (Тип 2)	57,3	
110	Кладовая	18,0	В3
111	Учебный кабинет (математика)	52,3	
112	Лестничная клетка (Тип Л1)	27,6	
113	Туалет для персонала	2,8	
114	Уборная для девочек	15,9	
115	Техническая лестница	18,0	
116	ПУИ	4,0	В4
117	Универсальная уборная для МГН	6,5	
118	Коридор	194,5	
119	Раздевальная Тип 1	19,0	
120	Душевая	6,5	
121	Уборная	5,3	
122	Уборная	5,3	
123	Душевая	6,5	
124	Раздевальная Тип 1	18,4	
125	Техническая лестница	18,8	
126	Уборная для мальчиков	18,0	
127	Лестничная клетка (Тип Л1)	27,6	
128	Тренинговая с санузлом	8,7	
129	Умывальная	10,1	
130	Обеденный зал	108,3	
131	Моечная для столовой посуды	17,3	В4
132	Коридор	13,1	
133	Кладовая и моечная оборотной тары	4,0	В4
134	Загрузочный цех	6,2	В4
135	Кладовая сухих продуктов	3,7	В4
136	Помещение персонала с санузлом	4,2	
137	Пом. для временного хранения пищевых отходов	4,4	В4
138	ПУИ	3,6	В4
139	Пом. подготовки блюд к реализации с участком мойки кухонной посуды	30,5	В4
140	Кабинет врача	18,9	
141	Процедурный (прибодочный) кабинет	13,2	
142	Пом. для хранения уборочного инвентаря, приготовления дезинфицирующих растворов	5,9	В4
143	Ожидальная мебелька	3,5	
144	Помещение СС	9,4	В4
145	Кабинет с рабочим пространством для учителей (Тип 1)	42,0	
146	Гардероб для учителей	19,4	
147	Гардероб для обучающихся	49,0	
148	Тамбур	2,0	
149	Венткамера	9,1	?
150	венткамера	15,5	
ИТОГО:		1271,4	

B1	Проектируемый хозяйственно-питьевой водопровод
T3	Подводящий трубопровод горячего водоснабжения
T4	Циркуляционный трубопровод горячего водоснабжения

							696/П-25-АНО-Р-ВК		
							Капитальный ремонт (осуществление бюджетного общеобразовательного учреждения города Москвы «Школа №1828 (Специальная)» по адресу: г. Москва, ул. Баболова, д. 1 корп. 1		
Изм.	Копия	Листы	Лист	№ док.	Подпись	Дата			
Разработана				Дизайн		06.26			
Гип				Чертеж		06.26			
							Капитальный ремонт		
							Система водоснабжения		
							Стоимость	Лист	Листов
							Р	3	
Неконтроль	Наблюдать					06.26	План 1-го этажа водоснабжение		
									

Экспликация помещений 2-го этажа			
Номер помеще-ния	Наименование	Площадь, м²	Кот. помеще-ния
201	Коридор с рекреацией	191,5	
202	Коридор с рекреацией	197,2	
203	Помещение СС	5,1	В4
204	Лестничная клетка I тип ЛП	27,4	
205	Лестничная клетка I тип ЛП	27,6	
206	Помещение СС	6,7	В4
207	Подсобное помещение	5,3	В4
208	Подсобное помещение	4,3	В4
209	Туалет для персонала	3,1	
210	Или	2,2	В4
211	Забора для девочек	19,1	
212	Забора для мальчиков	18,8	
213	Кабинет для индивидуальных занятий, в т.ч. с учителем-логопедом	18,1	
214	Административный кабинет. Тип 1	16,9	
215	Учебный кабинет	52,7	
216	Учебный кабинет	45,6	
217	Учебный кабинет	46,2	
218	Учебный кабинет	46,4	
219	Учебный кабинет	49,3	
220	Учебный кабинет	48,9	
221	Учебный кабинет	49,6	
222	Учебный кабинет	49,3	
223	Учебный кабинет	47,9	
224	Гимнастический зал	72,6	
225	Раздевальня Тип 1	9,5	
226	Раздевальня Тип 1	8,9	
227	Учебный кабинет	51,7	

Условные обозначения


- В1

Проектируемый хозяйственно-питьевой водопровод
- Т3

Подающий трубопровод горячего водоснабжения
- Т4

Циркуляционный трубопровод горячего водоснабжения

696/П-25-АНО-Р-ВК					
Капитальный ремонт Государственного бюджетного общеобразовательного учреждения города Москвы "Школа №1282 "Солнышки" по адресу: г. Москва, ул. Бардымова, д. 1 корп. 1					
Исполн.	Волков	Должн.	Директор	Дата	06.26
Разработчик	Борискин	Должн.	Проектировщик	Дата	06.26
Тип	Генеральный	Должн.	Проектировщик	Дата	06.26
Капитальный ремонт Система водоотведения				Стенда	Лист
План 2-го этажа водоснабжение				Р	4
Исполн.	Гилько	Должн.	Проектировщик	Дата	06.26
Копировал				Формат А0	

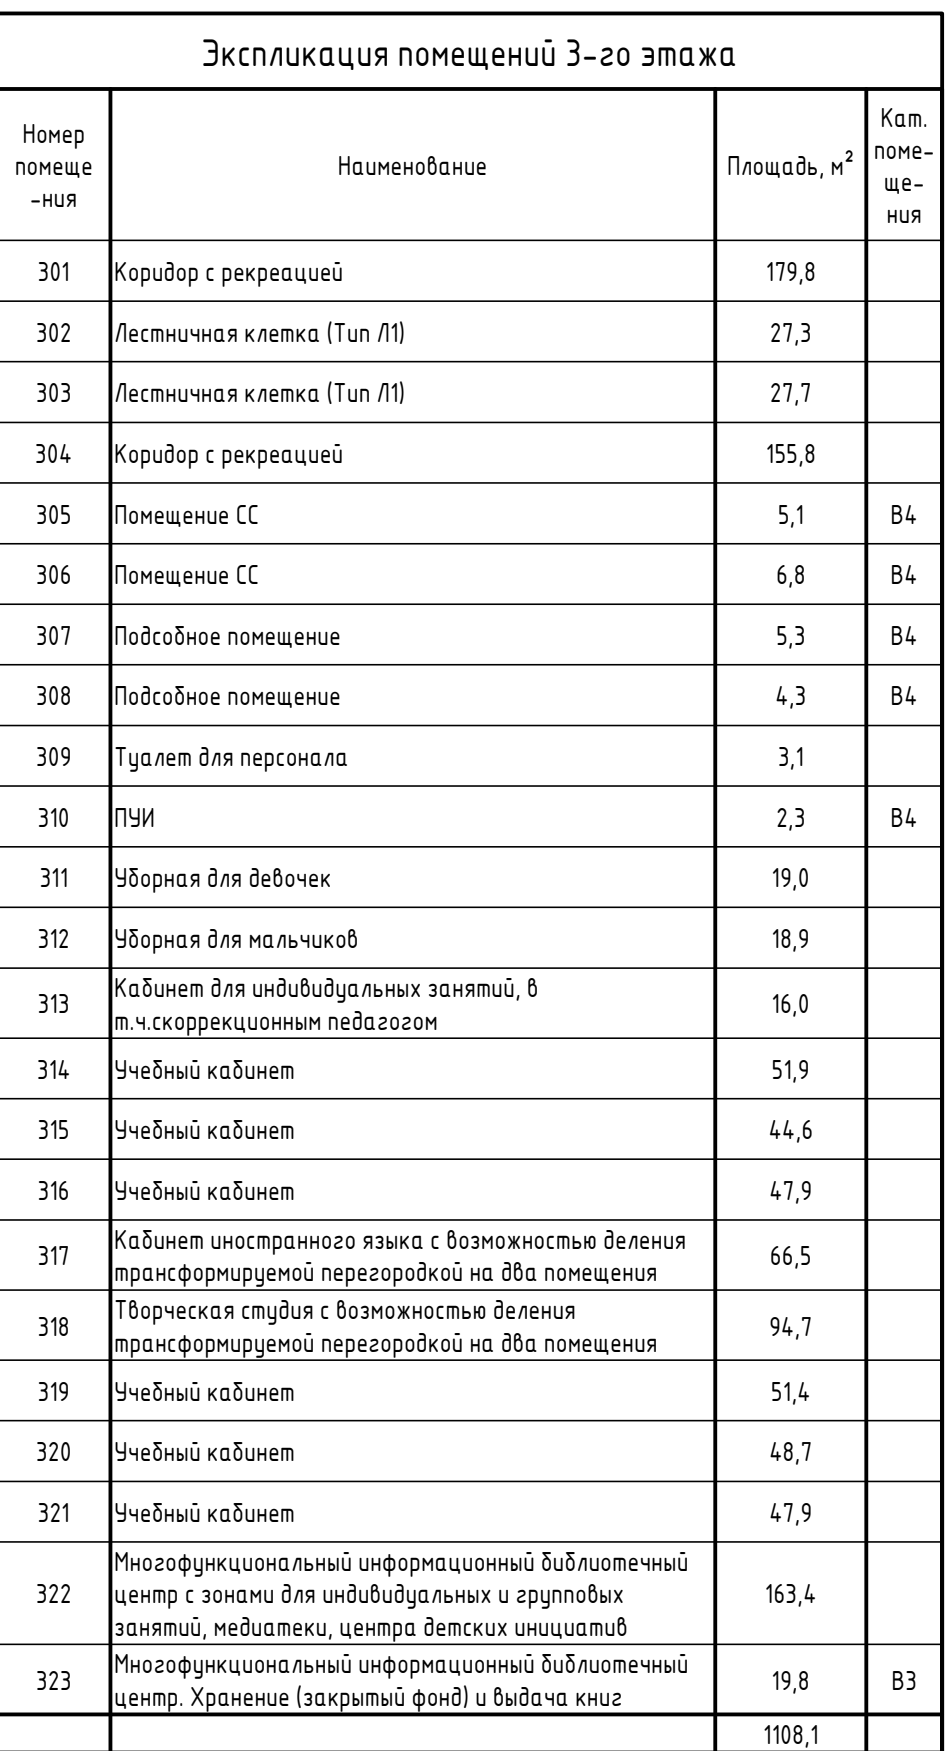

B1	Проектируемый хозяйственно-питьевой водопровод
T3	Подводящий трубопровод горячего водоснабжения
T4	Циркуляционный трубопровод горячего водоснабжения

Копировал Формат А

Экспликация помещений 4-го этажа			
Номер помеще-ния	Наименование	Площадь, м²	Кот. помеще-ния
401	Коридор с рекреацией	173,6	
402	Коридор с рекреацией	166,2	
403	Танбур	4,1	
404	Лестничная клетка (Тип Л1)	26,9	
405	Лестничная клетка (Тип Л1)	26,8	
406	Помещение СС	5,0	В4
407	Помещение СС	6,8	В4
408	Подсобное помещение	5,0	В4
409	Подсобное помещение	4,3	В4
410	Туалет для персонала	2,9	
411	РЗН	2,1	В4
412	Зубная для девочек	19,0	
413	Зубная для мальчиков	19,1	
414	Кабинет для индивидуальных занятий, в т.ч. логопедом-психологом	16,2	
415	Актовый зал (с эстрадой в рабоче пола)	131,1	
416	Технический центр	12,4	В3
417	Артистическая	6,9	
418	Кладовая инвентаря	6,1	В4
419	Кабинет математики	50,8	
420	Учебный кабинет (для изучения естественных биологич. географии Тип 2	92,4	
421	Лаборантская биологии	18,3	В3
422	Учебный кабинет (истории)	45,0	
423	Кабинет иностранного языка с возможностью деления трансформируемой перегородкой на два помещения	65,9	
424	Учебный кабинет информатики с возможностью деления трансформируемой перегородкой на два помещения	90,5	
425	Кабинет русского языка и литературы	53,4	
426	Кабинет русского языка и литературы	48,1	
		1098,9	

Условные обозначения



- В1

Проектируемый хозяйственно-питьевой водопровод
- Т3


Подающий трубопровод горячего водоснабжения
- Т4

Циркуляционный трубопровод горячего водоснабжения

						696/П-25-АНО-Р-ВК					
						Капитальный ремонт Государственного бюджетного Общественного Учреждения города Москвы "Школа №1282 "Семьинки" по адресу: г. Москва, ул. Бардымова, д. 1 корп. 1					
Испол.	Волгарь	Дата	18.08.2025	Подпись	Давыд	Разработал	Борискин	06.26			
ТИП	Гуляко	06.26				Капитальный ремонт Система водоотведения			Стенда	Лист	Листов
						План 4-го этажа водоснабжение			Р	6	
И.контр.	Гуляко	06.26									

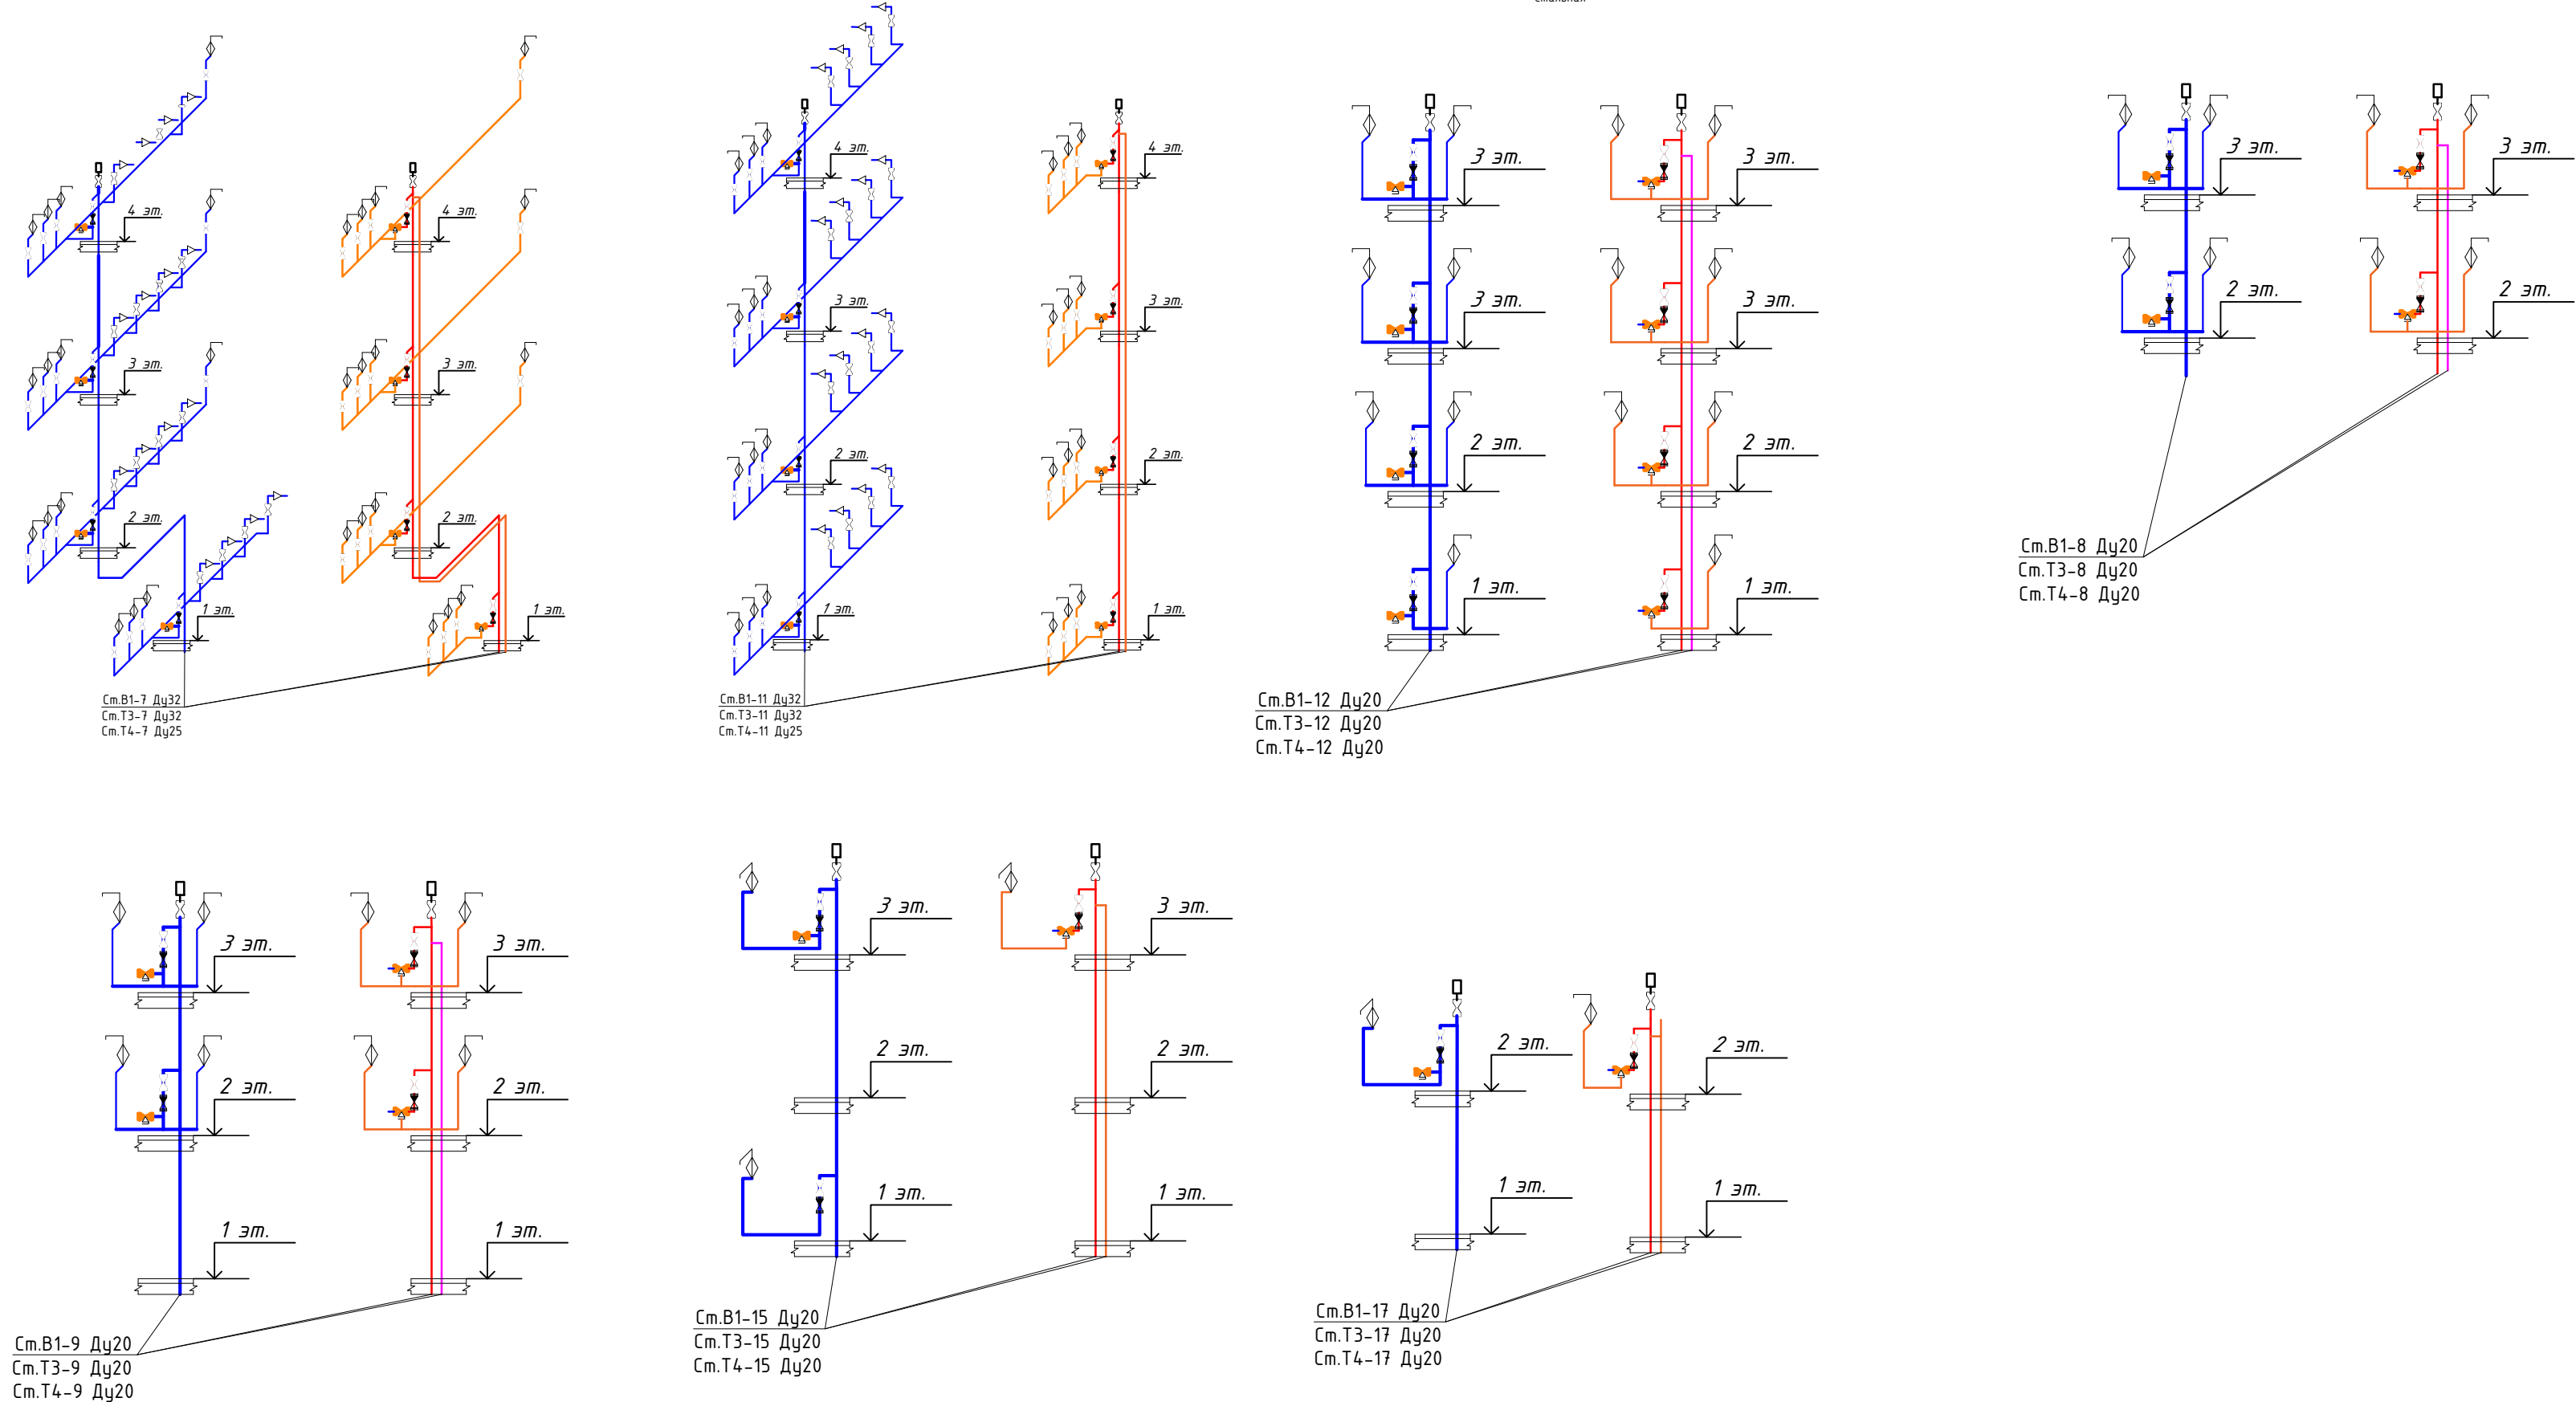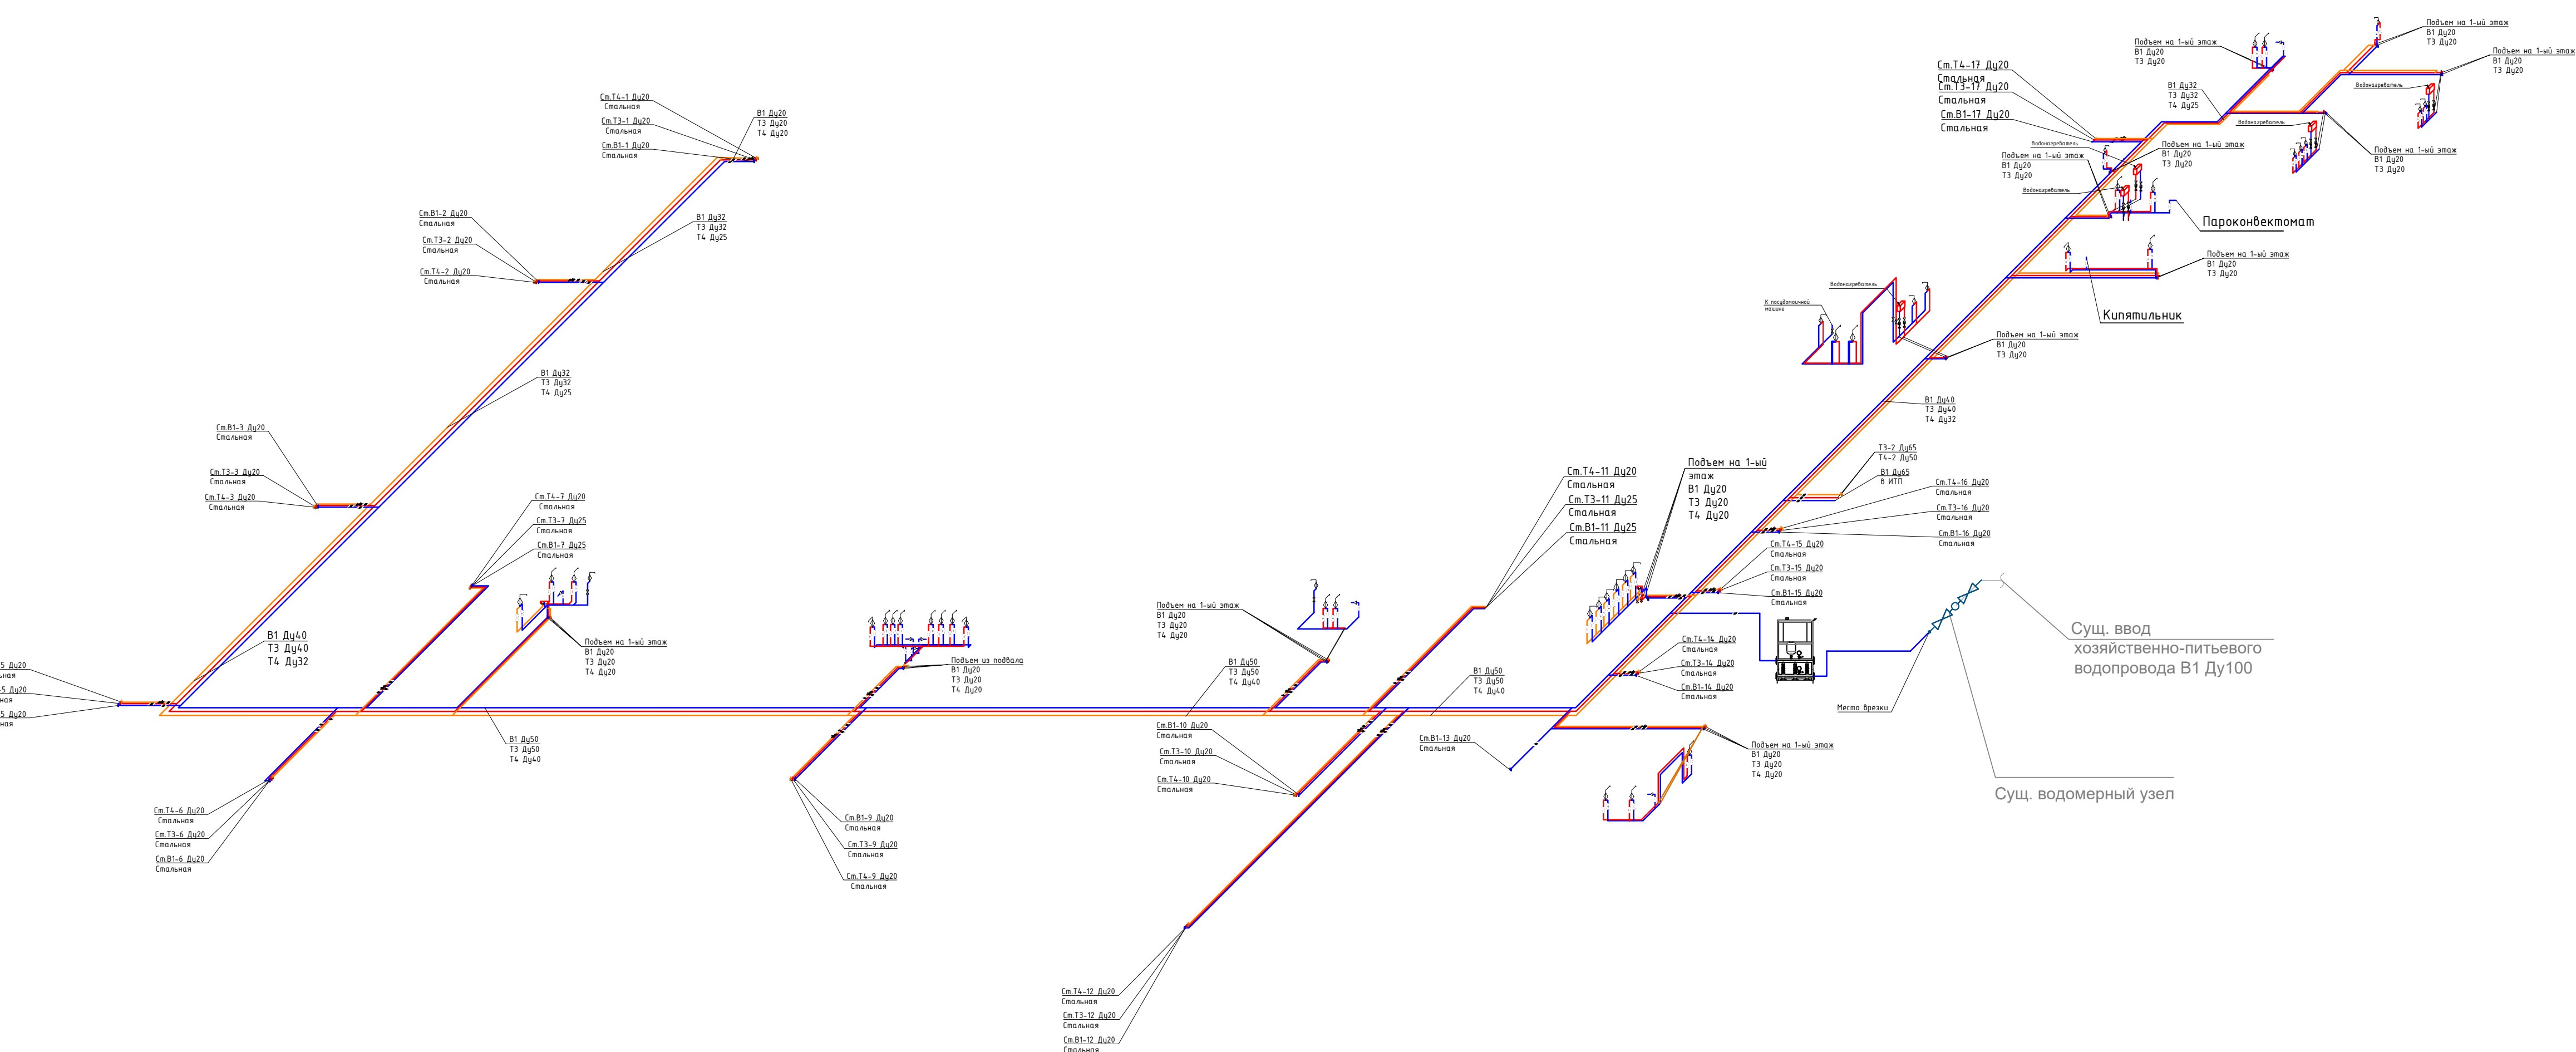


Узел прохода трубопровода через перекрытие

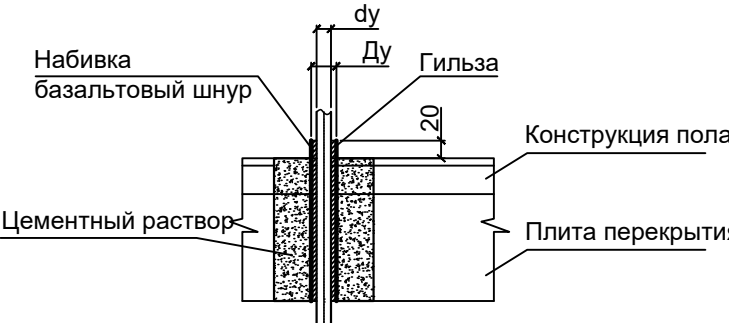


Внутренний диаметр стояка, фут	20	25	32	40	50
Внутренний диаметр футляра, Ду	32	40	50	70	80

Примечание:
Трубопровод в пределах футляра не должен иметь стыковых соединений.

Узел подключения водонагревателя

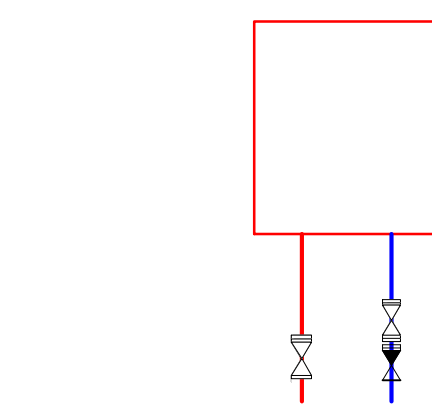

Узел прохода трубопровода через перегородку

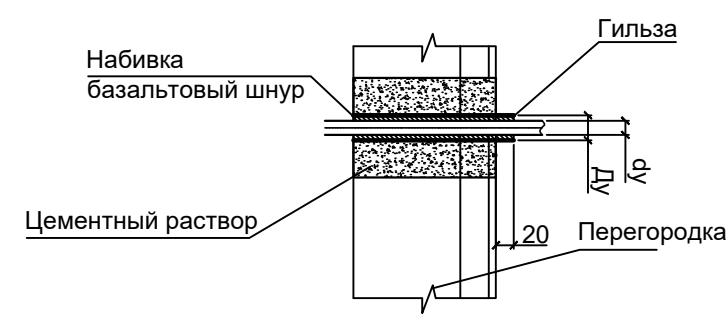

- Примечания (сети хозяйственно-питьевого противопожарного водоснабжения):
1. Монтаж и приемку сантехустройств производить в соответствии с СП 73.13330 "Внутренние санитарно-технические системы зданий".
 2. Монтаж трубопроводов холодного и горячего водоснабжения производить: из стальных водогазопроводных оцинкованных труб по ГОСТ 3262-75* (магистраль в подземной части здания и под потолком этажей, а также стояки); с резьбовыми или муфтовыми соединениями; подводя к сантехприборам из полипропиленовых труб, армированных стекловолокном, с применением 3. Стыковые соединения трубопроводов, соединяемых на резьбе, соединяемых с помощью других фитингов и подобных соединений выполнять в зоне доступа (на стояках в уровне расположения ревизионного люка).
 4. При соединении стояков холодного и горячего водоснабжения в качестве уплотнителя для резьбовых соединений применять льняную прядь, пропитанную свинцовым суриком или белыми, замешанными на натуральной олифе.
 5. Стояки и трубопроводы горячего водоснабжения в местах пересечения их с перекрытиями и внутренними стенами должны заключаться в гильзы из стали.
 6. Трубы прокладываются скрыто в конструкции пола и стен, за подшивным потолком, в подшивных коробах.
 7. Трубопроводы изолируются теплоизоляционным материалом.
 8. Расстояния между средствами крепления стальных трубопроводов при горизонтальной прокладке должны быть не более: для труб Ø15мм - 1,50м; Ø20мм - 2,0м; Ø25мм - 2,0м; Ø32мм - 2,50м; Ø50мм - 3,0м; Ø80мм - 4,0м. Средства крепления не располагать в местах соединений трубопроводов.
 9. Расстояния между средствами крепления трубопроводов из полипропилена принять согласно СП 40-101-96.
 10. При проведении отделочных работ предусмотреть монтаж лючков для обеспечения свободного доступа к 11. На планах и схемах водопровода и канализации указаны номера позиций приборов, соответствующие технологической части проекта.
 12. При обходе коммуникаций, предусмотреть установку крана для слива воды в нижних точках.


Условные обозначения:

- ☒ неподвижная опора
- ☒ кран шаровый
- ☒ задвижка
- ☒ регулятор давления с манометром
- ☒ обратный клапан
- ☒ фильтр сетчатый
- ☒ Термосмеситель
- ☒ Балансировочный клапан


						696/П-25-АНО-Р-ВК		
						Капитальный ремонт Государственного бюджетного общеобразовательного учреждения города Москвы - школы №1282, расположенного по адресу: г. Москва ул. Барболова, д. 1 корп. 1		
Изм.	Кол.ч.	Лист	№ док.	Подпись	Дата	Капитальный ремонт Система водоснабжения	Станд.	Лист
Разработал	Джаматов	09.25					Р	7
Исполнитель	Набегова	09.25						
						Схема сети водоснабжения		

Узлы крепления труб


Подвеска трубопровода к перекрытию

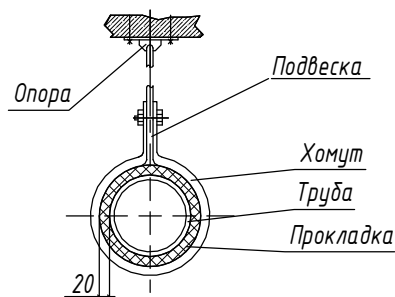


Вертикальная прокладка в стене

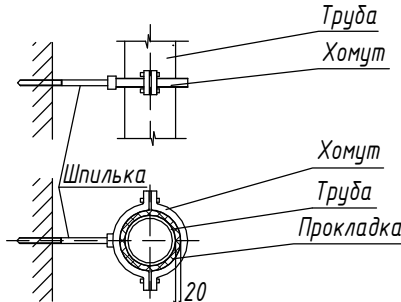


Крепеж трубы к полу

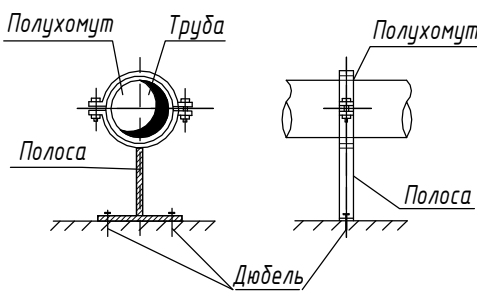

Вариант крепления подвески для нескольких труб

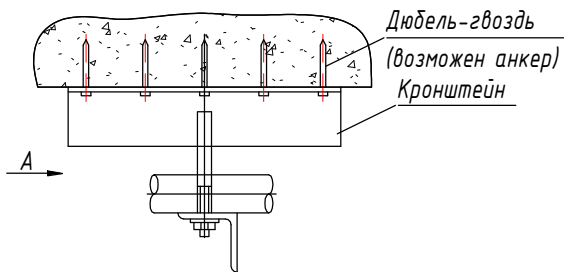

Вид А

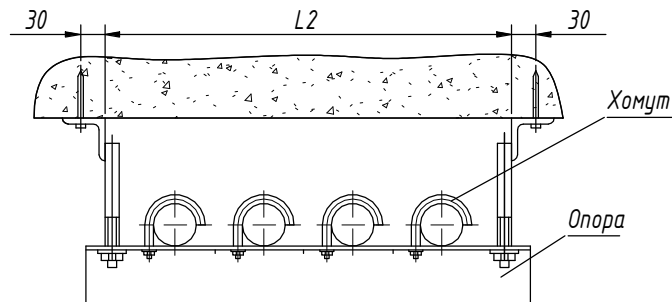

Примечания:

На чертеже показан один из вариантов крепления, на строительном объекте возможны и иные способы и варианты креплений

Наибольшее расстояние между средствами крепления стальных трубопроводов

Диаметр условного прохода трубы, мм	Наибольшее расстояние между средствами крепления трубопроводов, м	
	неизолированных	изолированных
15	2,5	1,5
20	3,0	2,0
25	3,5	2,0
32	4,0	2,5
150	4,5	3,0
50	5,0	3,0
70, 80	6,0	4,0
100	6,0	4,5
125	7,0	5,0
150	8,0	6,0

Согласовано					
Взам. инв. №					
Подп. и дата					
Инв. № подл.					

						696/П-25-АНО-Р-ВК			
						Капитальный ремонт Государственного Бюджетного Общеобразовательного Учреждения города Москвы "Школа №1282 "Сокольники" по адресу: г. Москва ул. Барболина, д. 1 корп. 1			
Изм.	Кол.уч.	Лист	№ док.	Подпись	Дата	Капитальный ремонт. Система водоотведения	Стадия	Лист	Листов
Разработал	Брусникин				06.26				
ГИП	Гулько				06.26		Р	8	
						Узлы крепления труб			
Н.контроль	Гулько				06.26				

Экспликация помещений подвала

Номер помеще-ния	Наименование	Площадь, м²	Кат. поме-ще-ния
001	Техническая лестница	13,7	
001a	Тамбур-шлюз 1-го типа	4,9	
002	Техническая лестница	9,8	
002a	Тамбур-шлюз 1-го типа	5,0	
003	Спортивный зал	262,5	
004	Снарядная	10,1	B3
005	ПУИ	3,5	
006	Снарядная	28,0	B3
007	Коридор	21,0	
008	Коридор	17,9	
009	Кладовая	21,4	B3
010	Венткамера	Не окружено	B4
011	Форкамера	Не окружено	B4
012	Форкамера	3,8	B4
013	Венткамера	37,5	B4
014	Коридор	63,3	
015	Коридор	9,8	
016	Коридор	19,3	
017	Коридор	8,3	
018	Насосная	14,8	B4
019	Венткамера	19,3	B4
020	Форкамера	5,2	B4
021	ИТП	75,6	Д
022	Венткамера	41,1	B4
ИТОГО:		695,8	

УСЛОВНЫЕ ОБОЗНАЧЕНИЯ

- K1

Хозяйственно-бытовая канализация

KдН


Напорная дренажная канализация


KЗ

Производственная канализация

Номер помещения	Наименование	Площадь, м ²	Кат. помещения
101	Тамбур	17,0	
102	Вестиболь	66,7	
103	Комната охраны (с диспетчерским пунктом)	16,0	
104	Гардероб для обучающихся	47,2	
105	Коридор	62,9	
106	Гардероб для обучающихся	54,2	
107	Учебный кабинет (Тип 1)	67,4	
108	Электрощитовая	15,5	В3
109	Учебный кабинет (Тип 2)	57,3	
110	Кладовая	18,0	В3
111	Учебный кабинет (математика)	52,3	
112	Лестничная клетка (Тип Л1)	27,6	
113	Туалет для персонала	2,8	
114	Уборная для девочек	15,9	
115	Техническая лестница	18,0	
116	ПУИ	4,0	В4
117	Универсальная уборная для МГН	6,5	
118	Коридор	194,5	
119	Раздевальная Тип 1	19,0	
120	Душевая	6,5	
121	Уборная	5,3	
122	Уборная	5,3	
123	Душевая	6,5	
124	Раздевальная Тип 1	18,4	
125	Техническая лестница	18,8	
126	Уборная для мальчиков	18,0	
127	Лестничная клетка (Тип Л1)	27,6	
128	Тренинговая с санузлом	8,7	
129	Умывальная	10,1	
130	Обеденный зал	108,3	
131	Моечная для столовой посуды	17,3	В4
132	Коридор	13,1	
133	Кладовая и моечная оборотной тары	4,0	В4
134	Загрузочный цех	6,2	В4
135	Кладовая сухих продуктов	3,7	В4
136	Помещение персонала с санузлом	4,2	
137	Пом. для временного хранения пищевых отходов	4,4	В4
138	ПУИ	3,6	В4
139	Пом. подготовки блюд к реализации с участком мойки кухонной посуды	30,5	В4
140	Кабинет врача	18,9	
141	Процедурный (прибавочный) кабинет	13,2	
142	Пом. для хранения уборочного инвентаря, приготовления дезинфицирующих растворов	5,9	В4
143	Ожидательная медблока	3,5	
144	Помещение СС	9,4	В4
145	Кабинет с рабочим пространством для учителей (Тип 1)	42,0	
146	Гардероб для учителей	19,4	
147	Гардероб для обучающихся	49,0	
148	Тамбур	2,0	
149	Венткамера	9,1	?
150	венткамера	15,5	
ИТОГО:		1271,4	

К1	Хозяйственно-бытовая канализация
КдН	Напорная дренажная канализация
КЗ	Производственная канализация

 					696/П-25-АНО-Р-ВК		
					Капитальный ремонт государственного бюджетного общеобразовательного учреждения «школа №282 "Смолячки" по адресу: г. Москва, ул. Бабушкина, д. 1 корп. 1		
Имя	Фамилия	Имя	Матр.	Подпись	Дата	Степень	Листов
Разработчик	Давыдов				06.06		
ГИП	Гуляко				06.06		
					Капитальный ремонт. Система водоотведения		
					План 1-го этажа с легкими канализация		
И.Контроль	Набокова				06.06	Р	9
					 Формат А0		

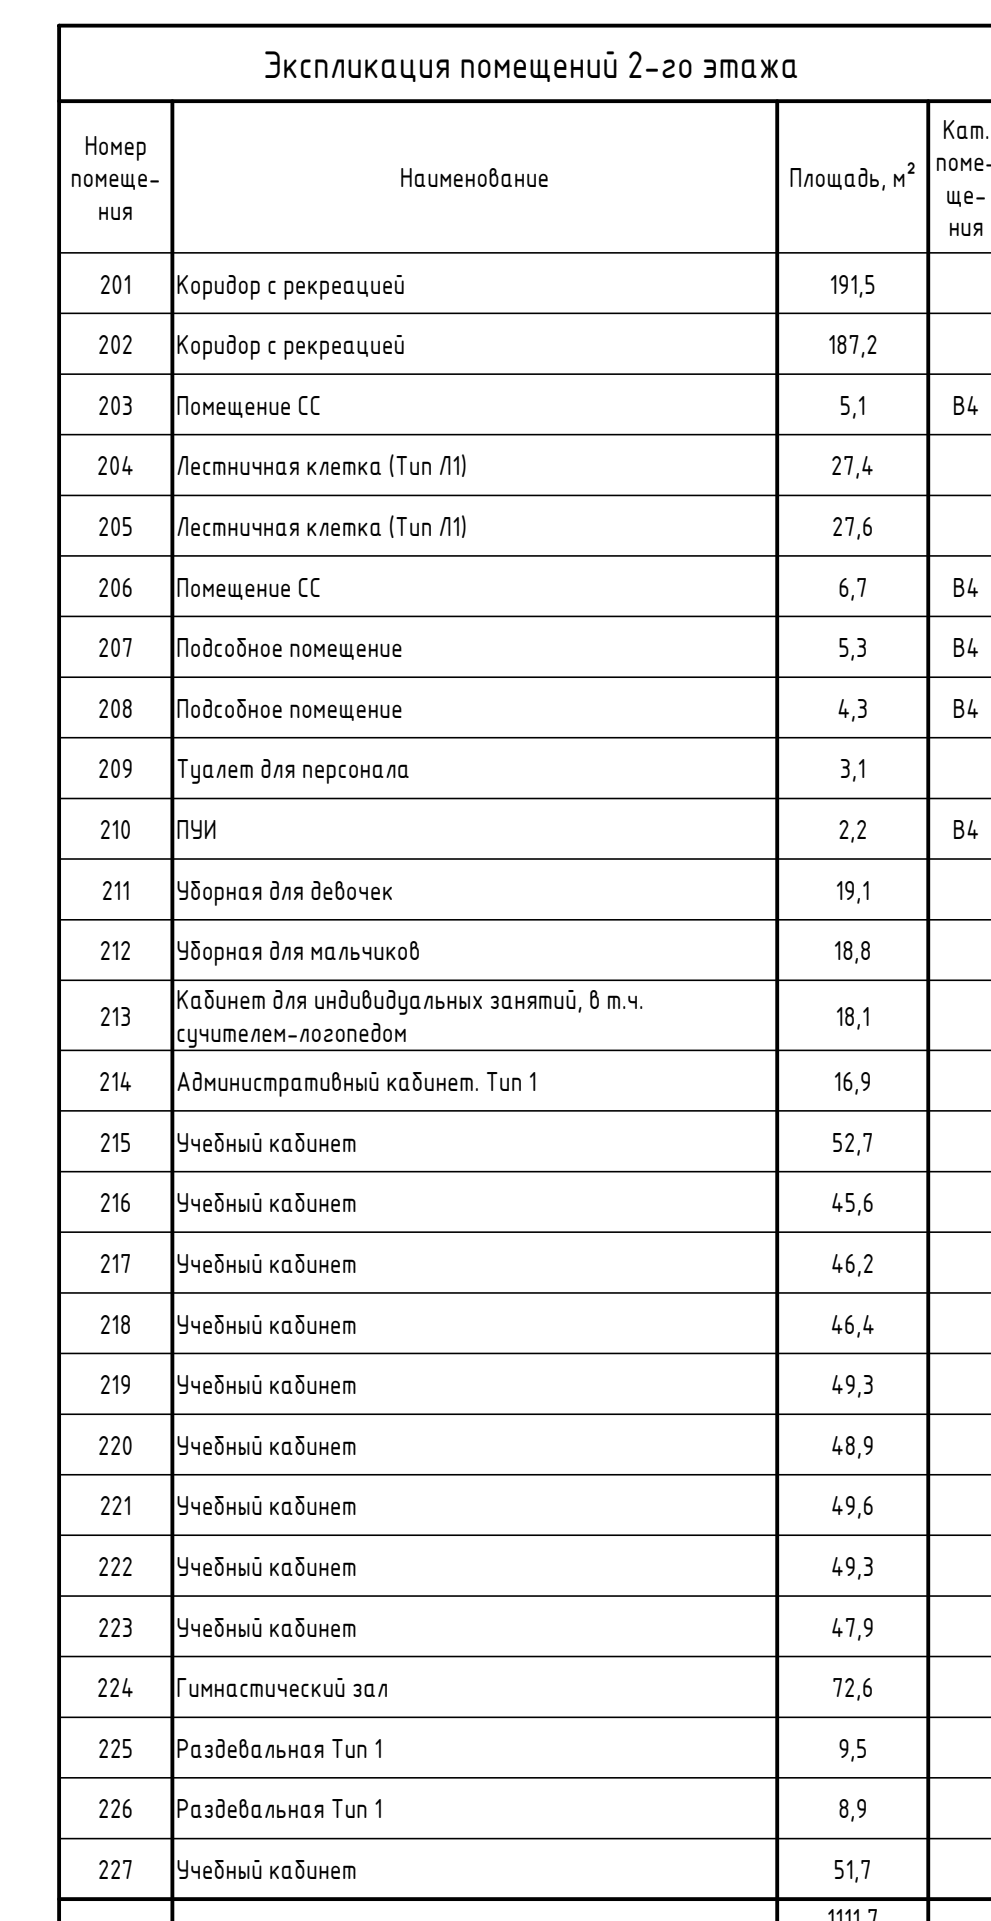




— K1 —	Хозяйственно-бытовая канализация
— КДН —	Напорная дренажная канализация
— КЗ —	Производственная канализация

Копировал	Формат А
-----------	----------




— K1 —	Хозяйственно-бытовая канализация
— КдН —	Напорная дренажная канализация
— КЗ —	Производственная канализация


Копировал	Формат А
-----------	----------

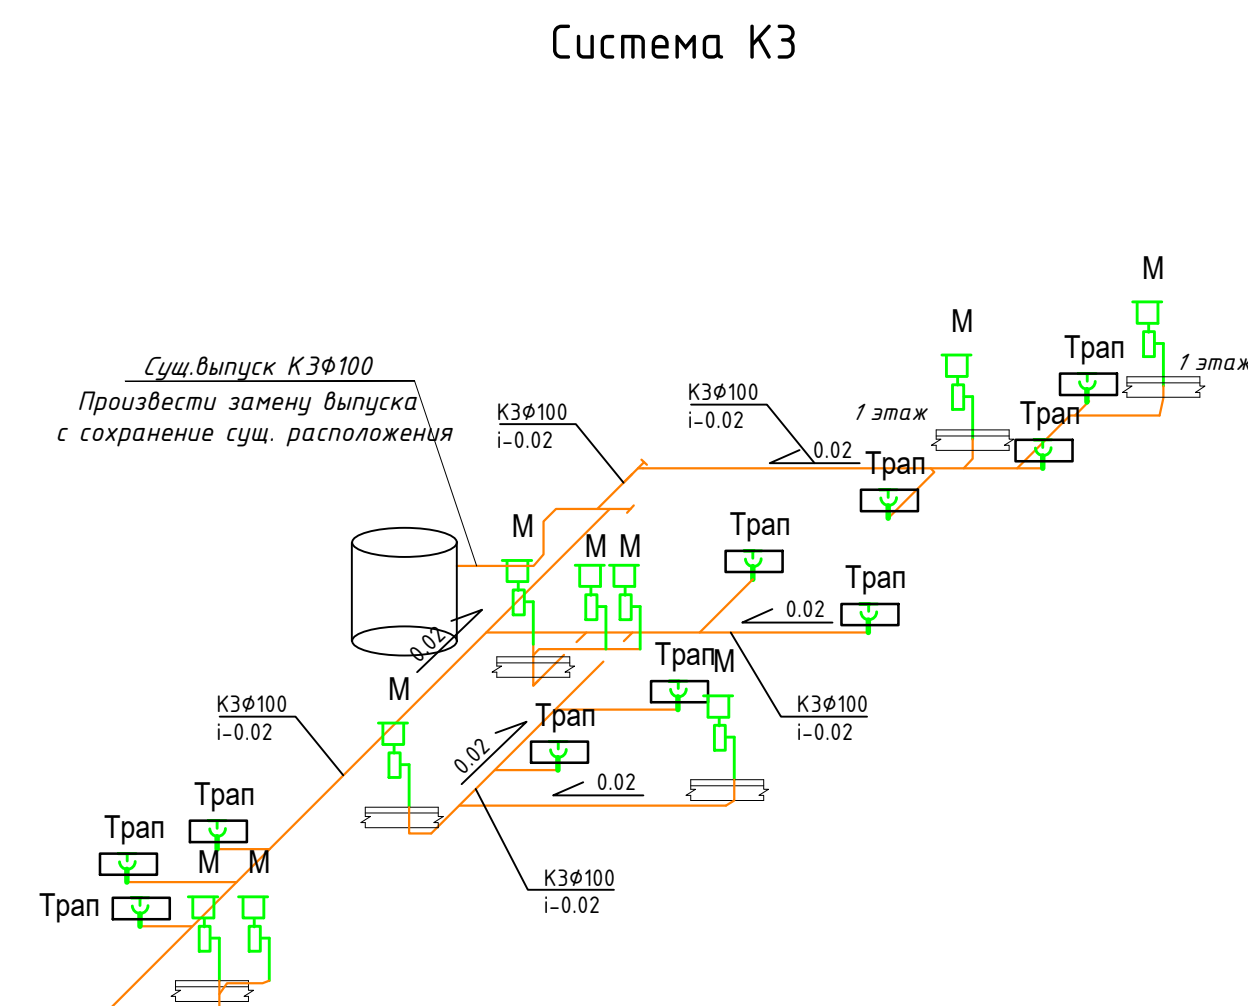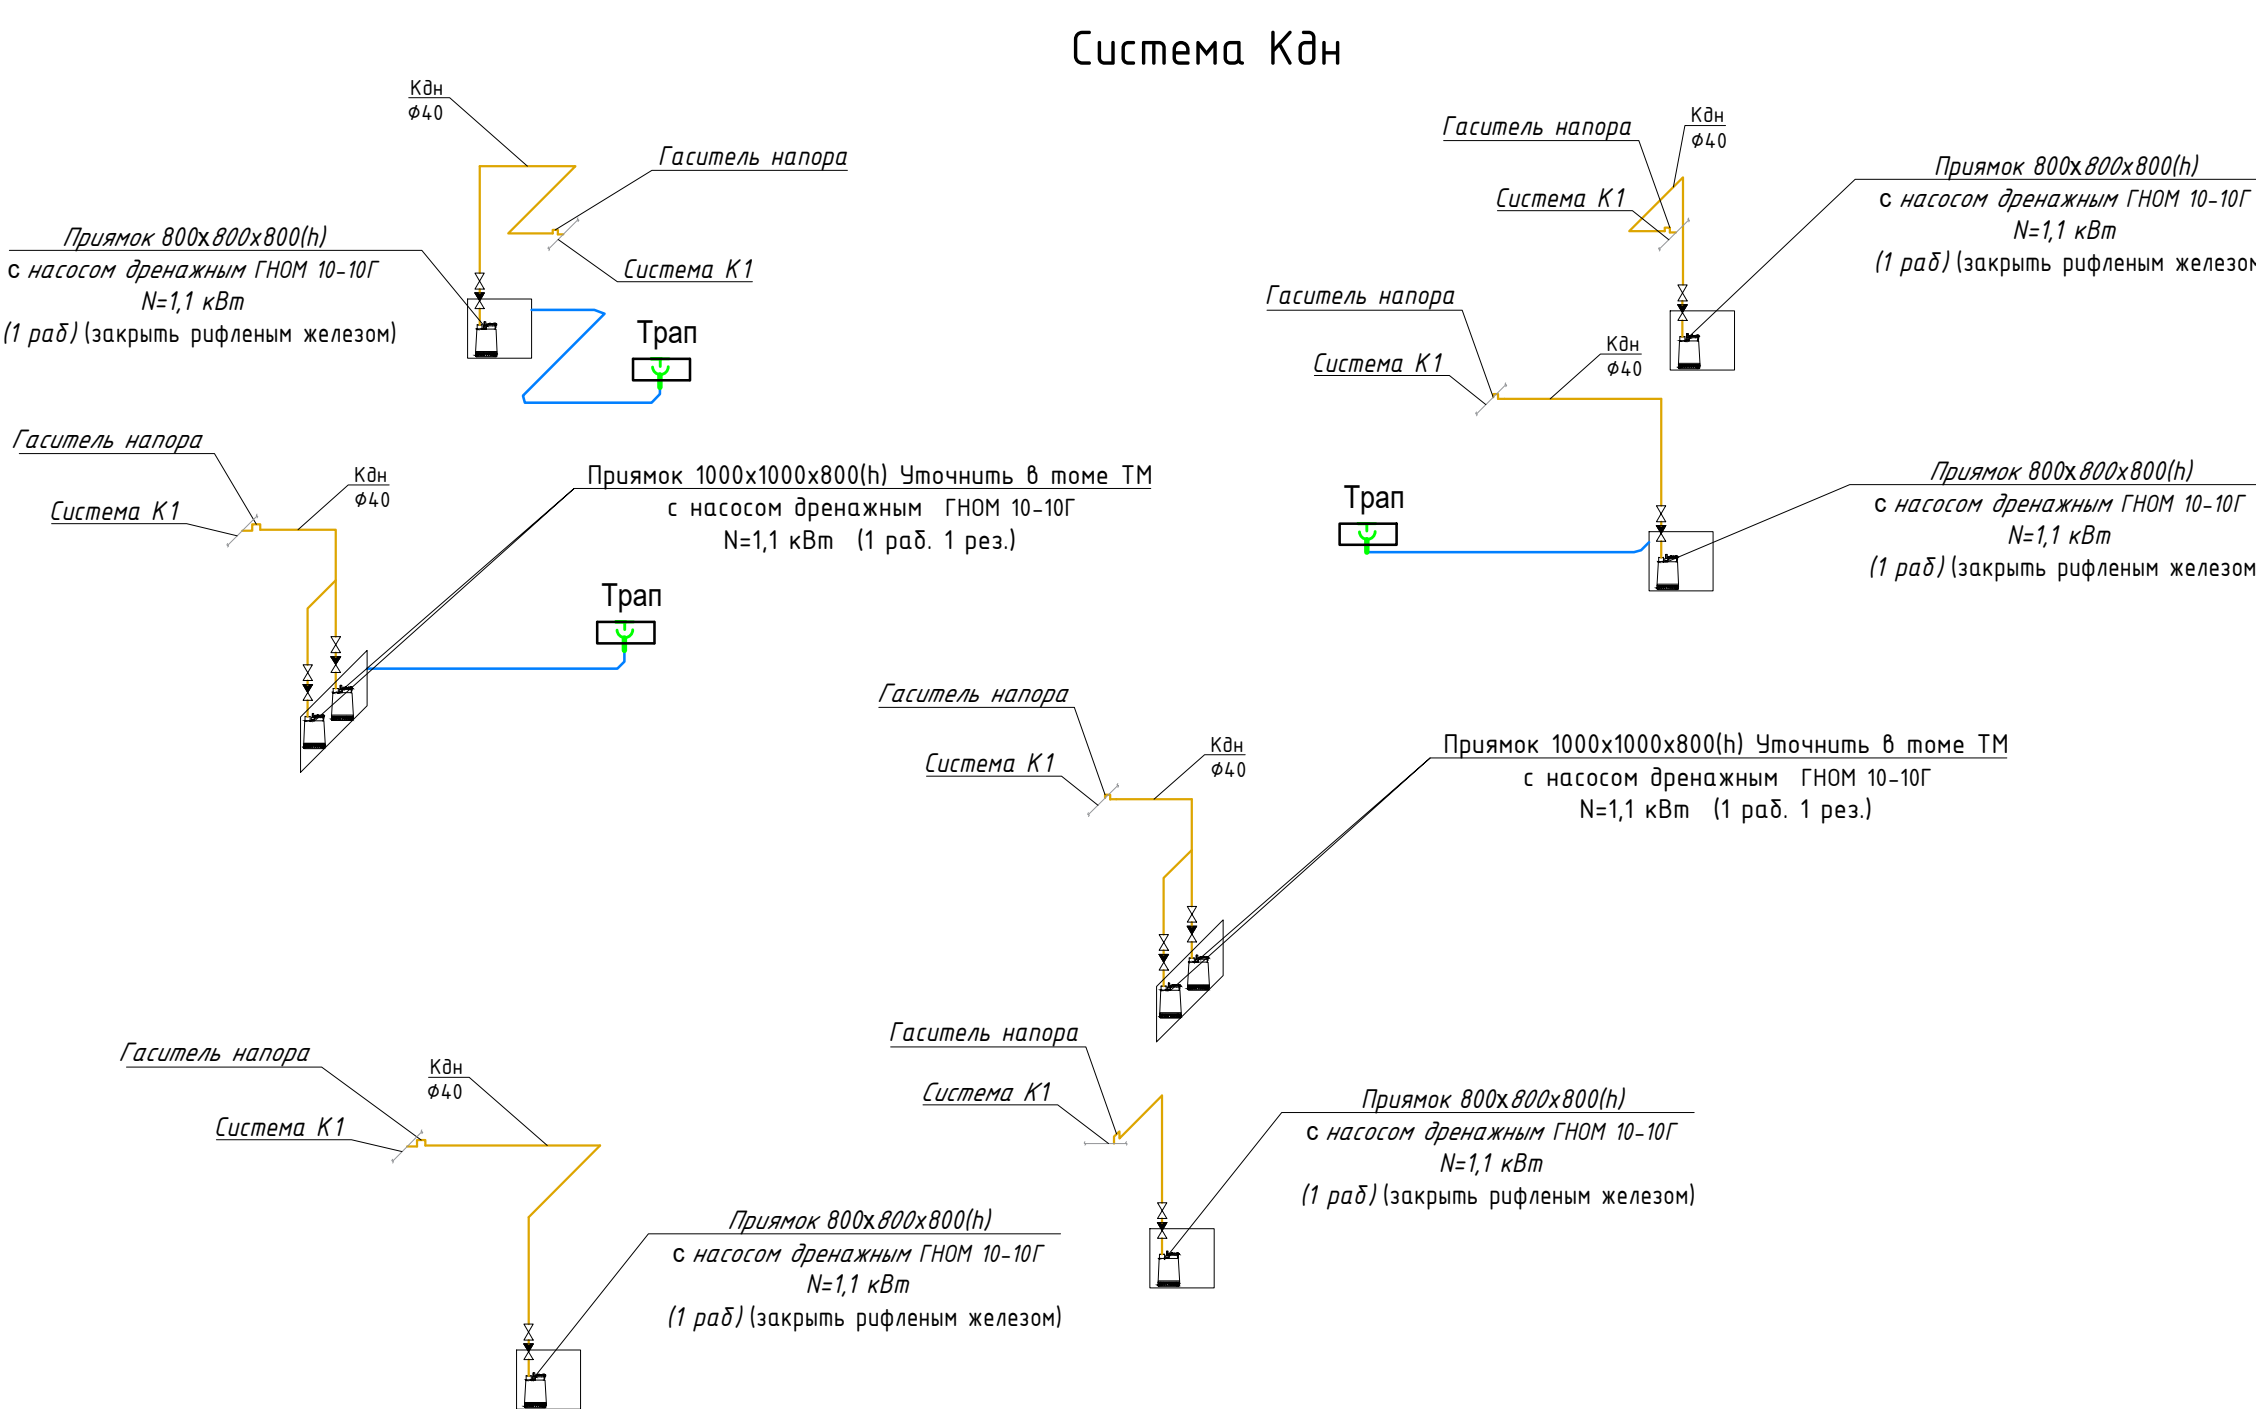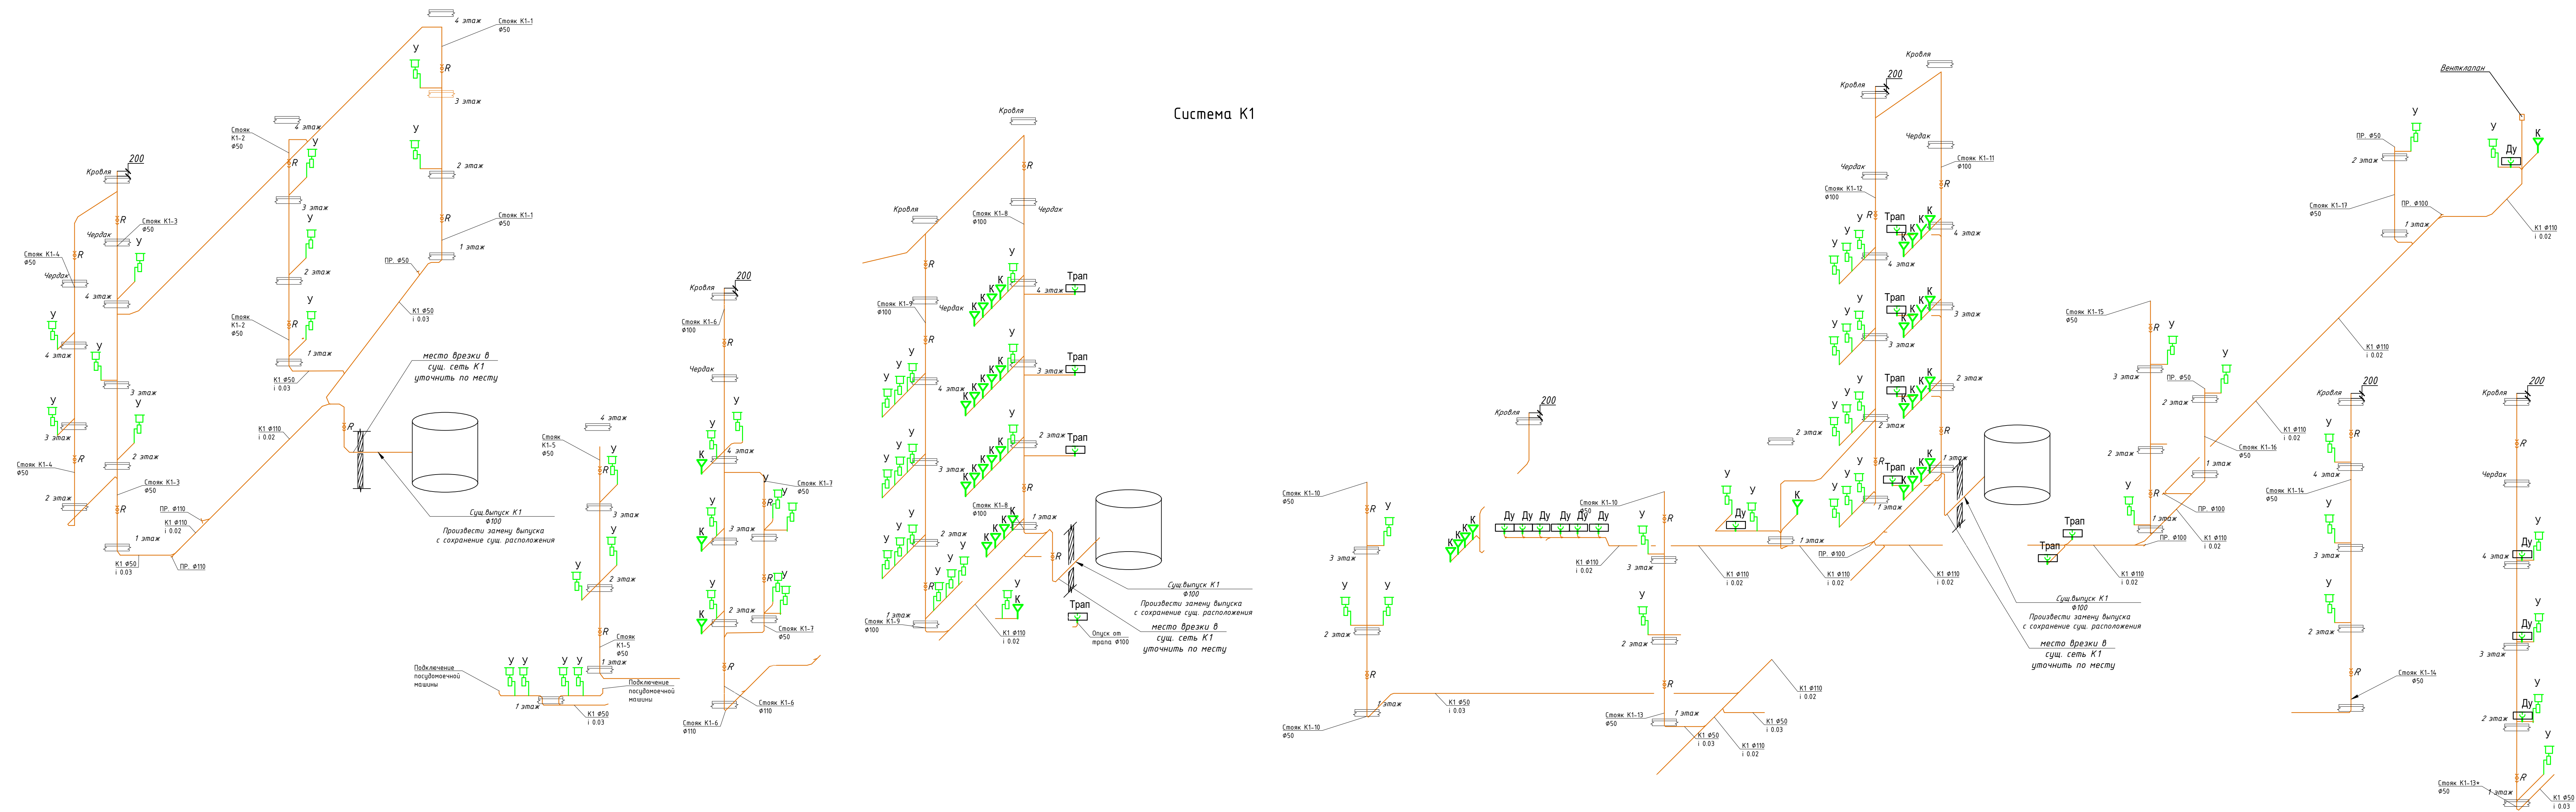

Типовой узел прохода трубопровода через перекрытие

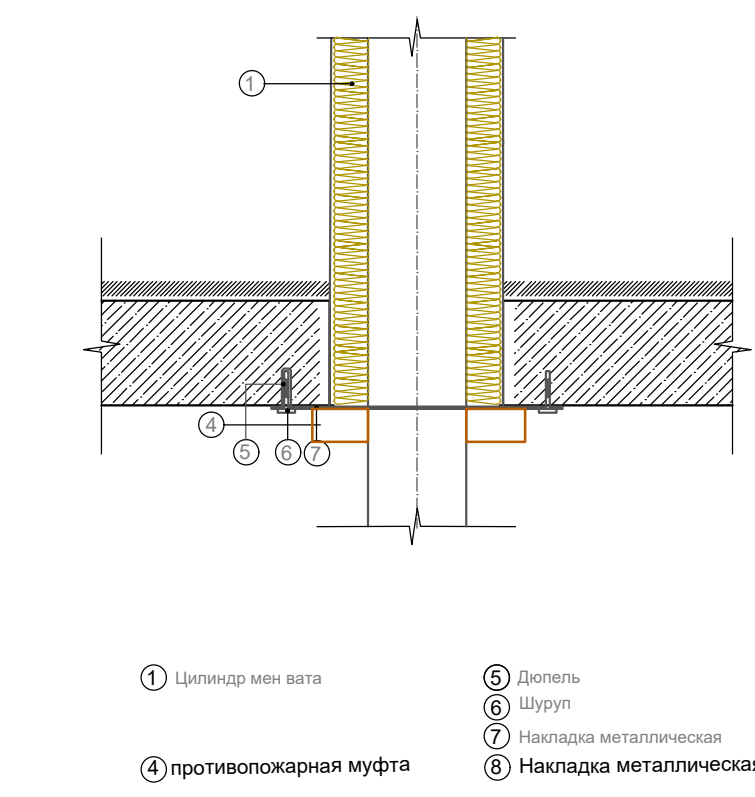


Типовой узел прохода трубопровода через стены

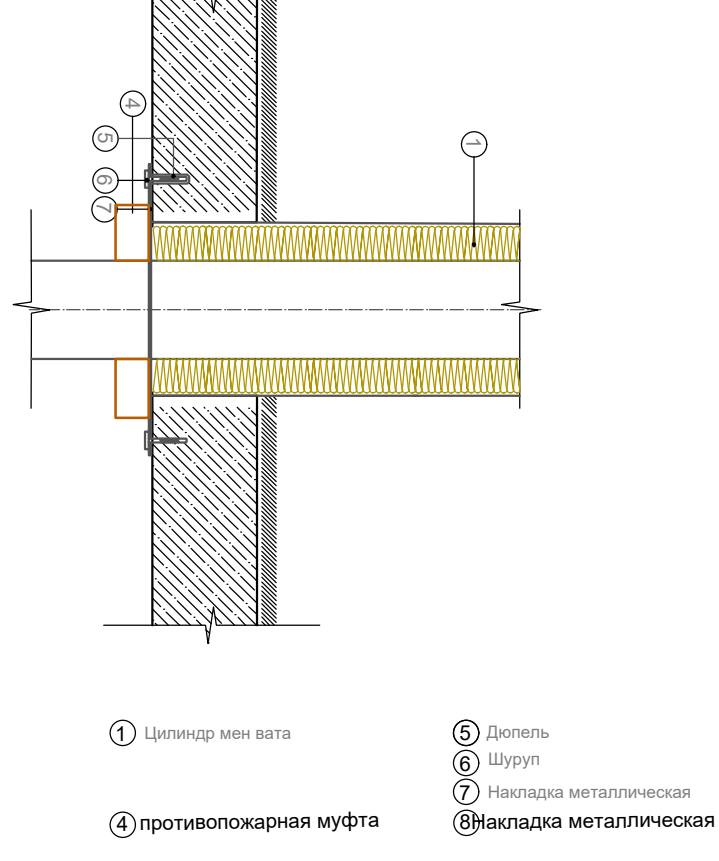


						696/П-25-АНО-Р-ВК					
						Капитальный ремонт Государственного бюджетного общеобразовательного учреждения города Москвы "Школа №1282 "Сокольники" по адресу: г. Москва, ул. Бардымова, д. 1, корп. 1					
Изм.	Кол.	Лист	№ Изм.	Подпись	Дата						
Разработчик		Детский			06.26						
ГИП		Гилько			06.26						
						Капитальный ремонт. Система водоотведения					
						Степан		Павел		Александр	
						Р		15			
						Схема системы канализации					
Исполнитель		Надзор			06.26						
											

Крепление трубопровода к стене

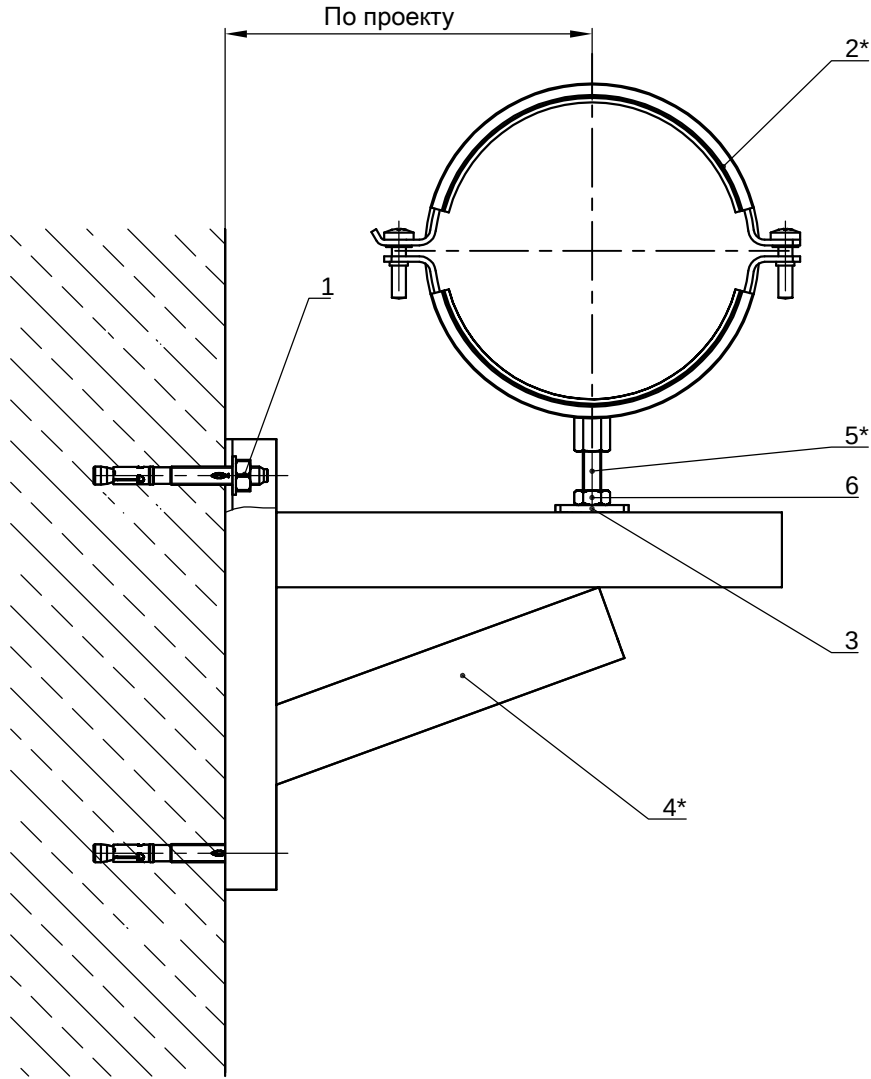

Крепление трубопровода к перекрытию

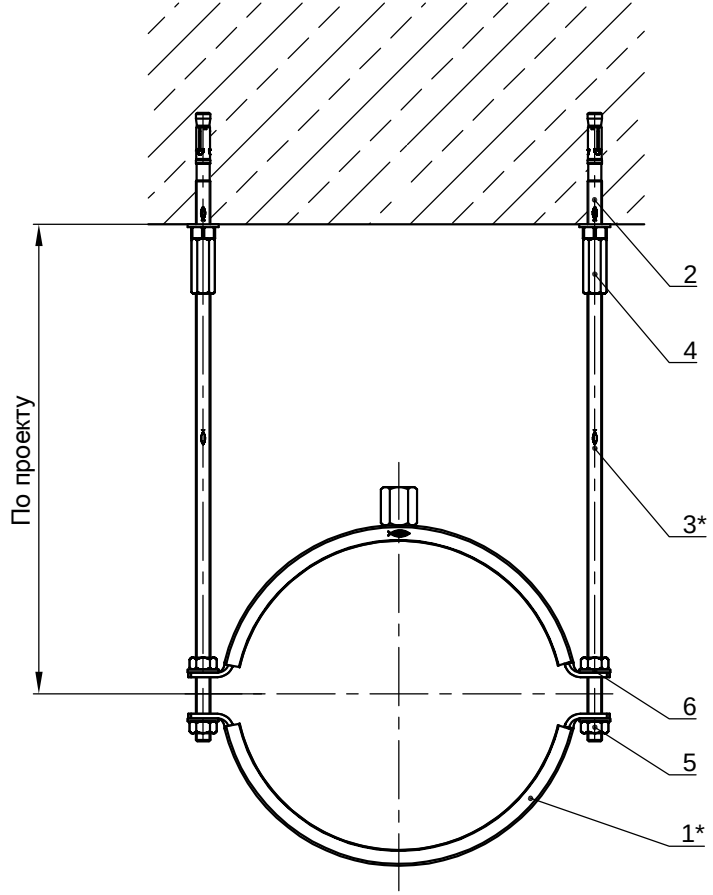

Согласовано		
Взам. инв. №		
Подп. и дата		
Инв. № подл.		

Поз.	Артикул	Наименование	Кол-во, шт
1	94981	Анкерный болт fischer FAZ II 10/10	2
2*		Хомут для трубопроводов fischer FRSM	1
3	504346	Гайка FCN Clix M 10	1
4*		Консоль fischer FCAM	1
5*		Шпилька резьбовая fischer G 10	1
6	79735	Гайка шестигранная fischer MU M10	1

Поз.	Артикул	Наименование	Кол-во, шт
1*		Хомут для трубопровода fischer FRSM	1
2	94871	Анкерный болт fischer FAZ II 8/10	2
3*		Шпилька fischer G8	2
4	79690	Муфта соединительная fischer VM M8	2
5	79734	Гайка шестигранная fischer MU M8	4
6	91477	Шайба fischer U 8x17	4

						696/П-25-АНО-Р-ВК			
						Капитальный ремонт Государственного бюджетного общеобразовательного учреждения города Москвы "Школа №1282 "Сокольники" по адресу: г. Москва, ул. Барболина, д.1, корп.1			
Изм.	Кол.уч.	Лист	№ док.	Подпись	Дата	Капитальный ремонт	Стадия	Лист	Листов
Разработал	Брусникин				06.26		Р	17	
ГИП	Гулько				06.26				
						Схема крепления труб канализации			
Н.контроль	Гулько				06.26				

Схема установки умывальника
Тип 1



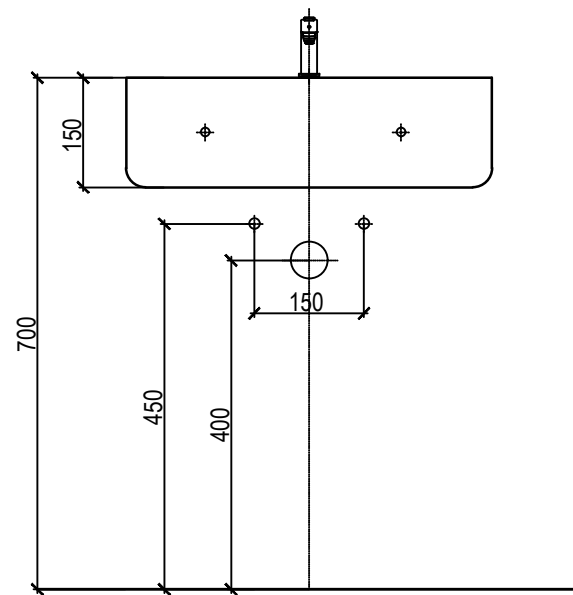


Схема установки умывальника
Тип 2

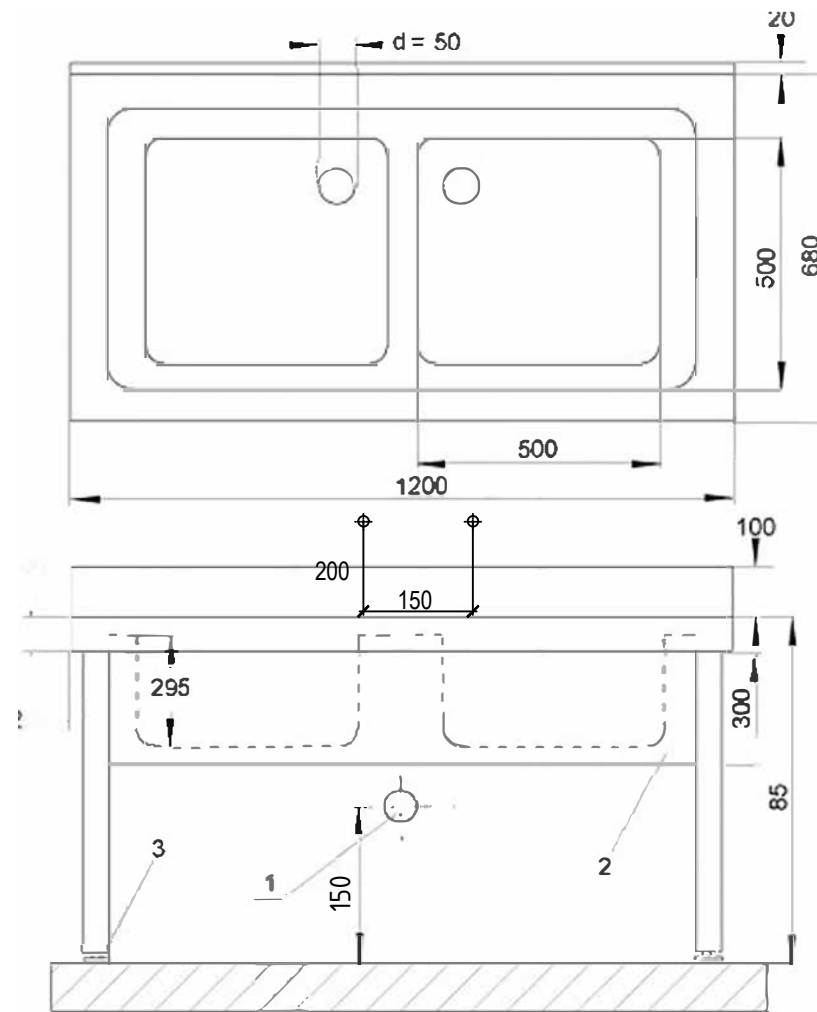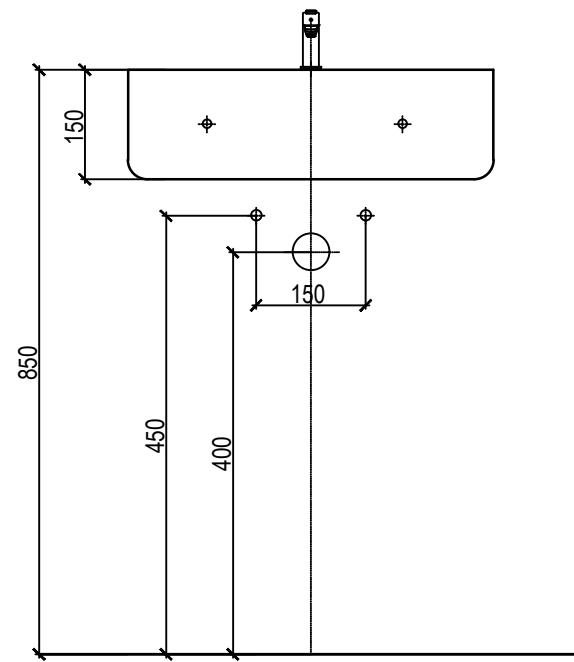

- 1 - отток
- 2 - облицование
- 3 - регулировочные винты



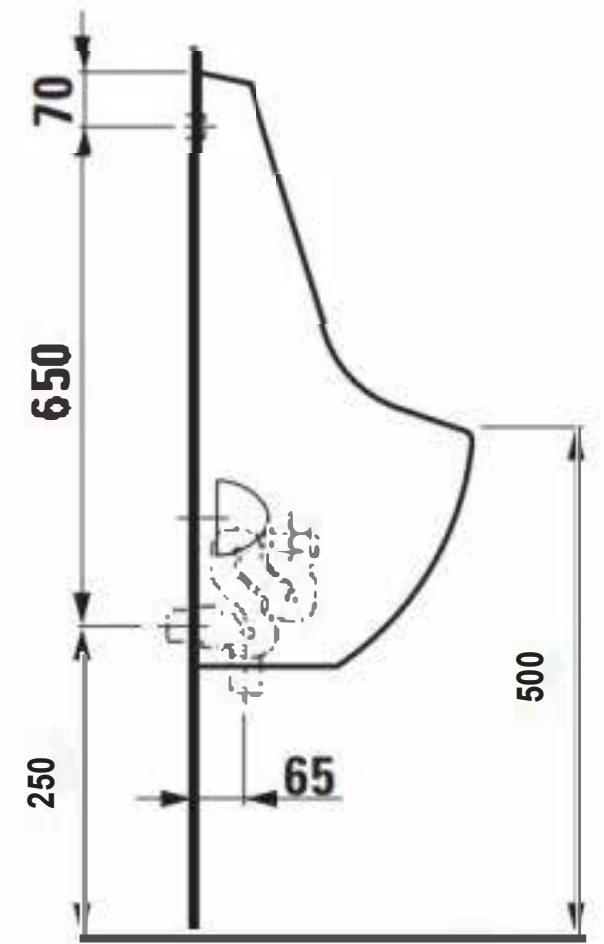


Схема установки Раковина
индивидуального изготовления
искусственный камень
Тип 3

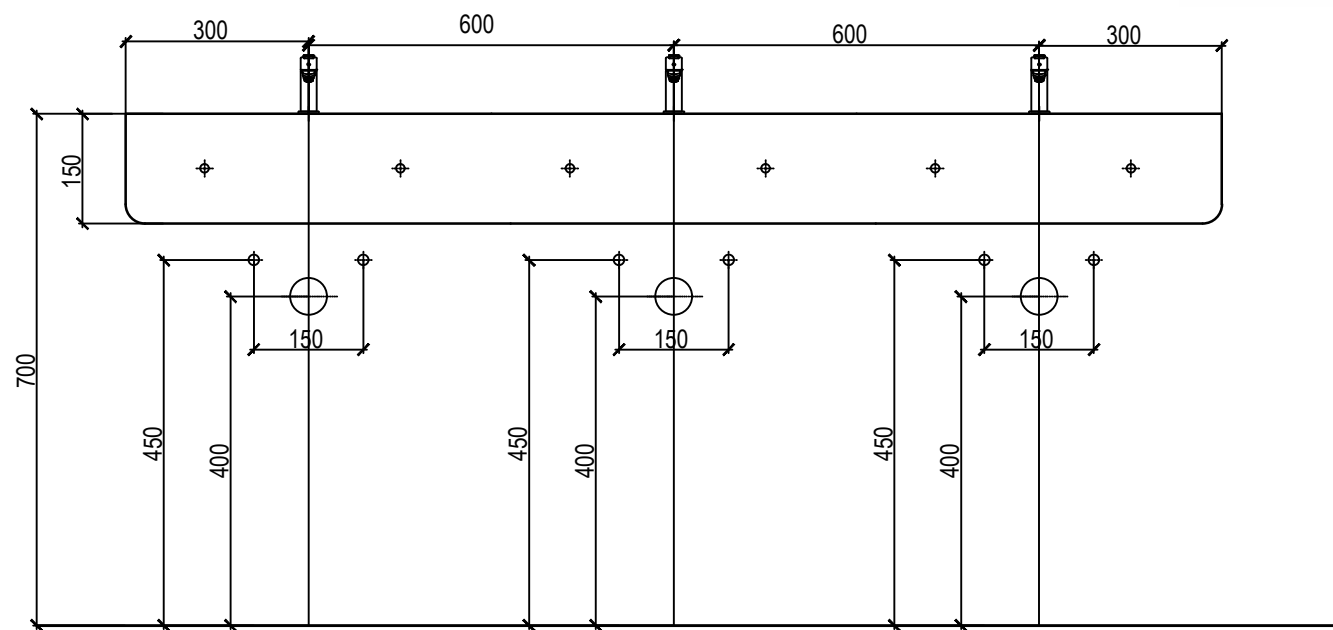

Подключения для Модуля кухонного

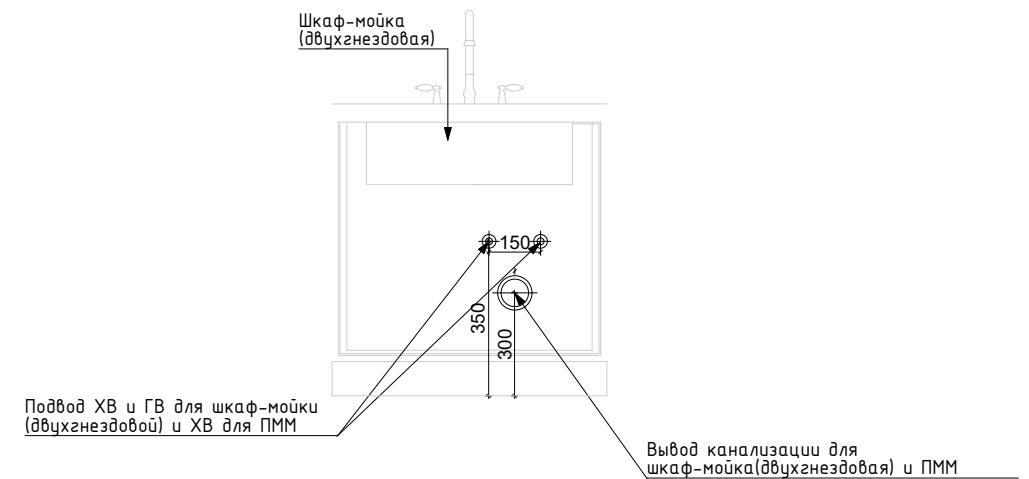


Примечание:


- 1. Душевой смеситель ставится на высоте 1500 мм
- 2. Унитаз на высоте 380 мм до кромки унитаза
- Высоту сантехприборов применять согласно "СП 73.13330.2016. СНиП 3.05.01-85. Свод правил. Внутренние санитарно-технические системы зданий"

Изм.	Кол.уч.	Лист	№	Подп.	Дата	696/П-25-АНО-Р-ВК	Лист
							2

План

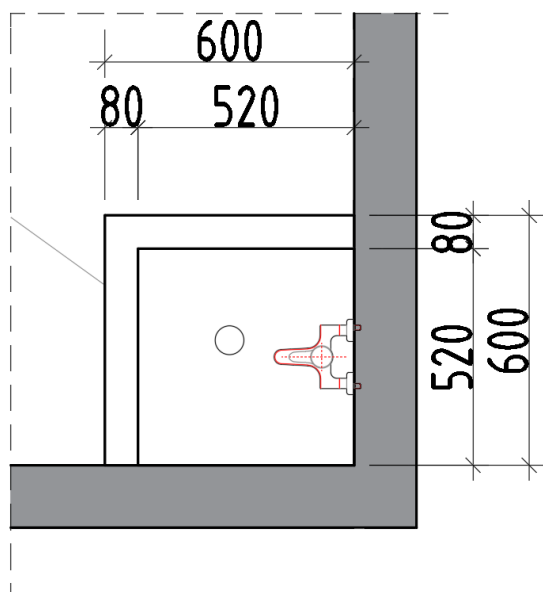

Вид сбоку

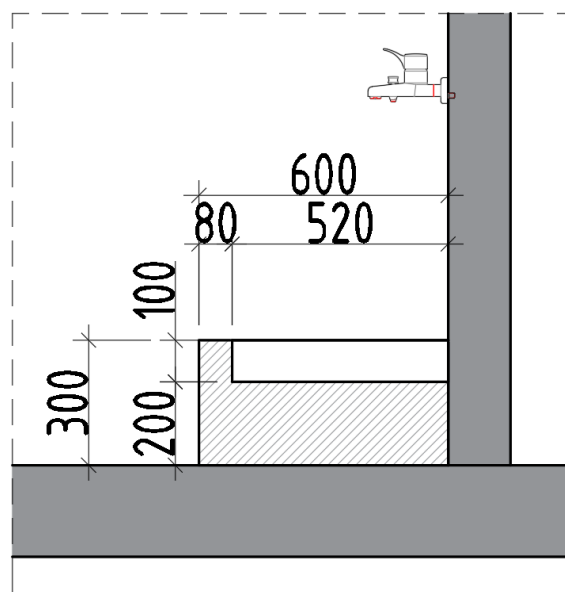

Поз.	Наименование и техническая характеристика	Тип, марка, обозначение документа, опросного листа	Код продукции	Поставщик	Единица измерения	Кол.	Масса 1 ед., кг	Примечание
	Хозяйственно-питьевой водопровод В1							
	Трубопроводная арматура							
	Кран шаровый латунный полнопроходной ВР/ВР: 1/2" (Ø15)	11Б27п Ду15		VALFEX (Россия)	шт.	129		
	Кран шаровый латунный полнопроходной ВР/ВР: 3/4" (Ø20)	11Б27п Ду20		VALFEX (Россия)	шт.	30		
	Кран шаровой латунный полнопроходный ВР/ВР: 1" (Ø25)	11Б27п Ду25		VALFEX (Россия)	шт.	2		
	Кран шаровой латунный полнопроходный ВР/ВР: (Ø32)	11Б27п Ду32		VALFEX (Россия)	шт.	4		
	Кран шаровой латунный полнопроходный ВР/ВР: (Ø50)	11Б27п Ду50		VALFEX (Россия)	шт.	1		
	Подводка для воды (гайка-гайка 1/2; 100 см;(к унитазу и писсуару)	04806		AQUALINE	шт.	44		
	Кран поливочный со штуцером для присоединения шланга, Ø25	BVR-VR Ду25		Ридан	шт.	4		
	Клапан обратный латунный 1/2"	VF.161.N.012		VALFEX (Россия)	шт.	18		
	Клапан обратный латунный 3/4"	VF.161.N.034		VALFEX (Россия)	шт.	78		
	Автоматический воздухоотводчик Ду15	VF.502.NV.04		VALFEX (Россия)	шт.	17		
	Трубопроводы							
	Трубы стальные водогазопроводные оцинкованные обыкновенные Ду20	ГОСТ 3262-75			м.п.	200		
	Трубы стальные водогазопроводные оцинкованные обыкновенные Ду25	ГОСТ 3262-75			м.п.	36		
	Трубы стальные водогазопроводные оцинкованные обыкновенные Ду32	ГОСТ 3262-75			м.п.	110		

Примечание:

						696/П-25-АНО-Р-ВК.СО			
						Капитальный ремонт Государственного бюджетного общеобразовательного учреждения города Москвы "Школа №1282 "Сокольники" по адресу: г. Москва, ул. Барболина, д.1, корп.1			
Изм.	Кол.уч	Лист	№ док	Подп.	Дата				
Разработал	Брицникин				06.26	Капитальный ремонт	Стадия	Лист	Листов
ГИП		Гулько			06.26		Р	1	4
						Спецификация оборудования, изделий и материалов			
Н.контроль	Гулько				06.26				

Согласовано	Взам. Инв. №	Подп. и дата	Инв. № Подл.	Поз.	Наименование и техническая характеристика	Тип, марка, обозначение документа, опросного листа	Код продукции	Поставщик	Единица измерения	Кол.	Масса 1 ед., кг	31 Примечание
					Трубы стальные водогазопроводные оцинкованные обыкновенные Ду40	ГОСТ 3262-75			м.п.	23		
					Трубы стальные водогазопроводные оцинкованные обыкновенные Ду50	ГОСТ 3262-75			м.п.	56		
					Трубопровод из полипропилена, армированный стекловолокном PP-R SDR7,4 (PN20) Ø 20x2,8	ГОСТ 32415-2013		VALFEX (Россия)	м.п.	210		включая фасонные части
					Трубопровод из полипропилена, армированный стекловолокном PP-R SDR7,4 (PN20) Ø 25x2,5	ГОСТ 32415-2013		VALFEX (Россия)	м.п.	88		включая фасонные части
					Трубопровод из полипропилена, армированный стекловолокном PP-R SDR7,4 (PN20) Ø 32x4,4	ГОСТ 32415-2013		VALFEX (Россия)	м.п.	10		включая фасонные части
					Трубы стальные водогазопроводные оцинкованные обыкновенные Ду65	ГОСТ 3262-75			м.п.	8		
					Трубы стальные водогазопроводные оцинкованные обыкновенные Ду100	ГОСТ 3262-75			м.п.	15		
					Трубопроводная теплоизоляция, δ=9 мм, для труб Ду20	K-flex ST 09x020	K-flex-трубка	«K-flex»	м.п.	200		
					Трубопроводная теплоизоляция δ=9 мм, для труб Ду25	K-flex ST 09x025	K-flex-трубка	«K-flex»	м.п.	36		
					Трубопроводная теплоизоляция δ=9 мм, для труб Ду32	K-flex ST 09x032	K-flex-трубка	«K-flex»	м.п.	110		
					Трубопроводная теплоизоляция δ=9 мм, для труб Ду40	K-flex ST 09x040	K-flex-трубка	«K-flex»	м.п.	23		
					Трубопроводная теплоизоляция δ=9 мм, для труб Ду50	K-flex ST 09x050	K-flex-трубка	«K-flex»	м.п.	56		
					Трубопроводная теплоизоляция δ=9 мм, для труб Ду65	K-flex ST 09x050	K-flex-трубка	«K-flex»	м.п.	8		
					Трубопроводная теплоизоляция δ=9 мм, для труб Ду100	K-flex ST 09x050	K-flex-трубка	«K-flex»	м.п.	15		
					Шаровый кран с электроприводом ду 20				шт.	2		
					Водопровод горячей воды с циркуляцией – Т3, Т4							
					Трубопроводная арматура							
					Кран шаровый латунный полнопроходной ВР/ВР: 1/2" (Ø15)	11Б27п Ду15		VALFEX (Россия)	шт.	71		
					Кран шаровой латунный полнопроходный ВР/ВР: 3/4" (Ø20)	11Б27п Ду20		VALFEX (Россия)	шт.	45		
					Кран шаровой латунный полнопроходный ВР/ВР: 1" (Ø25)	11Б27п Ду25		VALFEX (Россия)	шт.	7		
					Кран шаровой латунный полнопроходный ВР/ВР: 1 1/4" (Ø32)	11Б27п Ду32		VALFEX (Россия)	шт.	4		
					Клапан балансировочный, ручной Ду20	MSV-BD Ду20		Ридан	шт.	10		
	Клапан балансировочный, ручной Ду25	MSV-BD Ду25		Ридан	шт.	4						
	Термостатический смесительный клапан/смеситель 1/2"	TMV811-02		TIM	шт.	30						
	Термостатический смесительный клапан/смеситель 3/4"	TMV811-03		Zeissler	шт.	10						
	Клапан обратный латунный 1/2"	VF.161.N.012		VALFEX (Россия)	шт.	78						
	Клапан обратный латунный 3/4"	VF.161.N.034		VALFEX (Россия)	шт.	18						
						696/П-25-АНО-Р-ВК.СО						Лист
												2
Изм.	Кол.уч	Лист	№	Подп.	Дата							

Согласовано			Взам. Инв. №			Подп. и дата			Инв. № Подл.			32
Поз.	Наименование и техническая характеристика	Тип, марка, обозначение документа, опросного листа	Код продукции	Поставщик	Единица измерения	Кол.	Масса 1 ед., кг	Примечание				
	Автоматический воздухоотводчик Ду15	VF.502.NV.04		VALFEX (Россия)	шт.	34						
	Трубопроводы											
	Трубы стальные водогазопроводные оцинкованные обыкновенные Ду20	ГОСТ 3262-75			м.п.	246						
	Трубы стальные водогазопроводные оцинкованные обыкновенные Ду25	ГОСТ 3262-75			м.п.	154						
	Трубы стальные водогазопроводные оцинкованные обыкновенные Ду32	ГОСТ 3262-75			м.п.	189						
	Трубы стальные водогазопроводные оцинкованные обыкновенные Ду50	ГОСТ 3262-75			м.п.	80						
	Трубопровод из полипропилена, армированный стекловолокном PP-R SDR7,4 (PN20) Ø 20x3,4	ГОСТ 32415-2013		VALFEX (Россия)	м.п.	180		включая фасонные части				
	Трубопровод из полипропилена, армированный стекловолокном PP-R SDR7,4 (PN20) Ø 25x4,2	ГОСТ 32415-2013		VALFEX (Россия)	м.п.	68		включая фасонные части				
	Трубопровод из полипропилена, армированный стекловолокном PP-R SDR7,4 (PN20) Ø 32x4,4	ГОСТ 32415-2013		VALFEX (Россия)	м.п.	10		включая фасонные части				
	Материалы											
	Трубопроводная теплоизоляция, δ=13 мм для труб Ду20	K-flex ST 13x020	K-flex-трубка	«K-flex»	м.п.	478						
	Трубопроводная теплоизоляция δ=13 мм для труб Ду25	K-flex ST 13x025	K-flex-трубка	«K-flex»	м.п.	163						
	Трубопроводная теплоизоляция δ=13 мм для труб Ду32	K-flex ST 13x032	K-flex-трубка	«K-flex»	м.п.	189						
	Трубопроводная теплоизоляция δ=13 мм для труб Ду50	K-flex ST 13x050	K-flex-трубка	«K-flex»	м.п.	80						
	Крепления											
	Металлоконструкции для крепления стальных трубопроводов				кг	190						
	Комплект крепления для полипропиленовых труб											
	Ø20x2,8	9000000020		Политэк	шт.	210						
	Ø25x3,5	9000000025		Политэк	шт.	110						
	Ø32x4,4	9000000032		Политэк	шт.	10						
	Санитарно-техническое оборудование											
	Душевая стойка для подачи воды, хром глянec, комплектно с монтажная часть ole для душевого гарнитура, хром и встроенный однорычажный смеситель для душа с переключателем на два потока, хром глянec	69356KM.21.018 2299KM.21.018 69370KM.21.018		Керама Марацци (Россия)	шт	6		или аналог				
			Изм.	Кол.уч	Лист	№	Подп.	Дата	696/П-25-АНО-Р-ВК.СО			Лист
												3

[illegible]

Поз.	Наименование и техническая характеристика	Тип, марка, обозначение документа, опросного листа	Код продукции	Поставщик	Единица измерения	Кол.	Масса 1 ед., кг	Примечание
	<u>Канализация бытовая К1, К1Н</u>							
	<u>Сантехническое оборудование</u>							
29.	Унитаз подвесной	PLAZA MODERN		Kerama Marazzi	шт.	35		
30.	Инсталляция для подвесного унитаза, с кнопкой управления для скрытых систем инсталляции, хром-глянец	M101\1120KM+M571KMERN		Kerama Marazzi	шт.	36		
31.	Унитаз подвесной для МГН				шт.	1		
32.	Писсуар подвесной с крепежом, белый глянцевый, комплектно с системой смыва и инсталляцией	PROC.ur.02		Kerama Marazzi	шт.	8		
33.	Инсталляция для подвесного писсуара,с кнопкой смыва				компл.	8		или аналог
34.	Душевой поддон в строительном исполнении	APZ10-750KM		Kerama Marazzi	шт.	12		Закупка ДИОМ
35.	кухонный гарнитур				шт.	3		Закупка ДИОМ
36.	Тумба с раковиной в комплекте с локтевым смесителем				шт.	2		Закупка ДИОМ
37.	Ванна котломоечная двухсекционная					2		Закупка ДИОМ
38.	Ванна моечная односекционная тип 1				шт.	1		Закупка ДИОМ
39.	Ванна моечная двухсекционная тип 1				шт.	1		Закупка ДИОМ
40.	Ванна моечная трехсекционная тип 2				шт.	1		Закупка ДИОМ
41.	Тумба медицинская с двойной мойкой в комплекте с локтевым смесителем				шт.	1		Закупка ДИОМ
42.	Двойная мойка в кабинет врача				шт.	1		Закупка ДИОМ
	Раковина индивидуального изготовления искусственный камень				шт.	9		
	Тумба с раковиной				шт.	25		Закупка ДИОМ
	Рукомойник				шт.	6		
	Раковина мебельная\подвесная 50, белая глянцевая	PRO.WB.50		Kerama Marazzi	шт.	16		
	Раковина для МГН	5289B003-0001		Vitra	шт.	1		

696/П-25-АНО-Р-ВК.СО

Лист

3

--	--	

Согласовано			Взам. Инв. №			Подп. и дата			Инв. № Подл.			36
Поз.	Наименование и техническая характеристика	Тип, марка, обозначение документа, опросного листа	Код продукции	Поставщик	Единица измерения	Кол.	Масса 1 ед., кг	Примечание				
	Канализация дренажная напорная – КдН											
	Оборудование											
	Насос дренажный для монтажа в прямке, Q=10,0 м³/час; H=10,00 м; U=380В; N=1,1 кВт	ГНОМ 10–10Г или аналог		Россия	шт.	7						
	Насос дренажный для монтажа в прямке, Q=10,0 м³/час; H=10,00 м; U=380В; N=1,1 кВт	ГНОМ 10–10 или аналог		Россия	шт.	2		(1раб+рез)				
	Трубопроводная арматура											
	Кран шаровой латунный муфтовый Ø40	11627фтМ Ду40		Valfex	шт.	8						
	Клапан обратный латунный муфтовый Ø 40	VF.161.N.114 Ду40		Valfex	шт.	8						
	Трубопроводы											
	Трубопровод из стальных водогазопроводных оцинкованных труб Ø40	ГОСТ 3262–75			м.п.	64						
	Крепления											
	Хомут для труб Ду=40 мм с анкерными болтами и гайками	ТУ 4926-010-41989945-98		Россия	шт.	36						
	Производственная канализация КЗ, КЭН											
	Детали трубопроводов											
	Ревизия SML											
	Ø100				шт.	8						
	Ревизия-прочистка для труб				шт.	6						
	Противопожарная муфта											
	Ø50				шт.	50						
	Ø100				шт.	8						
	Вентиляционный клапан DN100 мм			Политэк (Россия)	шт.	3						
	Муфта переходная с ПВХ/ПП на чугун/сталь D110/100 с манжетой для внутренней канализации			Политэк (Россия)	шт.	6						
												Лист
						696/П-25-АНО-Р-ВК.СО						3
			Изм.	Кол.уч.	Лист	№	Подп.	Дата				

Согласовано	</
-------------	--	--	----

Согласовано	Взам. Инв. №	Подп. и дата	Инв. № Подл.	Поз.	Наименование и техническая характеристика	Тип, марка, обозначение документа, опросного листа	Код продукции	Поставщик	Единица измерения	Кол.	Масса 1 ед., кг	39 Примечание		
					Оборудование									
					Тумба с раковиной			Керама Марацци	шт.	29		Закупка департамента		
					Кухонный гарнитур				шт.	1		Закупка департамента		
					Тумба с раковиной в комплекте с локтевым смесителем				шт.	2		Закупка департамента		
					Тумба медицинская с двойной мойкой в комплекте с локтевым смесителем				шт.	1		Закупка департамента		
					Питьевой фонтанчик				шт.	8		Закупка департамента		
					Двойная мойка в кабинет врача				шт.	1		Закупка департамента		
					Ванна котломоечная двухсекционная				шт.	2		Закупка департамента		
					Ванна моечная односекционная тип 1				шт.	2		Закупка департамента		
					Ванна котломоечная двухсекционная				шт	1		Закупка департамента		
					Ванна моечная двухсекционная тип 1				шт	1		Закупка департамента		
					Ванна моечная трехсекционная тип 2				м.п.	1		Закупка департамента		
					Рукомойник				шт	7		Закупка департамента		
					Смеситель с душирующим устройством				шт	10		Закупка департамента		
					Смеситель для рукомойника				шт	7		Закупка департамента		
						696/П-25-АНО-Р-ВК.СО						Лист		
												6		
Изм.	Кол.уч	Лист	№	Подп.	Дата									

[illegible]


[illegible]

[illegible]

[illegible]

ЛИСТ ПОДБОРА

Насосная установка повышения
давления **ANTARUS X 2**
MLV6-2/01

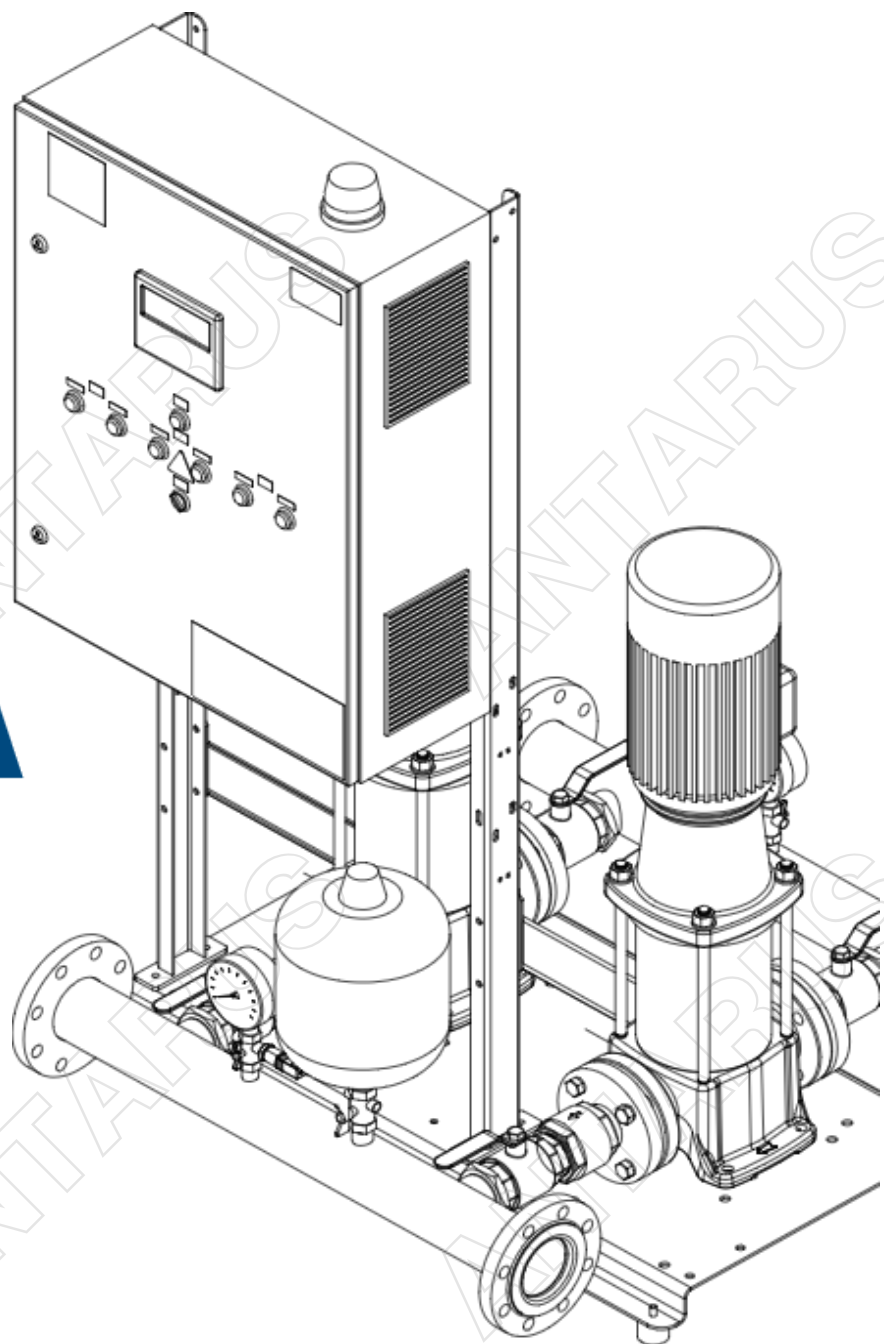

Артикул установки
660416




Онлайн-подбор
установки
по параметрам
за 30 секунд




Гарантия 5 лет
на установки
на насосах
ANTARUS



Производство
стандартных
моделей
2-3 недели

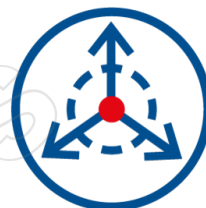

Онлайн-доступ
к BIM-моделям
всех продуктов
ANTARUS

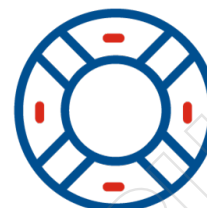



Сервисная
поддержка
по всей
России

*на изображении условно отображена линейка 2.0, чертеж вашей установки см. ниже

Насосная установка повышения давления **ANTARUS X 2 MLV6-2/01**



Артикул: 660416

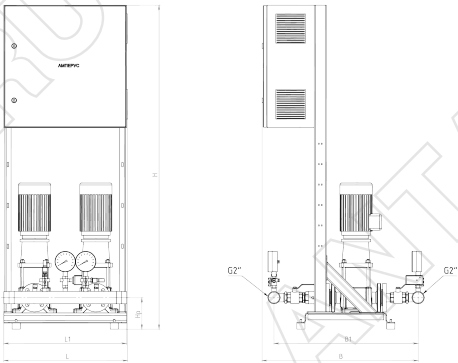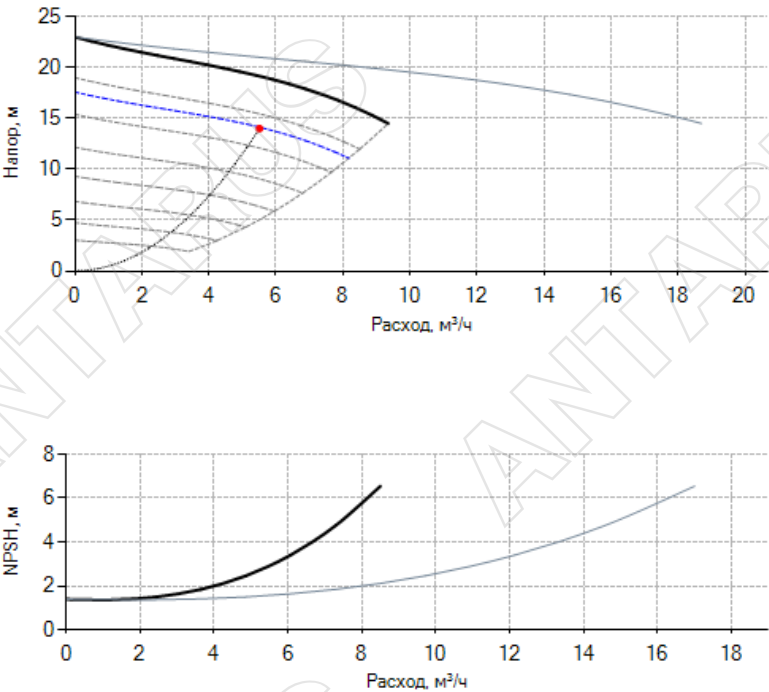

Запрашиваемые параметры:

Расход	5,51 м³/ч
Напор	14 м
Температура воды	0-70 °С

Фактические параметры:

Расход	5,51 м³/ч
Напор	14 м
Частота вращ. э/д	2 789 об/мин
Мощность на валу	0,29 кВт
Макс. уровень шума	53 дБа
Макс. раб. давление	16 бар
NPSH треб.	4,22 м
КПД насоса, %	65,6

Данные электродвигателя (одного):

Ном. мощность	0,55 кВт
Ном.напряжение	3х380 В, 50 гц
Ном. ток	1,24 А

Данные станции:

Вес	111 кг
Подключение	G 2"

Габариты установки:

L	600 мм
L1	600 мм
H	1 590 мм
Hn	154 мм
B	777 мм
B1	659 мм
B2	30 мм

Внимание! Фактические размеры и внешний вид установки могут незначительно отличаться от представленных.

Дополнительно:

№ п/п	Наименование	Количество	Ед. изм.
1	Основной насос ANTARUS MLV6-2/01-14	1	шт.
2	Резервный насос ANTARUS MLV6-2/01-14	1	шт.
3	Датчик давления	1	шт.
4	Манометр	2	шт.
5	Шаровой кран DN 32	4	шт.
6	Клапан обратный DN 32	2	шт.
7	Всасывающий коллектор из нерж. стали AISI 304 G 2"	1	шт.
8	Напорный коллектор из нерж. стали AISI 304 G 2"	1	шт.
9	Комплект виброопор	1	компл.
10	Шкаф управления	1	шт.

Описание

Готовая к подключению установка повышения давления. Комплект поставки:


- многоступенчатые насосы;
- всасывающий и напорный коллекторы из нержавеющей стали;
- рама-основание на регулируемых по высоте виброопорах;
- комплект запорной арматуры на всасывающих и напорных патрубках насосов, обратные клапаны на напорных патрубках;
- манометры, датчик давления, реле давления на всасывающем трубопроводе с диапазоном до 0,8МПа
- защита от «сухого» хода;

Автоматизация насосной станции ANTARUS X. Основные функции

1. Управление в автоматическом режиме 2-6 насосами
2. Поддержание давления при помощи преобразователей частоты и каскадного подключения/отключения насосов с использованием датчика давления
3. Выравнивание моторесурса насосов (ротация)
4. Защита насосов от сухого хода
5. Защита двигателей от перегрева, от перегрузки по току, от некачественного входного напряжения
6. Подключение резервных насосов при аварии основных
7. Удаленная диспетчеризация при помощи стандарта RS-485 по протоколу ModBus RTU



Схема внешних подключений

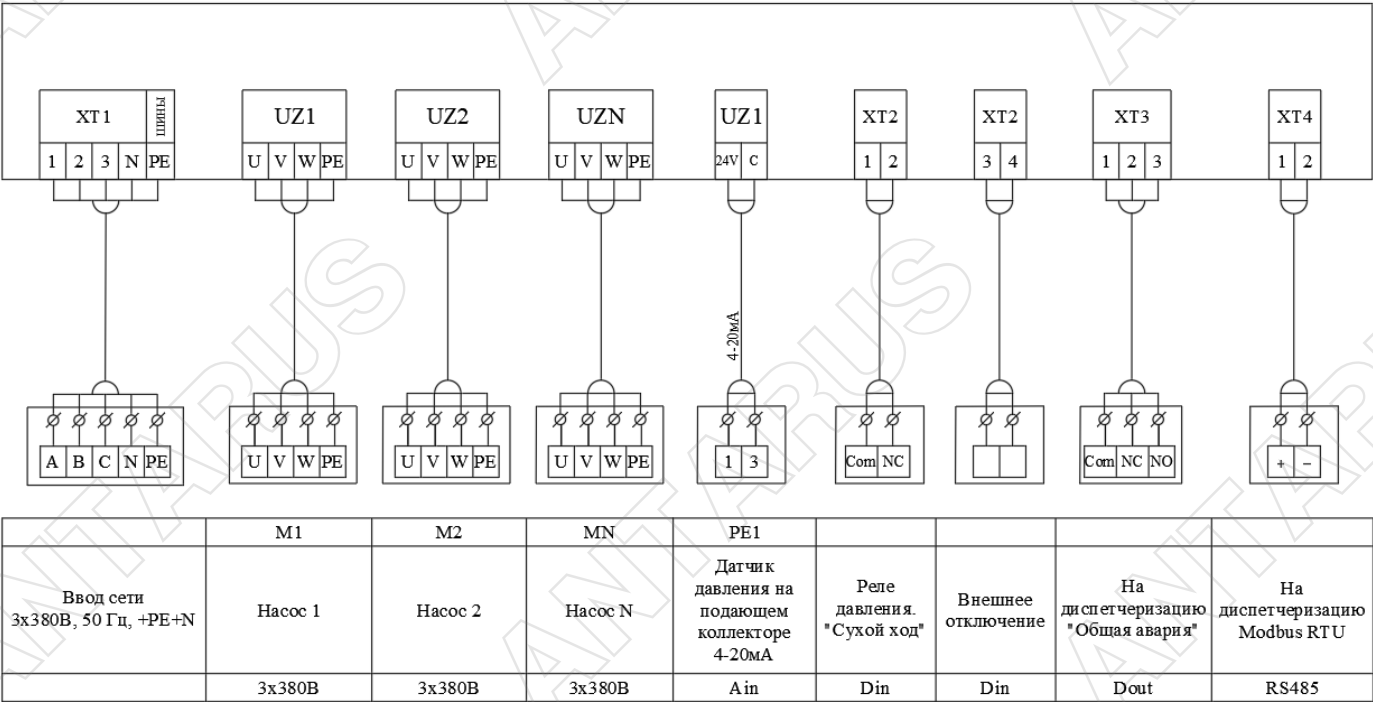



Online подбор за 30 секунд

Программа подбора насосных установок
ANTARUS SEARCH
search.antarus.su



Программа «Умная вода»

Программа для проектирования систем
внутреннего водопровода и канализации зданий
smartwater.su



Online библиотека

Документация, чертежи и модели по всем
продуктам ANTARUS
search.antarus.su/library

Для консультаций и заказа обращайтесь в ближайшее
к Вам отделение компании «Элита»

Москва
(495) 725-09-52

Екатеринбург
(343) 287-05-90

Омск
(3812) 50-21-48

Тюмень
(3452) 50-01-77

Санкт-Петербург
(812) 702-42-42

Иркутск
(914) 910-17-03

Пермь
(342) 254-55-76

Уфа
(347) 287-81-89

Архангельск
(911) 270-63-74

Казань
(843) 570-54-54

Ростов-на-Дону
(863) 206-16-26

Хабаровск
(4212) 75-50-95

Барнаул
(3852) 28-38-01

Краснодар
(861) 277-46-99

Самара
(846) 372-38-83

Челябинск
(351) 268-92-05

Владивосток
(4232) 79-00-79

Красноярск
(391) 274-60-02

Саратов
(8452) 57-69-83

Ярославль
(4852) 58-30-51

Волгоград
(8442) 26-00-01

Нижний Новгород
(831) 220-24-33

Сургут
(3462) 28-11-71

Воронеж
(473) 258-95-17

Новосибирск
(383) 354-05-34

Тверь
(4822) 65-50-19