

2026

Согласовано				
	Взам. инв. №			
	Погр. и дата			
	Инв. Неподр.			

Основной комплект рабочих чертежей комплекта ОВ			
№	Наименование	Формат	Прим.
1	Общие указания	A3	
2	Характеристики вентиляционного оборудования	A3	
3	План 1-ого этажа	A2	
4	План 2-ого этажа	A2	
5	План 3-ого этажа	A2	
6	План 4-ого этажа	A2	
7	План тех. этажа	A2	
8	План кровли	A2	
9	Аксонометрии систем К1-К5	A2	
10	Аксонометрии систем К6-К8рез	A3	

Ведомость прилагаемых и ссылочных документов		
Обозначение	Наименование	Прим.
	Ссылочные документы	
Серия 5904-1	Крепления воздуховодов	
Серия 5904-51	Зонты и дефлекторы	
	Прилагаемые документы	
696/Р-24-АНО-ПДВ.С	Спецификация оборудования и материалов	

Общие указания
1. Общие указания
Рабочая документация марки ПДВ разработана на основании проектных решений, принятых в проектной документации стадии П, задания на проектирование и исходных данных смежных разделов.
Объект: ГБОУ Школа № 1282 «Сокольники», г. Москва, ул. Барболина, д. 1, корп. 1.
Настоящим проектом решаются вопросы противодымной вентиляции проектируемого объекта. Проект выполнен на основании:

- утвержденной проектной документации;
- архитектурно-строительных чертежей;
- технологической части.

При разработке проекта учтены требования нормативных документов, в том числе:

- СП 60.13330.2020 «Отопление, вентиляция и кондиционирование воздуха»;
- СП 7.13130.2013 «Отопление, вентиляция и кондиционирование. Требования пожарной безопасности»;
- СП 131.13330.2020 «Строительная климатология»;
- СП 118.13330.2022 «Общественные здания и сооружения»;
- СП 51.13330.2011 «Защита от шума»;
- СП 73.13330.2016 «Внутренние санитарно-технические системы зданий»;
- СП 2.4.3648-20 «Санитарно-эпидемиологические требования к организациям воспитания и обучения, отдыха и оздоровления детей и молодежи»;
- СанПиН 1.2.3685-21 «Гигиенические нормативы и требования к обеспечению безопасности и (или) безвредности для человека факторов среды обитания»;
- ГОСТ 30494-2011 «Здания жилые и общественные. Параметры микроклимата в помещениях»;
- ГОСТ 12.1.005-88 «ССБТ. Общие санитарно-гигиенические требования к воздуху рабочей зоны».

За относительную отметку 0,000 принят уровень чистого пола первого этажа.

2. Климатологические данные района строительства

Расчетное барометрическое давление – 997 гПа. Расчетные параметры наружного воздуха:

а) Теплый период года:

- температура для расчета кондиционирования +23,0 °С;
- относительная влажность для кондиционирования 57 %.

б) Холодный период года:

- температура для расчета отопления и вентиляции –26 °С;
- относительная влажность 84 %.

Расчетные параметры внутреннего воздуха (температура воздуха в обслуживаемой зоне) в холодный период года приняты:


- учебные классы, административные помещения – +20 °С;
- актовый зал (многосветное пространство) – +20 °С;
- спортивные залы – +18 °С (гимнастический зал – +20 °С);
- раздевалки – +25 °С;
- помещения медблока – +23 °С;
- обеденный зал – +18 °С;
- производственные помещения пищеблока – +19 °С.

3. Все системы должны быть смонтированы в соответствии с СП 73.13330.2016,а также требованиям и рекомендациям производителя. При прокладке дренажа учесть уклон 0,01 в сторону канализационного стояка. Зазоры и отверстия в местах пропуска коммуникаций через конструкции следует заделать негорючим материалом; герметизацию продиваемых проемов после окончания монтажа восстановить.


						696/Р-24-АНО-ОВ3			
						Капитальный ремонт Государственного бюджетного общеобразовательного учреждения города Москвы Школа 1282 Сокольники по адресу: г. Москва, ул. Бараболина, д.1, корп.1			
Изм.	Кол. уч	Лист	№	Погр.	Дата	Капитальный ремонт	Стадия	Лист	Листов
Разраб.		Серегин			07.09.26		Р	1	10
Проверил		Селезнев			07.09.26				
ГИП					07.09.26	Общие данные	ООО "Проект+		
Н. контр.		Селезнев			07.09.26				

Согласовано				
Взам. инв. №	Погр. и дата		Инв. №подл.	

Характеристика отопительно-вентиляционного оборудования																									
Обозначение системы	Кол. систем	Наименование обслуживаемого помещения (технологического оборудования)	Тип установки	Вентилятор							Электродвигатель			Охладитель				Фильтр					Примечание		
				Тип, исполнение по взрывозащите	№	Схема исполнения	Положение	L, м3/ч	P, Па	n, об/мин.	Тип, исполнение по взрывозащите	N, кВт	n, об/мин.	Тип	Тем-ра, о м/до	Хо-ть, кВт	Δ кПа	Тип	Кол-во	P, Па	Концентрация, мг/м3				
																					начальная	конечная			
K1	1	Актный зал	ND-ICR-56C-V/X	Внутр	-	-	-	-	-	-	0.02		фреон	+26 / 20	6,3000	-							4 шт		
			ND-ON-335B-PRO/X	Вн	-	-	-	-	-	-	8.35		фреон	+26 / 20	33,5000										
K2	1	Обеденный зал	ND-ICR-56C-V/X	Внутр	-	-	-	-	-	-	0.02		фреон	+26 / 20	6,3000								2 шт		
			ND-ISR-36C-V/X	Внутр	-	-	-	-	-	-	0.02		фреон	+26 / 20	3,6000										
			ND-ISR-22C-V/X	Внутр	-	-	-	-	-	-	0.01		фреон	+26 / 20	2,2000										
			ND-ON-224B-3/X	Вн	-	-	-	-	-	-	6.74		фреон	+26 / 20	22,4000										
K3	1	Пом.322	ND-ICR-56C-V/X	Внутр	-	-	-	-	-	-	0.02		фреон	+26 / 20	6,3000										
			ND-ISR-36C-V/X	Внутр	-	-	-	-	-	-	0.02		фреон	+26 / 20	3,6000								3 шт		
			ND-ISR-22C-V/X	Внутр	-	-	-	-	-	-	0.01		фреон	+26 / 20	2,2000								2 шт		
			ND-ON-224B-3/X	Вн	-	-	-	-	-	-	6.74		фреон	+26 / 20	22,4000										
K4	1	Пом.424	ND-ISR-36C-V/X	Внутр	-	-	-	-	-	-	0.02		фреон	+26 / 20	3,6000								4 шт		
			ND-ON-140B-3/X	Вн	-	-	-	-	-	-	3.96		фреон	+26 / 20	14										
K5	1	Пом. 140,145,214	ND-ISR-45C-V/X	Внутр	-	-	-	-	-	-	0.03		фреон	+26 / 20	4,5000										
			ND-ISR-36C-V/X	Внутр	-	-	-	-	-	-	0.02		фреон	+26 / 20	3,6000										
			ND-ISR-22C-V/X	Внутр	-	-	-	-	-	-	0.01		фреон	+26 / 20	2,2000										
			ND-ON-100B-1/X	Вн	-	-	-	-	-	-	2.90		фреон	+26 / 20	3,2000										
K6/K6рез	2	Пом. 205,306,406	ND-IW-56C-V/X	Внутр	-	-	-	-	-	-	0.03		фреон	+26 / 18	5,6000								4 шт		
			ND-ON-255B-PRO/X	Вн	-	-	-	-	-	-	5.31		фреон	+26 / 18	25,2000										
K7/K7рез	2	Пом 103	ND-IW-45C-V/X	Внутр	-	-	-	-	-	-	0.03		фреон	+26 / 18	4,5000										
			ND-ON-080B-1/X	Вн	-	-	-	-	-	-	2.30		фреон	+26 / 18	8										
K8/K8рез	2	Пом 144,203,306,407	ND-IW-45C-V/X	Внутр	-	-	-	-	-	-	0.03		фреон	+26 / 18	4,5000								4 шт		
			ND-ON-140B-3/X	Вн	-	-	-	-	-	-	3.96		фреон	+26 / 20	14										
																		696/P-24-ANO-OB3							
																		Капитальный ремонт Государственного бюджетного общеобразовательного учреждения города Москвы Школа 1282 Сокольники по адресу: г. Москва, ул. Бараболина, д.1, корп.1							
												Изм.	Кол. уч.	Лист	№	Подп.	Дата	Капитальный ремонт					Стация	Лист	Листов
												Разраб.	Серегин			07.09.26	Р						2		
												Проверил	Селезнев			07.09.26									
												ГИП				07.09.26									
																	Характеристики вентиляционного оборудования					ООО "Проект+			
												Н. контр.	Селезнев			07.09.26									

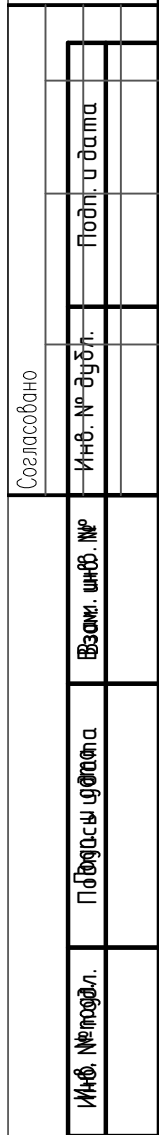


Формат A1

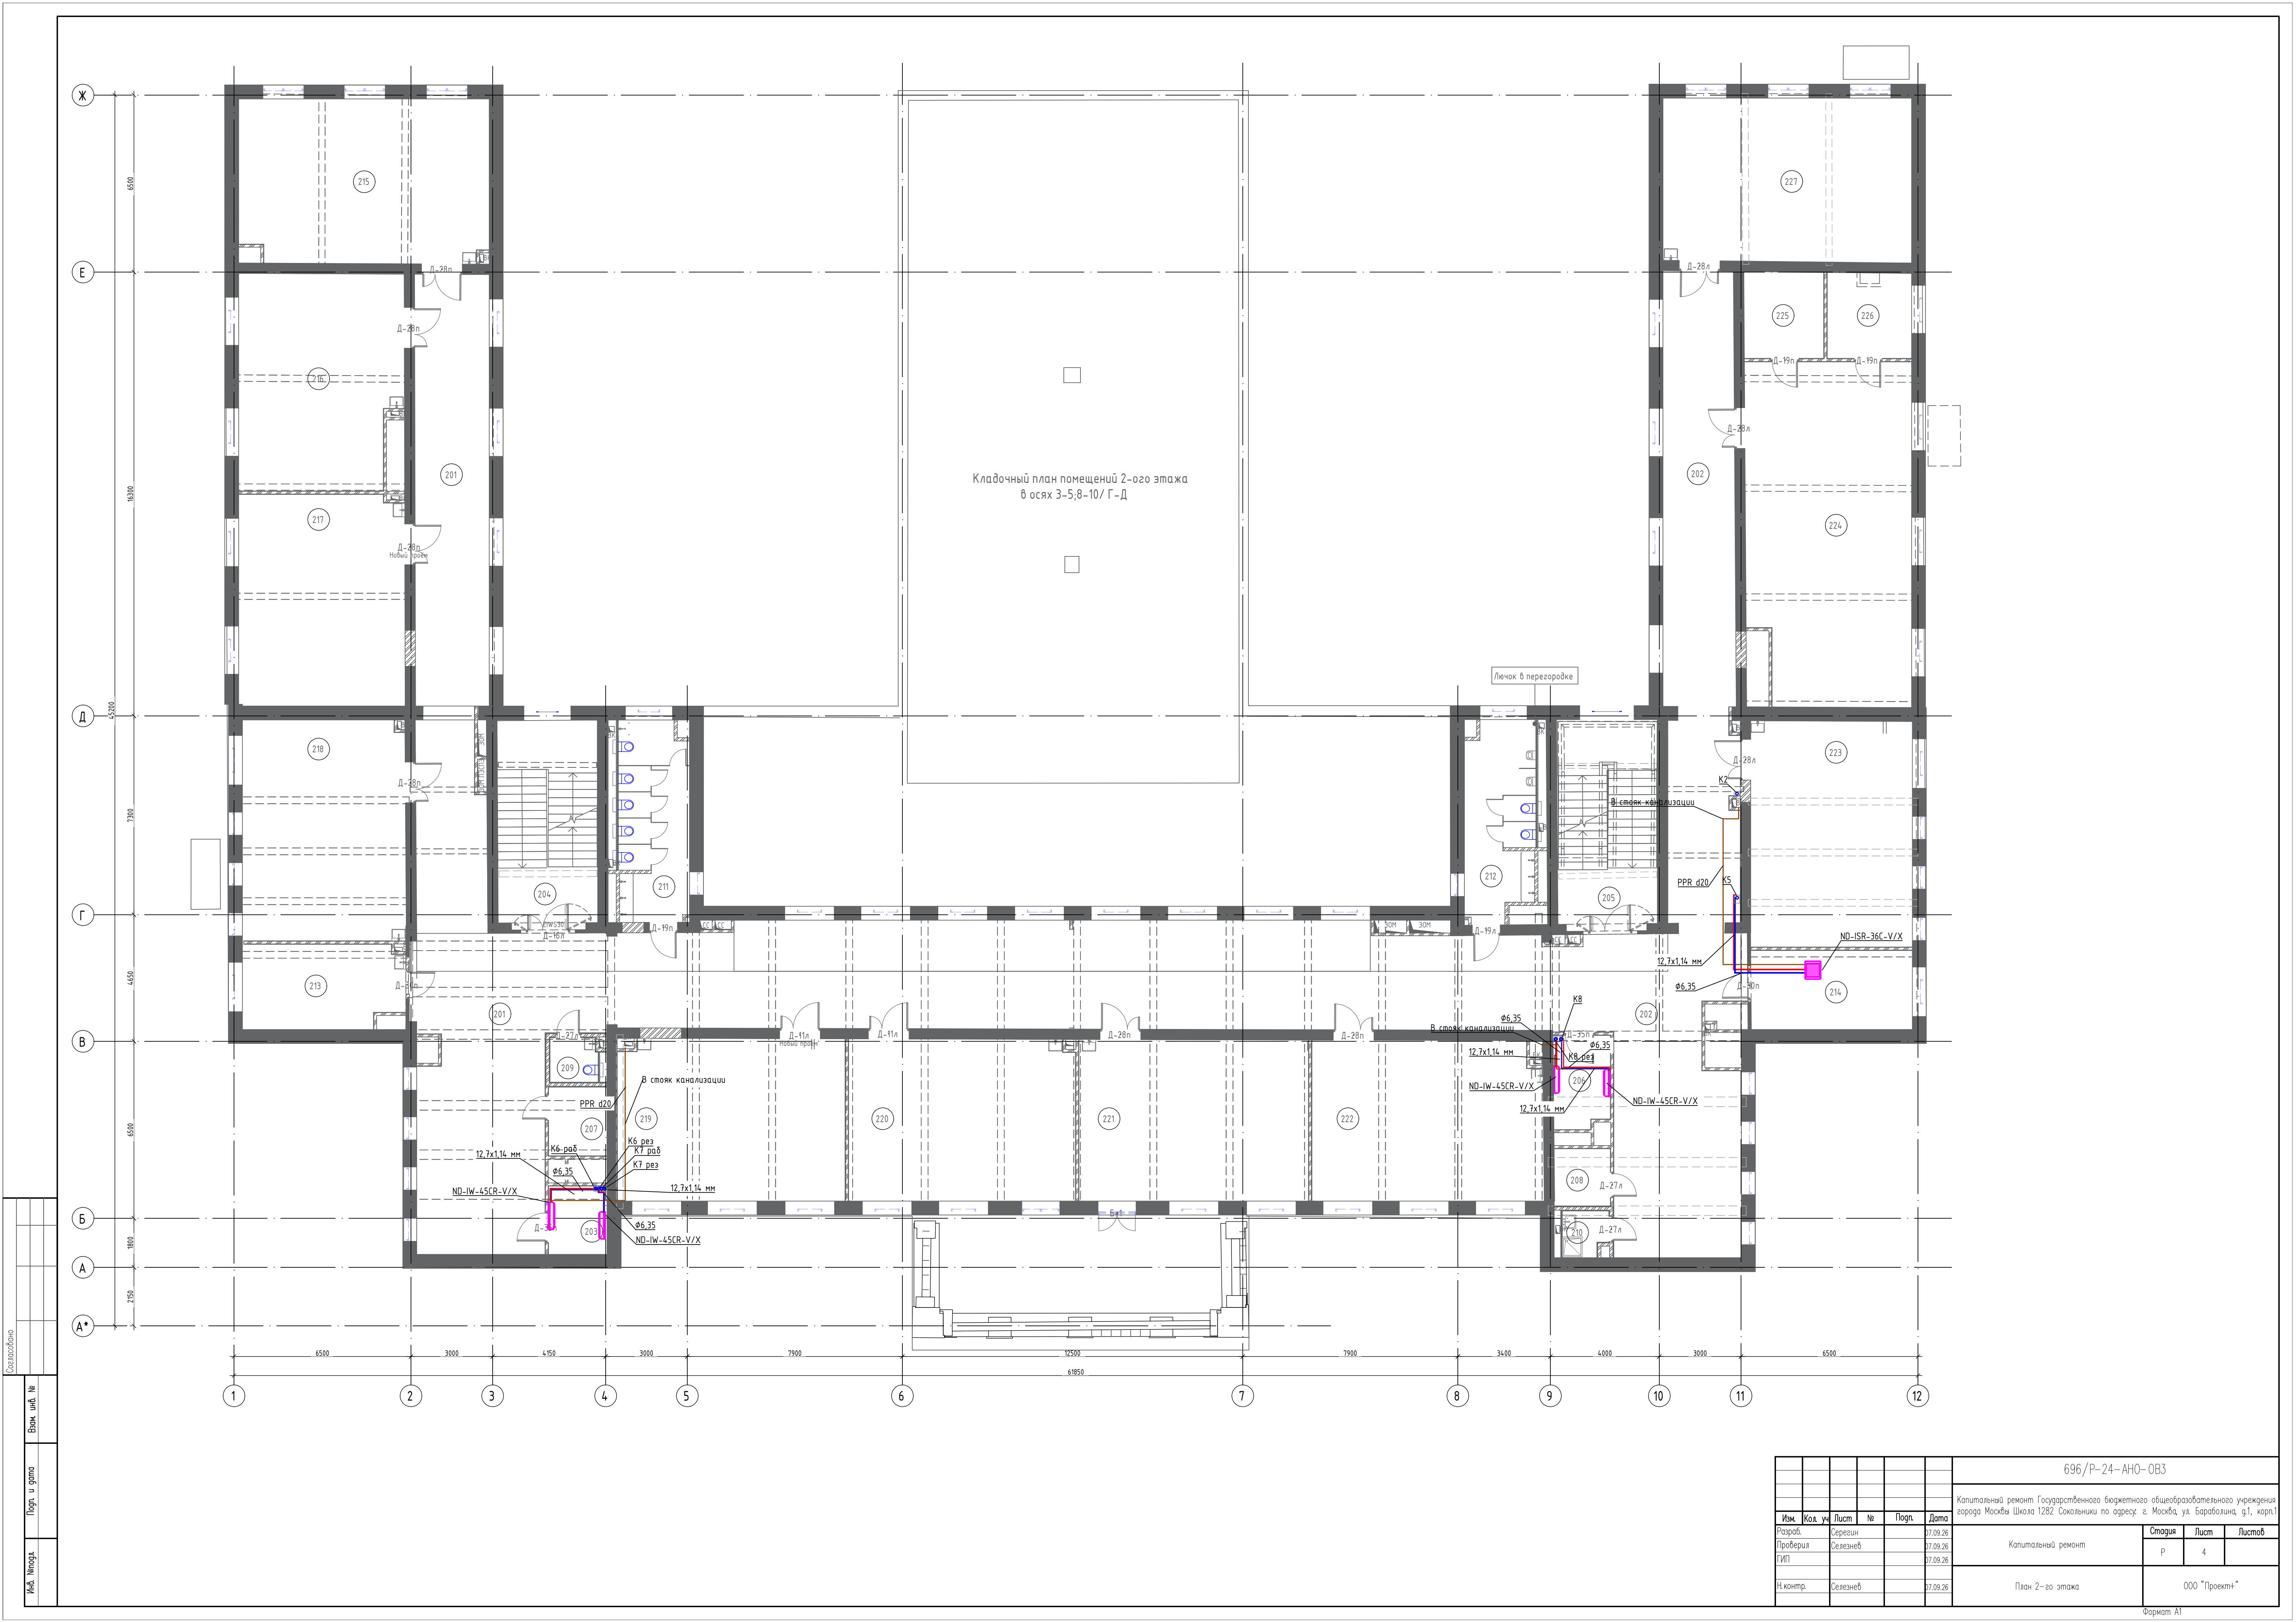

Составлено					
Взам. инв. №					
Лист					
Имя, Инициал					


696/Р-24-АНО-ОВ3					
Капитальный ремонт Государственного бюджетного общеобразовательного учреждения города Москвы Школа 1282 Сокольники по адресу: г. Москва, ул. Барболова, д.1, корпус 1					
Изм.	Код	Лист	№	Полн.	Дата
Разраб.	Сергеев				07.09.26
Проверил	Селезнев				07.09.26
ГИП					07.09.26
Н.контр.	Селезнев				07.09.26
Капитальный ремонт				Страница	Лист
План 2-го этажа				Р	4
				000 "Проект"	

Составлено					
Имя, Инициал	Полн. и дата	Взам. инд. №			

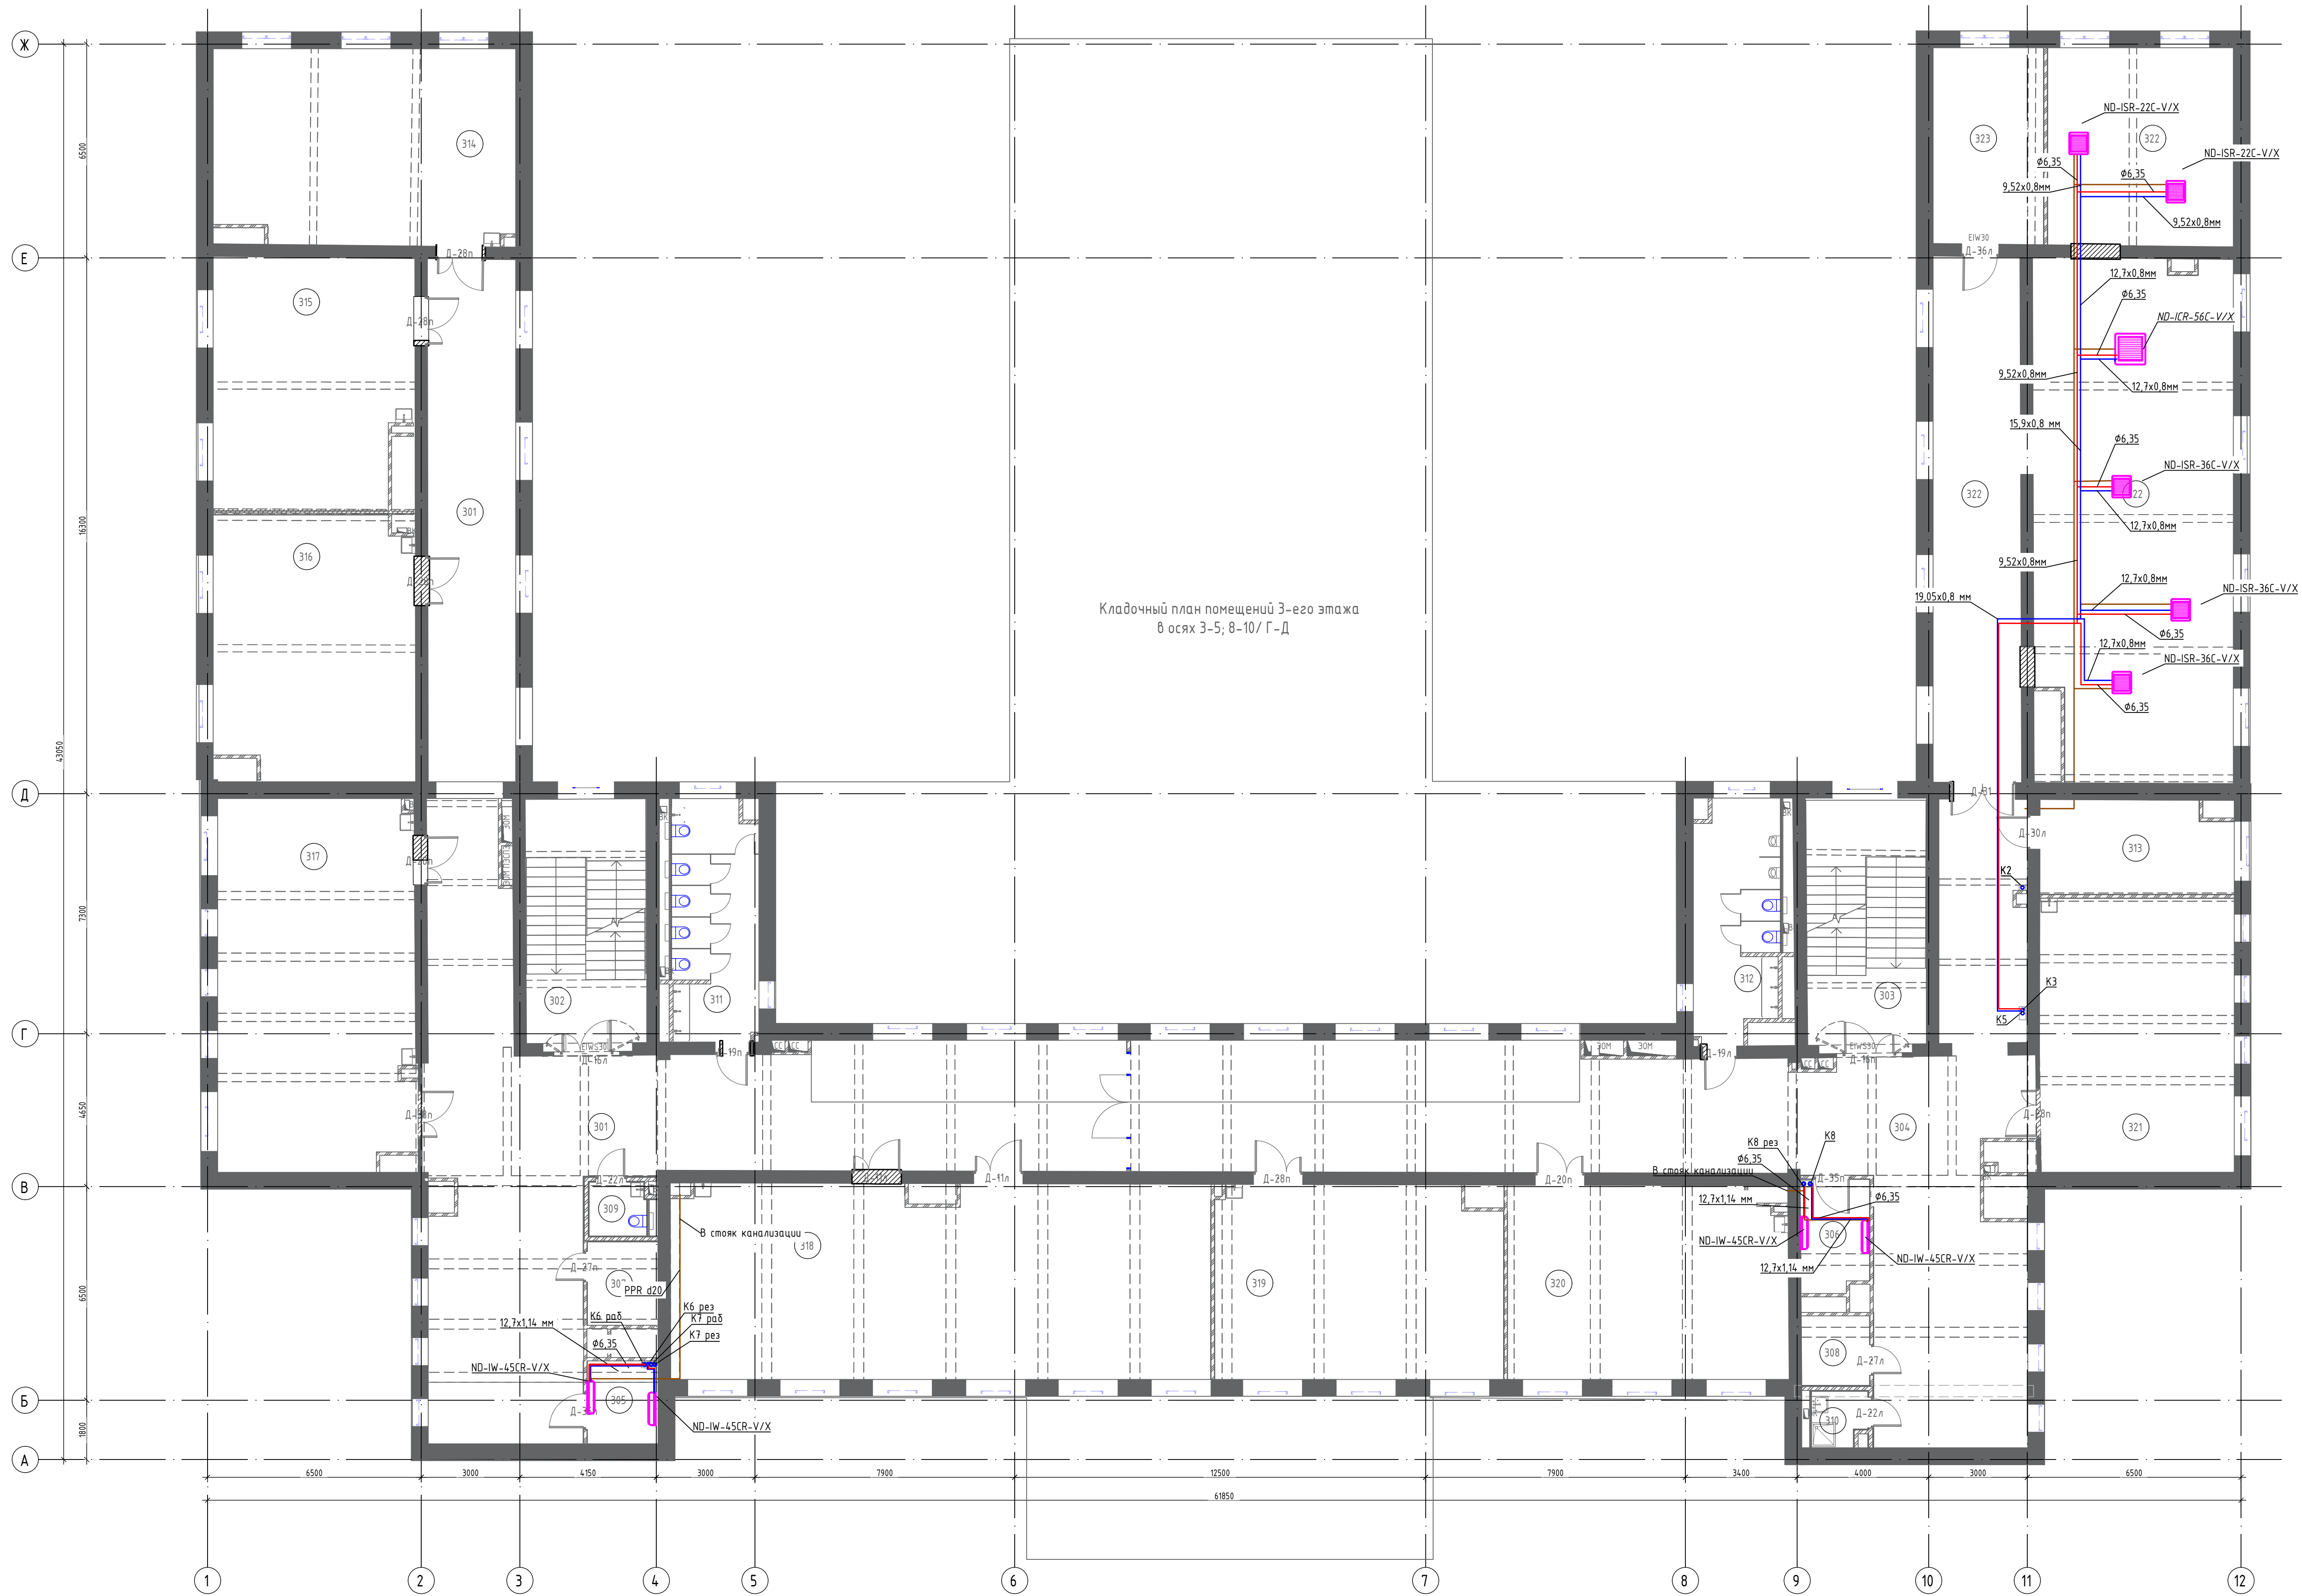


Кладочный план помещений 3-его этажа
в осях 3-5; 8-10/ Г-Д


						696/Р-24-АНО-ОВ3		
						Капитальный ремонт Государственного бюджетного общеобразовательного учреждения города Москвы Школа 1282 Сокольники по адресу: г. Москва, ул. Баровкина, д.1, корпус 1		
Изм.	Код	уч.	Лист	№	Полн.	Дата	Капитальный ремонт	Страница
Разработ.		Сергеев				07.09.26		Лист
Проверил		Селезнев				07.09.26		5
ГИП						07.09.26	План 3-го этажа	000 "Проект"
Н.контр.		Селезнев				07.09.26		

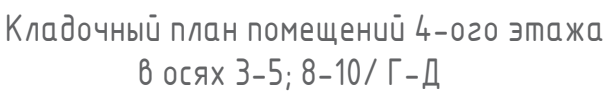

						696/П-24- АНО-ОВЗ			
						Капитальный ремонт Государственного бюджетного общеобразовательного учреждения города Москвы Школа 1282 Сокольники по адресу: г. Москва, ул. Барболова, д.1, корп.1			
Изм.	Код. ук	Лист	№	Погр.	Дата	Капитальный ремонт	Стация	Лист	Листов
Разработ.	Серезин				07.09.26		Р	6	
Проверил	Селезнев				07.09.26				
ТИП					07.09.26				
Исполнит.	Селезнев				07.09.26	План 4-го этажа	ООО "Проектн"		

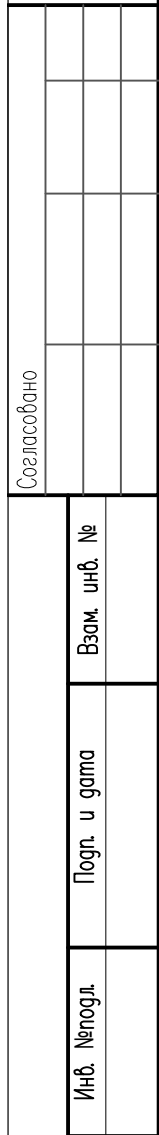

Формат A1

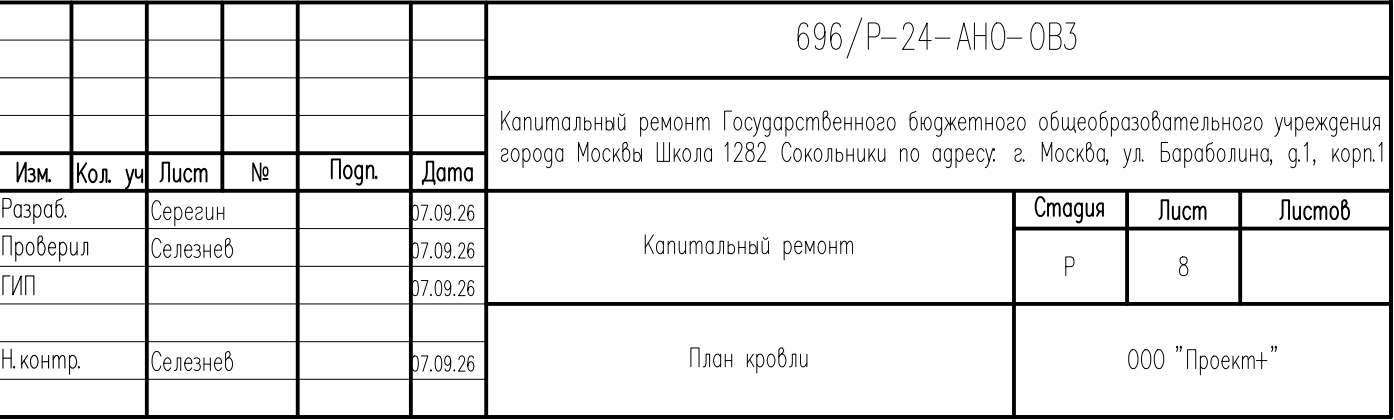

[illegible]

Согласовано				
	Взам. инв. №			
	Погр. и дата			
	Инв. №подл.			

№	Наименование	Тип, марка	Завод– изготовитель	Ед. изм	Кол– во	Масса ед, кг	Примечание
10	Ø15,88х0,81			м	7		
11	Ø19,05х0,81			м	28		
	К3						
1	Внутренний блок	ND-ICR-56C-V/X	NED	шт	1		
2	Внутренний блок	ND-ISR-36C-V/X	NED	шт	3		
3	Внутренний блок	ND-ISR-22C-V/X	NED	шт	2		
4	Наружный блок	ND-OH-224B-3/X	NED	шт	1		
	Рефнет разветвитель						
5		ND-REF-02-PRO	NED	шт	2		
6		ND-REF-01-PRO	NED	шт	3		
	Трубка медная						
7	Ø6,35х0,81			м	16		
8	Ø9,52х0,81			м	28		
9	Ø12,7х0,81			м	17		
10	Ø15,88х0,81			м	4		
11	Ø19,05х0,81			м	22		
	К4						
1	Внутренний блок	ND-ISR-36C-V/X	NED	шт	4		
2	Наружный блок	ND-OH-140B-3/X	NED	шт	1		
3	Рефнет разветвитель	ND-REF-01-PRO	NED	шт	3		
	Трубка медная						
7	Ø6,35х0,81			м	18		
8	Ø9,52х0,81			м	23		
9	Ø12,7х0,81			м	18		
10	Ø15,88х0,81			м	23		
	К5						
1	Внутренний блок	ND-ISR-45C-V/X	NED	шт	1		
2	Внутренний блок	ND-ISR-36C-V/X	NED	шт	1		
3	Внутренний блок	ND-ISR-22C-V/X	NED	шт	1		
4	Наружный блок	ND-OH-100B-1/X	NED	шт	1		
5	Рефнет разветвитель	ND-REF-01-PRO	NED	шт	2		

						696/P-24-AHO-OB3.C	Лист
Изм.	Кол. уч.	Лист	№ док	Погр.	Дата		2

Согласовано

	№	Наименование	Тип, марка	Завод- изготовитель	Ед. изм	Кол- во	Масса ед, кг	Примечание	
		Трубка медная							
	7	Ø6,35x0,81			м	20			
	8	Ø9,52x0,81			м	22			
	9	Ø12,7x0,81			м	20			
	10	Ø19,05x0,81			м	22			
		K6/K6рез							
	1	Внутренний блок настенный	ND-IW-56C-V/X	NED	шт	8			
	2	Наружний блок	ND-OH-255B-PRO/X	NED	шт	2			
		Рефнет разветвитель							
	3		ND-REF-02-PRO	NED	шт	2			
	4		ND-REF-01-PRO	NED	шт	4			
	5	Укрытие SNW-1		NED	шт	2			
	6	Нагреватели SNW-H-1		NED	шт	2			
	7	Щит автоматики SNW-AV-1		NED	шт	2			
	8	Рама несущая SNW-F-1		NED	шт	2			
	9	Модуль ротации кондиционеров MRC-2		NED	шт	4			
		Трубка медная							
		10	Ø6,35x0,81		м	46			
		11	Ø9,52x0,81		м	22			
	12	Ø12,7x0,81		м	46				
	13	Ø15,88x0,81		м	22				
		K7/K7рез							
	1	Внутренний блок настенный	ND-IW-45C-V/X	NED	шт	2			
	2	Наружний блок	ND-OH-080B-1/X	NED	шт	2			
	5	Укрытие SNW-6		NED	шт	1			
	6	Нагреватели SNW-H-6		NED	шт	1			
	7	Щит автоматики SNW-AV-6		NED	шт	1			
	8	Рама несущая SNW-F-6		NED	шт	1			
	9	Модуль ротации кондиционеров MRC-2		NED	шт	1			
		Трубка медная							
	10	Ø6,35x0,81		м	20				
	12	Ø12,7x0,81		м	20				
									Лист
									3
							696/P-24-AHO-OB3.C		

Согласовано				
	Взам. инв. №			
	Погр. и дата			
	Инв. №подл.			

№	Наименование	Тип, марка	Завод– изготовитель	Ед. изм	Кол– во	Масса ед, кг	Примечание
	К8/К8рез						
1	Внутренний блок настенный	ND-IW-45C-V/X	NED	шт	8		
2	Наружный блок	ND-OH-140B-3/X	NED	шт	2		
4	Рефнет разветвитель	ND-REF-01-PRO	NED	шт	4		
5	Укрытие SNW-6/2		NED	шт	1		
6	Нагреватели SNW-H-6/2		NED	шт	1		
7	Щит автоматики SNW-AV-6/2		NED	шт	1		
8	Рама несущая SNW-F-6/2		NED	шт	1		
9	Модуль ротации кондиционеров MRC-2		NED	шт	3		
	Трубка медная						
10	Ø6,35x0,81			м	36		
11	Ø9,52x0,81			м	14		
12	Ø12,7x0,81			м	36		
13	Ø15,88x0,81			м	14		
	Теплоизоляция фреоновых						
	трубки теплоизоляционные толщиной 13 мм	K-FLEX ST	ООО «К-ФЛЕКС»				
1	Ø6,35x0,81	ST 13x6		м	195		
2	Ø9,52x0,81	ST 13x12		м	140		
3	Ø12,7x0,81	ST 13x15		м	195		
4	Ø15,88x0,81	ST 13x18		м	96		
5	Ø19,05x0,81	ST 13x22		м	78		
6	25,4x1,14мм	ST 13x28		м	12		
7	лента для проклейки швов шириной 50 мм	K-FLEX		м	260		
8	клей для монтажа теплоизоляции	K-FLEX K414		л	26		
	Крепления						
	Подвесы с мет.хомутом	K-FLEX ST	ООО «К-ФЛЕКС»				
1		13x010 ST		шт	76		
2		13x012 ST		шт	54		
3		13x015 ST		шт	76		
4		13x018 ST		шт	40		
5		13x022 ST		шт	36		
6		13x028 ST		шт	12		
	Дренаж						
1	Труба PPR						
2	d20			м	54		
3	d25			м	20		
4	d32			м	30		

						696/P-24-AHO-OB3.C	Лист
Изм.	Кол. уч.	Лист	№ док	Погр.	Дата		4



Наружные блоки

Модель			ND-OH-080B-1	ND-OH-100B-1	ND-OH-125B-1	ND-OH-140B-1	ND-OH-160B-1
Тип питания		В/фаз/Гц	220~240/1/50				
Охлаждение	Производительность	кВт	8	10	12,5	14	16
	Потребляемая мощн.	кВт	2,15	2,68	3,38	3,96	4,57
	EER		3,72	3,70	3,69	3,52	3,50
Обогрев	Производительность	кВт	9	11,5	14	16	18
	Потребляемая мощн.	кВт	2,28	2,90	3,65	4,3	5,13
	COP		3,95	3,93	3,83	3,72	3,61
Уровень звукового давления		дБ(А)	45~56		45~58		45~58
Габариты блока (ДхШхВ)		мм	935×353×702	1032×400×810	1100×485×870		
Вес блока нетто		кг	80	80	89	89	96
Трубопроводы хладагента	Газ	мм	ø 15,9				
	Жидкость	мм	ø 9,53				
Макс. кол-во подключ. внутр. блоков		мм	4	5	6	7	8

Модель			ND-OH-180B-3	ND-OH-224B-3A	ND-OH-260B-3A	ND-OH-280M-3A	ND-OH-335M-3A
Тип питания		В/фаз/Гц	380~415/3/50				
Охлаждение	Производительность	кВт	18	22,4	26	28	33,5
	Потребляемая мощн.	кВт	5,18	6,74	7,54	8,32	9,45
	EER		3,47	3,32	3,45	3,37	3,54
Обогрев	Производительность	кВт	20	25	28,5	30,5	37,5
	Потребляемая мощн.	кВт	5,02	5,85	6,77	7,93	9
	COP		3,98	4,27	4,21	3,85	4,17
Уровень звукового давления		дБ(А)	45~58		45~50	47~60	48~62
Габариты блока (ШхВхГ)		мм	900×1328×345	1015×1430×450	1120×1549×528		
Вес блока нетто		кг	94,7	112,7	142	154	154
Трубопроводы хладагента	Газ	мм	ø 15,9	ø 9,52		ø 12,7	
	Жидкость	мм	ø 9,53	ø 19,05	ø 22,2	ø 28,6	
Макс. кол-во подключ. внутр. блоков		мм	9	10	12	15	18



Модель			ND-OH-252B-PRO	ND-OH-280B-PRO	ND-OH-335B-PRO	ND-OH-400B-PRO	ND-OH-450B-PRO	ND-OH-500B-PRO	ND-OH-560B-PRO
			8	10	12	14	16	18	20
Электропитание		В/фаз/Гц	380~415/3/50						
Кол-во присоединяемых внутр. блоков			13	16	19	23	26	29	33
Охлаждение	Производительность	кВт	25,2	28	33,5	40	45	50	56
	Сила тока	А	9,04	11,30	14,51	18,10	21,60	23,29	26,10
	Потребляемая мощн.	кВт	5,31	6,22	8,35	9,76	11,63	12,22	14,66
	EER		4,75	4,5	4,01	4,1	3,87	4,09	3,82
Обогрев	Производительность	кВт	27,4	31,5	37,5	45	50	56	63
	Сила тока	А	8,93	11,25	14,34	18,00	20,25	22,61	25,70
	Потребляемая мощн.	кВт	4,98	5,86	7,35	9,34	10,87	11,89	14,16
	COP		5,5	5,38	5,1	4,82	4,6	4,71	4,45
Макс. сила тока		А	23,1	24,7	25,5	30,8	31,7	37,4	41,1
Кол-во компрессоров			1	1	1	1	1	1	1
Заправка блока хладагентом		кг	9	9	11	14	14	15	16
Габариты (ШхВхГ)		мм	990×1740×840				1340×1740×840		
Вес		кг	228	228	230	275	275	285	290
Уровень шума		дБ(А)	58	58	60	60	61	62	63
Трубопроводы хладагента ≤90м	Жидкость	мм	ø 9,52	ø 9,52	ø 12,7		ø 12,7	ø 15,88	ø 15,88
	Газ	мм	ø 19,05	ø 22,2	ø 25,4		ø 28,6	ø 28,6	ø 28,6
Трубопроводы хладагента ≥90м	Жидкость	мм	ø 12,7	ø 12,7	ø 15,88		ø 15,88	ø 19,05	ø 19,05
	Газ	мм	ø 22,2	ø 25,4	ø 28,6		ø 31,8	ø 31,8	ø 31,8

Модель			ND-OH-615B-PRO	ND-OH-670B-PRO	ND-OH-730B-PRO	ND-OH-785B-PRO	ND-OH-850B-PRO	ND-OH-900B-PRO
			22	24	26	28	30	32
Электропитание		В/фаз/Гц	380~415/3/50					
Кол-во присоединяемых внутр. блоков			36	39	43	46	50	53
Охлаждение	Производительность	кВт	61,5	67	73	78,5	85	90
	Сила тока	А	29,06	29,09	32,59	36,13	40,36	44,73
	Потребляемая мощн.	кВт	16,62	16,71	18,18	20,03	22,37	24,79
	EER		3,70	4,01	4,02	3,92	3,80	3,63
Обогрев	Производительность	кВт	69	75	81,5	87,5	95	100
	Сила тока	А	28,40	28,65	30,28	33,38	38,52	43,90
	Потребляемая мощн.	кВт	16,80	14,72	16,78	18,50	21,35	24,33
	COP		4,11	5,10	4,86	4,73	4,45	4,11
Макс. сила тока		А	42,1	43,2	51,8	51,8	60,4	63,6
Кол-во компрессоров			1	2	2	2	1+1	1+1
Заправка блока хладагентом		кг	16	16	20	20	23	23
Габариты (ШхВхГ)		мм	1340×1740×840		1990×1740×840			
Вес		кг	297	388	433	433	480	480
Уровень шума		дБ(А)	63	62	63	63	64	64
Трубопроводы хладагента ≤90м	Жидкость	мм	ø 15,88			ø 19,1		
	Газ	мм	ø 28,6			ø 31,8		
Трубопроводы хладагента ≥90м	Жидкость	мм	ø 19,05			ø 22,2		
	Газ	мм	ø 31,8			ø 38,1		

Внутренние блоки

Кассетный компактный 600x600

- Низкий уровень шума: 22 дБ(А).
- Тонкий корпус, простой монтаж.
- Идеально вписывается в потолок Армстронг.
- Равномерная раздача воздуха в помещении.
- Встроенный дренажный насос обеспечивает подъем конденсата на 700 мм.



Модель			ND-ISR-22C-V/X	ND-ISR-28C-V/X	ND-ISR-36C-V/X	ND-ISR-45C-V/X	ND-ISR-56C-V/X
Электропитание		В/фаз/Гц	220~240/1/50				
Производительность	Охлаждение	кВт	2,2	2,8	3,6	4,5	5,6
	Нагрев	кВт	2,6	3,2	4,0	5,0	6,3
Потребляемая мощность		кВт	0,014	0,018	0,020	0,030	0,045
Расход воздуха макс/мин		м³/ч	480/300	520/320	560/380	670/400	780/510
Уровень звукового давления		дБ(А)	22~32	22~34	22~35	22~36	26~38
Трубопроводы хладагента	Газ	мм	ø 9,52	ø 9,52	ø 12,70	ø 12,70	ø 12,70
	Жидкость	мм	ø 6,35	ø 6,35	ø 6,35	ø 6,35	ø 6,35
Блок	Габаритные размеры	мм	655×570×260				
	Вес нетто	кг	16,60	17,50	18,00	18,00	18,00
ПАНЕЛЬ ND-ISR/X							
Панель	Габаритные размеры	мм	652×652×60				
	Вес нетто	кг	3				

Кассетный блок с раздачей 360°



- Распределение потока воздуха по всему пространству на 360°.
- Внутренний блок оснащен дренажным насосом с низким уровнем шума.
- Подъем конденсата на 1200 мм.
- Высота блоков от 210 мм.

Модель			ND-ICR-56C-V/X	ND-ICR-71C-V/X	ND-ICR-80C-V/X	ND-ICR-90C-V/X	ND-ICR-100C-V/X
Электропитание		В/фаз/Гц	220~240/1/50				
Производительность	Охлаждение	кВт	5,6	7,1	8,0	9,0	10,0
	Нагрев	кВт	6,3	8,0	9,0	10,0	11,2
Потребляемая мощность		кВт	0,022	0,032	0,032	0,05	0,05
Расход воздуха макс/мин		м³/ч	970/643	1240/720	1240/720	1600/1135	1600/1135
Уровень звукового давления		дБ(А)	25~32	28~37	28~37	29~38	29~38
Трубопроводы хладагента	Газ	мм	ø 12,7	ø 15,88	ø 15,88	ø 15,88	ø 15,88
	Жидкость	мм	ø 6,35	ø 9,52	ø 9,52	ø 9,52	ø 9,52
Блок	Габаритные размеры	мм	840×840×210			840×840×295	
	Вес нетто	кг	24	25		30	
			ПАНЕЛЬ ND-ICR-1C/X				
Панель	Габаритные размеры	мм	950×950×55				
	Вес нетто	кг	6				

Модель			ND-ICR-112C-V/X	ND-ICR-125C-V/X	ND-ICR-140C-V/X	ND-ICR-160C-V/X
Электропитание		В/фаз/Гц	220~240/1/50			
Производительность	Охлаждение	кВт	11,2	12,5	14,0	16,0
	Нагрев	кВт	12,5	15,0	16,0	18,0
Потребляемая мощность		кВт	0,07	0,078	0,078	0,17
Расход воздуха макс/мин		м³/ч	1750/1200	1820/1265	1820/1265	2072/1534
Уровень звукового давления		дБ(А)	33~41	34~43	34~43	37~46
Трубопроводы хладагента	Газ	мм	ø 15,88	ø 15,88	ø 15,88	ø 15,88
	Жидкость	мм	ø 9,52	ø 9,52	ø 9,52	ø 9,52
Блок	Габаритные размеры	мм	840×840×295			
	Вес нетто	кг	30			31,5
			ПАНЕЛЬ ND-ICR-1C/X			
Панель	Габаритные размеры	мм	950×950×55			
	Вес нетто	кг	6			

Кассетный однопоточный

- **Равномерное распределение температур при обслуживании помещений.**
- Низкий уровень шума от 30 дБ(А).
- Встроенный дренажный насос обеспечивает подъем конденсата на 1200 мм.
- Тонкий корпус для установки в ограниченном пространстве.



Модель			ND-IN-22C-V/X	ND-IN-28C-V/X	ND-IN-36C-V/X	ND-IN-45C-V/X	ND-IN-56C-V/X	ND-IN-71C-V/X
Электропитание		В/фаз/Гц	220~240/1/50					
Производительность	Охлаждение	кВт	2,2	2,8	3,6	4,5	5,6	7,1
	Нагрев	кВт	2,6	3,2	4	5	6,3	8
Потребляемая мощность		кВт	0,02	0,02	0,025	0,03	0,03	0,04
Расход воздуха макс/мин		м³/ч	533/321	533/321	608/361	690/466	886/558	1001/661
Уровень звукового давления		дБ(А)	30~36	30~36	30~36	30~38	33~40	38~47
Трубопроводы хладагента	Газ	мм	ø 9,52	ø 9,52	ø 12,7	ø 12,7	ø 12,7	ø 15,88
	Жидкость	мм	ø 6,35	ø 6,35	ø 6,35	ø 6,35	ø 6,35	ø 9,52
Корпус	Габаритные размеры	мм	943×468×245			1254×492×290		
	Вес нетто	кг	23			28,5	30	
			ПАНЕЛЬ ND-IN-1C/X			ПАНЕЛЬ ND-IN-2C/X		
Панель	Габаритные размеры	мм	1070×520×50			1380×550×50		
	Вес нетто	кг	3,5			5,35		

Настенный

- **Низкий уровень шума — от 22 дБ(А).**
- Выбор варианта присоединения фреонового трубопровода: с трех сторон в трех различных направлениях.
- Оптимальная подача воздуха в помещение: горизонтальный для режима охлаждения и вертикальный для режима нагрева.



Модель			ND-IW-15C-V/X	ND-IW-22C-V/X	ND-IW-28C-V/X	ND-IW-36C-V/X	ND-IW-45C-V/X	ND-IW-56C-V/X	ND-IW-71C-V/X
Электропитание		В/фаз/Гц	220~240/1/50						
Производительность	Охлаждение	кВт	1,5	2,2	2,8	3,6	4,5	5,6	7,1
	Нагрев	кВт	1,8	2,6	3,2	4,0	5,0	6,3	8,0
Потребляемая мощность		кВт	0,008	0,01	0,011	0,013	0,025	0,03	0,04
Расход воздуха макс/мин		м³/ч	383/300	519/336	519/336	519/383	706/560	720/505	801/560
Уровень звукового давления		дБ(А)	22~31	24~33	24~34	28~35	28~37	29~39	32~43
Трубопроводы хладагента	Газ	мм	ø 9,52	ø 9,52	ø 9,52	ø 12,7	ø 12,7	ø 12,7	ø 15,88
	Жидкость	мм	ø 6,35	ø 6,35	ø 6,35	ø 6,35	ø 6,35	ø 6,35	ø 9,52
Габаритные размеры		мм	805×198×295			805×198×295		990×219×316	
Вес блока нетто		кг	9,0	9,5			11,8		

Напольно-потолочный

- **Монтаж в напольном и в потолочном положении.**
- За счет применения высокопроизводительных низкошумных центробежных вентиляторов обеспечивается подача большого количества воздуха на большие расстояния.



Модель			ND-IX-45C-V/X	ND-IX-56C-V/X	ND-IX-71C-V/X	ND-IX-80C-V/X
Электропитание		В/фаз/Гц	220~240/1/50			
Производительность	Охлаждение	кВт	4,5	5,6	7,1	8
	Нагрев	кВт	5	6,3	8	9
Потребляемая мощность		кВт	0,05	0,05	0,06	0,06
Расход воздуха макс/мин		м³/ч	842/527	842/527	994/738	1153/738
Уровень звукового давления		дБ(А)	34~45	34~45	41~49	41~53
Трубопроводы хладагента	Газ	мм	ø 12,7	ø 12,7	ø 15,88	ø 15,88
	Жидкость	мм	ø 6,35	ø 6,35	ø 9,52	ø 9,52
Габаритные размеры		мм	1055×675×235			
Вес блока нетто		кг	24		25	

Модель			ND-IX-90C-V/X	ND-IX-112C-V/X	ND-IX-140C-V/X	ND-IX-160C-V/X
Электропитание		В/фаз/Гц	220~240/1/50			
Производительность	Охлаждение	кВт	9	11,2	14	16
	Нагрев	кВт	10	12,5	16	18
Потребляемая мощность		кВт	0,07	0,07	0,1	0,1
Расход воздуха макс/мин		м³/ч	1530/1031	1632/1160	1858/1332	2245/1332
Уровень звукового давления		дБ(А)	42~52	45~54	43~52	43~54
Трубопроводы хладагента	Газ	мм	ø 15,88	ø 15,88	ø 15,88	ø 15,88
	Жидкость	мм	ø 9,52	ø 9,52	ø 9,52	ø 9,52
Габаритные размеры		мм	1275×675×235		1635×675×235	
Вес блока нетто		кг	29		38	

Канальный низконапорный

• **Свободный напор 50 Па.**

- Компактный: высота — 200 мм.
- Низкий уровень шума — от 22 дБ(А).
- Дренажный патрубок выведен на левую и правую стороны.
- Фильтр в комплекте.



Модель			ND-IM-22C-V/X	ND-IM-28C-V/X	ND-IM-36C-V/X	ND-IM-45C-V/X	ND-IM-56C-V/X	ND-IM-71C-V/X
Электропитание		В/фаз/Гц	220~240/1/50					
Производительность	Охлаждение	кВт	2,2	2,8	3,6	4,5	5,6	7,1
	Нагрев	кВт	2,6	3,2	4	5	6,3	8
Потребляемая мощность		кВт	0,021	0,021	0,024	0,036	0,036	0,055
Статическое давление		Па	50	50	50	50	50	50
Расход воздуха макс/мин		м³/ч	625/300	625/300	675/395	925/510	940/540	1200/740
Уровень звукового давления		дБ(А)	22~30	22~30	25~31	27~33	29~35	30~36
Трубопроводы хладагента	Газ	мм	ø 9,52	ø 9,52	ø 12,7	ø 12,7	ø 12,7	ø 15,88
	Жидкость	мм	ø 6,35	ø 6,35	ø 6,35	ø 6,35	ø 6,35	ø 9,52
Габаритные размеры		мм	780×475×200			1090×475×200		1390×475×200
Вес блока нетто		кг	16,5			23		27

Канальный средненапорный

• **Свободный напор 80 Па.**

- Компактный: высота — 245 мм.
- Возможен забор воздуха как сзади, так и снизу.
- Дренажный патрубок выведен на левую и правую стороны.
- Фильтр в комплекте.



Модель			ND-IH-71C-V/X	ND-IH-80C-V/X	ND-IH-90C-V/X	ND-IH-100C-V/X	ND-IH-120C-V/X	ND-IH-150C-V/X
Электропитание		В/фаз/Гц	220~240/1/50					
Производительность	Охлаждение	кВт	7,1	8,0	9,0	10,0	12,5	15,0
	Нагрев	кВт	8,0	9,0	10,0	11,2	15,0	17,0
Потребляемая мощность		кВт	0,15	0,15	0,2	0,2	0,28	0,28
Статическое давление		Па	80	80	80	80	80	80
Расход воздуха макс/мин		м³/ч	1200/665	1200/665	1490/890	1490/890	1990/1100	1990/1100
Уровень звукового давления		дБ(А)	37~40	37~40	40~42	40~42	41~43	41~43
Трубопроводы хладагента	Газ	мм	ø 15,88	ø 15,88	ø 15,88	ø 15,88	ø 15,88	ø 15,88
	Жидкость	мм	ø 9,52	ø 9,52	ø 9,52	ø 9,52	ø 9,52	ø 9,52
Габаритные размеры		мм	1080×725×245			1480×725×245		
Вес блока нетто		кг	35			43		

Канальный высоконапорный

• **Свободный напор до 400 Па.**

- Тонкий корпус для экономии пространства за подвесным потолком.
- Холодопроизводительность до 56 кВт.
- Подача воздуха в помещениях с большими расстояниями и сложной конфигурацией.



Модель			ND-IU-71C-V/X	ND-IU-80C-V/X	ND-IU-90C-V/X	ND-IU-100C-V/X	ND-IU-120C-V/X	ND-IU-150C-V/X
Электропитание		В/фаз/Гц	220~240/1/50					
Производительность	Охлаждение	кВт	7,1	8,0	9,0	10,0	12,5	15,0
	Нагрев	кВт	8,0	9,0	10,0	11,2	15,0	17,0
Потребляемая мощность		кВт	0,096	0,1	0,11	0,13	0,155	0,21
Статическое давление		Па	160	160	160	160	160	160
Расход воздуха макс/мин		м³/ч	1192/663	1192/663	1490/888	1490/888	1989/1098	1989/1098
Уровень звукового давления		дБ(А)	37~41	37~41	38~44	38~44	40~46	40~46
Трубопроводы хладагента	Газ	мм	ø 15,88	ø 15,88	ø 15,88	ø 15,88	ø 15,88	ø 15,88
	Жидкость	мм	ø 9,52	ø 9,52	ø 9,52	ø 9,52	ø 9,52	ø 9,52
Габаритные размеры		мм	1080×725×245			1480×725×245		
Вес блока нетто		кг	35			43		

Модель			ND-IU-224C-V/X	ND-IU-260C-V/X	ND-IU-280C-V/X	ND-IU-450C-V/X	ND-IU-560C-V/X
Электропитание		В/фаз/Гц	220~240/1/50				
Производительность	Охлаждение	кВт	22,4	26,0	28,0	45,0	56,0
	Нагрев	кВт	27,4	28,5	31,5	50,0	63,0
Потребляемая мощность		кВт	0,58	0,8	0,9	1,75	2,25
Статическое давление		Па	250	250	250	400	400
Расход воздуха макс/мин		м³/ч	3500/2300	4000/2600	4500/3000	7000/4600	7800/5100
Уровень звукового давления		дБ(А)	45~52	46~53	48~55	51~59	56~63
Трубопроводы хладагента	Газ	мм	ø 22,2	ø 22,2	ø 22,2	ø 28,6	ø 28,6
	Жидкость	мм	ø 9,52	ø 9,52	ø 9,52	ø 15,88	ø 15,88
Габаритные размеры		мм	1520×901×542			2015×940×671	
Вес блока нетто		кг	122	122	130	191	202