

109548, г. Москва, Муниципальный Округ Печатники, ул. Шоссейная, д. 19, к. 1,
кв.117 e-mail PROEKTplus-work@yandex.ru

Свидетельство № СРО- П-110-009723217107-0532

СОГЛАСОВАНО:

Главный инженер

АО «МосводоканалСтройТрест»

_____ А.А. Вешкин

«__» _____ 2026г

**Капитальный ремонт Государственного Бюджетного
Общеобразовательного Учреждения города Москвы
«Школа № 1282 «Сокольники»
по адресу: г. Москва, ул. Барболина, д. 1, корп. 1
1 этап**

РАБОЧАЯ ДОКУМЕНТАЦИЯ

Основной комплект рабочих чертежей

Система охранного теленаблюдения

696/П-24-АНО-Р-СОТ

Генеральный директор

Главный инженер проекта



Н.А. Выходова

А.Н. Гулько

2026

Инв. № подл.	
Подп. И дата	
Взам. инв. №	

Согласовано

Взаминв.Н

Подпись и дата

инв.Нподл.

Ведомость рабочих чертежей основного комплекта

Лист	Наименование	Примечание
1	Общие данные	
2	Схема принципиальная оборудования СОТ	
3	План расположения оборудования СОТ в подвале	
4	План расположения оборудования СОТ на 1 этаже	
5	План расположения оборудования СОТ на 2 этаже	
6	План расположения оборудования СОТ на 3 этаже	
7	План расположения оборудования СОТ на 4 этаже	
8	Схема монтажа уличной камеры	
9	Схема монтажа внутренней камеры	
10	Типовая схема интеграции проектируемой СОТ в ЕЦХД СОТ	
11	Типовая схема коммутации оборудования МЭШ(+сегмент СОТ)	

Ведомость ссылочных и прилагаемых документов

Обозначение	Наименование	Примечание
ФЗ ТРoТПБ	Федеральный закон №123-ФЗ от 22.07.08 "Технический регламент о требованиях пожарной безопасности"	
СП 134.13330.2022	«Системы электросвязи зданий и сооружений. Основные положения проектирования»	
ГОСТ 31565-2012	Кабельные изделия. Требования пожарной безопасности.	
	Основные требования к проектной и рабочей документации	
ПУЭ	Правила устройства электроустановок и потребителей	
Прилагаемые документы		
2024-00236-01-0-СОТ.СО	Спецификация оборудования, изделий и материалов	

1.Общие данные

1.1. На объекте телевизионными камерами оборудуются: – периметр здания; – все основные и запасные входы и выходы; – эвакуационные выходы и лестницы; – зоны рекреации; – учебные кабинеты с высокотехнологичными пространствами; библиотечный центр, столовая, кабинет информатики.
1.2. Сервер, активное коммутационное оборудование(учтено разделом СКС и источники питания учтено разделом СКС устанавливаются в шкафах ШТК1.1, ШТК2.2, ШТК2.3, ШТК3.4, ШТК3.5.
1.3. Автоматизированное место оператора с двумя мониторами предусматривается в комнате охраны пом. 103.
1.4. В качестве сервера выбран Видеосервер NeuroStation 9800R/128, согласно п.17 “Реестра совместимого оборудования с управляющими системами ЕЦХД по второму типу интеграции”, совместим с управляющими системами ЕЦХД. Видеосервер коммутируется с коммутатором ядра МЭШ.
1.5. Кабельная линия системы охранного телевидения выполняется кабелем марки U/UTP Cat5e PVCLS n2(A)-LSLTx 4x2x0,52 мм и учтена разделом СКС.
1.6. Система охранного телевидения предназначена: – для визуального контроля в режиме реального времени прилегающей территории, входных групп и определенных внутренних зон и помещений, локально операторами системы на постах охраны; – для локального обеспечения записи, хранение, просмотра и выгрузки архива видеoinформации; – для обеспечения, по согласованному в соответствии с “Регламентом передачи информации об объектах видеонаблюдения в государственную систему “Единый центр хранения и обработки данных” из локальных систем видеонаблюдения” перечню (количеству) камер видеонаблюдения, месту расположения, зон и сцен обзора, трансляции видеоизображения в режиме реального времени Оператору государственной информационной системе “Единый центр хранения и обработки данных” (далее ЕЦХД), возможность удаленного доступа к трансляции архива, а также выгрузка архива видеоизображения из локальной системы видеонаблюдения (ЛСВН) в ЕЦХД.
Дополнительно для интеграции камер в ЕЦХД предусматриваются лицензии ПО TRASSIR ЕЦХД – (для передачи видеоданных в ЕЦХД, без ограничения срока действия).

1.7. Целью создания системы обеспечение безопасного пребывания людей в общественных зданиях, профилактики правонарушений и обеспечении расследования в случае совершения таковых.
2. КАБЕЛЕНЕСУЩИЕ КОНСТРУКЦИИ И КАБЕЛЬНЫЕ ЛИНИИ СИСТЕМЫ.
2.1. Кабельные линии от этажных коммутаторов до камер видеонаблюдения учтены разделом СКС.
2.2. Прокладку кабельных линий в коридорах и общественных зонах выполнить в кабеленесущих лотках. Лотки учтены в разделах СКС и СОС


3. ЭЛЕКТРОПИТАНИЕ СИСТЕМЫ.
3.1. В качестве источника переменного тока используется сеть бытового электропитания объекта ~220В, 50Гц по первой категории надежности.
Подключение к электросети шкафов осуществляется через кабельные вводы по проекту ЭОМ.
3.2. Электропитание оборудования в шкафах осуществляется специализированным кабелем от источника бесперебойного питания или от блока розеток, подключенного к источнику бесперебойного питания.
Электропитание видеокамер осуществляется по технологии PoE от коммутатора либо видеорегистратора.
4. ЗАЗЕМЛЕНИЕ.
4.1. Для обеспечения безопасности эксплуатации системы до начала работы металлические корпуса приборов, резервированные источники питания, блоки бесперебойного питания, металлические лотки заземляются (зануляются), присоединив к шине заземления (зануления).
4.2. Уличные камеры видеонаблюдения имеют встроенную молниезащиту и через клему заземления заземляются (зануляются) посредством присоединения к шине заземления.
4.3. Защитное заземление или зануление технических средств сигнализации должно соответствовать СНиП 3.05.06-85, ГОСТ 12.1.030-81 и технической документации на оборудование.
4.4. В качестве проводников для заземления станционной (пультовой) аппаратуры используется изолированный проводник сечением не менее 6 кв.мм.
5. ТРЕБОВАНИЯ К СИСТЕМЕ АДМИНИСТРИРОВАНИЯ.
5.1. Система администрирования включает в себя маркировку (идентификация) всех компонентов.
По окончании монтажных работ произвести чистовую маркировку всех элементов системы, в том числе кабельных трасс, телекоммуникационных шкафов, портов коммуникационных панелей, розеток и т.п., в соответствии с решениями, принятыми в настоящем проекте, а кабельные линии розетки и порты коммуникационных панелей в соответствии с “Кабельным журналом” (“Журналом кроссировки”) и с учетом окончательного варианта кроссировки.
5.2. Маркировку кабелей выполнить, в соответствии с требованиями ГОСТ Р 53246: – кабели горизонтальной и магистральной подсистем должны быть промаркированы как минимум с двух концов – вблизи места термирования в разъем и вблизи точки термирования к коммуникационной панели; – в местах отводов кабельных линий от магистральных трасс; – с обеих сторон проходов через межэтажные перекрытия, стены и перегородки.
5.4. Каждая метка элементов кабельных соединений должна быть долговременной, наноситься в доступном для наблюдения месте и позволять идентифицировать данные элементы согласно документации.
5.5. Прокладку кабельных линий в коридорах и общественных зонах выполнить в кабеленесущих лотках. Лотки учтены в разделах СКС и СОС
5.6. В телекоммуникационных шкафах предусмотрено резервное место для установки линейного оборудования СОТ (Благоустройство).
5.7. Проектом предусмотрен резерв (и возможность размещения дополнительных жестких дисков) дискового пространства для хранения информации с камер СОТ территории (Благоустройство).

6.РАСЧЁТ ГЛУБИНЫ АРХИВА ВИДЕОНАБЛЮДЕНИЯ
6.1 Количество внутренних IP камер видеонаблюдения 103 шт.
Срок хранения – 30 дней.
Количество часов записи в сутки по движению – 24ч.
Расчетный архив: 168 Тб. Запроектированный архив: 8x HDD 24TB.

7.После монтажа внести наименование камер в таблицу интеграции ЕЦХД.

							696/П-24-АНО-Р-СОТ
							Капитальный ремонт Государственного Бюджетного Общеобразовательного Учреждения города Москвы «Школа № 1282 «Сокольники» по адресу: г. Москва, ул. Барболина, д. 1, корп. 1
Изм.	Кол.уч	Лист	Ндок	Подпись	Дата		
Разработал.	Коняев						
Проверил.	Гулько					Система охранного теленаблюдения	Стадия Р
							Лист 1
Н. контр.	Гулько					Лист общих данных	
							

Формат А2 альбомная (420х594)

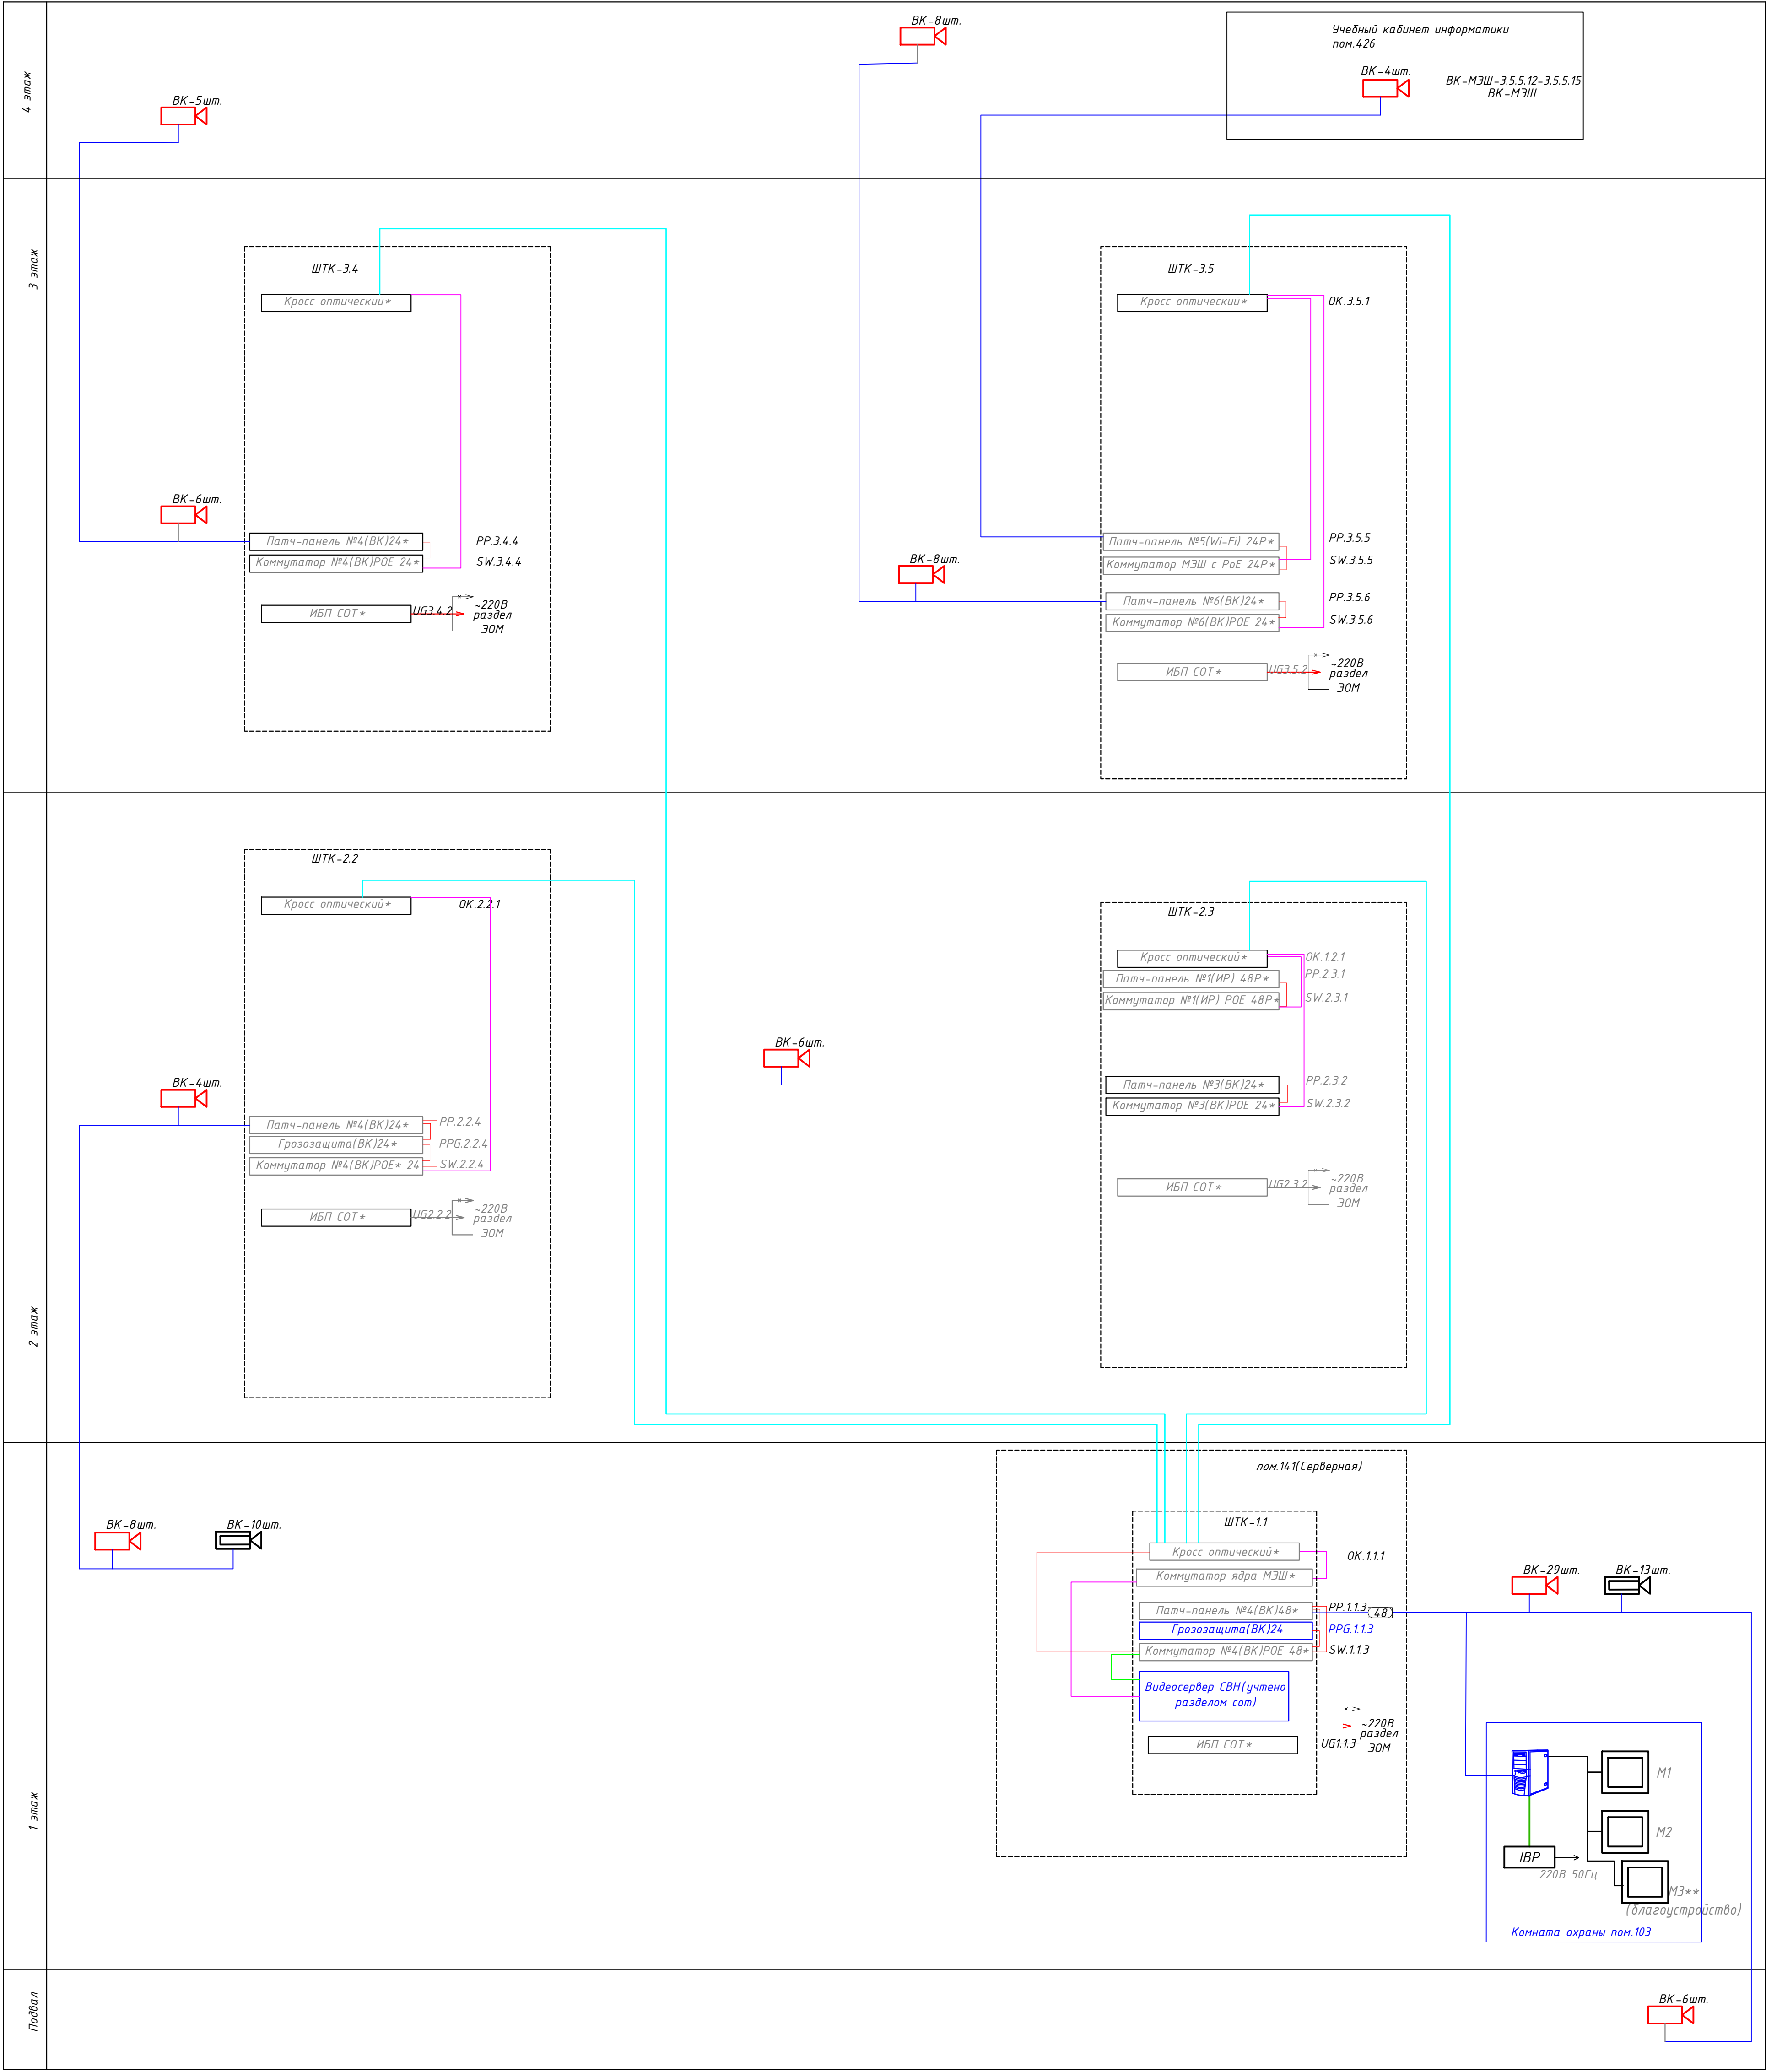


Условные обозначения:

- ВК - - камера видеонаблюдения купольная
TR-D3181PR3 v7 (2.8 мм) (внутри здания)
- ВК-У - - камера видеонаблюдения цилиндрическая
TR-D2181PR5 v7 (2.8 мм) (снаружи здания)
- — кабель типа витая пара *
- — кабель оптический *
- — патч-корд U/UTP 4x2x0.52*
- PC1 - - рабочая станция
- M1 - - монитор 27"
- ИБР - - ИБП*

Примечания:

- Оборудование, кабельные линии и материалы со знаком "*" учтены разделом СКС
- Оборудование, кабельные линии и материалы со знаком "***" учтены разделом Благоустройство


						696/П-24-АНО-Р-СОТ		
						Капитальный ремонт Государственного Бюджетного Общественного Учреждения города Москвы «Школа № 1282 «Сокольники» по адресу: г. Москва, ул. Барболина, д. 1, корп. 1		
Изм.	Кол.уч.	Лист	Изд.	Подпись	Дата	Система охранного телевидения	Статус	Лист
Разработал	Конев	Гулько					р	2
Проверил	Гулько							
Н. контр.	Гулько					Схема принципиальная		

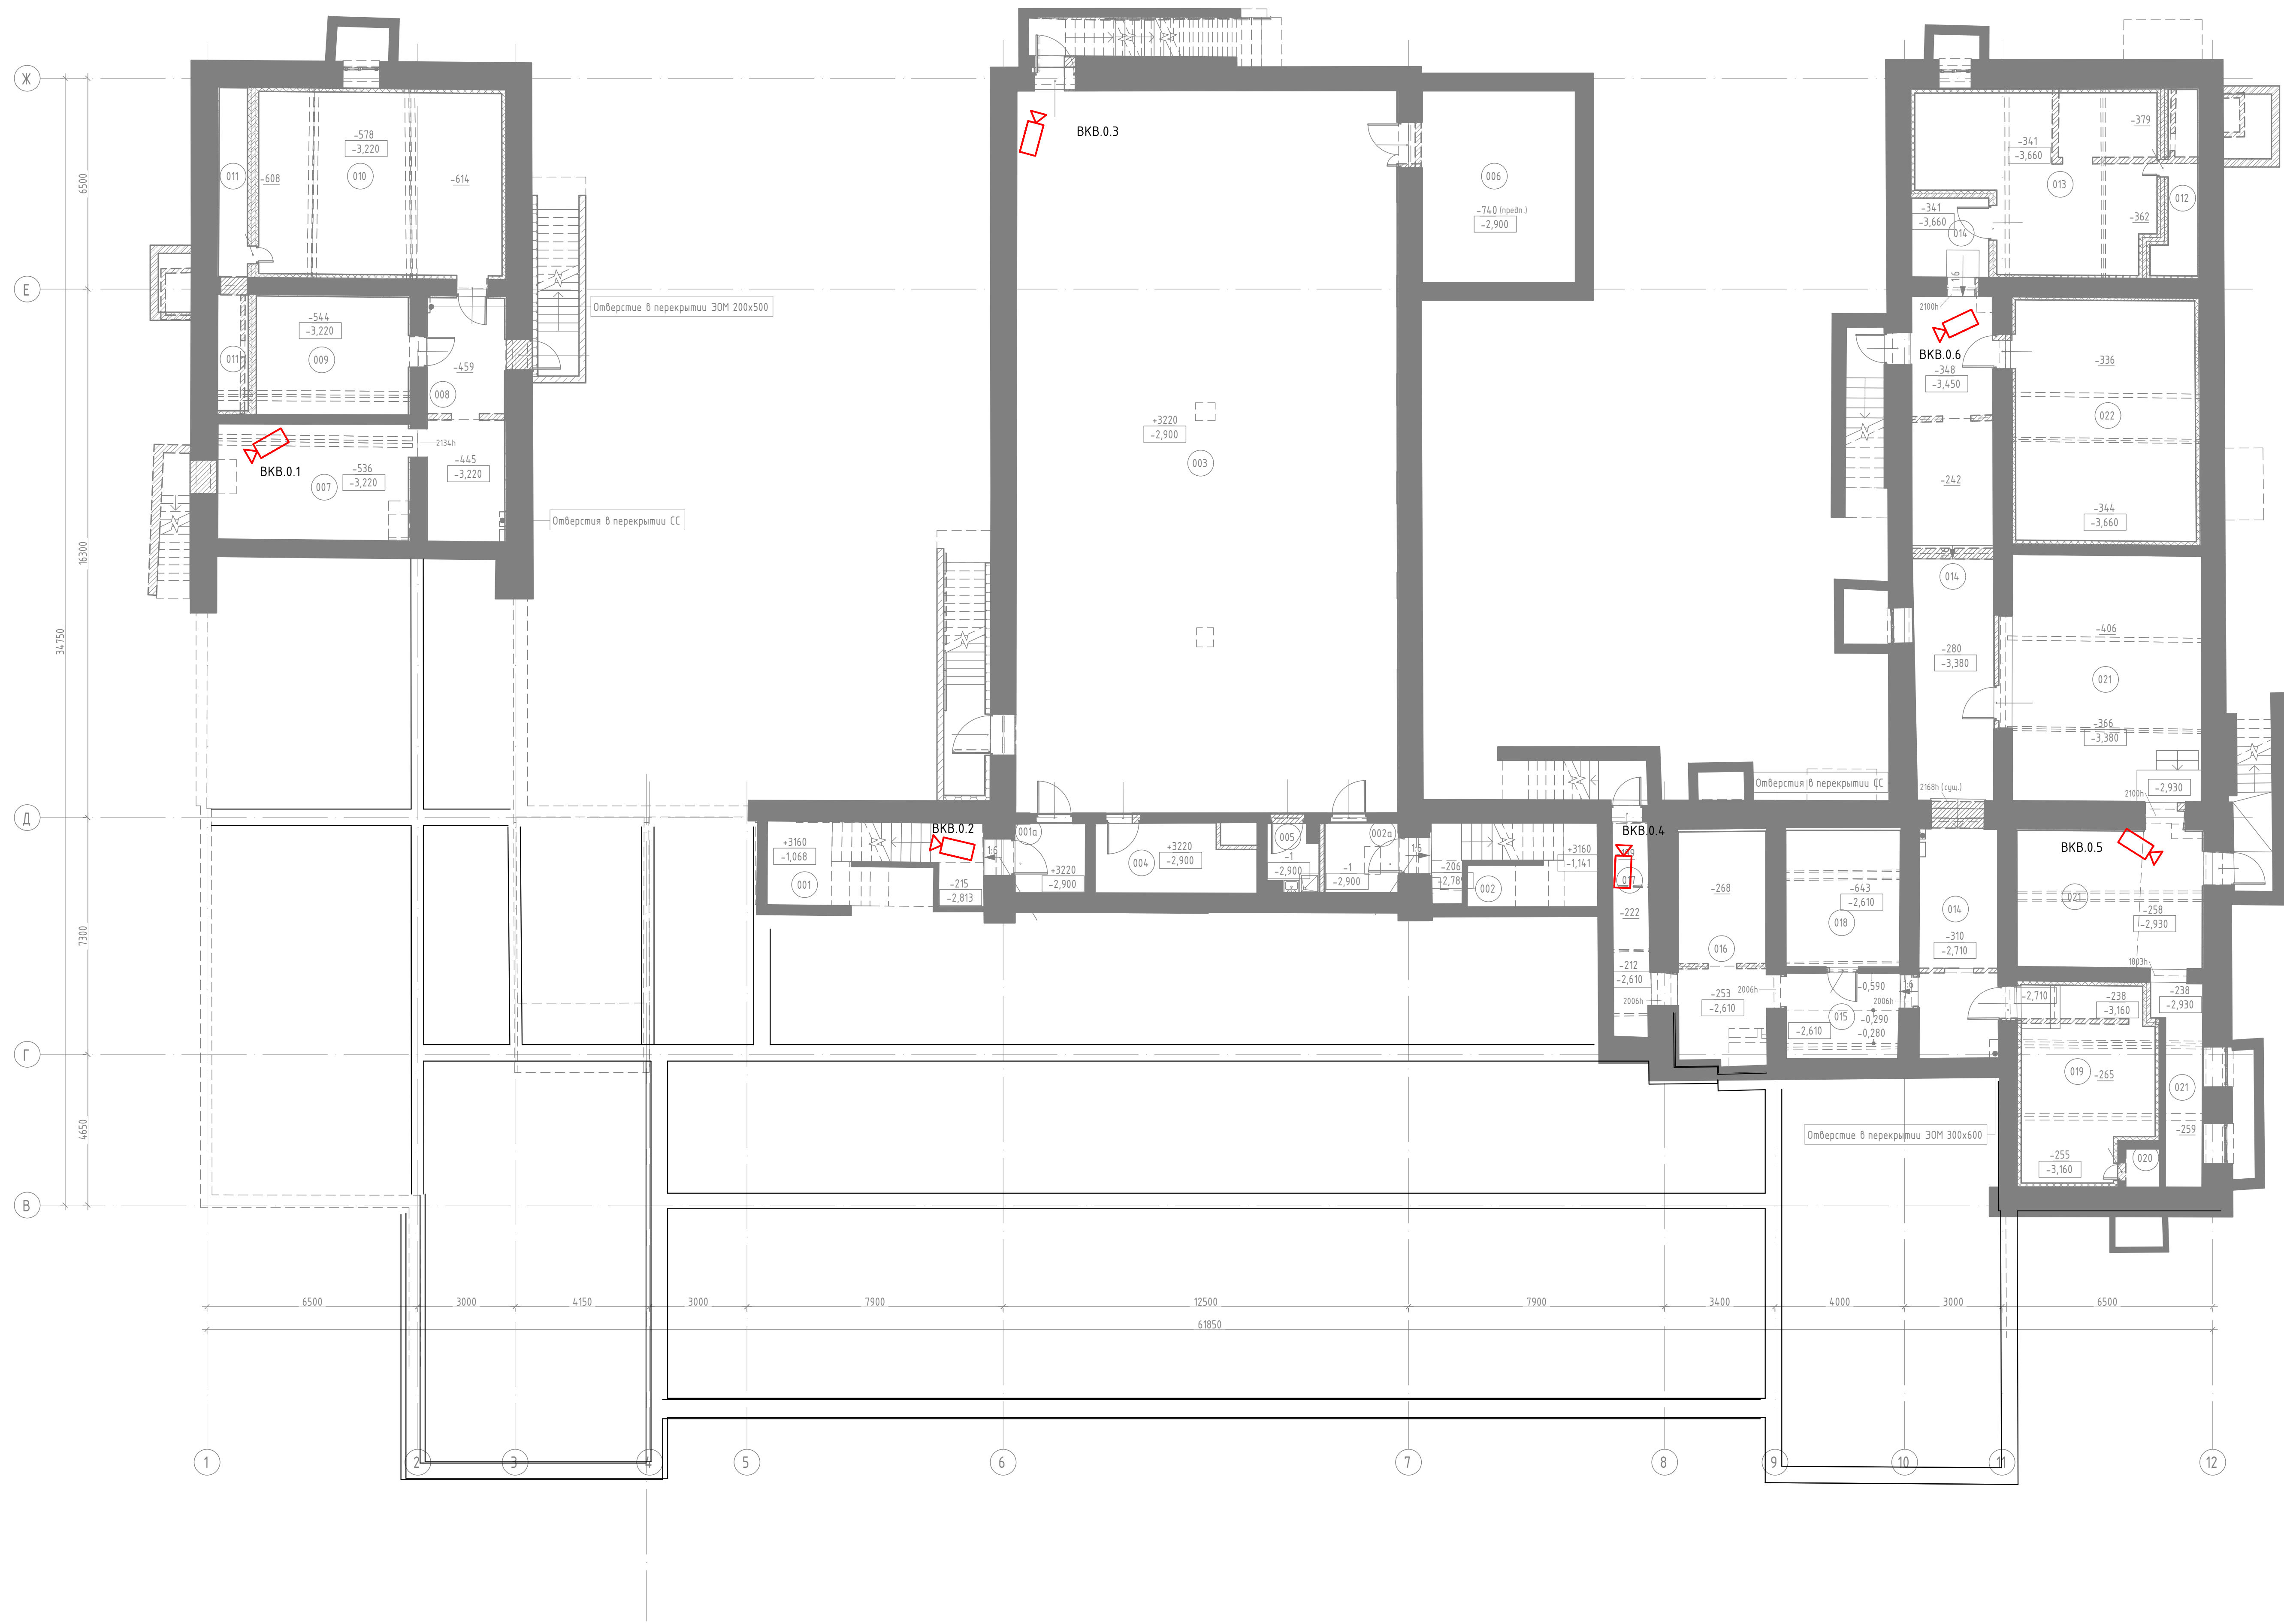

Экспликация помещений подвала			
Номер помеще-ния	Наименование	Площадь, м²	Кат. помеще-ния
001	Техническая лестница	13,7	
001а	Тандем-шифт 1-го типа	4,8	
002	Техническая лестница	9,8	
002а	Тандем-шифт 1-го типа	4,9	
003	Спортивный зал	262,5	
004	Складная	9,9	В3
005	ПВН	3,5	
006	Складная	28,0	В3
007	Коридор	21,0	
008	Коридор	17,9	
009	Жалюзая	17,1	В3
010	Венткамера	42,1	В4
011	Фармакара	8,9	В4
012	Фармакара	5,7	В4
013	Венткамера	34,6	В4
014	Коридор	63,3	
015	Коридор	9,8	
016	Коридор	20,0	
017	Коридор	8,3	
018	Насосная	14,8	В4
019	Венткамера	22,8	В4
020	Фармакара	1,2	В4
021	ИТП	77,8	Д
022	Венткамера	41,1	В4
ИТОГО:		743,4	

Примечания:
Железные ограждения, кабельная продукция и
кабельные конструкции заложены разделом ОК.


				696/П-24-АНО-Р-СОТ				
				Капитальный ремонт Государственного Бюджетного Общеразвлекательного Учреждения города Москвы «Цирка № 1202 «Солнечный по адресу: г. Москва, ул. Барбосова, д. 1, корп. 1				
Имя	Кол-во	Лист	Итого	Подпись	Дата	Страниц	Лист	Листов
Разработчик						р	3	
Проверенный				Гуляев		Система охранного телевидения		
Н. номер				Гуляев		План расположения оборудования. Подвал.		
								

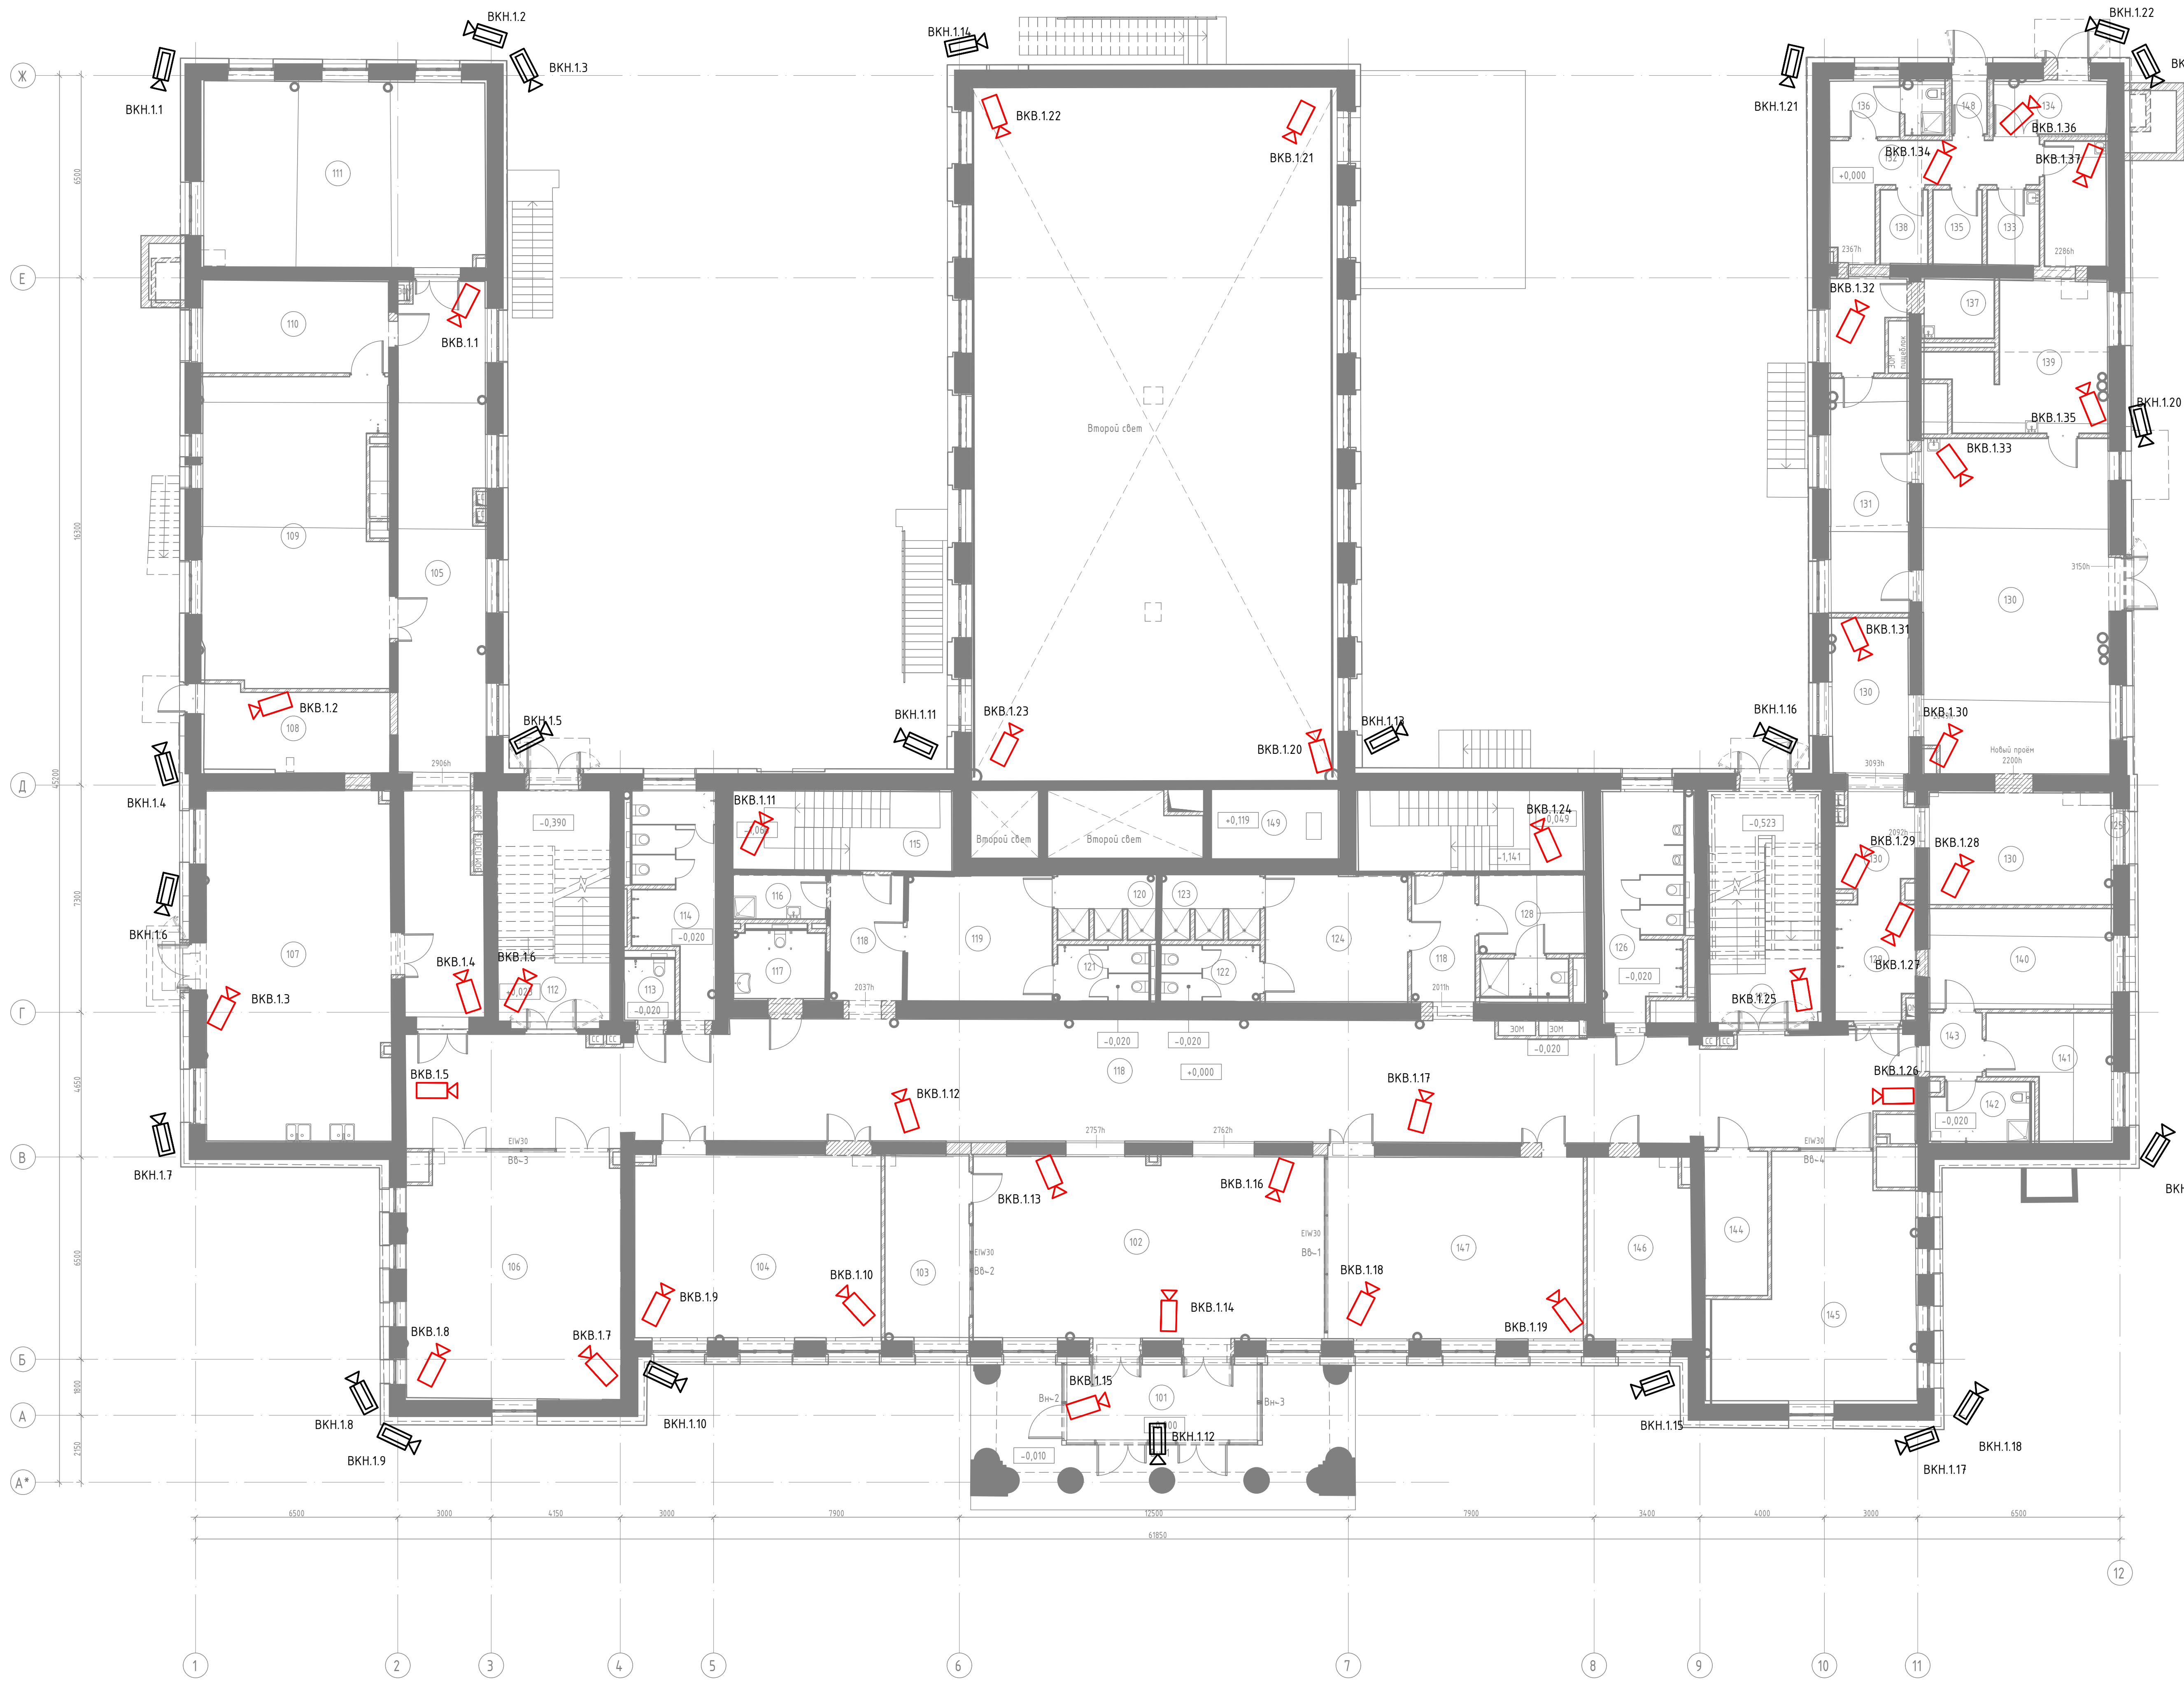

Экспликация помещений 1-го этажа			
Номер помеще-ния	Наименование	Площадь, м²	Кат. помеще-ния
101	Тайдур	11,0	
102	Вестибиль	67,2	
103	Канцелярия охраны (с диспетчерским пунктом)	16,4	
104	Гардероб для обучающихся	44,9	
105	Коридор	62,8	
106	Гардероб для обучающихся	54,2	
107	Учебный кабинет (Туп 1)	67,2	
108	Электрощитовая	15,6	B3
109	Учебный кабинет (Туп 2)	57,3	
110	Кладовая	18,0	B3
111	Учебный кабинет (капелланка)	54,6	
112	Лестничная клетка (Туп ЛП)	27,6	
113	Туалет для персонала	3,2	
114	Уборная для девочек	15,9	
115	Техническая лестница	18,0	
116	ЛПМ	4,2	B4
117	Универсальная уборная для МГН	6,6	
118	Коридор	198,7	
119	Раздевальная Туп 1	18,7	
120	Душевая	6,2	
121	Уборная	5,3	
122	Уборная	5,8	
123	Душевая	6,2	
124	Раздевальная Туп 1	18,6	
125	Техническая лестница	Не оборудована	
126	Уборная для мальчиков	18,0	
127	Лестничная клетка (Туп ЛП)	27,6	
128	Тренерская с санузлом	8,5	
129	Универсальная	9,2	
130	Объединенный зал	108,9	
131	Моечная для столовой посуды	18,8	B4
132	Коридор	13,1	
133	Кладовая и моечная оборотной тары	4,0	B4
134	Заварочный цех	6,2	B4
135	Кладовая сухих продуктов	3,7	B4
136	Помещение персонала с санузлом	4,2	
137	Пом. для временного хранения пищевых отходов	4,4	B4
138	ЛПМ	3,6	B4
139	Пом. подготовки белья к реализации с участием мойки кухонной посуды	30,3	B4
140	Кладовая тары	18,9	
141	Приватный (прибыльный) кабинет	13,2	
142	Пом. для хранения уборочного инвентаря, промывочных дезинфицирующих растворов	5,9	B4
143	Ожидающая медпункта	3,5	
144	Помещение СС	9,4	B4
145	Кабинет с рабочим пространством для учителей (Туп 1)	42,0	
146	Гардероб для учителей	19,4	
147	Гардероб для обучающихся	49,0	
148	Тайдур	2,0	
149	Ванная	9,1	?
Итого:		1245,1	

Примечания:
Железные ограждения, кабельная продукция и кабельные конструкции заложены разделом ОК.

696/П-24-АНО-Р-СОТ									
Капитальный ремонт Государственного бюджетного общеобразовательного учреждения города Москвы «Школа № 1292 «Специальная по адресу: г. Москва, ул. Барбарина, д. 1, корп. 1»									
Имя	Кол	Лист	Изд	Подпись	Дата				
Разработчик	Григорьев	Григорьев	Григорьев	Григорьев	Григорьев	Система	охранного	теплообеспечения	
Н. номер	Григорьев	Григорьев	Григорьев	Григорьев	Григорьев	Р	4	Листов	
План расположения оборудования, 1 этаж.						Формат А0 альбомная (841x1189)			

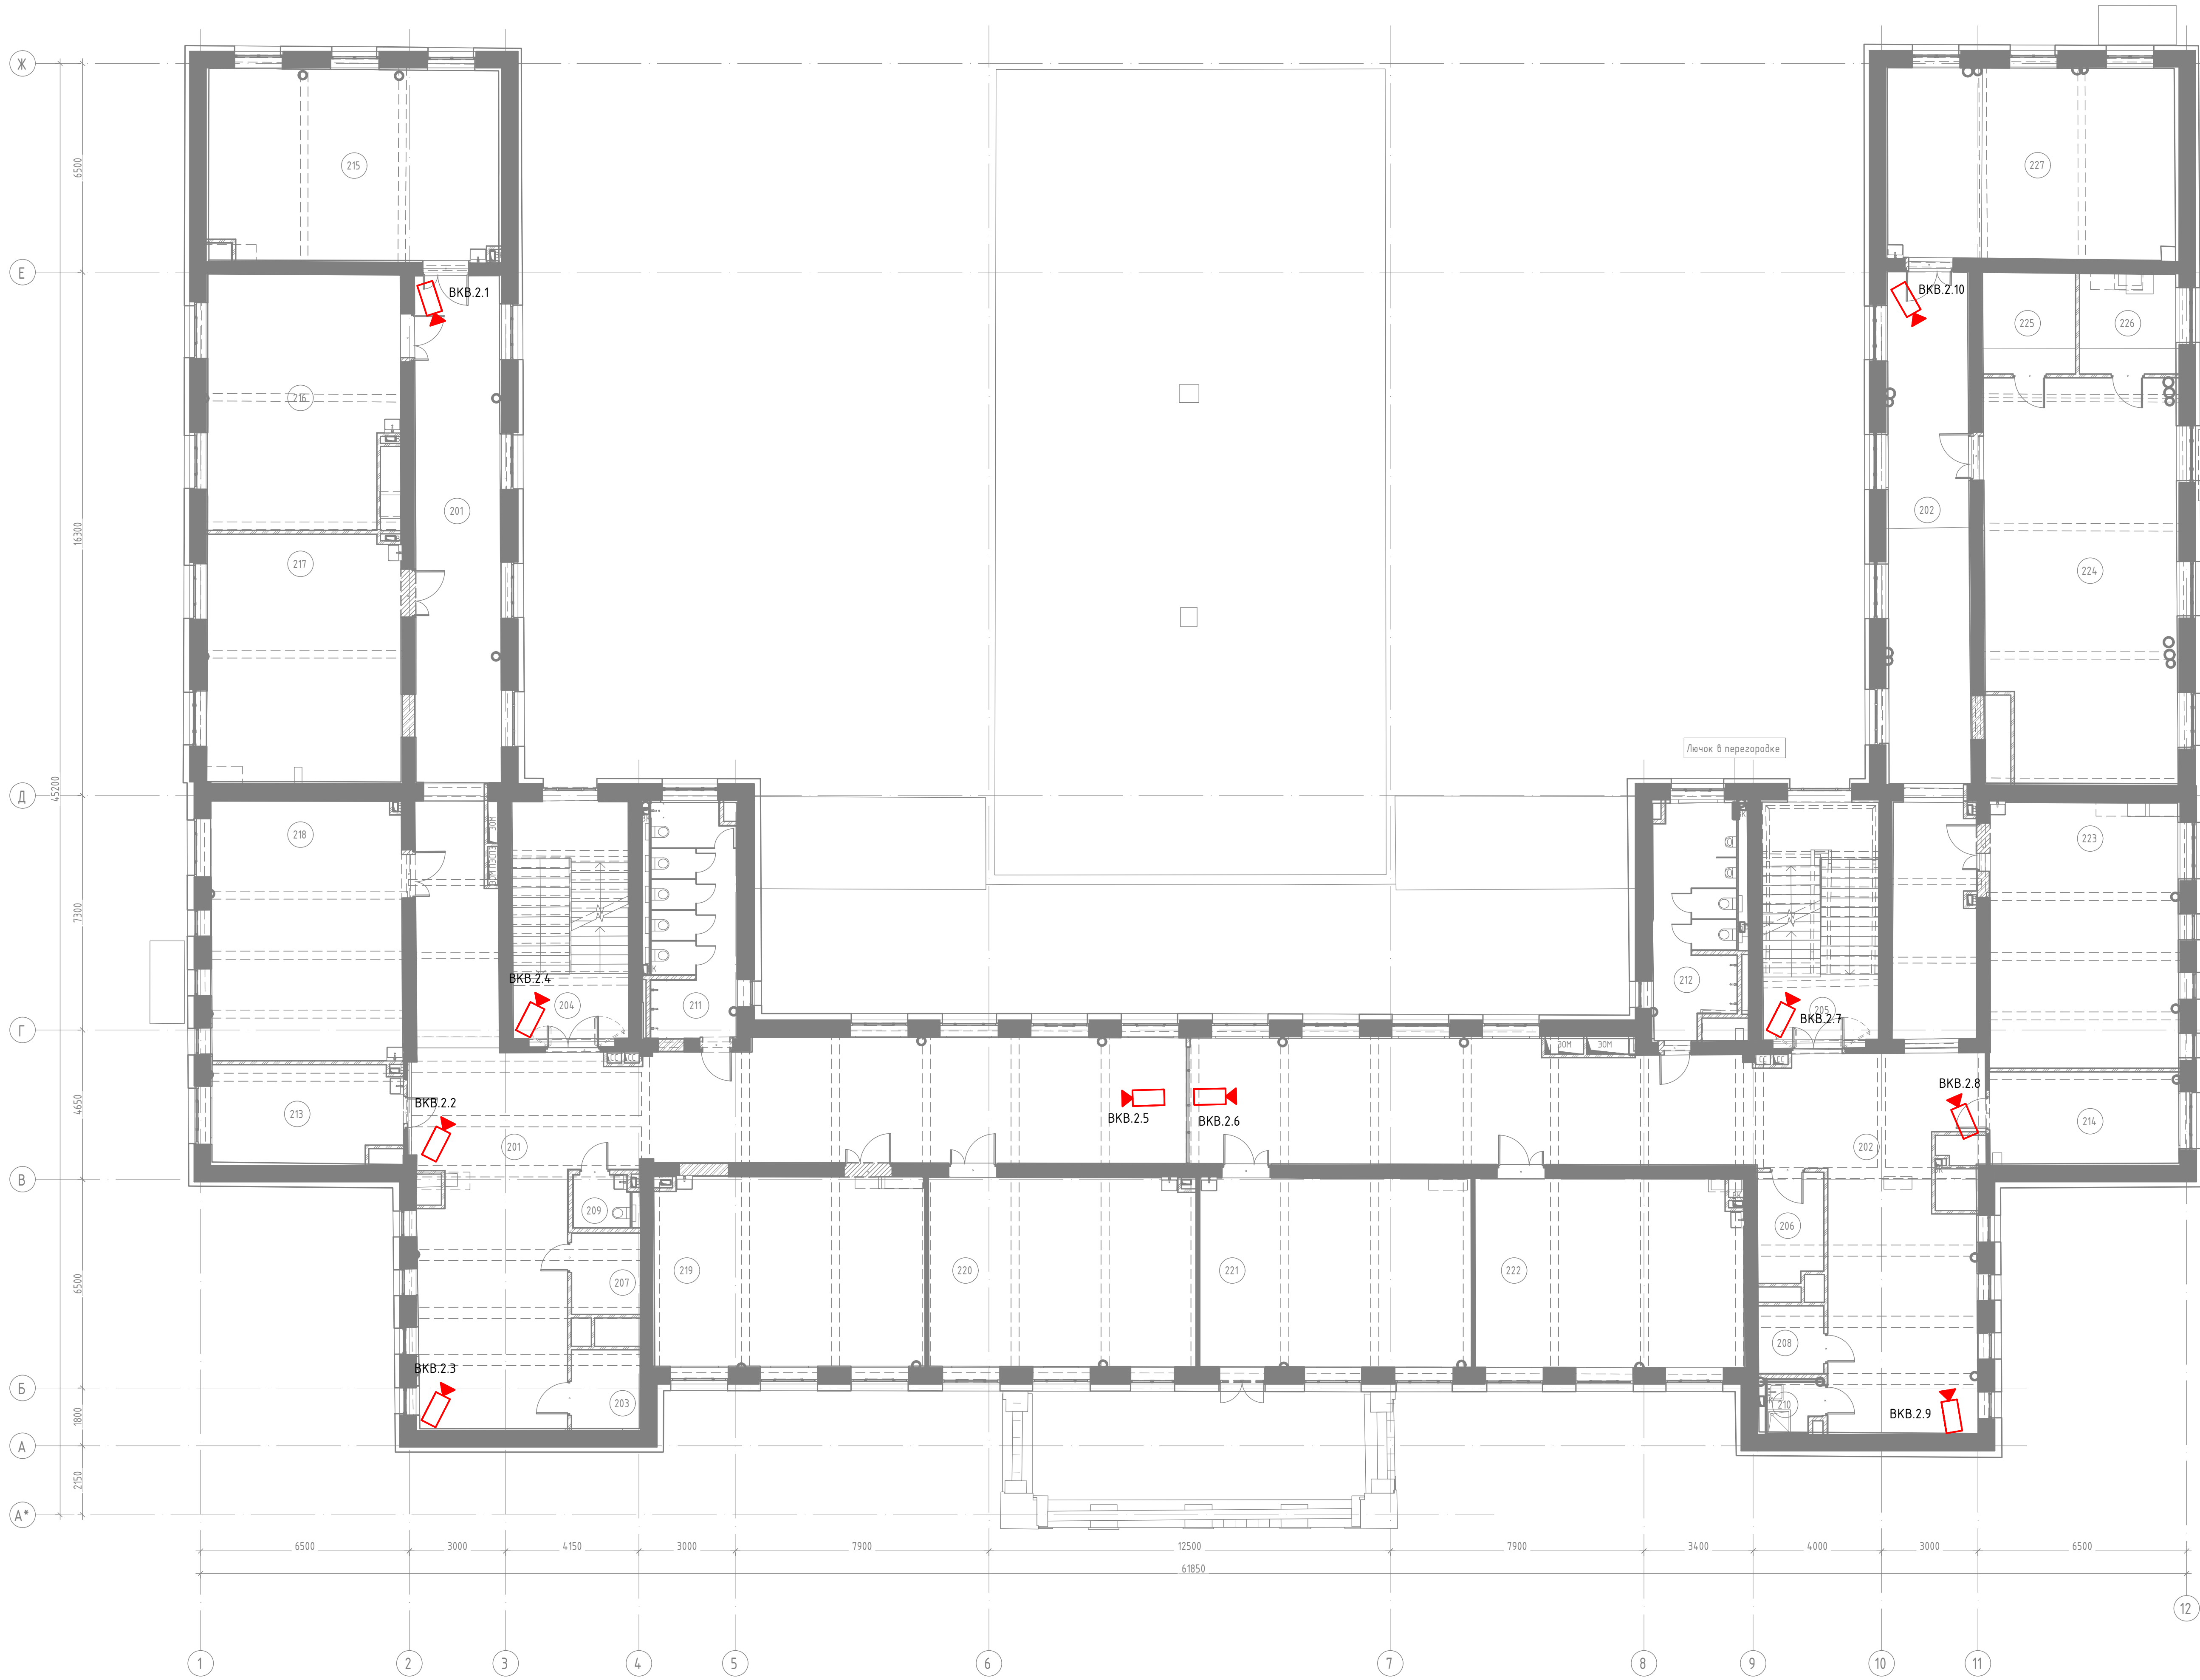


Экспликация помещений 2-го этажа

Номер помеще-ния	Наименование	Площадь, м²	Кат. помеще-ния
201	Коридор с рекреацией	180,6	
202	Коридор с рекреацией	188,2	
203	Помещение СС	5,5	Б4
204	Лестничная клетка (Тип А1)	27,4	
205	Лестничная клетка (Тип А1)	27,7	
206	Помещение СС	6,9	Б4
207	Подсобное помещение	5,4	Б4
208	Подсобное помещение	4,3	Б4
209	Турелл для персонала	2,8	
210	Т/М	2,6	Б4
211	Уборная для девочек	19,4	
212	Уборная для мальчиков	18,1	
213	Кабинет для индивидуальных занятий, в т.ч. с учителем-наставником	17,5	
214	Административный кабинет (Тип А)	17,0	
215	Учебный кабинет	53,5	
216	Учебный кабинет	45,8	
217	Учебный кабинет	46,5	
218	Учебный кабинет	48,0	
219	Учебный кабинет	49,5	
220	Учебный кабинет	48,9	
221	Учебный кабинет	49,8	
222	Учебный кабинет	48,7	
223	Учебный кабинет	49,0	
224	Патентный кабинет	73,7	
225	Раздевальня Тип 1	9,1	
226	Раздевальня Тип 1	9,5	
227	Учебный кабинет	53,6	
Итого:		1119,0	

Примечания:
Активные оборудование, кабельная продукция и кабельные конструкции заложены разделом ОК.


696/П-24-АНО-Р-СОТ					
Капитальный ремонт Государственного Бюджетного					
Общеразвивательного Учреждения города Москвы «Школа № 1202					
«Специализация по физкультуре и спорту» в Москве, ул. Барыкина, д. 1, корп. 1					
Имя	Кол	Лист	Итого	Подпись	Дата
Разработчик	Григорьев	Григорьев	Григорьев	Григорьев	Григорьев
Проверен	Григорьев	Григорьев	Григорьев	Григорьев	Григорьев
И. номер	Григорьев	Григорьев	Григорьев	Григорьев	Григорьев
План расположения оборудования.				Страница	Лист
3 этаж.				Р	5
Формат А0 альбомная (841х1189)				Листов	

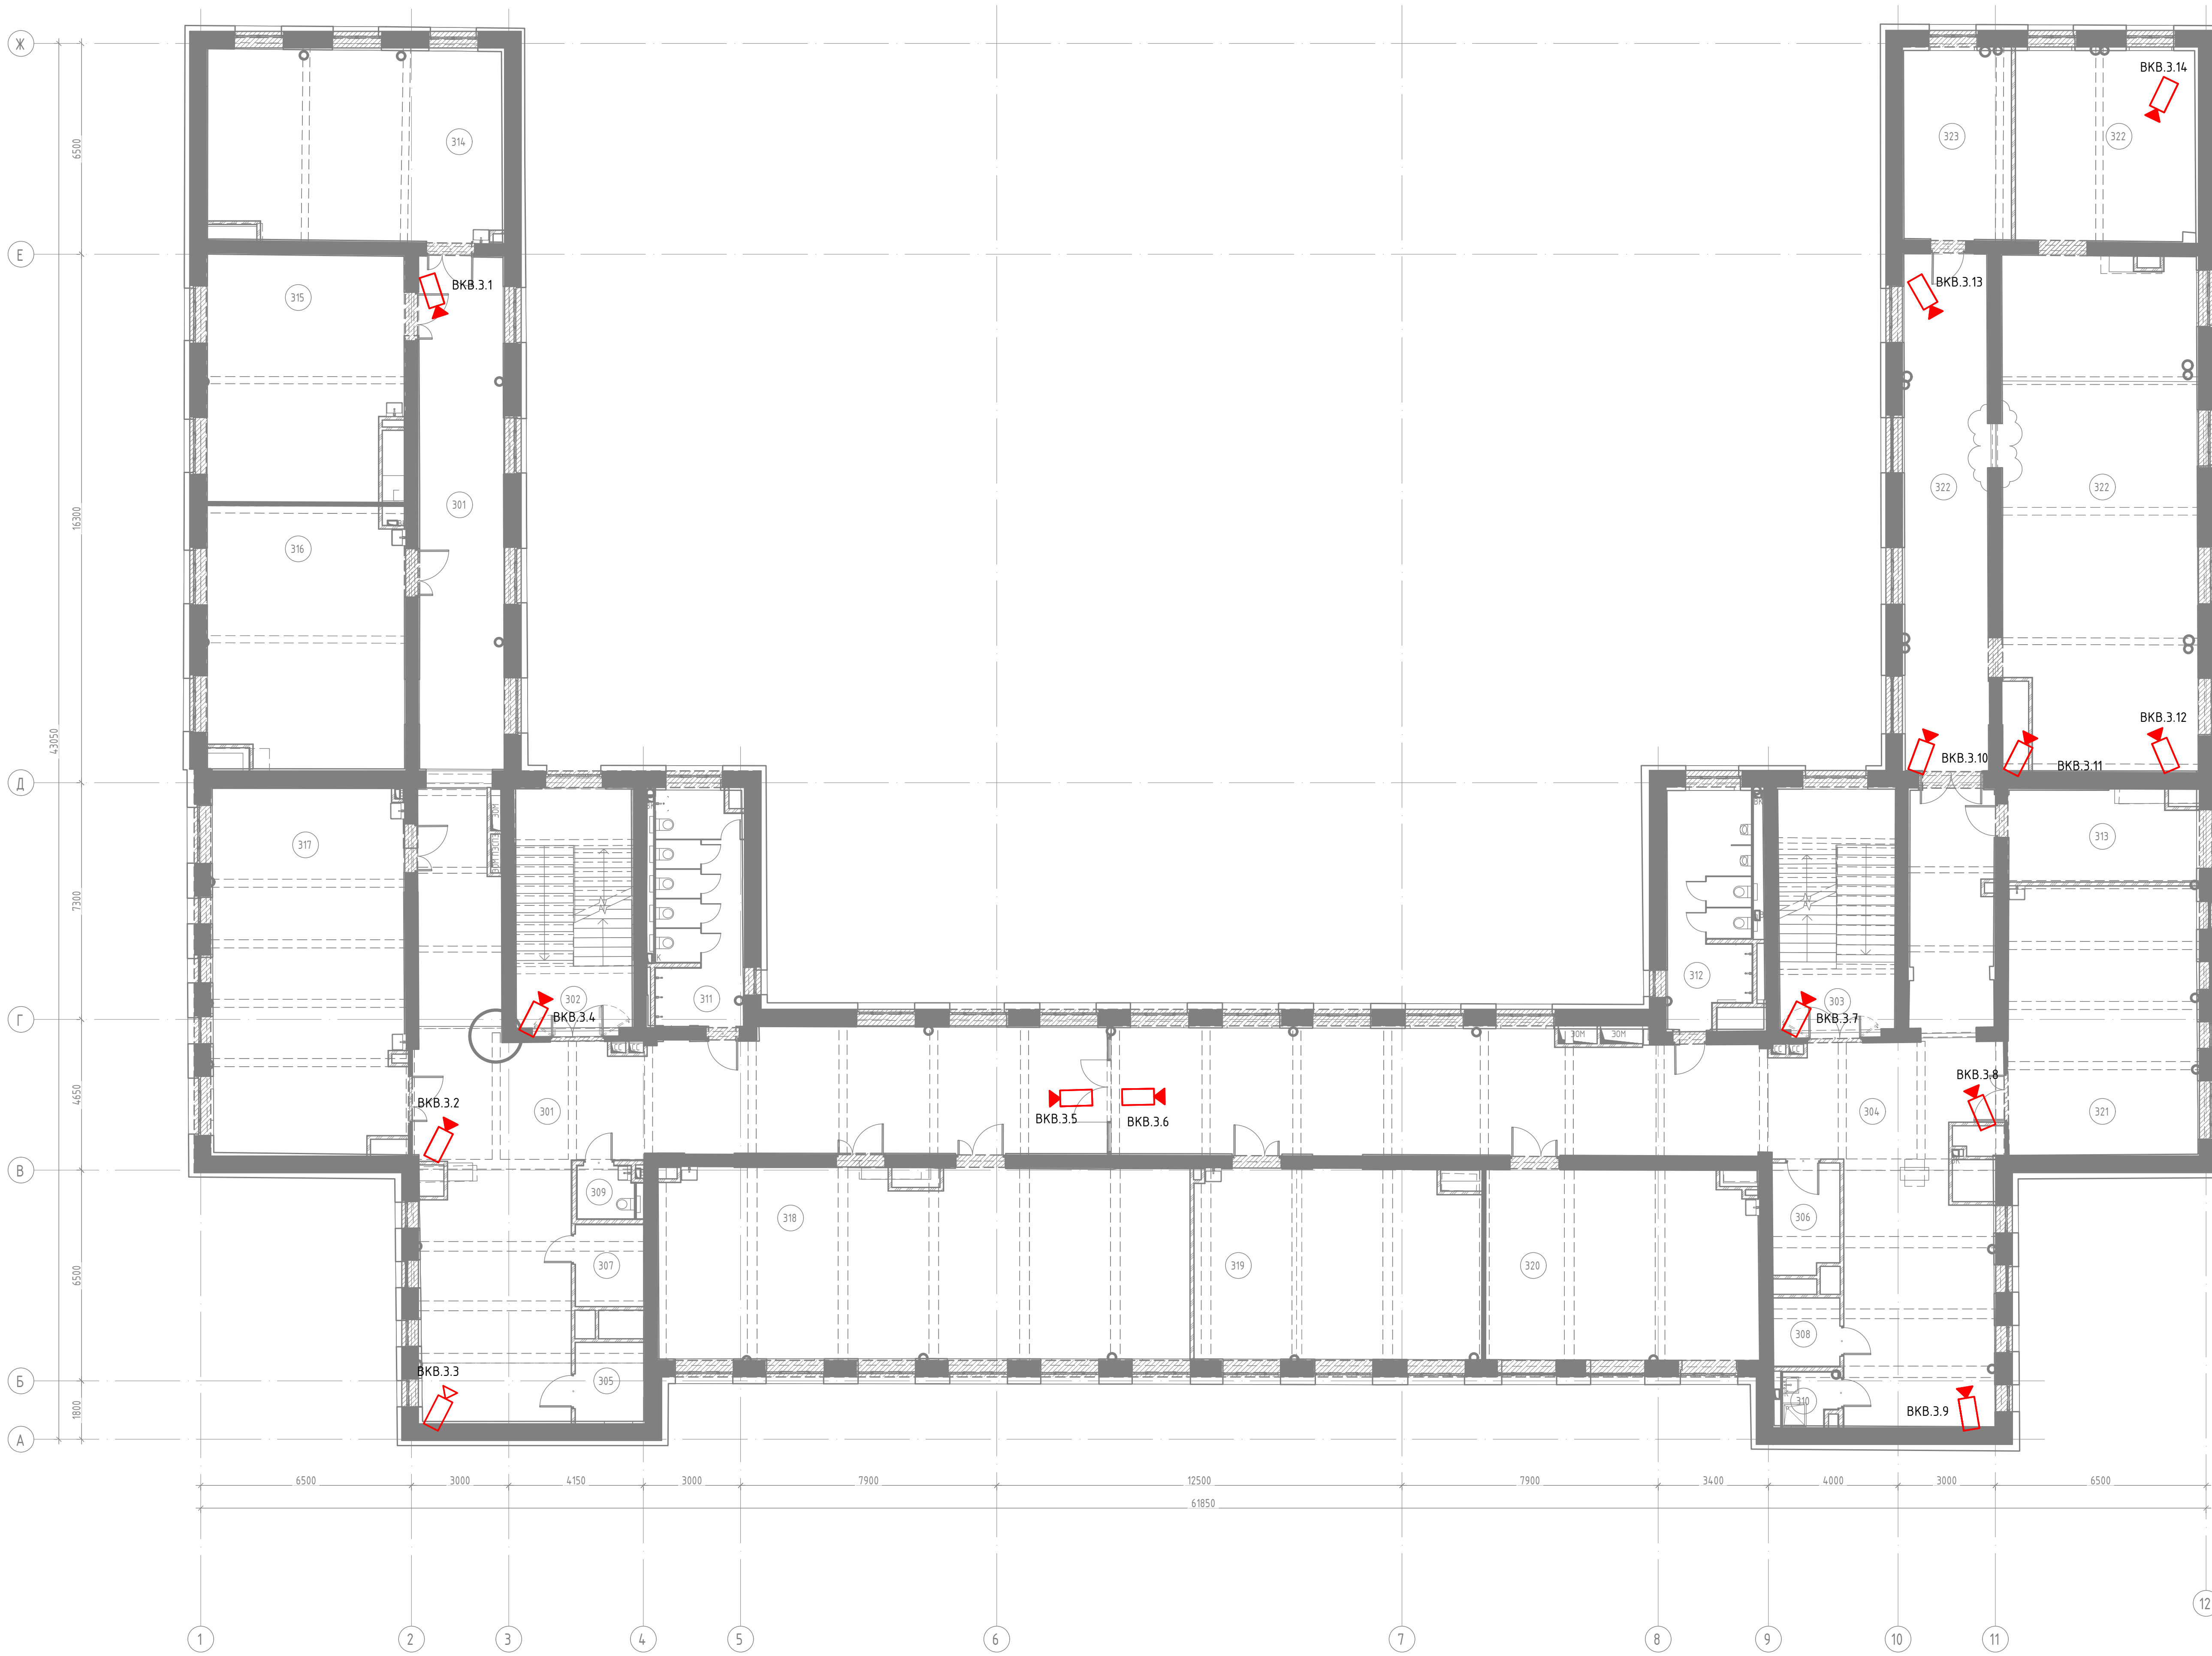

Экспликация помещений 3-го этажа			
Номер помеще-ния	Наименование	Площадь, м²	Кат. помеще-ния
301	Коридор с рекреацией	118,8	
302	Лестничная клетка (Тип Л0)	27,1	
303	Лестничная клетка (Тип Л0)	27,4	
304	Коридор с рекреацией	156,6	
305	Помещение СС	5,3	В4
306	Помещение СС	6,9	В4
307	Подсобное помещение	5,3	В4
308	Подсобное помещение	4,3	В4
309	Туалет для персонала	2,8	
310	ПМ	2,7	В4
311	Зубная для девочек	19,0	
312	Зубная для мальчиков	18,3	
313	Кабинет для индивидуальных занятий, В.м.ч. с коррекционным педагогом	15,9	
314	Учебный кабинет	53,0	
315	Учебный кабинет	44,6	
316	Учебный кабинет	48,0	
317	Кабинет иностранного языка с возможностью обучения трансформированной перегородкой на два помещения	66,1	
318	Музыкальная студия с возможностью деления трансформированной перегородкой на два помещения	95,4	
319	Учебный кабинет	51,0	
320	Учебный кабинет	48,5	
321	Учебный кабинет	48,5	
322	Многофункциональный информационный библиотечный центр с зонами для индивидуальных занятий, медиатеки, центра детских инициатив	169,7	
323	Многофункциональный информационный библиотечный центр. Хранение (закрытый фонд) и выдача книг	19,7	В3
Итого:		1115,0	

Примечания:
Активные оборудование, кабельная продукция и кабельные конструкции заложены разделом ОК.

				696/П-24-АНО-Р-СОТ		
				Капитальный ремонт Государственного бюджетного		
				Общественного учреждения города Москвы «Школа № 1202		
				«Специальная по адресу: г. Москва, ул. Барбарисов, д. 1, корп. 1		
Имя	Кол-во	Лист	Итого	Подпись	Дата	
Разработчик	Генерал	Генерал	Генерал	Генерал	Генерал	
Проектировщик	Генерал	Генерал	Генерал	Генерал	Генерал	
Н. инженер	Генерал	Генерал	Генерал	Генерал	Генерал	
				Система охранного видеонаблюдения		
				План расположения оборудования, 3 этаж.		
				Формат А0 альбомная (841x1189)		

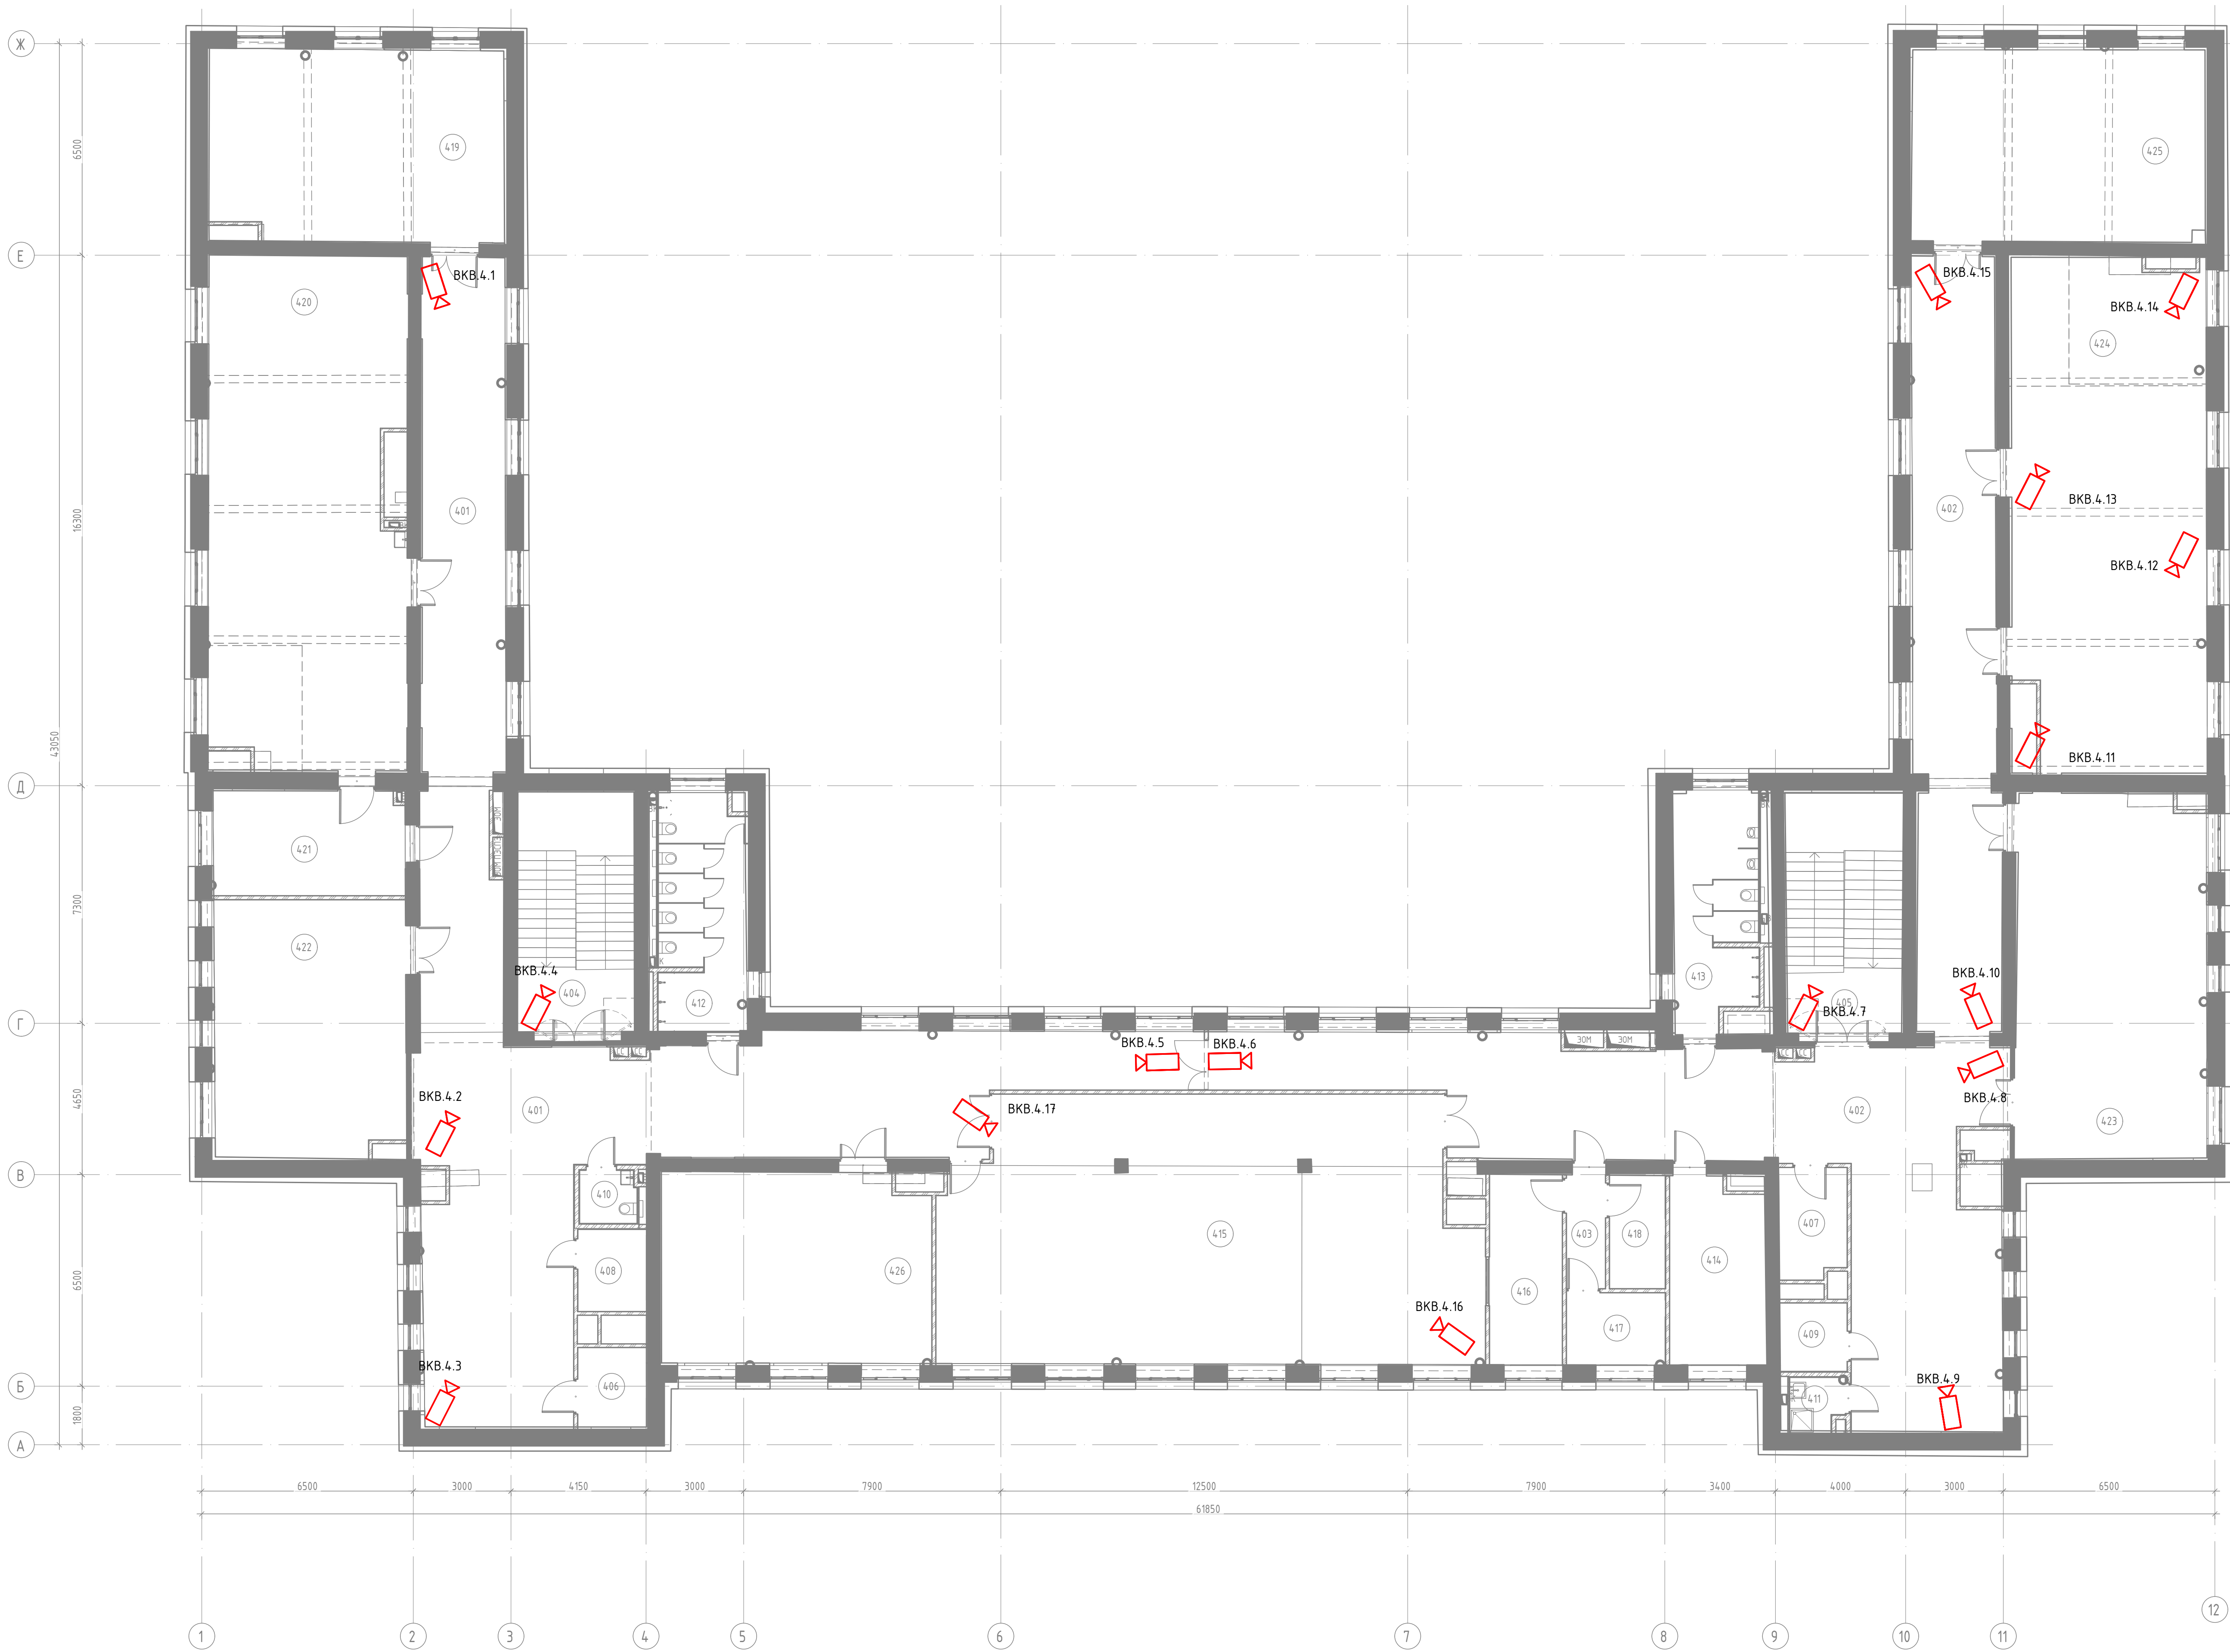

Экспликация помещений 4-го этажа


Номер помеще-ния	Наименование	Площадь, м²	Кат. помеще-ния
401	Коридор с рекреацией	175,9	
402	Коридор с рекреацией	172,6	
403	Тамбур	4,2	
404	Лестничная клетка (Тип Л1)	27,2	
405	Лестничная клетка (Тип Л1)	27,3	
406	Помещение СС	5,3	В4
407	Помещение СС	7,0	В4
408	Подсобное помещение	5,3	В4
409	Подсобное помещение	4,3	В4
410	Туалет для персонала	2,8	
411	ПМ	2,8	В4
412	Забирная для девочек	19,3	
413	Забирная для мальчиков	18,4	
414	Кабинет для индивидуальных занятий, в т.ч. с педагогом-психологом	16,5	
415	Автомобильная эстрада в учебном зале	130,7	
416	Технический центр	13,1	В3
417	Арт-студия	6,8	
418	Кладовая инвентаря	6,0	В4
419	Кабинет математики	53,1	
420	Учебный кабинет (для изучения естественных наук)	93,5	
421	Лаборатория биологии	19,2	В3
422	Учебный кабинет (история)	46,6	
423	Кабинет иностранного языка с возможностью деления трансформировавшейся перегородкой на два помещения	65,7	
424	Кабинет информатики с возможностью деления трансформировавшейся перегородкой на два помещения	92,1	
425	Кабинет русского языка и литературы	53,8	
426	Кабинет русского языка и литературы	48,4	
Итого		1119,0	

Примечания:
Активные оборудование, кабельная продукция и кабельные конструкции заложены разделом ОК.

696/П-24-АНД-Р-СОТ					
Капитальный ремонт Государственного бюджетного общеобразовательного учреждения города Москвы «Школа № 1202 «Секретный по адресу: г. Москва, ул. Барбосова, д. 1, корп. 1					
Имя	Кол-во	Лист	Итого	Подпись	Дата
Разработчик	Кол-во	Лист	Итого	Подпись	Дата
Проверен	Кол-во	Лист	Итого	Подпись	Дата
Н. инициал	Кол-во	Лист	Итого	Подпись	Дата
Система охранного видеонаблюдения				Страница	Лист
План расположения оборудования, 3 этаж.				Р	7
Формат А0 альбомная (841х1189)					

Согласовано	
Взам.инв.Н	
Подпись и дата	
инв.Нподл.	

ТИПОВОЙ УЗЕЛ КРЕПЛЕНИЯ КАМЕРЫ

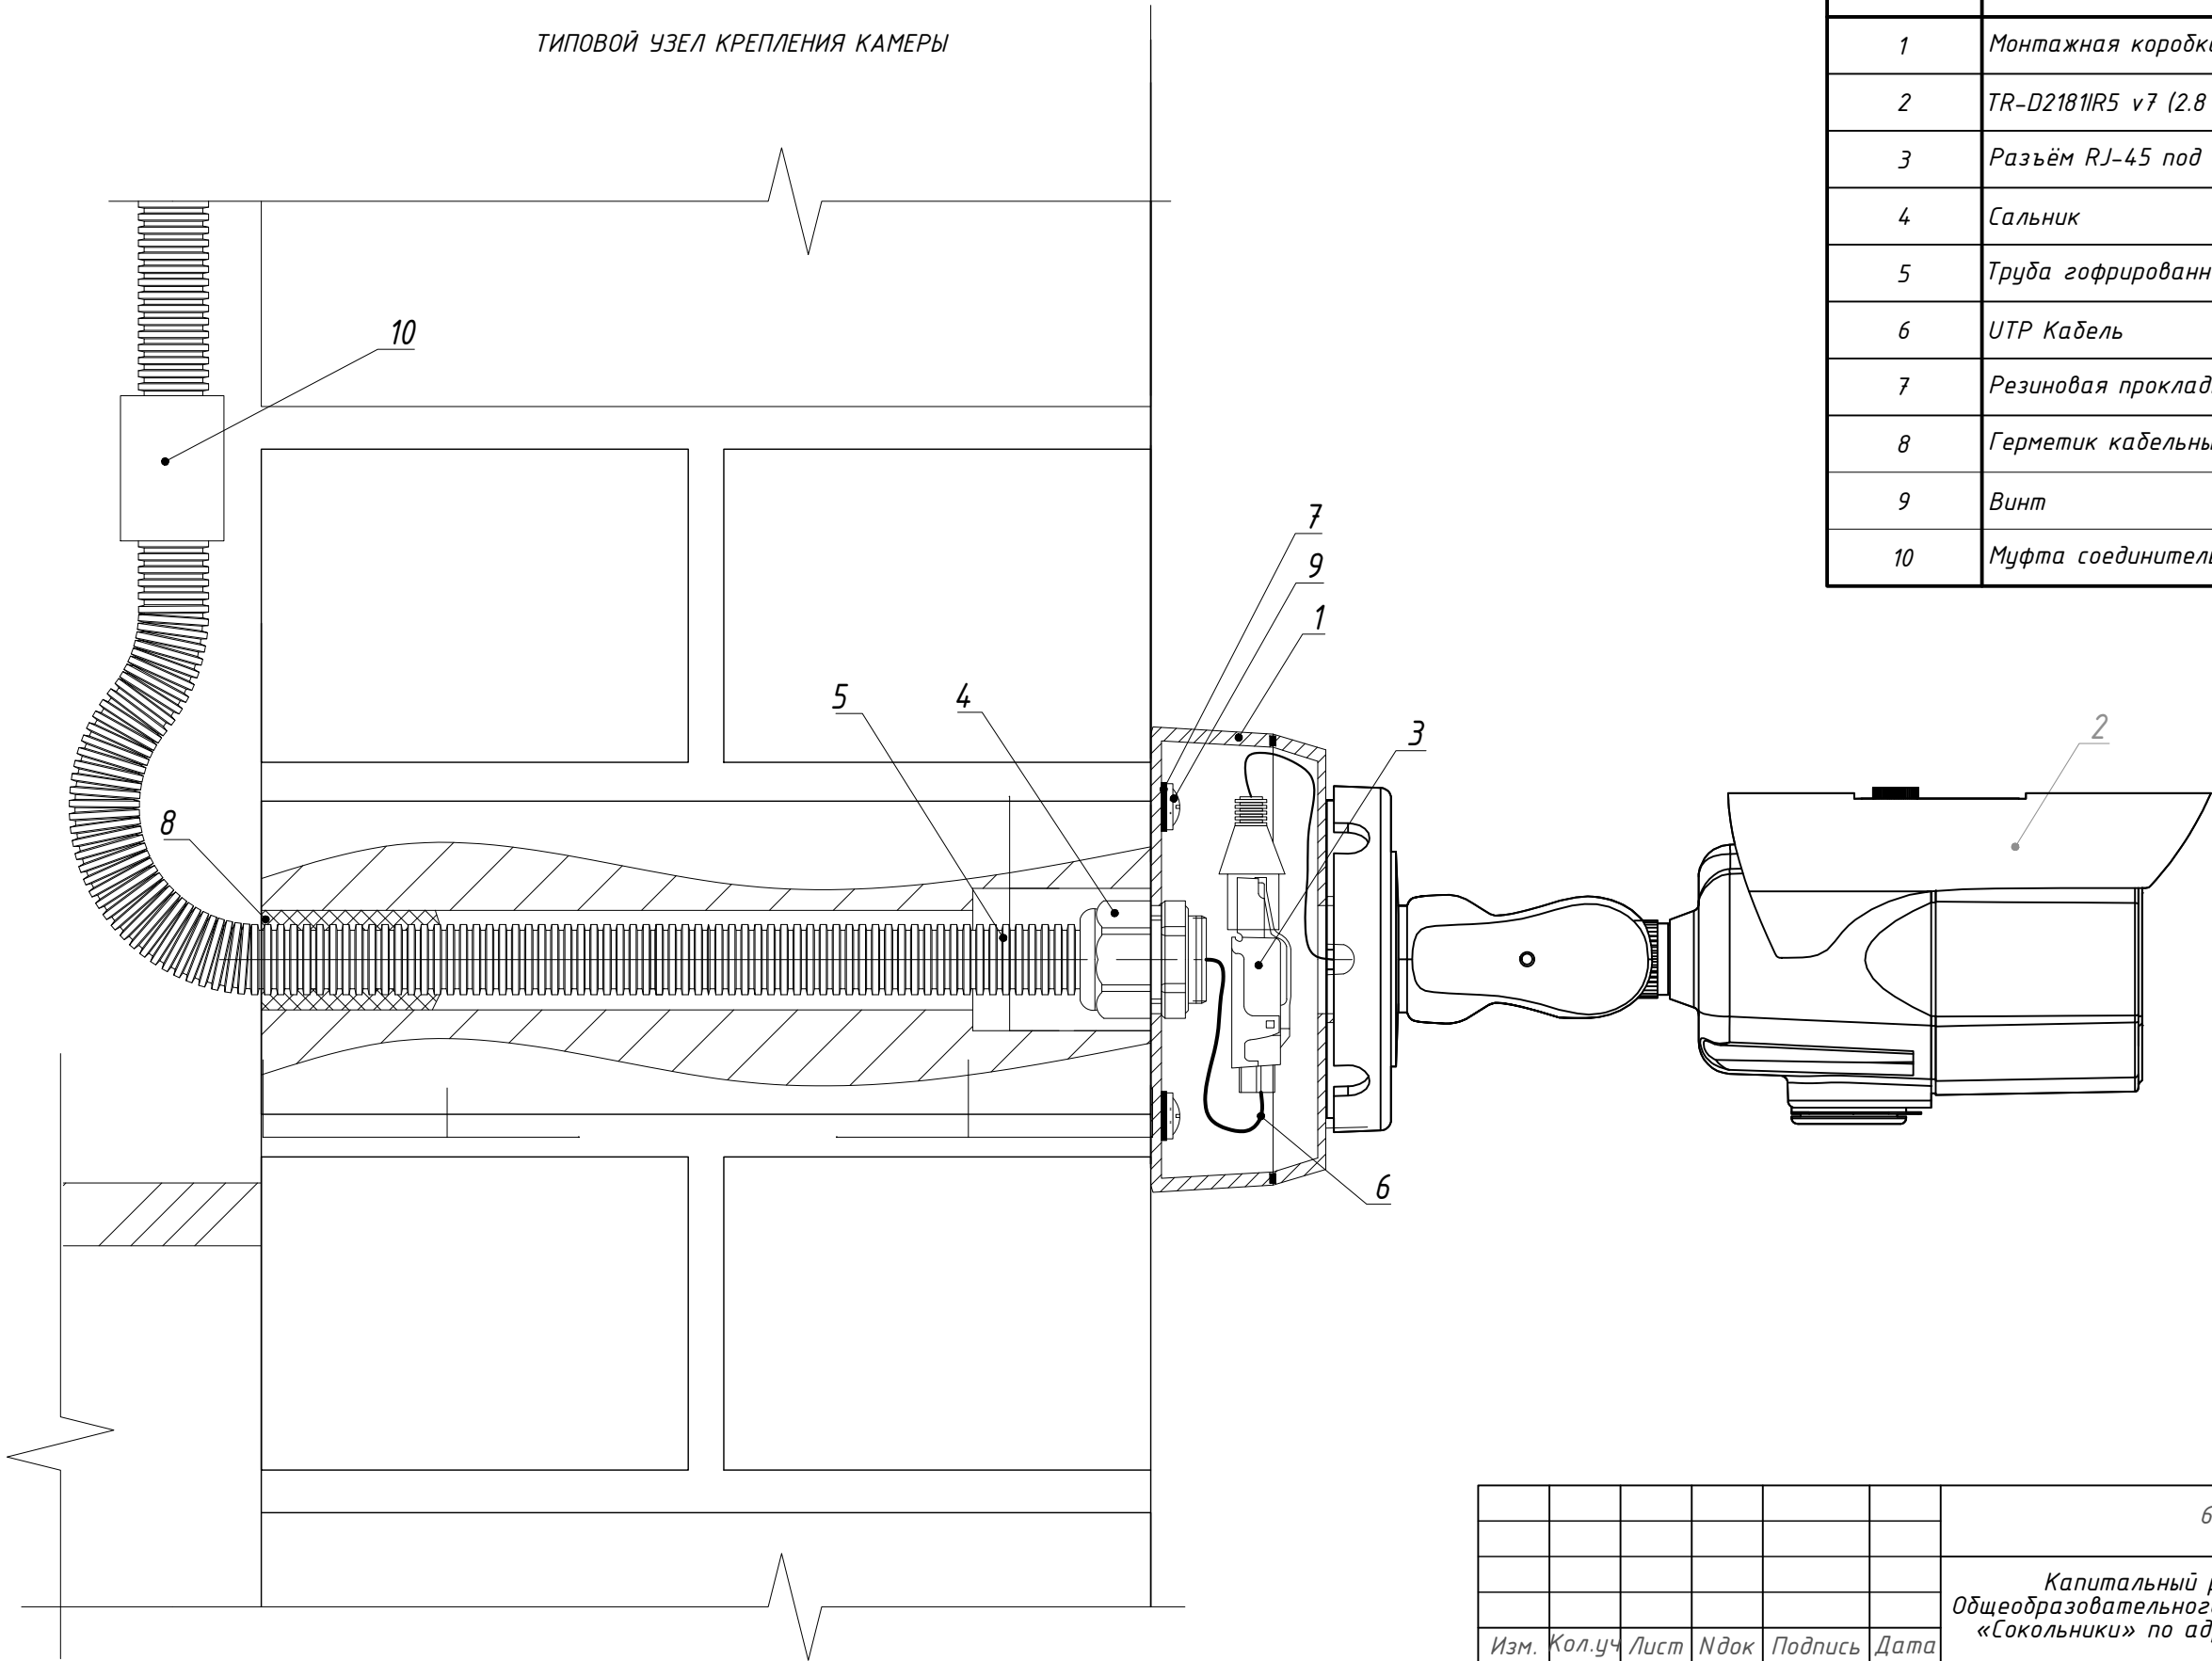


Поз. обозначени я	Наименование
1	Монтажная коробка TR-JB306
2	TR-D2181IR5 v7 (2.8 мм)
3	Разъём RJ-45 под витую пару
4	Сальник
5	Труба гофрированная с зондом
6	УТР Кабель
7	Резиновая прокладка
8	Герметик кабельных вводов
9	Винт
10	Муфта соединительная

						696/П-24-АНО-Р-СОТ			
						Капитальный ремонт Государственного Бюджетного Общеобразовательного Учреждения города Москвы «Школа № 1282 «Сокольники» по адресу: г. Москва, ул. Барболина, д. 1, корп. 1			
Изм.	Кол.уч	Лист	Ндок	Подпись	Дата	Система охранного теленаблюдения	Стадия	Лист	Листов
Разработал	Коняев						Р	8	
Проверил.	Гулько					Схема монтажа внешней камеры			
Н. контр.	Гулько								

Согласовано				
Взам.инв.Н				
Подпись и дата				
инв.Нподл.				


ТИПОВОЙ УЗЕЛ КРЕПЛЕНИЯ КАМЕРЫ

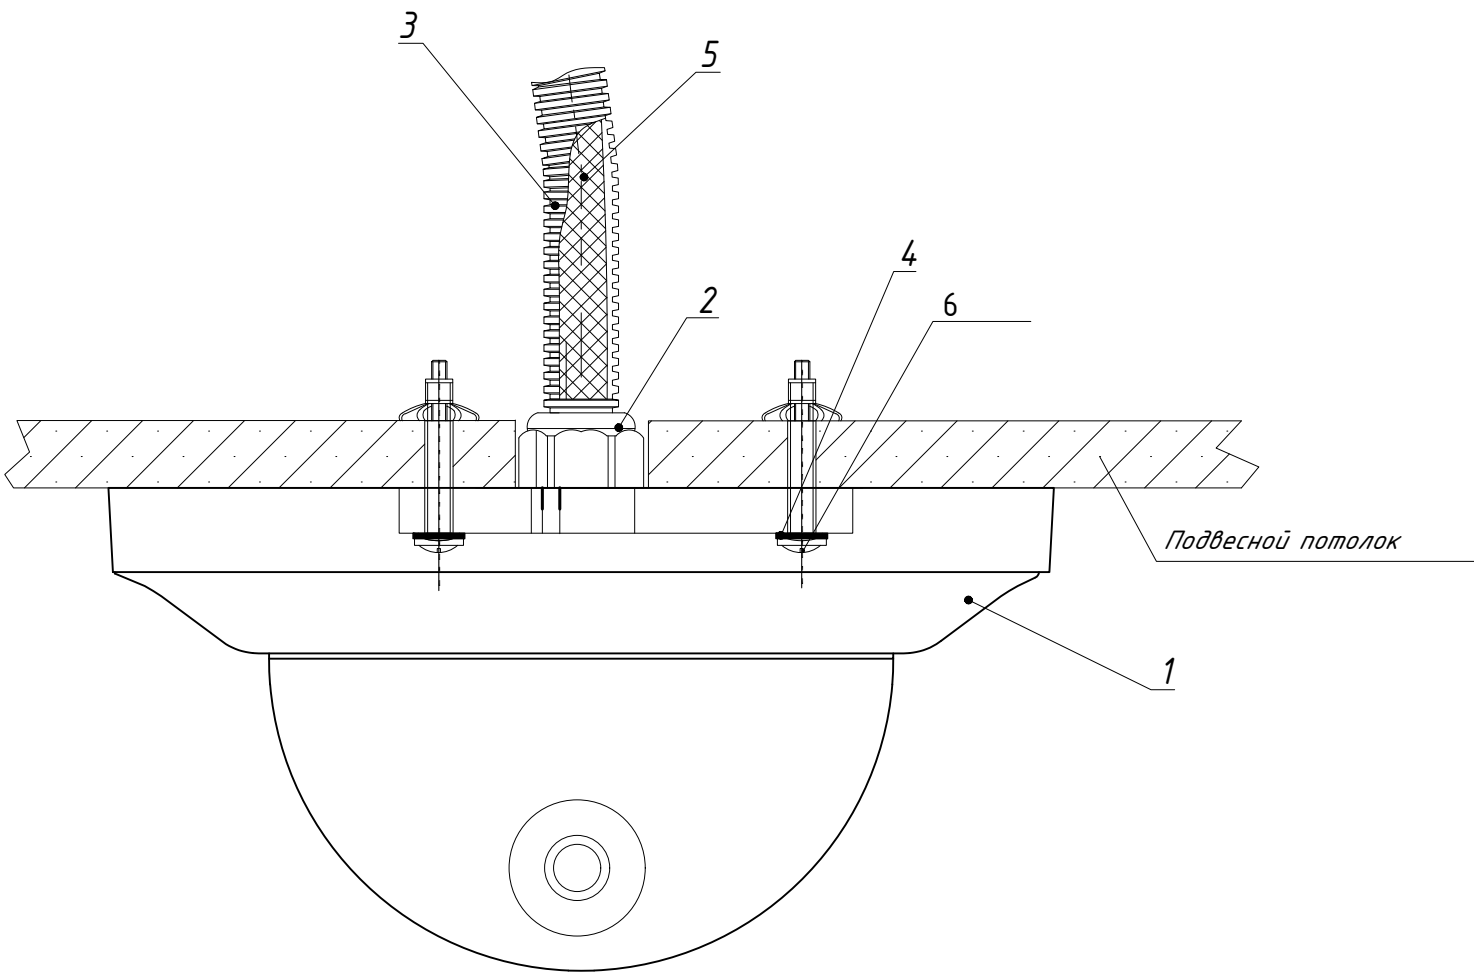


Поз. обозначени я	Наименование
1	Камера TR-D3181IR3 v7 (2.8 мм)
2	Сальник
3	Труба гофрированная с зондом Ø 20
4	Резиновая прокладка
5	Герметик кабельных вводов
6	Винт

						696/П-24-АНО-Р-СОТ			
						Капитальный ремонт Государственного Бюджетного Общеобразовательного Учреждения города Москвы «Школа № 1282 «Сокольники» по адресу: г. Москва, ул. Барболина, д. 1, корп. 1			
Изм.	Кол.уч	Лист	Ндок	Подпись	Дата	Система охранного теленаблюдения	Стадия	Лист	Листов
Разработал	Коняев						Р	9	
Проверил.	Гулько								
						Схема монтажа внутренней камеры			
Н. контр.	Гулько								

Схема интеграции внешней системы IP видеонаблюдения в ЕЦХД

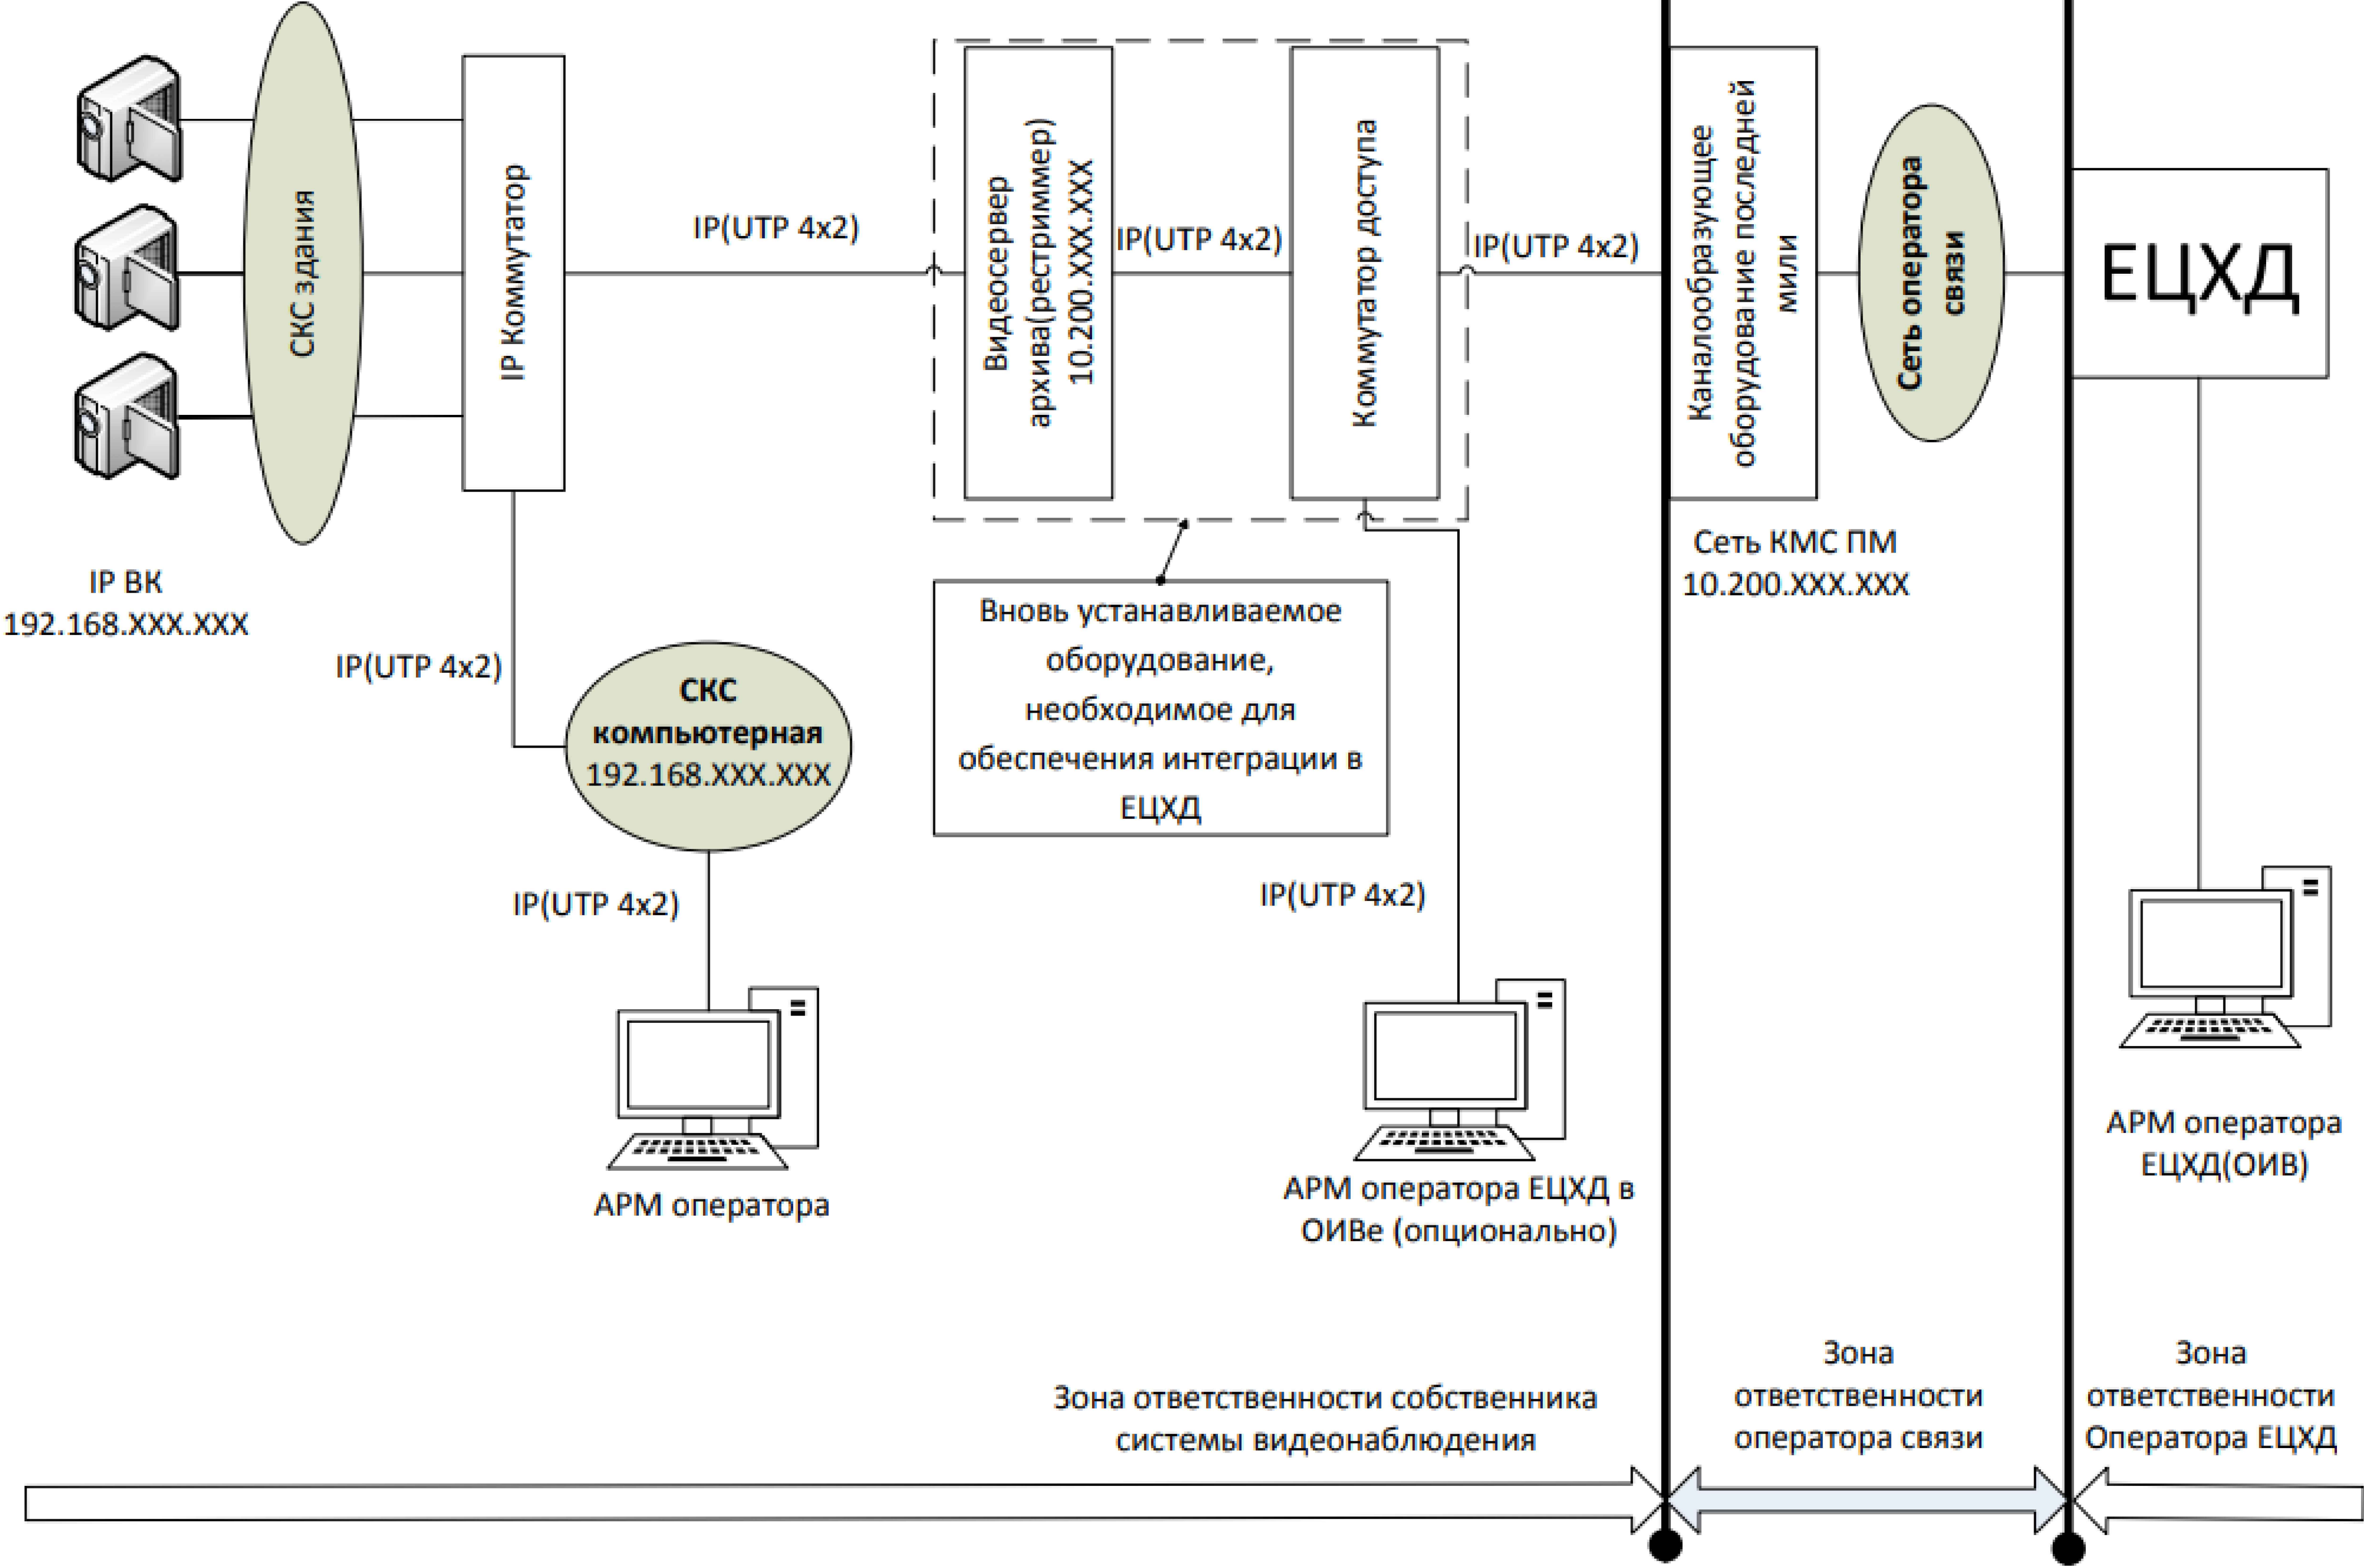

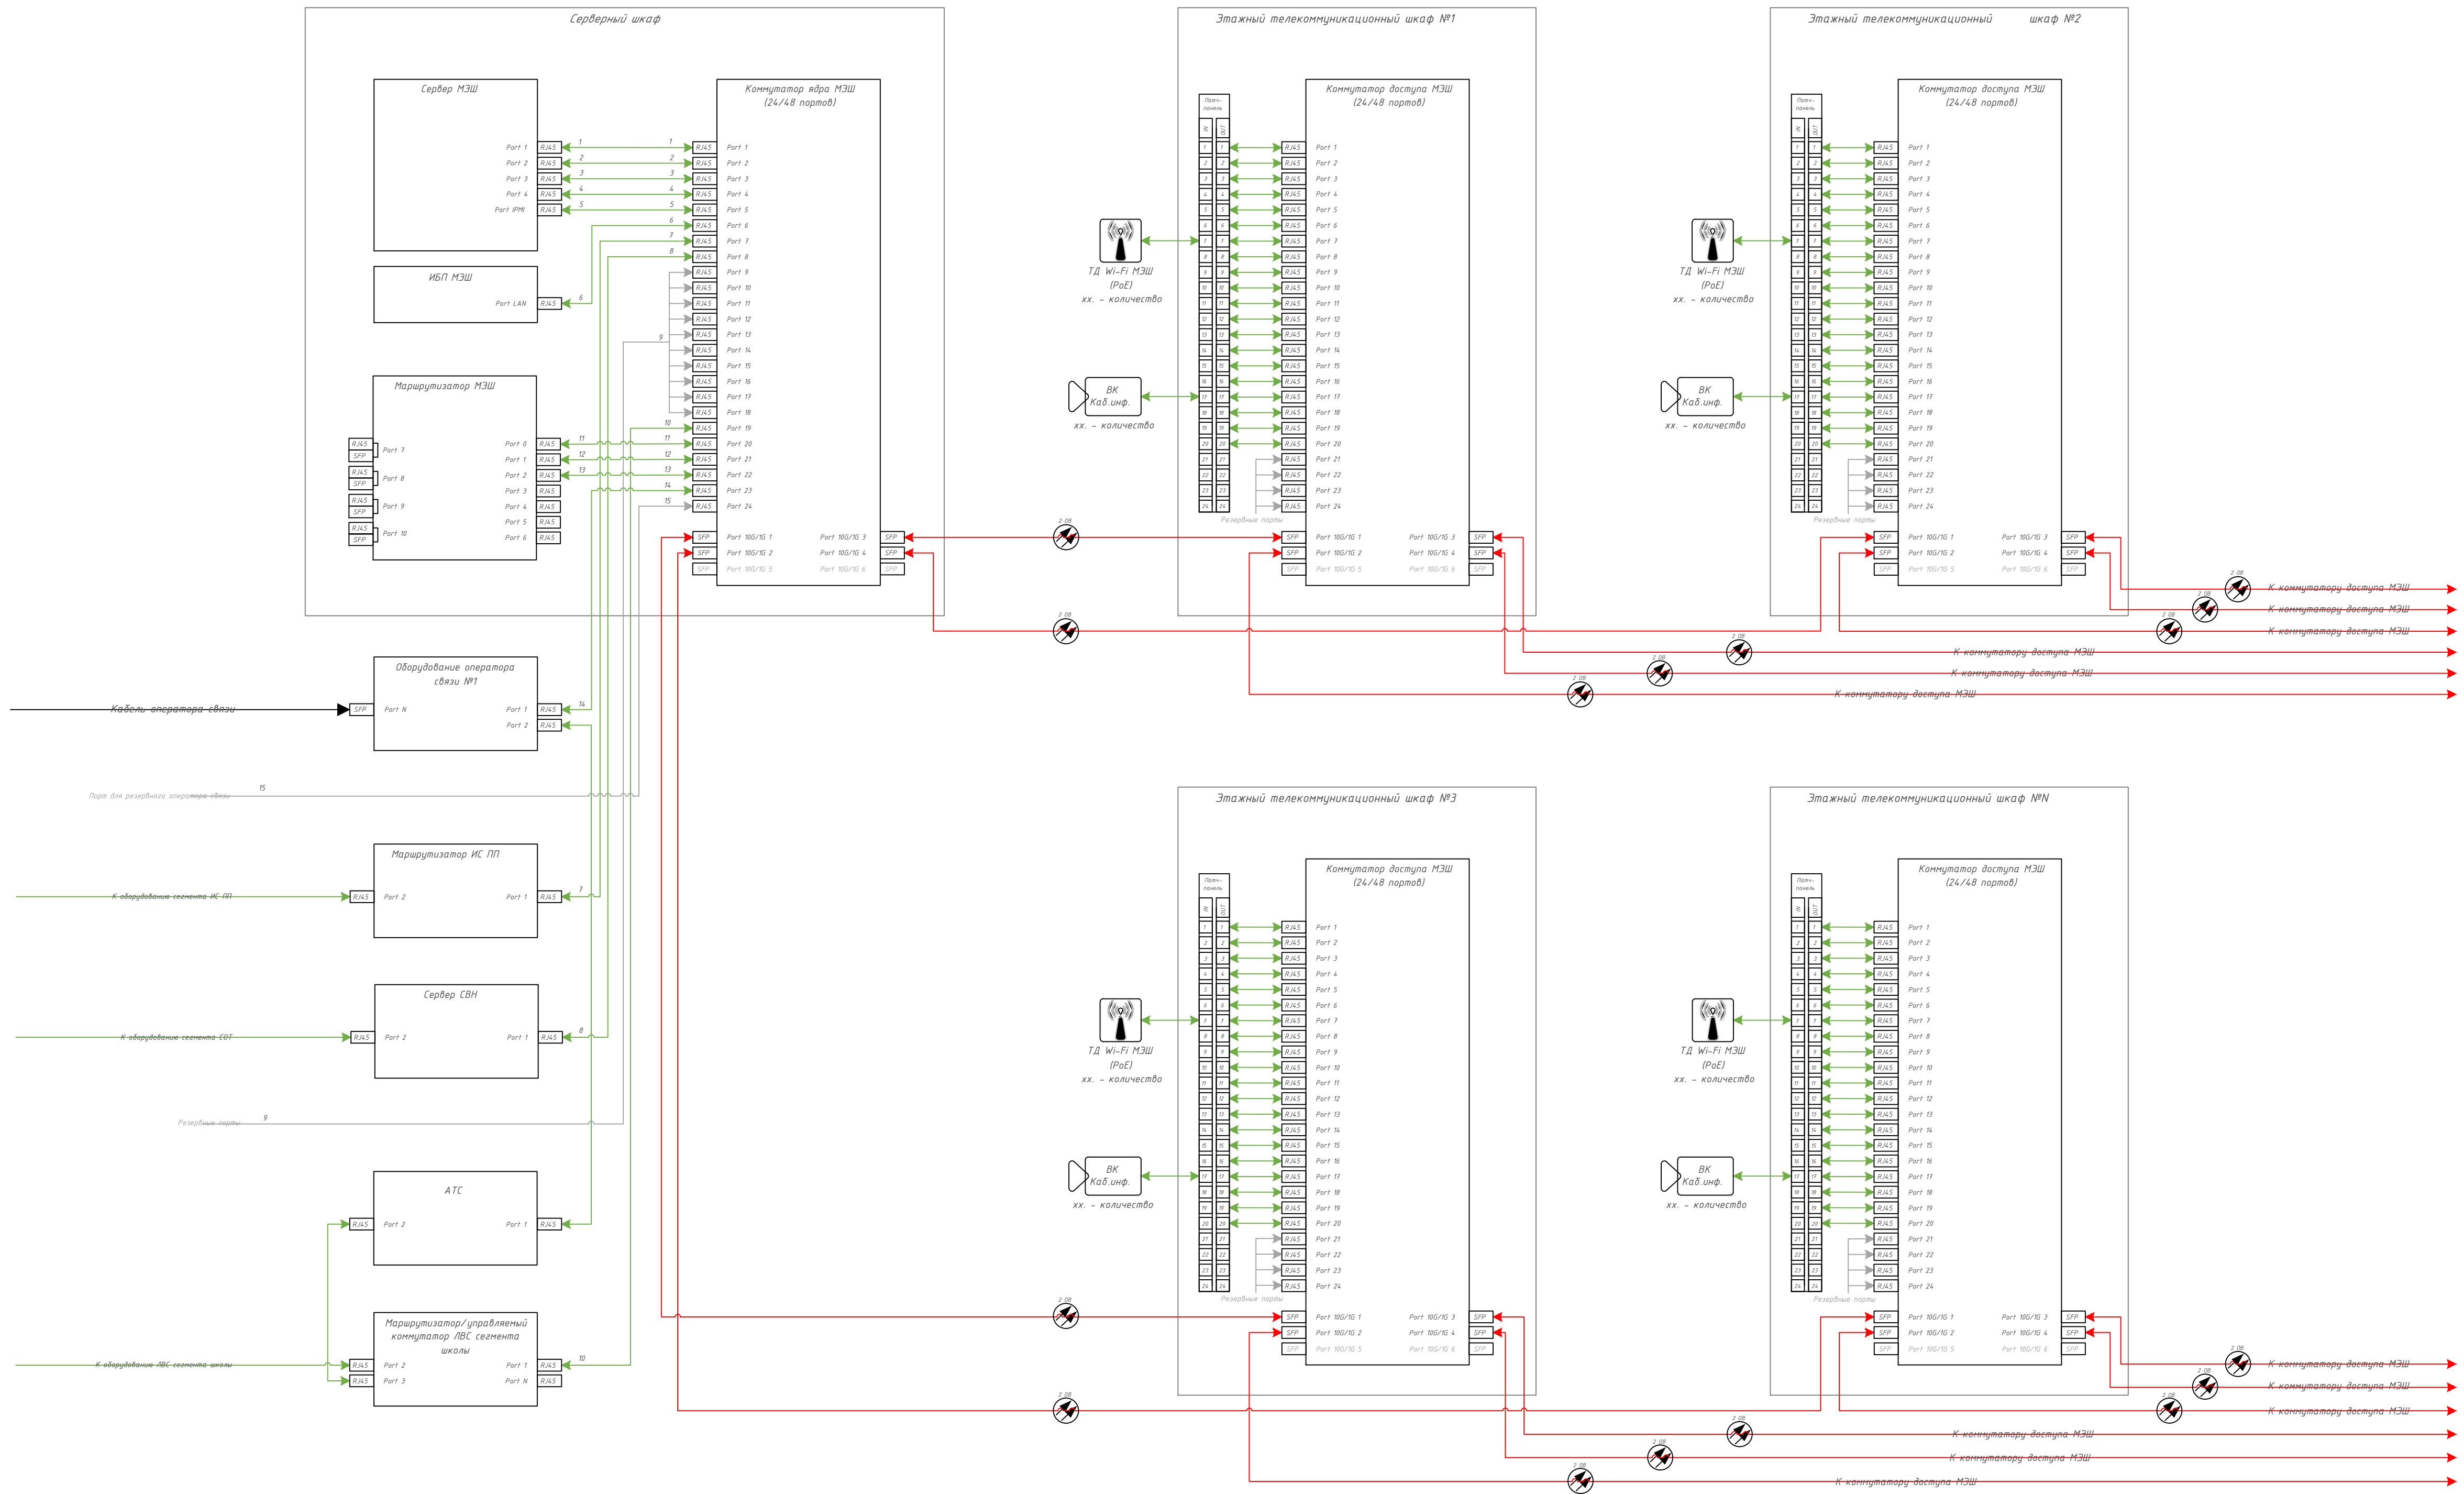

Согласовано
Взвешено
Подпись и дата
инициалы

					696/П-24-АНО-Р-СОТ				
					Капитальный ремонт Государственного Бюджетного Общественного Учреждения города Москвы «Школа № 1262 «Сокольники» по адресу: г. Москва, ул. Барболина, д. 1, корп. 1				
Изм.	Кол.уч	Лист	Индок	Подпись	Дата	Система охранного телевидения	Страница	Лист	Листов
Разработал	Конев					р	11		
Проверил	Гулько					Схема подключения			
Н. контр.	Гулько								

Согласовано:			
Взам. инв. №			
Подпись и дата			
Инв. №подл.			

Поз.	Наименование и техническая характеристика	Тип, марка, обозначение документа, опросного листа	Код продукции	Поставщик	Ед. изме-рения	Кол.	Масса 1 ед., кг	Примечание
1.	Раздел: Система охранного телевидения (COT)							
2.	Подраздел: Оборудование							
3.	IP-камера TRASSIR	TR-D3181IR3 v7 (2.8 мм)		TRASSIR	шт.	81		
4.	IP-камера TRASSIR	TR-D2181IR5 v7 (2.8 мм)		TRASSIR	шт.	23		
5.	RVi-2NCD2279	RVi-2NCD2279		RVI	шт.	4		Для кабинета ин-форматики
6.	Нейросетевой IP-видеорегистратор TRASSIR	NeuroStation 9800R/128		TRASSIR	шт.	1		
7.	Жесткий диск 24TB	WD240PURP		Western Digital	шт.	8		
8.	Модуль интеграции TRASSIR ЕЦХД(для передачи видеоданных в ЕЦХД, без ограничения срока действия)	TRASSIR ЕЦХД		TRASSIR	шт.	1		
9.	АРМ оператора	ПК iRU Game 520B5G TWR [2061477]		IRU	шт.	1		
10.	Модуль грозозащиты	NAG-1P		Beward	шт.	21		
11.	Устройства грозозащиты	RVi-1NSP20-24GP			шт.	2		
12.	Блок розеток	БР 16-008		ЦМО	шт.	1		
13.	Монитор 27”	M2701/2K(PN:TFT)		Бештай	шт.	3		
14.	Материалы							
15.	Монтажная коробка	TR-JB303		TRASSIR	шт	81		
16.	Монтажная коробка	TR-JB306		TRASSIR	шт	23		

						465/П-25-АНО-Р-COT.CO			
Изм.	Кол.у	Лист	№ док	Подпись	Дата	Спецификация	Стадия	Лист	Листов
Разработал		Коняев					Р	1	2
Проверил		Гулько							
Н.контр.		Гулько							
							 ООО "ПРОЕКТ +"		