

109548, г. Москва, Муниципальный Округ Печатники, ул. Шоссейная, д. 19, к. 1,  
кв.117 e-mail [PROEKTplus-work@yandex.ru](mailto:PROEKTplus-work@yandex.ru)

Свидетельство № СРО- П-110-009723217107-0532

СОГЛАСОВАНО:  
Главный инженер  
АО «МосводоканалСтройТрест»

\_\_\_\_\_ А.А. Вешкин

«\_\_» \_\_\_\_\_ 2026г

**Капитальный ремонт Государственного Бюджетного  
Общеобразовательного Учреждения города Москвы  
«Школа № 1282 «Сокольники»  
по адресу: г. Москва, ул. Барболина, д. 1, корп. 1  
1 этап**

**РАБОЧАЯ ДОКУМЕНТАЦИЯ**

Основной комплект рабочих чертежей

Система двухсторонней связи

**696/П-24-АНО-Р-СДС**

Генеральный директор

Главный инженер проекта




Н.А. Выходова

А.Н. Гулько

2026


|              |  |
|--------------|--|
| Инв. № подл. |  |
| Подп. И дата |  |
| Взам. инв. № |  |



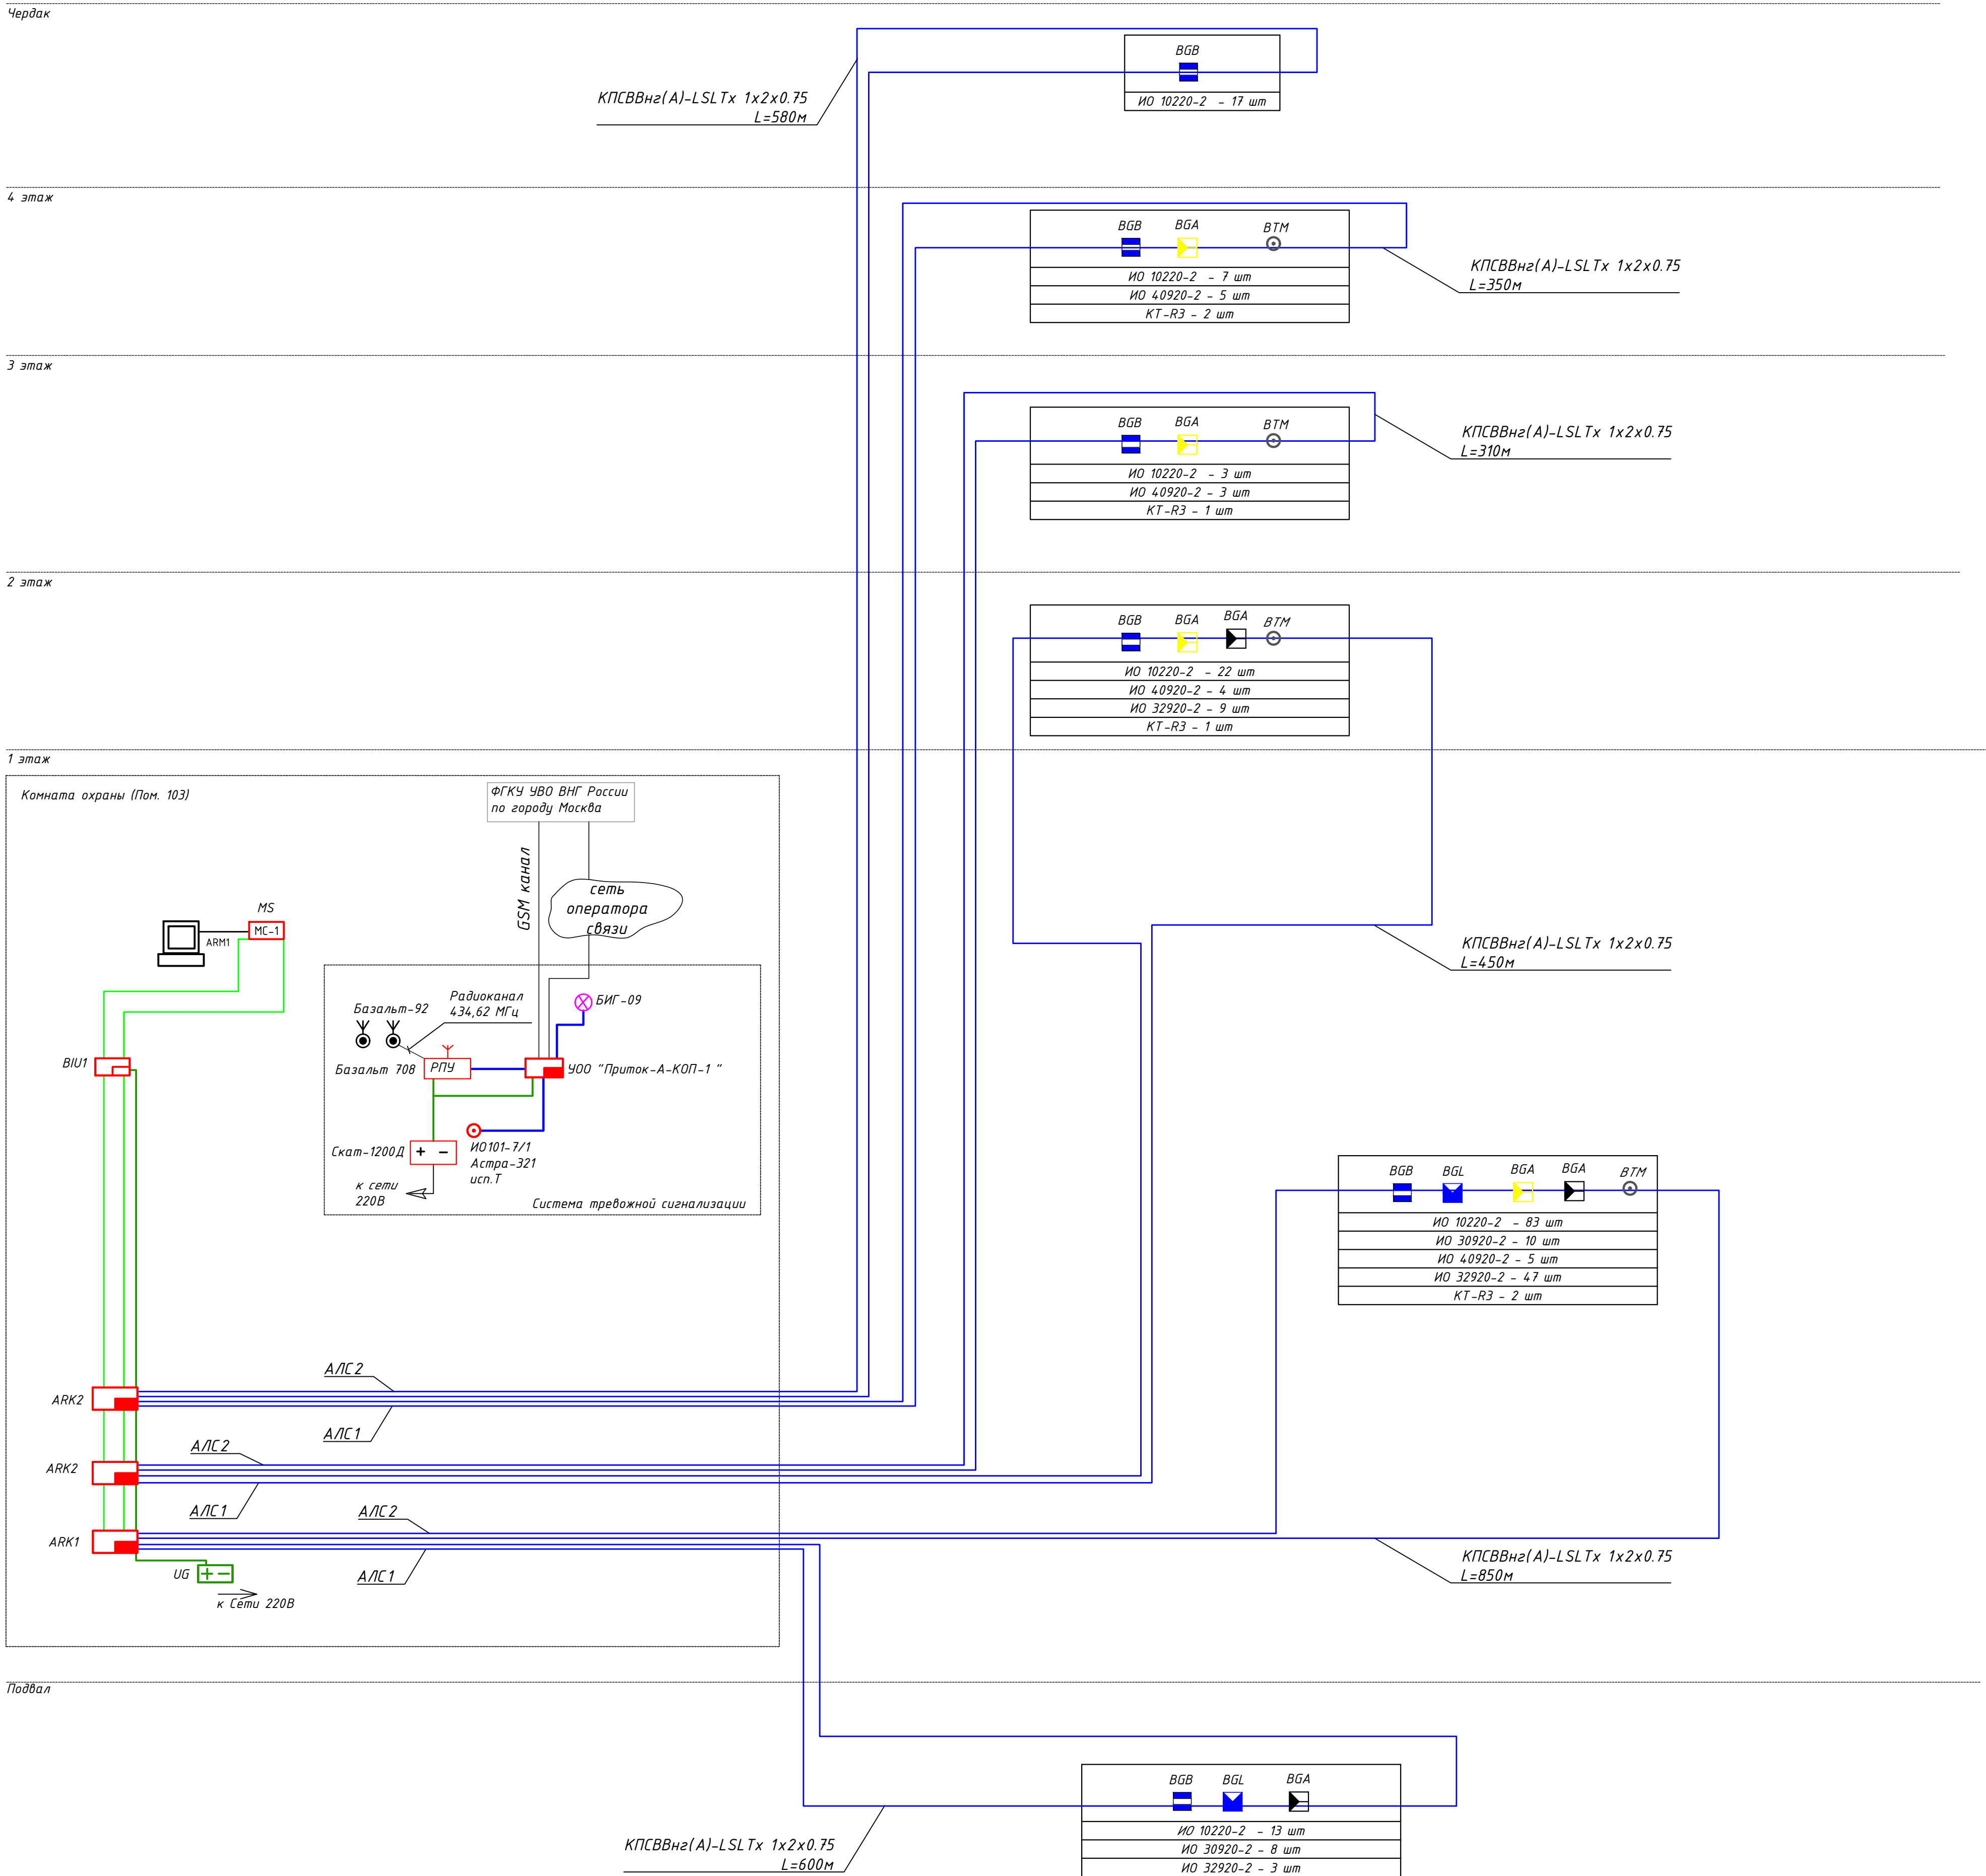

- Условные графические обозначения
- БГВ - извещатель магнито-контактный ИО 10220-2;
  - БГЛ - извещатель оптико-электронный поверхностный ИО 30920-2;
  - БГА - извещатель звуковой ИО 32920-2;
  - БГА - извещатель объемный оптико-электронный ИО 40920-2;
  - АРК - прибор приемно-контрольный ППКП "РЗ-Рубеж-20П";
  - ВНУ - блок индикации и управления "РЗ-Рубеж-БИУ";
  - УГ - источник вторичного электропитания ИВЭПР 12/5 2x40 БР;
  - МС - модуль сопряжения МС-1;
  - ВТМ - кнопка тревожная КТ-РЗ;
  - линия сигнализации (кабель КПСВВнз(А)-LSLTx 1x2x0.75);
  - линия питания (кабель ВВГнг(А)-LSLTx 2x1.5);
  - кабель У/ИТР (У/ИТР нз(А)-LSLTx 4x2x0.52);
  - слаботочная шахта
  - Устройство оконечное объектовое Приток-А-КОП-01;
  - РПУ - Радиоприемное устройство Базальт-708;
  - Б - Брелок радиоканальный Базальт-92;
  - ⊙ - Извещатель охранной ручной точечный электроконтактный Астра-321 Т
  - ⊗ - Индикатор прибытия наряда БИГ-09

|            |         |      |      |         |       |   |        |      |
|------------|---------|------|------|---------|-------|---|--------|------|
|            |         |      |      |         |       | 696/П-25-АНО-Р-СОТС                                                                                                  |        |      |
|            |         |      |      |         |       | Капитальный ремонт Государственного Бюджетного Общеобразовательного Учреждения города Москвы «Школа №1283(Сколково)» |        |      |
|            |         |      |      |         |       | по адресу: г. Москва, ул. Барболина, д. 1, корп. 1                                                                   |        |      |
| Изм.       | Кол.уч. | Лист | Инд. | Подпись | Дата  | Система охранной сигнализации                                                                                        | Стадия | Лист |
| Разработал | Конев   |      |      |         | 10.24 |   | Р      | 2    |
| Проверил   | Гулько  |      |      |         | 10.24 |   |        | 11   |
| Н. контр.  | Гулько  |      |      |         | 10.24 |   |        |      |
|            |         |      |      |         |       | Принципиальная схема системы ОС                                                                                      |        |      |

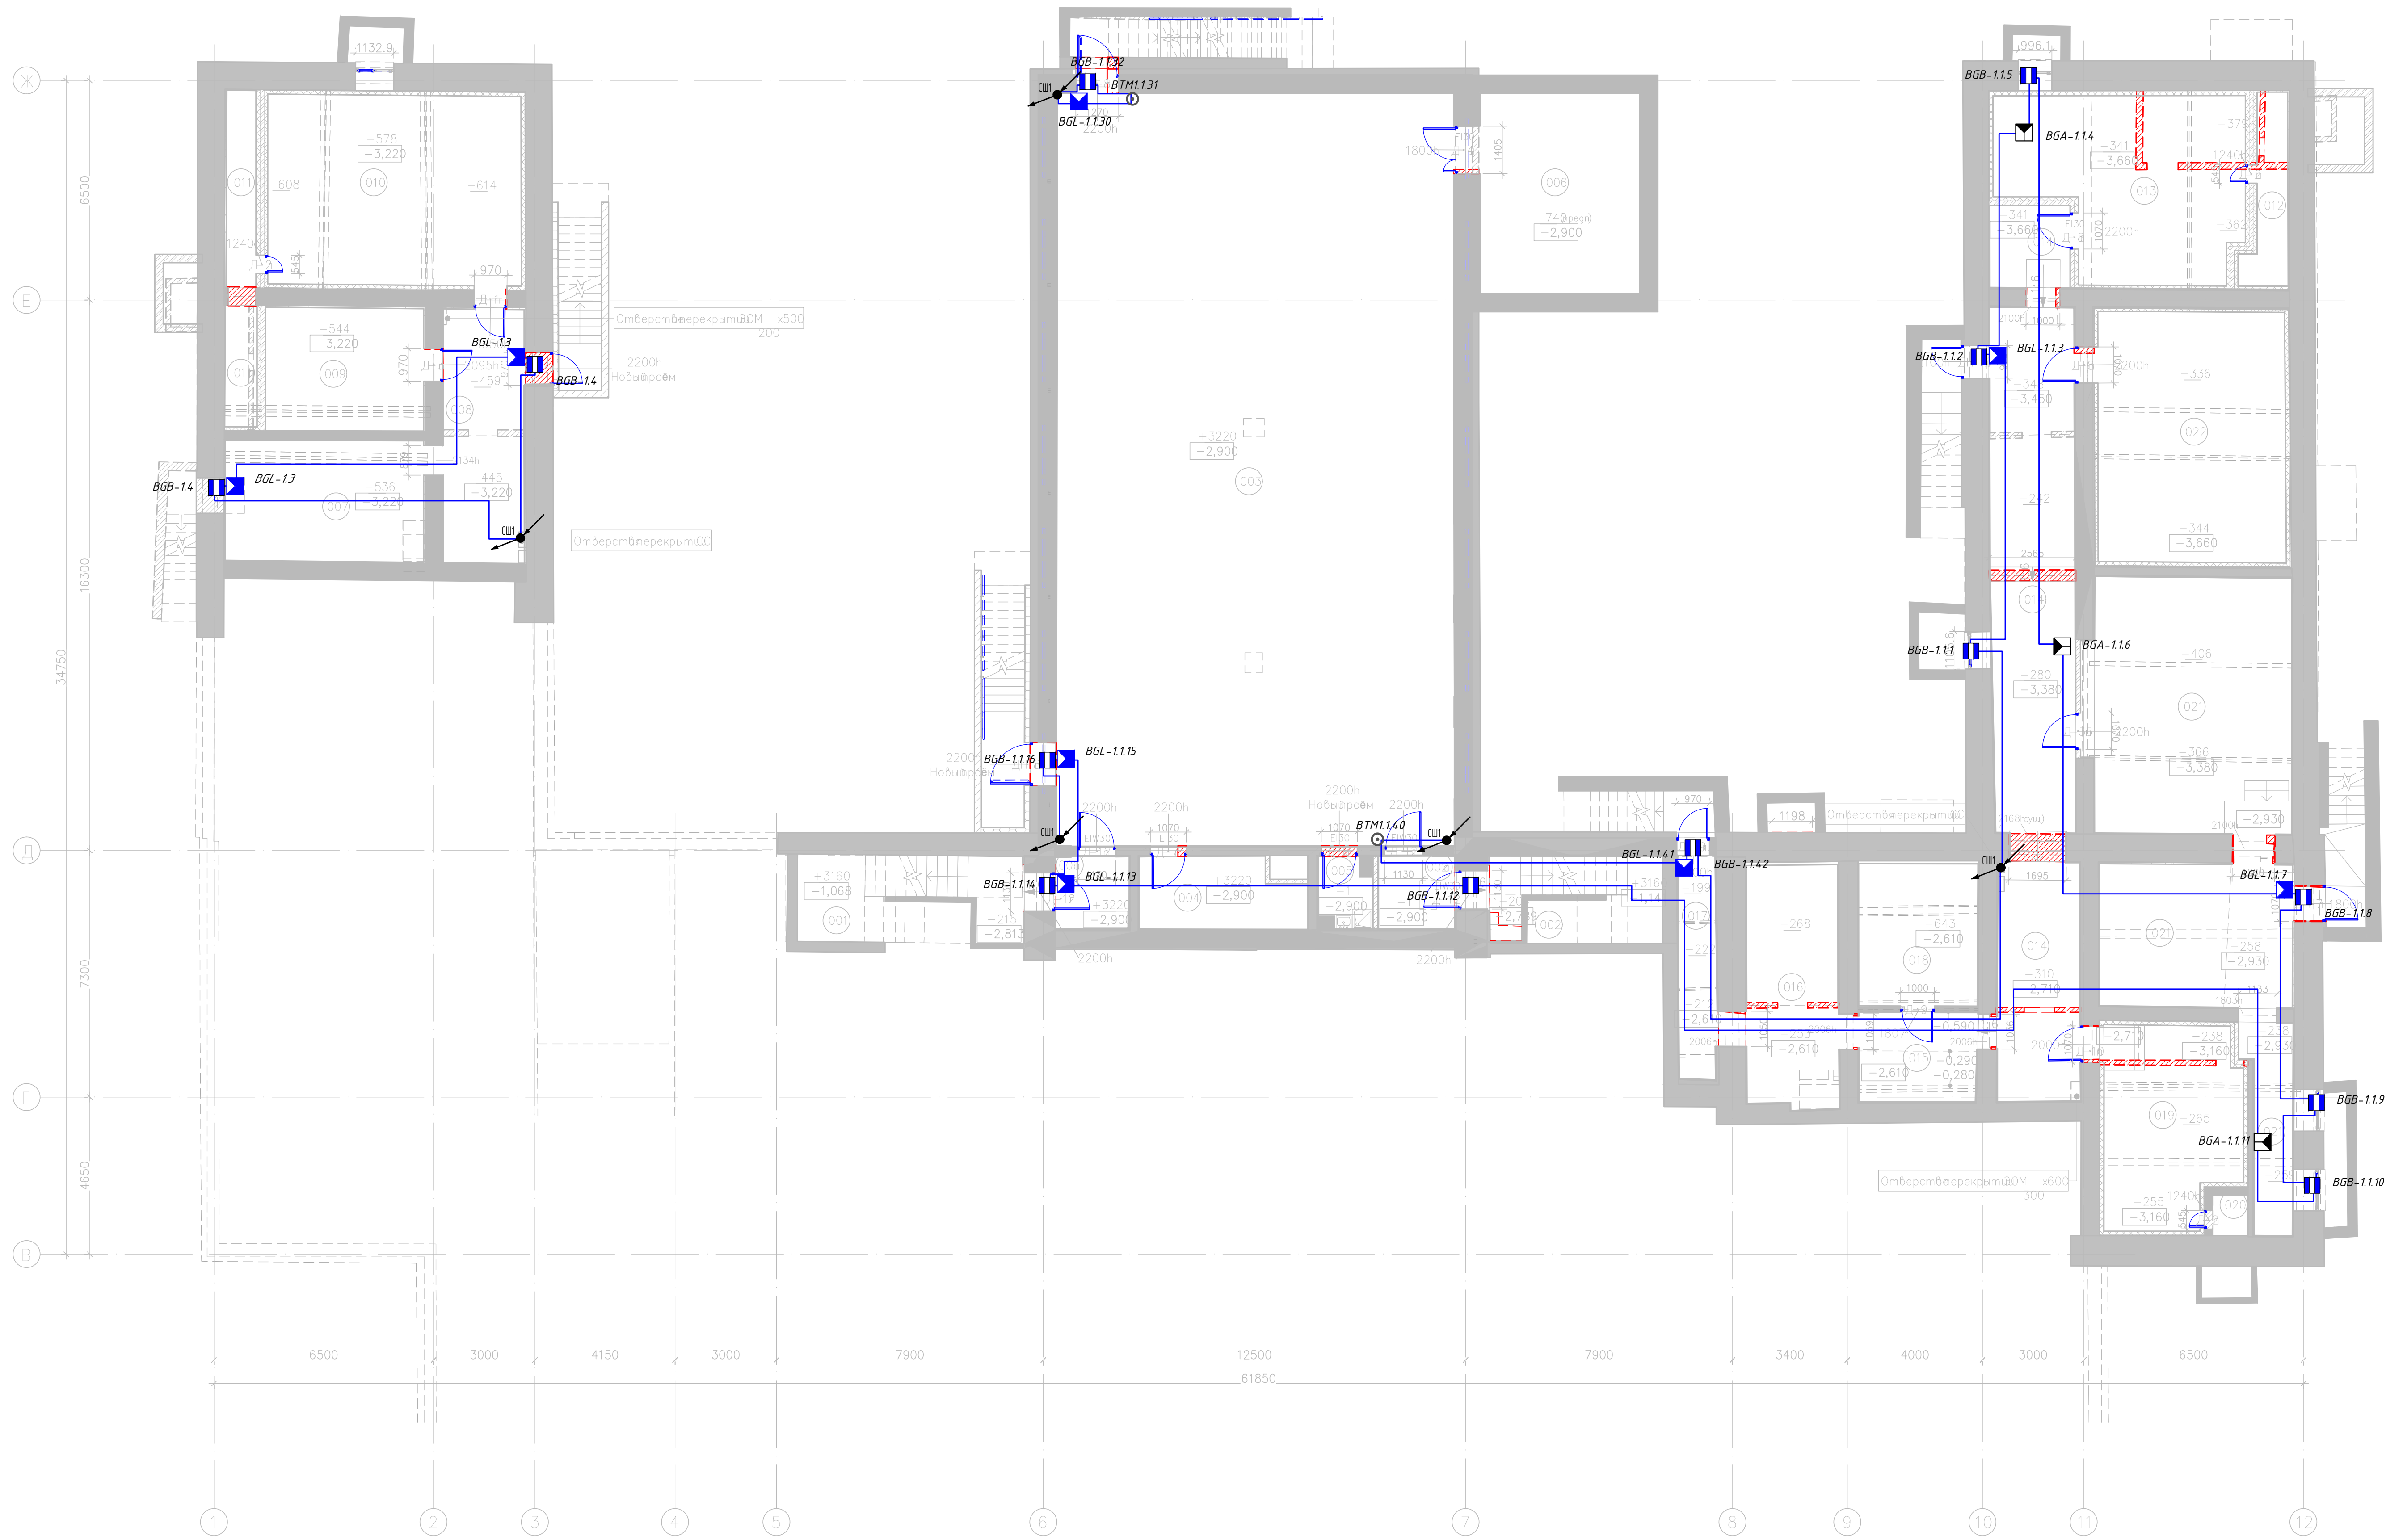


| Экспликация помещений |                        |             |                |
|-----------------------|------------------------|-------------|----------------|
| Номер помещения       | Наименование           | Площадь, м² | Кат. помещения |
| 001                   | Техническая лестница   | 13,7        |                |
| 001a                  | Тамбур-шлюз 1-го этажа | 4,8         |                |
| 002                   | Техническая лестница   | 9,8         |                |
| 002a                  | Тамбур-шлюз 1-го этажа | 4,9         |                |
| 003                   | Спортивный зал         | 262,5       |                |
| 004                   | Спортивная             | 9,9         | B3             |
| 005                   | Видеонаблюдение        | 3,5         |                |
| 006                   | Охранная               | 28,0        | B3             |
| 007                   | Коридор                | 21,0        |                |
| 008                   | Коридор                | 17,9        |                |
| 009                   | Кладовая               | 17,1        | B3             |
| 010                   | Венткамера             | 42,1        | B4             |
| 011                   | Формкамера             | 8,9         | B4             |
| 012                   | Формкамера             | 5,7         | B4             |
| 013                   | Венткамера             | 34,6        | B4             |
| 014                   | Коридор                | 63,3        |                |
| 015                   | Коридор                | 9,8         |                |
| 016                   | Коридор                | 20,0        |                |
| 017                   | Коридор                | 8,3         |                |
| 018                   | Насосная               | 14,8        | B4             |
| 019                   | Венткамера             | 22,8        | B4             |
| 020                   | Формкамера             | 1,2         | B4             |
| 021                   | ИТП                    | 77,8        | Д              |
| 022                   | Венткамера             | 41,1        | B4             |
| Итого:                |                        | 743,4       |                |

- Условные графические обозначения
- БВВ - извещатель магнито-контактный ИО 10220-2;
  - БВЛ - извещатель оптико-электронный поверхностный ИО 30920-2;
  - БВБ - извещатель звуковой ИО 32920-2;
  - БВБ - извещатель объемный оптико-электронный ИО 40920-2;
  - БВБ - кнопка тревожная КТ-БЗ;
  - БВБ - кнопка тревожная Аспра-321;
  - БВБ - линия сигнализации (кабель КТСВВне(А)-LSLTx 1x2x0,75);
  - БВБ - складочная шпала

|                               |        |        |        |   |       |                                                      |
|-------------------------------|--------|--------|--------|---|-------|------------------------------------------------------|
| 696/П-25-АНО-Р-СОТС           |        |        |        | Капитальный ремонт Государственного бюджетного общеобразовательного учреждения города Москвы школы №1782 (Специализированная школа №1782) |       |                                                      |
| Имя                           | Кол-во | Лист   | Итого  | Подпись   | Дата  | по адресу: г. Москва, ул. Барбарисово, д. 1, корп. 1 |
| Выбор                         | Выбор  | Выбор  | Выбор  | Выбор   | 05.24 | Система охранной сигнализации                        |
| И. Имя                        | И. Имя | И. Имя | И. Имя | И. Имя   | 05.24 | План расположения оборудования ОС в подвале          |
| Формат А0 альбомная (84x1189) |        |        |        | Лист 11   |       |                                                      |



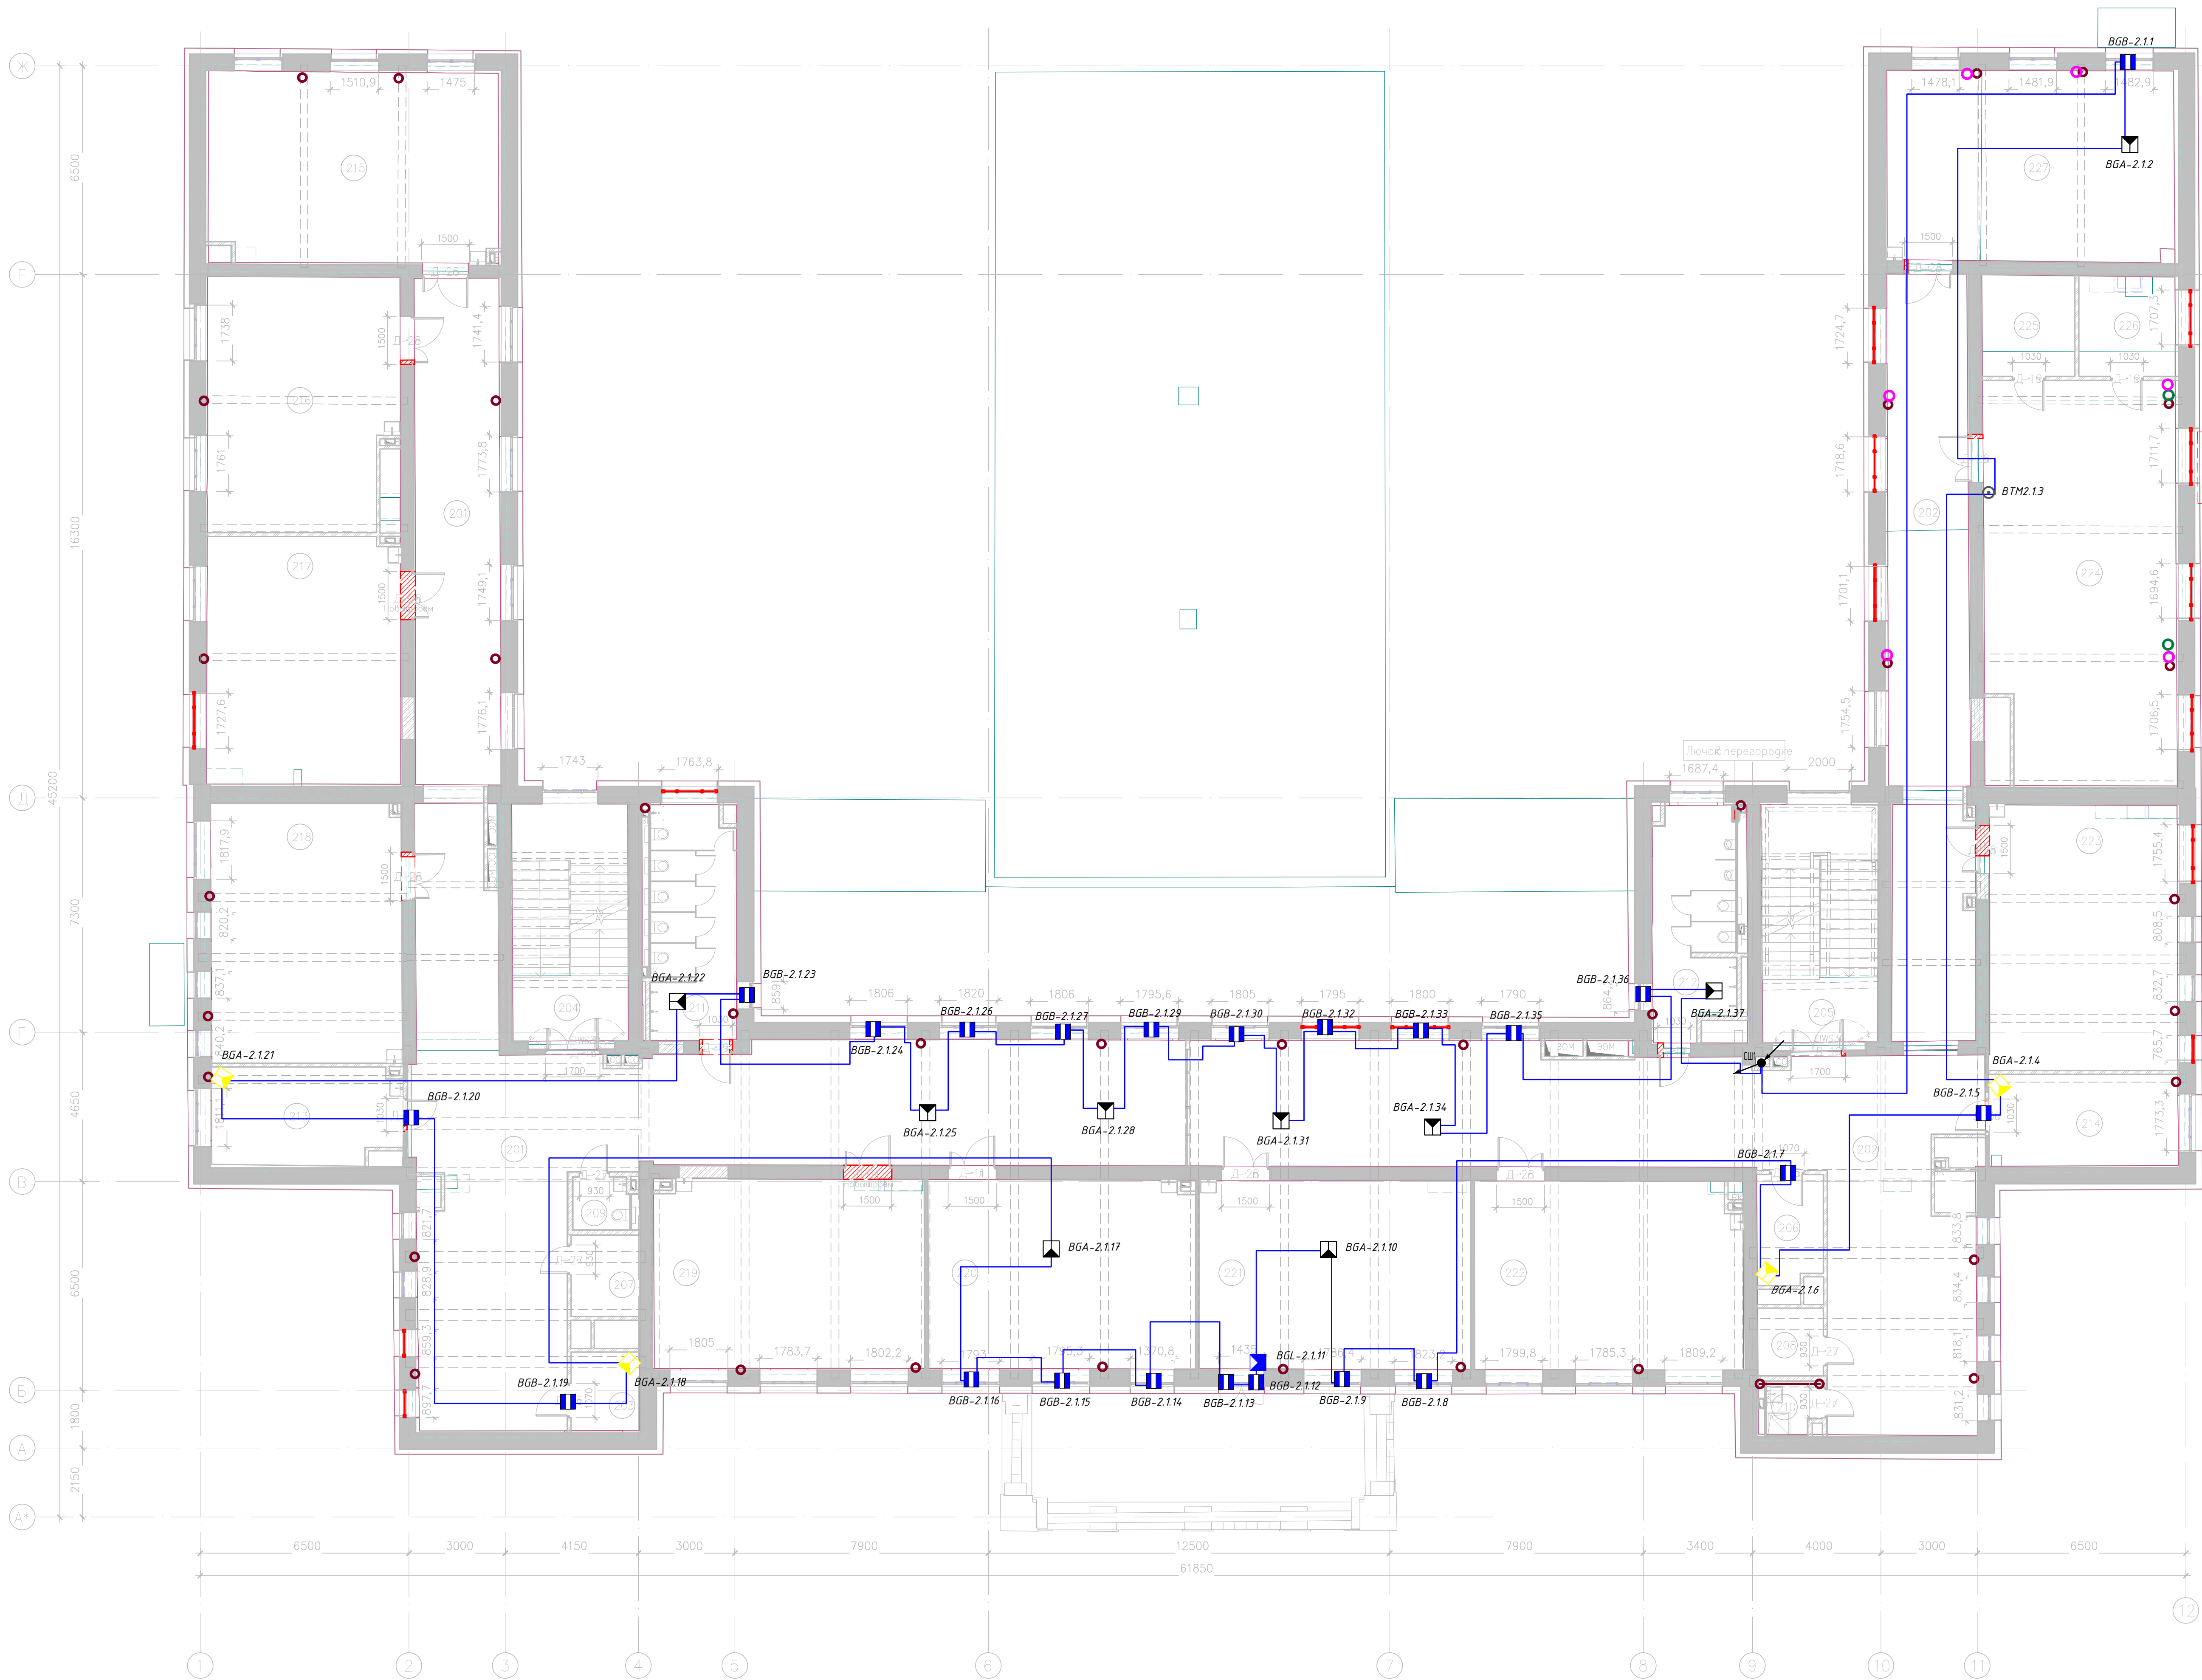


Экспликация помещений 2-го

| Номер помещения | ЭПОЖО<br>Наименование           | Площадь, м² | Кот. помещения |
|-----------------|---------------------------------|-------------|----------------|
| 201             | Коридор с декоративной отделкой | 190,6       |                |
| 202             | Коридор с декоративной отделкой | 188,2       |                |
| 203             | Помещение                       | 5,5         | Б4             |
| 204             | Лестничная клетка (Тип 1)       | 27,4        |                |
| 205             | Лестничная клетка (Тип 1)       | 27,7        |                |
| 206             | Помещение                       | 6,9         | Б4             |
| 207             | Помещение                       | 5,4         | Б4             |
| 208             | Помещение                       | 4,3         | Б4             |
| 209             | Помещение                       | 2,8         |                |
| 210             | Помещение                       | 2,6         | Б4             |
| 211             | Уборная для персонала           | 19,4        |                |
| 212             | Уборная для персонала           | 18,1        |                |
| 213             | Уборная для персонала           | 17,5        |                |
| 214             | Уборная для персонала           | 17,0        |                |
| 215             | Уборная для персонала           | 53,5        |                |
| 216             | Уборная для персонала           | 45,8        |                |
| 217             | Уборная для персонала           | 46,5        |                |
| 218             | Уборная для персонала           | 48,0        |                |
| 219             | Уборная для персонала           | 49,5        |                |
| 220             | Уборная для персонала           | 48,9        |                |
| 221             | Уборная для персонала           | 49,8        |                |
| 222             | Уборная для персонала           | 48,7        |                |
| 223             | Уборная для персонала           | 49,0        |                |
| 224             | Уборная для персонала           | 73,7        |                |
| 225             | Уборная для персонала           | 9,1         |                |
| 226             | Уборная для персонала           | 9,5         |                |
| 227             | Уборная для персонала           | 53,6        |                |
| Итого:          |                                 | 1119,0      |                |

ПРИМЕЧАНИЕ:  
В соответствии с требованиями пожарной безопасности, в помещениях, где хранятся горючие материалы, должны быть установлены пожарные извещатели.

- Условные графические обозначения
- BGB - извещатель магнито-контактный ИО 10220-2;
  - BGA - извещатель оптико-электронный поверхностный ИО 30920-2;
  - BGA - извещатель звуковой ИО 32920-2;
  - BGA - извещатель объемный оптико-электронный ИО 40920-2;
  - BTM - кнопка тревожная КТ-Р3;
  - линия сигнализации (кабель КТКВВнг(A)-LSLY 1x2x0,75);
  - слаботочная шина

|                                                      |        |      |       |      |  |
|------------------------------------------------------|--------|------|-------|------|--|
| 696/П-25-АН0-Р-СОТС                                  |        |      |       |      |  |
| Капитальный ремонт Государственного Бюджетного       |        |      |       |      |  |
| Общественного учреждения города Москвы «Школа №1282» |        |      |       |      |  |
| по адресу: г. Москва, ул. Барбарисов, д. 1, корп. 1  |        |      |       |      |  |
| Имя                                                  | В.И.И. | Лист | №     | Дата |  |
| Результат                                            | Имя    | №    | 10.24 |      |  |
| Проверка                                             | Имя    | №    | 10.24 |      |  |
| И.И.И.                                               | Имя    | №    | 10.24 |      |  |
| И.И.И.                                               | Имя    | №    | 10.24 |      |  |
| Система охранной сигнализации                        |        |      |       |      |  |
| План расположения оборудования ОС на 2 этаже         |        |      |       |      |  |
| Формат А4, альбомная (Б4,х1189)                      |        |      |       |      |  |

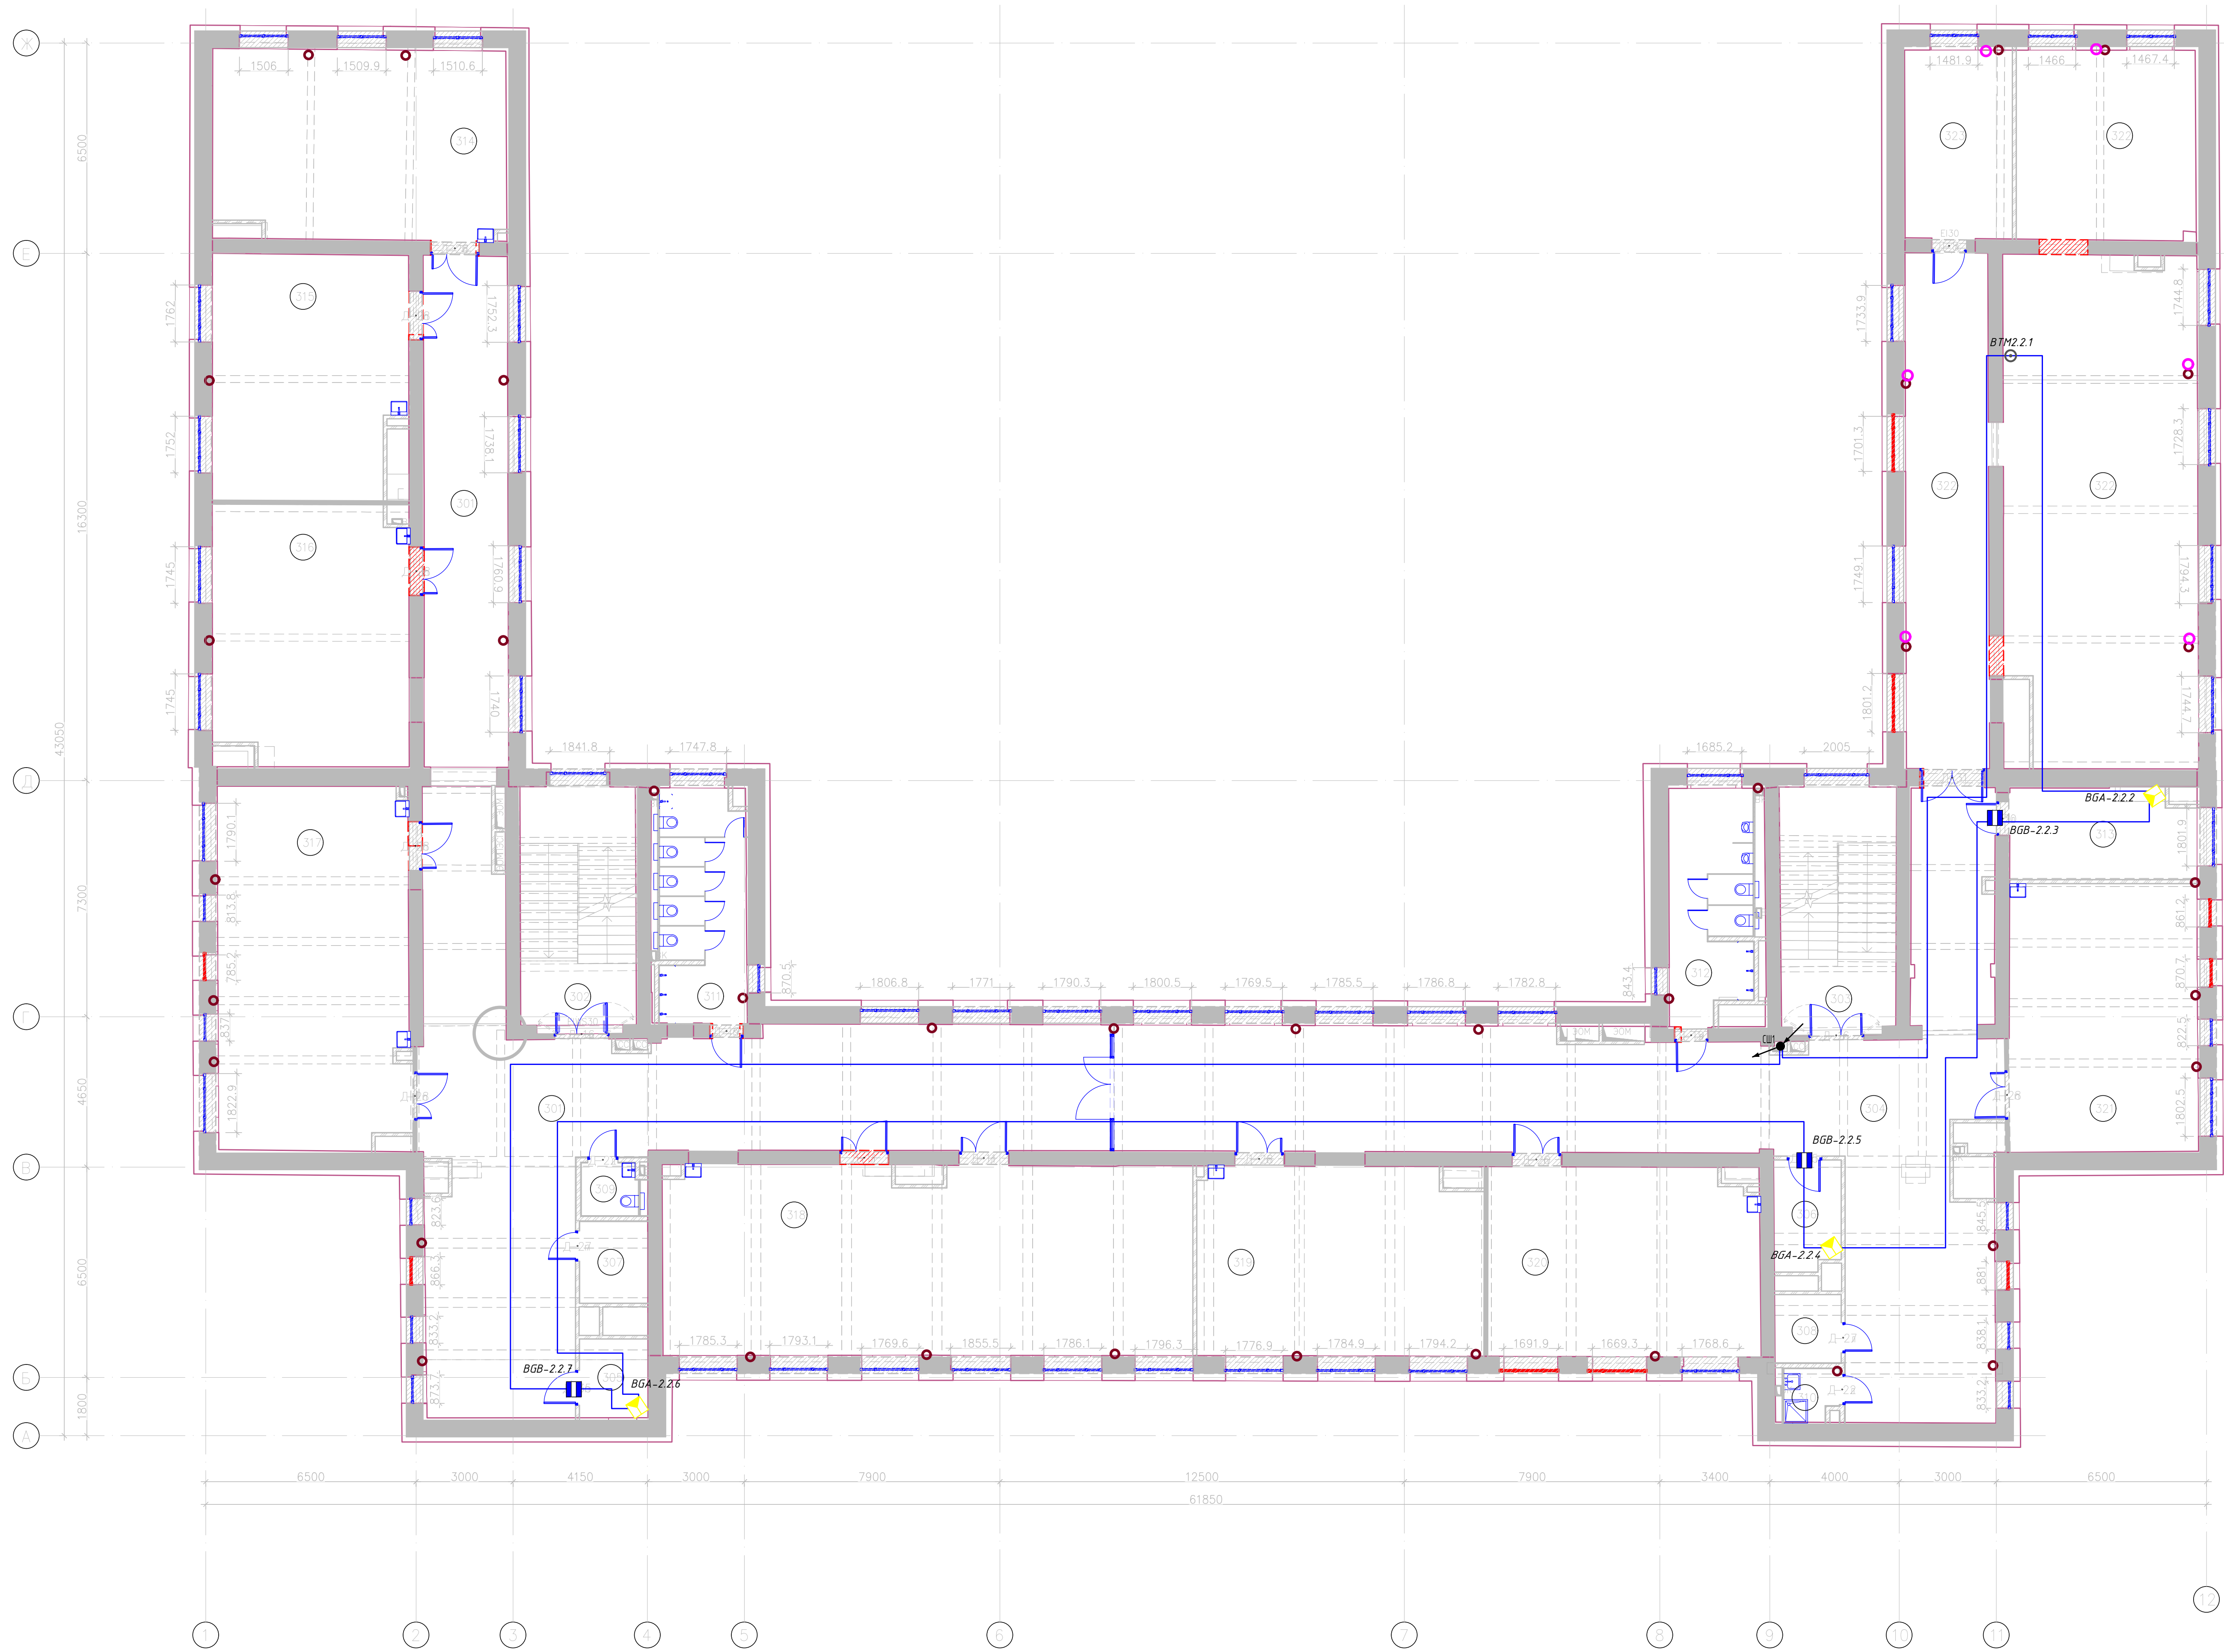


Экспликация помещений 3-го

| Номер помещения | Этаж | Наименование                                                           | Площадь, м² | Кот. помеще-ния |
|-----------------|------|------------------------------------------------------------------------|-------------|-----------------|
| 301             | 3    | Коридор с рекреацией                                                   | 178,8       |                 |
| 302             | 3    | Лестничная клетка (Тип 10)                                             | 27,1        |                 |
| 303             | 3    | Лестничная клетка (Тип 10)                                             | 27,4        |                 |
| 304             | 3    | Коридор с рекреацией                                                   | 156,6       |                 |
| 305             | 3    | Помещение                                                              | 5,3         | B4              |
| 306             | 3    | Помещение                                                              | 6,9         | B4              |
| 307             | 3    | Помещение                                                              | 5,3         | B4              |
| 308             | 3    | Помещение                                                              | 4,3         | B4              |
| 309             | 3    | Туалет для персонала                                                   | 2,8         |                 |
| 310             | 3    | УИ                                                                     | 2,7         | B4              |
| 311             | 3    | Уборная для персонала                                                  | 19,0        |                 |
| 312             | 3    | Уборная для персонала                                                  | 18,3        |                 |
| 313             | 3    | Коридор с рекреацией для индивидуальных занятий, 6 м.ч. с компьютерами | 15,9        |                 |
| 314             | 3    | Переводом кабинет                                                      | 53,0        |                 |
| 315             | 3    | Учебный кабинет                                                        | 44,6        |                 |
| 316             | 3    | Учебный кабинет                                                        | 48,0        |                 |
| 317             | 3    | Кабинет для преподавателя иностранного языка                           | 66,1        |                 |
| 318             | 3    | Помещение для проведения занятий с преподавателем                      | 95,4        |                 |
| 319             | 3    | Учебный кабинет                                                        | 51,0        |                 |
| 320             | 3    | Учебный кабинет                                                        | 48,5        |                 |
| 321             | 3    | Учебный кабинет                                                        | 48,5        |                 |
| 322             | 3    | Информационный центр с зонами для индивидуальных и групповых занятий   | 169,7       |                 |
| 323             | 3    | Информационный центр с зонами для индивидуальных и групповых занятий   | 19,7        | B3              |
| ИТОГО:          |      | всего книг                                                             | 1115,0      |                 |

ПРИМЕЧАНИЕ  
Высоты проема люка в перекрытии указаны в скобках, мм  
исключительно для информационных целей в 2200  
Спецификация дана в Внутреннем документе

- Условные графические обозначения
- BGV - извещатель магнито-контактный ИО 10220-2;
  - BGA - извещатель оптико-электронный поверхностный ИО 30920-2;
  - BGA - извещатель звуковой ИО 32920-2;
  - BGA - извещатель объемный оптико-электронный ИО 40920-2;
  - BTM - кнопка тревожная КТ-РЗ;
  - BTM - кнопка тревожная Астра-371;
  - линия сигнализации (кабель КТСВне(А)-LSLTx 1x2x0.75);
  - слаботочная шина


|   |           |      |     |         |       |
|---|-----------|------|-----|---------|-------|
| 696/П-25-АН0-Р-СОТС   |           |      |     |         |       |
| Капитальный ремонт Государственного бюджетного общеобразовательного учреждения школы №1282 «Сокольники» по адресу: г. Москва, ул. Барбариха, д. 1, корп. 1 |           |      |     |         |       |
| Имя   | В.И.И.    | Лист | №10 | Подпись | Дата  |
| Выборка   | Григорьев | Лист | №10 | Дата    | 10.24 |
| И.И.И.   | Григорьев | Лист | №10 | Дата    | 10.24 |
| Система охранной сигнализации   |           |      |     | Р       | 6     |
| План расположения оборудования ОС на 3 этаже   |           |      |     | Л       | 11    |
| Формат А0 альбомная (84х1189)   |           |      |     |         |       |

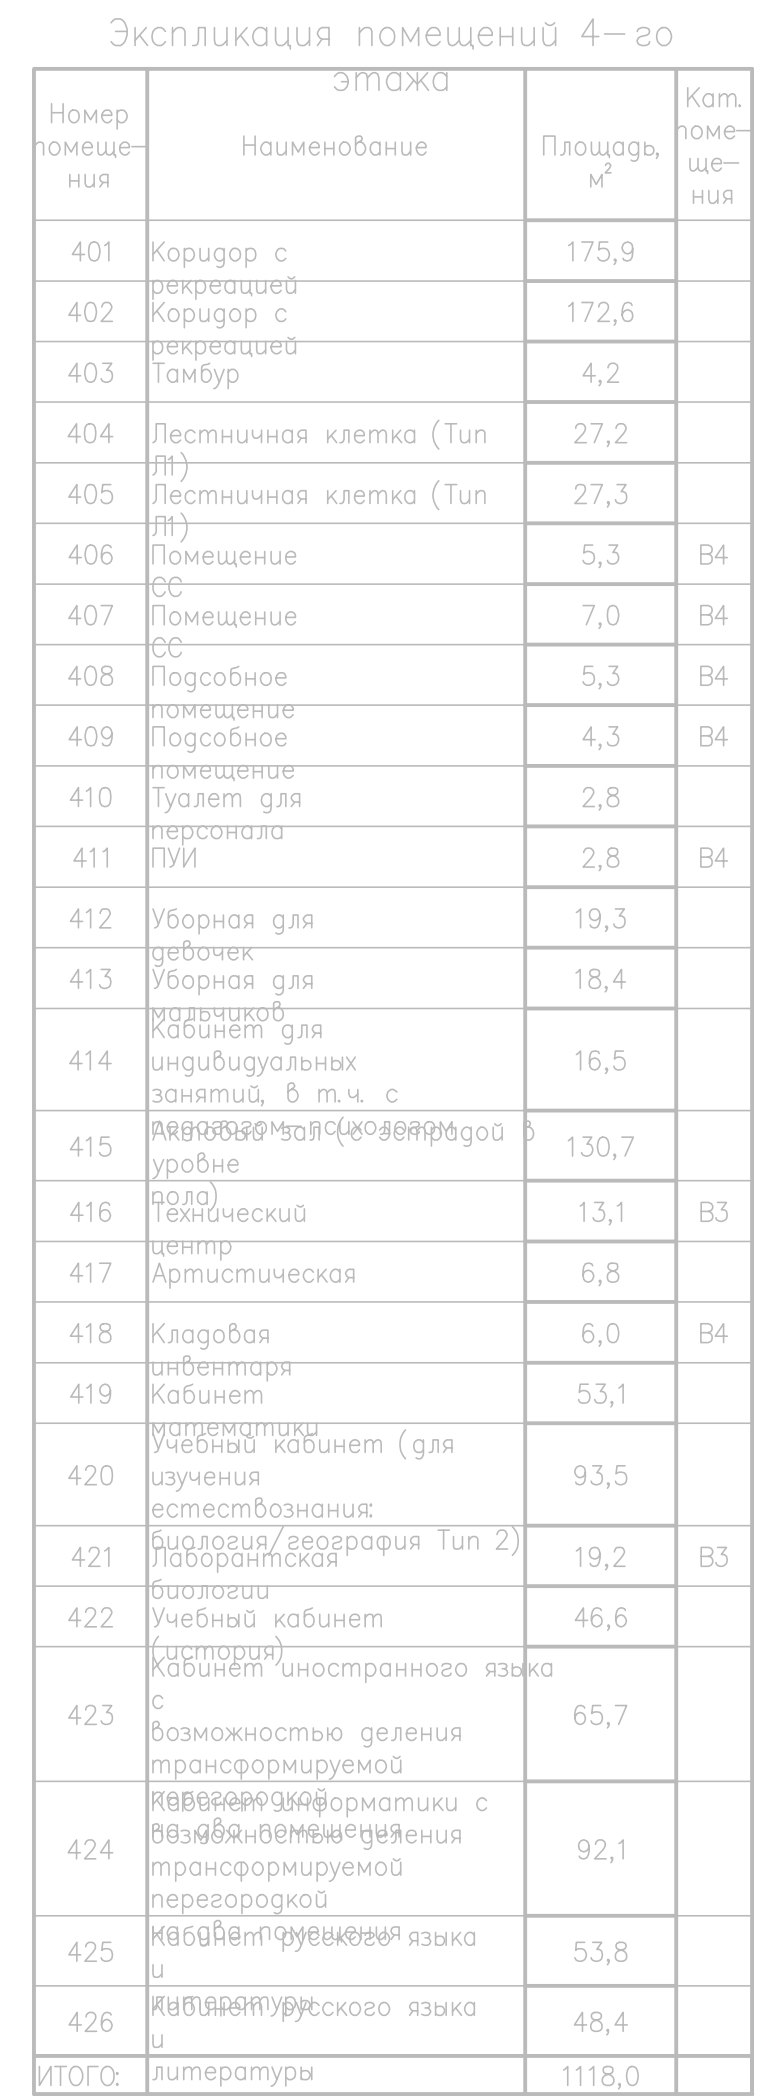

Символы электрических обозначений

|                                                                                       |     |                                                           |
|---------------------------------------------------------------------------------------|-----|-----------------------------------------------------------|
|  | BGB | - извещатель магнитно-контактный ИО 10220-2;              |
|  | ВВГ | - извещатель оптико-электронный поверхностный ИО 30920-2; |
|  | BGA | - извещатель звуковой ИО 32920-2;                         |
|  | ВГА | - извещатель объемный оптико-электронный ИО 40920-2;      |
|  | OTM | - кнопка тревожная КТ-Р3;                                 |
|  | OTM | - кнопка тревожная Астра-321;                             |
|  |     | - линия сигнализации (кабель КПСВН(А)-LSLTm 1х2х0,75);    |
|  |     | - слаботочная шхота                                       |


[illegible]

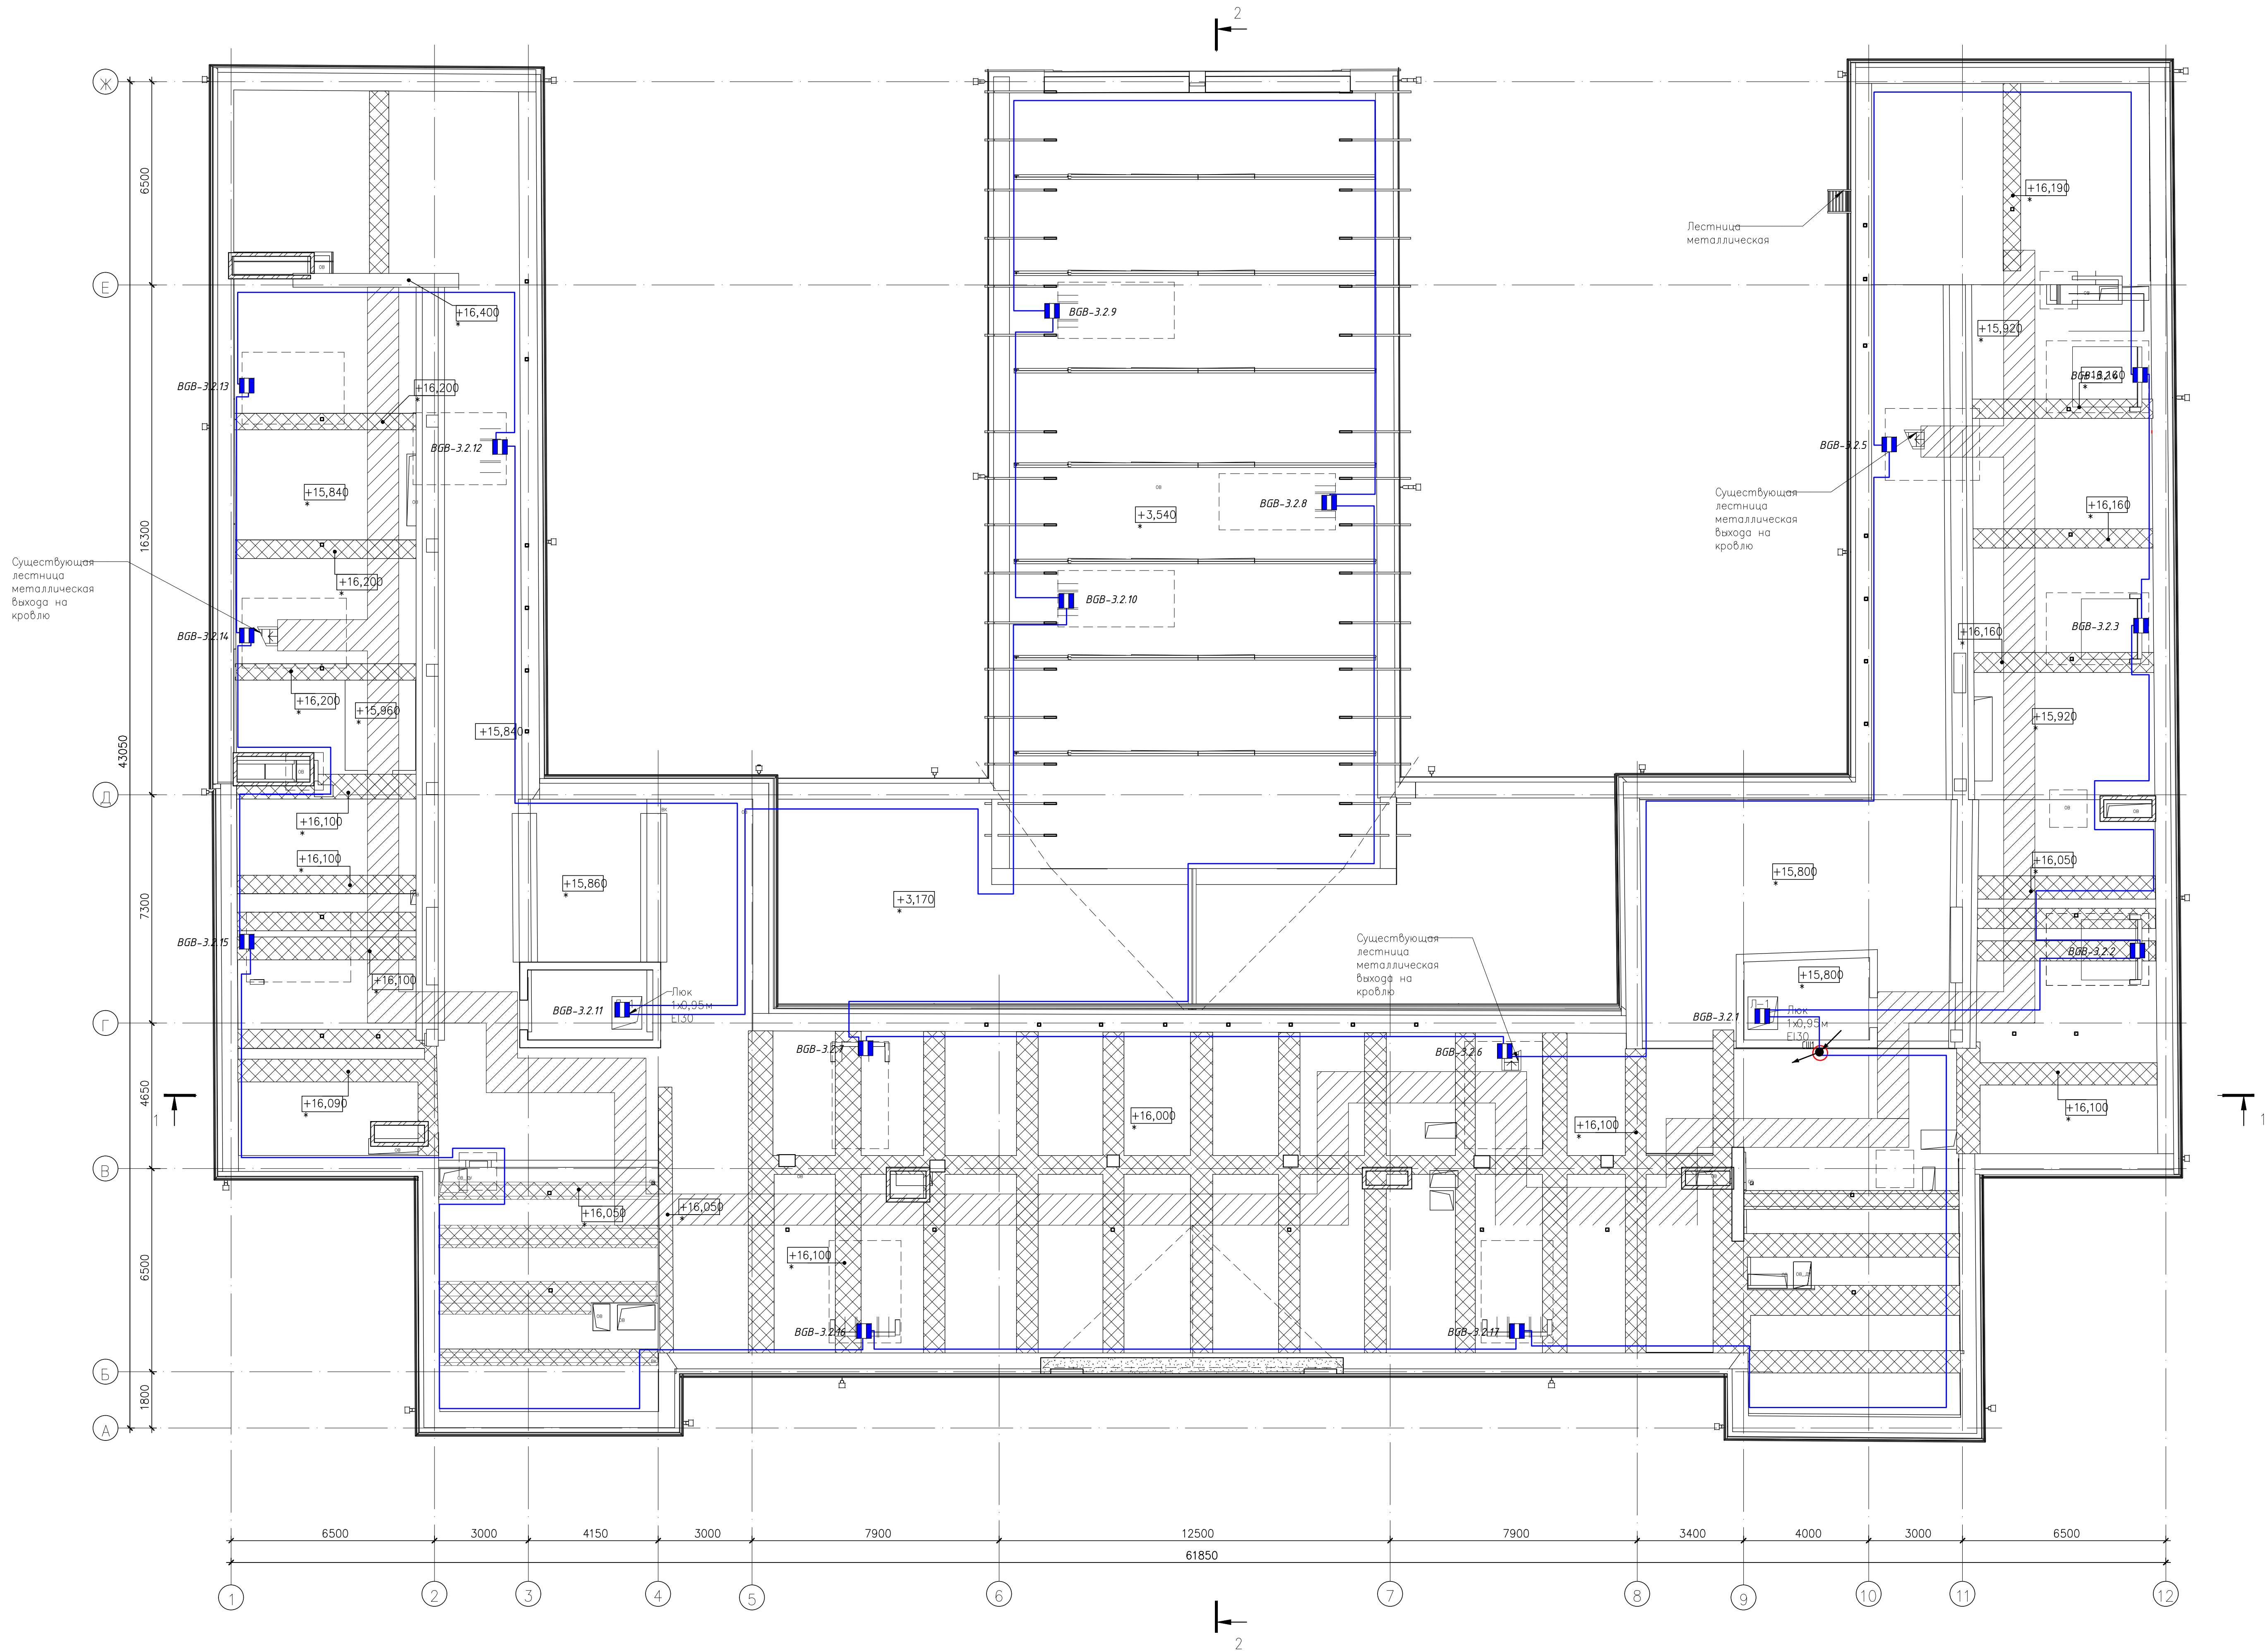

- Условные графические обозначения
- БВВ - извещатель пассивно-адресный ИО 10220-2;
  - БВЛ - извещатель оптико-электронный поверхностный 30920-2;
  - БВЗ - извещатель звуковой ИО 33920-2;
  - БВВ - извещатель адресный оптико-электронный ИО 40920-2;
  - БВМ - кнопка тревожная КТ-РЗ;
  - БВМ - кнопка тревожная Агара-321;
  - БВМ - линия сигнализации кабель КПСВВн(А)-LSLTx 1x2x0.75;
  - БВМ - слаботочная штепсельная розетка.

|             |           |           |       |   |       |          |        |
|-------------|-----------|-----------|-------|---|-------|----------|--------|
|             |           |           |       | 696/П-25-АН0-Р-СОТС                                                                                                  |       |          |        |
|             |           |           |       | Капитальный ремонт Государственного бюджетного общеобразовательного учреждения города Москвы «Школа №1282» (Сколько) |       |          |        |
|             |           |           |       | по адресу: г. Москва, ул. Барбарина, д. 1, корп. 1                                                                   |       |          |        |
| Масштаб     | 1:50      | Лист      | 11    | Подпись   | Дата  | Страница | Листов |
| Разработчик | Григорьев | Григорьев | 10.24 | 10.24   | 10.24 | Р        | 8      |
| И. номер    | Григорьев | Григорьев | 10.24 | 10.24   | 10.24 | Р        | 8      |
|             |           |           |       | План расположения оборудования ОС на чердаке                                                                         |       |          |        |
|             |           |           |       | Формат А4, альбомная (84x1189)                                                                                       |       |          |        |

|                |  |  |  |  |
|----------------|--|--|--|--|
| Согласовано    |  |  |  |  |
|                |  |  |  |  |
|                |  |  |  |  |
| Взам.инв.Н     |  |  |  |  |
|                |  |  |  |  |
|                |  |  |  |  |
| Подпись и дата |  |  |  |  |
|                |  |  |  |  |
|                |  |  |  |  |
| инв.Подл.      |  |  |  |  |
|                |  |  |  |  |
|                |  |  |  |  |

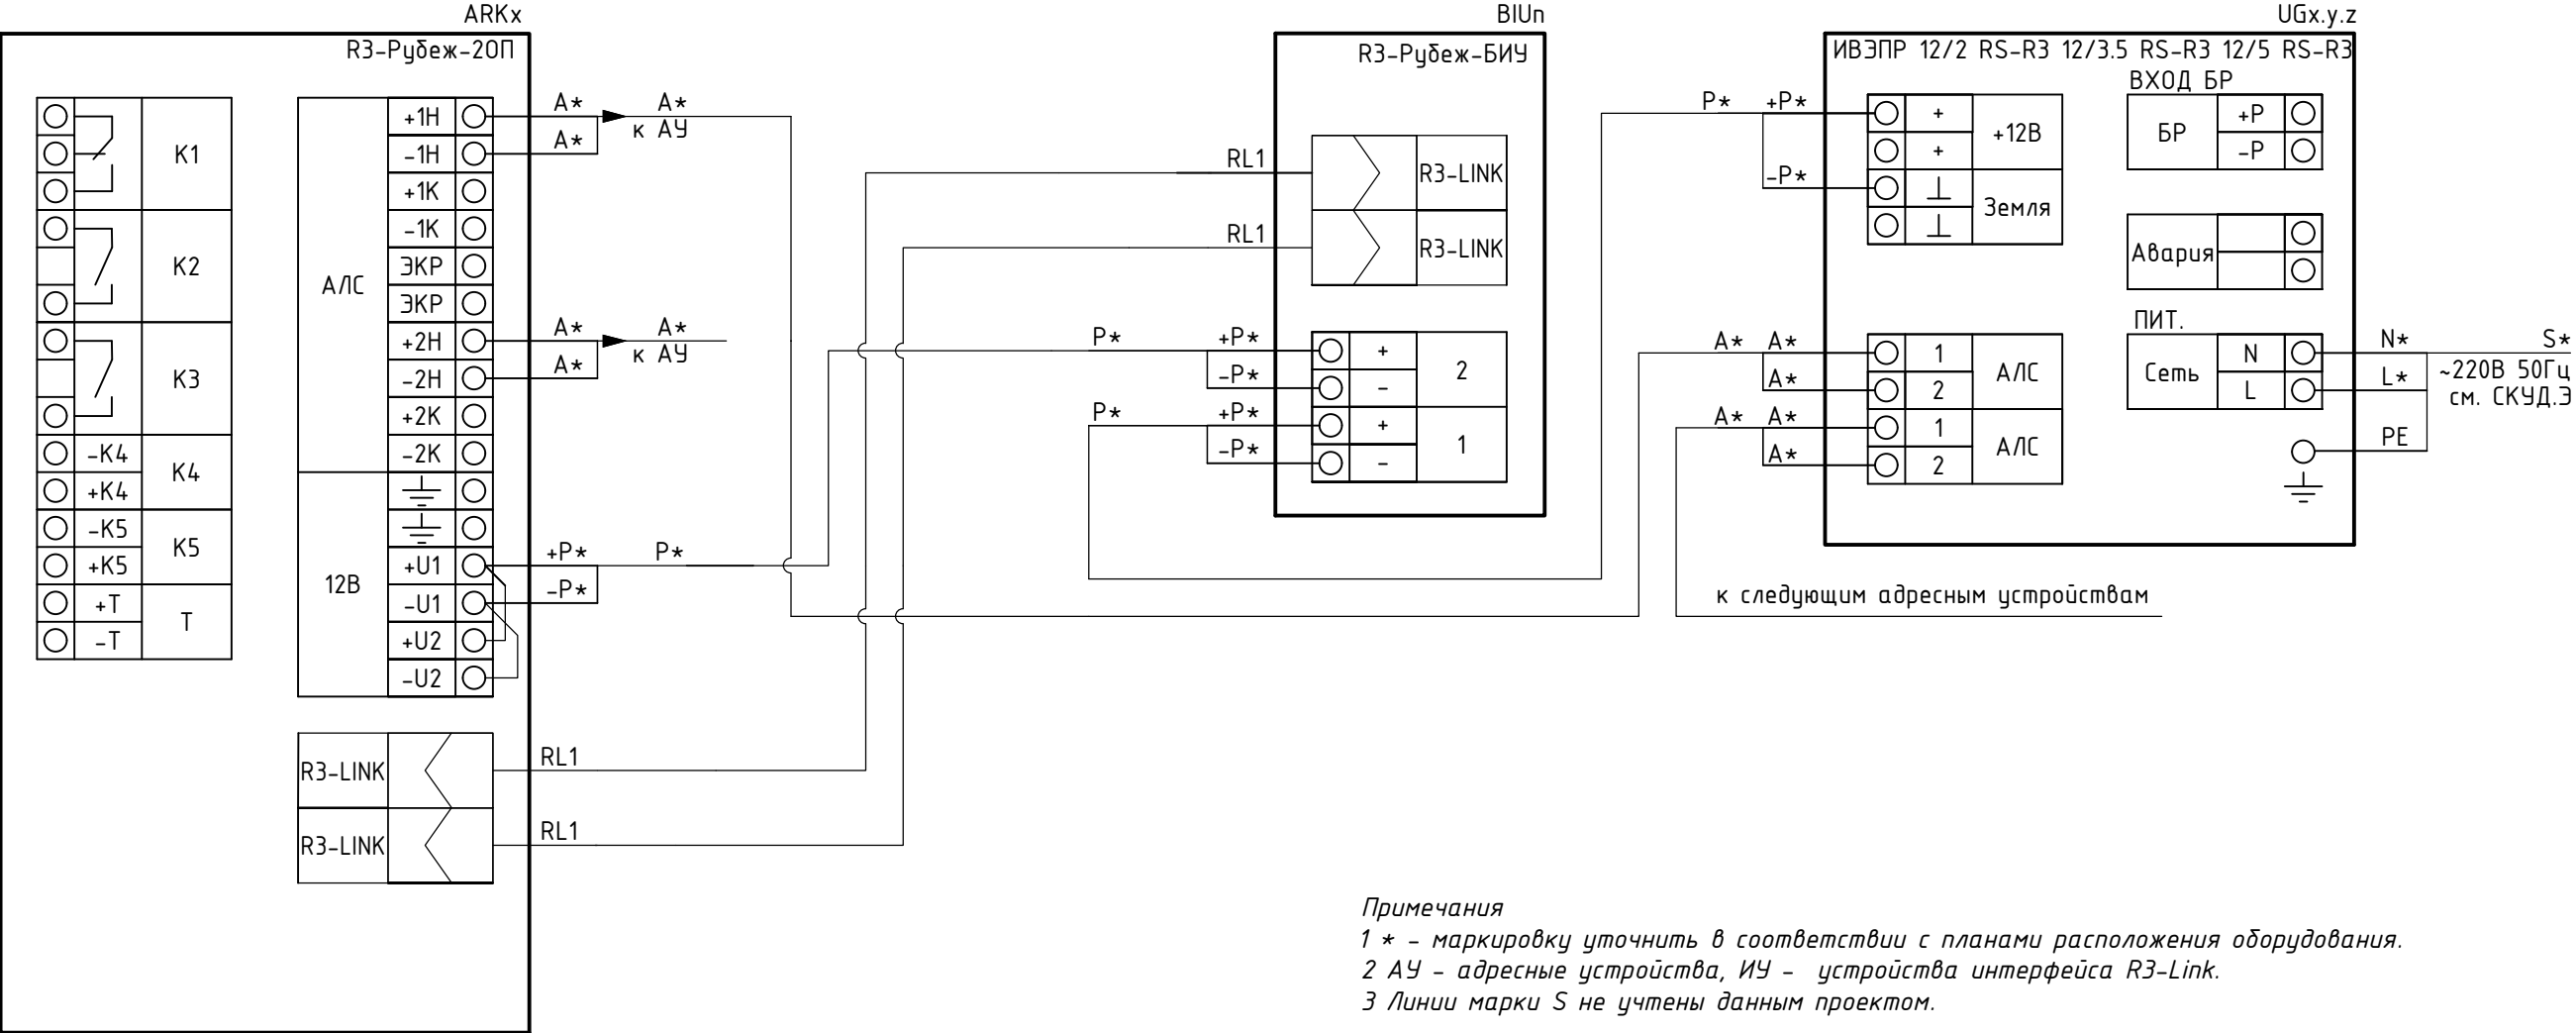

|            |           |      |      |                                                                                       |       |   |                                                                                       |      |        |
|------------|-----------|------|------|---------------------------------------------------------------------------------------|-------|---|---------------------------------------------------------------------------------------|------|--------|
|            |           |      |      |                                                                                       |       | 696/П-25-АНО-Р-СОТС   |                                                                                       |      |        |
|            |           |      |      |                                                                                       |       | Капитальный ремонт Государственного Бюджетного<br>Общеобразовательного Учреждения города Москвы «Школа<br>№1282«Сокольники»<br>по адресу: г. Москва, ул. Барболина, д. 1, корп. 1 |                                                                                       |      |        |
| Изм.       | Кол.уч    | Лист | Ндок | Подпись                                                                               | Дата  | Система охранной сигнализации   | Стадия                                                                                | Лист | Листов |
| Разработал | Кочнев    |      |      |  | 10.24 |   | Р                                                                                     | 9    | 11     |
| Проверил   | Григорьев |      |      |  | 10.24 |   |                                                                                       |      |        |
|            |           |      |      |                                                                                       |       | Схема подключения оборудования<br>системы ОС   |  |      |        |
| Инж.контр. | Пилько    |      |      |  | 10.24 |   |                                                                                       |      |        |

Диаграмма направленности

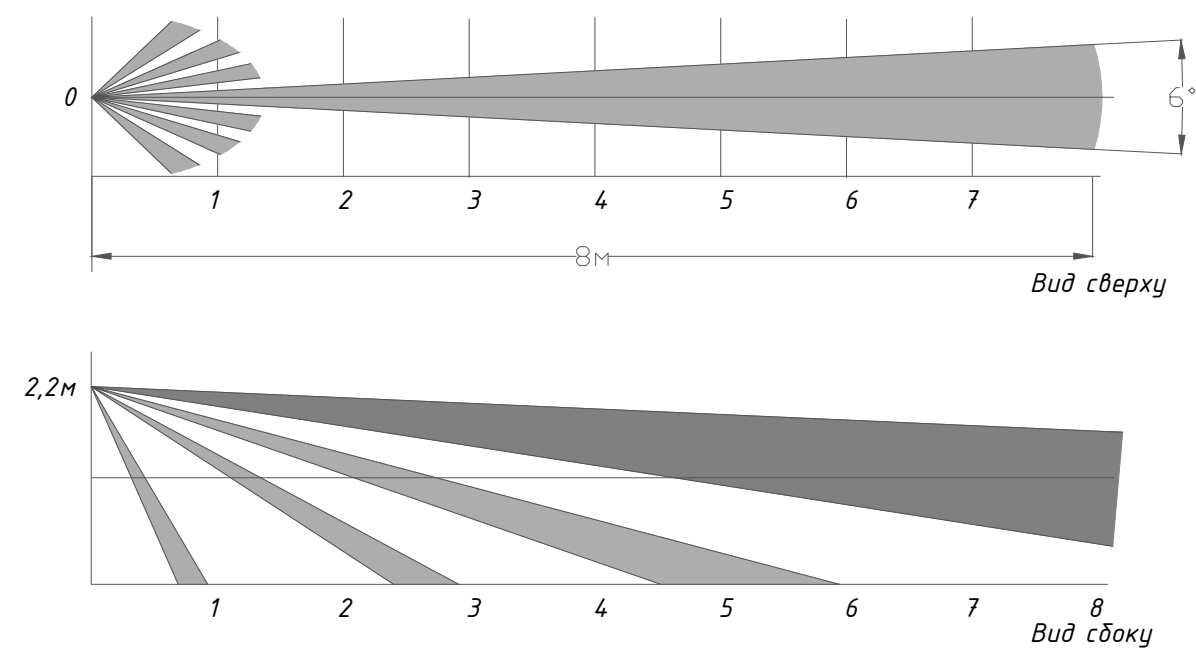


Diagram illustrating the recommended placement of smoke detectors in a room corner. The detectors are mounted on the ceiling and the walls. A vertical dimension line indicates a height range of 2,0-2,4m for the wall-mounted detectors.

Труба гофрированная  
Труба жесткая  
Рукав металлический  
Скоба металлическая  
СМО (СМД\*)  
Кабель  
Саморез  
Дюбель металлический универсальный

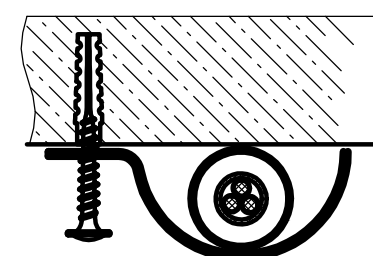


Diagram illustrating the assembly of a cable joint with fireproofing:

- Кабель (Cable)
- Гофрированная труба (Ribboned tube)
- Стена (Wall)
- Металлическая гильза (Metal sleeve)
- Гофрированная труба (Ribboned tube)
- Двухкомпонентная огнестойкая пена DN1201 или аналогичный состав (Two-component fire-resistant foam DN1201 or similar composition)

1. Перед началом монтажа металлической гильзы в стену обработать острые грани для формирования фаски.
2. Перед началом монтажа металлической гильзы в стену после механической обработки покрыть все поверхности гильзы краской по металлу.
3. После прокладки кабелей через гильзу заполнить все пустоты гильзы двухкомпонентной огнестойкой пеной ДКС DN1201 или аналогичным огнеупорным составом.

|             |         |      |      |            |       |   |        |      |        |
|-------------|---------|------|------|------------|-------|---|--------|------|--------|
|             |         |      |      |            |       | 696/П-25-АНО-Р-СОТС   |        |      |        |
|             |         |      |      |            |       | Капитальный ремонт Государственного Бюджетного<br>Общеобразовательного Учреждения города Москвы «Школа<br>№1282«Сокольники»<br>по адресу: г. Москва, ул. Бардовская, д. 1, корп. 1 |        |      |        |
| Изм.        | Кол.уч. | Лист | Идок | Подпись    | Дата  | Система охранной сигнализации   | Статья | Лист | Листов |
| Разработчик |         |      |      | В.И.Иванов | 07.26 |   | Р      | 10   | 11     |
| Проверил    |         |      |      | В.И.Иванов | 07.26 |   |        |      |        |
|             |         |      |      |            |       | Типовые схемы монтажа оборудования   |        |      |        |
| Инженер     |         |      |      | В.И.Иванов | 07.26 |   |        |      |        |

Формат А2 альбомная (420х594)

инв.Подл.

| Обозначение кабеля | Трасса                     |                            | Кабель            |                                  |          |       |                                         |          |
|--------------------|----------------------------|----------------------------|-------------------|----------------------------------|----------|-------|-----------------------------------------|----------|
|                    | Начало                     | Конец                      | Марка             | Кол.кабелей, число и сечение жил | Длина, м | Марка | Кол. кабелей, число и сеч. жил, напряж. | Длина, м |
| 1                  | ППКП1 "R3-Рудеж-20П (АЛС1) | ППКП1 "R3-Рудеж-20П (АЛС1) | КПСВВнг (А)-LSLTx | 1x2x0.75                         | 600      |       |                                         |          |
| 2                  | ППКП1 "R3-Рудеж-20П (АЛС2) | ППКП1 "R3-Рудеж-20П (АЛС2) | КПСВВнг (А)-LSLTx | 1x2x0.75                         | 850      |       |                                         |          |
| 3                  | ППКП2 "R3-Рудеж-20П (АЛС1) | ППКП2 "R3-Рудеж-20П (АЛС1) | КПСВВнг (А)-LSLTx | 1x2x0.75                         | 450      |       |                                         |          |
| 4                  | ППКП2 "R3-Рудеж-20П (АЛС2) | ППКП2 "R3-Рудеж-20П (АЛС2) | КПСВВнг (А)-LSLTx | 1x2x0.75                         | 310      |       |                                         |          |
| 5                  | ППКП3 "R3-Рудеж-20П (АЛС1) | ППКП2 "R3-Рудеж-20П (АЛС1) | КПСВВнг (А)-LSLTx | 1x2x0.75                         | 350      |       |                                         |          |
| 6                  | ППКП3 "R3-Рудеж-20П (АЛС2) | ППКП3 "R3-Рудеж-20П (АЛС2) | КПСВВнг (А)-LSLTx | 1x2x0.75                         | 580      |       |                                         |          |

|                |  |  |
|----------------|--|--|
| Согласовано    |  |  |
|                |  |  |
|                |  |  |
|                |  |  |
| Взам.инв.Н     |  |  |
|                |  |  |
| Подпись и дата |  |  |
|                |  |  |
| инв.Иподл.     |  |  |

|            |        |          |      |                                                                                       |       |   |                                                                                       |      |        |
|------------|--------|----------|------|---------------------------------------------------------------------------------------|-------|---|---------------------------------------------------------------------------------------|------|--------|
|            |        |          |      |                                                                                       |       | 696/П-25-АНО-Р-СОТС   |                                                                                       |      |        |
|            |        |          |      |                                                                                       |       | Капитальный ремонт Государственного Бюджетного<br>Общеобразовательного Учреждения города Москвы «Школа<br>№1282«Сокольники»<br>по адресу: г. Москва, ул. Барболина, д. 1, корп. 1 |                                                                                       |      |        |
| Изм.       | Кол.уч | Лист     | Идок | Подпись                                                                               | Дата  | Система охранной сигнализации   | Стадия                                                                                | Лист | Листов |
| Разработал |        | Вьюжский |      |  | 07.26 |   | Р                                                                                     | 11   | 11     |
| Проверил   |        | Вьюжский |      |  | 07.26 |   |                                                                                       |      |        |
|            |        |          |      |                                                                                       |       | Кабельный журнал   |  |      |        |
| Иж.интр.   |        | Вьюжский |      |  | 07.26 |   |                                                                                       |      |        |
|            |        |          |      |                                                                                       |       |   |                                                                                       |      |        |

Согласовано:

Дата

Подпись

Фамилия

№ отд. долж.

Взам. инв. №

Подпись и дата

Инов. № подл.

| № п/п | Наименование и техническая характеристика                                        | Тип, марка, обозначение документа, опросного листа | Код оборудования, изделия, материала | Завод изготовитель           | Единица измерения | Количество | Масса единицы, кг | Примечание |
|-------|----------------------------------------------------------------------------------|----------------------------------------------------|--------------------------------------|------------------------------|-------------------|------------|-------------------|------------|
|       |                                                                                  |                                                    |                                      |                              |                   |            |                   |            |
|       | <b>Охранныя сигнализация</b>                                                     |                                                    |                                      |                              |                   |            |                   |            |
|       | <b>Оборудование</b>                                                              |                                                    |                                      |                              |                   |            |                   |            |
|       | 1. Прибор приемно-контрольный и управления охранно-пожарный адресный             | R3-Рубеж-2ОП                                       |                                      | Рубеж                        | шт.               | 3          |                   |            |
|       | 2. Блок индикации и управления                                                   | R3-Рубеж-БИУ                                       |                                      | -//-                         | шт.               | 1          |                   |            |
|       | 3. Источник вторичного электропитания резервированный адресный                   | ИВЭПР 12/5 RS-R3 2x40 БР                           |                                      | -//-                         | шт.               | 1          |                   |            |
|       | 4. Извещатель охранный поверхностный звуковой                                    | ИО 32920-2                                         |                                      | -//-                         | шт.               | 59         |                   |            |
|       | 5. Извещатель охранный поверхностный оптико-электронный                          | ИО 30920-2                                         |                                      | -//-                         | шт.               | 18         |                   |            |
|       | 6. Извещатель охранный оптико-электронный объемный адресный                      | ИО 40920-2                                         |                                      | -//-                         | шт.               | 17         |                   |            |
|       | 7. Извещатель охранный магнитоконтактный                                         | ИО 10220-2                                         |                                      | -//-                         | шт.               | 145        |                   |            |
|       | 8. Кронштейн универсальный                                                       |                                                    | Rbz-163009                           | -//-                         | шт.               | 94         |                   |            |
|       | 9. Модуль сопряжения                                                             | R3-MC                                              |                                      | -//-                         | шт.               | 1          |                   |            |
|       | 10. Аккумулятор свинцово-кислотный 12В 26А/ч                                     | Delta DT1226                                       |                                      | Delta                        | шт.               | 2          |                   |            |
|       | 11.Кнопка тревожной сигнализации                                                 | КТ-R3                                              |                                      | Рубеж                        | шт.               | 6          |                   |            |
|       | 11. Устройство оконечной объектовое Приток-А-КОП-01                              | Приток-А-КОП-01 исп.1                              |                                      | Сократ                       | шт.               | 1          |                   |            |
|       | 12. Устройство радиоприемное                                                     | Базальт 708                                        |                                      | Базальт                      | шт.               | 1          |                   |            |
|       | 13. Брелок радиоканальный                                                        | Базальт-92                                         |                                      | Базальт                      | шт.               | 2          |                   |            |
|       | 4. Кнопка тревожной сигнализации                                                 | Астра-321 Т(ИО101-7/1)                             |                                      | Теко                         | шт.               | 1          |                   |            |
|       | 5. Индикатор прибытия наряда                                                     | БИГ-09                                             |                                      | ПЭАП                         | шт.               | 1          |                   |            |
|       | 6. Источник бесперебойного питания                                               | Скат 1200Д                                         |                                      | Бастион                      | шт.               | 1          |                   |            |
|       | 7. Аккумуляторная батарея                                                        | Delta1217                                          |                                      | Delta                        | шт.               | 1          |                   |            |
|       |                                                                                  |                                                    |                                      |                              |                   |            |                   |            |
|       | <b>Автоматизированное рабочее место в составе:</b>                               |                                                    |                                      |                              |                   |            |                   |            |
|       | 1. Моноблок iRU 23IM 1972080 Intel Core i5-1035G4 3.7 ГГц, RAM 16 Гб, SSD 512 Гб | 1972080                                            |                                      | «iRU»                        | шт                | 1          |                   |            |
|       | 2. Источник бесперебойного питания                                               | «ИБП 1 кВА ИДП-1-1/1-1-220-А»                      |                                      | АО Электромаш                | шт.               | 1          |                   |            |
|       | 3. ПО FireSec3-Pro+мультисервисная задача                                        |                                                    |                                      | ООО «КБ Пожарной Автоматики» | шт.               | 1          |                   |            |

|            |        |      |       |         |       |                        |  |  |        |      |        |  |
|------------|--------|------|-------|---------|-------|------------------------|--|--|--------|------|--------|--|
|            |        |      |       |         |       | 696/П-25-АНО-Р-COTC.CO |  |  |        |      |        |  |
|            |        |      |       |         |       |                        |  |  |        |      |        |  |
| Изм.       | Кол.у  | Лист | №док. | Подпись | Дата  | Спецификация           |  |  | Стадия | Лист | Листов |  |
| Разработал | Коняев |      |       |         | 10.24 |                        |  |  | Р      | 1    | 2      |  |
| Проверил   | Гулько |      |       |         | 10.24 |                        |  |  |        |      |        |  |
|            |        |      |       |         |       |                        |  |  |        |      |        |  |
| Н.контроль | Гулько |      |       |         | 10.24 |                        |  |  |        |      |        |  |
|            |        |      |       |         |       |                        |  |  |        |      |        |  |

|               |                |              |
|---------------|----------------|--------------|
| Инва. № подл. | Подпись и дата | Взам. инв. № |
|               |                |              |

| № п/п | Наименование и техническая характеристика                                                                                                | Тип, марка, обозначение документа, опросного листа | Код оборудования, изделия, материала | Завод изготовитель  | Единица измерения      | Количество | Масса единицы, кг | Примечание |
|-------|---|----------------------------------------------------|--------------------------------------|---------------------|------------------------|------------|-------------------|------------|
|       | Кабельные изделия   |                                                    |                                      |                     |                        |            |                   |            |
|       | 1. Кабель категории 5е, U/UTP нг(А)-LSLTx                                                                                                | ParLan U/UTP Cat5e PVCLS нг(А)-LSLTx 4x2x0,52      |                                      | Паритет             | м.                     | 30         |                   |            |
|       | 2. Кабель для систем передачи данных пониженной пожароопасности с низким дымо- и газовыделением, с низкой токсичностью продуктов горения | КПСВВнг(А)-LSLTx 1x2x0,75                          |                                      | СПКБ-Техно          | м.                     | 3140       |                   |            |
|       | 3. Силовой кабель огнестойкий   | ВВГнг(А)-LSLTx 2x1,5                               |                                      | Спецкабель          | м.                     | 30         |                   |            |
|       | Материалы   |                                                    |                                      |                     |                        |            |                   |            |
|       | 1. Гофрированная труба из ПВХ (серия 9), Дном.=16                                                                                        | 91916                                              |                                      | ЗАО «ДКС»           | м.                     | 3200       |                   |            |
|       | 2. Скоба металлическая Дном 16   |                                                    |                                      | Россия              | шт.                    | 9600       |                   |            |
|       | 3. Крепежные материалы   |                                                    |                                      |                     | шт.                    | 10000      |                   |            |
|       | 4. Коробка коммутационная   | КС-4                                               |                                      | Россия              | шт.                    | 145        |                   |            |
|       | 5.Гильзы в стенах и перегородках из труб стальных 25мм.                                                                                  |                                                    |                                      | ЗАО "Электромонтаж" | м.                     | 15         |                   |            |
|       | 6.Гидроизоляционная огнеупорная мастика                                                                                                  | АМ-05                                              |                                      |                     | кг                     | 15         |                   |            |
|       |   |                                                    |                                      |                     |                        |            |                   |            |
|       |   |                                                    |                                      |                     | 696/П-25-АНО-Р-СОТС.СО |            |                   | Лист       |
|       |   |                                                    |                                      |                     |                        |            |                   | 2          |
| Изм.  | Кол.уч   | Лист                                               | № док.                               | Подпись             | Дата                   |            |                   |            |