



109548, г. Москва, Муниципальный Округ Печатники, ул. Шоссейная, д. 19, к. 1,
кв.117 e-mail PROEKTplus-work@yandex.ru

Свидетельство № СРО- П-110-009723217107-0532

СОГЛАСОВАНО:
Главный инженер
АО «МосводоканалСтройТрест»

_____ А.А. Вешкин

«__» _____ 2026г

**Капитальный ремонт Государственного Бюджетного
Общеобразовательного Учреждения города Москвы
«Школа № 1282 «Сокольники»
по адресу: г. Москва, ул. Барболина, д. 1, корп. 1
1 этап**

РАБОЧАЯ ДОКУМЕНТАЦИЯ

Основной комплект рабочих чертежей

Система кабельного телевидения

696/П-24-АНО-Р-ТВ

Генеральный директор

Главный инженер проекта



Н.А. Выходова

А.Н. Гулько

2026

Име. № подл.	Подп. И дата	Взам. инв. №

Согласовано

Взам.инв.Н

Подпись и дата

инв.Нподл.

Ведомость основных комплектов рабочих чертежей		
Обозначение	Наименование	Примечание
696/П-24-АНО-Р-ТВ	Система кабельного телевидения	
Ведомость рабочих чертежей основного комплекта		
Лист	Наименование	Примечание
1	Общие данные	
2	Ситуационный план	
3	Схема принципиальная СКТ	
4	План расположения оборудования СКТ на 1 этаже	
5	План расположения оборудования СКТ на 2 этаже	
6	План расположения оборудования СКТ на 3 этаже	
7	План расположения оборудования СКТ на 4 этаже	
8	План расположения оборудования СКТ на кровле	
9	Шкаф ТШ-РСО-ДОНМ. План расположения оборудования в шкафу.	
10	Кабельный журнал	
Обозначение	Наименование	Примечание
	Ссылочные документы	
№384-ФЗ	Технический регламент о безопасности зданий и сооружений	
ГОСТ Р 21.101-2020	Основные требования к проектной и рабочей документации	
ГОСТ 31565-2012	Кабельные изделия. Требования пожарной безопасности	
СП 118.13330.2022	Общественные здания и сооружения	
СП 133.13330.2012	Сети проводного радиовещания и оповещения в зданиях и сооружениях. Нормы проектирования	
СП 134.13330.2022	Системы электросвязи зданий и сооружений. Основные положения проектирования (с Изменением N 1)	
Р 078-2019	Методологические рекомендации. "Инженерно-техническая укрепленность и оснащение техническими средствами.	
ПУЭ	Правила устройства электроустановок. Издание 7	
	Прилагаемые документы	
696/П-24-АНО-Р-ТВ.СО	Спецификация оборудования, изделий и материалов	

Общие указания

1 Система кабельного телевидения.

Проектом предусмотрено:

1) Установка на кровле здания в зоне уверенного приема сигналов телевидения (1-й и 2-й мультиплекс) антенны ДМВ-диапазона.

Установка в комнате охраны (пом. 103, 1 этаж) шкафа ТШ-РСО-ДОНМ (учтен томом 696/П-24-АНО-Р-РФ) с оборудованием головной станции (Мини-ГС).

2) Прокладка антенного коаксиального кабеля РК 75-7-327нз(А)-LSLTx (75 Ом) от антенны ДМВ диапазона до входа в Мини-ГС .

3) Установка в слаботочных шкафах каждого этажа абонентских ответвителей согласно структурной схемы.

4) Прокладка распределительного коаксиального кабеля РК 75-7-327нз(А)-LSLTx (75 Ом) от выхода Мини-ГС до и между абонентскими ответвителями.

5) Установка в телефицируемых помещениях ТВ розетки оконечные, не далее 1м от розеток эл. сети 220 В.

6) Прокладка абонентского коаксиального кабеля РК 75-4,8-319нз(А)-LSLTx (75 Ом) от отводов абонентских ответвителей до ТВ розеток.

7) Обеспечен прием и распределение:

- первого федерального пакета, вещаемого по 30 ТВ каналу в формате DVB/T2 с конвертирование 30/23.
- второго федерального пакета, вещаемого по 24 ТВ каналу в формате DVB/T2 с конвертирование 24/25.

3 Техника безопасности.:

- лица не ознакомленные с правилами техники безопасности, не должны допускаться к строительно-монтажным работам;
- при выполнении работ с использованием оборудования, механизмов, устройств и приборов необходимо соблюдать меры техники безопасности, указанные в соответствующих инструкциях по их эксплуатации.

4 Все проектные решения согласованы с заинтересованными организациями.

5 На основании принятых проектных решений определены объемы работ, составлена спецификация материалов и изделий.

6 Прокладку слаботочных кабелей осуществить по потолку в коридорах и общественных зонах в перфорированных лотках или в жестких гладких трубах, отводы до оборудования в помещениях с фальшпотолком предусмотреть в гофрированных трубах.

Рабочие чертежи разработаны в соответствии с требованиями экологических, противопожарных и других норм, действующих на территории Российской Федерации и обеспечивают безопасную для жизни и здоровья людей эксплуатацию объекта при соблюдении предусмотренных рабочими чертежами мероприятий.


Главный инженер проекта

А.Н. Гулько

						696/П-24-АНО-Р-ТВ			
						Капитальный ремонт Государственного Бюджетного Общеобразовательного Учреждения города Москвы «Школа №1282 «Сокольники» по адресу: г. Москва, ул. Барболина, д. 1, корп. 1			
Изм.	Кол.уч	Лист	Ндок	Подпись	Дата	Система кабельного телевидения	Стадия	Лист	Листов
Разработал	Коняев				07.26		Р	1	10
Проверил	Гулько				07.26				
						Общие данные			
Н.контр.	Гулько				07.26				

СИТУАЦИОННЫЙ ПЛАН

ГБОУ «Школа №1282 «Сокольники» по адресу: г. Москва, ул. Барболина, д. 1, корп. 1

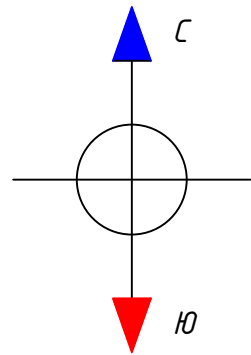


Условные графические обозначения:

— зона действия проектируемого оборудования

						696/П-24-АНО-Р-ТВ			
						Капитальный ремонт Государственного Бюджетного Общеобразовательного Учреждения города Москвы «Школа №1282 «Сокольники» по адресу: г. Москва, ул. Бардолина, д. 1, корп. 1			
Изм.	Кол.уч	Лист	Ндок	Подпись	Дата	Система кабельного телевидения	Стадия	Лист	Листов
Разработал	Коняев				07.26		Р	2	
Проверил	Гулько				07.26	Ситуационный план			
Н.контр.	Гулько				07.26				

Согласовано				
Взам.инв.Н				
Подпись и дата				
инв.Нподл.				

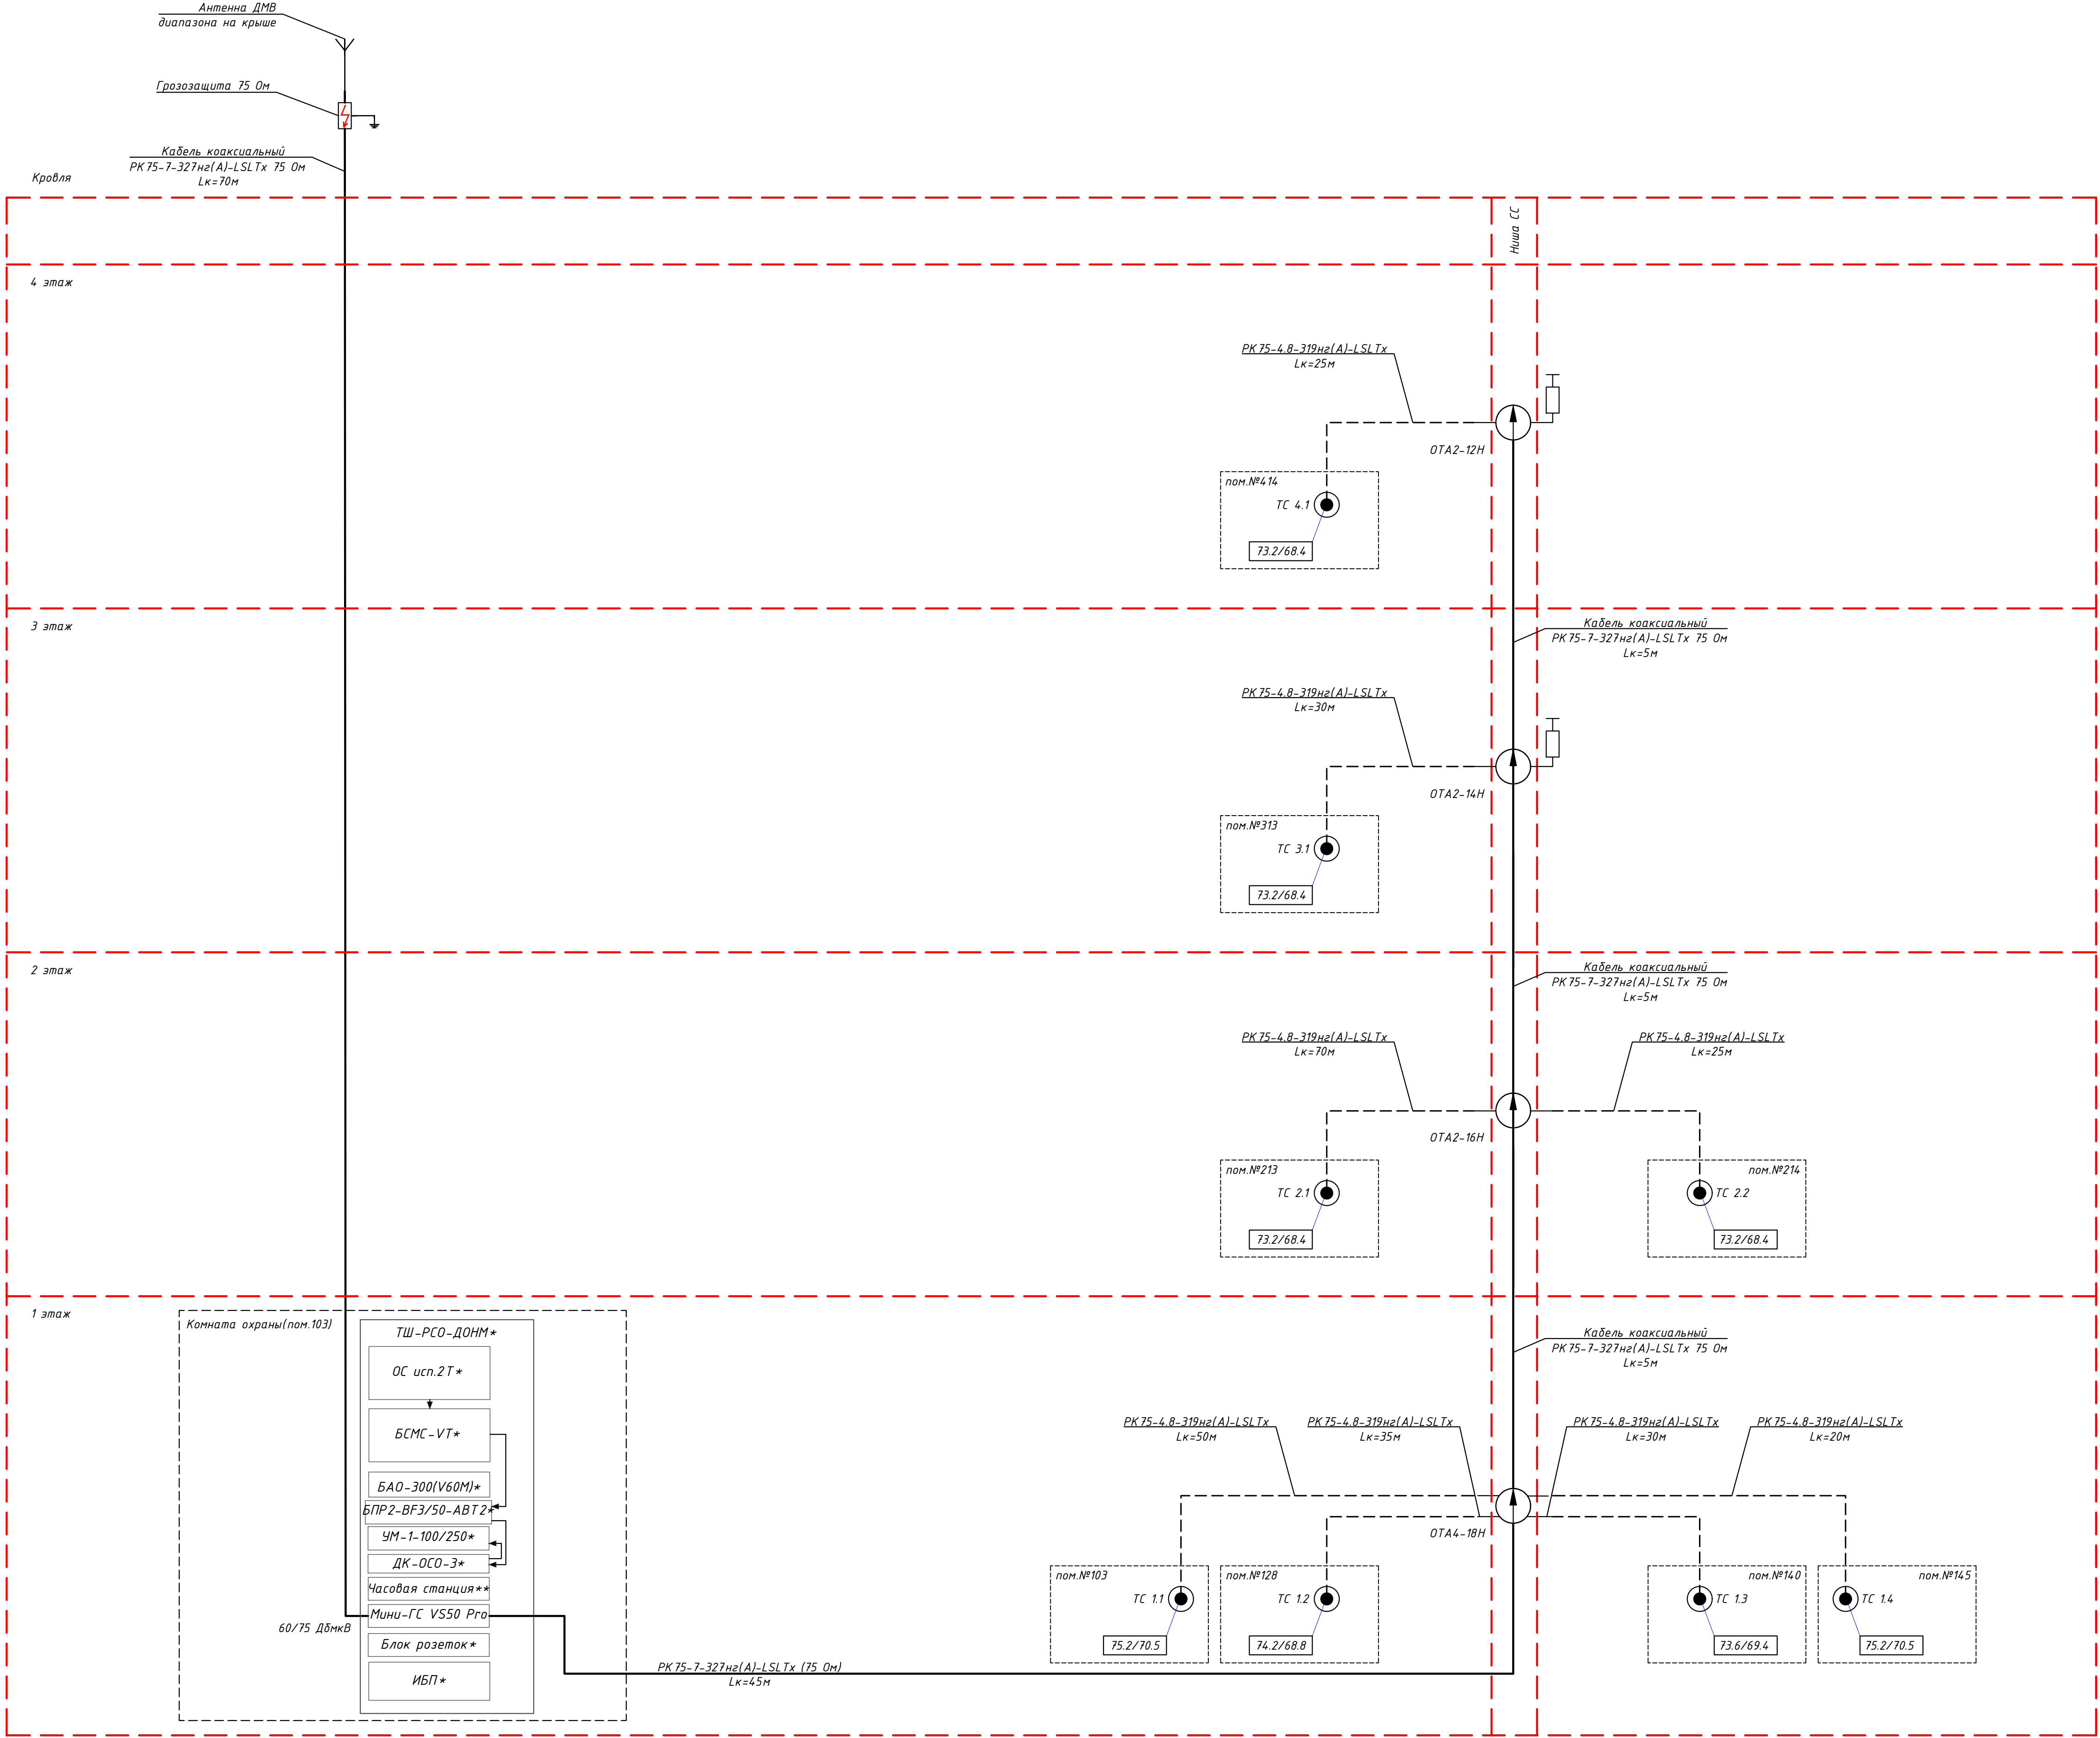

Условные графические обозначения:

- грозозащита для коаксиальных линий (75 Ом)
- Оборудование Мини-ГС
- кабель коаксиальный PK 75-4,8-319Hz(A)-LSLTx (75 Ом)
- кабель коаксиальный PK 75-7-327Hz(A)-LSLTx (75 Ом)
- абонентский ответвитель на 2 отвода
- нагрузка согласованная 75 Ом
- розетка ТВ оконечная
- абонентский ответвитель на 4 отвода


Примечание:

- На кровле установить на существующей мачте (установка учтена разделом РС) антенну ДМВ диапазона.
- В помещении охраны (пом. 103, 1 этаж) установить Мини-ГС VS50 Pro в шкаф ТШ-РСО-ДОММ (учтен томом 696/П-24-АНО-Р-РФ). Корпус шкафа заземлить.
- Антенный усилитель АВ011 установить при недостаточном уровне сигнала на входе Мини ГС менее 60 дБ.
- Домовая распределительная сеть выполняется кабелем марки PK 75-7-327Hz(A)-LSLTx.
- Абонентская распределительная сеть выполняется кабелем марки PK 75-4,8-319 Hz(A)-LSLTx.
- Участки, где длина кабеля не указана, выполнять кабелем PK 75-4,8-319 Hz(A)-LSLTx из расчета 1 м.
- Оконечные ТВ розетки устанавливаются в помещениях согласно проекта.
- Расчет СКТ произведен из условий обеспечения уровней сигнала на отводах абонентских ответвителей в пределах 72-84дБ/мкВ и на абонентских ТВ розетках в пределах 60-80дБ/мкВ на 2/69 ТВ каналах.
- Перед нарезкой кабелей, их длины уточняются промером трасс прокладки групп на месте монтажа.

Примечание:

- *Учтена томом 696/П-24-АНО-Р-РФ
- **Учтено томом 696/П-24-АНО-Р-ЧФ

						696/П-24-АНО-Р-ТВ		
						Капитальный ремонт Государственного Бюджетного Общеобразовательного Учреждения города Москвы «Школа №1282 «Сколково» по адресу: г. Москва, ул. Бардольна, д. 1, корп. 1		
Изм.	Кол.ч.	Лист	Издок	Подпись	Дата	Система кабельного телевидения	Стадия	Лист
Разработал	Конев				07.26		р	3
Проверил	Гулько				07.26	Схема принципиальная СКТ		
Н.контр.	Гулько				07.26			

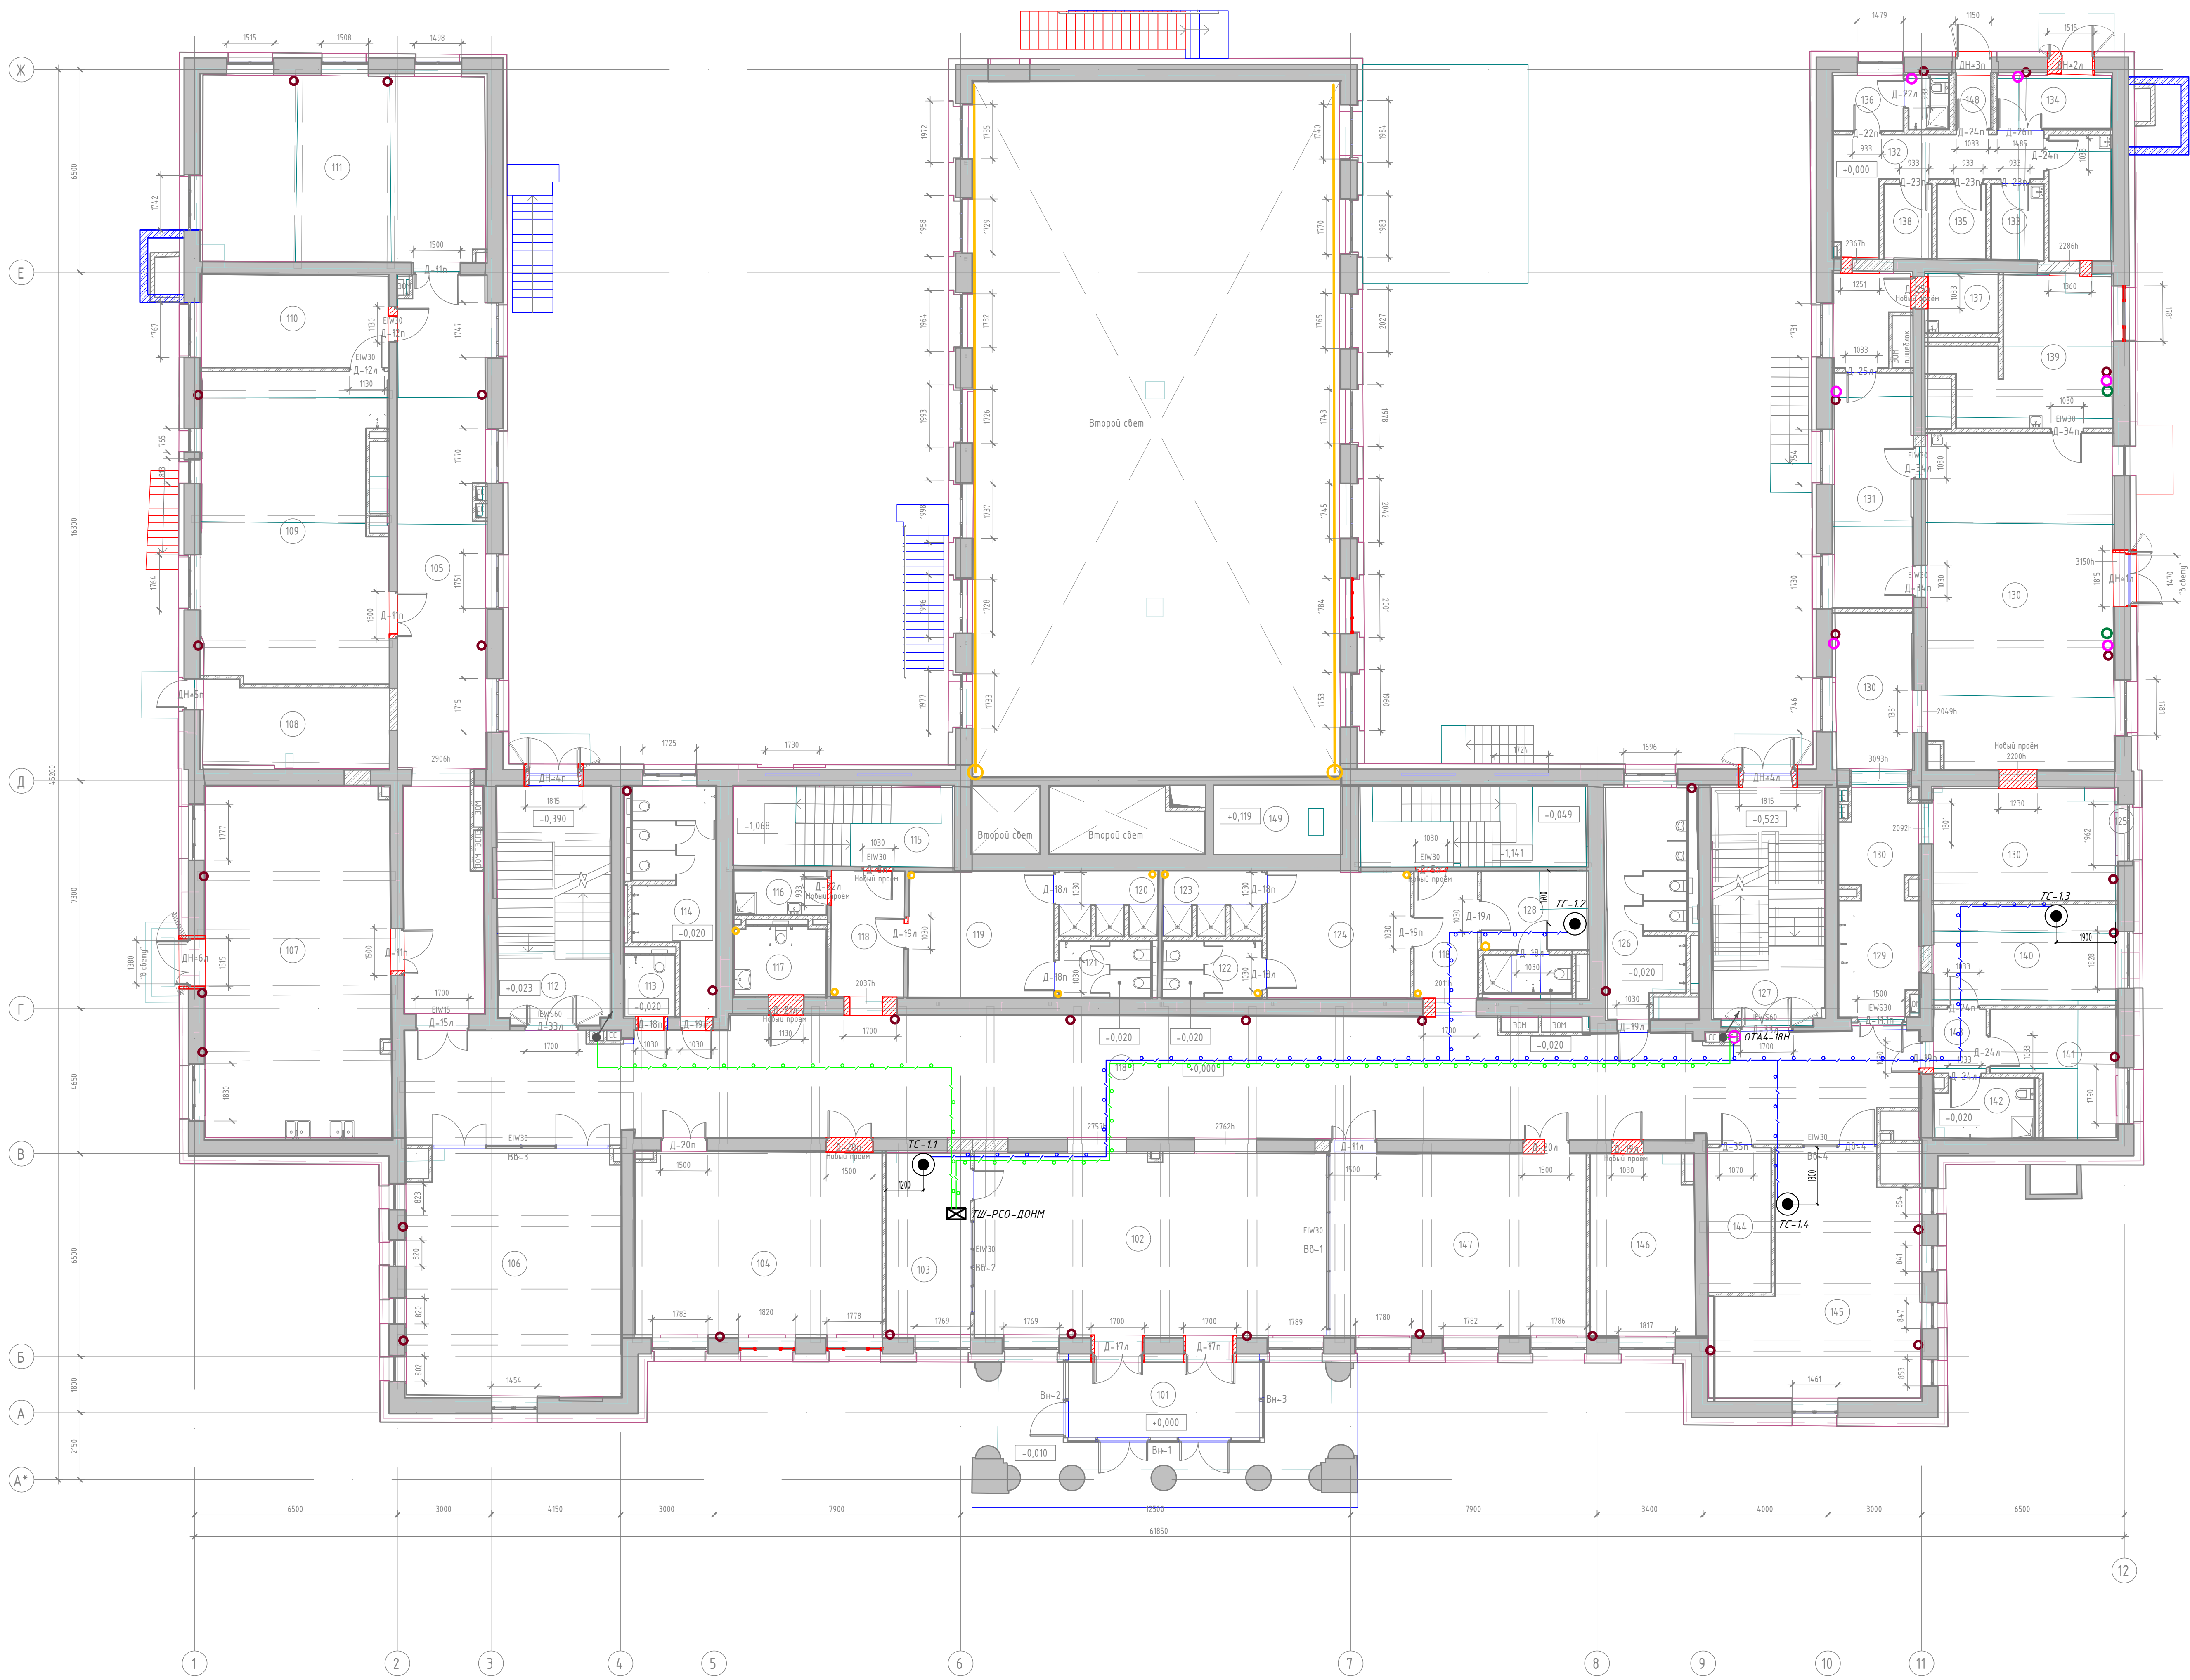


Экспликация помещений 1-го этажа			
Номер помеще-ния	Наименование	Площадь, м²	Кол. помеще-ния
101	Танцбур	17,0	
102	Вестибюль	67,2	
103	Комната охраны (с диспетчерским пунктом)	16,4	
104	Гардероб для обучающихся	44,9	
105	Коридор	62,8	
106	Гардероб для обучающихся	54,2	
107	Учебный кабинет (Тип 1)	67,2	
108	Электрощитовая	15,6	В3
109	Учебный кабинет (Тип 2)	57,3	
110	Кладовая	18,0	В3
111	Учебный кабинет (математика)	54,6	
112	Лестничная клетка (Тип Л1)	27,6	
113	Туалет для персонала	3,2	
114	Уборная для девочек	15,9	
115	Техническая лестница	18,0	
116	ПМЖ	4,2	В4
117	Универсальная уборная для МЖ	6,6	
118	Коридор	198,7	
119	Раздевальня Тип 1	18,7	
120	Душевая	6,2	
121	Уборная	5,3	
122	Уборная	5,8	
123	Душевая	6,2	
124	Раздевальня Тип 1	18,6	
125	Техническая лестница	Не определена	
126	Уборная для мальчиков	18,0	
127	Лестничная клетка (Тип Л1)	27,6	
128	Тренировочная с санузлом	8,5	
129	Учебная	9,2	
130	Обеденный зал	108,9	
131	Меченая для столовой посуды	18,8	В4
132	Коридор	13,1	
133	Кладовая и моченая оборотной тары	4,0	В4
134	Загрузочный цех	6,2	В4
135	Кладовая сухих продуктов	3,7	В4
136	Помещение персонала с санузлом	4,2	
137	Пом. для временного хранения вещей отходов	4,4	В4
138	ПМЖ	3,6	В4
139	Пом. подготовки введ. к реализации с участием мойки кулальной посуды	30,3	В4
140	Кабинет врача	18,9	
141	Присадный (приводной) кабинет	13,2	
142	Пом. для хранения уборочного инвентаря, приготовления дезинфицирующих растворов	5,9	В4
143	Ожидающая мебель	3,5	
144	Помещение СС	9,4	В4
145	Кабинет с рабочим пространством для учителя (Тип 1)	42,0	
146	Гардероб для учителей	19,4	
147	Гардероб для обучающихся	49,0	
148	Танцбур	2,0	
149	Ванная	9,1	?
ИТОГО:		1245,1	

Условные графические обозначения

- розетка телевизионная;
- ответитель ОТА;
- телекоммуникационный шкаф;
- кабель коаксиальный в гофротрубе РК 75-4,8-319на(А)-LSLTx (75 Ом);
- кабель коаксиальный в гофротрубе РК 75-7-327на(А)-LSLTx (75 Ом);
- кабельная шахта;

Примечание:
1. ТВ розетки устанавливаются в одну розеточную группу РС и ЗОМ согласно приложению.

656/П-24-АНД-Р-ТВ			
Капитальный ремонт Государственного бюджетного общеобразовательного учреждения «Школа №1282 «Секандинки» по адресу: г. Москва, ул. Барбарина, д. 1, корп. 1			
Мат. Всп. Р. Лист	Итого	Подпись	Дата
Разработчик	Рисовал	Проверил	07.26
Инженер	Гулько	07.26	
План расположения оборудования СКТ на 1 этаже		Р	4
Формат А0 альбомная (84х1189)			

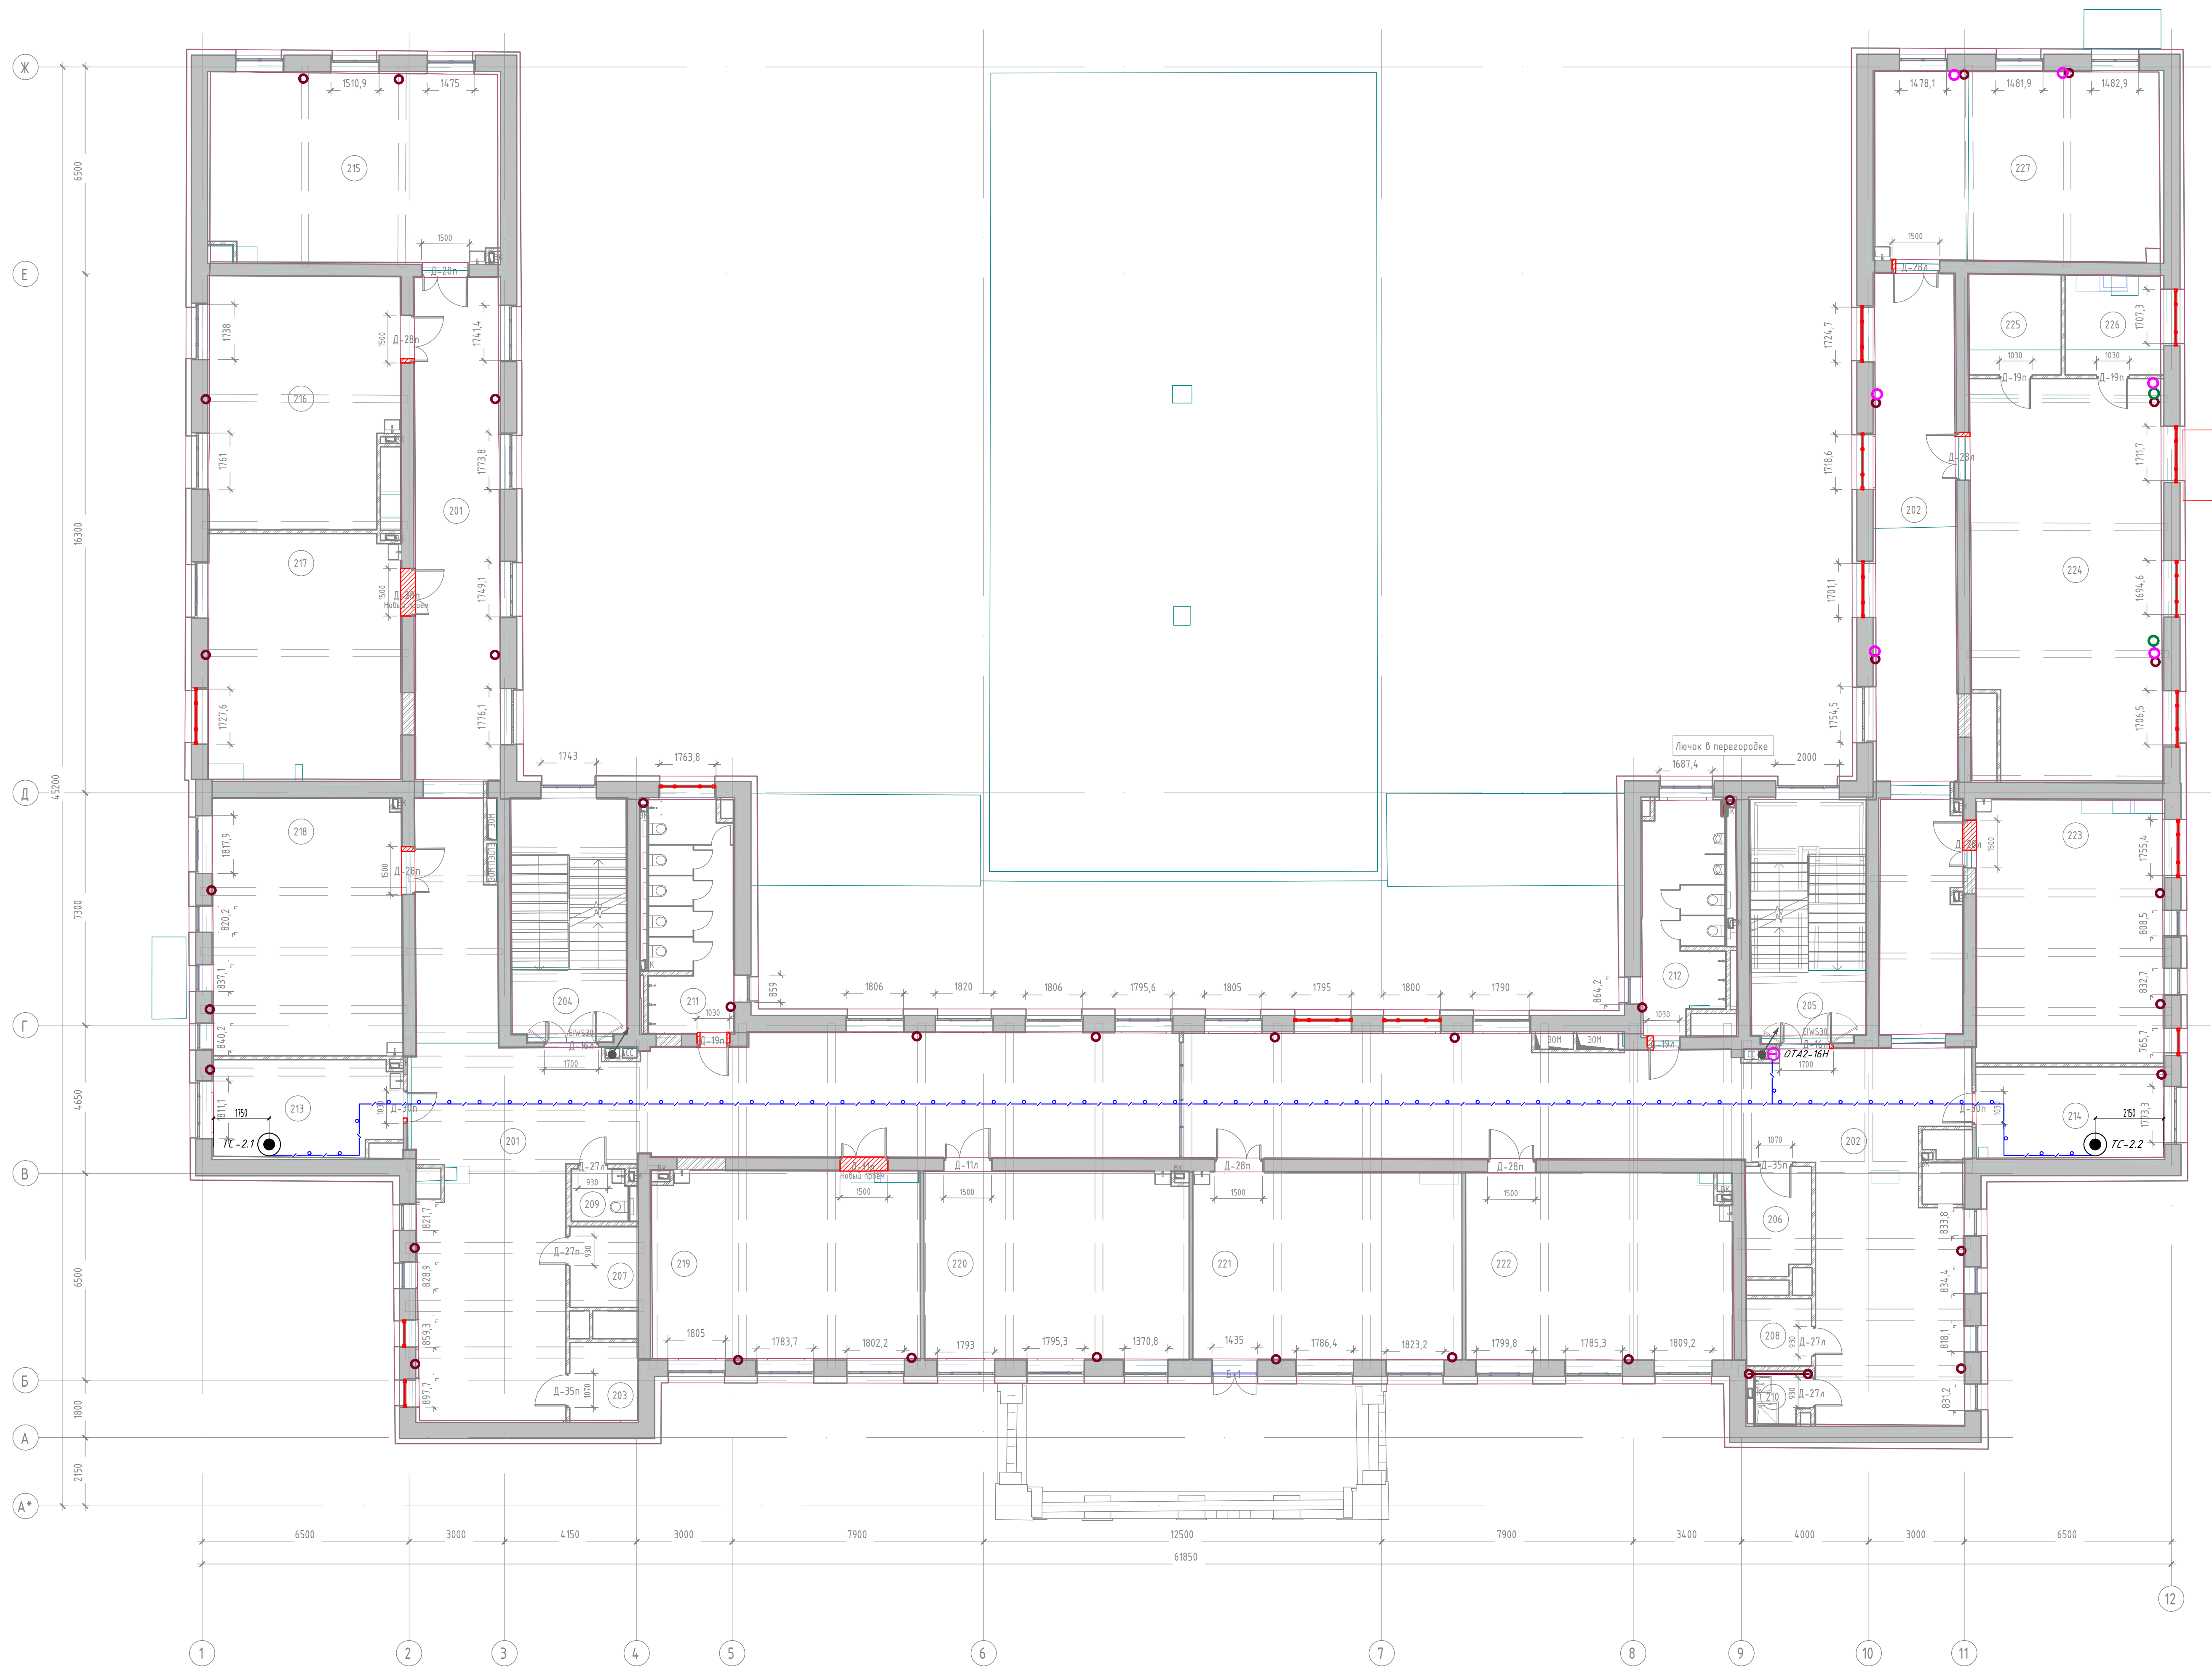

Экспликация помещений 2-го этажа

Номер помеще-ния	Наименование	Площадь, м²	Класс помеще-ния
201	Коридор с рекреацией	190,6	
202	Коридор с рекреацией	188,2	
203	Помещение СС	5,5	В4
204	Лестничная клетка (Тип Л1)	27,4	
205	Лестничная клетка (Тип Л1)	27,7	
206	Помещение СС	6,9	В4
207	Подсобное помещение	5,4	В4
208	Подсобное помещение	4,3	В4
209	Туалет для персонала	2,8	
210	ЛМ	2,6	В4
211	Зубная для девочек	19,4	
212	Зубная для мальчиков	18,1	
213	Кабинет для индивидуальных занятий, в т.ч. с учителем, логопедом	17,5	
214	Административный кабинет (Тип В)	17,0	
215	Учебный кабинет	53,5	
216	Учебный кабинет	45,8	
217	Учебный кабинет	46,5	
218	Учебный кабинет	48,0	
219	Учебный кабинет	49,5	
220	Учебный кабинет	48,9	
221	Учебный кабинет	49,8	
222	Учебный кабинет	48,7	
223	Учебный кабинет	49,0	
224	Гимнастический зал	73,7	
225	Раздевальня Тип 1	9,1	
226	Раздевальня Тип 1	9,5	
227	Учебный кабинет	53,6	
Итого:		1119,0	


Условные графические обозначения

- розетка телевизионная;
- ответитель ОТА;
- телекоммуникационный шкаф;
- кабель коаксиальный в гофротрубе РК75-4,8-319на(А)-LSLTx (75 Ом);
- кабель коаксиальный в гофротрубе РК75-7-327на(А)-LSLTx (75 Ом);
- кабельная шахта;

Примечание:

1. ТВ розетки устанавливаются в одну розеточную группу РС и ЗОМ согласно приложению.

				656/П-24-АНД-Р-ТВ			
				Капитальный ремонт Государственного бюджетного общеобразовательного учреждения «Школа №1282 «Секандинки» по адресу: г. Москва, ул. Бардовская, д. 1 корп. 1			
Мат. Вкл. в Лист	Мат. вкл. в Лист	Подпись	Дата	Система кабельного телевидения	Лист	Листов	
Разработал	Рисовал	Гулько	07.26		Р	5	
Исполн.	Гулько	07.26		План расположения оборудования СКТ на 2 этаже			

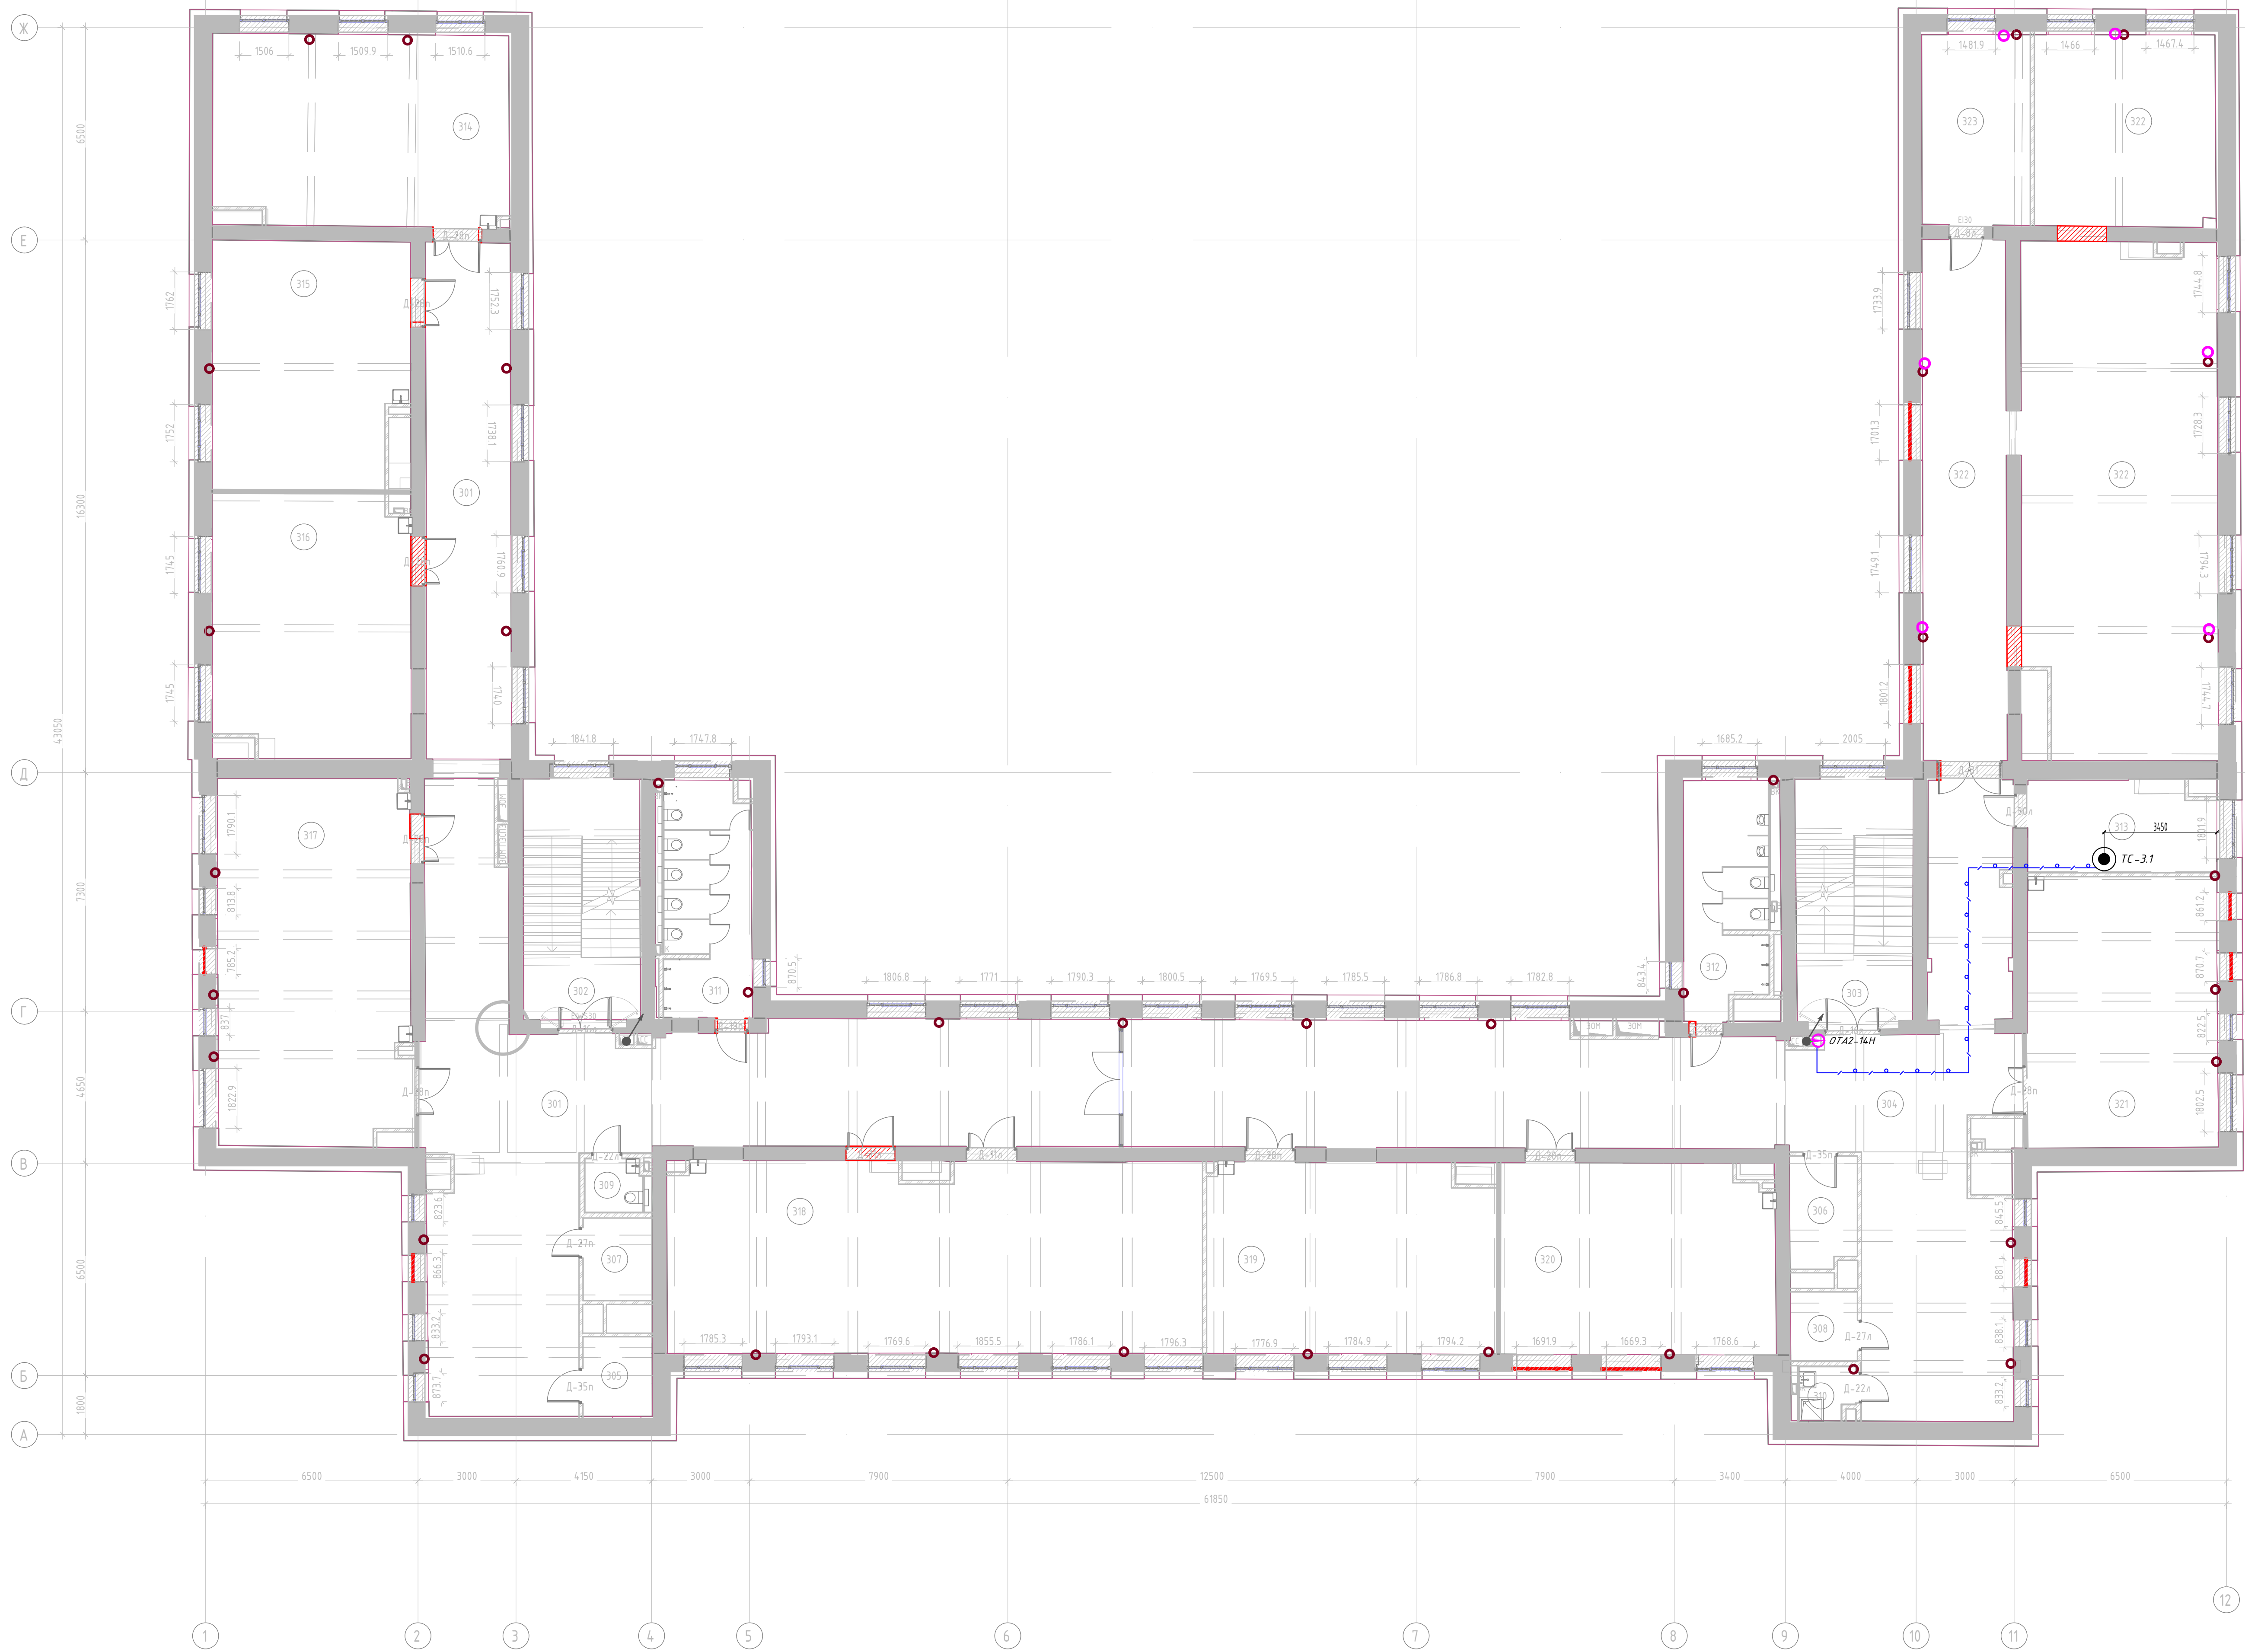


Экспликация помещений 3-го этажа			
Номер помеще-ния	Наименование	Площадь, м²	Кан-пече-ния
301	Коридор с рекреацией	178,8	
302	Лесничья клетка (Топ ЛП)	27,1	
303	Лесничья клетка (Топ ЛП)	27,4	
304	Коридор с рекреацией	156,6	
305	Помещение СС	5,3	В4
306	Помещение СС	6,9	В4
307	Подсобное помещение	5,3	В4
308	Подсобное помещение	4,3	В4
309	Туалет для персонала	2,8	
310	Л/М	2,7	В4
311	Уборная для девочек	19,0	
312	Уборная для мальчиков	18,3	
313	Кабинет для индивидуальных занятий, 6 м.к. с коррекционным кабинетом	15,9	
314	Учебный кабинет	53,0	
315	Учебный кабинет	44,6	
316	Учебный кабинет	48,0	
317	Кабинет иностранного языка с возможностью деления трансформироваемой перегородкой на 80а помещения	66,1	
318	Творческая студия с возможностью деления трансформироваемой перегородкой на 80а помещения	95,4	
319	Учебный кабинет	51,0	
320	Учебный кабинет	48,5	
321	Учебный кабинет	48,5	
322	Мультифункциональный информационный библиотечный центр с зоной для индивидуальных и групповых занятий, методички, центры детских инициатив	169,7	
323	Мультифункциональный информационный библиотечный центр. Хранилище (закрытый фонд) и видеотека кино	19,7	В3
Итого:		1115,0	

Условные графические обозначения

- розетка телевизионная;
- ответвитель ОТА;
- телекоммуникационный шкаф;
- кабель коаксиальный в гофротрубе РК 75-4,8-319на(А)-LSLTx (75 Ом);
- кабель коаксиальный в гофротрубе РК 75-7-327на(А)-LSLTx (75 Ом);
- кабельная шахта;

Примечание:
1. ТВ розетки устанавливаются в одну розеточную группу РС и ЗОМ согласно приложению.

				656/П-24-АНД-Р-ТВ			
				Капитальный ремонт Государственного бюджетного общеобразовательного учреждения «Школа №1282 «Сокольники» по адресу: г. Москва, ул. Барбарисов, д. 1, корт. 1			
Мат. Вкл. в Лист	Мат. в Лист	Подпись	Дата	Система кабельного телевидения	Лист	Листов	
Разработал	Гулько	07.26	07.26	Р	6		
Исполн	Гулько	07.26	07.26	План расположения оборудования СКТ на 3 этаже			
				Формат А0 альбомная (841х1189)			

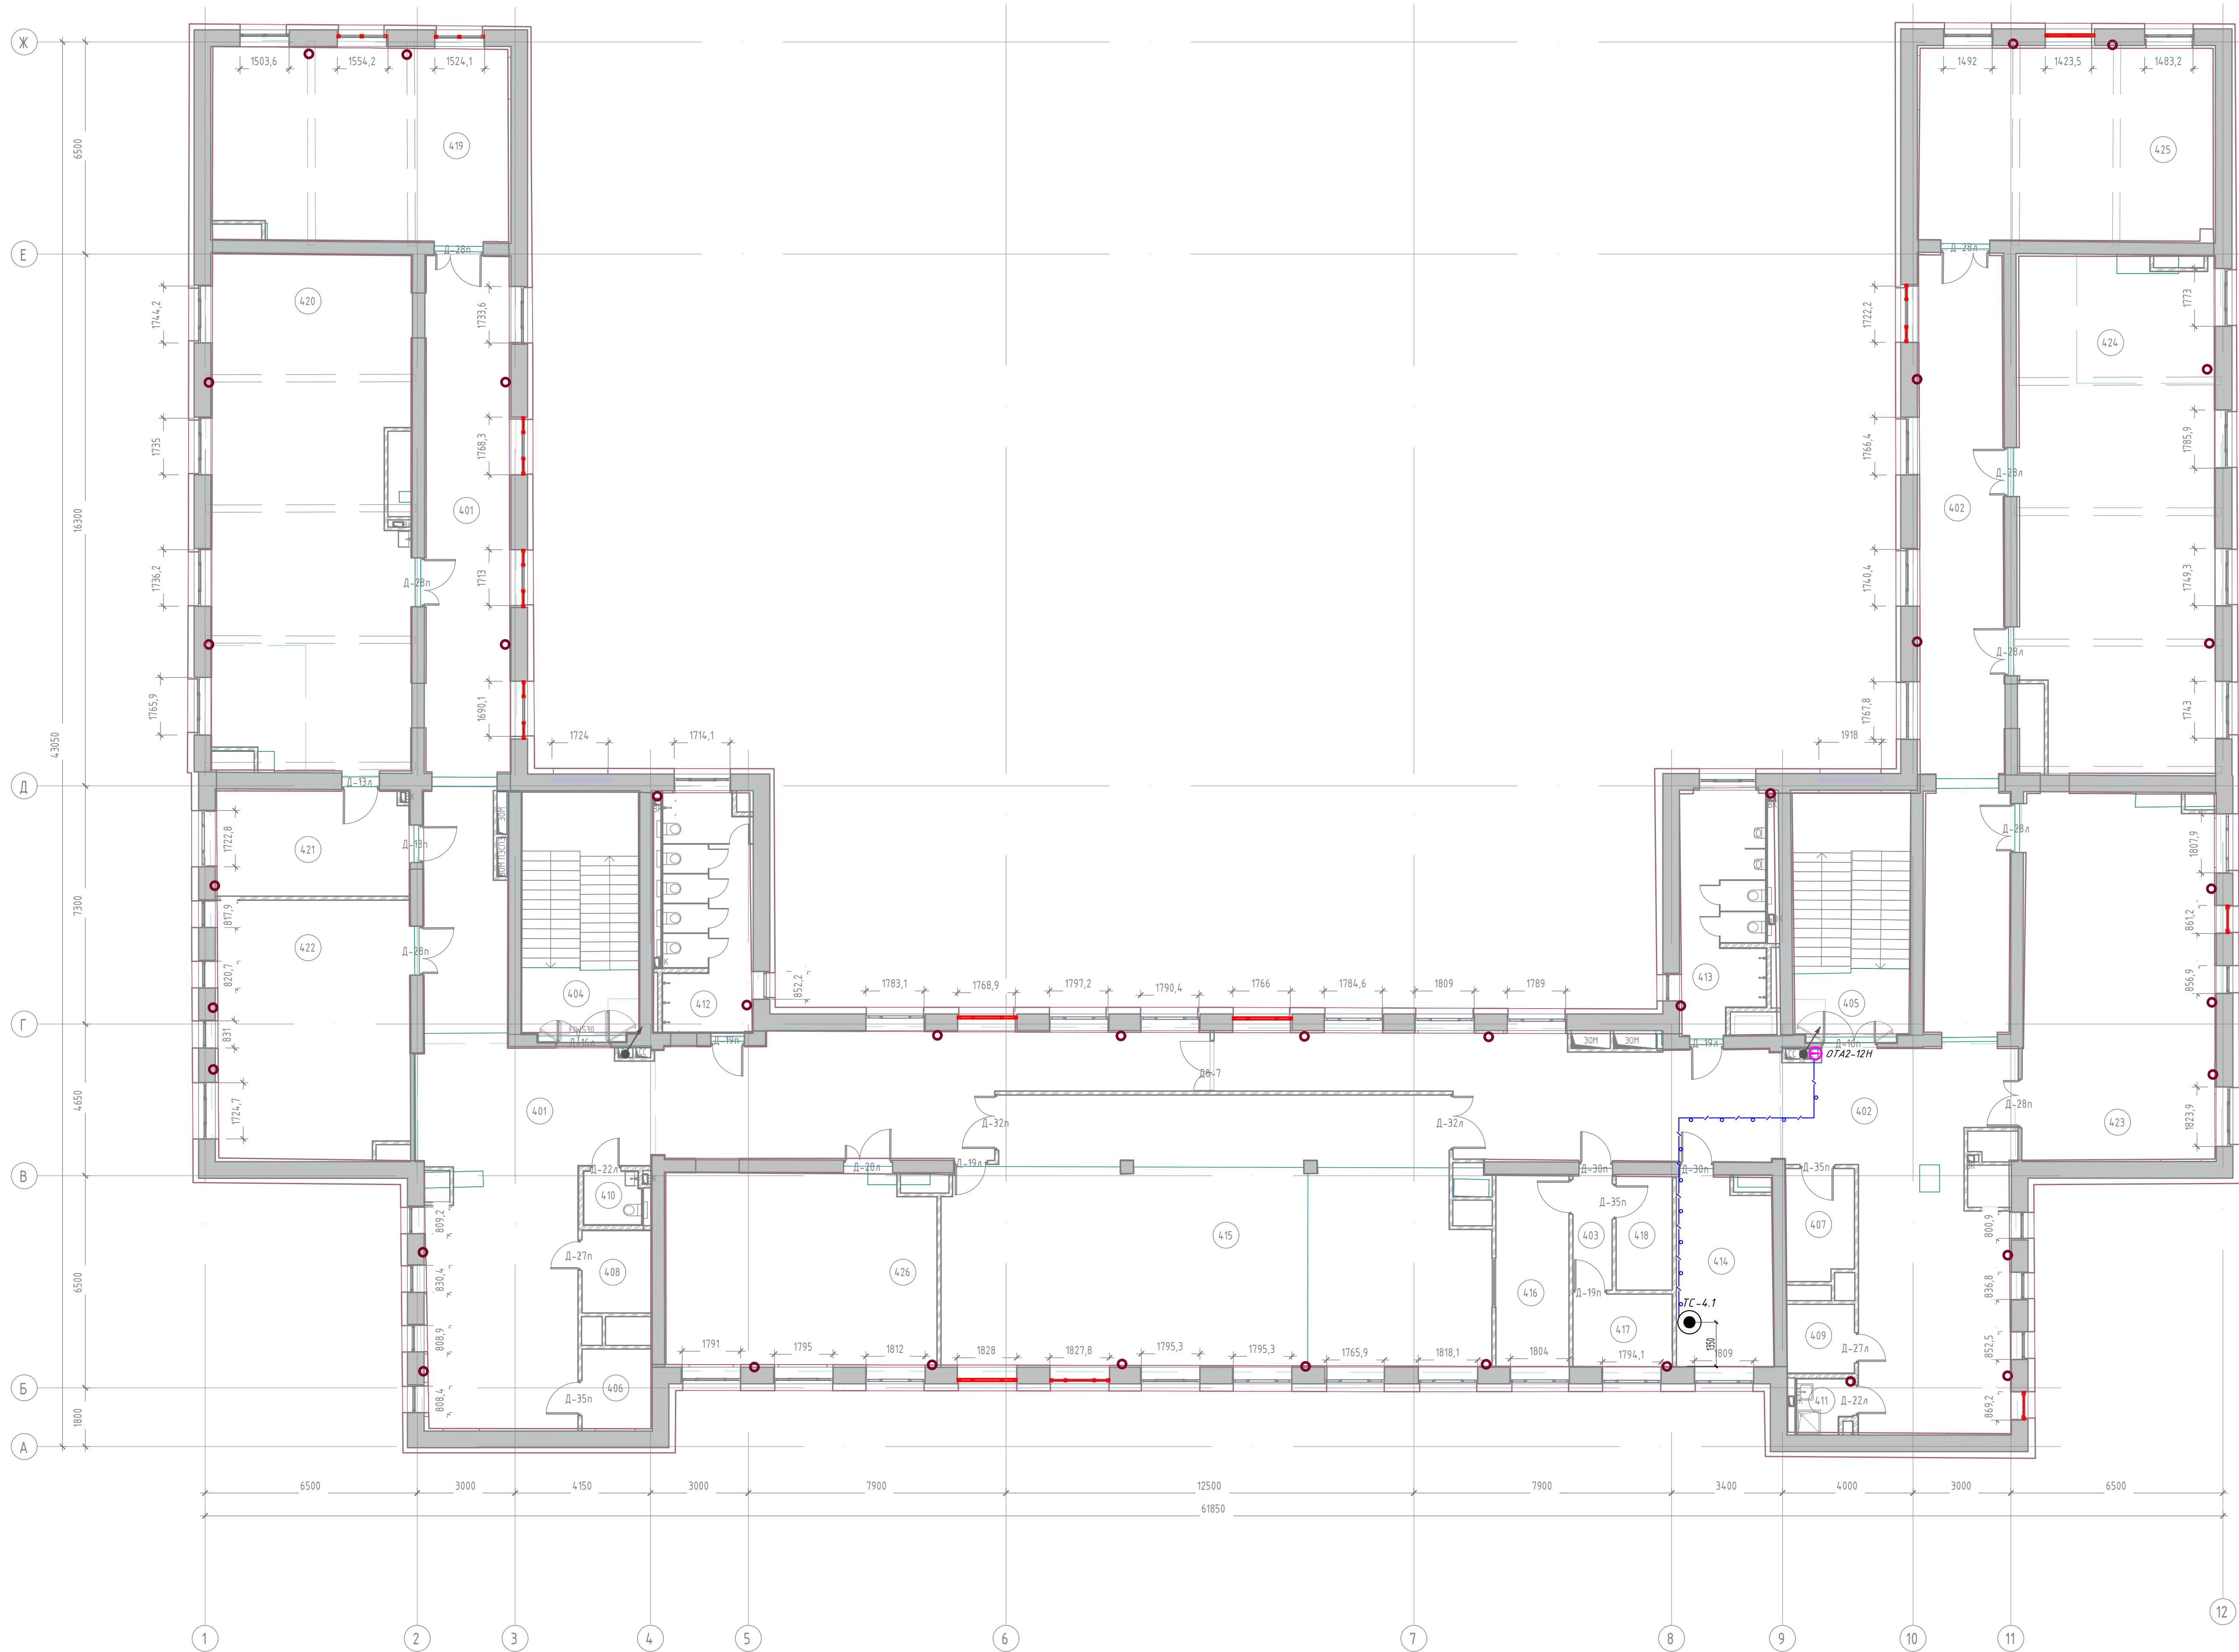


Экспликация помещений 4-го этажа			
Номер помеще-ния	Наименование	Площадь, м²	Кол. поме-ще-ний
401	Коридор с рекреацией	175,9	
402	Коридор с рекреацией	172,6	
403	Танцев	4,2	
404	Лесничная клетка (Тип А)	27,2	
405	Лесничная клетка (Тип А)	27,3	
406	Помещение СС	5,3	В4
407	Помещение СС	7,0	В4
408	Подсобное помещение	5,3	В4
409	Подсобное помещение	4,3	В4
410	Туалет для персонала	2,8	
411	ПМ	2,8	В4
412	Воронка для девочек	19,3	
413	Воронка для мальчиков	18,4	
414	Кабинет для индивидуальных занятий, 8 м.ч. с видеозаписью-наблюдением	16,5	
415	Автомобиль или (с эскалатором в цокольном этаже)	130,7	
416	Технический центр	13,1	В3
417	Архитектурная	6,8	
418	Классовый кабинет	6,0	В4
419	Кабинет математики	53,1	
420	Экспертный кабинет (для изучения особенностей)	93,5	
421	Наблюдательная вышка	19,2	В3
422	Экспертный кабинет (история)	48,6	
423	Кабинет иностранного языка с возможностью деления трансформированной перегородкой на 80 помещений	65,7	
424	Кабинет информатики с возможностью деления трансформированной перегородкой на 80 помещений	92,1	
425	Кабинет русского языка и литературы	53,8	
426	Кабинет русского языка и литературы	48,4	
Итого		1118,0	

- Условные графические обозначения
- розетка телевизионная;
 - ответитель ОТА;
 - телекоммуникационный шкаф;
 - кабель коаксиальный в гофротрубе РК 75-4,8-319на(А)-LSL Tx (75 Ом);
 - кабель коаксиальный в гофротрубе РК 75-7-327на(А)-LSL Tx (75 Ом);
 - кабельная шахта;

Примечание:
1. ТВ розетки устанавливаются в одну розеточную группу РС и ЗОМ согласно приложению.

656/П-24-АНД-Р-ТВ					
Капитальный ремонт Государственного бюджетного общеобразовательного учреждения «Школа №1282 «Сокольники» по адресу: г. Москва, ул. Бардовская, д. 1, корп. 1					
Исполн.	В.П.Р.	Лист	1/10	Дата	07.25
Разработчик	Роман	Иванов	07.25	Технический	Лист
Рисовал	Григорьев	07.25	Система кабельного телевидения	Р	7
Исполн.	Григорьев	07.25	План расположения оборудования СКТ на 4 этаже	Лист	1

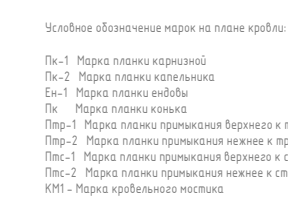[illegible]

-  антенна;
-  кабель коаксиальный в гофротрубе РК 75-7-327нг(А)-LSL Tx (75 Ом);
- кабельная шахта;

1. *Размеры для справки.
2. Мачту М450 крепится к стене надстройки на кровле по месту используя хронитетин.
3. В зоне уверенного приема каналов радиодиффракции.
4. Мачту заземляют к контуру молниезащиты стальным тросом diam. 8,3 мм, устройством молниезащиты смотри части АР и ЭО.
5. Учтено, что мачты, молниезащита учтена разделом РС.
6. Антенна ДНВ диапазона устанавливается на мачте М450, смотри эскиз.
5. После ввода в эксплуатацию в здание отверстие мачты загерметизируют.


Формат А0 альбомная (841x1189,

Шкаф
телекоммуникационный 27U –
УЧО-ТШ-РСО-ДОНМ *

Вид спереди

Вид сзади

27U
26U
25U
24U
23U
22U
21U
20U
19U
18U
17U
16U
15U
14U
13U
12U
11U
10U
9U
8U
7U
6U
5U
4U
3U
2U
1U

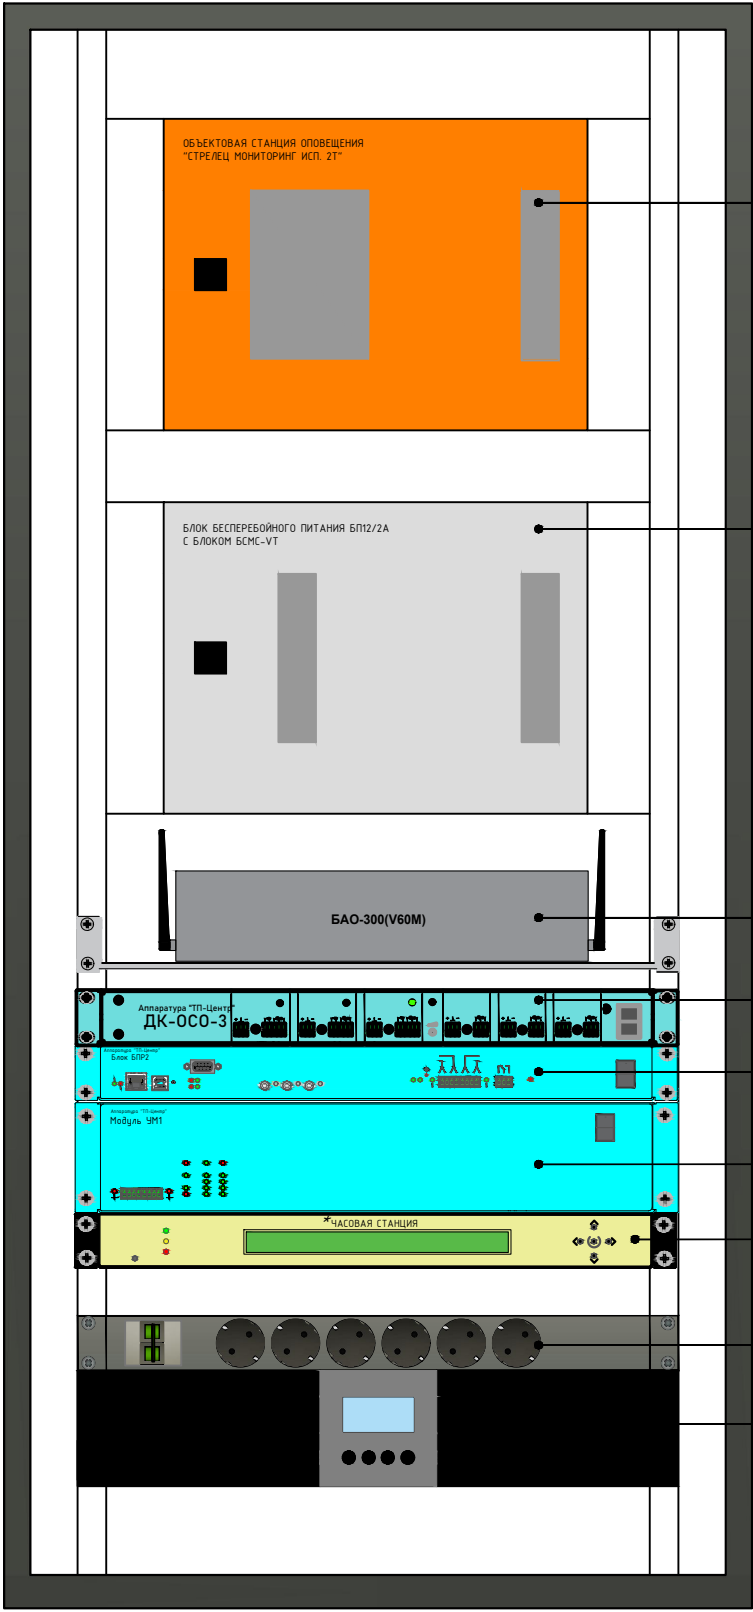

Объектовая станция
"Стрелец-Мониторинг" исп.
2Т *

Блок управления
оповещением БСНС-VT исп.К
с БП *

Блок акустического оповещения
БАО-300 (V60M) *


Блок коммутации сигналов
ДК-ОСО-3 *

Трёхпрограммный
радиотрансляционный узел
Блок БП2-BF3/50-ABT2 *
Усилитель мощности
трансляционный Модуль УМ1 *

Часовая станция**

Блок розеток *

Источник бесперебойного *
питания

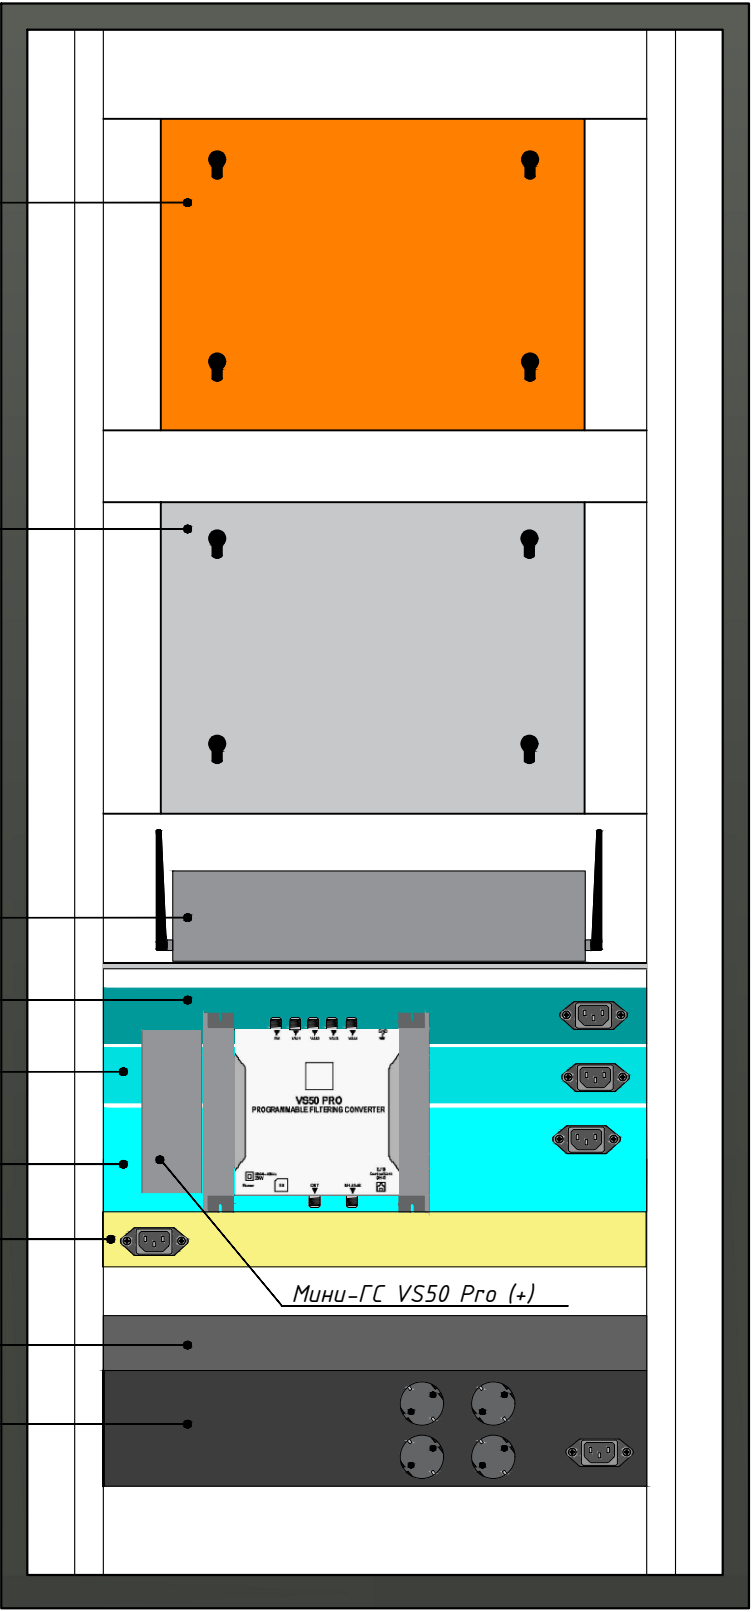

Мини-ТС VS50 Pro (+)

Примечание:

*Учтено томом 696/П-24-АНО-Р-РФ
**Учтено томом 696/П-24-АНО-Р-ЧФ

Согласовано				
Взам.инв.Н				
Подпись и дата				
инв.Нподл.				

						696/П-24-АНО-Р-ТВ			
						Капитальный ремонт Государственного Бюджетного Общеобразовательного Учреждения города Москвы «Школа №1282 «Сокольники» по адресу: г. Москва, ул. Барболина, д. 1, корп. 1			
Изм.	Кол.уч	Лист	Ндок	Подпись	Дата	Система кабельного телевидения	Стадия	Лист	Листов
Разработал	Коняев				07.26		Р	9	
Проверил	Гулько				07.26				
						Шкаф ТШ-РСО-ДОНМ. План расположения оборудования в шкафу.			
Н.контр.	Гулько				07.26				

Согласовано		
Взам.инв.Н		
Подпись и дата		
инв.Нподл.		

Обозначение кабеля	Трасса		Кабель		
	Начало	Конец	Марка	Кол.кабелей, число и сечение жил	Длина, м
1	Антенна ДМВ	Мини-ГС	PK 75-7-327нз(А)-LSL Tx (75 Ом)		70
2	Мини-ГС	ОТА4-18Н	PK 75-7-327нз(А)-LSL Tx (75 Ом)		45
3	ОТА4-18Н	ОТА2-16Н	PK 75-7-327нз(А)-LSL Tx (75 Ом)		5
4	ОТА2-16Н	ОТА2-14Н	PK 75-7-327нз(А)-LSL Tx (75 Ом)		5
5	ОТА2-14Н	ОТА2-12Н	PK 75-7-327нз(А)-LSL Tx (75 Ом)		5
6	ОТА4-18Н	ТС-1.1	PK 75-4,8-319нз(А)-LSL Tx (75 Ом)		50
7	ОТА4-18Н	ТС-1.2	PK 75-4,8-319нз(А)-LSL Tx (75 Ом)		35
8	ОТА4-18Н	ТС-1.3	PK 75-4,8-319нз(А)-LSL Tx (75 Ом)		30
9	ОТА4-18Н	ТС-1.4	PK 75-4,8-319нз(А)-LSL Tx (75 Ом)		20
10	ОТА2-16Н	ТС-2.1	PK 75-4,8-319нз(А)-LSL Tx (75 Ом)		70
11	ОТА2-16Н	ТС-2.2	PK 75-4,8-319нз(А)-LSL Tx (75 Ом)		25
12	ОТА2-14Н	ТС-3.1	PK 75-4,8-319нз(А)-LSL Tx (75 Ом)		30
13	ОТА2-12Н	ТС-4.1	PK 75-4,8-319нз(А)-LSL Tx (75 Ом)		25

*Кабельный журнал не является основанием для нарезки кабеля.

						696/П-24-АНО-Р-ТВ			
						Капитальный ремонт Государственного Бюджетного Общеобразовательного Учреждения города Москвы «Школа №1282 «Сокольники» по адресу: г. Москва, ул. Барболина, д. 1, корп. 1			
Изм.	Кол.уч	Лист	Ндок	Подпись	Дата	Система кабельного телевидения	Стадия	Лист	Листов
Разработал	Коняев				07.26		Р	10	
Проверил	Гулько				07.26	Кабельный журнал			
Н.контр.	Гулько				07.26				

Согласовано:

№ отд. долж.

Подпись

Дата

Изм. № подл.

Подпись и дата

Взам. инв. №

№ п/п	Наименование и техническая характеристика	Тип, марка, обозначение документа, опросного листа	Код оборудования, изделия, материала	Завод изготовитель	Единица измерения	Количество	Масса единицы, кг	Примечание
	Система кабельного телевидения							
	Оборудование							
	1. Мини головная станция VS50 Pro	Мини-ГС		ООО «Корпорация ИнформТелеСеть»	шт.	1		
	2. Антенна ДМВ диапазона	ЕВ45LTE		САТЕЛЛИТ ЛТД	шт.	1		
	3. Грозозащита 75 Ом	ОВР		САТЕЛЛИТ ЛТД	шт.	1		
	4. Ответвитель абонентский на 2 отвода, серия Н	ОТА2-12Н		САТЕЛЛИТ ЛТД	шт.	1		
	5. Ответвитель абонентский на 2 отвода, серия Н	ОТА2-14Н		САТЕЛЛИТ ЛТД	шт.	1		
	6. Ответвитель абонентский на 2 отвода, серия Н	ОТА2-16Н		САТЕЛЛИТ ЛТД	шт.	1		
	7. Ответвитель абонентский на 4 отвода, серия Н	ОТА4-18Н		САТЕЛЛИТ ЛТД	шт.	1		
	8. Розетка TV оконечная в стену, "Avanti", "Белое облако"	4400503		ЗАО «ДКС»	шт.	8		
	9. Разъем ВЧ «F-разъем» на кабель РК75-4,8	DV55		САТЕЛЛИТ ЛТД	шт.	8		
	10. Разъем ВЧ «F-разъем» на кабель РК75-7	DV54		САТЕЛЛИТ ЛТД	шт.	11		
	11. Нагрузка согласованная 75 Ом	DV24		САТЕЛЛИТ ЛТД	шт.	2		
	Материалы							
	1. Труба ПНД гофрированная легкая, с зондом, без галогена 20 мм 20120HF-GR	20120HF-GR		Ecoplast	м	215		
	2. Труба гладкая самозатухающая «Т ПВХ» 20 мм	РТК-2-3-02		РТК	м	200		
	3. Скоба оцинкованная с одним отверстием, для трубы D20 мм	43720		Ecoplast	шт.	1245		
	Кабельные изделия							
	1. Коаксиальный кабель 75 Ом	РК 75-4,8-319нг(А)-LSLTx		Паритет	м	285		
	2. Коаксиальный кабель 75 Ом	РК 75-7-327нг(А)-LSLTx		Паритет	м	130		

Изм.

Разработал

Проверил

Н.контр.

Кол.у

Коняев

Гулько

Гулько

Лист

№док.

Подпись







Дата

07.26

07.26

07.26

696/П-24-АНО-Р-ТВ.СО

Стадия

Р

Лист

1

Листов

1

Спецификация

Система кабельного телевидения

