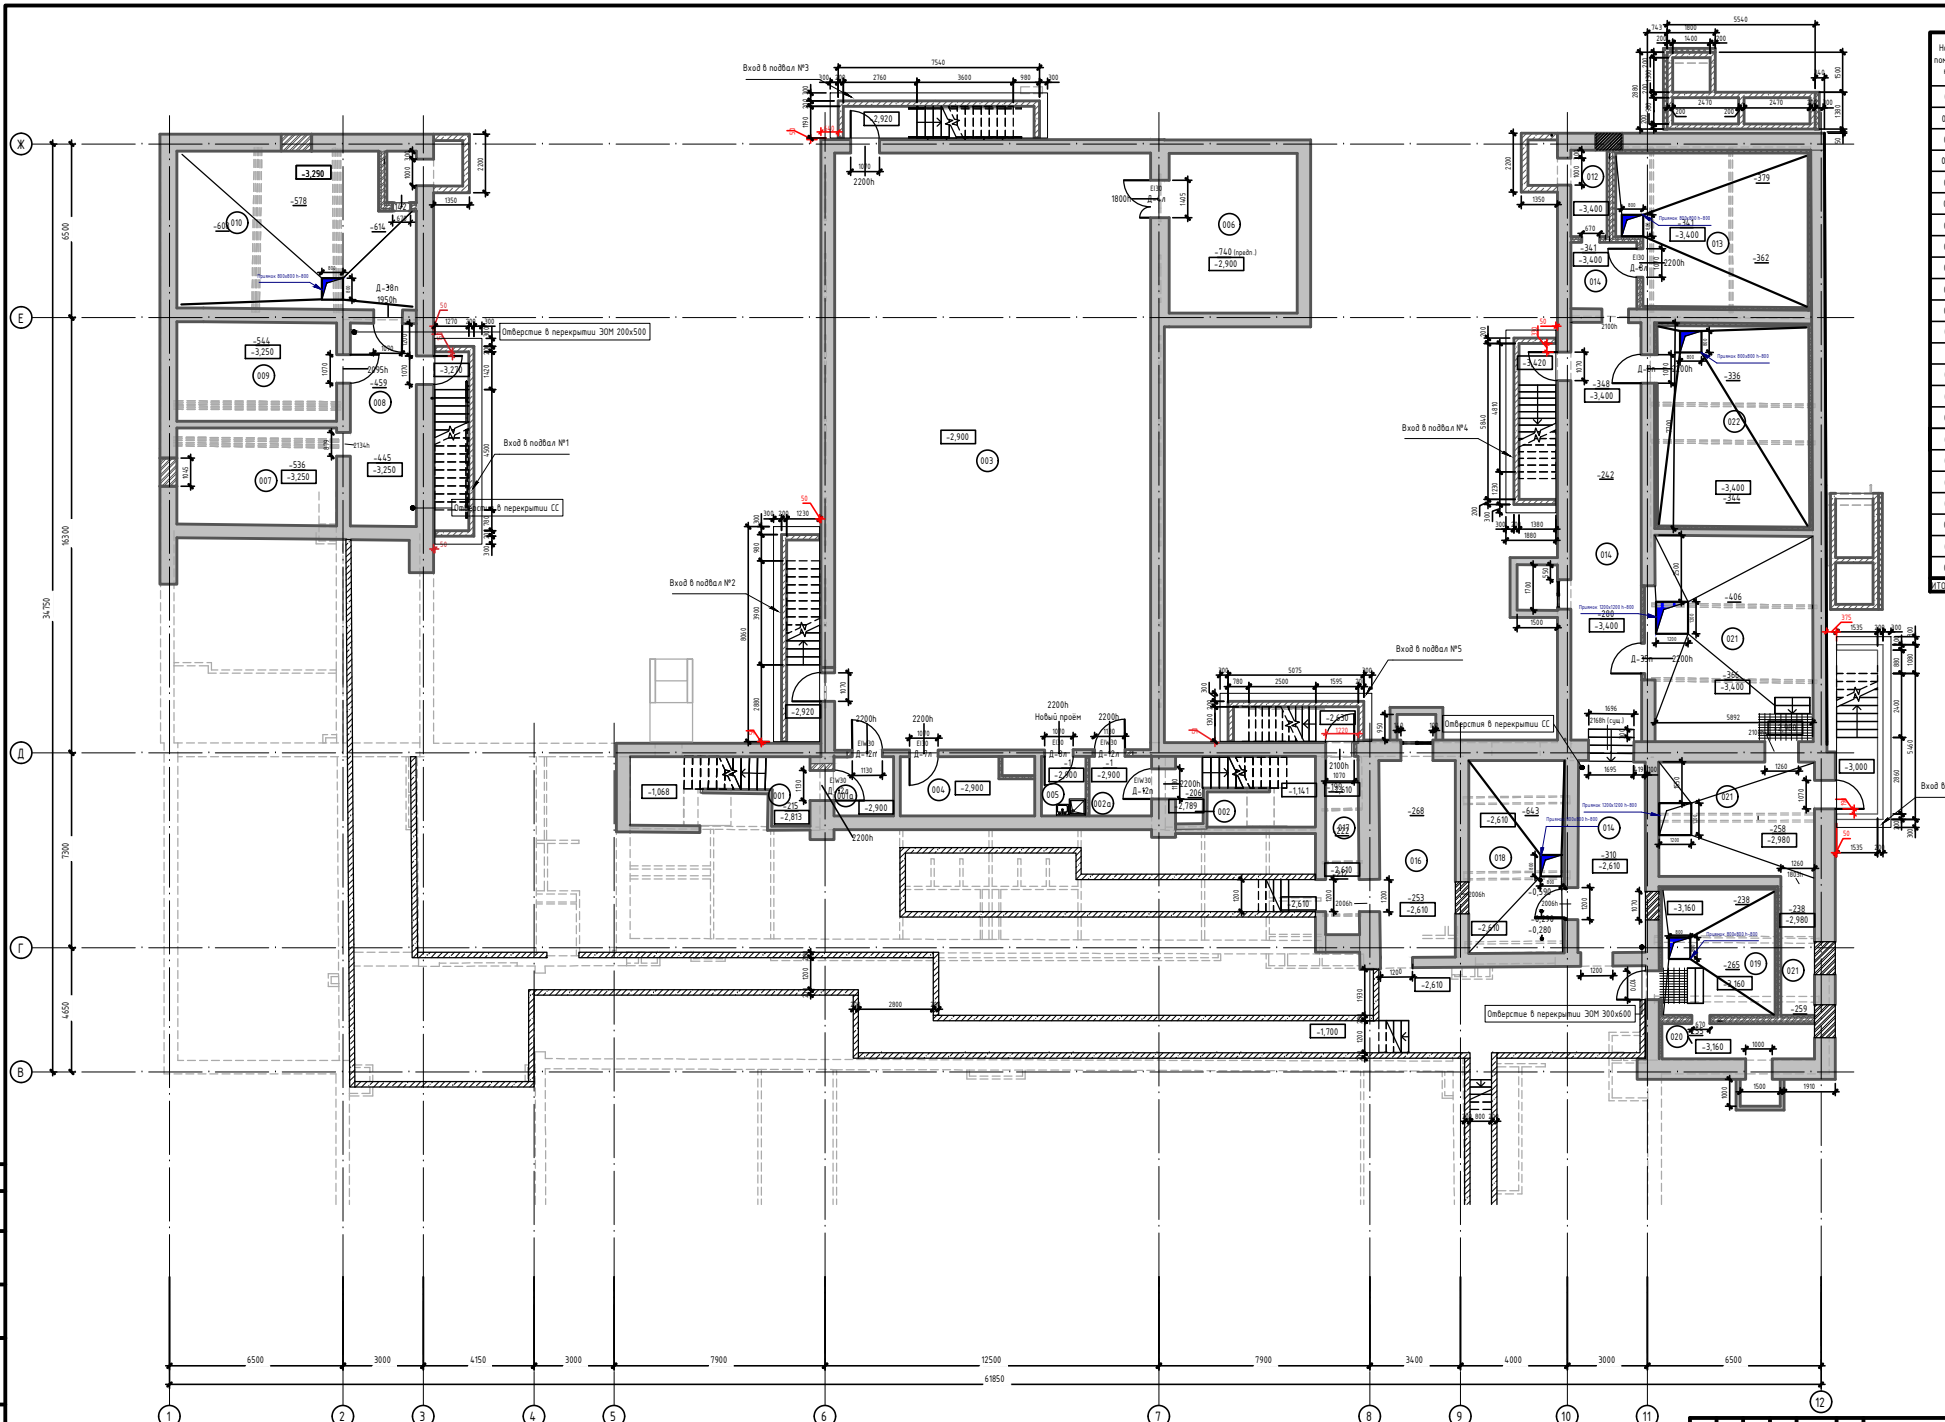


Экспликация помещений подвала

Номер помещения	Наименование	Площадь, м²	Категория помещения
001	Техническая лестница	13,7	
001а	Тамбур-шлюз 1-го типа	4,9	
002	Техническая лестница	9,8	
002а	Тамбур-шлюз 1-го типа	5,0	
003	Спортивный зал	262,5	
004	Снарядная	10,1	В3
005	ПЫИ	3,5	
006	Снарядная	28,0	В3
007	Коридор	21,0	
008	Коридор	17,9	
009	Кладовая	21,4	В3
010	Венткамера	50,4	В4
011	Форкамера	Не окружено	В4
012	Форкамера	4,0	В4
013	Венткамера	38,9	В4
014	Коридор	57,0	
016	Коридор	19,3	
017	Коридор	7,4	
018	Насосная	24,0	В4
019	Венткамера	20,0	В4
020	Форкамера	5,3	В4
021	ИТП	45,8	Д
022	Венткамера	42,7	В4
ИТОГО:		712,7	

Условные обозначения:

-3,160 – отметка уровня чистового пола

-255 – отметка низа перекрытия

– конструкции, расположенные выше плоскости сечения вида

Изм.	Кол.уч.	Лист	№док.	Подп.	Дата
Разработал		Ихонтова			06/26/24
Проверил		Колобина			06/26/24
ГИП		Гулько			06/26/24
Норм.контр.		Быкодова			06/26/24

696/П-24-АНО – АР

Капитальный ремонт Государственного бюджетного общеобразовательного учреждения города Москвы Школа №1282 Сокольники по адресу: г. Москва, ул. Барболина, д.1, корп.1

Капитальный ремонт

Стадия	Лист	Листов
Р	03	

План подвала М 1:100 Кладочный

ООО "ПРОЕКТ+"

Формат А1А

Согласовано

Взам. инв. №

Подп. и дата

Инв. № подл.