План демонтажа подвального этажа

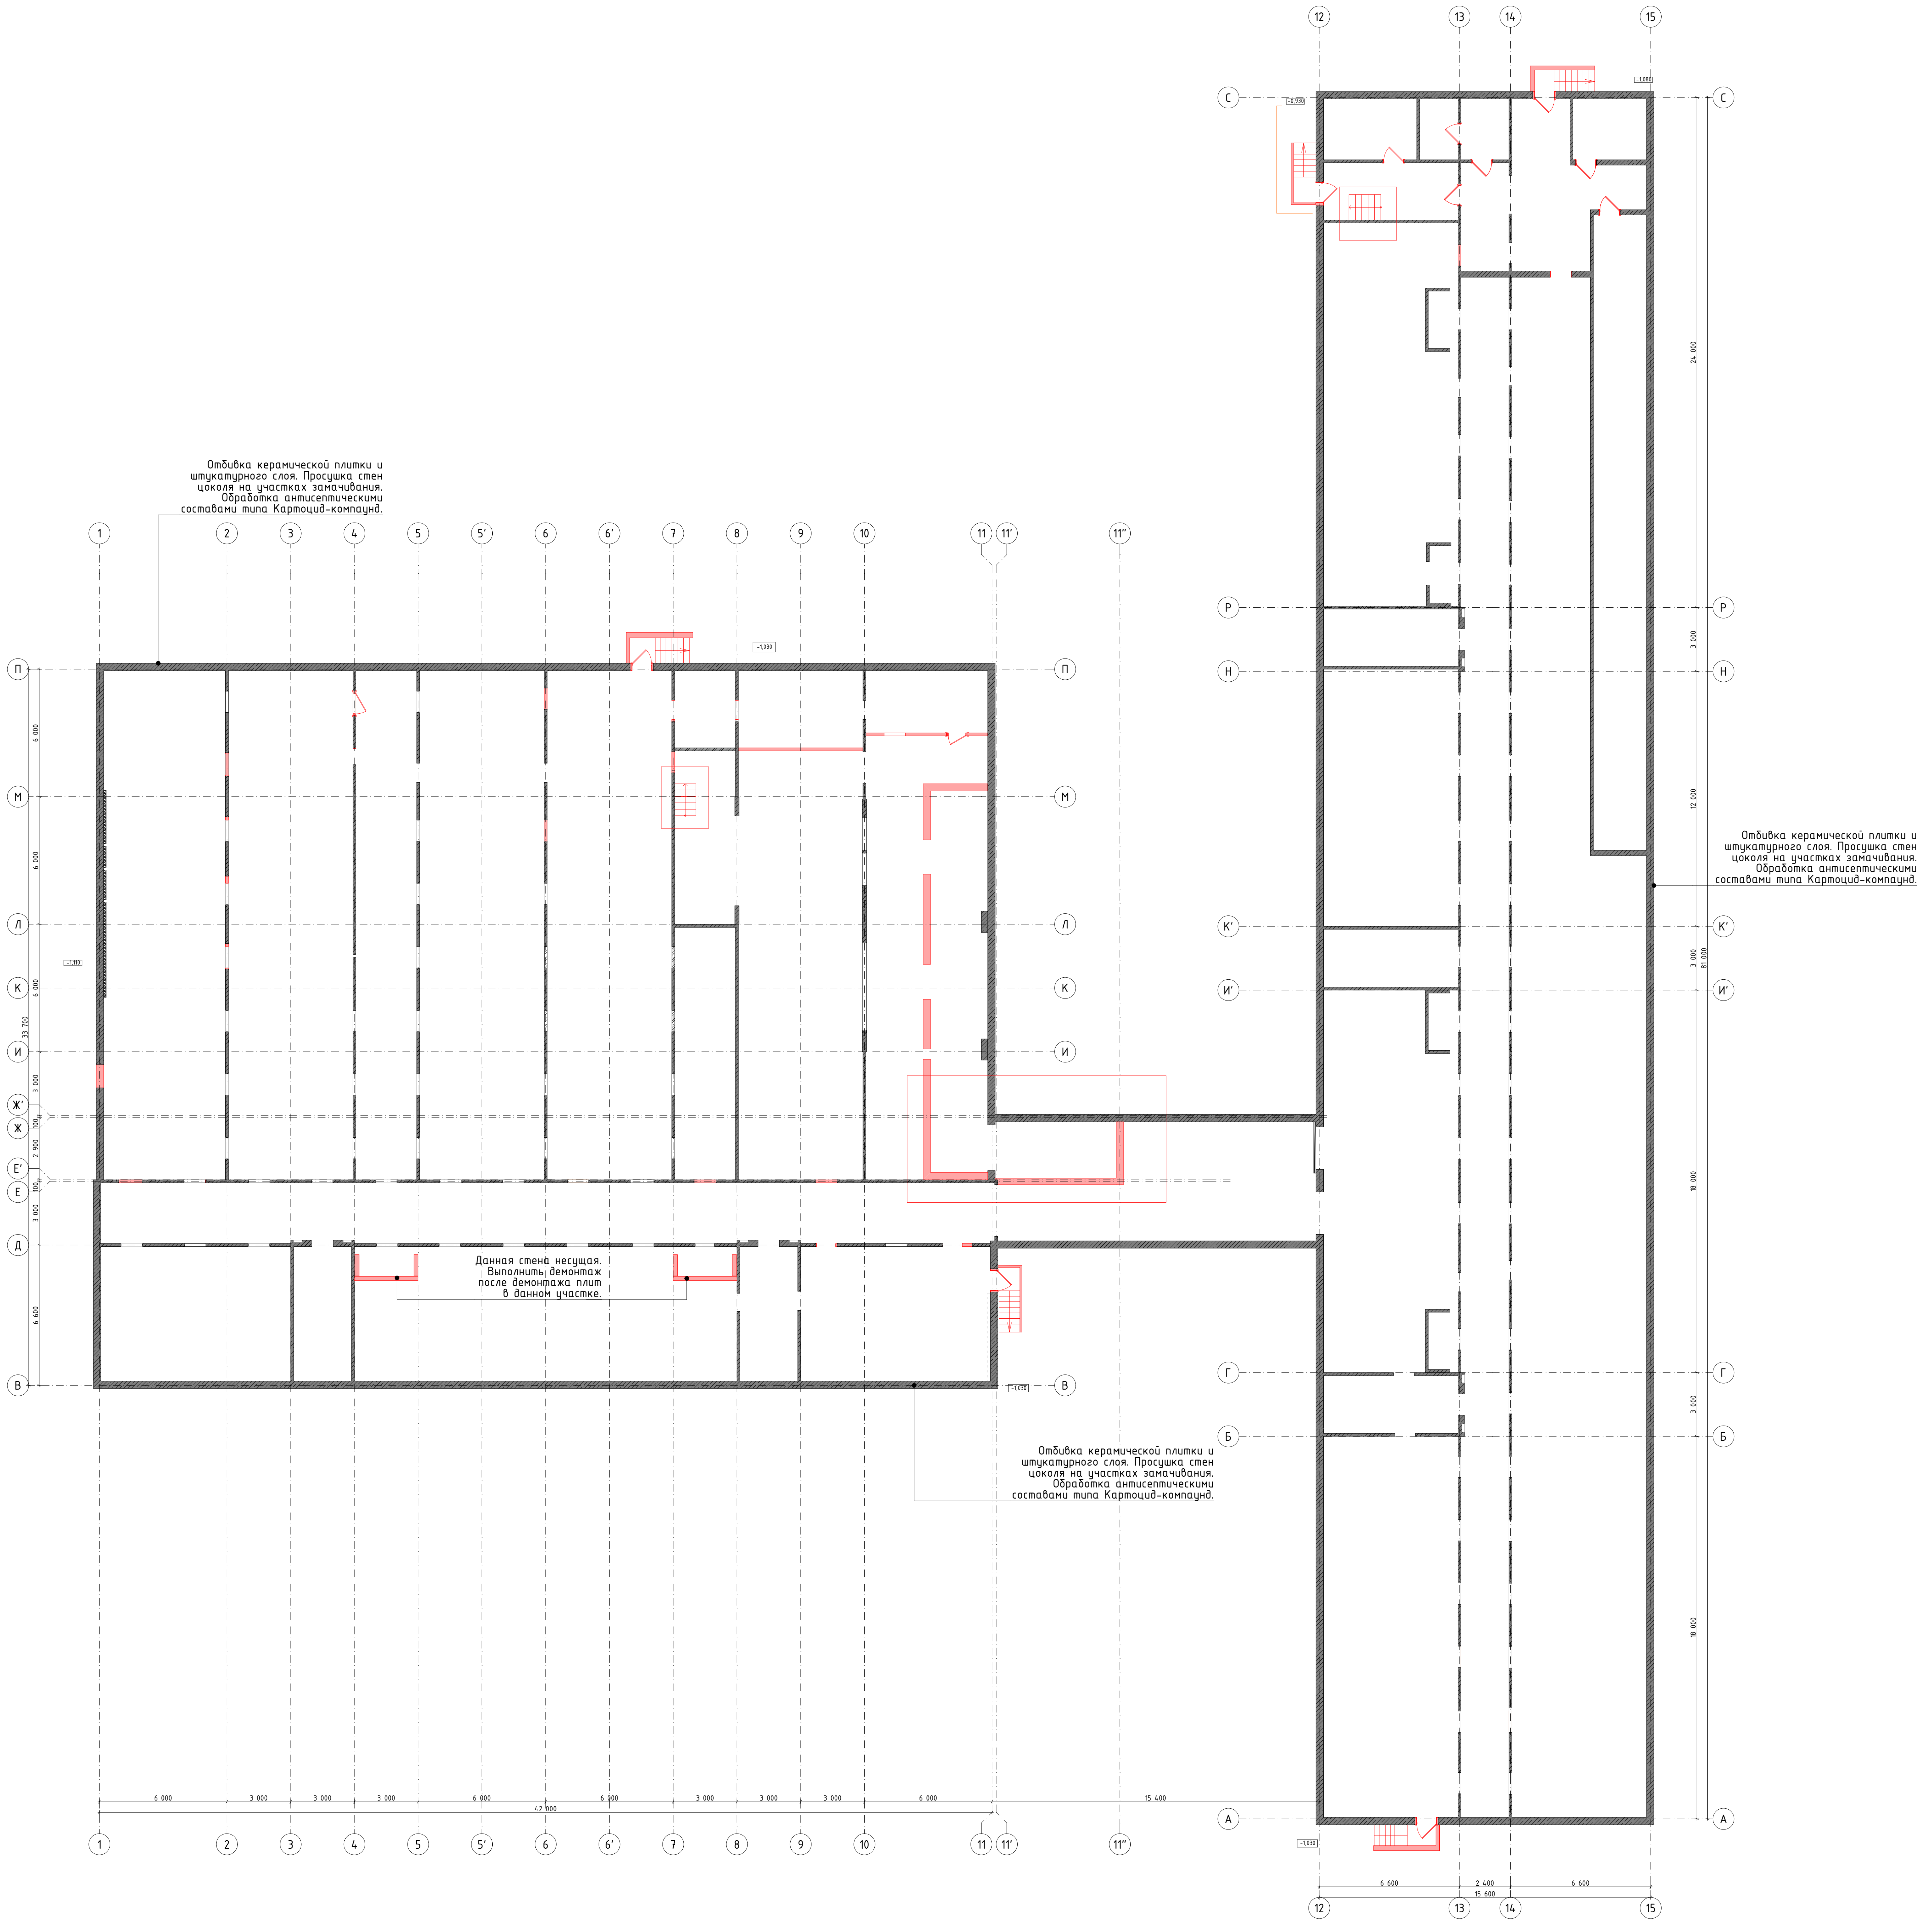

Отбивка керамической плитки и штукатурного слоя. Просушка стен цоколя на участках замачивания. Обработка антисептическими составами типа Картоцид-компаунд.

Данная стена несущая. Выполнить демонтаж после демонтажа плит в данном участке.

Отбивка керамической плитки и штукатурного слоя. Просушка стен цоколя на участках замачивания. Обработка антисептическими составами типа Картоцид-компаунд.

Отбивка керамической плитки и штукатурного слоя. Просушка стен цоколя на участках замачивания. Обработка антисептическими составами типа Картоцид-компаунд.

Условные обозначения

▨ – сущ. стена Ж/Б

▨ – сущ. кирпичная перегородка

🟥 – демонтируемые стены/перегородки

– демонтаж дверей

– демонтаж лестниц

ПРИМЕЧАНИЕ:
1. Наружные работы по фасаду:
- Выполнить отбивку керамической плитки и штукатурного слоя;
- Выполнить просушку стен цоколя на участках замачивания, обработать антисептическими составами типа Картоцид-компаунд.

(Возможна корректировка проекта после прохождения «МГЭ» Московской Государственной Экспертизы)

0,000=168,265

						ГИП-28/24-Р-АР		
Изм.	Кол.уч.	Лист	№Док.	Подп.	Дата	ГБОУ Школа № 218, расположенная по адресу: г. Москва, ул. Вучетича, д. 6		
Разработал	Белова Е.С.				02.25	Средняя общеобразовательная школа	Стадия	Лист	Листов
Проверил	Дубинин С.В.				02.25		П	3	6
ГАП	Дубинин С.В.				02.25				
ГИП	Гущин А.В.				02.25	План демонтажа подвального этажа	И-ГРУПП ПРОЕКТНО-СТРОИТЕЛЬНАЯ КОМПАНИЯ		
Н.контроль	Шукшин В.В.				02.25				

План демонтажа 1 этажа

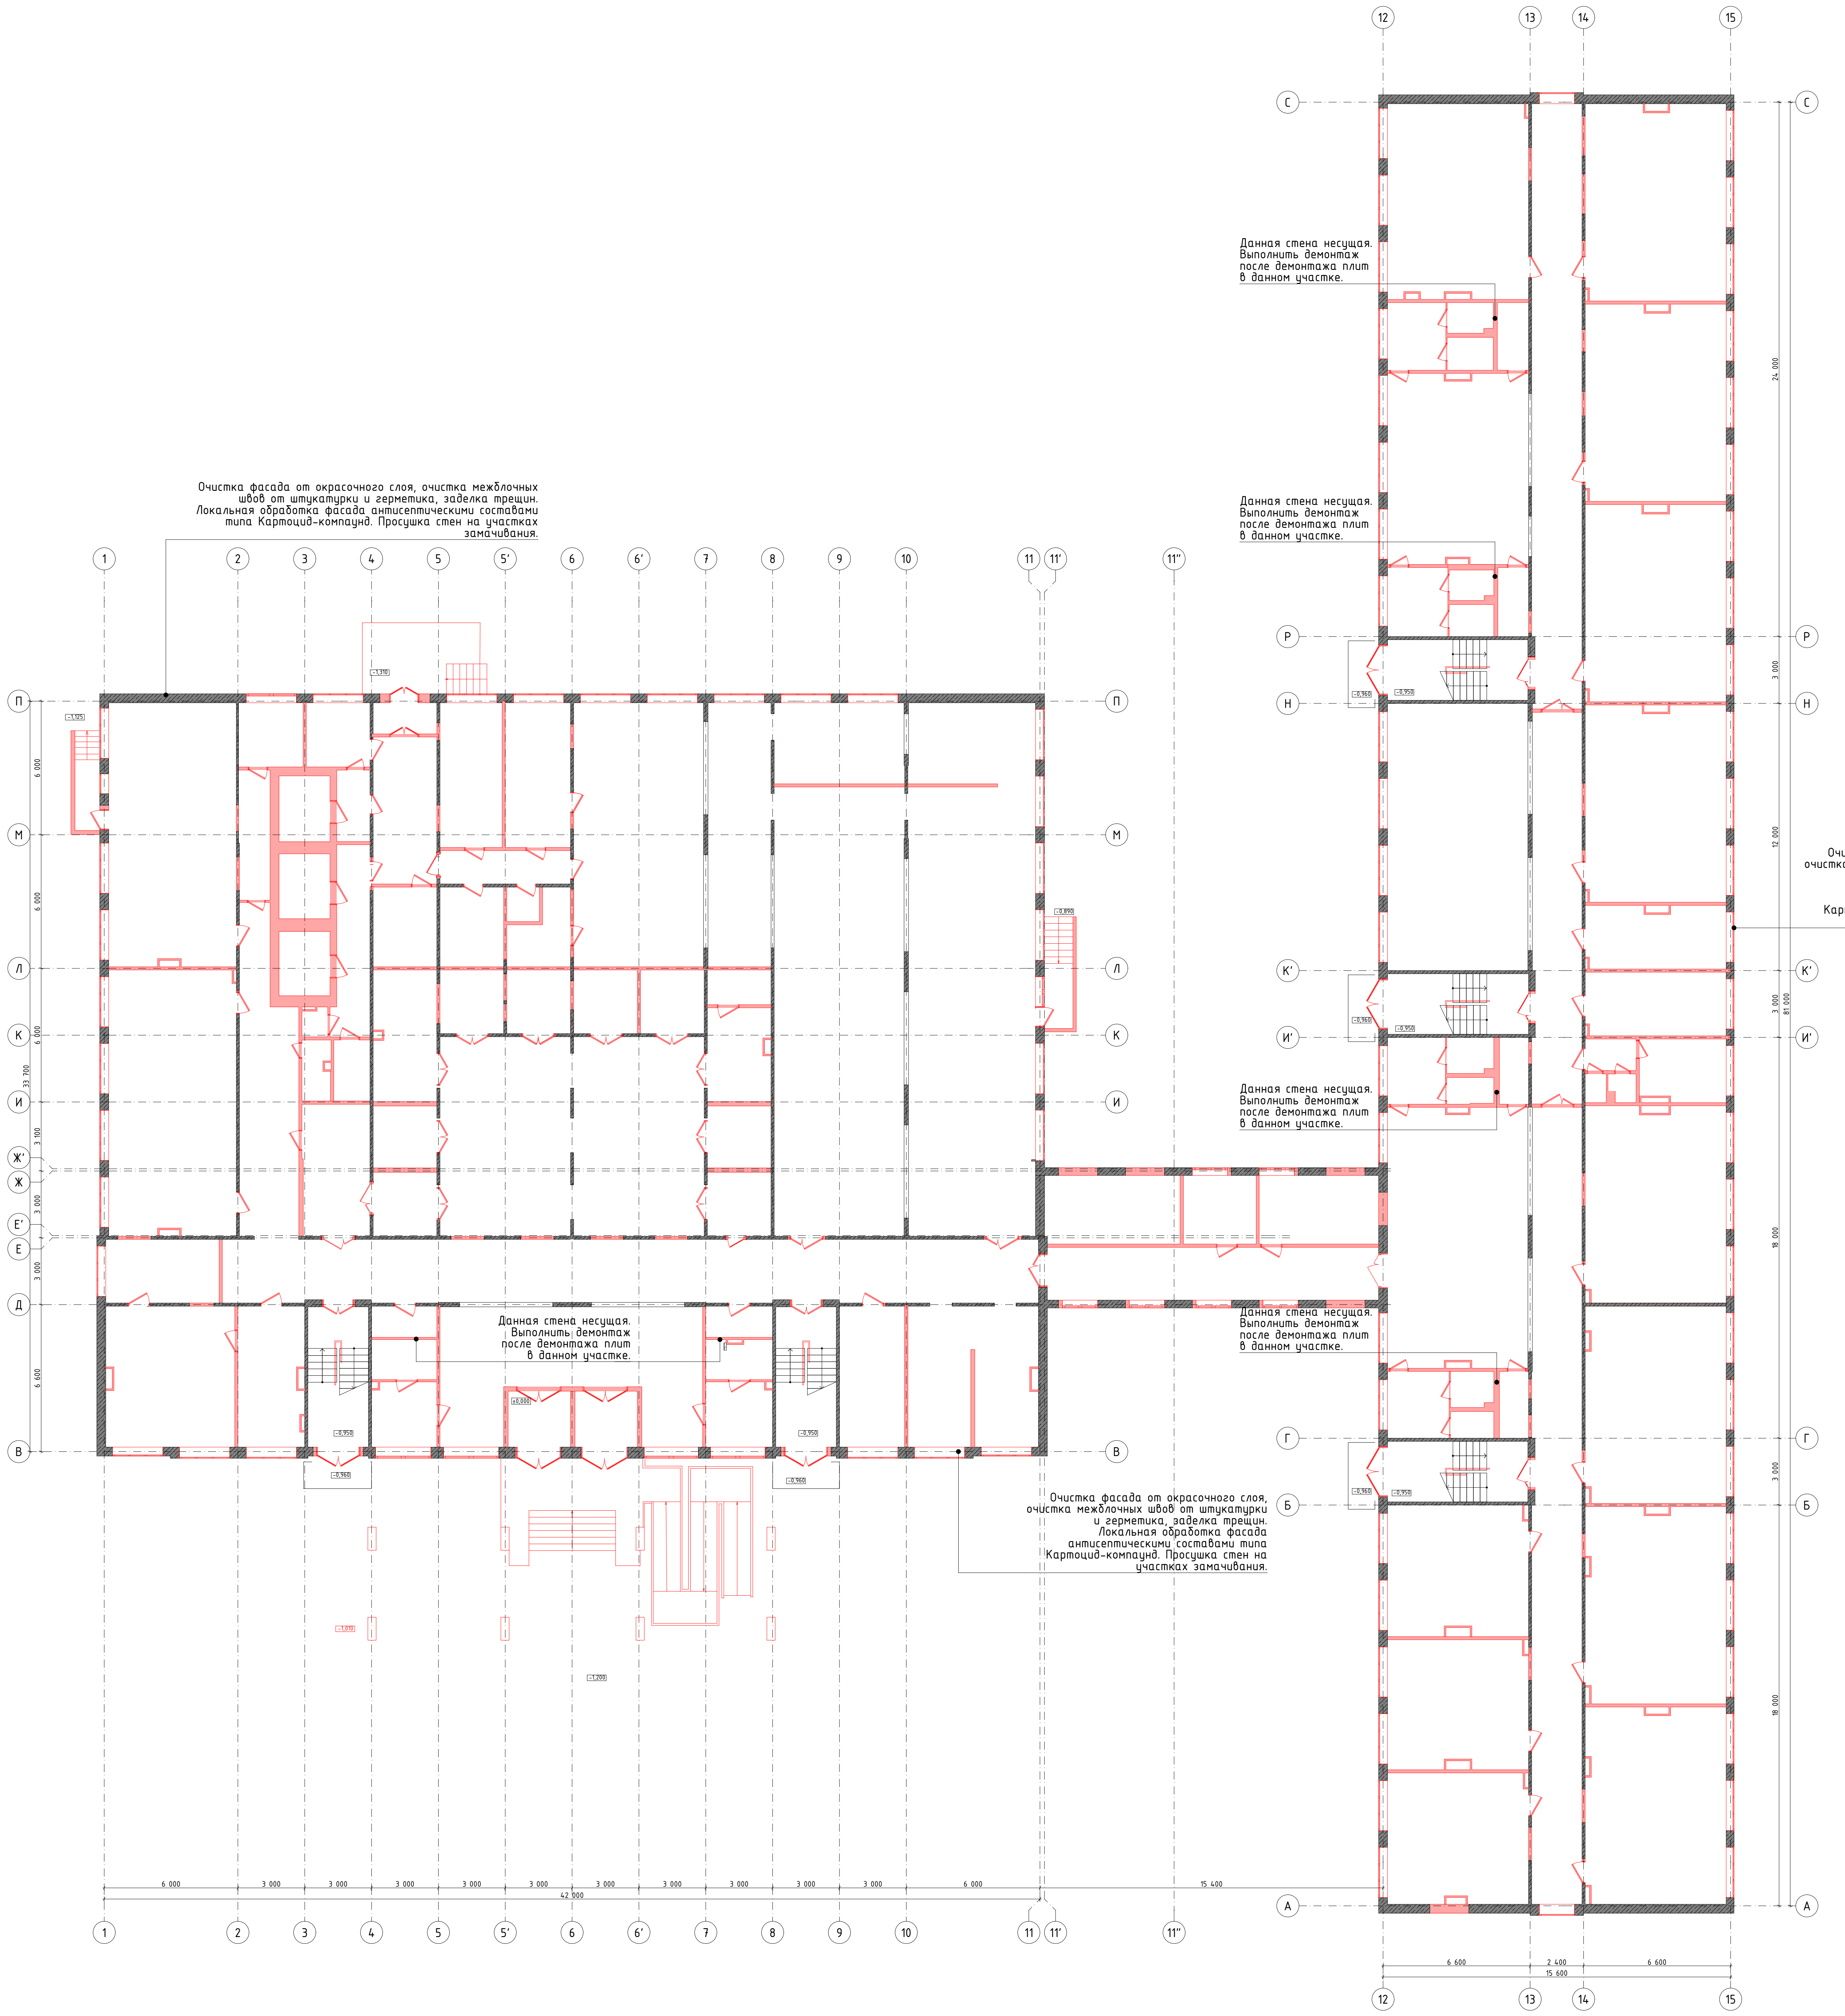

Очистка фасада от окрасочного слоя, очистка межблочных швов от штукатурки и герметика, заделка трещин. Локальная обработка фасада антисептическими составами типа Картоцид-компаунд. Просушка стен на участках замачивания.

Данная стена несущая. Выполнить демонтаж после демонтажа плит в данном участке.

Данная стена несущая. Выполнить демонтаж после демонтажа плит в данном участке.

Очистка фасада от окрасочного слоя, очистка межблочных швов от штукатурки и герметика, заделка трещин. Локальная обработка фасада антисептическими составами типа Картоцид-компаунд. Просушка стен на участках замачивания.

Данная стена несущая. Выполнить демонтаж после демонтажа плит в данном участке.

Данная стена несущая. Выполнить демонтаж после демонтажа плит в данном участке.

Данная стена несущая. Выполнить демонтаж после демонтажа плит в данном участке.

Очистка фасада от окрасочного слоя, очистка межблочных швов от штукатурки и герметика, заделка трещин. Локальная обработка фасада антисептическими составами типа Картоцид-компаунд. Просушка стен на участках замачивания.

Условные обозначения

▨	– сущ. стена Ж/Б
🟥	– демонтируемые стены/перегородки
⌒	– демонтаж сущ. дверей
▤	– демонтаж лестниц
▭	– демонтаж сущ. окон

ПРИМЕЧАНИЕ:

1. Наружные работы по фасаду:
- Очистка фасада от окрасочного слоя, очистка межблочных швов от штукатурки и герметика, заделка трещин.
- Локальная обработка фасада антисептическими составами типа Картоцид-компаунд.
- Просушка стен на участках замачивания.

(Возможна корректировка проекта после прохождения «МГЭ» Московской Государственной Экспертизы)

0,000=168,265

ГИП-28/24-Р-АР

ГБОУ Школа № 218, расположенная по адресу:
г. Москва, ул. Вучетича, д. 6

Изм.	Кол.уч.	Лист	№Док.	Подп.	Дата
Разработал		Белова Е.С.			02.25
Проверил		Дубинин С.В.			02.25
ГАП		Дубинин С.В.			02.25
ГИП		Гущин А.В.			02.25
Н.контроль		Шукшин В.В.			02.25

Средняя общеобразовательная школа

Стадия	Лист	Листов
П	4	6

План демонтажа 1 этажа

И-ГРУПП
ПРОЕКТНО-СТРОИТЕЛЬНАЯ КОМПАНИЯ

План демонтажа 2 этажа

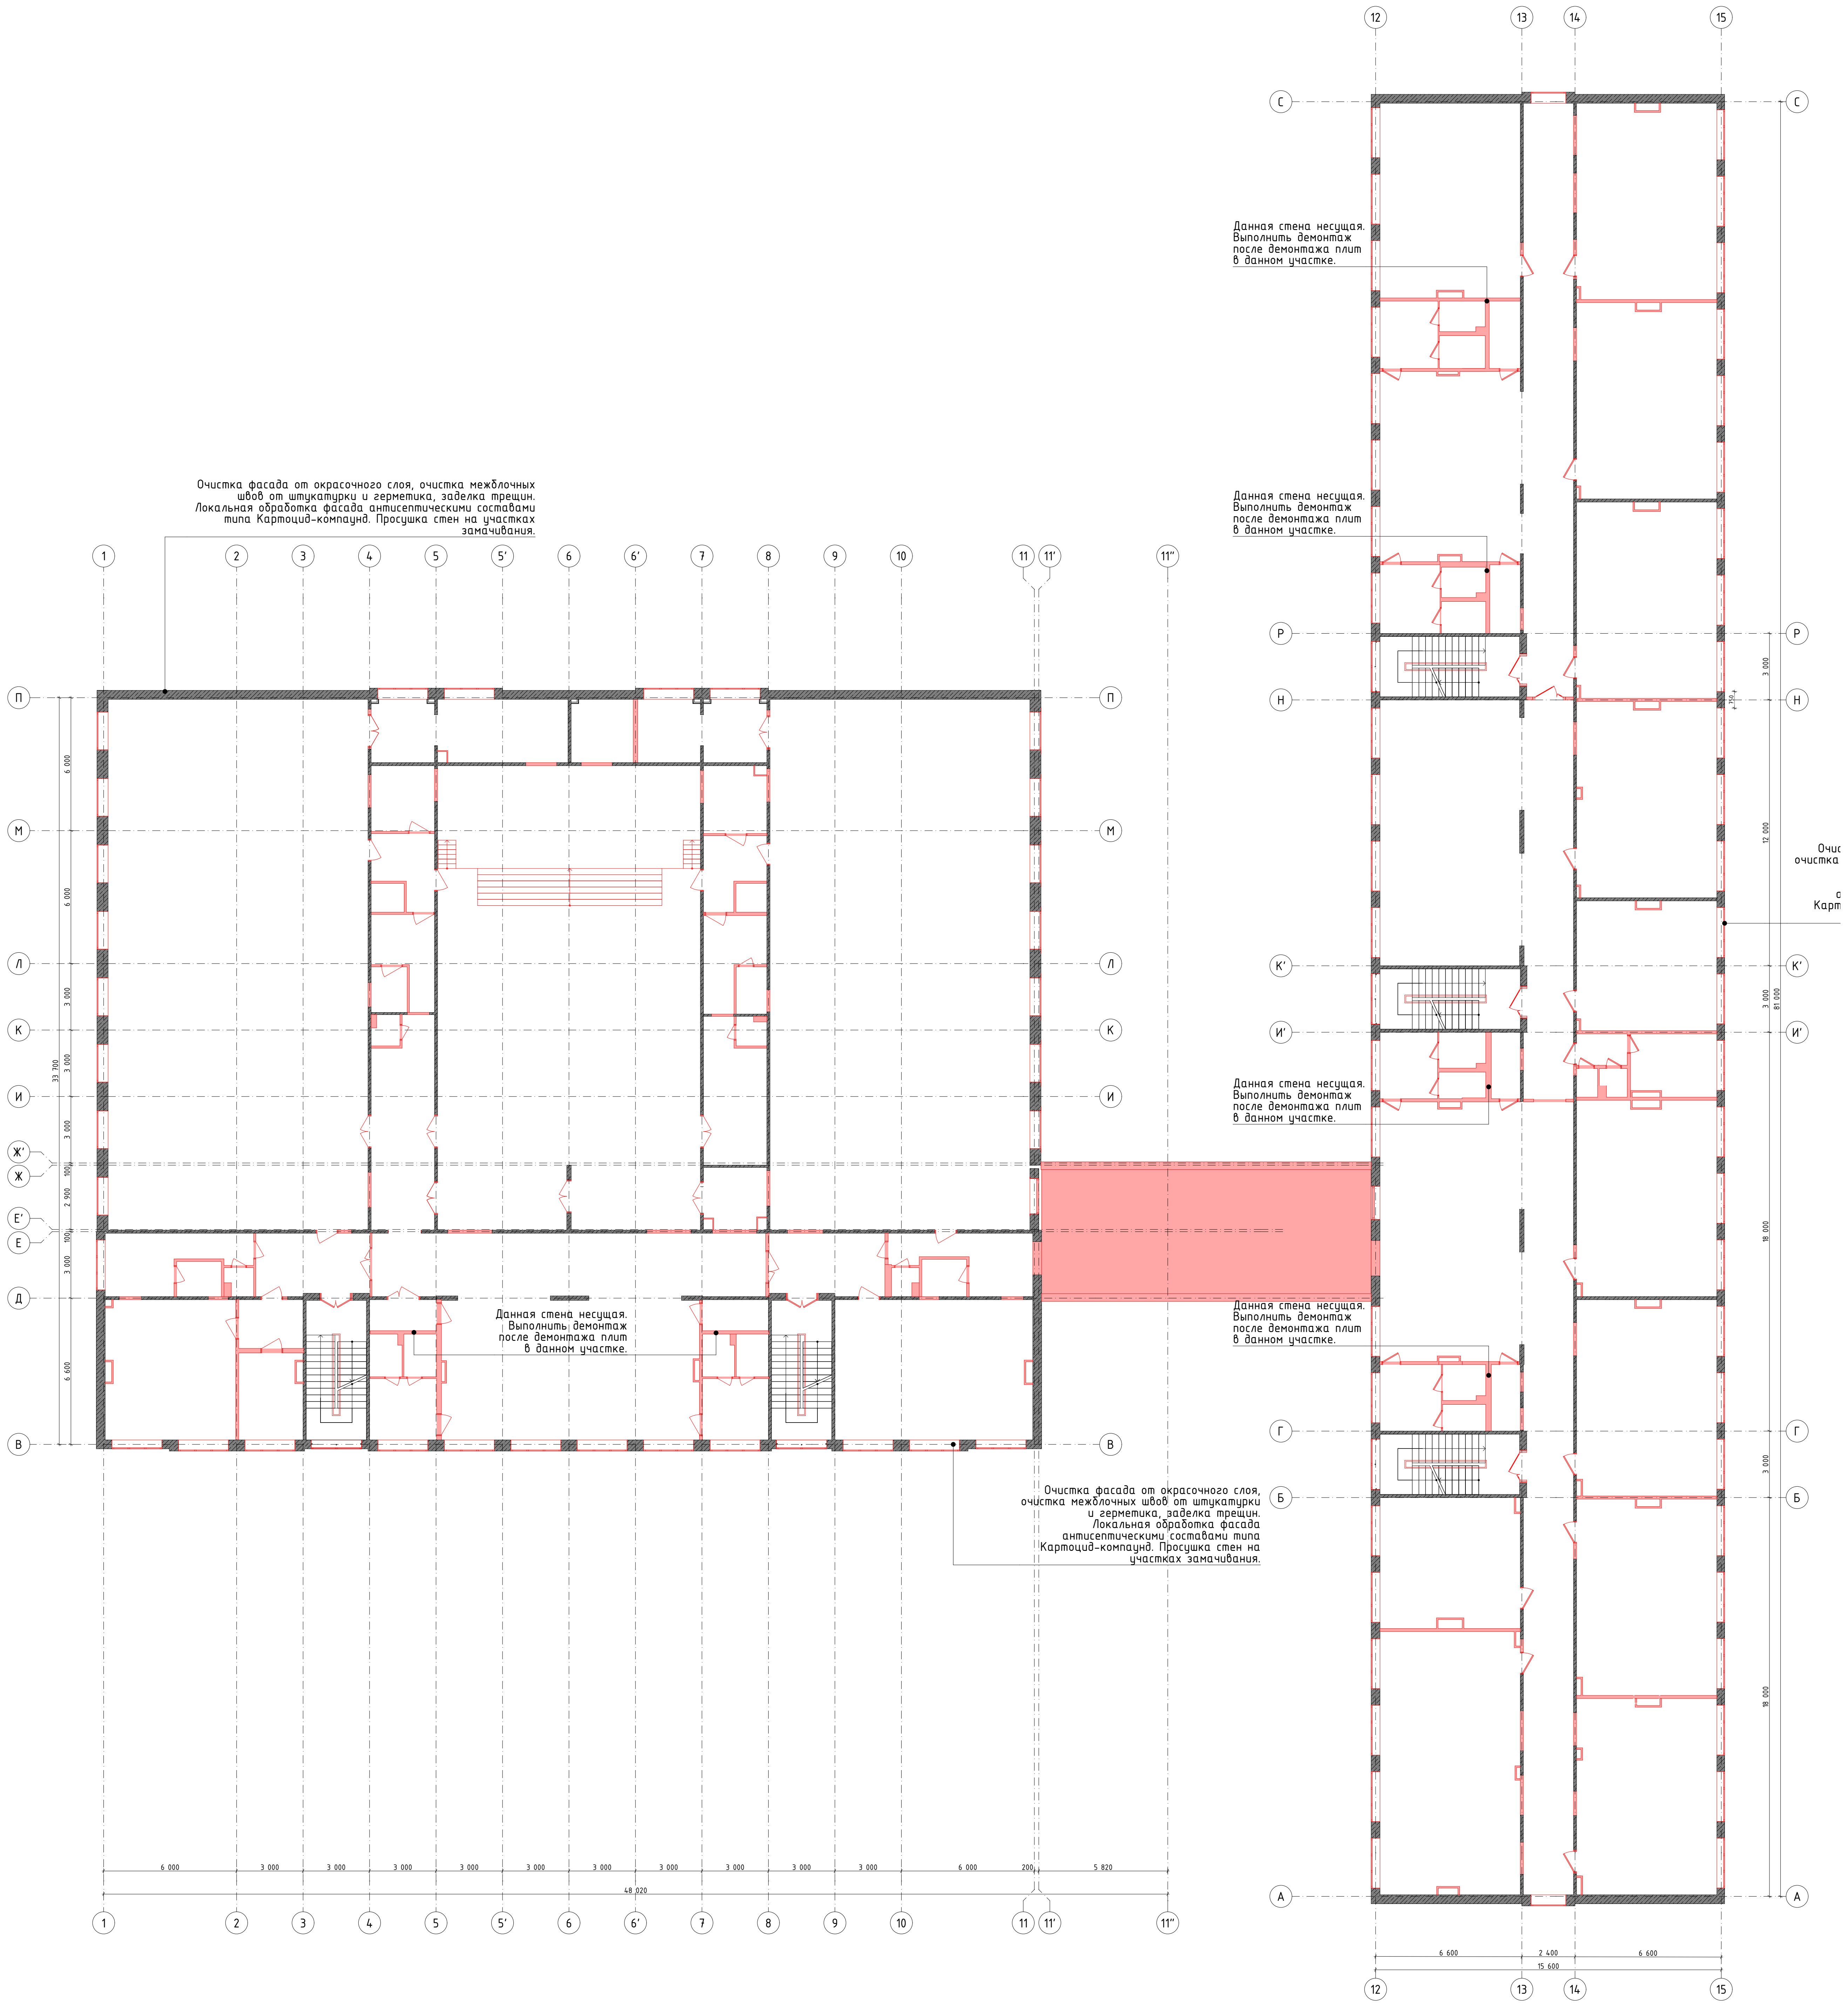
Очистка фасада от окрасочного слоя, очистка межблочных швов от штукатурки и герметика, заделка трещин. Локальная обработка фасада антисептическими составами типа Картоцид-компаунд. Просушка стен на участках замачивания.
Данная стена несущая. Выполнить демонтаж после демонтажа плит в данном участке.
Данная стена несущая. Выполнить демонтаж после демонтажа плит в данном участке.
Данная стена несущая. Выполнить демонтаж после демонтажа плит в данном участке.
Данная стена несущая. Выполнить демонтаж после демонтажа плит в данном участке.
Данная стена несущая. Выполнить демонтаж после демонтажа плит в данном участке.
Очистка фасада от окрасочного слоя, очистка межблочных швов от штукатурки и герметика, заделка трещин. Локальная обработка фасада антисептическими составами типа Картоцид-компаунд. Просушка стен на участках замачивания.
Очис
очистка
Карт
1
2
3
4
5
5'
6
6'
7
8
9
10
11
11'
11''
12
13
14
15
П
М
Л
К
И
Ж'
Ж
Е'
Е
Д
В
С
Р
Н
К'
И'
Г
Б
А
6 000
3 000
3 000
3 000
3 000
3 000
3 000
3 000
3 000
3 000
3 000
6 000
200
5 820
48 020
6 600
2 400
6 600
15 600
3 000
750
12 000
3 000
81 000
18 000
3 000
18 000

ПРИМЕЧАНИЕ:

1. Наружные работы по фасаду:
- Очистка фасада от окрасочного слоя, очистка межблочных швов от штукатурки и герметика, заделка трещин.
- Локальная обработка фасада антисептическими составами типа Картоцид-компаунд.
- Просушка стен на участках замачивания.

(Возможна корректировка проекта после прохождения «МГЭ»
Московской Государственной Экспертизы)

Условные обозначения

- ▨ – сущ. стена Ж/Б
- 🟥 – демонтируемые перегородки
- ⌒ – демонтаж сущ. дверей
- ▭ – демонтаж сущ. окон

0,000=168,265

ГИП-28/24-Р-АР

ГБОУ Школа № 218, расположенная по адресу:
г. Москва, ул. Вучетича, д. 6

Изм.	Кол.уч.	Лист	№Док.	Подп.	Дата
Разработал		Белова Е.С.			02.25
Проверил		Дубинин С.В.			02.25
ГАП		Дубинин С.В.			02.25
ГИП		Гущин А.В.			02.25
Н.контроль		Шукшин В.В.			02.25

Средняя общеобразовательная школа

Стадия	Лист	Листов
П	5	6

План демонтажа 2 этажа

И-ГРУПП
ПРОЕКТНО-СТРОИТЕЛЬНАЯ КОМПАНИЯ

План демонтажа 3 этажа

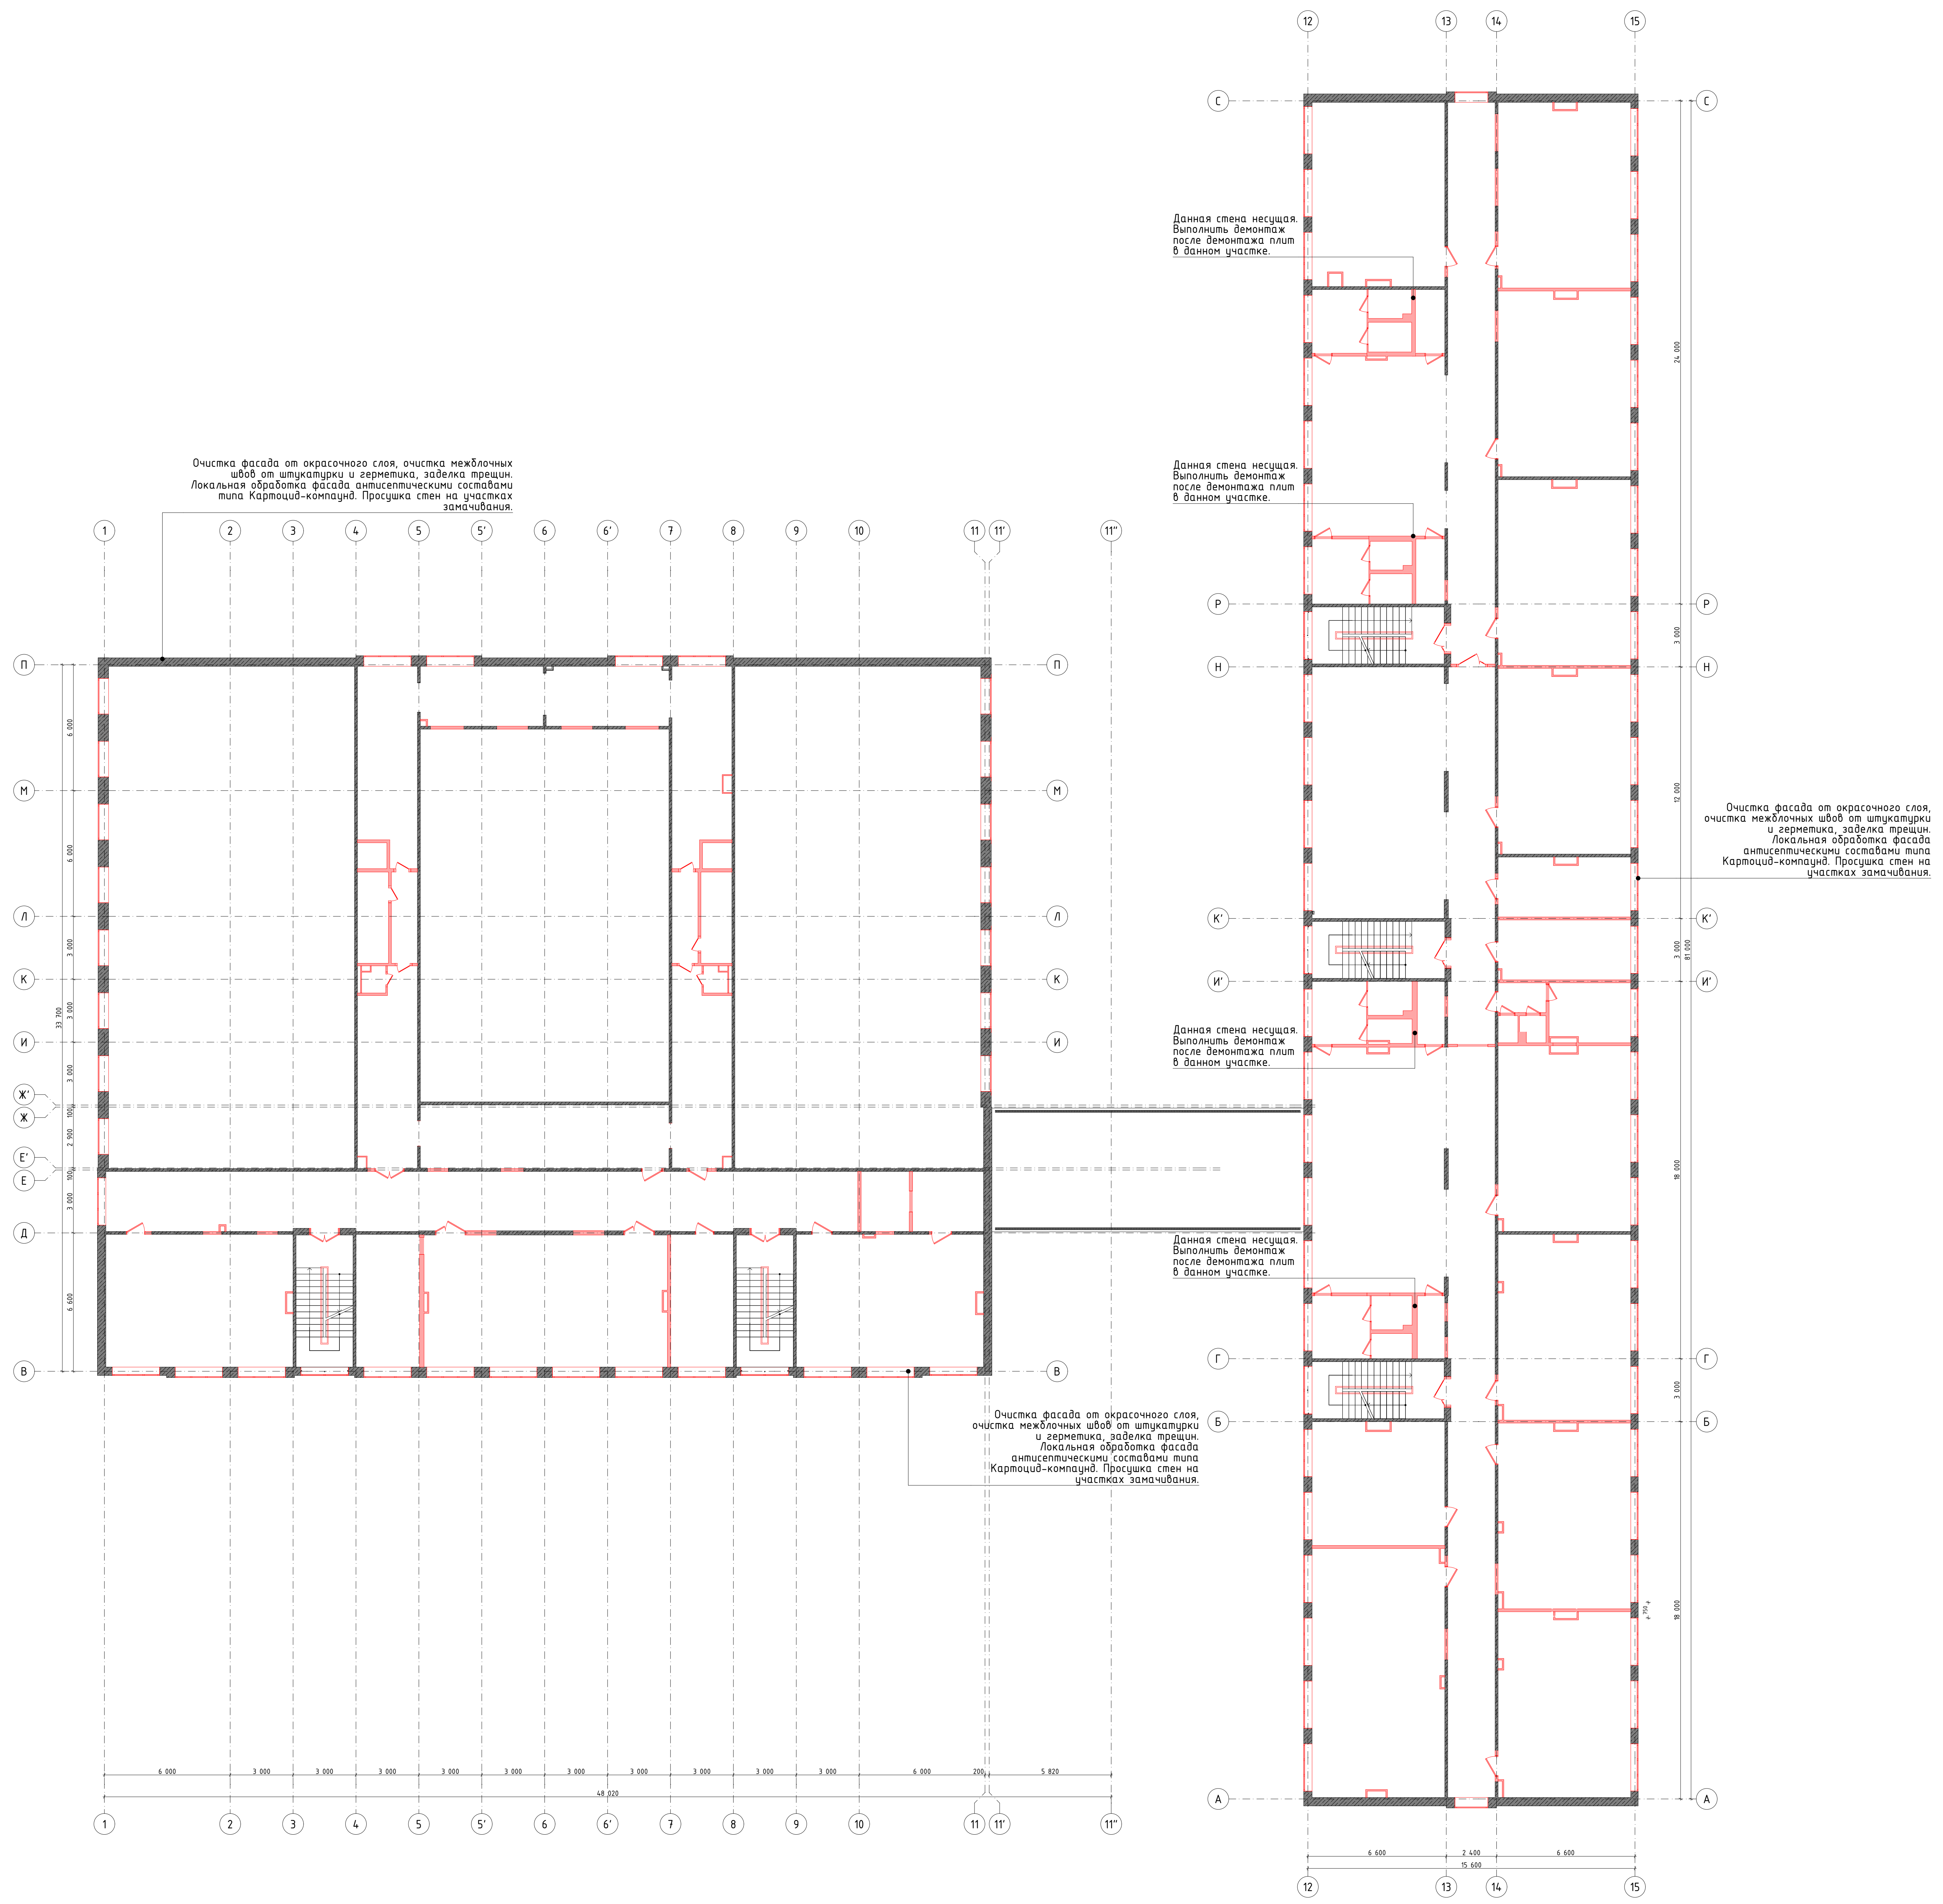
1
2
3
4
5
5'
6
6'
7
8
9
10
11
11'
11''
12
13
14
15
П
М
Л
К
И
Ж'
Ж
Е'
Е
Д
В
С
Р
Н
К'
И'
Г
Б
А
6 000
6 000
3 000
3 000
3 000
100
2 900
100
3 000
6 600
33 700
6 000
3 000
3 000
3 000
3 000
3 000
3 000
3 000
3 000
3 000
6 000
200
5 820
48 020
6 600
2 400
6 600
15 600
24 000
3 000
12 000
3 000
81 000
18 000
3 000
18 000
750
Очистка фасада от окрасочного слоя, очистка межблочных швов от штукатурки и герметика, заделка трещин. Локальная обработка фасада антисептическими составами типа Картоцид-компаунд. Просушка стен на участках замачивания.
Данная стена несущая. Выполнить демонтаж после демонтажа плит в данном участке.
Данная стена несущая. Выполнить демонтаж после демонтажа плит в данном участке.
Очистка фасада от окрасочного слоя, очистка межблочных швов от штукатурки и герметика, заделка трещин. Локальная обработка фасада антисептическими составами типа Картоцид-компаунд. Просушка стен на участках замачивания.
Данная стена несущая. Выполнить демонтаж после демонтажа плит в данном участке.
Данная стена несущая. Выполнить демонтаж после демонтажа плит в данном участке.
Очистка фасада от окрасочного слоя, очистка межблочных швов от штукатурки и герметика, заделка трещин. Локальная обработка фасада антисептическими составами типа Картоцид-компаунд. Просушка стен на участках замачивания.

Условные обозначения

▨ – сущ. стена Ж/Б

🟥 – демонтируемые перегородки

– демонтаж сущ. дверей

– демонтаж сущ. окон

ПРИМЕЧАНИЕ:
1. Наружные работы по фасаду:
- Очистка фасада от окрасочного слоя, очистка межблочных швов от штукатурки и герметика, заделка трещин.
- Локальная обработка фасада антисептическими составами типа Картоцид-компаунд.
- Просушка стен на участках замачивания.

(Возможна корректировка проекта после прохождения «МГЭ»
Московской Государственной Экспертизы)

0,000=168,265

Изм.	Кол.уч.	Лист	№Док.	Подп.	Дата	ГИП-28/24-Р-АР		
						ГБОУ Школа № 218, расположенная по адресу: г. Москва, ул. Вучетича, д. 6		
Разработал		Белова Е.С.			02.25	Средняя общеобразовательная школа	Стадия	Лист	Листов
Проверил		Дубинин С.В.			02.25		П	6	6
ГАП		Дубинин С.В.			02.25				
ГИП		Гущин А.В.			02.25	План демонтажа 3 этажа	И-ГРУПП ПРОЕКТНО-СТРОИТЕЛЬНАЯ КОМПАНИЯ		
Н.контроль		Шукшин В.В.			02.25				

План демонтажа 4 этажа

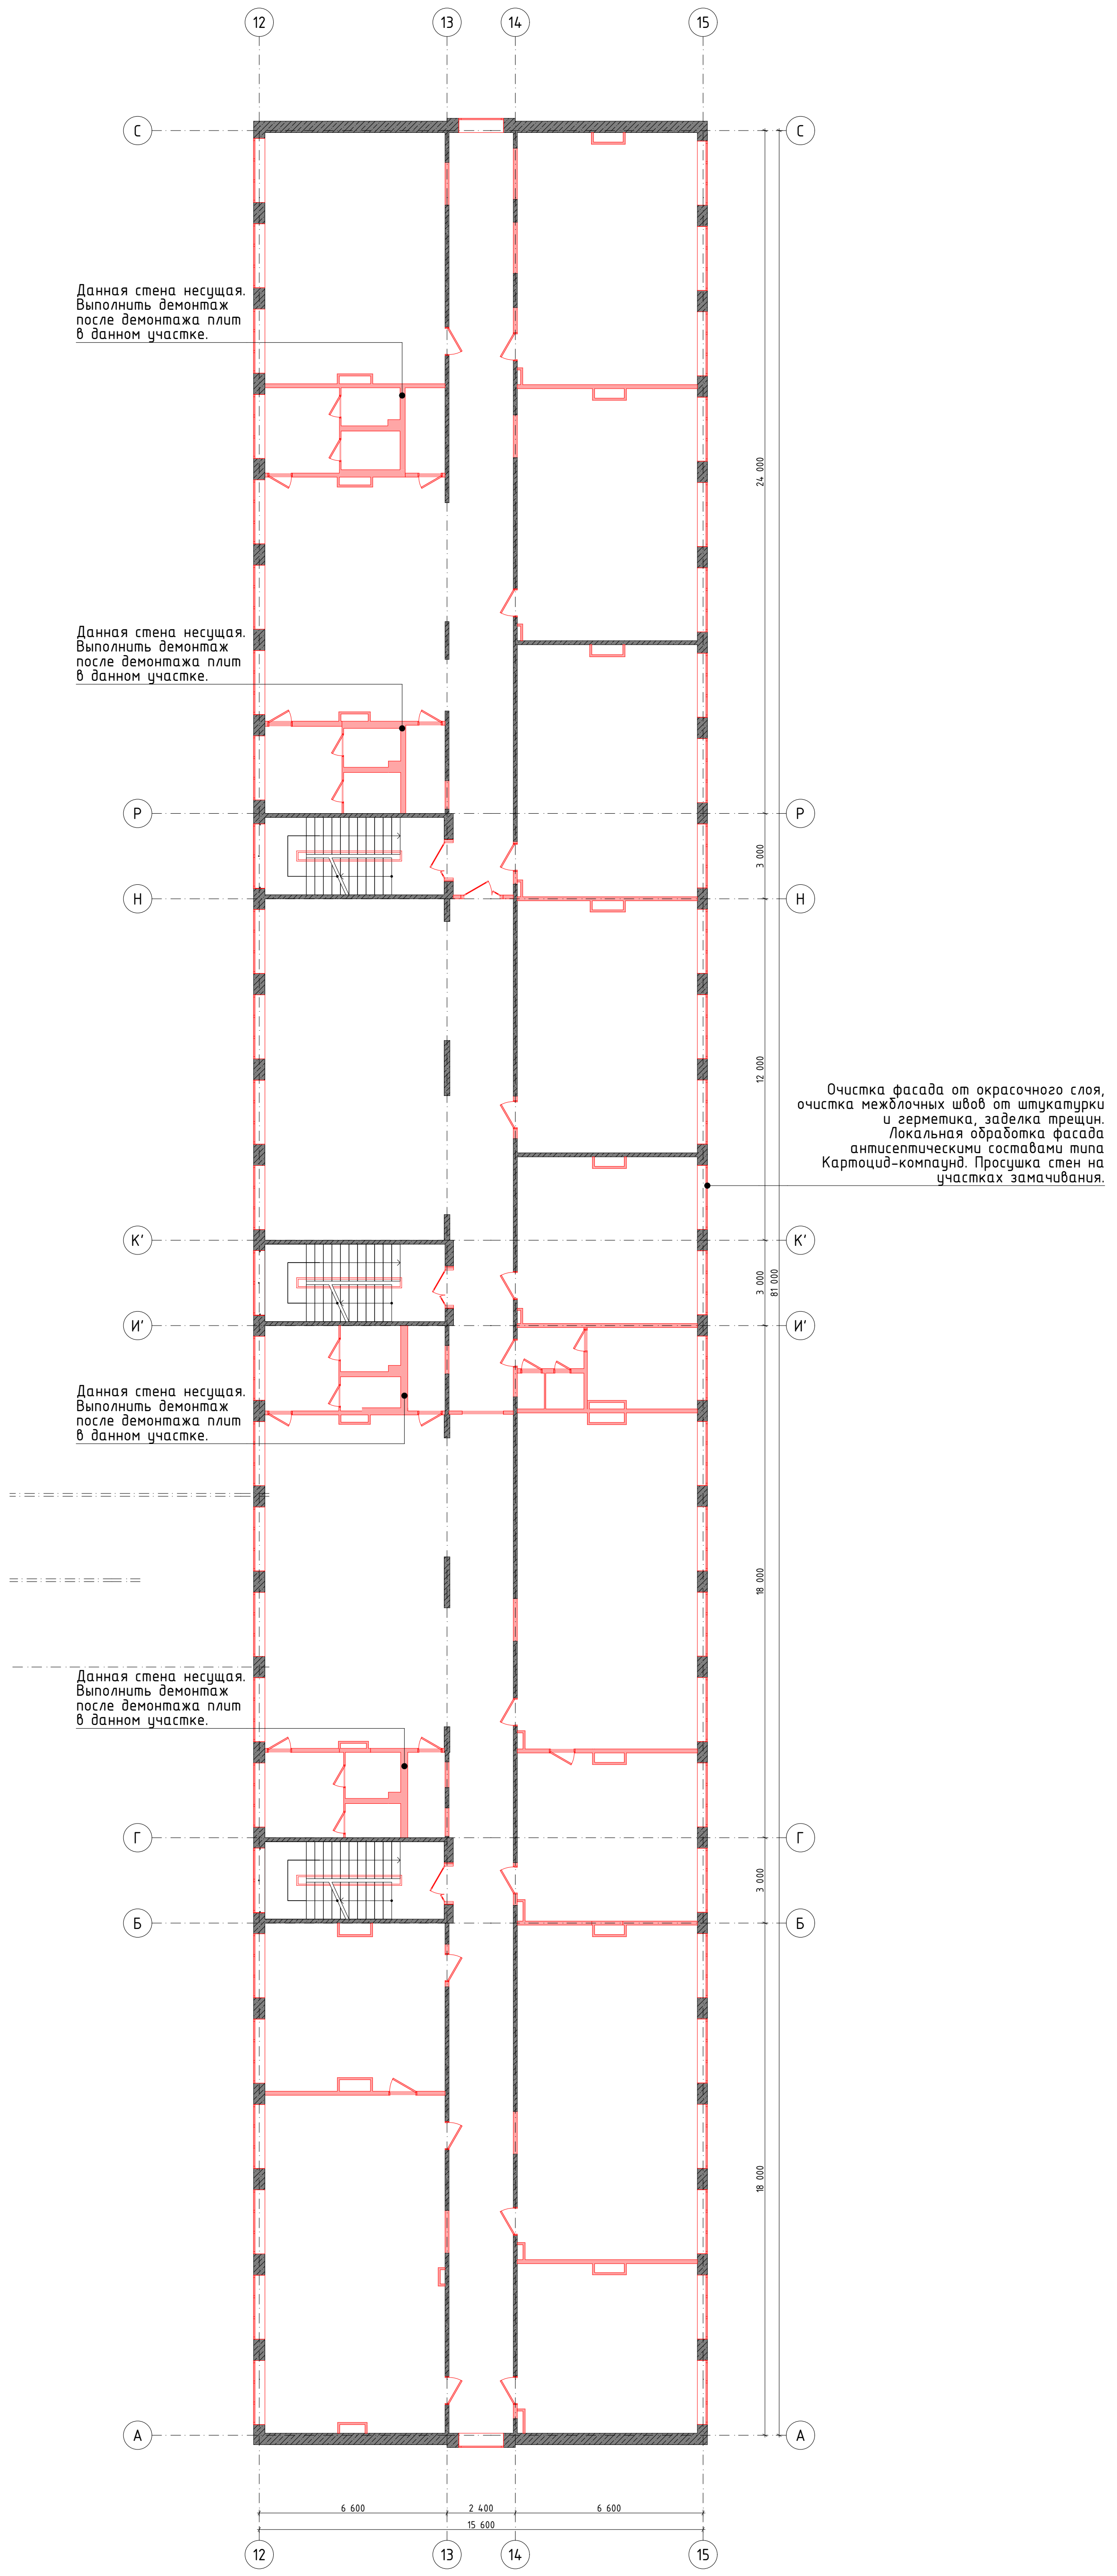

Данная стена несущая. Выполнить демонтаж после демонтажа плит в данном участке.

Данная стена несущая. Выполнить демонтаж после демонтажа плит в данном участке.

Очистка фасада от окрасочного слоя, очистка межблочных швов от штукатурки и герметика, заделка трещин. Локальная обработка фасада антисептическими составами типа Картоцид-компаунд. Просушка стен на участках замачивания.

Данная стена несущая. Выполнить демонтаж после демонтажа плит в данном участке.

Данная стена несущая. Выполнить демонтаж после демонтажа плит в данном участке.

Условные обозначения

▨ - сущ. стена Ж/Б

🟥 - демонтируемые перегородки

- демонтаж сущ. дверей

- демонтаж сущ. окон

ПРИМЕЧАНИЕ:
1. Наружные работы по фасаду:
- Очистка фасада от окрасочного слоя, очистка межблочных швов от штукатурки и герметика, заделка трещин.
- Локальная обработка фасада антисептическими составами типа Картоцид-компаунд.
- Просушка стен на участках замачивания.

**(Возможна корректировка проекта после прохождения «МГЭ»
Московской Государственной Экспертизы)**

0,000=168,265

						ГИП-28/24-Р-АР		
Изм.	Кол.уч.	Лист	№Док.	Подп.	Дата	ГБОУ Школа № 218, расположенная по адресу: г. Москва, ул. Вучетича, д. 6		
Разработал		Белова Е.С.			02.25	Средняя общеобразовательная школа	Стадия	Лист	Листов
Проверил		Дубинин С.В.			02.25		П	7	6
ГАП		Дубинин С.В.			02.25	План демонтажа 4 этажа	И-ГРУПП ПРОЕКТНО-СТРОИТЕЛЬНАЯ КОМПАНИЯ		
ГИП		Гущин А.В.			02.25				
Н.контроль		Шукшин В.В.			02.25				

План демонтажа кровли

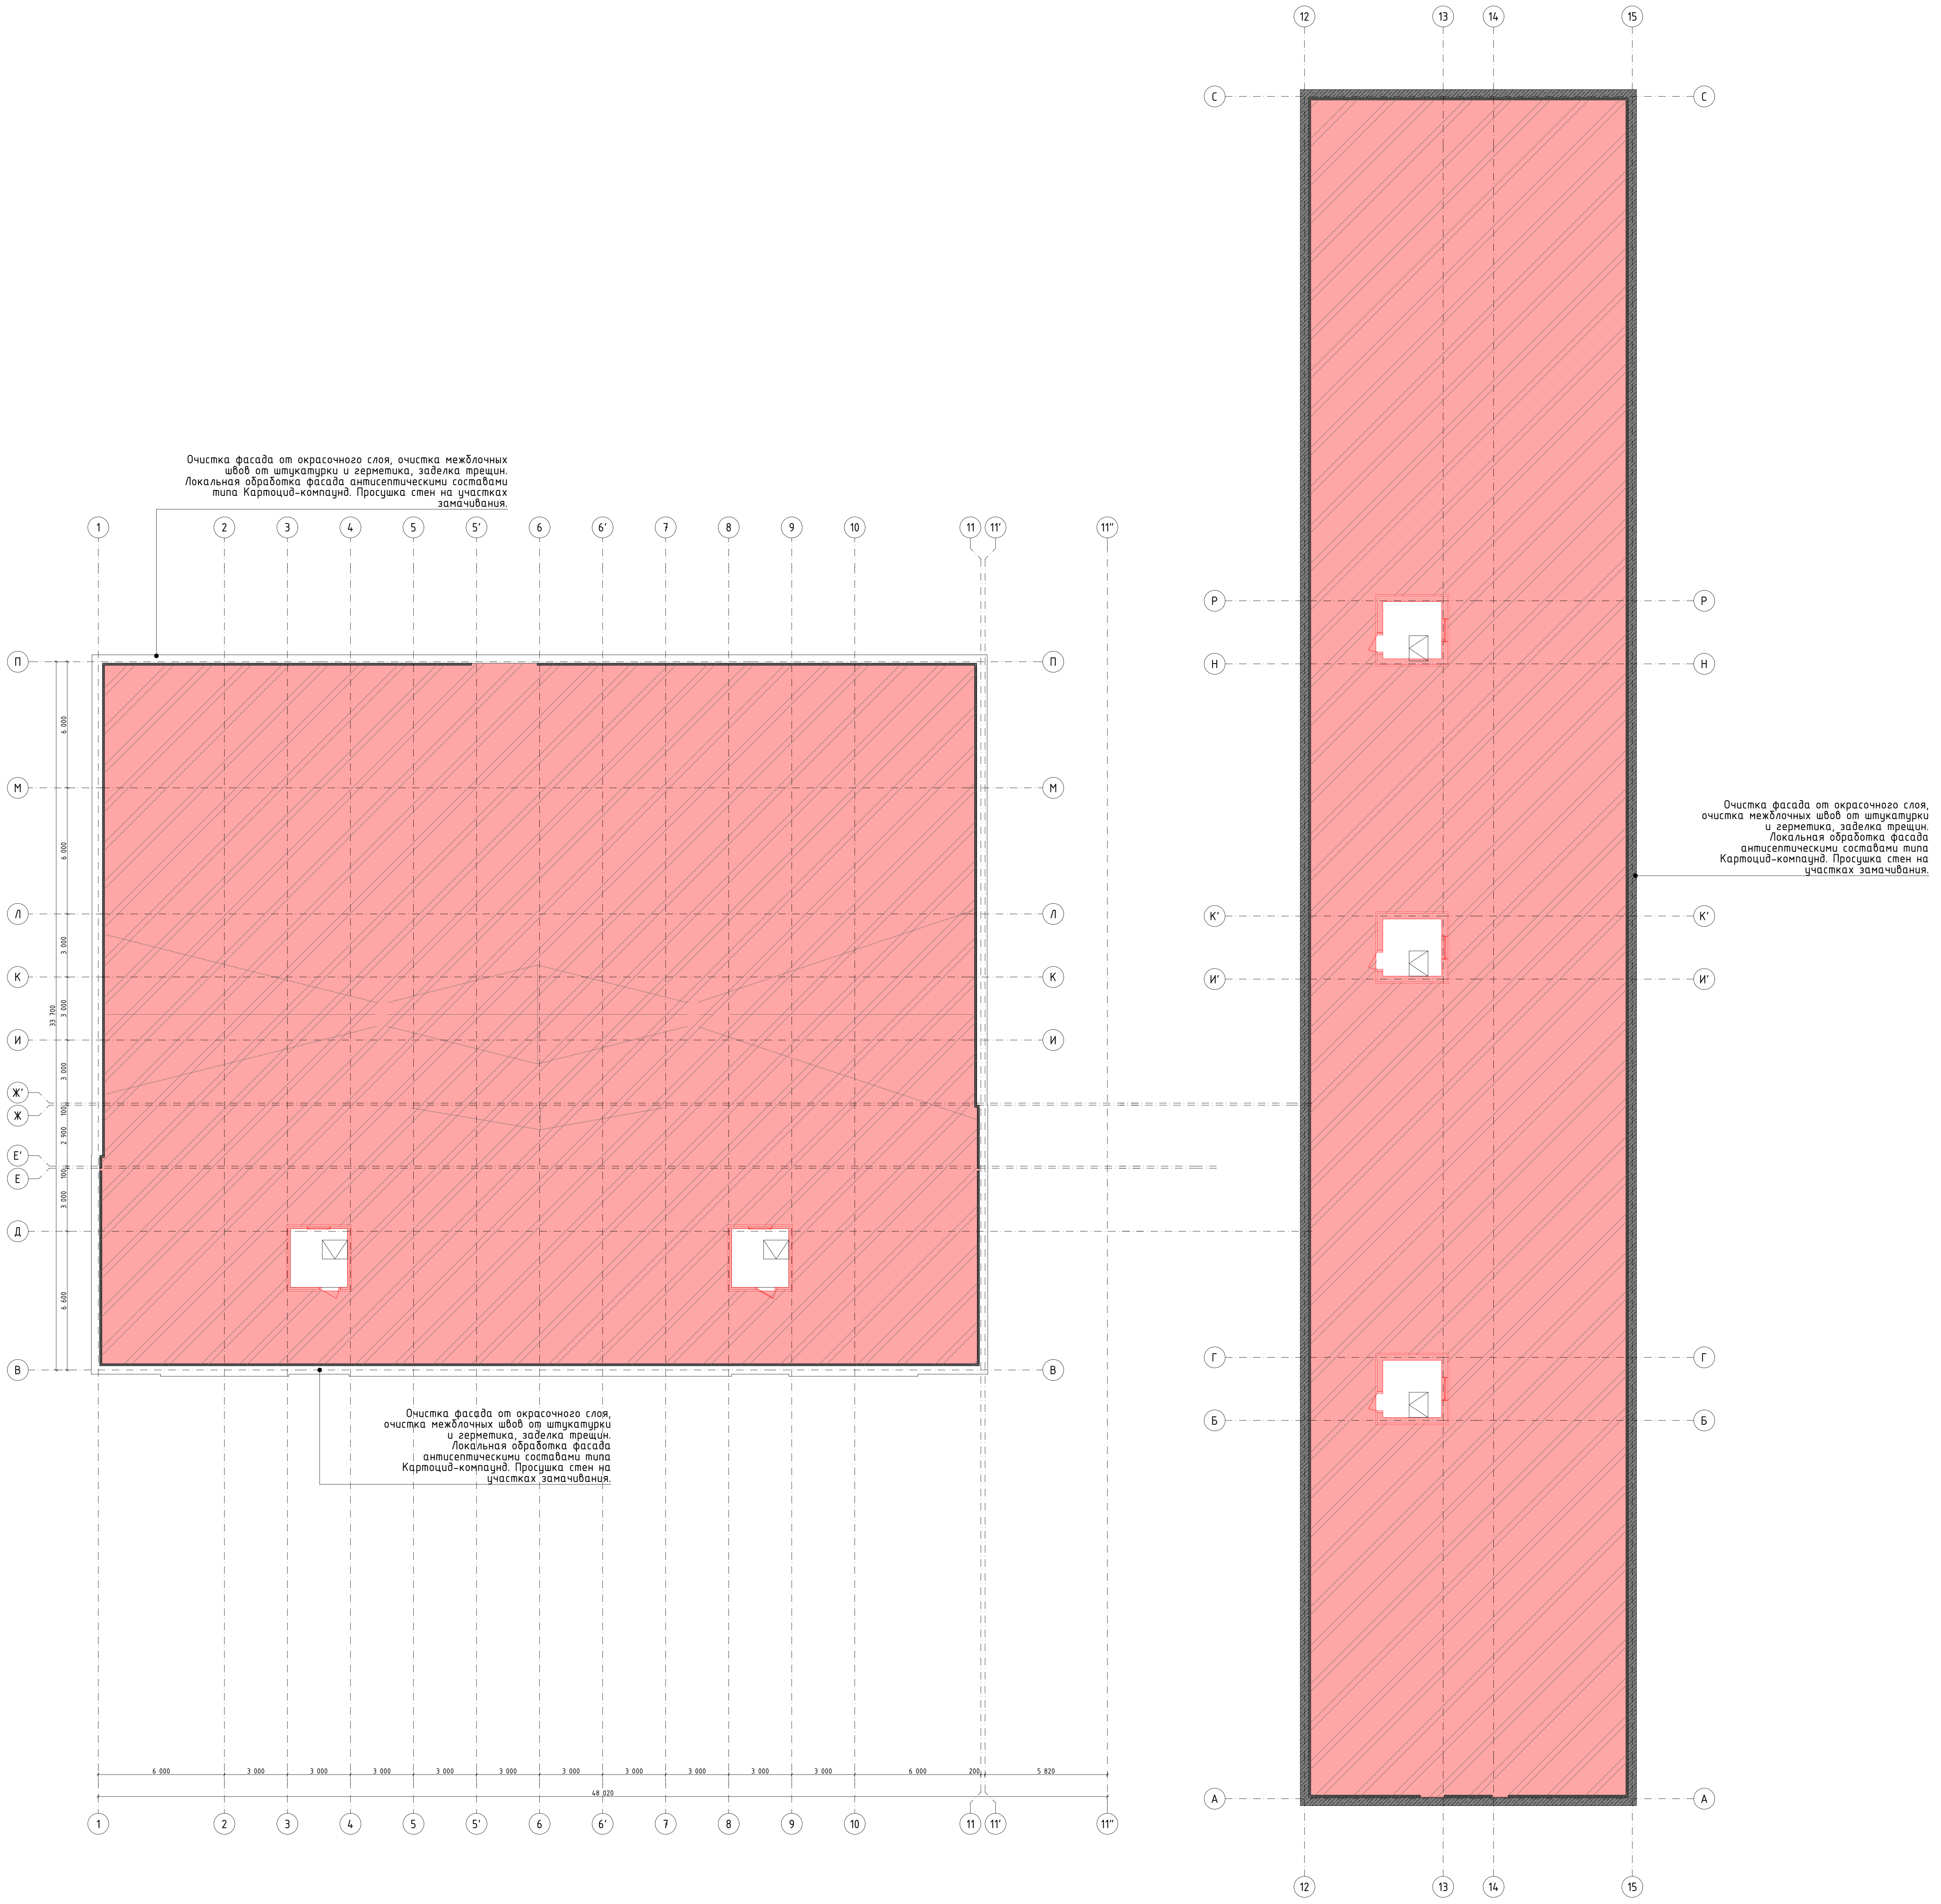

Очистка фасада от окрасочного слоя, очистка межблочных швов от штукатурки и герметика, заделка трещин. Локальная обработка фасада антисептическими составами типа Картоцид-компаунд. Просушка стен на участках замачивания.

Очистка фасада от окрасочного слоя, очистка межблочных швов от штукатурки и герметика, заделка трещин. Локальная обработка фасада антисептическими составами типа Картоцид-компаунд. Просушка стен на участках замачивания.

Очистка фасада от окрасочного слоя, очистка межблочных швов от штукатурки и герметика, заделка трещин. Локальная обработка фасада антисептическими составами типа Картоцид-компаунд. Просушка стен на участках замачивания.

Условные обозначения

▨ – сущ. стена Ж/Б
▬ – демонтируемые перегородки
▨ – демонтаж покрытия кровли

ПРИМЕЧАНИЕ:
1. Наружные работы по фасаду:
- Очистка фасада от окрасочного слоя, очистка межблочных швов от штукатурки и герметика, заделка трещин.
- Локальная обработка фасада антисептическими составами типа Картоцид-компаунд.
- Просушка стен на участках замачивания.

(Возможна корректировка проекта после прохождения «МГЭ»
Московской Государственной Экспертизы)

0,000=168,265

						ГИП-28/24-Р-АР		
Изм.	Кол.уч.	Лист	№Док.	Подп.	Дата	ГБОУ Школа № 218, расположенная по адресу: г. Москва, ул. Вучетича, д. 6		
Разработал		Белова Е.С.			02.25	Средняя общеобразовательная школа	Стадия	Лист	Листов
Проверил		Дубинин С.В.			02.25		П	8	6
ГАП		Дубинин С.В.			02.25				
ГИП		Гущин А.В.			02.25	План демонтажа кровли	И-ГРУПП ПРОЕКТНО-СТРОИТЕЛЬНАЯ КОМПАНИЯ		
Н.контроль		Шукшин В.В.			02.25				