ООО «И-Групп»

Ассоциация в области архитектурно-строительного проектирования
«Саморегулируемая организация «СОВЕТ ПРОЕКТИРОВЩИКОВ»
(СРО-П-011-16072009). Регистрационный номер: П-011-007722770040-1134.

Заказчик: Автономная некоммерческая организация
«Развитие Городских Технологий» (АНО «РГТ»)

Договор № 423/П-24-АНО от 26.04.2024 г.

«Капитальный ремонт общеобразовательного учреждения
ГБОУ Школа № 218, расположенного по адресу:
г. Москва, ул. Вучетича, д. 6»

1 этап

ПРОЕКТНАЯ ДОКУМЕНТАЦИЯ

Раздел 5. Сведения об инженерном оборудовании, о сетях инженерно-технического обеспечения, перечень инженерно-технических мероприятий, содержание технологических решений

Подраздел 5. Сети связи

Часть 6. Система двухсторонней связи (СДС)

ГИП-28/24-П-ИОС5.6

Том 5.5.6

2024 г.

ООО «И-Групп»

Ассоциация в области архитектурно-строительного проектирования
«Саморегулируемая организация «СОВЕТ ПРОЕКТИРОВЩИКОВ»
(СРО-П-011-16072009). Регистрационный номер: П-011-007722770040-1134.

Заказчик: Автономная некоммерческая организация
«Развитие Городских Технологий» (АНО «РГТ»)

Договор № 423/П-24-АНО от 26.04.2024 г.

«Капитальный ремонт общеобразовательного учреждения
ГБОУ Школа № 218, расположенного по адресу:
г. Москва, ул. Вучетича, д. 6»

1 этап

ПРОЕКТНАЯ ДОКУМЕНТАЦИЯ

Раздел 5. Сведения об инженерном оборудовании, о сетях инженерно-технического обеспечения, перечень инженерно-технических мероприятий, содержание технологических решений

Подраздел 5. Сети связи

Часть 6. Система двухсторонней связи (СДС)

ГИП-28/24-П-ИОС5.6

Том 5.5.6

Генеральный директор: М. В. Татошвили

Главный инженер проекта: А. В. Гущин

2024 г.

Содержание тома

Шифр	Наименование	Примечание
	Титульный лист	
ГИП-28/24-П-ИОС5.6.С	Содержание тома	
ГИП-28/24-П-ИОС5.6.ПЗ	Пояснительная записка	
ГИП-28/24-П-ИОС5.6	Графическая часть	
ГИП-28/24-П-ИОС5.6.СО	Приложение 1. Спецификация оборудования, изделий и материалов	

Взам. инв. №

Подпись и дата

Инв. № подл.

Изм.	Кол. уч.	Лист	№ док.	Подпись	Дата	ГИП-28/24-П-ИОС5.6.С		
Разработал		Козлова			11.2024	Содержание тома	Стадия	Лист	Листов
Проверил		Улитина			11.2024		П	1	1
ГИП		Гущин			11.2024				
Н. контр.		Шукшин			11.2024				

И-ГРУПП
ПРОЕКТНО-СТРОИТЕЛЬНАЯ КОМПАНИЯ

ПОЯСНИТЕЛЬНАЯ ЗАПИСКА

ВВЕДЕНИЕ

В настоящей проектной документации рассматриваются принципы организации, устройство и работа системы двухсторонней связи (СДС) в ходе выполнения капитального ремонта общеобразовательного учреждения (ГБОУ Школа № 218), расположенного по адресу: г. Москва, ул. Вучетича, д. 6.

Проектная документация разработана на основании:

- договора;
- архитектурно-строительных чертежей, а также других исходных данных, полученных от Заказчика.

Проектная документация разработана в соответствии с Заданием на проектирование, техническими регламентами, нормами, стандартами и правилами, соответствуют требованиям экологических, санитарно - гигиенических, противопожарных и других норм, действующих на территории Российской Федерации, и обеспечивает безопасную для жизни и здоровья людей эксплуатацию системы, при выполнении мероприятий, предусмотренных проектной документацией.

Предусматриваемое проектной документацией оборудование сертифицировано и разрешено к применению.

Основными нормативными документами для проектирования являются:

- Постановление Правительства Российской Федерации от 16 февраля 2008 года № 87 «О составе разделов проектной документации и требованиях к их содержанию» с учетом изменений на 27.05.2022 г.;
- Федеральный закон №123-ФЗ «Технический регламент о требованиях пожарной безопасности» от 22.07.2008 г.;
- ГОСТ Р 21.101-2020 «Система проектной документации для строительства. Основные требования к проектной и рабочей документации»;
- ПУЭ «Правила устройства электроустановок»;
- СП 31-110-2003 «Свод правил по проектированию и строительству. Проектирование и монтаж электроустановок жилых и общественных зданий»;

- СП 134.13330.2012 «Системы электросвязи зданий и сооружений. Основные положения проектирования»;
- СП 251.1325800.2016 «Здания общеобразовательных организаций. Правила проектирования»;
- СП 59.13330.2020 «Доступность зданий и сооружений для маломобильных групп населения»;
- ГОСТ Р 51671-2020 «Средства связи и информации технические общего пользования, доступные для инвалидов. Классификация. Требования доступности и безопасности»
- ГОСТ 31565-2012 «Кабельные изделия. Требования пожарной безопасности».
- СП 132.13330.2011 "Обеспечение антитеррористической защищенности зданий и сооружений. Общие требования проектирования";

1. СВЕДЕНИЯ О ЕМКОСТИ ПРИСОЕДИНЯЕМОЙ СЕТИ СВЯЗИ ОБЪЕКТА КАПИТАЛЬНОГО СТРОИТЕЛЬСТВА К СЕТИ СВЯЗИ ОБЩЕГО ПОЛЬЗОВАНИЯ

Проектом предусматривается оснащение системой двухсторонней связи (СДС) санузла для МГН на 1 этаже и зону отдыха МГН. Предусмотрено оснащение переговорными устройствами центрального входа. Так же предусмотрена организация двухсторонней связи помещения охраны с входами в здание и помещениями с одновременным пребыванием более 50 человек. Проектируемая система носит локальный характер и не требует подключения к другим сетям связи.

2. ХАРАКТЕРИСТИКА ПРОЕКТИРУЕМЫХ СООРУЖЕНИЙ И ЛИНИЙ СВЯЗИ, В ТОМ ЧИСЛЕ ЛИНЕЙНО-КАБЕЛЬНЫХ, ДЛЯ ОБЪЕКТОВ ПРОИЗВОДСТВЕННОГО НАЗНАЧЕНИЯ

Данный пункт не разрабатывается.

3. ХАРАКТЕРИСТИКА СОСТАВА И СТРУКТУРЫ СООРУЖЕНИЙ И ЛИНИЙ СВЯЗИ

Санузел для МГН на первом этаже (пом. 104а) здания оснащается комплектом вызова персонала, переговорными устройствами. Устанавливается следующее оборудование:

- кнопка вызова со шнуром GC-0423W2;
- кнопка сброса GC-0421W2;
- переговорное устройство GC-2001W3.

Непосредственно над входной дверью в санузел МГН, снаружи помещения, размещается сигнальная лампа (светозвуковой сигнализатор) GC-0611W4.

Источник питания ББП-50 располагается на 1 этаже и служит для питания сигнальной лампы GC-0611W4.

В помещении охраны (пом. 103) размещается пульт диспетчерской связи на 12 абонентов GC-1036F2.

Центральный вход оборудуется переговорными устройствами GC-2001P5. Устройство располагается перед подъемом на пандус на стойке Штольц (на высоте в соответствии с ГОСТ Р 51671-2020 пункт 7.2.2.3 на высоте от 1,0 до 1,2 м от уровня доступной для инвалида поверхности передвижения) и непосредственно перед входной дверью. Вызывные панели подключены к пульту диспетчерской связи в помещении охраны.

Зона отдыха МГН оборудуется переговорным устройством GC-2001P5. Вызывные панели подключены к пульту диспетчерской связи в помещении охраны.

В соответствии с СП 132.13330.2011 в помещении 103 (помещение охраны) предусматривается пульт селекторной связи GC-1036F2, обеспечивающий организацию оперативной громкоговорящей связи с помещениями с массовым пребыванием людей (пом. 131, 146) и всех входов посредством установки абонентских устройств громкой селекторной связи GC-2001P5.

Используемая кабельная продукция соответствует ГОСТ 31565-2012 и другим нормативным документам, действующих на территории РФ.

Шлейфы подключения всех типов устройств выполняются кабелем КПСВВнг(А)-LSLTx 1х2х0,5.

Шлейфы питания выполняются кабелем ВВГнг(А)-LSLTx 1х2х1,5.

Прокладка кабеля внутри здания выполняется в гофрированных ПВХ трубах диаметром 20 мм в запотолочном пространстве, опуски в штробах. Снаружи прокладка кабелей в ПНД трубах диам. 20 мм.

Проход кабельных линий через стены, перекрытия выполняется в стальных гильзах диам. 25 мм. После прокладки отверстия заделываются противопожарным герметиком.

4. ОБОСНОВАНИЕ СПОСОБА, С ПОМОЩЬЮ КОТОРОГО УСТАНАВЛИВАЮТСЯ СОЕДИНЕНИЯ СЕТЕЙ СВЯЗИ (НА МЕСТНОМ, ВНУТРИЗОНОМ И МЕЖДУГОРОДНЕМ УРОВНЯХ)

Проектом предусматривается оснащение системой двухсторонней связи (СДС) санузла для МГН на 1 этаже и зону отдыха МГН. Предусмотрено оснащение переговорными устройствами центрального входа. Так же предусмотрена организация двухсторонней связи помещения охраны с входами в здание и помещениями с одновременным пребыванием более 50 человек. Проектируемая система носит локальный характер и не требует подключения к другим сетям связи.

5. МЕСТОПОЛОЖЕНИЕ ТОЧЕК ПРИСОЕДИНЕНИЯ И ТЕХНИЧЕСКИЕ ПАРАМЕТРЫ В ТОЧКАХ ПИСОЕДИНЕНИЯ СЕТЕЙ СВЯЗИ

Данный пункт не разрабатывается.

6. ОБОСНОВАНИЕ СПОСОБОВ УЧЕТА ТРАФИКА

Данный пункт не разрабатывается.

7. ПЕРЕЧЕНЬ МЕРОПРИЯТИЙ ПО ОБЕСПЕЧЕНИЮ ВЗАИМОДЕЙСТВИЯ СИСТЕМ УПРАВЛЕНИЯ И ТЕХНИЧЕСКОЙ ЭКСПЛУАТАЦИИ, В ТОМ ЧИСЛЕ ОБОСНОВАНИЕ СПОСОБА ОРГАНИЗАЦИИ ВЗАИМОДЕЙСТВИЯ МЕЖДУ ЦЕНТРАМИ УПРАВЛЕНИЯ РИСОЕДИНЯЕМОЙ СЕТИ СВЯЗИ И СЕТИ СВЯЗИ ОБЩЕГО ПОЛЬЗОВАНИЯ, ВЗАИМОДЕЙСТВИЕ СИСТЕМ СИНХРОНИЗАЦИИ

Данный пункт не разрабатывается.

8. ПЕРЕЧЕНЬ МЕРОПРИЯТИЙ ПО ОБЕСПЕЧЕНИЮ УСТОЙЧИВОГО ФУНКЦИОНИРОВАНИЯ СЕТЕЙ СВЯЗИ, В ТОМ ЧИСЛЕ В ЧРЕЗВЫЧАЙНЫХ СИТУАЦИЯХ

Устойчивое функционирование запроектированной системы обеспечивается за счет:
- защитного заземления в соответствии с требованиями паспортов заводов-изготовителей и соблюдением действующей нормативно-технической документации;
- применения источников бесперебойного питания, которые поддерживают автономную работу систем при пропадании напряжения питания на основном вводе.

Система имеет автономное вторичное электропитание от внутренних аккумуляторных батарей и способного обеспечить нормальное функционирование, в условиях отсутствия внешнего напряжения питания 220 В. При пропадании основного электропитания, происходит автоматическое переключение на автономное вторичное электропитание от аккумуляторных батарей.

При монтаже электропроводки выполнить цветовую маркировку жил кабелей в соответствии с требованиями гл.2.1. ПУЭ.

Защитное заземление (зануление) электрооборудования и устройств системы СДС выполнить в соответствии с ПУЭ, СП 76.13330.2016, требованиями ГОСТ 12.1.030-81 и технической документации заводов-изготовителей на проектируемое оборудование.

9. ОПИСАНИЕ ТЕХНИЧЕСКИХ РЕШЕНИЙ ПО ЗАЩИТЕ ИНФОРМАЦИИ

Данный пункт не разрабатывается.

10. ХАРАКТЕРИСТИКА И ОБОСНОВАНИЕ ПРИНЯТЫХ ТЕХНИЧЕСКИХ РЕШЕНИЙ В ОТНОШЕНИИ ТЕХНОЛОГИЧЕСКИХ СЕТЕЙ СВЯЗИ, ПРЕДНАЗНАЧЕННЫХ ДЛЯ ОБЕСПЕЧЕНИЯ ПРОИЗВОДСТВЕННОЙ ДЕЯТЕЛЬНОСТИ НА ОБЪЕКТЕ КАПИТАЛЬНОГО СТРОИТЕЛЬСТВА, УПРАВЛЕНИЯ ТЕХНОЛОГИЧЕСКИМИ ПРОЦЕССАМИ ПРОИЗВОДСТВА (СИСТЕМУ ВНУТРЕННЕЙ СВЯЗИ, ЧАСОФИКАЦИЮ, РАДИОФИКАЦИЮ (ВКЛЮЧАЯ ЛОКАЛЬНЫЕ СИСТЕМЫ ОПОВЕЩЕНИЯ В РАЙОНАХ РАЗМЕЩЕНИЯ ПОТЕНЦИАЛЬНОГО ТЕЛЕНАБЛЮДЕНИЯ) – ДЛЯ ОБЪЕКТОВ ПРОИЗВОДСТВЕННОГО НАЗНАЧЕНИЯ

Данный пункт не разрабатывается.

11. ОПИСАНИЕ СИСТЕМЫ ВНУТРЕННЕЙ СВЯЗИ, ЧАСОФИКАЦИИ, РАДИОФИКАЦИИ, ТЕЛЕВИДЕНИЯ – ДЛЯ ОБЪЕКТОВ НЕПРОИЗВОДСТВЕННОГО НАЗНАЧЕНИЯ

Санузел для МГН на первом этаже (пом. 104а) здания оснащается комплектом вызова персонала, переговорными устройствами. Устанавливается следующее оборудование:

- кнопка вызова со шнуром GC-0423W2;
- кнопка сброса GC-0421W2;
- переговорное устройство GC-2001W3.

Непосредственно над входной дверью в санузел МГН, снаружи помещения, размещается сигнальная лампа (светозвуковой сигнализатор) GC-0611W4.

Источник питания ББП-50 располагается на 1 этаже и служит для питания сигнальной лампы GC-0611W4.

В помещении охраны (пом. 103) размещается пульт диспетчерской связи на 12 абонентов GC-1036F2.

Центральный вход оборудуется переговорными устройствами GC-2001P5. Устройство располагается перед подъемом на пандус на стойке Штольц (на высоте в соответствии с ГОСТ Р 51671-2020 пункт 7.2.2.3 на высоте от 1,0 до 1,2 м от уровня доступной для инвалида поверхности передвижения) и непосредственно перед входной дверью. Вызывные панели подключены к пульту диспетчерской связи в помещении охраны.

Зона отдыха МГН оборудуется переговорным устройством GC-2001P5. Вызывные панели подключены к пульту диспетчерской связи в помещении охраны.

В соответствии с СП 132.13330.2011 в помещении 103 (помещение охраны) предусматривается пульт селекторной связи GC-1036F2, обеспечивающий организацию оперативной громкоговорящей связи с помещениями с массовым пребыванием людей (пом. 131, 146) и всех входов посредством установки абонентских устройств громкой селекторной связи GC-2001P5.

12. ОБОСНОВАНИЕ ПРИМЕНЯЕМОГО КОММУТАЦИОННОГО ОБОРУДОВАНИЯ, ПОЗВОЛЯЮЩЕГО ПРОИЗВОДИТЬ УЧЕТ ИСХОДЯЩЕГО ТРАФИКА НА ВСЕХ УРОВНЯХ ПРИСОЕДИНЕНИЯ


Данный пункт не разрабатывается.

13. ХАРАКТЕРИСТИКА ПРИНЯТОЙ ЛОКАЛЬНОЙ ВЫЧИСЛИТЕЛЬНОЙ СЕТИ (ПРИ НАЛИЧИИ) – ДЛЯ ОБЪЕКТОВ ПРОИЗВОДСТВЕННОГО НАЗНАЧЕНИЯ

Данный пункт не разрабатывается.

14. ОБОСНОВАНИЕ ВЫБРАННОЙ ТРАССЫ ЛИНИИ СВЯЗИ К УСТАНОВЛЕННОЙ ТЕХНИЧЕСКИМИ УСЛОВИЯМИ ТОЧКИ ПРИСОЕДИНЕНИЯ, В ТОМ ЧИСЛЕ ВОЗДУШНЫХ И ПОДЗЕМНЫХ УЧАСТКОВ. ОПРЕДЕЛЕНИЕ ГРАНИЦ ОХРАННЫХ ЗОН ЛИНИЙ СВЯЗИ ИСХОДЯ ИЗ ОСОБЫХ УСЛОВИЙ ПОЛЬЗОВАНИЯ

Данный пункт не разрабатывается.

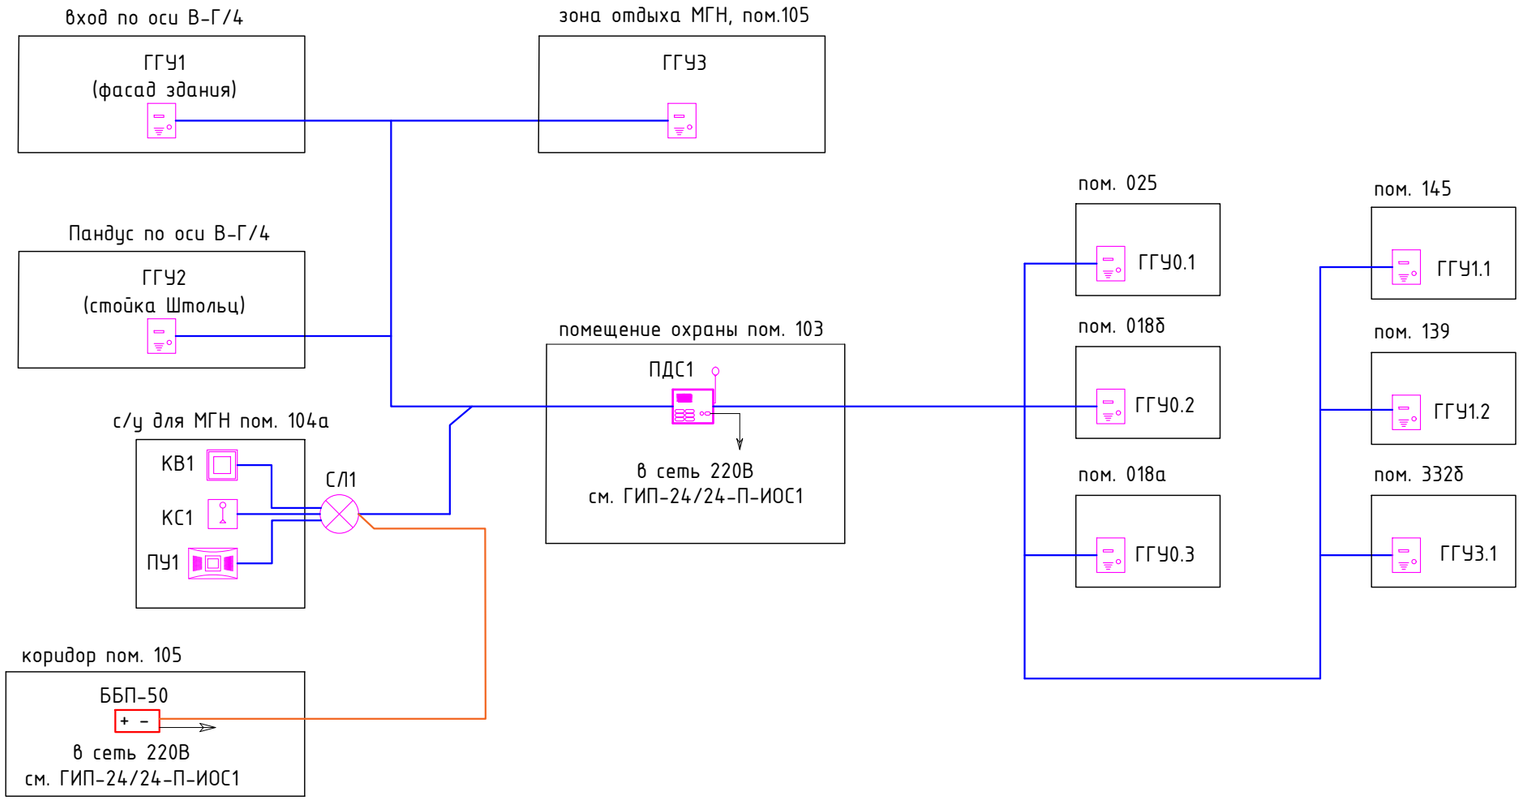

Условные обозначения:

- пульт диспетчерской связи на 12 абонентов GC-1036F2 (ПДС)
- громкоговорящее переговорное устройство GC-2001P5 (ГГУ) с указанием порядкового номера
- переговорное устройство GC-2001W3 (ГГУ) с указанием порядкового номера
- сигнальная лампа GC-0611W4 (СЛ) с указанием порядкового номера
- кнопка сброса GC-0421W2 (КС) с указанием порядкового номера
- кнопка вызова со шнуром GC-0423W2 (КВ) с указанием порядкового номера
- блок питания ББП-50 (ББП-50)
- кабель КПСВВнг(А)-LSLTx 1х2х0,5
- кабель питания ВВГнг(А)-LSLTx 1х2х1,5


Примечание:

1. Данный лист рассматривать совместно с листами 2-4.
2. Все кабельные концы промаркировать в соответствии с типами подключаемых устройств.
3. Электропитание учтено смежным разделом ГИП-28/24-П-ИОС1.

						ГИП-28/24-П-ИОС5.6	
						Капитальный ремонт общеобразовательного учреждения ГБОУ Школа № 218, расположенного по адресу: г. Москва, ул. Вучетича, д. 6	
Изм.	Кол.уч	Лист	№док	Подп.	Дата		
Разраб.		Козлова			11.2024	Общеобразовательное учреждение	Стадия: П; Лист: 1; Листов: 4
Проверил		Улитина			11.2024		
ГИП		Гущин			11.2024	Принципиальная схема	И-ГРУПП ПРОЕКТНО-СТРОИТЕЛЬНАЯ КОМПАНИЯ
Н.контр.		Шукшин			11.2024		

Взам. инв.№ | Подпись и дата | Инв. № подл.

Формат А3

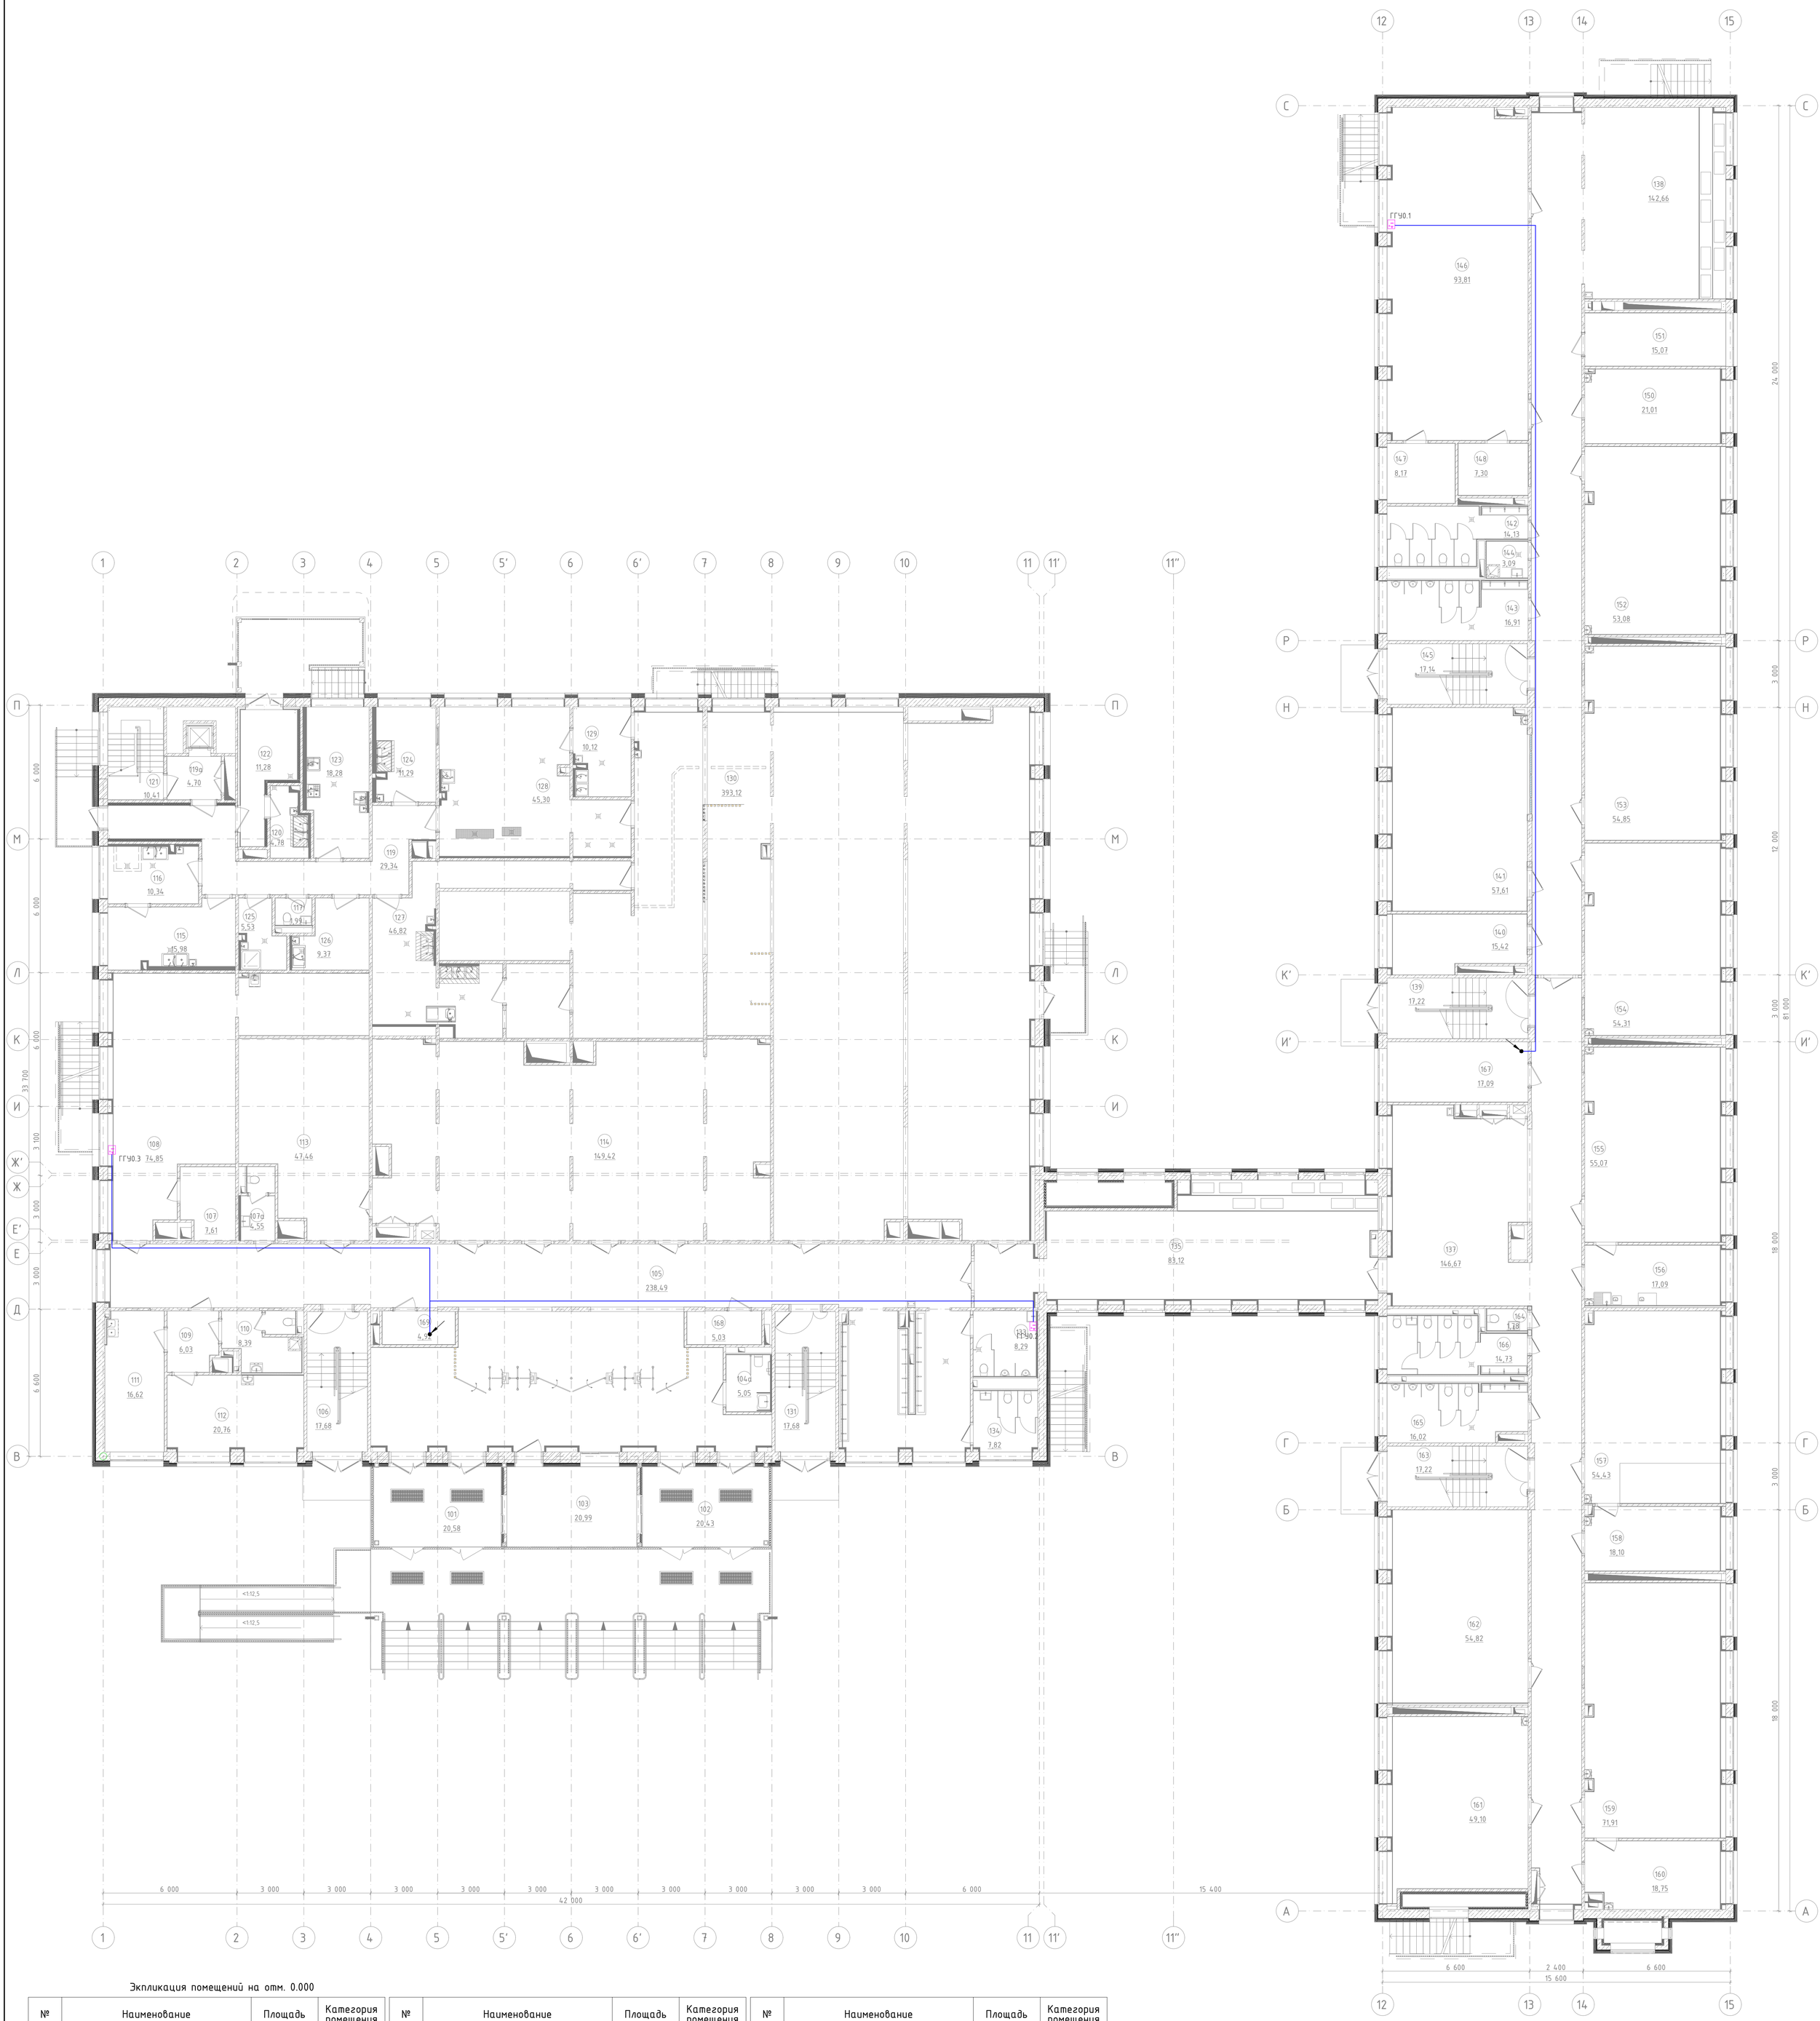

Экспликация помещений на отм. 0.000

№	Наименование	Площадь	Категория помещения
101	Тамбур	20,58	
102	Тамбур	20,43	
103	Комната охраны с диспетчерским пунктом	20,99	
104а	Сан. узел МГН	5,05	
105	Вестибюль	238,49	
106	Лестничная клетка (тип Н2)	17,68	
107	Гардеробная комната (для учителей)	7,61	
107а	Сан. узел для персонала	4,55	
108	Кабинет с рабочим пространством для учителей Тип 2	74,85	
109	Тамбур	6,03	
110	Туалет медблока с местом для приготовления дезинфицирующих средств и хранения уборочного инвентаря	8,39	
111	Процедурный (прививочный) кабинет	16,62	
112	Кабинет врача	20,76	
113	Гардероб для обучающихся	47,46	
114	Гардероб для обучающихся	149,42	
115	Цех вторичной обработки овощей	15,98	В3
116	Цех первичной обработки овощей	10,34	В3
117	Сан. узел для персонала	1,99	
119	Коридор	29,34	
119а	Тамбур	4,70	
120	Моечная обратной тары	4,78	В4
121	Лестничная клетка (для персонала)	10,41	
122	Загрузочный цех	11,28	В3
123	Мясо-рыбный цех	18,28	В3

№	Наименование	Площадь	Категория помещения
124	Моечная кухонной посуды	11,29	В3
125	ПУИ	5,53	
126	Помещение временного хранения пищевых отходов	9,37	В4
127	Моечная столовой посуды	46,82	В4
128	Горячий цех	45,30	В3
129	Холодный цех	10,12	В3
130	Обеденный зал	393,12	
131	Лестничная клетка (тип Н2)	17,68	
133	Сан. узел для мальчиков	8,29	
134	Сан. узел для девочек	7,82	
135	Коридор	83,12	
137	Коридор	146,67	
138	Коридор	142,66	
139	Лестничная клетка (тип Л1)	17,22	
140	Административный кабинет Тип 1	15,42	
141	Учебный кабинет	57,61	
142	Сан. узел для девочек	14,13	
143	Сан. узел для мальчиков	16,91	
144	ПУИ	3,09	В4
145	Лестничная клетка (тип Л1)	17,14	
146	Гимнастический зал	93,81	
147	Раздевальные	8,17	
148	Раздевальные	7,30	
150	Кабинет для индивидуальных занятий, в т.ч. с коррекционным педагогом	21,01	

№	Наименование	Площадь	Категория помещения
151	Помещение для прокладки инженерных коммуникаций	15,07	В3
152	Учебный кабинет	53,08	
153	Учебный кабинет	54,85	
154	Учебный кабинет	54,31	
155	Учебные кабинет для изучения естествознания: химия	55,07	
156	Лабораторская кабинета химии	17,09	В3
157	Учебные кабинет для изучения естествознания: физика	54,43	
158	Лабораторская кабинета физики	18,10	В3
159	Учебные кабинеты для изучения естествознания: биологии + ОБЗР	71,91	
160	Лабораторская кабинета биологии	18,75	В3
161	Кабинет материальной технологии Тип 2	49,10	В3
162	Кабинет материальной технологии Тип 1	54,82	В3
163	Лестничная клетка (тип Л1)	17,22	
164	Сан. узел персонала	1,78	
165	Сан. узел для мальчиков	16,02	
166	Сан. узел для девочек с комнатой личной гигиены	14,73	
167	Серверная	17,09	В3
168	Кроссовая	5,03	В3
169	Кроссовая	4,92	В3
		2 558,98 м²	

Условные обозначения:

– громкоговорящее переговорное устройство GC-2001PS (ГГУ) с указанием порядкового номера

– кабель КПСВВнг(А)-LSLTx 1х2х0,5

Примечания:

1. Принципиальную схему см. лист 1.
2. Установку оборудования выполнить в соответствии с действующими нормативными документами.
3. Пульт диспетчерской связи разместить в помещениях охраны на 1 этаже согласно графической части.
4. Линии связи выполнить кабелем КПСВВнг(А)-LSLTx 1х2х0,5. Шлейфы питания выполнить кабелем ВВГнг(А)-LSLTx 1х2х1,5.
5. Прокладка кабеля внутри здания выполняется в гофрированных ПВХ трубах диаметром 20 мм в запотолочном пространстве, опуски по стенам в штробах.
6. Трассы и способы прокладки могут быть изменены с обязательным соблюдением действующих норм.
7. Оборудование размещать с учетом архитектурных особенностей.
8. Проход кабельных линий через стены, перекрытия выполнить в стальных гильзах диам. 25 мм. После прокладки отверстия заделать противопожарным герметиком.

Согласовано

Взам. инв.N

Подпись и дата

Инв.N подл.

Изм.	Кол.уч	Лист	№док	Подп.	Дата
Разраб.		Козлова			11.2024
Проверил		Улитина			11.2024
ГИП		Гущин			11.2024
Н.контр.		Шукшин			11.2024

ГИП-28/24-П-ИОС5.6

Капитальный ремонт общеобразовательного учреждения ГБОУ Школа № 218, расположенного по адресу: г. Москва, ул. Вучетича, д. 6


Общеобразовательное учреждение

Стадия	Лист	Листов
П	2	

План подвала

И-ГРУПП ПРОЕКТНО-СТРОИТЕЛЬНАЯ КОМПАНИЯ

Формат А0

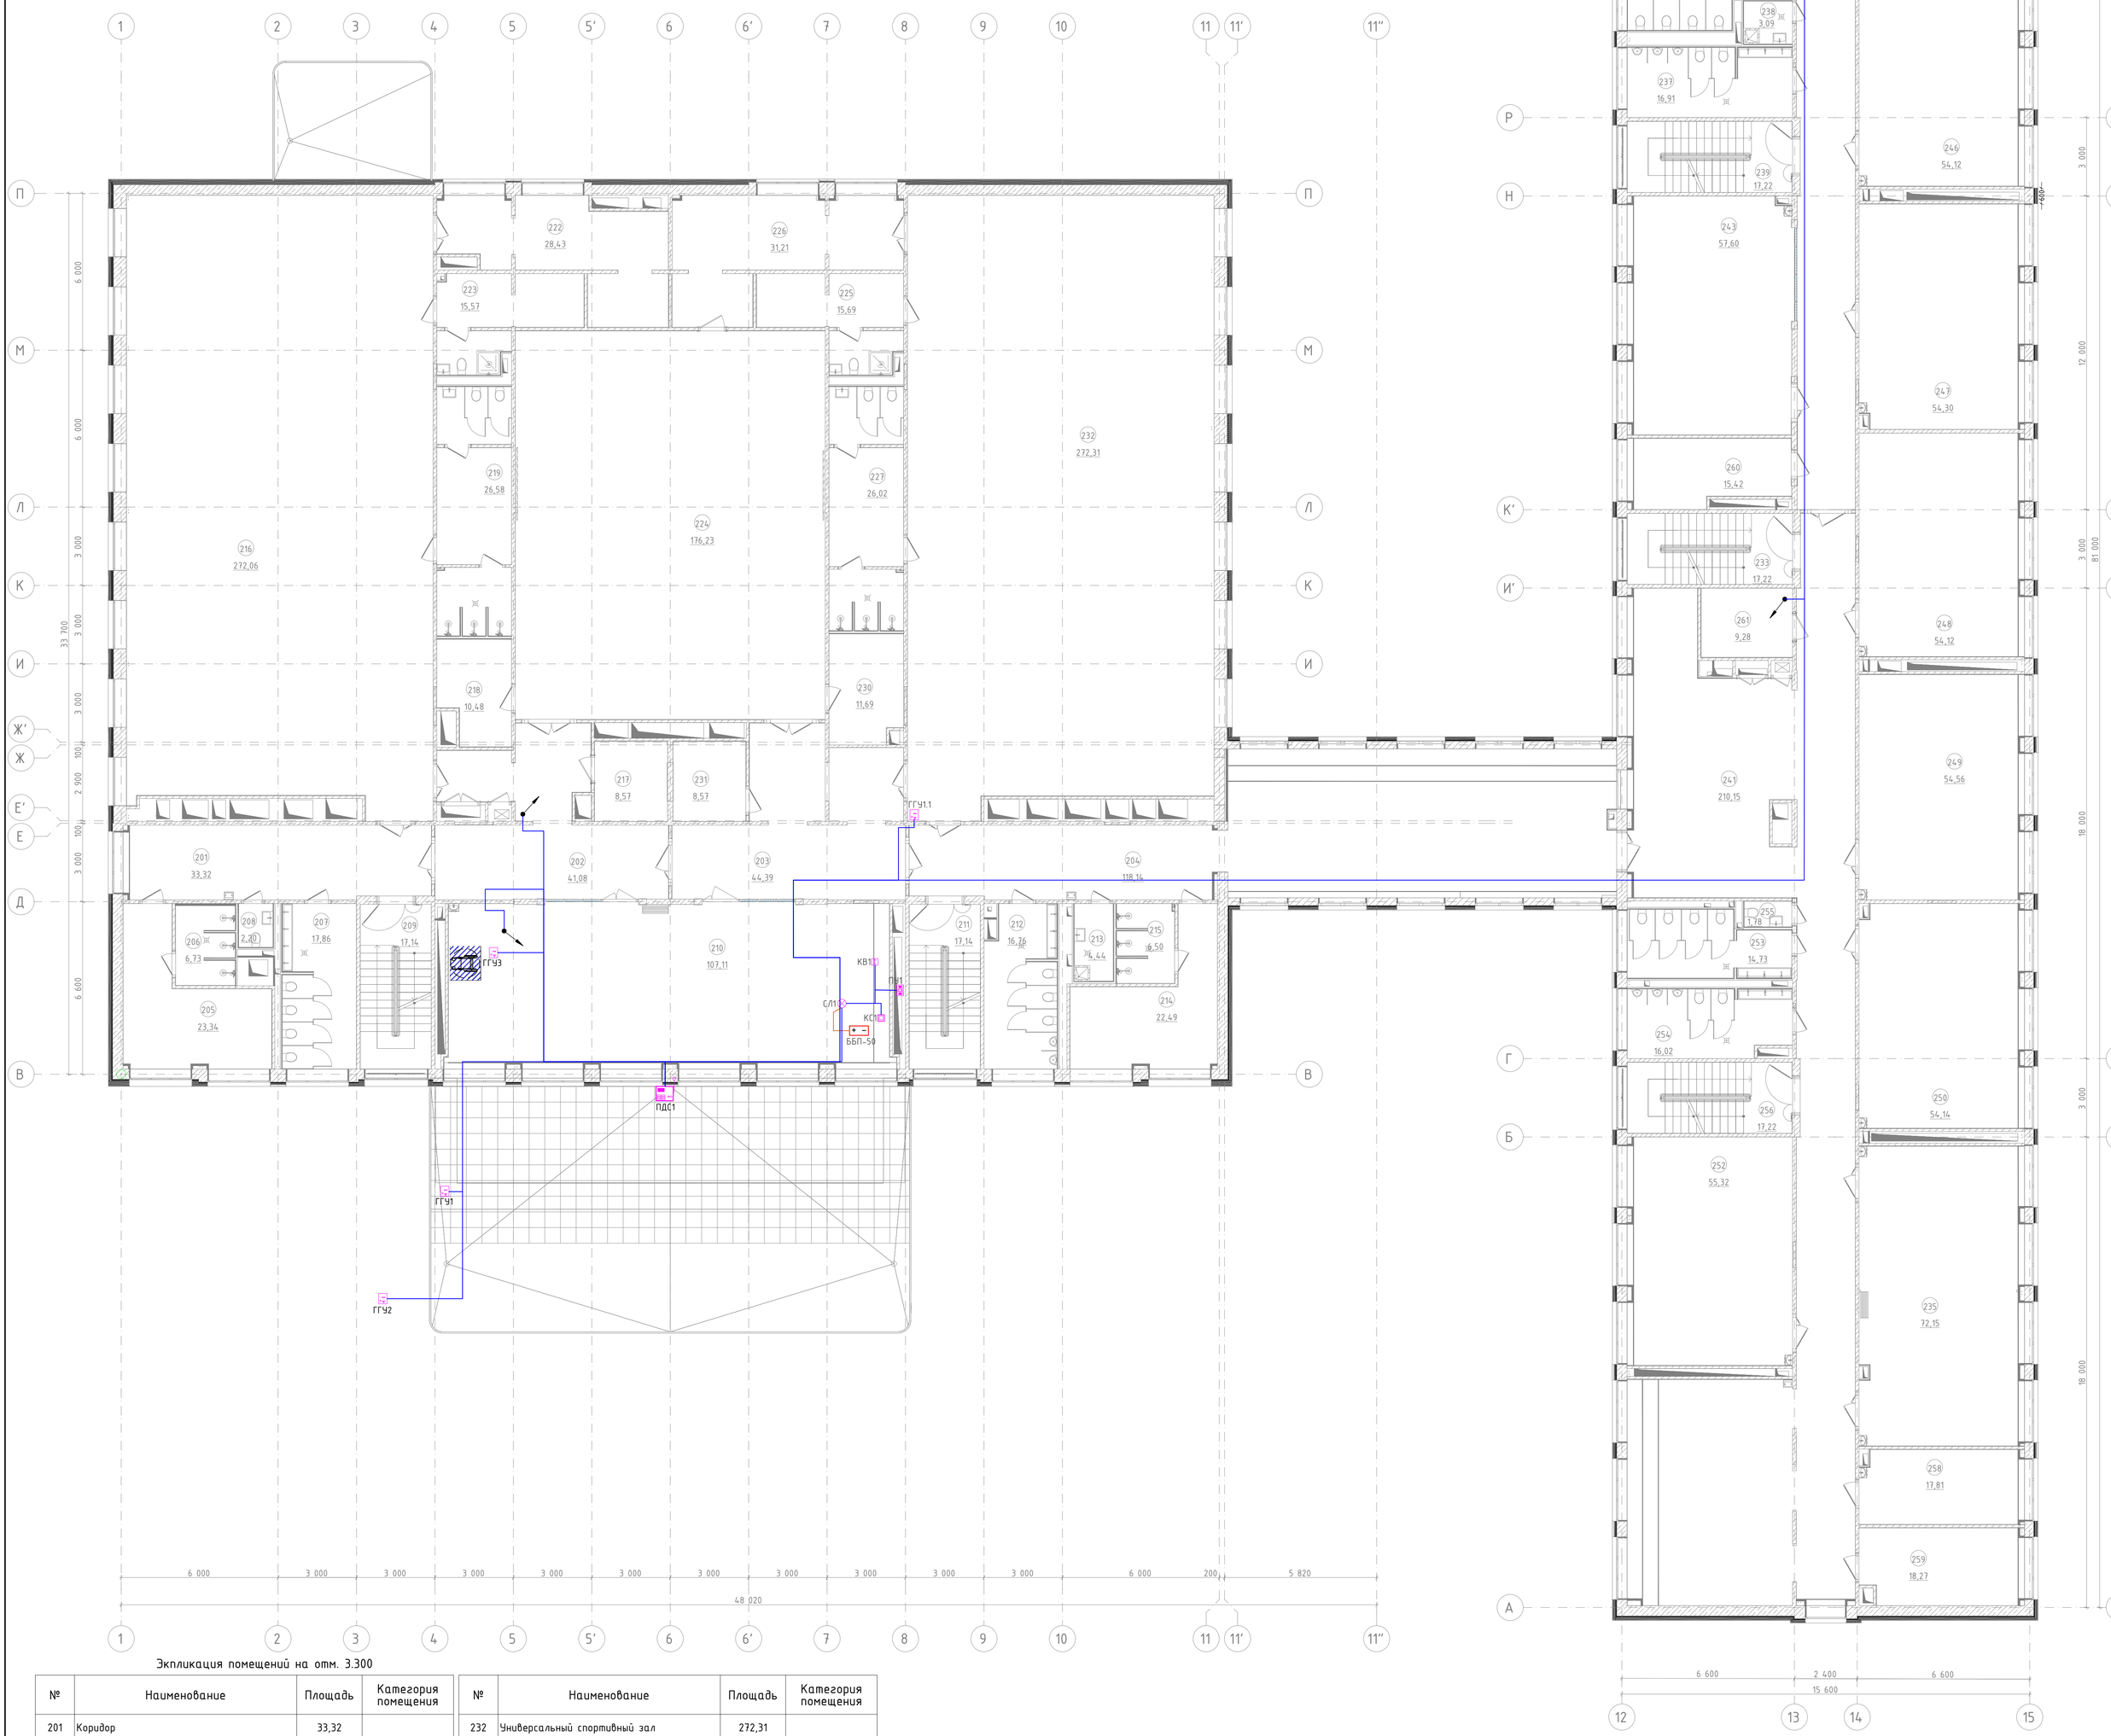

Экспликация помещений на отм. 3.300

№	Наименование	Площадь	Категория помещения
201	Коридор	33,32	
202	Коридор	41,08	
203	Коридор	44,39	
204	Коридор	118,14	
205	Раздевальная	23,34	
206	Душевая	6,73	
207	Сан. узел для девочек	17,86	
208	Сан. узел для персонала	2,20	
209	Лестничная клетка (тип Н2)	17,14	
210	Кабинет ИЗО	107,11	
211	Лестничная клетка (тип Н2)	17,14	
212	Сан. узел для мальчиков	16,76	
213	ПУИ	4,44	В4
214	Раздевальная	22,49	
215	Душевая	6,50	
216	Универсальный спортивный зал	272,06	
217	Кроссовая	8,57	В3
218	Артистическая с хранением костюмов	10,48	В3
219	Раздевальная	26,58	
222	Снарядная	28,43	В3
223	Комната инструктора с душем и сан. узлом	15,57	
224	Актовый зал	176,23	
225	Комната инструктора с душем и сан. узлом	15,69	
226	Снарядная	31,21	В3
227	Раздевальная	26,02	
230	Артистическая с хранением костюмов	11,69	В3
231	Кладовая инвентаря	8,57	В4

№	Наименование	Площадь	Категория помещения
232	Универсальный спортивный зал	272,31	
233	Лестничная клетка (тип Л1)	17,22	
235	Кабинет иностранного языка	72,15	
236	Сан. узел для девочек	13,84	
237	Сан. узел для мальчиков	16,91	
238	ПУИ	3,09	В4
239	Лестничная клетка (тип Л1)	17,22	
240	Кабинет естествознания Тип 1	110,06	
241	Коридор	210,15	
243	Учебный кабинет	57,60	
244	Коридор	141,66	
245	Учебный кабинет	54,36	
246	Учебный кабинет	54,12	
247	Учебный кабинет	54,30	
248	Учебный кабинет	54,12	
249	Учебный кабинет	54,56	
250	Учебный кабинет	54,14	
252	Учебный кабинет	55,32	
253	Сан. узел для девочек	14,73	
254	Сан. узел для мальчиков	16,02	
255	Сан. узел для персонала	1,78	
256	Лестничная клетка (тип Л1)	17,22	
258	Кабинет для индивидуальных занятий, в т.ч. с учителем логопедом	17,81	
259	Административный кабинет Тип 1	18,27	
260	Административный кабинет Тип 1	15,42	
261	Кроссовая	9,28	В3
		2 533,40 м²	

Условные обозначения:

- пульт диспетчерской связи на на 12 абонентов GC-1036F2 (ПДС)
- громкоговорящее переговорное устройство GC-2001P5 (ГГУ) с указанием порядкового номера
- переговорное устройство GC-2001W3 (ГГУ) с указанием порядкового номера
- сигнальная лампа GC-0611W4 (СЛ) с указанием порядкового номера
- кнопка сброса GC-0421W2 (КС) с указанием порядкового номера
- кнопка вызова со шнуром GC-0423W2 (КВ) с указанием порядкового номера
- блок питания ББП-50 (ББП-50)
- кабель КПСВВнг(А)-LSLTx 1х2х0,5
- кабель питания ВВГнг(А)-LSLTx 1х2х1,5
- зона отдыха МГН

Примечания:

1. Принципиальную схему см. лист 1.
2. Установку оборудования выполнить в соответствии с действующими нормативными документами.
3. Пульт диспетчерской связи разместить в помещениях охраны на 1 этаже согласно графической части.
4. Линии связи выполнить кабелем КПСВВнг(А)-LSLTx 1х2х0,5. Шлейфы питания выполнить кабелем ВВГнг(А)-LSLTx 1х2х1,5.
5. Прокладка кабеля внутри здания выполняется в гофрированных ПВХ трубах диаметром 20 мм в запотолочном пространстве, опуски по стенам в штробах.
6. Трассы и способы прокладки могут быть изменены с обязательным соблюдением действующих норм.
7. Оборудование размещать с учетом архитектурных особенностей.
8. Проход кабельных линий через стены, перекрытия выполнить в стальных гильзах диам. 25 мм. После прокладки отверстия заделать противопожарным герметиком.

Изм.	Кол.уч	Лист	№док	Подп.	Дата	ГИП-28/24-П-ИОС5.6		
						Капитальный ремонт общеобразовательного учреждения ГБОУ Школа № 218, расположенного по адресу: г. Москва, ул. Вучетича, д. 6		
Разраб.		Козлова			11.2024	Общеобразовательное учреждение	Стадия	Лист	Листов
Проверил		Улитина			11.2024		П	3	
ГИП		Гущин			11.2024	План 1 этажа	И-ГРУПП ПРОЕКТНО-СТРОИТЕЛЬНАЯ КОМПАНИЯ		
Н.контр.		Шукшин			11.2024				


Согласовано

Взам. инв.N

Подпись и дата

Инв.N подл.

Формат А0

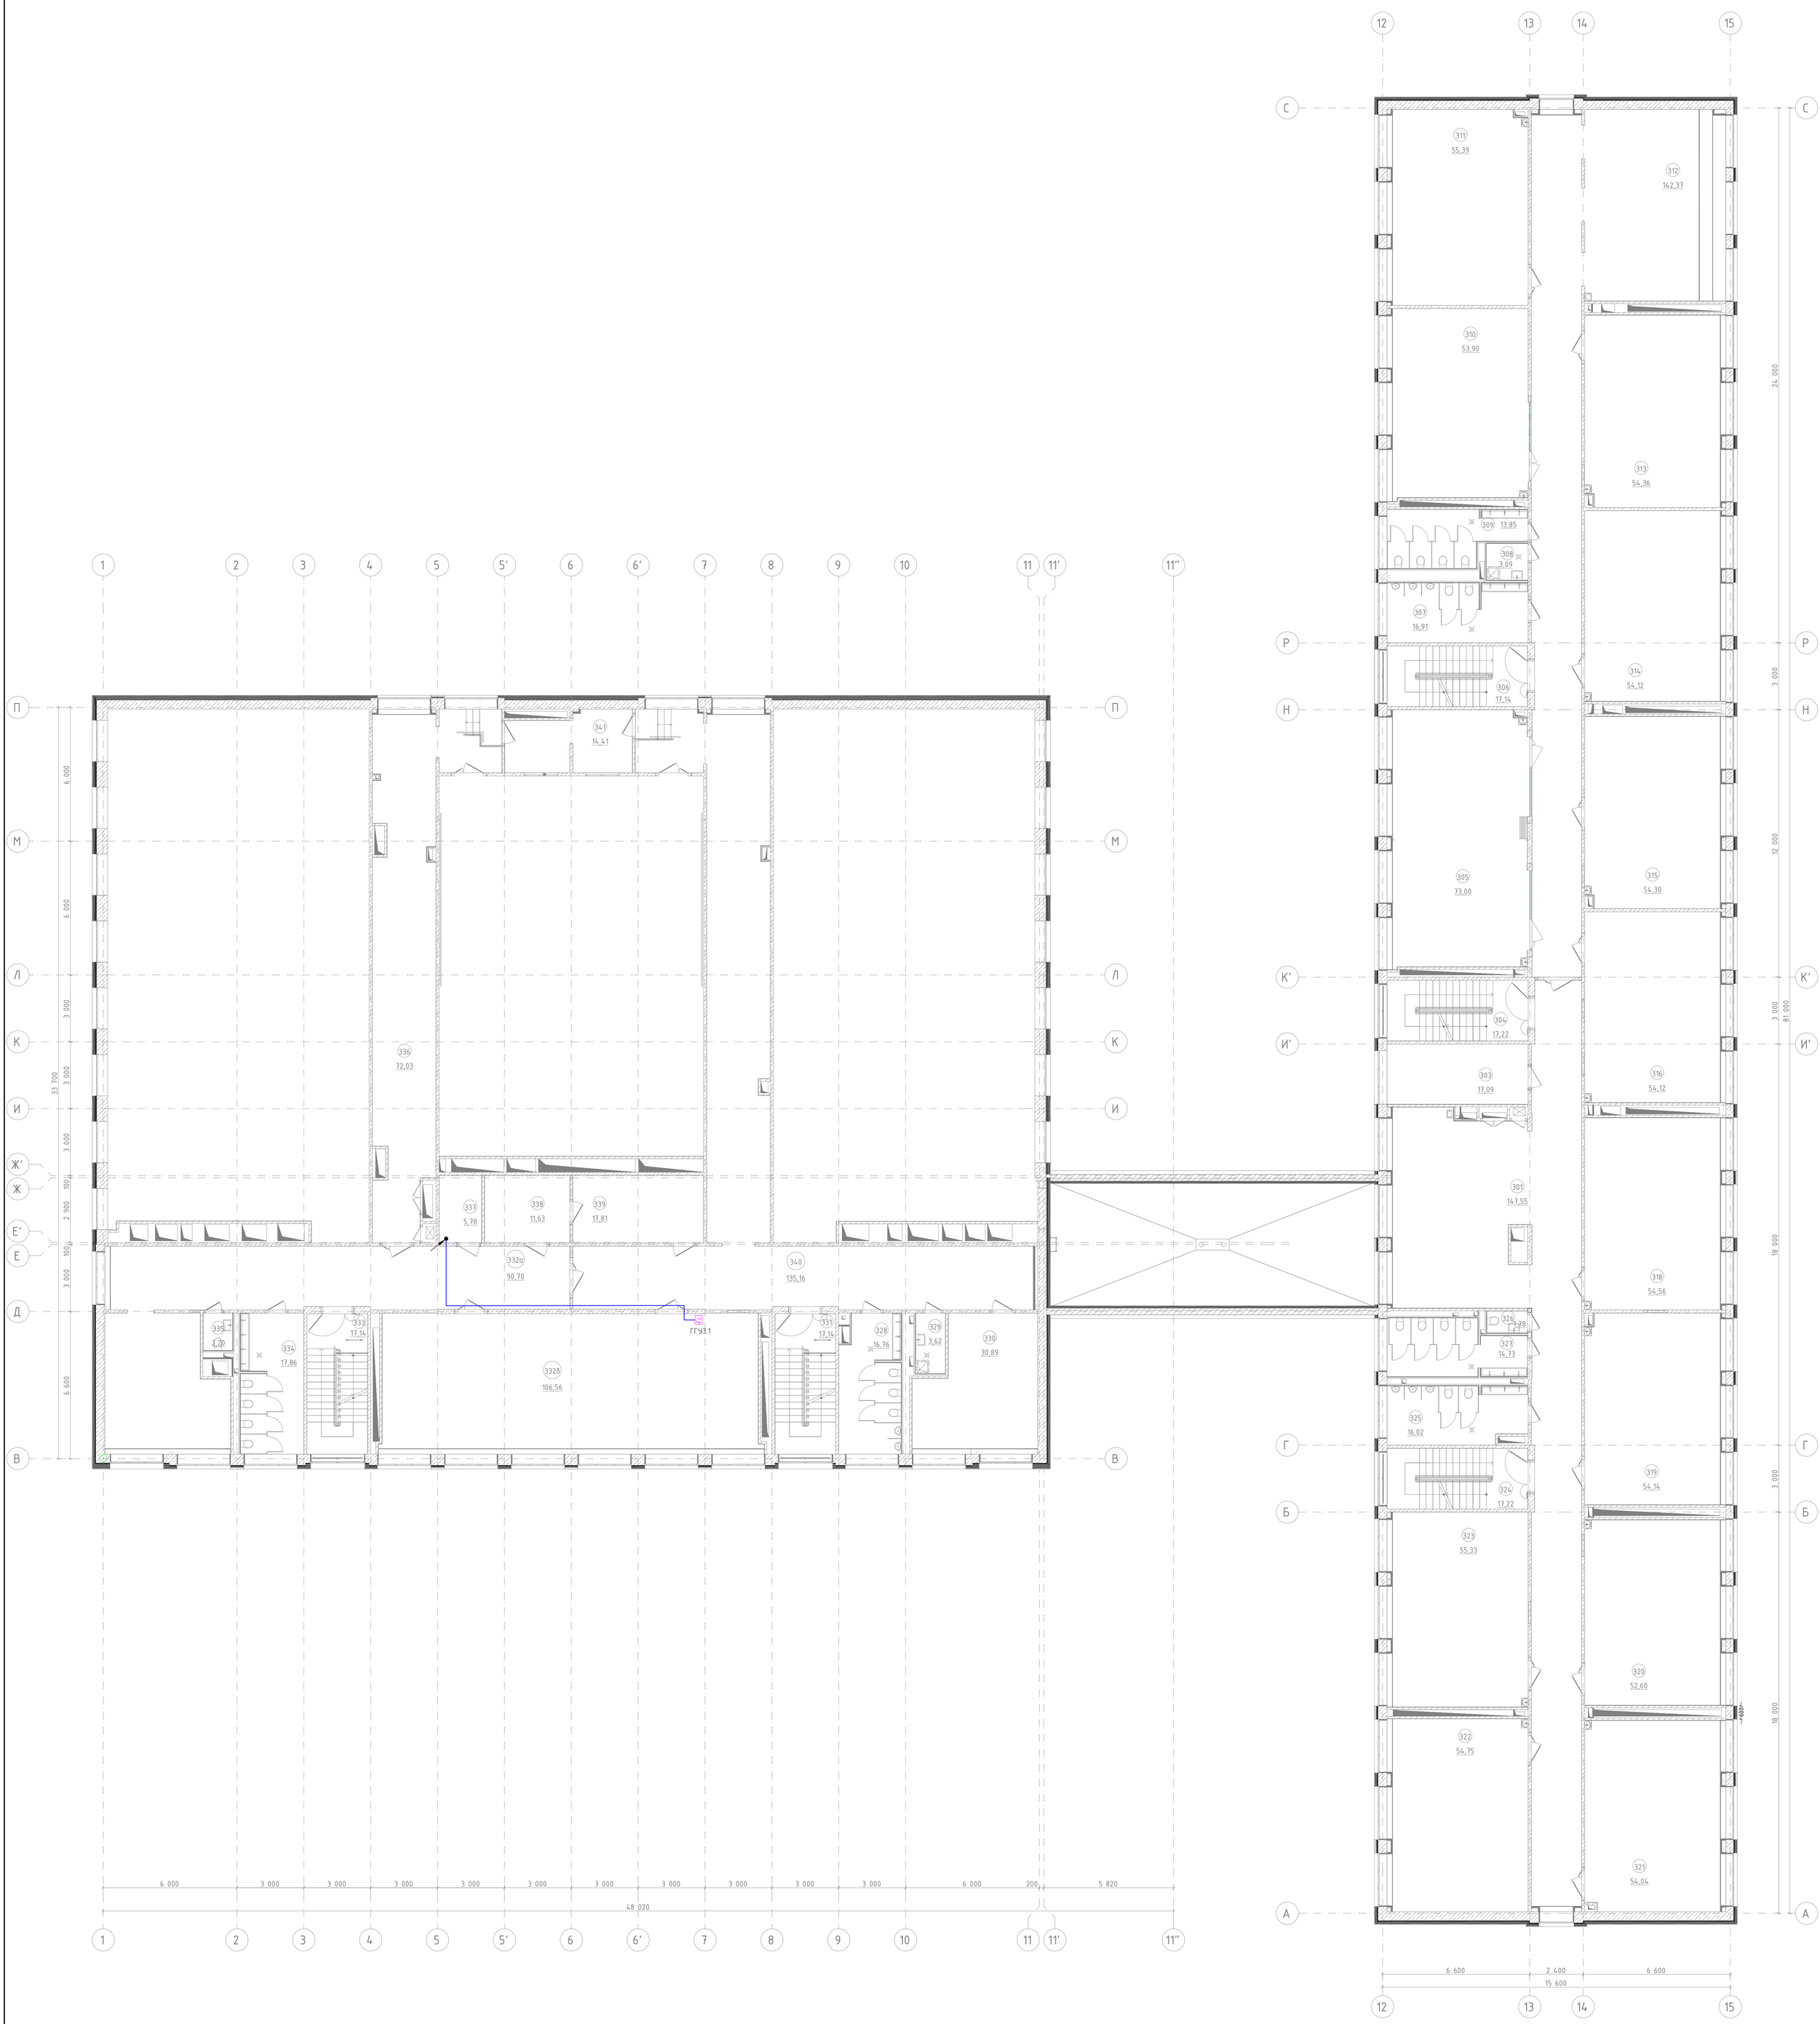

Экспликация помещений на отм. 6.600

№	Наименование	Площадь	Категория помещения
301	Коридор	147,55	
303	Серверная	17,09	В3
304	Лестничная клетка (тип Л1)	17,22	
305	Кабинет иностранного языка	73,00	
306	Лестничная клетка (тип Л1)	17,14	
307	Сан. узел для мальчиков	16,91	
308	ПУИ	3,09	В4
309	Сан. узел для девочек	13,85	
310	Учебный кабинет	53,90	
311	Учебный кабинет	55,39	
312	Коридор	142,37	
313	Учебный кабинет	54,36	
314	Учебный кабинет	54,12	
315	Учебный кабинет	54,30	
316	Учебный кабинет	54,12	
318	Учебный кабинет	54,56	
319	Учебный кабинет	54,14	
320	Учебный кабинет	52,60	
321	Учебный кабинет	54,04	
322	Учебный кабинет	54,75	
323	Учебный кабинет	55,33	

№	Наименование	Площадь	Категория помещения
324	Лестничная клетка (тип Л1)	17,22	
325	Сан. узел для мальчиков	16,02	
326	Сан. узел персонала	1,78	
327	Сан. узел для девочек	14,73	
328	Сан. узел для мальчиков	16,76	
329	ПУИ	3,62	В4
330	Библиотека. Фонд хранения	30,89	В3
331	Лестничная клетка (тип Н2)	17,14	
332а	Коридор	90,70	
332б	Читальный зал	106,56	
333	Лестничная клетка (тип Н2)	17,14	
334	Сан. узел для девочек	17,86	
335	Сан. узел для персонала	2,20	
336	Коридор	72,03	
337	Кроссовая	5,78	В3
338	Кабинет для индивидуальных занятий. Студия звукозаписи	11,63	
339	Медиакласс	17,81	
340	Коридор	135,16	
341	Технический центр	14,41	В3
		1 709,27 м²	

Условные обозначения:

ГГУ3.1 – громкоговорящее переговорное устройство GC-2001P5 (ГГУ) с указанием порядкового номера

– кабель КПСВВнг(А)-LSLTx 1х2х0,5

Примечания:

1. Принципиальную схему см. лист 1.
2. Установку оборудования выполнить в соответствии с действующими нормативными документами.
3. Пульт диспетчерской связи разместить в помещениях охраны на 1 этаже согласно графической части.
4. Линии связи выполнить кабелем КПСВВнг(А)-LSLTx 1х2х0,5. Шлейфы питания выполнить кабелем ВВГнг(А)-LSLTx 1х2х1,5.
5. Прокладка кабеля внутри здания выполняется в гофрированных ПВХ трубах диаметром 20 мм в запотолочном пространстве, опуски по стенам в штробах.
6. Трассы и способы прокладки могут быть изменены с обязательным соблюдением действующих норм.
7. Оборудование размещать с учетом архитектурных особенностей.
8. Проход кабельных линий через стены, перекрытия выполнить в стальных гильзах диам. 25 мм. После прокладки отверстия заделать противопожарным герметиком.

Изм.	Кол.уч	Лист	№док.	Подп.	Дата	ГИП-28/24-П-ИОС5.6		
						Капитальный ремонт общеобразовательного учреждения ГБОУ Школа № 218, расположенного по адресу: г. Москва, ул. Вучетича, д. 6		
Разраб.		Козлова			11.2024	Общеобразовательное учреждение	Стадия	Лист	Листов
Проверил		Улитина			11.2024		П	4	
ГИП		Гущин			11.2024	План 3 этажа	И-ГРУПП ПРОЕКТНО-СТРОИТЕЛЬНАЯ КОМПАНИЯ		
Н.контр.		Шукшин			11.2024				

Формат А0

Согласовано

Взам. инв.№

Подпись и дата

Инв.№ подл.

Позиция	Наименования и техническая характеристика	Тип, марка, обозначение документа, опросного листа	Код оборудования, изделия, материала	Завод изготовитель	Единица измерения	Коли-чество	Масса единицы, кг.	Примечания
1	**2**	3	4	5	6	7	8	9
	Оборудование							
1	Кнопка вызова со шнуром	GC-0423W2		ООО «СКБ Телси»	шт	1		
2	Кнопка сброса	GC-0421W2		ООО «СКБ Телси»	шт	1		
3	Сигнальная лампа	GC-0611W4		ООО «СКБ Телси»	шт	1		
4	Переговорное устройство	GC-2001W3		ООО «СКБ Телси»	шт	1		
5	Громкоговорящее переговорное устройство	GC-2001P5		ООО «СКБ Телси»	шт	9		
6	Блок питания	ББП-50 исп. 1		AccordTec	шт	1		
7	Аккумулятор герметичный свинцово-кислотный 12В/7Ач	DT 1207		Delta	шт	1		
8	Пульт диспетчерской связи на 12 абонентов	GC-1036F2		ООО «СКБ Телси»	шт	1		
	Кабельные изделия							
1	Кабель	КПСВВнг(А)-LSLTx 1х2х0,5		СПКБ-Техно	м	540		
2	Кабель	ВВГнг(А)-LSLTx 1х2х1,5		Сегмент Энерго	м	5		
	Материалы							
1	Труба HFFRLS гибкая с зондом D=20 с комплектом креплений (скоба однолапковая, дюбель металлический)	60120HFFRLS		Экопласт	м	540		
2	Стойка Штольц			ООО «СКБ Телси»	шт	1		
3	Труба стальная для гильз D=25			Россия	м	5		
4	Герметик противопожарный	Огнеза-ГТ		Огнеза	бал.	2		
5	Труба ПНД диам. 20мм с комплектом креплений	CTG20-20-K02-050-1		IEK	м	15		

Согласовано | Гл. специалист | Нач. группы

Изм.	Кол.	Лист	№	Подпись	Дата	ГИП-28/24-П-ИОС5.6.СО		
Разработал		Козлова			11.2024	Приложение 1. Спецификация оборудования, изделий и материалов	Стадия	Лист	Листов
Проверил		Улитина			11.2024		П	1	1
ГИП		Гущин			11.2024		И-ГРУПП ПРОЕКТНО-СТРОИТЕЛЬНАЯ КОМПАНИЯ		
Н.контр.		Шукшин			11.2024				

Формат А3