ООО «И-Групп»

Ассоциация в области архитектурно-строительного проектирования
«Саморегулируемая организация «СОВЕТ ПРОЕКТИРОВЩИКОВ»
(СРО-П-011-16072009). Регистрационный номер: П-011-007722770040-1134.

Заказчик: Автономная некоммерческая организация
«Развитие Городских Технологий» (АНО «РГТ»)

Договор № 423/П-24-АНО от 26.04.2024 г.

«Выполнение проектно-изыскательских работ на капитальный ремонт общеобразовательного учреждения (ГБОУ Школа № 218), расположенного по адресу: г. Москва, ул. Вучетича, д. 6»

ПРОЕКТНАЯ ДОКУМЕНТАЦИЯ

Раздел 3 «Объемно-планировочные и архитектурные решения. Ведомость объемов работ»

Приложение к П-АР.ВОР

ГИП-28/24-П-АР

2025 г.

ООО «И-Групп»

Ассоциация в области архитектурно-строительного проектирования
«Саморегулируемая организация «СОВЕТ ПРОЕКТИРОВЩИКОВ»
(СРО-П-011-16072009). Регистрационный номер: П-011-007722770040-1134.

Заказчик: Автономная некоммерческая организация
«Развитие Городских Технологий» (АНО «РГТ»)

Договор № 423/П-24-АНО от 26.04.2024 г.

«Выполнение проектно-изыскательских работ на капитальный ремонт общеобразовательного учреждения (ГБОУ Школа № 218), расположенного по адресу: г. Москва, ул. Вучетича, д. 6»

ПРОЕКТНАЯ ДОКУМЕНТАЦИЯ

Раздел 3 «Объемно-планировочные и архитектурные решения. Ведомость объемов работ»

Приложение к П-АР.ВОР

ГИП-28/24-П-АР

Генеральный директор: М.В. Татошвили

Главный инженер проекта: А.В. Гущин

2025 г.

Лист	Наименование	Примечание
2	Ведомость рабочих чертежей	
3	План демонтажа стен подвала	
4	План демонтажа стен 1 этажа	
5	План демонтажа стен 2 этажа	
6	План демонтажа стен 3 этажа	
7	План демонтажа стен 4 этажа	
8	План демонтажа стен выходов на кровлю	
9	План демонтажа кровли	
10	Кладочный план подвала	
11	Кладочный план 1 этажа	
12	Кладочный план 2 этажа	
13	Кладочный план 3 этажа	
14	Кладочный план 4 этажа	
15	Кладочный план выходов на кровлю	
16	План демонтажа полов подвального этажа	
17	План демонтажа полов 1 этажа на отм. 0,000	
18	План демонтажа полов 2 этажа на отм. +3.300	
19	План демонтажа полов 3 этажа на отм. +6.600	
20	План демонтажа полов 4 этажа на отм. +9.900	
21	План демонтажа полов выходов на кровлю	
22	План полов подвального этажа	
23	План полов 1 этажа на отм. 0,000	
24	План полов 2 этажа на отм. +3.300	
25	План полов 3 этажа на отм. +6.600	
26	План полов 4 этажа на отм. +9.900	
27	План полов выходов на кровлю	
28	План демонтажа потолков подвального этажа	
29	План демонтажа потолков 1 этажа	
30	План демонтажа потолков 2 этажа	
31	План демонтажа потолков 3 этажа	
32	План демонтажа потолков 4 этажа	
33	План демонтажа потолков выходов на кровлю	
34	План потолков подвального этажа	
35	План потолков 1 этажа на отм. 0,000	
36	План потолков 2 этажа на отм. +3.300	
37	План потолков 3 этажа на отм. +6.600	
38	План потолков 4 этажа на отм. +9.900	
39	План потолков выходов на кровлю	
40	План подоконников 1 этажа на отм. 0,000	
41	План подоконников 2 этажа на отм. +3.300	
42	План подоконников 3 этажа на отм. +6.600	
43	План подоконников 4 этажа на отм. +9.900	
44	План подвального этажа	
45	План 1 этажа на отм. 0,000	
46	План 2 этажа на отм. +3.300	
47	План 3 этажа на отм. +6.600	
48	План 4 этажа на отм. +9.900	
49	Ведомость отделки подвала	

Лист	Наименование	Примечание
50	Ведомость отделки 1 этажа	
51	Ведомость отделки 1 этажа	
52	Ведомость отделки 1 этажа	
53	Ведомость отделки 1 этажа	
54	Ведомость отделки 1 этажа	
55	Ведомость отделки 2 этажа	
56	Ведомость отделки 2 этажа	
57	Ведомость отделки 2 этажа	
58	Ведомость отделки 2 этажа	
59	Ведомость отделки 3 этажа	
60	Ведомость отделки 3 этажа	
61	Ведомость отделки 3 этажа	
62	Ведомость отделки 4 этажа	
63	Ведомость отделки 4 этажа	

0,000=168,265

						ГИП-28/24-П-АР			
						ГБОУ Школа № 218, расположенная по адресу: г. Москва, ул. Вучетича, д. 6			
Изм.	Кол.уч.	Лист	№Док.	Подп.	Дата	Средняя общеобразовательная школа	Стадия	Лист	Листов
Разработал		Белова Е.С.			09.25		Р	2	
Проверил		Дубинин С.В.			09.25				
ГАП		Дубинин С.В.			09.25				
ГИП		Гущин А.В.				Ведомость рабочих чертежей	И-ГРУПП ПРОЕКТНО-СТРОИТЕЛЬНАЯ КОМПАНИЯ		
Н.контроль		Шукшин В.В.			09.25				

План демонтажа стен подвала

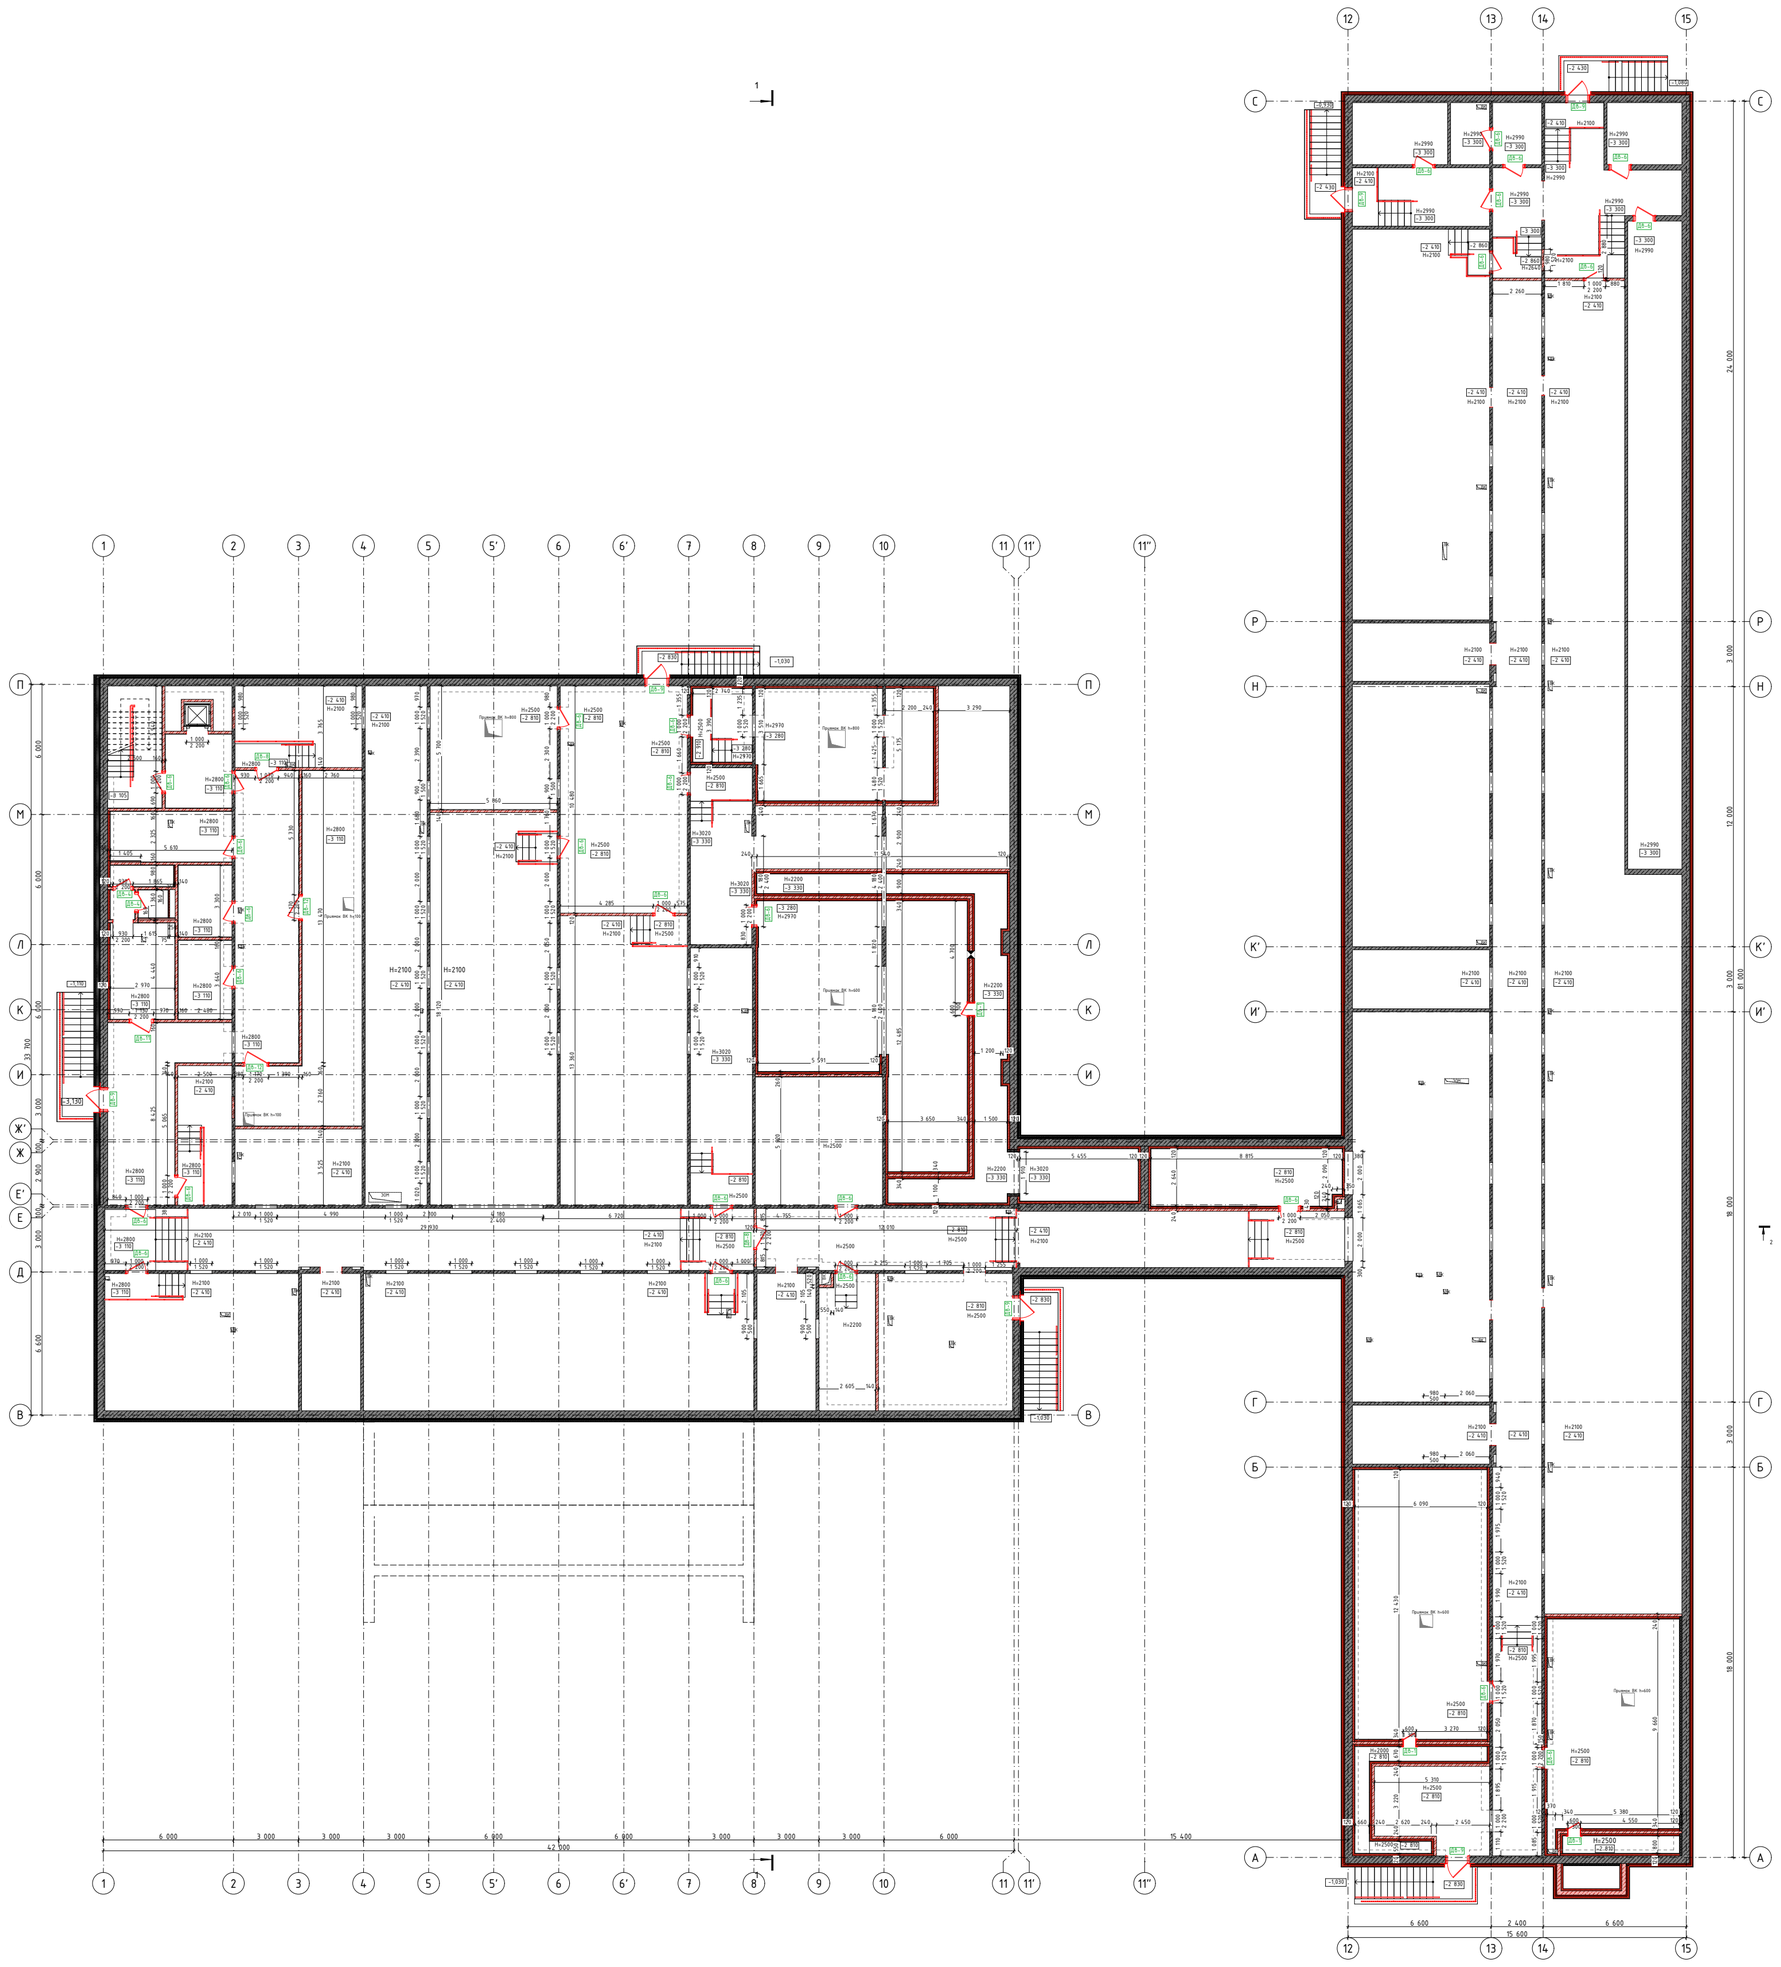

Условные обозначения

- сущ. стена Ж/Б

перегородка: штукатурка,минераловатный утеплитель 100 мм, кирпич 120 мм, штукатурка

- перегородка: кирпич 120 мм, штукатурка
- перегородка из цементной плиты 75 мм
- минераловатный утеплитель 100 мм, штукатурка
- перегородка из цементной плиты 75 мм

						ГИП-28/24-П-АР	
						ГБОУ Школа № 218, расположенная по адресу: г. Москва, ул. Вучетича, д. 6	
Изм.	Колуч.	Лист	№Док.	Подп.	Дата		
Разработал		Белова Е.С.			09.25	Средняя общеобразовательная школа	Стадия: П; Лист: 3; Листов:
Проверил		Дубинин С.В.			09.25		
ГАП		Дубинин С.В.			09.25		
ГИП		Гущин А.В.				План демонтажа стен подвала	И-ГРУПП ПРОЕКТНО-СТРОИТЕЛЬНАЯ КОМПАНИЯ
Н.контроль		Шукшин В.В.			09.25		

План демонтажа стен 1 этажа

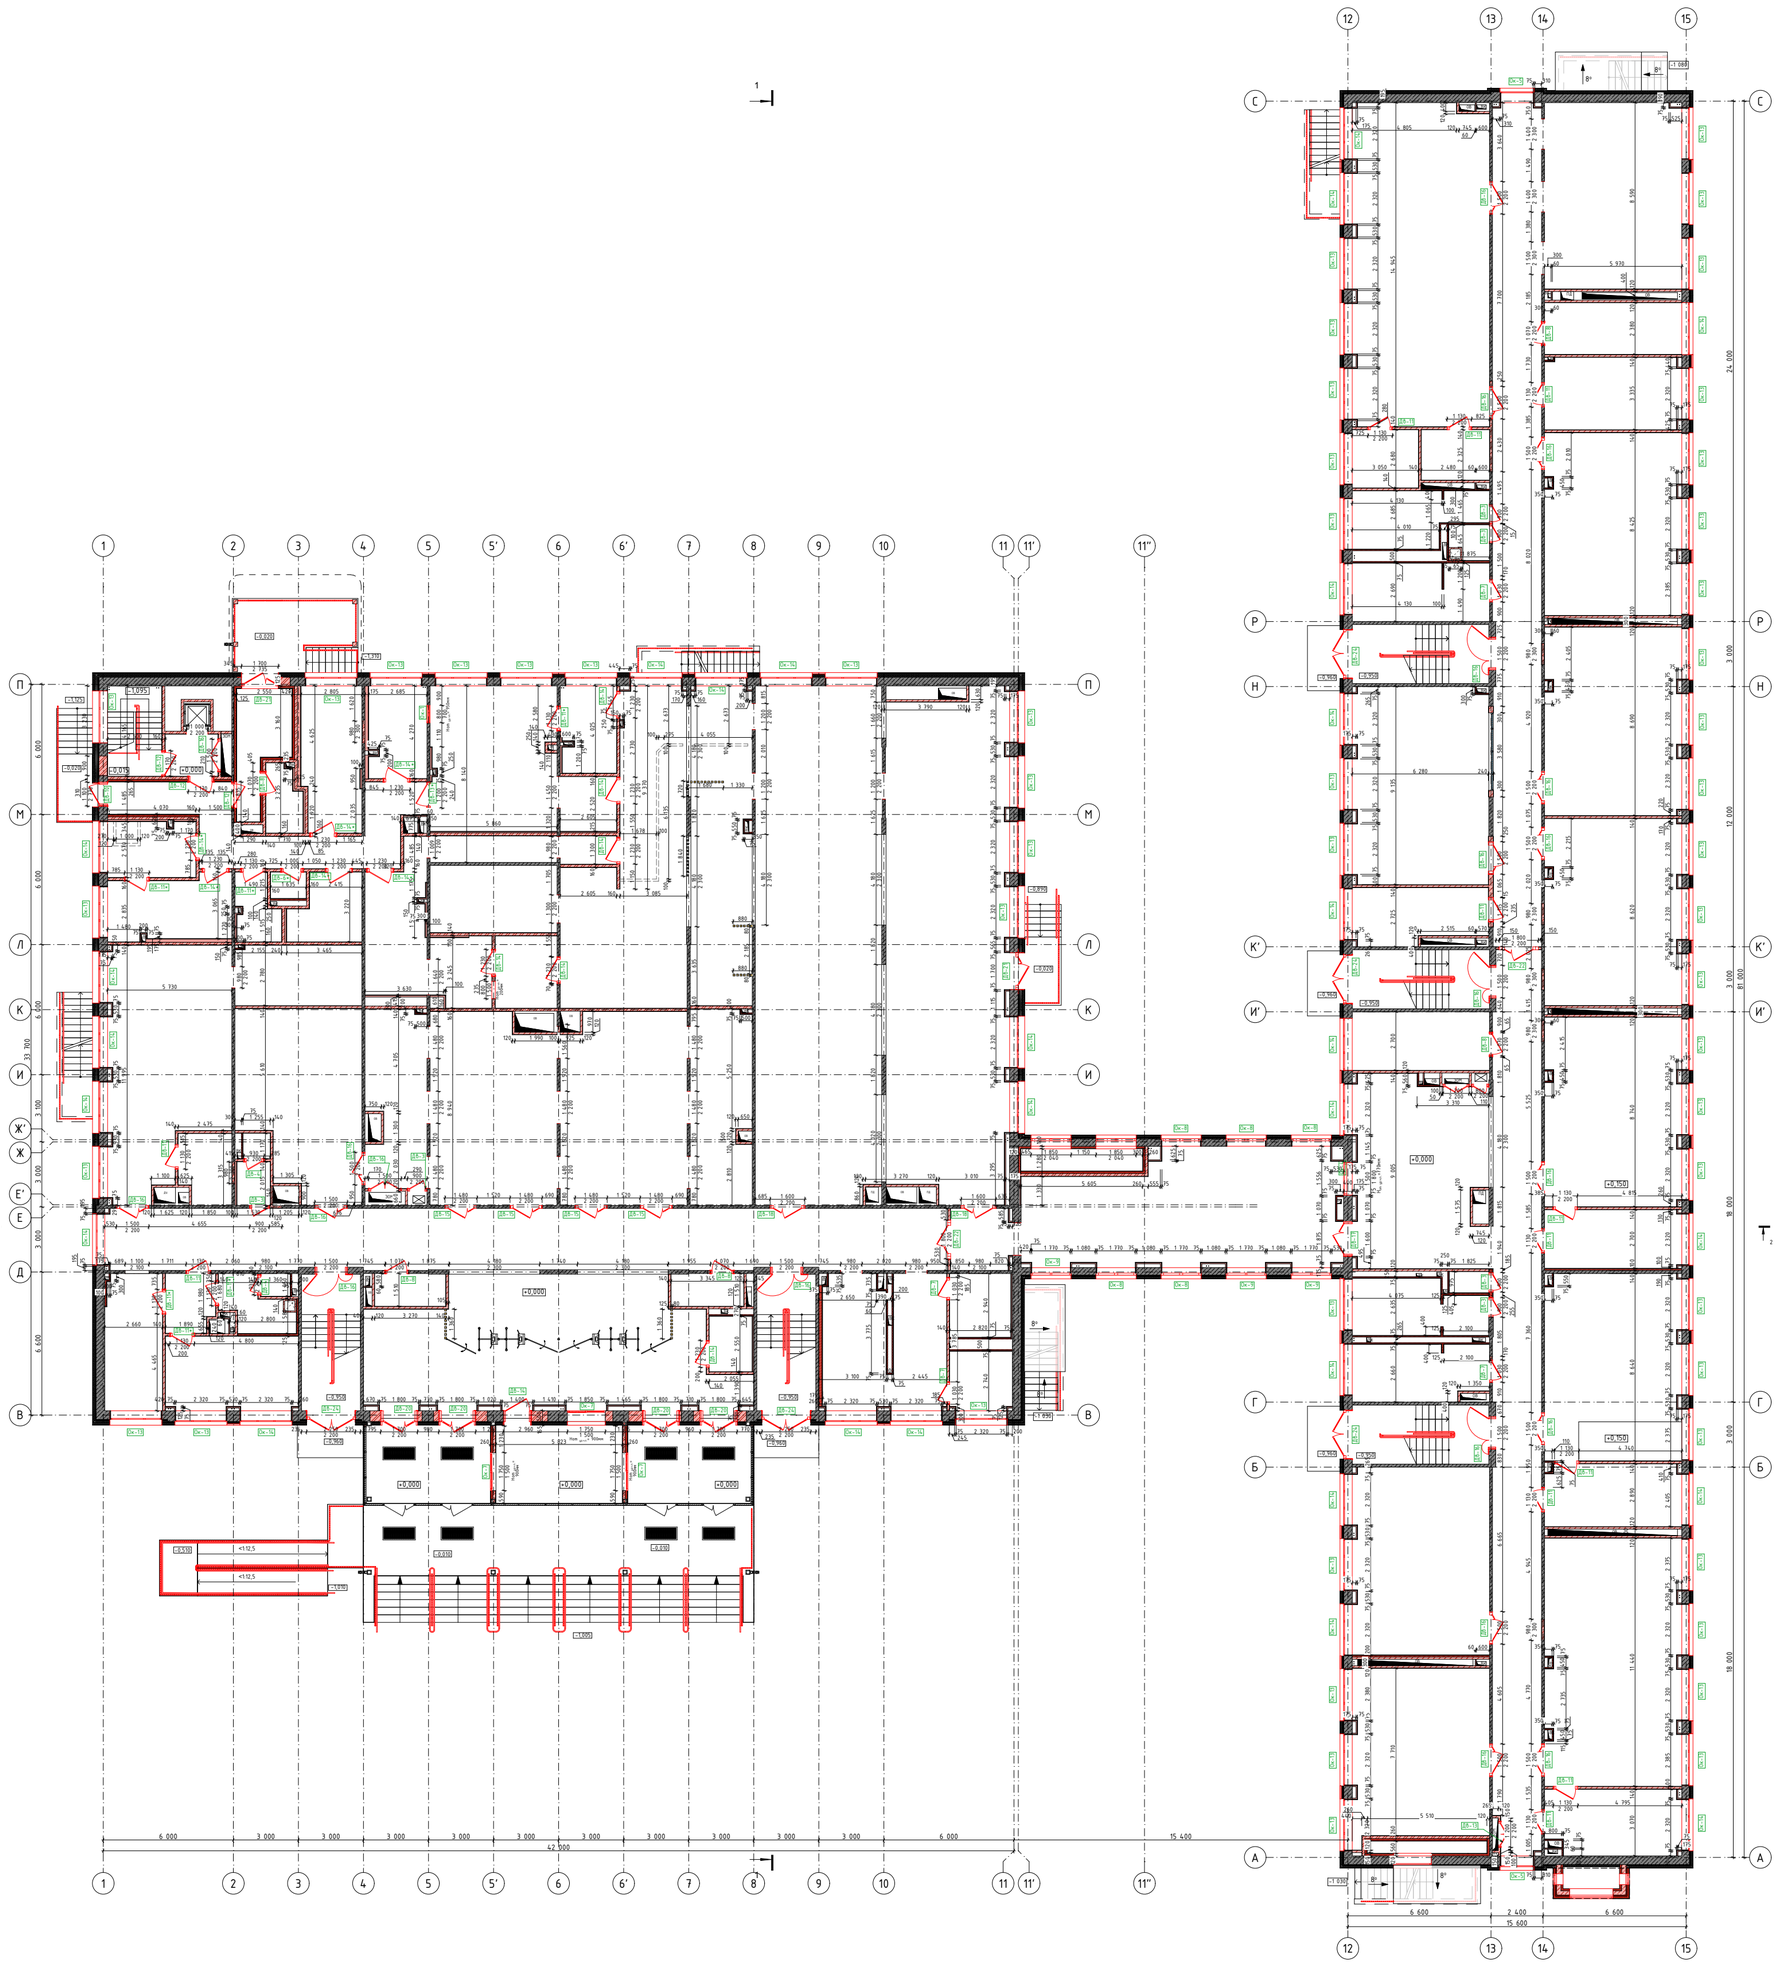

Условные обозначения

- сущ. стена Ж/Б
- перегородка: штукатурка,минераловатный утеплитель 100 мм, кирпич 120 мм, штукатурка
- кладка из кирпича 65 мм, штукатурка
- перегородка: штукатурка, кирпич 120 мм, перегородка из цементной плиты 75 мм, штукатурка
- перегородка: штукатурка, кирпич 120 мм, перегородка из цементной плиты 75мм
- перегородка: штукатурка, кирпич 120 мм, перегородка из цементной плиты 125 мм
- перегородка из цементной плиты 100мм, кирпич 120 мм, перегородка из цементной плиты 125мм
- перегородка из цементной плиты 100 мм, кирпич 120 мм, перегородка из цементной плиты 125мм
- перегородка из цементной плиты 100мм, кирпич 120 мм, перегородка из цементной плиты 175 мм
- газоблок 100 мм, штукатурка 20 мм с 2-х сторон
- газоблок 100 мм, штукатурка 20 мм с 1-ой стороны
- газоблок 100 мм
- газоблок 200 мм, штукатурка 20 мм с 2-х сторон
- перегородка: штукатурка, минераловатный утеплитель 100 мм, газоблок 100 мм, штукатурка
- устройство оконного откоса 40 мм
- перегородка из ГСП 60 мм
- перегородка из цементной плиты 75 мм
- перегородка из цементной плиты 100 мм
- перегородка из цементной плиты 150 мм
- перегородка из цементной плиты 200мм
- перегородка из цементной плиты 100 мм
- минераловатный утеплитель 100 мм, штукатурка
- перегородка из цементной плиты 175 мм
- перегородка из цементной плиты 100 мм
- перегородка из цементной плиты 175 мм
- перегородка из цементной плиты 125 мм
- стеклянная перегородка

						ГИП-28/24-П-АР	
						ГБОУ Школа № 218, расположенная по адресу: г. Москва, ул. Вучетича, д. 6	
Изм.	Колуч.	Лист	№Док.	Подп.	Дата		
Разработал		Белова Е.С.			09.25	Средняя общеобразовательная школа	Стадия: П; Лист: 4; Листов:
Проверил		Дубинин С.В.			09.25		
ГАП		Дубинин С.В.			09.25		
ГИП		Гущин А.В.				План демонтажа стен 1 этажа	И-ГРУПП ПРОЕКТНО-СТРОИТЕЛЬНАЯ КОМПАНИЯ
Н.контроль		Шукшин В.В.			09.25		

План демонтажа стен 2 этажа

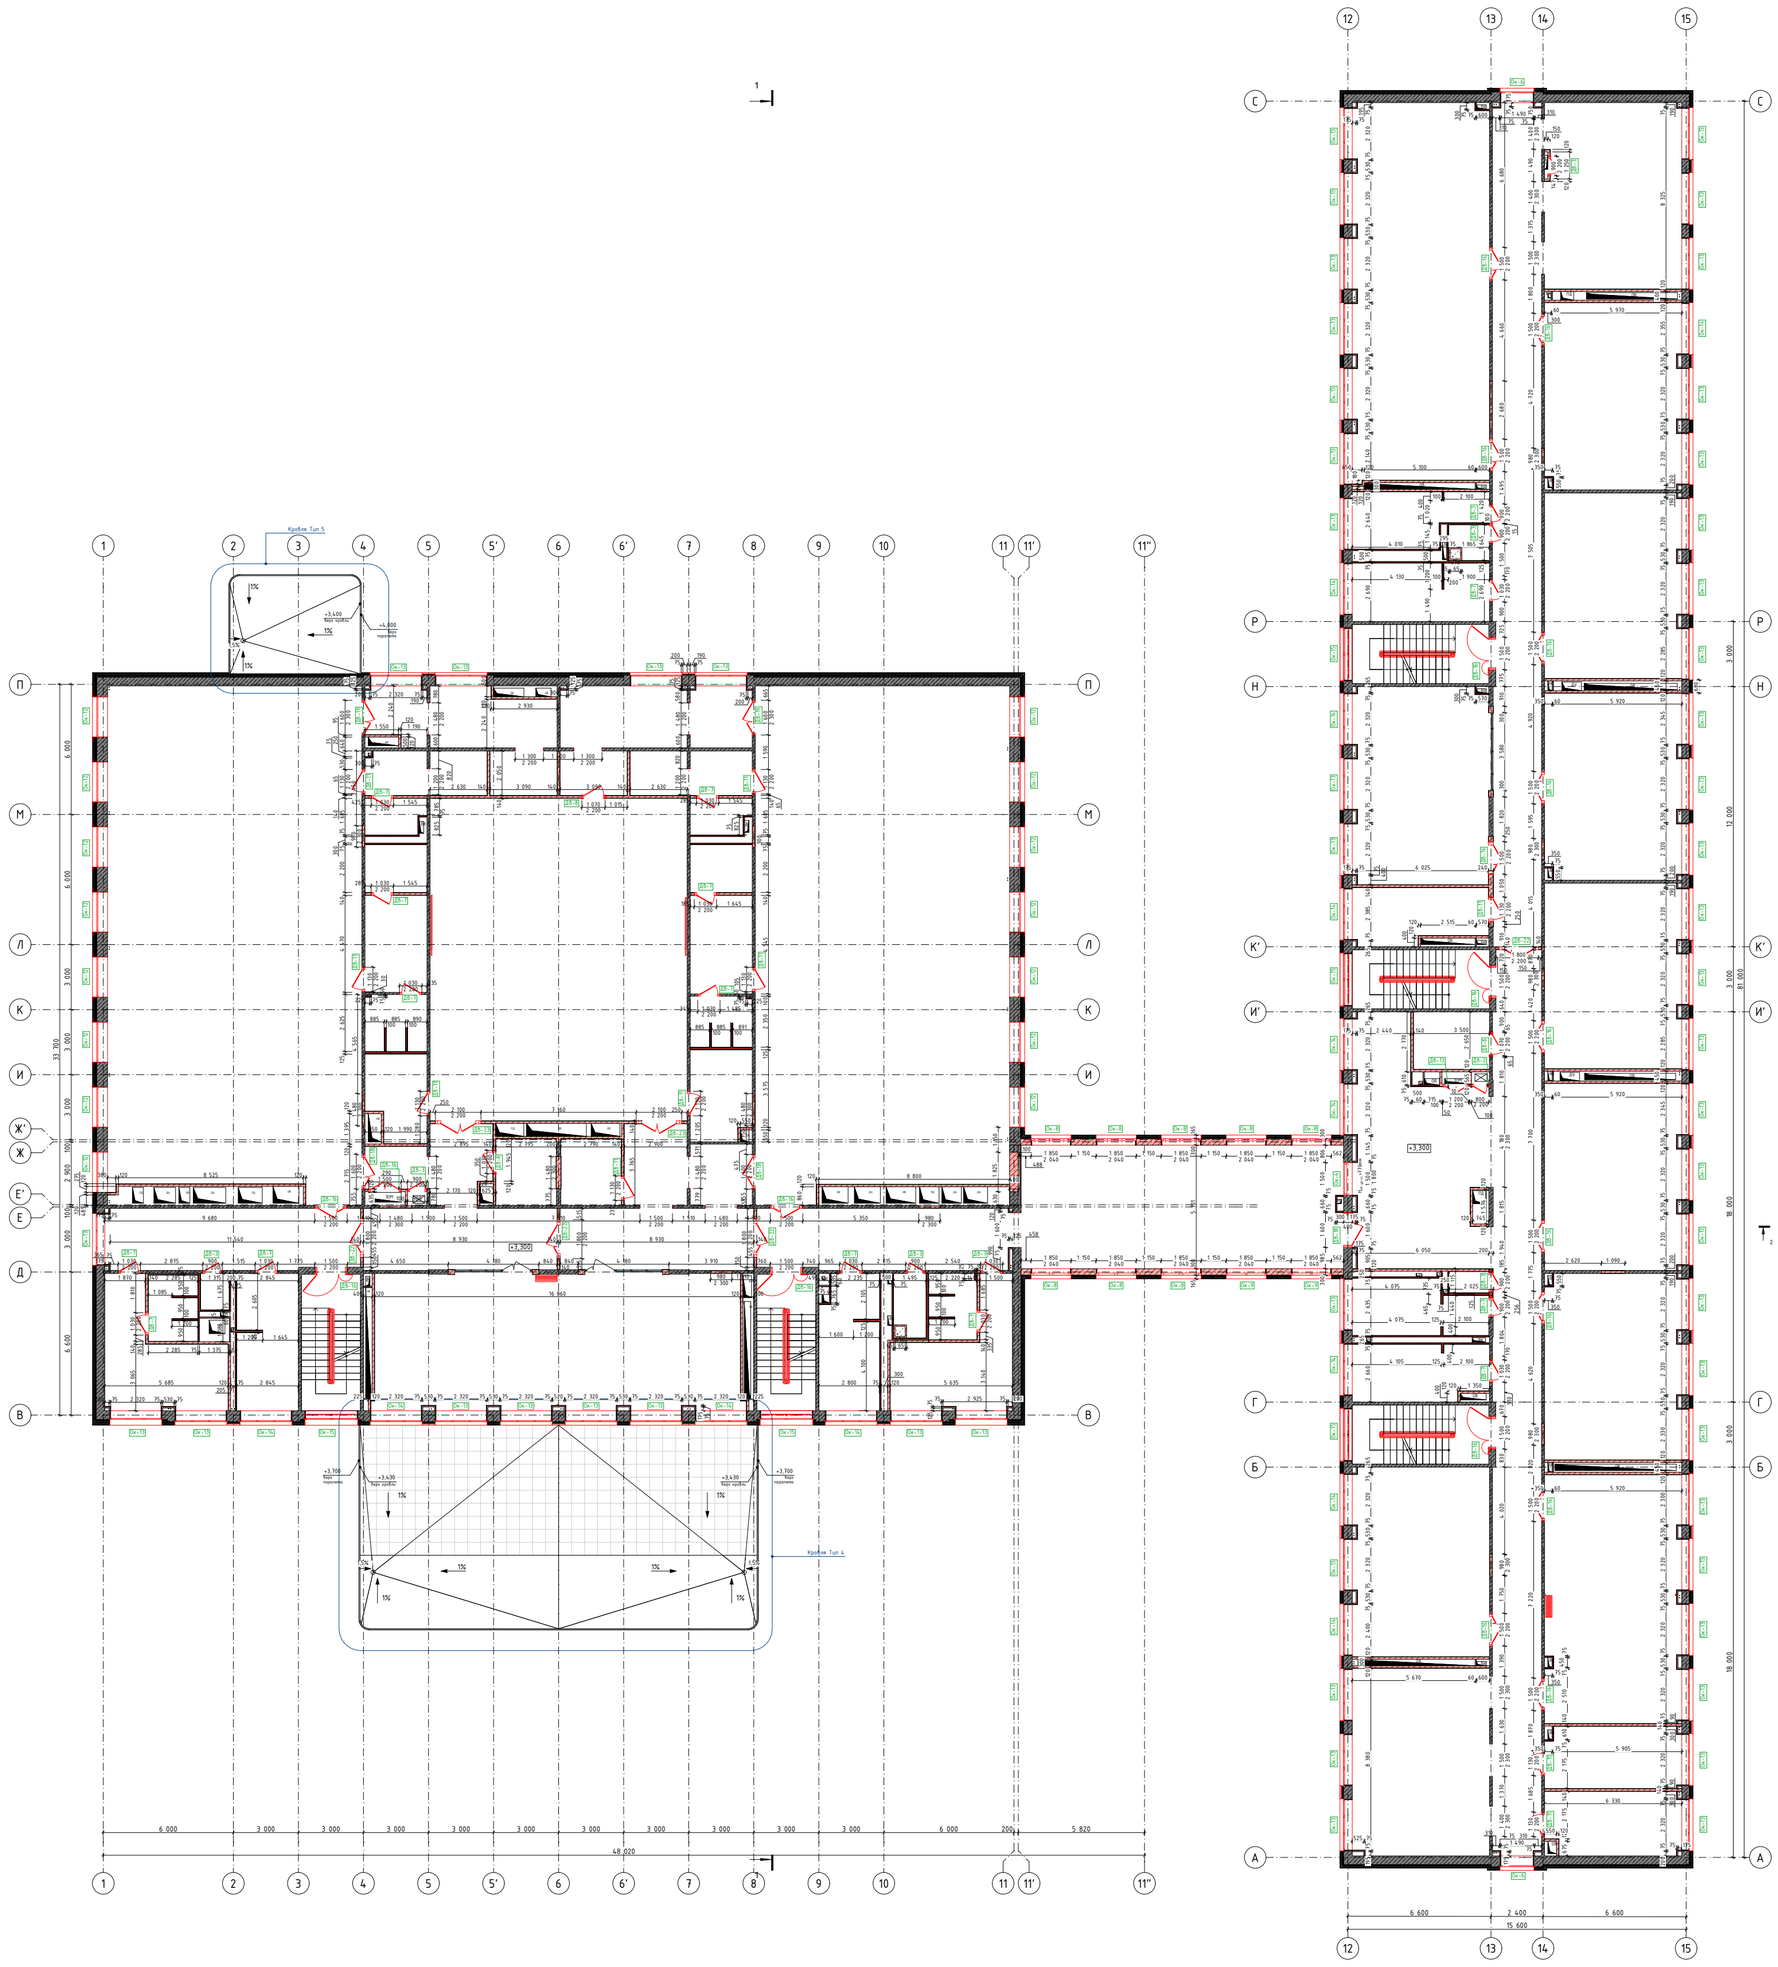

Условные обозначения

- сущ. стена Ж/Б
- кладка из кирпича 65 мм, штукатурка
- газоблок 100 мм, штукатурка 20 мм с 2-х сторон
- газоблок 100 мм, штукатурка 20 мм с 1-ой стороны
- газоблок 100 мм
- газоблок 200 мм, штукатурка 20 мм с 2-х сторон
- перегородка: штукатурка, минераловатный утеплитель 100 мм, газоблок 100 мм, штукатурка
- устройство оконного откоса 40 мм
- перегородка из ГСП 60 мм
- перегородка из цементной плиты 75 мм
- перегородка из цементной плиты 100 мм
- перегородка из цементной плиты 150 мм
- перегородка из цементной плиты 200мм
- перегородка из цементной плиты 100 мм
- стеклянная перегородка

						ГИП-28/24-П-АР	
						ГБОУ Школа № 218, расположенная по адресу: г. Москва, ул. Вучетича, д. 6	
Изм.	Колуч.	Лист	№Док.	Подп.	Дата		
Разработал		Белова Е.С.			09.25	Средняя общеобразовательная школа	Стадия: П; Лист: 5; Листов:
Проверил		Дубинин С.В.			09.25		
ГАП		Дубинин С.В.			09.25		
ГИП		Гущин А.В.				План демонтажа стен 2 этажа	И-ГРУПП ПРОЕКТНО-СТРОИТЕЛЬНАЯ КОМПАНИЯ
Н.контроль		Шукшин В.В.			09.25		

План демонтажа стен 3 этажа

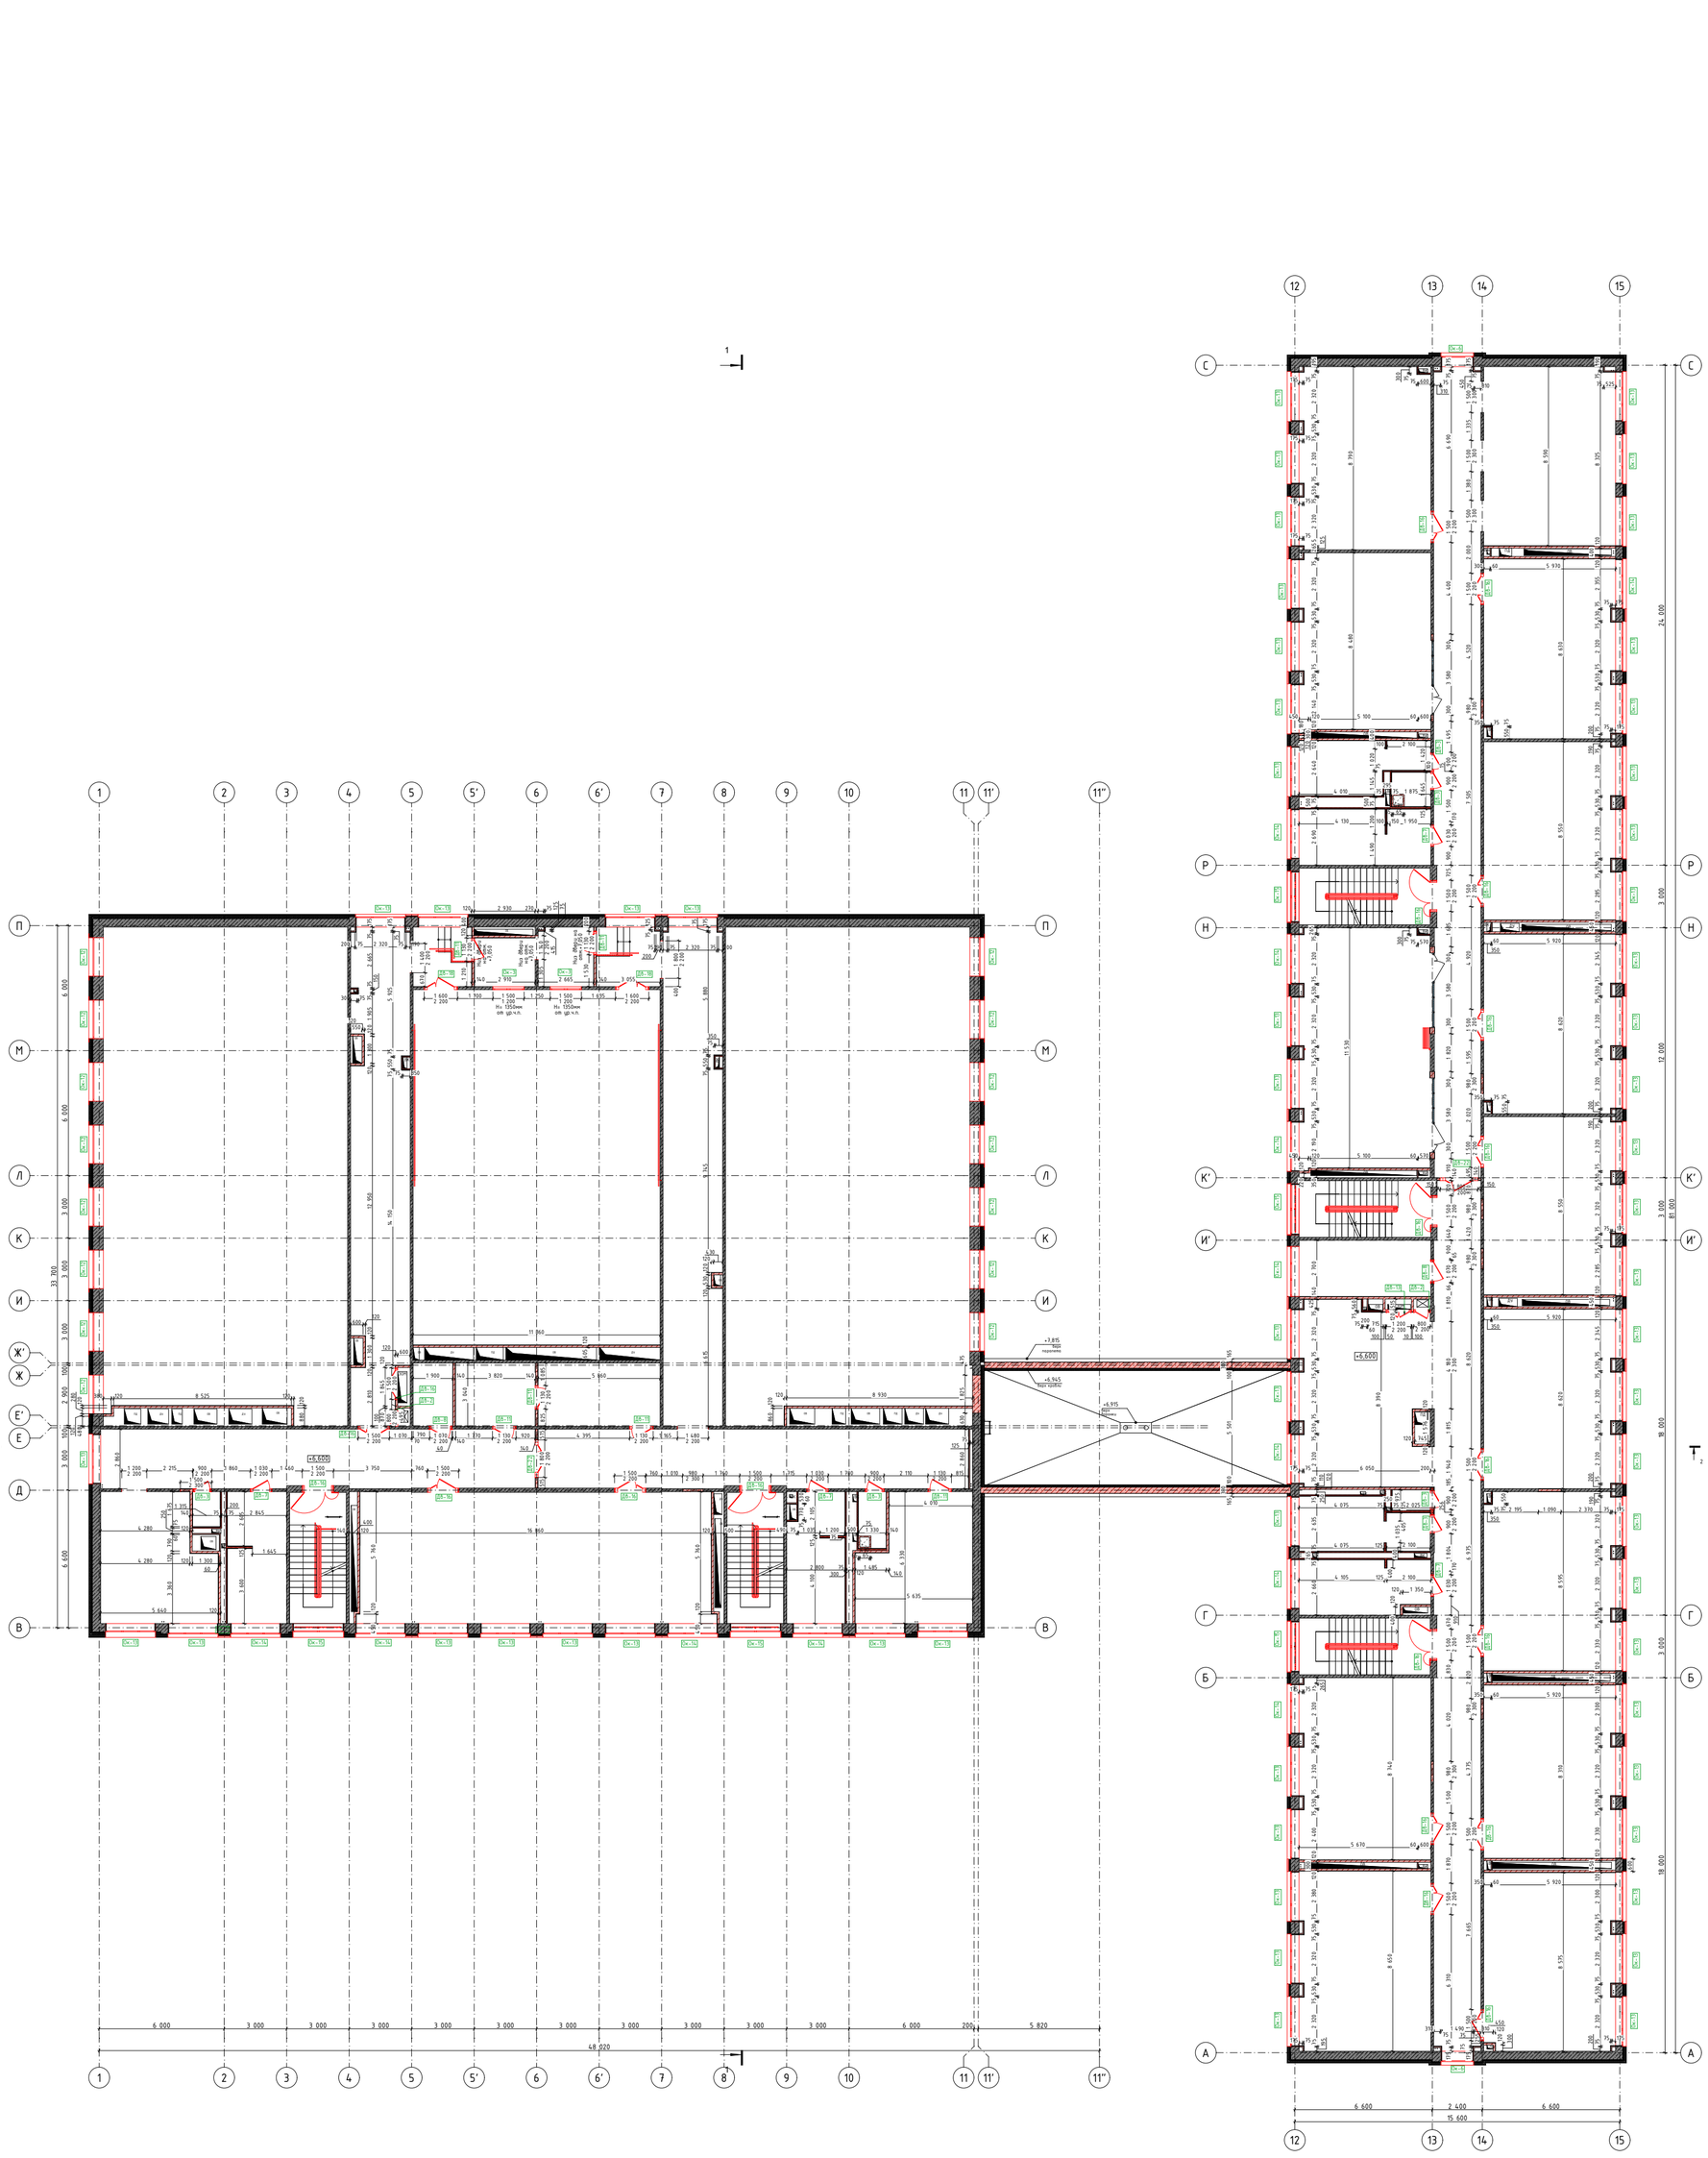

Условные обозначения

- сущ. стена Ж/Б
- кладка из кирпича 65 мм, штукатурка
- газоблок 100 мм, штукатурка 20 мм с 2-х сторон
- газоблок 100 мм, штукатурка 20 мм с 1-ой стороны
- газоблок 100 мм
- газоблок 200 мм, штукатурка 20 мм с 2-х сторон
- перегородка: штукатурка, минераловатный утеплитель 100 мм, газоблок 100 мм, штукатурка
- устройство оконного откоса 40 мм
- перегородка из ГСП 60 мм
- перегородка из цементной плиты 75 мм
- перегородка из цементной плиты 100 мм
- перегородка из цементной плиты 150 мм
- перегородка из цементной плиты 200мм
- перегородка из цементной плиты 100 мм
- стеклянная перегородка

						ГИП-28/24-П-АР	
						ГБОУ Школа № 218, расположенная по адресу: г. Москва, ул. Вучетича, д. 6	
Изм.	Колуч.	Лист	№Док.	Подп.	Дата		
Разработал		Белова Е.С.			09.25	Средняя общеобразовательная школа	Стадия: П; Лист: 6; Листов:
Проверил		Дубинин С.В.			09.25		
ГАП		Дубинин С.В.			09.25		
ГИП		Гущин А.В.				План демонтажа стен 3 этажа	И-ГРУПП ПРОЕКТНО-СТРОИТЕЛЬНАЯ КОМПАНИЯ
Н.контроль		Шукшин В.В.			09.25		

План демонтажа стен 4 этажа

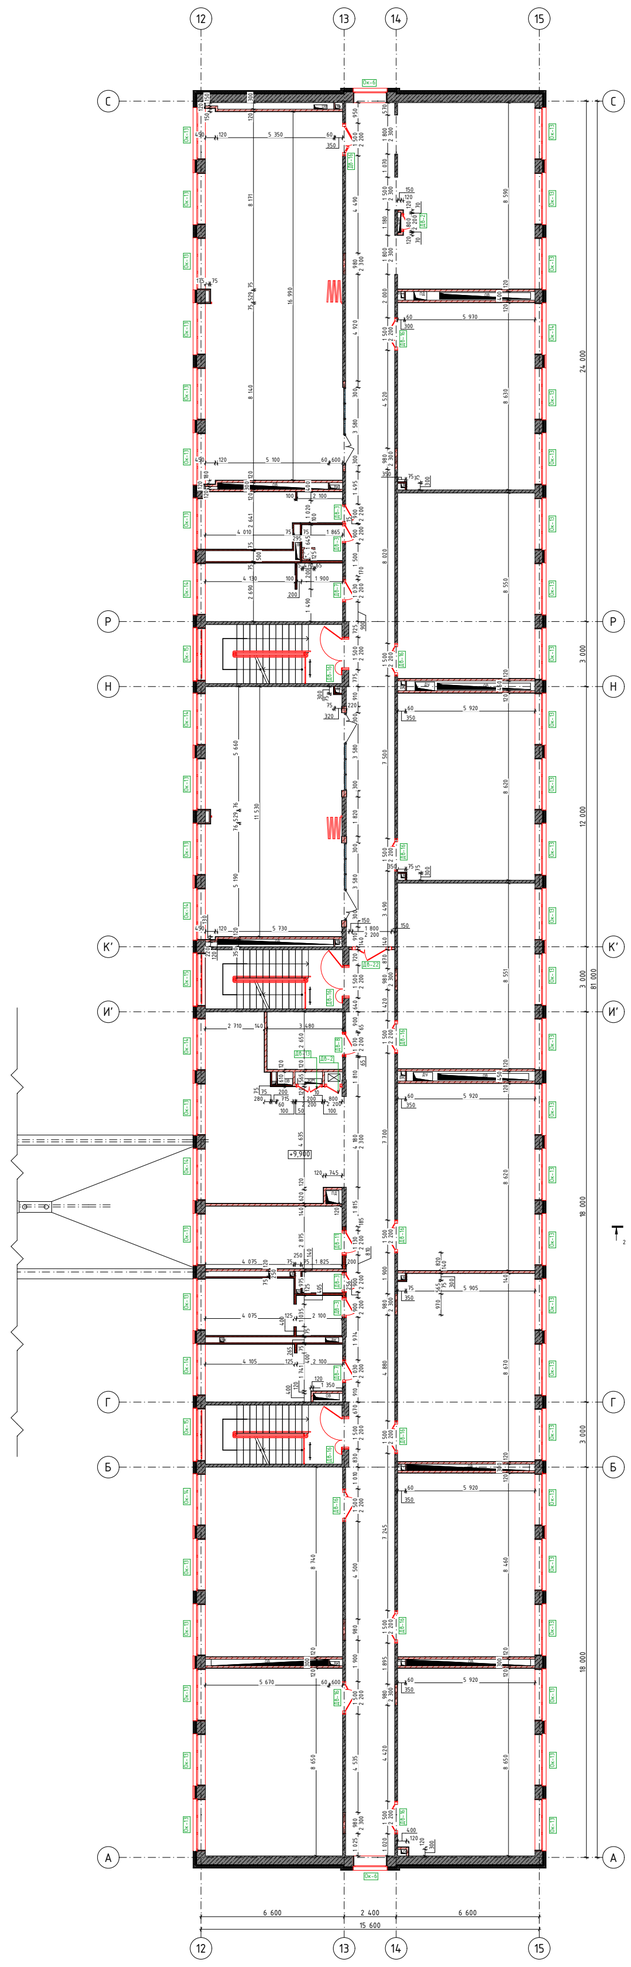

Условные обозначения

- сущ. стена Ж/Б
- кладка из кирпича 65 мм, штукатурка
- газоблок 100 мм, штукатурка 20 мм с 2-х сторон
- газоблок 100 мм, штукатурка 20 мм с 1-ой стороны
- газоблок 100 мм
- газоблок 200 мм, штукатурка 20 мм с 2-х сторон
- перегородка: штукатурка, минераловатный утеплитель 100 мм, газоблок 100 мм, штукатурка
- устройство оконного откоса 40 мм
- перегородка из ГСП 60 мм
- перегородка из цементной плиты 75 мм
- перегородка из цементной плиты 100 мм
- перегородка из цементной плиты 150 мм
- перегородка из цементной плиты 200мм
- перегородка из цементной плиты 100 мм
- стеклянная перегородка

						ГИП-28/24-П-АР
						ГБОУ Школа № 218, расположенная по адресу: г. Москва, ул. Вучетича, д. 6
Изм.	Колуч.	Лист	№Док.	Подп.	Дата	
Разработал		Белова Е.С.			09.25	Средняя общеобразовательная школа
Проверил		Дубинин С.В.			09.25	
ГАП		Дубинин С.В.			09.25	
ГИП		Гущин А.В.				План демонтажа стен 4 этажа
Н.контроль		Шукшин В.В.			09.25	

Стадия	Лист	Листов
П	7	

И-ГРУПП
ПРОЕКТНО-СТРОИТЕЛЬНАЯ КОМПАНИЯ

План демонтажа стен выходов на кровлю

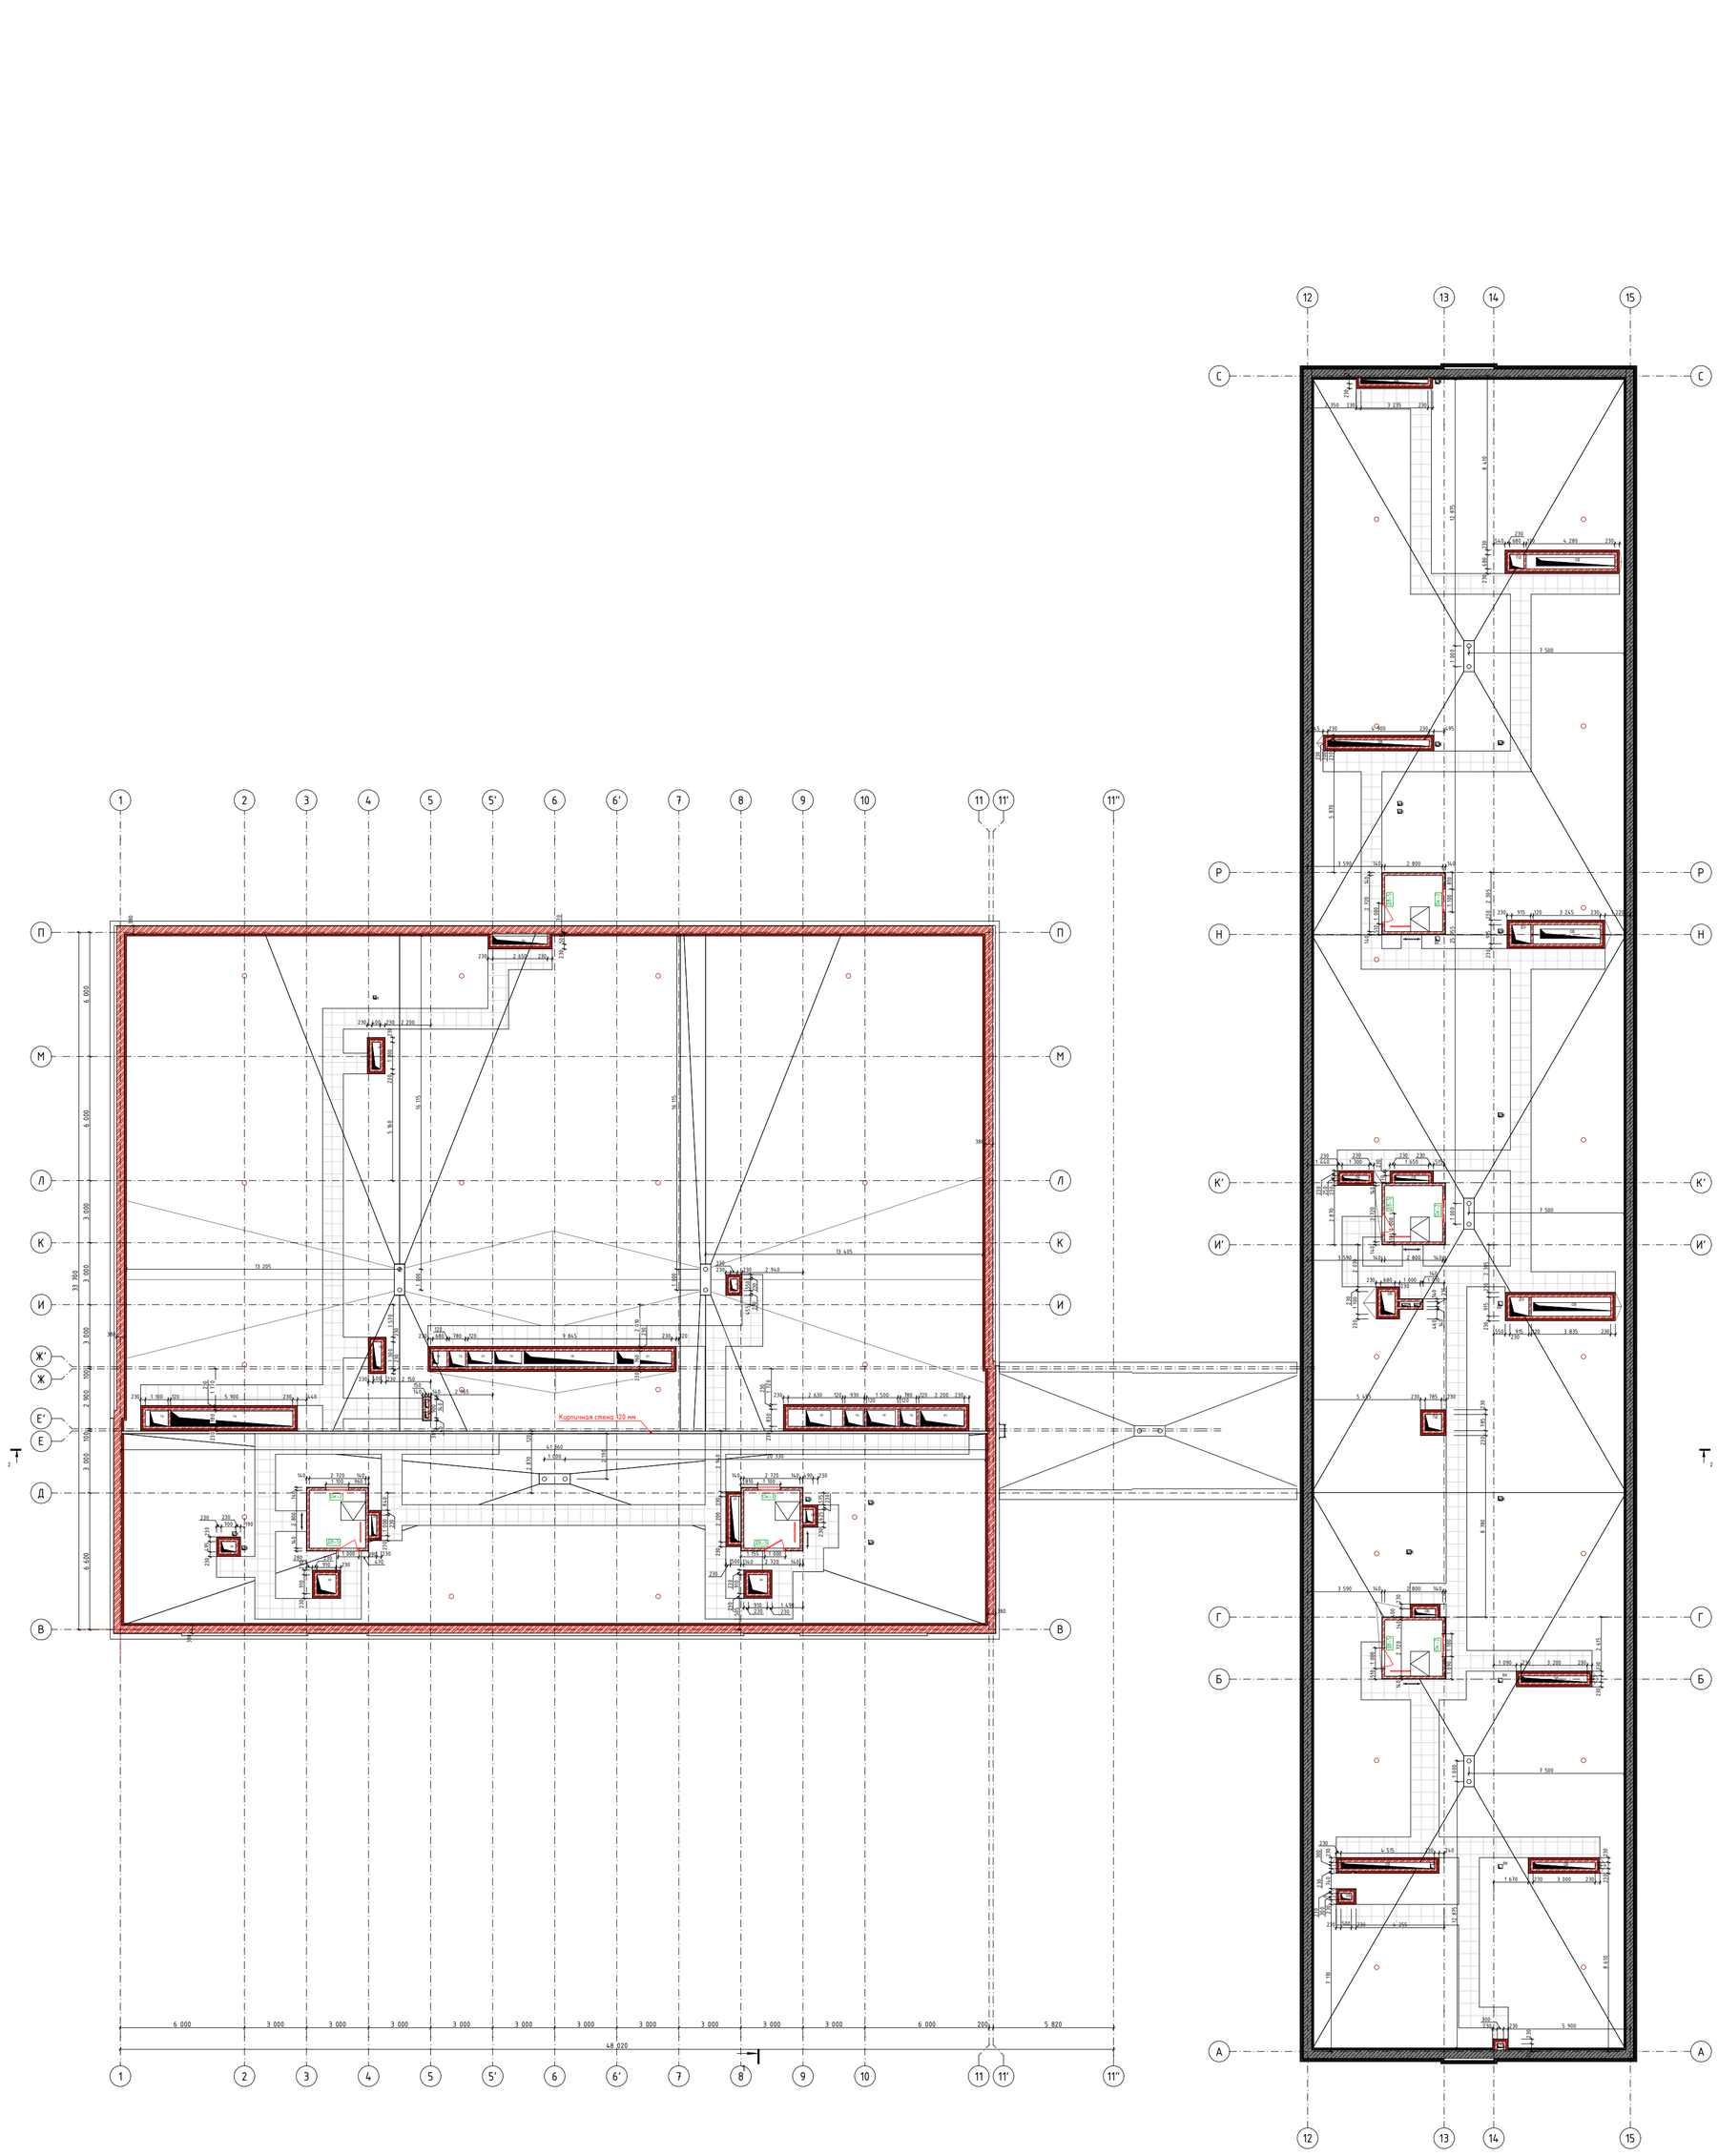

Условные обозначения

- сущ. стена Ж/Б
- перегородка из кирпича 120 мм
- перегородка из кирпича 120 мм, штукатурка с двух сторон
- перегородка: минераловатный утеплитель 100 мм, кирпич 120 мм, штукатурка
- стена из кирпичной кладки 380 мм
- стена из кирпичной кладки 510 мм

						ГИП-28/24-П-АР	
						ГБОУ Школа № 218, расположенная по адресу: г. Москва, ул. Вучетича, д. 6	
Изм.	Колуч.	Лист	№Док.	Подп.	Дата		
Разработал		Белова Е.С.			09.25	Средняя общеобразовательная школа	Стадия: П; Лист: 8; Листов:
Проверил		Дубинин С.В.			09.25		
ГАП		Дубинин С.В.			09.25		
ГИП		Гущин А.В.				План демонтажа стен выходов на кровлю	И-ГРУПП ПРОЕКТНО-СТРОИТЕЛЬНАЯ КОМПАНИЯ
Н.контроль		Шукшин В.В.			09.25		

План демонтажа кровли

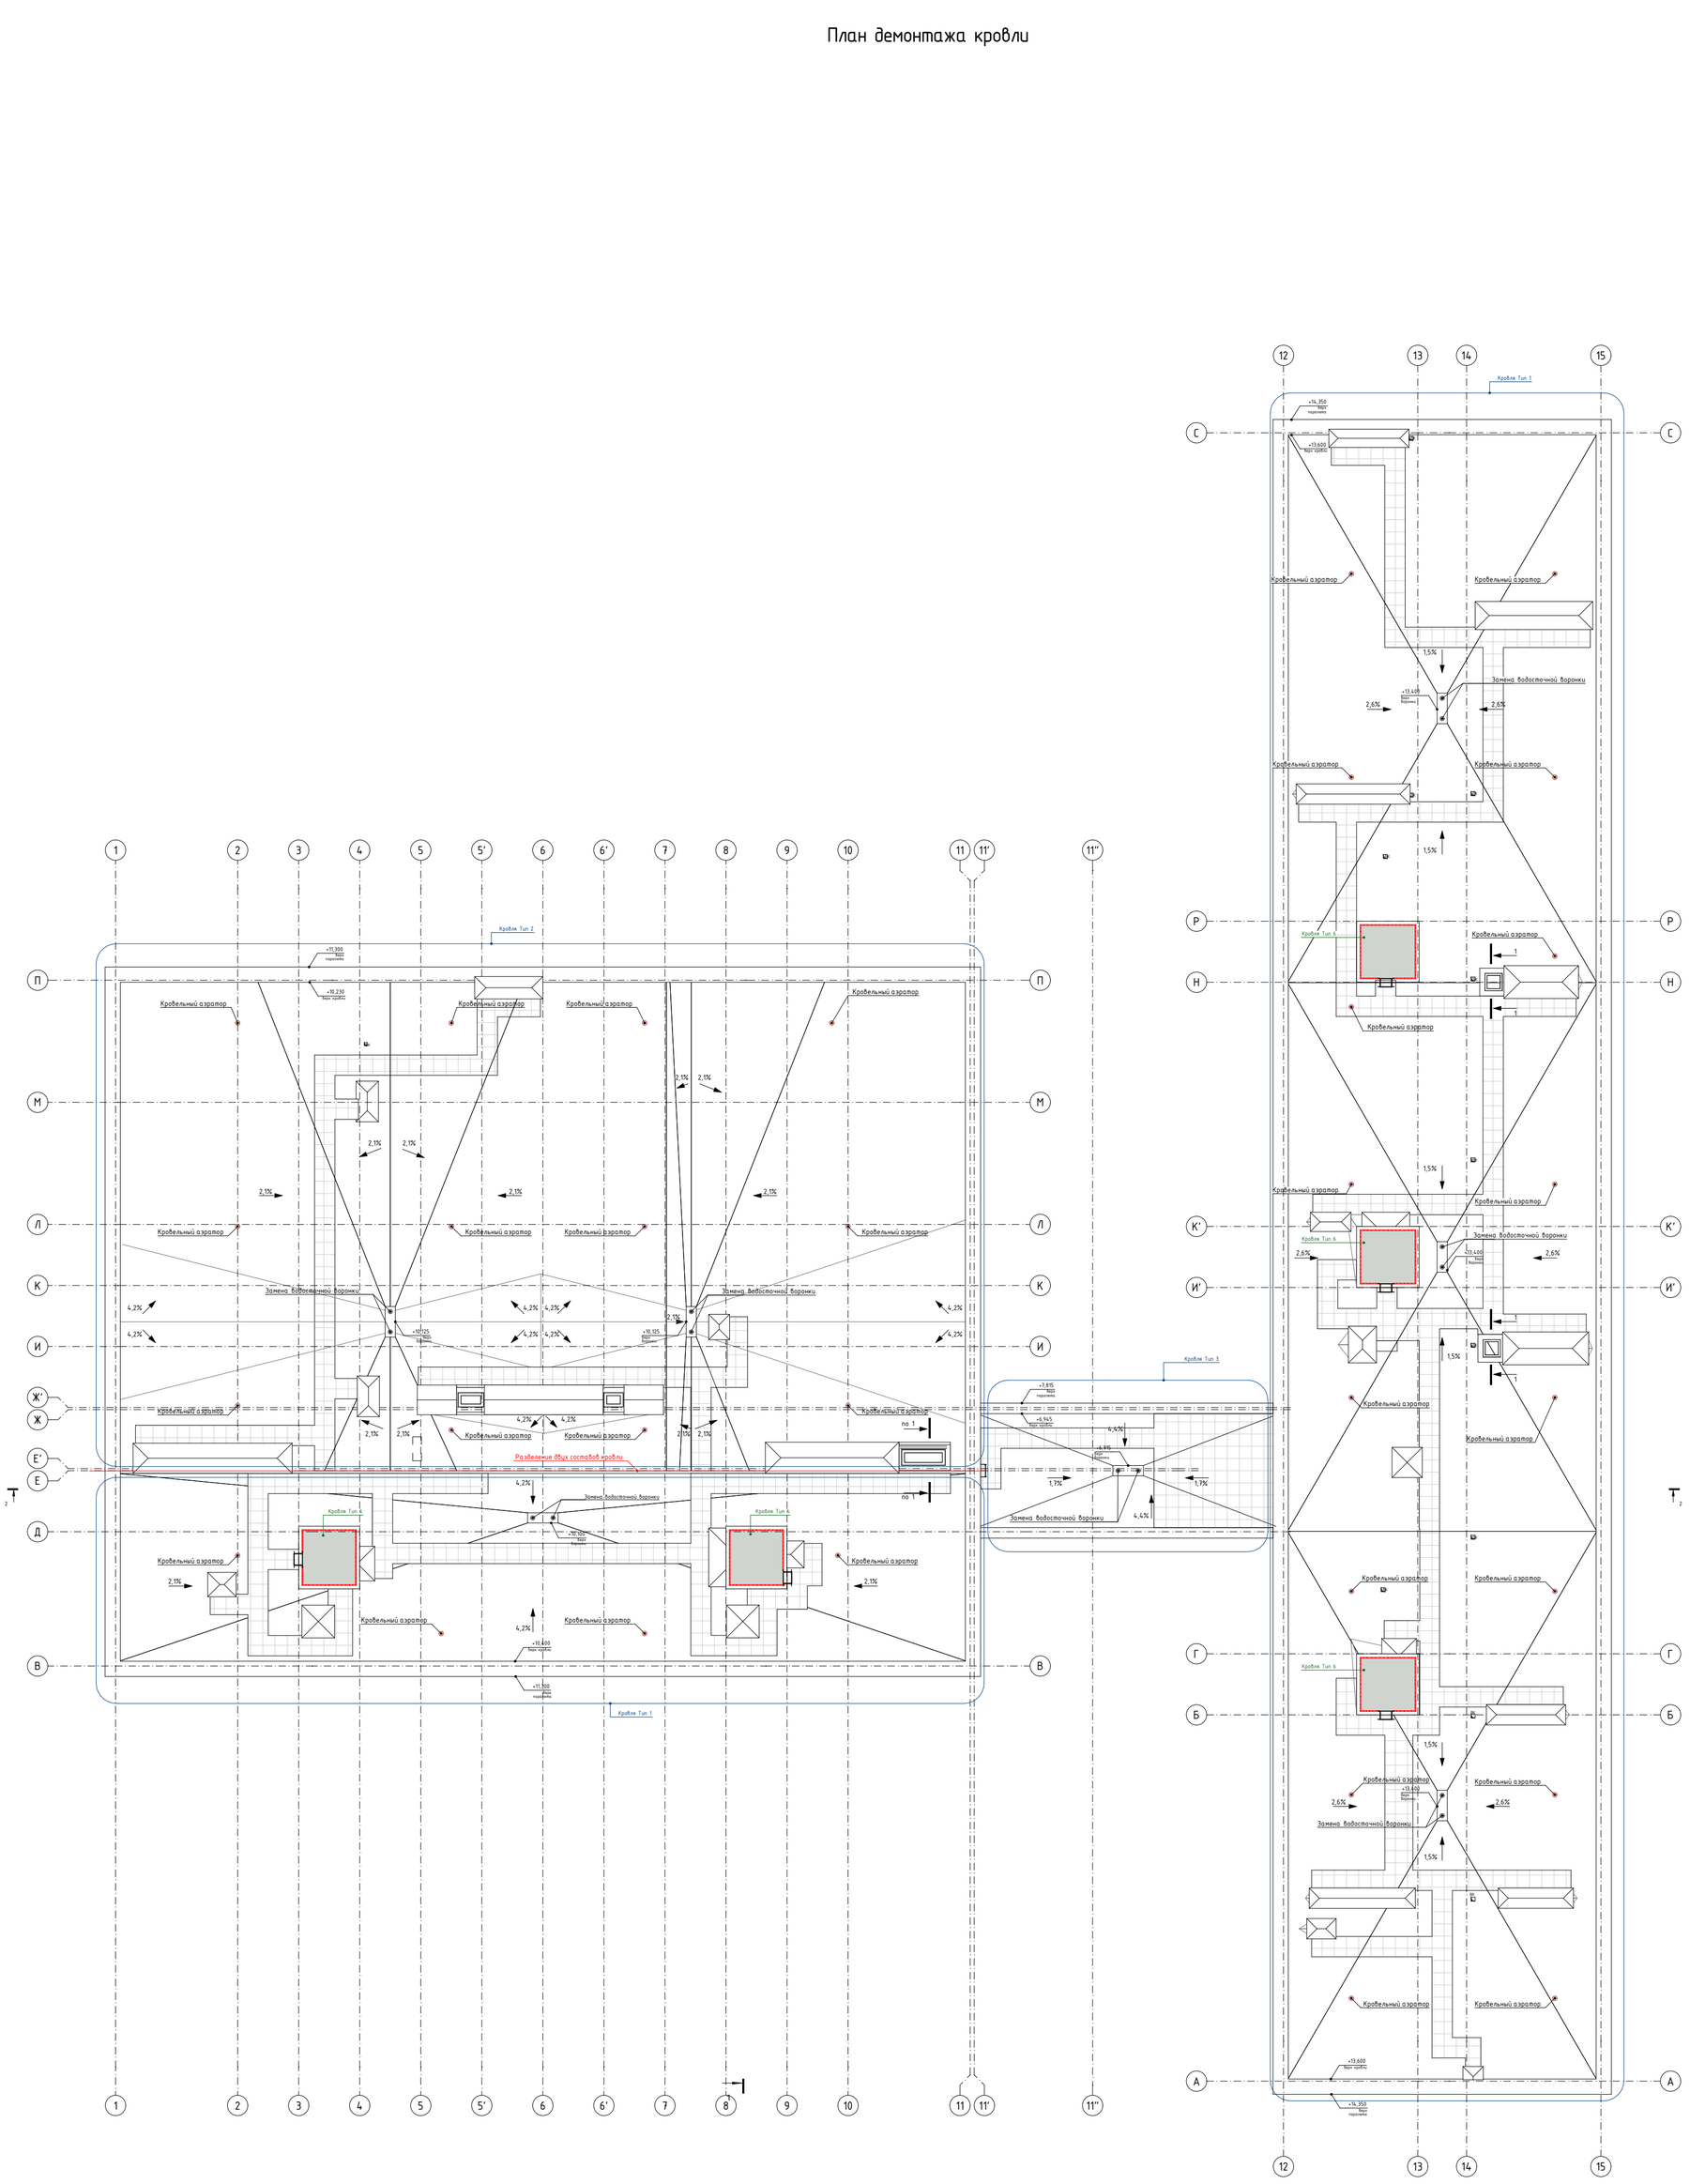

						ГИП-28/24-П-АР	
						ГБОУ Школа № 218, расположенная по адресу: г. Москва, ул. Вучетича, д. 6	
Изм.	Колуч.	Лист	№Док.	Подп.	Дата		
Разработал		Белова Е.С.			09.25	Средняя общеобразовательная школа	Стадия: П; Лист: 9; Листов:
Проверил		Дубинин С.В.			09.25		
ГАП		Дубинин С.В.			09.25		
ГИП		Гущин А.В.				План демонтажа кровли	И-ГРУПП ПРОЕКТНО-СТРОИТЕЛЬНАЯ КОМПАНИЯ
Н.контроль		Шукшин В.В.			09.25		

Кладочный план подвала
М 1:200

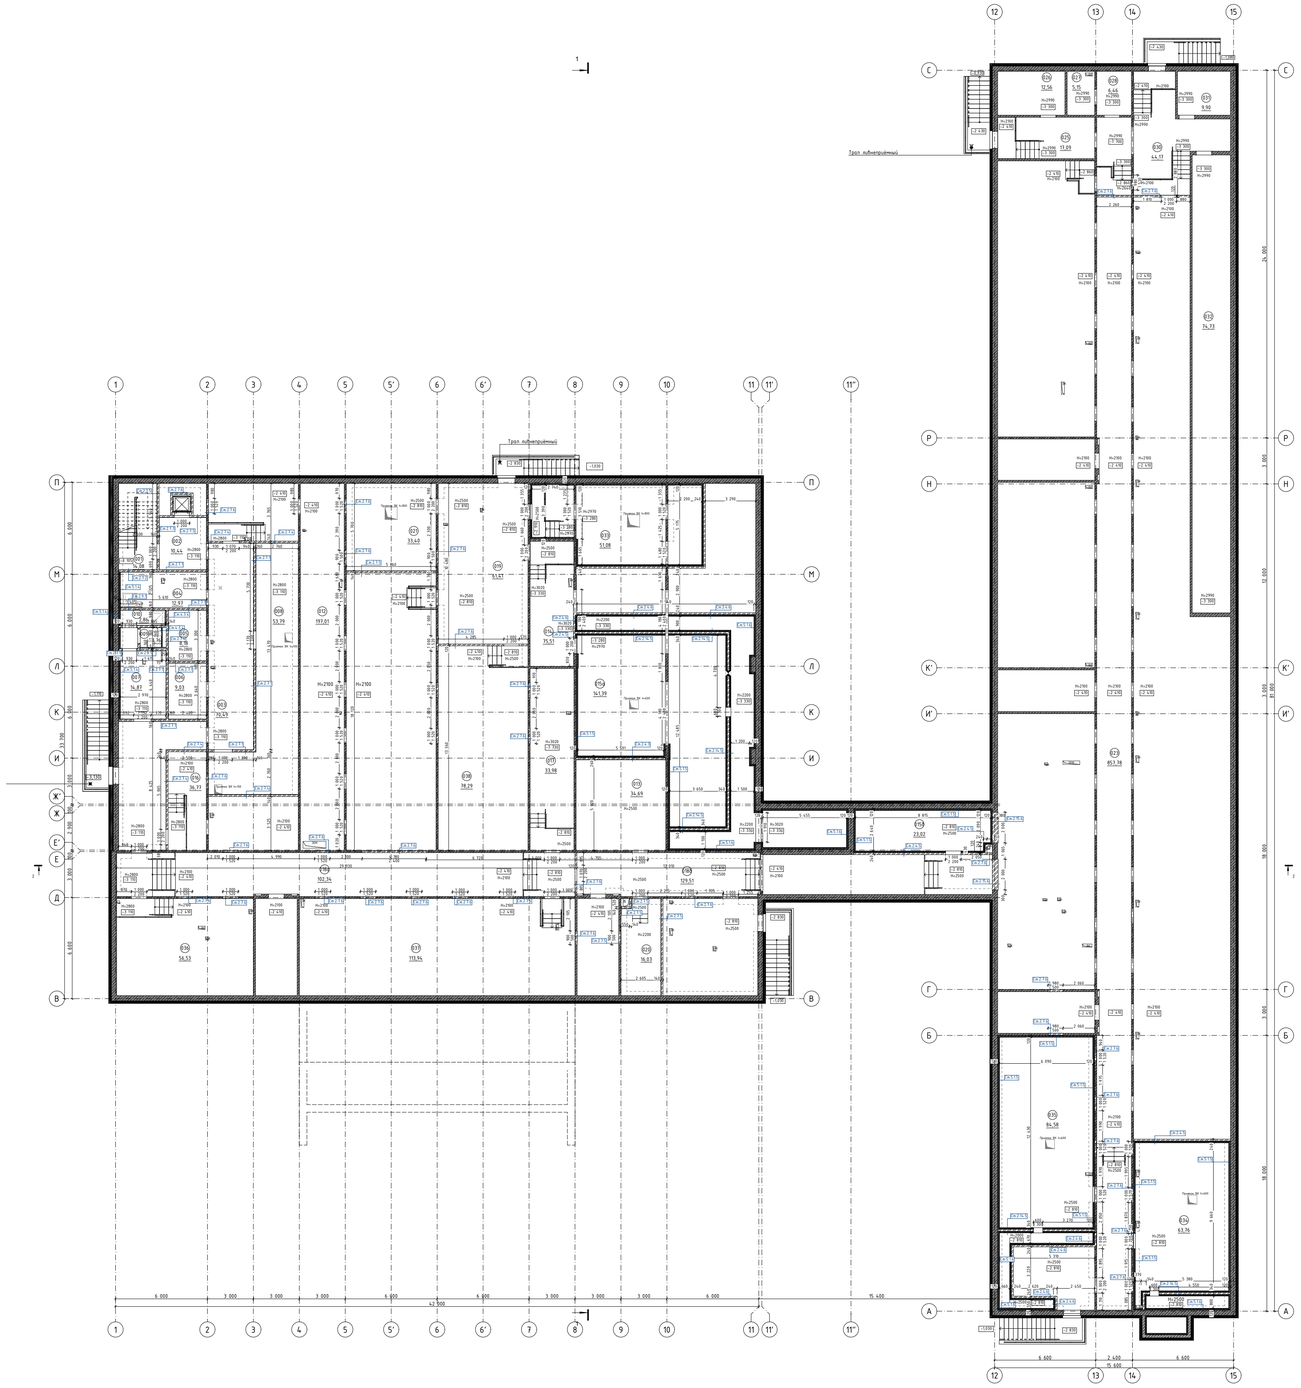
Трап лабиринтный
Трап лабиринтный
1
2
3
4
5
5'
6
6'
7
8
9
10
11
11'
11*
12
13
14
15
А
Б
В
Г
Д
Е
Е'
Ж
Ж'
И
И'
К
К'
Л
М
Н
Р
П
6 000
3 000
3 000
3 000
6 000
6 000
3 000
3 000
3 000
6 000
42 500
75 400
2 400
6 600
6 600
6 600
6 600
2 400
6 600
18 900
18 900
3 900
3 900
6 000
6 000
6 000

Кладочный план 1 этажа
М 1:200

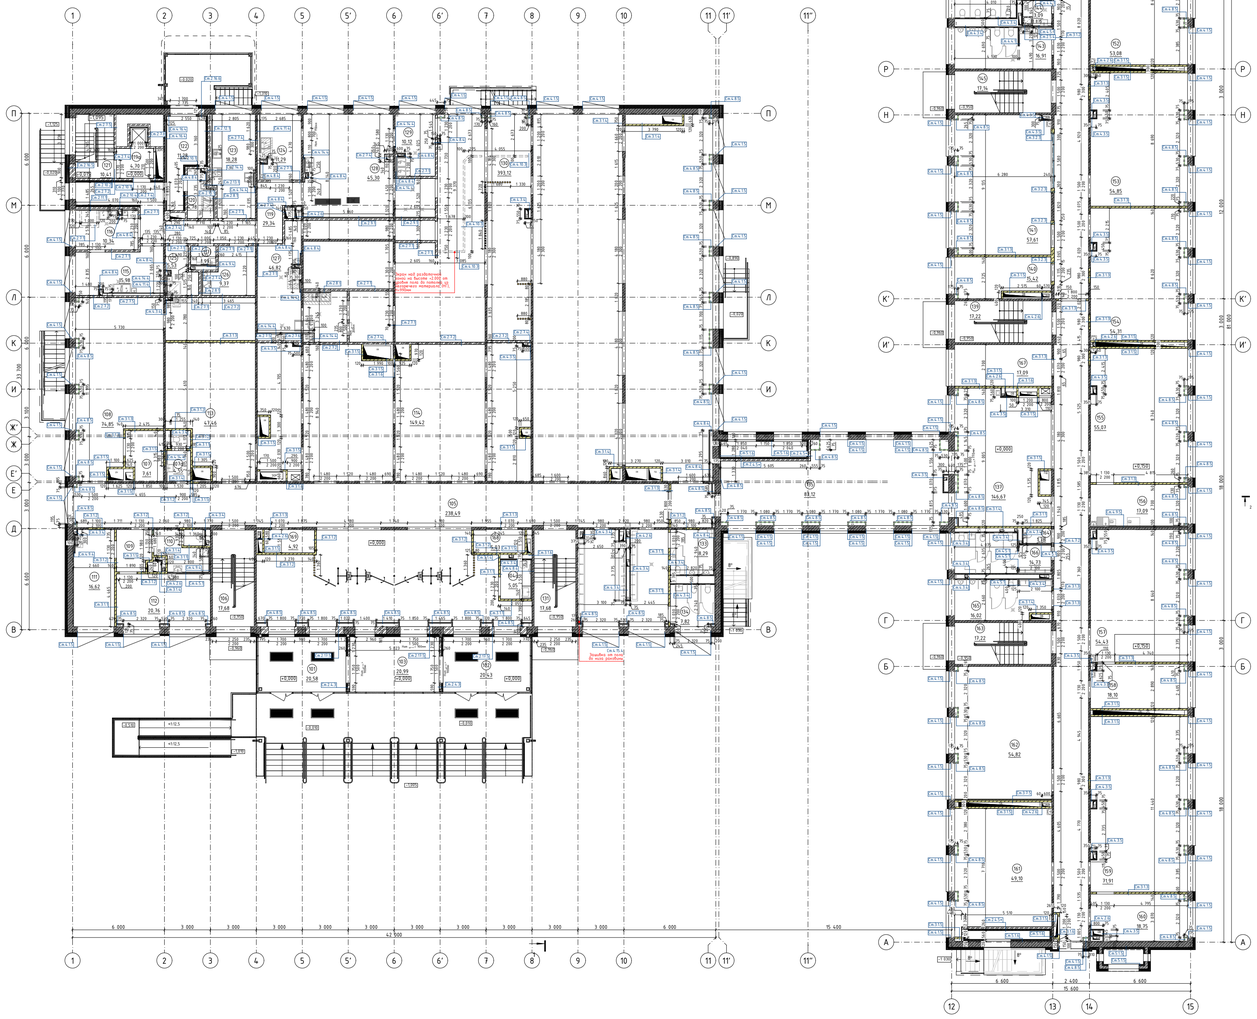

Экпликация помещений на отм. 0.000

№	Наименование	Площадь	Категория помещения
101	Тамбур	20,58	
102	Тамбур	20,43	
103	Комната охраны с диспетчерским пунктом	20,99	
104а	Сан. узел МГН	5,05	
105	Вестибюль	238,49	
106	Лестничная клетка (тип Н2)	17,68	
107	Гардеробная комната (для учителей)	7,61	
107а	Сан. узел для персонала	4,55	
108	Кабинет с рабочим пространством для учителей Тип 2	74,85	
109	Тамбур	6,03	
110	Туалет медблока с местом для приготовления дезинфицирующих средств и хранения уборочного инвентаря	8,39	
111	Процедурный (прививочный) кабинет	16,62	
112	Кабинет врача	20,76	
113	Гардероб для обучающихся	47,46	
114	Гардероб для обучающихся	149,42	
115	Цех вторичной обработки овощей	15,98	В3
116	Цех первичной обработки овощей	10,34	В3
117	Сан. узел для персонала	1,99	
119	Коридор	29,34	
119а	Тамбур	4,70	
120	Моечная обратной тары	4,78	В4
121	Лестничная клетка (для персонала)	10,41	
122	Загрузочный цех	11,28	В3
123	Мясо-рыбный цех	18,28	В3
124	Моечная кухонной посуды	11,29	В3
125	ПУИ	5,53	
126	Помещение временного хранения пищевых отходов	9,37	В4
127	Моечная столовой посуды	46,82	В4
128	Горячий цех	45,30	В3
129	Холодный цех	10,12	В3
130	Обеденный зал	393,12	
131	Лестничная клетка (тип Н2)	17,68	
133	Сан. узел для мальчиков	8,29	
134	Сан. узел для девочек	7,82	
135	Коридор	83,12	
137	Коридор	146,67	
138	Коридор	142,66	
139	Лестничная клетка (тип Л1)	17,22	
140	Административный кабинет Тип 1	15,42	
141	Учебный кабинет	57,61	
142	Сан. узел для девочек	14,13	
143	Сан. узел для мальчиков	16,91	
144	ПУИ	3,09	В4
145	Лестничная клетка (тип Л1)	17,14	
146	Гимнастический зал	93,81	
147	Раздевальные	8,17	
148	Раздевальные	7,30	
150	Кабинет для индивидуальных занятий, в т.ч. с коррекционным педагогом	21,01	
151	Помещение для прокладки инженерных коммуникаций	15,07	В3
152	Учебный кабинет	53,08	
153	Учебный кабинет	54,85	
154	Учебный кабинет	54,31	
155	Учебные кабинет для изучения естествознания: химия	55,07	
156	Лаборанстская кабинета химии	17,09	В3
157	Учебные кабинет для изучения естествознания: физика	54,43	
158	Лаборанстская кабинета физики	18,10	В3
159	Учебные кабинеты для изучения естествознания: биологии + ОБЗР	71,91	
160	Лаборанстская кабинета биологии	18,75	В3
161	Кабинет материальной технологии Тип 2	49,10	В3
162	Кабинет материальной технологии Тип 1	54,82	В3
163	Лестничная клетка (тип Л1)	17,22	
164	Сан. узел персонала	1,78	
165	Сан. узел для мальчиков	16,02	
166	Сан. узел для девочек с комнатой личной гигиены	14,73	
167	Серверная	17,09	В3
168	Кроссовая	5,03	В3
169	Кроссовая	4,92	В3
		2 558,98 м²	

Условные обозначения

- сущ. стена Ж/Б
- Ст.2.4 – заменяемая перегородка: штукатурка,минераловатный утеплитель 100 мм, кирпич 120 мм, штукатурка
- Ст.2.5 – кладка из кирпича 65 мм, штукатурка
- Ст.2.8 – заменяемая перегородка: штукатурка, кирпич 120 мм, перегородка из плиты Аквапанель В 2 слоя 12,5 мм (с одной стороны), по металл. каркасу система "Кнауф" 75 мм, штукатурка
- Ст.2.9 – заменяемая перегородка: штукатурка, кирпич 120 мм, перегородка из плиты Аквапанель В 2 слоя 12,5 мм (с одной стороны), по металл. каркасу система "Кнауф" 50 мм, штукатурка
- Ст.2.10 – заменяемая перегородка: штукатурка, кирпич 120 мм, перегородка из плиты Аквапанель В 2 слоя 12,5 мм (с одной стороны), по металл. каркасу система "Кнауф" 100 мм с минераловатным утеплителем, штукатурка
- Ст.2.11 – заменяемая перегородка: перегородка из плиты Аквапанель В 2 слоя 12,5 мм (с одной стороны), по металл. каркасу система "Кнауф" 75 мм, кирпич 120 мм, перегородка из плиты Аквапанель В 2 слоя 12,5 мм (с одной стороны), по металл. каркасу система "Кнауф" 100 мм с минераловатным утеплителем, штукатурка
- Ст.2.12 – заменяемая перегородка: перегородка из плиты Аквапанель В 2 слоя 12,5 мм (с одной стороны), по металл. каркасу система "Кнауф" 75 мм, кирпич 120 мм, перегородка из плиты Аквапанель В 2 слоя 12,5 мм (с одной стороны), по металл. каркасу система "Кнауф" 100 мм с минераловатным утеплителем, штукатурка
- Ст.2.13 – заменяемая перегородка: перегородка из плиты Аквапанель В 2 слоя 12,5 мм (с одной стороны), по металл. каркасу система "Кнауф" 75 мм, кирпич 120 мм, перегородка из плиты Аквапанель В 2 слоя 12,5 мм (с одной стороны), по металл. каркасу система "Кнауф" 150 мм, штукатурка
- Ст.3.1 – заменяемый газобок 100 мм, штукатурка 20 мм с 2-х сторон
- Ст.3.1 – заменяемый газобок 100 мм, штукатурка 20 мм с 1-ой стороны
- Ст.3.1 – заменяемый газобок 100 мм
- Ст.3.2 – заменяемый газобок 200 мм, штукатурка 20 мм с 2-х сторон
- Ст.3.5 – заменяемая перегородка: штукатурка, минераловатный утеплитель 100 мм, газобок 100 мм, штукатурка
- Ст.4.1 – устройство оконного откоса из плиты Аквапанель В 1 слой 12,5 мм (с одной стороны), по металл. каркасу система "Кнауф" 27 мм
- Ст.4.2 – заменяемая перегородка из ГСП В 1 слой 12,5 мм (с одной стороны), по металл. каркасу система "Кнауф" 50 мм
- Ст.4.3 – заменяемая перегородка из плиты Аквапанель В 2 слоя 12,5 мм (с одной стороны), по металл. каркасу система "Кнауф" 50 мм с минераловатным утеплителем
- Ст.4.4 – заменяемая перегородка из плиты Аквапанель В 2 слоя 12,5 мм (с двух сторон), по металл. каркасу система "Кнауф" 50 мм с минераловатным утеплителем
- Ст.4.5 – заменяемая перегородка из плиты Аквапанель В 2 слоя 12,5 мм (с двух сторон), по металл. каркасу система "Кнауф" 75 мм с минераловатным утеплителем
- Ст.4.6 – заменяемая перегородка из плиты Аквапанель В 2 слоя 12,5 мм (с двух сторон), по металл. каркасу система "Кнауф" 100 мм с минераловатным утеплителем
- Ст.4.7 – заменяемая перегородка из плиты Аквапанель В 2 слоя 12,5 мм (с двух сторон), по металл. каркасу система "Кнауф" 150 мм с минераловатным утеплителем
- Ст.4.8 – заменяемая перегородка из плиты Аквапанель В 2 слоя 12,5 мм (с одной стороны), по металл. каркасу система "Кнауф" 75 мм с минераловатным утеплителем
- Ст.4.9 – заменяемая перегородка из плиты Аквапанель В 2 слоя 12,5 мм (с одной стороны), по металл. каркасу система "Кнауф" 75 мм с минераловатным утеплителем
- ст.5.1 – минераловатный утеплитель 100 мм, штукатурка
- Ст.4.10 – заменяемая перегородка КНАУФ САПФИР SL03.ru общей толщиной 100мм с однослойной обшивкой с 2 сторон из КНАУФ-листов САПФИР полиг. 12,5 мм
- Ст.4.11 – заменяемая перегородка из плиты Аквапанель В 2 слоя 12,5 мм (с одной стороны), по металл. каркасу система "Кнауф" 150 мм
- Ст.4.14 – заменяемая перегородка из плиты Аквапанель В 2 слоя 12,5 мм (с одной стороны), по металл. каркасу система "Кнауф" 75 мм
- Ст.4.15 – заменяемая перегородка из плиты Аквапанель В 2 слоя 12,5 мм (с одной стороны), по металл. каркасу система "Кнауф" 150 мм с минераловатным утеплителем
- Ст.4.16 – заменяемая перегородка из плиты Аквапанель В 2 слоя 12,5 мм (с одной стороны), по металл. каркасу система "Кнауф" 100 мм с минераловатным утеплителем
- (100) – марка помещения

0,000=168,265

						ГИП-28/24-П-АР	
						ГБОУ Школа № 218, расположенная по адресу: г. Москва, ул. Вучетича, д. 6	
Изм.	Колуч.	Лист	№Док.	Подп.	Дата		
Разработал		Белова Е.С.			09.25	Средняя общеобразовательная школа	Стадия: П; Лист: 11; Листов: 64
Проверил		Дубинин С.В.			09.25		
ГАП		Дубинин С.В.			09.25		
ГИП		Гущин А.В.				Кладочный план 1 этажа	И-ГРУПП ПРОЕКТНО-СТРОИТЕЛЬНАЯ КОМПАНИЯ
Н.контроль		Щукшин В.В.			09.25		

Кладочный план 2 этажа
М 1:200

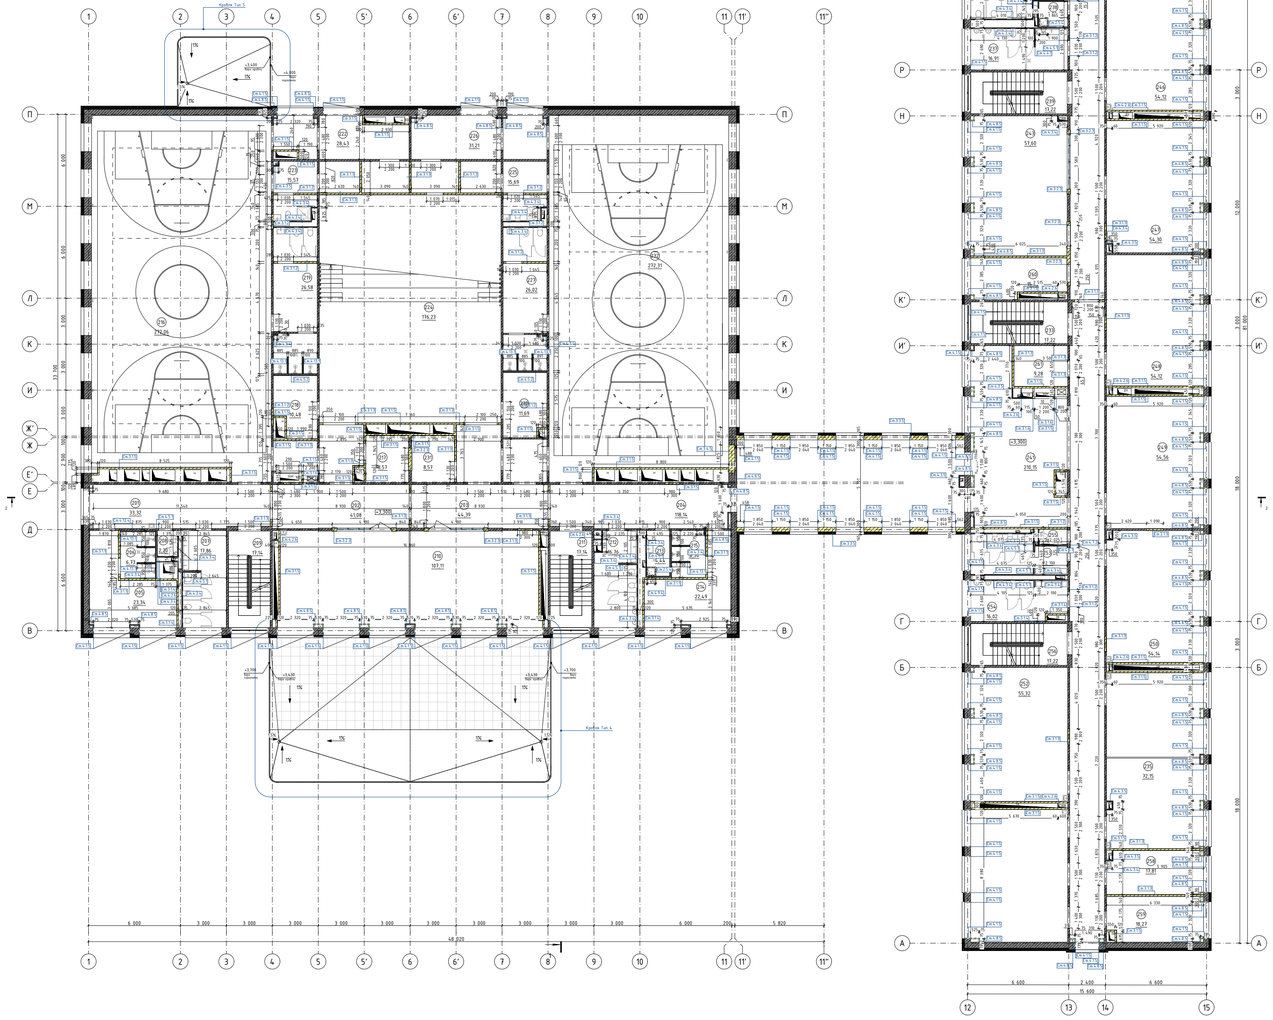

Экспликация помещений на отм. 3.300

№	Наименование	Площадь	Категория помещения
201	Коридор	33,32	
202	Коридор	41,08	
203	Коридор	44,39	
204	Коридор	118,14	
205	Раздевальная	23,34	
206	Душевая	6,73	
207	Сан. узел для девочек	17,86	
208	Сан. узел для персонала	2,20	
209	Лестничная клетка (тип Н2)	17,14	
210	Кабинет ИЗО	107,11	
211	Лестничная клетка (тип Н2)	17,14	
212	Сан. узел для мальчиков	16,76	
213	ПУИ	4,44	В4
214	Раздевальная	22,49	
215	Душевая	6,50	
216	Универсальный спортивный зал	272,06	
217	Кроссовая	8,57	В3
218	Артистическая с хранением костюмов	10,48	В3
219	Раздевальная	26,58	
222	Снарядная	28,43	В3
223	Комната инструктора с душем и сан. узлом	15,57	
224	Актовый зал	176,23	
225	Комната инструктора с душем и сан. узлом	15,69	
226	Снарядная	31,21	В3
227	Раздевальная	26,02	
230	Артистическая с хранением костюмов	11,69	В3
231	Кладовая инвентаря	8,57	В4
232	Универсальный спортивный зал	272,31	
233	Лестничная клетка (тип Л1)	17,22	
235	Кабинет иностранного языка	72,15	
236	Сан. узел для девочек	13,84	
237	Сан. узел для мальчиков	16,91	

№	Наименование	Площадь	Категория помещения
238	ПУИ	3,09	В4
239	Лестничная клетка (тип Л1)	17,22	
240	Кабинет естесствознания Тип 1	110,06	
241	Коридор	210,15	
243	Учебный кабинет	57,60	
244	Коридор	141,66	
245	Учебный кабинет	54,36	
246	Учебный кабинет	54,12	
247	Учебный кабинет	54,30	
248	Учебный кабинет	54,12	
249	Учебный кабинет	54,56	
250	Учебный кабинет	54,14	
252	Учебный кабинет	55,32	
253	Сан. узел для девочек	14,73	
254	Сан. узел для мальчиков	16,02	
255	Сан. узел для персонала	1,78	
256	Лестничная клетка (тип Л1)	17,22	
258	Кабинет для индивидуальных занятий, в т.ч. с учителем логопедом	17,81	
259	Административный кабинет Тип 1	18,27	
260	Административный кабинет Тип 1	15,42	
261	Кроссовая	9,28	В3
		2 533,40 м²	

Условные обозначения

- сущ. стена Ж/Б
- Ст.2.5 - кладка из кирпича 65 мм, штукатурка
- СТ.3.1 - заменяемый газобок 100 мм, штукатурка 20 мм с 2-х сторон
- СТ.3.1 - заменяемый газобок 100 мм, штукатурка 20 мм с 1-ой стороны
- СТ.3.1 - заменяемый газобок 100 мм
- СТ.3.2 - заменяемый газобок 200 мм, штукатурка 20 мм с 2-х сторон
- СТ.3.3 - заменяемый газобок 300 мм, штукатурка 20 мм с 1-ой стороны
- СТ.3.4 - заменяемый газобок 400 мм, штукатурка 20 мм с 1-ой стороны
- СТ.3.6 - заменяемая перегородка: штукатурка, минераловатный утеплитель 100 мм, газобок 300 мм, штукатурка
- Ст.4.1 - устройство оконного откоса из плиты Аквапанель В 1 слой 12,5 мм (с одной стороны), по металл. каркасу система "Кнауф" 27 мм
- СТ.4.2 - заменяемая перегородка из ГСП В 1 слой 12,5 мм (с одной стороны), по металл. каркасу система "Кнауф" 50 мм
- СТ.4.3 - заменяемая перегородка из плиты Аквапанель В 2 слоя 12,5 мм (с одной стороны), по металл. каркасу система "Кнауф" 50 мм с минераловатным утеплителем
- СТ.4.4 - заменяемая перегородка из плиты Аквапанель В 2 слоя 12,5 мм (с двух сторон), по металл. каркасу система "Кнауф" 50 мм с минераловатным утеплителем
- СТ.4.5 - заменяемая перегородка из плиты Аквапанель В 2 слоя 12,5 мм (с двух сторон), по металл. каркасу система "Кнауф" 75 мм с минераловатным утеплителем
- СТ.4.6 - заменяемая перегородка из плиты Аквапанель В 2 слоя 12,5 мм (с двух сторон), по металл. каркасу система "Кнауф" 100 мм с минераловатным утеплителем
- СТ.4.7 - заменяемая перегородка из плиты Аквапанель В 2 слоя 12,5 мм (с двух сторон), по металл. каркасу система "Кнауф" 150 мм с минераловатным утеплителем
- СТ.4.8 - заменяемая перегородка из плиты Аквапанель В 2 слоя 12,5 мм (с одной стороны), по металл. каркасу система "Кнауф" 50 мм. h от ур.ч.п. - 770 мм.
- Ст.4.9 - заменяемая перегородка из плиты Аквапанель В 2 слоя 12,5 мм (с одной стороны), по металл. каркасу система "Кнауф" 75 мм с минераловатным утеплителем
- (100) - марка помещения

0,000=168,265

						ГИП-28/24-П-АР	
						ГБОУ Школа № 218, расположенная по адресу: г. Москва, ул. Вучетича, д. 6	
Изм.	Колуч.	Лист	№Док.	Подп.	Дата		
Разработал		Белова Е.С.			09.25	Средняя общеобразовательная школа	Стадия: П; Лист: 12; Листов: 64
Проверил		Дубинин С.В.			09.25		
ГАП		Дубинин С.В.			09.25		
ГИП		Гущин А.В.				Кладочный план 2 этажа	И-ГРУПП ПРОЕКТНО-СТРОИТЕЛЬНАЯ КОМПАНИЯ
Н.контроль		Шукшин В.В.			09.25		

Кладочный план 3 этажа
М 1:200

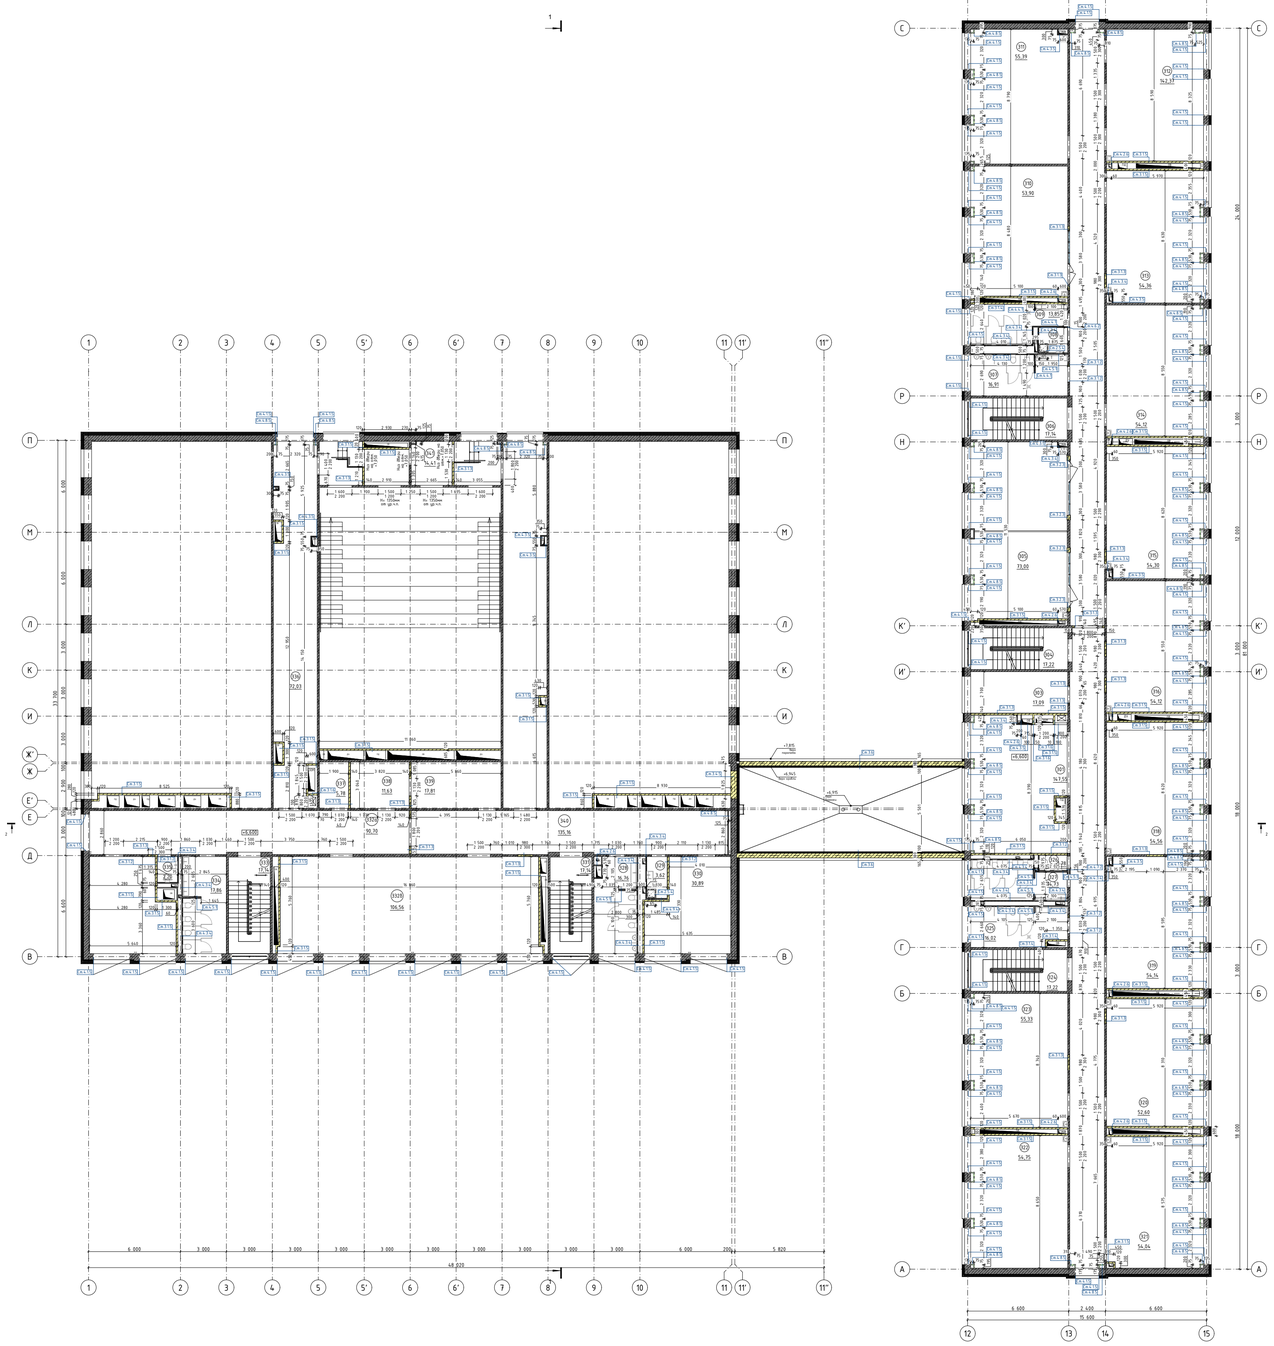

Экспликация помещений на отм. 6.600

№	Наименование	Площадь	Категория помещения
301	Коридор	147,55	
303	Серверная	17,09	В3
304	Лестничная клетка (тип Л1)	17,22	
305	Кабинет иностранного языка	73,00	
306	Лестничная клетка (тип Л1)	17,14	
307	Сан. узел для мальчиков	16,91	
308	ПУИ	3,09	В4
309	Сан. узел для девочек	13,85	
310	Учебный кабинет	53,90	
311	Учебный кабинет	55,39	
312	Коридор	142,37	
313	Учебный кабинет	54,36	
314	Учебный кабинет	54,12	
315	Учебный кабинет	54,30	
316	Учебный кабинет	54,12	
318	Учебный кабинет	54,56	
319	Учебный кабинет	54,14	
320	Учебный кабинет	52,60	
321	Учебный кабинет	54,04	
322	Учебный кабинет	54,75	
323	Учебный кабинет	55,33	
324	Лестничная клетка (тип Л1)	17,22	
325	Сан. узел для мальчиков	16,02	
326	Сан. узел персонала	1,78	
327	Сан. узел для девочек	14,73	
328	Сан. узел для мальчиков	16,76	
329	ПУИ	3,62	В4
330	Библиотека. Фонд хранения	30,89	В3
331	Лестничная клетка (тип Н2)	17,14	
332а	Коридор	90,70	
332б	Читальный зал	106,56	
333	Лестничная клетка (тип Н2)	17,14	
334	Сан. узел для девочек	17,86	
335	Сан. узел для персонала	2,20	
336	Коридор	72,03	
337	Кроссовая	5,78	В3
338	Кабинет для индивидуальных занятий. Студия звукозаписи	11,63	
339	Медиакласс	17,81	
340	Коридор	135,16	
341	Технический центр	14,41	В3
		1 709,27 м²	

Условные обозначения

- сущ. стена Ж/Б
- Ст.2.5 – кладка из кирпича 65 мм, штукатурка
- СТ.3.1 – заменяемый газобок 100 мм, штукатурка 20 мм с 2-х сторон
- СТ.3.1 – заменяемый газобок 100 мм, штукатурка 20 мм с 1-ой стороны
- СТ.3.1 – заменяемый газобок 100 мм
- СТ.3.2 – заменяемый газобок 200 мм, штукатурка 20 мм с 2-х сторон
- СТ.3.3 – заменяемый газобок 300 мм, штукатурка 20 мм с 1-ой стороны
- СТ.3.4 – заменяемый газобок 400 мм, штукатурка 20 мм с 1-ой стороны
- СТ.3.6 – заменяемая перегородка: штукатурка, минераловатный утеплитель 100 мм, газобок 300 мм, штукатурка
- Ст.4.1 – устройство оконного откоса из плиты Аквапанель В 1 слой 12,5 мм (с одной стороны), по металл. каркасу система "Кнауф" 27 мм
- СТ.4.2 – заменяемая перегородка из ГСП В 1 слой 12,5 мм (с одной стороны), по металл. каркасу система "Кнауф" 50 мм
- СТ.4.3 – заменяемая перегородка из плиты Аквапанель В 2 слоя 12,5 мм (с одной стороны), по металл. каркасу система "Кнауф" 50 мм с минераловатным утеплителем
- СТ.4.4 – заменяемая перегородка из плиты Аквапанель В 2 слоя 12,5 мм (с двух сторон), по металл. каркасу система "Кнауф" 50 мм с минераловатным утеплителем
- СТ.4.5 – заменяемая перегородка из плиты Аквапанель В 2 слоя 12,5 мм (с двух сторон), по металл. каркасу система "Кнауф" 75 мм с минераловатным утеплителем
- СТ.4.6 – заменяемая перегородка из плиты Аквапанель В 2 слоя 12,5 мм (с двух сторон), по металл. каркасу система "Кнауф" 100 мм с минераловатным утеплителем
- СТ.4.7 – заменяемая перегородка из плиты Аквапанель В 2 слоя 12,5 мм (с двух сторон), по металл. каркасу система "Кнауф" 150 мм с минераловатным утеплителем
- СТ.4.8 – заменяемая перегородка из плиты Аквапанель В 2 слоя 12,5 мм (с одной стороны), по металл. каркасу система "Кнауф" 50 мм. h от ур.ч.п. - 770 мм.
- Ст.4.9 – заменяемая перегородка из плиты Аквапанель В 2 слоя 12,5 мм (с одной стороны), по металл. каркасу система "Кнауф" 75 мм с минераловатным утеплителем
- (100) – марка помещения

0,000=168,265

Изм.	Колуч.	Лист	№Док.	Подп.	Дата	ГИП-28/24-П-АР			
						ГБОУ Школа № 218, расположенная по адресу: г. Москва, ул. Вучетича, д. 6			
Разработал		Белова Е.С.			09.25		Стадия	Лист	Листов
Проверил		Дубинин С.В.			09.25	Средняя общеобразовательная школа	П	13	64
ГАП		Дубинин С.В.			09.25				
ГИП		Гущин А.В.							
						Кладочный план 3 этажа	И-ГРУПП ПРОЕКТНО-СТРОИТЕЛЬНАЯ КОМПАНИЯ		
Н.контроль		Шукшин В.В.			09.25				

Кладочный план 4 этажа
М 1:200

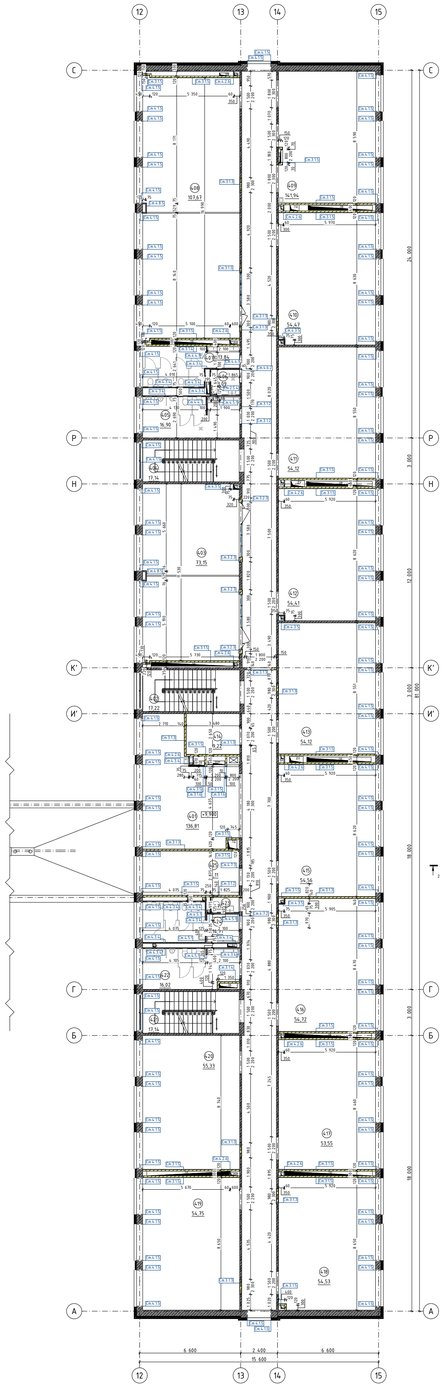

Экспликация помещений на отм. 9.900

№	Наименование	Площадь	Категория помещения
401	Коридор	136,81	
402	Лестничная клетка (тип Л1)	17,22	
403	Кабинет иностранного языка	73,15	
404	Лестничная клетка (тип Л1)	17,14	
405	Сан. узел для мальчиков	16,90	
406	ПУИ	3,09	В4
407	Сан. узел для девочек	13,84	
408	Кабинет информатики и информационных технологий	107,67	
409	Коридор	141,94	
410	Кабинет русского языка и литературы	54,47	
411	Кабинет русского языка и литературы	54,12	
412	Кабинет русского языка и литературы	54,41	
413	Кабинет математики	54,12	
414	Кроссовая	9,22	В3
415	Кабинет математики	54,56	
416	Кабинет истории Тип 1	54,72	
417	Кабинет географии	53,55	
418	Универсальный учебный кабинет	54,53	
419	Кабинет математики	54,75	
420	Кабинет истории Тип 1	55,33	
421	Лестничная клетка (тип Л1)	17,14	
422	Сан. узел для мальчиков	16,02	
423	Сан. узел персонала	1,78	
424	Сан. узел для девочек с комнатой личной гигиены	14,71	
425	Кабинет для индивидуальных занятий, в т.ч. с педагогом психологом	18,11	
		1 149,30 м²	

Условные обозначения

- суц. стена Ж/Б
- Ст.2.5 – кладка из кирпича 65 мм, штукатурка
- СТ.3.1 – заменяемый газобок 100 мм, штукатурка 20 мм с 2-х сторон
- СТ.3.1 – заменяемый газобок 100 мм, штукатурка 20 мм с 1-ой стороны
- СТ.3.1 – заменяемый газобок 100 мм
- СТ.3.2 – заменяемый газобок 200 мм, штукатурка 20 мм с 2-х сторон
- СТ.3.3 – заменяемый газобок 300 мм, штукатурка 20 мм с 1-ой стороны
- СТ.3.4 – заменяемый газобок 400 мм, штукатурка 20 мм с 1-ой стороны
- СТ.3.6 – заменяемая перегородка: штукатурка, минераловатный утеплитель 100 мм, газобок 300 мм, штукатурка
- Ст.4.1 – устройство оконного откоса из плиты Аквапанель В 1 слой 12,5 мм (с одной стороны), по металл. каркасу система "Кнауф" 27 мм
- СТ.4.2 – заменяемая перегородка из ГСП В 1 слой 12,5 мм (с одной стороны), по металл. каркасу система "Кнауф" 50 мм
- СТ.4.3 – заменяемая перегородка из плиты Аквапанель В 2 слоя 12,5 мм (с одной стороны), по металл. каркасу система "Кнауф" 50 мм с минераловатным утеплителем
- СТ.4.4 – заменяемая перегородка из плиты Аквапанель В 2 слоя 12,5 мм (с двух сторон), по металл. каркасу система "Кнауф" 50 мм с минераловатным утеплителем
- СТ.4.5 – заменяемая перегородка из плиты Аквапанель В 2 слоя 12,5 мм (с двух сторон), по металл. каркасу система "Кнауф" 75 мм с минераловатным утеплителем
- СТ.4.6 – заменяемая перегородка из плиты Аквапанель В 2 слоя 12,5 мм (с двух сторон), по металл. каркасу система "Кнауф" 100 мм с минераловатным утеплителем
- СТ.4.7 – заменяемая перегородка из плиты Аквапанель В 2 слоя 12,5 мм (с двух сторон), по металл. каркасу система "Кнауф" 150 мм с минераловатным утеплителем
- СТ.4.8 – заменяемая перегородка из плиты Аквапанель В 2 слоя 12,5 мм (с одной стороны), по металл. каркасу система "Кнауф" 50 мм. h от ур.ч.п. – 770 мм.
- Ст.4.9 – заменяемая перегородка из плиты Аквапанель В 2 слоя 12,5 мм (с одной стороны), по металл. каркасу система "Кнауф" 75 мм с минераловатным утеплителем
- (100) – марка помещения

0,000=168,265

						ГИП-28/24-П-АР
						ГБОУ Школа № 218, расположенная по адресу: г. Москва, ул. Вучетича, д. 6
Изм.	Колуч.	Лист	№Док.	Подп.	Дата	
Разработал		Белова Е.С.			09.25	Средняя общеобразовательная школа
Проверил		Дубинин С.В.			09.25	
ГАП		Дубинин С.В.			09.25	
ГИП		Гущин А.В.				Кладочный план 4 этажа
Н.контроль		Шукшин В.В.			09.25	

Стадия	Лист	Листов
П	14	64

И-ГРУПП
ПРОЕКТНО-СТРОИТЕЛЬНАЯ КОМПАНИЯ

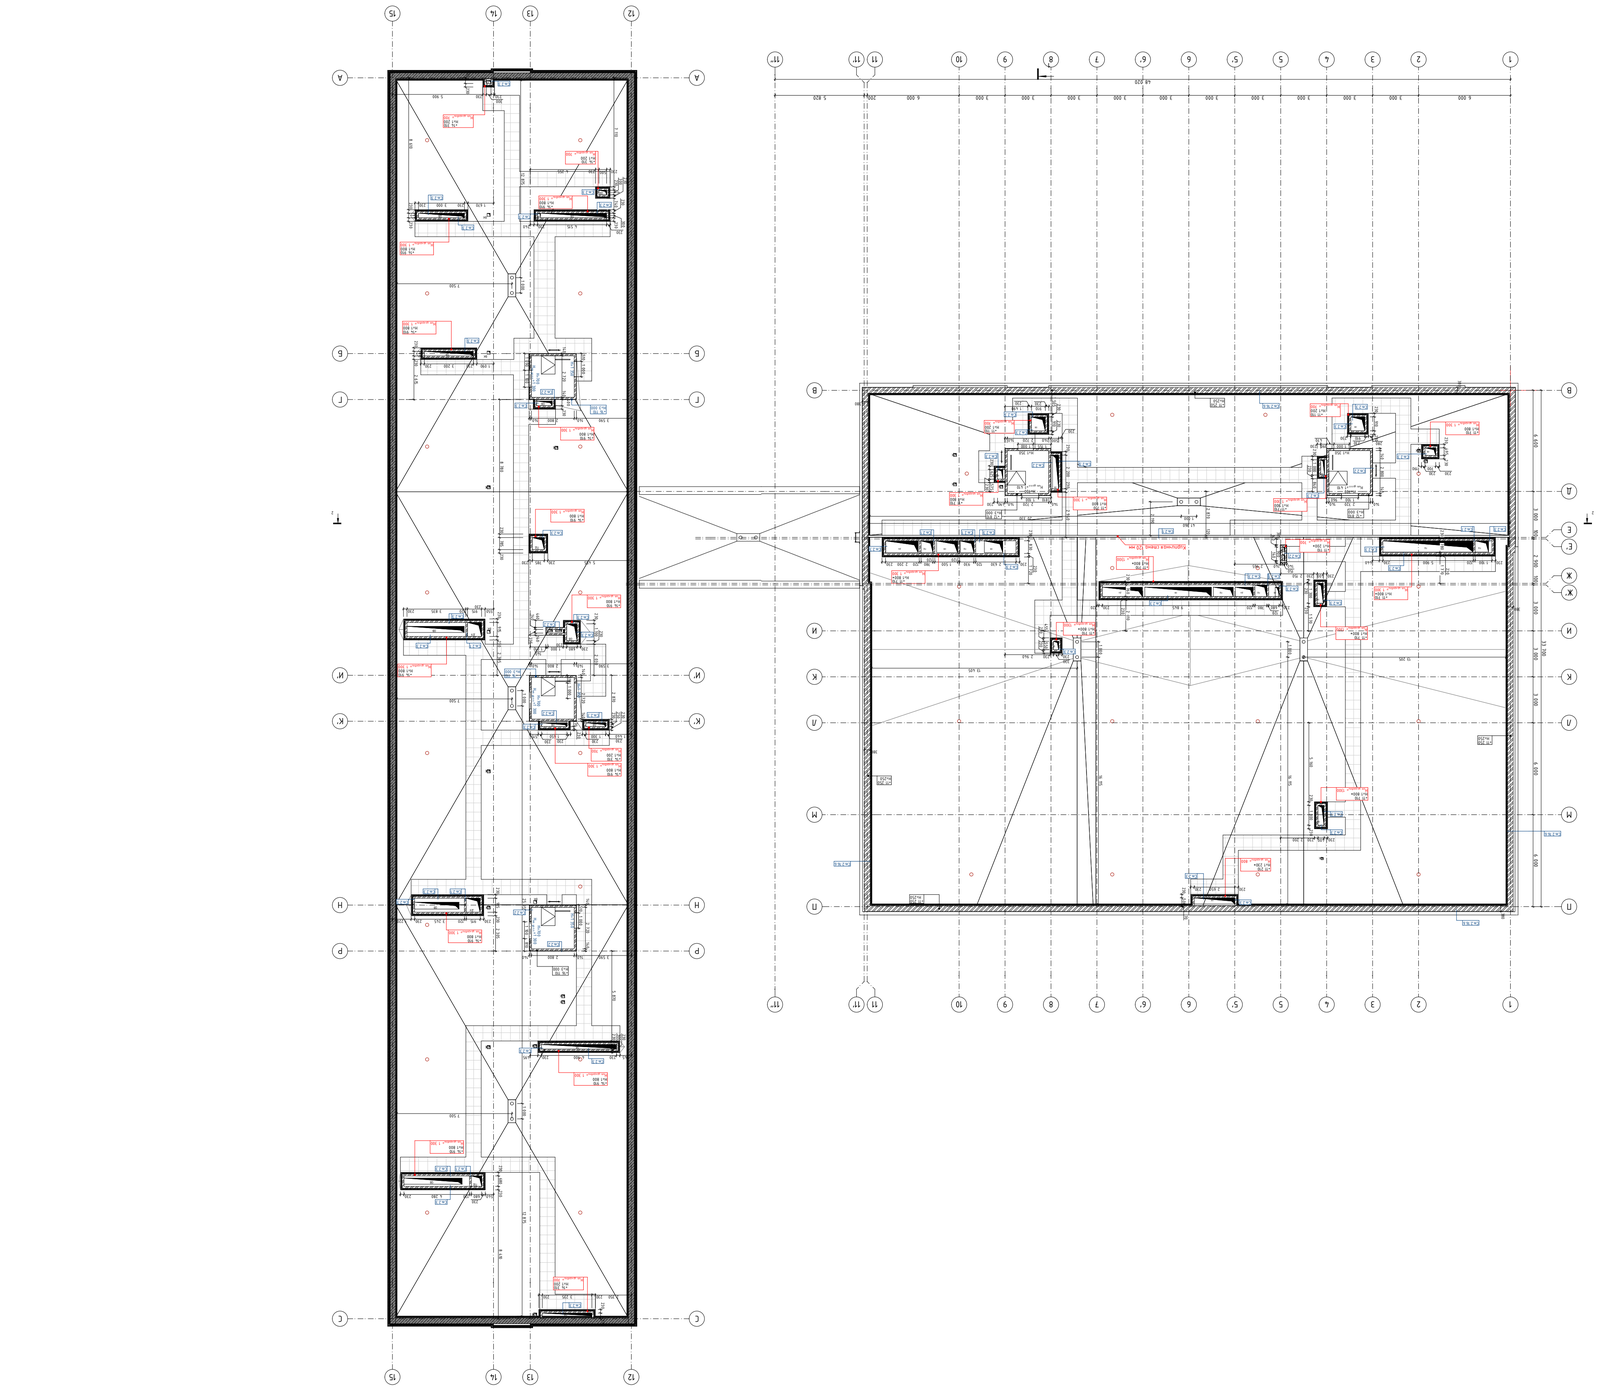

Кладочный план выходов на кровлю
М 1:200

0,000=168,265

Изм.	Кол.уч.	Лист	№док.	Подп.	Дата
Разработал	Беляев Е.С.			09.25	
Проверил	Ардышев С.В.			09.25	
ГАП	Ардышев С.В.			09.25	
ГИП	Гущин А.В.				
Н.контроль	Шухцов В.В.			09.25	

ГИП-28/24-Л-АР

ГБОУ Школа № 218, расположенная по адресу:
г. Москва, ул. Вучетича, д. 6

Стадия | Лист | Листов
П | 15 | 64

Средняя общеобразовательная школа

Кладочный план выходов на кровлю

Н-РУММ
ПРОЕКТНО-СТРОИТЕЛЬНАЯ КОМПАНИЯ

План демонтажа полов подвального этажа

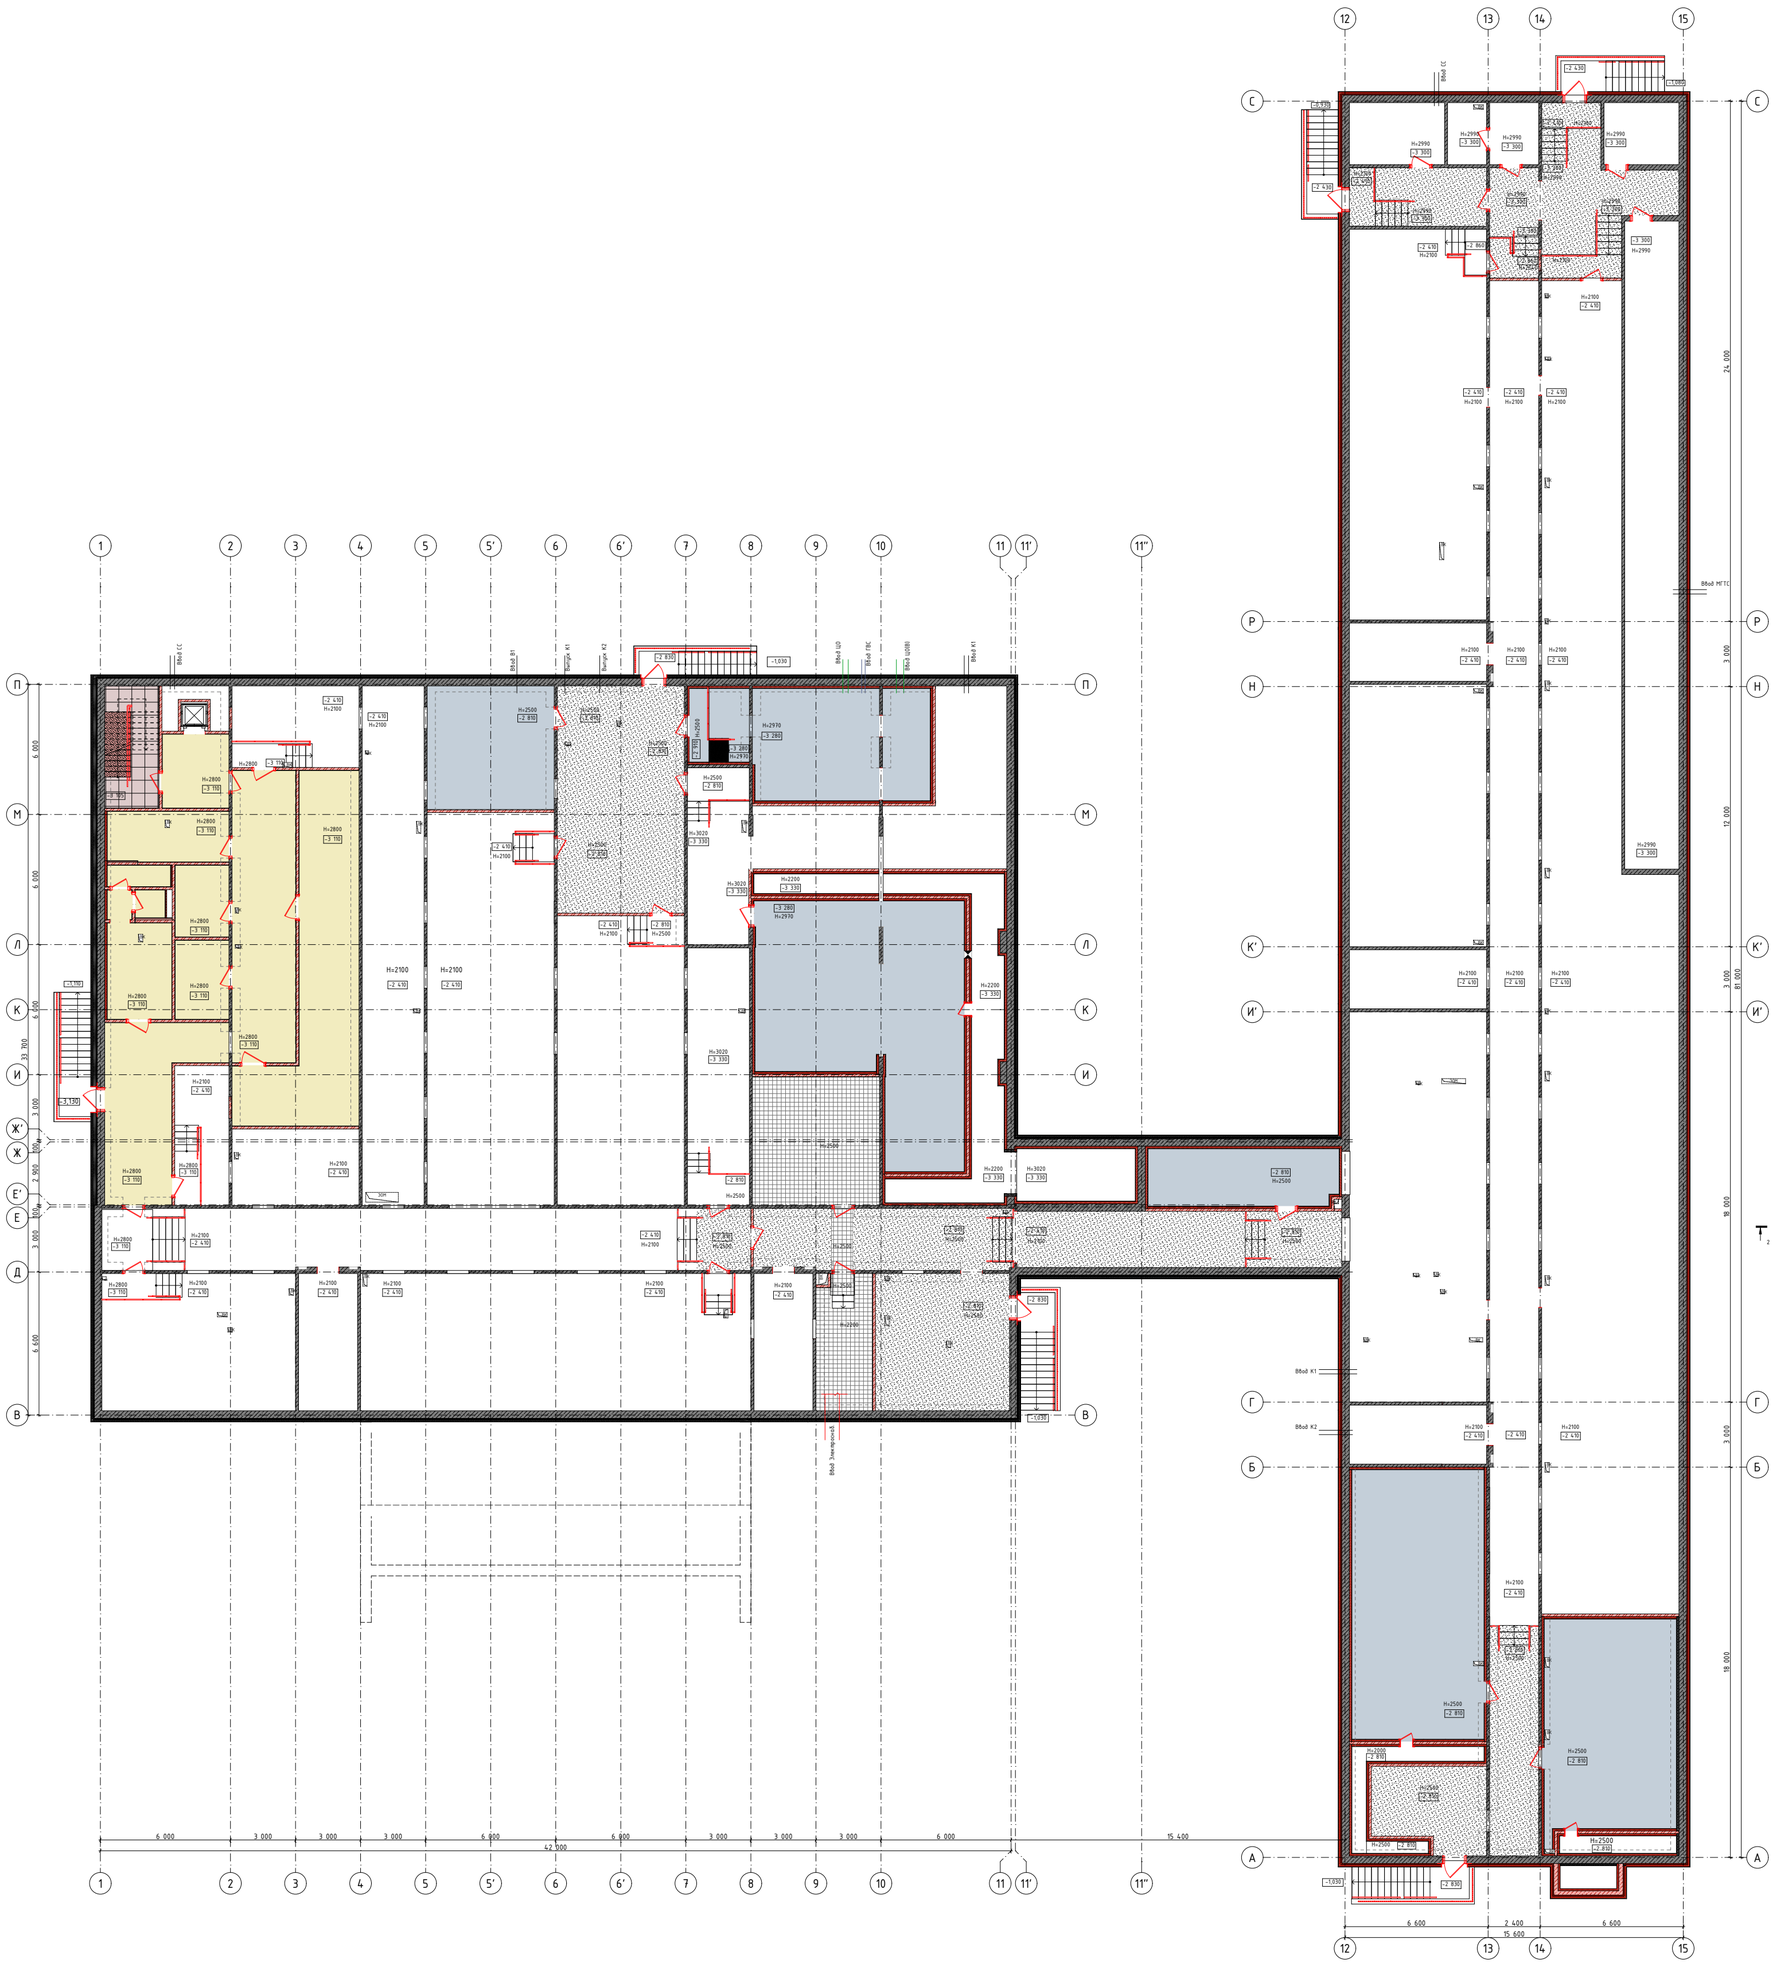

Условные обозначения

- Тип 2
- Тип 4
- Тип 4*
- Тип 11
- Тип 12
- Тип 13

						ГИП-28/24-П-АР	
						ГБОУ Школа № 218, расположенная по адресу: г. Москва, ул. Вучетича, д. 6	
Изм.	Колуч.	Лист	№Док.	Подп.	Дата		
Разработал		Белова Е.С.			09.25	Средняя общеобразовательная школа	Стадия: П; Лист: 16; Листов:
Проверил		Дубинин С.В.			09.25		
ГАП		Дубинин С.В.			09.25		
ГИП		Гущин А.В.				План демонтажа полов подвального этажа	И-ГРУПП ПРОЕКТНО-СТРОИТЕЛЬНАЯ КОМПАНИЯ
Н.контроль		Шукшин В.В.			09.25		

План демонтажа полов 1 этажа на отм. 0,000

План демонтажа полов 2 этажа на отм. +3.300

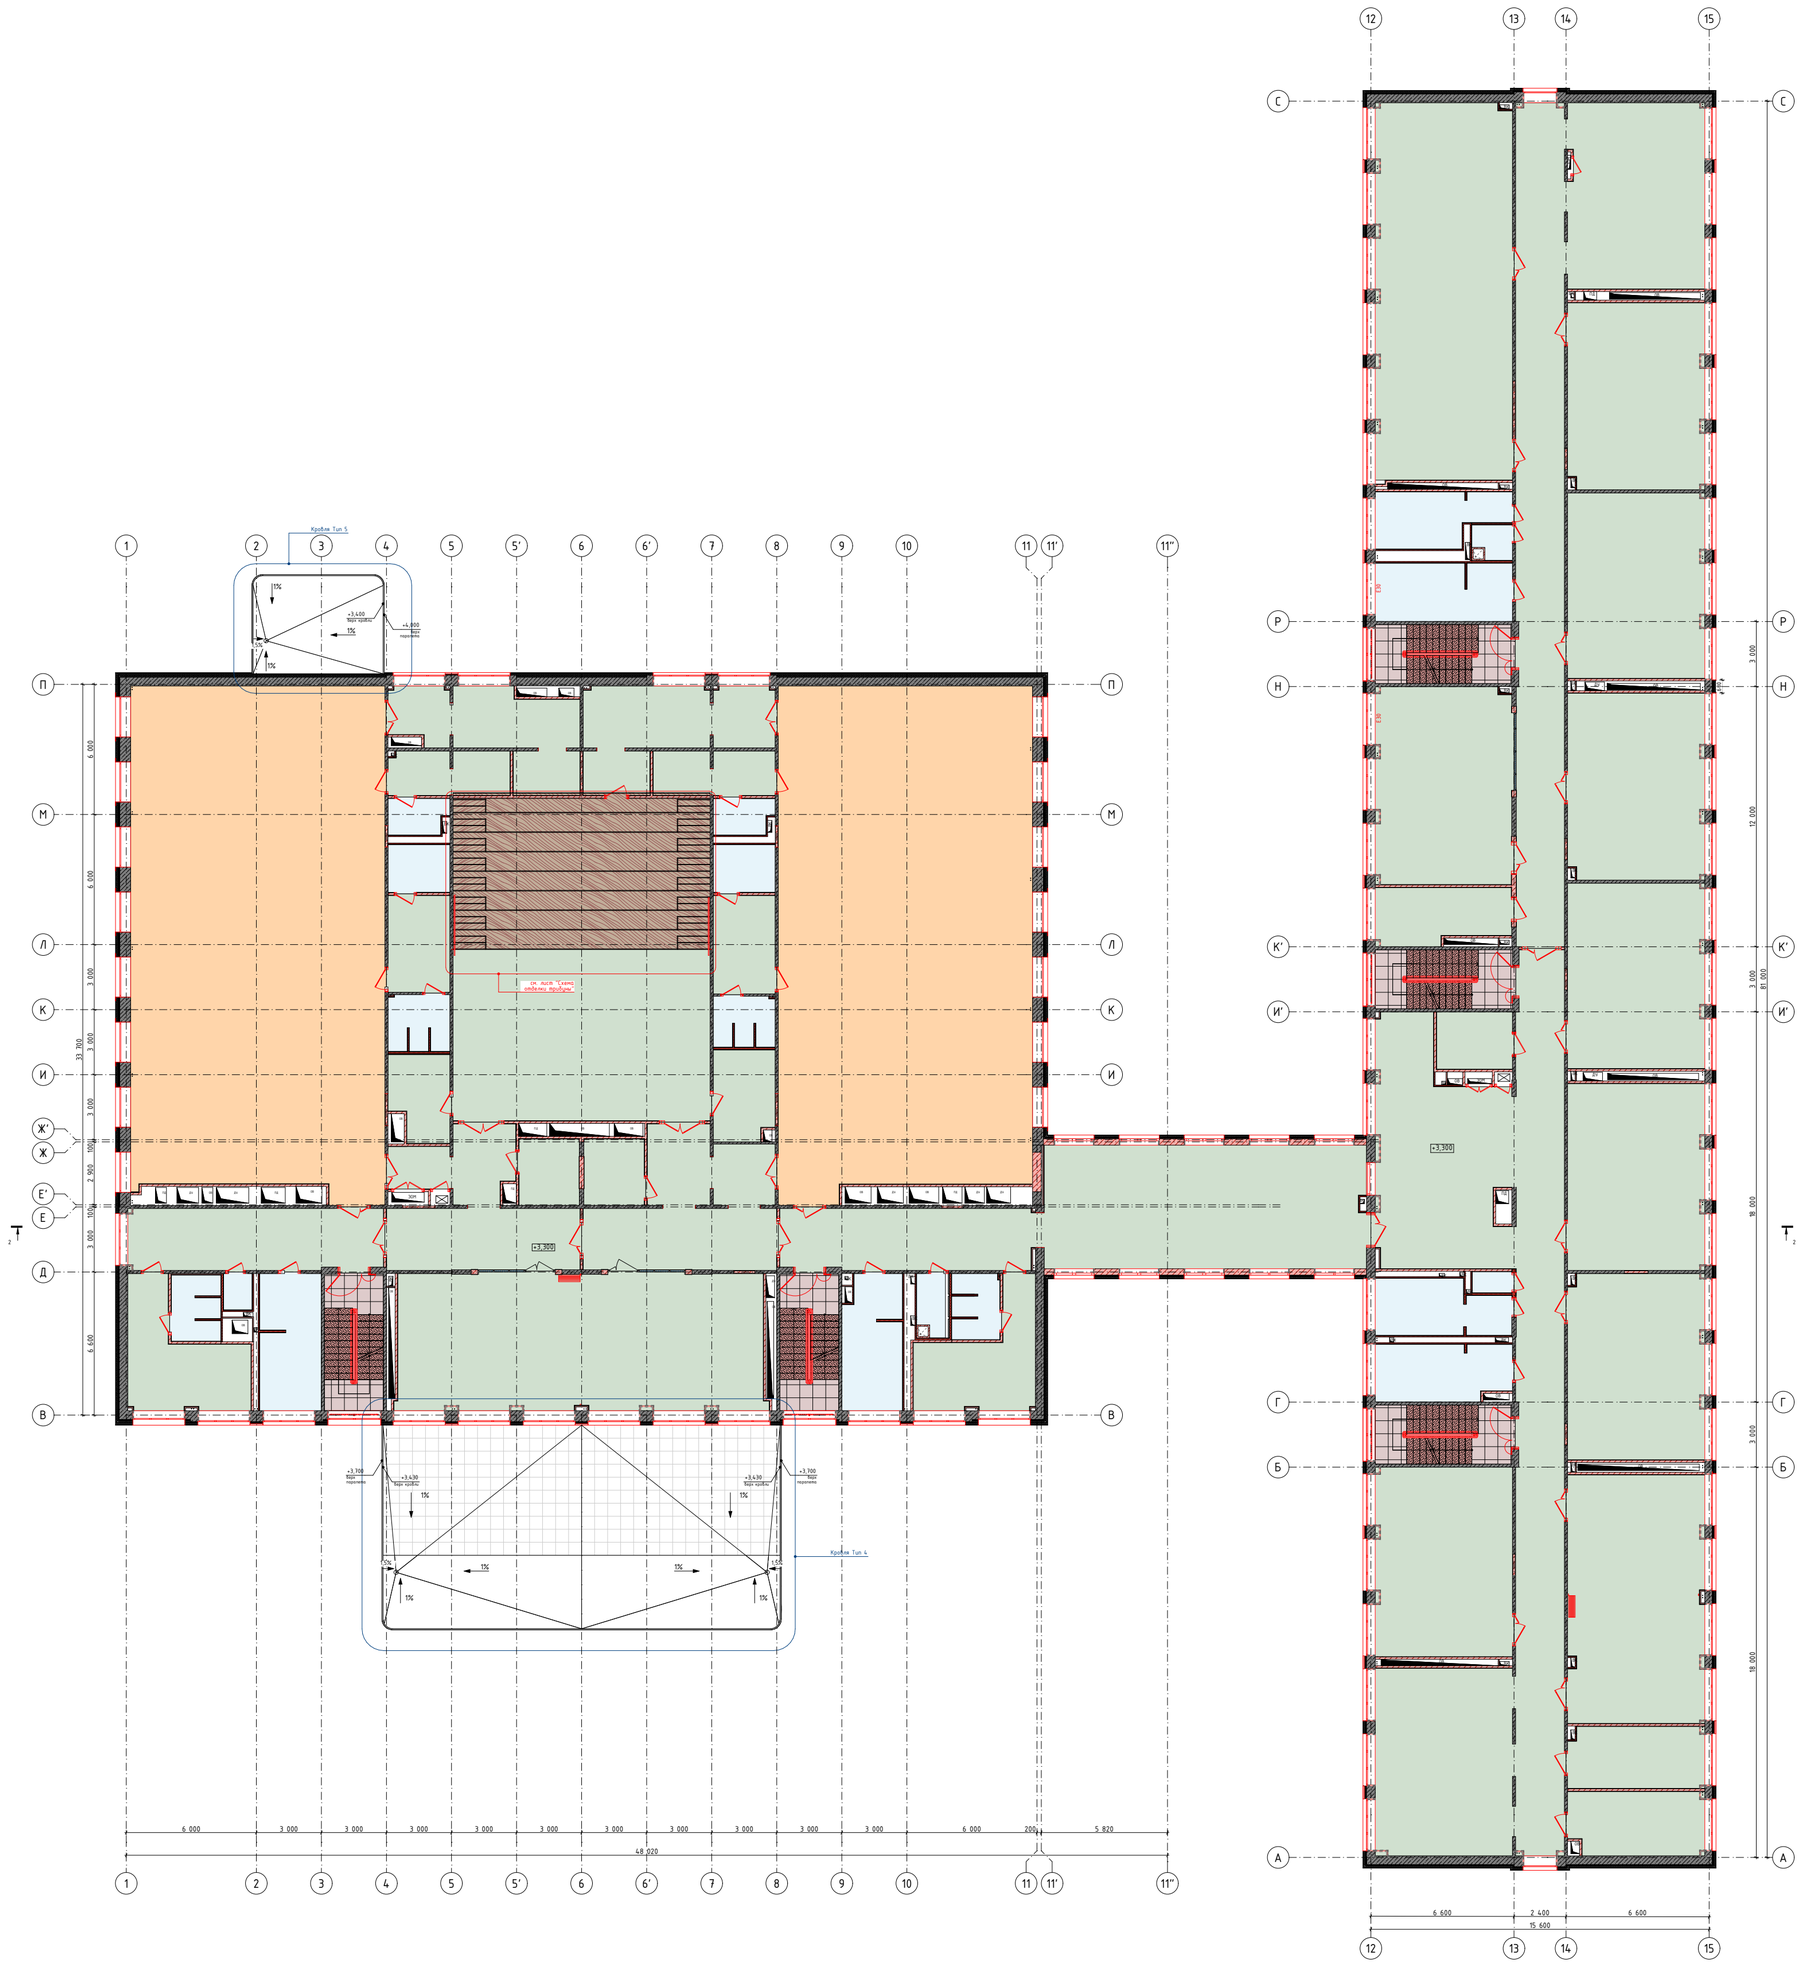

Условные обозначения

- Тип 1
- Тип 6
- Тип 10
- Тип 12
- Тип 13

						ГИП-28/24-П-АР	
						ГБОУ Школа № 218, расположенная по адресу: г. Москва, ул. Вучетича, д. 6	
Изм.	Колуч.	Лист	№Док.	Подп.	Дата		
Разработал		Белова Е.С.			09.25	Средняя общеобразовательная школа	Стадия: П; Лист: 18; Листов:
Проверил		Дубинин С.В.			09.25		
ГАП		Дубинин С.В.			09.25		
ГИП		Гущин А.В.				План демонтажа полов 2 этажа на отм. +3.300	И-ГРУПП ПРОЕКТНО-СТРОИТЕЛЬНАЯ КОМПАНИЯ
Н.контроль		Шукшин В.В.			09.25		

						ГИП-28/24-П-АР
Изм.	Кол.уч.	Лист	№док.	Подп.	Дата	ГБОУ Школа №218, расположенная по адресу: г. Москва, ул. Вучетича, д. 6
Разработал		Беляева Е.С.			09.25	
Проверил		Дубинин С.В.			09.25	
ГАП		Дубинин С.В.			09.25	Средняя общеобразовательная школа
ГИП		Гущин А.В.				
Н.контроль		Шухшин В.В.			09.25	План демонтажа полов 3 этажа на отм. +6.600

Стадия	Лист	Листов
П	19	

ГЕОДЕЗИЧЕСКО-СТРОИТЕЛЬНАЯ КОМПАНИЯ

Условные обозначения

- Тип 1
- Тип 6
- Тип 8
- Тип 12
- Тип 13

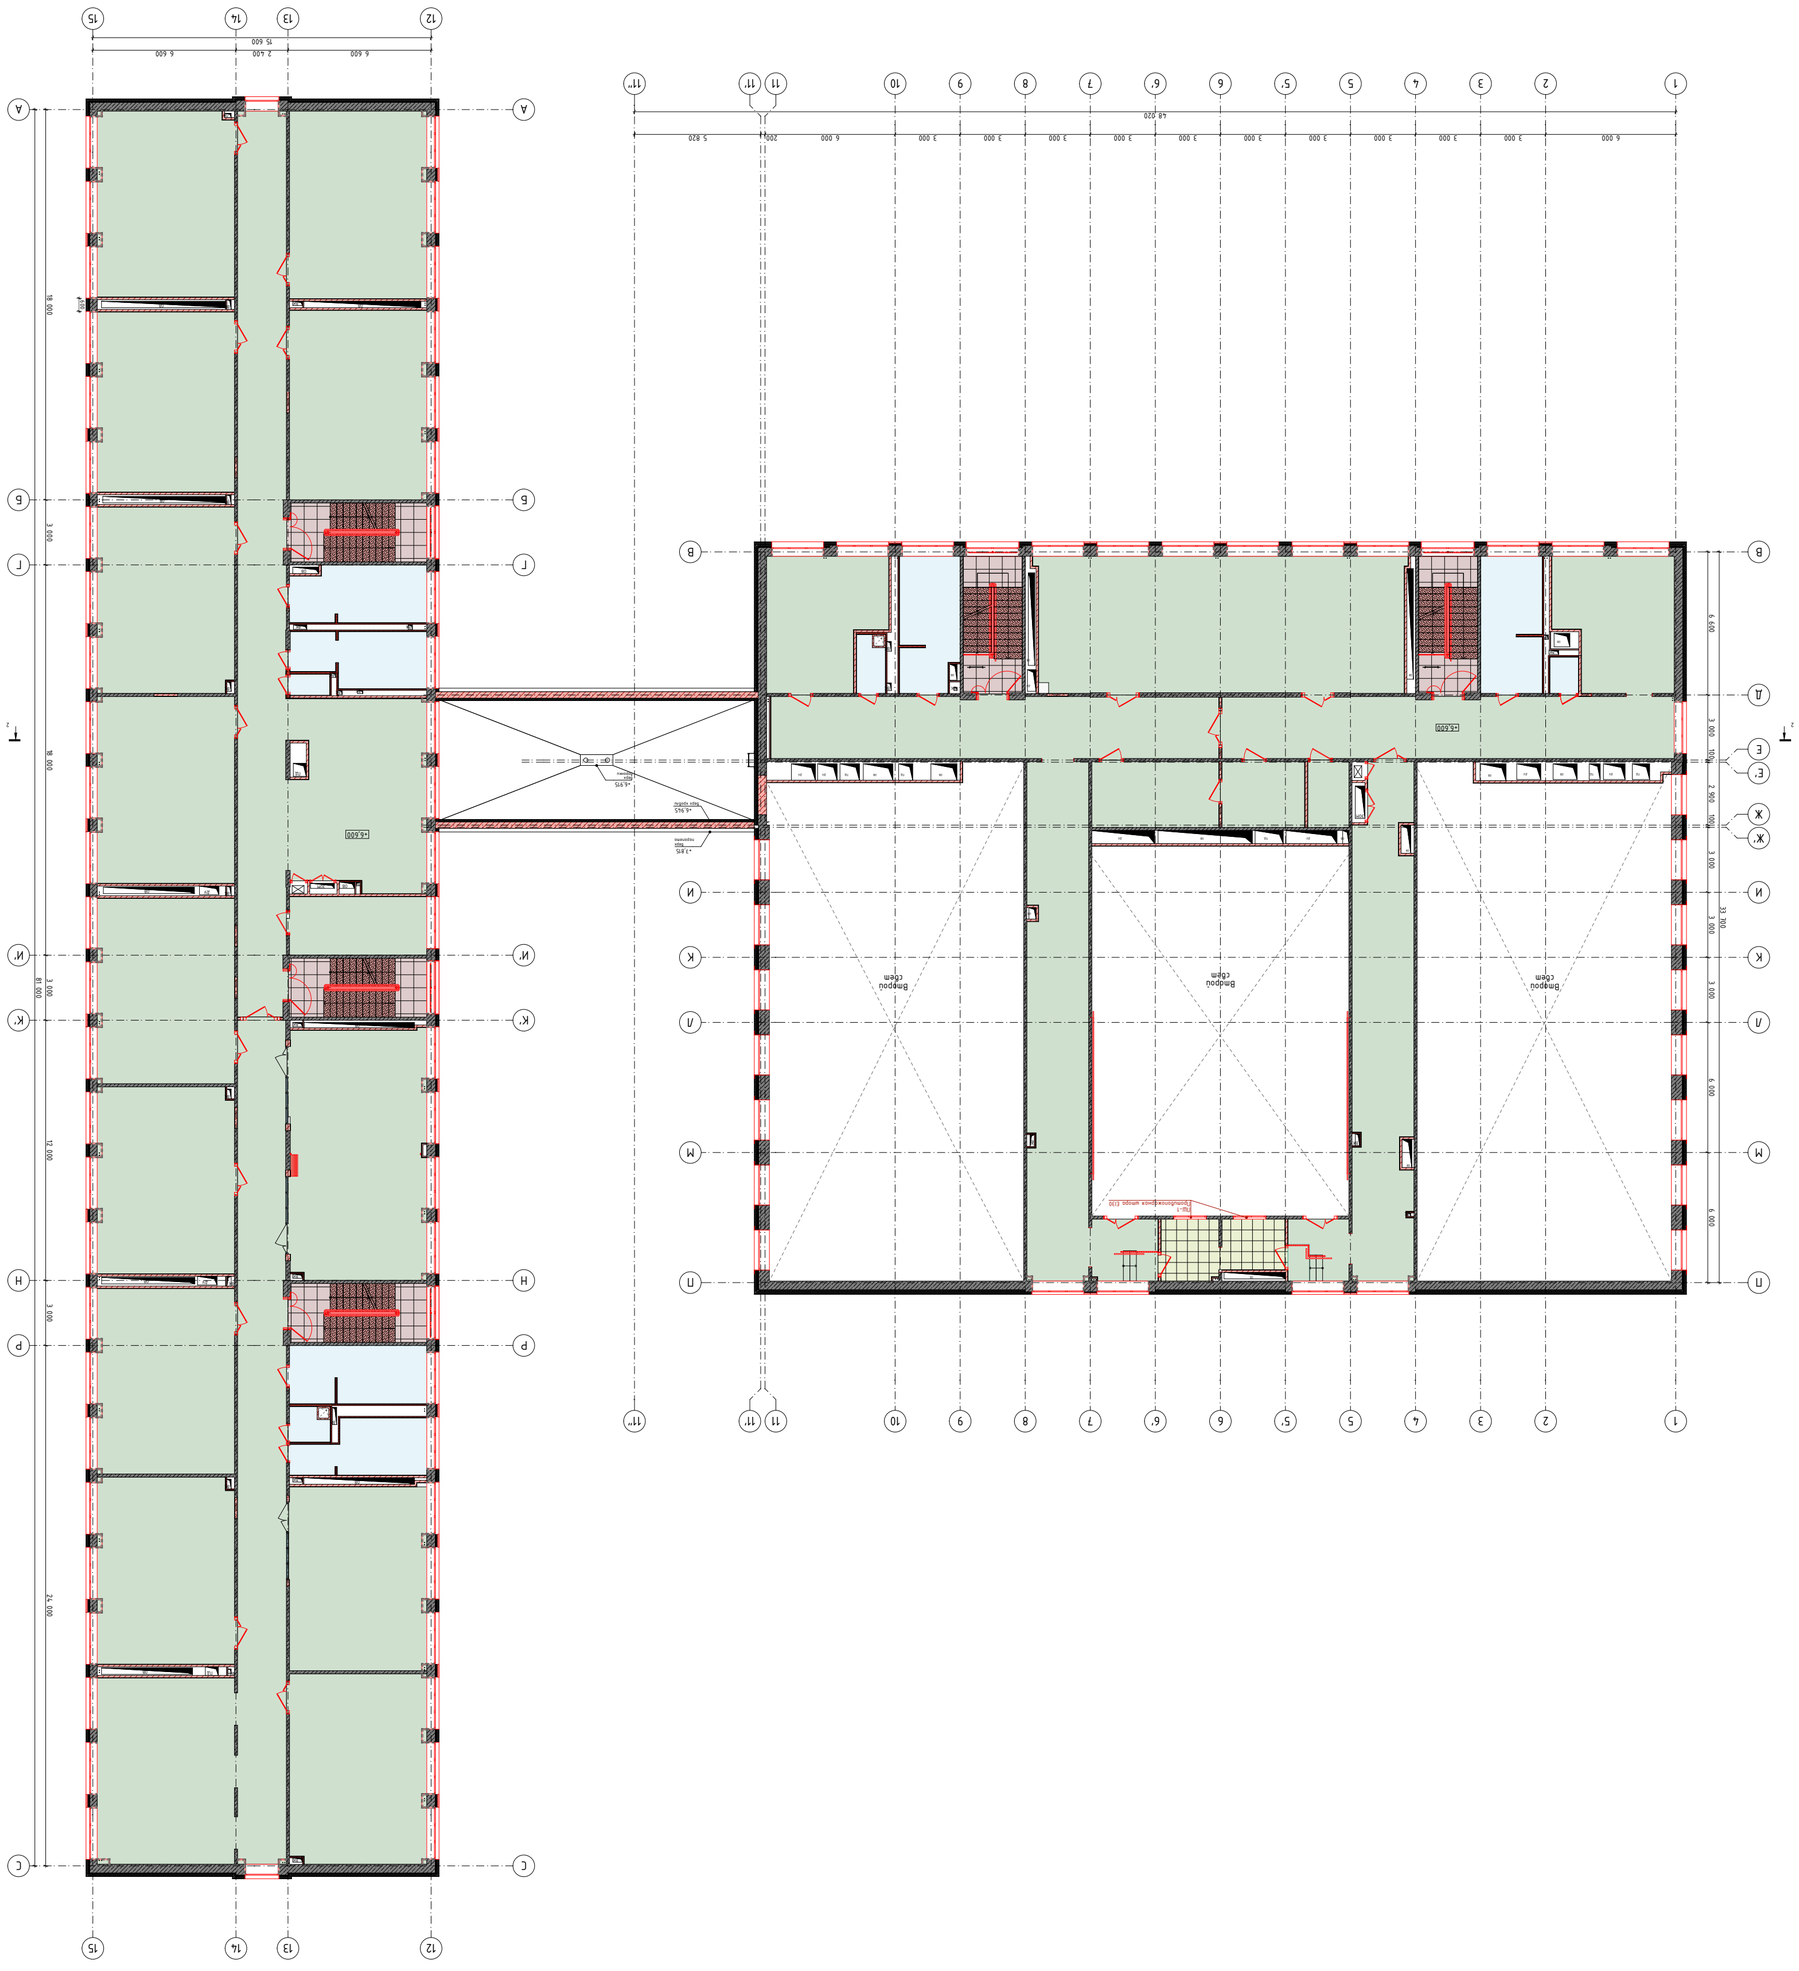
Вводно-распределительное устройство ВРУ-1
Венткамера
Венткамера
Венткамера
-4.915
-4.945
+6.000
+6.600
1 2 3 4 5 5' 6 6' 7 8 9 10 11 11' 11''
А Б В Г Д Е Ж И К Л М Н П Р С Т У
6 000 3 000 3 000 3

План полов подвального этажа
М 1:200

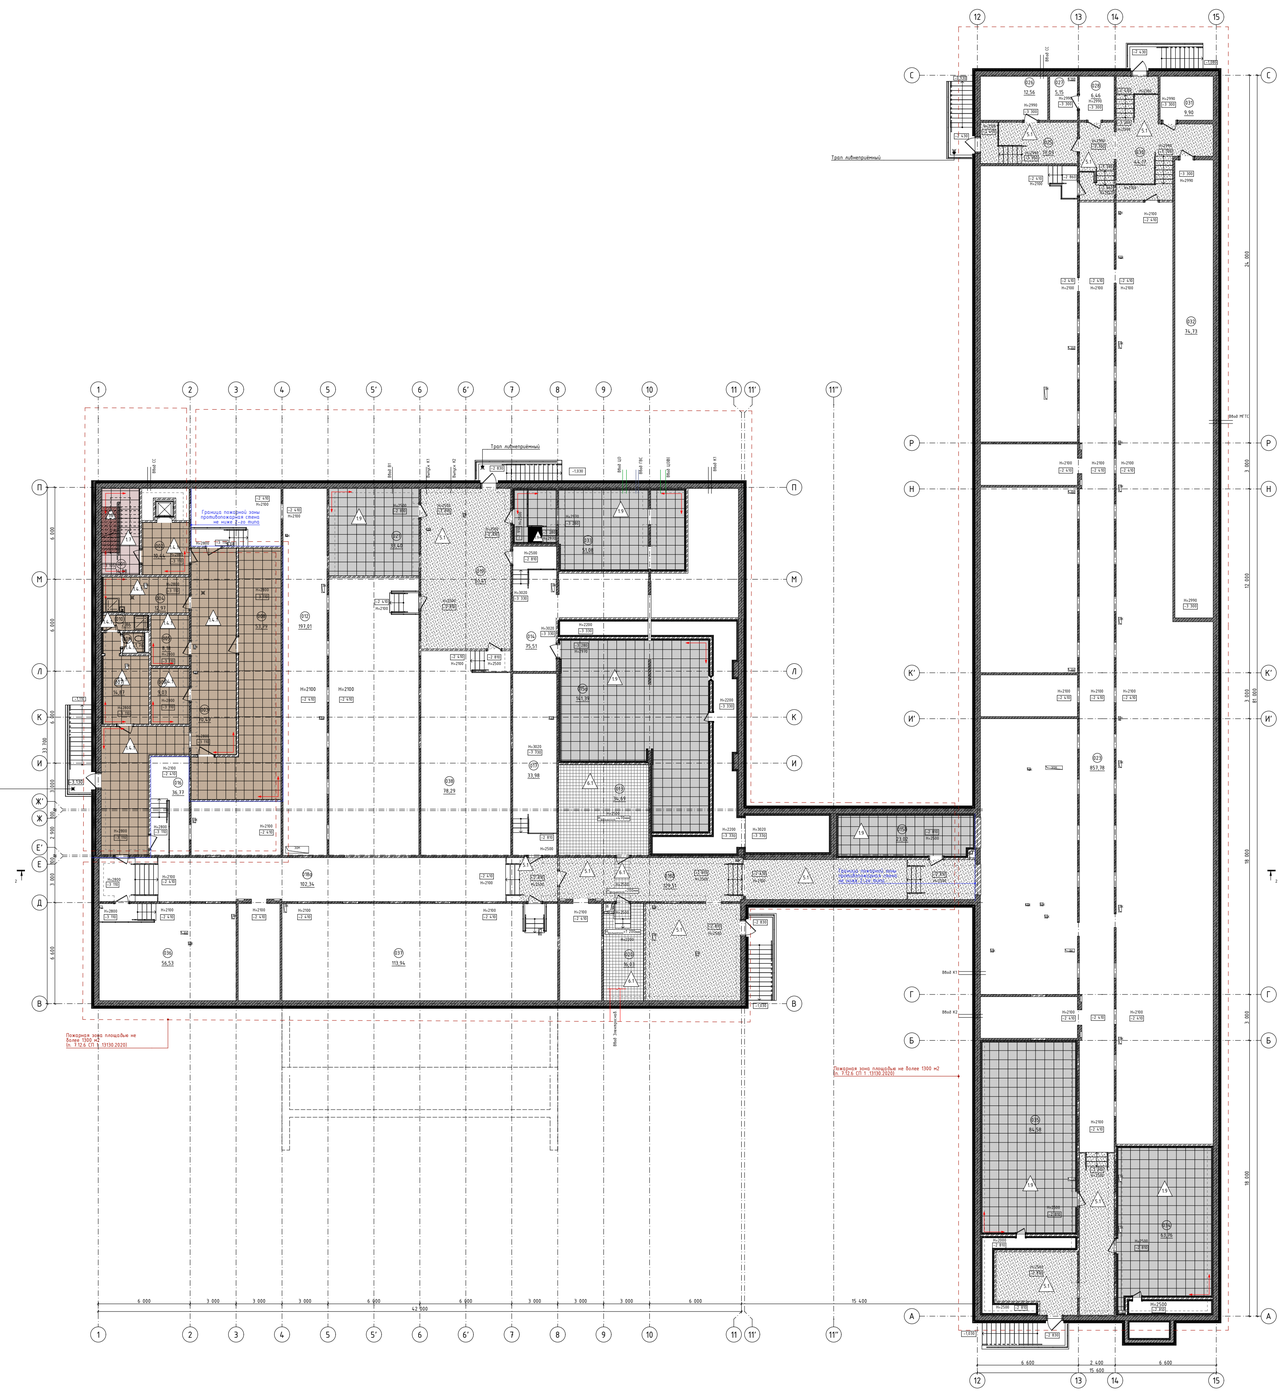

Экспликация помещений на отм. -3.000

№	Наименование	Площадь	Категория помещения
001	Лестничная клетка технологическая (для персонала)	14,08	
002	Тамбур-шлюз 1-го типа	10,44	
003	Коридор	70,49	
004	ПУИ	12,97	В3
005	Кладовая овощей	8,18	В4
006	Кладовая сухих продуктов	9,03	В4
007	Помещение персонала (не более 5 чел.)	14,87	
008	Помещение для установки холодильных камер	53,79	В3
009	Сан. узел	1,76	
010	Душевая	2,86	
012	Техническое помещение (для прокладки инженерных коммуникаций)	197,01	В4
013	Электрощитовая	34,69	В3
014	Техническое помещение (для прокладки инженерных коммуникаций)	75,51	В4
015а	Венткамера	141,39	В4
015б	Венткамера	23,02	В4
016	Техническое помещение (для прокладки инженерных коммуникаций)	36,77	В4
017	Техническое помещение (для прокладки инженерных коммуникаций)	33,98	В4
018а	Коридор	102,34	
018б	Коридор	129,51	
019	Коридор	61,41	
020	Электрощитовая	16,03	В3
021	Водомерный узел	33,40	Д
023	Техническое помещение (для прокладки инженерных коммуникаций)	857,78	В4
025	Коридор	17,09	
026	Техническое помещение (для прокладки инженерных коммуникаций)	12,56	В4
027	Техническое помещение (для прокладки инженерных коммуникаций)	5,15	В4
028	Техническое помещение (для прокладки инженерных коммуникаций)	6,46	В4
030	Коридор	44,17	
031	Техническое помещение (для прокладки инженерных коммуникаций)	9,90	В4
032	Техническое помещение (для прокладки инженерных коммуникаций)	74,73	В4
033	ИТП	51,08	В4
034	Венткамера	63,76	В4
035	Венткамера	84,58	В4
036	Техническое помещение (для прокладки инженерных коммуникаций)	56,53	В4
037	Техническое помещение (для прокладки инженерных коммуникаций)	113,94	В4
038	Техническое помещение (для прокладки инженерных коммуникаций)	78,29	В4
36		2 559,55 м²	

Условные обозначения:

14.1 - Керамогранит крупноформатный
Размер: 600x600x9мм Производитель: Kerama Marazzi Фондаменто Пепельный светлый обрезной Артикул: DL600920R

17 - Керамогранит крупноформатный
600x600x9мм Производитель: Kerama Marazzi Артикул: DD641020R

18 - ступень забальцованная с противоскользящей насечкой
600x300x9мм Производитель: Kerama Marazzi Артикул: DD205320R

19 - Керамическая плитка 600x600x9мм

5.1 - обеспыливание

6.1 - Фальшпол,см. раздел КР

0,000=168,265

Изм.	Колич.	Лист	№Док.	Подп.	Дата
Разработал		Белова Е.С.			09.25
Проверил		Дубинин С.В.			09.25
ГАП		Дубинин С.В.			09.25
ГИП		Гущин А.В.			
Н.контроль		Шукшин В.В.			09.25

ГИП-28/24-П-АР

ГБОУ Школа № 218, расположенная по адресу: г. Москва, ул. Вучетича, д. 6

Средняя общеобразовательная школа

Стадия	Лист	Листов
П	22	64

План полов подвального этажа

И-ГРУПП
ПРОЕКТНО-СТРОИТЕЛЬНАЯ КОМПАНИЯ

План полов 1 этажа на отм. 0,000
М 1:200

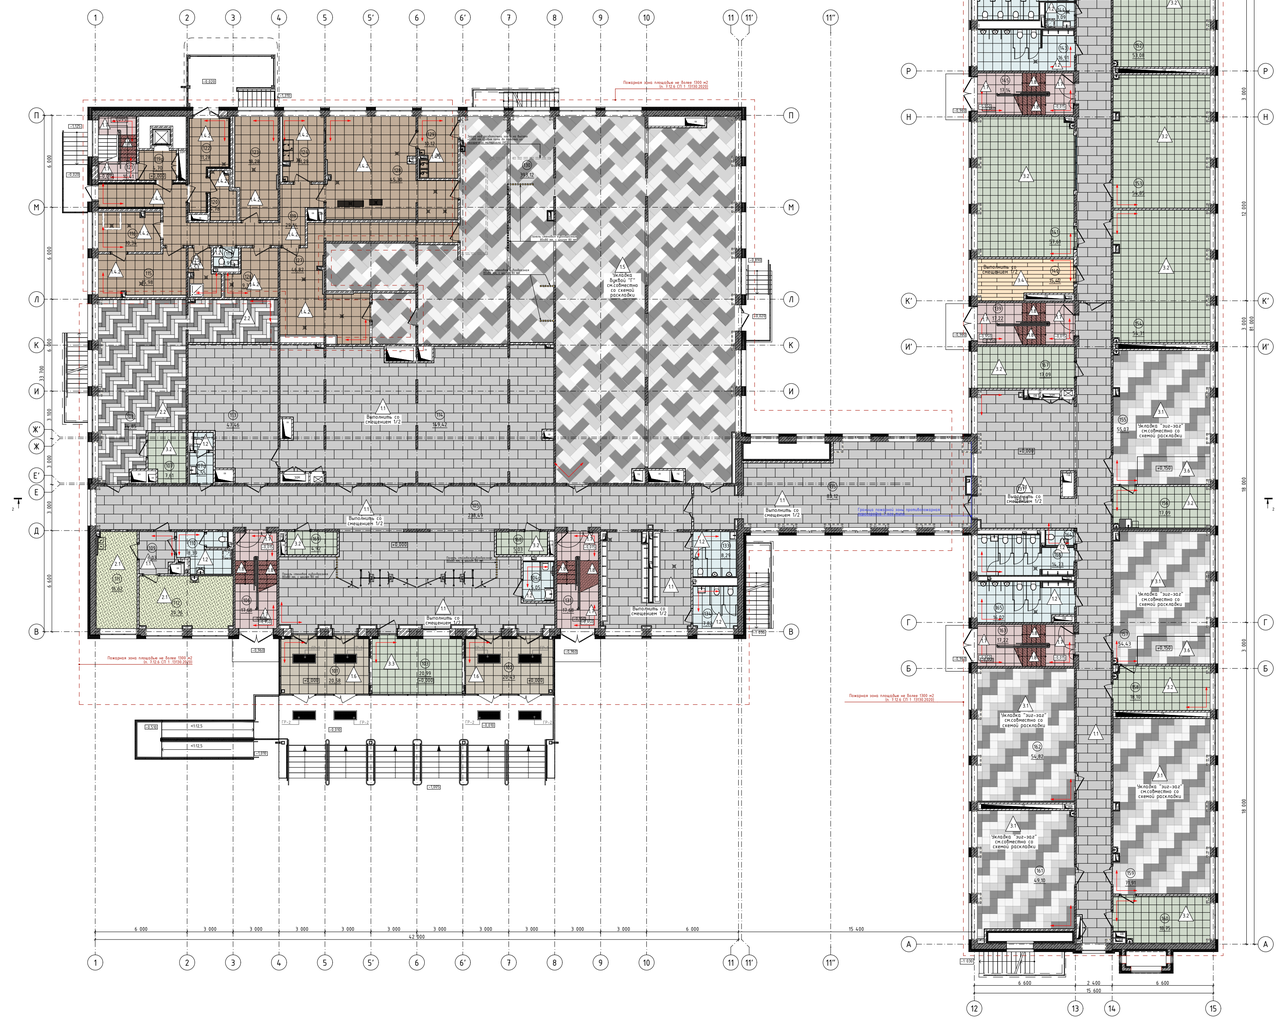

Экпликация помещений на отм. 0.000

№	Наименование	Площадь	Категория помещения
101	Тамбур	20,58	
102	Тамбур	20,43	
103	Комната охраны с диспетчерским пунктом	20,99	
104а	Сан. узел МГН	5,05	
105	Вестибюль	238,49	
106	Лестничная клетка (тип Н2)	17,68	
107	Гардеробная комната (для учителей)	7,61	
107а	Сан. узел для персонала	4,55	
108	Кабинет с рабочим пространством для учителей Тип 2	74,85	
109	Тамбур	6,03	
110	Туалет медблока с местом для приготовления дезинфицирующих средств и хранения уборочного инвентаря	8,39	
111	Процедурный (прививочный) кабинет	16,62	
112	Кабинет врача	20,76	
113	Гардероб для обучающихся	47,46	
114	Гардероб для обучающихся	149,42	
115	Цех вторичной обработки овощей	15,98	В3
116	Цех первичной обработки овощей	10,34	В3
117	Сан. узел для персонала	1,99	
119	Коридор	29,34	
119а	Тамбур	4,70	
120	Моечная обратной тары	4,78	В4
121	Лестничная клетка (для персонала)	10,41	
122	Загрузочный цех	11,28	В3
123	Мясо-рыбный цех	18,28	В3
124	Моечная кухонной посуды	11,29	В3
125	ПУИ	5,53	
126	Помещение временного хранения пищевых отходов	9,37	В4
127	Моечная столовой посуды	46,82	В4
128	Горячий цех	45,30	В3
129	Холодный цех	10,12	В3
130	Обеденный зал	393,12	
131	Лестничная клетка (тип Н2)	17,68	
133	Сан. узел для мальчиков	8,29	
134	Сан. узел для девочек	7,82	
135	Коридор	83,12	
137	Коридор	146,67	
138	Коридор	142,66	
139	Лестничная клетка (тип Л1)	17,22	
140	Административный кабинет Тип 1	15,42	
141	Учебный кабинет	57,61	
142	Сан. узел для девочек	14,13	
143	Сан. узел для мальчиков	16,91	
144	ПУИ	3,09	В4
145	Лестничная клетка (тип Л1)	17,14	
146	Гимнастический зал	93,81	
147	Раздевальные	8,17	
148	Раздевальные	7,30	
150	Кабинет для индивидуальных занятий, в т.ч. с коррекционным педагогом	21,01	
151	Помещение для прокладки инженерных коммуникаций	15,07	В3
152	Учебный кабинет	53,08	
153	Учебный кабинет	54,85	
154	Учебный кабинет	54,31	
155	Учебные кабинет для изучения естествознания: химия	55,07	
156	Лаборанская кабинета химии	17,09	В3
157	Учебные кабинет для изучения естествознания: физика	54,43	
158	Лаборанская кабинета физики	18,10	В3
159	Учебные кабинеты для изучения естествознания: биологии + ОБЗР	71,91	
160	Лаборанская кабинета биологии	18,75	В3
161	Кабинет материальной технологии Тип 2	49,10	В3
162	Кабинет материальной технологии Тип 1	54,82	В3
163	Лестничная клетка (тип Л1)	17,22	
164	Сан. узел персонала	1,78	
165	Сан. узел для мальчиков	16,02	
166	Сан. узел для девочек с комнатой личной гигиены	14,73	
167	Серверная	17,09	В3
168	Кроссовая	5,03	В3
169	Кроссовая	4,92	В3
		2 558,98 м²	

Условные обозначения:

- Керамогранит крупноформатный Размер: 1195х600х9мм Производитель: Kerama Marazzi Фондаменто Пепельный светлый обрезной Артикул: DL600720R
- Керамогранит крупноформатный 600х600х9мм Производитель: Kerama Marazzi Фонаменто Пепельный светлый обрезной Артикул: DL600720R
- Керамогранит крупноформатный Размер: 600х600х9мм Производитель: Kerama Marazzi Фондаменто Пепельный светлый обрезной Артикул: DL600920R
- Керамогранит крупноформатный Размер: 1200х600х9мм Производитель: Kerama Marazzi Артикул: DL500720R, DL500820R, DL501020R
- Керамогранит крупноформатный Размер: 600х600х9мм Производитель: Kerama Marazzi Артикул: DD600320R
- Керамогранит крупноформатный 600х600х9мм Производитель: Kerama Marazzi Артикул: DD641020R
- ступень завальцованная с противоскользящей насечкой 600х300х9мм Производитель: Kerama Marazzi Артикул: DD205320R
- линолеум, толщ. 2 мм Производитель: Forbo Артикул: 6361SB*
- текстильное коммерческое напольное флокированное покрытие Forbo Flotex в планках (артикулы 151001 (black wood), 151002 (grey wood), 151003 (silver wood); характеристики: размеры 100х25 см
- дизайн-плитка ПВХ 500х500х2,55мм Производитель: Forbo Артикул: 8121 Slit Imprint Concrete PRO, 8066 Slit Concrete PRO, 8065 T Dark Concrete PRO
- дизайн-плитка ПВХ 500х500х2,55мм Производитель: Forbo Артикул: 8061 T Natural Concrete PRO
- дизайн-плитка ПВХ 500х500х2,55мм Производитель: Forbo Артикул: 8043 White Fine Oak PRO
- спортивный паркет 1800х300х20мм Производитель: Krast School Артикул: KS57
- дизайн-плитка ПВХ 500х500х2,55мм Производитель: Forbo Артикул: 8121 Slit Imprint Concrete PRO, 8066 Slit Concrete PRO, 8065 T Dark Concrete PRO

0,000=168,265

Изм.	Колуч.	Лист	№Док.	Подп.	Дата
Разработал	Белова Е.С.				09.25
Проверил	Дубинин С.В.				09.25
ГАП	Дубинин С.В.				09.25
ГИП	Гущин А.В.				
Н.контроль	Шукшин В.В.				09.25

ГИП-28/24-П-АР

ГБОУ Школа № 218, расположенная по адресу: г. Москва, ул. Вучетича, д. 6

Средняя общеобразовательная школа

Стадия	Лист	Листов
П	23	64

План полов 1 этажа на отм. 0,000

И-ГРУПП
ПРОЕКТНО-СТРОИТЕЛЬНАЯ КОМПАНИЯ

План полов 2 этажа на отм. +3.300
М 1:200

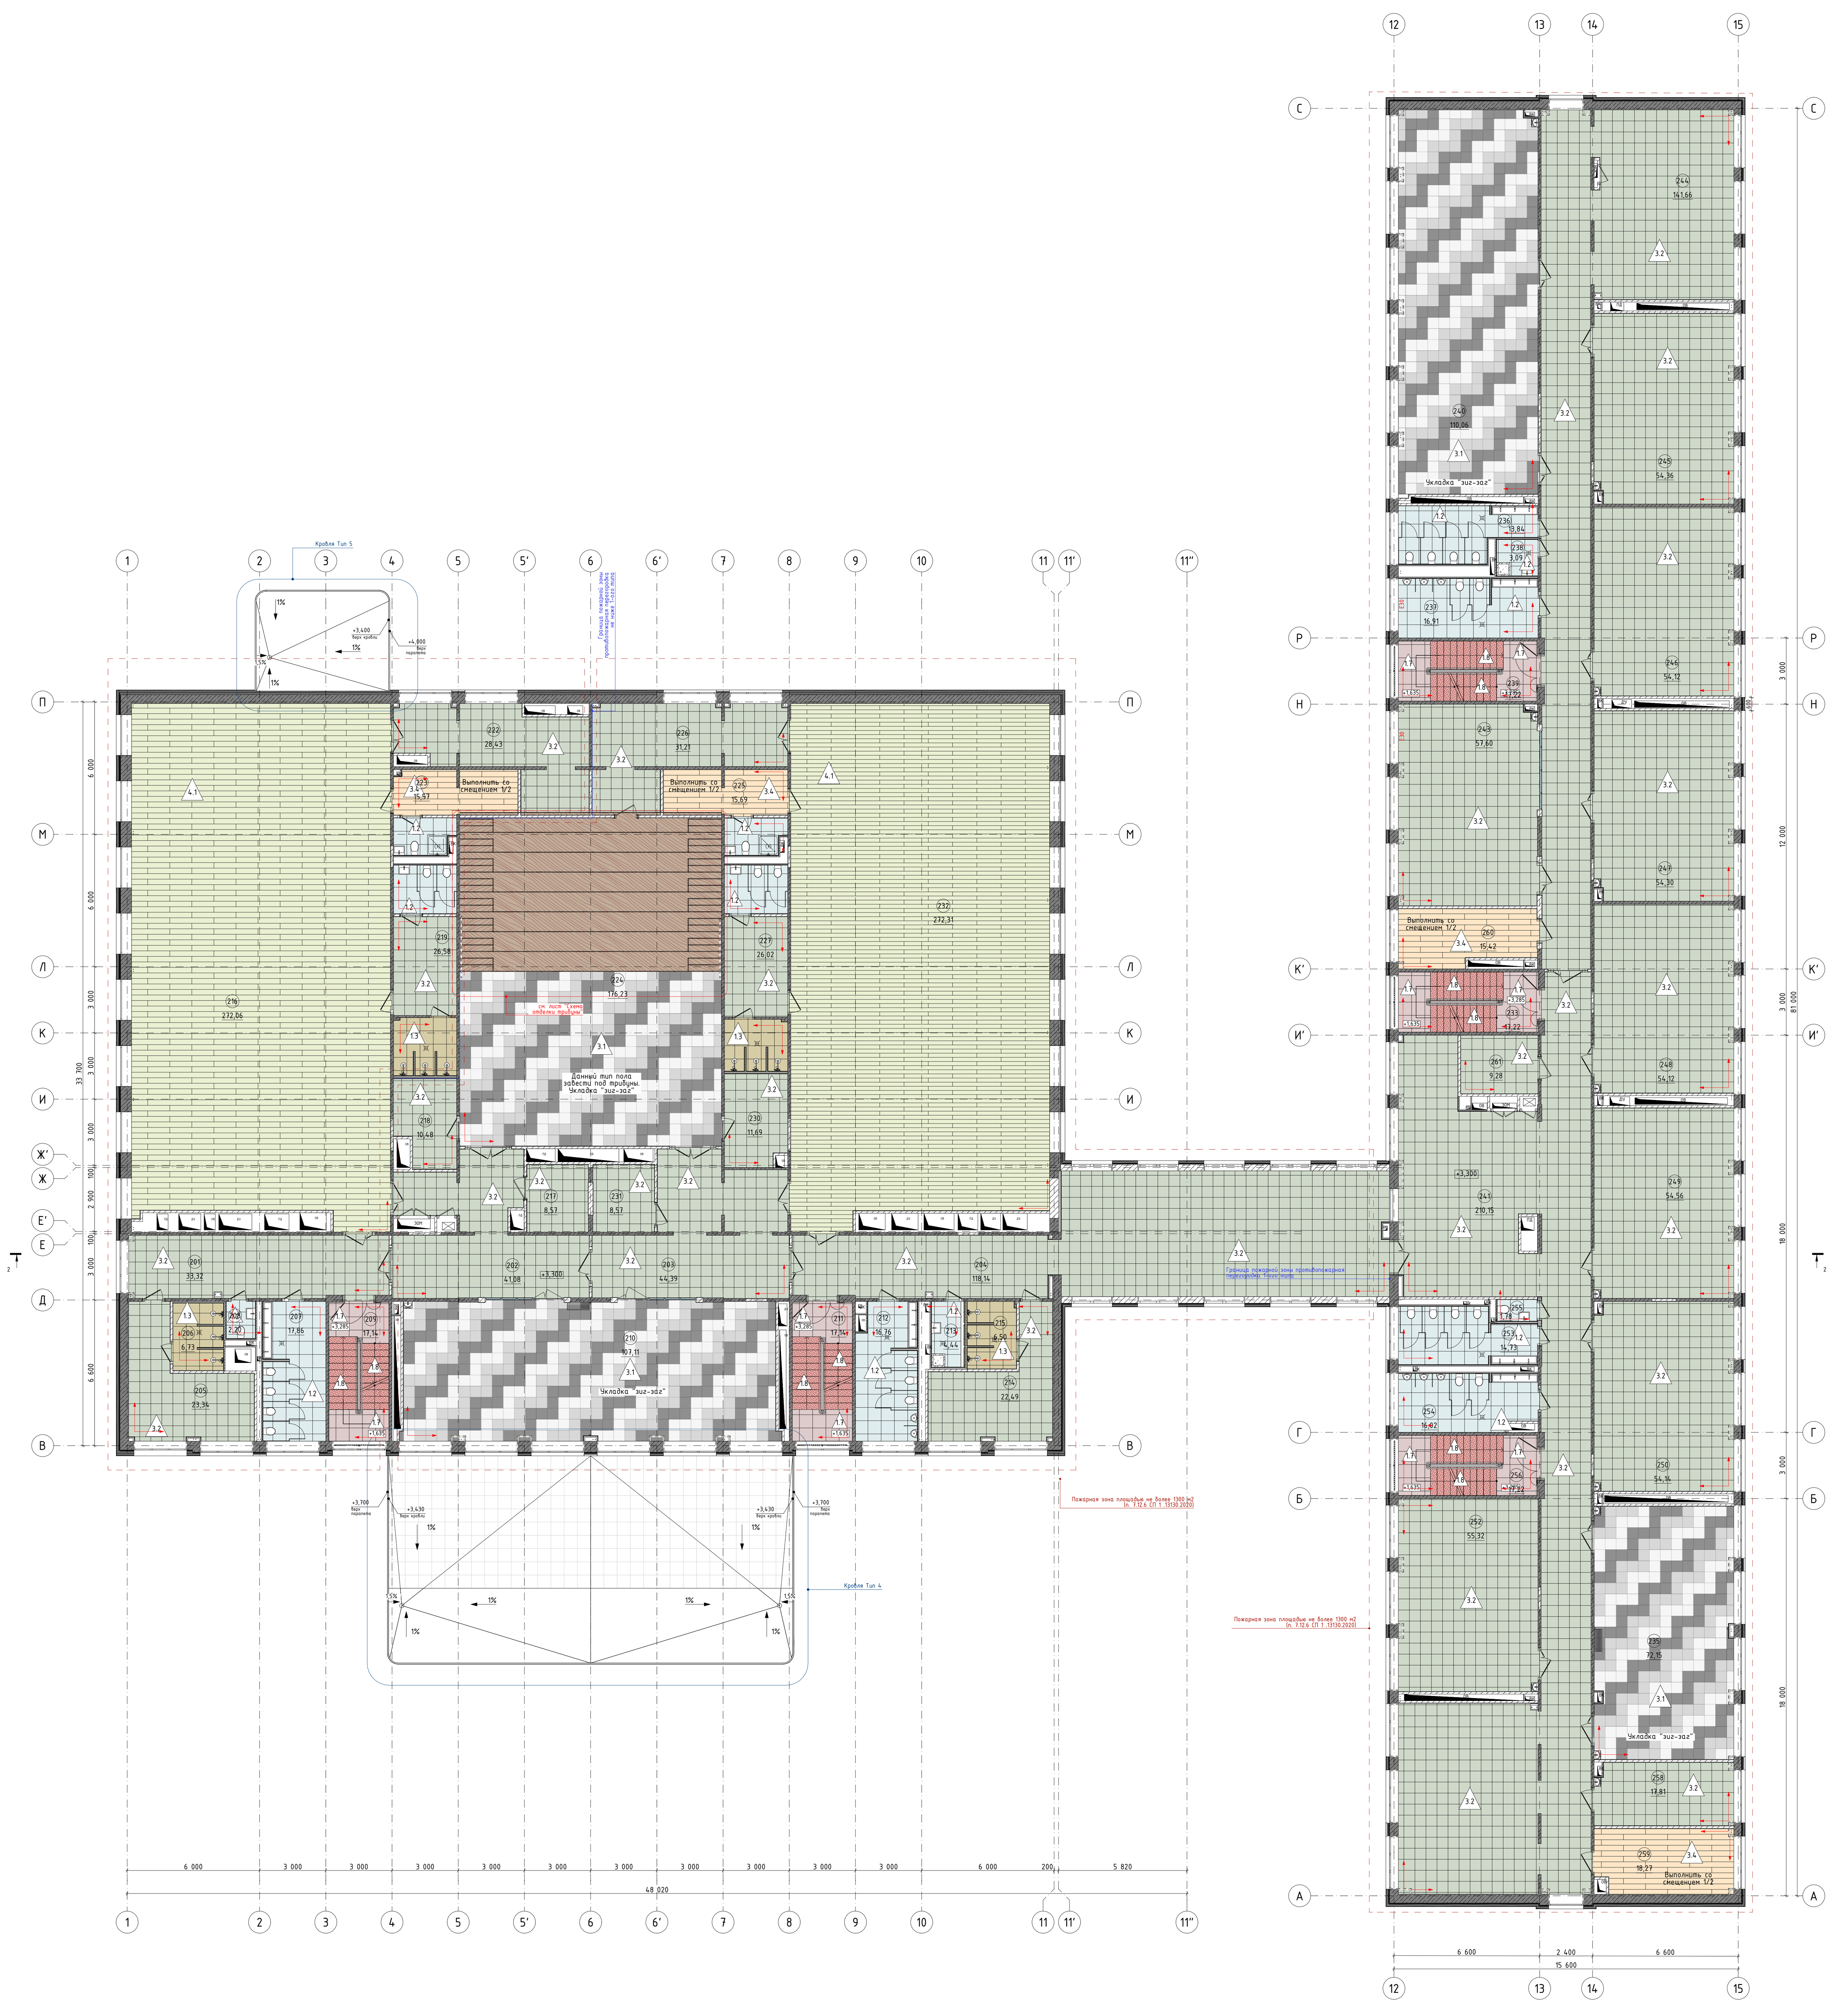

Экпликация помещений на отм. 3.300

№	Наименование	Площадь	Категория помещения
201	Коридор	33,32	
202	Коридор	41,08	
203	Коридор	44,39	
204	Коридор	118,14	
205	Раздевальная	23,34	
206	Душевая	6,73	
207	Сан. узел для девочек	17,86	
208	Сан. узел для персонала	2,20	
209	Лестничная клетка (тип Н2)	17,14	
210	Кабинет ИЗО	107,11	
211	Лестничная клетка (тип Н2)	17,14	
212	Сан. узел для мальчиков	16,76	
213	ПУИ	4,44	В4
214	Раздевальная	22,49	
215	Душевая	6,50	
216	Универсальный спортивный зал	272,06	
217	Кроссовая	8,57	В3
218	Артистическая с хранением костюмов	10,48	В3
219	Раздевальная	26,58	
222	Снарядная	28,43	В3
223	Комната инструктора с душем и сан. узлом	15,57	
224	Актовый зал	176,23	
225	Комната инструктора с душем и сан. узлом	15,69	
226	Снарядная	31,21	В3
227	Раздевальная	26,02	
230	Артистическая с хранением костюмов	11,69	В3
231	Кладовая инвентаря	8,57	В4
232	Универсальный спортивный зал	272,31	
233	Лестничная клетка (тип Л1)	17,22	
235	Кабинет иностранного языка	72,15	
236	Сан. узел для девочек	13,84	
237	Сан. узел для мальчиков	16,91	
238	ПУИ	3,09	В4
239	Лестничная клетка (тип Л1)	17,22	
240	Кабинет естесствознания Тип 1	110,06	
241	Коридор	210,15	
243	Учебный кабинет	57,60	
244	Коридор	141,66	
245	Учебный кабинет	54,36	
246	Учебный кабинет	54,12	
247	Учебный кабинет	54,30	
248	Учебный кабинет	54,12	
249	Учебный кабинет	54,56	
250	Учебный кабинет	54,14	
252	Учебный кабинет	55,32	
253	Сан. узел для девочек	14,73	
254	Сан. узел для мальчиков	16,02	
255	Сан. узел для персонала	1,78	
256	Лестничная клетка (тип Л1)	17,22	
258	Кабинет для индивидуальных занятий, в т.ч. с учителем логопедом	17,81	
259	Административный кабинет Тип 1	18,27	
260	Административный кабинет Тип 1	15,42	
261	Кроссовая	9,28	В3
		2 533,40 м²	

Условные обозначения:

- 1.2 – Керамогранит крупноформатный 600х600х9мм Производитель: Kerama Marazzi Фонаменто Пепельный светлый обрезной Артикул: DL600720R
- 1.3 – Керамогранит крупноформатный Размер: 600х600х9мм Производитель: Kerama Marazzi Артикул: DD600320R
- 1.7 – Керамогранит крупноформатный 600х600х9мм Производитель: Kerama Marazzi Артикул: DD641020R
- 1.8 – ступень завальцованная с противоскользящей насечкой 600х300х9мм Производитель: Kerama Marazzi Артикул: DD205320R
- 3.1 – дизайн-плитка ПВХ 500х500х2,55мм Производитель: Forbo Артикул: 8121 Slit Imprint Concrete PRO, 8066 Slit Concrete PRO, 8065 T Dark Concrete PRO
- 3.2/3.3 – дизайн-плитка ПВХ 500х500х2,55мм Производитель: Forbo Артикул: 8061 T Natural Concrete PRO
- 3.4 – дизайн-плитка ПВХ 500х500х2,55мм Производитель: Forbo Артикул: 8043 White Fine Oak PRO
- 4.1 – спортивный паркет 1800х300х20мм Производитель: Krast School Артикул: KS57
- 6.1 – Фанера березовая трудногорючая

0,000=168,265

Изм.	Кол.уч.	Лист	№Док.	Подп.	Дата
Разработал		Белова Е.С.			09.25
Проверил		Дубинин С.В.			09.25
ГАП		Дубинин С.В.			09.25
ГИП		Гущин А.В.			
Н.контроль		Шукшин В.В.			09.25

ГИП-28/24-П-АР

ГБОУ Школа № 218, расположенная по адресу: г. Москва, ул. Вучетича, д. 6

Средняя общеобразовательная школа

Стадия	Лист	Листов
П	24	64

План полов 2 этажа на отм. +3.300

И-ГРУПП ПРОЕКТНО-СТРОИТЕЛЬНАЯ КОМПАНИЯ

План полов 3 этажа на отм. +6.600
М 1:200

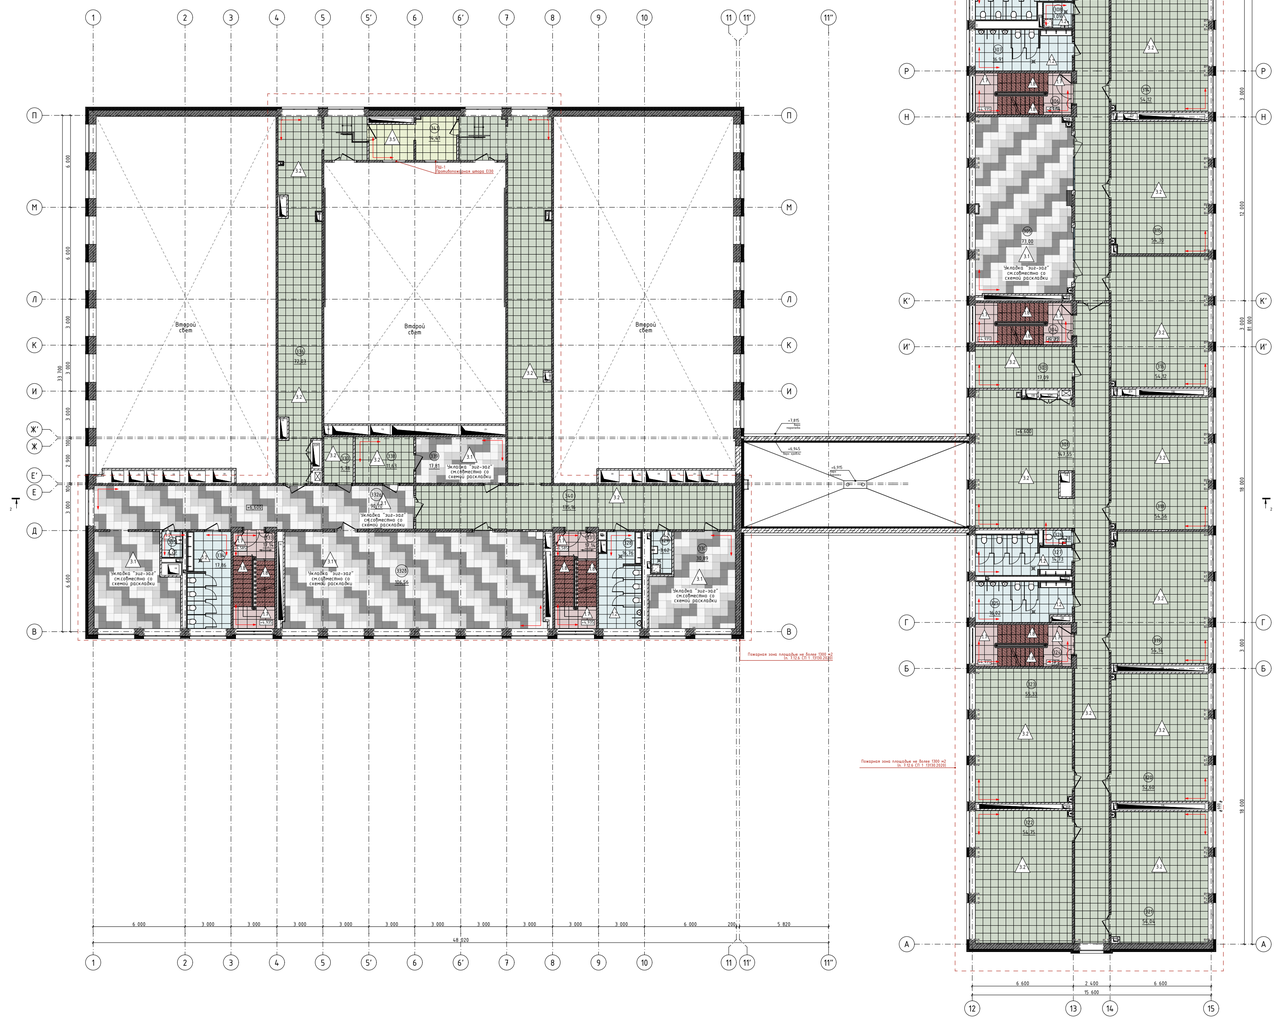

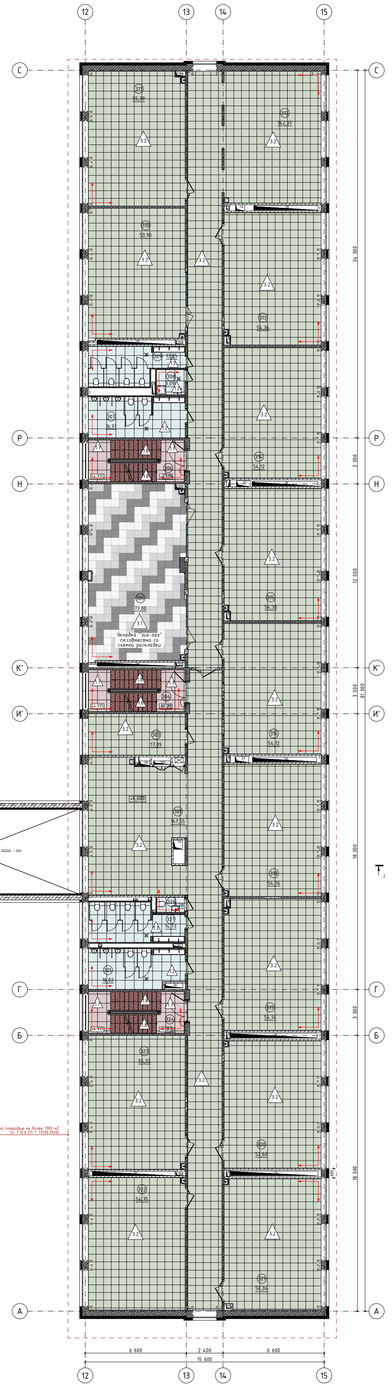

Экспликация помещений на отм. 6.600

№	Наименование	Площадь	Категория помещения
301	Коридор	147,55	
303	Серверная	17,09	В3
304	Лестничная клетка (тип Л1)	17,22	
305	Кабинет иностранного языка	73,00	
306	Лестничная клетка (тип Л1)	17,14	
307	Сан. узел для мальчиков	16,91	
308	ПУИ	3,09	В4
309	Сан. узел для девочек	13,85	
310	Учебный кабинет	53,90	
311	Учебный кабинет	55,39	
312	Коридор	142,37	
313	Учебный кабинет	54,36	
314	Учебный кабинет	54,12	
315	Учебный кабинет	54,30	
316	Учебный кабинет	54,12	
318	Учебный кабинет	54,56	
319	Учебный кабинет	54,14	
320	Учебный кабинет	52,60	
321	Учебный кабинет	54,04	
322	Учебный кабинет	54,75	
323	Учебный кабинет	55,33	
324	Лестничная клетка (тип Л1)	17,22	
325	Сан. узел для мальчиков	16,02	
326	Сан. узел персонала	1,78	
327	Сан. узел для девочек	14,73	
328	Сан. узел для мальчиков	16,76	
329	ПУИ	3,62	В4
330	Библиотека. Фонд хранения	30,89	В3
331	Лестничная клетка (тип Н2)	17,14	
332а	Коридор	90,70	
332б	Читальный зал	106,56	
333	Лестничная клетка (тип Н2)	17,14	
334	Сан. узел для девочек	17,86	
335	Сан. узел для персонала	2,20	
336	Коридор	72,03	
337	Кроссовая	5,78	В3
338	Кабинет для индивидуальных занятий. Студия звукозаписи	11,63	
339	Медиакласс	17,81	
340	Коридор	135,16	
341	Технический центр	14,41	В3
		1 709,27 м²	

Условные обозначения:

- Керамогранит крупноформатный 600x600x9мм Производитель: Kerama Marazzi Фонтанелла Пепельный светлый обрезной Артикул: DL600720R
- Керамогранит крупноформатный 600x600x9мм Производитель: Kerama Marazzi Артикул: DD641020R
- ступень завальцованная с противоскользящей насечкой 600x300x9мм Производитель: Kerama Marazzi Артикул: DD205320R
- дизайн-плитка ПВХ 500x500x2,55мм Производитель: Forbo Артикул: 8121 Slit Imprint Concrete PRO, 8066 Slit Concrete PRO, 8065 T Dark Concrete PRO
- дизайн-плитка ПВХ 500x500x2,55мм Производитель: Forbo Артикул: 8061 T Natural Concrete PRO
- дизайн-плитка ПВХ 500x500x2,55мм Производитель: Forbo Артикул: 8061 T Natural Concrete PRO

0,000=168,265

ГИП-28/24-П-АР

ГБОУ Школа № 218, расположенная по адресу:
г. Москва, ул. Вучетича, д. 6

Изм.	Колуч.	Лист	№Док.	Подп.	Дата
Разработал		Белова Е.С.			09.25
Проверил		Дубинин С.В.			09.25
ГАП		Дубинин С.В.			09.25
ГИП		Гущин А.В.			
Н.контроль		Шукшин В.В.			09.25

Средняя общеобразовательная школа

Стадия	Лист	Листов
П	25	64

План полов 3 этажа на отм. +6.600

И-ГРУПП
ПРОЕКТНО-СТРОИТЕЛЬНАЯ КОМПАНИЯ

План полов 4 этажа на отм. +9.900
М 1:200

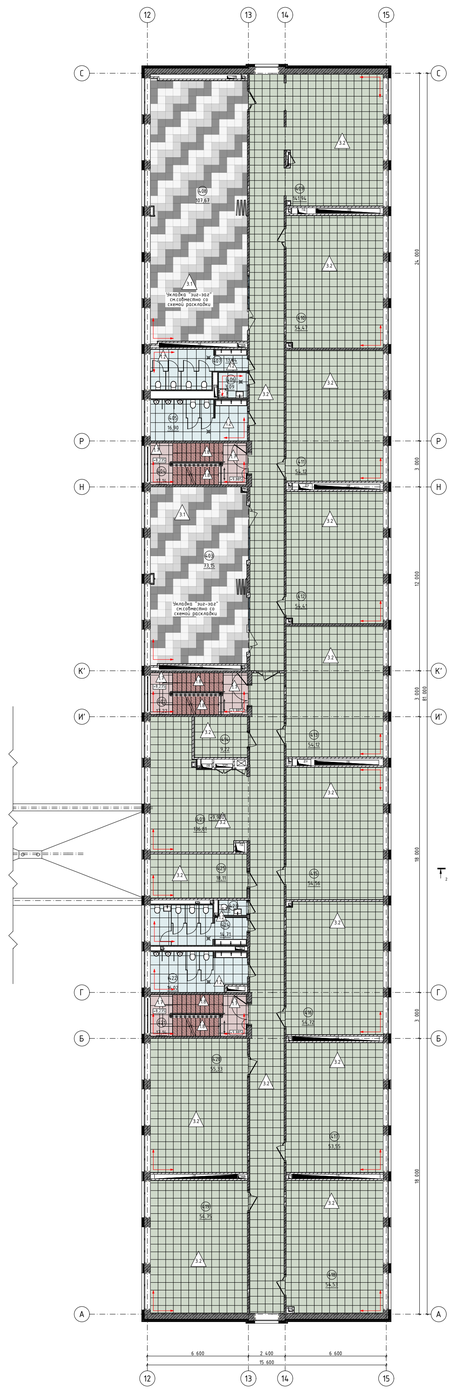

Экспликация помещений на отм. 9.900

№	Наименование	Площадь	Категория помещения
401	Коридор	136,81	
402	Лестничная клетка (тип Л1)	17,22	
403	Кабинет иностранного языка	73,15	
404	Лестничная клетка (тип Л1)	17,14	
405	Сан. узел для мальчиков	16,90	
406	ПУИ	3,09	В4
407	Сан. узел для девочек	13,84	
408	Кабинет информатики и информационных технологий	107,67	
409	Коридор	141,94	
410	Кабинет русского языка и литературы	54,47	
411	Кабинет русского языка и литературы	54,12	
412	Кабинет русского языка и литературы	54,41	
413	Кабинет математики	54,12	
414	Кроссовая	9,22	В3
415	Кабинет математики	54,56	
416	Кабинет истории Тип 1	54,72	
417	Кабинет географии	53,55	
418	Универсальный учебный кабинет	54,53	
419	Кабинет математики	54,75	
420	Кабинет истории Тип 1	55,33	
421	Лестничная клетка (тип Л1)	17,14	
422	Сан. узел для мальчиков	16,02	
423	Сан. узел персонала	1,78	
424	Сан. узел для девочек с комнатой личной гигиены	14,71	
425	Кабинет для индивидуальных занятий, в т.ч. с педагогом психологом	18,11	
		1 149,30 м²	

Условные обозначения:

1.2 – Керамогранит крупноформатный 600x600x9мм Производитель: Kerama Marazzi Фонамента Пепельный светлый обрезной Артикул: DL600720R

1.7 – Керамогранит крупноформатный 600x600x9мм Производитель: Kerama Marazzi Артикул: DD641020R

1.8 – ступень забальцованная с противоскользящей насечкой 600x300x9мм Производитель: Kerama Marazzi Артикул: DD205320R

3.3 – дизайн-плитка ПВХ 500x500x2,55мм Производитель: Forbo Артикул: 8121 Slit Imprint Concrete PRO, 8066 Slit Concrete PRO, 8065 T Dark Concrete PRO

2.2 3.3 – дизайн-плитка ПВХ 500x500x2,55мм Производитель: Forbo Артикул: 8061 T Natural Concrete PRO

0,000=168,265

						ГИП-28/24-П-АР	
						ГБОУ Школа № 218, расположенная по адресу: г. Москва, ул. Вучетича, д. 6	
Изм.	Колуч.	Лист	№Док.	Подп.	Дата		
Разработал		Белова Е.С.			09.25	Средняя общеобразовательная школа	Стадия: П; Лист: 26; Листов: 64
Проверил		Дубинин С.В.			09.25		
ГАП		Дубинин С.В.			09.25		
ГИП		Гущин А.В.				План полов 4 этажа на отм. +9.900	И-ГРУПП ПРОЕКТНО-СТРОИТЕЛЬНАЯ КОМПАНИЯ
Н.контроль		Шукшин В.В.			09.25		

План полов выходов на кровлю
М 1:200

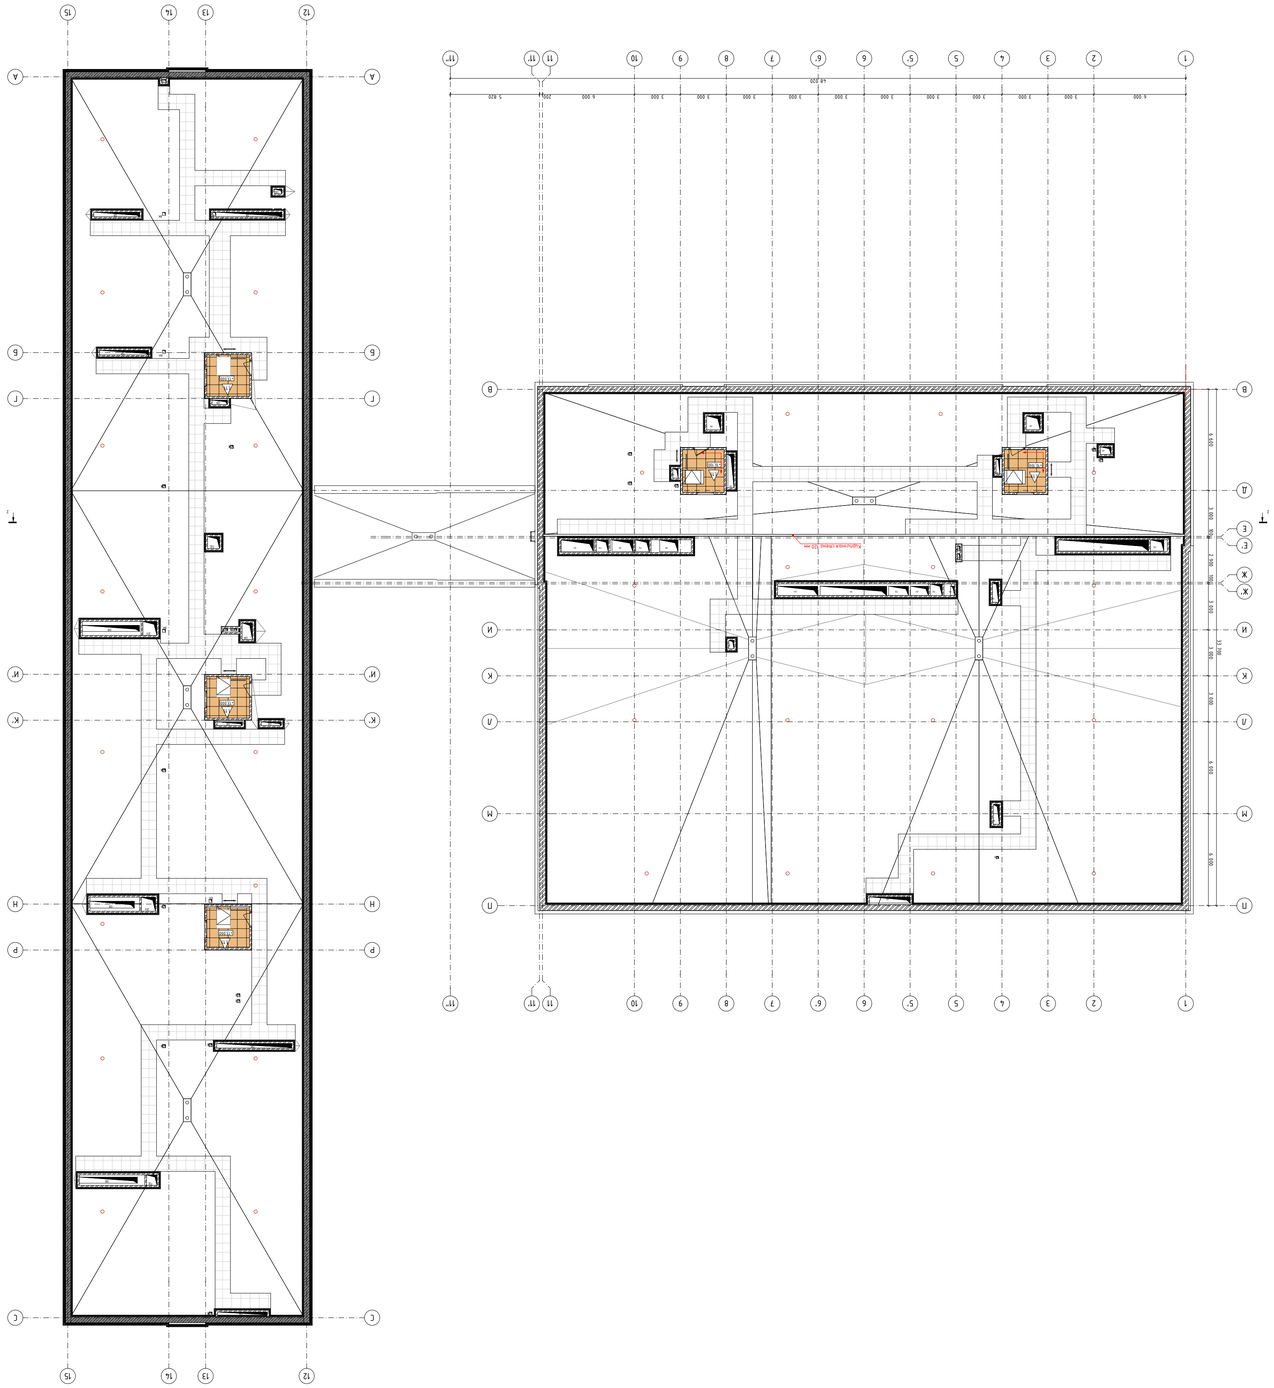

						ГИП-28/24-П-АР
Изм.	Кол.уч.	Лист	№док.	Подп.	Дата	ГБОУ Школа №218, расположенная по адресу: г. Москва, ул. Вучетича, д. 6
Разработал		Белобов Е.С.			09.25	
Проверил		Дубинин С.В.			09.25	
ГАП		Дубинин С.В.			09.25	
ГИП		Гущин А.В.				
Н.контроль				Шухшин В.В.	09.25	

Стадия	Лист	Листов
П	28	

Средняя общеобразовательная школа

План демонтажа помолков подбалконого этажа

И-ГРУПП
ПРОЕКТНО-СТРОИТЕЛЬНАЯ КОМПАНИЯ

План демонтажа помолков подбалконого этажа

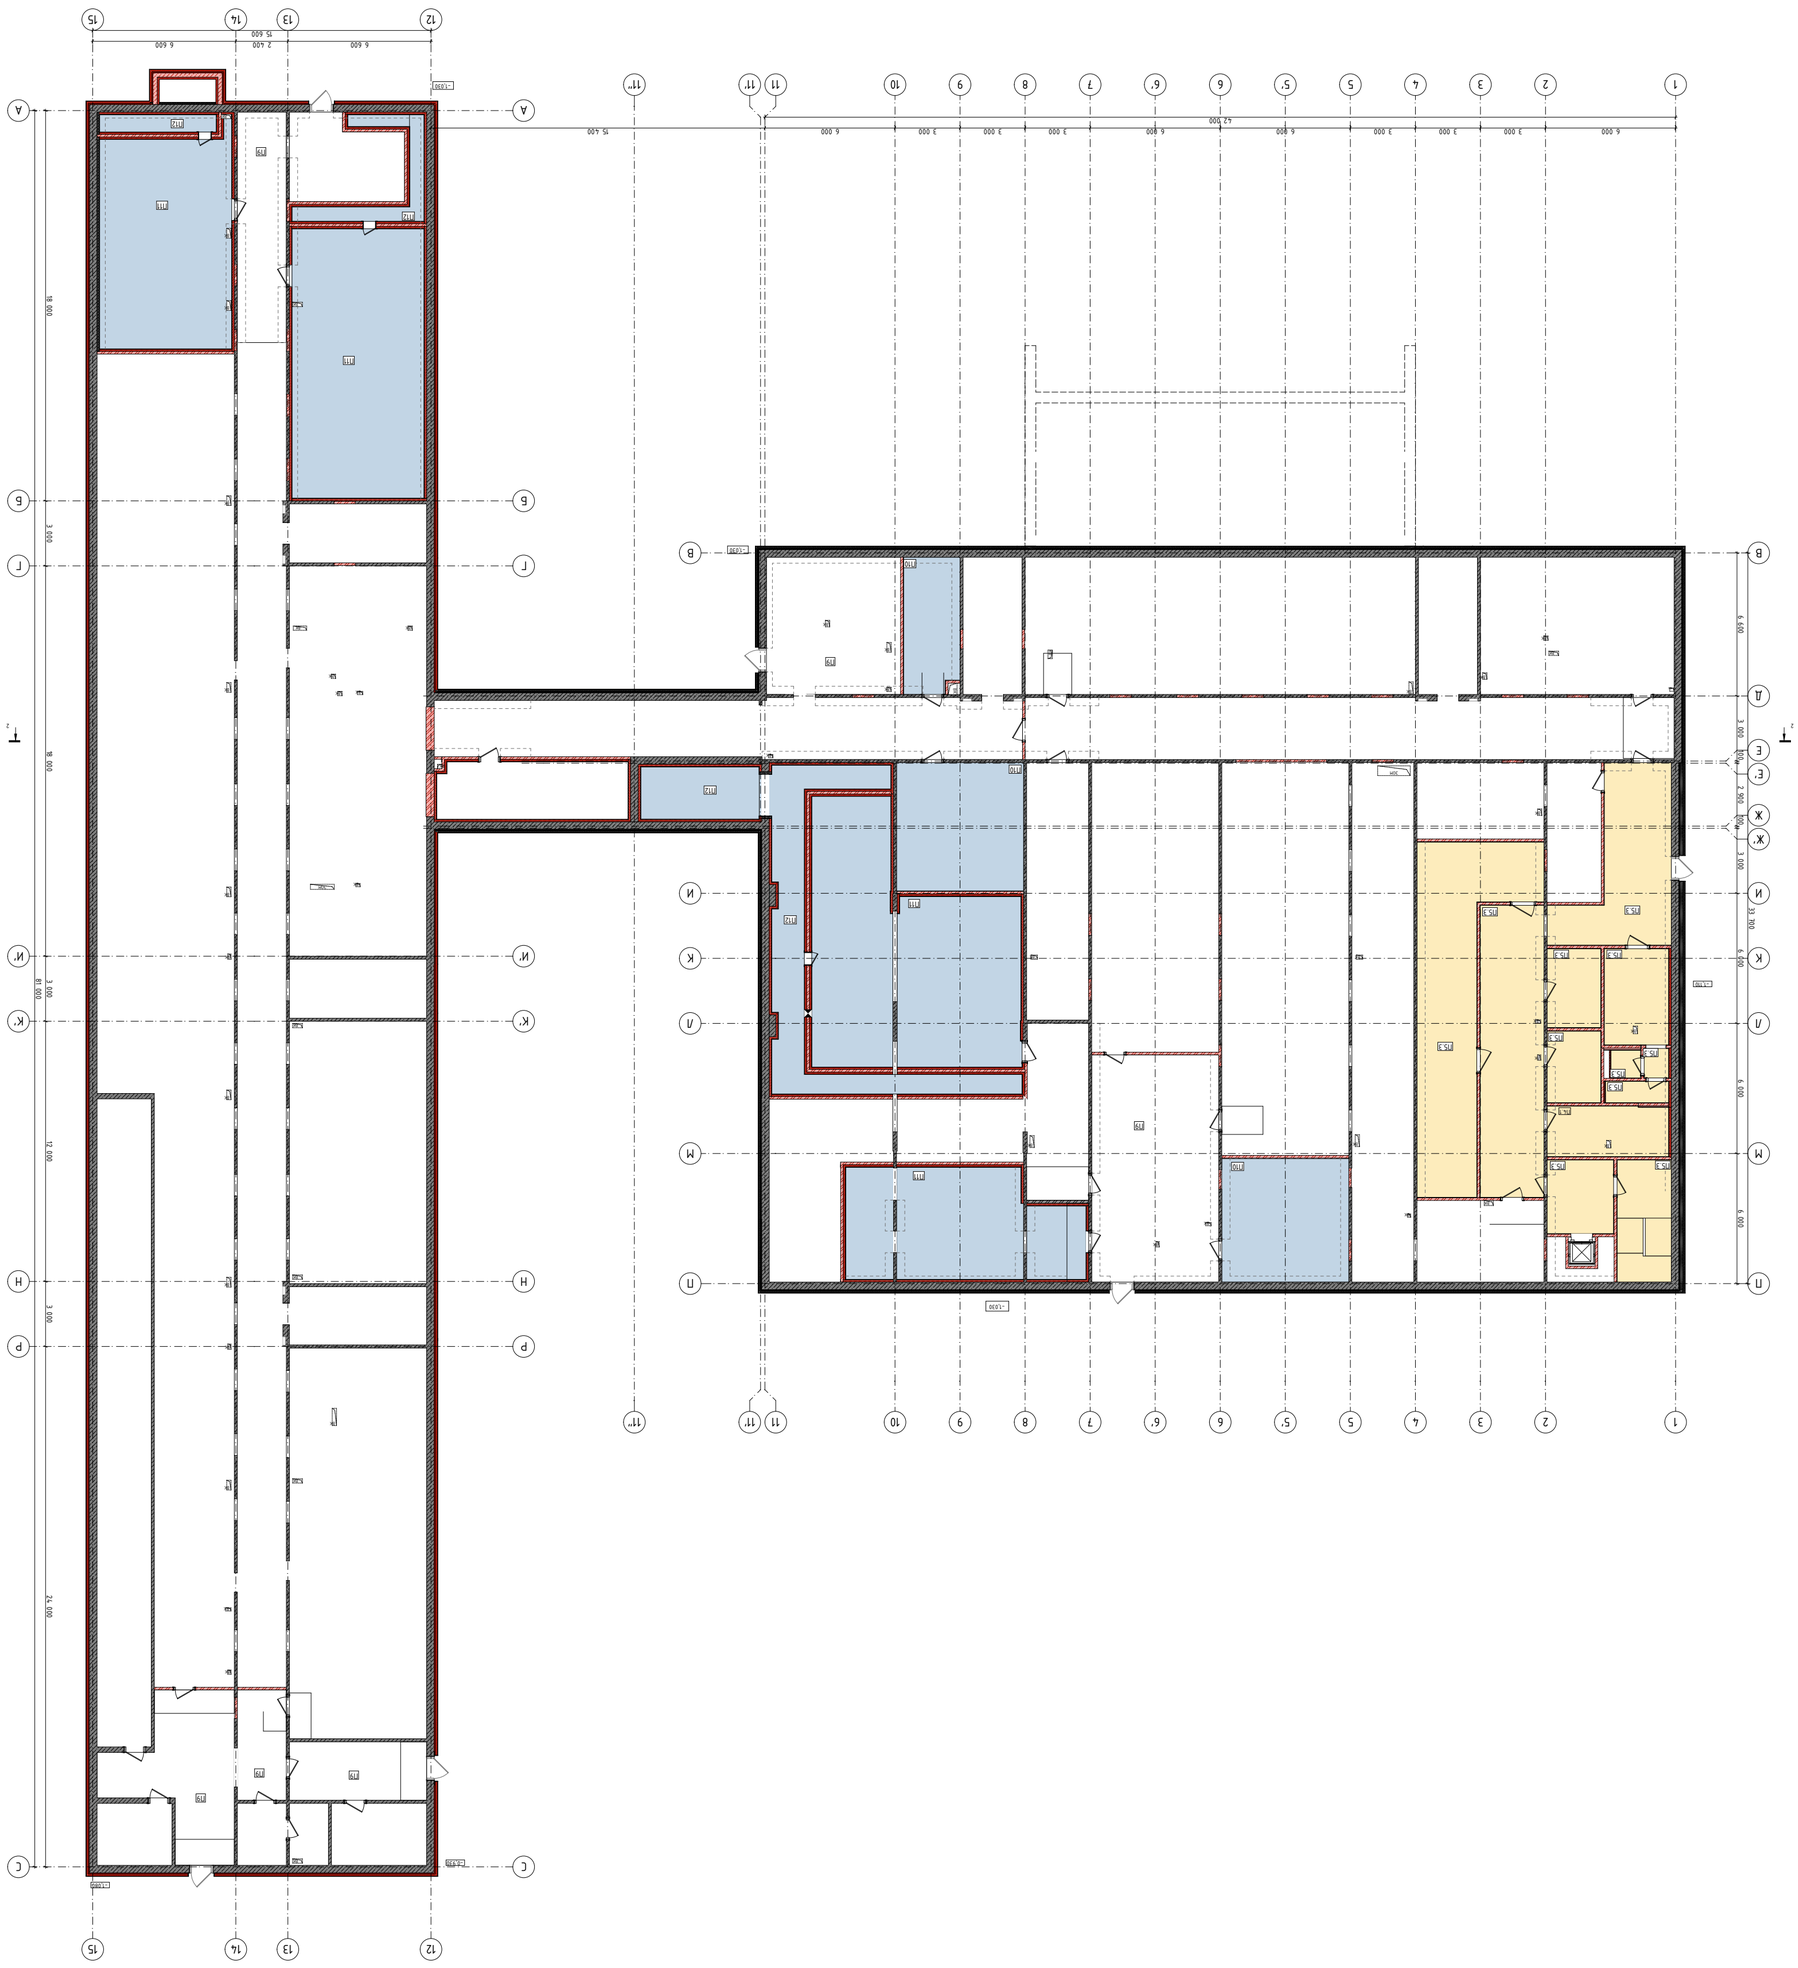

План демонтажа потолков 1 этажа

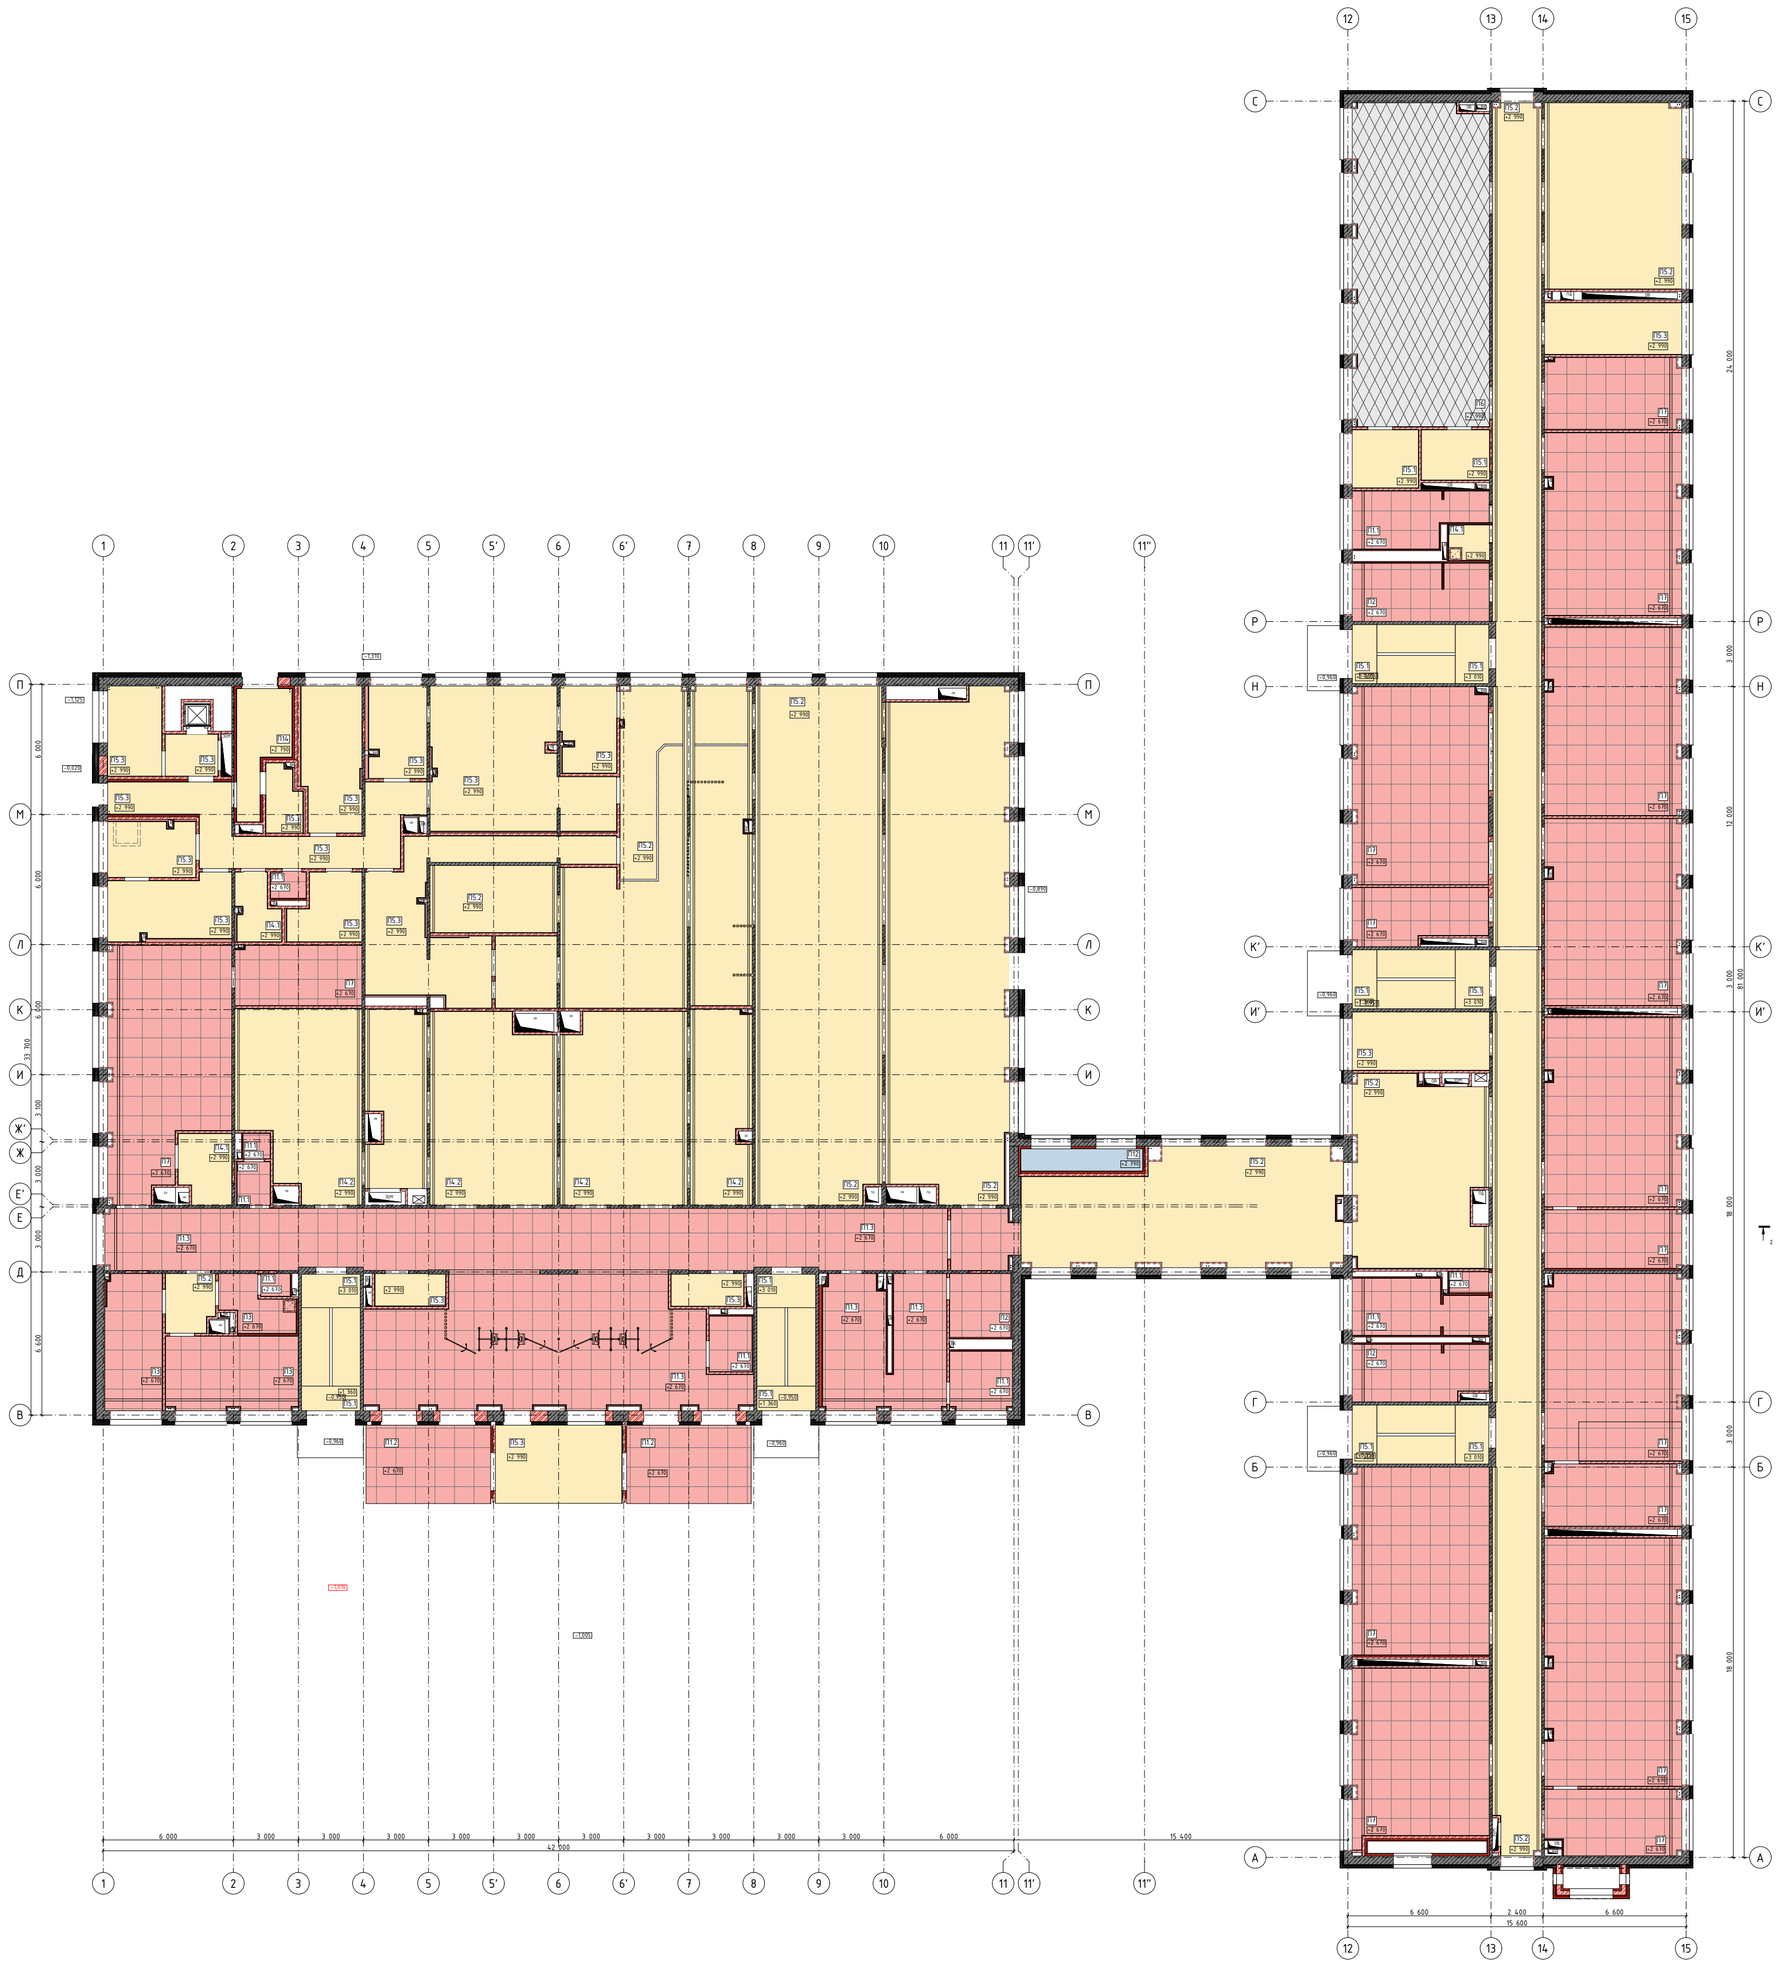

Условные обозначения

- минераловатный утеплитель+побелка
- покраска
- подвесной потолок
- покраска+сетка защитная

						ГИП-28/24-П-АР
						ГБОУ Школа № 218, расположенная по адресу: г. Москва, ул. Вучетича, д. 6
Изм.	Кол.уч.	Лист	№Док.	Подп.	Дата	
Разработал		Белова Е.С.			09.25	Средняя общеобразовательная школа
Проверил		Дубинин С.В.			09.25	
ГАП		Дубинин С.В.			09.25	
ГИП		Гущин А.В.				План демонтажа потолков 1 этажа
Н.контроль		Шукшин В.В.			09.25	

Стадия	Лист	Листов
П	29	

И-ГРУПП ПРОЕКТНО-СТРОИТЕЛЬНАЯ КОМПАНИЯ

План демонтажа потолков 2 этажа

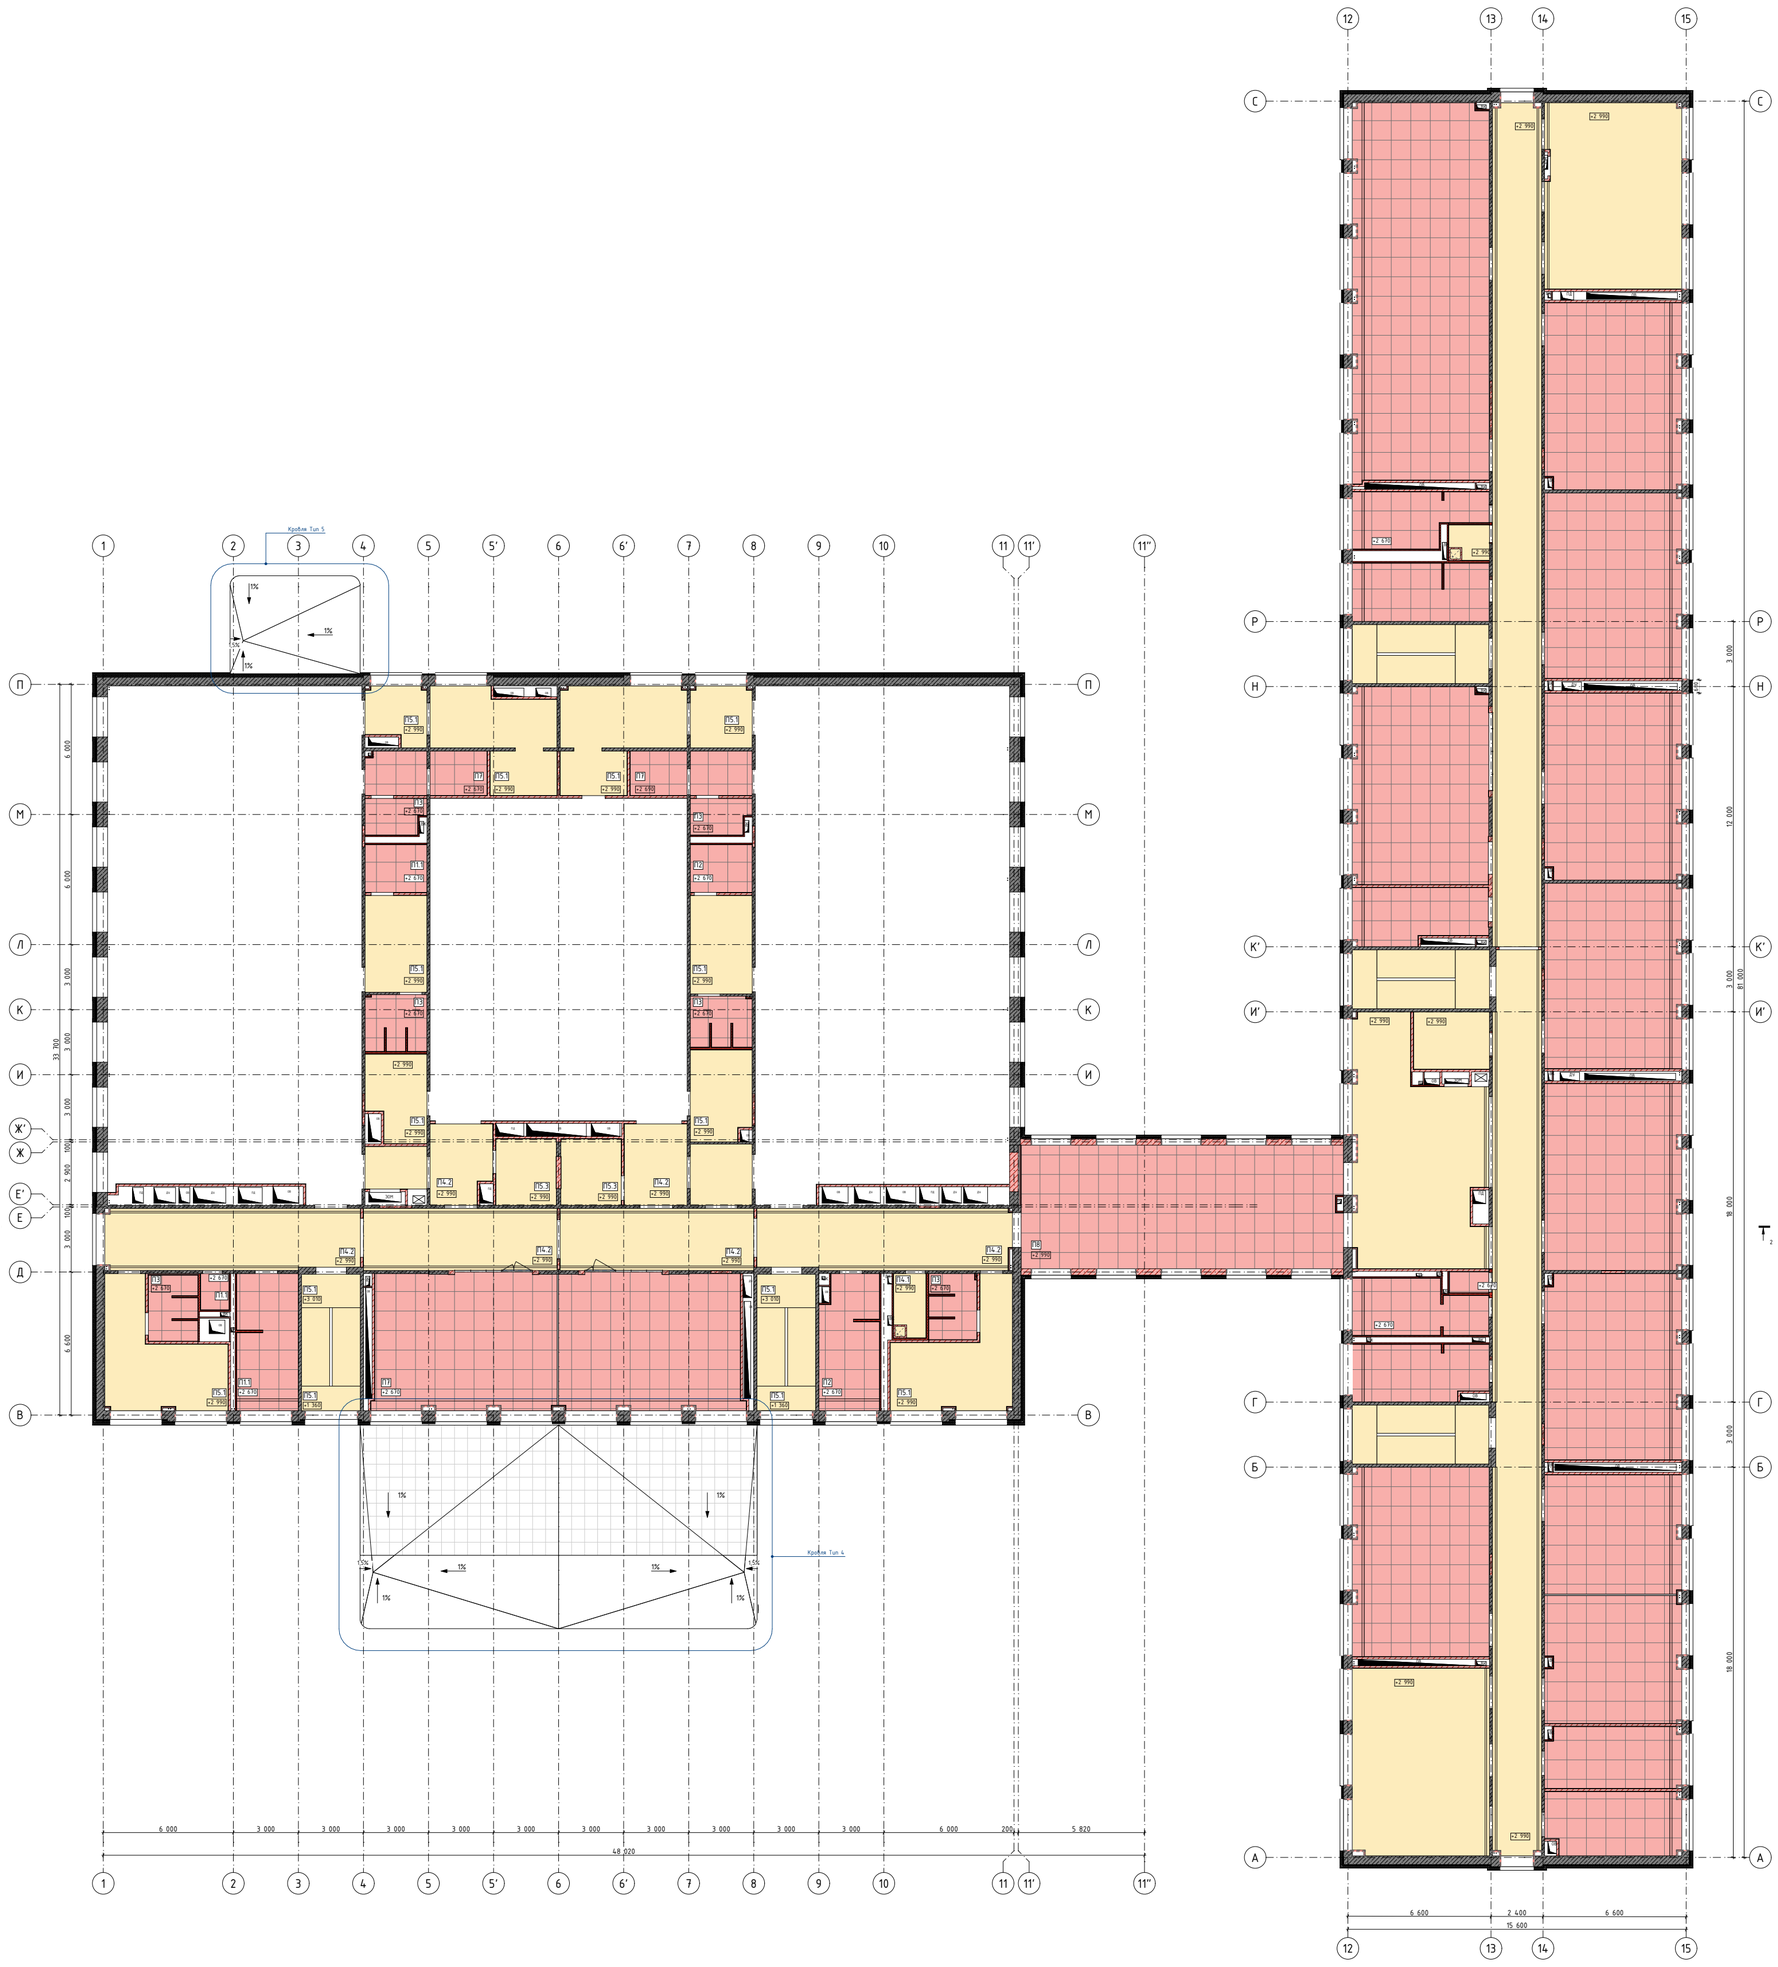

Условные обозначения

- минераловатный утеплитель+побелка
- покраска
- подвесной потолок
- покраска+сетка защитная

						ГИП-28/24-П-АР
						ГБОУ Школа № 218, расположенная по адресу: г. Москва, ул. Вучетича, д. 6
Изм.	Кол.уч.	Лист	№Док.	Подп.	Дата	
Разработал		Белова Е.С.			09.25	Средняя общеобразовательная школа
Проверил		Дубинин С.В.			09.25	
ГАП		Дубинин С.В.			09.25	
ГИП		Гущин А.В.				План демонтажа потолков 2 этажа
Н.контроль		Шукшин В.В.			09.25	

Стадия	Лист	Листов
П	30	

И-ГРУПП
ПРОЕКТНО-СТРОИТЕЛЬНАЯ КОМПАНИЯ

План демонтажа потолков 3 этажа

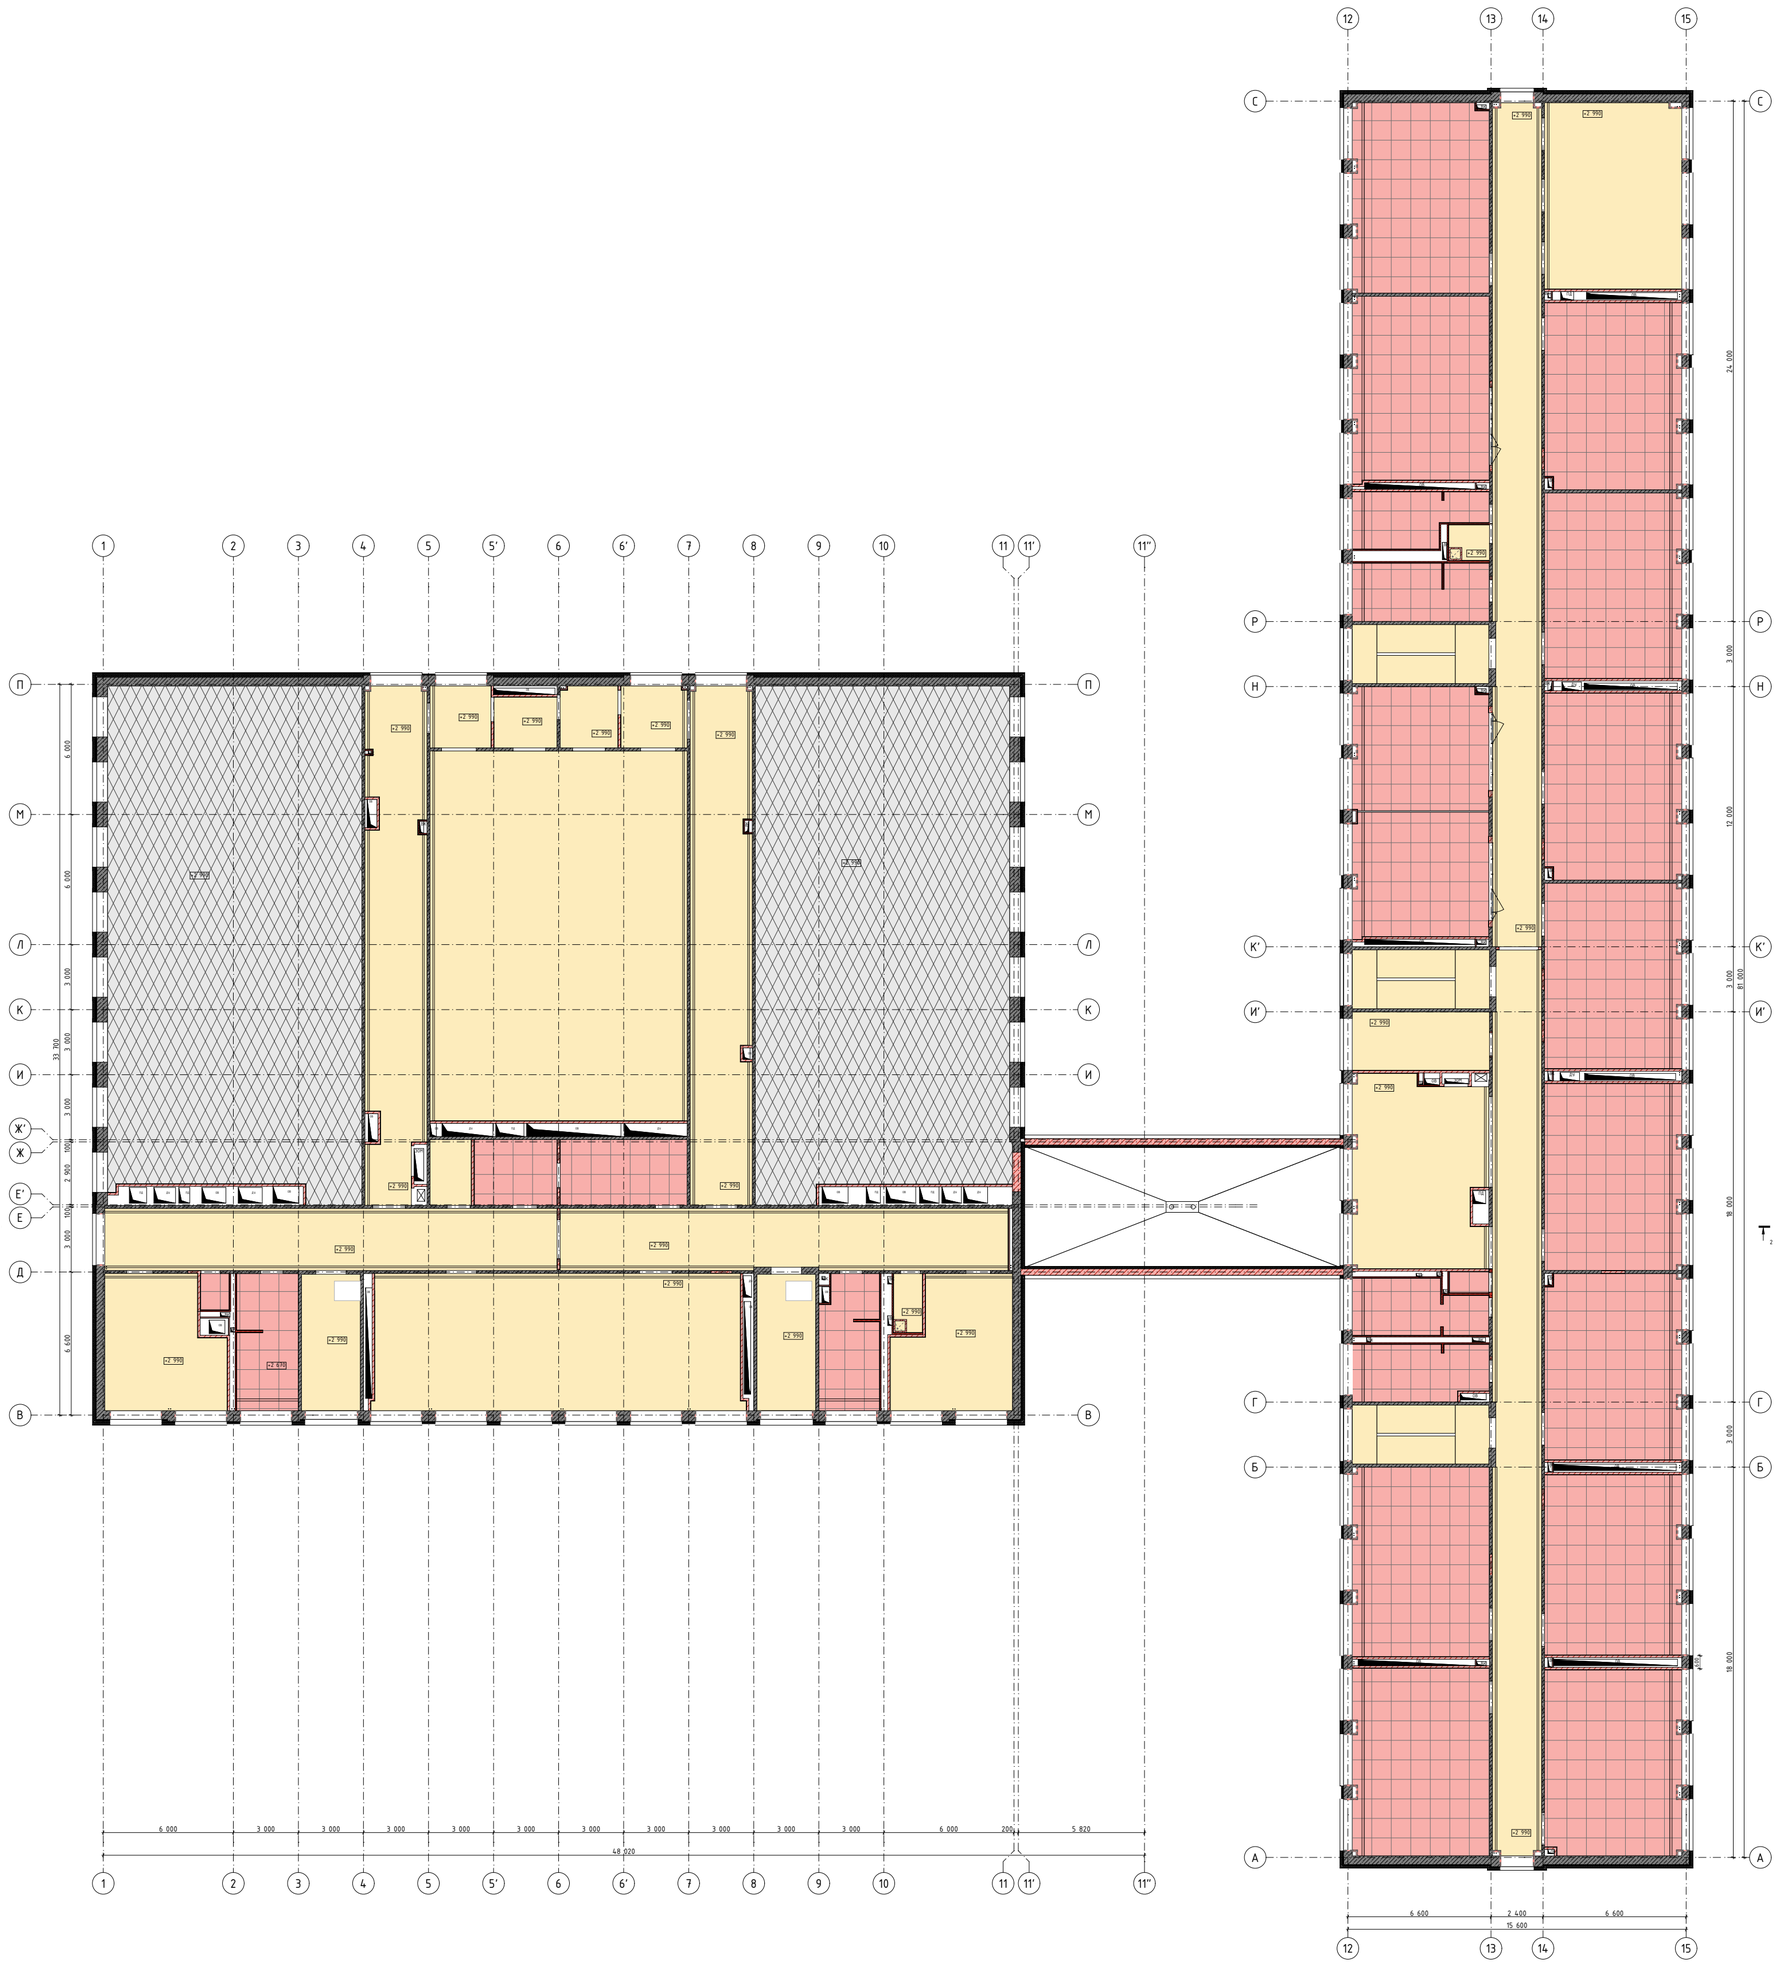

Условные обозначения

- минераловатный утеплитель+побелка
- покраска
- подвесной потолок
- покраска+сетка защитная

						ГИП-28/24-П-АР
						ГБОУ Школа № 218, расположенная по адресу: г. Москва, ул. Вучетича, д. 6
Изм.	Кол.уч.	Лист	№Док.	Подп.	Дата	
Разработал		Белова Е.С.			09.25	Средняя общеобразовательная школа
Проверил		Дубинин С.В.			09.25	
ГАП		Дубинин С.В.			09.25	
ГИП		Гущин А.В.				План демонтажа потолков 3 этажа
Н.контроль		Шукшин В.В.			09.25	

Стадия	Лист	Листов
П	31	

И-ГРУПП
ПРОЕКТНО-СТРОИТЕЛЬНАЯ КОМПАНИЯ

План демонтажа потолков 4 этажа

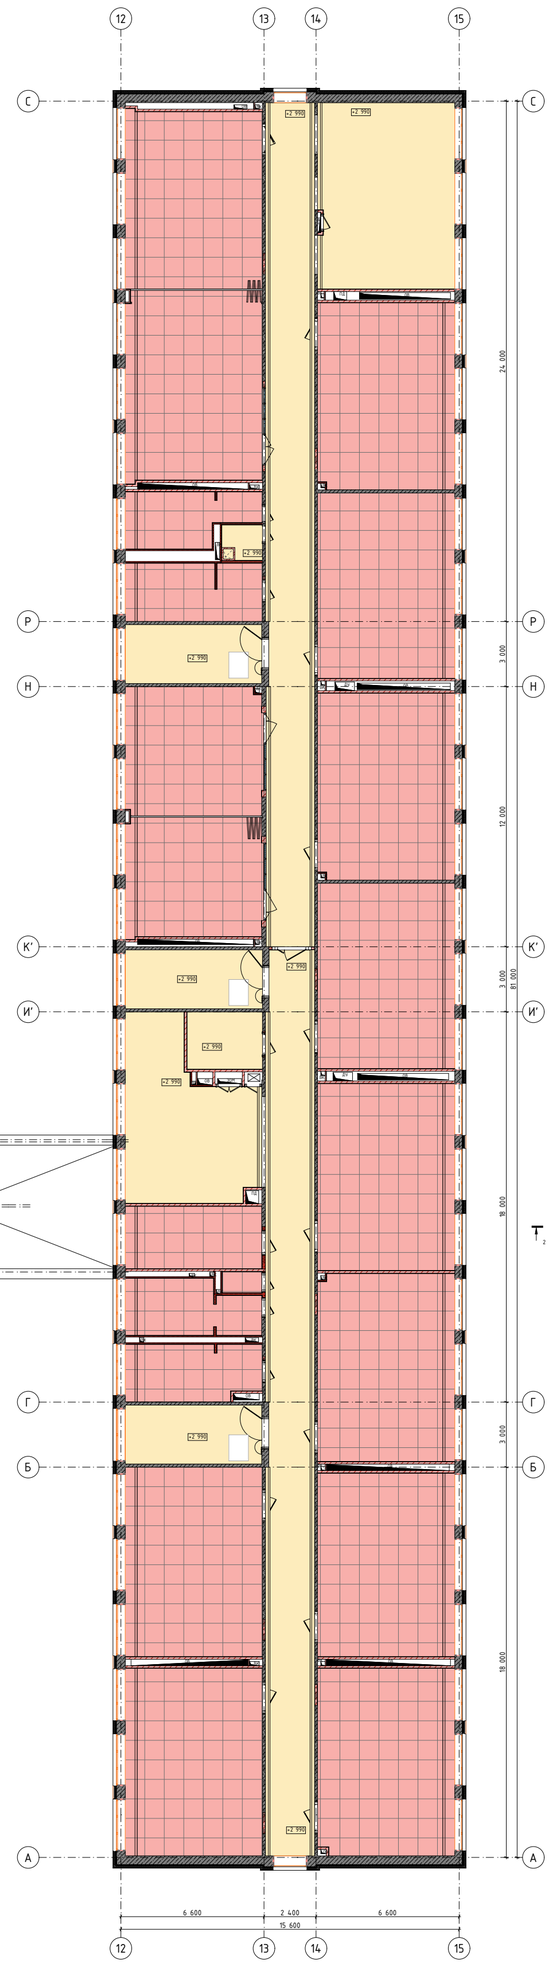

Условные обозначения

- минераловатный утеплитель+побелка
- покраска
- подвесной потолок
- покраска+сетка защитная

						ГИП-28/24-П-АР
						ГБОУ Школа № 218, расположенная по адресу: г. Москва, ул. Вучетича, д. 6
Изм.	Кол.уч.	Лист	№Док.	Подп.	Дата	
Разработал		Белова Е.С.			09.25	Средняя общеобразовательная школа
Проверил		Дубинин С.В.			09.25	
ГАП		Дубинин С.В.			09.25	
ГИП		Гущин А.В.				План демонтажа потолков 4 этажа
Н.контроль		Шукшин В.В.			09.25	

Стадия	Лист	Листов
П	32	

И-ГРУПП
ПРОЕКТНО-СТРОИТЕЛЬНАЯ КОМПАНИЯ

								ГИП-28/24-П-АР	
Изм.	Кол.уч.	Лист	№док.	Подп.	Дата	ГБОУ Школа №218, расположенная по адресу: г. Москва, ул. Вучетича, д. 6			
Разработал	Беляева Е.С.				09.25				
Проверил	Дудышин С.В.				09.25	Средняя общеобразовательная школа	Стадия	Лист	Листов
ГАП	Дудышин С.В.				09.25		П	33	
ГИП	Гущин А.В.					План демонтажа помолков выходов на кровлю			
Н.контроль		Шухшин В.В.			09.25		ИПУМП ПРОЕКТНО-СТРОИТЕЛЬНАЯ КОМПАНИЯ		

Условные обозначения

– подвесной помолок из цементных плит с покрасской

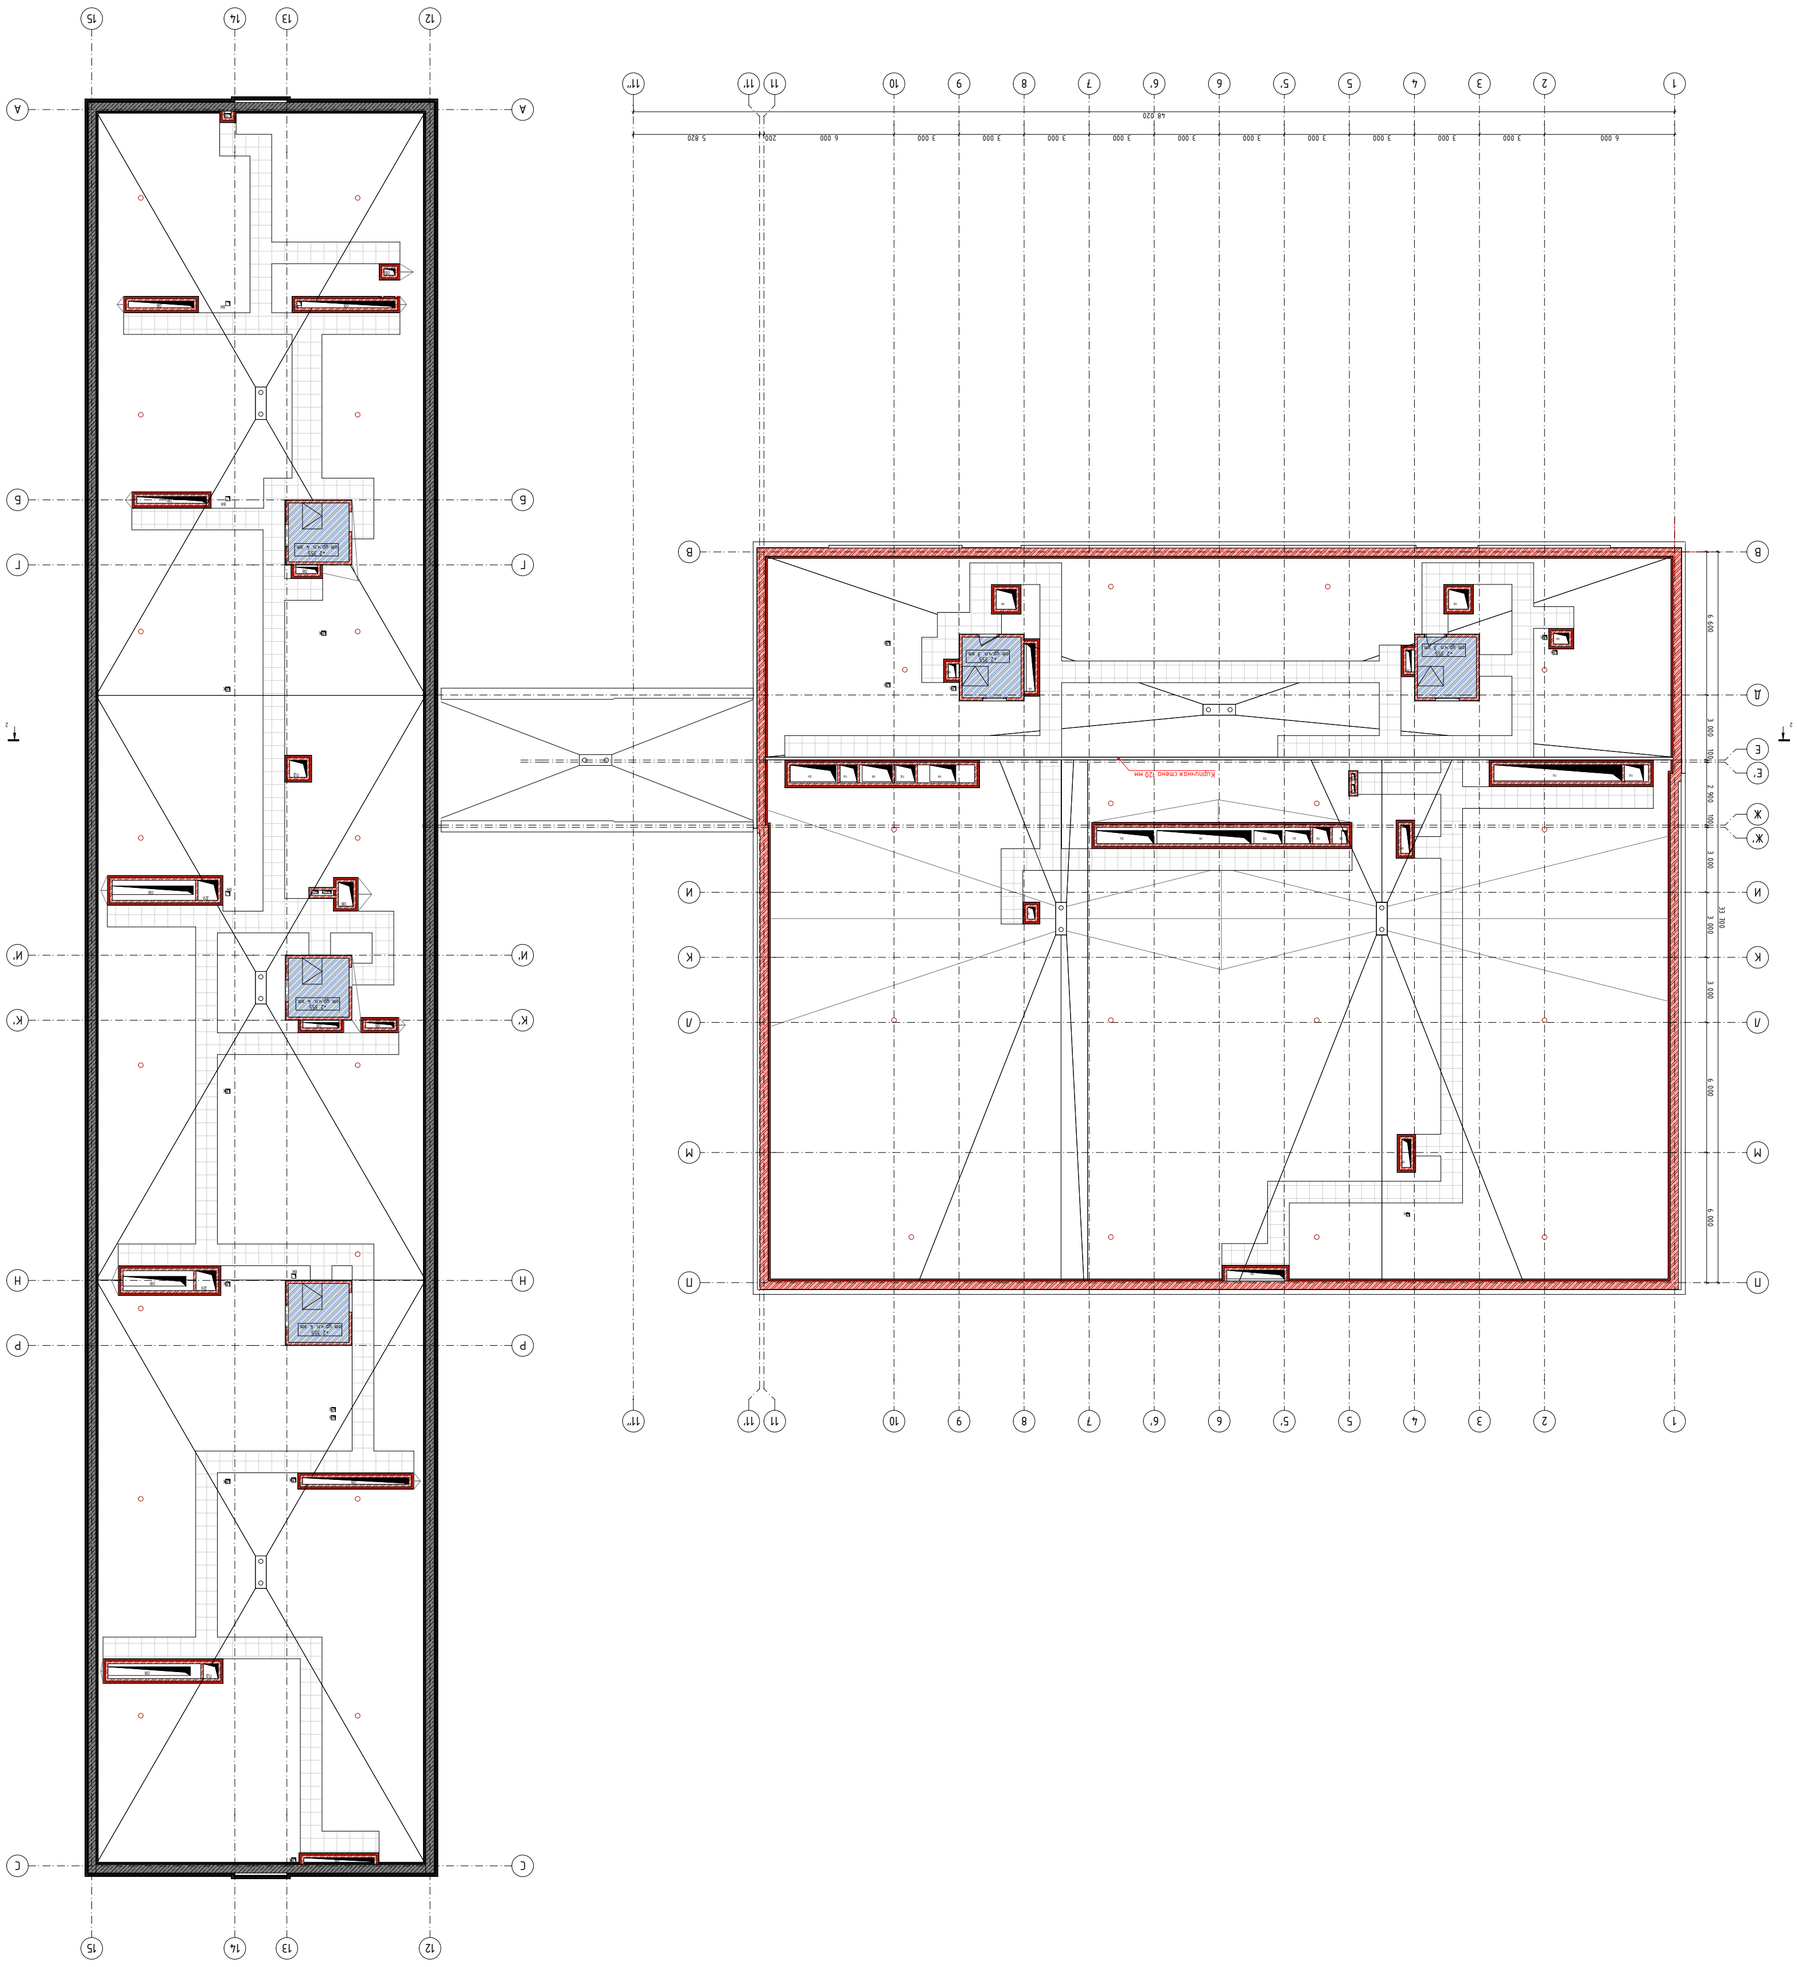

План демонтажа помолков выходов на кровлю

План потолков подвального этажа
М 1:200

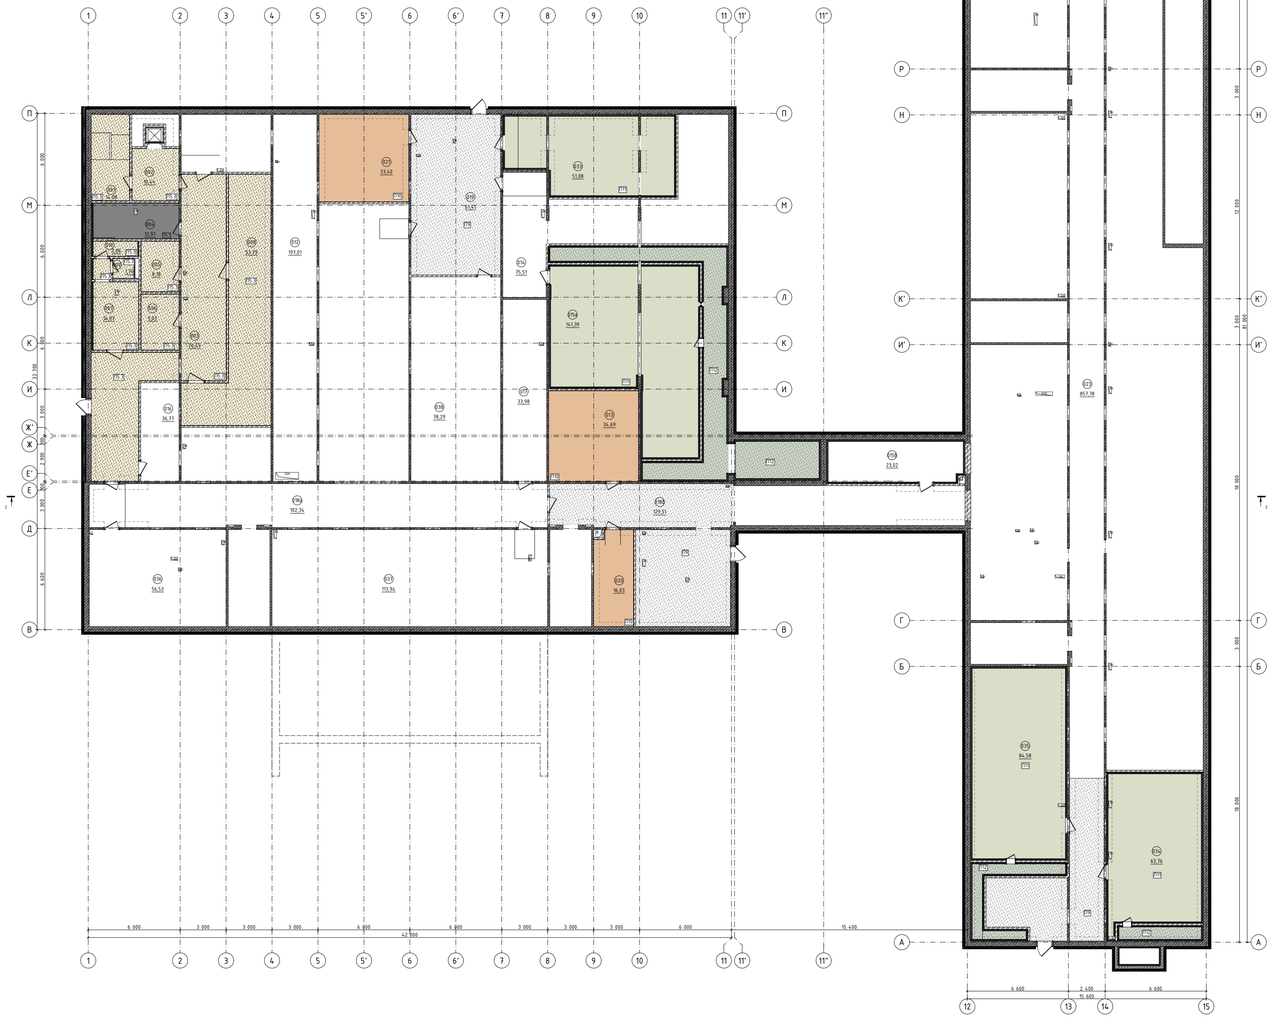

Экспликация помещений на отм. -3.000

№	Наименование	Площадь	Категория помещения
001	Лестничная клетка технологическая (для персонала)	14,08	
002	Тамбур-шлюз 1-го типа	10,44	
003	Коридор	70,49	
004	ПУИ	12,97	В3
005	Кладовая овощей	8,18	В4
006	Кладовая сухих продуктов	9,03	В4
007	Помещение персонала (не более 5 чел.)	14,87	
008	Помещение для установки холодильных камер	53,79	В3
009	Сан. узел	1,76	
010	Душевая	2,86	
012	Техническое помещение (для прокладки инженерных коммуникаций)	197,01	В4
013	Электрощитовая	34,69	В3
014	Техническое помещение (для прокладки инженерных коммуникаций)	75,51	В4
015а	Венткамера	141,39	В4
015б	Венткамера	23,02	В4
016	Техническое помещение (для прокладки инженерных коммуникаций)	36,77	В4
017	Техническое помещение (для прокладки инженерных коммуникаций)	33,98	В4
018а	Коридор	102,34	
018б	Коридор	129,51	
019	Коридор	61,41	
020	Электрощитовая	16,03	В3
021	Водомерный узел	33,40	Д
023	Техническое помещение (для прокладки инженерных коммуникаций)	857,78	В4
025	Коридор	17,09	
026	Техническое помещение (для прокладки инженерных коммуникаций)	12,56	В4
027	Техническое помещение (для прокладки инженерных коммуникаций)	5,15	В4
028	Техническое помещение (для прокладки инженерных коммуникаций)	6,46	В4
030	Коридор	44,17	
031	Техническое помещение (для прокладки инженерных коммуникаций)	9,90	В4
032	Техническое помещение (для прокладки инженерных коммуникаций)	74,73	В4
033	ИТП	51,08	В4
034	Венткамера	63,76	В4
035	Венткамера	84,58	В4
036	Техническое помещение (для прокладки инженерных коммуникаций)	56,53	В4
037	Техническое помещение (для прокладки инженерных коммуникаций)	113,94	В4
038	Техническое помещение (для прокладки инженерных коммуникаций)	78,29	В4
Условные обозначения:		2 559,55 м²	

Условные обозначения осветительных приборов:

Условное обозначение	Наименование	Цвет корпуса	Габариты, мм
1	Светодиодный светильник накладной ZCS S 25Вт 65 4000 WH	белый	Ø220x70
6.10L	Светодиодный светильник подвесной с силикатным стеклом OPTIMA 5771S P 1500 HB 40Вт 54 4000 GL BK	черный	1500
6.10L.a.EM2	Светодиодный светильник подвесной с силикатным стеклом с БАП OPTIMA 5771S P 1500 HB 40Вт 54 4000 EM2 GL BK	черный	1500
7	Светодиодный светильник подвесной OPTIMA 5771S P 1500 HB 28Вт 40 4000	Белый	1500x57x71
7.a	Светодиодный светильник подвесной с БАП OPTIMA 5771S P 1500 HB 28Вт 40 4000 EM2 BK	Белый	1500x57x71
8	Светодиодный светильник подвесной OPTIMA 5771S P 1500 HB 28Вт 54 4000 BK	черный	1500
11.1L	Светодиодный светильник подвесной OPTIMA 5771S P 1000 HB 26Вт 54 4000 BK	черный	1000
212	Светодиодный светильник накладной/подвесной ARCTIC DUST-12S 35Вт 65 4000 GR	серый	1200
212.a	Светодиодный светильник накладной/подвесной с БАП ARCTIC DUST-12S 35Вт 65 4000 EM2 GR	серый	1200

П4.1
– покраска НГ краской 9011

П5.1
– покраска НГ краской RAL 9003

П9
– обеспыливание

П10
– побелка

П11
– минераловатный утеплитель толщ.100мм, штукатурка 20мм, побелка

П12
– минераловатный утеплитель толщ.180мм, штукатурка 20мм, побелка

Примечания:
1. Согласно табл. 7.4 СП 71.13330.2017 подготовительный слой горизонтальных поверхностей в помещениях следует принять как:
1. Улучшенная штукатурка применяется в технических помещениях и помещениях пищеблока (кроме помещений, где предусмотрена обеспыливание и помещения, где отделка не предусмотрена);
2. Высококачественная штукатурка применяется во всех помещениях с пребыванием детей.

0,000=168,265

Изм.	Колич.	Лист	№Док.	Подп.	Дата	ГИП-28/24-П-АР			
						ГБОУ Школа № 218, расположенная по адресу: г. Москва, ул. Вучетича, д. 6			
Разработал		Белова Е.С.			09.25	Средняя общеобразовательная школа	Стадия	Лист	Листов
Проверил		Дубинин С.В.			09.25		П	34	64
ГАП		Дубинин С.В.			09.25				
ГИП		Гущин А.В.				План потолков подвального этажа	И-ГРУПП ПРОЕКТНО-СТРОИТЕЛЬНАЯ КОМПАНИЯ		
Н.контроль		Шукшин В.В.			09.25				

План потолков 1 этажа на отм. 0,000
М 1:200

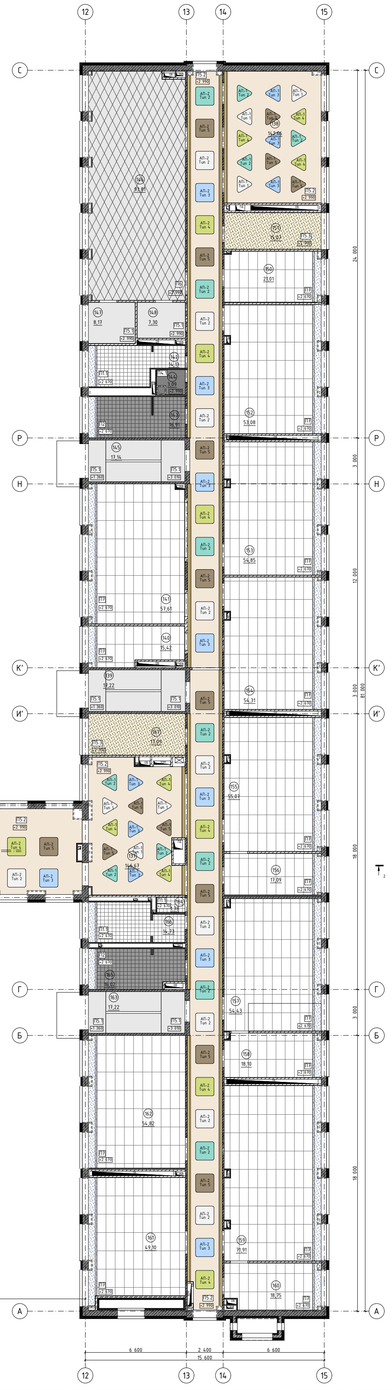

Условные обозначения:

- П1.1 – Грильятто 50х50, Белый, Негорючая окраска запотолочного пространства и коммуникаций RAL 9011
- П1.2 – Грильятто 100х100, белый, Негорючая окраска запотолочного пространства и коммуникаций RAL 9011
- П1.3 – Грильятто 100х100, белый, Негорючая окраска запотолочного пространства и коммуникаций RAL 9011
- П2 – Грильятто 50х50, черный, Негорючая окраска запотолочного пространства и коммуникаций RAL 9011
- П3 – алюминиевый кассетный потолок АЛБЕС 600х600
- П4.1 – покраска НГ краской RAL 9011
- П4.2 – покраска водоэмульсионной краской RAL 9011
- П5.1 – покраска НГ краской RAL 9003
- АП-1 Акустические подвесные панели из минерального стекловолокна. Размер панели 1100х953х40 (трапеция со скругленными краями). Цвет: RAL 9010, RAL 200 80 25, RAL 240 70 20, RAL 110 80 40, Текстура "под дерево"
- АП-2 Акустические подвесные панели из минерального стекловолокна. Размер панели 1192х1192х40 (квадрат). Цвет: RAL 9010, RAL 200 80 25, RAL 240 70 20, RAL 110 80 40, Текстура "под дерево"
- П5.2 – покраска водоэмульсионной краской RAL 9003
- П5.3 – покраска НГ краской RAL 9003
- П6 – сетка защитная 100х100мм+покраска НГ краской RAL 9003
- П7 – Кассетный акустический потолок 1200х600
- П12 – минераловатный утеплитель толщ.180мм, штукатурка 20мм, побелка
- П14 – минераловатный утеплитель толщ.180мм, штукатурка 20мм, покраска НГ краской RAL 9003
- ПН-1 – Потолочная ниша из Акваланели, RAL 9003
- ОР-1 – обшивка ригеля Акваланелью на стальном каркасе, RAL 9011
- ОР-2 – обшивка ригеля Акваланелью на стальном каркасе, RAL 9003

П12.2	Светодиодный светильник накладной/подвесной с БАП ARCTIC DUST-12S 35Вт 65 4000 EM2 GR	серый	1200
П7	Светодиодный светильник настенный кососвет OFL Desk S 1200 42Вт 40 4000	RAL	1200х50х50

Примечания:
1. Предусмотреть крепление подвесов подвесных потолков к плитам перекрытия с применением анкер-клина.
2. Согласно табл. 7.4 СП 71.13330.2017 подготовительный слой горизонтальных поверхностей в помещениях следует принять как:
1. Улучшенная штукатурка применяется в технических помещениях и помещениях пищеблока (кроме помещений, где предусмотрено обеспыливание и помещения, где отделка не предусмотрена);
2. Высококачественная штукатурка применяется во всех помещениях с предбыванием детей.

Экпликация помещений на отм. 0.000

№	Наименование	Площадь	Категория помещения
101	Тамбур	20,58	
102	Тамбур	20,43	
103	Комната охраны с диспетчерским пунктом	20,99	
104а	Сан. узел МГН	5,05	
105	Вестибюль	238,49	
106	Лестничная клетка (тип Н2)	17,68	
107	Гардеробная комната (для учителей)	7,61	
107а	Сан. узел для персонала	4,55	
108	Кабинет с рабочим пространством для учителей Тип 2	74,85	
109	Тамбур	6,03	
110	Туалет медблока с местом для приготовления дезинфицирующих средств и хранения уборочного инвентаря	8,39	
111	Процедурный (прививочный) кабинет	16,62	
112	Кабинет врача	20,76	
113	Гардероб для обучающихся	47,46	
114	Гардероб для обучающихся	149,42	
115	Цех вторичной обработки овощей	15,98	В3
116	Цех первичной обработки овощей	10,34	В3
117	Сан. узел для персонала	1,99	
119	Коридор	29,34	
119а	Тамбур	4,70	
120	Моечная обратной тары	4,78	В4
121	Лестничная клетка (для персонала)	10,41	
122	Загрузочный цех	11,28	В3
123	Мясо-рыбный цех	18,28	В3
124	Моечная кухонной посуды	11,29	В3
125	ПУИ	5,53	
126	Помещение временного хранения пищевых отходов	9,37	В4
127	Моечная столовой посуды	46,82	В4
128	Горячий цех	45,30	В3
129	Холодный цех	10,12	В3
130	Обеденный зал	393,12	
131	Лестничная клетка (тип Н2)	17,68	
133	Сан. узел для мальчиков	8,29	
134	Сан. узел для девочек	7,82	
135	Коридор	83,12	
137	Коридор	146,67	
138	Коридор	142,66	
139	Лестничная клетка (тип Л1)	17,22	
140	Административный кабинет Тип 1	15,42	
141	Учебный кабинет	57,61	
142	Сан. узел для девочек	14,13	
143	Сан. узел для мальчиков	16,91	
144	ПУИ	3,09	В4
145	Лестничная клетка (тип Л1)	17,14	
146	Гимнастический зал	93,81	
147	Раздевальные	8,17	
148	Раздевальные	7,30	
150	Кабинет для индивидуальных занятий, в т.ч. с коррекционным педагогом	21,01	
151	Помещение для прокладки инженерных коммуникаций	15,07	В3
152	Учебный кабинет	53,08	
153	Учебный кабинет	54,85	
154	Учебный кабинет	54,31	
155	Учебные кабинет для изучения естествознания: химия	55,07	
156	Лаборанстская кабинета химии	17,09	В3
157	Учебные кабинет для изучения естествознания: физика	54,43	
158	Лаборанстская кабинета физики	18,10	В3
159	Учебные кабинеты для изучения естествознания: биологии + ОБЗР	71,91	
160	Лаборанстская кабинета биологии	18,75	В3
161	Кабинет материальной технологии Тип 2	49,10	В3
162	Кабинет материальной технологии Тип 1	54,82	В3
163	Лестничная клетка (тип Л1)	17,22	
164	Сан. узел персонала	1,78	
165	Сан. узел для мальчиков	16,02	
166	Сан. узел для девочек с комнатой личной гигиены	14,73	
167	Серверная	17,09	В3
168	Кроссовая	5,03	В3
169	Кроссовая	4,92	В3
		2 558,98 м²	

Условные обозначения осветительных приборов:

Условное обозначение	Наименование	Цвет корпуса	Габариты, мм
1	Светодиодный светильник встраиваемый даунлайт CANZAS DL-011S R D150 20Вт 65 4000 WH	белый	Ø150х40
2	Светодиодный светильник накладной ZCS S 25Вт 65 4000 WH	белый	Ø220х70
3	Дизайнерский светодиодный светильник накладной NOVA 80S S 750 HB 60Вт 40 4000 BK	черный	Ø750х80
3а	Дизайнерский светодиодный светильник накладной с БАП NOVA 80S S 750 HB 60Вт 40 4000 EM2 BK	черный	Ø750х80
5	Светодиодный светильник подвесной OPTIMA 5771S P 1500 HB 56Вт 54 4000 BK	черный	1500
5а	Светодиодный светильник подвесной с БАП OPTIMA 5771S P 1500 HB 56Вт 54 4000 EM2 BK	черный	1500
6	Светодиодный светильник подвесной OPTIMA 5771S P 1500 HB 40Вт 40 4000 BK	черный	1500
6а	Светодиодный светильник подвесной с БАП OPTIMA 5771S P 1500 HB 40Вт 40 4000 EM2 BK	черный	1500
7	Светодиодный светильник подвесной OPTIMA 5771S P 1500 HB 28Вт 40 4000	Белый	1500х57х71
7а	Светодиодный светильник подвесной с БАП OPTIMA 5771S P 1500 HB 28Вт 40 4000 EM2 BK	Белый	1500х57х71
8	Светодиодный светильник подвесной OPTIMA 5771S P 1500 HB 28Вт 54 4000 BK	черный	1500
8а	Светодиодный светильник подвесной с БАП OPTIMA 5771S P 1500 HB 28Вт 54 4000 EM2 BK	черный	1500
11	Светодиодный светильник подвесной OPTIMA 5771S P 1000 HB 37Вт 54 4000 WH	белый	1000
	Светодиодный светильник подвесной OPTIMA 5771S P 1000 HB 26Вт 54 4000 BK	черный	1000
12	Светодиодный светильник накладной с защитной решеткой UNIVERSAL SC SPORT S 595х595 HB 40Вт 40 4000 WH	белый	595х595х50
12а	Светодиодный светильник накладной с защитной решеткой с БАП UNIVERSAL SC SPORT S 595х595 HB 40Вт 40 4000 EM2 WH	белый	595х595х50

1	Светодиодный светильник встраиваемый UNIVERSAL SC R 595х595 HB 30Вт 40 4000 WH	белый	595х595х50
1а	Светодиодный светильник встраиваемый с БАП UNIVERSAL SC R 595х595 HB 30Вт 40 4000 EM2 WH	белый	595х595х50
10	Светодиодный светильник встраиваемый ClipIN S R 600х600 HB 35Вт 54 4000 WH	белый	600х600х50
10а	Светодиодный светильник встраиваемый с БАП ClipIN S R 600х600 HB 35Вт 54 4000 EM2 WH	белый	600х600х50
16	Светодиодный светильник встраиваемый Grilyato Combo S 100х100 HB 8Вт 40 4000 WH		
16а	Светодиодный светильник встраиваемый с БАП Grilyato Combo S 100х100 HB 8Вт 40 4000 EM2 WH	белый	100х100
17	Светодиодный светильник встраиваемый Grilyato Combo S 100х100 HB 8Вт 54 4000 WH	белый	100х100
17а	Светодиодный светильник встраиваемый с БАП Grilyato Combo S 100х100 HB 8Вт 54 4000 EM2 WH	белый	100х100
18	Светодиодный светильник встраиваемый Grilyato Combo S 100х100 HB 8Вт 54 4000 BK	черный	100х100
18а	Светодиодный светильник встраиваемый с БАП Grilyato Combo S 100х100 HB 8Вт 54 4000 EM2 WH	черный	100х100
П12	Светодиодный светильник накладной/подвесной ARCTIC DUST-12S 35Вт 65 4000 GR	серый	1200

0,000=168,265

Изм.	Колич.	Лист	№Док.	Подп.	Дата
Разработал		Белова Е.С.			09.25
Проверил		Дубинин С.В.			09.25
ГАП		Дубинин С.В.			09.25
ГИП		Гущин А.В.			
Н.контроль		Шукшин В.В.			09.25

ГИП-28/24-П-АР

ГБОУ Школа № 218, расположенная по адресу: г. Москва, ул. Вучетича, д. 6

Средняя общеобразовательная школа

Стадия	Лист	Листов
П	35	64

План потолков 1 этажа на отм. 0,000

И-ГРУПП
ПРОЕКТНО-СТРОИТЕЛЬНАЯ КОМПАНИЯ

План потолков 2 этажа на отм. +3.300
М 1:200

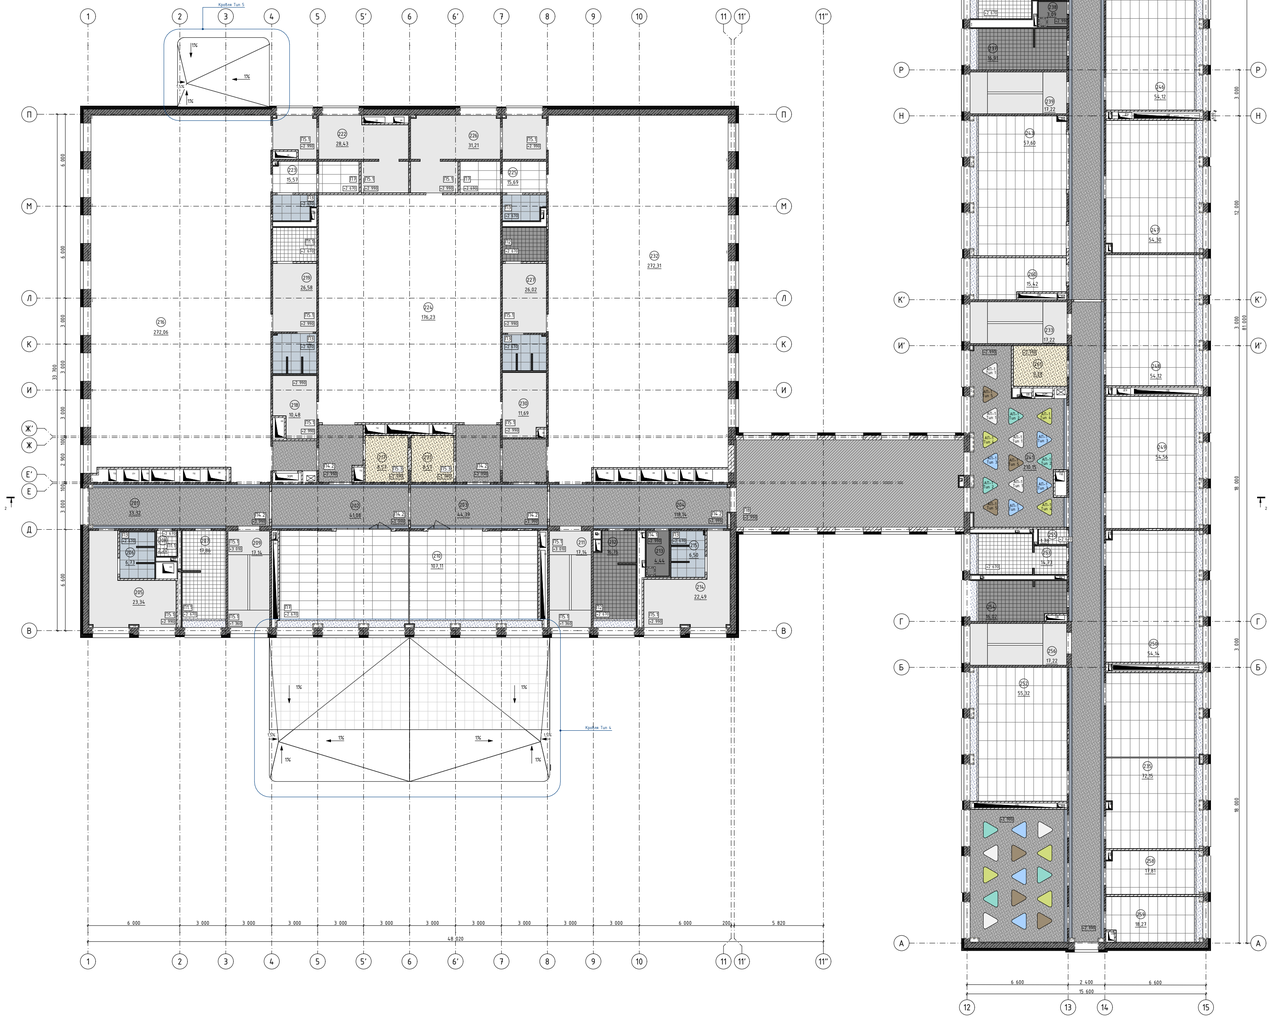

Экспликация помещений на отм. 3.300

№	Наименование	Площадь	Категория помещения
201	Коридор	33,32	
202	Коридор	41,08	
203	Коридор	44,39	
204	Коридор	118,14	
205	Раздевальная	23,34	
206	Душевая	6,73	
207	Сан. узел для девочек	17,86	
208	Сан. узел для персонала	2,20	
209	Лестничная клетка (тип Н2)	17,14	
210	Кабинет ИЗО	107,11	
211	Лестничная клетка (тип Н2)	17,14	
212	Сан. узел для мальчиков	16,76	
213	ПУИ	4,44	В4
214	Раздевальная	22,49	
215	Душевая	6,50	
216	Универсальный спортивный зал	272,06	
217	Кроссовая	8,57	В3
218	Артистическая с хранением костюмов	10,48	В3
219	Раздевальная	26,58	
222	Снарядная	28,43	В3
223	Комната инструктора с душем и сан. узлом	15,57	
224	Актовый зал	176,23	
225	Комната инструктора с душем и сан. узлом	15,69	
226	Снарядная	31,21	В3
227	Раздевальная	26,02	
230	Артистическая с хранением костюмов	11,69	В3
231	Кладовая инвентаря	8,57	В4
232	Универсальный спортивный зал	272,31	
233	Лестничная клетка (тип Л1)	17,22	
235	Кабинет иностранного языка	72,15	
236	Сан. узел для девочек	13,84	
237	Сан. узел для мальчиков	16,91	
238	ПУИ	3,09	В4
239	Лестничная клетка (тип Л1)	17,22	
240	Кабинет естествознания Тип 1	110,06	
241	Коридор	210,15	
243	Учебный кабинет	57,60	
244	Коридор	141,66	
245	Учебный кабинет	54,36	
246	Учебный кабинет	54,12	
247	Учебный кабинет	54,30	
248	Учебный кабинет	54,12	
249	Учебный кабинет	54,56	
250	Учебный кабинет	54,14	
252	Учебный кабинет	55,32	
253	Сан. узел для девочек	14,73	
254	Сан. узел для мальчиков	16,02	
255	Сан. узел для персонала	1,78	
256	Лестничная клетка (тип Л1)	17,22	
258	Кабинет для индивидуальных занятий, в т.ч. с учителем логопедом	17,81	
259	Административный кабинет Тип 1	18,27	
260	Административный кабинет Тип 1	15,42	
261	Кроссовая	9,28	В3
		2 533,40 м²	

Условные обозначения:

- П1.1 – Грильятто 50х50, белый, Негоричая окраска запотолочного пространства и коммуникаций RAL 9011
- П2 – Грильятто 50х50, черный, Негоричая окраска запотолочного пространства и коммуникаций RAL 9011
- П3 – алюминиевый кассетный потолок АЛБЕС 600х600
- П4.1 – покраска НГ краской RAL 9011
- П4.2 – покраска водоэмульсионной краской 9011
- П5.1 – покраска НГ краской RAL 9003
- П7 – Кассетный акустический потолок 1200х600
- П8 – подвесной потолок из акваланели с покраской водоэмульсионной краской 9011
- ПН-1 – Потолочная ниша из Акваланели, RAL 9003
- ОР-1 – обшивка ригеля Акваланелью на стальном каркасе, RAL 9011
- АП-1 Акустические подвесные панели из минерального стекловолокна. Размер панели 1100х953х40 Трегольник со скругленными краями. Цвет: RAL 9010, RAL 200 80 25, RAL 240 70 20, RAL 110 80 40, Текстура "под дерево"

Условные обозначения осветительных приборов:

Условное обозначение	Наименование	Цвет корпуса	Габариты, мм
1	Дизайнерский светодиодный светильник накладной NOVA 80S S 750 HB 60Вт 40 4000 BK	черный	Ø750x80
1а	Дизайнерский светодиодный светильник накладной с БАП NOVA 80S S 750 HB 60Вт 40 4000 EM2 BK	черный	Ø750x80
4	Дизайнерский светодиодный светильник подвесной NOVA 80S P 900 HB 60Вт 40 4000 BK	черный	Ø900x80
4а	Дизайнерский светодиодный светильник подвесной с БАП NOVA 80S P 900 HB 60Вт 40 4000 EM2 BK	черный	Ø900x80
5 OL	Светодиодный светильник подвесной с силикатным стеклом OPTIMA 5771S P 1500 HB 56Вт 54 4000 GL BK	черный	1500
5 OL а БАП	Светодиодный светильник подвесной с силикатным стеклом с БАП OPTIMA 5771S P 1500 HB 56Вт 54 4000 EM2 GL BK	черный	1500
6	Светодиодный светильник подвесной OPTIMA 5771S P 1500 HB 40Вт 40 4000 BK	черный	1500
6а	Светодиодный светильник подвесной с БАП OPTIMA 5771S P 1500 HB 40Вт 40 4000 EM2 BK	черный	1500
6 OL	Светодиодный светильник подвесной с силикатным стеклом OPTIMA 5771S P 1500 HB 40Вт 54 4000 GL BK	черный	1500
6 OL а БАП	Светодиодный светильник подвесной с силикатным стеклом с БАП OPTIMA 5771S P 1500 HB 40Вт 54 4000 EM2 GL BK	черный	1500
7	Светодиодный светильник подвесной OPTIMA 5771S P 1500 HB 28Вт 40 4000	Белый	1500x57x71
7а	Светодиодный светильник подвесной с БАП OPTIMA 5771S P 1500 HB 28Вт 40 4000 EM2 BK	Белый	1500x57x71
8 OL	Светодиодный светильник подвесной с силикатным стеклом OPTIMA 5771S P 1500 HB 28Вт 54 4000 GL BK	черный	1500
10 OL	Светодиодный светильник подвесной с силикатным стеклом OPTIMA 5771S P 1000 HB 26Вт 54 4000 GL BK	черный	1000
11	Светодиодный светильник встраиваемый UNIVERSAL SC R 595x595 HB 30Вт 40 4000 WH	белый	595x595x50
11а	Светодиодный светильник встраиваемый с БАП UNIVERSAL SC R 595x595 HB 30Вт 40 4000 EM2 WH	белый	595x595x50
11 OL	Светодиодный светильник встраиваемый с силикатным стеклом UNIVERSAL SC R 595x595 HB 30Вт 40 4000 GL WH	белый	595x595x50
11 OL а БАП	Светодиодный светильник встраиваемый с силикатным стеклом с БАП UNIVERSAL SC R 595x595 HB 30Вт 54 4000 EM2 GL WH	белый	595x595x50
15	Светодиодный светильник встраиваемый ClipIN S R 60	белый	600x600x50
17	Светодиодный светильник встраиваемый Grilyato Combo S 100x100 HB 8Вт 54 4000 WH	белый	100x100
18	Светодиодный светильник встраиваемый Grilyato Combo S 100x100 HB 8Вт 54 4000 BK	черный	100x100
20	Светодиодный светильник настенный кососвет OFL Desk S 1200 42Вт 40 4000	RAL	1200x50x50

0,000=168,265

Примечания:
1. Предусмотреть крепление подвесов подвесных потолков к плитам перекрытия с применением анкер-клина.
2. Согласно табл. 7.4 СП 71.13330.2017 подготовительный слой горизонтальных поверхностей в помещениях следует принять как:
1. Улучшенная штукатурка применяется в технических помещениях и помещениях пищеблока (кроме помещений, где предусмотрено обеспыливание и помещения, где отделка не предусмотрена);
2. Высококачественная штукатурка применяется во всех помещениях с предбыванием детей.

Изм.	Колич.	Лист	№Док.	Подп.	Дата
Разработал		Белова Е.С.			09.25
Проверил		Дубинин С.В.			09.25
ГАП		Дубинин С.В.			09.25
ГИП		Гущин А.В.			
Н.контроль		Шукшин В.В.			09.25

ГИП-28/24-П-АР

ГБОУ Школа № 218, расположенная по адресу: г. Москва, ул. Вучетича, д. 6

Средняя общеобразовательная школа

Стадия	Лист	Листов
П	36	64

План потолков 2 этажа на отм. +3.300

И-ГРУПП
ПРОЕКТНО-СТРОИТЕЛЬНАЯ КОМПАНИЯ

План потолков 3 этажа на отм. +6.600
М 1:200

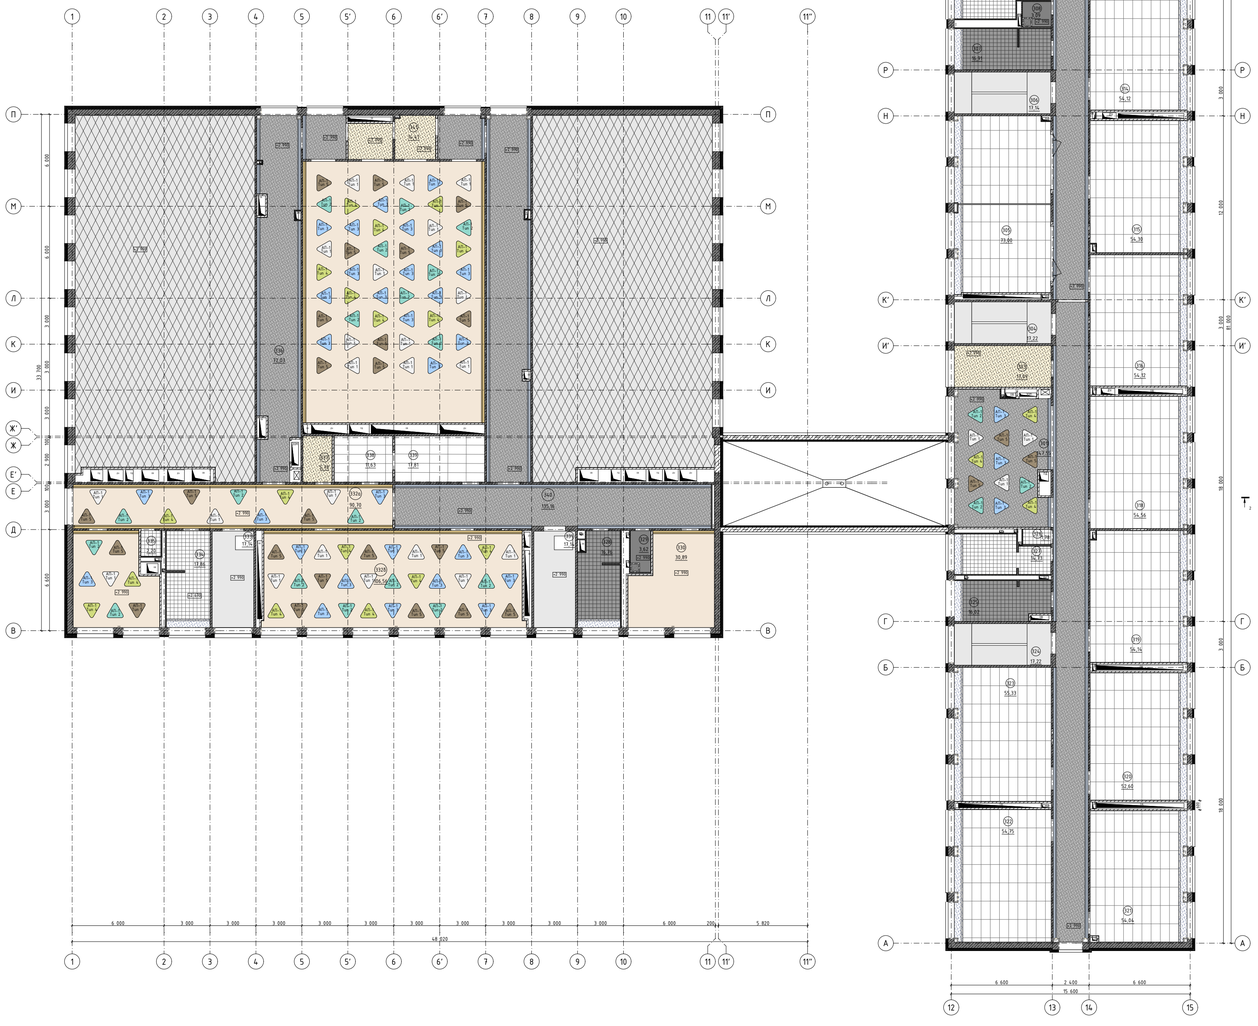

Экспликация помещений на отм. 6.600

№	Наименование	Площадь	Категория помещения
301	Коридор	147,55	
303	Серверная	17,09	В3
304	Лестничная клетка (тип Л1)	17,22	
305	Кабинет иностранного языка	73,00	
306	Лестничная клетка (тип Л1)	17,14	
307	Сан. узел для мальчиков	16,91	
308	ПУИ	3,09	В4
309	Сан. узел для девочек	13,85	
310	Учебный кабинет	53,90	
311	Учебный кабинет	55,39	
312	Коридор	142,37	
313	Учебный кабинет	54,36	
314	Учебный кабинет	54,12	
315	Учебный кабинет	54,30	
316	Учебный кабинет	54,12	
318	Учебный кабинет	54,56	
319	Учебный кабинет	54,14	
320	Учебный кабинет	52,60	
321	Учебный кабинет	54,04	
322	Учебный кабинет	54,75	
323	Учебный кабинет	55,33	
324	Лестничная клетка (тип Л1)	17,22	
325	Сан. узел для мальчиков	16,02	
326	Сан. узел персонала	1,78	
327	Сан. узел для девочек	14,73	
328	Сан. узел для мальчиков	16,76	
329	ПУИ	3,62	В4
330	Библиотека. Фонд хранения	30,89	В3
331	Лестничная клетка (тип Н2)	17,14	
332а	Коридор	90,70	
332б	Читальный зал	106,56	

№	Наименование	Площадь	Категория помещения
333	Лестничная клетка (тип Н2)	17,14	
334	Сан. узел для девочек	17,86	
335	Сан. узел для персонала	2,20	
336	Коридор	72,03	
337	Кроссовая	5,78	В3
338	Кабинет для индивидуальных занятий. Студия звукозаписи	11,63	
339	Медиакласс	17,81	
340	Коридор	135,16	
341	Технический центр	14,41	В3
		1 709,27 м²	

Условные обозначения:

- П1.1 – Грильятто 50х50, белый, Негорючая окраска запотолочного пространства и коммуникаций RAL 9011
- П2 – Грильятто 50х50, черный, Негорючая окраска запотолочного пространства и коммуникаций RAL 9011
- П4.1 – покраска НГ краской RAL 9011
- П4.2 – покраска водоэмульсионной краской 9011
- П5.1 – покраска НГ краской RAL 9003
- П5.2 – покраска водоэмульсионной краской RAL 9003
- П6 – сетка защитная 100х100мм + покраска НГ краской RAL 9003
- П7 – Кассетный акустический потолок 1200х600
- ПН-1 – Потолочная ниша из Акваланели, RAL 9003
- ОР-1 – обшивка ригеля Акваланелью на стальном каркасе, RAL
- ОР-2 – обшивка ригеля Акваланелью на стальном каркасе, RAL

Условные обозначения осветительных приборов:

Условное обозначение	Наименование	Цвет корпуса	Габариты, мм
3	Дизайнерский светодиодный светильник накладной NOVA 80S S 750 НВ 60Вт 40 4000 ВК	черный	Ø750x80
3а	Дизайнерский светодиодный светильник накладной с БАП NOVA 80S S 750 НВ 60Вт 40 4000 EM2 ВК	черный	Ø750x80
4	Дизайнерский светодиодный светильник подвесной NOVA 80S P 900 НВ 60Вт 40 4000 ВК	черный	Ø900x80
4а	Дизайнерский светодиодный светильник подвесной с БАП NOVA 80S P 900 НВ 60Вт 40 4000 EM2 ВК	черный	Ø900x80
5.1Д	Светодиодный светильник подвесной с силикатным стеклом OPTIMA 5771S P 1500 НВ 56Вт 54 4000 GL ВК	черный	1500
5.1Д.а.БАП	Светодиодный светильник подвесной с силикатным стеклом с БАП OPTIMA 5771S P 1500 НВ 56Вт 54 4000 EM2 GL ВК	черный	1500
6	Светодиодный светильник подвесной OPTIMA 5771S P 1500 НВ 40Вт 40 4000 ВК	черный	1500
6а	Светодиодный светильник подвесной с БАП OPTIMA 5771S P 1500 НВ 40Вт 40 4000 EM2 ВК	черный	1500
6.1Д	Светодиодный светильник подвесной с силикатным стеклом OPTIMA 5771S P 1500 НВ 40Вт 54 4000 GL ВК	черный	1500
6.1Д.а.БАП	Светодиодный светильник подвесной с силикатным стеклом с БАП OPTIMA 5771S P 1500 НВ 40Вт 54 4000 EM2 GL ВК	черный	1500
7	Светодиодный светильник подвесной OPTIMA 5771S P 1500 НВ 28Вт 40 4000	Белый	1500x57x71
7а	Светодиодный светильник подвесной с БАП OPTIMA 5771S P 1500 НВ 28Вт 40 4000 EM2 ВК	Белый	1500x57x71
9.1Д	Светодиодный светильник подвесной с силикатным стеклом OPTIMA 5771S P 1500 НВ 28Вт 54 4000 GL ВК	черный	1500
9.1Д.а	Светодиодный светильник подвесной с силикатным стеклом с БАП OPTIMA 5771S P 1500 НВ 28Вт 54 4000 EM2 GL ВК	черный	1500
11.2Д	Светодиодный светильник подвесной с силикатным стеклом OPTIMA 5771S P 1000 НВ 26Вт 54 4000 GL ВК	черный	1000
12	Светодиодный светильник накладной с защитной решеткой UNIVERSAL SC SPORT S 595x595 НВ 40Вт 40 4000 WH	белый	595x595x50
12а	Светодиодный светильник накладной с защитной решеткой с БАП UNIVERSAL SC SPORT S 595x595 НВ 40Вт 40 4000 EM2 WH	белый	595x595x50
13	Светодиодный светильник встраиваемый UNIVERSAL SC R 595x595 НВ 30Вт 40 4000 WH	белый	595x595x50
13а	Светодиодный светильник встраиваемый с БАП UNIVERSAL SC R 595x595 НВ 30Вт 40 4000 EM2 WH	белый	595x595x50
17	Светодиодный светильник встраиваемый Grilyato Combo S 100x100 НВ 8Вт 54 4000 WH	белый	100x100
18	Светодиодный светильник встраиваемый Grilyato Combo S 100x100 НВ 8Вт 54 4000 BK	черный	100x100
20	Светодиодный светильник настенный кососвет OFL Desk S 1200 42Вт 40 4000	RAL	1200x50x50

АП-1
Акустические подвесные панели из минерального стекловолокна. Размер панели 1100х953х40 (трапецоидальное со скругленными краями). Цвет: RAL 9010, RAL 200 80 25, RAL 240 70 20, RAL 110 80 40, Текстура "под дерево"

Примечания:
1. Предусмотреть крепление подвесов подвесных потолков к плитам перекрытия с применением анкер-клина.
2. Согласно табл. 7.4 СП 71.13330.2017 подготовительный слой горизонтальных поверхностей в помещениях следует принять как:
1. Улучшенная штукатурка применяется в технических помещениях и помещениях пищеблока (кроме помещений, где предусмотрено обеспыливание и помещения, где отделка не предусмотрена);
2. Высококачественная штукатурка применяется во всех помещениях с предыванием детей.

0,000=168,265

Изм.	Колич.	Лист	№Док.	Подп.	Дата
Разработал		Белова Е.С.			09.25
Проверил		Дубинин С.В.			09.25
ГАП		Дубинин С.В.			09.25
ГИП		Гущин А.В.			
Н.контроль		Шукшин В.В.			09.25

ГИП-28/24-П-АР

ГБОУ Школа № 218, расположенная по адресу: г. Москва, ул. Вучетича, д. 6

Средняя общеобразовательная школа

Стадия	Лист	Листов
П	37	64

План потолков 3 этажа на отм. +6.600

И-ГРУПП
ПРОЕКТНО-СТРОИТЕЛЬНАЯ КОМПАНИЯ

План потолков 4 этажа на отм. +9.900
М 1:200

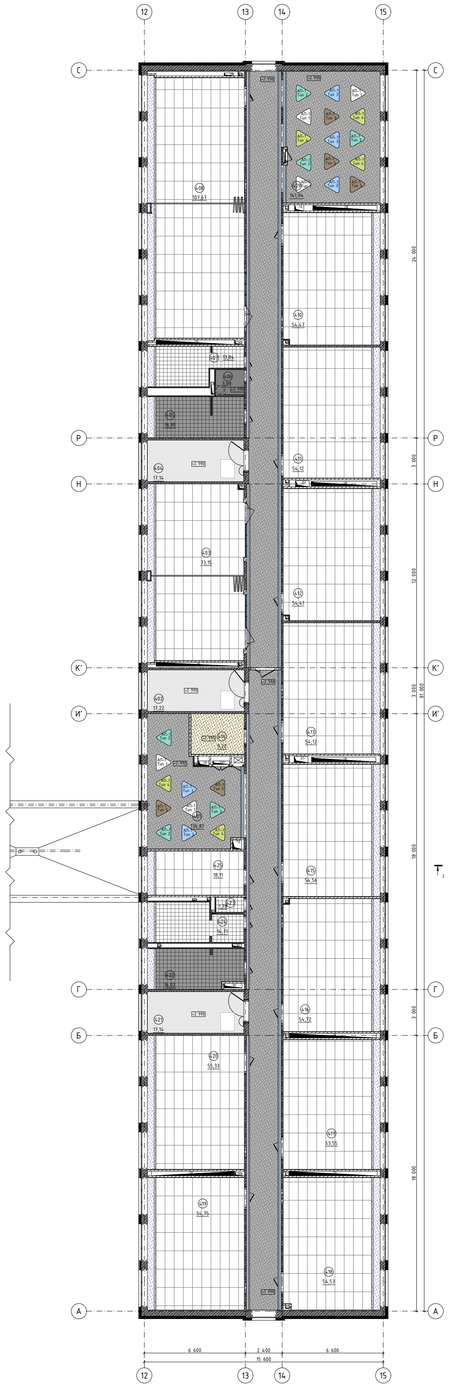

Экспликация помещений на отм. 9.900

№	Наименование	Площадь	Категория помещения
401	Коридор	136,81	
402	Лестничная клетка (тип Л1)	17,22	
403	Кабинет иностранного языка	73,15	
404	Лестничная клетка (тип Л1)	17,14	
405	Сан. узел для мальчиков	16,90	
406	ПУИ	3,09	В4
407	Сан. узел для девочек	13,84	
408	Кабинет информатики и информационных технологий	107,67	
409	Коридор	141,94	
410	Кабинет русского языка и литературы	54,47	
411	Кабинет русского языка и литературы	54,12	
412	Кабинет русского языка и литературы	54,41	
413	Кабинет математики	54,12	
414	Кроссовая	9,22	В3
415	Кабинет математики	54,56	
416	Кабинет истории Тип 1	54,72	
417	Кабинет географии	53,55	
418	Универсальный учебный кабинет	54,53	
419	Кабинет математики	54,75	
420	Кабинет истории Тип 1	55,33	
421	Лестничная клетка (тип Л1)	17,14	
422	Сан. узел для мальчиков	16,02	
423	Сан. узел персонала	1,78	
424	Сан. узел для девочек с комнатой личной гигиены	14,71	
425	Кабинет для индивидуальных занятий, в т.ч. с педагогом психологом	18,11	
		1 149,30 м²	

Условные обозначения:

- П1.1 – Грильятто 50х50, белый, Негорючая окраска запотолочного пространства и коммуникаций RAL 9011
- П2 – Грильятто 50х50, черный, Негорючая окраска запотолочного пространства и коммуникаций RAL 9011
- П4.1 – покраска НГ краской RAL 9011
- П4.2 – покраска водоэмульсионной краской 9011
- П5.1 – покраска НГ краской RAL 9003
- П7 – Кассетный акустический потолок 1200х600
- П13 – подвесной потолок из акваланели с покраской водоэмульсионной краской 9010
- ПН-1 – Потолочная ниша из Акваланели, RAL 9003
- ОР-1 – обшивка ригеля Акваланелью на стальном каркасе, RAL 901'

АП-1
Акустические подвесные панели из минерального стекловолокна. Размер панели 1100х953х40 (трецслойник со скругленными краями). Цвет: RAL 9010, RAL 200 80 25, RAL 240 70 20, RAL 110 80 40, Текстура "под дерево"

Условные обозначения осветительных приборов:

Условное обозначение	Наименование	Цвет корпуса	Габариты, мм
3	Дизайнерский светодиодный светильник накладной NOVA 80S S 750 НВ 60Вт 40 4000 ВК	черный	Ø750х80
3а	Дизайнерский светодиодный светильник накладной с БАП NOVA 80S S 750 НВ 60Вт 40 4000 ЕМ2 ВК	черный	Ø750х80
4	Дизайнерский светодиодный светильник подвесной NOVA 80S P 900 НВ 60Вт 40 4000 ВК	черный	Ø900х80
4а	Дизайнерский светодиодный светильник подвесной с БАП NOVA 80S P 900 НВ 60Вт 40 4000 ЕМ2 ВК	черный	Ø900х80
5.1Д	Светодиодный светильник подвесной с силикатным стеклом OPTIMA 5771S P 1500 НВ 56Вт 54 4000 GL BK	черный	1500
5.1Д а.БАП	Светодиодный светильник подвесной с силикатным стеклом с БАП OPTIMA 5771S P 1500 НВ 56Вт 54 4000 ЕМ2 GL BK	черный	1500
7	Светодиодный светильник подвесной OPTIMA 5771S P 1500 НВ 28Вт 40 4000	Белый	1500х57х71
7а	Светодиодный светильник подвесной с БАП OPTIMA 5771S P 1500 НВ 28Вт 40 4000 ЕМ2 ВК	Белый	1500х57х71
11.1Д	Светодиодный светильник подвесной с силикатным стеклом OPTIMA 5771S P 1000 НВ 26Вт 54 4000 GL BK	черный	1000
13	Светодиодный светильник встраиваемый UNIVERSAL SC R 595х595 НВ 30Вт 40 4000 WH	белый	595х595х50
13а	Светодиодный светильник встраиваемый с БАП UNIVERSAL SC R 595х595 НВ 30Вт 40 4000 ЕМ2 WH	белый	595х595х50
17	Светодиодный светильник встраиваемый Grilyato Combo S 100х100 НВ 8Вт 54 4000 WH	белый	100х100
18	Светодиодный светильник встраиваемый Grilyato Combo S 100х100 НВ 8Вт 54 4000 ВК	черный	100х100
20	Светодиодный светильник настенный кососвет OFL Desk S 1200 42Вт 40 4000	RAL	1200х50х50

Примечания:
1. Предусмотреть крепление подвесов подвесных потолков к плитам перекрытия с применением анкер-клина.
2. Согласно табл. 7.4 СП 71.13330.2017 подготовительный слой горизонтальных поверхностей в помещениях следует принять как:
1. Улучшенная штукатурка применяется в технических помещениях и помещениях пищеблока (кроме помещений, где предусмотрено обеспыливание и помещения, где отделка не предусмотрена);
2. Высококачественная штукатурка применяется во всех помещениях с пребыванием детей.

0,000=168,265

Изм.	Колуч.	Лист	№Док.	Подп.	Дата
Разработал	Белова Е.С.				09.25
Проверил	Дубинин С.В.				09.25
ГАП	Дубинин С.В.				09.25
ГИП	Гущин А.В.				
Н.контроль	Шукшин В.В.				09.25

ГИП-28/24-П-АР

ГБОУ Школа № 218, расположенная по адресу: г. Москва, ул. Вучетича, д. 6

Средняя общеобразовательная школа

Стадия	Лист	Листов
П	38	64

План потолков 4 этажа на отм. +9.900

И-ГРУПП
ПРОЕКТНО-СТРОИТЕЛЬНАЯ КОМПАНИЯ

План потолков выходов на кровлю
М 1:200

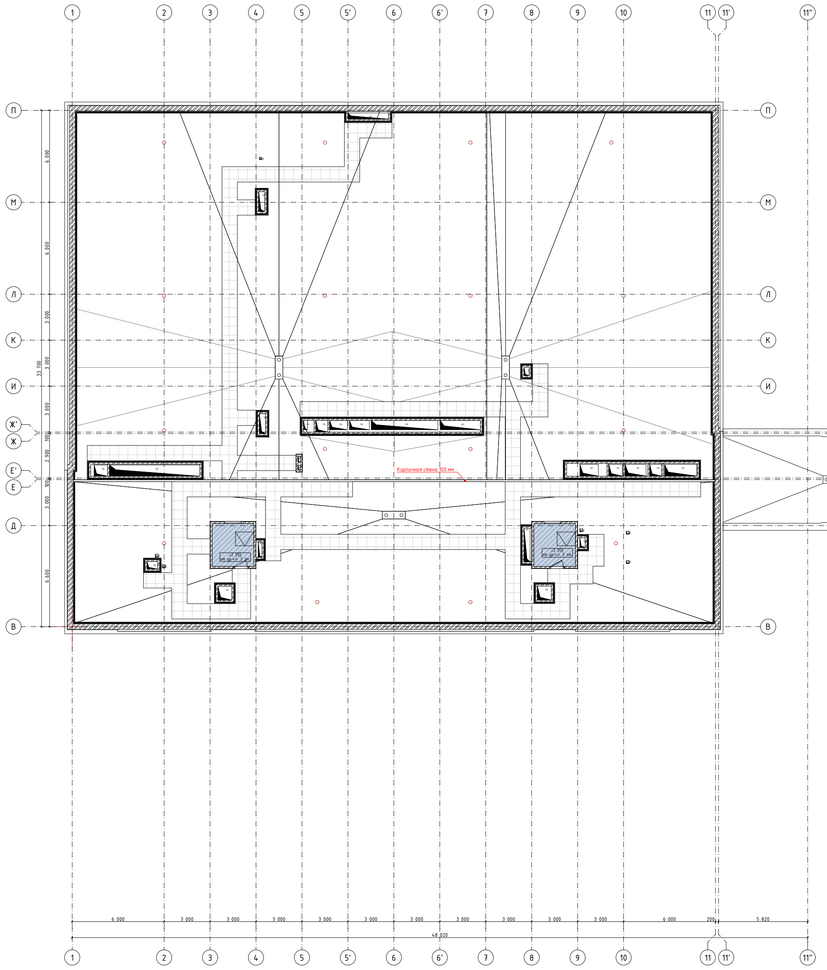

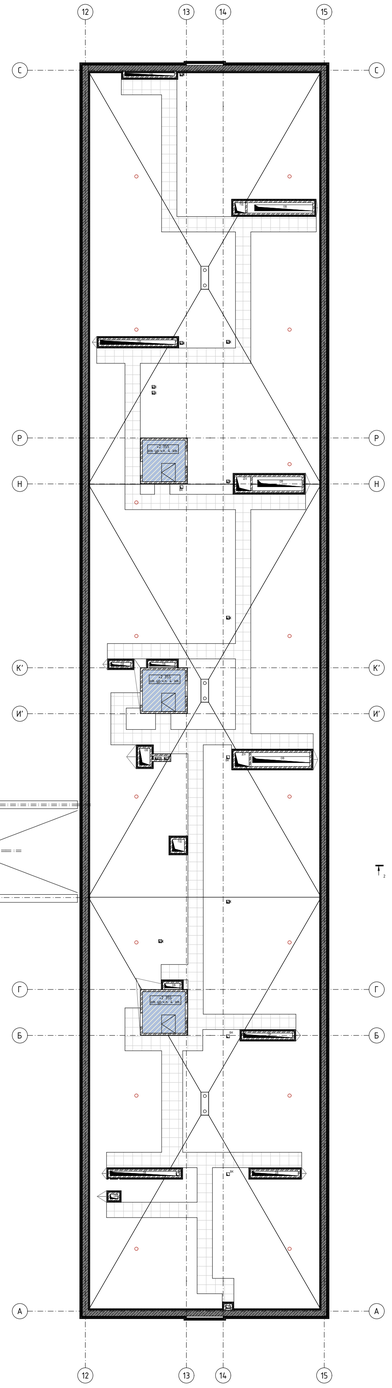

Условные обозначения:

П13
– подвесной потолок из акваланели с покраской водоэмульсионной краской 9010

Примечания:
1. Предусмотреть крепление подвесов подвесных потолков к плитам перекрытия с применением анкер-клина.
2. Согласно табл. 7.4 СП 71.13330.2017 подготовительный слой горизонтальных поверхностей в помещениях следует принять как:
1. Улучшенная штукатурка применяется в технических помещениях и помещениях пищеблока (кроме помещений, где предусмотрена обеспыливание и помещения, где отделка не предусмотрена);
2. Высококачественная штукатурка применяется во всех помещениях с предыванием детей.

0,000=168,265

						ГИП-28/24-П-АР	
						ГБОУ Школа № 218, расположенная по адресу: г. Москва, ул. Вучетича, д. 6	
Изм.	Колуч.	Лист	№Док.	Подп.	Дата		
Разработал		Белова Е.С.			09.25	Средняя общеобразовательная школа	Стадия: П; Лист: 39; Листов: 64
Проверил		Дубинин С.В.			09.25		
ГАП		Дубинин С.В.			09.25		
ГИП		Гущин А.В.				План потолков выходов на кровлю	И-ГРУПП ПРОЕКТНО-СТРОИТЕЛЬНАЯ КОМПАНИЯ
Н.контроль		Шукшин В.В.			09.25		

План подоконников 1 этажа на отм. 0,000
М 1:200

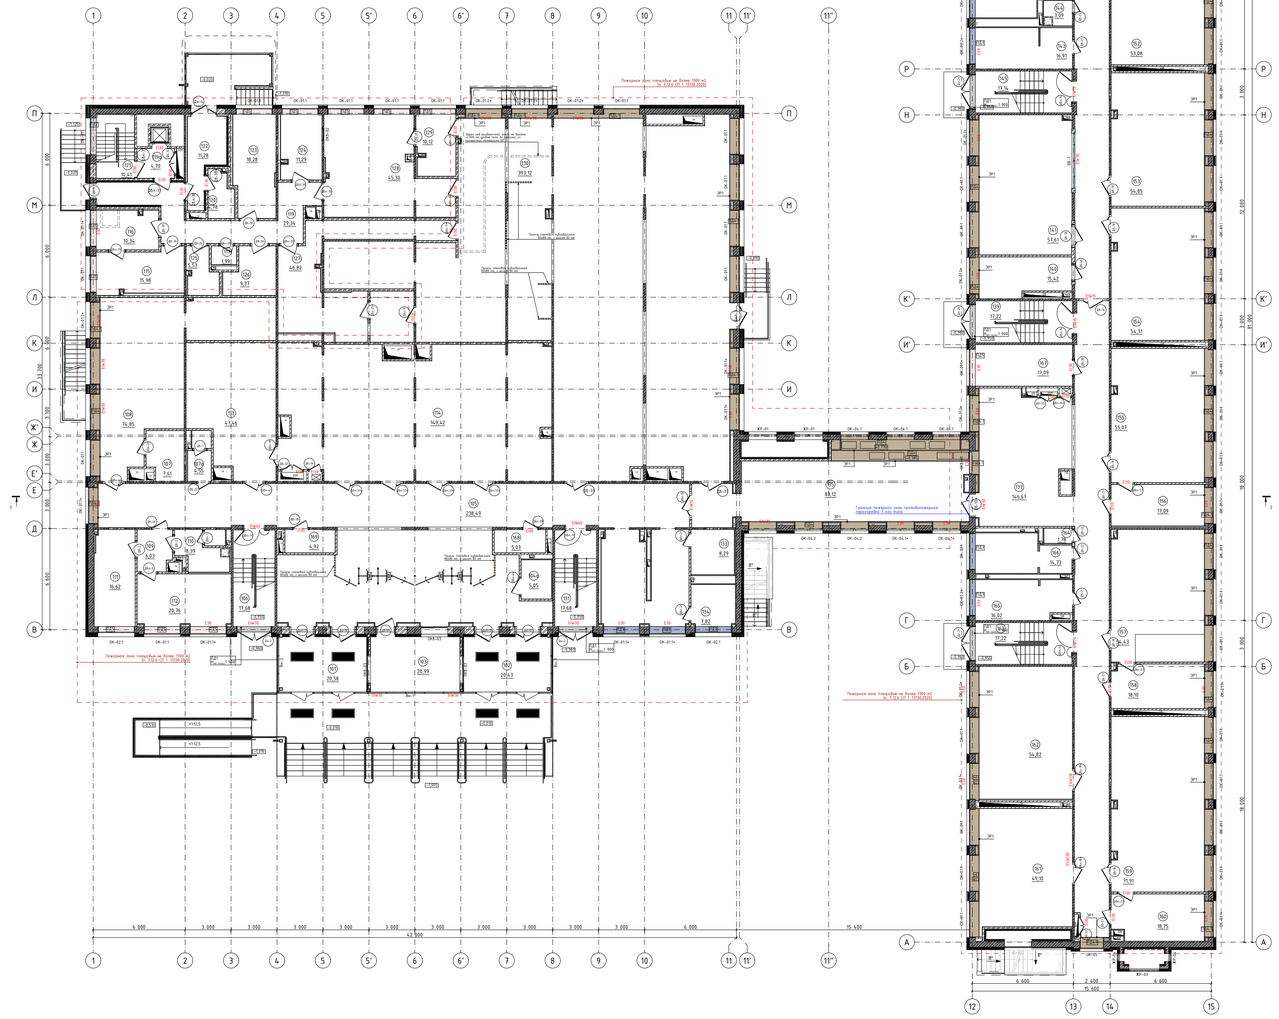

Экпликация помещений на отм. 0.000

№	Наименование	Площадь	Категория помещения
101	Тамбур	20,58	
102	Тамбур	20,43	
103	Комната охраны с диспетчерским пунктом	20,99	
104а	Сан. узел МГН	5,05	
105	Вестибюль	238,49	
106	Лестничная клетка (тип Н2)	17,68	
107	Гардеробная комната (для учителей)	7,61	
107а	Сан. узел для персонала	4,55	
108	Кабинет с рабочим пространством для учителей Тип 2	74,85	
109	Тамбур	6,03	
110	Туалет медблока с местом для приготовления дезинфицирующих средств и хранения уборочного инвентаря	8,39	
111	Процедурный (прививочный) кабинет	16,62	
112	Кабинет врача	20,76	
113	Гардероб для обучающихся	47,46	
114	Гардероб для обучающихся	149,42	
115	Цех вторичной обработки овощей	15,98	В3
116	Цех первичной обработки овощей	10,34	В3
117	Сан. узел для персонала	1,99	
119	Коридор	29,34	
119а	Тамбур	4,70	
120	Моечная обратной тары	4,78	В4
121	Лестничная клетка (для персонала)	10,41	
122	Загрузочный цех	11,28	В3
123	Мясо-рыбный цех	18,28	В3
124	Моечная кухонной посуды	11,29	В3
125	ПУИ	5,53	
126	Помещение временного хранения пищевых отходов	9,37	В4
127	Моечная столовой посуды	46,82	В4
128	Горячий цех	45,30	В3
129	Холодный цех	10,12	В3
130	Обеденный зал	393,12	
131	Лестничная клетка (тип Н2)	17,68	
133	Сан. узел для мальчиков	8,29	
134	Сан. узел для девочек	7,82	
135	Коридор	83,12	
137	Коридор	146,67	
138	Коридор	142,66	
139	Лестничная клетка (тип Л1)	17,22	
140	Административный кабинет Тип 1	15,42	
141	Учебный кабинет	57,61	
142	Сан. узел для девочек	14,13	
143	Сан. узел для мальчиков	16,91	
144	ПУИ	3,09	В4
145	Лестничная клетка (тип Л1)	17,14	
146	Гимнастический зал	93,81	
147	Раздевальные	8,17	
148	Раздевальные	7,30	
150	Кабинет для индивидуальных занятий, в т.ч. с коррекционным педагогом	21,01	
151	Помещение для прокладки инженерных коммуникаций	15,07	В3
152	Учебный кабинет	53,08	
153	Учебный кабинет	54,85	
154	Учебный кабинет	54,31	
155	Учебные кабинет для изучения естествознания: химия	55,07	
156	Лаборанстская кабинета химии	17,09	В3
157	Учебные кабинет для изучения естествознания: физика	54,43	
158	Лаборанстская кабинета физики	18,10	В3
159	Учебные кабинеты для изучения естествознания: биологии + ОБЗР	71,91	
160	Лаборанстская кабинета биологии	18,75	В3
161	Кабинет материальной технологии Тип 2	49,10	В3
162	Кабинет материальной технологии Тип 1	54,82	В3
163	Лестничная клетка (тип Л1)	17,22	
164	Сан. узел персонала	1,78	
165	Сан. узел для мальчиков	16,02	
166	Сан. узел для девочек с комнатой личной гигиены	14,73	
167	Серверная	17,09	В3
168	Кроссовая	5,03	В3
169	Кроссовая	4,92	В3
		2 558,98 м²	

Условные обозначения:

ПД1
– Подоконник керамогранитный Kerama Marazzi ПРО ЛАЙМСТОУН Серый светлый Материальный DD641029R. Размер 600x600x9;

ПД2
– Окраска негорючей акриловой матовой моющейся краской, цвет RAL9010, типа BRAVO

ПД3
– Подоконник керамогранитный Kerama Marazzi Фонтанелато Пепельный светлый обрезной DL600720R. Размер 1200x600ммx9мм;

ПД4
– Шпонированная березовая фанера не менее 24 мм с продуктами; Противопожарная обработка КМ1.

ПД4.1
– Шпонированная березовая фанера не менее 24 мм с продуктами; Противопожарная обработка КМ0.

ПД5
– Подоконник Kerama Marazzi Монфорте Белый матовый обрезной 14010R. Размер 1200x400ммx9мм

0,000=168,265

Изм.	Колуч.	Лист	№Док.	Подп.	Дата
Разработал		Белова Е.С.			09.25
Проверил		Дубинин С.В.			09.25
ГАП		Дубинин С.В.			09.25
ГИП		Гущин А.В.			
Н.контроль		Щукшин В.В.			09.25

ГИП-28/24-П-АР

ГБОУ Школа № 218, расположенная по адресу: г. Москва, ул. Вучетича, д. 6

Средняя общеобразовательная школа

Стадия	Лист	Листов
П	40	64

План подоконников 1 этажа на отм. 0,000

И-ГРУПП
ПРОЕКТНО-СТРОИТЕЛЬНАЯ КОМПАНИЯ

План подоконников 2 этажа на отм. +3.300
М 1:200

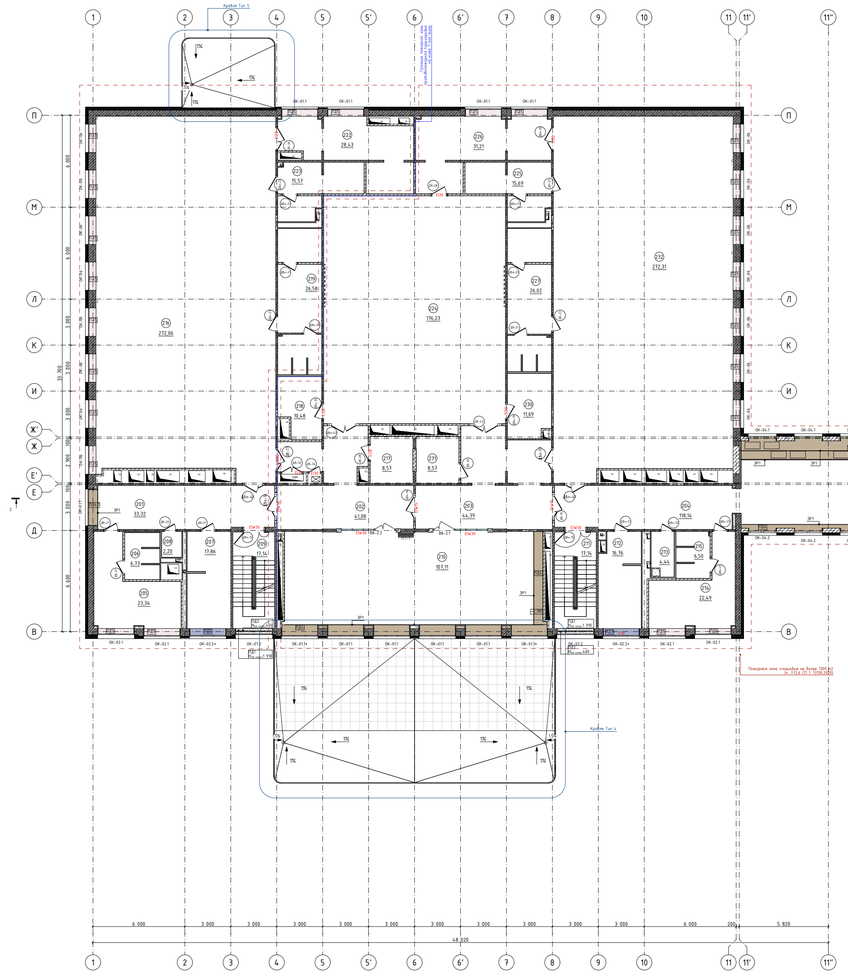

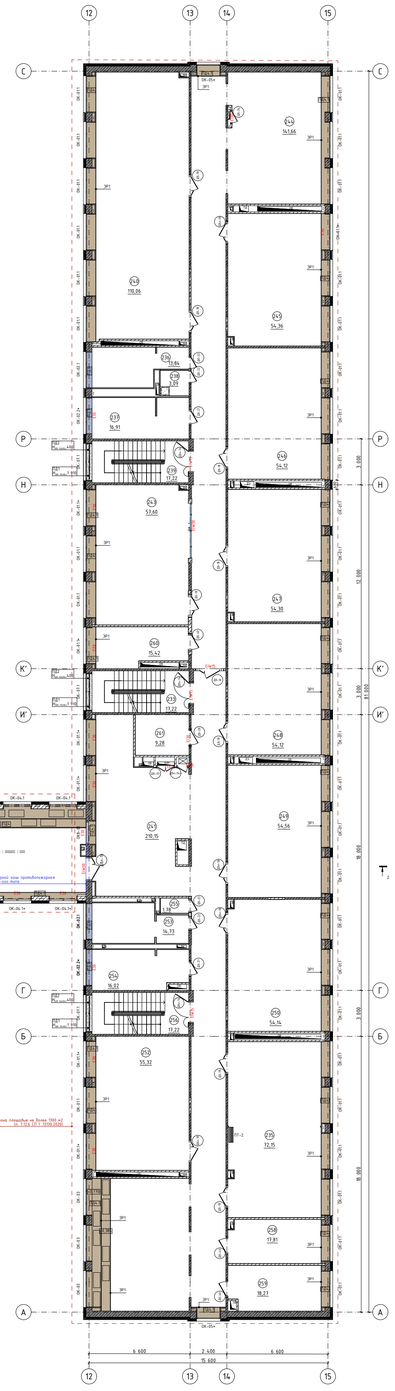

Экспликация помещений на отм. 3.300

№	Наименование	Площадь	Категория помещения
201	Коридор	33,32	
202	Коридор	41,08	
203	Коридор	44,39	
204	Коридор	118,14	
205	Раздевальная	23,34	
206	Душевая	6,73	
207	Сан. узел для девочек	17,86	
208	Сан. узел для персонала	2,20	
209	Лестничная клетка (тип Н2)	17,14	
210	Кабинет ИЗО	107,11	
211	Лестничная клетка (тип Н2)	17,14	
212	Сан. узел для мальчиков	16,76	
213	ПУИ	4,44	В4
214	Раздевальная	22,49	
215	Душевая	6,50	
216	Универсальный спортивный зал	272,06	
217	Кроссовая	8,57	В3
218	Артистическая с хранением костюмов	10,48	В3
219	Раздевальная	26,58	
222	Снарядная	28,43	В3
223	Комната инструктора с душем и сан. узлом	15,57	
224	Актовый зал	176,23	
225	Комната инструктора с душем и сан. узлом	15,69	
226	Снарядная	31,21	В3
227	Раздевальная	26,02	
230	Артистическая с хранением костюмов	11,69	В3
231	Кладовая инвентаря	8,57	В4
232	Универсальный спортивный зал	272,31	
233	Лестничная клетка (тип Л1)	17,22	
235	Кабинет иностранного языка	72,15	
236	Сан. узел для девочек	13,84	
237	Сан. узел для мальчиков	16,91	

№	Наименование	Площадь	Категория помещения
238	ПУИ	3,09	В4
239	Лестничная клетка (тип Л1)	17,22	
240	Кабинет естесствознания Тип 1	110,06	
241	Коридор	210,15	
243	Учебный кабинет	57,60	
244	Коридор	141,66	
245	Учебный кабинет	54,36	
246	Учебный кабинет	54,12	
247	Учебный кабинет	54,30	
248	Учебный кабинет	54,12	
249	Учебный кабинет	54,56	
250	Учебный кабинет	54,14	
252	Учебный кабинет	55,32	
253	Сан. узел для девочек	14,73	
254	Сан. узел для мальчиков	16,02	
255	Сан. узел для персонала	1,78	
256	Лестничная клетка (тип Л1)	17,22	
258	Кабинет для индивидуальных занятий, в т.ч. с учителем логопедом	17,81	
259	Административный кабинет Тип 1	18,27	
260	Административный кабинет Тип 1	15,42	
261	Кроссовая	9,28	В3
		2 533,40 м²	

Условные обозначения:

ПД1
– Подоконник керамогранитный Kerama Marazzi ПРО_ЛАЙМСТОУН Серый Светлый Натуральный DD641020R. Размер 600х600х9;

ПД2
– Окраска негорючей акриловой матовой моющейся краской, цвет RAL9010, типа BRAVO

ПД3
– Подоконник керамогранитный Kerama Marazzi Фонаменто Пепельный светлый обрезной DL600720R. Размер 1200х600ммх9мм;

ПД4
– Шпонированная березовая фанера не менее 24 мм с продухами; Противопожарная обработка КМ1.

ПД4.1
– Шпонированная березовая фанера не менее 24 мм с продухами; Противопожарная обработка КМ0.

ПД5
– Подоконник Kerama Marazzi Монфорте Белый матовый обрезной 14010R. Размер 1200х400ммх9мм

0,000=168,265

Изм.	Колуч.	Лист	№Док.	Подп.	Дата
Разработал		Белова Е.С.			09.25
Проверил		Дубинин С.В.			09.25
ГАП		Дубинин С.В.			09.25
ГИП		Гущин А.В.			
Н.контроль		Шукшин В.В.			09.25

ГИП-28/24-П-АР

ГБОУ Школа № 218, расположенная по адресу: г. Москва, ул. Вучетича, д. 6

Средняя общеобразовательная школа

Стадия	Лист	Листов
П	41	64

План подоконников 2 этажа на отм. +3.300

И-ГРУПП
ПРОЕКТНО-СТРОИТЕЛЬНАЯ КОМПАНИЯ

План подоконников 3 этажа на отм. +6.600
М 1:200

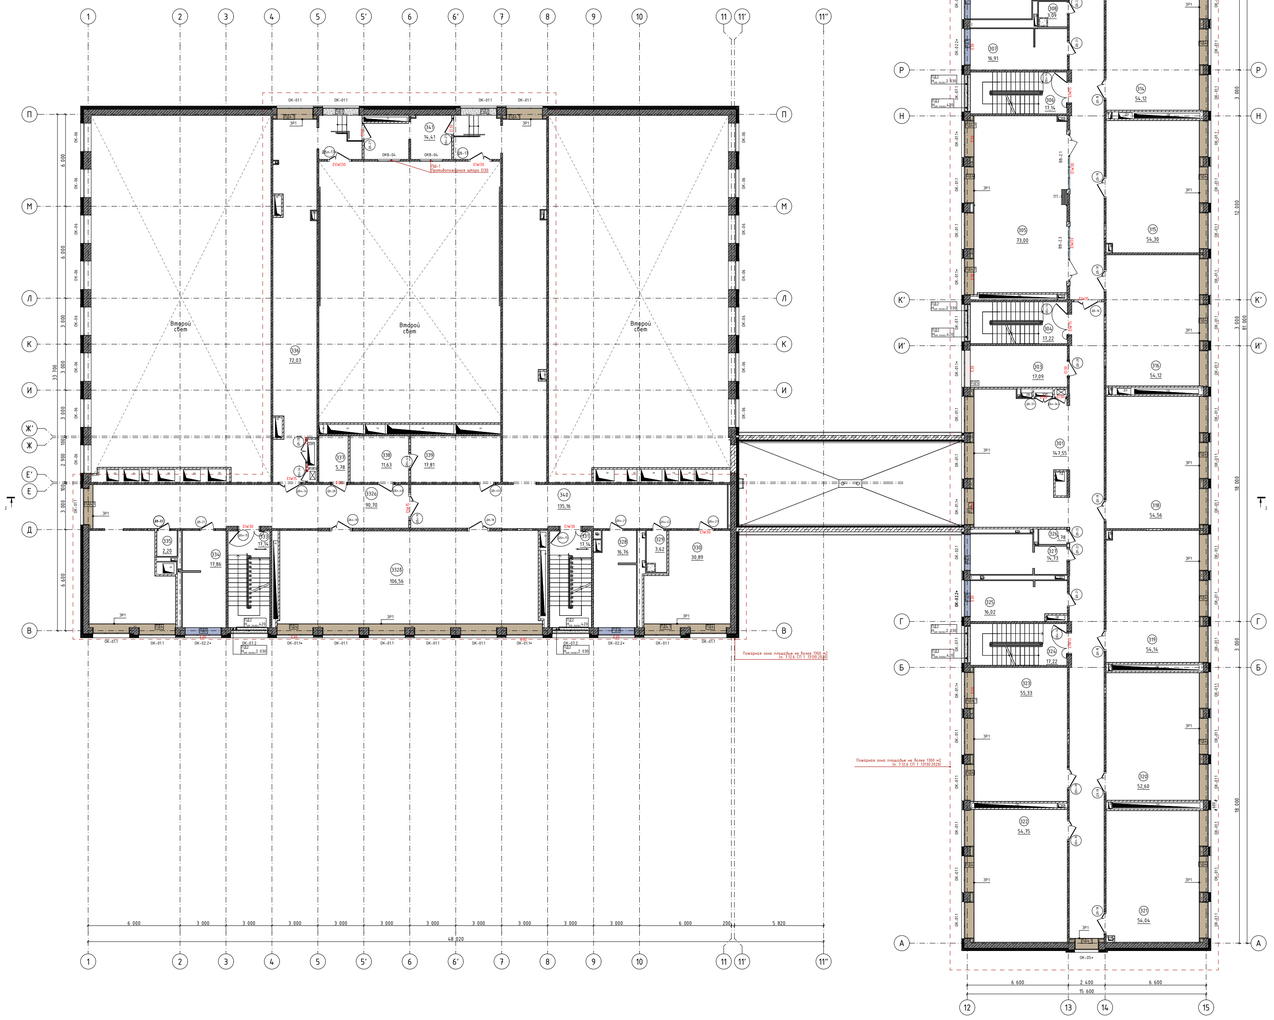

Экспликация помещений на отм. 6.600

№	Наименование	Площадь	Категория помещения
301	Коридор	147,55	
303	Серверная	17,09	В3
304	Лестничная клетка (тип Л1)	17,22	
305	Кабинет иностранного языка	73,00	
306	Лестничная клетка (тип Л1)	17,14	
307	Сан. узел для мальчиков	16,91	
308	ПУИ	3,09	В4
309	Сан. узел для девочек	13,85	
310	Учебный кабинет	53,90	
311	Учебный кабинет	55,39	
312	Коридор	142,37	
313	Учебный кабинет	54,36	
314	Учебный кабинет	54,12	
315	Учебный кабинет	54,30	
316	Учебный кабинет	54,12	
318	Учебный кабинет	54,56	
319	Учебный кабинет	54,14	
320	Учебный кабинет	52,60	
321	Учебный кабинет	54,04	
322	Учебный кабинет	54,75	
323	Учебный кабинет	55,33	
324	Лестничная клетка (тип Л1)	17,22	
325	Сан. узел для мальчиков	16,02	
326	Сан. узел персонала	1,78	
327	Сан. узел для девочек	14,73	
328	Сан. узел для мальчиков	16,76	
329	ПУИ	3,62	В4
330	Библиотека. Фонд хранения	30,89	В3
331	Лестничная клетка (тип Н2)	17,14	
332а	Коридор	90,70	
332б	Читальный зал	106,56	
333	Лестничная клетка (тип Н2)	17,14	
334	Сан. узел для девочек	17,86	
335	Сан. узел для персонала	2,20	
336	Коридор	72,03	
337	Кроссовая	5,78	В3
338	Кабинет для индивидуальных занятий. Студия звукозаписи	11,63	
339	Медиакласс	17,81	
340	Коридор	135,16	
341	Технический центр	14,41	В3
		1 709,27 м²	

Условные обозначения:

ПД1
– Подоконник керамогранитный Kerama Marazzi ПРО ЛАЙМСТОУН Серый Светлый Натуральный DD641020R. Размер 600х600х9;

ПД2
– Окраска негорючей акриловой матовой моющейся краской, цвет RAL9010, типа BRAVO

ПД3
– Подоконник керамогранитный Kerama Marazzi Фондаменто Пепельный светлый обрезной DL600720R. Размер 1200х600ммх9мм;

ПД4
– Шпонированная березовая фанера не менее 24 мм с прадуками; Противопожарная обработка КМ1.

ПД4.1
– Шпонированная березовая фанера не менее 24 мм с прадуками; Противопожарная обработка КМ0.

ПД5
– Подоконник Kerama Marazzi Монфорте Белый матовый обрезной 14010R. Размер 1200х400ммх9мм

0,000=168,265

Изм.	Колуч.	Лист	№Док.	Подп.	Дата	ГИП-28/24-П-АР			
						ГБОУ Школа № 218, расположенная по адресу: г. Москва, ул. Вучетича, д. 6			
Разработал		Белова Е.С.			09.25	Средняя общеобразовательная школа	Стадия	Лист	Листов
Проверил		Дубинин С.В.			09.25		П	42	64
ГАП		Дубинин С.В.			09.25				
ГИП		Гущин А.В.				План подоконников 3 этажа на отм. +6.600	И-ГРУПП ПРОЕКТНО-СТРОИТЕЛЬНАЯ КОМПАНИЯ		
Н.контроль		Шукшин В.В.			09.25				

План подоконников 4 этажа на отм. +9.900
М 1:200

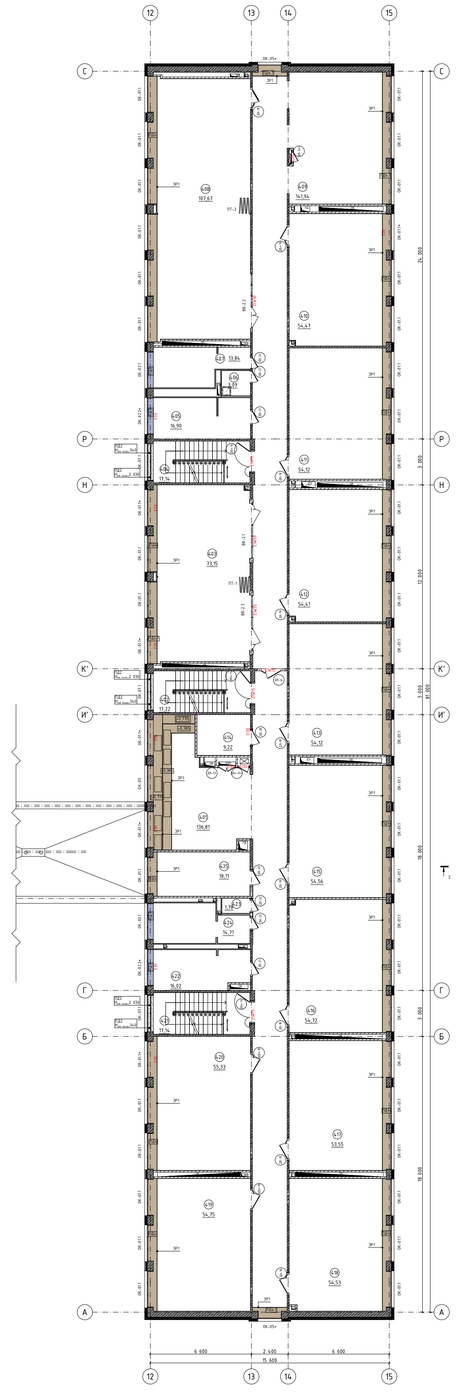

Экспликация помещений на отм. 9.900

№	Наименование	Площадь	Категория помещения
401	Коридор	136,81	
402	Лестничная клетка (тип Л1)	17,22	
403	Кабинет иностранного языка	73,15	
404	Лестничная клетка (тип Л1)	17,14	
405	Сан. узел для мальчиков	16,90	
406	ПУИ	3,09	В4
407	Сан. узел для девочек	13,84	
408	Кабинет информатики и информационных технологий	107,67	
409	Коридор	141,94	
410	Кабинет русского языка и литературы	54,47	
411	Кабинет русского языка и литературы	54,12	
412	Кабинет русского языка и литературы	54,41	
413	Кабинет математики	54,12	
414	Кроссовая	9,22	В3
415	Кабинет математики	54,56	
416	Кабинет истории Тип 1	54,72	
417	Кабинет географии	53,55	
418	Универсальный учебный кабинет	54,53	
419	Кабинет математики	54,75	
420	Кабинет истории Тип 1	55,33	
421	Лестничная клетка (тип Л1)	17,14	
422	Сан. узел для мальчиков	16,02	
423	Сан. узел персонала	1,78	
424	Сан. узел для девочек с комнатой личной гигиены	14,71	
425	Кабинет для индивидуальных занятий, в т.ч. с педагогом психологом	18,11	
		1 149,30 м²	

Условные обозначения:

ПД1
– Подоконник керамогранитный Kerama Marazzi ПРФ ЛАЙМСТОУН Серый Светлый Натуральный DD641020R. Размер 600х600х9;

ПД2
– Окраска негорючей акриловой матовой моющейся краской, цвет RAL9010, типа BRAVO

ПД3
– Подоконник керамогранитный Kerama Marazzi Фондаменто Пепельный светлый обрезной DL600720R. Размер 1200х600ммх9мм;

ПД4
– Шпонированная березовая фанера не менее 24 мм с пробуками; Противопожарная обработка КМ1.

ПД4.1
– Шпонированная березовая фанера не менее 24 мм с пробуками; Противопожарная обработка КМ0.

ПД5
– Подоконник Kerama Marazzi Монфорте Белый матовый обрезной 14010R. Размер 1200х400ммх9мм

0,000=168,265

Изм.	Колич.	Лист	№Док.	Подп.	Дата
Разработал		Белова Е.С.			09.25
Проверил		Дубинин С.В.			09.25
ГАП		Дубинин С.В.			09.25
ГИП		Гущин А.В.			
Н.контроль		Шукшин В.В.			09.25

ГИП-28/24-П-АР

ГБОУ Школа № 218, расположенная по адресу:
г. Москва, ул. Вучетича, д. 6

Средняя общеобразовательная школа

Стадия	Лист	Листов
П	43	64

План подоконников 4 этажа на отм. +9.900

И-ГРУПП
ПРОЕКТНО-СТРОИТЕЛЬНАЯ КОМПАНИЯ

План подвального этажа
М 1:200

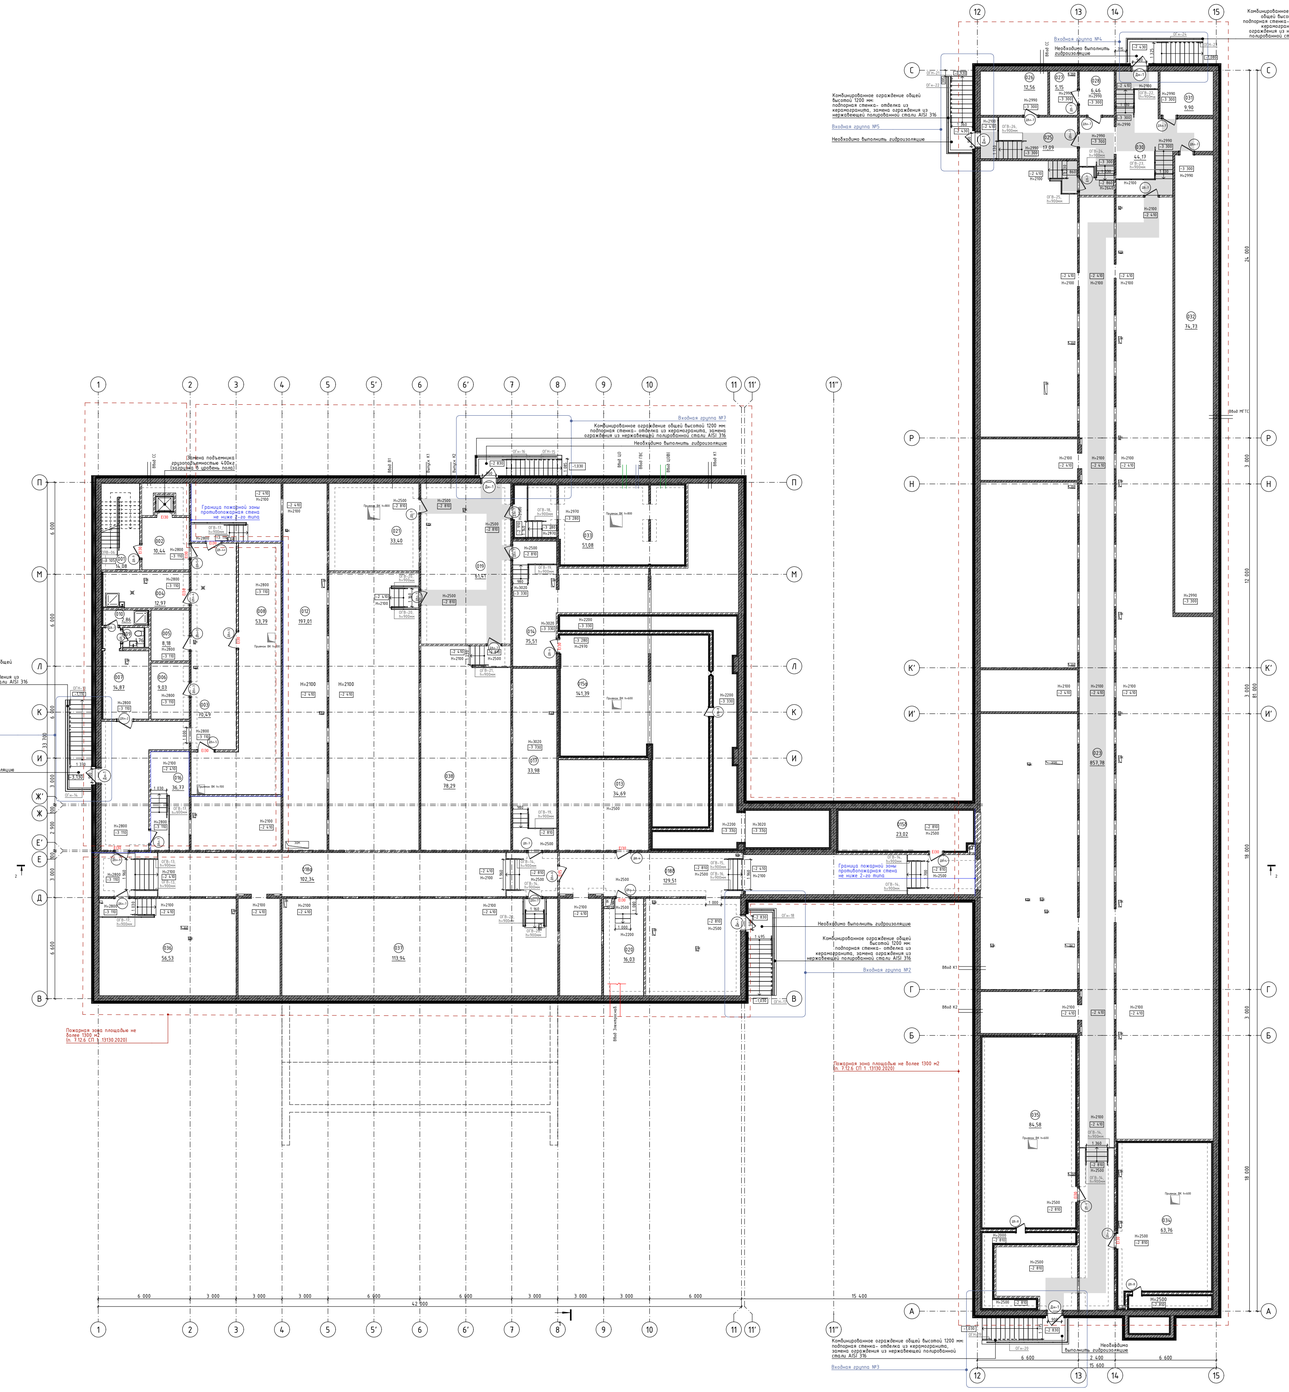

Экспликация помещений на отм. -3.000

№	Наименование	Площадь	Категория помещения
001	Лестничная клетка технологическая (для персонала)	14,08	
002	Тамбур-шлюз 1-го типа	10,44	
003	Коридор	70,49	
004	ПУИ	12,97	В3
005	Кладовая овощей	8,18	В4
006	Кладовая сухих продуктов	9,03	В4
007	Помещение персонала (не более 5 чел.)	14,87	
008	Помещение для установки холодильных камер	53,79	В3
009	Сан. узел	1,76	
010	Душевая	2,86	
012	Техническое помещение (для прокладки инженерных коммуникаций)	197,01	В4
013	Электрощитовая	34,69	В3
014	Техническое помещение (для прокладки инженерных коммуникаций)	75,51	В4
015а	Венткамера	141,39	В4
015б	Венткамера	23,02	В4
016	Техническое помещение (для прокладки инженерных коммуникаций)	36,77	В4
017	Техническое помещение (для прокладки инженерных коммуникаций)	33,98	В4
018а	Коридор	102,34	
018б	Коридор	129,51	
019	Коридор	61,41	
020	Электрощитовая	16,03	В3
021	Водомерный узел	33,40	Д
023	Техническое помещение (для прокладки инженерных коммуникаций)	857,78	В4
025	Коридор	17,09	
026	Техническое помещение (для прокладки инженерных коммуникаций)	12,56	В4
027	Техническое помещение (для прокладки инженерных коммуникаций)	5,15	В4
028	Техническое помещение (для прокладки инженерных коммуникаций)	6,46	В4
030	Коридор	44,17	
031	Техническое помещение (для прокладки инженерных коммуникаций)	9,90	В4
032	Техническое помещение (для прокладки инженерных коммуникаций)	74,73	В4
033	ИТП	51,08	В4
034	Венткамера	63,76	В4
035	Венткамера	84,58	В4
036	Техническое помещение (для прокладки инженерных коммуникаций)	56,53	В4
037	Техническое помещение (для прокладки инженерных коммуникаций)	113,94	В4
038	Техническое помещение (для прокладки инженерных коммуникаций)	78,29	В4
36		2 559,55 м²	

0,000=168,265

Изм.	Колич.	Лист	№Док.	Подп.	Дата
Разработал		Белова Е.С.			09.25
Проверил		Дубинин С.В.			09.25
ГАП		Дубинин С.В.			09.25
ГИП		Гущин А.В.			
Н.контроль		Шукшин В.В.			09.25

ГИП-28/24-П-АР

ГБОУ Школа № 218, расположенная по адресу: г. Москва, ул. Вучетича, д. 6

Средняя общеобразовательная школа

Стадия	Лист	Листов
П	44	64

План подвального этажа

И-ГРУПП
ПРОЕКТНО-СТРОИТЕЛЬНАЯ КОМПАНИЯ

План 1 этажа на отм. 0,000
М 1:200

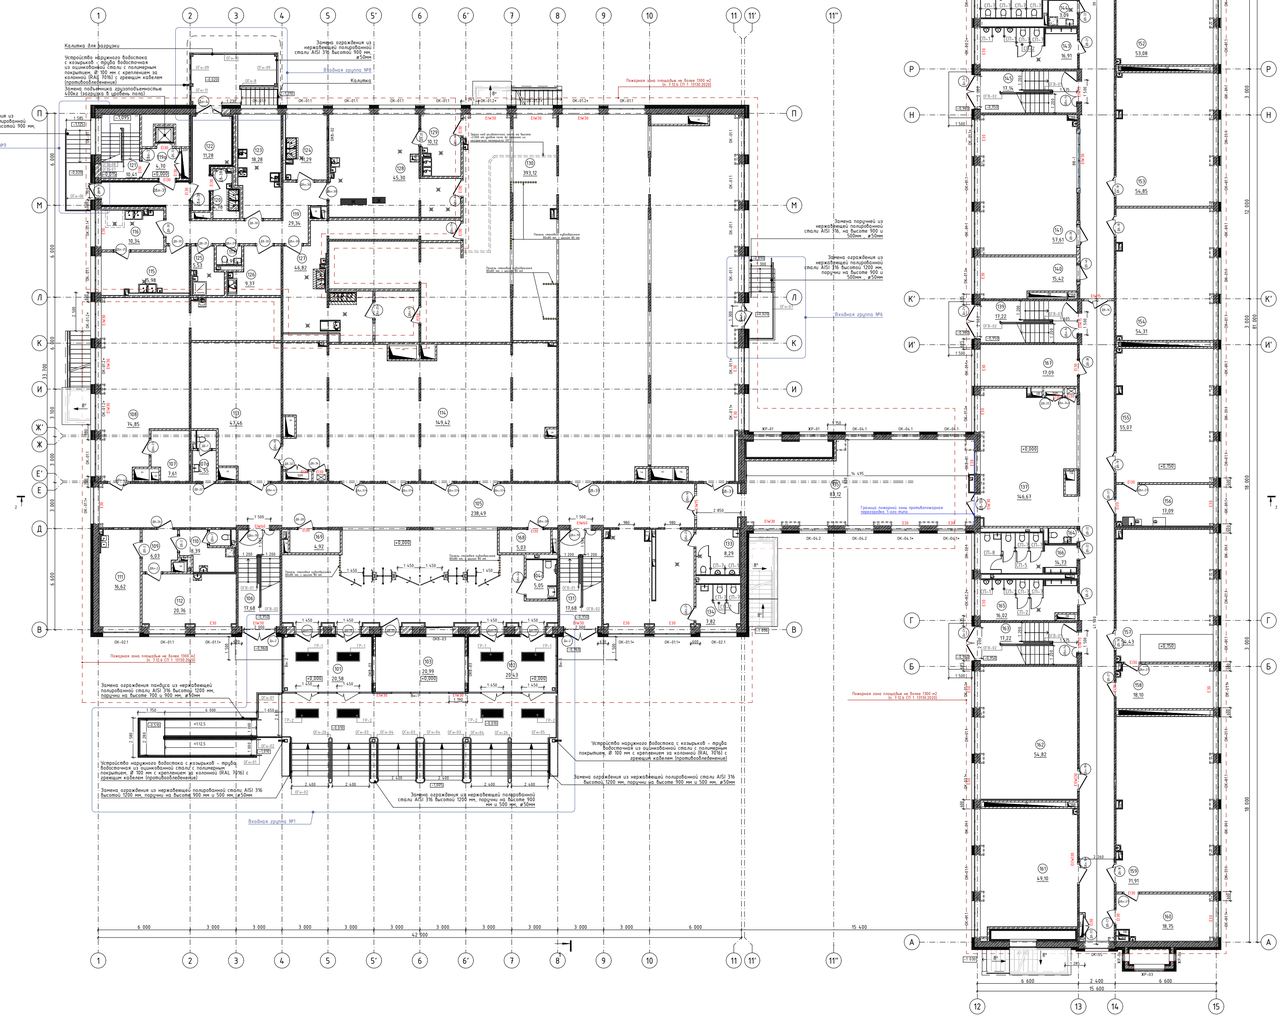
Ограждение кровли из нержавеющей полуфабрикатной стали AISI 316 высотой 900 мм, ø50мм
Ограждение кровли из нержавеющей полуфабрикатной стали AISI 316 высотой 1200 мм, ø50мм
Козырек над входом из Алюм 1200 мл
Пожарная зона площадью не более 1200 м2
Ограждение кровли из нержавеющей полуфабрикатной стали AISI 316 высотой 900 мм, ø50мм
Ограждение кровли из нержавеющей полуфабрикатной стали AISI 316 высотой 1200 мм, ø50мм
Козырек над входом из Алюм 1200 мл
Пожарная зона площадью не более 1200 м2
Ограждение кровли из нержавеющей полуфабрикатной стали AISI 316 высотой 1200 мм, ø50мм
Ограждение кровли из нержавеющей полуфабрикатной стали AISI 316 высотой 900 мм, ø50мм
Ограждение кровли из нержавеющей полуфабрикатной стали AISI 316 высотой 1200

План 2 этажа на отм. +3.300
М 1:200

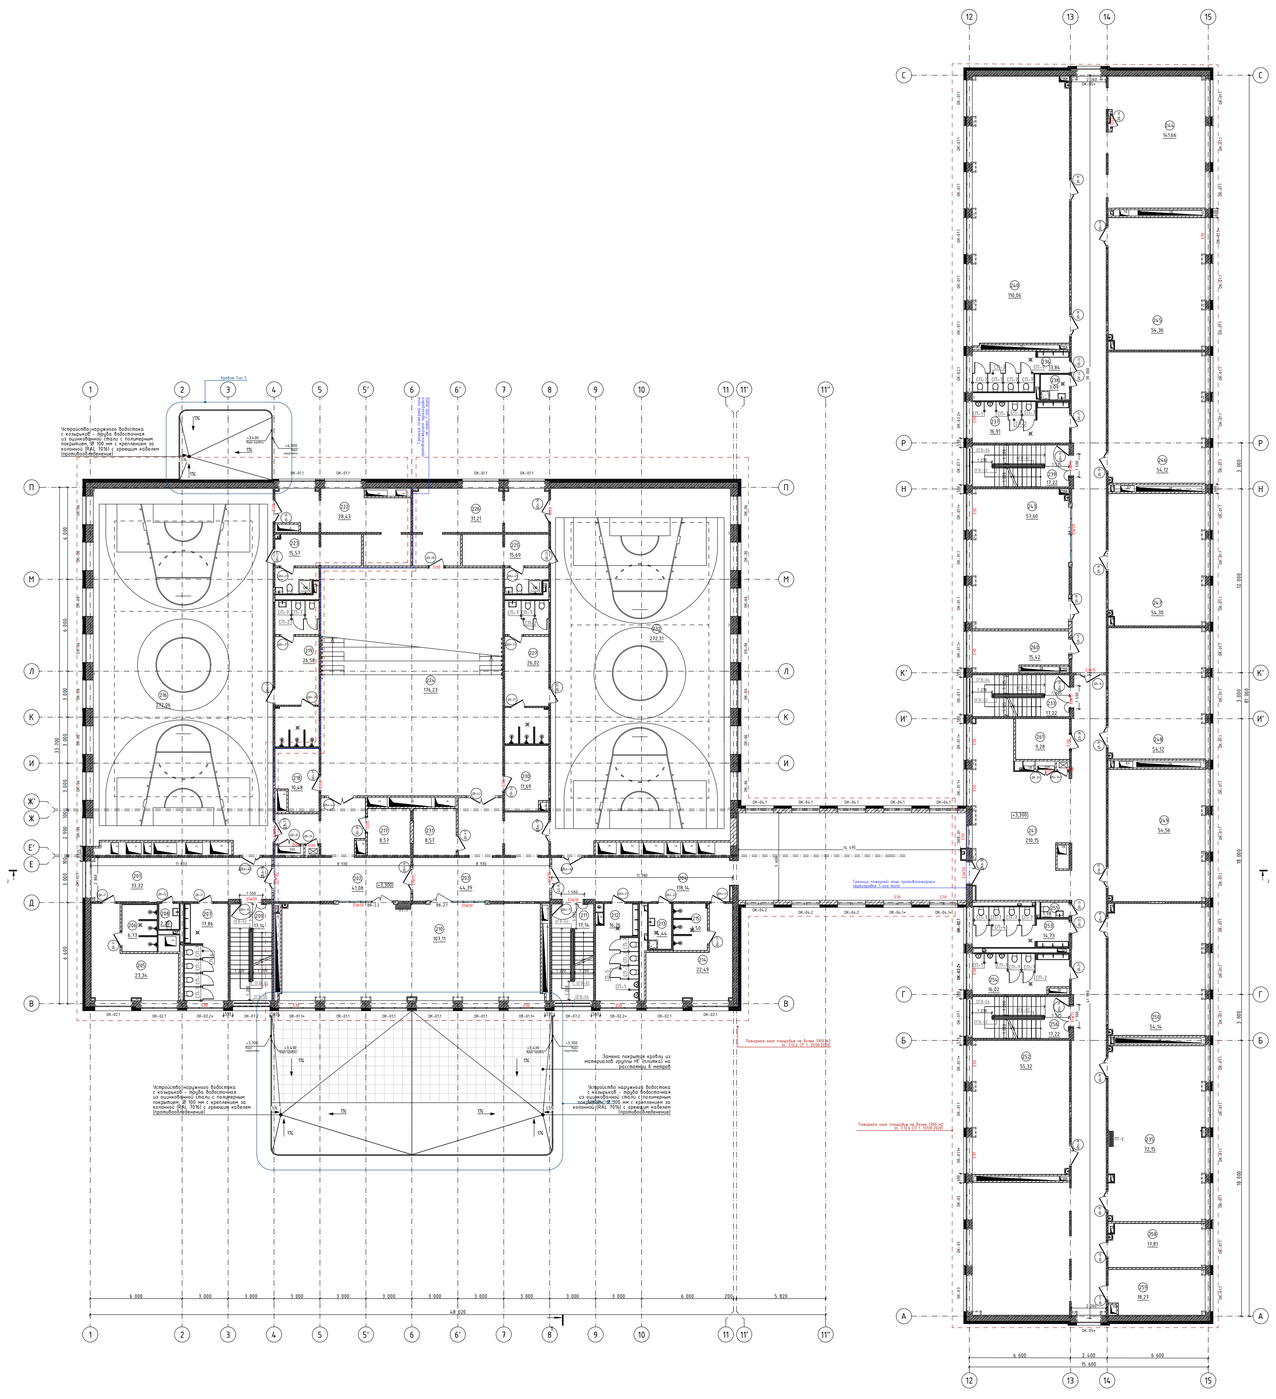
Устройство наружного водостока с козырьком - труба водосточная из оцинкованной стали с полимерным покрытием Ø90, RAL 7024 с кронштейном на планке-держателе, длина кронштейна 450 мм, RAL 7024 с крепежом на горизонтальной поверхности
Устройство наружного водостока с козырьком - труба водосточная из оцинкованной стали с полимерным покрытием Ø90, RAL 7024 с кронштейном на планке-держателе, длина кронштейна 450 мм, RAL 7024 с крепежом на горизонтальной поверхности
Замена покрытия кровли из материалов группы НГ (плитка) на рулонные, h материала 6 мм
Граница покрытия зоны пребывания маломобильных групп населения
Пожарная зона открытая на Кровле (ПЗО) №1 S=1 153,57 ГОСТ 31937-2011
Пожарная зона открытая на Кровле (ПЗО) №2 S=1 153,57 ГОСТ 31937-2011
Кровля Тип 3
Граница покрытия зоны пребывания маломобильных групп населения
Граница покрытия зоны пребывания маломобильных групп населения
Граница покрытия зоны пребывания маломобильных групп населения

План 3 этажа на отм. +6.600
М 1:200

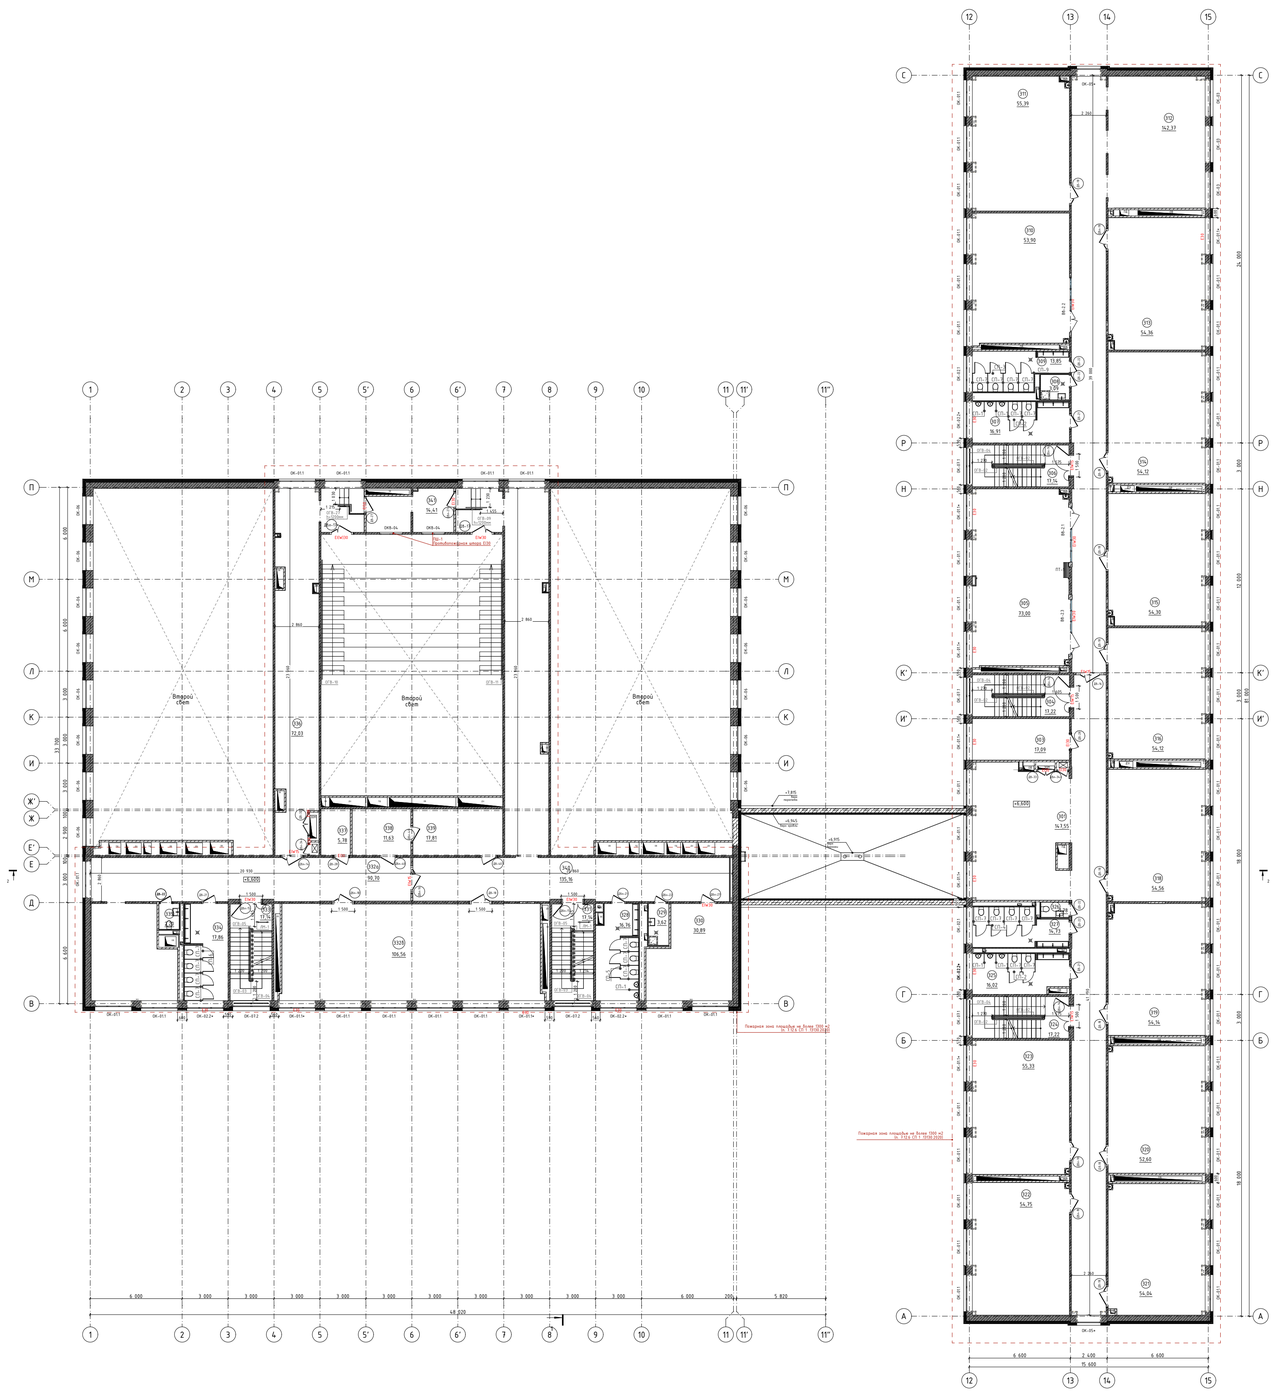

Экспликация помещений на отм. 6.600

№	Наименование	Площадь	Категория помещения
301	Коридор	147,55	
303	Серверная	17,09	В3
304	Лестничная клетка (тип Л1)	17,22	
305	Кабинет иностранного языка	73,00	
306	Лестничная клетка (тип Л1)	17,14	
307	Сан. узел для мальчиков	16,91	
308	ПУИ	3,09	В4
309	Сан. узел для девочек	13,85	
310	Учебный кабинет	53,90	
311	Учебный кабинет	55,39	
312	Коридор	142,37	
313	Учебный кабинет	54,36	
314	Учебный кабинет	54,12	
315	Учебный кабинет	54,30	
316	Учебный кабинет	54,12	
318	Учебный кабинет	54,56	
319	Учебный кабинет	54,14	
320	Учебный кабинет	52,60	
321	Учебный кабинет	54,04	
322	Учебный кабинет	54,75	
323	Учебный кабинет	55,33	
324	Лестничная клетка (тип Л1)	17,22	
325	Сан. узел для мальчиков	16,02	
326	Сан. узел персонала	1,78	
327	Сан. узел для девочек	14,73	
328	Сан. узел для мальчиков	16,76	
329	ПУИ	3,62	В4
330	Библиотека. Фонд хранения	30,89	В3
331	Лестничная клетка (тип Н2)	17,14	
332а	Коридор	90,70	
332б	Читальный зал	106,56	
333	Лестничная клетка (тип Н2)	17,14	

№	Наименование	Площадь	Категория помещения
334	Сан. узел для девочек	17,86	
335	Сан. узел для персонала	2,20	
336	Коридор	72,03	
337	Кроссовая	5,78	В3
338	Кабинет для индивидуальных занятий. Студия звукозаписи	11,63	
339	Медиакласс	17,81	
340	Коридор	135,16	
341	Технический центр	14,41	В3
		1 709,27 м²	

Условные обозначения

- сущ. стена
- сущ. перегородка
- перегородка: штукатурка, кирпич полнотелый, штукатурка
- ДВ-1 – марка двери/окна
- 001 – марка помещения

0,000=168,265

Изм.	Колуч.	Лист	№Док.	Подп.	Дата
Разработал		Белова Е.С.			09.25
Проверил		Дубинин С.В.			09.25
ГАП		Дубинин С.В.			09.25
ГИП		Гущин А.В.			
Н.контроль		Шукшин В.В.			09.25

ГИП-28/24-П-АР

ГБОУ Школа № 218, расположенная по адресу: г. Москва, ул. Вучетича, д. 6

Средняя общеобразовательная школа

Стадия	Лист	Листов
П	47	64

План 3 этажа на отм. +6.600

И-ГРУПП
ПРОЕКТНО-СТРОИТЕЛЬНАЯ КОМПАНИЯ

План 4 этажа на отм. +9.900
М 1:200

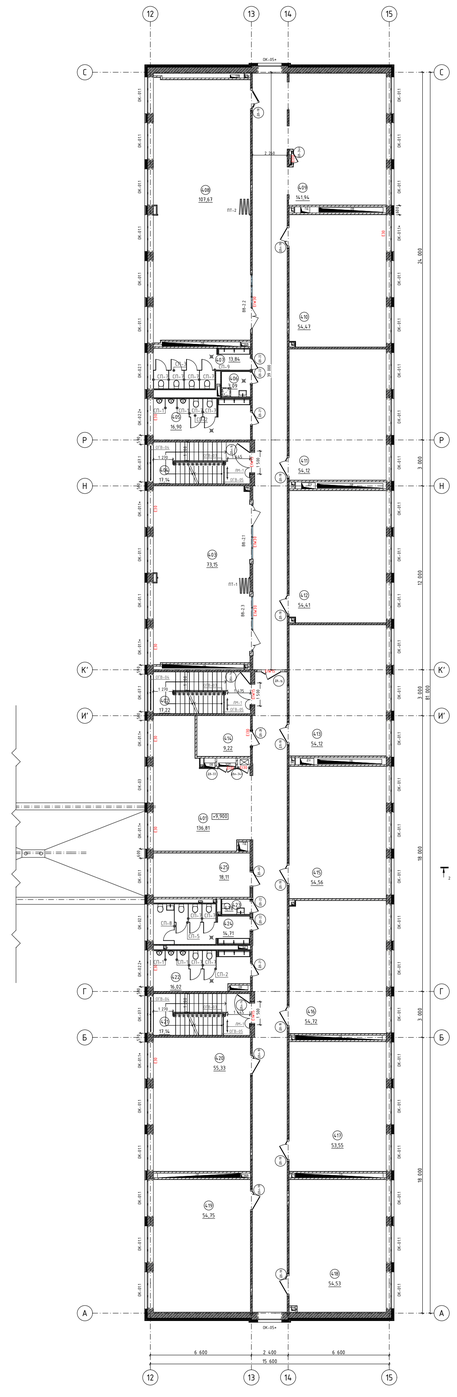

Условные обозначения

- суш. стена
- суш. перегородка
- перегородка: штукатурка, кирпич полнотелый, штукатурка
- 28-1 – марка двери/окна
- 001 – марка помещения

Экспликация помещений на отм. 9.900

№	Наименование	Площадь	Категория помещения
401	Коридор	136,81	
402	Лестничная клетка (тип Л1)	17,22	
403	Кабинет иностранного языка	73,15	
404	Лестничная клетка (тип Л1)	17,14	
405	Сан. узел для мальчиков	16,90	
406	ПУИ	3,09	В4
407	Сан. узел для девочек	13,84	
408	Кабинет информатики и информационных технологий	107,67	
409	Коридор	141,94	
410	Кабинет русского языка и литературы	54,47	
411	Кабинет русского языка и литературы	54,12	
412	Кабинет русского языка и литературы	54,41	
413	Кабинет математики	54,12	
414	Кроссовая	9,22	В3
415	Кабинет математики	54,56	
416	Кабинет истории Тип 1	54,72	
417	Кабинет географии	53,55	
418	Универсальный учебный кабинет	54,53	
419	Кабинет математики	54,75	
420	Кабинет истории Тип 1	55,33	
421	Лестничная клетка (тип Л1)	17,14	
422	Сан. узел для мальчиков	16,02	
423	Сан. узел персонала	1,78	
424	Сан. узел для девочек с комнатой личной гигиены	14,71	
425	Кабинет для индивидуальных занятий, в т.ч. с педагогом психологом	18,11	
		1 149,30 м²	

0,000=168,265

						ГИП-28/24-П-АР
						ГБОУ Школа № 218, расположенная по адресу: г. Москва, ул. Вучетича, д. 6
Изм.	Колуч.	Лист	№Док.	Подп.	Дата	
Разработал		Белова Е.С.			09.25	Средняя общеобразовательная школа
Проверил		Дубинин С.В.			09.25	
ГАП		Дубинин С.В.			09.25	
ГИП		Гущин А.В.				План 4 этажа на отм. +9.900
Н.контроль		Шукшин В.В.			09.25	

Стадия	Лист	Листов
П	48	64

И-ГРУПП
ПРОЕКТНО-СТРОИТЕЛЬНАЯ КОМПАНИЯ

Ведомость отделки подвала
М 1:200

№ пом.	Название Зоны	Стены, Тип-1	Стены, Тип-1, м2	Стены, Тип-2	Стены, Тип-2, м2
001	Лестничная клетка технологическая (для персонала)	2.2.1 Окраска стен Производитель: BRAVO Class Profi FW-55/NEOLAIN SATIN RAL 9010	43,64	-	0,00
002	Тамбур-шлюз 1-го типа	2.11 Плитка керамическая Размер: 200x200 мм Производитель: Kerama Marazzi КАЛЕЙДОСКОП БЕЛЫЙ МАТОВЫЙ 5009*	28,82	-	0,00
003	Коридор	2.11 Плитка керамическая Размер: 200x200 мм Производитель: Kerama Marazzi КАЛЕЙДОСКОП БЕЛЫЙ МАТОВЫЙ 5009*	148,10	-	0,00
004	ПУИ	2.6 Керамогранит крупноформатный Размер: 600x600 мм Производитель: Kerama Marazzi Фонфаменто пепельный светлый обрезной Артикул: DL600720R	41,03	-	0,00
005	Кладовая овощей	2.11 Плитка керамическая Размер: 200x200 мм Производитель: Kerama Marazzi КАЛЕЙДОСКОП БЕЛЫЙ МАТОВЫЙ 5009*	28,97	-	0,00
006	Кладовая сухих продуктов	2.11 Плитка керамическая Размер: 200x200 мм Производитель: Kerama Marazzi КАЛЕЙДОСКОП БЕЛЫЙ МАТОВЫЙ 5009*	30,99	-	0,00
007	Помещение персонала	2.11 Плитка керамическая Размер: 200x200 мм Производитель: Kerama Marazzi КАЛЕЙДОСКОП БЕЛЫЙ МАТОВЫЙ 5009*	46,82	-	0,00
008	Помещение для установки холодильных камер	2.11 Плитка керамическая Размер: 200x200 мм Производитель: Kerama Marazzi КАЛЕЙДОСКОП БЕЛЫЙ МАТОВЫЙ 5009*	106,13	-	0,00
009	Сан. узел	2.7 Керамогранит крупноформатный Размер: 600x600 мм Производитель: Kerama Marazzi Про Стоун серый светлый обрезной Артикул: DD503820R	9,67	2.17 Плитка керамическая Размер: 200x800 мм Производитель: Kerama Marazzi Клин Вуд бежевый SG705790R	3,86
010	Душевая	2.7 Керамогранит крупноформатный Размер: 600x600 мм Производитель: Kerama Marazzi Про Стоун серый светлый обрезной Артикул: DD503820R	20,03	-	0,00
012	Техническое помещение (для прокладки инженерных коммуникаций)	Обеспыливание	206,49	-	0,00
013	Электрощитовая	2.2.1 Окраска стен Производитель: BRAVO Class Profi FW-55/NEOLAIN SATIN RAL 9010	69,63	-	0,00
014	Техническое помещение (для прокладки инженерных коммуникаций)	Обеспыливание	182,80	-	0,00
015а	Венткамера	2.2.1 Окраска стен Производитель: BRAVO Class Profi FW-55/NEOLAIN SATIN RAL 9010	211,90	Обеспыливание	166,65

№ пом.	Название Зоны	Стены, Тип-1	Стены, Тип-1, м2	Стены, Тип-2	Стены, Тип-2, м2
015б	Венткамера	Обеспыливание	50,82	-	0,00
016	Техническое помещение (для прокладки инженерных коммуникаций)	Обеспыливание	51,36	-	0,00
017	Техническое помещение (для прокладки инженерных коммуникаций)	Обеспыливание	39,90	-	0,00
018	Коридор	Обеспыливание	242,25	-	0,00
018б	Коридор	Обеспыливание	294,95	-	0,00
019	Коридор	Обеспыливание	46,62	-	0,00
020	Электрощитовая	2.2.1 Окраска стен Производитель: BRAVO Class Profi FW-55/NEOLAIN SATIN RAL 9010	42,47	-	0,00
021	Водомерный узел	2.2.1 Окраска стен Производитель: BRAVO Class Profi FW-55/NEOLAIN SATIN RAL 9010	51,70	-	0,00
023	Техническое помещение (для прокладки инженерных коммуникаций)	-	1344,45	-	0,00
025	Коридор	Обеспыливание	39,25	-	0,00
026	Техническое помещение (для прокладки инженерных коммуникаций)	Обеспыливание	28,48	-	0,00
027	Техническое помещение (для прокладки инженерных коммуникаций)	Обеспыливание	17,61	-	0,00
028	Техническое помещение (для прокладки инженерных коммуникаций)	Обеспыливание	17,57	-	0,00
030	Коридор	Обеспыливание	86,81	-	0,00

№ пом.	Название Зоны	Стены, Тип-1	Стены, Тип-1, м2	Стены, Тип-2	Стены, Тип-2, м2
031	Техническое помещение (для прокладки инженерных коммуникаций)	Обеспыливание	24,58	-	0,00
032	Техническое помещение (для прокладки инженерных коммуникаций)	Обеспыливание	191,73	-	0,00
033	ИТП	2.2.1 Окраска стен Производитель: BRAVO Class Profi FW-55/NEOLAIN SATIN RAL 9010	129,74	-	0,00
034	Венткамера	2.2.1 Окраска стен Производитель: BRAVO Class Profi FW-55/NEOLAIN SATIN RAL 9010	82,50	Обеспыливание	30,90
035	Венткамера	2.2.1 Окраска стен Производитель: BRAVO Class Profi FW-55/NEOLAIN SATIN RAL 9010	105,26	Обеспыливание	55,44
036	Техническое помещение (для прокладки инженерных коммуникаций)	Обеспыливание	61,05	-	0,00
037	Техническое помещение (для прокладки инженерных коммуникаций)	Обеспыливание	94,14	-	0,00
038	Техническое помещение (для прокладки инженерных коммуникаций)	Обеспыливание	81,69	-	0,00

Примечание:
Согласно табл. 7.4 СП 71.13330.2017 подготовительный слой отделки вертикальных и горизонтальных поверхностей в помещениях следует принять как :
1. Улучшенная штукатурка применяется в технических помещениях и помещениях пищеблока (кроме помещений, где предусмотрено обеспыливание и помещения, где отделка не предусмотрена);
2. Высококачественная штукатурка применяется во всех помещениях с предыванием детей.

0,000=168,265

ГИП-28/24-П-АР

ГБОУ Школа № 218, расположенная по адресу:
г. Москва, ул. Вучетича, д. 6

Изм.	Колуч.	Лист	№Док.	Подп.	Дата
Разработал		Белова Е.С.			09.25
Проверил		Дубинин С.В.			09.25
ГАП		Дубинин С.В.			09.25
ГИП		Гущин А.В.			
Н.контроль		Шукшин В.В.			09.25

Средняя общеобразовательная школа

Стадия	Лист	Листов
П	49	64

Ведомость отделки подвала

И-ГРУПП
ПРОЕКТНО-СТРОИТЕЛЬНАЯ КОМПАНИЯ

Ведомость отделки 1 этажа

№ пом.	Название Зоны	Запотолочное пр-во,стены	Запотолочное пр-во,стены,м2	Стены, Тип-1	Стены, Тип-1, м2	Стены, Тип-2	Стены, Тип-2, м2	Стены, Тип-3	Стены, Тип-3, м2	Стены, Тип-4	Стены, Тип-4, м2	Стены, Тип-5	Стены, Тип-5, м2	Тип плинтуса	Плинтус, м.п. (Р пом.)
101	Тамбур	Негорючая краска КМ0 Bravo decor Class profi НГ W-200* RAL 9011	5,85	2.2.1 Окраска стен Производитель: BRAVO Class Profi FW-55/NEOLAIN SATIN RAL 9010	10,32	2.5. Бетонная плитка под кирпич Размер: 205x60x18 Производитель: BRICK WALL Артикул: Bremen BR-001	7,89	-	18,97	-	0,00	-	0,00	Плинтус керамогранитный завальцованный Kerama Marazzi Про Стоун Светлый Серый обрезной DD200320R/3BT*	13,61
102	Тамбур	Негорючая краска КМ0 Bravo decor Class profi НГ W-200* RAL 9011	5,85	2.2.1 Окраска стен Производитель: BRAVO Class Profi FW-55/NEOLAIN SATIN RAL 9010	10,33	2.5. Бетонная плитка под кирпич Размер: 205x60x18 Производитель: BRICK WALL Артикул: Bremen BR-001	7,89	-	18,97	-	0,00	-	0,00	Плинтус керамогранитный завальцованный Kerama Marazzi Про Стоун Светлый Серый обрезной DD200320R/3BT*	13,61
103	Комната охраны с диспетчерским пунктом	-	0,00	2.2.1 Окраска стен Производитель: BRAVO Class Profi FW-55/NEOLAIN SATIN RAL 9010	21,83	2.5. Бетонная плитка под кирпич Размер: 205x60x18 Производитель: BRICK WALL Артикул: Bremen BR-001	11,20	-	18,50	-	0,00	-	0,00	Плинтус гибкий ПВХ Первый профильный завод PL100SD* RAL 9004	18,07
104а	Сан. узел МГН	Негорючая краска КМ0 Bravo decor Class profi НГ W-200* RAL 9011	2,70	2.6 Керамогранит крупноформатный Размер: 600x600 мм Производитель: Kerama Marazzi Фондаменто пепельный светлый обрезной Артикул: DL600720R	17,25	2.17 Плитка керамическая Размер: 200x800 мм Производитель: Kerama Marazzi Клин Вуд бежевый SG705790R	4,84	-	0,00	-	0,00	-	0,00	-	8,01
105	Вестибюль	Негорючая краска КМ0 Bravo decor Class profi НГ W-200* RAL 9005	46,26	2.2.1 Окраска стен Производитель: BRAVO Class Profi FW-55/NEOLAIN SATIN RAL 9010	178,29	2.5. Бетонная плитка под кирпич Размер: 205x60x18 Производитель: BRICK WALL Артикул: Bremen BR-001	60,85	2.1.9 Окраска стен (акцентная) Bravo Class Profi FW-55/NEOLAIN SATIN RAL 230 70 20	9,74	2.10 Плитка керамическая Размер: 285x85 мм Производитель: Kerama Marazzi Аккорд белый грань глянцевый 8,5x28,5 RAL 9010	97,73	-	0,00	Плинтус керамогранитный завальцованный Kerama Marazzi Фондаменто Пепельный Светлый обрезной DD500720R/6BT*	124,01
106	Лестничная клетка (тип Н2)	-	0,00	2.3 Окраска стен Производитель: BRAVO Class Profi W-200 НГ RAL 9010	23,50	2.4.1 Окраска антивандальной краской лестничных клеток и в зоне поручня Производитель: BRAVO Class Profi W-200 НГ RAL 200 80 25	24,30	-	0,00	-	0,00	-	0,00	Плинтус керамогранитный для /К Kerama Marazzi Про Лаймстоун Светлый Серый натуральный DD205320R/3BT*	14,89
107	Гардеробная комната (для учителей)	-	0,00	2.2.1 Окраска стен Производитель: BRAVO Class Profi FW-55/NEOLAIN SATIN RAL 9010	25,33	2.1.6 Окраска стен (акцентная) Bravo Class Profi FW-55/NEOLAIN SATIN RAL 000 85 00	7,40	-	0,00	-	0,00	-	0,00	Плинтус гибкий ПВХ Первый профильный завод PL100SD* RAL 9004	10,68
107а	Сан. узел для персонала	Негорючая краска КМ0 Bravo decor Class profi НГ W-200* RAL 9011	3,12	2.7 Керамогранит крупноформатный Размер: 600x600 мм Производитель: Kerama Marazzi Про Стоун серый светлый обрезной Артикул: DD503820R	23,21	2.17 Плитка керамическая Размер: 200x800 мм Производитель: Kerama Marazzi Клин Вуд бежевый SG705790R	3,09	-	0,00	-	0,00	-	0,00	-	9,60
108	Кабинет с рабочим пространством для учителей Тип 2	Обеспыливание	15,35	2.2.1 Окраска стен Производитель: BRAVO Class Profi FW-55/NEOLAIN SATIN RAL 9010	82,12	2.1.8 Окраска стен (акцентная) Bravo Class Profi FW-55/NEOLAIN SATIN RAL 210 50 40	30,20	2.10 Плитка керамическая Размер: 285x85 мм Производитель: Kerama Marazzi Аккорд белый грань глянцевый 8,5x28,5 RAL 9010	5,44	-	0,00	-	0,00	Плинтус гибкий ПВХ Первый профильный завод PL100SD* RAL 9004	50,27
109	Коридор медблока	-	0,00	2.2.1 Окраска стен Производитель: BRAVO Class Profi FW-55/NEOLAIN SATIN RAL 9010	22,70	-	0,00	-	0,00	-	0,00	-	0,00	Плинтус керамогранитный завальцованный Kerama Marazzi Фондаменто Пепельный Светлый обрезной DD500720R/6BT*	6,52
110	Туалет медблока с местом для приготовления дезинфицирующих средств и хранения уборочного инвентаря	Обеспыливание	4,82	2.11 Плитка керамическая Размер: 200x200 мм Производитель: Kerama Marazzi КАЛЕЙДОСКОП БЕЛЫЙ МАТОВЫЙ 5009*	28,38	2.17 Плитка керамическая Размер: 200x800 мм Производитель: Kerama Marazzi Клин Вуд бежевый SG705790R	2,69	2.7 Керамогранит крупноформатный Размер: 600x600 мм Производитель: Kerama Marazzi Про Стоун серый светлый обрезной Артикул: DD503820R	10,24	-	0,00	-	0,00	-	15,16
111	Процедурный (прививочный) кабинет	Обеспыливание	5,39	2.11 Плитка керамическая Размер: 200x200 мм Производитель: Kerama Marazzi КАЛЕЙДОСКОП БЕЛЫЙ МАТОВЫЙ 5009*	19,89	2.12 Плитка керамическая Размер:200x200 мм Производитель: Kerama Marazzi КАЛЕЙДОСКОП ГОЛУБОЙ СВЕТЛЫЙ МАТОВЫЙ 5280*	22,09	-	0,00	-	0,00	-	0,00	Плинтус коннелюрный ТК 25 ТИП3*	17,08
112	Кабинет врача	Обеспыливание	5,86	2.11 Плитка керамическая Размер: 200x200 мм Производитель: Kerama Marazzi КАЛЕЙДОСКОП БЕЛЫЙ МАТОВЫЙ 5009*	21,92	2.12 Плитка керамическая Размер:200x200 мм Производитель: Kerama Marazzi КАЛЕЙДОСКОП ГОЛУБОЙ СВЕТЛЫЙ МАТОВЫЙ 5280*	19,73	-	0,00	-	0,00	-	0,00	Плинтус коннелюрный ТК 25 ТИП3*	18,63
113	Гардероб для обучающихся	-	0,00	2.2.1 Окраска стен Производитель: BRAVO Class Profi FW-55/NEOLAIN SATIN RAL 9010	61,89	2.1.6 Окраска стен (акцентная) Bravo Class Profi FW-55/NEOLAIN SATIN RAL 000 85 00	17,52	-	0,00	-	0,00	-	0,00	Плинтус керамогранитный завальцованный Kerama Marazzi Фондаменто Пепельный Светлый обрезной DD500720R/6BT*	25,37
114	Гардероб для обучающихся	-	0,00	2.2.1 Окраска стен Производитель: BRAVO Class Profi FW-55/NEOLAIN SATIN RAL 9010	147,29	2.1.6 Окраска стен (акцентная) Bravo Class Profi FW-55/NEOLAIN SATIN RAL 000 85 00	39,40	-	0,00	-	0,00	-	0,00	Плинтус керамогранитный завальцованный Kerama Marazzi Фондаменто Пепельный Светлый обрезной DD500720R/6BT*	55,05
115	Цех вторичной обработки овощей	-	0,00	2.11 Плитка керамическая Размер: 200x200 мм Производитель: Kerama Marazzi КАЛЕЙДОСКОП БЕЛЫЙ МАТОВЫЙ 5009*	46,65	-	0,00	-	0,00	-	0,00	-	0,00	-	16,54

Примечание:
Согласно табл. 7.4 СП 71.13330.2017 подготовительный слой отделки вертикальных поверхностей в помещениях следует принять как :
1. Улучшенная штукатурка применяется в технических помещениях и помещениях пищеблока (кроме помещений, где предусмотрено обеспыливание и помещения, где отделка не предусмотрена);
2. Высококачественная штукатурка применяется во всех помещениях с предыванием детей.
3. Предусмотреть Г-образные уголки алюминиевые матовые в строительном исполнении для фартуков раковин и фонтанчиков.
4. Применить к мозаике затирку Чваровит зеленый глянцевый МС4140 или аналог по согласованию с ГКУ ДИОМ - litokol s.420 verde prato (эпоксидная) или аналог по согласованию с ГКУ ДИОМ, Мороксит голубой глянцевый МС4080 или аналог по согласованию с ГКУ ДИОМ - litokol LLE.365 лазурно-серый (полимер-цементная) или аналог по согласованию с ГКУ ДИОМ, Жадеит светло-бирюзовый МС4040 или аналог по согласованию с ГКУ ДИОМ - litokol s.410 verde prato (эпоксидная) или аналог по согласованию с ГКУ ДИОМ, Малахит бирюзовый глянцевый МС4020 или аналог по согласованию с ГКУ ДИОМ - litokol LLE.390 малахит (полимер-цементная) или аналог по согласованию с ГКУ ДИОМ.
5. Применить к плитке медблока Kerama Marazzi КАЛЕЙДОСКОП ГОЛУБОЙ СВЕТЛЫЙ МАТОВЫЙ или аналог по согласованию с ГКУ ДИОМ - затирку litokol LLE.375 Турмалин (полимер-цементная) или аналог по согласованию с ГКУ ДИОМ.
6. Принять ширину шва не более 3-4 мм для бетонной плитки под кирпич с эпоксидной затиркой швов под окраску RAL 9010.
7. Применить затирку в цвете RAL 9002 в умывальной зоне к керамической плитке Аккорд размером 85*285 или аналог по согласованию с ГКУ ДИОМ.
8. Применить высоту расклайки плитки в обеденном зале до ригеля (в случае отсутствия - до потолка).

0,000=168,265

Изм.	Колуч.	Лист	№Док.	Подп.	Дата
Разработал		Белова Е.С.			09.25
Проверил		Дубинин С.В.			09.25
ГАП		Дубинин С.В.			09.25
ГИП		Гущин А.В.			
Н.контроль		Шукшин В.В.			09.25

ГИП-28/24-П-АР

ГБОУ Школа № 218, расположенная по адресу: г. Москва, ул. Вучетича, д. 6

Стадия	Лист	Листов
П	50	64

Средняя общеобразовательная школа

Ведомость отделки 1 этажа

И-ГРУПП
ПРОЕКТНО-СТРОИТЕЛЬНАЯ КОМПАНИЯ

№ пом.	Название Зоны	Запотолочное пр-во,стены	Запотолочное пр-во,стены,м2	Стены, Тип-1	Стены, Тип-1, м2	Стены, Тип-2	Стены, Тип-2, м2	Стены, Тип-3	Стены, Тип-3, м2	Стены, Тип-4	Стены, Тип-4, м2	Стены, Тип-5	Стены, Тип-5, м2	Тип плинтуса	Плинтус, м.п. (Р пом.)
116	Цех первичной обработки овощей	-	0,00	2.11 Плитка керамическая Размер: 200x200 мм Производитель: Kerama Marazzi КАЛЕЙДОСКОП БЕЛЫЙ МАТОВЫЙ 5009*	33,10	-	0,00	-	0,00	-	0,00	-	0,00	-	11,98
117	Сан. узел для персонала	Негорючая краска КМ0 Bravo decor Class profi НГ W-200* RAL 9011	1,77	2.7 Керамогранит крупноформатный Размер: 600x600 мм Производитель: Kerama Marazzi Про Стоун серый светлый обрезной Артикул: DD503820R	9,66	2.17 Плитка керамическая Размер: 200x800 мм Производитель: Kerama Marazzi Клин Вуд бежевый SG705790R	4,54	-	0,00	-	0,00	-	0,00	-	5,10
119	Коридор	-	0,00	2.11 Плитка керамическая Размер: 200x200 мм Производитель: Kerama Marazzi КАЛЕЙДОСКОП БЕЛЫЙ МАТОВЫЙ 5009*	104,72	-	0,00	-	0,00	-	0,00	-	0,00	-	31,90
119а	Тамбур	-	0,00	2.11 Плитка керамическая Размер: 200x200 мм Производитель: Kerama Marazzi КАЛЕЙДОСКОП БЕЛЫЙ МАТОВЫЙ 5009*	4,58	-	0,00	-	0,00	-	0,00	-	0,00	-	-1,60
120	Моечная обратной тары	-	0,00	2.11 Плитка керамическая Размер: 200x200 мм Производитель: Kerama Marazzi КАЛЕЙДОСКОП БЕЛЫЙ МАТОВЫЙ 5009*	27,68	-	0,00	-	0,00	-	0,00	-	0,00	-	8,99
121	Лестничная клетка (для персонала)	-	0,00	2.2.1 Окраска стен Производитель: BRAVO Class Profi FW-55/NEOLAIN SATIN RAL 9010	33,53	-	0,00	-	0,00	-	0,00	-	0,00	-	12,45
122	Загрузочный цех	-	0,00	2.11 Плитка керамическая Размер: 200x200 мм Производитель: Kerama Marazzi КАЛЕЙДОСКОП БЕЛЫЙ МАТОВЫЙ 5009*	43,91	-	0,00	-	0,00	-	0,00	-	0,00	-	15,61
123	Мясо-рыбный цех	-	0,00	2.11 Плитка керамическая Размер: 200x200 мм Производитель: Kerama Marazzi КАЛЕЙДОСКОП БЕЛЫЙ МАТОВЫЙ 5009*	50,75	-	0,00	-	0,00	-	0,00	-	0,00	-	18,18
124	Моечная кухонной посуды	-	0,00	2.11 Плитка керамическая Размер: 200x200 мм Производитель: Kerama Marazzi КАЛЕЙДОСКОП БЕЛЫЙ МАТОВЫЙ 5009*	42,48	-	0,00	-	0,00	-	0,00	-	0,00	-	13,91
125	ПУИ	-	0,00	2.6 Керамогранит крупноформатный Размер: 600x600 мм Производитель: Kerama Marazzi Фондаменто пепельный светлый обрезной Артикул: DL600720R	31,90	-	0,00	-	0,00	-	0,00	-	0,00	Плинтус гибкий ПВХ Первый профильный завод PL100SD* RAL 9004	10,40
126	Помещение временного хранения пищевых отходов	-	0,00	2.11 Плитка керамическая Размер: 200x200 мм Производитель: Kerama Marazzi КАЛЕЙДОСКОП БЕЛЫЙ МАТОВЫЙ 5009*	35,78	-	0,00	-	0,00	-	0,00	-	0,00	-	11,37
127	Моечная столовой посуды	-	0,00	2.11 Плитка керамическая Размер: 200x200 мм Производитель: Kerama Marazzi КАЛЕЙДОСКОП БЕЛЫЙ МАТОВЫЙ 5009*	168,51	-	0,00	-	0,00	-	0,00	-	0,00	-	55,60
128	Горячий цех	-	0,00	2.11 Плитка керамическая Размер: 200x200 мм Производитель: Kerama Marazzi КАЛЕЙДОСКОП БЕЛЫЙ МАТОВЫЙ 5009*	90,39	-	0,00	-	0,00	-	0,00	-	0,00	-	32,94
129	Холодный цех	-	0,00	2.11 Плитка керамическая Размер: 200x200 мм Производитель: Kerama Marazzi КАЛЕЙДОСКОП БЕЛЫЙ МАТОВЫЙ 5009*	34,80	-	0,00	-	0,00	-	0,00	-	0,00	-	12,61
130	Обеденный зал	-	0,00	2.9 Керамогранит крупноформатный Размер: 400x1200 мм Производитель: Kerama Marazzi Монфорте белый матовый обрезной 14010R	152,18	2.8 Керамогранит Размер: 200x500 мм Производитель: Kerama Marazzi Аулетти бежевый матовый Kerama Marazzi 7211	57,58	2.2.1 Окраска стен Производитель: BRAVO Class Profi FW-55/NEOLAIN SATIN RAL 9010	111,58	2.10 Плитка керамическая Размер: 285x85 мм Производитель: Kerama Marazzi Аккорд белый грань глянцевый 8,5x28,5 RAL 9010	79,90	-	0,00	Плинтус керамогранитный завальцованный Kerama Marazzi Фондаменто Пепельный Светлый обрезной DD500720R/6BT*	72,13
131	Лестничная клетка (тип H2)	-	0,00	2.3 Окраска стен Производитель: BRAVO Class Profi W-200 НГ RAL 9010	23,52	2.4.1 Окраска антивандальной краской лестничных клеток и в зоне поручня Производитель: BRAVO Class Profi W-200 НГ RAL 200 80 25	24,30	-	0,00	-	0,00	-	0,00	Плинтус керамогранитный для ЛК Kerama Marazzi Про Лаймстоун Светлый Серый натуральный DD205320R73BT*	14,90

Примечание:
Согласно табл. 7.4 СП 71.13330.2017 подготовительный слой отделки вертикальных поверхностей в помещениях следует принять как :
1. Улучшенная штукатурка применяется в технических помещениях и помещениях пищеблока (кроме помещений, где предусмотрено обеспыливание и помещения, где отделка не предусмотрена);
2. Высококачественная штукатурка применяется во всех помещениях с пребыванием детей.
3. Предусмотреть Г-образные уголки алюминиевые матовые в строительном исполнении для фартуков раковин и фонтанчиков.
4. Применить к мозаике затирку Уваровит зеленый глянцевый MC4140 или аналог по согласованию с ГКУ ДИОМ - litokol s.420 verde prato (эпоксидная) или аналог по согласованию с ГКУ ДИОМ, Мороксит голубой глянцевый MC4080 или аналог по согласованию с ГКУ ДИОМ - litokol LLE.365 лазурно-серый (полимер-цементная) или аналог по согласованию с ГКУ ДИОМ, Жадеит светло-бирюзовый MC4040 или аналог по согласованию с ГКУ ДИОМ - litokol s.410 verde prato (эпоксидная) или аналог по согласованию с ГКУ ДИОМ, Малахит бирюзовый глянцевый MC4020 или аналог по согласованию с ГКУ ДИОМ - litokol LLE.390 малахит (полимер-цементная) или аналог по согласованию с ГКУ ДИОМ.
5. Применить к плитке медблока Kerama Marazzi КАЛЕЙДОСКОП ГОЛУБОЙ СВЕТЛЫЙ МАТОВЫЙ или аналог по согласованию с ГКУ ДИОМ - затирку litokol LLE.375 Турмалин (полимер-цементная) или аналог по согласованию с ГКУ ДИОМ.
6. Принять ширину шва не более 3-4 мм для бетонной плитки под кирпич с эпоксидной затиркой швов под окраску RAL 9010.
7. Применить затирку в цвете RAL 9002 в умывальной зоне к керамической плитке Аккорд размером 85*285 или аналог по согласованию с ГКУ ДИОМ.
8. Применить высоту расклайки плитки в обеденном зале до ригеля (в случае отсутствия - до потолка).

0,000=168,265

| | | |

Ведомость отделки 1 этажа

№ пом.	Название Зоны	Запотолочное пр-во,стены	Запотолочное пр-во,стены,м2	Стены, Тип-1	Стены, Тип-1, м2	Стены, Тип-2	Стены, Тип-2, м2	Стены, Тип-3	Стены, Тип-3, м2	Стены, Тип-4	Стены, Тип-4, м2	Стены, Тип-5	Стены, Тип-5, м2	Тип плинтуса	Плинтус, м.п. (Р пом.)
133	Сан. узел для мальчиков	Негорючая краска КМ0 Bravo decor Class profi НГ W-200* RAL 9011	3,46	2.6 Керамогранит крупноформатный Размер: 600x600 мм Производитель: Kerama Marazzi Фондаменто пепельный светлый обрезной Артикул: DL600720R	23,26	2.15 Мозаика стеклянная - Роскошная мозаика «Мороксит голубой глянцевый»	1,34	-	0,00	-	0,00	-	0,00	-	10,62
134	Сан. узел для девочек	Негорючая краска КМ0 Bravo decor Class profi НГ W-200* RAL 9011	3,38	2.6 Керамогранит крупноформатный Размер: 600x600 мм Производитель: Kerama Marazzi Фондаменто пепельный светлый обрезной Артикул: DL600720R	25,60	2.16 Мозаика стеклянная - Роскошная мозаика «Уваровит глянцевый»	2,83	-	0,00	-	0,00	-	0,00	-	10,37
135	Коридор	-	0,00	2.3 Окраска стен Производитель: BRAVO Class Profi W-200 НГ RAL 9010	121,88	2.1.9 Окраска стен (акцентная) Bravo Class Profi FW-55/NEOLAIN SATIN RAL 230 70 20	28,10	-	0,00	-	0,00	-	0,00	Плинтус керамогранитный завальцованный Kerama Marazzi Фондаменто Пепельный Светлый обрезной DD500720R/6BT*	50,16
137	Коридор	-	0,00	2.2.1 Окраска стен Производитель: BRAVO Class Profi FW-55/NEOLAIN SATIN RAL 9010	238,05	2.1.9 Окраска стен (акцентная) Bravo Class Profi FW-55/NEOLAIN SATIN RAL 230 70 20	5,23	-	0,00	-	0,00	-	0,00	Плинтус керамогранитный завальцованный Kerama Marazzi Фондаменто Пепельный Светлый обрезной DD500720R/6BT*	81,48
137	Коридор	-	0,00	2.3 Окраска стен Производитель: BRAVO Class Profi W-200 НГ RAL 9010	40,01	2.1.8 Окраска стен (акцентная) Bravo Class Profi FW-55/NEOLAIN SATIN RAL 210 50 40	5,80	2.5. Бетонная плитка под кирпич Размер: 205x60x18 Производитель: BRICK WALL Артикул: Bremen BR-001	18,69	2.21 Покрытие настенное (грифельное), во всю высоту стены	4,48	2.10 Плитка керамическая Размер: 285x85 мм Производитель: Kerama Marazzi Аккорд белый грань глянцевый 8,5x28,5 RAL 9010	4,23	Плинтус керамогранитный завальцованный Kerama Marazzi Фондаменто Пепельный Светлый обрезной DD500720R/6BT*	24,60
138	Коридор	-	0,00	2.2.1 Окраска стен Производитель: BRAVO Class Profi FW-55/NEOLAIN SATIN RAL 9010	216,28	2.1.9 Окраска стен (акцентная) Bravo Class Profi FW-55/NEOLAIN SATIN RAL 230 70 20	7,64	-	0,00	-	0,00	-	0,00	Плинтус керамогранитный завальцованный Kerama Marazzi Фондаменто Пепельный Светлый обрезной DD500720R/6BT*	78,04
138	Коридор	-	0,00	2.3 Окраска стен Производитель: BRAVO Class Profi W-200 НГ RAL 9010	26,05	2.21 Покрытие настенное (грифельное), во всю высоту стены	4,48	2.1.8 Окраска стен (акцентная) Bravo Class Profi FW-55/NEOLAIN SATIN RAL 210 50 40	16,54	2.5. Бетонная плитка под кирпич Размер: 205x60x18 Производитель: BRICK WALL Артикул: Bremen BR-001	17,14	2.10 Плитка керамическая Размер: 285x85 мм Производитель: Kerama Marazzi Аккорд белый грань глянцевый 8,5x28,5 RAL 9010	4,40	Плинтус керамогранитный завальцованный Kerama Marazzi Фондаменто Пепельный Светлый обрезной DD500720R/6BT*	26,10
139	Лестничная клетка (тип Л1)	-	0,00	2.3 Окраска стен Производитель: BRAVO Class Profi W-200 НГ RAL 9010	22,32	2.4.1 Окраска антивандальной краской лестничных клеток и в зоне поручня Производитель: BRAVO Class Profi W-200 НГ RAL 200 80 25	24,30	-	0,00	-	0,00	-	0,00	Плинтус керамогранитный для ЛК Kerama Marazzi Про Лаймстоун Светлый Серый натуральный DD205320R/3BT*	14,53
140	Административный кабинет Тип 1 (основная и старшая школа)	Обеспыливание	5,41	2.2.1 Окраска стен Производитель: BRAVO Class Profi FW-55/NEOLAIN SATIN RAL 9010	23,47	2.1.7 Окраска стен (акцентная) Bravo Class Profi FW-55/NEOLAIN SATIN RAL 240 70 20	16,75	-	0,00	-	0,00	-	0,00	Плинтус гибкий ПВХ Первый профильный завод PL100SD* RAL 9004	16,22
141	Учебный кабинет (1-й класс)	Обеспыливание	9,31	2.2.1 Окраска стен Производитель: BRAVO Class Profi FW-55/NEOLAIN SATIN RAL 9010	47,08	2.1.3 Окраска стен (акцентная) Bravo Class Profi FW-55/NEOLAIN SATIN RAL 110 85 50	16,02	2.10 Плитка керамическая Размер: 285x85 мм Производитель: Kerama Marazzi Аккорд белый грань глянцевый 8,5x28,5 RAL 9010	2,27	-	0,00	-	0,00	Плинтус гибкий ПВХ Первый профильный завод PL100SD* RAL 9004	28,84
142	Сан. узел для девочек начальной школы	Негорючая краска КМ0 Bravo decor Class profi НГ W-200* RAL 9011	5,65	2.6 Керамогранит крупноформатный Размер: 600x600 мм Производитель: Kerama Marazzi Фондаменто пепельный светлый обрезной Артикул: DL600720R	34,68	2.16 Мозаика стеклянная - Роскошная мозаика «Уваровит глянцевый»	5,60	-	0,00	-	0,00	-	0,00	-	16,04
143	Сан. узел для мальчиков начальной школы	Негорючая краска КМ0 Bravo decor Class profi НГ W-200* RAL 9011	6,13	2.6 Керамогранит крупноформатный Размер: 600x600 мм Производитель: Kerama Marazzi Фондаменто пепельный светлый обрезной Артикул: DL600720R	42,99	2.15 Мозаика стеклянная - Роскошная мозаика «Мороксит голубой глянцевый»	5,60	-	0,00	-	0,00	-	0,00	-	19,54
144	ПУИ	-	0,00	2.6 Керамогранит крупноформатный Размер: 600x600 мм Производитель: Kerama Marazzi Фондаменто пепельный светлый обрезной Артикул: DL600720R	19,16	-	0,00	-	0,00	-	0,00	-	0,00	Плинтус гибкий ПВХ Первый профильный завод PL100SD* RAL 9004	6,14
145	Лестничная клетка (тип Л1)	-	0,00	2.3 Окраска стен Производитель: BRAVO Class Profi W-200 НГ RAL 9010	22,14	2.4.1 Окраска антивандальной краской лестничных клеток и в зоне поручня Производитель: BRAVO Class Profi W-200 НГ RAL 200 80 25	24,30	-	0,00	-	0,00	-	0,00	Плинтус керамогранитный для ЛК Kerama Marazzi Про Лаймстоун Светлый Серый натуральный DD205320R/3BT*	14,47
146	Универсальное помещение с возможностью организации гимнастического зала (хореографии)	-	0,00	2.2.1 Окраска стен Производитель: BRAVO Class Profi FW-55/NEOLAIN SATIN RAL 9010	127,22	-	0,00	-	0,00	-	0,00	-	0,00	Плинтус вентилируемый Krast School SA22*	42,55
147	Раздевальные	-	0,00	2.2.1 Окраска стен Производитель: BRAVO Class Profi FW-55/NEOLAIN SATIN RAL 9010	27,88	-	0,00	-	0,00	-	0,00	-	0,00	Плинтус гибкий ПВХ Первый профильный завод PL100SD* RAL 9004	10,56

Примечание:
Согласно табл. 7.4 СП 71.13330.2017 подготовительный слой отделки вертикальных поверхностей в помещениях следует принять как :
1. Улучшенная штукатурка применяется в технических помещениях и помещениях пищеблока (кроме помещений, где предусмотрено обеспыливание и помещения, где отделка не предусмотрена);
2. Высококачественная штукатурка применяется во всех помещениях с пребыванием детей.
3. Предусмотреть Г-образные уголки алюминиевые матовые в строительном исполнении для фартуков раковин и фонтанчиков.
4. Применить к мозаике затирку Уваровит зеленый глянцевый MC4140 или аналог по согласованию с ГКУ ДИОМ - litokol s.420 verde prato (эпоксидная) или аналог по согласованию с ГКУ ДИОМ, Мороксит голубой глянцевый MC4080 или аналог по согласованию с ГКУ ДИОМ - litokol LLE.365 лазурно-серый (полимер-цементная) или аналог по согласованию с ГКУ ДИОМ, Жадеит светло-бирюзовый MC4040 или аналог по согласованию с ГКУ ДИОМ - litokol s.410 verde prato (эпоксидная) или аналог по согласованию с ГКУ ДИОМ, Малахит бирюзовый глянцевый MC4020 или аналог по согласованию с ГКУ ДИОМ - litokol LLE.390 малахит (полимер-цементная) или аналог по согласованию с ГКУ ДИОМ.
5. Применить к плитке мебблока Kerama Marazzi КАЛЕЙДОСКОП ГОЛУБОЙ СВЕТЛЫЙ МАТОВЫЙ или аналог по согласованию с ГКУ ДИОМ - затирку litokol LLE.375 Турмалин (полимер-цементная) или аналог по согласованию с ГКУ ДИОМ.
6. Принять ширину шва не более 3-4 мм для бетонной плитки под кирпич с эпоксидной затиркой швов под окраску RAL 9010.
7. Применить затирку в цвете RAL 9002 в умывальной зоне к керамической плитке Аккорд размером 85*285 или аналог по согласованию с ГКУ ДИОМ.
8. Применить высоту раскладки плитки в обеденном зале до ригеля (в случае отсутствия - до потолка).

0,000=168,265

Изм.	Колуч.	Лист	№Док.	Подп.	Дата
Разработал		Белова Е.С.			09.25
Проверил		Дубинин С.В.			09.25
ГАП		Дубинин С.В.			09.25
ГИП		Гущин А.В.			
Н.контроль		Шукшин В.В.			09.25

ГИП-28/24-П-АР

ГБОУ Школа № 218, расположенная по адресу: г. Москва, ул. Вучетича, д. 6

Стадия	Лист	Листов
П	52	64

Средняя общеобразовательная школа

Ведомость отделки 1 этажа

И-ГРУПП ПРОЕКТНО-СТРОИТЕЛЬНАЯ КОМПАНИЯ

Ведомость отделки 1 этажа

№ пом.	Название Зоны	Запотолочное пр-во,стены	Запотолочное пр-во,стены,м2	Стены, Тип-1	Стены, Тип-1, м2	Стены, Тип-2	Стены, Тип-2, м2	Стены, Тип-3	Стены, Тип-3, м2	Стены, Тип-4	Стены, Тип-4, м2	Стены, Тип-5	Стены, Тип-5, м2	Тип плинтуса	Плинтус, м.п. (Р пом.)
148	Раздевальные	-	0,00	2.2.1 Окраска стен Производитель: BRAVO Class Profi FW-55/NEOLAIN SATIN RAL 9010	31,06	-	0,00	-	0,00	-	0,00	-	0,00	Плинтус гибкий ПВХ Первый профильный завод PL100SD* RAL 9004	10,12
150	Кабинет для индивидуальных занятий, в т.ч. с коррекционным педагогом	Обеспыливание	5,80	2.2.1 Окраска стен Производитель: BRAVO Class Profi FW-55/NEOLAIN SATIN RAL 9010	26,89	2.1.7 Окраска стен (акцентная) Bravo Class Profi FW-55/NEOLAIN SATIN RAL 240 70 20	16,24	2.10 Плитка керамическая Размер: 285x85 мм Производитель: Kerama Marazzi Аккорд белый грань глянцевый 8,5x28,5 RAL 9010	2,27	-	0,00	-	0,00	Плинтус гибкий ПВХ Первый профильный завод PL100SD* RAL 9004	18,33
151	Техническое помещение	-	0,00	2.2.1 Окраска стен Производитель: BRAVO Class Profi FW-55/NEOLAIN SATIN RAL 9010	45,49	-	0,00	-	0,00	-	0,00	-	0,00	Плинтус гибкий ПВХ Первый профильный завод PL100SD* RAL 9004	16,42
152	Учебный кабинет (1-й класс)	Обеспыливание	9,11	2.2.1 Окраска стен Производитель: BRAVO Class Profi FW-55/NEOLAIN SATIN RAL 9010	45,78	2.1.3 Окраска стен (акцентная) Bravo Class Profi FW-55/NEOLAIN SATIN RAL 110 85 50	16,90	2.10 Плитка керамическая Размер: 285x85 мм Производитель: Kerama Marazzi Аккорд белый грань глянцевый 8,5x28,5 RAL 9010	2,27	-	0,00	-	0,00	Плинтус гибкий ПВХ Первый профильный завод PL100SD* RAL 9004	28,96
153	Учебный кабинет (1-й класс)	Обеспыливание	9,27	2.2.1 Окраска стен Производитель: BRAVO Class Profi FW-55/NEOLAIN SATIN RAL 9010	48,80	2.1.3 Окраска стен (акцентная) Bravo Class Profi FW-55/NEOLAIN SATIN RAL 110 85 50	15,30	2.10 Плитка керамическая Размер: 285x85 мм Производитель: Kerama Marazzi Аккорд белый грань глянцевый 8,5x28,5 RAL 9010	2,27	-	0,00	-	0,00	Плинтус гибкий ПВХ Первый профильный завод PL100SD* RAL 9004	29,49
154	Учебный кабинет (1-й класс)	Обеспыливание	9,23	2.2.1 Окраска стен Производитель: BRAVO Class Profi FW-55/NEOLAIN SATIN RAL 9010	47,49	2.1.3 Окраска стен (акцентная) Bravo Class Profi FW-55/NEOLAIN SATIN RAL 110 85 50	16,24	2.10 Плитка керамическая Размер: 285x85 мм Производитель: Kerama Marazzi Аккорд белый грань глянцевый 8,5x28,5 RAL 9010	2,27	-	0,00	-	0,00	Плинтус гибкий ПВХ Первый профильный завод PL100SD* RAL 9004	29,35
155	Учебные кабинет для изучения естествознания: химия	Обеспыливание	9,30	2.2.1 Окраска стен Производитель: BRAVO Class Profi FW-55/NEOLAIN SATIN RAL 9010	46,97	2.1.4 Окраска стен (акцентная) Bravo Class Profi FW-55/NEOLAIN SATIN RAL 190 70 30	15,30	2.10 Плитка керамическая Размер: 285x85 мм Производитель: Kerama Marazzi Аккорд белый грань глянцевый 8,5x28,5 RAL 9010	2,27	-	0,00	-	0,00	Плинтус гибкий ПВХ Первый профильный завод PL100SD* RAL 9004	28,59
156	Лаборанстская кабинета химии	Обеспыливание	5,42	2.2.1 Окраска стен Производитель: BRAVO Class Profi FW-55/NEOLAIN SATIN RAL 9010	19,94	2.1.4 Окраска стен (акцентная) Bravo Class Profi FW-55/NEOLAIN SATIN RAL 190 70 30	16,24	2.10 Плитка керамическая Размер: 285x85 мм Производитель: Kerama Marazzi Аккорд белый грань глянцевый 8,5x28,5 RAL 9010	3,70	-	0,00	-	0,00	Плинтус гибкий ПВХ Первый профильный завод PL100SD* RAL 9004	16,06
157	Учебные кабинет для изучения естествознания: физика	Обеспыливание	8,98	2.2.1 Окраска стен Производитель: BRAVO Class Profi FW-55/NEOLAIN SATIN RAL 9010	39,74	2.1.4 Окраска стен (акцентная) Bravo Class Profi FW-55/NEOLAIN SATIN RAL 190 70 30	17,89	2.10 Плитка керамическая Размер: 285x85 мм Производитель: Kerama Marazzi Аккорд белый грань глянцевый 8,5x28,5 RAL 9010	2,27	-	0,00	-	0,00	Плинтус гибкий ПВХ Первый профильный завод PL100SD* RAL 9004	26,54
158	Лаборанстская кабинета физики	Обеспыливание	5,53	2.2.1 Окраска стен Производитель: BRAVO Class Profi FW-55/NEOLAIN SATIN RAL 9010	20,89	2.1.4 Окраска стен (акцентная) Bravo Class Profi FW-55/NEOLAIN SATIN RAL 190 70 30	16,90	2.10 Плитка керамическая Размер: 285x85 мм Производитель: Kerama Marazzi Аккорд белый грань глянцевый 8,5x28,5 RAL 9010	2,27	-	0,00	-	0,00	Плинтус гибкий ПВХ Первый профильный завод PL100SD* RAL 9004	16,04
159	Учебные кабинеты для изучения естествознания: биологии + ОБЗР	Обеспыливание	11,17	2.2.1 Окраска стен Производитель: BRAVO Class Profi FW-55/NEOLAIN SATIN RAL 9010	58,01	2.1.4 Окраска стен (акцентная) Bravo Class Profi FW-55/NEOLAIN SATIN RAL 190 70 30	16,90	2.10 Плитка керамическая Размер: 285x85 мм Производитель: Kerama Marazzi Аккорд белый грань глянцевый 8,5x28,5 RAL 9010	2,27	-	0,00	-	0,00	Плинтус гибкий ПВХ Первый профильный завод PL100SD* RAL 9004	34,86
160	Лаборанстская кабинета биологии	Обеспыливание	5,64	2.2.1 Окраска стен Производитель: BRAVO Class Profi FW-55/NEOLAIN SATIN RAL 9010	23,45	2.1.4 Окраска стен (акцентная) Bravo Class Profi FW-55/NEOLAIN SATIN RAL 190 70 30	16,24	2.10 Плитка керамическая Размер: 285x85 мм Производитель: Kerama Marazzi Аккорд белый грань глянцевый 8,5x28,5 RAL 9010	2,27	-	0,00	-	0,00	Плинтус гибкий ПВХ Первый профильный завод PL100SD* RAL 9004	16,84
161	Кабинет материальной технологии Тип 2	Обеспыливание	8,83	2.2.1 Окраска стен Производитель: BRAVO Class Profi FW-55/NEOLAIN SATIN RAL 9010	42,28	2.1.4 Окраска стен (акцентная) Bravo Class Profi FW-55/NEOLAIN SATIN RAL 190 70 30	18,69	2.10 Плитка керамическая Размер: 285x85 мм Производитель: Kerama Marazzi Аккорд белый грань глянцевый 8,5x28,5 RAL 9010	2,27	-	0,00	-	0,00	Плинтус гибкий ПВХ Первый профильный завод PL100SD* RAL 9004	28,02
162	Кабинет материальной технологии Тип 1	Обеспыливание	8,99	2.2.1 Окраска стен Производитель: BRAVO Class Profi FW-55/NEOLAIN SATIN RAL 9010	41,96	2.1.4 Окраска стен (акцентная) Bravo Class Profi FW-55/NEOLAIN SATIN RAL 190 70 30	16,90	2.10 Плитка керамическая Размер: 285x85 мм Производитель: Kerama Marazzi Аккорд белый грань глянцевый 8,5x28,5 RAL 9010	5,20	-	0,00	-	0,00	Плинтус гибкий ПВХ Первый профильный завод PL100SD* RAL 9004	28,51
163	Лестничная клетка (тип Л1)	-	0,00	2.3 Окраска стен Производитель: BRAVO Class Profi W-200 НГ RAL 9010	22,32	2.4.1 Окраска антивандальной краской лестничных клеток и в зоне поручня Производитель: BRAVO Class Profi W-200 НГ RAL 200 80 25	24,30	-	0,00	-	0,00	-	0,00	Плинтус керамогранитный для ЛК Kerama Marazzi Про Лаймстоун Светлый Серый натуральный DD205320R/3BT*	14,53
164	Сан. узел персонала	Негорючая краска КМ0 Bravo decor Class profi НГ W-200* RAL 9011	1,68	2.7 Керамогранит крупноформатный Размер: 600x600 мм Производитель: Kerama Marazzi Про Стоун серый светлый обрезной Артикул: DD503620R	10,51	2.17 Плитка керамическая Размер: 200x800 мм Производитель: Kerama Marazzi Клин Вуд бежевый SG705790R	2,67	-	0,00	-	0,00	-	0,00	-	4,70

Примечание:
Согласно табл. 7.4 СП 71.13330.2017 подготовительный слой отделки вертикальных поверхностей в помещениях следует принять как :
1. Улучшенная штукатурка применяется в технических помещениях и помещениях пищеблока (кроме помещений, где предусмотрено обеспыливание и помещения, где отделка не предусмотрена);
2. Высококачественная штукатурка применяется во всех помещениях с предыванием детей.
3. Предусмотреть Г-образные уголки алюминиевые матовые в строительном исполнении для фартуков раковин и фонтанчиков.
4. Применить к мозаике затирку Уваровит зеленый глянцевый MC4140 или аналог по согласованию с ГКУ ДИОМ - litokol s.420 verde prato (эпоксидная) или аналог по согласованию с ГКУ ДИОМ, Мороксит голубой глянцевый MC4080 или аналог по согласованию с ГКУ ДИОМ - litokol LLE.365 лазурно-серый (полимер-цементная) или аналог по согласованию с ГКУ ДИОМ, Жадеит светло-бирюзовый MC4040 или аналог по согласованию с ГКУ ДИОМ - litokol s.410 verde prato (эпоксидная) или аналог по согласованию с ГКУ ДИОМ, Малахит бирюзовый глянцевый MC4020 или аналог по согласованию с ГКУ ДИОМ - litokol LLE.390 малахит (полимер-цементная) или аналог по согласованию с ГКУ ДИОМ.
5. Применить к плитке медблока Kerama Marazzi КАЛЕЙДОСКОП ГОЛУБОЙ СВЕТЛЫЙ МАТОВЫЙ или аналог по согласованию с ГКУ ДИОМ - затирку litokol LLE.375 Турмалин (полимер-цементная) или аналог по согласованию с ГКУ ДИОМ.
6. Принять ширину шва не более 3-4 мм для бетонной плитки под кирпич с эпоксидной затиркой швов под окраску RAL 9010.
7. Применить затирку в цвете RAL 9002 в умывальной зоне к керамической плитке Аккорд размером 85*285 или аналог по согласованию с ГКУ ДИОМ.
8. Применить высоту расклайки плитки в обеденном зале до ригеля (в случае отсутствия - до потолка).

0,000=168,265

							ГИП-28/24-П-АР		
							ГБОУ Школа № 218, расположенная по адресу: г. Москва, ул. Вучетича, д. 6		
Изм.	Колуч.	Лист	№Док.	Подп.	Дата				
Разработал		Белова Е.С.			09.25		Средняя общеобразовательная школа	Стадия	Лист	Листов
Проверил		Дубинин С.В.			09.25			П	53	64
ГАП		Дубинин С.В.			09.25					
ГИП		Гущин А.В.					Ведомость отделки 1 этажа	И-ГРУПП ПРОЕКТНО-СТРОИТЕЛЬНАЯ КОМПАНИЯ	
Н.контроль		Шукшин В.В.			09.25				

Ведомость отделки 1 этажа

№ пом.	Название Зоны	Запотолочное пр-во,стены	Запотолочное пр-во,стены,м2	Стены, Тип-1	Стены, Тип-1, м2	Стены, Тип-2	Стены, Тип-2, м2	Стены, Тип-3	Стены, Тип-3, м2	Стены, Тип-4	Стены, Тип-4, м2	Стены, Тип-5	Стены, Тип-5, м2	Тип плинтуса	Плинтус, м.п. (Р пом.)
165	Сан. узел для мальчиков основной и старшей школы	Негорючая краска КМ0 Bravo decor Class profi НГ W-200* RAL 9011	5,63	2.6 Керамогранит крупноформатный Размер: 600х600 мм Производитель: Kerama Marazzi Фондаменто пепельный светлый обрезной Артикул: DL600720R	38,36	2.13 Мозаика стеклянная - Роскошная мозаика «Малахит бирюзовый глянцевый»	5,60	-	0,00	-	0,00	-	0,00	-	17,80
166	Сан. узел для девочек основной и старшей школы с комнатой личной гигиены	Негорючая краска КМ0 Bravo decor Class profi НГ W-200* RAL 9011	5,86	2.6 Керамогранит крупноформатный Размер: 600х600 мм Производитель: Kerama Marazzi Фондаменто пепельный светлый обрезной Артикул: DL600720R	36,28	2.14 Мозаика стеклянная - Роскошная мозаика «Жадеит светло-бирюзовый глянцевый»	5,60	-	0,00	-	0,00	-	0,00	-	16,60
167	Серверная	-	0,00	2.2.1 Окраска стен Производитель: BRAVO Class Profi FW-55/NEOLAIN SATIN RAL 9010	47,44	-	0,00	-	0,00	-	0,00	-	0,00	Плинтус гибкий ПВХ Первый профильный завод PL100SD* RAL 9004	17,08
168	Кроссовая	-	0,00	2.2.1 Окраска стен Производитель: BRAVO Class Profi FW-55/NEOLAIN SATIN RAL 9010	26,62	-	0,00	-	0,00	-	0,00	-	0,00	Плинтус гибкий ПВХ Первый профильный завод PL100SD* RAL 9004	8,61
169	Кроссовая	-	0,00	2.2.1 Окраска стен Производитель: BRAVO Class Profi FW-55/NEOLAIN SATIN RAL 9010	26,29	-	0,00	-	0,00	-	0,00	-	0,00	Плинтус гибкий ПВХ Первый профильный завод PL100SD* RAL 9004	8,50

Примечание:
Согласно табл. 7.4 СП 71.13330.2017 подготовительный слой отделки вертикальных поверхностей в помещениях следует принять как :
1. Улучшенная штукатурка применяется в технических помещениях и помещениях пищеблока (кроме помещений, где предусмотрено обеспыливание и помещения, где отделка не предусмотрена);
2. Высококачественная штукатурка применяется во всех помещениях с пребыванием детей.
3. Предусмотреть Г-образные уголки алюминиевые матовые в строительном исполнении для фартуков раковин и фонтанчиков.
4. Применить к мозаике затирку Уваровит зеленый глянцевый МС4140 или аналог по согласованию с ГКУ ДИОМ - litokol s.420 verde prato (эпоксидная) или аналог по согласованию с ГКУ

ДИОМ, Мороксит голубой глянцевый МС4080 или аналог по согласованию с ГКУ ДИОМ - litokol LLE.365 лазурно-серый (полимер-цементная) или аналог по согласованию с ГКУ ДИОМ, Жадеит светло-бирюзовый МС4040 или аналог по согласованию с ГКУ ДИОМ - litokol s.410 verde prato (эпоксидная) или аналог по согласованию с ГКУ ДИОМ, Малахит бирюзовый глянцевый МС4020 или аналог по согласованию с ГКУ ДИОМ - litokol LLE.390 малахит (полимер-цементная) или аналог по согласованию с ГКУ ДИОМ.
5. Применить к плитке медблока Kerama Marazzi КАЛЕЙДОСКОП ГОЛУБОЙ СВЕТЛЫЙ МАТОВЫЙ или аналог по согласованию с ГКУ ДИОМ - затирку litokol LLE.375 Турмалин (полимер-цементная) или аналог по согласованию с ГКУ ДИОМ.
6. Принять ширину шва не более 3-4 мм для бетонной плитки под кирпич с эпоксидной затиркой швов под окраску RAL 9010.
7. Применить затирку в цвете RAL 9002 в умывальной зоне к керамической плитке Аккорд размером 85*285 или аналог по согласованию с ГКУ ДИОМ.
8. Применить высоту раскладки плитки в обеденном зале до ригеля (в случае отсутствия - до потолка).

0,000=168,265

Изм.	Колуч.	Лист	№Док.	Подп.	Дата	ГИП-28/24-П-АР			
						ГБОУ Школа № 218, расположенная по адресу: г. Москва, ул. Вучетича, д. 6			
Разработал		Белова Е.С.			09.25	Средняя общеобразовательная школа	Стадия	Лист	Листов
Проверил		Дубинин С.В.			09.25		П	54	64
ГАП		Дубинин С.В.			09.25				
ГИП		Гущин А.В.				Ведомость отделки 1 этажа	И-ГРУПП ПРОЕКТНО-СТРОИТЕЛЬНАЯ КОМПАНИЯ		
Н.контроль		Шукшин В.В.			09.25				

Ведомость отделки 2 этажа

М 1:200

№ пом.	Название Зоны	Запотолочное пространство	Запотолочное пр-во,стены,м2	Стены, Тип-1	Стены, Тип-1, м2	Стены, Тип-2	Стены, Тип-2, м2	Стены, Тип-3	Стены, Тип-3, м2	Стены, Тип-4	Стены, Тип-4, м2	Стены, Тип-5	Стены, Тип-5, м2	Тип плинтуса	Плинтус, м.п.
201	Коридор	-	0,00	2.2.1 Окраска стен Производитель: BRAVO Class Profi FW-55/NEOLAIN SATIN RAL 9010	60,03	2.1.9 Окраска стен (акцентная) Bravo Class Profi FW-55/NEOLAIN SATIN RAL 230 70 20	5,15	2.10 Плитка керамическая Размер: 285x85 мм Производитель: Kerama Marazzi Аккорд белый грань глянцевый 8,5x28,5 RAL 9010	2,40	-	0,00	-	0,00	Плинтус гибкий ПВХ Первый профильный завод PL100SD* RAL 9004	22,03
202	Коридор	-	0,00	2.2.1 Окраска стен Производитель: BRAVO Class Profi FW-55/NEOLAIN SATIN RAL 9010	92,21	2.1.9 Окраска стен (акцентная) Bravo Class Profi FW-55/NEOLAIN SATIN RAL 230 70 20	5,40	-	0,00	-	0,00	-	0,00	Плинтус гибкий ПВХ Первый профильный завод PL100SD* RAL 9004	29,88
203	Коридор	-	0,00	2.2.1 Окраска стен Производитель: BRAVO Class Profi FW-55/NEOLAIN SATIN RAL 9010	92,26	2.1.9 Окраска стен (акцентная) Bravo Class Profi FW-55/NEOLAIN SATIN RAL 230 70 20	5,40	-	0,00	-	0,00	-	0,00	Плинтус гибкий ПВХ Первый профильный завод PL100SD* RAL 9004	29,79
204	Коридор	-	0,00	2.2.1 Окраска стен Производитель: BRAVO Class Profi FW-55/NEOLAIN SATIN RAL 9010	145,49	2.1.9 Окраска стен (акцентная) Bravo Class Profi FW-55/NEOLAIN SATIN RAL 230 70 20	39,18	2.10 Плитка керамическая Размер: 285x85 мм Производитель: Kerama Marazzi Аккорд белый грань глянцевый 8,5x28,5 RAL 9010	2,40	-	0,00	-	0,00	Плинтус гибкий ПВХ Первый профильный завод PL100SD* RAL 9004	60,05
205	Раздевальная	-	0,00	2.2.1 Окраска стен Производитель: BRAVO Class Profi FW-55/NEOLAIN SATIN RAL 9010	42,36	2.1.1 Окраска стен (акцентная) Bravo Class Profi FW-55/NEOLAIN SATIN RAL 110 80 40	16,37	-	0,00	-	0,00	-	0,00	Плинтус гибкий ПВХ Первый профильный завод PL100SD* RAL 9004	22,07
206	Душевая	Обеспыливание	4,64	2.7 Керамогранит крупноформатный Размер: 600x600 мм Производитель: Kerama Marazzi Про Стоун серый светлый обрезной Артикул: DD503820R	33,42	2.16 Мозаика стеклянная - Роскошная мозаика «Уваровит глянцевый»	6,14	-	0,00	-	0,00	-	0,00	-	14,49
207	Сан. узел для девочек	Негорючая краска KM0 Bravo decor Class profi НГ W-200* RAL 9011	6,23	2.6 Керамогранит крупноформатный Размер: 600x600 мм Производитель: Kerama Marazzi Фондаменто пепельный светлый обрезной Артикул: DL600720R	45,49	2.14 Мозаика стеклянная - Роскошная мозаика «Жадеит светло-бирюзовый глянцевый»	3,77	-	0,00	-	0,00	-	0,00	-	19,77
208	Сан. узел для персонала	Негорючая краска KM0 Bravo decor Class profi НГ W-200* RAL 9011	1,79	2.7 Керамогранит крупноформатный Размер: 600x600 мм Производитель: Kerama Marazzi Про Стоун серый светлый обрезной Артикул: DD503820R	10,50	2.17 Плитка керамическая Размер: 200x800 мм Производитель: Kerama Marazzi Клин Вуд бежевый SG705790R	3,53	-	0,00	-	0,00	-	0,00	-	5,00
209	Лестничная клетка (тип Н2)	-	0,00	2.3 Окраска стен Производитель: BRAVO Class Profi W-200 НГ RAL 9010	22,83	2.4.1 Окраска антивандальной краской лестничных клеток и в зоне поручня Производитель: BRAVO Class Profi W-200 НГ RAL 200 80 25	24,30	-	0,00	-	0,00	-	0,00	Плинтус керамогранитный для ЛК Kerama Marazzi Про Лаймстоун Светлый Серый натуральный DD205320R/3BT*	16,57
210	Кабинет ИЗО	Обеспыливание	14,47	2.2.1 Окраска стен Производитель: BRAVO Class Profi FW-55/NEOLAIN SATIN RAL 9010	74,48	2.1.4 Окраска стен (акцентная) Bravo Class Profi FW-55/NEOLAIN SATIN RAL 190 70 30	19,91	2.10 Плитка керамическая Размер: 285x85 мм Производитель: Kerama Marazzi Аккорд белый грань глянцевый 8,5x28,5 RAL 9010	2,20	-	0,00	-	0,00	Плинтус гибкий ПВХ Первый профильный завод PL100SD* RAL 9004	45,30
211	Лестничная клетка (тип Н2)	-	0,00	2.3 Окраска стен Производитель: BRAVO Class Profi W-200 НГ RAL 9010	22,83	2.4.1 Окраска антивандальной краской лестничных клеток и в зоне поручня Производитель: BRAVO Class Profi W-200 НГ RAL 200 80 25	24,30	-	0,00	-	0,00	-	0,00	Плинтус керамогранитный для ЛК Kerama Marazzi Про Лаймстоун Светлый Серый натуральный DD205320R/3BT*	16,57
212	Сан. узел для мальчиков	Негорючая краска KM0 Bravo decor Class profi НГ W-200* RAL 9011	6,20	2.6 Керамогранит крупноформатный Размер: 600x600 мм Производитель: Kerama Marazzi Фондаменто пепельный светлый обрезной Артикул: DL600720R	45,25	2.13 Мозаика стеклянная - Роскошная мозаика «Малахит бирюзовый глянцевый»	3,77	-	0,00	-	0,00	-	0,00	-	19,68
213	ПУИ	-	0,00	2.6 Керамогранит крупноформатный Размер: 600x600 мм Производитель: Kerama Marazzi Фондаменто пепельный светлый обрезной Артикул: DL600720R	23,66	-	0,00	-	0,00	-	0,00	-	0,00	-	7,62
214	Раздевальная	-	0,00	2.2.1 Окраска стен Производитель: BRAVO Class Profi FW-55/NEOLAIN SATIN RAL 9010	43,23	2.1.1 Окраска стен (акцентная) Bravo Class Profi FW-55/NEOLAIN SATIN RAL 110 80 40	16,40	-	0,00	-	0,00	-	0,00	Плинтус гибкий ПВХ Первый профильный завод PL100SD* RAL 9004	22,37
215	Душевая	Обеспыливание	4,70	2.7 Керамогранит крупноформатный Размер: 600x600 мм Производитель: Kerama Marazzi Про Стоун серый светлый обрезной Артикул: DD503820R	34,03	2.15 Мозаика стеклянная - Роскошная мозаика «Мороксит голубой глянцевый»	6,06	-	0,00	-	0,00	-	0,00	-	14,69
216	Универсальный спортивный зал	-	0,00	2.2.1 Окраска стен Производитель: BRAVO Class Profi FW-55/NEOLAIN SATIN RAL 9010	382,49	-	0,00	-	0,00	-	0,00	-	0,00	Плинтус вентилируемый Krast School SA22*	65,29

Примечание:
Согласно табл. 7.4 СП 71.13330.2017 подготовительный слой отделки вертикальных поверхностей в помещениях следует принять как :
1. Улучшенная штукатурка применяется в технических помещениях и помещениях пищеблока (кроме помещений, где предусмотрено обеспыливание и помещения, где отделка не предусмотрена);
2. Высококачественная штукатурка применяется во всех помещениях с пребыванием детей.
3. Предусмотреть Г-образные уголки алюминиевые матовые в строительном исполнении для фартуков раковин и фонтанчиков.
4. Применить к мозаике затирку Уваровит зеленый глянцевый МС4140 или аналог по согласованию с ГКУ ДИОМ - litokol s.420 verde prato (эпоксидная) или аналог по согласованию с ГКУ ДИОМ, Мороксит голубой глянцевый МС4080 или аналог по согласованию с ГКУ ДИОМ - litokol LLE.365 лазурно-серый (полимер-цементная) или аналог по согласованию с ГКУ ДИОМ, Жадеит светло-бирюзовый МС4040 или аналог по согласованию с ГКУ ДИОМ - litokol s.410 verde prato (эпоксидная) или аналог по согласованию с ГКУ ДИОМ, Малахит бирюзовый глянцевый МС4020 или аналог по согласованию с ГКУ ДИОМ - litokol LLE.390 малахит (полимер-цементная) или аналог по согласованию с ГКУ ДИОМ.
5. Применить к плитке медблока Kerama Marazzi КАЛЕЙДОСКОП ГОЛУБОЙ СВЕТЛЫЙ МАТОВЫЙ или аналог по согласованию с ГКУ ДИОМ - затирку litokol LLE.375 Турмалин (полимер-цементная) или аналог по согласованию с ГКУ ДИОМ.
6. Принять ширину шва не более 3-4 мм для бетонной плитки под кирпич с эпоксидной затиркой швов под окраску RAL 9010.
7. Применить затирку в цвете RAL 9002 в умывальной зоне к керамической плитке Аккорд размером 85*285 или аналог по согласованию с ГКУ ДИОМ.
8. Применить высоту раскладки плитки в обеденном зале до ригеля (в случае отсутствия - до потолка).

0,000=168,265

Изм.	Колуч.	Лист	№Док.	Подп.	Дата
Разработал		Белова Е.С.			09.25
Проверил		Дубинин С.В.			09.25
ГАП		Дубинин С.В.			09.25
ГИП		Гущин А.В.			
Н.контроль		Шукшин В.В.			09.25

ГИП-28/24-П-АР

ГБОУ Школа № 218, расположенная по адресу: г. Москва, ул. Вучетича, д. 6

Средняя общеобразовательная школа

Стадия	Лист	Листов
П	55	64

Ведомость отделки 2 этажа

И-ГРУПП
ПРОЕКТНО-СТРОИТЕЛЬНАЯ КОМПАНИЯ

Ведомость отделки 2 этажа

М 1:200

№ пом.	Название Зоны	Запотолочное пространство	Запотолочное пр-во,стены,м2	Стены, Тип-1	Стены, Тип-1, м2	Стены, Тип-2	Стены, Тип-2, м2	Стены, Тип-3	Стены, Тип-3, м2	Стены, Тип-4	Стены, Тип-4, м2	Стены, Тип-5	Стены, Тип-5, м2	Тип плинтуса	Плинтус, м.п.
217	Крассовая	-	0,00	2.2.1 Окраска стен Производитель: BRAVO Class Profi FW-55/NEOLAIN SATIN RAL 9010	32,98	-	0,00	-	0,00	-	0,00	-	0,00	Плинтус гибкий ПВХ Первый профильный завод PL100SD* RAL 9004	10,74
218	Артистическая	-	0,00	2.2.1 Окраска стен Производитель: BRAVO Class Profi FW-55/NEOLAIN SATIN RAL 9010	39,53	-	0,00	-	0,00	-	0,00	-	0,00	Плинтус гибкий ПВХ Первый профильный завод PL100SD* RAL 9004	12,93
219	Раздевальная	-	0,00	2.2.1 Окраска стен Производитель: BRAVO Class Profi FW-55/NEOLAIN SATIN RAL 9010	14,49	2.1.1 Окраска стен (акцентная) Bravo Class Profi FW-55/NEOLAIN SATIN RAL 110 80 40	12,00	2.6 Керамогранит крупноформатный Размер: 600x600 мм Производитель: Kerama Marazzi Фондаменто пепельный светлый обрезной Артикул: DL600720R	22,00	2.7 Керамогранит крупноформатный Размер: 600x600 мм Производитель: Kerama Marazzi Про Стоун серый светлый обрезной Артикул: DD503820R	32,20	2.14 Мозаика стеклянная - Роскошная мозаика «Хадеит светло-бирюзовый глянцевый»	2,83	Плинтус гибкий ПВХ Первый профильный завод PL100SD* RAL 9004	29,29
222	Снарядная	-	0,00	2.2.1 Окраска стен Производитель: BRAVO Class Profi FW-55/NEOLAIN SATIN RAL 9010	88,62	-	0,00	-	0,00	-	0,00	-	0,00	Плинтус гибкий ПВХ Первый профильный завод PL100SD* RAL 9004	32,19
223	Комната инструктора с душем и сан. узлом	Обеспыливание	7,16	2.2.1 Окраска стен Производитель: BRAVO Class Profi FW-55/NEOLAIN SATIN RAL 9010	34,58	2.1.9 Окраска стен (акцентная) Bravo Class Profi FW-55/NEOLAIN SATIN RAL 230 70 20	5,48	2.6 Керамогранит крупноформатный Размер: 600x600 мм Производитель: Kerama Marazzi Фондаменто пепельный светлый обрезной Артикул: DL600720R	15,57	2.17 Плитка керамическая Размер: 200x800 мм Производитель: Kerama Marazzi Клин Вуд бежевый SG705790R	6,54	-	0,00	Плинтус гибкий ПВХ Первый профильный завод PL100SD* RAL 9004	22,90
224	Актовый зал	-	0,00	2.2.1 Окраска стен Производитель: BRAVO Class Profi FW-55/NEOLAIN SATIN RAL 9010	248,09	2.1.6 Окраска стен (акцентная) Bravo Class Profi FW-55/NEOLAIN SATIN RAL 000 85 00	74,60	-	0,00	-	0,00	-	0,00	Плинтус гибкий ПВХ Первый профильный завод PL100SD* RAL 9004	47,46
225	Комната инструктора с душем и сан. узлом	Обеспыливание	7,16	2.2.1 Окраска стен Производитель: BRAVO Class Profi FW-55/NEOLAIN SATIN RAL 9010	34,58	2.1.9 Окраска стен (акцентная) Bravo Class Profi FW-55/NEOLAIN SATIN RAL 230 70 20	5,48	2.6 Керамогранит крупноформатный Размер: 600x600 мм Производитель: Kerama Marazzi Фондаменто пепельный светлый обрезной Артикул: DL600720R	15,57	2.17 Плитка керамическая Размер: 200x800 мм Производитель: Kerama Marazzi Клин Вуд бежевый SG705790R	6,54	-	0,00	Плинтус гибкий ПВХ Первый профильный завод PL100SD* RAL 9004	22,90
226	Снарядная	-	0,00	2.2.1 Окраска стен Производитель: BRAVO Class Profi FW-55/NEOLAIN SATIN RAL 9010	88,30	-	0,00	-	0,00	-	0,00	-	0,00	Плинтус гибкий ПВХ Первый профильный завод PL100SD* RAL 9004	32,08
227	Раздевальная	-	0,00	2.2.1 Окраска стен Производитель: BRAVO Class Profi FW-55/NEOLAIN SATIN RAL 9010	13,30	2.1.1 Окраска стен (акцентная) Bravo Class Profi FW-55/NEOLAIN SATIN RAL 110 80 40	12,00	2.6 Керамогранит крупноформатный Размер: 600x600 мм Производитель: Kerama Marazzi Фондаменто пепельный светлый обрезной Артикул: DL600720R	22,00	2.7 Керамогранит крупноформатный Размер: 600x600 мм Производитель: Kerama Marazzi Про Стоун серый светлый обрезной Артикул: DD503820R	32,20	2.13 Мозаика стеклянная - Роскошная мозаика «Малахит бирюзовый глянцевый»	2,83	Плинтус гибкий ПВХ Первый профильный завод PL100SD* RAL 9004	28,89
230	Артистическая	-	0,00	2.2.1 Окраска стен Производитель: BRAVO Class Profi FW-55/NEOLAIN SATIN RAL 9010	40,43	-	0,00	-	0,00	-	0,00	-	0,00	Плинтус гибкий ПВХ Первый профильный завод PL100SD* RAL 9004	13,23
231	Кладовая инвентаря	-	0,00	2.2.1 Окраска стен Производитель: BRAVO Class Profi FW-55/NEOLAIN SATIN RAL 9010	32,87	-	0,00	-	0,00	-	0,00	-	0,00	Плинтус гибкий ПВХ Первый профильный завод PL100SD* RAL 9004	10,70
232	Универсальный спортивный зал	-	0,00	2.2.1 Окраска стен Производитель: BRAVO Class Profi FW-55/NEOLAIN SATIN RAL 9010	385,00	-	0,00	-	0,00	-	0,00	-	0,00	Плинтус вентилируемый Krast School SA22*	64,54
233	Лестничная клетка (тип Л1)	-	0,00	2.3 Окраска стен Производитель: BRAVO Class Profi W-200 HF RAL 9010	23,01	2.4.1 Окраска антивандальной краской лестничных клеток и в зоне поручня Производитель: BRAVO Class Profi W-200 HF RAL 200 80 25	24,30	-	0,00	-	0,00	-	0,00	Плинтус керамогранитный для ЛК Kerama Marazzi Про Лаймстоун Светлый Серый натуральный DD205320R/3BT*	16,63
235	Кабинет иностранного языка (начальная школа)	Обеспыливание	11,08	2.2.1 Окраска стен Производитель: BRAVO Class Profi FW-55/NEOLAIN SATIN RAL 9010	54,91	2.1.2 Окраска стен (акцентная) Bravo Class Profi FW-55/NEOLAIN SATIN RAL 200 80 25	15,75	2.10 Плитка керамическая Размер: 285x85 мм Производитель: Kerama Marazzi Аккорд белый грань глянцевый 8,5x28,5 RAL 9010	4,53	-	0,00	-	0,00	Плинтус гибкий ПВХ Первый профильный завод PL100SD* RAL 9004	34,00
236	Сан. узел для девочек начальной школы	Негорючая краска KM0 Bravo decor Class profi HF W-200* RAL 9011	5,62	2.6 Керамогранит крупноформатный Размер: 600x600 мм Производитель: Kerama Marazzi Фондаменто пепельный светлый обрезной Артикул: DL600720R	32,38	2.16 Мозаика стеклянная - Роскошная мозаика «Уваровит глянцевый»	5,60	-	0,00	-	0,00	-	0,00	-	14,97
237	Сан. узел для мальчиков начальной школы	Негорючая краска KM0 Bravo decor Class profi HF W-200* RAL 9011	6,13	2.6 Керамогранит крупноформатный Размер: 600x600 мм Производитель: Kerama Marazzi Фондаменто пепельный светлый обрезной Артикул: DL600720R	43,00	2.15 Мозаика стеклянная - Роскошная мозаика «Мороксит голубой глянцевый»	5,60	-	0,00	-	0,00	-	0,00	-	19,54

Примечание:
Согласно табл. 7.4 СП. 71.13330.2017 подготовительный слой отделки вертикальных поверхностей в помещениях следует принять как :
1. Улучшенная штукатурка применяется в технических помещениях и помещениях пищеблока (кроме помещений, где предусмотрено обеспыливание и помещения, где отделка не предусмотрена);
2. Высококачественная штукатурка применяется во всех помещениях с пребыванием детей.
3. Предусмотреть Г-образные уголки алюминиевые матовые в строительном исполнении для фартуков раковин и фонтанчиков.
4. Применить к мозаике затирку Уваровит зеленый глянцевый МС4140 или аналог по согласованию с ГКУ ДИОМ - litokol s.420 verde prato (эпоксидная) или аналог по согласованию с ГКУ ДИОМ, Мороксит голубой глянцевый МС4080 или аналог по согласованию с ГКУ ДИОМ - litokol LLE.365 лазурно-серый (полимер-цементная) или аналог по согласованию с ГКУ ДИОМ, Хадеит светло-бирюзовый МС4040 или аналог по согласованию с ГКУ ДИОМ - litokol s.410 verde prato (эпоксидная) или аналог по согласованию с ГКУ ДИОМ, Малахит бирюзовый глянцевый МС4020 или аналог по согласованию с ГКУ ДИОМ - litokol LLE.390 малахит (полимер-цементная) или аналог по согласованию с ГКУ ДИОМ.
5. Применить к плитке медблока Kerama Marazzi КАЛЕЙДОСКОП ГОЛУБОЙ СВЕТЛЫЙ МАТОВЫЙ или аналог по согласованию с ГКУ ДИОМ - затирку litokol LLE.375 Турмалин (полимер-цементная) или аналог по согласованию с ГКУ ДИОМ.
6. Принять ширину шва не более 3-4 мм для бетонной плитки под кирпич с эпоксидной затиркой швов под окраску RAL 9010.
7. Применить затирку в цвете RAL 9002 в умывальной зоне к керамической плитке Аккорд размером 85*285 или аналог по согласованию с ГКУ ДИОМ.
8. Применить высоту раскладки плитки в обеденном зале до ригеля (в случае отсутствия - до потолка).

0,000=168,265

ГИП-28/24-П-АР

ГБОУ Школа № 218, расположенная по адресу: г. Москва, ул. Вучетича, д. 6

Изм.	Колуч.	Лист	№Док.	Подп.	Дата
Разработал		Белова Е.С.			09.25
Проверил		Дубинин С.В.			09.25
ГАП		Дубинин С.В.			09.25
ГИП		Гущин А.В.			
Н.контроль		Шукшин В.В.			09.25

Средняя общеобразовательная школа

Стадия	Лист	Листов
П	56	64

Ведомость отделки 2 этажа

И-ГРУПП
ПРОЕКТНО-СТРОИТЕЛЬНАЯ КОМПАНИЯ

Ведомость отделки 2 этажа

М 1:200

№ пом.	Название Зоны	Запотолочное пространство	Запотолочное пр-во,стены,м2	Стены, Тип-1	Стены, Тип-1, м2	Стены, Тип-2	Стены, Тип-2, м2	Стены, Тип-3	Стены, Тип-3, м2	Стены, Тип-4	Стены, Тип-4, м2	Стены, Тип-5	Стены, Тип-5, м2	Тип плинтуса	Плинтус, м.п.
238	ПУИ	-	0,00	2.6 Керамогранит крупноформатный Размер: 600x600 мм Производитель: Kerama Marazzi Фондаменто пепельный светлый обрезной Артикул: DL600720R	19,16	-	0,00	-	0,00	-	0,00	-	0,00	-	6,14
239	Лестничная клетка (тип Л1)	-	0,00	2.3 Окраска стен Производитель: BRAVO Class Profi W-200 HF RAL 9010	23,01	2.4.1 Окраска антивандальной краской лестничных клеток и в зоне поручня Производитель: BRAVO Class Profi W-200 HF RAL 200 80 25	24,30	-	0,00	-	0,00	-	0,00	Плинтус керамогранитный для ЛК Kerama Marazzi Про Лаймстоун Светлый Серый натуральный DD205320R/3BT*	16,63
240	Кабинет естесствознания Тип 1	Обеспыливание	14,35	2.2.1 Окраска стен Производитель: BRAVO Class Profi FW-55/NEOLAIN SATIN RAL 9010	109,05	2.1.4 Окраска стен (акцентная) Bravo Class Profi FW-55/NEOLAIN SATIN RAL 190 70 30	17,40	2.10 Плитка керамическая Размер: 285x85 мм Производитель: Kerama Marazzi Аккорд белый грань глянцевый 8,5x28,5 RAL 9010	2,27	-	0,00	-	0,00	Плинтус гибкий ПВХ Первый профильный завод PL100SD* RAL 9004	47,85
241	Коридор	-	0,00	2.2.1 Окраска стен Производитель: BRAVO Class Profi FW-55/NEOLAIN SATIN RAL 9010	334,71	2.1.8 Окраска стен (акцентная) Bravo Class Profi FW-55/NEOLAIN SATIN RAL 210 50 40	29,82	2.1.9 Окраска стен (акцентная) Bravo Class Profi FW-55/NEOLAIN SATIN RAL 230 70 20	4,49	2.21 Покрытие настенное (грифельное), во всю высоту стены	8,98	2.10 Плитка керамическая Размер: 285x85 мм Производитель: Kerama Marazzi Аккорд белый грань глянцевый 8,5x28,5 RAL 9010	3,47	Плинтус гибкий ПВХ Первый профильный завод PL100SD* RAL 9004	129,28
243	Учебный кабинет (1 класс)	Обеспыливание	9,31	2.2.1 Окраска стен Производитель: BRAVO Class Profi FW-55/NEOLAIN SATIN RAL 9010	38,25	2.1.3 Окраска стен (акцентная) Bravo Class Profi FW-55/NEOLAIN SATIN RAL 110 85 50	16,07	2.10 Плитка керамическая Размер: 285x85 мм Производитель: Kerama Marazzi Аккорд белый грань глянцевый 8,5x28,5 RAL 9010	2,27	-	0,00	-	0,00	Плинтус гибкий ПВХ Первый профильный завод PL100SD* RAL 9004	24,66
244	Коридор	-	0,00	2.2.1 Окраска стен Производитель: BRAVO Class Profi FW-55/NEOLAIN SATIN RAL 9010	262,49	2.1.8 Окраска стен (акцентная) Bravo Class Profi FW-55/NEOLAIN SATIN RAL 210 50 40	16,54	2.1.9 Окраска стен (акцентная) Bravo Class Profi FW-55/NEOLAIN SATIN RAL 230 70 20	4,49	2.21 Покрытие настенное (грифельное), во всю высоту стены	4,48	2.10 Плитка керамическая Размер: 285x85 мм Производитель: Kerama Marazzi Аккорд белый грань глянцевый 8,5x28,5 RAL 9010	4,41	Плинтус гибкий ПВХ Первый профильный завод PL100SD* RAL 9004	101,07
245	Учебный кабинет (2-4 классы)	Обеспыливание	8,98	2.2.1 Окраска стен Производитель: BRAVO Class Profi FW-55/NEOLAIN SATIN RAL 9010	44,73	2.1.3 Окраска стен (акцентная) Bravo Class Profi FW-55/NEOLAIN SATIN RAL 110 85 50	16,90	2.10 Плитка керамическая Размер: 285x85 мм Производитель: Kerama Marazzi Аккорд белый грань глянцевый 8,5x28,5 RAL 9010	2,27	-	0,00	-	0,00	Плинтус гибкий ПВХ Первый профильный завод PL100SD* RAL 9004	28,45
246	Учебный кабинет (2-4 классы)	Обеспыливание	8,93	2.2.1 Окраска стен Производитель: BRAVO Class Profi FW-55/NEOLAIN SATIN RAL 9010	44,96	2.1.3 Окраска стен (акцентная) Bravo Class Profi FW-55/NEOLAIN SATIN RAL 110 85 50	16,24	2.10 Плитка керамическая Размер: 285x85 мм Производитель: Kerama Marazzi Аккорд белый грань глянцевый 8,5x28,5 RAL 9010	2,27	-	0,00	-	0,00	Плинтус гибкий ПВХ Первый профильный завод PL100SD* RAL 9004	28,29
247	Учебный кабинет (2-4 классы)	Обеспыливание	8,97	2.2.1 Окраска стен Производитель: BRAVO Class Profi FW-55/NEOLAIN SATIN RAL 9010	44,67	2.1.3 Окраска стен (акцентная) Bravo Class Profi FW-55/NEOLAIN SATIN RAL 110 85 50	16,90	2.10 Плитка керамическая Размер: 285x85 мм Производитель: Kerama Marazzi Аккорд белый грань глянцевый 8,5x28,5 RAL 9010	2,27	-	0,00	-	0,00	Плинтус гибкий ПВХ Первый профильный завод PL100SD* RAL 9004	28,43
248	Учебный кабинет (2-4 классы)	Обеспыливание	8,93	2.2.1 Окраска стен Производитель: BRAVO Class Profi FW-55/NEOLAIN SATIN RAL 9010	44,96	2.1.3 Окраска стен (акцентная) Bravo Class Profi FW-55/NEOLAIN SATIN RAL 110 85 50	16,24	2.10 Плитка керамическая Размер: 285x85 мм Производитель: Kerama Marazzi Аккорд белый грань глянцевый 8,5x28,5 RAL 9010	2,27	-	0,00	-	0,00	Плинтус гибкий ПВХ Первый профильный завод PL100SD* RAL 9004	28,29
249	Учебный кабинет (2-4 классы)	Обеспыливание	8,97	2.2.1 Окраска стен Производитель: BRAVO Class Profi FW-55/NEOLAIN SATIN RAL 9010	44,70	2.1.3 Окраска стен (акцентная) Bravo Class Profi FW-55/NEOLAIN SATIN RAL 110 85 50	16,90	2.10 Плитка керамическая Размер: 285x85 мм Производитель: Kerama Marazzi Аккорд белый грань глянцевый 8,5x28,5 RAL 9010	2,24	-	0,00	-	0,00	Плинтус гибкий ПВХ Первый профильный завод PL100SD* RAL 9004	28,43
250	Учебный кабинет (2-4 классы)	Обеспыливание	8,95	2.2.1 Окраска стен Производитель: BRAVO Class Profi FW-55/NEOLAIN SATIN RAL 9010	43,54	2.1.3 Окраска стен (акцентная) Bravo Class Profi FW-55/NEOLAIN SATIN RAL 110 85 50	17,90	2.10 Плитка керамическая Размер: 285x85 мм Производитель: Kerama Marazzi Аккорд белый грань глянцевый 8,5x28,5 RAL 9010	2,27	-	0,00	-	0,00	Плинтус гибкий ПВХ Первый профильный завод PL100SD* RAL 9004	28,38
252	Учебный кабинет (1 класс)	Обеспыливание	9,04	2.2.1 Окраска стен Производитель: BRAVO Class Profi FW-55/NEOLAIN SATIN RAL 9010	46,47	2.1.3 Окраска стен (акцентная) Bravo Class Profi FW-55/NEOLAIN SATIN RAL 110 85 50	15,75	2.10 Плитка керамическая Размер: 285x85 мм Производитель: Kerama Marazzi Аккорд белый грань глянцевый 8,5x28,5 RAL 9010	2,27	-	0,00	-	0,00	Плинтус гибкий ПВХ Первый профильный завод PL100SD* RAL 9004	28,67
253	Сан. узел для девочек начальной школы	Негорючая краска KM0 Bravo decor Class profi HF W-200* RAL 9011	5,84	2.6 Керамогранит крупноформатный Размер: 600x600 мм Производитель: Kerama Marazzi Фондаменто пепельный светлый обрезной Артикул: DL600720R	36,15	2.16 Мозаика стеклянная - Роскошная мозаика «Уваровит глянцевый»	5,60	-	0,00	-	0,00	-	0,00	-	16,55
254	Сан. узел для мальчиков начальной школы	Негорючая краска KM0 Bravo decor Class profi HF W-200* RAL 9011	5,63	2.6 Керамогранит крупноформатный Размер: 600x600 мм Производитель: Kerama Marazzi Фондаменто пепельный светлый обрезной Артикул: DL600720R	38,36	2.15 Мозаика стеклянная - Роскошная мозаика «Мороксит голубой глянцевый»	5,60	-	0,00	-	0,00	-	0,00	-	17,80
255	Сан. узел для персонала	Негорючая краска KM0 Bravo decor Class profi HF W-200* RAL 9011	1,68	2.7 Керамогранит крупноформатный Размер: 600x600 мм Производитель: Kerama Marazzi Про Стоун серый светлый обрезной Артикул: DD503820R	10,58	2.17 Плитка керамическая Размер: 200x800 мм Производитель: Kerama Marazzi Клин Вуд бежевый SG705790R	2,60	-	0,00	-	0,00	-	0,00	-	4,70

Примечание:
Согласно табл. 7.4 СП 71.13330.2017 подготовительный слой отделки вертикальных поверхностей в помещениях следует принять как :
1. Улучшенная штукатурка применяется в технических помещениях и помещениях пищеблока (кроме помещений, где предусмотрено обеспыливание и помещения, где отделка не предусмотрена);
2. Высококачественная штукатурка применяется во всех помещениях с пребыванием детей.
3. Предусмотреть Г-образные уголки алюминиевые матовые в строительном исполнении для фартуков раковин и фонтанчиков.
4. Применить к мозаике затирку Уваровит зеленый глянцевый МС4140 или аналог по согласованию с ГКУ ДИОМ - litokol s.420 verde prato (эпоксидная) или аналог по согласованию с ГКУ ДИОМ, Мороксит голубой глянцевый МС4080 или аналог по согласованию с ГКУ ДИОМ - litokol LLE.365 лазурно-серый (полимер-цементная) или аналог по согласованию с ГКУ ДИОМ, Жадеит светло-бирюзовый МС4040 или аналог по согласованию с ГКУ ДИОМ - litokol s.410 verde prato (эпоксидная) или аналог по согласованию с ГКУ ДИОМ, Малахит бирюзовый глянцевый МС4020 или аналог по согласованию с ГКУ ДИОМ - litokol LLE.390 малахит (полимер-цементная) или аналог по согласованию с ГКУ ДИОМ.
5. Применить к плитке медблока Kerama Marazzi КАЛЕЙДОСКОП ГОЛУБОЙ СВЕТЛЫЙ МАТОВЫЙ или аналог по согласованию с ГКУ ДИОМ - затирку litokol LLE.375 Турмалин (полимер-цементная) или аналог по согласованию с ГКУ ДИОМ.
6. Принять ширину шва не более 3-4 мм для бетонной плитки под кирпич с эпоксидной затиркой швов под окраску RAL 9010.
7. Применить затирку в цвете RAL 9002 в умывальной зоне к керамической плитке Аккорд размером 85*285 или аналог по согласованию с ГКУ ДИОМ.
8. Применить высоту раскладки плитки в обеденном зале до ригеля (в случае отсутствия - до потолка).

0,000=168,265

						ГИП-28/24-П-АР		
						ГБОУ Школа № 218, расположенная по адресу: г. Москва, ул. Вучетича, д. 6		
Изм.	Колуч.	Лист	№Док.	Подп.	Дата			
Разработал		Белова Е.С.			09.25	Средняя общеобразовательная школа	Стадия	Лист	Листов
Проверил		Дубинин С.В.			09.25		П	57	64
ГАП		Дубинин С.В.			09.25				
ГИП		Гущин А.В.				Ведомость отделки 2 этажа	И-ГРУПП ПРОЕКТНО-СТРОИТЕЛЬНАЯ КОМПАНИЯ	
Н.контроль		Шукшин В.В.			09.25			

Ведомость отделки 2 этажа

М 1:200

№ пом.	Название Зоны	Запотолочное пространство	Запотолочное пр-во,стены,м2	Стены, Тип-1	Стены, Тип-1, м2	Стены, Тип-2	Стены, Тип-2, м2	Стены, Тип-3	Стены, Тип-3, м2	Стены, Тип-4	Стены, Тип-4, м2	Стены, Тип-5	Стены, Тип-5, м2	Тип плинтуса	Плинтус, м.п.
256	Лестничная клетка (тип Л1)	-	0,00	2.3 Окраска стен Производитель: BRAVO Class Profi W-200 НГ RAL 9010	20,97	2.4.1 Окраска антивандальной краской лестничных клеток и в зоне поручня Производитель: BRAVO Class Profi W-200 НГ RAL 200 80 25	24,30	-	0,00	-	0,00	-	0,00	Плинтус керамогранитный для ЛК Kerama Marazzi Про Лайтстоун Светлый Серый натуральный DD205320R\3BT*	16,57
258	Кабинет для индивидуальных занятий, в т.ч. с учителем логопедом	Обеспыливание	5,51	2.2.1 Окраска стен Производитель: BRAVO Class Profi FW-55/NEOLAIN SATIN RAL 9010	23,98	2.1.7 Окраска стен (акцентная) Bravo Class Profi FW-55/NEOLAIN SATIN RAL 240 70 20	16,94	2.10 Плитка керамическая Размер: 285x85 мм Производитель: Kerama Marazzi Аккорд белый грань глянцевый 8,5x28,5 RAL 9010	1,96	-	0,00	-	0,00	Плинтус гибкий ПВХ Первый профильный завод PL100SD* RAL 9004	17,40
259	Административный кабинет Тип 1 (начальная школа)	Обеспыливание	5,57	2.2.1 Окраска стен Производитель: BRAVO Class Profi FW-55/NEOLAIN SATIN RAL 9010	25,05	2.1.7 Окраска стен (акцентная) Bravo Class Profi FW-55/NEOLAIN SATIN RAL 240 70 20	18,37	-	0,00	-	0,00	-	0,00	Плинтус гибкий ПВХ Первый профильный завод PL100SD* RAL 9004	17,60
260	Административный кабинет Тип 1 (начальная школа)	Обеспыливание	5,41	2.2.1 Окраска стен Производитель: BRAVO Class Profi FW-55/NEOLAIN SATIN RAL 9010	23,47	2.1.7 Окраска стен (акцентная) Bravo Class Profi FW-55/NEOLAIN SATIN RAL 240 70 20	16,75	-	0,00	-	0,00	-	0,00	Плинтус гибкий ПВХ Первый профильный завод PL100SD* RAL 9004	16,22
261	Кроссовая	-	0,00	2.2.1 Окраска стен Производитель: BRAVO Class Profi FW-55/NEOLAIN SATIN RAL 9010	34,72	-	0,00	-	0,00	-	0,00	-	0,00	Плинтус гибкий ПВХ Первый профильный завод PL100SD* RAL 9004	11,32

Примечание:
Согласно табл. 7.4 СП 71.13330.2017 подготовительный слой отделки вертикальных поверхностей в помещениях следует принять как :
1. Улучшенная штукатурка применяется в технических помещениях и помещениях пищеблока (кроме помещений, где предусмотрено обеспыливание и помещения, где отделка не предусмотрена);
2. Высококачественная штукатурка применяется во всех помещениях с пребыванием детей.
3. Предусмотреть Г-образные уголки алюминиевые матовые в строительном исполнении для фартуков раковин и фонтанчиков.
4. Применить к мозаике затирку Уваровит зеленый глянцевый МС4140 или аналог по согласованию с ГКУ ДИОМ – litokol s.420 verde prato (эпоксидная) или аналог по согласованию с ГКУ ДИОМ, Мороксит голубой глянцевый МС4080 или аналог по согласованию с ГКУ ДИОМ – litokol LLE.365 лазурно-серый (полимер-цементная) или аналог по согласованию с ГКУ ДИОМ, Жадеит светло-бирюзовый МС4040 или аналог по согласованию с ГКУ ДИОМ – litokol s.410 verde prato (эпоксидная) или аналог по согласованию с ГКУ ДИОМ, Малахит бирюзовый глянцевый МС4020 или аналог по согласованию с ГКУ ДИОМ – litokol LLE.390 малахит (полимер-цементная) или аналог по согласованию с ГКУ ДИОМ.
5. Применить к плитке медблока Kerama Marazzi КАЛЕЙДОСКОП ГОЛУБОЙ СВЕТЛЫЙ МАТОВЫЙ или аналог по согласованию с ГКУ ДИОМ – затирку litokol LLE.375 Турмалин (полимер-цементная) или аналог по согласованию с ГКУ ДИОМ.
6. Принять ширину шва не более 3-4 мм для бетонной плитки под кирпич с эпоксидной затиркой швов под окраску RAL 9010.
7. Применить затирку в цвете RAL 9002 в умывальной зоне к керамической плитке Аккорд размером 85*285 или аналог по согласованию с ГКУ ДИОМ.
8. Применить высоту раскладки плитки в обеденном зале до ригеля (в случае отсутствия – до потолка).

0,000=168,265

ГИП-28/24-П-АР

ГБОУ Школа № 218, расположенная по адресу:
г. Москва, ул. Вучетича, д. 6

Изм.	Колуч.	Лист	№Док.	Подп.	Дата
Разработал		Белова Е.С.			09.25
Проверил		Дубинин С.В.			09.25
ГАП		Дубинин С.В.			09.25
ГИП		Гущин А.В.			
Н.контроль		Шукшин В.В.			09.25

Средняя общеобразовательная школа

Стадия	Лист	Листов
П	58	64

Ведомость отделки 2 этажа

И-ГРУПП
ПРОЕКТНО-СТРОИТЕЛЬНАЯ КОМПАНИЯ

Ведомость отделки 3 этажа

М 1:200

№ пом.	Название Зоны	Запотолочное пространство	Запотолочное пр-во,стены,м2	Стены, Тип-1	Стены, Тип-1, м2	Стены, Тип-2	Стены, Тип-2, м2	Стены, Тип-3	Стены, Тип-3, м2	Стены, Тип-4	Стены, Тип-4, м2	Стены, Тип-5	Стены, Тип-5, м2	Тип плинтуса	Плинтус, м.п.
301	Коридор (начальная школа)	-	0,00	2.2.1 Окраска стен Производитель: BRAVO Class Profi FW-55/NEOLAIN SATIN RAL 9010	272,80	2.1.8 Окраска стен (акцентная) Bravo Class Profi FW-55/NEOLAIN SATIN RAL 210 50 40	18,69	2.1.9 Окраска стен (акцентная) Bravo Class Profi FW-55/NEOLAIN SATIN RAL 230 70 20	4,48	2.21 Покрытие настенное (грифельное), во всю высоту стены	4,48	2.10 Плитка керамическая Размер: 285x85 мм Производитель: Kerama Marazzi Аккорд белый грань глянцевый 8,5x28,5 RAL 9010	4,23	Плинтус гибкий ПВХ Первый профильный завод PL100SD* RAL 9004	105,17
303	Серверная	-	0,00	2.2.1 Окраска стен Производитель: BRAVO Class Profi FW-55/NEOLAIN SATIN RAL 9010	47,44	-	0,00	-	0,00	-	0,00	-	0,00	Плинтус гибкий ПВХ Первый профильный завод PL100SD* RAL 9004	17,08
304	Лестничная клетка (тип Л1)	-	0,00	2.3 Окраска стен Производитель: BRAVO Class Profi W-200 НГ RAL 9010	23,01	2.4.1 Окраска антивандальной краской лестничных клеток и в зоне поручня Производитель: BRAVO Class Profi W-200 НГ RAL 200 80 25	24,30	-	0,00	-	0,00	-	0,00	Плинтус керамогранитный для ЛК Kerama Marazzi Про Лаймстоун Светлый Серый натуральный DD205320R/3BT*	16,63
305	Кабинет иностранного языка (начальная школа)	Обеспыливание	11,04	2.2.1 Окраска стен Производитель: BRAVO Class Profi FW-55/NEOLAIN SATIN RAL 9010	45,12	2.1.2 Окраска стен (акцентная) Bravo Class Profi FW-55/NEOLAIN SATIN RAL 200 80 25	16,02	2.10 Плитка керамическая Размер: 285x85 мм Производитель: Kerama Marazzi Аккорд белый грань глянцевый 8,5x28,5 RAL 9010	2,27	-	0,00	-	0,00	Плинтус гибкий ПВХ Первый профильный завод PL100SD* RAL 9004	28,43
306	Лестничная клетка (тип Л1)	-	0,00	2.3 Окраска стен Производитель: BRAVO Class Profi W-200 НГ RAL 9010	22,83	2.4.1 Окраска антивандальной краской лестничных клеток и в зоне поручня Производитель: BRAVO Class Profi W-200 НГ RAL 200 80 25	24,30	-	0,00	-	0,00	-	0,00	Плинтус керамогранитный для ЛК Kerama Marazzi Про Лаймстоун Светлый Серый натуральный DD205320R/3BT*	16,57
307	Сан. узел для мальчиков начальной школы	Негорючая краска KM0 Bravo decor Class profi НГ W-200* RAL 9011	6,13	2.6 Керамогранит крупноформатный Размер: 600x600 мм Производитель: Kerama Marazzi Фондаменто пепельный светлый обрезной Артикул: DL600720R	43,00	2.15 Мозаика стеклянная - Роскошная мозаика «Мороксит голубой глянцевый»	5,60	-	0,00	-	0,00	-	0,00	-	19,54
308	ПУИ	-	0,00	2.6 Керамогранит крупноформатный Размер: 600x600 мм Производитель: Kerama Marazzi Фондаменто пепельный светлый обрезной Артикул: DL600720R	19,16	-	0,00	-	0,00	-	0,00	-	0,00	-	6,14
309	Сан. узел для девочек начальной школы	Негорючая краска KM0 Bravo decor Class profi НГ W-200* RAL 9011	5,62	2.6 Керамогранит крупноформатный Размер: 600x600 мм Производитель: Kerama Marazzi Фондаменто пепельный светлый обрезной Артикул: DL600720R	34,44	2.16 Мозаика стеклянная - Роскошная мозаика «Уваровит глянцевый»	5,60	-	0,00	-	0,00	-	0,00	-	15,95
310	Учебный кабинет (2-4 классы)	Обеспыливание	9,02	2.2.1 Окраска стен Производитель: BRAVO Class Profi FW-55/NEOLAIN SATIN RAL 9010	49,17	2.1.3 Окраска стен (акцентная) Bravo Class Profi FW-55/NEOLAIN SATIN RAL 110 85 50	16,02	2.10 Плитка керамическая Размер: 285x85 мм Производитель: Kerama Marazzi Аккорд белый грань глянцевый 8,5x28,5 RAL 9010	2,27	-	0,00	-	0,00	Плинтус гибкий ПВХ Первый профильный завод PL100SD* RAL 9004	30,06
311	Учебный кабинет (2-4 классы)	Обеспыливание	9,07	2.2.1 Окраска стен Производитель: BRAVO Class Profi FW-55/NEOLAIN SATIN RAL 9010	46,13	2.1.3 Окраска стен (акцентная) Bravo Class Profi FW-55/NEOLAIN SATIN RAL 110 85 50	16,23	2.10 Плитка керамическая Размер: 285x85 мм Производитель: Kerama Marazzi Аккорд белый грань глянцевый 8,5x28,5 RAL 9010	2,27	-	0,00	-	0,00	Плинтус гибкий ПВХ Первый профильный завод PL100SD* RAL 9004	28,84
312	Коридор (начальная школа)	-	0,00	2.2.1 Окраска стен Производитель: BRAVO Class Profi FW-55/NEOLAIN SATIN RAL 9010	249,78	2.1.8 Окраска стен (акцентная) Bravo Class Profi FW-55/NEOLAIN SATIN RAL 210 50 40	16,54	2.1.9 Окраска стен (акцентная) Bravo Class Profi FW-55/NEOLAIN SATIN RAL 230 70 20	4,48	2.21 Покрытие настенное (грифельное), во всю высоту стены	4,80	2.10 Плитка керамическая Размер: 285x85 мм Производитель: Kerama Marazzi Аккорд белый грань глянцевый 8,5x28,5 RAL 9010	4,80	Плинтус гибкий ПВХ Первый профильный завод PL100SD* RAL 9004	97,05
313	Учебный кабинет (2-4 классы)	Обеспыливание	8,98	2.2.1 Окраска стен Производитель: BRAVO Class Profi FW-55/NEOLAIN SATIN RAL 9010	44,59	2.1.3 Окраска стен (акцентная) Bravo Class Profi FW-55/NEOLAIN SATIN RAL 110 85 50	16,90	2.10 Плитка керамическая Размер: 285x85 мм Производитель: Kerama Marazzi Аккорд белый грань глянцевый 8,5x28,5 RAL 9010	2,27	-	0,00	-	0,00	Плинтус гибкий ПВХ Первый профильный завод PL100SD* RAL 9004	28,52
314	Учебный кабинет (2-4 классы)	Обеспыливание	8,93	2.2.1 Окраска стен Производитель: BRAVO Class Profi FW-55/NEOLAIN SATIN RAL 9010	44,82	2.1.3 Окраска стен (акцентная) Bravo Class Profi FW-55/NEOLAIN SATIN RAL 110 85 50	16,24	2.10 Плитка керамическая Размер: 285x85 мм Производитель: Kerama Marazzi Аккорд белый грань глянцевый 8,5x28,5 RAL 9010	2,27	-	0,00	-	0,00	Плинтус гибкий ПВХ Первый профильный завод PL100SD* RAL 9004	28,36
315	Учебный кабинет (2-4 классы)	Обеспыливание	8,97	2.2.1 Окраска стен Производитель: BRAVO Class Profi FW-55/NEOLAIN SATIN RAL 9010	44,04	2.1.3 Окраска стен (акцентная) Bravo Class Profi FW-55/NEOLAIN SATIN RAL 110 85 50	16,90	2.10 Плитка керамическая Размер: 285x85 мм Производитель: Kerama Marazzi Аккорд белый грань глянцевый 8,5x28,5 RAL 9010	2,77	-	0,00	-	0,00	Плинтус гибкий ПВХ Первый профильный завод PL100SD* RAL 9004	28,50
316	Учебный кабинет (2-4 классы)	Обеспыливание	8,93	2.2.1 Окраска стен Производитель: BRAVO Class Profi FW-55/NEOLAIN SATIN RAL 9010	44,82	2.1.3 Окраска стен (акцентная) Bravo Class Profi FW-55/NEOLAIN SATIN RAL 110 85 50	16,24	2.10 Плитка керамическая Размер: 285x85 мм Производитель: Kerama Marazzi Аккорд белый грань глянцевый 8,5x28,5 RAL 9010	2,27	-	0,00	-	0,00	Плинтус гибкий ПВХ Первый профильный завод PL100SD* RAL 9004	28,36
318	Учебный кабинет (2-4 классы)	Обеспыливание	8,97	2.2.1 Окраска стен Производитель: BRAVO Class Profi FW-55/NEOLAIN SATIN RAL 9010	45,27	2.1.3 Окраска стен (акцентная) Bravo Class Profi FW-55/NEOLAIN SATIN RAL 110 85 50	16,90	2.10 Плитка керамическая Размер: 285x85 мм Производитель: Kerama Marazzi Аккорд белый грань глянцевый 8,5x28,5 RAL 9010	1,54	-	0,00	-	0,00	Плинтус гибкий ПВХ Первый профильный завод PL100SD* RAL 9004	28,50

Примечание:
Согласно табл. 7.4 СП 71.13330.2017 подготовительный слой отделки вертикальных поверхностей в помещениях следует принять как :
1. Улучшенная штукатурка применяется в технических помещениях и помещениях пищеблока (кроме помещений, где предусмотрено обеспыливание и помещения, где отделка не предусмотрена);
2. Высококачественная штукатурка применяется во всех помещениях с пребыванием детей.
3. Предусмотреть Г-образные уголки алюминиевые матовые в строительном исполнении для фартуков раковин и фонтанчиков.
4. Применить к мозаике затирку Уваровит зеленый глянцевый MC4140 или аналог по согласованию с ГКУ ДИОМ - litokol s.420 verde prato (эпоксидная) или аналог по согласованию с ГКУ ДИОМ, Мороксит голубой глянцевый MC4080 или аналог по согласованию с ГКУ ДИОМ - litokol LLE.365 лазурно-серый (полимер-цементная) или аналог по согласованию с ГКУ ДИОМ, Жадеит светло-бирюзовый MC4040 или аналог по согласованию с ГКУ ДИОМ - litokol s.410 verde prato (эпоксидная) или аналог по согласованию с ГКУ ДИОМ, Малахит бирюзовый глянцевый MC4020 или аналог по согласованию с ГКУ ДИОМ - litokol LLE.390 малахит (полимер-цементная) или аналог по согласованию с ГКУ ДИОМ.
5. Применить к плитке медблока Kerama Marazzi КАЛЕЙДОСКОП ГОЛУБОЙ СВЕТЛЫЙ МАТОВЫЙ или аналог по согласованию с ГКУ ДИОМ - затирку litokol LLE.375 Турмалин (полимер-цементная) или аналог по согласованию с ГКУ ДИОМ.
6. Принять ширину шва не более 3-4 мм для бетонной плитки под кирпич с эпоксидной затиркой швов под окраску RAL 9010.
7. Применить затирку в цвете RAL 9002 в умывальной зоне к керамической плитке Аккорд размером 85*285 или аналог по согласованию с ГКУ ДИОМ.
8. Применить высоту раскладки плитки в обеденном зале до ригеля (в случае отсутствия - до потолка).

0,000=168,265

| | | |

Ведомость отделки 3 этажа

М 1:200

№ пом.	Название Зоны	Запотолочное пространство	Запотолочное пр-во,стены,м2	Стены, Тип-1	Стены, Тип-1, м2	Стены, Тип-2	Стены, Тип-2, м2	Стены, Тип-3	Стены, Тип-3, м2	Стены, Тип-4	Стены, Тип-4, м2	Стены, Тип-5	Стены, Тип-5, м2	Тип плинтуса	Плинтус, м.п.
319	Учебный кабинет (2-4 классы)	Обеспыливание	8,95	2.2.1 Окраска стен Производитель: BRAVO Class Profi FW-55/NEOLAIN SATIN RAL 9010	44,54	2.1.3 Окраска стен (акцентная) Bravo Class Profi FW-55/NEOLAIN SATIN RAL 110 85 50	16,77	2.10 Плитка керамическая Размер: 285x85 мм Производитель: Kerama Marazzi Аккорд белый грань глянцевый 8,5x28,5 RAL 9010	2,27	-	0,00	-	0,00	Плинтус гибкий ПВХ Первый профильный завод PL100SD* RAL 9004	28,45
320	Учебный кабинет (2-4 классы)	Обеспыливание	8,78	2.2.1 Окраска стен Производитель: BRAVO Class Profi FW-55/NEOLAIN SATIN RAL 9010	44,02	2.1.3 Окраска стен (акцентная) Bravo Class Profi FW-55/NEOLAIN SATIN RAL 110 85 50	15,75	2.10 Плитка керамическая Размер: 285x85 мм Производитель: Kerama Marazzi Аккорд белый грань глянцевый 8,5x28,5 RAL 9010	2,27	-	0,00	-	0,00	Плинтус гибкий ПВХ Первый профильный завод PL100SD* RAL 9004	27,88
321	Учебный кабинет (2-4 классы)	Обеспыливание	8,94	2.2.1 Окраска стен Производитель: BRAVO Class Profi FW-55/NEOLAIN SATIN RAL 9010	45,45	2.1.3 Окраска стен (акцентная) Bravo Class Profi FW-55/NEOLAIN SATIN RAL 110 85 50	15,75	2.10 Плитка керамическая Размер: 285x85 мм Производитель: Kerama Marazzi Аккорд белый грань глянцевый 8,5x28,5 RAL 9010	2,27	-	0,00	-	0,00	Плинтус гибкий ПВХ Первый профильный завод PL100SD* RAL 9004	28,41
322	Учебный кабинет (2-4 классы)	Обеспыливание	8,99	2.2.1 Окраска стен Производитель: BRAVO Class Profi FW-55/NEOLAIN SATIN RAL 9010	45,36	2.1.3 Окраска стен (акцентная) Bravo Class Profi FW-55/NEOLAIN SATIN RAL 110 85 50	16,24	2.10 Плитка керамическая Размер: 285x85 мм Производитель: Kerama Marazzi Аккорд белый грань глянцевый 8,5x28,5 RAL 9010	2,27	-	0,00	-	0,00	Плинтус гибкий ПВХ Первый профильный завод PL100SD* RAL 9004	28,56
323	Учебный кабинет (2-4 классы)	Обеспыливание	9,04	2.2.1 Окраска стен Производитель: BRAVO Class Profi FW-55/NEOLAIN SATIN RAL 9010	46,34	2.1.3 Окраска стен (акцентная) Bravo Class Profi FW-55/NEOLAIN SATIN RAL 110 85 50	15,75	2.10 Плитка керамическая Размер: 285x85 мм Производитель: Kerama Marazzi Аккорд белый грань глянцевый 8,5x28,5 RAL 9010	2,27	-	0,00	-	0,00	Плинтус гибкий ПВХ Первый профильный завод PL100SD* RAL 9004	28,74
324	Лестничная клетка (тип Л1)	-	0,00	2.3 Окраска стен Производитель: BRAVO Class Profi W-200 НГ RAL 9010	26,55	2.4.1 Окраска антивандальной краской лестничных клеток и в зоне поручня Производитель: BRAVO Class Profi W-200 НГ RAL 200 80 25	24,30	-	0,00	-	0,00	-	0,00	Плинтус керамогранитный для ЛК Kerama Marazzi Про Лаймстоун Светлый Серый натуральный DD205320R/3BT*	16,57
325	Сан. узел для мальчиков начальной школы	Негорючая краска KM0 Bravo decor Class profi НГ W-200* RAL 9011	5,63	2.6 Керамогранит крупноформатный Размер: 600x600 мм Производитель: Kerama Marazzi Фондаменто пепельный светлый обрезной Артикул: DL600720R	38,36	2.15 Мозаика стеклянная - Роскошная мозаика «Мороксит голубой глянцевый»	5,60	-	0,00	-	0,00	-	0,00	-	17,80
326	Сан. узел персонала	Негорючая краска KM0 Bravo decor Class profi НГ W-200* RAL 9011	1,68	2.7 Керамогранит крупноформатный Размер: 600x600 мм Производитель: Kerama Marazzi Про Стоун серый светлый обрезной Артикул: DD503820R	10,58	2.17 Плитка керамическая Размер: 200x800 мм Производитель: Kerama Marazzi Клин Вуд бежевый SG705790R	2,60	-	0,00	-	0,00	-	0,00	-	4,70
327	Сан. узел для девочек начальной школы	Негорючая краска KM0 Bravo decor Class profi НГ W-200* RAL 9011	5,84	2.6 Керамогранит крупноформатный Размер: 600x600 мм Производитель: Kerama Marazzi Фондаменто пепельный светлый обрезной Артикул: DL600720R	36,15	2.16 Мозаика стеклянная - Роскошная мозаика «Уваровит глянцевый»	5,60	-	0,00	-	0,00	-	0,00	-	16,55
328	Сан. узел для мальчиков	Негорючая краска KM0 Bravo decor Class profi НГ W-200* RAL 9011	6,20	2.6 Керамогранит крупноформатный Размер: 600x600 мм Производитель: Kerama Marazzi Фондаменто пепельный светлый обрезной Артикул: DL600720R	45,25	2.13 Мозаика стеклянная - Роскошная мозаика «Малахит бирюзовый глянцевый»	3,77	-	0,00	-	0,00	-	0,00	-	19,68
329	ПУИ	-	0,00	2.6 Керамогранит крупноформатный Размер: 600x600 мм Производитель: Kerama Marazzi Фондаменто пепельный светлый обрезной Артикул: DL600720R	22,64	-	0,00	-	0,00	-	0,00	-	0,00	-	7,28
330	Библиотека. Фонд хранения	-	0,00	2.2.1 Окраска стен Производитель: BRAVO Class Profi FW-55/NEOLAIN SATIN RAL 9010	43,59	2.1.5 Окраска стен (акцентная) Bravo Class Profi FW-55/NEOLAIN SATIN RAL 220 50 25	16,90	-	0,00	-	0,00	-	0,00	Плинтус гибкий ПВХ Первый профильный завод PL100SD* RAL 9004	22,95
331	Лестничная клетка (тип Н2)	-	0,00	2.3 Окраска стен Производитель: BRAVO Class Profi W-200 НГ RAL 9010	22,83	2.4.1 Окраска антивандальной краской лестничных клеток и в зоне поручня Производитель: BRAVO Class Profi W-200 НГ RAL 200 80 25	24,30	-	0,00	-	0,00	-	0,00	Плинтус керамогранитный для ЛК Kerama Marazzi Про Лаймстоун Светлый Серый натуральный DD205320R/3BT*	16,57
332а	Коридор	-	0,00	2.2.1 Окраска стен Производитель: BRAVO Class Profi FW-55/NEOLAIN SATIN RAL 9010	124,82	2.1.5 Окраска стен (акцентная) Bravo Class Profi FW-55/NEOLAIN SATIN RAL 220 50 25	18,50	2.21 Покрытие настенное (грифельное), во всю высоту стены	4,48	-	0,00	-	0,00	Плинтус гибкий ПВХ Первый профильный завод PL100SD* RAL 9004	60,32
332б	Читальный зал	-	0,00	2.2.1 Окраска стен Производитель: BRAVO Class Profi FW-55/NEOLAIN SATIN RAL 9010	57,24	2.1.5 Окраска стен (акцентная) Bravo Class Profi FW-55/NEOLAIN SATIN RAL 220 50 25	19,83	2.21 Покрытие настенное (грифельное), во всю высоту стены	4,48	-	0,00	-	0,00	Плинтус гибкий ПВХ Первый профильный завод PL100SD* RAL 9004	38,16
333	Лестничная клетка (тип Н2)	-	0,00	2.3 Окраска стен Производитель: BRAVO Class Profi W-200 НГ RAL 9010	22,83	2.4.1 Окраска антивандальной краской лестничных клеток и в зоне поручня Производитель: BRAVO Class Profi W-200 НГ RAL 200 80 25	24,30	-	0,00	-	0,00	-	0,00	Плинтус керамогранитный для ЛК Kerama Marazzi Про Лаймстоун Светлый Серый натуральный DD205320R/3BT*	16,57

Примечание:
Согласно табл. 7.4 СП 71.13330.2017 подготовительный слой отделки вертикальных поверхностей в помещениях следует принять как :
1. Улучшенная штукатурка применяется в технических помещениях и помещениях пищеблока (кроме помещений, где предусмотрено обеспыливание и помещения, где отделка не предусмотрена);
2. Высококачественная штукатурка применяется во всех помещениях с пребыванием детей.
3. Предусмотреть Г-образные уголки алюминиевые матовые в строительном исполнении для фартуков раковин и фонтанчиков.
4. Применить к мозаике затирку Уваровит зеленый глянцевый МС4140 или аналог по согласованию с ГКУ ДИОМ - litokol s.420 verde prato (эпоксидная) или аналог по согласованию с ГКУ ДИОМ, Мороксит голубой глянцевый МС4080 или аналог по согласованию с ГКУ ДИОМ - litokol LLE.365 лазурно-серый (полимер-цементная) или аналог по согласованию с ГКУ ДИОМ, Жадеит светло-бирюзовый МС4040 или аналог по согласованию с ГКУ ДИОМ - litokol s.410 verde prato (эпоксидная) или аналог по согласованию с ГКУ ДИОМ, Малахит бирюзовый глянцевый МС4020 или аналог по согласованию с ГКУ ДИОМ - litokol LLE.390 малахит (полимер-цементная) или аналог по согласованию с ГКУ ДИОМ.
5. Применить к плитке меддблока Kerama Marazzi КАЛЕЙДОСКОП ГОЛУБОЙ СВЕТЛЫЙ МАТОВЫЙ или аналог по согласованию с ГКУ ДИОМ - затирку litokol LLE.375 Турмалин (полимер-цементная) или аналог по согласованию с ГКУ ДИОМ.
6. Принять ширину шва не более 3-4 мм для бетонной плитки под кирпич с эпоксидной затиркой швов под окраску RAL 9010.
7. Применить затирку в цвете RAL 9002 в умывальной зоне к керамической плитке Аккорд размером 85*285 или аналог по согласованию с ГКУ ДИОМ.
8. Применить высоту расклайки плитки в обеденном зале до ригеля (в случае отсутствия - до потолка).

0,000=168,265

Изм.	Колуч.	Лист	№Док.	Подп.	Дата
Разработал		Белова Е.С.			09.25
Проверил		Дубинин С.В.			09.25
ГАП		Дубинин С.В.			09.25
ГИП		Гущин А.В.			
Н.контроль		Шукшин В.В.			09.25

ГИП-28/24-П-АР

ГБОУ Школа № 218, расположенная по адресу: г. Москва, ул. Вучетича, д. 6

Средняя общеобразовательная школа

Стадия	Лист	Листов
П	60	64

Ведомость отделки 3 этажа

И-ГРУПП
ПРОЕКТНО-СТРОИТЕЛЬНАЯ КОМПАНИЯ

Ведомость отделки 3 этажа

М 1:200

№ пом.	Название Зоны	Запотолочное пространство	Запотолочное пр-во,стены,м2	Стены, Тип-1	Стены, Тип-1, м2	Стены, Тип-2	Стены, Тип-2, м2	Стены, Тип-3	Стены, Тип-3, м2	Стены, Тип-4	Стены, Тип-4, м2	Стены, Тип-5	Стены, Тип-5, м2	Тип плинтуса	Плинтус, м.п.
334	Сан. узел для девочек	Негорючая краска KM0 Bravo decor Class profi НГ W-200* RAL 9011	6,23	2.6 Керамогранит крупноформатный Размер: 600x600 мм Производитель: Kerama Marazzi Фондаменто пепельный светлый обрезной Артикул: DL600720R	45,49	2.14 Мозаика стеклянная - Роскошная мозаика «Жадеит светло-бирюзовый глянцевый»	3,77	-	0,00	-	0,00	-	0,00	-	19,77
335	Сан. узел для персонала	Негорючая краска KM0 Bravo decor Class profi НГ W-200* RAL 9011	1,79	2.7 Керамогранит крупноформатный Размер: 600x600 мм Производитель: Kerama Marazzi Про Стоун серый светлый обрезной Артикул: DD503820R	10,52	2.17 Плитка керамическая Размер: 200x800 мм Производитель: Kerama Marazzi Клин Вуд бежевый SG705790R	3,51	-	0,00	-	0,00	-	0,00	-	5,00
336	Коридор	-	0,00	2.2.1 Окраска стен Производитель: BRAVO Class Profi FW-55/NEOLAIN SATIN RAL 9010	174,53	2.1.7 Окраска стен (акцентная) Bravo Class Profi FW-55/NEOLAIN SATIN RAL 240 70 20	6,63	2.1.9 Окраска стен (акцентная) Bravo Class Profi FW-55/NEOLAIN SATIN RAL 230 70 20	3,38	-	0,00	-	0,00	Плинтус гибкий ПВХ Первый профильный завод PL100SD* RAL 9004	63,97
337	Кроссовая	-	0,00	2.2.1 Окраска стен Производитель: BRAVO Class Profi FW-55/NEOLAIN SATIN RAL 9010	27,48	-	0,00	-	0,00	-	0,00	-	0,00	Плинтус гибкий ПВХ Первый профильный завод PL100SD* RAL 9004	8,90
338	Кабинет для индивидуальных занятий. Студия звукозаписи	Обеспыливание	4,12	2.2.1 Окраска стен Производитель: BRAVO Class Profi FW-55/NEOLAIN SATIN RAL 9010	25,91	2.1.4 Окраска стен (акцентная) Bravo Class Profi FW-55/NEOLAIN SATIN RAL 190 70 30	6,88	-	0,00	-	0,00	-	0,00	Плинтус гибкий ПВХ Первый профильный завод PL100SD* RAL 9004	11,76
339	Медиакласс	Обеспыливание	5,34	2.2.1 Окраска стен Производитель: BRAVO Class Profi FW-55/NEOLAIN SATIN RAL 9010	35,66	2.1.5 Окраска стен (акцентная) Bravo Class Profi FW-55/NEOLAIN SATIN RAL 220 50 25	8,11	-	0,00	-	0,00	-	0,00	Плинтус гибкий ПВХ Первый профильный завод PL100SD* RAL 9004	15,84
340	Коридор	-	0,00	2.2.1 Окраска стен Производитель: BRAVO Class Profi FW-55/NEOLAIN SATIN RAL 9010	288,22	2.1.9 Окраска стен (акцентная) Bravo Class Profi FW-55/NEOLAIN SATIN RAL 230 70 20	4,43	2.1.7 Окраска стен (акцентная) Bravo Class Profi FW-55/NEOLAIN SATIN RAL 240 70 20	15,18	-	0,00	-	0,00	Плинтус гибкий ПВХ Первый профильный завод PL100SD* RAL 9004	104,91
341	Технический центр	-	0,00	2.2.1 Окраска стен Производитель: BRAVO Class Profi FW-55/NEOLAIN SATIN RAL 9010	53,10	-	0,00	-	0,00	-	0,00	-	0,00	Плинтус гибкий ПВХ Первый профильный завод PL100SD* RAL 9004	18,57

Примечание:
Согласно табл. 7.4 СП 71.13330.2017 подготовительный слой отделки вертикальных поверхностей в помещениях следует принять как :
1. Улучшенная штукатурка применяется в технических помещениях и помещениях пищеблока (кроме помещений, где предусмотрено обеспыливание и помещения, где отделка не предусмотрена);
2. Высококачественная штукатурка применяется во всех помещениях с пребыванием детей.
3. Предусмотреть Г-образные уголки алюминиевые матовые в строительном исполнении для фартуков раковин и фонтанчиков.
4. Применить к мозаике затирку Уваровит зеленый глянцевый MC4140 или аналог по согласованию с ГКУ ДИОМ - litokol s.420 verde prato (эпоксидная) или аналог по согласованию с ГКУ

ДИОМ, Мороксит голубой глянцевый MC4080 или аналог по согласованию с ГКУ ДИОМ - litokol LLE.365 лазурно-серый (полимер-цементная) или аналог по согласованию с ГКУ ДИОМ, Жадеит светло-бирюзовый MC4040 или аналог по согласованию с ГКУ ДИОМ - litokol s.410 verde prato (эпоксидная) или аналог по согласованию с ГКУ ДИОМ, Малахит бирюзовый глянцевый MC4020 или аналог по согласованию с ГКУ ДИОМ - litokol LLE.390 малахит (полимер-цементная) или аналог по согласованию с ГКУ ДИОМ.
5. Применить к плитке медблока Kerama Marazzi КАЛЕЙДОСКОП ГОЛУБОЙ СВЕТЛЫЙ МАТОВЫЙ или аналог по согласованию с ГКУ ДИОМ - затирку litokol LLE.375 Турмалин (полимер-цементная) или аналог по согласованию с ГКУ ДИОМ.
6. Принять ширину шва не более 3-4 мм для бетонной плитки под кирпич с эпоксидной затиркой швов под окраску RAL 9010.
7. Применить затирку в цвете RAL 9002 в умывальной зоне к керамической плитке Аккорд размером 85*285 или аналог по согласованию с ГКУ ДИОМ.
8. Применить высоту раскладки плитки в обеденном зале до ригеля (в случае отсутствия - до потолка).

0,000=168,265

Изм.	Колуч.	Лист	№Док.	Подп.	Дата
Разработал		Белова Е.С.			09.25
Проверил		Дубинин С.В.			09.25
ГАП		Дубинин С.В.			09.25
ГИП		Гущин А.В.			
Н.контроль		Шукшин В.В.			09.25

ГИП-28/24-П-АР

ГБОУ Школа № 218, расположенная по адресу: г. Москва, ул. Вучетича, д. 6

Средняя общеобразовательная школа

Стадия	Лист	Листов
П	61	64

Ведомость отделки 3 этажа

И-ГРУПП
ПРОЕКТНО-СТРОИТЕЛЬНАЯ КОМПАНИЯ

Ведомость отделки 4 этажа

М 1:200

№ пом.	Название Зоны	Запотолочное пространство	Запотолочное пр-во,стены,м2	Стены, Тип-1	Стены, Тип-1, м2	Стены, Тип-2	Стены, Тип-2, м2	Стены, Тип-3	Стены, Тип-3, м2	Стены, Тип-4	Стены, Тип-4, м2	Стены, Тип-5	Стены, Тип-5, м2	Тип плинтуса	Плинтус, м.п.
401	Коридор	-	0,00	2.2.1 Окраска стен Производитель: BRAVO Class Profi FW-55/NEOLAIN SATIN RAL 9010	277,02	2.1.9 Окраска стен (акцентная) Bravo Class Profi FW-55/NEOLAIN SATIN RAL 230 70 20	2,99	2.1.8 Окраска стен (акцентная) Bravo Class Profi FW-55/NEOLAIN SATIN RAL 210 50 40	21,63	2.21 Покрытие настенное (грифельное), во всю высоту стены	4,48	2.10 Плитка керамическая Размер: 285x85 мм Производитель: Kerama Marazzi Аккорд белый грань глянцевый 8,5x28,5 RAL 9010	2,77	Плинтус гибкий ПВХ Первый профильный завод PL100SD* RAL 9004	106,58
402	Лестничная клетка (тип Л1)	-	0,00	2.3 Окраска стен Производитель: BRAVO Class Profi W-200 НГ RAL 9010	22,32	2.4.1 Окраска антивандальной краской лестничных клеток и в зоне поручня Производитель: BRAVO Class Profi W-200 НГ RAL 200 80 25	24,30	-	0,00	-	0,00	-	0,00	Плинтус керамогранитный для ЛК Kerama Marazzi Про Лайстоун Светлый Серый натуральный DD205320R/3BT*	14,53
403	Кабинет иностранного языка	Обеспыливание	11,04	2.2.1 Окраска стен Производитель: BRAVO Class Profi FW-55/NEOLAIN SATIN RAL 9010	37,24	2.1.4 Окраска стен (акцентная) Bravo Class Profi FW-55/NEOLAIN SATIN RAL 190 70 30	17,17	-	0,00	-	0,00	-	0,00	Плинтус гибкий ПВХ Первый профильный завод PL100SD* RAL 9004	28,43
404	Лестничная клетка (тип Л1)	-	0,00	2.3 Окраска стен Производитель: BRAVO Class Profi W-200 НГ RAL 9010	22,14	2.4.1 Окраска антивандальной краской лестничных клеток и в зоне поручня Производитель: BRAVO Class Profi W-200 НГ RAL 200 80 25	24,30	-	0,00	-	0,00	-	0,00	Плинтус керамогранитный для ЛК Kerama Marazzi Про Лайстоун Светлый Серый натуральный DD205320R/3BT*	14,47
405	Сан. узел для мальчиков основной и старшей школы	Негорючая краска KM0 Bravo decor Class profi НГ W-200* RAL 9011	6,13	2.6 Керамогранит крупноформатный Размер: 600x600 мм Производитель: Kerama Marazzi Фондаменто пепельный светлый обрезной Артикул: DL600720R	42,99	2.13 Мозаика стеклянная - Роскошная мозаика «Малахит бирюзовый глянцевый»	5,60	-	0,00	-	0,00	-	0,00	-	19,54
406	ПУИ	-	0,00	2.6 Керамогранит крупноформатный Размер: 600x600 мм Производитель: Kerama Marazzi Фондаменто пепельный светлый обрезной Артикул: DL600720R	19,01	-	0,00	-	0,00	-	0,00	-	0,00	-	6,09
407	Сан. узел для девочек основной и старшей школы	Негорючая краска KM0 Bravo decor Class profi НГ W-200* RAL 9011	5,62	2.6 Керамогранит крупноформатный Размер: 600x600 мм Производитель: Kerama Marazzi Фондаменто пепельный светлый обрезной Артикул: DL600720R	34,44	2.14 Мозаика стеклянная - Роскошная мозаика «Жадеит светло-бирюзовый глянцевый»	5,60	-	0,00	-	0,00	-	0,00	-	15,95
408	Кабинет информатики и информационных технологий	Обеспыливание	14,36	2.2.1 Окраска стен Производитель: BRAVO Class Profi FW-55/NEOLAIN SATIN RAL 9010	81,89	2.1.4 Окраска стен (акцентная) Bravo Class Profi FW-55/NEOLAIN SATIN RAL 190 70 30	17,17	-	0,00	-	0,00	-	0,00	Плинтус гибкий ПВХ Первый профильный завод PL100SD* RAL 9004	46,48
409	Коридор	-	0,00	2.2.1 Окраска стен Производитель: BRAVO Class Profi FW-55/NEOLAIN SATIN RAL 9010	268,02	2.1.9 Окраска стен (акцентная) Bravo Class Profi FW-55/NEOLAIN SATIN RAL 230 70 20	2,99	2.1.8 Окраска стен (акцентная) Bravo Class Profi FW-55/NEOLAIN SATIN RAL 210 50 40	14,44	2.10 Плитка керамическая Размер: 285x85 мм Производитель: Kerama Marazzi Аккорд белый грань глянцевый 8,5x28,5 RAL 9010	4,40	2.21 Покрытие настенное (грифельное), во всю высоту стены	4,48	Плинтус гибкий ПВХ Первый профильный завод PL100SD* RAL 9004	102,66
410	Кабинет русского языка и литературы	Обеспыливание	8,98	2.2.1 Окраска стен Производитель: BRAVO Class Profi FW-55/NEOLAIN SATIN RAL 9010	50,08	2.1.1 Окраска стен (акцентная) Bravo Class Profi FW-55/NEOLAIN SATIN RAL 110 80 40	16,90	-	0,00	-	0,00	-	0,00	Плинтус гибкий ПВХ Первый профильный завод PL100SD* RAL 9004	29,92
411	Кабинет русского языка и литературы	Обеспыливание	8,93	2.2.1 Окраска стен Производитель: BRAVO Class Profi FW-55/NEOLAIN SATIN RAL 9010	47,85	2.1.1 Окраска стен (акцентная) Bravo Class Profi FW-55/NEOLAIN SATIN RAL 110 80 40	18,70	-	0,00	-	0,00	-	0,00	Плинтус гибкий ПВХ Первый профильный завод PL100SD* RAL 9004	29,76
412	Кабинет русского языка и литературы	Обеспыливание	8,97	2.2.1 Окраска стен Производитель: BRAVO Class Profi FW-55/NEOLAIN SATIN RAL 9010	47,97	2.1.1 Окраска стен (акцентная) Bravo Class Profi FW-55/NEOLAIN SATIN RAL 110 80 40	16,90	-	0,00	-	0,00	-	0,00	Плинтус гибкий ПВХ Первый профильный завод PL100SD* RAL 9004	28,92
413	Кабинет математики	Обеспыливание	8,93	2.2.1 Окраска стен Производитель: BRAVO Class Profi FW-55/NEOLAIN SATIN RAL 9010	49,66	2.1.1 Окраска стен (акцентная) Bravo Class Profi FW-55/NEOLAIN SATIN RAL 110 80 40	16,90	-	0,00	-	0,00	-	0,00	Плинтус гибкий ПВХ Первый профильный завод PL100SD* RAL 9004	29,76
414	Крассовая	-	0,00	2.2.1 Окраска стен Производитель: BRAVO Class Profi FW-55/NEOLAIN SATIN RAL 9010	34,60	-	0,00	-	0,00	-	0,00	-	0,00	Плинтус гибкий ПВХ Первый профильный завод PL100SD* RAL 9004	11,28
415	Кабинет математики	Обеспыливание	8,97	2.2.1 Окраска стен Производитель: BRAVO Class Profi FW-55/NEOLAIN SATIN RAL 9010	50,03	2.1.1 Окраска стен (акцентная) Bravo Class Profi FW-55/NEOLAIN SATIN RAL 110 80 40	16,90	-	0,00	-	0,00	-	0,00	Плинтус гибкий ПВХ Первый профильный завод PL100SD* RAL 9004	29,90
416	Кабинет истории Тип 1	Обеспыливание	9,00	2.2.1 Окраска стен Производитель: BRAVO Class Profi FW-55/NEOLAIN SATIN RAL 9010	49,36	2.1.1 Окраска стен (акцентная) Bravo Class Profi FW-55/NEOLAIN SATIN RAL 110 80 40	17,84	-	0,00	-	0,00	-	0,00	Плинтус гибкий ПВХ Первый профильный завод PL100SD* RAL 9004	30,00

Примечание:
Согласно табл. 7.4 СП 71.13330.2017 подготовительный слой отделки вертикальных поверхностей в помещениях следует принять как :
1. Улучшенная штукатурка применяется в технических помещениях и помещениях пищеблока (кроме помещений, где предусмотрено обеспыливание и помещения, где отделка не предусмотрена);
2. Высококачественная штукатурка применяется во всех помещениях с предъявлением детей.
3. Предусмотреть Г-образные уголки алюминиевые матовые в строительном исполнении для фартуков раковин и фонтанчиков.
4. Применить к мозаике затирку Уваровит зеленый глянцевый МС4140 или аналог по согласованию с ГКУ ДИОМ - litokol s.420 verde prato (эпоксидная) или аналог по согласованию с ГКУ ДИОМ, Мороксит голубой глянцевый МС4080 или аналог по согласованию с ГКУ ДИОМ - litokol LLE.365 лазурно-серый (полимер-цементная) или аналог по согласованию с ГКУ ДИОМ, Жадеит светло-бирюзовый МС4040 или аналог по согласованию с ГКУ ДИОМ - litokol s.410 verde prato (эпоксидная) или аналог по согласованию с ГКУ ДИОМ, Малахит бирюзовый глянцевый МС4020 или аналог по согласованию с ГКУ ДИОМ - litokol LLE.390 малахит (полимер-цементная) или аналог по согласованию с ГКУ ДИОМ.
5. Применить к плитке мебблока Kerama Marazzi КАЛЕЙДОСКОП ГОЛУБОЙ СВЕТЛЫЙ МАТОВЫЙ или аналог по согласованию с ГКУ ДИОМ - затирку litokol LLE.375 Турмалин (полимер-цементная) или аналог по согласованию с ГКУ ДИОМ.
6. Принять ширину шва не более 3-4 мм для бетонной плитки под кирпич с эпоксидной затиркой швов под окраску RAL 9010.
7. Применить затирку в цвете RAL 9002 в умывальной зоне к керамической плитке Аккорд размером 85*285 или аналог по согласованию с ГКУ ДИОМ.
8. Применить высоту расклайки плитки в обеденном зале до ригеля (в случае отсутствия - до потолка).

0,000=168,265

						ГИП-28/24-П-АР
						ГБОУ Школа № 218, расположенная по адресу: г. Москва, ул. Вучетича, д. 6
Изм.	Колуч.	Лист	№Док.	Подп.	Дата	
Разработал		Белова Е.С.			09.25	Средняя общеобразовательная школа
Проверил		Дубинин С.В.			09.25	
ГАП		Дубинин С.В.			09.25	
ГИП		Гущин А.В.				Ведомость отделки 4 этажа
Н.контроль		Шукшин В.В.			09.25	

Стадия	Лист	Листов
П	62	64

И-ГРУПП
ПРОЕКТНО-СТРОИТЕЛЬНАЯ КОМПАНИЯ

Ведомость отделки 4 этажа

М 1:200

№ пом.	Название Зоны	Запотолочное пространство	Запотолочное пр-во,стены,м2	Стены, Тип-1	Стены, Тип-1, м2	Стены, Тип-2	Стены, Тип-2, м2	Стены, Тип-3	Стены, Тип-3, м2	Стены, Тип-4	Стены, Тип-4, м2	Стены, Тип-5	Стены, Тип-5, м2	Тип плинтуса	Плинтус, м.п.
417	Кабинет географии	Обеспыливание	8,87	2.2.1 Окраска стен Производитель: BRAVO Class Profi FW-55/NEOLAIN SATIN RAL 9010	49,17	2.1.1 Окраска стен (акцентная) Bravo Class Profi FW-55/NEOLAIN SATIN RAL 110 80 40	16,90	-	0,00	-	0,00	-	0,00	Плинтус гибкий ПВХ Первый профильный завод PL100SD* RAL 9004	29,58
418	Универсальный учебный кабинет	Обеспыливание	8,99	2.2.1 Окраска стен Производитель: BRAVO Class Profi FW-55/NEOLAIN SATIN RAL 9010	50,19	2.1.1 Окраска стен (акцентная) Bravo Class Profi FW-55/NEOLAIN SATIN RAL 110 80 40	16,90	-	0,00	-	0,00	-	0,00	Плинтус гибкий ПВХ Первый профильный завод PL100SD* RAL 9004	29,96
419	Кабинет математики	Обеспыливание	8,99	2.2.1 Окраска стен Производитель: BRAVO Class Profi FW-55/NEOLAIN SATIN RAL 9010	50,19	2.1.1 Окраска стен (акцентная) Bravo Class Profi FW-55/NEOLAIN SATIN RAL 110 80 40	16,90	-	0,00	-	0,00	-	0,00	Плинтус гибкий ПВХ Первый профильный завод PL100SD* RAL 9004	29,96
420	Кабинет истории Тип 1	Обеспыливание	9,05	2.2.1 Окраска стен Производитель: BRAVO Class Profi FW-55/NEOLAIN SATIN RAL 9010	50,79	2.1.1 Окраска стен (акцентная) Bravo Class Profi FW-55/NEOLAIN SATIN RAL 110 80 40	16,90	-	0,00	-	0,00	-	0,00	Плинтус гибкий ПВХ Первый профильный завод PL100SD* RAL 9004	30,18
421	Лестничная клетка (тип Л1)	-	0,00	2.3 Окраска стен Производитель: BRAVO Class Profi W-200 НГ RAL 9010	22,14	2.4.1 Окраска антивандальной краской лестничных клеток и в зоне поручня Производитель: BRAVO Class Profi W-200 НГ RAL 200 80 25	24,30	-	0,00	-	0,00	-	0,00	Плинтус керамогранитный для ЛК Kerama Marazzi Про Лаймстоун Светлый Серый натуральный DD205320R/3BT*	14,47
422	Сан. узел для мальчиков основной и старшей школы	Негорючая краска KM0 Bravo decor Class profi НГ W-200* RAL 9011	5,63	2.6 Керамогранит крупноформатный Размер: 600x600 мм Производитель: Kerama Marazzi Фондаменто пепельный светлый обрезной Артикул: DL600720R	38,36	2.13 Мозаика стеклянная - Роскошная мозаика «Малахит бирюзовый глянцевый»	5,60	-	0,00	-	0,00	-	0,00	-	17,80
423	Сан. узел персонала	Негорючая краска KM0 Bravo decor Class profi НГ W-200* RAL 9011	1,70	2.7 Керамогранит крупноформатный Размер: 600x600 мм Производитель: Kerama Marazzi Про Стоун серый светлый обрезной Артикул: DD503820R	10,64	2.17 Плитка керамическая Размер: 200x800 мм Производитель: Kerama Marazzi Клин Вуд бежевый SG705790R	2,70	-	0,00	-	0,00	-	0,00	-	4,76
424	Сан. узел для девочек основной и старшей школы с комнатой личной гигиены	Негорючая краска KM0 Bravo decor Class profi НГ W-200* RAL 9011	5,84	2.6 Керамогранит крупноформатный Размер: 600x600 мм Производитель: Kerama Marazzi Фондаменто пепельный светлый обрезной Артикул: DL600720R	36,15	2.14 Мозаика стеклянная - Роскошная мозаика «Жадеит светло-бирюзовый глянцевый»	5,60	-	0,00	-	0,00	-	0,00	-	16,55
425	Кабинет для индивидуальных занятий, в т.ч. с педагогом психологом	Обеспыливание	5,51	2.2.1 Окраска стен Производитель: BRAVO Class Profi FW-55/NEOLAIN SATIN RAL 9010	21,64	2.1.7 Окраска стен (акцентная) Bravo Class Profi FW-55/NEOLAIN SATIN RAL 240 70 20	16,80	-	0,00	-	0,00	-	0,00	Плинтус гибкий ПВХ Первый профильный завод PL100SD* RAL 9004	15,29

Примечание:
Согласно табл. 7.4 СП 71.13330.2017 подготовительный слой отделки вертикальных поверхностей в помещениях следует принять как :
1. Улучшенная штукатурка применяется в технических помещениях и помещениях пищеблока (кроме помещений, где предусмотрено обеспыливание и помещения, где отделка не предусмотрена);
2. Высококачественная штукатурка применяется во всех помещениях с пребыванием детей.
3. Предусмотреть Г-образные уголки алюминиевые матовые в строительном исполнении для фартуков раковин и фонтанчиков.
4. Применить к мозаике затирку Чаровит зеленый глянцевый MC4140 или аналог по согласованию с ГКУ ДИОМ - litokol s.420 verde prato (эпоксидная) или аналог по согласованию с ГКУ ДИОМ, Мороксит голубой глянцевый MC4080 или аналог по согласованию с ГКУ ДИОМ - litokol LLE.365 лазурно-серый (полимер-цементная) или аналог по согласованию с ГКУ ДИОМ, Жадеит светло-бирюзовый MC4040 или аналог по согласованию с ГКУ ДИОМ - litokol s.410 verde prato (эпоксидная) или аналог по согласованию с ГКУ ДИОМ, Малахит бирюзовый глянцевый MC4020 или аналог по согласованию с ГКУ ДИОМ - litokol LLE.390 малахит (полимер-цементная) или аналог по согласованию с ГКУ ДИОМ.
5. Применить к плитке медблока Kerama Marazzi КАЛЕЙДОСКОП ГОЛУБОЙ СВЕТЛЫЙ МАТОВЫЙ или аналог по согласованию с ГКУ ДИОМ - затирку litokol LLE.375 Турмалин (полимер-цементная) или аналог по согласованию с ГКУ ДИОМ.
6. Принять ширину шва не более 3-4 мм для бетонной плитки под кирпич с эпоксидной затиркой швов под окраску RAL 9010.
7. Применить затирку в цвете RAL 9002 в умывальной зоне к керамической плитке Аккорд размером 85*285 или аналог по согласованию с ГКУ ДИОМ.
8. Применить высоту расклайки плитки в обеденном зале до ригеля (в случае отсутствия - до потолка).

0,000=168,265

						ГИП-28/24-П-АР		
						ГБОУ Школа № 218, расположенная по адресу: г. Москва, ул. Вучетича, д. 6		
Изм.	Колуч.	Лист	№Док.	Подп.	Дата			
Разработал		Белова Е.С.			09.25		Стадия	Лист	Листов
Проверил		Дубинин С.В.			09.25	Средняя общеобразовательная школа	П	63	64
ГАП		Дубинин С.В.			09.25				
ГИП		Гущин А.В.							
						Ведомость отделки 4 этажа	И-ГРУПП ПРОЕКТНО-СТРОИТЕЛЬНАЯ КОМПАНИЯ	
Н.контроль		Шукшин В.В.			09.25			