



АРТИС
Артис - искусство проектирования

109341, г. Москва, ул. Марксистская, дом 3, стр. 1

+7 (495) 647-85-99

mail@rosartis.ru

rosartis.ru



Экз. № _____

Заказчик: АНО «РГТ»

**Капитальный ремонт общеобразовательного
учреждения ГБОУ Школа № 1210 по адресу:
г.Москва, ул. Живописная д. 32**

ПРОЕКТНАЯ ДОКУМЕНТАЦИЯ

Этап 1

**Раздел 11 «Мероприятия по обеспечению доступа инвалидов к
объектам капитального строительства»**

708/П-24-АНО-ОДИ

Том 11



АРТИС
Артис - искусство проектирования

109341, г. Москва, ул. Марксистская, дом 3, стр. 1

+7 (495) 647-85-99

mail@rosartis.ru

rosartis.ru



Экз. № _____

Заказчик: АНО «РГТ»

**Капитальный ремонт общеобразовательного
учреждения ГБОУ Школа № 1210 по адресу:
г. Москва, ул. Живописная д. 32**

ПРОЕКТНАЯ ДОКУМЕНТАЦИЯ

Этап 1

**Раздел 11 «Мероприятия по обеспечению доступа инвалидов к
объектам капитального строительства»**

708/П-24-АНО-ОДИ

Том 11

Генеральный директор:



Цибизов В.В.

СОДЕРЖАНИЕ

№ п/п	Наименование документа	Примечание
1	2	3
1	Титульный лист	
2	Содержание раздела	
3	Текстовая часть	
	Общие данные	5
	а) перечень мероприятий по обеспечению доступа инвалидов к объектам, указанным в подпункте "в" пункта 3 части 7 статьи 51 Градостроительного кодекса Российской Федерации;	6
	б) обоснование принятых конструктивных, объемно-планировочных и иных технических решений, обеспечивающих безопасное перемещение инвалидов на объектах, указанных в подпункте "а" настоящего пункта, а также их эвакуацию из указанных объектов в случае пожара или стихийного бедствия;	6
	в) описание проектных решений по обустройству рабочих мест инвалидов (при необходимости);	11
	Графическая часть	
	Фрагмент план 1го этажа. Схема движения и эвакуации маломобильных групп населения.	Лист 1
	Принципиальная схема расположения оборудования универсальной кабины для МГН.	Лист 2
	Спецификация оборудования и материалов для МГН.	Лист 3

Согласовано		

Взам. инв. №	
--------------	--

Подп. и дата	
--------------	--

Инв. № подл.	
--------------	--

						708П-24-АНО-ОДИ.С			
Изм.	Кол.уч.	Лист	№ док.	Подпись	Дата				
Разработал	Юденкова				04.24	Содержание тома	Стадия	Лист	Листов
Н. контроль	Лукашова				04.24		П	1	
ГАП	Фролова				04.24		Общество с ограниченной ответственностью ООО «АРТИС» 2024		
ГИП	Старов				04.24				

Проектная документация раздела 11 «Мероприятия по обеспечению доступа инвалидов» по объекту: «Капитальный ремонт здания Государственное бюджетное общеобразовательное учреждение «Школа № 1210», города Москвы, по адресу: г. Москва, ул. Живописная, д. 32», выполнена на основании:

- Задания на проектирование;
- раздела «Объемно-планировочные и архитектурные решения»;
- раздела «Технологические решения»;
- Задания на проектирование;
- Медико-технологического задания.

Перечень нормативных документов:

- Постановлением Правительства РФ от 16. 02. 2008 № 87 «О составе разделов проектной документации и требованиях к их содержанию»;
- Федеральным законом РФ от 24.11.1995 № 181-ФЗ «О социальной защите инвалидов в Российской Федерации»;
- Законом г. Москвы от 17.01.2001 № 3 «Об обеспечении беспрепятственного доступа инвалидов и иных маломобильных граждан к объектам социальной, транспортной и инженерной инфраструктур города Москвы»;
- Федеральным законом от 30.12.2009 № 384-ФЗ «Технический регламент о безопасности зданий и сооружений»;
- Федеральным законом от 22.07.2008 № 123-ФЗ «Технический регламент о требованиях пожарной безопасности»(в действующей редакции);
- ГОСТ 12.1.004-91 «Пожарная безопасность. Общие требования»;
- СП 1.13130.2020 «Системы противопожарной защиты. Эвакуационные пути и выходы»;
- СП 3.13130.2009 «Система оповещения и управления эвакуацией людей при пожаре»;
- 104-03 «Проектирование систем оповещения людей о пожаре в зданиях и сооружениях»;
- СП 118.13330.2012 «Общественные здания и сооружения»;
- СП 59.13330.2020 «Доступность зданий и сооружений для маломобильных групп населения»;
- СП 31-102-99 «Требования доступности общественных зданий и сооружений для инвалидов и других маломобильных посетителей»;
- СП 35-101-2001 «Проектирование зданий и сооружений с учетом доступности для маломобильных групп населения. Общие положения»;
- СП 35-103-2001 «Общественные здания и сооружения, доступные маломобильным посетителям»;
- СП 136.13330.2012 «Здания и сооружения. Общие положения проектирования с учетом доступности для маломобильных групп населения»;
- СП 138.13330.2012 «Общественные здания и сооружения, доступные маломобильным группам населения. Правила проектирования»;
- СП 140.13330.2012 «Городская среда. Правила проектирования для маломобильных групп населения»;
- ГОСТ 12.4.026-2015 «Цвета сигнальные, знаки безопасности и разметка сигнальная»;
- ГОСТ Р 52131-2019 «Средства отображения информации знаковые для инвалидов. Технические требования»;
- ГОСТ Р 51261-2017 «Устройства опорные стационарные реабилитационные. Типы и технические требования»;

708П-24-АНО-ОДИ.ТЧ

Изм. Кол.уч. Лист № док. Подпись Дата

Ин в. № по дл.							Текстовая часть	Стадия	Лист	Листов
								П	1	
	Разработал	Юденкова			04.24					
	Н.контроль	Лукашова			04.24					
	ГАП	Фролова			04.24					
	ГИП	Старов			04.24					



комплексное проектирование промышленных и гражданских объектов

ООО "АРТИС"

На территории предусмотрены условия беспрепятственного, безопасного и удобного передвижения МГН по участку к доступным входам в здание с учетом требований СП 42.13330.

Пешеходные пути имеют непрерывную связь с внешними, по отношению к участку, транспортными и пешеходными коммуникациями, остановочными пунктами пассажирского транспорта общего пользования.

Система средств информационной поддержки и навигации предусматривается на всех путях движения, доступных для МГН на часы работы организации (учреждения или предприятия).

Согласно Задания на проектирование и Протокола оперативного совещания по вопросу реализации Городской программы по модернизации объектов образования от 14.12.2023 доступ маломобильных групп населения М1-М4 предусматривается только на 1-й этаж здания школы в помещения коридора с зоной ожидания и санузел для МГН. Зоны доступные для МГН отображены на л.1 графической части.

б) обоснование принятых конструктивных, объемно-планировочных и иных технических решений, обеспечивающих безопасное перемещение инвалидов на объектах, указанных в подпункте "а" настоящего пункта, а также их эвакуацию из указанных объектов в случае пожара или стихийного бедствия;

В рамках капитального ремонта проектом предусмотрено восстановление доступа МГН согласно п. 4.1 СП 136.13330.2012 по варианту Б доступности объекта «Разумное приспособление».

Проектом комплексного капитального ремонта здания общеобразовательного учреждения ГБОУ Школа №1210, перепланировка помещений и здания, а также изменение их функционального назначения, параметров путей эвакуации и эвакуационных выходов – не предусмотрены и соответствуют существующему положению, что соответствует заданию на разработку проектной документации «Капитальный ремонт общеобразовательного учреждения ГБОУ Школа №1210 по адресу: г. Москва, ул. Живописная, д.32» от 24.09.2024г.

Вз ам. ин в. №	согласно п. 4.1 СП 136.13330.2012 по варианту Б доступности объекта «Разумное приспособление». Проектом комплексного капитального ремонта здания общеобразовательного учреждения ГБОУ Школа №1210, перепланировка помещений и здания, а также изменение их функционального назначения, параметров путей эвакуации и эвакуационных выходов – не предусмотрены и соответствуют существующему положению, что соответствует заданию на разработку проектной документации «Капитальный ремонт общеобразовательного учреждения ГБОУ Школа №1210 по адресу: г. Москва, ул. Живописная, д.32» от 24.09.2024г.							
По дп ис и да та								
Ин в. № по дл.								
						708П-24-АНО-ОДИ.ТЧ		Лист
Изм. Кол.уч. Лист № док. Подпись Дата								

Проектными решениями предусмотрены следующие виды работ:

В рамках капитального ремонта доступ МГН в здание школы предусматривается по существующему положению и только через главный вход в осях «7-13/А».

1. Входная группа:

Замена входной группы главного входа, расположенной в осях «7-13/А», включая замену пандуса для МГН и замену ограждений на крыльце, лестнице и на пандусе.

Ступени лестницы имеют одинаковую геометрию и размеры 300x150 мм, на проступях краевых ступеней лестничных маршей нанесены противоскользящие полосы общей шириной 0,1 м, контрастные с поверхностью ступени (желтого цвета) (п.6.2.8 СП 59.13330.2020). Предусмотрено устройство перед входной лестницей за 300мм от края первой ступени тактильных указателей (мнемосхема) согласно ГОСТ Р 52875.

Вдоль обеих сторон лестницы установлены ограждения с поручнями на высоте 0,9 м и 0,5м. Завершающие части поручня длиннее марша на 0,3 м (п.5.1.13 СП 59.13330.2020).

Замена пандуса главного входа, уклоном $i=1:12.5(8\%)$, с ограждением из нержавеющей стали, высота ограждения $h=900$ мм, поручни с нетравмирующим окончанием на высоте $h=900$ мм и $h=700$ мм. Предусмотрен горизонтальный участок размерам не менее $1,5 \times 1,5$ м. Ширина марша пандуса (расстояние между поручнями ограждений пандуса) принята $1,0$ м. Длина одного подъема пандуса не превышает $6,0$ м.

Замена покрытия ступеней, пандуса и площадки главной входной группы на термообработанный гранит с шероховатой поверхностью, не скользящей при намокании и с шириной швов не более 10мм. Поперечный уклон входной площадки составляет 1 — 2%. Входная площадка с пандусом имеют размеры не менее 2,2х2,2м. Входная группа имеет навес. Предусмотрено устройство организованного наружного водоотведения с козырьков.

Входные двери главного входа предусмотрены двустворчатыми с шириной рабочей створки не менее 0,9м.

Тамбур при входе имеет размеры не менее 2,45х1,6 м (п. 6.1.8 СП 59.13330.2020).

В тамбуре и на входной площадке вместо тактильных указателей предусмотрены грязесборные решетки соответствующих размеров и размещения согласно ГОСТ Р 52875 (п 6.1.8 СП 59.13330.2020).

Дренажные и водосборные решетки, устанавливаемые в полу тамбуров или на входных площадках, устанавливаются на одном уровне с поверхностью покрытия пола.

2. Пути передвижения:

Проектом не предусматривается перемещение МГН по этажам здания.

Ширина коридоров здания школы составляет не менее: 2,0м.

Вз ам. ин в. №	В тамбуре и на входной площадке вместо тактильных указателей предусмотрены грязесборные решетки соответствующих размеров и размещения согласно ГОСТ Р 52875 (п 6.1.8 СП 59.13330.2020).							
По дп исъ и да та	Дренажные и водосборные решетки, устанавливаемые в полу тамбуров или на входных площадках, устанавливаются на одном уровне с поверхностью покрытия пола. 2. Пути передвижения: Проектом не предусматривается перемещение МГН по этажам здания. Ширина коридоров здания школы составляет не менее: 2,0м.							
Ин в. № по дл.							708П-24-АНО-ОДИ.ТЧ	Лист
	Изм.	Кол.уч.	Лист	№ док.	Подпись	Дата		

Глубина пространства для маневрирования кресла-коляски перед дверью при открывании от себя составляет не менее 1,2 м, а при открывании к себе - не менее 1,5 м при ширине не менее 1,5 м (п.6.2.2 СП 59.13330.2020).

3. Пути эвакуации:

Эвакуационные пути, используемые маломобильными группами населения, имеют следующую ширину (в свету):

- коридоры не менее 2 м;
- выходы из помещений для МГН не менее 0,9 м;

Высота путей эвакуации не менее 2,7 м.

Эвакуация МГН групп мобильности М1-М3 может осуществляться через главный вход в осях «7-13/А», а также лестничную клетку в осях «15-16/В-Д». Эвакуация МГН групп мобильности М4 может осуществляться только через главный вход в осях «7-13/А».

На путях эвакуации из здания предусмотрены фотолюминисцентные эвакуационные знаки, указывающие направление эвакуации из здания. Знаки располагаются на высоте 2.2м от у.ч.п.

При замене внутренней отделки (полов, потолков, стен, двери) помещений на путях движения и эвакуации МГН, применяемые материалы соответствуют нормативным требованиям и обеспечивают беспрепятственное и безопасное передвижение и эвакуацию инвалидов из всех доступных помещений 1-го этажа, в частности:

- цвет отделки поверхностей стен, полов и потолков предусмотрен контрастных оттенков друг к другу;
- покрытия полов предусмотрено твердым нескользящим с шероховатой поверхностью;
- высота порогов в дверных проемах, на путях передвижения МГН не превышает 0,014 м (п. 6.2.4 СП 59.13330.2020 и п. 9.3.8 СП 1.13130.2020). При необходимости

Вз ам. ин в. №	При замене внутренней отделки (полов, потолков, стен, двери) помещений на путях движения и эвакуации МГН, применяемые материалы соответствуют нормативным требованиям и обеспечивают беспрепятственное и безопасное передвижение и эвакуацию инвалидов из всех доступных помещений 1-го этажа, в частности: - цвет отделки поверхностей стен, полов и потолков предусмотрен контрастных оттенков друг к другу; - покрытия полов предусмотрено твердым нескользящим с шероховатой поверхностью; - высота порогов в дверных проемах, на путях передвижения МГН не превышает 0,014 м (п. 6.2.4 СП 59.13330.2020 и п. 9.3.8 СП 1.13130.2020). При необходимости						Лист
	708П-24-АНО-ОДИ.ТЧ						
По дп исъ и да та							
Ин в. № по дл.							
	Изм.	Кол.уч.	Лист	№ док.	Подпись	Дата	

Конструктивные элементы и устройства внутри зданий, а также декоративные элементы, размещаемые в габаритах путей движения на стенах и других вертикальных поверхностях, кроме пожарного оборудования, выступающего из стены не более чем на 0,20 м, имеют закругленные края и не выступают более чем на 0,1 м на высоте от 0,7 до 2,1 м от уровня пола. При размещении устройств, указателей на отдельно стоящей опоре они не выступают более чем на 0,3 м (п. 6.2.6 СП 59.13330.2020).

Ручки, рычаги, краны и кнопки различных аппаратов следует размещать на высоте 0,85 - 1,1 м от уровня пола, на расстоянии не менее 0,6 м от боковой стены помещения. Приборы для открывания и закрытия дверей, горизонтальные поручни, которыми могут воспользоваться МГН внутри здания, установлены на высоте 1,0м. Выключатели в помещениях предусмотрены на высоте 0,8 м от уровня пола (п. 6.4.2 СП 59.13330.2020).

Приборы для открывания и закрывания дверей, дверные горизонтальные поручни следует располагать на высоте 0,8 - 1,1 м. Свободное пространство со стороны ручки двери должно быть: при открывании от себя - не менее 0,3 м; при открывании к себе - не менее 0,6 м (п 6.1.8 СП 59.13330.2020 и п. 6.4.3 СП 59.13330.2020).

6. Средства информационной поддержки:

В здании предусмотрена замена комплексной системы средств информации и сигнализации об опасности, и осуществляются меры по оснащению здания визуальной, звуковой и тактильной информацией в помещениях, предназначенных для пребывания маломобильных групп населения.

Для решения задач по обеспечению вызывной сигнализацией для МГН объекта предусматривается оснащение двусторонней вызывной сигнализацией и системой двусторонней селекторной связи кабины санузла для МГН (пом. 121) и помещения охраны (пом. 103) (п. 6.5.8 СП 59.13330.2020). В помещении охраны (пом. 103) предусмотрена установка пульта селекторной связи на 6 абонентов (на 6 точек контроля).

Визуальная информация должна располагаться на контрастном фоне с размерами знаков, соответствующими расстоянию распознавания, быть увязана с художественным решением интерьера и располагаться на высоте согласно ГОСТ 51671. Шрифт и уровень контраста надписей принимают по ГОСТ 51671.

Проектом предусмотрены информирующие обозначения помещений и здания, дублирующиеся рельефными знаками, в частности:

- знак обозначения универсальной кабины для МГН возле входа в помещение санузла;
- знак обозначения кнопки экстренного вызова возле унитаза в универсальной кабин для МГН;
- знак обозначения места кратковременного ожидания для МГН в вестибюле 1го этажа;

Вз
ам.
ин
в.
№

По
оп
исъ
и
да
та

Ин
в.
№
по
дл.

- на путях эвакуации из здания предусмотрены фотолюминисцентные эвакуационные знаки, указывающие направление эвакуации из здания. Знаки располагаются на высоте 2.2м от у.ч.п;
- знаки доступности здания для инвалидов по слуху, зрению и передвигающихся на креслах-колясках, на входе в здание;
- тактильную табличку с наименованием здания;
- знак кнопки вызова ситуационной помощи на входе в здание и возле пандуса.

Вся визуальная информация предусмотрена согласно ГОСТ Р 52131, ГОСТ Р 51671.


в) описание проектных решений по обустройству рабочих мест инвалидов (при необходимости);

Согласно Задания на проектирование рабочие места для сотрудников МГН не предусматриваются.

Учебные места для МГН не предусматриваются.

[illegible]

Фрагмент плана 1 этажа со схемой движения МГН

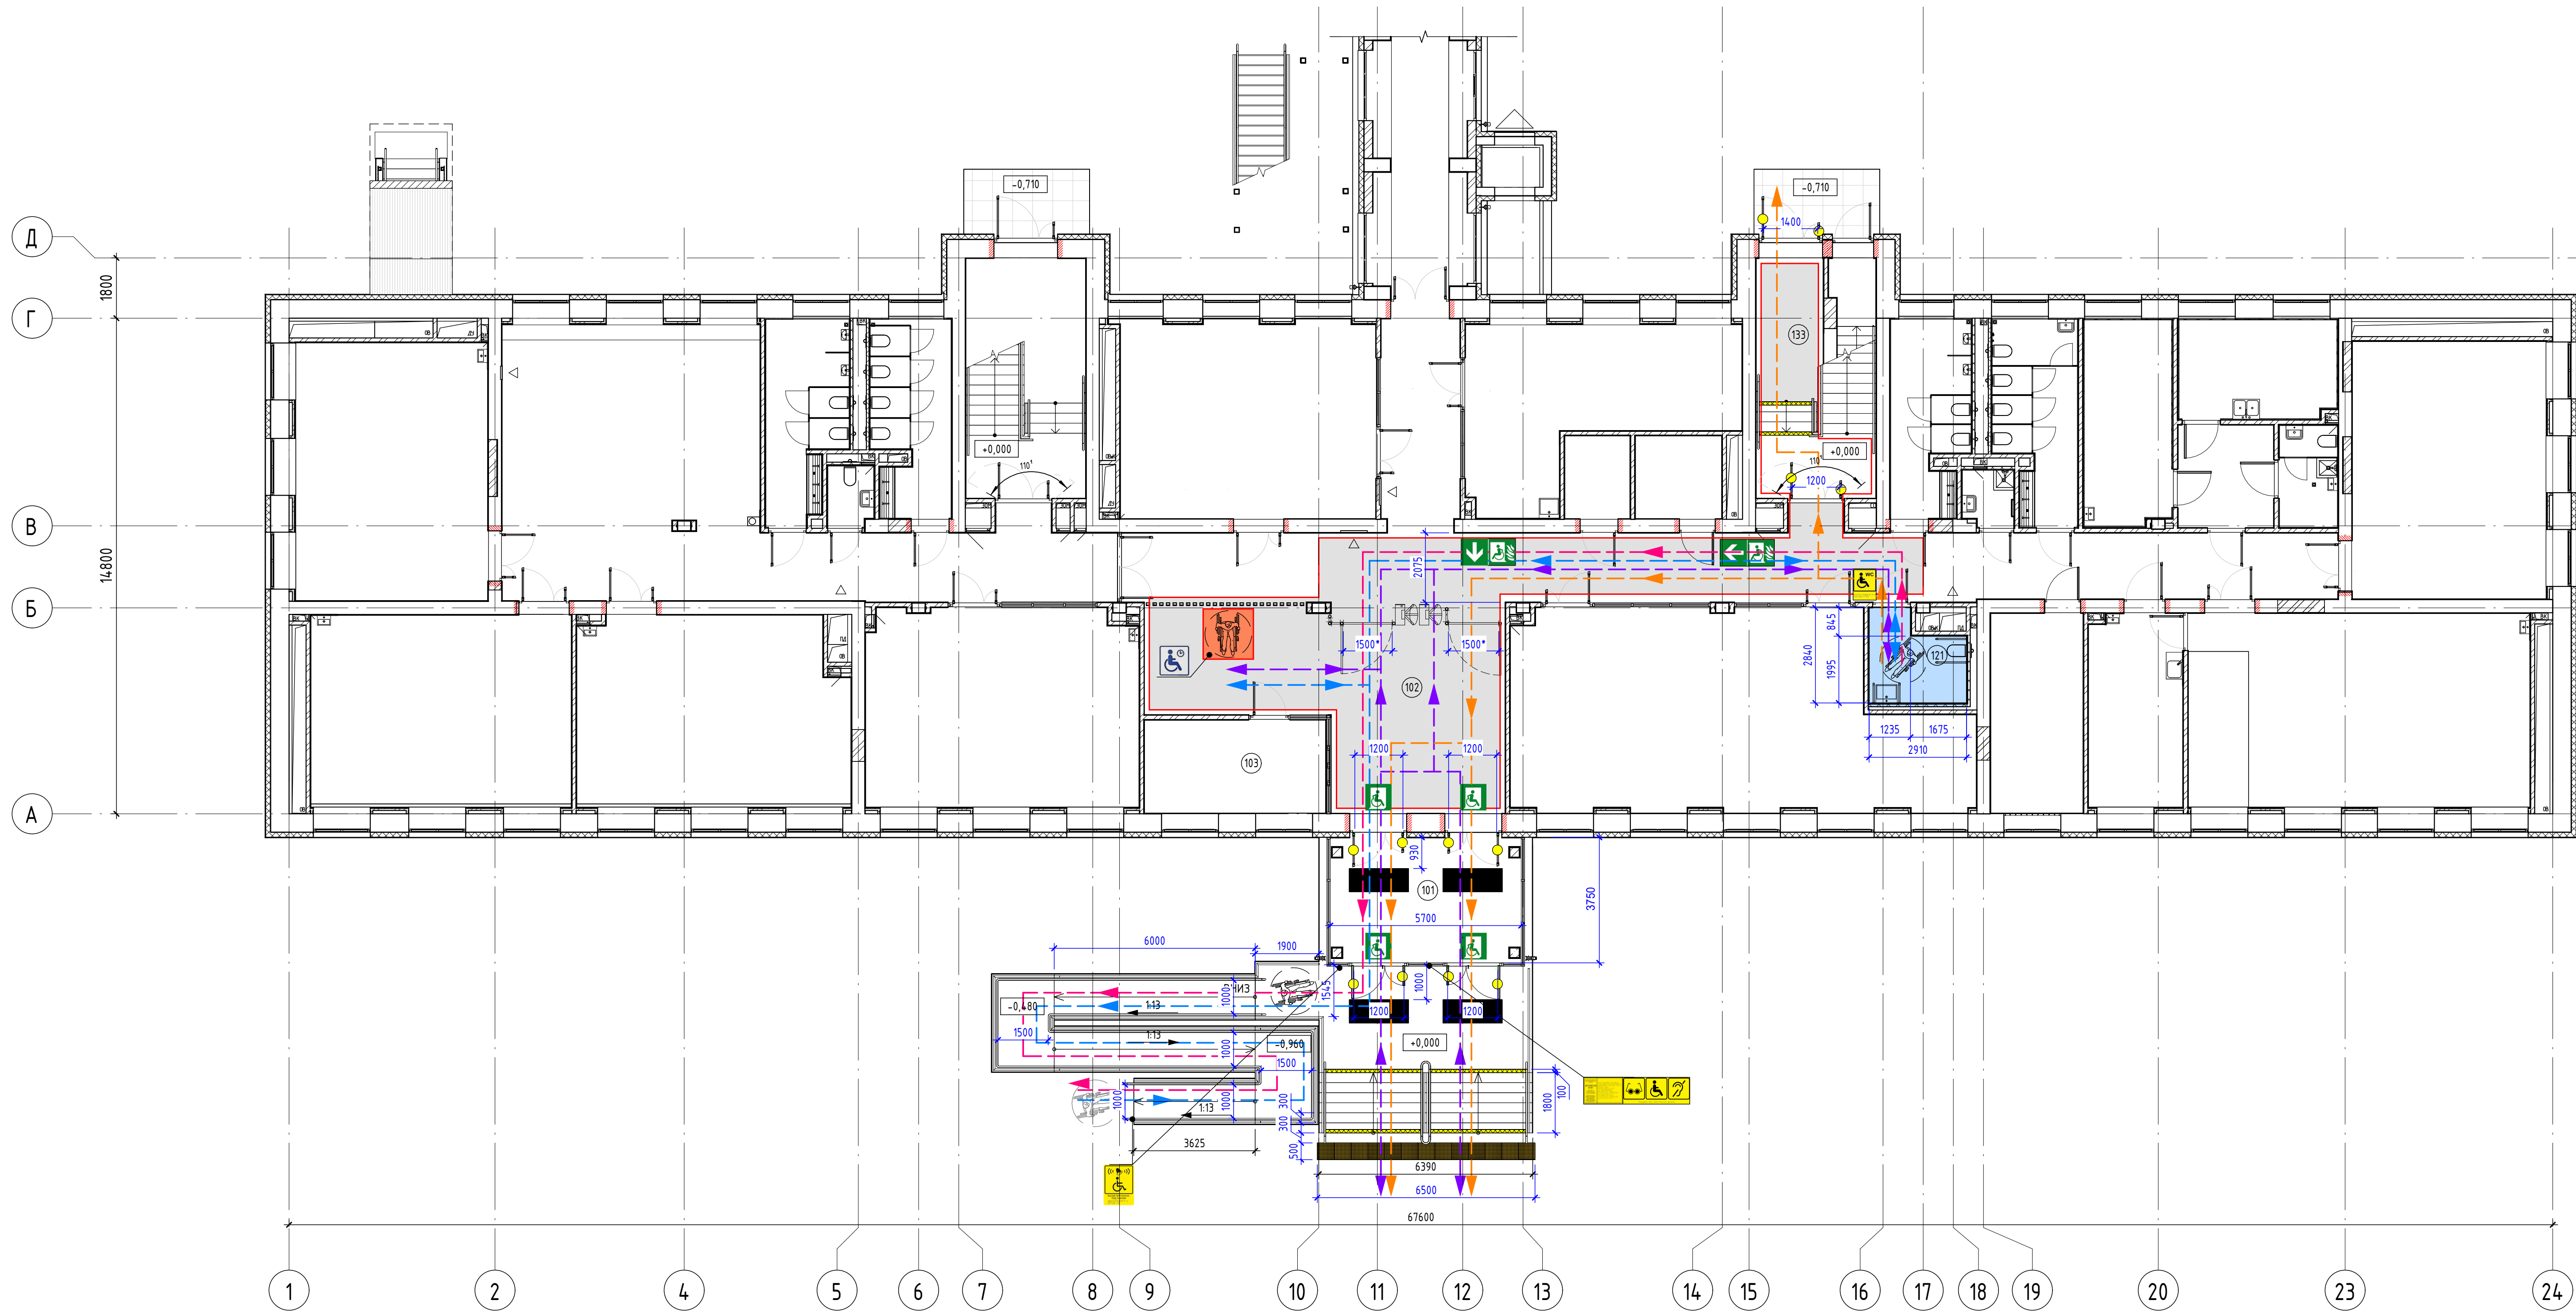

Условные обозначения:

- зоны доступные для МГН
- универсальные кабины для МГН
- пути передвижения МГН групп мобильности М1-М3
- пути передвижения МГН групп мобильности М4
- пути эвакуации МГН группы мобильности М1-М3
- пути эвакуации МГН групп мобильности М4
- Специализированный сервисный знак "Знак доступности объекта для инвалидов, передвигающихся на креслах-колясках", 200х200мм, полистирол(пластик)
- Специализированный сервисный знак "Знак доступности объекта для инвалидов по слуху"
- Специализированный сервисный знак "Знак доступности объекта для инвалидов по зрению"
- Знак "Кнопка вызова ситуационной помощи" на основе ГОСТ Р 52131.2019, пластик
- Тактильные таблички/вывески с азбукой Брайля, желтая, пластик
- Круг для контрастной маркировки дверных проемов, желтый, 200мм
- Знак обозначения обособленного туалета или отдельной кабины, доступных для инвалидов на кресле-коляске
- Знак "Место кратковременного отдыха и ожидания для инвалидов", бело-синий, уф-печать


- Фотолюминесцентный знак "Эвакуационный знак выход для инвалида на кресле-коляске, Звезд", 150х150 мм
- Фотолюминесцентный знак "Путь эвакуации для инвалидов, Стрелка", 150х150 мм
- Фотолюминесцентный знак "Эвакуационный путь для инвалида на кресле-коляске", налево, 150х150мм
- Плита бетонная тротуарная ГОСТ 17608-2017, ГОСТ Р 52875-2018, тактильная, толщина 100 мм, цвет серый
- Накладка на ступень с желтой вставкой в алюминиевой корпусе, 100мм

Примечание:
1. На остекленных дверях и перегородках входных групп предусмотрена контрастная маркировка в виде круга в 2-х уровнях на высотах 0,9-1,0 м и 1,3-1,4 м.
2. Возле дверей входных групп на высоте от 1,4 до 1,6 м предусмотрены тактильно-контрастные таблички с наименованием учреждения, режимом работы, адресом объекта, а также тактильные пиктограммы доступности объекта для инвалидов.
3. Принципиальные схемы расположения оборудования универсальной кабины для МГН см. лист 2.


Экспликация помещений первого этажа			
Номер помеще-ния	Наименование	Площадь, м²	Кат. помеще-ния
101	Танбур	214,6	
102	Вестибюль	141,58	
103	Комната охраны с диспетчерским пунктом	15,14	
104	Учебный кабинет	49,44	
105	Учебный кабинет	46,78	
106	Учебный кабинет	46,19	
107	Учебный кабинет	45,74	
108	Коридор с рекреацией	88,05	
110	Санузел персонала	2,45	
112	Санузел для мальчиков	13,31	
113	Санузел для девочек	13,27	
114	Лестничная клетка (типа Л1)	25,65	
115	Гардероб для обучающихся	45,13	
116	Кабинет с рабочим пространством для учителей тип 1	34,97	
117	Гардеробная комната (для учителей)	4,86	
118	Серверная	6,42	Б3
119	Коридор	8,81	
120	Гардероб для обучающихся	73,54	
121	Санузел для МГН на 1-м этаже	6,85	
122	Электрощитовая	16,55	Б3
123	Лабораторная кабинет химии	16,75	Б3
124	Учебный кабинет для изучения естественных наук - химия	61,08	
125	Кабинет математики	46,06	
126	Приватный (приватный) кабинет	14,05	
127	Помещение для разбора и утилизации отходов, предназначенных для помещений медицинского назначения	3,63	Б4
128	Вестибюль	1,67	
129	Кабинет врача (офис) не менее 5,5 м²	16,25	
130	Санузел для работы с компьютерной техникой	13,79	
131	ПМ	2,51	Б4
132	Санузел для мальчиков	13,00	
133	Лестничная клетка (типа Л1)	25,27	
134	Коридор	4,24	
135	Лестничная клетка (типа Л1)	86,98	
136	Обеденный зал	175,77	
137	Моечная для столовой посуды	215,3	Б4
138	Коридор пищеблока	2,96	
139	Лестничная клетка (типа Л1)	13,25	
140	Коридор пищеблока	5,91	
141	Помещение подготовки блюд к реализации с участком мойки кухонной посуды	26,74	Б4
142	Коридор	18,29	
143	Раздевалка мужская	9,36	
144	Туалет мужской	2,21	
145	Раздевалка женская	13,38	
146	ПМ	2,72	Б4
147	Туалет женский	2,25	
148	Гимнастический зал	71,00	
149	Библиотека	93,09	
150	Книгохранилище	30,00	Б3
151	Лаборатория пищеблока	19,10	Б3

				708П-24-АНО - ОДИ		
				Капитальный ремонт общеобразовательного учреждения ГБОУ Школа № 1210 по адресу: г. Москва, ул. Жилинская, д.32		
Имя	Колос	Лист	МФП	Подп.	Дата	
Разработал	Фролова	12.25				
ГАП	Фролова	12.25				
				Мероприятия по обеспечению доступа инвалидов		
				Страница	Лист	Листов
				1	1	
				Формат А4		
				Всего 1189		


Пом. 159 – универсальная кабина для МГН. Принципиальная схема расположения оборудования для МГН.

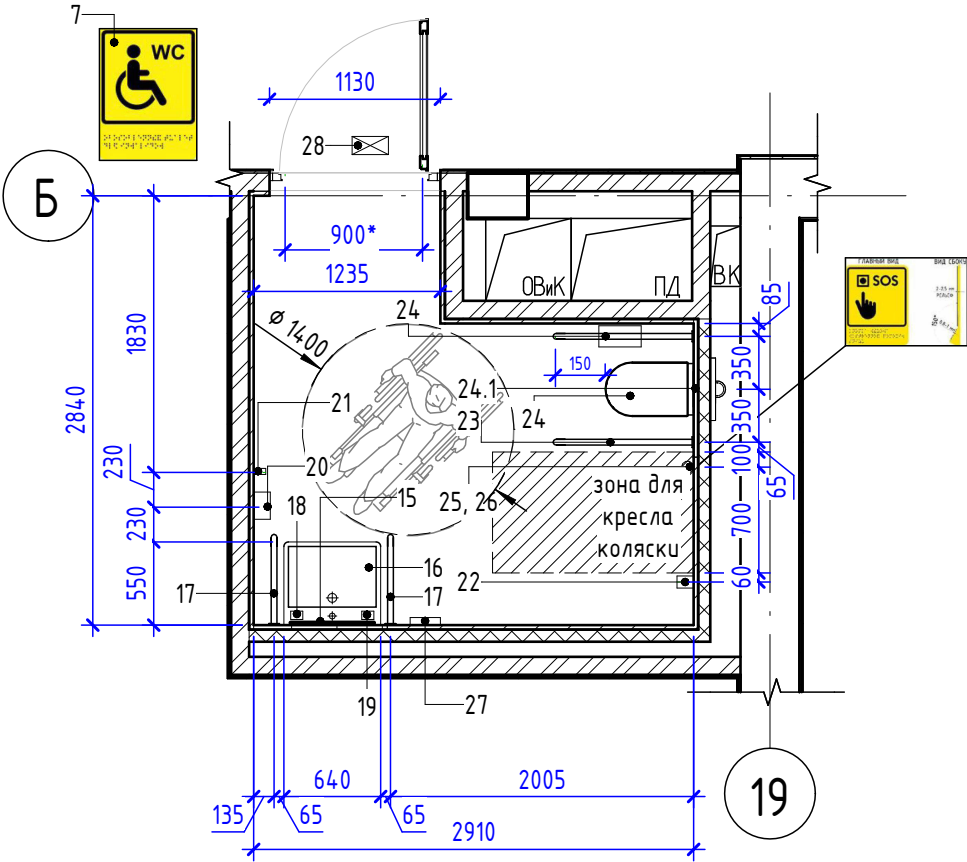

Расположение поручней возле унитаза принято согласно рис.19 ГОСТ 51261-2022.

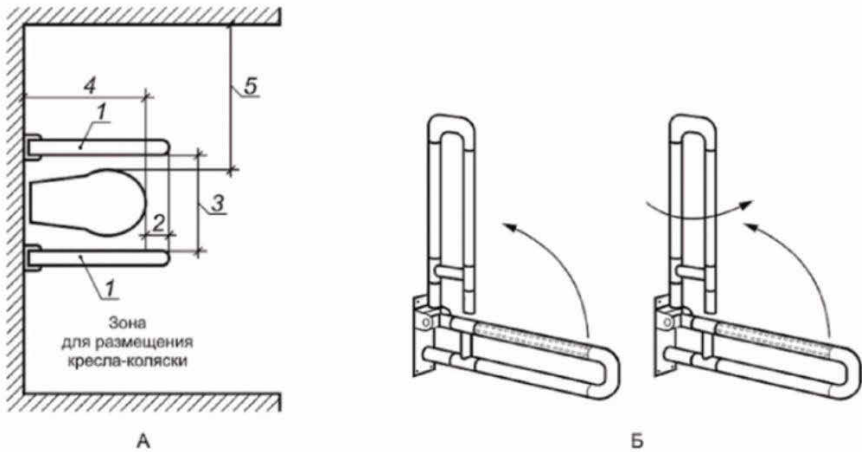

1 – откидной поручень; 2 – вынос поручня – 150 мм; 3 – расстояние между поручнями 700 – 750 мм; 4 – длина зоны для размещения кресла-коляски 700 мм; 5 – ширина зоны для размещения кресла-коляски > 800 мм
А – расположение откидных поручней в универсальной кабине;
Б – конструкция откидных и поворотнo-откидных поручней

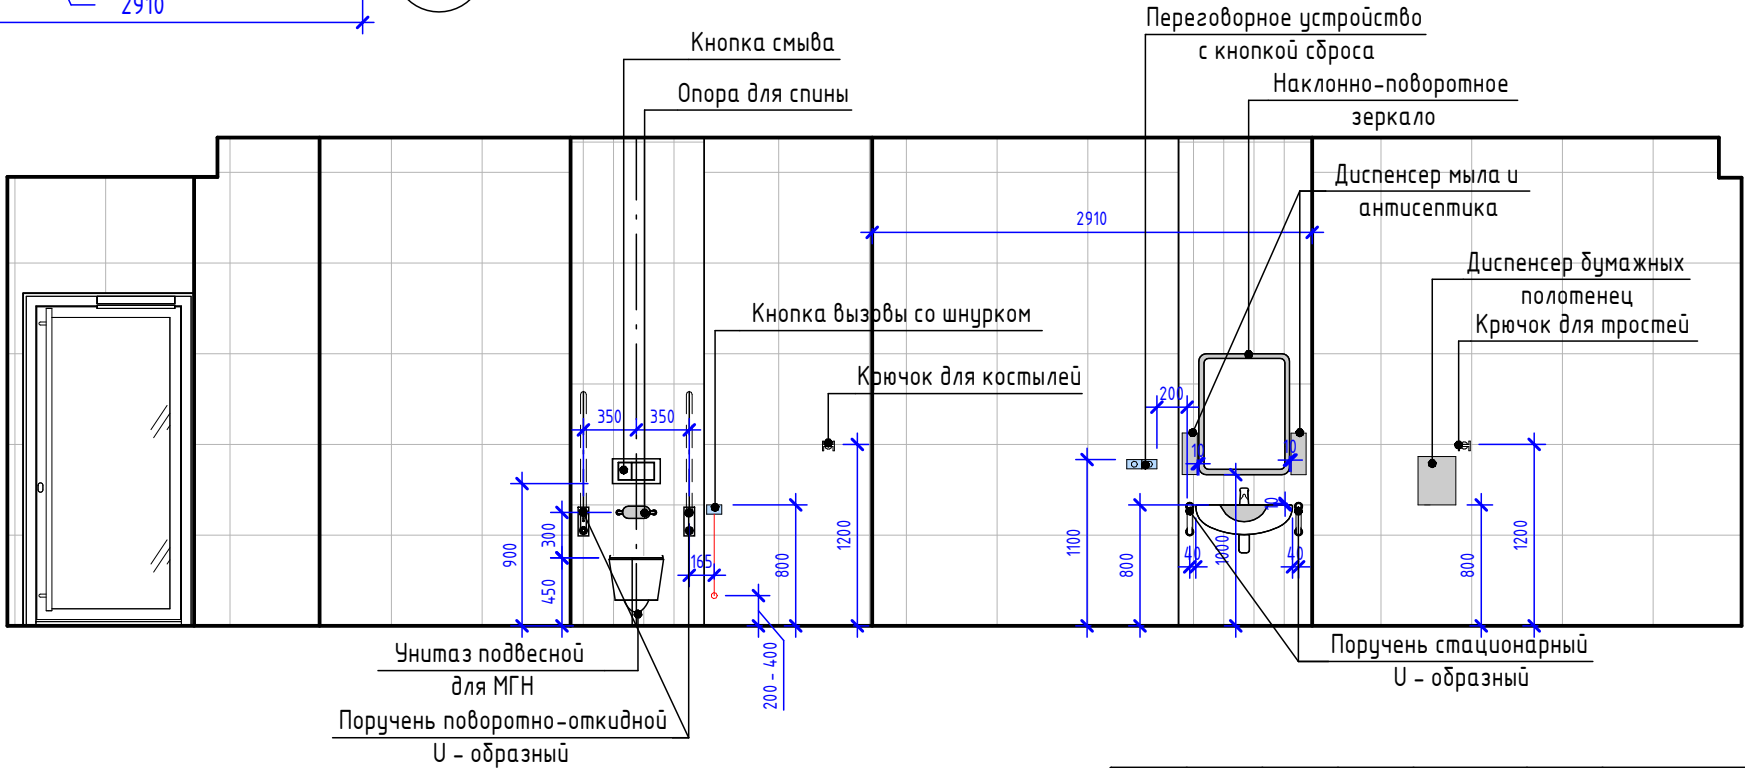


Примечание:
1. Возле дверей на расстоянии 100 мм от края двери и на высоте от 1400мм до 1600мм предусмотрена тактильная пиктограмма "Обособленный туалет или отдельная кабина, доступная для инвалида на кресле-коляске".
2. Над кнопкой тревожной сигнализации предусмотрена тактильная пиктограмма "Кнопка вызова экстренной помощи".
3. Вызывное устройство в кабине предусмотрено согласно ГОСТ 51671 на высоте 0,8 м от ур.ч.п. в зоне унитаза. Кнопка вызова дополняется шнуром красного цвета с рамкой, находящейся вблизи пола на уровне от 0,2 до 0,4 м, которая позволит при падении надежно захватить шнур человеку с нарушенной функцией верхних конечностей.
4. Унитаз предусмотрен на высоте 450мм от ур.ч.п.
5. Раковина предусмотрена на высоте 800мм от ур.ч.п. до верхнего края раковины.
6. Диспенсеры жидкого мыла и бумажных полотенец предусмотрен на высоте 1100мм от ур.ч.п. до низа диспенсеров. Марки диспенсеров см. ТХ
7. Все поручни предусмотрены на высоте 850мм от ур.ч.п.
8. Лист см. совместно со спецификацией санузлов для МГН.

Спецификация оборудования и материалов универсальных кабин для МГН	
Поз.	Наименование
14	Зеркало настенное поворотное 600х400 мм, Арт. 2237
15	Раковина для инвалидов DS Y4 640х550х165 мм
16	Поручень для раковины настенный двухпорный стационарный U-образный 800х230х600мм Y 32, арт. 8071-600
17	Диспенсер для жидкого мыла
18	Диспенсер для антисептика
19	Диспенсер для бумажных полотенец
20	Крючок-держатель для тростей и других вещей, арт. 2202
21	Крючок-держатель для костылей (травмобезопасный)
22	Поручень к унитазу откидной U-образный на стойке, 800х150х850 мм, Y32, Арт. 8090
23	Поручень к унитазу откидной U-образный с бумагодержателем на стойке, 800х250х995 мм, Y32 мм, Арт. 8074
24	Унитаз для инвалидов с инсталляцией в комплекте (унитаз с сиденьем подвесной, рамная инсталляция с креплением, кнопка смыва)
25	Специализированный сервисный тактильно-визуальный знак "Знак обозначения кнопки вызова экстренной помощи", акрил белый матовый 3мм, уф-печать, 150х180мм
26	Кнопка вызова экстренной помощи со шнурком
26	Переговорное устройство с кнопкой сброса
26	Коридорная лампа 2-х цветная индикация

						708П-24-АНО - ОДИ		
						Капитальный ремонт общеобразовательного учреждения ГБОУ Школа № 1210 по адресу: г. Москва, ул. Живописная, д.32		
Изм.	Кол.уч.	Лист	№ док.	Подп.	Дата	Архитектурные решения	Стадия	Лист
Разработал	Юденкова	Юденкова	12.25				П	2
ГАП	Фролова		12.25					
Н.Контроль	Лукашова		12.25			Принципиальная схема расположения оборудования универсальной кабины для МГН.		
ГИП	Старов		12.25					

Схема организации земельного участка с указанием путей перемещения маломобильных групп населения М1-М3, М4 М 1:200

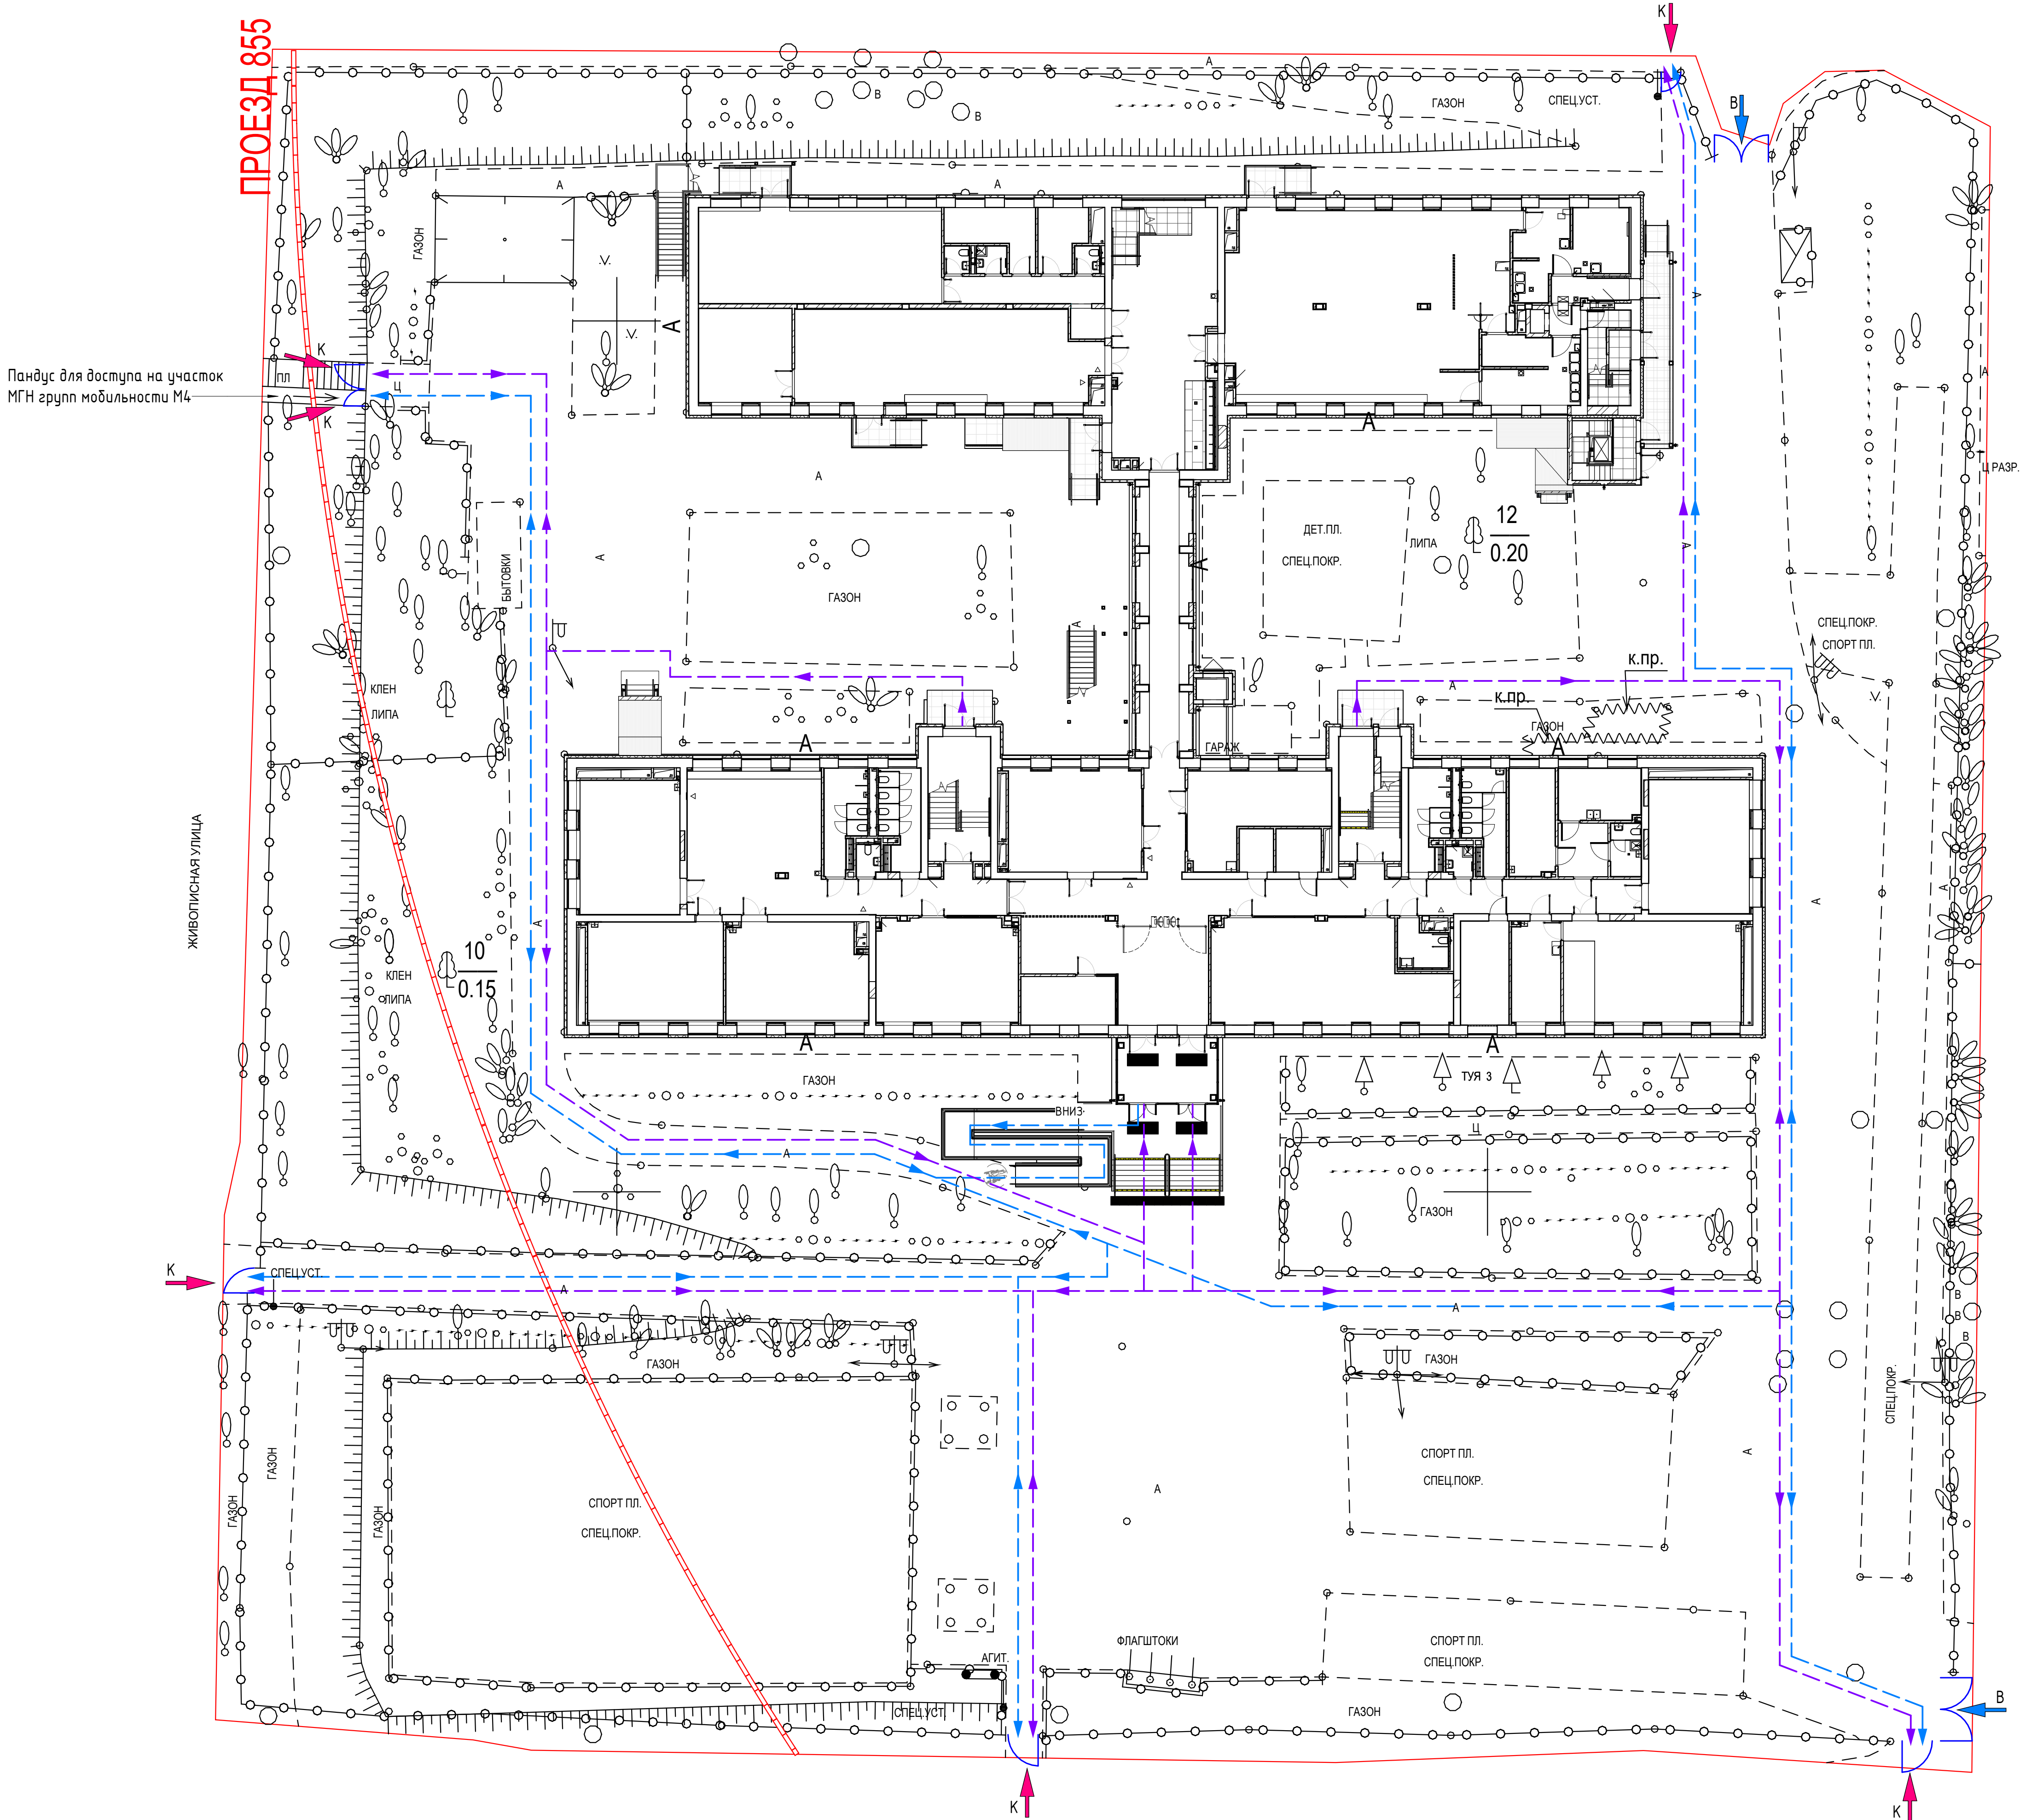

Условные обозначения:

- Граница участка
- Калитки
- Ворота
- Пути передвижения МГН групп мобильности М1-М3
- Пути передвижения МГН групп мобильности М4

						708П-24-АНО - ОДИ		
						Капитальный ремонт общеобразовательного учреждения ГБОУ Школа № 1210 по адресу: г. Москва, ул. Животисная, д.32		
Изм.	Жел.ч.	Лист	№ док.	Подп.	Дата	Мероприятия по обеспечению доступа инвалидов	Стадия	Лист
Разработал	Юденкова	12.25					П	3
ГАП	Фролова	12.25						
						Схема организации земельного участка с указанием путей перемещения маломобильных групп населения М 1:200		
Н.Контроль	Лукашова	12.25						
ГИП	Старов	12.25						