



Демонтаж четвертей оконных проемов в осях 5-7/Г, 9/Г и 14/Г, 16-18/Г

Демонтаж четвертей оконных проемов, за исключением проемов, прилегающим к лестничным клеткам учебного корпуса

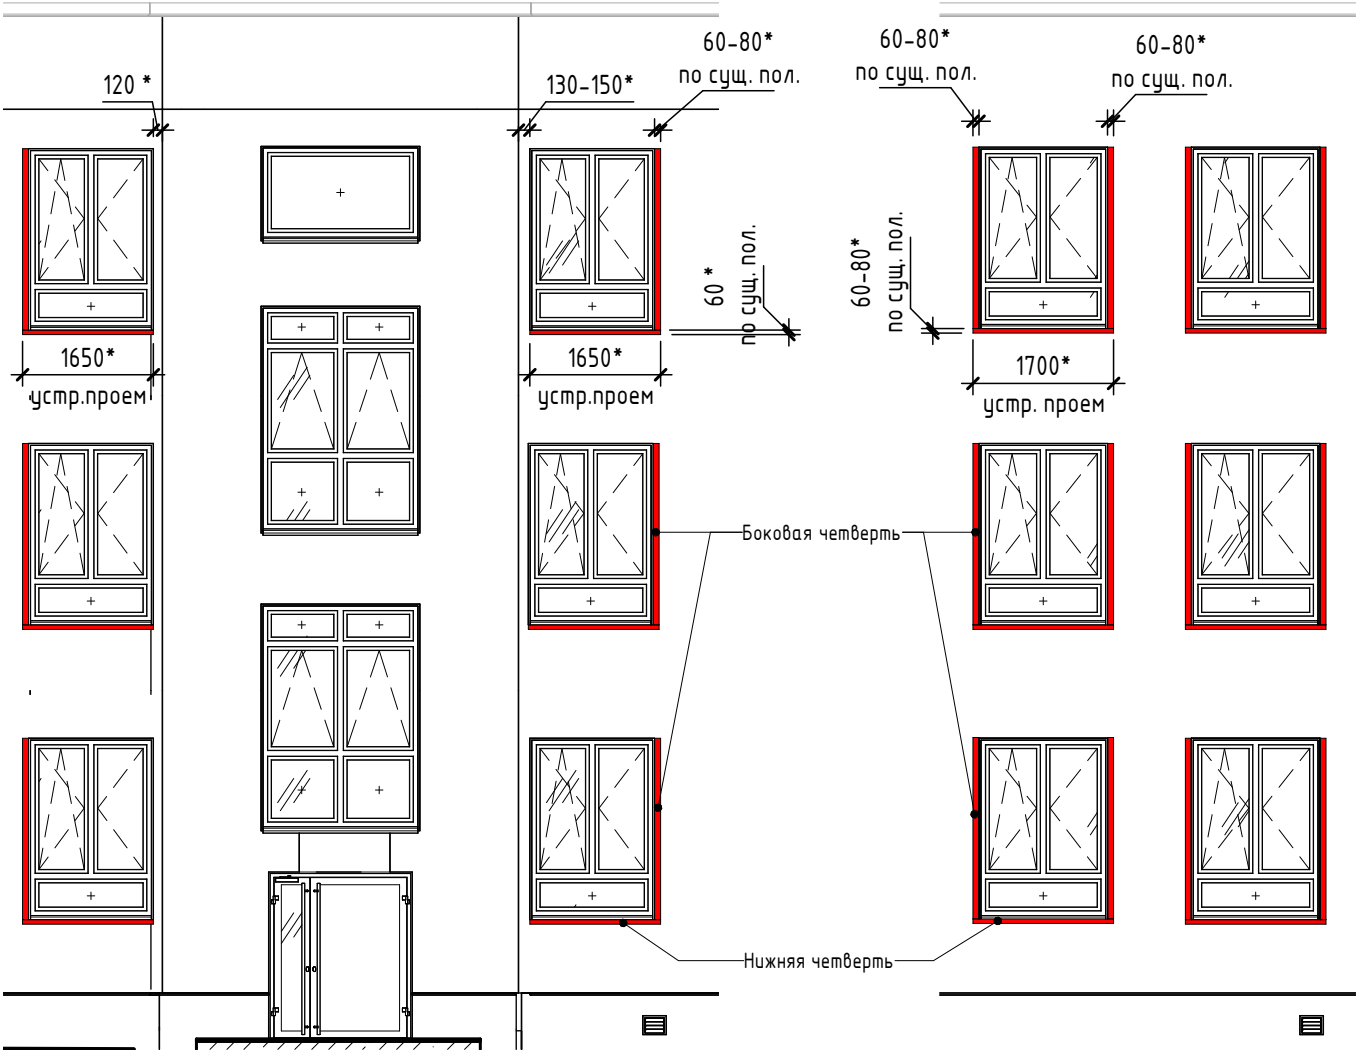

Примыкание к оконному блоку с недемонтируемой четвертью

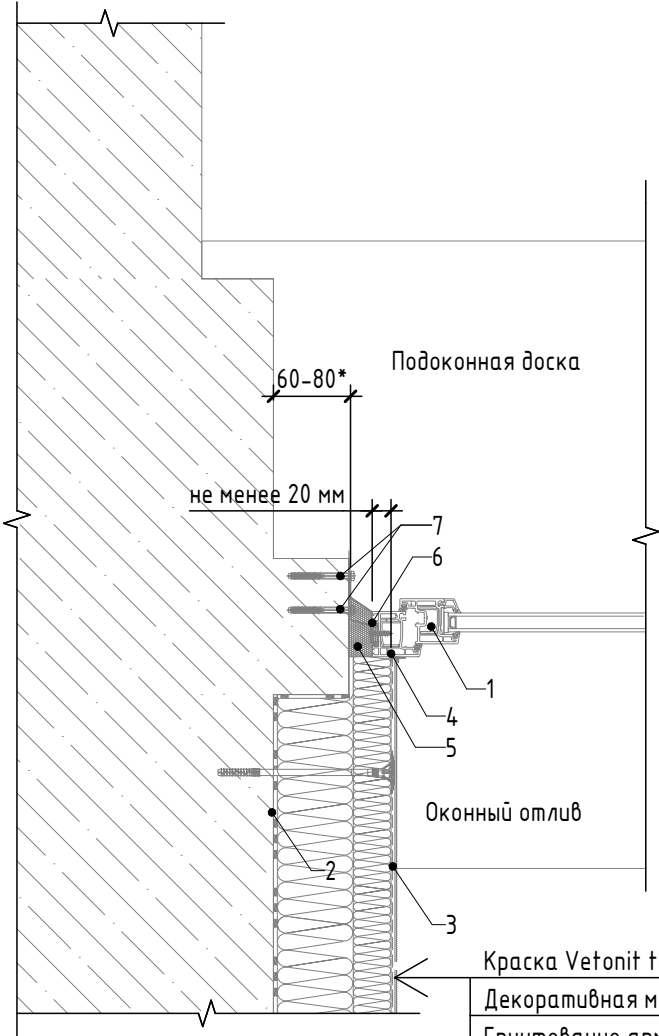

- 1. Оконный блок (показан условно)
- 2. Тарельчатый дюбель
- 3. Угловой элемент с сеткой
- 4. Профиль примыкания
- 5. Пенополистирол ПСБ-С
- 6. Гибкая анкерная пластина
- 7. Дюбель распорный

Условные обозначения:

- Полностью демонтируемая оконная четверть
- УСТР. ПРОЕМ - минимальный устраиваемый проем под новый оконный блок
- ПО СУЩ. ПОЛ. - по существующему положению, уточнить размер после зачистки отделки и монтажных зазоров

Ведомость объема работ по демонтажу оконных четвертей			
№	Наименование работ	Ед.изм.	Объем работ
1	Демонтаж нижних и боковых оконных четвертей	п.м.	1407,93

Краска Vetonit ton Silikat(или аналог);	
Декоративная минеральная штукатурка Weber.min Шуба(2 мм)	-5-8 мм
Грунтование армирующего слоя - Vetonit Prim Facade;	
Армирующий слой - Weber.Therm S100	
со стеклосеткой - Weber.therm 2000 (крепикс 2000) 55м;	-4-5 м
МВ-утеплитель (q0=110-130 кг/м3)	-150 мм
Клеевой слой	
Существующая керамзитобетонная панель	

						708П-24-АНО - АР.РД			
						Капитальный ремонт общеобразовательного учреждения ГБОУ Школа № 1210 по адресу: г. Москва, ул. Живописная, д.32			
Изм.	Кол.уч.	Лист	№ док.	Подп.	Дата				
Разработал	Юденкова				06.26	Архитектурные решения	Стадия	Лист	Листов
ГАП	Фролова				06.26		П	53.9	
Н.Контроль	Лукашова				06.26	Демонтаж оконных четвертей	 000 "АРТИС"		
ГИП	Старов				06.26				