



АРТИС
Артис - искусство проектирования

109341, г. Москва, ул. Марксистская, дом 3, стр. 1

+7 (495) 647-85-99

mail@rosartis.ru

rosartis.ru



Экз. № _____

Заказчик: АНО «РГТ»

**Капитальный ремонт общеобразовательного
учреждения ГБОУ Школа № 1210 по адресу:
г.Москва, ул. Живописная д. 32**

РАБОЧАЯ ДОКУМЕНТАЦИЯ

**«Мероприятия по обеспечению доступа инвалидов к объектам
капитального строительства»**

708/П-24-АНО-ОДИ



АРТИС
Артис - искусство проектирования

109341, г. Москва, ул. Марксистская, дом 3, стр. 1

+7 (495) 647-85-99

mail@rosartis.ru

rosartis.ru



Экз. № _____

Заказчик: АНО «РГТ»

**Капитальный ремонт общеобразовательного
учреждения ГБОУ Школа № 1210 по адресу:
г. Москва, ул. Живописная д. 32**

РАБОЧАЯ ДОКУМЕНТАЦИЯ

**«Мероприятия по обеспечению доступа инвалидов к объектам
капитального строительства»**

708/П-24-АНО-ОДИ

Генеральный директор:



Цибизов В.В.

Ведомость чертежей

Лист	Наименование	Примечание
0.ОДИ	Ведомость чертежей	
1.ОДИ	Фрагмент план 1-го этажа. Схема передвижения и эвакуации маломобильных групп населения М1-М3, М4	
2.ОДИ	Принципиальная схема расположения оборудования универсальной кабины для МГН.	
3.ОДИ	Схема организации земельного участка с указанием путей перемещения маломобильных групп населения М 1.200	

Общие указания :

- Объект образования г. Москвы (общеобразовательное учреждение ГБОУ Школа № 1210), расположен по адресу: г. Москва, ул. Живописная, д. 32. Здание 3-х этажное с подвалом. Доступ маломобильных групп населения М1-М4 предусматривается по существующему положению только на 1-й этаж, в следующие помещения: вестибюль и санузел для МГН.
- Перечень нормативных документов, использованных при разработке рабочей проектной документации.
 - Постановление Правительства РФ от 16.02.2008 № 87 ¼О составе разделов проектной документации и требованиях к их содержанию ½;
 - Федеральный закон РФ от 24.11.1995 № 181-ФЗ ¼О социальной защите инвалидов в Российской Федерации ½;
 - Закон г. Москвы от 17.01.2001 № 3 ¼Об обеспечении беспрепятственного доступа инвалидов и иных маломобильных граждан к объектам социальной, транспортной и инженерной инфраструктур города Москвы ½;
 - Федеральный закон от 30.12.2009 № 384-ФЗ ¼Технический регламент о безопасности зданий и сооружений ½;
 - Федеральный закон от 22.07.2008 № 123-ФЗ ¼Технический регламент о требованиях пожарной безопасности ½в действующей редакции ½;
 - ГОСТ 12.1.004-91 ¼Пожарная безопасность. Общие требования ½;
 - СП 1.13130.2020 ¼Системы противопожарной защиты. Эвакуационные пути и выходы ½;
 - СП 3.13130.2009 ¼Система оповещения и управления эвакуацией людей при пожаре ½;
 - 104-03 ¼Проектирование систем оповещения людей о пожаре в зданиях и сооружениях ½;
 - СП 118.13330.2012 ¼Общественные здания и сооружения ½;
 - СП 59.13330.2020 ¼Доступность зданий и сооружений для маломобильных групп населения ½;
 - СП 31-102-99 ¼Требования доступности общественных зданий и сооружений для инвалидов и других маломобильных посетителей ½;
 - СП 35-101-2001 ¼Проектирование зданий и сооружений с учетом доступности для маломобильных групп населения. Общие положения ½;
 - СП 35-103-2001 ¼Общественные здания и сооружения, доступные маломобильным посетителям ½;
 - СП 136.13330.2012 ¼Здания и сооружения. Общие положения проектирования с учетом доступности для маломобильных групп населения ½;
 - СП 138.13330.2012 ¼Общественные здания и сооружения, доступные маломобильным группам населения. Правила проектирования ½;
 - СП 140.13330.2012 ¼Городская среда. Правила проектирования для маломобильных групп населения ½;
 - ГОСТ 12.4.026-2015 ¼Цвета сигнальные, знаки безопасности и разметка сигнальная ½;
 - ГОСТ Р 52131-2019 ¼Средства отображения информации знаковые для инвалидов. Технические требования ½;
 - ГОСТ Р 51261-2017 ¼Устройства опорные стационарные реабилитационные. Типы и технические требования ½;
 - ГОСТ Р 50602-93 ¼Кресла-коляски. Максимальные габаритные размеры ½;
 - ГОСТ Р 52875-2018 ¼Указатели тактильные наземные для инвалидов по зрению. Технические требования ½;
 - ГОСТ Р 51671-2020 ¼Средства связи и информации технические общего пользования, доступные для инвалидов ½и другими действующими нормативными правовыми актами.
- Перечень мероприятий, предусмотренный разделом:
 - Замена указателей и оборудования в рамках замены главной входной группы в осях "7-13/10", включая замену ограждений;
 - Проектом не предусмотрено перемещение МГН по этажам здания;
 - Эвакуационные пути, используемые маломобильными группами населения предусмотрены с шириной в свету: коридоры – не менее 2,0м, выходы из помещений для МГН – не менее 0,9 м;
 - Эвакуация групп мобильности М1-М3 осуществляется через выход в осях "7-13/А" и выход через лестничную клетку в осях "15-16/В-Д", эвакуация групп мобильности М4 осуществляется только через выход в осях "7-13/А";
 - На путях эвакуации из здания предусмотрены фотoluminesцентные эвакуационные знаки, указывающие направление эвакуации из здания. Знаки располагаются на высоте 2.2м от у.ч.п;
 - Высота порогов в дверных проемах, на путях передвижения МГН не превышает 0,014м;
 - На 1-ом этаже предусмотрена универсальная уборная кабина, доступная для всех категорий маломобильных групп населения, в т.ч. для инвалидов-колясочников;
 - Помещение универсальной кабины, предназначенное для МГН, оборудовано системой двухсторонней громкоговорящей связи;
 - На 1-м этаже предусмотрено место для кратковременного отдыха и ожидания МГН на два-три места в вестибюле при входе;
 - Проектом предусмотрены информирующие обозначения помещений и здания, дублирующие рельефными знаками – тактильно-визуальные схемы;
 - Приборы для открывания и закрывания дверей, дверные горизонтальные поручни располагаются на высоте 0,8 – 1,1 м.
- Данный раздел смотреть совместно с разделами АР, КР и МГН.

Согласовано

Взам. инв. №


Подп. и дата

Инв. № подл.

10


708П-24-АНО – ОДИ

Капитальный ремонт общеобразовательного учреждения ГБОУ Школа № 1210 по адресу: г. Москва, ул. Живописная, д.32

 Разработал	Юденкова		12.25	Мероприятия по обеспечению доступа	Стадия	Лист	Листов
ГАП	Фролова		12.25		Р	0.ОДИ	
Н.Контроль	Лукашова		12.25	Ведомость чертежей		ООО "АРТИС"	
ГИП	Фролова		12.25				

Ведомость чертежей

Фрагмент плана 1 этажа со схемой движения МГН

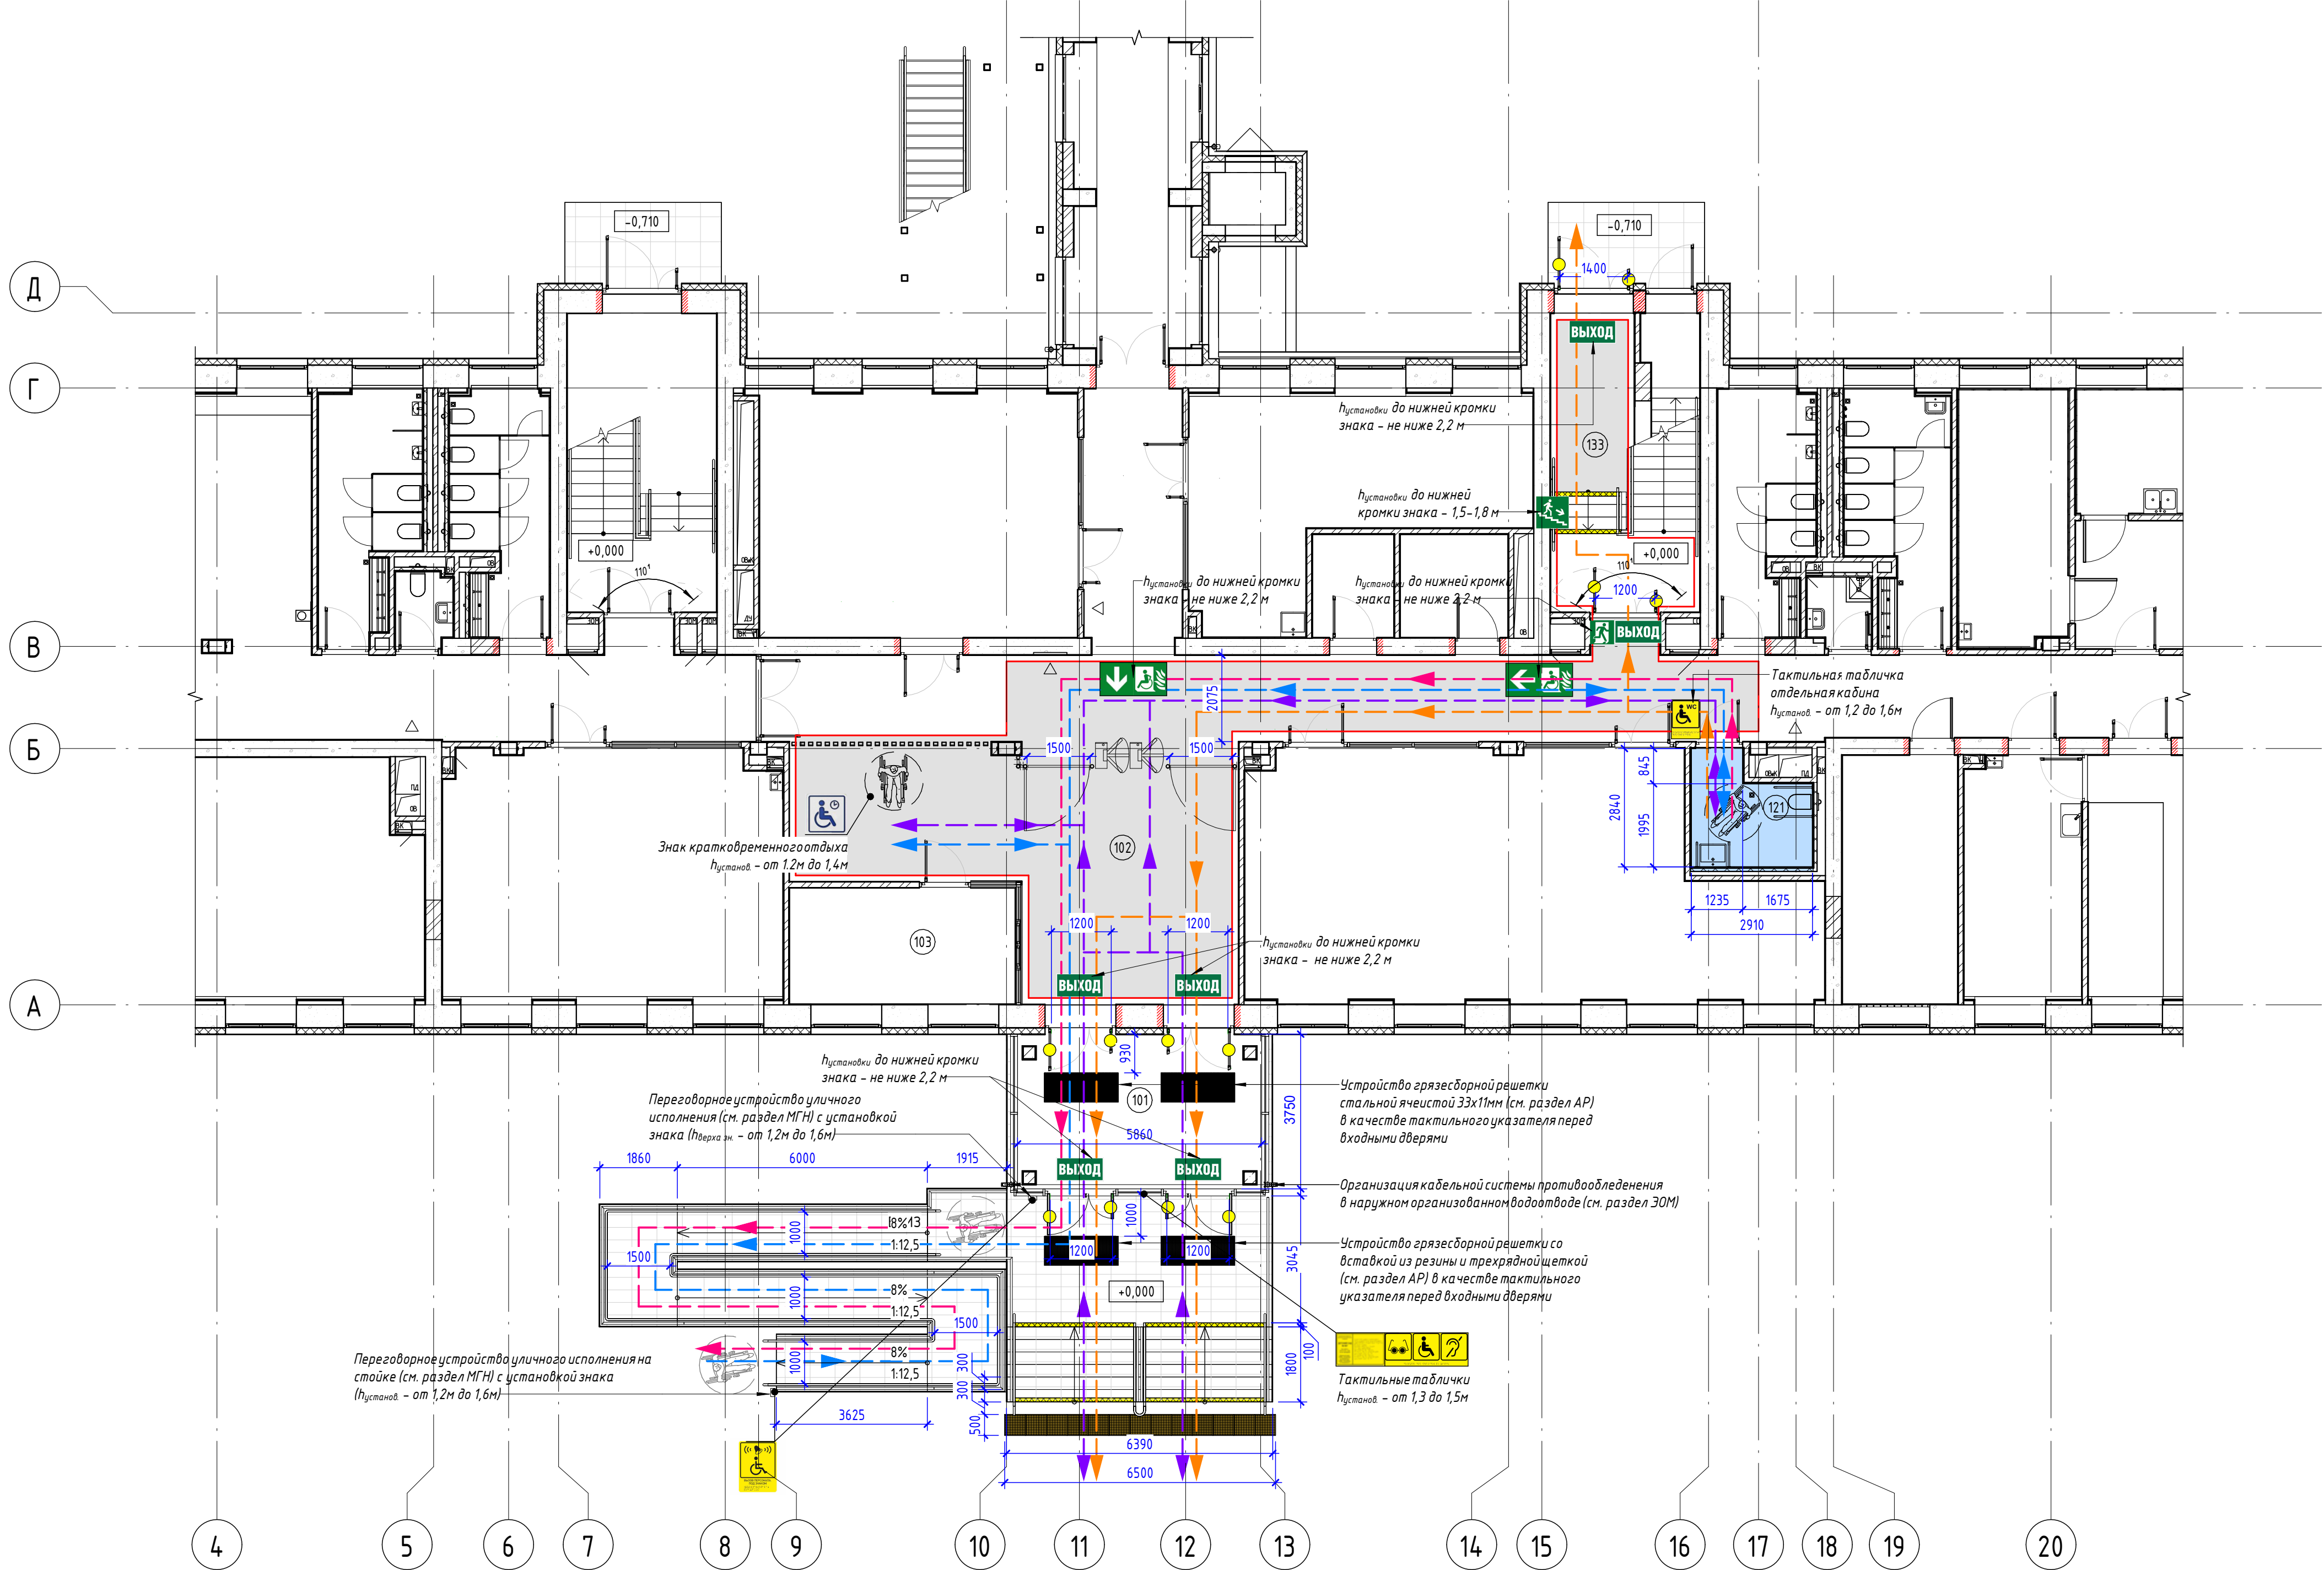

Экспликация помещений первого этажа

Номер помеще-ния	Наименование	Площадь, м²	Кат. поме-ще-ния
101	Тамбур	22,45	
102	Вестибюль	141,58	
103	Комната охраны с диспетчерским пунктом	15,14	
121	Санузел для МГН на 1-м этаже	6,85	

Условные обозначения:

- зоны доступные для МГН
- универсальные кабины для МГН
- пути передвижения МГН групп мобильности М1-М3
- пути передвижения МГН групп мобильности М4
- пути эвакуации МГН группы мобильности М1-М3
- пути эвакуации МГН группы мобильности М4
- Специализированный сервисный знак "Знак доступности объекта для инвалидов, передвигающихся на креслах-колясках", 200х200мм, полистирол(пластик)
- Специализированный сервисный знак "Знак доступности объекта для инвалидов по слуху"
- Специализированный сервисный знак "Знак доступности объекта для инвалидов по зрению"
- Знак "Кнопка вызова ситуационной помощи" на основе ГОСТ Р 52131.2019, пластик
- Тактильные таблички/вывески с азбукой Брайля, желтая, пластик
- Круг для контрастной маркировки дверных проемов, желтый, d200мм
- Знак обозначения обособленного туалета или отдельной кабины, доступных для инвалидов на кресле-коляске
- Знак "Место кратковременного отдыха и ожидания для инвалидов", бело-синий, уф-печать
- ВЫХОД** - Фотолюминисцентный знак "Указатель выхода", 150х300 мм
- Фотолюминисцентный знак "Выход здесь (правосторонний)", 150х150 мм
- Фотолюминисцентный знак "Направление к эвакуационному выходу по лестнице вниз", 150х150 мм
- Фотолюминисцентный знак "Путь эвакуации для инвалидов, Стрелка", 150х150 мм
- Фотолюминисцентный знак "Эвакуационный путь для инвалида на кресле-коляске", налево, 150х150мм
- Плита бетонная тротуарная ГОСТ 17608-2017, ГОСТ Р 52875-2018, тактильная, толщина 100 мм, цвет серый (см. раздел АР)
- Накладка на ступень с желтой вставкой в алюминиевой корпусе, 100мм

Примечание:
1. На остекленных дверях и перегородках входных групп предусмотрена контрастная маркировка в виде круга в 2-х уровнях на высотах 0,9-1,0м и 1,3-1,4 м.
2. Возле дверей входных групп на высоте от 1,4 до 1,6 м предусмотрены тактильно-контрастные таблички с наименованием учреждения, режимом работы, адресом объекта, а также тактильные пиктограммы доступности объекта для инвалидов.
3. Принципиальные схемы расположения оборудования универсальной кабины для МГН см. лист 2.
4. Оборудование системы вызова и сигнализации МГН учтено разделом МГН.



Спецификация материалов и знаковых средств отображения информации для инвалидов			
№	Наименование работ	Ед.изм.	Объем работ
1	Специализированный сервисный знак "Знак доступности объекта для инвалидов, передвигающихся на креслах-колясках", 200х200мм, полистирол(пластик), арт.4690-200, ПТК "Доступная страна"	шт.	1
2	Специализированный сервисный знак "Знак доступности объекта для инвалидов по слуху", 200х200мм, полистирол(пластик), арт.4691-200, ПТК "Доступная страна"	шт.	1
3	Специализированный сервисный знак "Знак доступности объекта для инвалидов по зрению", 200х200мм, полистирол(пластик), арт.4692-150, ПТК "Доступная страна"	шт.	1
4	Знак "Кнопка вызова ситуационной помощи" на основе ГОСТ Р 52131.2019, пластик, 200х200мм	шт.	2
5	Тактильные таблички/вывески с азбукой Брайля, желтая, пластик, 400х600мм	шт.	1
6	Круг для контрастной маркировки дверных проемов в двух уровнях с обеих сторон дверной створки, желтый, 200мм	шт.	48
7	Знак обозначения обособленного туалета или отдельной кабины, доступных для инвалидов на кресле-коляске, акрил белый матовый 3мм, уф-печать, 150х180мм	шт.	1
8	Знак "Место кратковременного отдыха и ожидания для инвалидов", бело-синий, уф-печать, 150х150мм	шт.	1
9	Фотолюминисцентный знак "Указатель выхода", 150х300 мм, ПВХ	шт.	6

Спецификация материалов и знаковых средств отображения информации для инвалидов			
№	Наименование работ	Ед.изм.	Объем работ
10	Фотолюминисцентный знак "Выход здесь (правосторонний)", 150х300 мм, ПВХ	шт.	1
11	Фотолюминисцентный знак "Направление к эвакуационному выходу по лестнице вниз", 150х150мм, ПВХ	шт.	1
12	Фотолюминисцентный знак "Путь эвакуации для инвалидов, Стрелка", 150х150мм, ПВХ	шт.	2
13	Фотолюминисцентный знак "Эвакуационный путь для инвалида на кресле-коляске", налево, 150х150мм, ПВХ	шт.	2
14	Плита бетонная тротуарная 500х500мм, ГОСТ 17608-2017, ГОСТ Р 52875-2018, тактильная, толщина 100 мм, цвет серый	шт.	3,25
15	Накладка на ступень с желтой вставкой в алюминиевой корпусе, ширина 100мм	п.м.	16


						708П-24-АНО - ОДИ		
						Капитальный ремонт общеобразовательного учреждения ГБОУ Школа № 1210 по адресу: г. Москва, ул. Жилинская, д.32		
Изм.	Жол.уч.	Лист	№ док.	Подп.	Дата	Мероприятия по обеспечению доступа инвалидов	Стадия	Лист
Разработал	Юденкова	12.25					Р	1.ОДИ
ГАП	Фролова	12.25				Фрагмент план 1-го этажа. Схема передвижения и эвакуации маломобильных групп населения М1-М3, М4		
Н.Контроль	Лукашова	12.25						
ГИП	Старов	12.25						

Пом. 159 – универсальная кабина для МГН. Принципиальная схема расположения оборудования для МГН.

Расположение поручней возле унитаза принято согласно рис.19 ГОСТ 51261-2022.

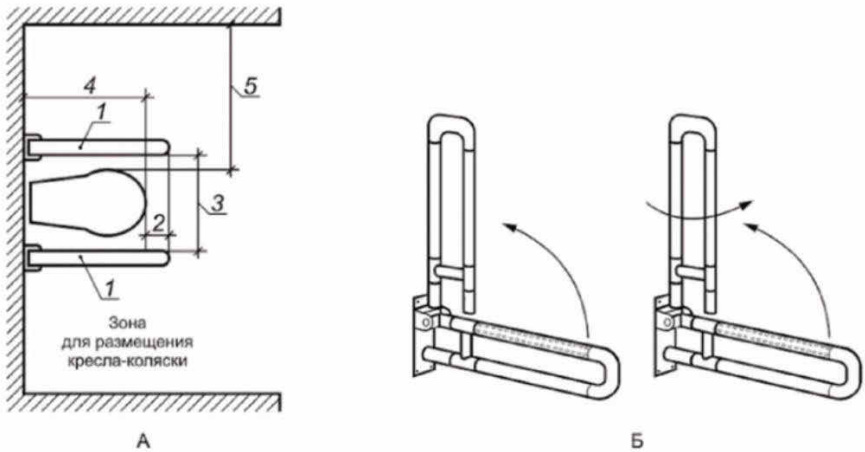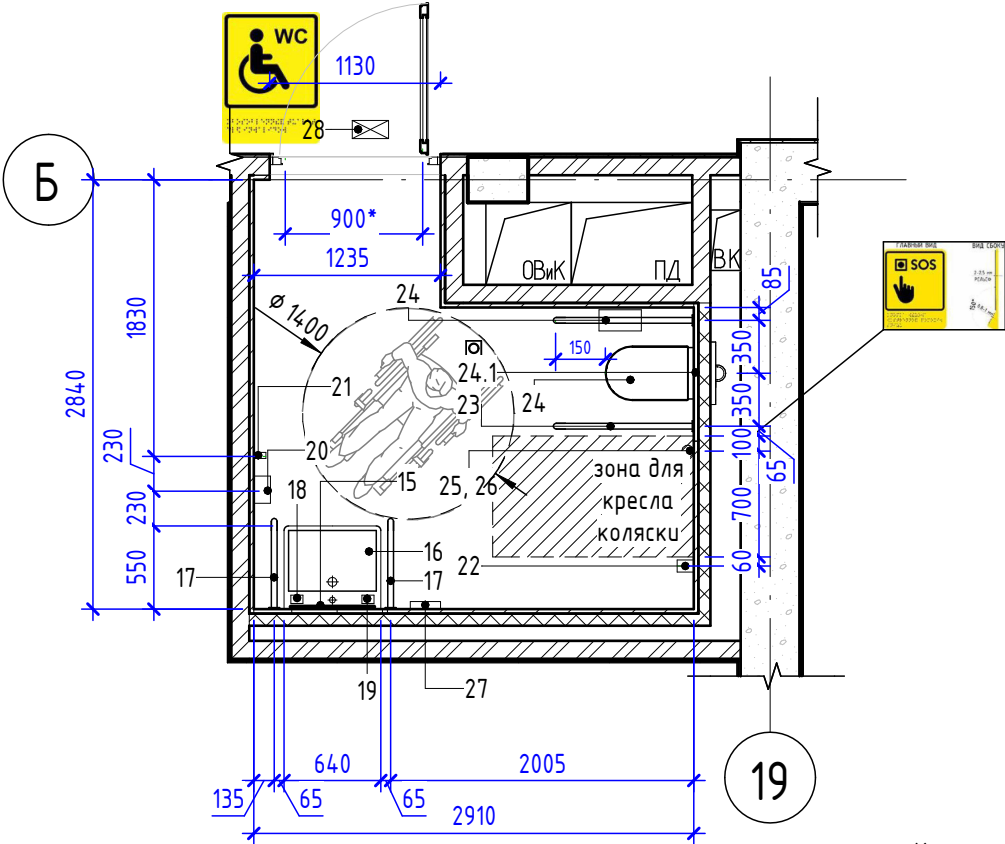

1 – откидной поручень; 2 – вынос поручня – 150 мм; 3 – расстояние между поручнями 700 – 750 мм; 4 – длина зоны для размещения кресла-коляски 700 мм; 5 – ширина зоны для размещения кресла-коляски > 800 мм
А – расположение откидных поручней в универсальной кабине;
Б – конструкция откидных и поворотных-откидных поручней

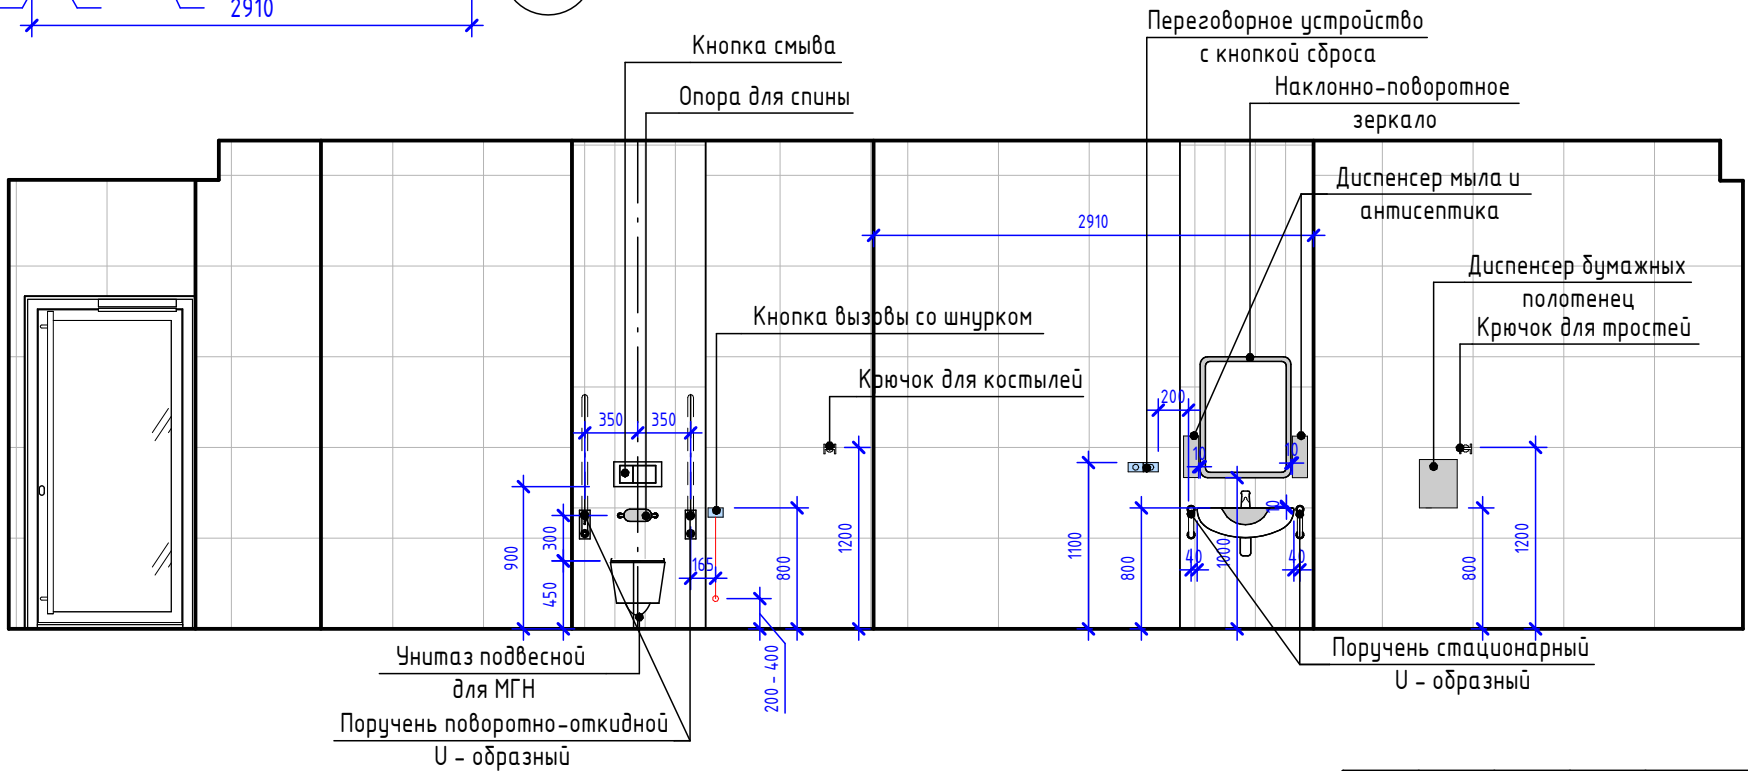

Спецификация материалов, оборудования и знаковых средств отображения информации для инвалидов в кабине МГН


№	Наименование работ	Ед. изм.	Объем работ
16	Зеркало наклонно-поворотное с регулируемым углом наклона 600х400, арт 2237, ПТК "Доступная страна" или аналог	шт.	1
17	Раковина для инвалидов DS Y4 640х550х165 мм	-	-
18	Поручень для раковины настенный двухопорный стационарный U-образный 800х230х600мм Y 32, арт. 8071-600 ПТК "Доступная страна" или аналог	шт.	2
19	Диспенсер для жидкого мыла	шт.	1
20	Диспенсер для антисептика	шт.	1
21	Диспенсер для бумажных полотенец	шт.	1
22	Крючок-держатель для тростей и других вещей, арт. 2202 ПТК "Доступная страна" или аналог	шт.	1
23	Крючок-держатель для костылей (травмобезопасный)	шт.	1
24	Поручень к унитазу откидной U-образный на стойке, 800х150х850 мм, Y32, Арт. 8090 ПТК "Доступная страна" или аналог	шт.	1
25	Поручень к унитазу откидной U-образный с бумагодержателем на стойке, 800х250х995 мм, Y32 мм, Арт. 8074 ПТК "Доступная страна" или аналог	шт.	1
26	Унитаз для инвалидов с инсталляцией в комплекте (унитаз с сиденьем подвесной, рамная инсталляция с креплением, кнопка смыва)	-	-
27	Специализированный сервисный тактильно-визуальный знак "Знак обозначения кнопки вызова экстренной помощи", акрил белый матовый 3мм, УФ-печать, 150х180мм	шт.	1
28	Кнопка вызова экстренной помощи со шнуром	-	-
29	Переговорное устройство с кнопкой сброса	-	-
30	Коридорная лампа 2-х цветная индикация	-	-

Примечание:

- Возле дверей на расстоянии 100 мм от края двери и на высоте от 1400мм до 1600мм предусмотрена тактильная пиктограмма "Обособленный туалет или отдельная кабина, доступная для инвалида на кресле-коляске".
- Над кнопкой тревожной сигнализации предусмотрена тактильная пиктограмма "Кнопка вызова экстренной помощи".
- Вызывное устройство в кабине предусмотрено согласно ГОСТ 51671 на высоте 0,8 м от ур.ч.п. в зоне унитаза. Кнопка вызова дополняется шнуром красного цвета с рамкой, находящейся вблизи пола на уровне от 0,2 до 0,4 м, которая позволит при падении надежно захватить шнур человеку с нарушенной функцией верхних конечностей.
- Унитаз предусмотрен на высоте 450мм от ур.ч.п.
- Раковина предусмотрена на высоте 800мм от ур.ч.п. до верхнего края раковины.
- Диспенсеры жидкого мыла и бумажных полотенец предусмотрен на высоте 1100мм от ур.ч.п. до низа диспенсеров. Марки диспенсеров см. ТХ
- Все поручни предусмотрены на высоте 850мм от ур.ч.п.
- Лист см. совместно со спецификацией санузлов для МГН.

						708П-24-АНО - ОДИ			
						Капитальный ремонт общеобразовательного учреждения ГБОУ Школа № 1210 по адресу: г. Москва, ул. Живописная, д.32			
Изм.	Кол.уч.	Лист	№ док.	Подп.	Дата	Архитектурные решения	Стадия	Лист	Листов
Разработал	Юденкова	Юденкова	12.25				Р	2.ОДИ	
ГАП	Фролова		12.25						
						Принципиальная схема расположения оборудования универсальной кабины для МГН.		ООО "АРТИС"	
Н.Контроль	Лукашова		12.25						
ГИП	Старов		12.25						

Схема организации земельного участка с указанием путей перемещения маломобильных групп населения М1-М3, М4 М 1:200

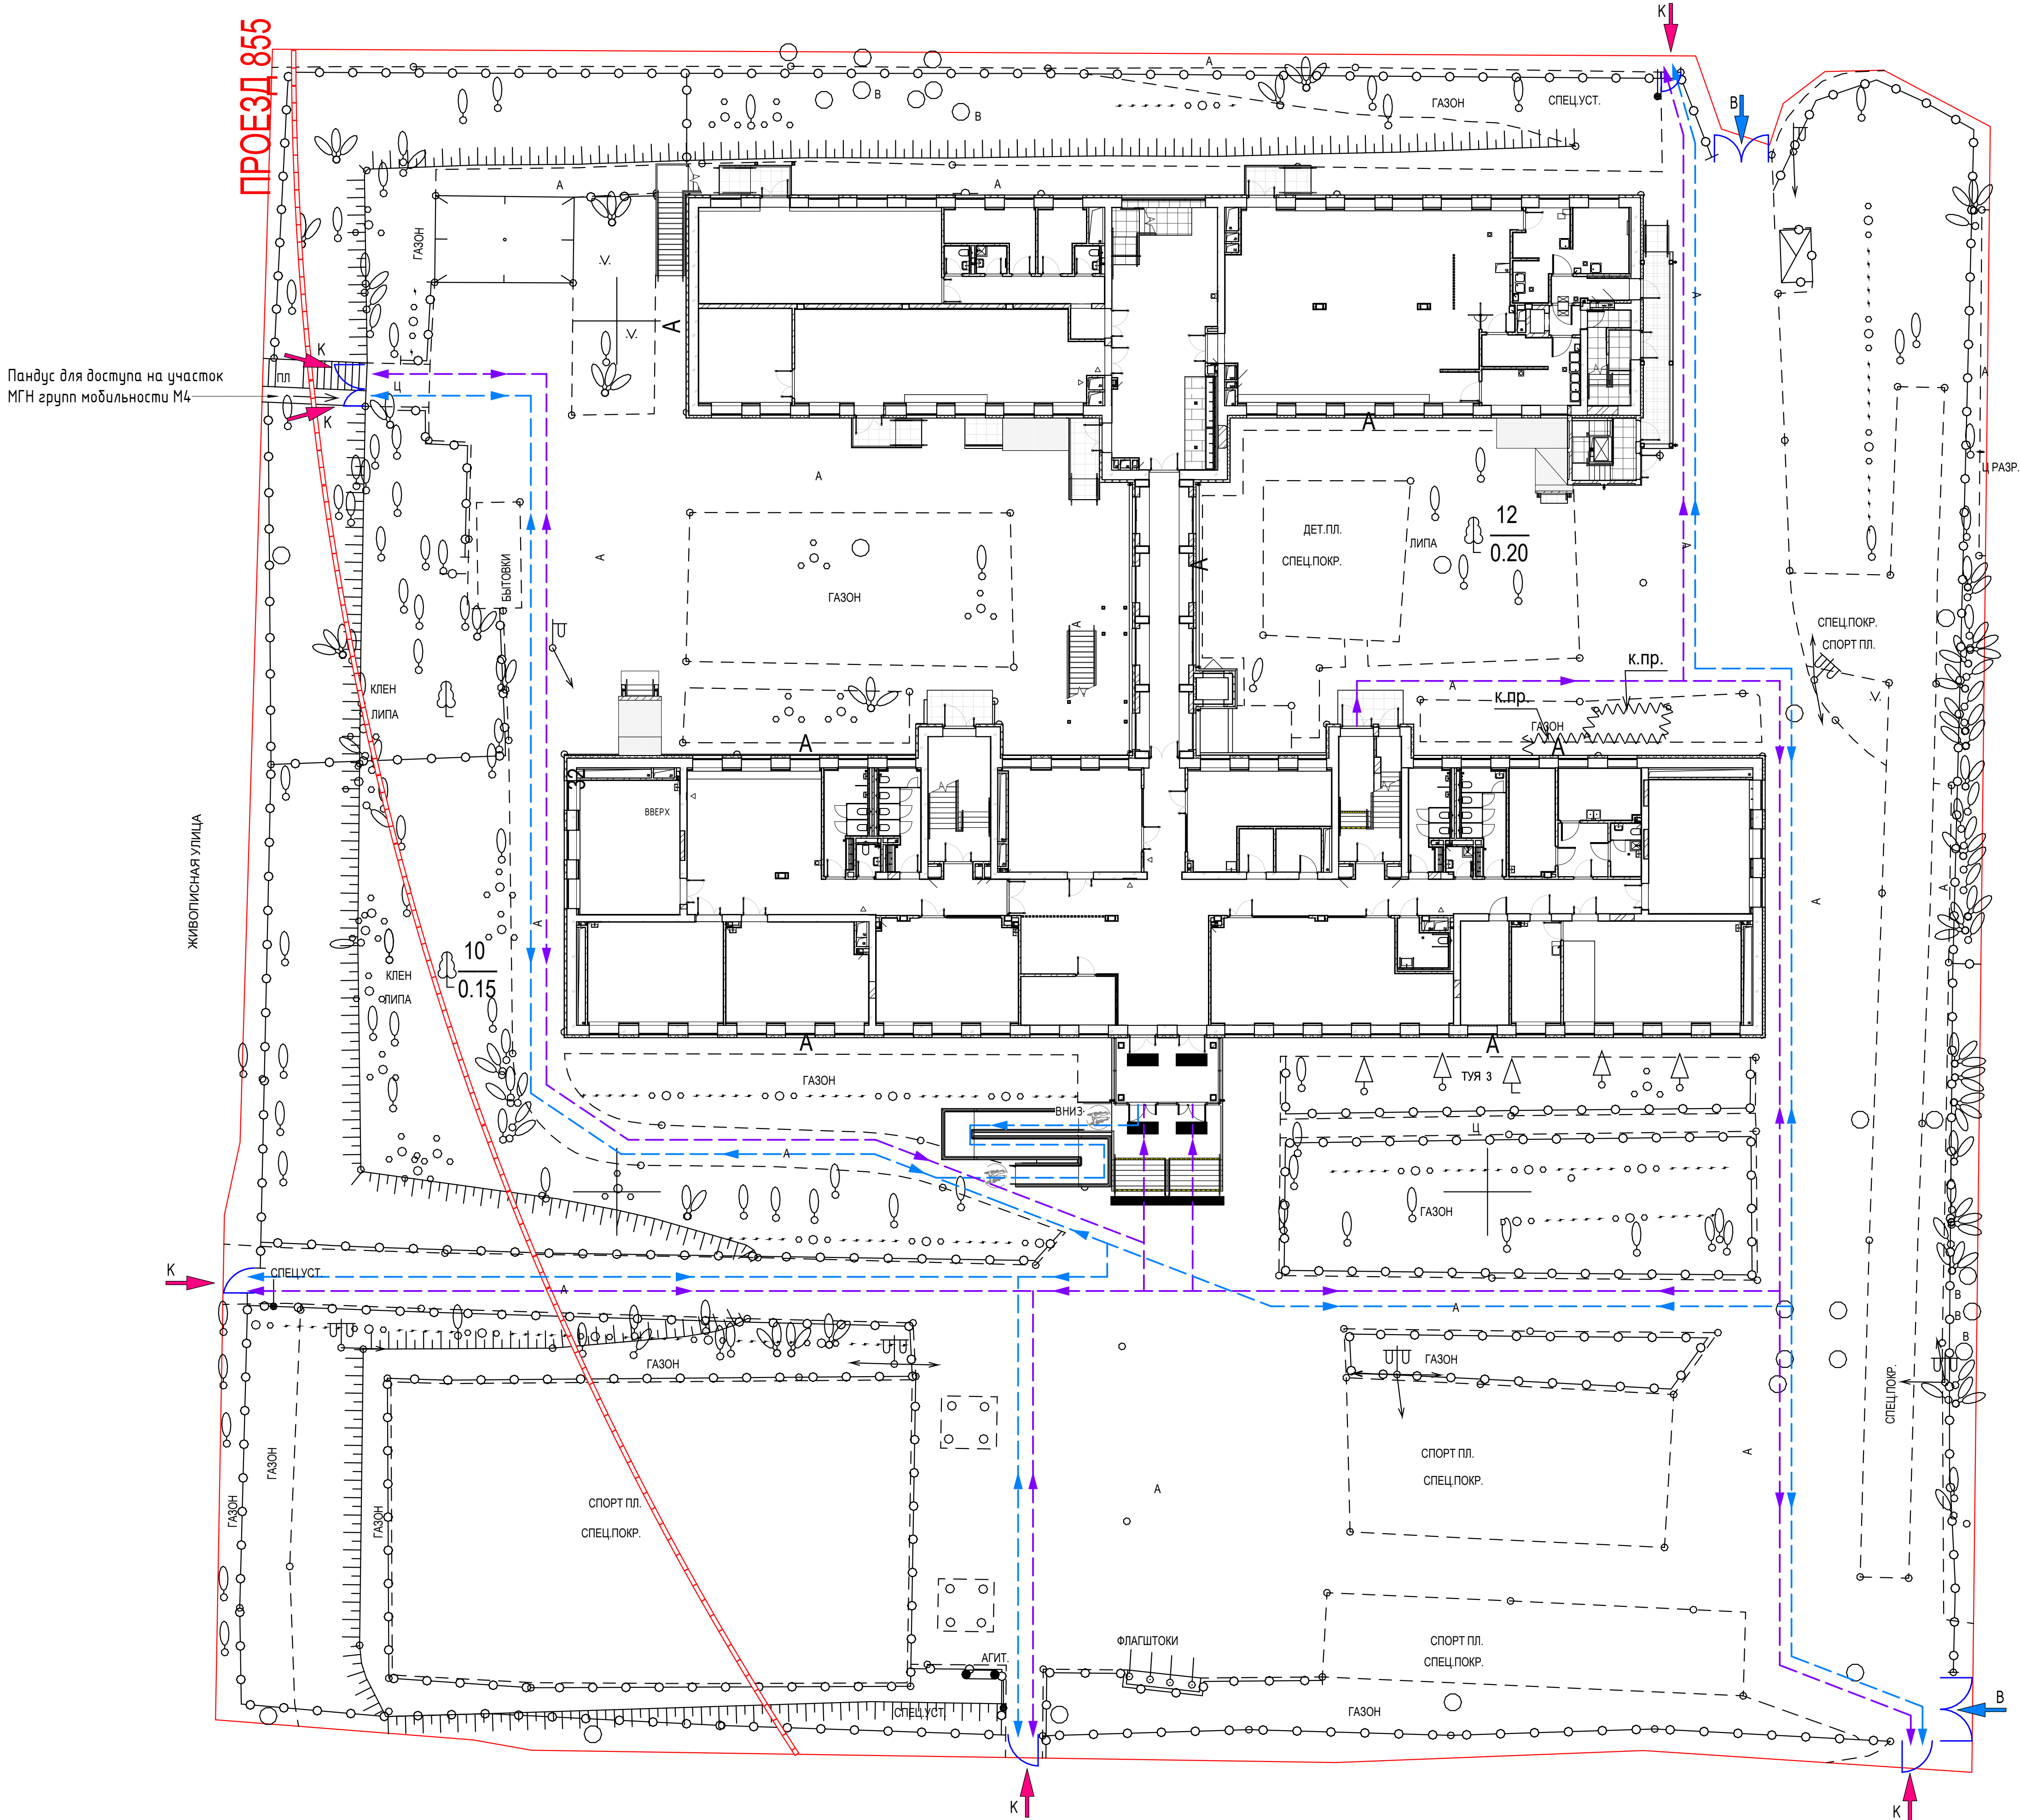

Условные обозначения:

- Граница участка
- Калитки
- Ворота
- Пути передвижения МГН групп мобильности М1-М3
- Пути передвижения МГН групп мобильности М4

						708П-24-АНО - ОДИ		
						Капитальный ремонт общеобразовательного учреждения ГБОУ Школа № 1210 по адресу: г. Москва, ул. Животиская, д.32		
Изм.	Жел.ч.	Лист	№ док.	Подп.	Дата	Мероприятия по обеспечению доступа инвалидов	Стадия	Лист
Разработал	Юденкова	12.25					Р	3.ОДИ
ГАП	Фролова	12.25						
						Схема организации земельного участка с указанием путей перемещения маломобильных групп населения М 1:200		
Н.Контроль	Лукашова	12.25						
ГИП	Старов	12.25						