



АРТИС
Артис - искусство проектирования

109341, г. Москва, ул. Марксистская, дом 3, стр. 1

+7 (495) 647-85-99

mail@rosartis.ru

rosartis.ru

3d-artis.ru



Экз. № _____

Заказчик: АНО «РГТ»

**Капитальный ремонт общеобразовательного
учреждения ГБОУ Школа № 1210 по адресу:
г. Москва, ул. Живописная д. 32**

Этап 1

РАБОЧАЯ ДОКУМЕНТАЦИЯ

Раздел.4. Конструктивные решения

708/П-24-АНО-КР



АРТИС
Артис - искусство проектирования

109341, г. Москва, ул. Марксистская, дом 3, стр. 1

+7 (495) 647-85-99

mail@rosartis.ru

rosartis.ru

3d-artis.ru



Экз. № _____

Заказчик: АНО «РГТ»

**Капитальный ремонт общеобразовательного
учреждения ГБОУ Школа № 1210 по адресу:
г. Москва, ул. Живописная д. 32**

Этап 1

РАБОЧАЯ ДОКУМЕНТАЦИЯ

Раздел.4. Конструктивные решения

708/П-24-АНО-КР

Генеральный директор:



Цибизов В.В.

ВЕДОМОСТЬ ЧЕРТЕЖЕЙ ОСНОВНОГО КОМПЛЕКТА		
11	Общие сведения	
1	План подвала с указанием проводимых работ	
2	План 1-го этажа с указанием проводимых работ	
3	План 2-го этажа с указанием проводимых работ	
4	План 3-го этажа с указанием проводимых работ	
5	Схема устройства усиления проема Пр-1	
6	Схема устройства усиления проема Пр-2	
7	Схема устройства усиления проема Пр-3..5, 9	
8	Схема устройства усиления проема Пр-7	
9	Схема устройства усиления проемов Пр-6, 23	
10	Схема устройства усиления проемов Пр-8	
11	Схема устройства усиления проемов Пр-10..15	
12	Схема устройства усиления проема Пр-12	
13	Схема устройства усиления проемов Пр-17..22, 26, 27	
14	Схема устройства усиления проемов Пр-24	
15	Схема устройства усиления проемов Пр-25	
15.1-15.6	Спецификации материалов на усиление проемов	
16-18	Схемы усиления проемов для прохождения вентиляции	
19	Узлы ремонта ступеней, плит перекрытий и покрытий	
20	Схема устройства входа в осях "25/П"	
21	Схема устройства входа в осях "13-14/П"	
22	Схема устройства входа в осях "10/Л-М"	
23	Схема устройства входа в осях "26/М"	
24	Схема устройства входа в осях "27/М"	
25	Схема устройства козырька входа в осях "27/М"	
26	Схема устройства входа в осях "1-2/Г-Д"	
27	Схема устройства входа в осях "1-2/Г-Д"	
28	Схема устройства входа в осях "21/Г"	
29	Схема устройства козырька входа в осях "27/М"	
30	Опалубочный план крыльца в осях Д-Е/7-8	
31	Опалубочный план крыльца в осях Д-Е/15-16	
32	Схема устройства входа в осях "8-13/А"	
33	Схема устройства козырька входа в осях "10-13/А"	
34	Разрез 1-1, 4-4	
35	Разрез 2-2	
36	Разрез 3-3	
37	Схема армирования плиты основания входа в осях "9-13/А"	
38	Армирование. Разрез 1-1, 5-5. Схема армирования балки покрытия	
39	Армирование. Разрез 2-2	
39.1	Спецификация материалов на устройство входа в осях "8-13/А"	
39.2	Ведомость деталей	
40	Дебаркадер. План на отм. -3.100, 0.000, +3.650. Разрез 1-1..4-4	
41	Дебаркадер. Виды 1-8	
42	Дебаркадер. Плита покрытия ПП-1	
43	Дебаркадер. Колонна К1, К2. Ведомость элементов	
45	Схемы устройства монолитных лестниц в осях "21-22/М-Н"	
46	Схема размещения подпорной стены и плиты пола подвала	
47	Подпорная стена. ПС-11, 2.1, 2.2	

48	Подпорная стена ПС-3.1, 4.1	
49	Подпорная стена ПС-5.1, 5.2	
50	Подпорная стена ПС-6.1	
51	Спецификация материалов на устройство подпорной стены и лестниц подвала	
52	Схема армирования плит подвала. Ведомость деталей	
53	Прямак ПР-2. Спецификация материалов	
55	Схема демонтажа плит перекрытия подвала	
56	Схема демонтажа плит перекрытия 1 этажа	
57	Схема демонтажа плит перекрытия 2 этажа	
58	Схема демонтажа плит перекрытия 3 этажа	
59	Схема устройства монолитных участков плит перекрытия подвала	
60	Схема устройства монолитных участков плит перекрытия 1 этажа	
61	Схема устройства монолитных участков плит перекрытия 2 этажа	
62	Схема устройства монолитных участков плит перекрытия 3 этажа	
63	Монолитные участки УМ-1, УМ-2	
63.1	Схема устройства усиления плит перекрытия в местах повышенных нагрузок	
64	Лестница Л-1 в осях 11-12/И-Л на отм. +6.400	
65	Лестница Л-1 в осях 10-11/Д-Ж на отм. +3.460	
66	Фундамент ФМ-1, ФМ-2	
67	Косоур К-1, К-2. Узел 1, 2, 3	
68	Площадка на отм. +1250, +3.200	
69	Лестница Л-3 в осях 3-25/Н-П на отм. +3.300	
70	Фундамент ФМ-1, ФМ-2	
71	Косоур К-1, К-2. Узел 1, 2, 3	
72	Площадки на отм. +1220, +3.300	
73	Схема рамы на кровле для оборудования кондиционирования	
74	Схема рамы на кровле для оборудования кондиционирования в осях М/17, М/21, В/7	
75	Схема рамы на кровле для оборудования кондиционирования в осях В/7, А/14-16	
75.1	Спецификация материалов на изготовление рамы для оборудования кондиционирования	
76	Схема ремонта гидроизоляции стен подвала	
77	Инъекцирование трещин в межблочных стеновых швах	
78	Узел заделки примыкания простеночных блоков наружных стен из крупноблочных керамзитобетонных блоков	
79	Схемы устройства рам для установки баскетбольных щитов	
80	Схемы устройства зрительной трибуны	
81	Схема устройства пожарных лестниц ПЛ-1..ПЛ-3. Спецификация материалов	

Общие данные:
ТРЕБОВАНИЯ К БЕТОНУ

1. Класс бетона по прочности на сжатие для всех монолитных конструкций - В25. Марка бетона по водонепроницаемости - не ниже W6. Марка бетона по морозостойкости - не ниже F100.

2. Корректировка состава бетонных смесей на строительной площадке исключается.

3. Бетонные смеси должны соответствовать требованиям ГОСТ 7473-2010 "Смеси бетонные. Технические условия".

ТРЕБОВАНИЯ К АРМАТУРЕ

1. Арматура для всех конструкций класса А-500 и А-240 по ГОСТ 34028-2016.

2. Стыковку арматуры выполнять внахлестку в соответствии с чертежами данного комплекта. При стыковке арматуры внахлестку выполнять разбежку стыков как в плоскости армирования, так и из плоскости (в продольном и поперечном направлении стены).

3. Изготовление гнутых стержней производить в холодном состоянии на оправках диаметром 5d для стержней диаметром менее 20 мм, и 8d для стержней диаметром 20 мм и более.

4. Особое внимание следует обратить на точность установки и вертикальность продольного армирования пояса. Допуск на отклонение вертикальных и наклонных стержней от проектного положения в плане составляет 5 мм.

ТРЕБОВАНИЯ К ПРОИЗВОДСТВУ РАБОТ

1. Работы выполнять в соответствии с СП 70.13330.2012 "Несущие и ограждающие конструкции".

2. Перед монтажом арматуры должен быть произведен контроль правильности установки опалубки и ее креплений.

3. Арматуру следует монтировать в последовательности, обеспечивающей правильное ее положение и закрепление. Для обеспечения проектного защитного слоя бетона запрещается применение подкладок из обрезков арматуры, деревянных брусков и щебня. Смонтированная арматура должна быть закреплена от смещения и защищена от повреждений.

4. Перед укладкой бетонной смеси должны быть проверены и приняты все конструкции и их элементы, закрываемые в процессе последующего производства работ, с составлением акта на скрытые работы. Непосредственно перед бетонированием опалубка должна быть очищена от мусора и грязи.

5. При бетонировании необходимо сохранять проектное положение арматуры и закладных деталей. В случае необходимости установить дополнительные стержни или хомуты и согласовать расстановку с представителями авторского надзора.

6. Должны быть предусмотрены мероприятия для начального периода твердения бетона: защита от попадания атмосферных осадков, защита от высыхания, поддержание температурно-влажностной режим с созданием условий, обеспечивающих нарастание его прочности.

7. Распалубочная прочность бетона составляет не менее 12 МПа

8. При приемке работ по бетонированию железобетонных конструкций обязательно наличие заключения лаборатории по прочности бетона и исполнительной геодезической съемки.

ТРЕБОВАНИЯ К КОНТРОЛЮ КАЧЕСТВА БЕТОНА

1. Контроль качества бетона допускается вести методами косвенного неразрушающего контроля по ГОСТ 22690-88 (метод упругого отскока) и по ГОСТ 17624-87 (ультразвуковой метод).


2. В Заключениях по результатам контроля прочности бетона следует включать планы с указанием и маркировкой всех точек контроля.

3. Требуемая прочность бетона в возрасте 28 суток, определенная на основании испытаний методами прямого и косвенного контроля на стройплощадке, с учетом требований ГОСТ18105-2010 "Бетоны. Правила контроля и оценки прочности" должна быть для бетона класса В25 - не ниже 29 МПа.


						708/П-24-АНО-КР			
						Капитальный ремонт общеобразовательного учреждения ГБОУ "Школа №1210" по адресу: г. Москва, ул. Живописная, д.32			
Изм.	Колуч.	Лист	№ док.	Подп.	Дата	Конструктивные решения	Стадия	Лист	Листов
Разработал	Торшин				04.26		Р	11	
ГАП	Фролова				04.26				
						Общие данные		комплексное проектирование промышленных и гражданских объектов ООО "АРТИС"	
Н.Контроль	Лукашова				04.26				
ГИП	Зыкин				04.26				

Экспликация помещений

Экспликация технических пространств

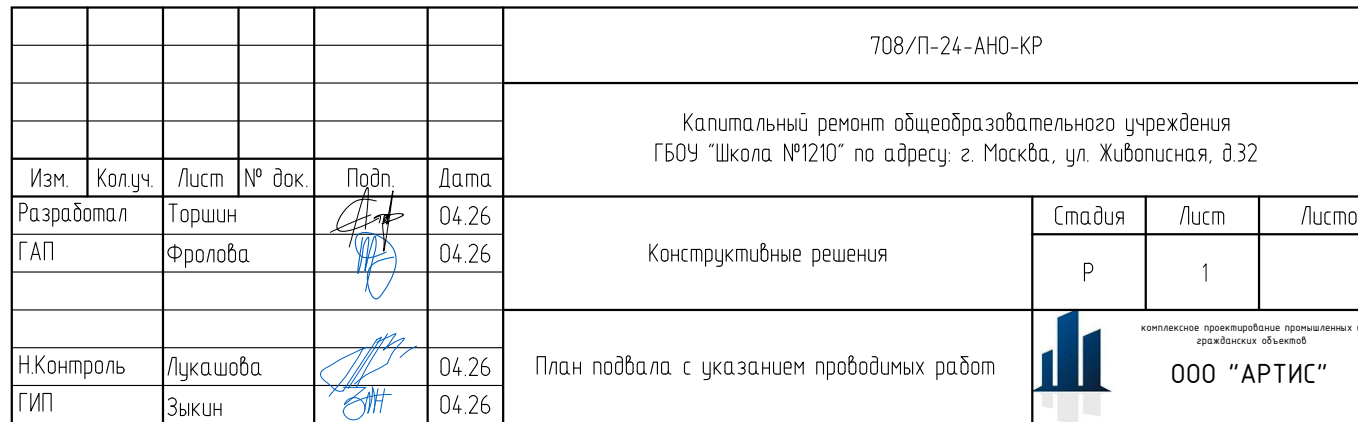


План 1-го этажа с указанием проводимых работ

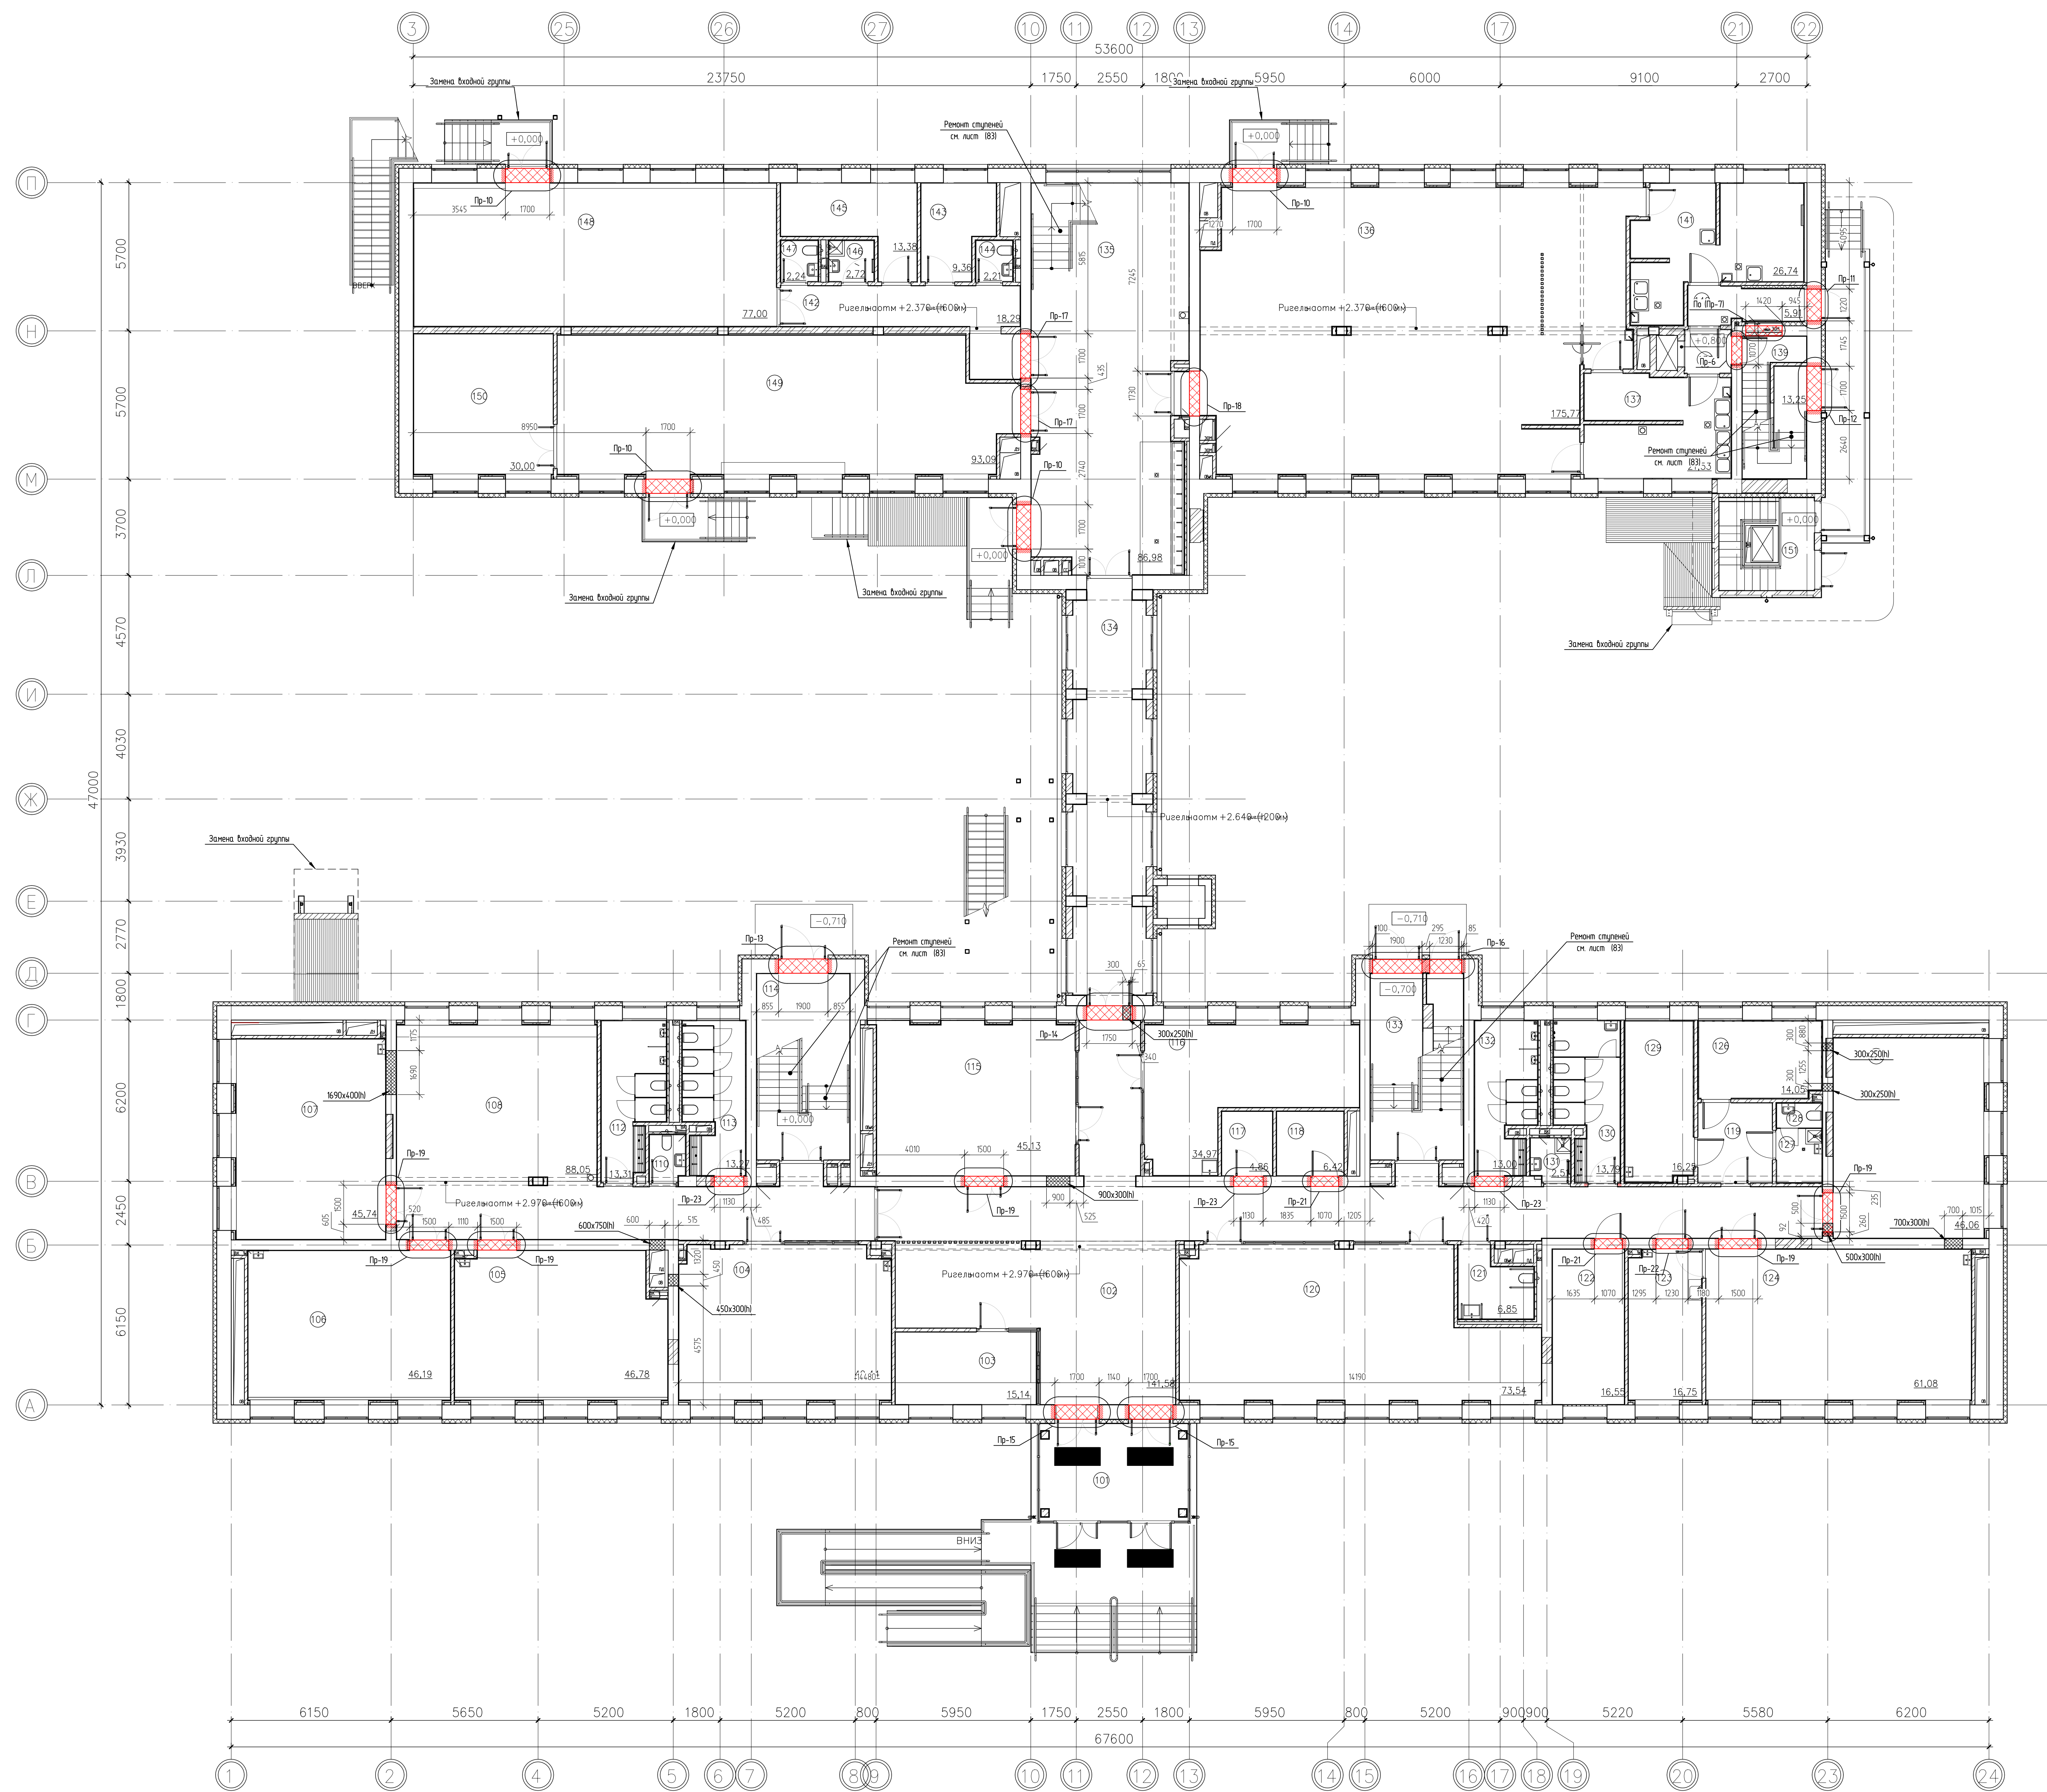

Экспликация помещений первого этажа				Экспликация помещений первого этажа			
Номер помещения	Наименование	Площадь, м ²	Кол-во помещений	Номер помещения	Наименование	Площадь, м ²	Кол-во помещений
101	Тамбур	21,46		129	Кабинет брано (длиной не менее 5-6 м)	16,25	
102	Вестибюль	141,58		130	Санузел для девочек с комнатой личной гигиены	13,79	
103	Комната охраны с диспетчерским	15,14		131	ТМ	2,51	84
104	Учебная кабинет	49,44		132	Санузел для мальчиков	13,00	
105	Учебная кабинет	46,78		133	Пестичная клетка (типа П)	25,27	
106	Учебная кабинет	46,19		134	Коридор	43,34	
107	Кабинет учебная	45,74		135	Пестичная клетка (типа П)	86,98	
108	Кабинет с Коридор	88,05		136	Общедневная зал	175,77	
110	Санузел для персонала	2,45		137	Моечная для столовых	21,53	84
112	Санузел для девочек	13,31		138	Коридор	2,96	
113	Кабинет Санузел для девочек	13,27		139	Пестичная клетка (типа П)	13,25	
114	Пестичная клетка (типа П)	25,65		140	Коридор	5,91	
115	Коридор для девочек	45,13		141	Кабинет для подготовки блог к реализации с учебным	27,12	84
116	Кабинет с рабочим пространством для учителя тип 1	34,97		142	Кухня, ванная, санузел	18,29	
117	Кабинет с рабочим пространством для учителя (кабинет)	4,86		143	Раздевалка	9,36	
118	Тамбур	6,42	83	144	Уютная	2,21	
119	Тамбур	8,81		145	Кухня	13,38	
120	Гардероб для обучающихся	73,54		146	ТМ	2,72	84
121	Санузел для МН на 1-м этаже	6,85		147	Уютная	2,24	
122	Электрощитовая	16,55	83	148	Кабинет личностный	77,00	
123	Лабораторная кабинет	16,75	83	149	Библиотека	93,09	
124	Учебный кабинет для изучения естественных наук	108,08		150	Книгохранилище	30,00	83
125	Кабинет	46,06		151	Детский кабинет	13,10	83
126	Кабинет Просторная (прибыточная) кабинет	14,05		152	Общая	1558,50	
127	Кабинет кабинет для разбора и уборочного инвентаря, предназначенных для помещений медицинского кабинета	3,63	84				
128	Кабинет Санузел	1,67					

						708/П-24-АМ-КР											
						Капитальный ремонт общеобразовательного учреждения ГБОУ Школа №202 по адресу г. Москва, ул. Халдеевская, 832											
						Конструктивные решения											
						Специальное				Лист				Листов			
						р.				2							
Итого:						Подпись _____ ООО "АРТИЗ"											

План 2-го этажа с указанием проводимых работ

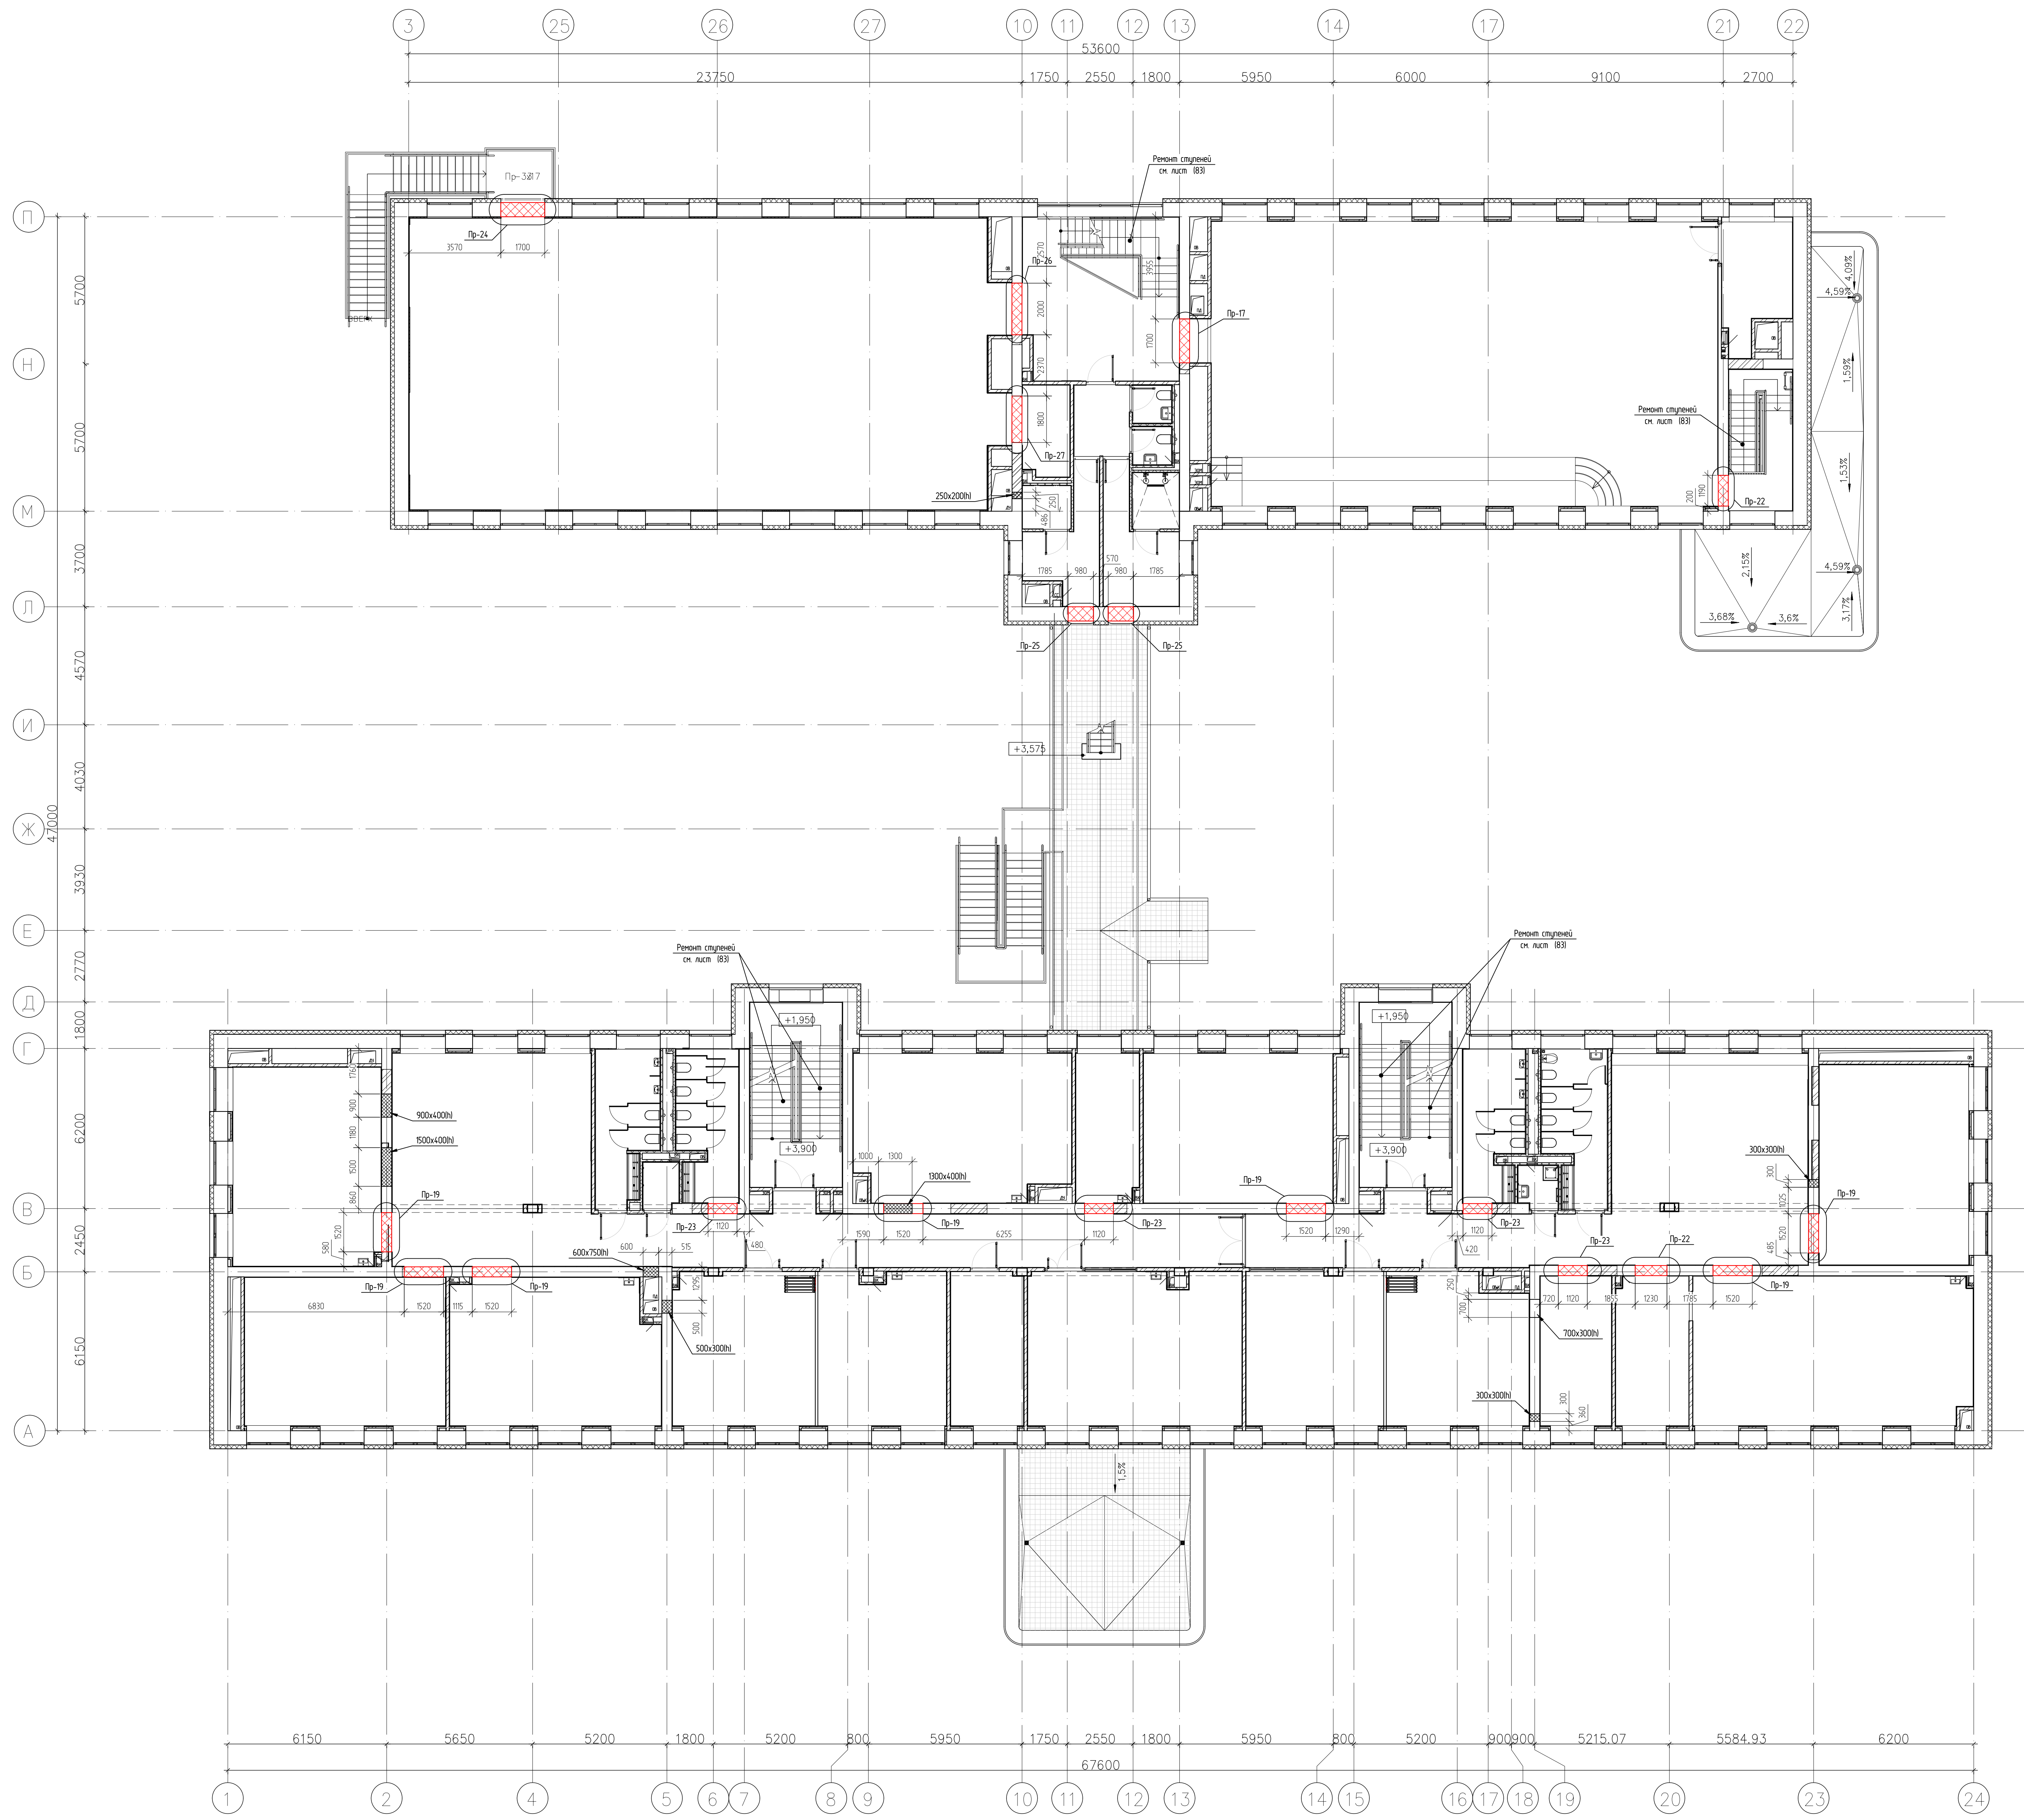

						T08/P-2-AH-KP
						Капитальный ремонт образовательного учреждения г/ош "Школа №7010" по адресу с Москва, ул. Мухоморова, 832
Изм.	Копия	Лист	№ док.	Подп.	Дата	Конструктивные решения
Разработка ГЭП		Горкин Фролов		[подпись]	04.26	
					04.26	Р з Листов
Н.Контроль РАП		Анучина Виктория		[подпись]	04.26	 ООО "АРТИМС" полное товарищество с ограниченной ответственностью
		Выдан			04.26	
						План 2-го этажа с указанием проводных сетей

[illegible][illegible]

Схема демонтажа стены из блоков ФБС под проем Пр-1



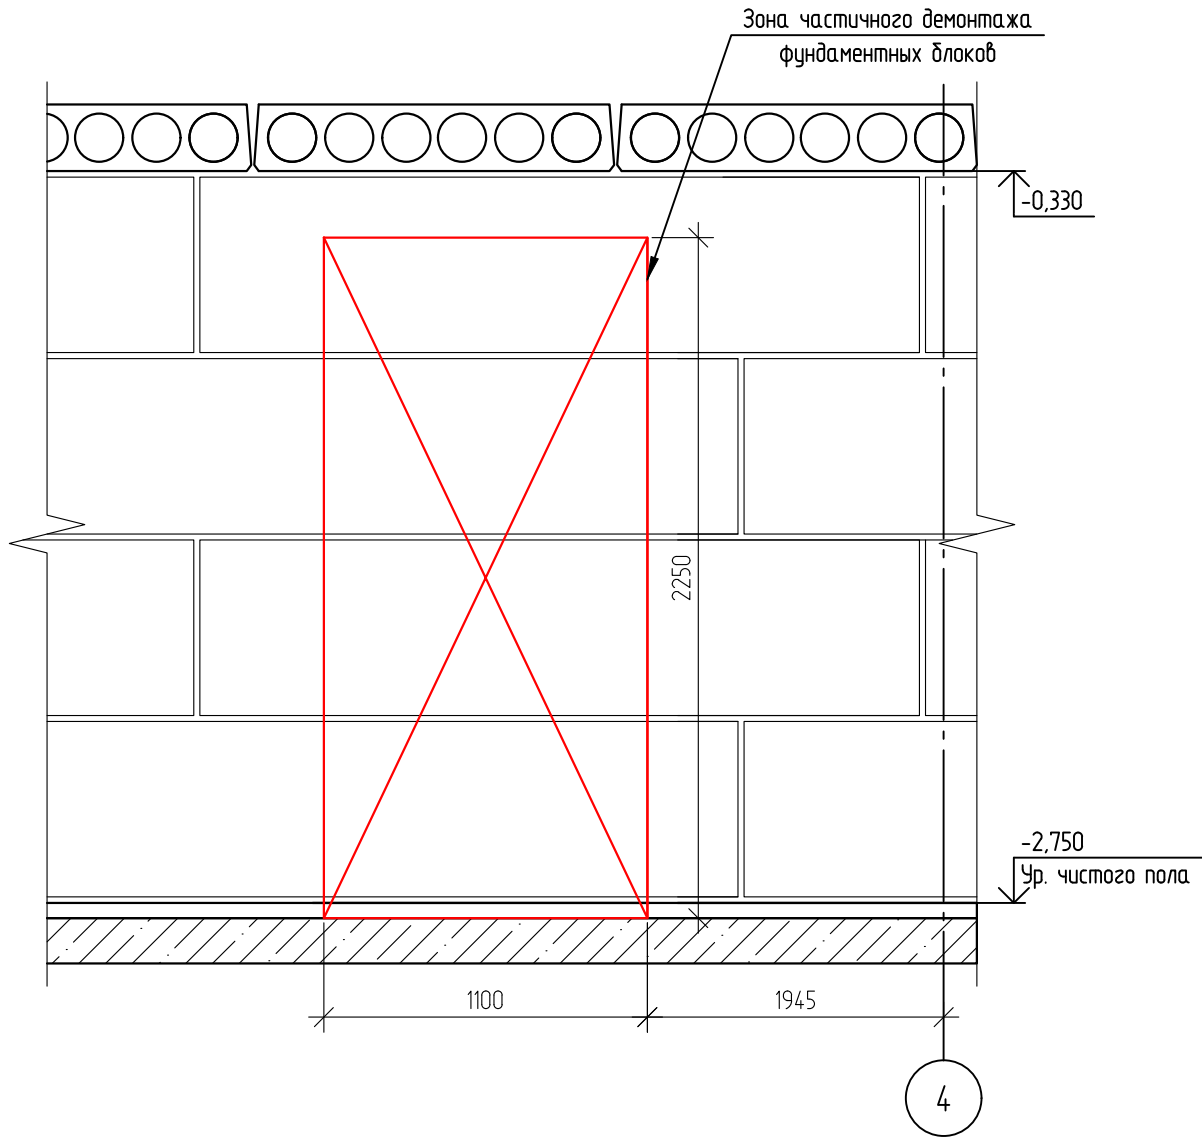




Схема устройства усиления проема Пр-1

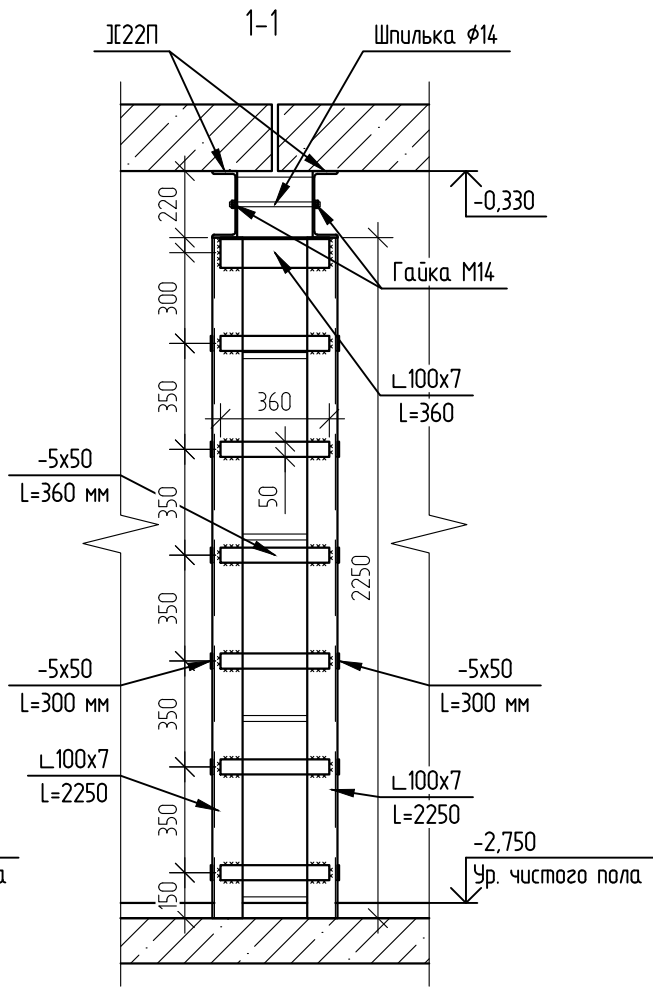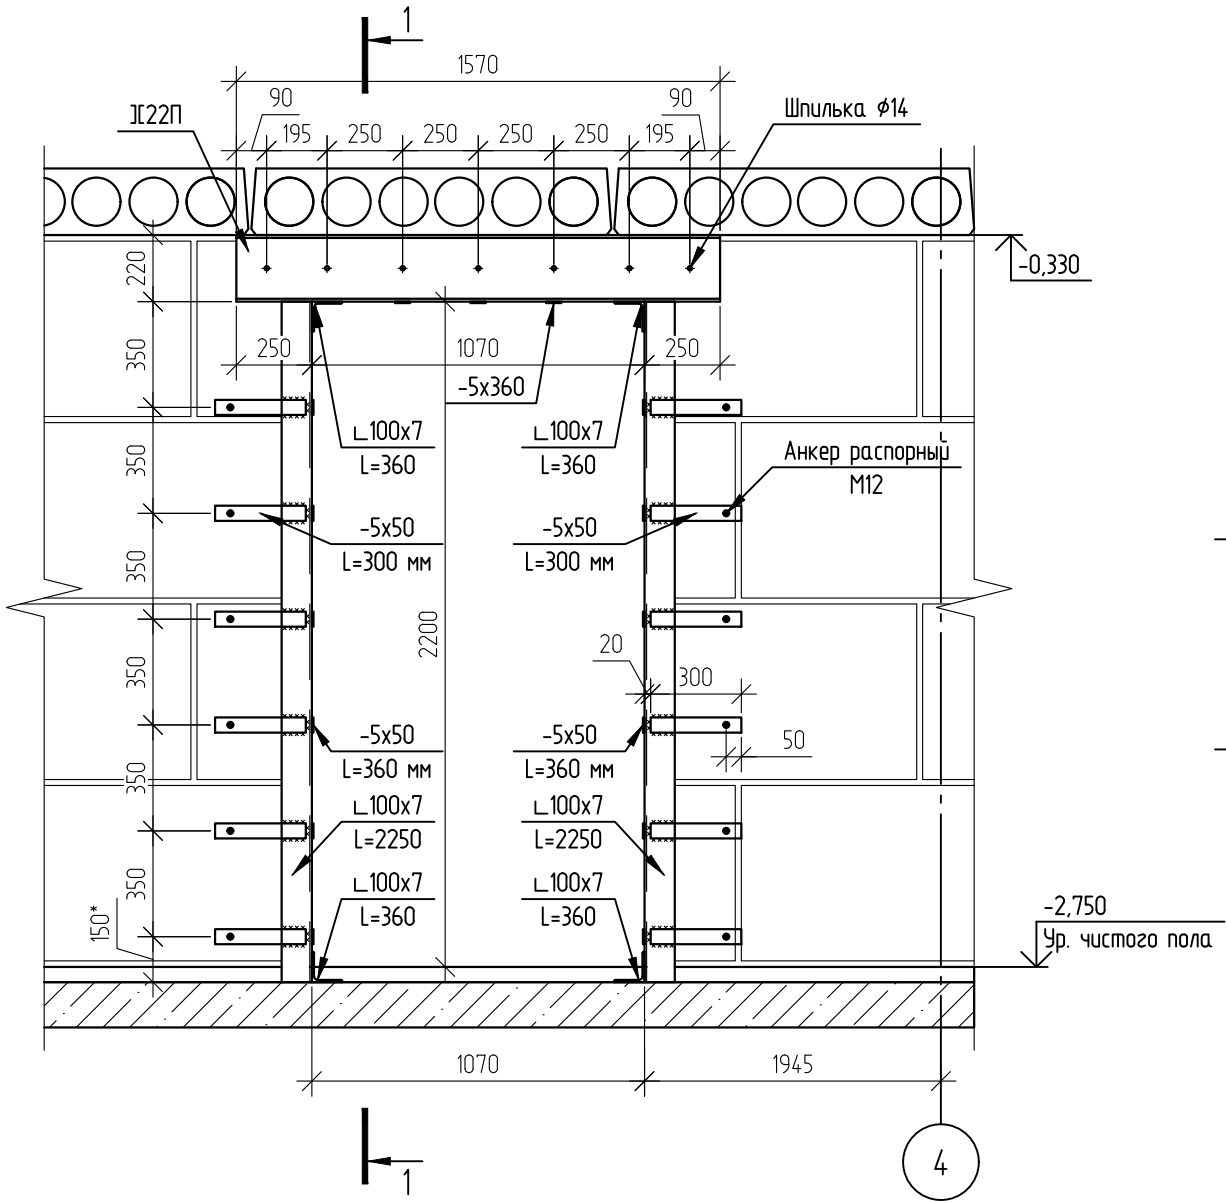

- Порядок выполнения работ по усилению проема:
1. Установить временные разгрузочные стойки под перекрытие.
 2. Подготовить штробы глубиной 80 мм с двух сторон.
 3. Просверлить отверстия Ø16 под шпильки.
 4. Установить перемычки из швеллеров с зачеканкой зазоров между элементами перемычек и кладкой цементно-песчаным раствором по всей длине.
 5. Установить шпильки (Ø14 А240).
 6. Прорезку проема начинать от перемычки вниз и от середины проема к краям. Предварительно пилами с режущими дисками произвести надрезку кладки по периметру проема, а затем произвести разборку кладки.
 7. После прорезки проема к элементам перемычек приварить снизу стальные планки.
 8. Установить стальные обоймы из L 100x7 по периметру откосов и прикрепить их к кладке планками с отверстиями Ø14, закрепить анкерами, соединить уголки планками на сварке.
 9. К планкам привязать стальную сетку 20-06 ГОСТ 5336-80* и оштукатурить ее цементным раствором М100.
 10. Электроды для сварки З42А по ГОСТ 9467-75*.
 11. Строительно-монтажные работы должны производиться специальной организацией, имеющей лицензию на выполнение таких работ.
 12. При производстве сварочных работ необходимо соблюдать требования СП 70.13330.2012, глава 10 и "Правил пожарной безопасности при проведении сварочных работ.."
 13. После окончания монтажа металлоконструкций должен быть составлен акт на скрытые работы.

						708/П-24-АНО-КР			
						Капитальный ремонт общеобразовательного учреждения ГБОУ "Школа №1210" по адресу: г. Москва, ул. Живописная, д.32			
Изм.	Кол.уч.	Лист	№ док.	Подп.	Дата	Конструктивные решения	Стадия	Лист	Листов
Разработал		Торшин			04.26		Р	5	
ГАП		Фролова			04.26				
Н.Контроль		Лукашова			04.26	Схема устройства усиления проема Пр-1	 комплексное проектирование промышленных и гражданских объектов ООО "АРТИС"		
ГИП		Зыкин			04.26				



Схема устройства усиления проема Пр-2

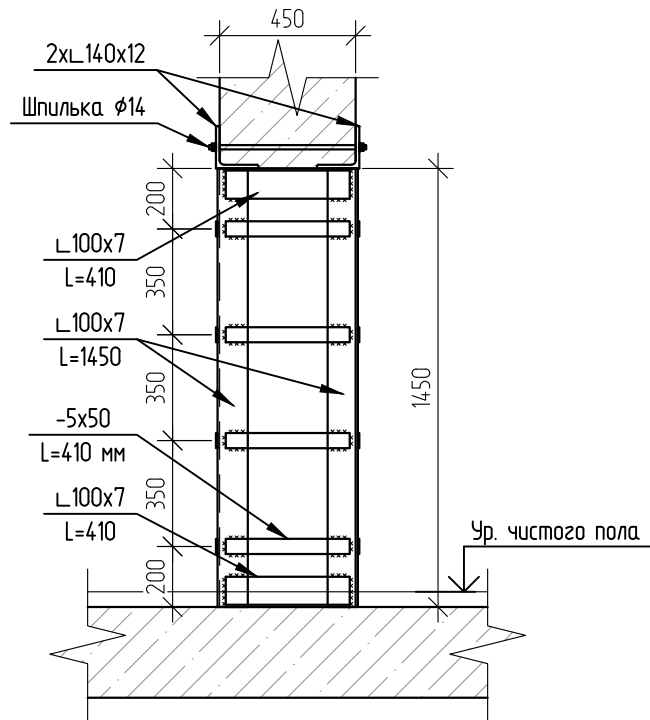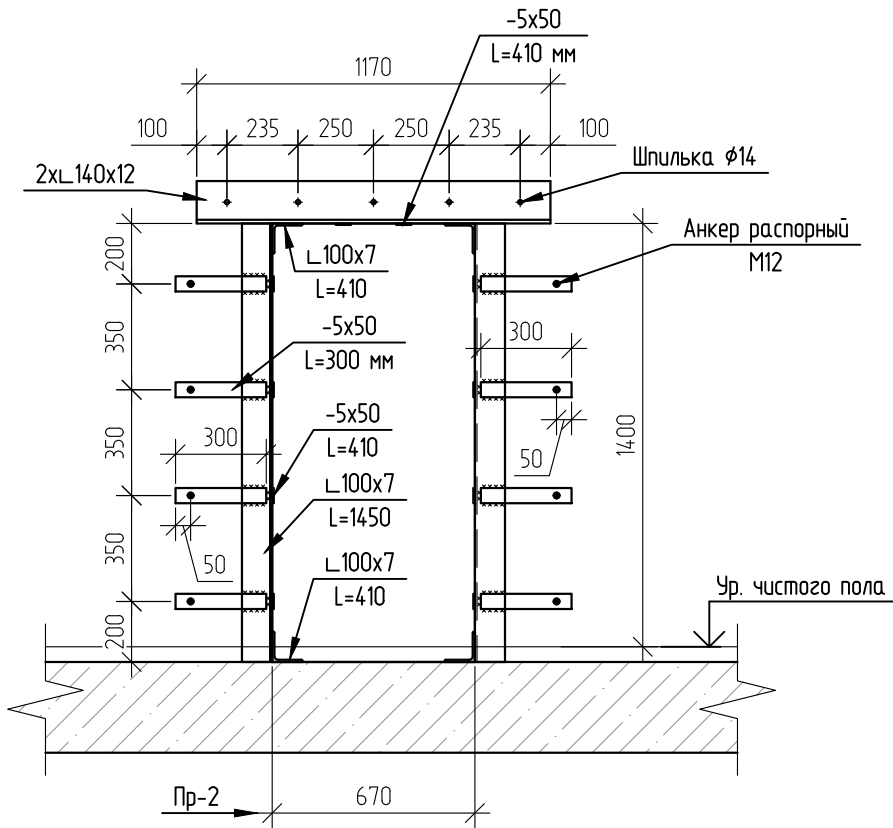

- Порядок выполнения работ по усилению проема:
1. Установить стальные обоймы из L 100x7 по периметру откосов и прикрепить их к кладке планками с отверстиями $\phi 14$, закрепить анкерами, соединить уголки планками на сварке.
 2. К планкам привязать стальную сетку 20-0Б ГОСТ 5336-80* и оштукатурить ее цементным раствором М100.
 3. Электроды для сварки Э42А по ГОСТ 9467-75*.
 4. Строительно-монтажные работы должны производиться специальной организацией, имеющей лицензию на выполнение таких работ.
 5. При производстве сварочных работ необходимо соблюдать требования СП 70.13330.2012, глава 10 и "Правил пожарной безопасности при проведении сварочных работ..."
 6. После окончания монтажа металлоконструкций должен быть составлен акт на скрытые работы.

						708/П-24-АНО-КР		
						Капитальный ремонт общеобразовательного учреждения ГБОУ "Школа №1210" по адресу: г. Москва, ул. Живописная, д.32		
Изм.	Кол.уч.	Лист	№ док.	Подп.	Дата	Конструктивные решения	Стадия	Лист
Разработал	Торшин				04.26		Р	6
ГАП	Фралова				04.26			
Н.Контроль	Лукашова				04.26	Схема устройства усиления проема Пр-2	 комплексное проектирование промышленных и гражданских объектов ООО "АРТИС"	
ГИП	Зыкин				04.26			




Схема устройства усиления проемов Пр-3...5, 9

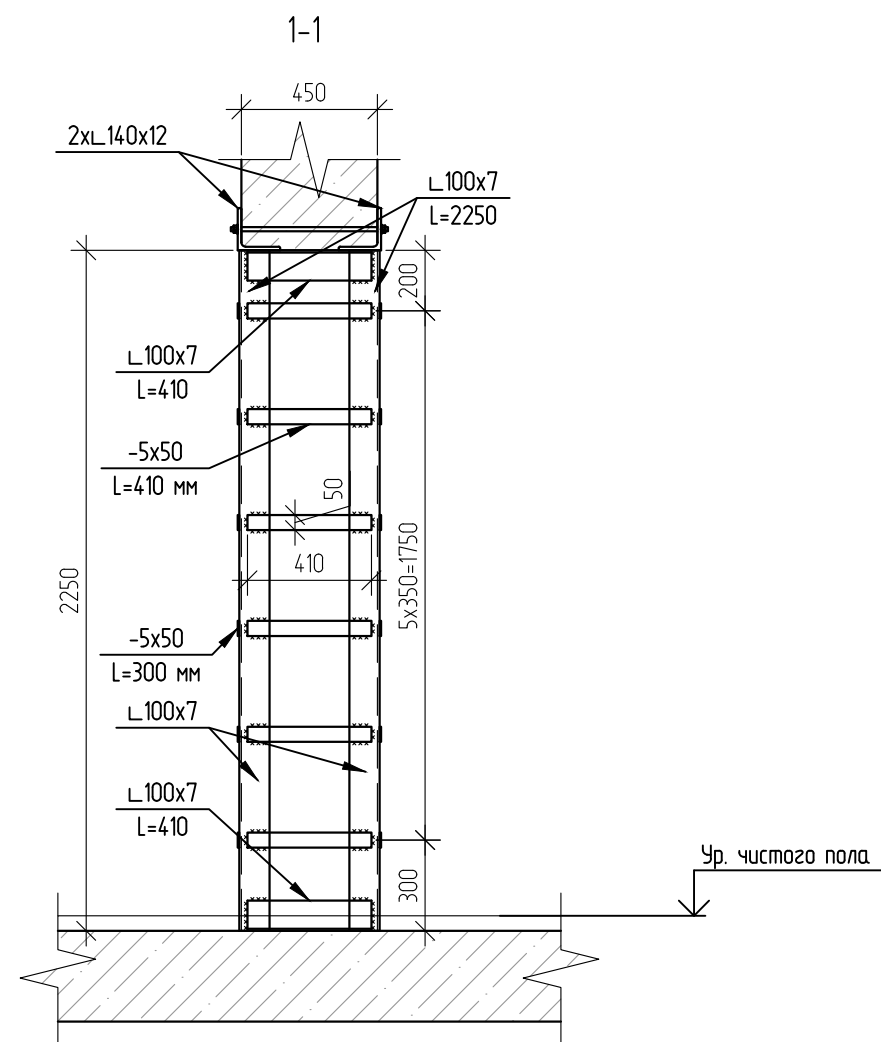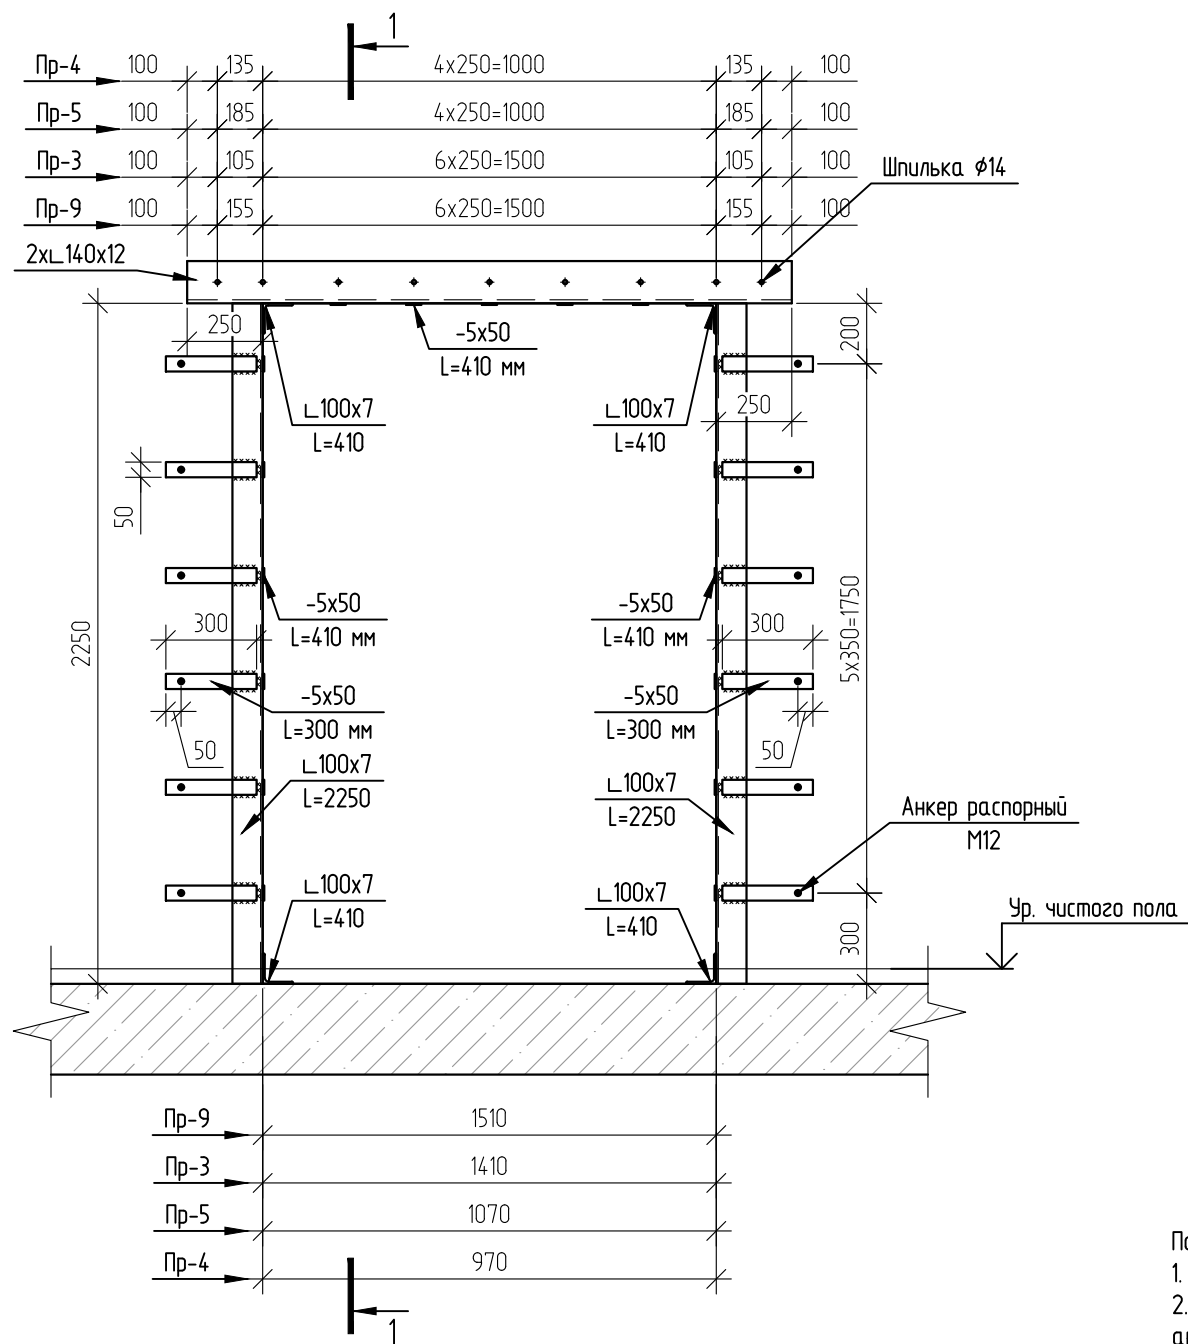

- Порядок выполнения работ по усилению проема:
1. Установить перемычку с двух сторон из L 140x12 и стянуть их шпильками М14.
 2. Установить стальные обоймы из L 100x7 по вертикальным граням и прикрепить их к кладке планками с отверстиями Ø14, закрепить анкерами, соединить уголки планками на сварке.
 3. К планкам привязать стальную сетку 20-06 ГОСТ 5336-80* и оштукатурить ее цементным раствором М100.
 4. Electroды для сварки Э42А по ГОСТ 9467-75*.
 5. Строительно-монтажные работы должны производиться специальной организацией, имеющей лицензию на выполнение таких работ.
 6. При производстве сварочных работ необходимо соблюдать требования СП 70.13330.2012, глава 10 и "Правил пожарной безопасности при проведении сварочных работ..."
 7. После окончания монтажа металлоконструкций должен быть составлен акт на скрытые работы.

						708/П-24-АНО-КР		
						Капитальный ремонт общеобразовательного учреждения ГБОУ "Школа №1210" по адресу: г. Москва, ул. Живописная, д.32		
Изм.	Кол.уч.	Лист	№ док.	Подп.	Дата	Конструктивные решения	Стадия	Лист
Разработал	Торшин				04.26		Р	7
ГАП	Фралова				04.26			
Н.Контроль	Лукашова				04.26	Схема устройства усиления проема Пр-3...5, 9	 ООО "АРТИС"	
ГИП	Зыкин				04.26			




Схема устройства усиления проема Пр-7

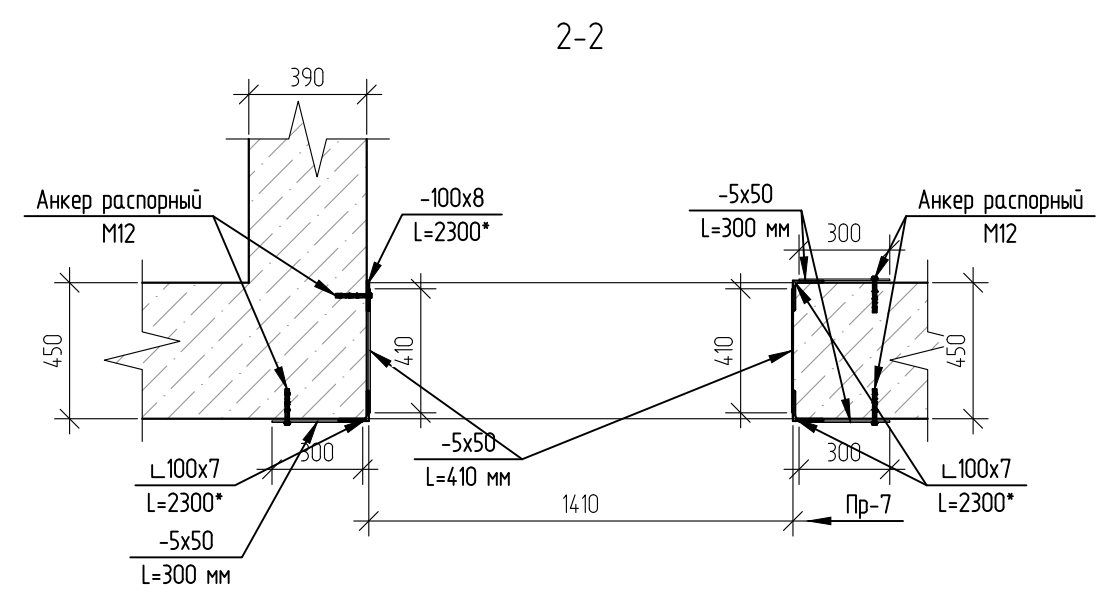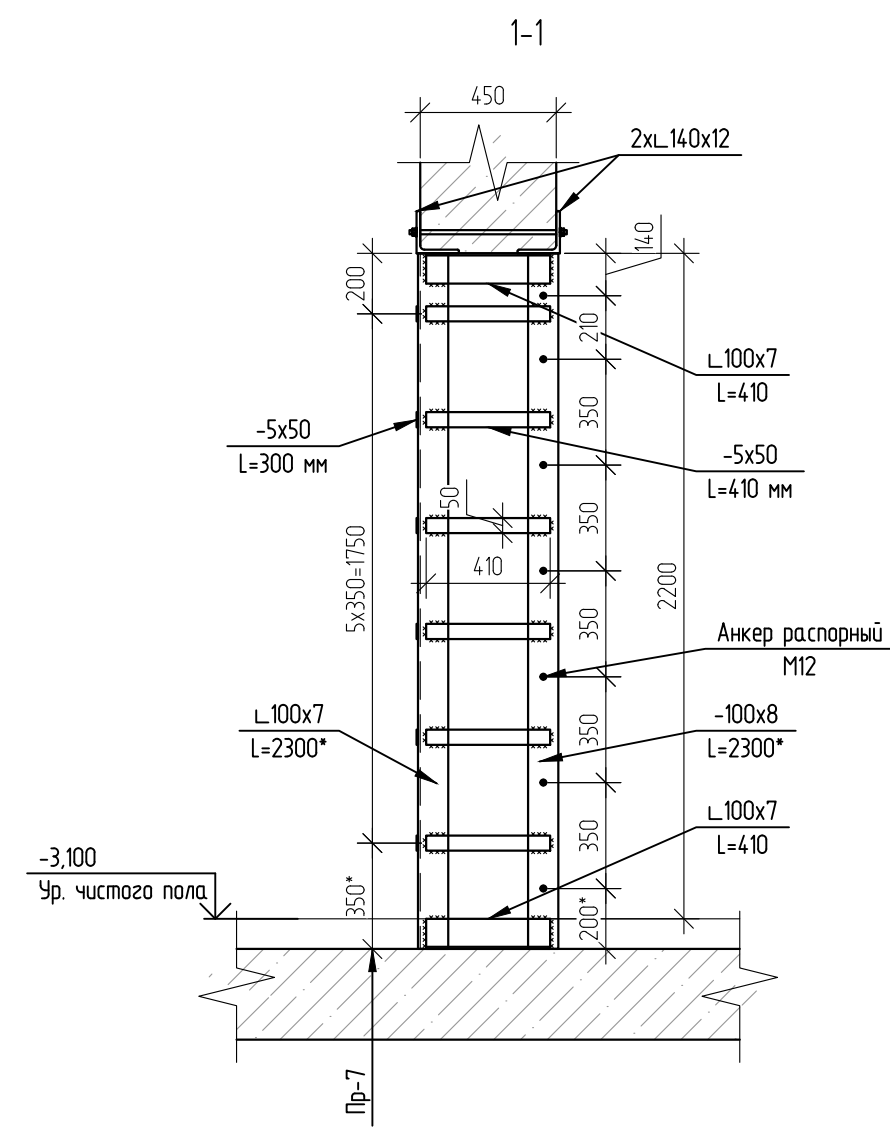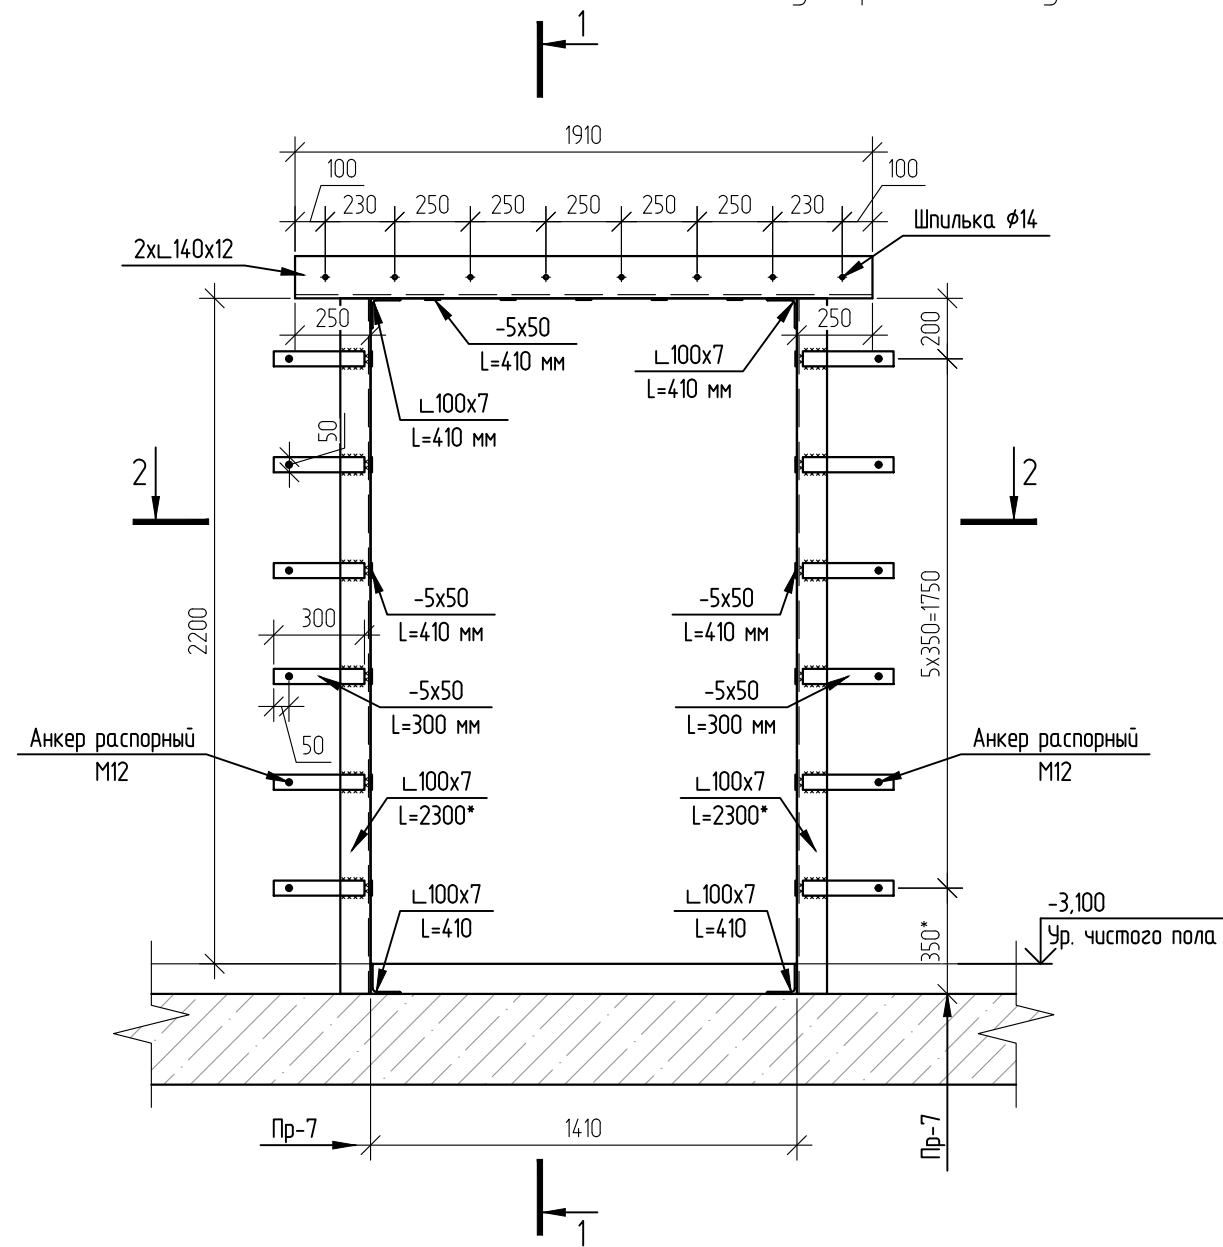

- Порядок выполнения работ по усилению проема:
1. Установить перемычку с двух сторон из L 140x12 и стянуть их шпильками М14.
 2. Установить стальные обоймы из L 100x7 по вертикальным граням и прикрепить их к кладке планками с отверстиями Ø14, закрепить анкерами, соединить уголки планками на сварке.
 3. К планкам привязать стальную сетку 20-06 ГОСТ 5336-80* и оштукатурить ее цементным раствором М100.
 4. Электроды для сварки Э42А по ГОСТ 9467-75*.
 5. Строительно-монтажные работы должны производиться специальной организацией, имеющей лицензию на выполнение таких работ.
 6. При производстве сварочных работ необходимо соблюдать требования СП 70.13330.2012, глава 10 и "Правил пожарной безопасности при проведении сварочных работ..."
 7. После окончания монтажа металлоконструкций должен быть составлен акт на скрытые работы.

						708/П-24-АНО-КР			
						Капитальный ремонт общеобразовательного учреждения ГБОУ "Школа №1210" по адресу: г. Москва, ул. Живописная, д.32			
Изм.	Колуч.	Лист	№ док.	Подп.	Дата	Конструктивные решения	Стадия	Лист	Листов
Разработал	Торшин				04.26		Р	8	
ГАП	Фролова				04.26				
Н.Контроль	Лукашова				04.26	Схема устройства усиления проема Пр-7		комплексное проектирование промышленных и гражданских объектов ООО "АРТИС"	
ГИП	Зыкин				04.26				


1 Схема устройства усиления проемов Пр-6, 23

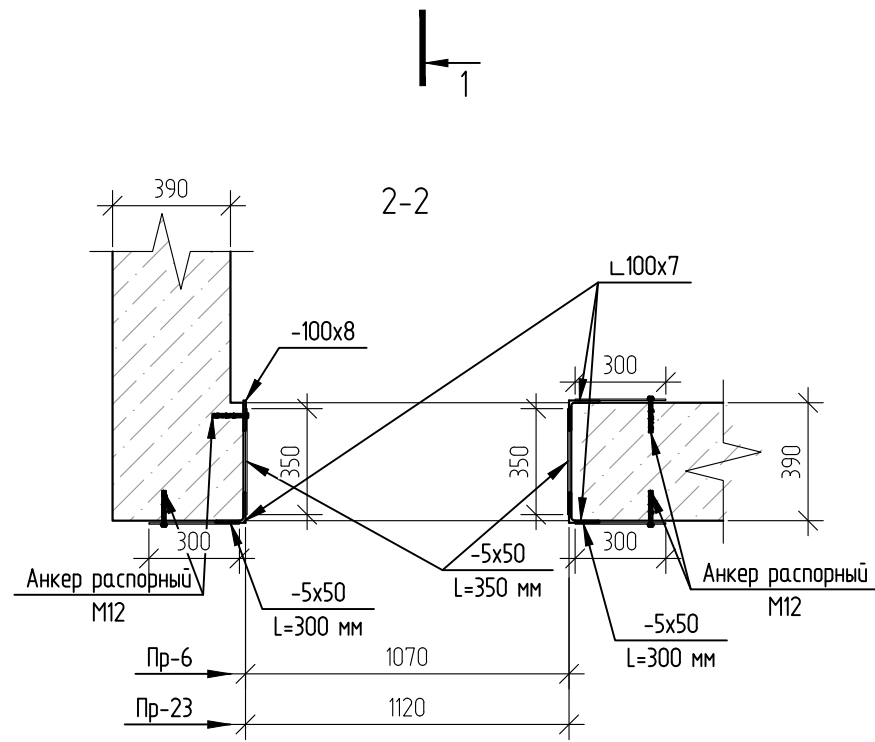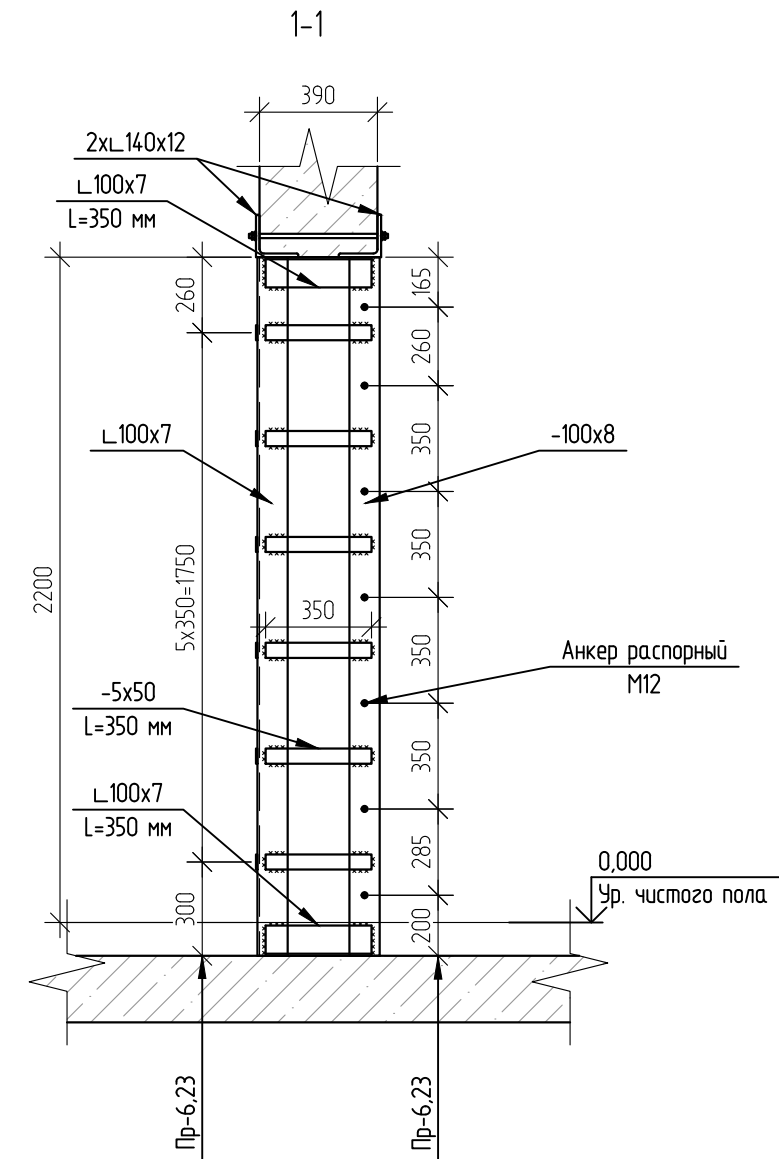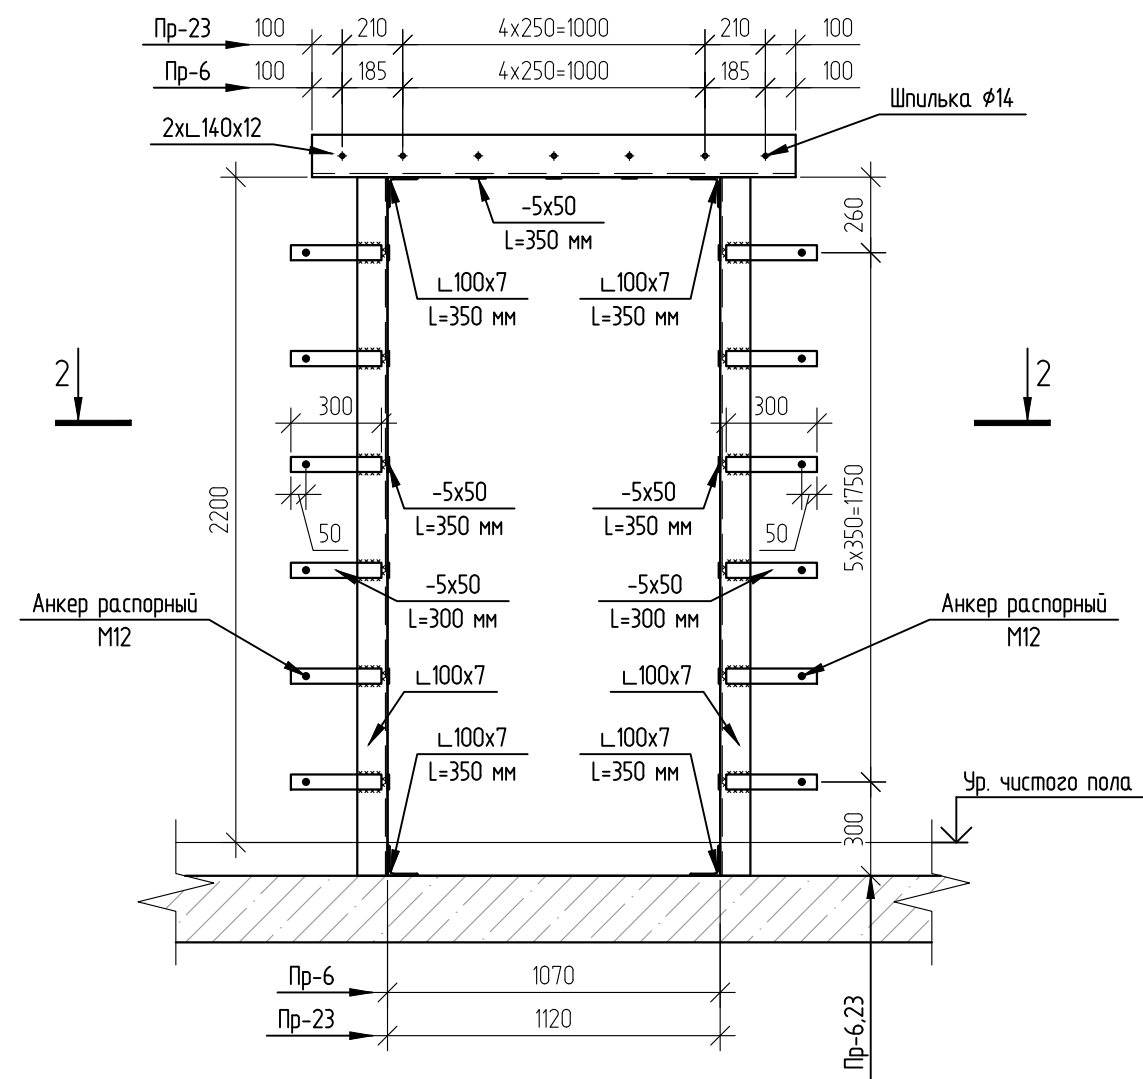

- Порядок выполнения работ по усилению проема:
1. Установить перемычку с двух сторон из L 140x12 и стянуть их шпильками М14.
 2. Установить стальные обоймы из L 100x7 по вертикальным граням и прикрепить их к кладке планками с отверстиями Ø14, закрепить анкерами, соединить уголки планками на сварке.
 3. К планкам привязать стальную сетку 20-0Б ГОСТ 5336-80* и оштукатурить ее цементным раствором М100.
 4. Electrodes for welding Э42А по ГОСТ 9467-75*.
 5. Строительно-монтажные работы должны производиться специальной организацией, имеющей лицензию на выполнение таких работ.
 6. При производстве сварочных работ необходимо соблюдать требования СП 70.13330.2012, глава 10 и "Правил пожарной безопасности при проведении сварочных работ..."
 7. После окончания монтажа металлоконструкций должен быть составлен акт на скрытые работы.

						708/П-24-АНО-КР			
						Капитальный ремонт общеобразовательного учреждения ГБОУ "Школа №1210" по адресу: г. Москва, ул. Живописная, д.32			
Изм.	Кол.уч.	Лист	№ док.	Подп.	Дата	Конструктивные решения	Стадия	Лист	Листов
Разработал	Торшин				04.26		Р	9	
ГАП	Фролова				04.26				
						Схема устройства усиления проемов Пр-6, 23	 комплексное проектирование промышленных и гражданских объектов ООО "АРТИС"		
Н.Контроль	Лукашова				04.26				
ГИП	Зыкин				04.26				


Схема устройства усиления проемов Пр-10-15

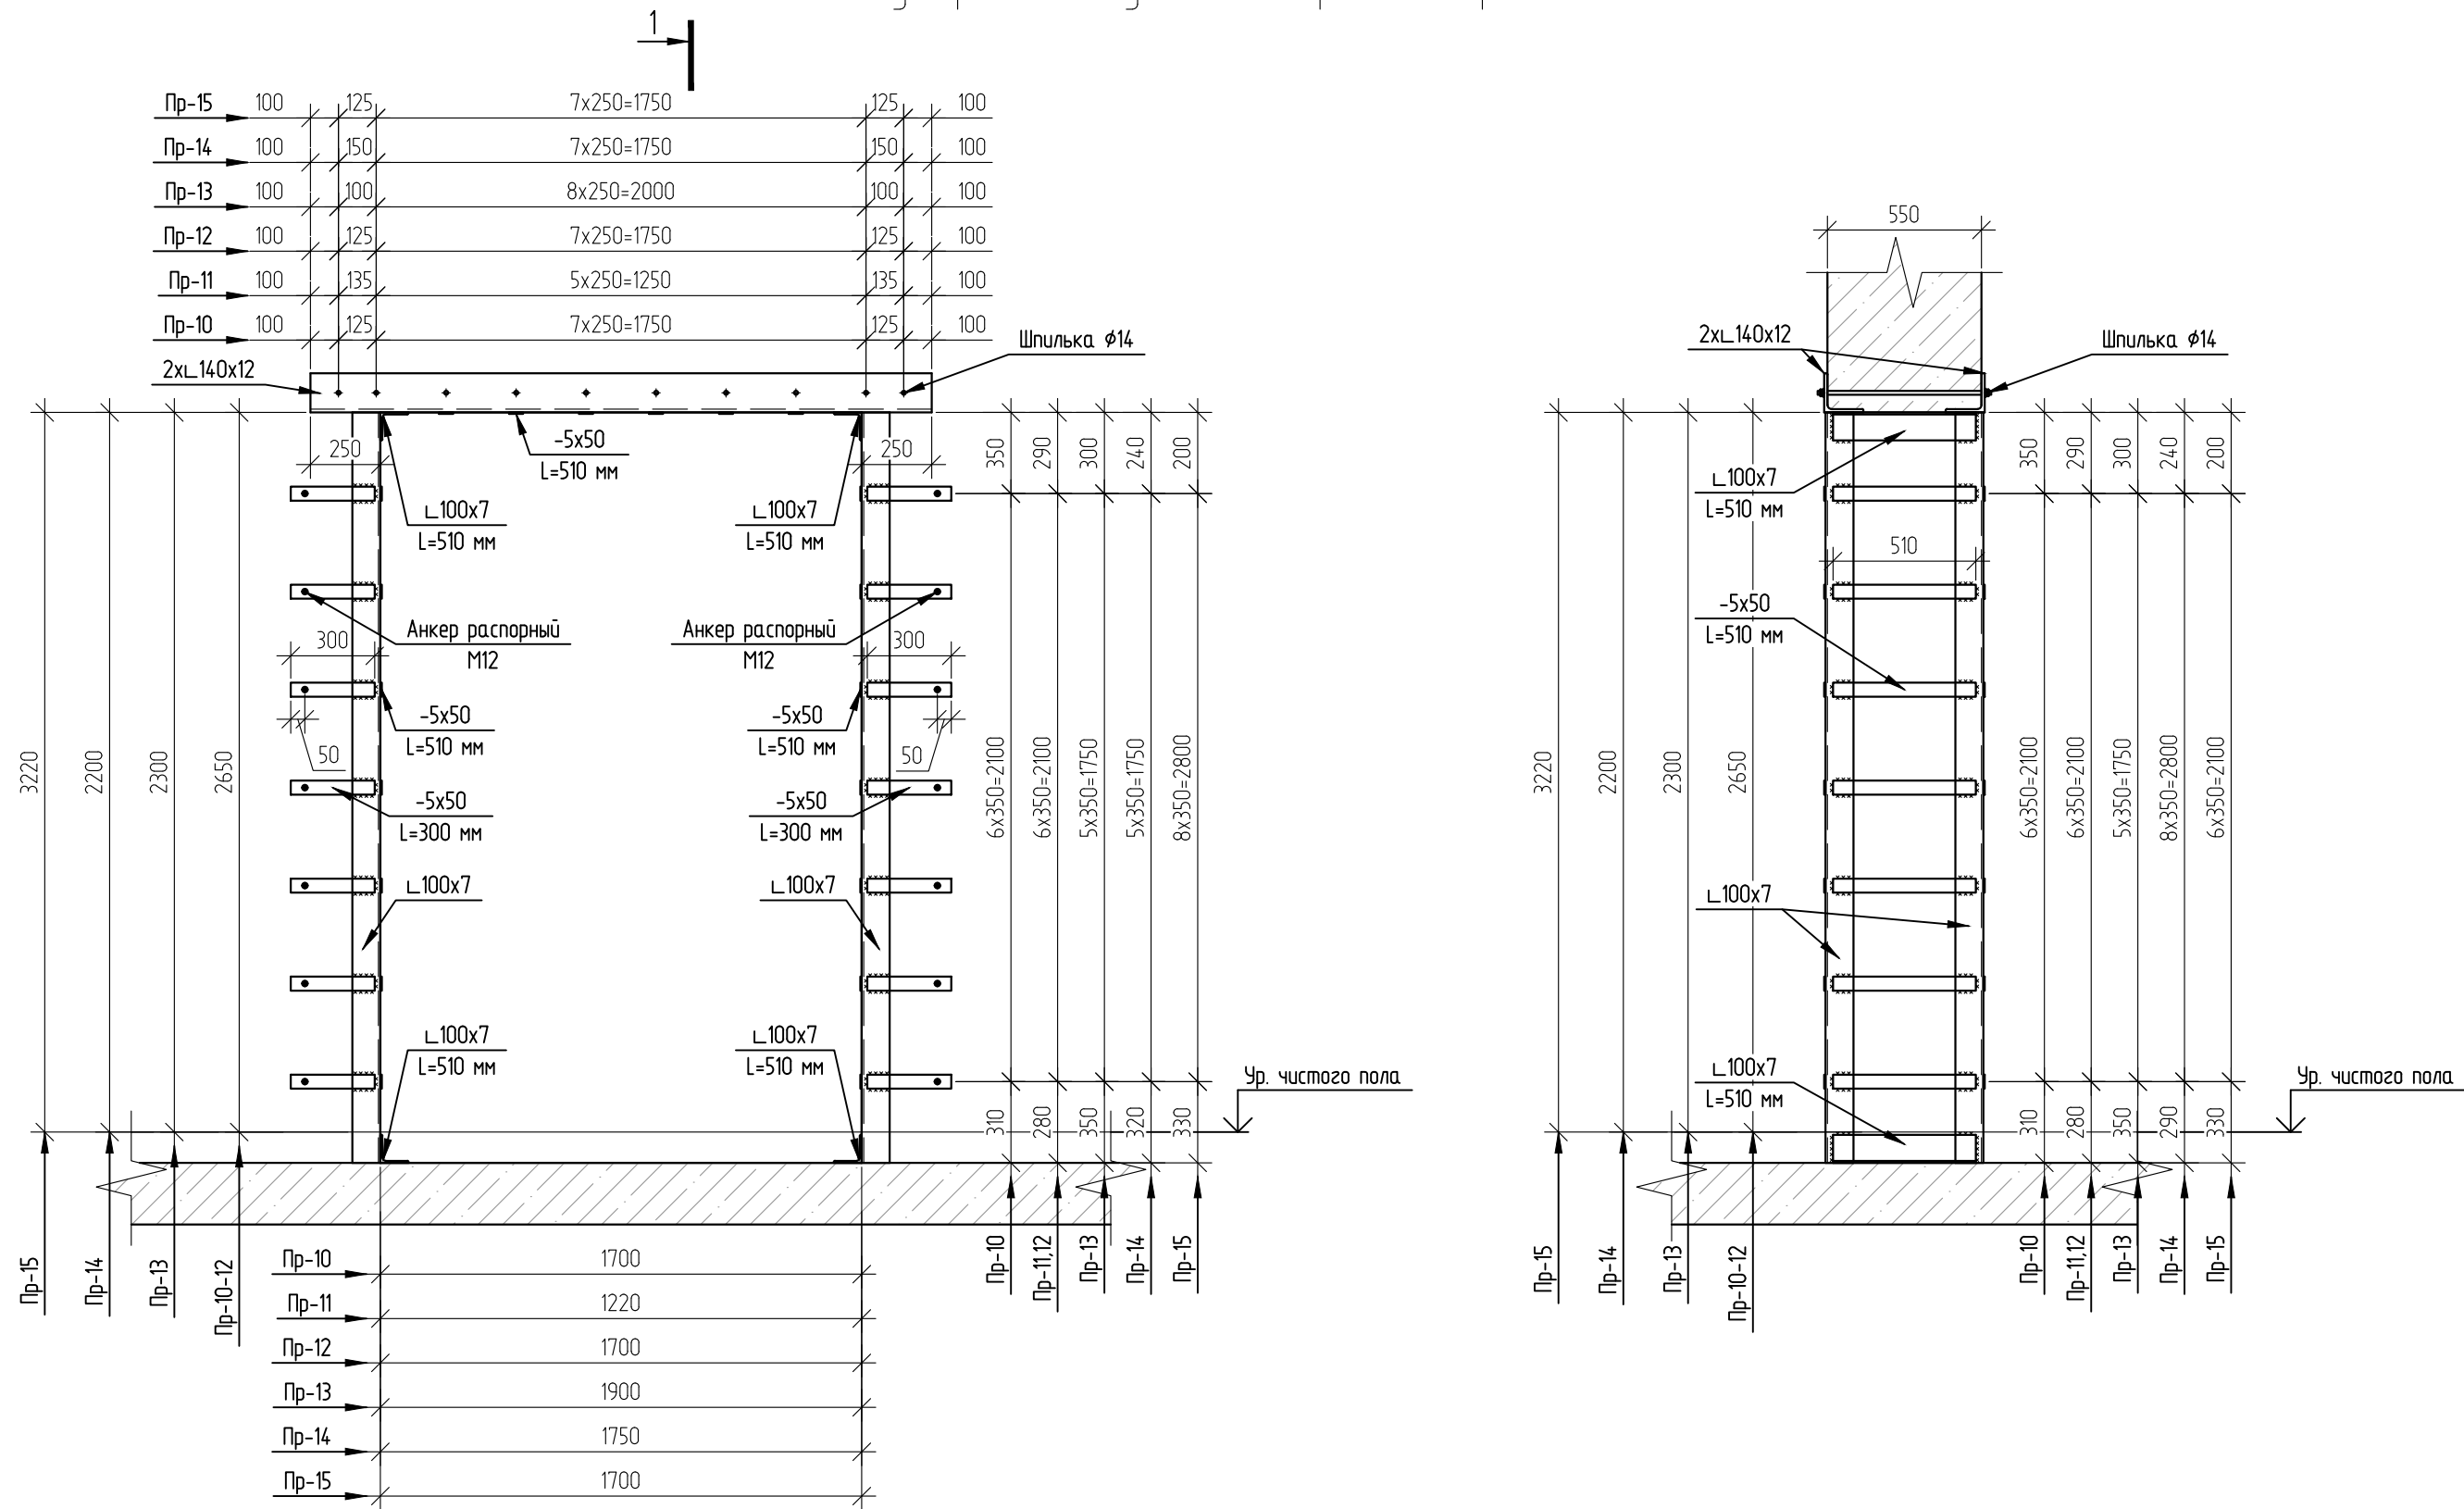

- Порядок выполнения работ по усилению проема:
1. Установить перемычку с двух сторон из L 140x12 и стянуть их шпильками M14.
 2. Установить стальные обоймы из L 100x7 по вертикальным граням и прикрепить их к кладке планками с отверстиями Ø14, закрепить анкерами, соединить уголки планками на сварке.
 3. К планкам привязать стальную сетку 20-0Б ГОСТ 5336-80* и оштукатурить ее цементным раствором М100.
 4. Электроды для сварки Э42А по ГОСТ 9467-75*.
 5. Строительно-монтажные работы должны производиться специальной организацией, имеющей лицензию на выполнение таких работ.
 6. При производстве сварочных работ необходимо соблюдать требования СП 70.13330.2012, глава 10 и "Правил пожарной безопасности при проведении сварочных работ..."
 7. После окончания монтажа металлоконструкций должен быть составлен акт на скрытые работы.

						708/П-24-АНО-КР			
						Капитальный ремонт общеобразовательного учреждения ГБОУ "Школа №1210" по адресу: г. Москва, ул. Живописная, д.32			
Изм.	Кол.уч.	Лист	№ док.	Подп.	Дата	Конструктивные решения	Стадия	Лист	Листов
Разработал	Торшин				04.26		Р	11	
ГАП	Фролова				04.26				
						Схема устройства усиления проемов Пр-10...15		комплексное проектирование промышленных и гражданских объектов ООО "АРТИС"	
Н.Контроль	Лукашова				04.26				
ГИП	Зыкин				04.26				

Схема устройства усиления проема Пр-16


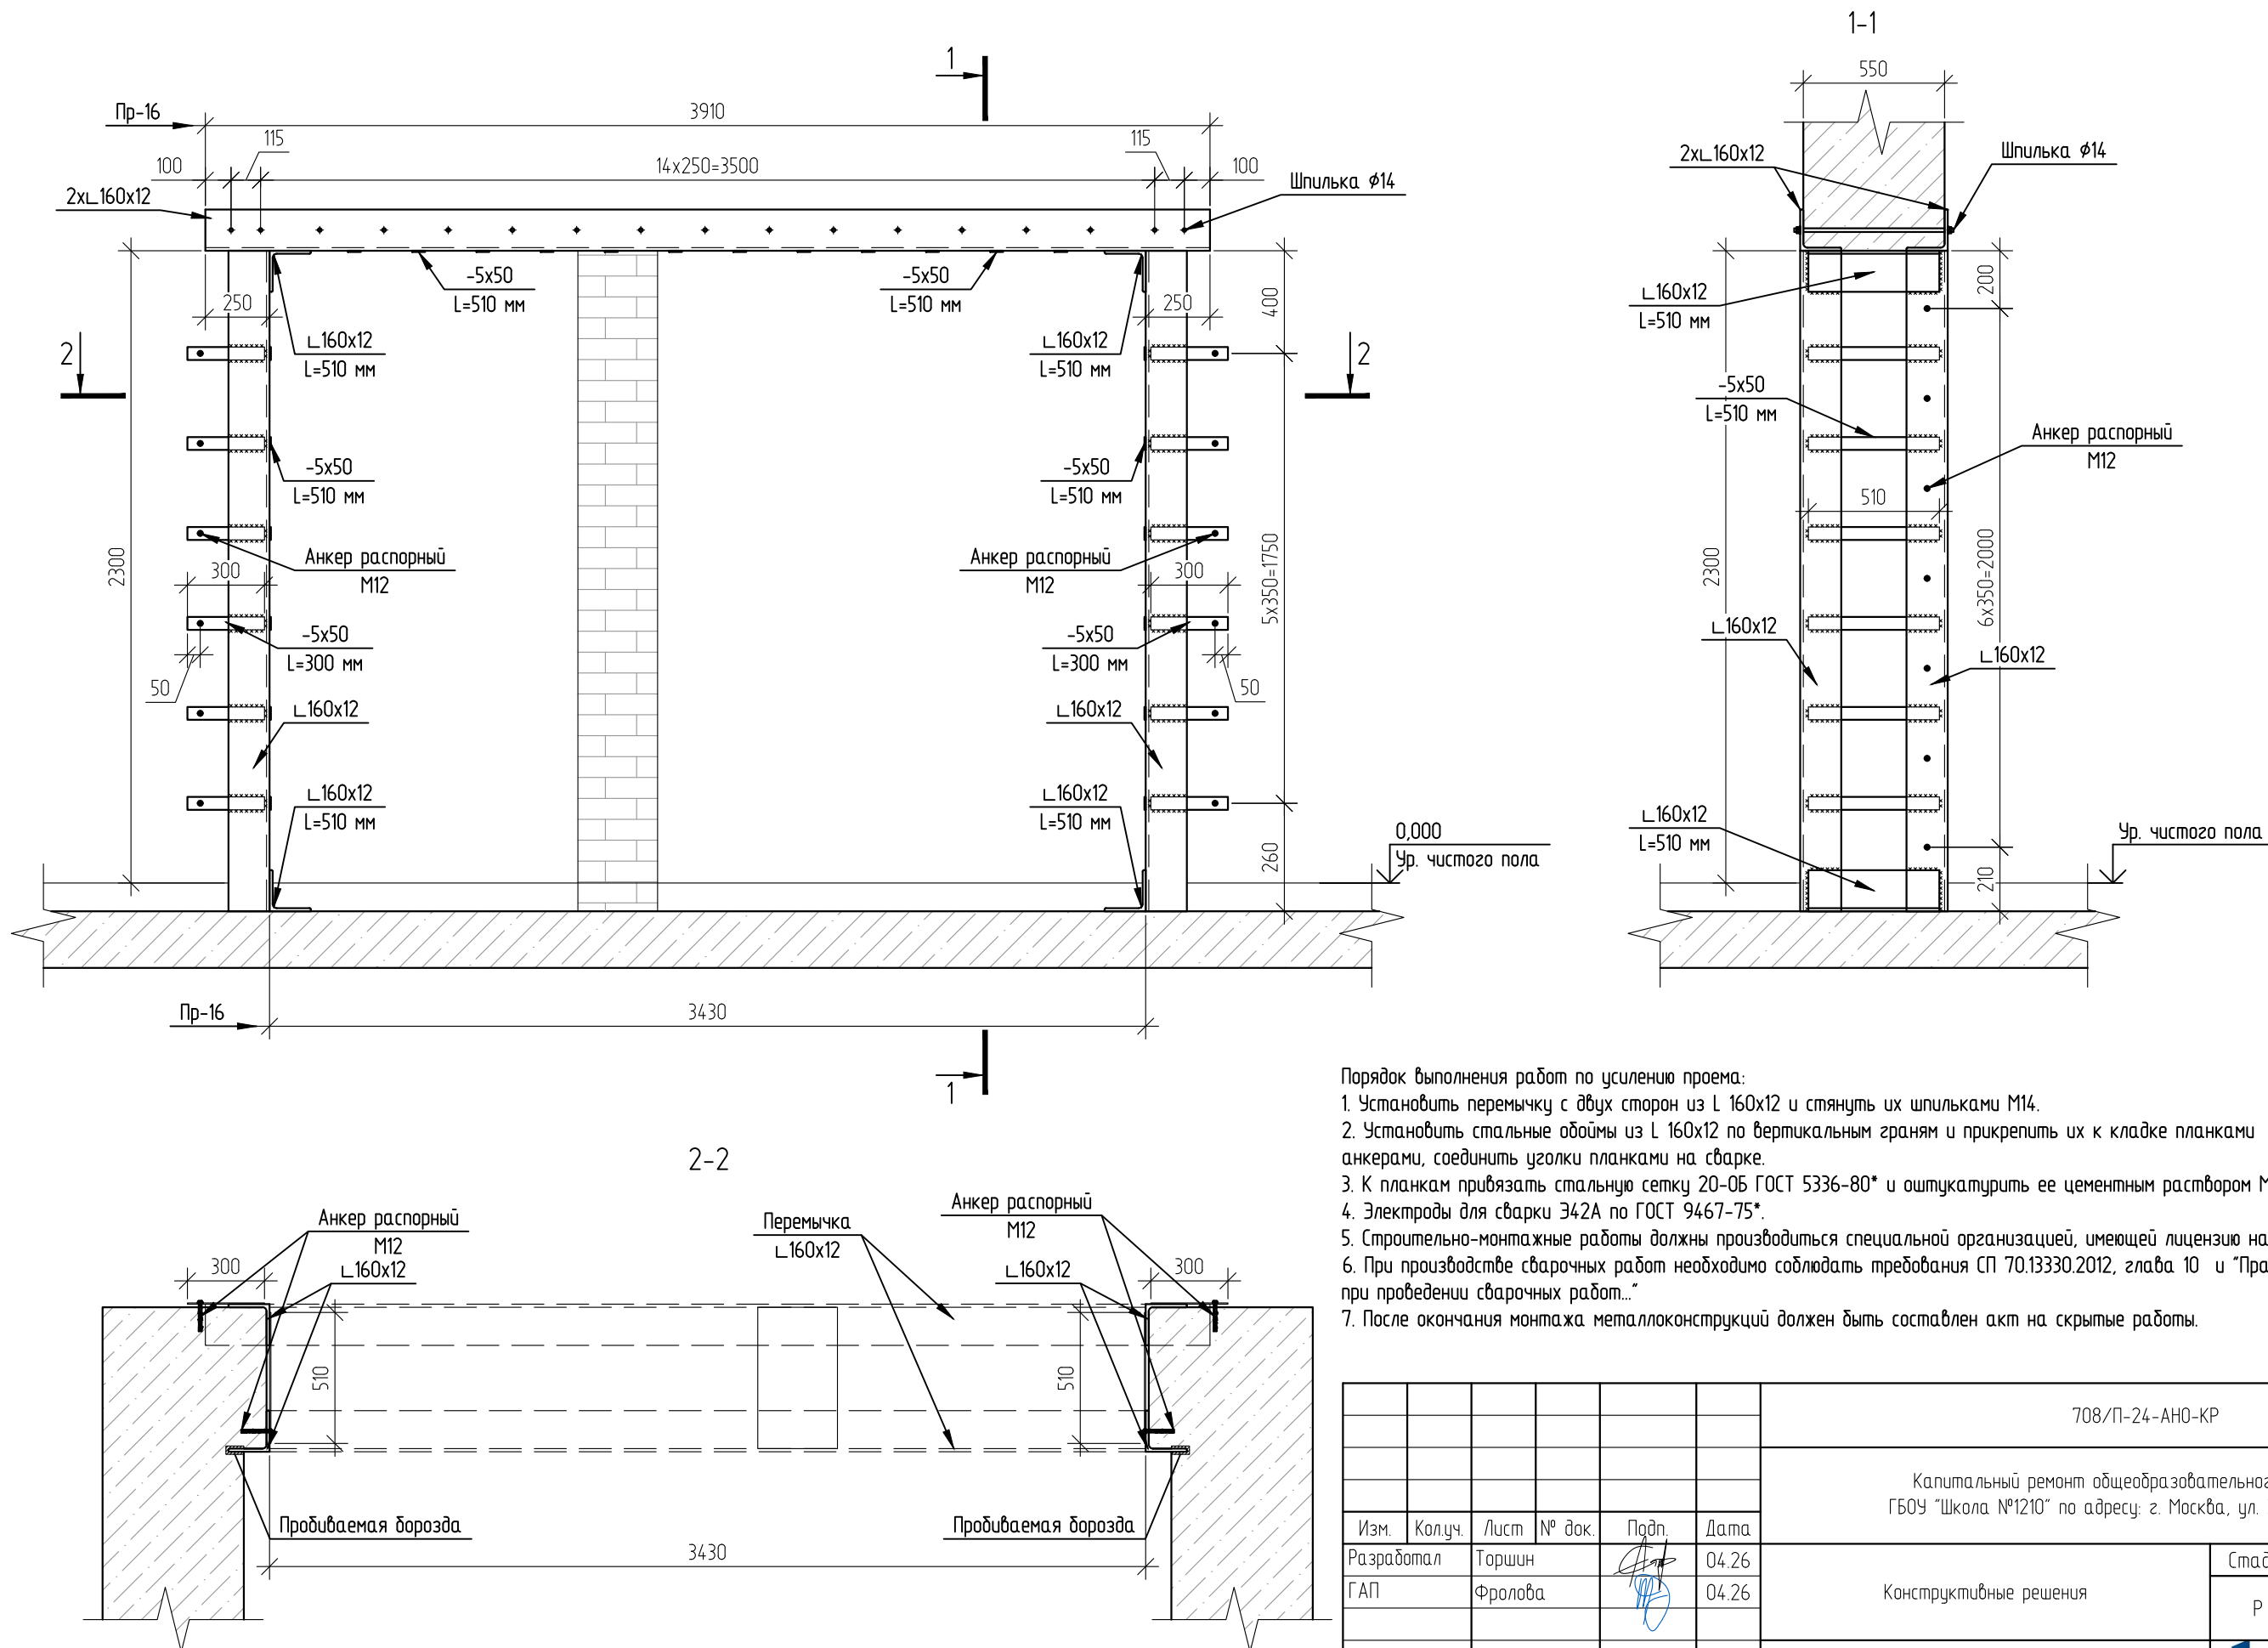


Порядок выполнения работ по усилению проема:

1. Установить перемычку с двух сторон из L 160x12 и стянуть их шпильками M14.
2. Установить стальные ободы из L 160x12 по вертикальным граням и прикрепить их к кладке планками с отверстиями $\phi 14$, закрепить анкерами, соединить уголки планками на сварке.
3. К планкам привязать стальную сетку 20-06 ГОСТ 5336-80* и оштукатурить ее цементным раствором М100.
4. Электроды для сварки Э42А по ГОСТ 9467-75*.
5. Строительно-монтажные работы должны производиться специальной организацией, имеющей лицензию на выполнение таких работ.
6. При производстве сварочных работ необходимо соблюдать требования СП 70.13330.2012, глава 10 и "Правил пожарной безопасности при проведении сварочных работ..."
7. После окончания монтажа металлоконструкций должен быть составлен акт на скрытые работы.

						708/П-24-АНО-КР		
						Капитальный ремонт общеобразовательного учреждения ГБОУ "Школа №1210" по адресу: г. Москва, ул. Живописная, д.32		
Изм.	Кол.уч.	Лист	№ док.	Подп.	Дата	Конструктивные решения	Стадия	Лист
Разработал	Торшин				04.26		Р	12
ГАП	Фралова				04.26	Схема устройства усиления проема Пр-16		ООО "АРТИС"
Н.Контроль	Лукашова				04.26			
ГИП	Зыкин				04.26			

Схема устройства усиления проемов Пр-17-22

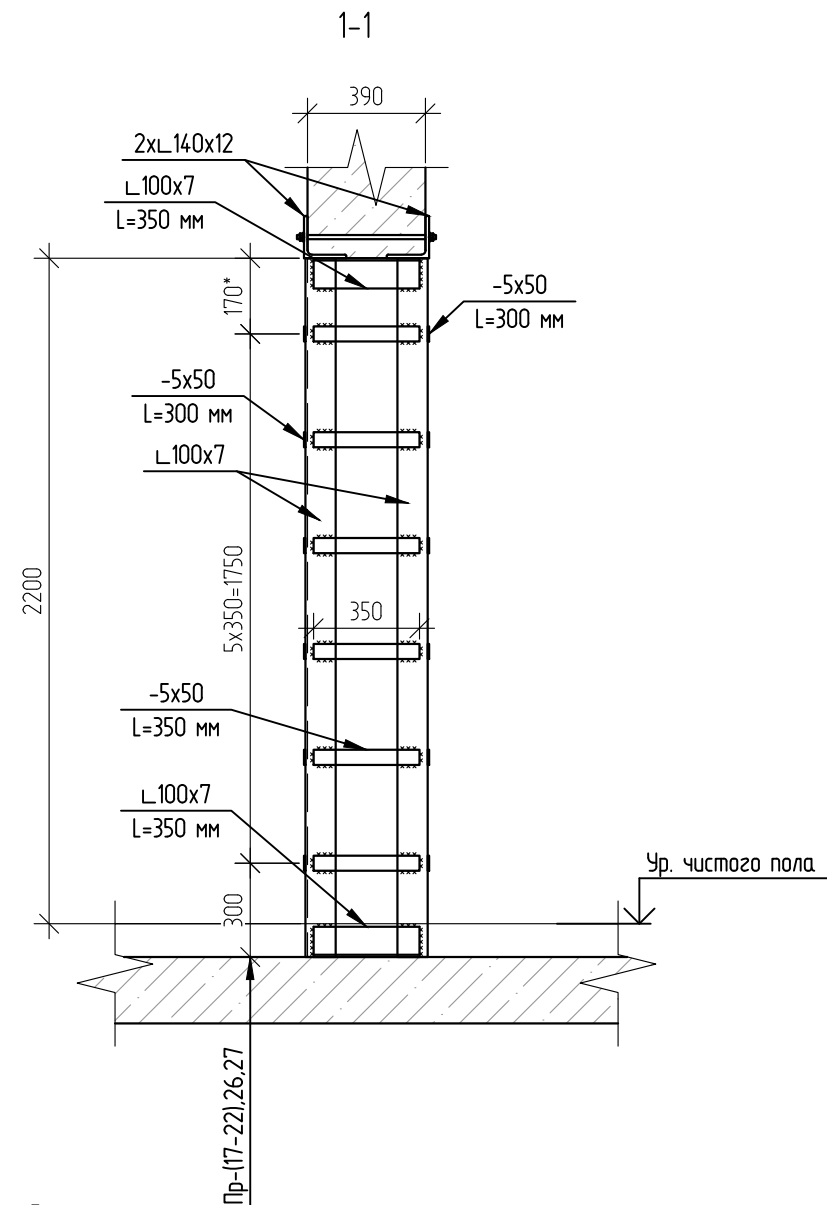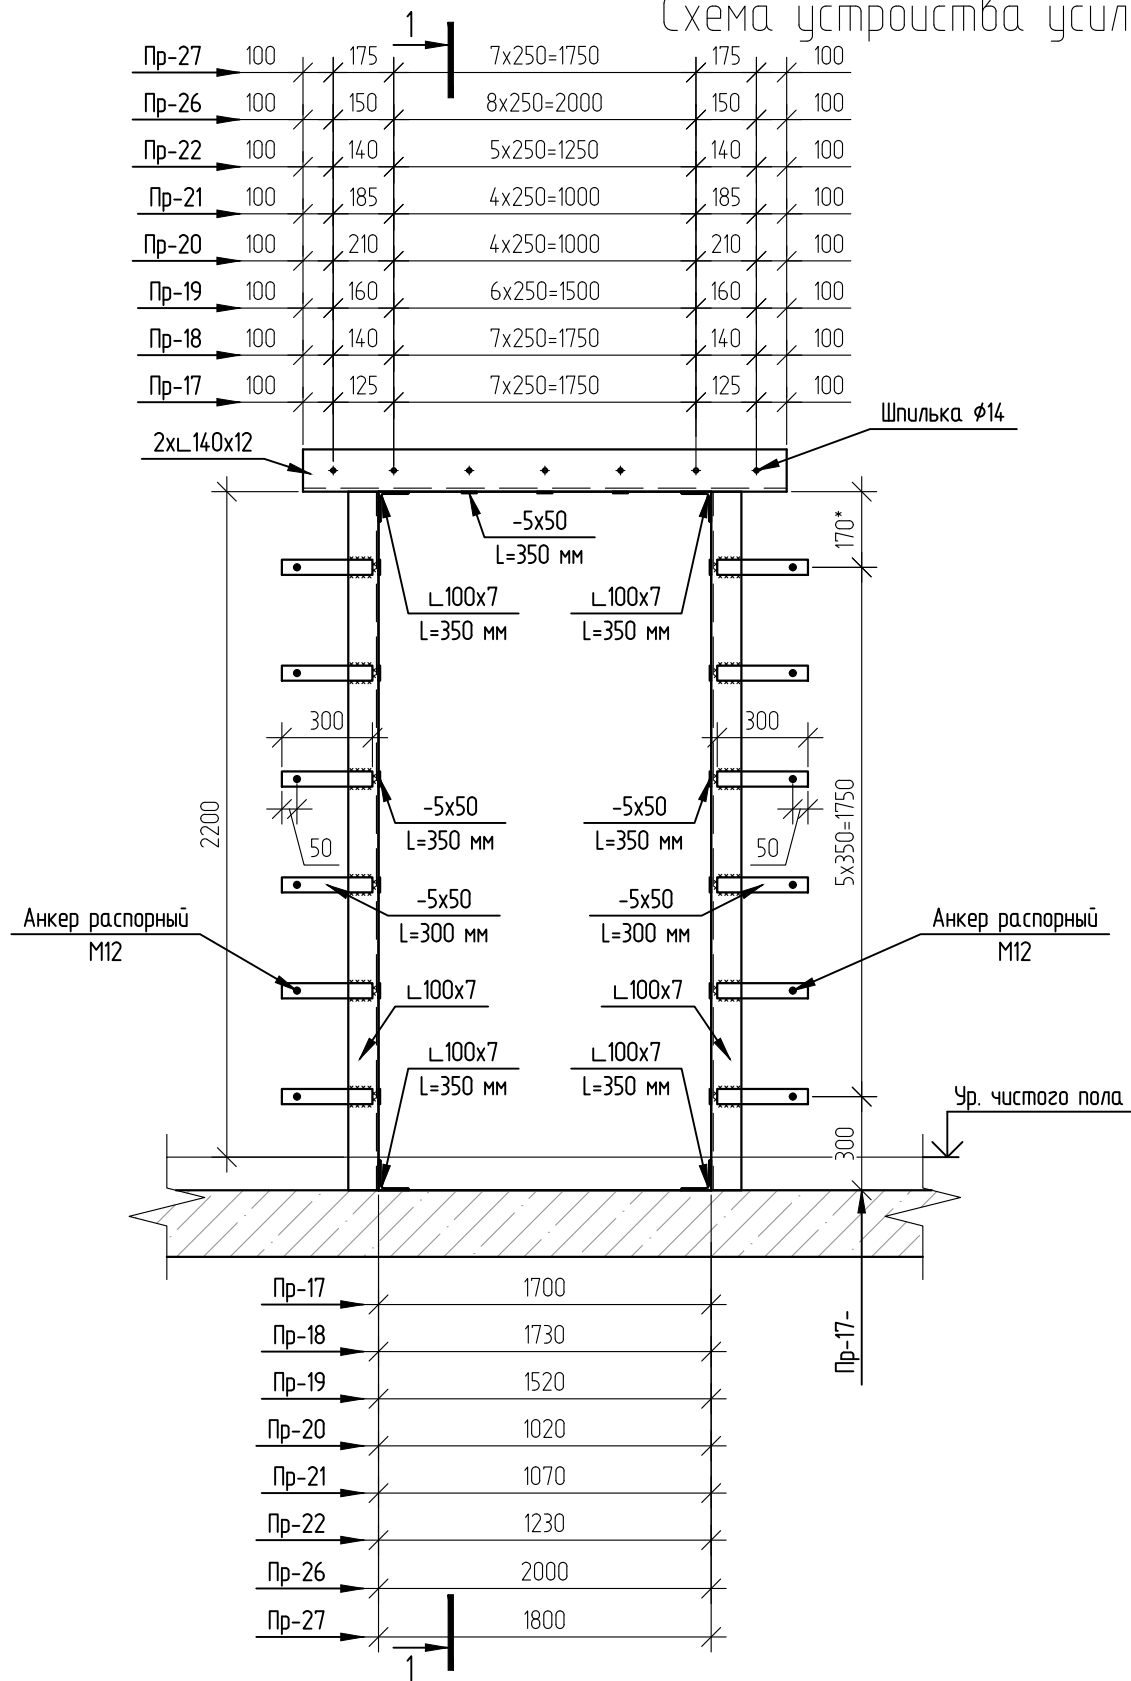


Порядок выполнения работ по усилению проема:

1. Установить перемычку с двух сторон из L 140x12 и стянуть их шпильками М14.
2. Установить стальные обоймы из L 100x7 по вертикальным граням и прикрепить их к кладке планками с отверстиями Ø14, закрепить анкерами, соединить уголки планками на сварке.
3. К планкам привязать стальную сетку 20-0Б ГОСТ 5336-80* и оштукатурить ее цементным раствором М100.
4. Electroды для сварки З42А по ГОСТ 9467-75*.
5. Строительно-монтажные работы должны производиться специальной организацией, имеющей лицензию на выполнение таких работ.
6. При производстве сварочных работ необходимо соблюдать требования СП 70.13330.2012, глава 10 и "Правил пожарной безопасности при проведении сварочных работ..."
7. После окончания монтажа металлоконструкций должен быть составлен акт на скрытые работы.

						708/П-24-АНО-КР		
						Капитальный ремонт общеобразовательного учреждения ГБОУ "Школа №1210" по адресу: г. Москва, ул. Живописная, д.32		
Изм.	Кол.уч.	Лист	№ док.	Подп.	Дата	Конструктивные решения	Стадия	Лист
Разработал	Торшин				04.26		Р	13
ГАП	Фралова				04.26			
						Схема устройства усиления проемов Пр-17...22, 26, 27	 ООО "АРТИС"	
Н.Контроль	Лукашова				04.26			
ГИП	Зыкин				04.26			



Схема устройства усиления проемов Пр-24

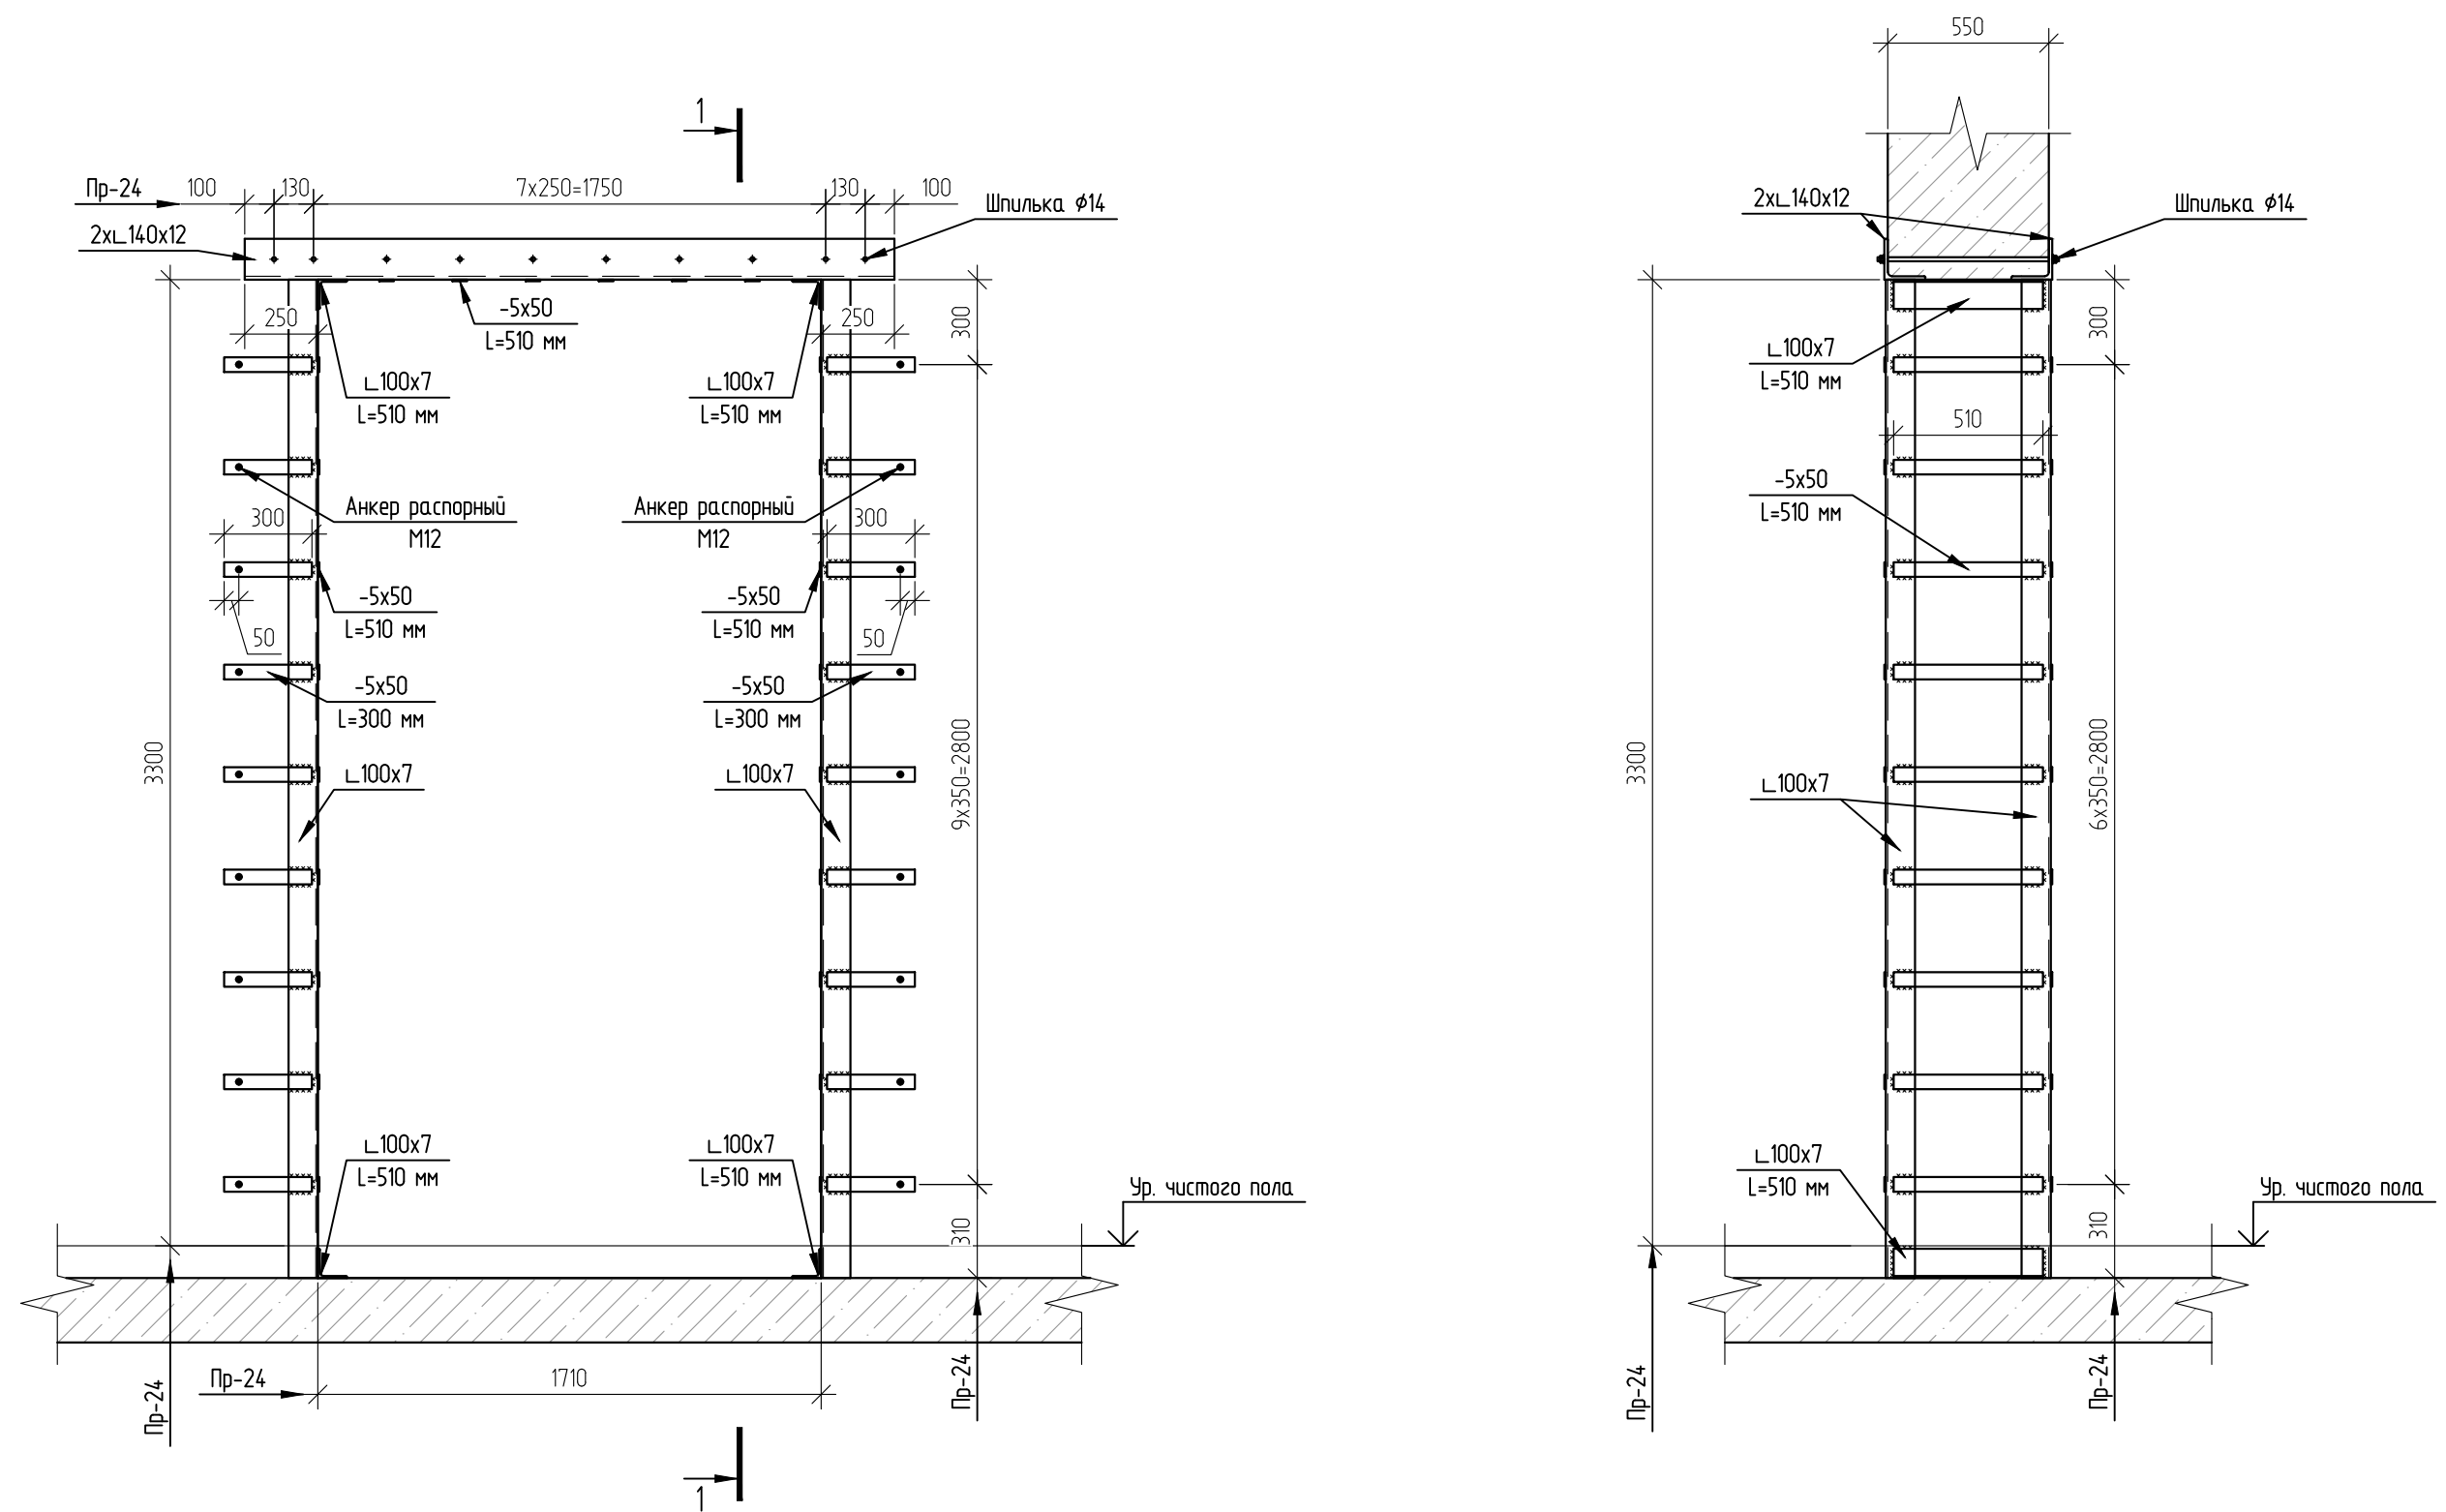

- Порядок выполнения работ по усилению проема:
1. Установить перемычку с двух сторон из L 140x12 и стянуть их шпильками М14.
 2. Установить стальные обоймы из L 100x7 по вертикальным граням и прикрепить их к кладке планками с отверстиями Ø14, закрепить анкерами, соединить уголки планками на сварке.
 3. К планкам привязать стальную сетку 20-0Б ГОСТ 5336-80* и оштукатурить ее цементным раствором М100.
 4. Electrodes for welding Э42А по ГОСТ 9467-75*.
 5. Строительно-монтажные работы должны производиться специальной организацией, имеющей лицензию на выполнение таких работ.
 6. При производстве сварочных работ необходимо соблюдать требования СП 70.13330.2012, глава 10 и "Правил пожарной безопасности при проведении сварочных работ..."
 7. После окончания монтажа металлоконструкций должен быть составлен акт на скрытые работы.

						708/П-24-АНО-КР		
						Капитальный ремонт общеобразовательного учреждения ГБОУ "Школа №1210" по адресу: г. Москва, ул. Живописная, д.32		
Изм.	Кол.уч.	Лист	№ док.	Подп.	Дата	Конструктивные решения	Стадия	Лист
Разработал	Торшин				04.26		Р	14
ГАП	Фралова				04.26	Схема устройства усиления проемов Пр-24	 ООО "АРТИС" комплексное проектирование промышленных и гражданских объектов	
Н.Контроль	Лукашова				04.26			
ГИП	Зыкин				04.26			

Схема устройства усиления проемов Пр-25

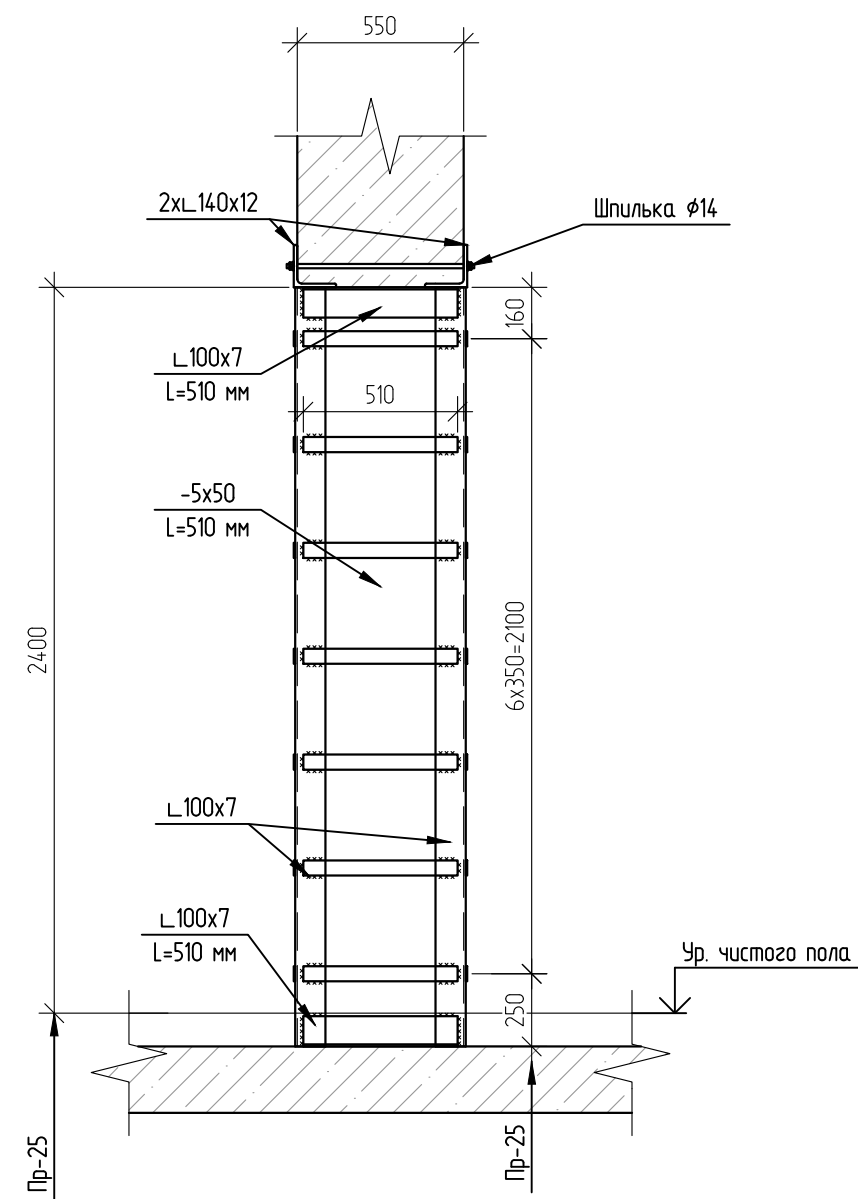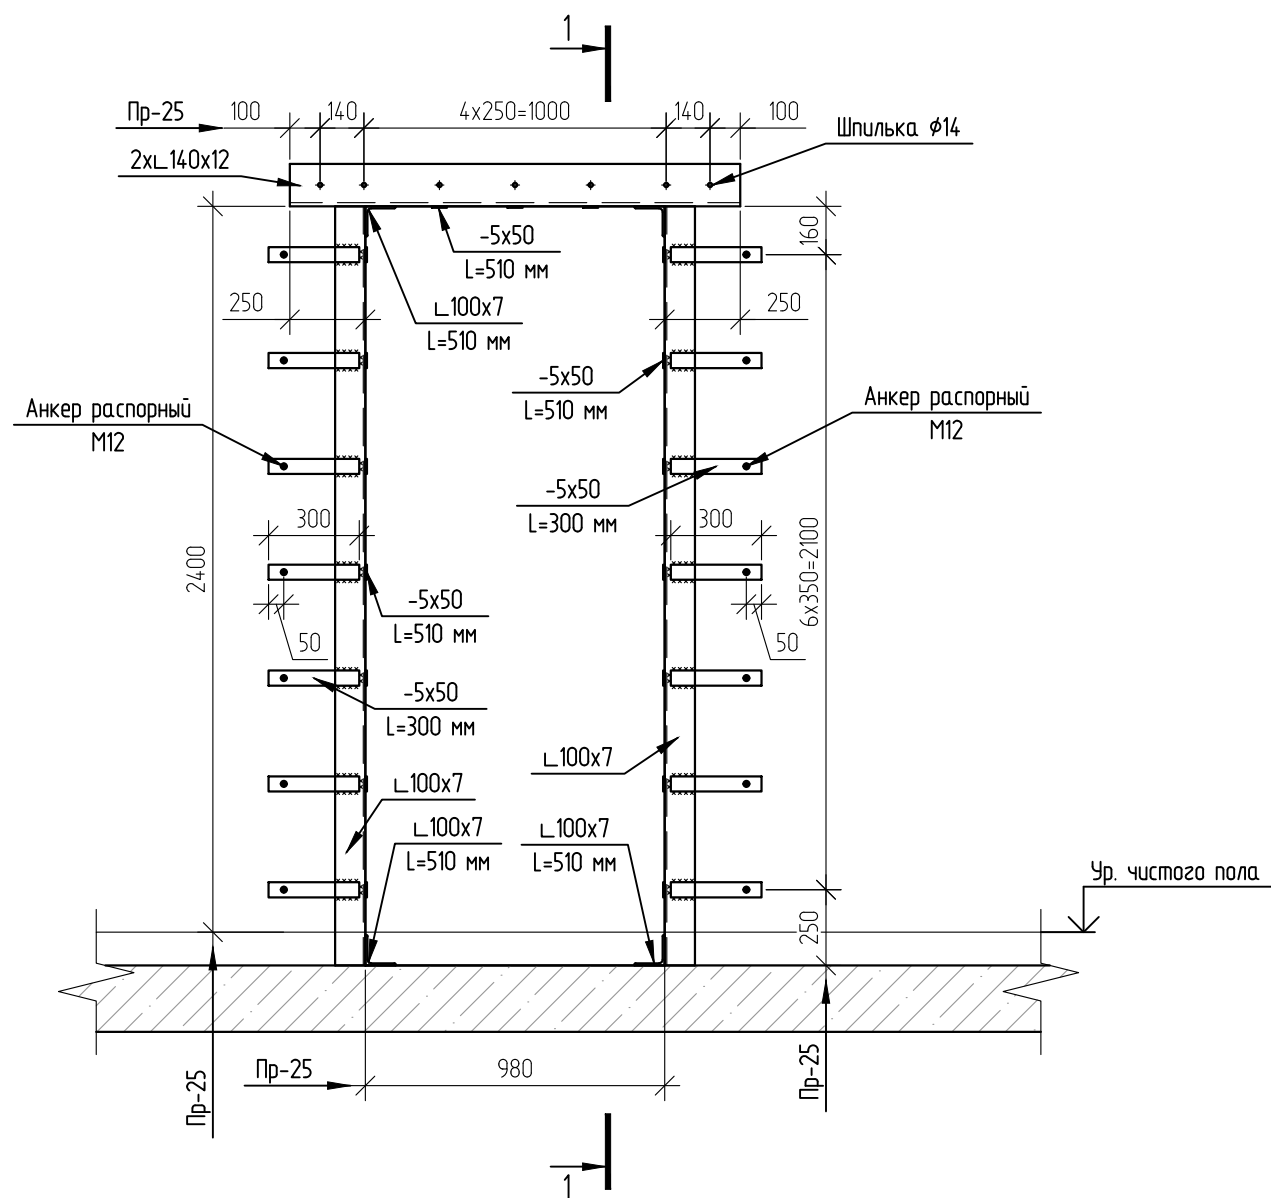

- Порядок выполнения работ по усилению проема:
1. Установить перемычку с двух сторон из L 140x12 и стянуть их шпильками М14.
 2. Установить стальные обоймы из L 100x7 по вертикальным граням и прикрепить их к кладке планками с отверстиями Ø14, закрепить анкерами, соединить уголки планками на сварке.
 3. К планкам привязать стальную сетку 20-0Б ГОСТ 5336-80* и оштукатурить ее цементным раствором М100.
 4. Electroды для сварки Э42А по ГОСТ 9467-75*.
 5. Строительно-монтажные работы должны производиться специальной организацией, имеющей лицензию на выполнение таких работ.
 6. При производстве сварочных работ необходимо соблюдать требования СП 70.13330.2012, глава 10 и "Правил пожарной безопасности при проведении сварочных работ..."
 7. После окончания монтажа металлоконструкций должен быть составлен акт на скрытые работы.

						708/П-24-АНО-КР		
						Капитальный ремонт общеобразовательного учреждения ГБОУ "Школа №1210" по адресу: г. Москва, ул. Живописная, д.32		
Изм.	Кол.уч.	Лист	№ док.	Подп.	Дата	Конструктивные решения	Стадия	Лист
Разработал	Торшин				04.26		Р	15
ГАП	Фралова				04.26	Схема устройства усиления проемов Пр-25	 ООО "АРТИС" комплексное проектирование промышленных и гражданских объектов	
Н.Контроль	Лукашова				04.26			
ГИП	Зыкин				04.26			

Спецификация материалов на устройство усиления					
Поз.	Обозначение	Наименование	Кол.	Масса, ед. кг	Примечание
		Проем Пр-1 1070х2200	1		
	ГОСТ 8240-89	Швеллер 22П, L=1570	2	33.2	66.4
	ГОСТ 8509-93	Уголок 100х7, L=2250	4	24.3	97.2
	ГОСТ 8509-93	Уголок 100х7, L=360	4	3.9	15.6
	ГОСТ 19903-2015	Лист 5х50, L=300	24	0.6	14.4
	ГОСТ 19903-2015	Лист 5х50, L=360	15	0.71	10.7
	ГОСТ 5915-70	Гайка М14-6Н5.016	14		
	ГОСТ6958-70	Шайба 14.01.016	14		
	ГОСТ 22042-76	Шпилька М14-6gx440.58.016	7		
		Анкер распорный М12	24		
		Проем Пр-2 670х1400	1		
	ГОСТ 8240-89	Уголок 140х12, L=1170	2	30,2	60.4
	ГОСТ 8509-93	Уголок 100х7, L=1450	4	15,7	62.8
	ГОСТ 8509-93	Уголок 100х7, L=410	4	4.5	18.0
	ГОСТ 19903-2015	Лист 5х50, L=300	14	0.6	8.4
	ГОСТ 19903-2015	Лист 5х50, L=410	10	0.8	8.0
	ГОСТ 5915-70	Гайка М14-6Н5.016	10		
	ГОСТ6958-70	Шайба 14.01.016	10		
	ГОСТ 22042-76	Шпилька М14-6gx440.58.016	5		
		Анкер распорный М12	24		
		Проем Пр-3 1410х2200	1		
	ГОСТ 8509-93	Уголок 140х12, L=1910	2	49	98.0
	ГОСТ 8509-93	Уголок 100х7, L=2250	4	24.3	97.2
	ГОСТ 8509-93	Уголок 100х7, L=410	4	4.4	17.6
	ГОСТ 19903-2015	Лист 5х50, L=300	24	0.6	14.4
	ГОСТ 19903-2015	Лист 5х50, L=410	17	0.8	13.6
	ГОСТ 5915-70	Гайка М14-6Н5.016	18		
	ГОСТ6958-70	Шайба 14.01.016	18		
	ГОСТ 22042-76	Шпилька М14-6gx440.58.016	9		
		Анкер распорный М12	24		

Спецификация материалов на устройство усиления					
Поз.	Обозначение	Наименование	Кол.	Масса, ед. кг	Примечание
		Проем Пр-4 970х2200	1		
	ГОСТ 8509-93	Уголок 140х12, L=1470	2	37,8	75.6
	ГОСТ 8509-93	Уголок 100х7, L=2250	4	24,3	97.2
	ГОСТ 8509-93	Уголок 100х7, L=410	4	4.43	17.7
	ГОСТ 19903-2015	Лист 5х50, L=300	24	0.6	14.4
	ГОСТ 19903-2015	Лист 5х50, L=410	16	0.8	12.8
	ГОСТ 5915-70	Гайка М14-6Н5.016	16		
	ГОСТ6958-70	Шайба 14.01.016	16		
	ГОСТ 22042-76	Шпилька М14-6gx440.58.016	8		
		Анкер распорный М12	24		
		Проем Пр-5 1070х2200	1		
	ГОСТ 8509-93	Уголок 140х12, L=1570	2	40,3	80.6
	ГОСТ 8509-93	Уголок 100х7, L=2250	4	24,3	97.2
	ГОСТ 8509-93	Уголок 100х7, L=410	4	4.43	17.7
	ГОСТ 19903-2015	Лист 5х50, L=300	24	0.6	14.4
	ГОСТ 19903-2015	Лист 5х50, L=410	16	0.8	12.8
	ГОСТ 5915-70	Гайка М14-6Н5.016	16		
	ГОСТ6958-70	Шайба 14.01.016	16		
	ГОСТ 22042-76	Шпилька М14-6gx440.58.016	8		
		Анкер распорный М12	24		

						708/П-24-АНО-КР				
						Капитальный ремонт общеобразовательного учреждения ГБОУ "Школа №1210" по адресу: г. Москва, ул. Живописная, д.32				
Изм.	Кол.уч.	Лист	№ док.	Подп.	Дата	Конструктивные решения	Стадия	Лист	Листов	
Разработал	Торшин				04.26		Р	15.1		
ГАП	Фролова				04.26					
						Спецификации	 комплексное проектирование промышленных и гражданских объектов ООО "АРТИС"			
Н.Контроль	Лукашова				04.26					
ГИП	Зыкин				04.26					

Спецификация материалов на устройство усиления					
Поз.	Обозначение	Наименование	Кол.	Масса, ед. кг	Примечание
		Проем Пр-6 1070х2200	1		
	ГОСТ 8509-93	Уголок 140х12, L=1570	2	40,3	80,6
	ГОСТ 8509-93	Уголок 100х7, L=2310	3	25	75,0
	ГОСТ 8509-93	Уголок 100х7, L=350	4	3,8	15,2
	ГОСТ 19903-2015	Лист 8х100, L=2310	1	14,5	14,5
	ГОСТ 19903-2015	Лист 5х50, L=300	20	0,6	12,0
	ГОСТ 19903-2015	Лист 5х50, L=350	14	0,7	9,8
	ГОСТ 5915-70	Гайка М14-6Н5.016	14		
	ГОСТ6958-70	Шайба 14.01.016	14		
	ГОСТ 22042-76	Шпилька М14-6gx440.58.016	7		
		Анкер распорный М12	20		
		Проем Пр-7 1410х2200	2		
	ГОСТ 8509-93	Уголок 140х12, L=1910	2	49	98,0
	ГОСТ 8509-93	Уголок 100х7, L=2300	3	24,8	74,4
	ГОСТ 8509-93	Уголок 100х7, L=410	4	4,4	17,6
	ГОСТ 19903-2015	Лист 8х100, L=2300	1	14,4	14,4
	ГОСТ 19903-2015	Лист 5х50, L=300	18	0,6	10,8
	ГОСТ 19903-2015	Лист 5х50, L=410	15	0,8	12,0
	ГОСТ 5915-70	Гайка М14-6Н5.016	16		
	ГОСТ6958-70	Шайба 14.01.016	16		
	ГОСТ 22042-76	Шпилька М14-6gx440.58.016	8		
		Анкер распорный М12	24		
		Проем Пр-8 1170х2200	1		
	ГОСТ 8509-93	Уголок 160х12, L=3135	2	92,2	184,4
	ГОСТ 8509-93	Уголок 100х7, L=2300	8	24,9	199,2
	ГОСТ 8509-93	Уголок 100х7, L=410	8	4,5	36,0
	ГОСТ 19903-2015	Лист 5х50, L=300	21	0,6	12,6
	ГОСТ 19903-2015	Лист 8х100, L=2300	1	14,4	14,4
	ГОСТ 19903-2015	Лист 5х50, L=255	12	0,5	6,0
	ГОСТ 19903-2015	Лист 5х50, L=410	50	0,8	40,0
	ГОСТ 5915-70	Гайка М14-6Н5.016	26		
	ГОСТ6958-70	Шайба 14.01.016	26		
	ГОСТ 22042-76	Шпилька М14-6gx440.58.016	13		
		Анкер распорный М12	28		

Спецификация материалов на устройство усиления					
Поз.	Обозначение	Наименование	Кол.	Масса, ед. кг	Примечание
		Проем Пр-9 1410х2200	1		
	ГОСТ 8509-93	Уголок 140х12, L=1910	2	51,3	102,6
	ГОСТ 8509-93	Уголок 100х7, L=2250	4	24,3	97,2
	ГОСТ 8509-93	Уголок 100х7, L=410	4	4,4	17,6
	ГОСТ 19903-2015	Лист 5х50, L=300	24	0,6	14,4
	ГОСТ 19903-2015	Лист 5х50, L=410	17	0,8	13,6
	ГОСТ 5915-70	Гайка М14-6Н5.016	18		
	ГОСТ6958-70	Шайба 14.01.016	18		
	ГОСТ 22042-76	Шпилька М14-6gx440.58.016	9		
		Анкер распорный М12	24		
		Проем Пр-10 1700х2650	4		
	ГОСТ 8509-93	Уголок 140х12, L=2200	2	56,4	112,8
	ГОСТ 8509-93	Уголок 100х7, L=2760	4	30	120,0
	ГОСТ 8509-93	Уголок 100х7, L=510	4	5,4	21,6
	ГОСТ 19903-2015	Лист 5х50, L=300	28	0,6	16,8
	ГОСТ 19903-2015	Лист 5х50, L=510	21	1	21,0
	ГОСТ 5915-70	Гайка М14-6Н5.016	22		
	ГОСТ6958-70	Шайба 14.01.016	22		
	ГОСТ 22042-76	Шпилька М14-6gx440.58.016	11		
		Анкер распорный М12	28		

						708/П-24-АНО-КР				
						Капитальный ремонт общеобразовательного учреждения ГБОУ "Школа №1210" по адресу: г. Москва, ул. Живописная, д.32				
Изм.	Кол.уч.	Лист	№ док.	Подп.	Дата	Конструктивные решения	Стадия	Лист	Листов	
Разработал	Торшин				04.26		Р	15.2		
ГАП	Фролова				04.26					
						Спецификации	 комплексное проектирование промышленных и гражданских объектов ООО "АРТИС"			
Н.Контроль	Лукашова				04.26					
ГИП	Зыкин				04.26					

Спецификация материалов на устройство усиления					
Поз.	Обозначение	Наименование	Кол.	Масса, ед. кг	Примечание
		Проем Пр-11 1220х2650	1		
	ГОСТ 8509-93	Уголок 140х12, L=1720	2	44.2	88.4
	ГОСТ 8509-93	Уголок 100х7, L=2760	4	30	120.0
	ГОСТ 8509-93	Уголок 100х7, L=510	4	5.4	21.6
	ГОСТ 19903-2015	Лист 5х50, L=300	28	0.6	16.8
	ГОСТ 19903-2015	Лист 5х50, L=510	21	1	21.0
	ГОСТ 5915-70	Гайка М14-6Н5.016	18		
	ГОСТ6958-70	Шайба 14.01.016	18		
	ГОСТ 22042-76	Шпилька М14-6gx440.58.016	9		
		Анкер распорный М12	28		
		Проем Пр-12 1700х2650	1		
	ГОСТ 8509-93	Уголок 140х12, L=2200	2	55.9	111.8
	ГОСТ 8509-93	Уголок 100х7, L=2760	4	30	120.0
	ГОСТ 8509-93	Уголок 100х7, L=510	4	5.4	21.6
	ГОСТ 19903-2015	Лист 5х50, L=300	28	0.6	16.8
	ГОСТ 19903-2015	Лист 5х50, L=510	21	1	21.0
	ГОСТ 5915-70	Гайка М14-6Н5.016	24		
	ГОСТ6958-70	Шайба 14.01.016	24		
	ГОСТ 22042-76	Шпилька М14-6gx440.58.016	12		
		Анкер распорный М12	28		
		Проем Пр-13 1900х2300	1		
	ГОСТ 8509-93	Уголок 140х12, L=2400	2	61.5	123.0
	ГОСТ 8509-93	Уголок 100х7, L=2410	4	26	104.0
	ГОСТ 8509-93	Уголок 100х7, L=510	4	5.4	21.6
	ГОСТ 19903-2015	Лист 5х50, L=300	24	0.6	14.4
	ГОСТ 19903-2015	Лист 5х50, L=510	21	1	21.0
	ГОСТ 5915-70	Гайка М14-6Н5.016	26		
	ГОСТ6958-70	Шайба 14.01.016	26		
	ГОСТ 22042-76	Шпилька М14-6gx440.58.016	13		
		Анкер распорный М12	24		

Спецификация материалов на устройство усиления					
Поз.	Обозначение	Наименование	Кол.	Масса, ед. кг	Примечание
		Проем Пр-14 1750х2200	1		
	ГОСТ 8509-93	Уголок 140х12, L=2250	2	57.7	115.4
	ГОСТ 8509-93	Уголок 100х7, L=2310	4	25	100.0
	ГОСТ 8509-93	Уголок 100х7, L=510	4	5.4	21.6
	ГОСТ 19903-2015	Лист 5х50, L=300	24	0.6	14.4
	ГОСТ 19903-2015	Лист 5х50, L=510	21	1	21.0
	ГОСТ 5915-70	Гайка М14-6Н5.016	22		
	ГОСТ6958-70	Шайба 14.01.016	22		
	ГОСТ 22042-76	Шпилька М14-6gx440.58.016	11		
		Анкер распорный М12	24		
		Проем Пр-15 1700х3220	2		
	ГОСТ 8509-93	Уголок 140х12, L=2200	2	56	112.0
	ГОСТ 8509-93	Уголок 100х7, L=3330	4	36	144.0
	ГОСТ 8509-93	Уголок 100х7, L=350	4	3.8	15.2
	ГОСТ 19903-2015	Лист 5х50, L=300	36	0.6	21.6
	ГОСТ 19903-2015	Лист 5х50, L=350	26	0.7	18.2
	ГОСТ 5915-70	Гайка М14-6Н5.016	22		
	ГОСТ6958-70	Шайба 14.01.016	22		
	ГОСТ 22042-76	Шпилька М14-6gx440.58.016	11		
		Анкер распорный М12	36		

						708/П-24-АНО-КР			
						Капитальный ремонт общеобразовательного учреждения ГБОУ "Школа №1210" по адресу: г. Москва, ул. Живописная, д.32			
Изм.	Кол.уч.	Лист	№ док.	Подп.	Дата	Конструктивные решения	Стадия	Лист	Листов
Разработал	ГАП	Торшин	Фралова		04.26		Р	15.3	
Н.Контроль	ГИП	Лукашова	Зыкин		04.26	Спецификации	 комплексное проектирование промышленных и гражданских объектов ООО "АРТИС"		

Спецификация материалов на устройство усиления					
Поз.	Обозначение	Наименование	Кол.	Масса, ед. кг	Примечание
		Проем Пр-16 3430х2300	1		
	ГОСТ 8509-93	Уголок 160х12, L=3930	2	115.4	230.8
	ГОСТ 8509-93	Уголок 100х7, L=2410	4	26	104.0
	ГОСТ 8509-93	Уголок 100х7, L=510	4	5.5	22.0
	ГОСТ 19903-2015	Лист 5х50, L=300	24	0.6	14.4
	ГОСТ 19903-2015	Лист 5х50, L=510	24	1	24.0
	ГОСТ 5915-70	Гайка М14-6Н5.016	34		
	ГОСТ6958-70	Шайба 14.01.016	34		
	ГОСТ 22042-76	Шпилька М14-6gx440.58.016	17		
		Анкер распорный М12	24		
		Проем Пр-17 1700х2200	3		
	ГОСТ 8509-93	Уголок 140х12, L=2200	2	56.4	112.8
	ГОСТ 8509-93	Уголок 100х7, L=2310	4	25	100.0
	ГОСТ 8509-93	Уголок 100х7, L=350	4	3.8	15.2
	ГОСТ 19903-2015	Лист 5х50, L=300	24	0.6	14.4
	ГОСТ 19903-2015	Лист 5х50, L=350	16	0.7	11.2
	ГОСТ 5915-70	Гайка М14-6Н5.016	14		
	ГОСТ6958-70	Шайба 14.01.016	14		
	ГОСТ 22042-76	Шпилька М14-6gx440.58.016	7		
		Анкер распорный М12	24		
		Проем Пр-18 1730х2200	1		
	ГОСТ 8509-93	Уголок 140х12, L=2230	2	57.2	114.4
	ГОСТ 8509-93	Уголок 100х7, L=2310	4	26.5	106.0
	ГОСТ 8509-93	Уголок 100х7, L=350	4	3.8	15.2
	ГОСТ 19903-2015	Лист 5х50, L=300	24	0.6	14.4
	ГОСТ 19903-2015	Лист 5х50, L=350	16	0.7	11.2
	ГОСТ 5915-70	Гайка М14-6Н5.016	18		
	ГОСТ6958-70	Шайба 14.01.016	18		
	ГОСТ 22042-76	Шпилька М14-6gx440.58.016	9		
		Анкер распорный М12	24		

Спецификация материалов на устройство усиления					
Поз.	Обозначение	Наименование	Кол.	Масса, ед. кг	Примечание
		Проем Пр-19 1520х2200	21		
	ГОСТ 8509-93	Уголок 140х12, L=2020	2	51.3	102.6
	ГОСТ 8509-93	Уголок 100х7, L=2310	4	26.5	106.0
	ГОСТ 8509-93	Уголок 100х7, L=350	4	3.8	15.2
	ГОСТ 19903-2015	Лист 5х50, L=300	24	0.6	14.4
	ГОСТ 19903-2015	Лист 5х50, L=350	16	0.7	11.2
	ГОСТ 5915-70	Гайка М14-6Н5.016	16		
	ГОСТ6958-70	Шайба 14.01.016	16		
	ГОСТ 22042-76	Шпилька М14-6gx440.58.016	8		
		Анкер распорный М12	24		
		Проем Пр-20 1020х2200	3		
	ГОСТ 8509-93	Уголок 140х12, L=1520	2	41.9	83.8
	ГОСТ 8509-93	Уголок 100х7, L=2310	4	26.5	106.0
	ГОСТ 8509-93	Уголок 100х7, L=350	4	3.8	15.2
	ГОСТ 19903-2015	Лист 5х50, L=300	24	0.6	14.4
	ГОСТ 19903-2015	Лист 5х50, L=350	16	0.7	11.2
	ГОСТ 5915-70	Гайка М14-6Н5.016	12		
	ГОСТ6958-70	Шайба 14.01.016	12		
	ГОСТ 22042-76	Шпилька М14-6gx440.58.016	6		
		Анкер распорный М12	24		

						708/П-24-АНО-КР				
						Капитальный ремонт общеобразовательного учреждения ГБОУ "Школа №1210" по адресу: г. Москва, ул. Живописная, д.32				
Изм.	Кол.уч.	Лист	№ док.	Подп.	Дата	Конструктивные решения	Стадия	Лист	Листов	
Разработал	Торшин				04.26		Р	15.4		
ГАП	Фролова				04.26					
						Спецификации	 комплексное проектирование промышленных и гражданских объектов ООО "АРТИС"			
Н.Контроль	Лукашова				04.26					
ГИП	Зыкин				04.26					

Спецификация материалов на устройство усиления					
Поз.	Обозначение	Наименование	Кол.	Масса, ед. кг	Примечание
		Проем Пр-21 1070х2200	2		
	ГОСТ 8509-93	Уголок 140х12, L=1570	2	40.3	80.6
	ГОСТ 8509-93	Уголок 100х7, L=2310	4	26.5	106.0
	ГОСТ 8509-93	Уголок 100х7, L=350	4	3.8	15.2
	ГОСТ 19903-2015	Лист 5х50, L=300	24	0.6	14.4
	ГОСТ 19903-2015	Лист 5х50, L=350	15	0.7	10.5
	ГОСТ 5915-70	Гайка М14-6Н.5.016	12		
	ГОСТ6958-70	Шайба 14.01.016	12		
	ГОСТ 22042-76	Шпилька М14-6gx440.58.016	6		
		Анкер распорный М12	24		
		Проем Пр-22 1230х2200	3		
	ГОСТ 8509-93	Уголок 140х12, L=1730	2	44.4	88.8
	ГОСТ 8509-93	Уголок 100х7, L=2310	4	26.5	106.0
	ГОСТ 8509-93	Уголок 100х7, L=350	4	3.8	15.2
	ГОСТ 19903-2015	Лист 5х50, L=300	24	0.6	14.4
	ГОСТ 19903-2015	Лист 5х50, L=350	16	0.7	11.2
	ГОСТ 5915-70	Гайка М14-6Н.5.016	14		
	ГОСТ6958-70	Шайба 14.01.016	14		
	ГОСТ 22042-76	Шпилька М14-6gx440.58.016	7		
		Анкер распорный М12	24		
		Проем Пр-23 1120х2200	7		
	ГОСТ 8509-93	Уголок 140х12, L=1620	2	41.9	83.8
	ГОСТ 8509-93	Уголок 100х7, L=2310	3	25	75.0
	ГОСТ 8509-93	Уголок 100х7, L=350	4	3.8	15.2
	ГОСТ 19903-2015	Лист 8х100, L=2310	1	14.5	14.5
	ГОСТ 19903-2015	Лист 5х50, L=300	20	0.6	12.0
	ГОСТ 19903-2015	Лист 5х50, L=350	14	0.7	9.8
	ГОСТ 5915-70	Гайка М14-6Н.5.016	14		
	ГОСТ6958-70	Шайба 14.01.016	14		
	ГОСТ 22042-76	Шпилька М14-6gx440.58.016	7		
		Анкер распорный М12	20		

Спецификация материалов на устройство усиления					
Поз.	Обозначение	Наименование	Кол.	Масса, ед. кг	Примечание
		Проем Пр-24 1710х3300	1		
	ГОСТ 8509-93	Уголок 140х12, L=2210	2	56.4	112.8
	ГОСТ 8509-93	Уголок 100х7, L=3410	4	36.9	147.6
	ГОСТ 8509-93	Уголок 100х7, L=510	4	5.5	22.0
	ГОСТ 19903-2015	Лист 5х50, L=300	36	0.6	21.6
	ГОСТ 19903-2015	Лист 5х50, L=510	26	1	26.0
	ГОСТ 5915-70	Гайка М14-6Н.5.016	20		
	ГОСТ6958-70	Шайба 14.01.016	20		
	ГОСТ 22042-76	Шпилька М14-6gx440.58.016	10		
		Анкер распорный М12	36		
		Проем Пр-25 980х2400	4		
	ГОСТ 8509-93	Уголок 140х12, L=1480	2	38	76.0
	ГОСТ 8509-93	Уголок 100х7, L=2510	4	27.2	108.8
	ГОСТ 8509-93	Уголок 100х7, L=510	4	5.5	22.0
	ГОСТ 19903-2015	Лист 5х50, L=300	28	0.6	16.8
	ГОСТ 19903-2015	Лист 5х50, L=510	17	1	17.0
	ГОСТ 5915-70	Гайка М14-6Н.5.016	14		
	ГОСТ6958-70	Шайба 14.01.016	14		
	ГОСТ 22042-76	Шпилька М14-6gx440.58.016	7		
		Анкер распорный М12	28		

						708/П-24-АНО-КР				
						Капитальный ремонт общеобразовательного учреждения ГБОУ "Школа №1210" по адресу: г. Москва, ул. Живописная, д.32				
Изм.	Кол.уч.	Лист	№ док.	Подп.	Дата	Конструктивные решения	Стадия	Лист	Листов	
Разработал	Торшин				04.26		Р	15.5		
ГАП	Фролова				04.26					
						Спецификации	 комплексное проектирование промышленных и гражданских объектов ООО "АРТИС"			
Н.Контроль	Лукашова				04.26					
ГИП	Зыкин				04.26					

Спецификация материалов на устройство усиления

Поз.	Обозначение	Наименование	Кол.	Масса, ед. кг	Примечание
		<u>Проем Пр-26 2000x2200</u>	1		
	ГОСТ 8509-93	Уголок 140x12, L=2500	2	64	128.0
	ГОСТ 8509-93	Уголок 100x7, L=2310	3	25	75.0
	ГОСТ 8509-93	Уголок 100x7, L=350	4	3,8	15.2
	ГОСТ 19903-2015	Лист 5x50, L=300	20	0,6	12.0
	ГОСТ 19903-2015	Лист 5x50, L=350	16	0.7	11.2
	ГОСТ 5915-70	Гайка М14-6Н5.016	24		
	ГОСТ 6958-70	Шайба 14.01.016	24		
	ГОСТ 22042-76	Шпилька М14-6gx440.58.016	12		
		Анкер распорный М12	20		
		<u>Проем Пр-27 1800x2200</u>	1		
	ГОСТ 8509-93	Уголок 140x12, L=2300	2	58.7	117.4
	ГОСТ 8509-93	Уголок 100x7, L=2310	3	25	75.0
	ГОСТ 8509-93	Уголок 100x7, L=350	4	3,8	15.2
	ГОСТ 19903-2015	Лист 5x50, L=300	20	0,6	12.0
	ГОСТ 19903-2015	Лист 5x50, L=350	15	0.7	10.5
	ГОСТ 5915-70	Гайка М14-6Н5.016	22		
	ГОСТ 6958-70	Шайба 14.01.016	22		
	ГОСТ 22042-76	Шпилька М14-6gx440.58.016	11		
		Анкер распорный М12	20		

Ведомость расхода стали, кг


Марка элемента	Изделия стандартные										
	Прокат марки									Всего	Всего (+5%)
	С255										
	ГОСТ 8240-89		ГОСТ 8509-93				ГОСТ 19903-2015				
	С22П	Итого	Л160х12	Л140х12	Л100х7	Итого	-8х100	-5х50	Итого		
	66.4	66.4	415.2	6461.8	8151.8	15028.8	159.2	2003.7	2162.9	17258.1	18121.01

						708/П-24-АНО-КР					
						Капитальный ремонт общеобразовательного учреждения ГБОУ "Школа №1210" по адресу: г. Москва, ул. Живописная, д.32					
Изм.	Кол.уч.	Лист	№ док.	Подп.	Дата	Конструктивные решения			Стадия	Лист	Листов
Разработал	Торшин				04.26				Р	15.6	
ГАП	Фролова				04.26						
						Спецификации			 комплексное проектирование промышленных и гражданских объектов ООО "АРТИС"		
Н.Контроль	Лукашова				04.26						
ГИП	Зыкин				04.26						


Схемы усиления проемов для прохождения вентиляции

Спецификация материалов на обрание отверстий для прохождения коммуникаций

Поз.	Обозначение	Наименование	Кол.	Масса ед, кг	Примечание общ. вес кг
	ГОСТ 8509-93	Л 75х6, п.м.	58,4	6,89	402,38
	ГОСТ 19903-2015	-5х50, п.м.	14,4	2	28,8

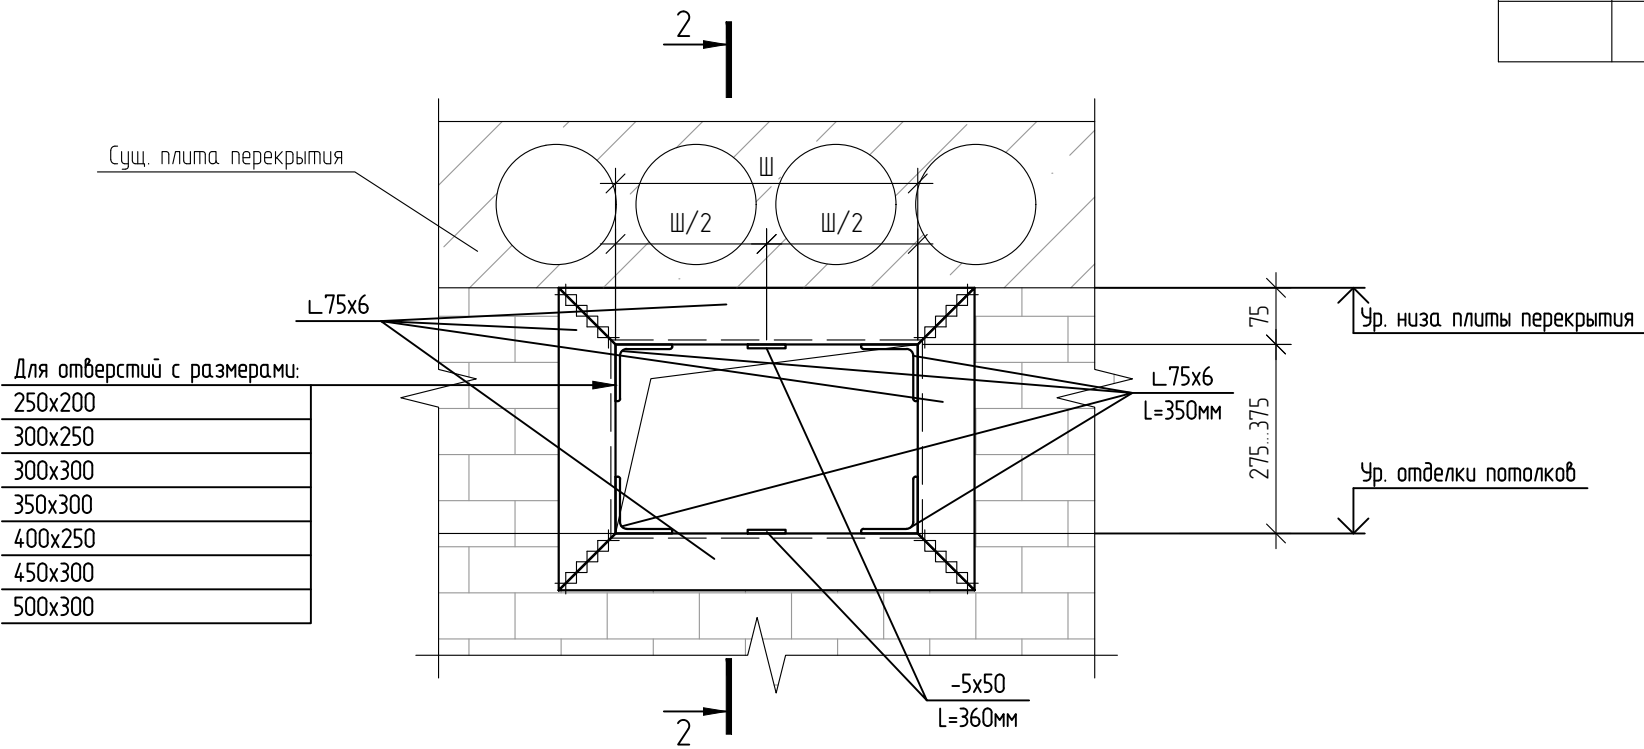

Для отверстий с размерами:
250х200
300х250
300х300
350х300
400х250
450х300
500х300

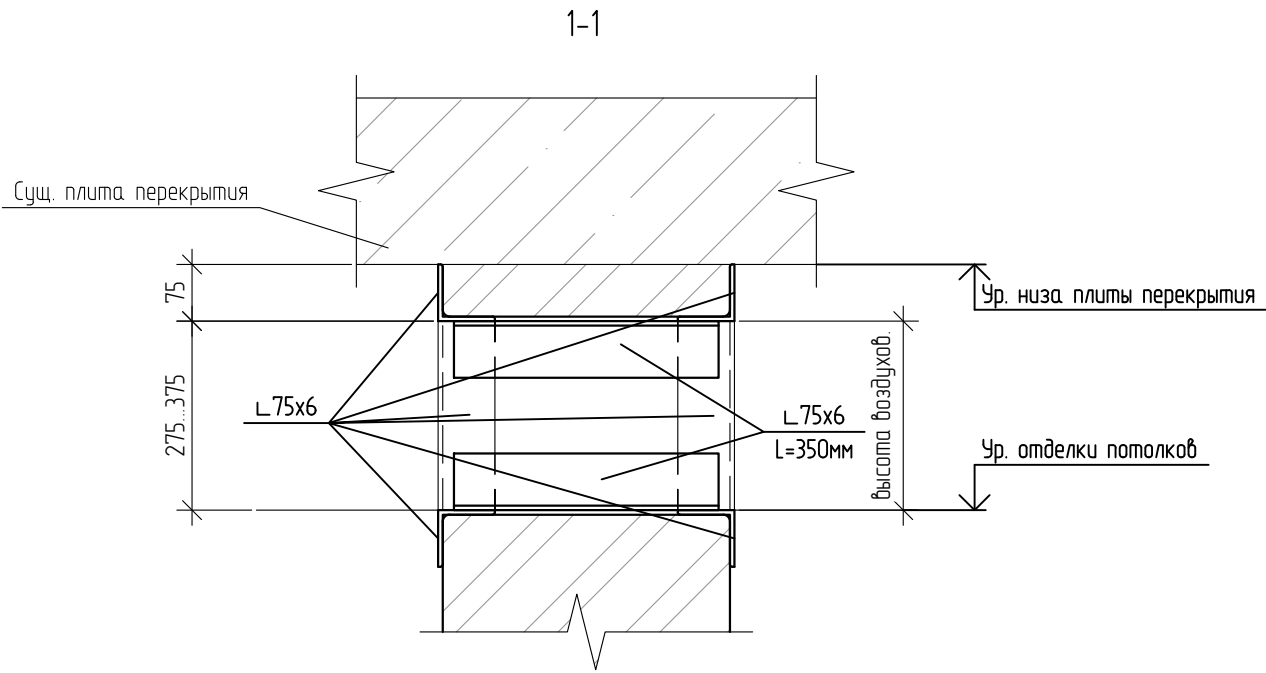

Примечание:
1. Материал для металлических конструкций - сталь С245 по ГОСТ 27772-2021;
2. Сварные соединения - по ГОСТ 5264-80. Электродом Э-42 по ГОСТ 9467-75*;
3. Минимальный катет сварного шва - по наименьшей толщине свариваемых элементов;
4. Все конструкции окрасить одним слоем эмали ПФ-115 ГОСТ 6465-76 по двум слоям грунта ГФ-021 ГОСТ 25129-82.



Согласовано				
Взам. инв. №				
Подп. и дата				
Инв. № подл.				

						708/П-24-АНО-КР			
						Капитальный ремонт общеобразовательного учреждения ГБОУ "Школа №1210" по адресу: г. Москва, ул. Живописная, д.32			
Изм.	Кол.уч.	Лист	№ док.	Подп.	Дата	Конструктивные решения	Стадия	Лист	Листов
Разработал		Торшин			04.26		Р	16	
ГАП		Фролова			04.26				
						Схемы усиления проемов для прохождения вентиляции		комплексное проектирование промышленных и гражданских объектов	
Н.Контроль		Лукашова			04.26			000 "АРТИС"	
ГИП		Зыкин			04.26				

Схемы усиления проемов для прохождения вентиляции

Спецификация материалов на обработку отверстий для прохождения коммуникаций

Поз.	Обозначение	Наименование	Кол.	Масса ед, кг	Примечание общ. вес кг
	ГОСТ 8240-89	№12, п.м.	78,8	10,4	819,52
	ГОСТ 8509-93	Л75х6, п.м.	91,4	6,89	629,746
	ГОСТ 19903-2015	-5х50, п.м.	32,24	2	64,48
	ГОСТ 22042-76	Шпилька М14-4gx420.58.016, шт	145		
	ГОСТ 6958-70	Шайба 14.01.016, шт	290		
	ГОСТ 5915-70	Гайка М14-6Н.5.016, шт	290		

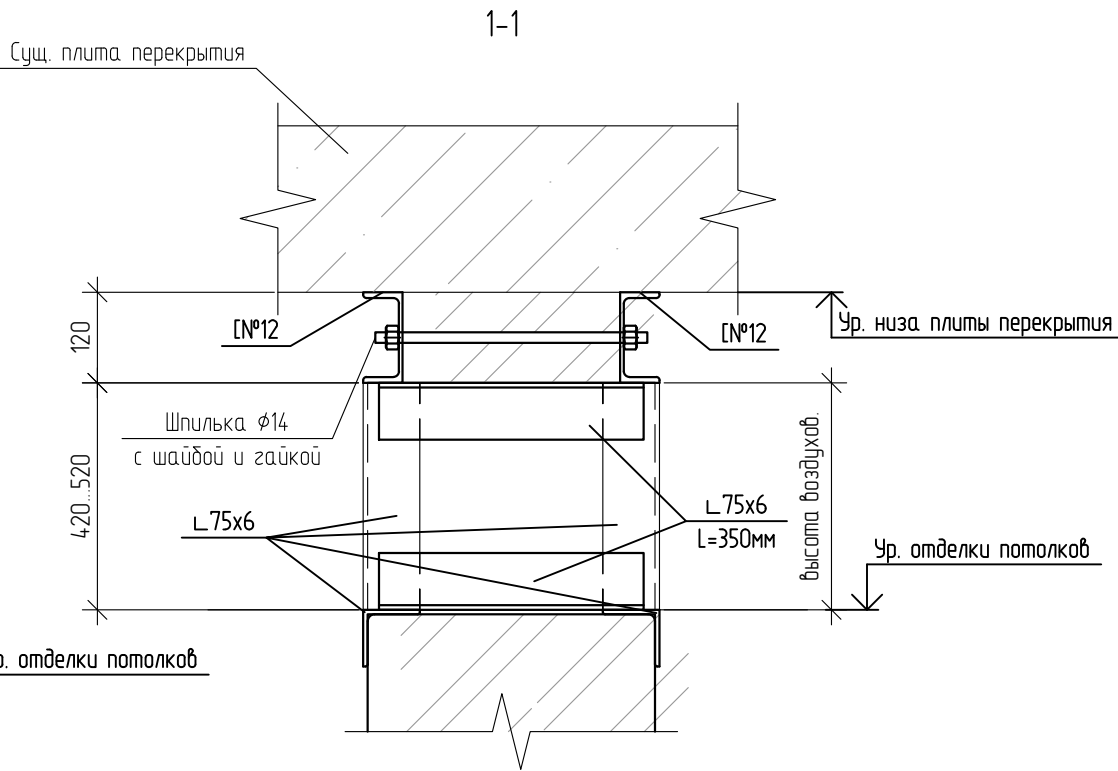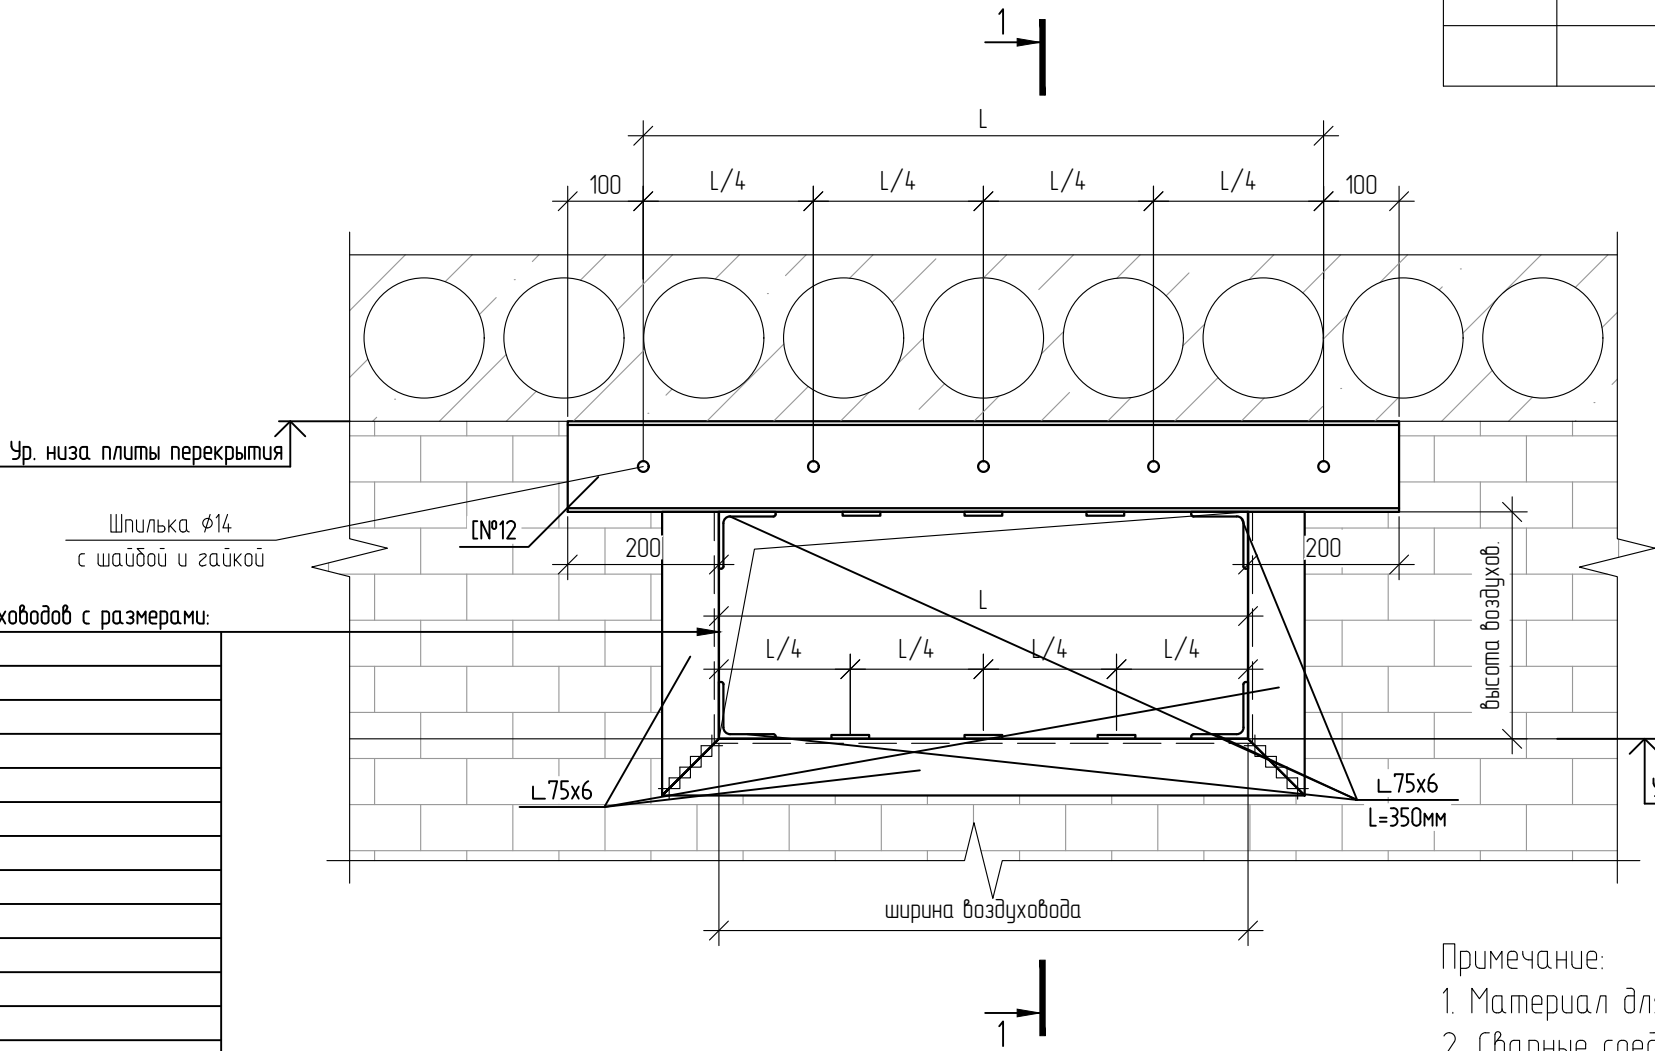

Примечание:
1. Материал для металлических конструкций - сталь С245 по ГОСТ 27772-2021;
2. Сварные соединения - по ГОСТ 5264-80. Электродом Э-42 по ГОСТ 9467-75*;
3. Минимальный катет сварного шва - по наименьшей толщине свариваемых элементов;
4. Все конструкции окрасить одним слоем эмали ПФ-115 ГОСТ 6465-76 по двум слоям грунта ГФ-021 ГОСТ 25129-82.



Согласовано		
Взам. инв. №	Для воздуховодов с размерами:	
	550х350	
	600х300	
	700х300	
	720х250	
	750х300	
	785х500	
	800х400	
	815х400	
	900х300	
Подп. и дата	900х400	
	1000х500	
	1300х400	
	1355х700	
	1500х400	
	1560х450	
	1580х450	
	1610х400	
	1670х550	
	1690х400	
Инв. № подл.	1700х750	

						708/П-24-АНО-КР		
						Капитальный ремонт общеобразовательного учреждения ГБОУ "Школа №1210" по адресу: г. Москва, ул. Живописная, д.32		
Изм.	Кол.уч.	Лист	№ док.	Подп.	Дата	Конструктивные решения	Стадия	Лист
Разработал	Торшин				04.26		Р	17
ГАП	Фророва				04.26	Схемы усиления проемов для прохождения вентиляции		ООО "АРТИС"
Н.Контроль	Лукашова				04.26			
ГИП	Зыкин				04.26			

Схемы усиления проемов для прохождения вентиляции

Спецификация материалов на обращение отверстий для прохождения коммуникаций


Поз.	Обозначение	Наименование	Кол.	Масса ед, кг	Примечание общ. вес кг
	ГОСТ 8240-89	№12, п.м.	9,2	10,4	95,68
	ГОСТ 8509-93	Л 75х6, п.м.	31,4	6,89	216,346
	ГОСТ 19903-2015	-5х50, п.м.	9,58	2	19,16
	ГОСТ 22042-76	Шпилька М14-4gx420.58.016, шт	24		
	ГОСТ 6958-70	Шайба 14.01.016, шт	48		
	ГОСТ 5915-70	Гайка М14-6Н.5.016, шт	48		

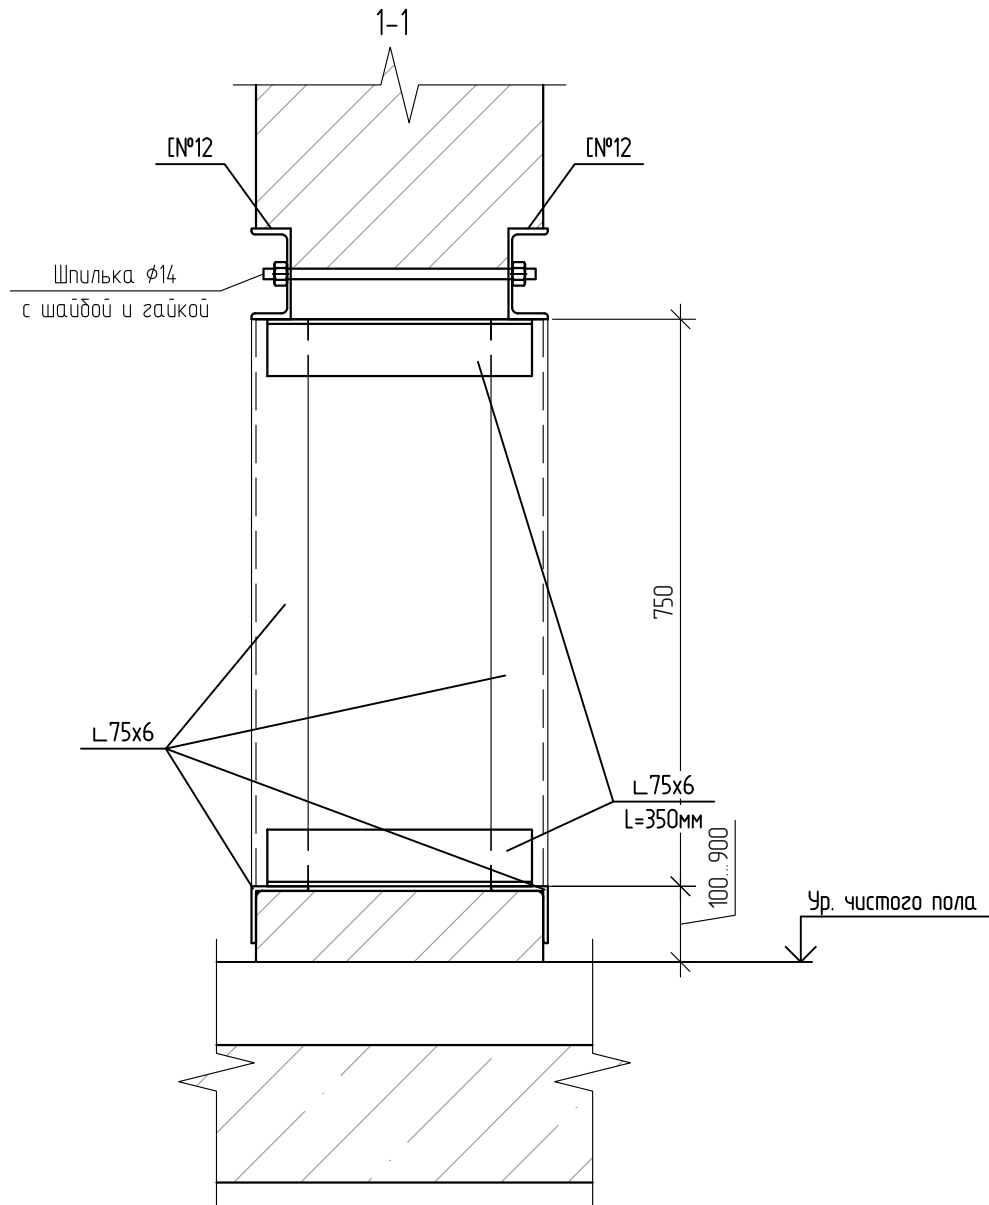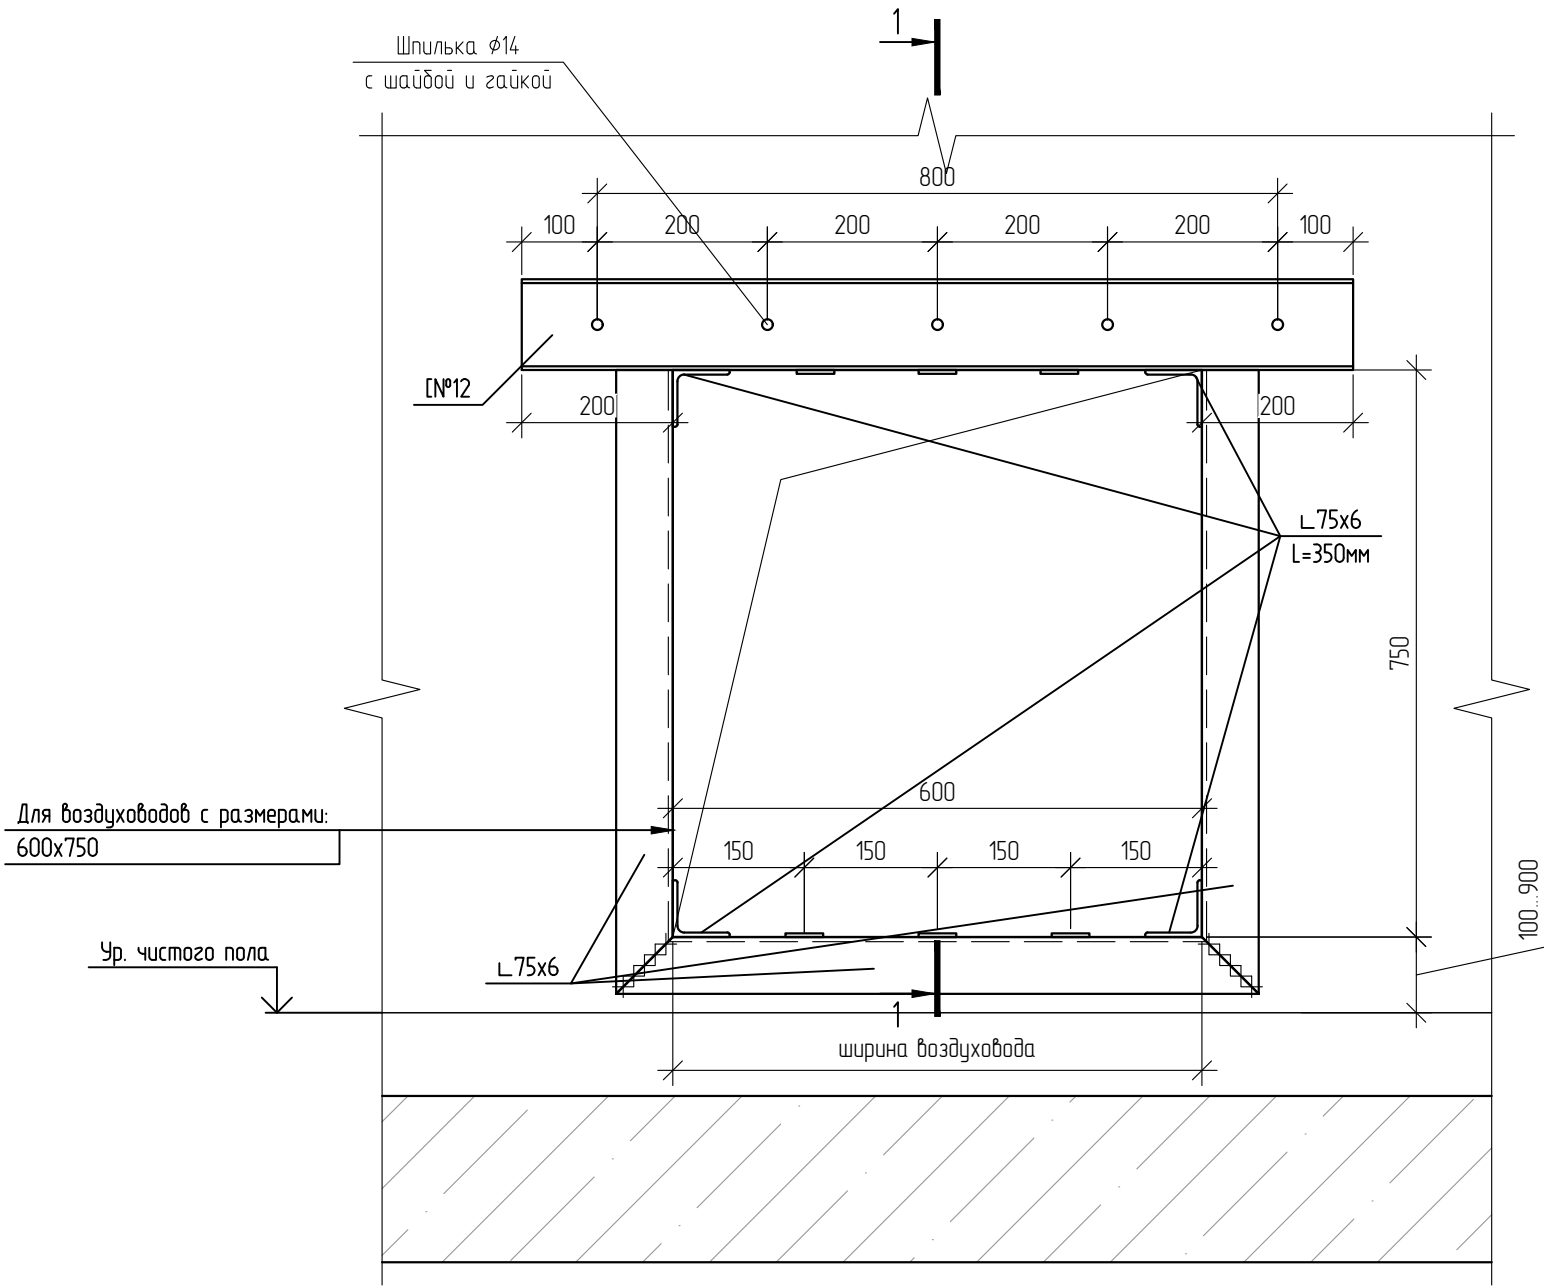


Примечание:
1. Материал для металлических конструкций - сталь С245 по ГОСТ 27772-2021;
2. Сварные соединения - по ГОСТ 5264-80. Электродом Э-42 по ГОСТ 9467-75*;
3. Минимальный катет сварного шва - по наименьшей толщине свариваемых элементов;
4. Все конструкции окрасить одним слоем эмали ПФ-115 ГОСТ 6465-76 по двум слоям грунта ГФ-021 ГОСТ 25129-82.

						708/П-24-АНО-КР			
						Капитальный ремонт общеобразовательного учреждения ГБОУ "Школа №1210" по адресу: г. Москва, ул. Живописная, д.32			
Изм.	Кол.уч.	Лист	№ док.	Подп.	Дата	Конструктивные решения	Стадия	Лист	Листов
Разработал		Торшин			04.26		Р	18	
ГАП		Фролова			04.26				
						Схемы усиления проемов для прохождения вентиляции		комплексное проектирование промышленных и гражданских объектов	
Н.Контроль		Лукашова			04.26			ООО "АРТИС"	
ГИП		Зыкин			04.26				

Согласовано				
		Взам. инв. №		
		Подп. и дата		
Инв. № подл.				

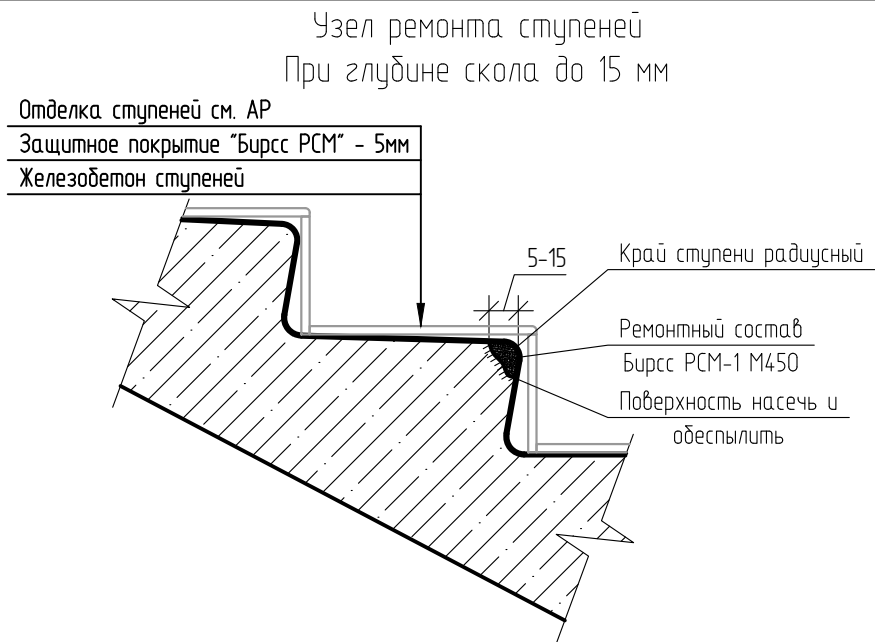

Узел ремонта плит перекрытий в местах прохождения коммуникаций

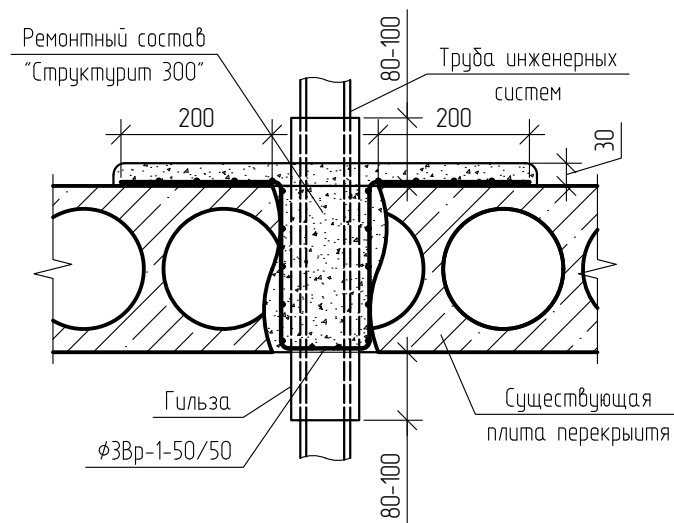

Узел заделки стыков сопряжений плит перекрытий и покрытий


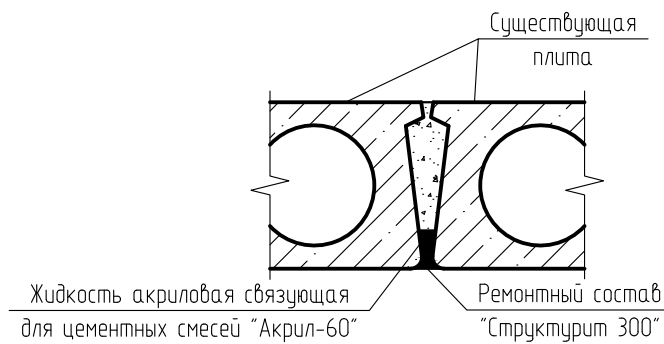


Схема заделки трещин в плитах перекрытия

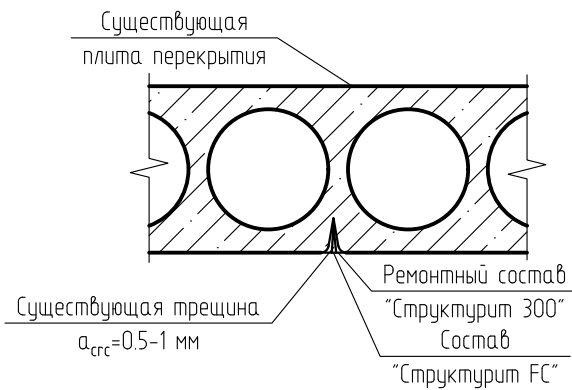

Спецификация материалов на ремонт ступеней лестниц

Поз.	Обозначение	Наименование	Кол.	Масса ед, кг	Примечание общ. вес кг
		Материалы			
		Ремонтный состав Бирсс РСМ-1 М450, м ²	16,2	19	307,8
		Защитное покрытие Бирсс РСМ, м ²	25,7	9	231,3

Спецификация материалов на ремонт плит перекрытий в местах прохождения коммуникаций

Поз.	Обозначение	Наименование	Кол.	Масса ед, кг	Примечание общ. вес кг
		Материалы			
	ГОСТ Р 52544-2006	Сетка $\phi 38p1-50/50$, м ²	2,1	2,3	4,83
		Структурит 300, м ³	0,15	1920	288

Спецификация материалов на заделку стыков сопряжений плит перекрытий и покрытий








Поз.	Обозначение	Наименование	Кол.	Масса ед, кг	Примечание общ. вес кг
		Расчистка ремонтируемых стыков, м.п.	25		
		Материалы			
		Грунтовочный состав Акрил 60, м ²	3	0,3	0,9
		Структурит 300, м ³	0,03	1920	96

Спецификация материалов на заделку трещин в плитах

Поз.	Обозначение	Наименование	Кол.	Масса ед, кг	Примечание общ. вес кг
		Расшивка трещин, м	6,6		
		Материалы			
		Структурит 300 (1920 кг/м ³), м ³	0,001	1920	1,92
		Структурит FC, м ²	0,06	0,3	0,02
		Грунтовочный состав Акрил 60, м ²	0,06	0,8	0,05

						708/П-24-АНО-КР			
						Капитальный ремонт общеобразовательного учреждения ГБОУ "Школа №1210" по адресу: г. Москва, ул. Живописная, д.32			
Изм.	Кол.уч.	Лист	№ док.	Подп.	Дата	Конструктивные решения	Стадия	Лист	Листов
Разработал	Торшин				04.26		Р	19	
ГАП	Фролова				04.26				
Н.Контроль	Лукашова				04.26	Узлы ремонта ступеней, плит перекрытий и покрытий		комплексное проектирование промышленных и гражданских объектов ООО "АРТИС"	
ГИП	Зыкин				04.26				

Схема устройства входа в осях "25/П"

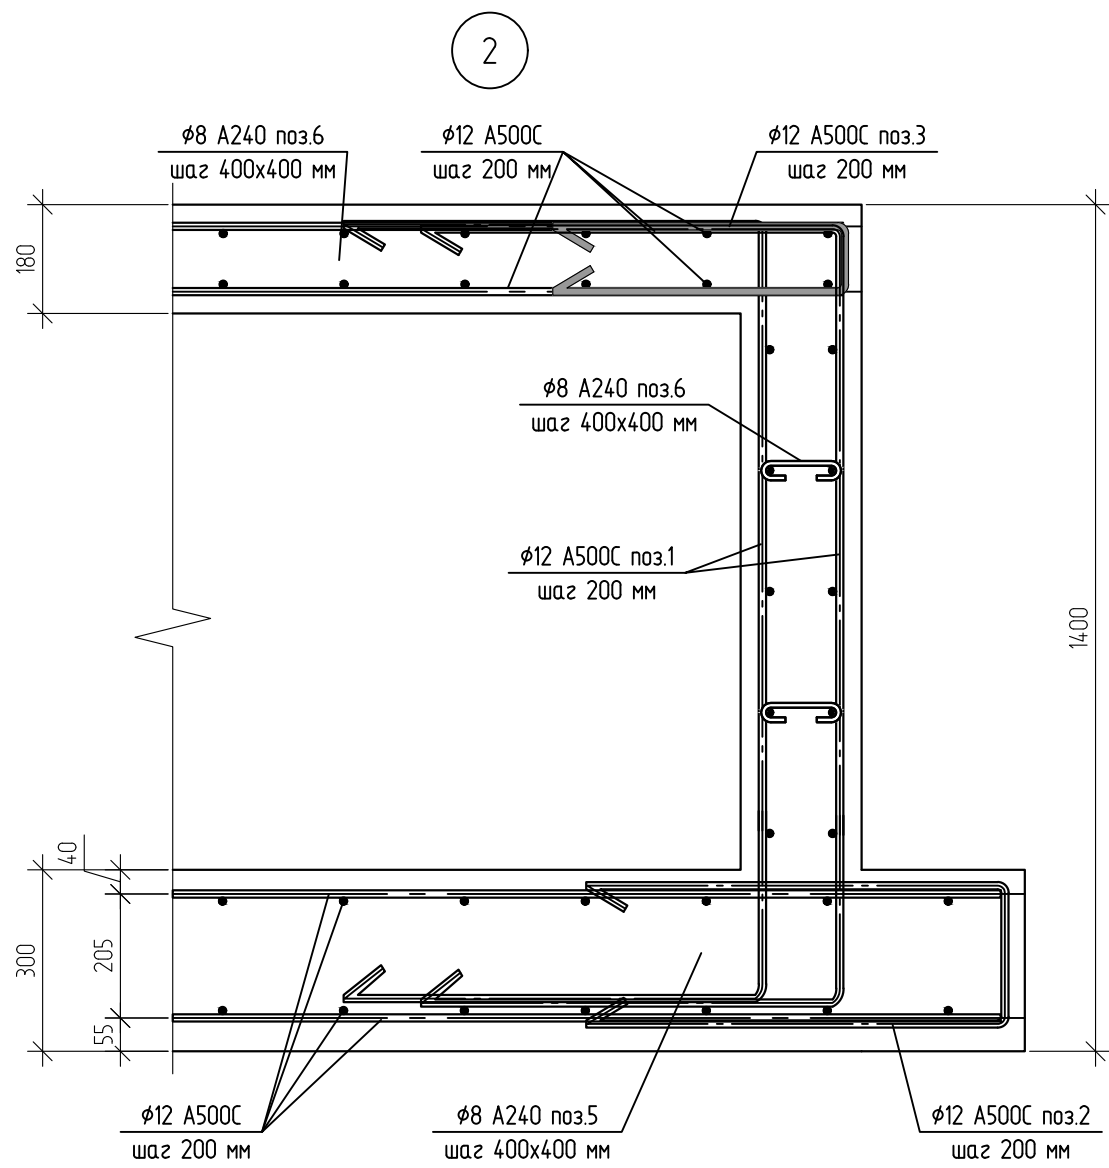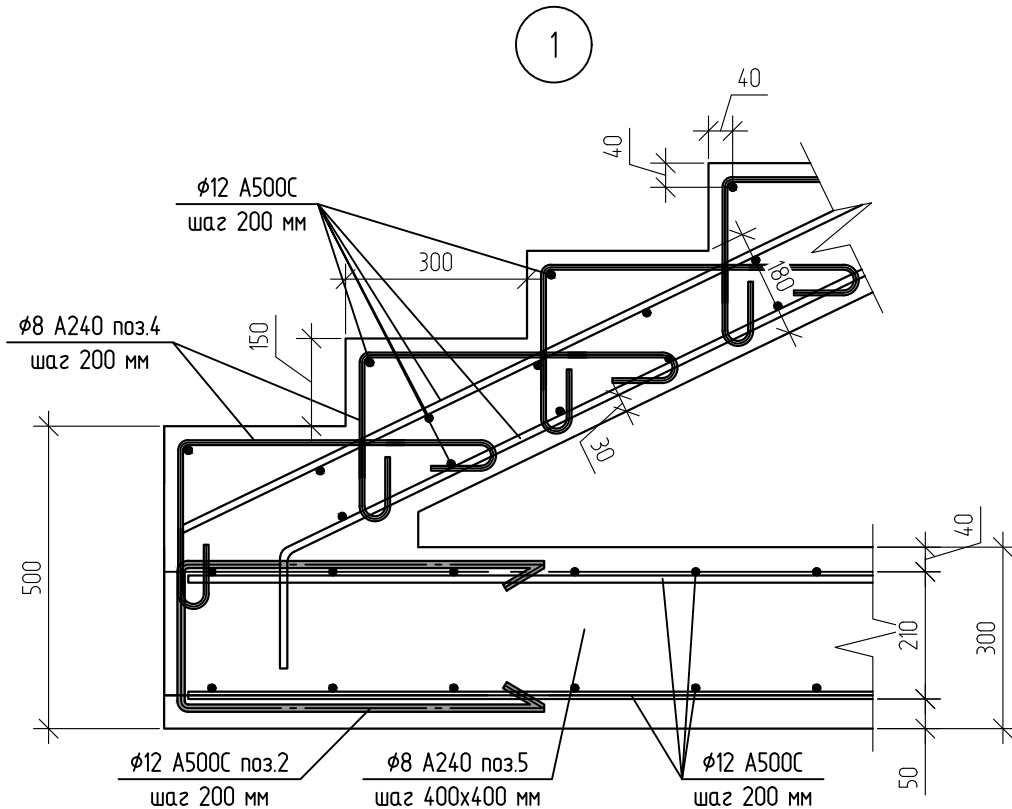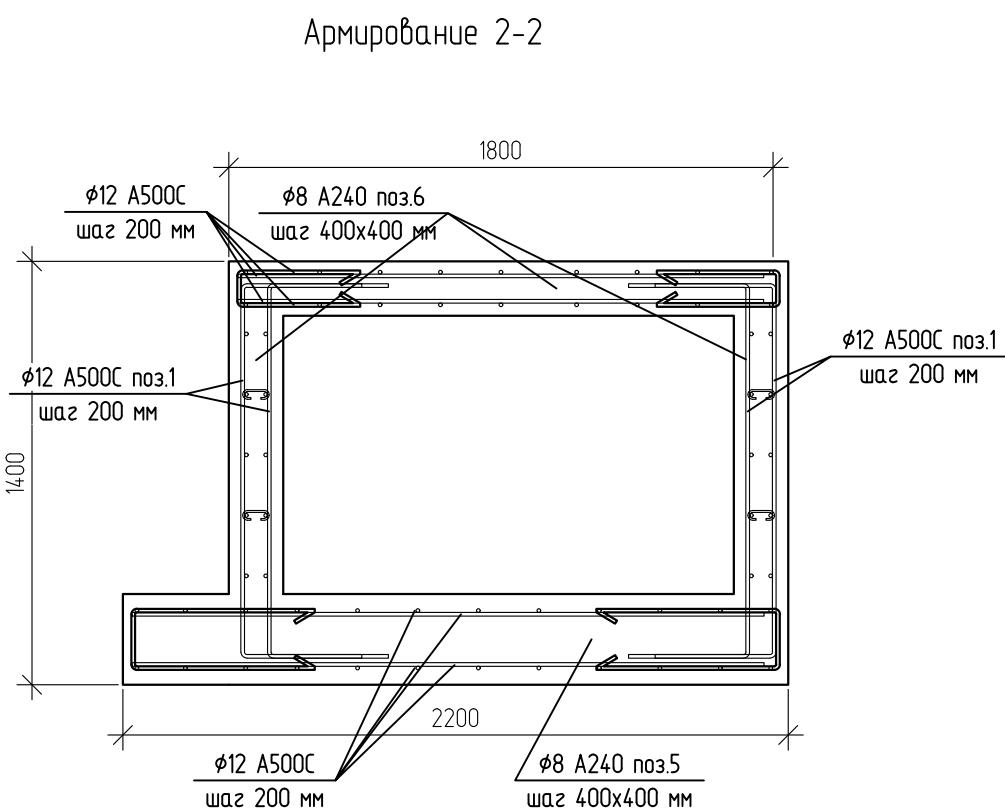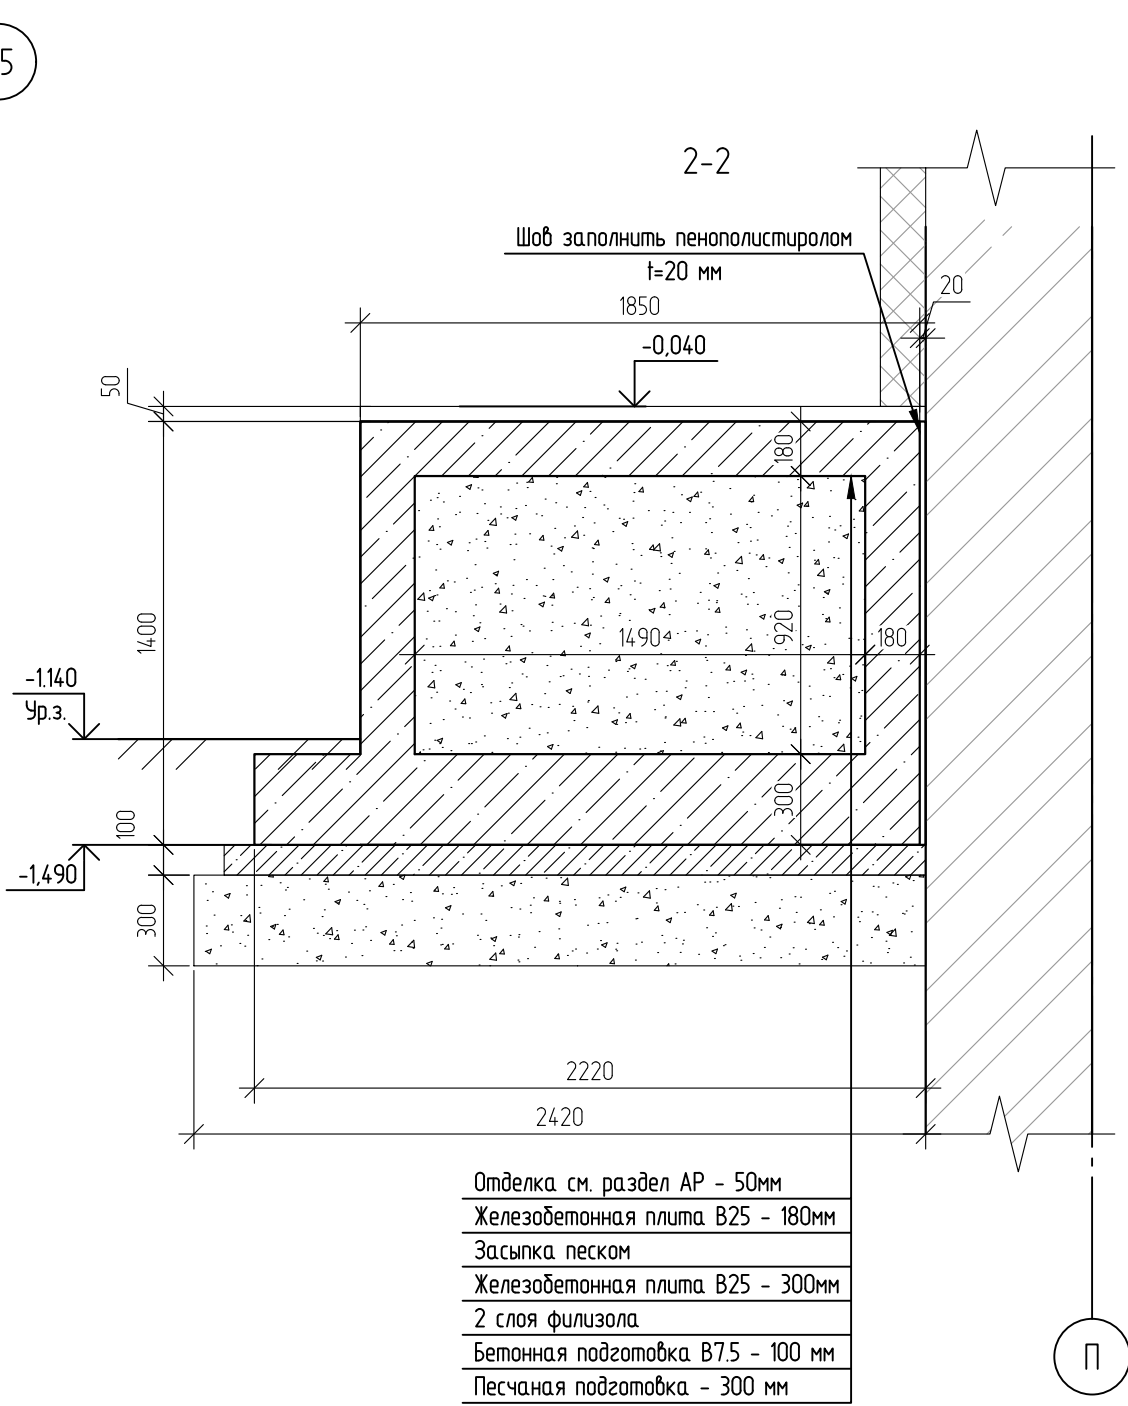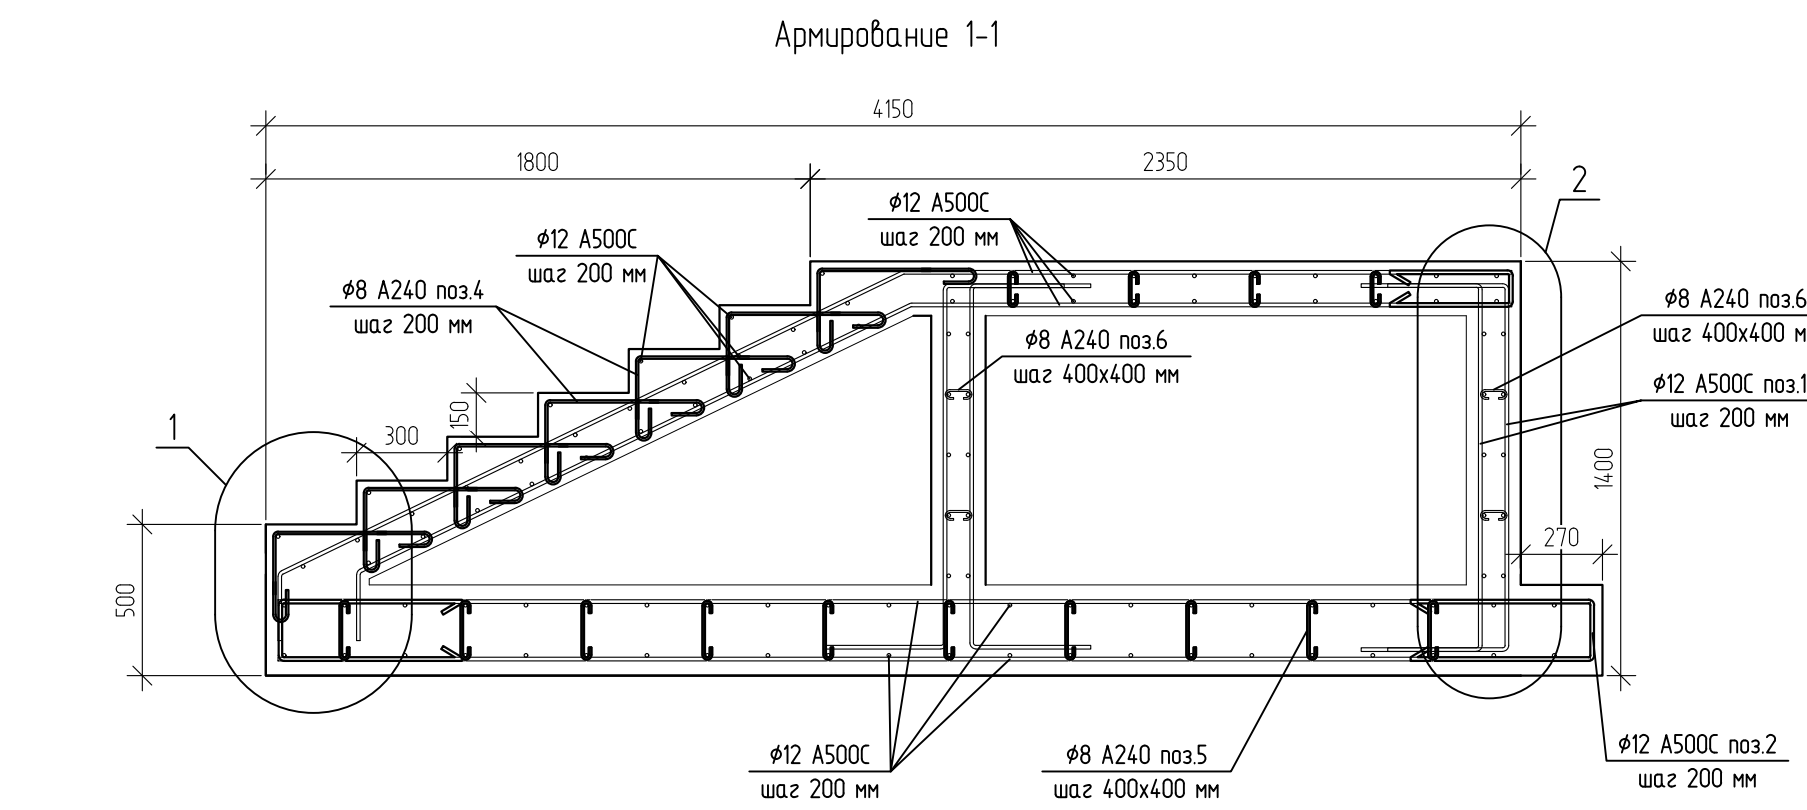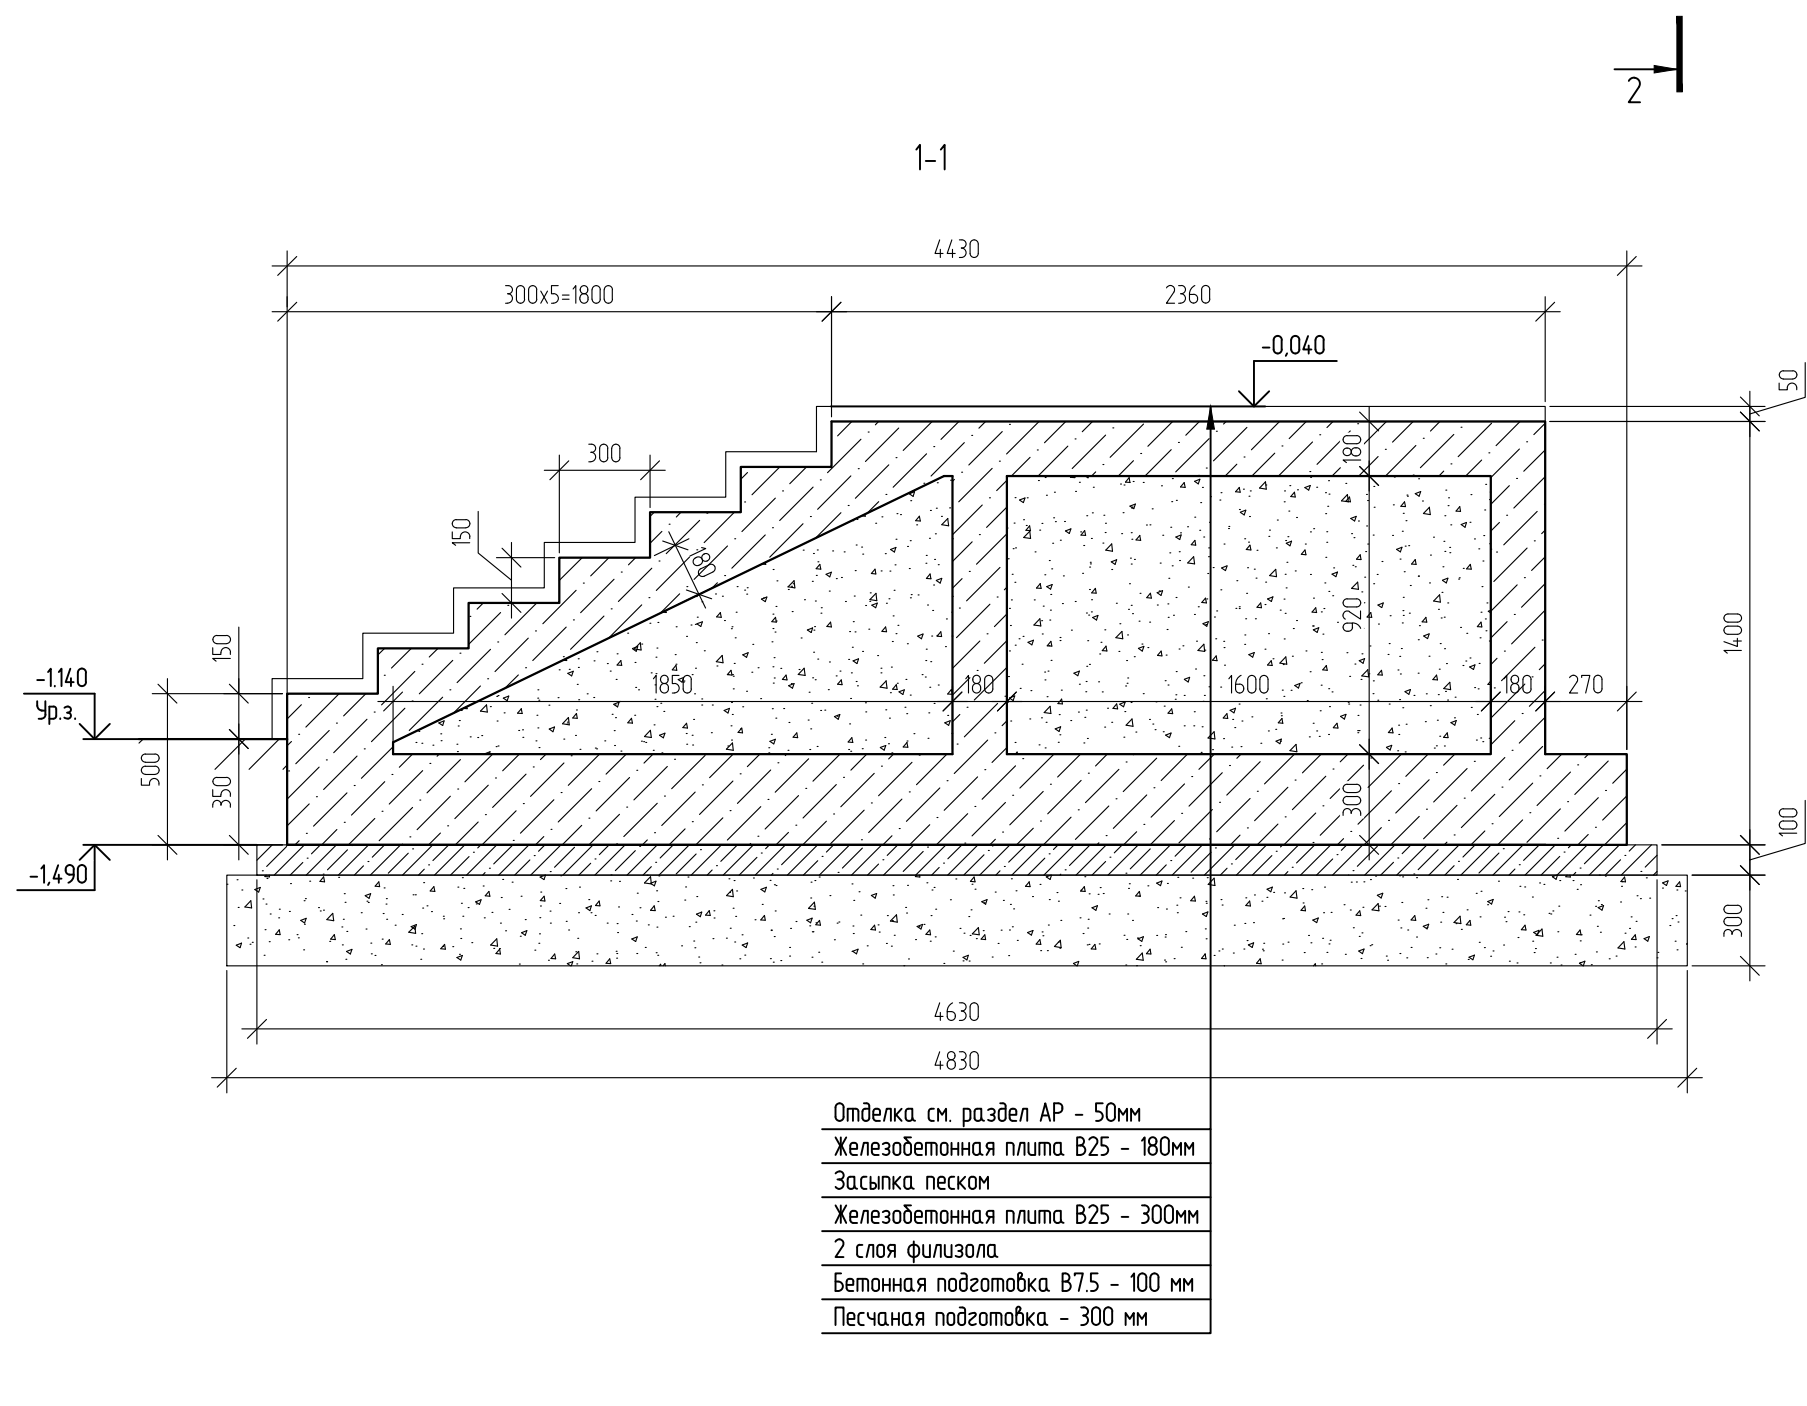
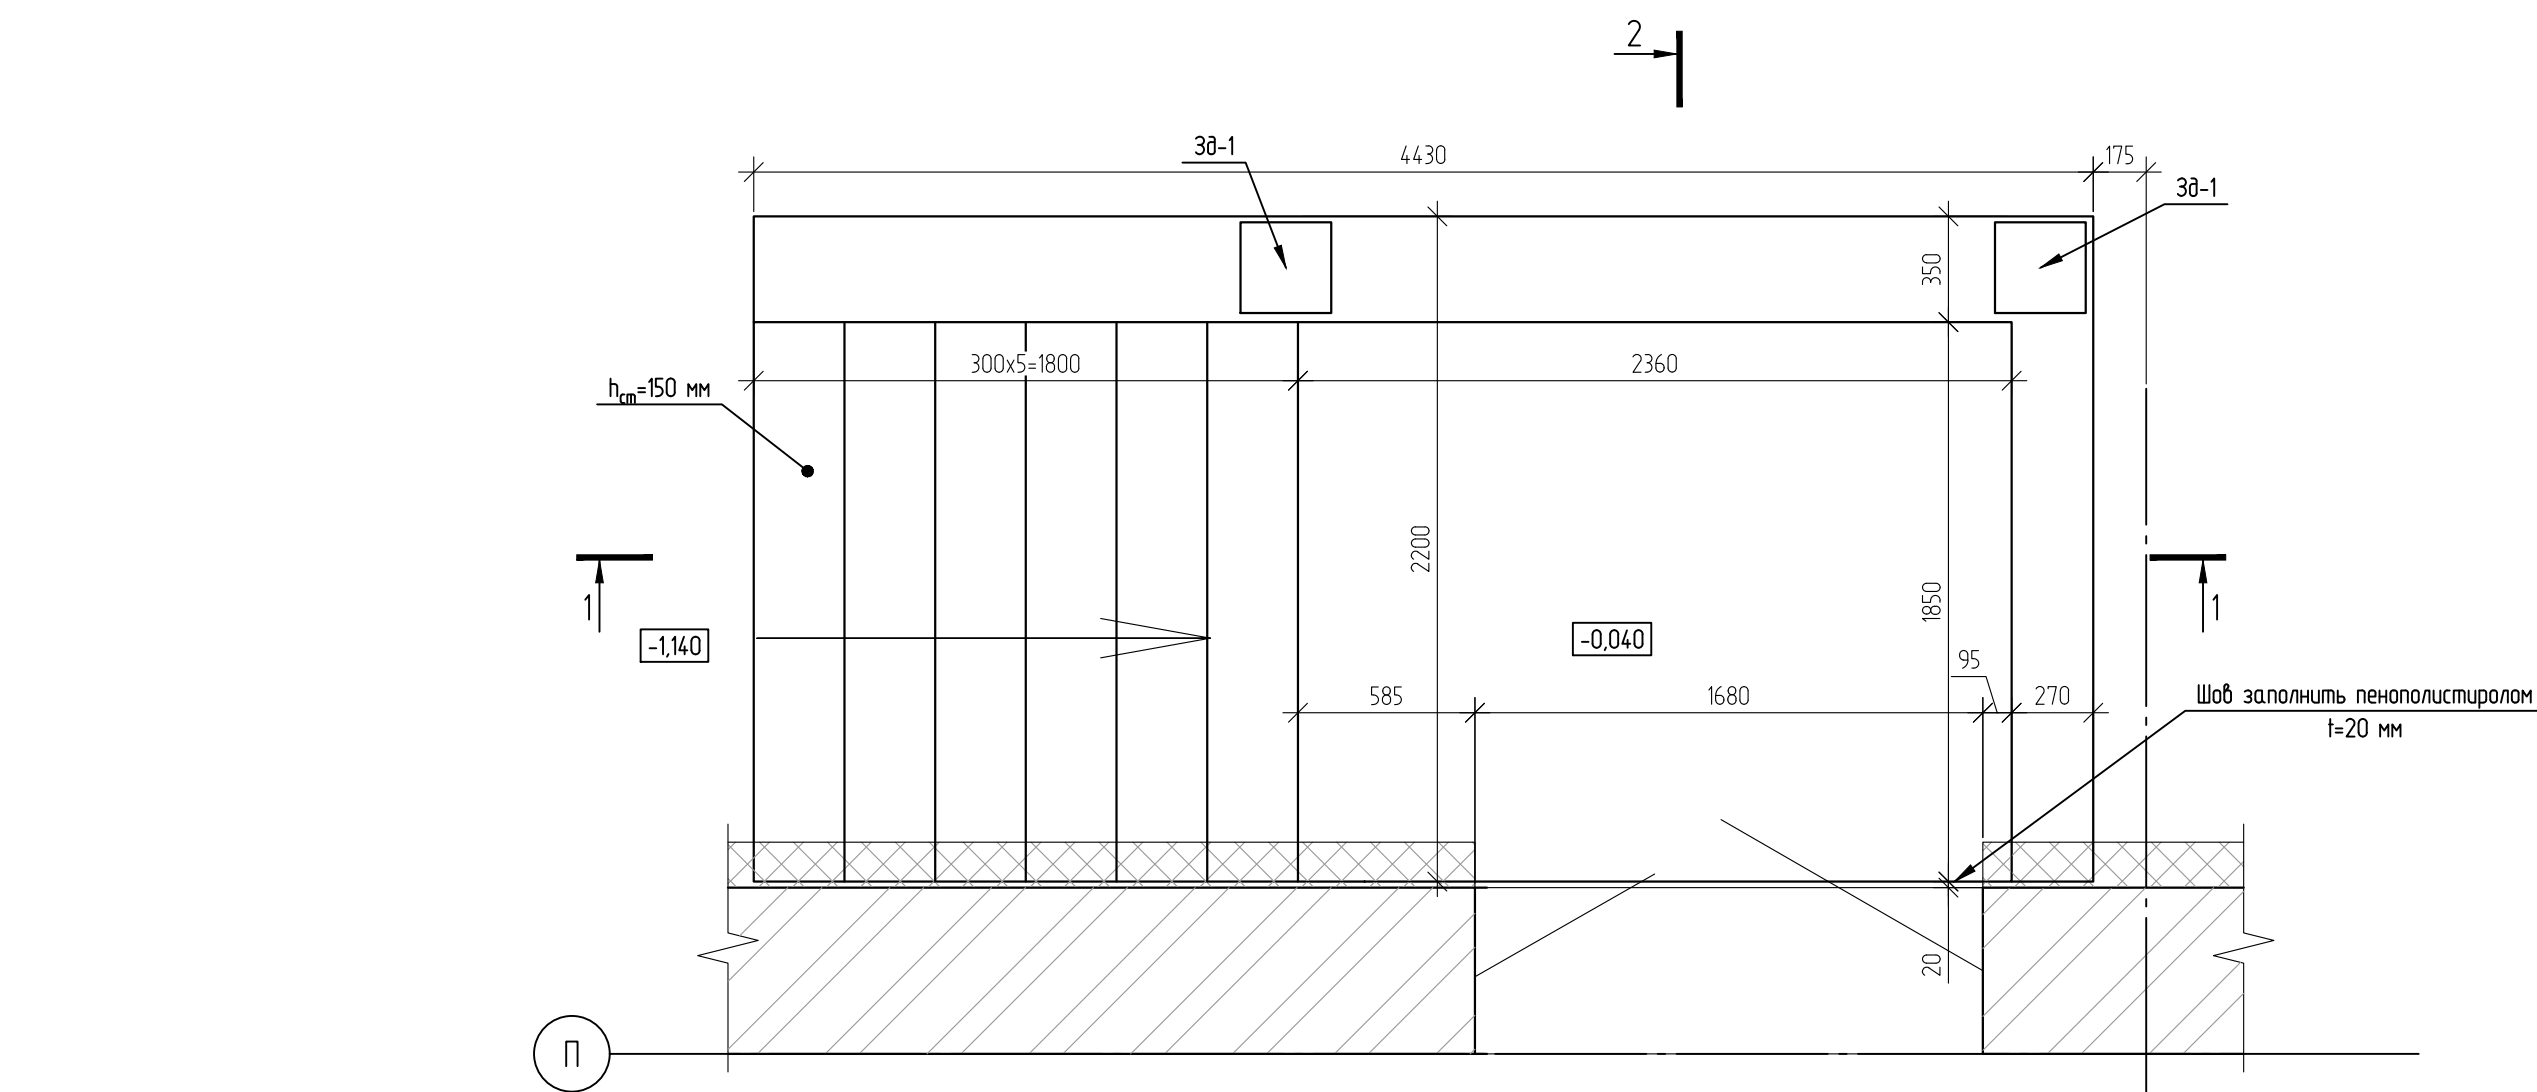


Ведомость деталей	
Поз.	Эскиз
1	
2	
3	
4	
5	
6	

Спецификация на устройство входа в осях "4-6/П"					
Поз.	Обозначение	Наименование	Кол.	Масса 1 дет., кг	Примеч. общ. вес кг
		Конструкции выше Ур.з.			
	ГОСТ 34028-2016	#12 A500C, п.м	216	0.888	191.81
1	ГОСТ 34028-2016	#12 A500C, L=1995 мм, шт	76	1.78	135.28
3	ГОСТ 34028-2016	#12 A500C, L=920 мм, шт	36	0.81	29.16
4	ГОСТ 34028-2016	#8 A240, L=860 мм, шт	56	0.36	20.16
6	ГОСТ 34028-2016	#8 A240, L=200 мм, шт	65	0.08	5.2
		Фундаментная плита			
	ГОСТ 34028-2016	#12 A500C, п.м	156	0.888	138.53
2	ГОСТ 34028-2016	#12 A500C, L=1390 мм, шт	58	1.23	71.34
5	ГОСТ 34028-2016	#8 A240, L=300 мм, шт	45	0.12	5.4
		30-1	2		
	ГОСТ 34028-2016	#12 A500C, L=250 мм, шт	4	0.222	0.89
	ГОСТ 19903-2015	-300x300x10 мм, шт	1	7.06	7.06
		Материалы			
		Бетон В25, W6, F150, м³	6.7		
		Бетон В7,5, м³	0.86		
		Песок средней крупности, м³	6.3		
		Гидроизоляция, м²	10		
		Пенополистирол l=20 мм, м²	5.15		

Ведомость расхода стали, кг


Марка элемента	Изделия арматурные			
	Арматура класса		Всего	
	A500C	A240		
	ГОСТ 34028-2016	ГОСТ 34028-2016		
	#12	Итого	#8	Итого
	567.9	567.9	30.76	30.76
			598.66	

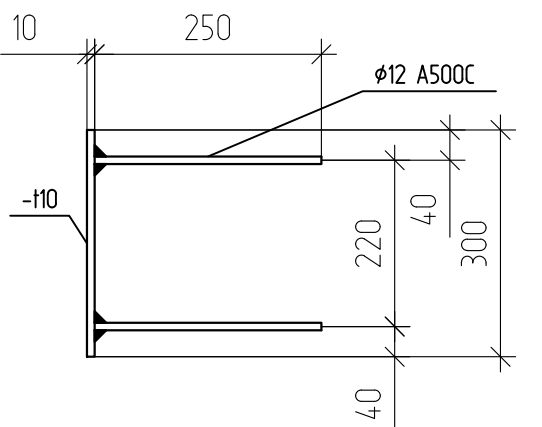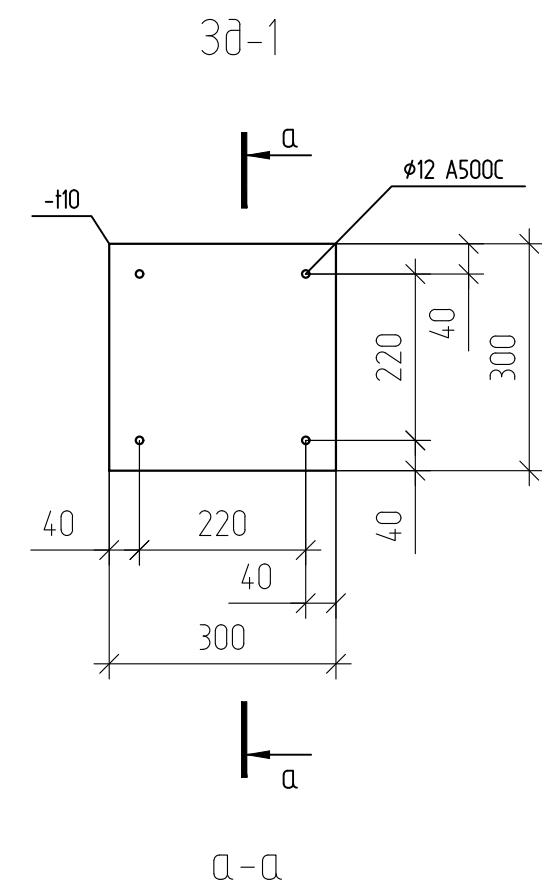


1. Фундаментную плиту, плиту площадки армировать отдельными стержнями #12 A500C с шагом 200x200 мм. Вся рабочая арматура соединяется в сетки с помощью вязальной проволоки. В сетках вязке подлежат пересечения стержней через одно в шахматном порядке.
2. Соединение стержней по длине производить внахлест с перелупом не менее 45 диаметров стыкуемой арматуры. В одном условном сечении не более 50% стыкуемой арматуры.
3. Размеры хомутов и гнутых деталей даны для справки. Данные размеры следует уточнять и корректировать по месту для соответствия нижней и верхней сеток проектному.
4. Стыки смежных стержней размещать в шахматном порядке.
5. Фиксаторы положения сеток (лягушки) на чертеже не показаны и в спецификации не учтены.

						708/П-24-АНО-КР					
						Капитальный ремонт общеобразовательного учреждения ГБОУ "Школа №120" по адресу г. Москва, ул. Животновская, д.32					
Изм.	Копия	Лист	№ док	Подп.	Дата	Конструктивные решения			Стация	Лист	Листов
Разработал	Горшин				04.26				Р	20	
ГАП	Фролова				04.26	Схема устройства входа в осях "25/П"			 ООО "АРТИС"		
Н.Контроль	Лукашова				04.26						
ГИП	Зыкин				04.26						



Схема устройства входа в осях "13-14/П"

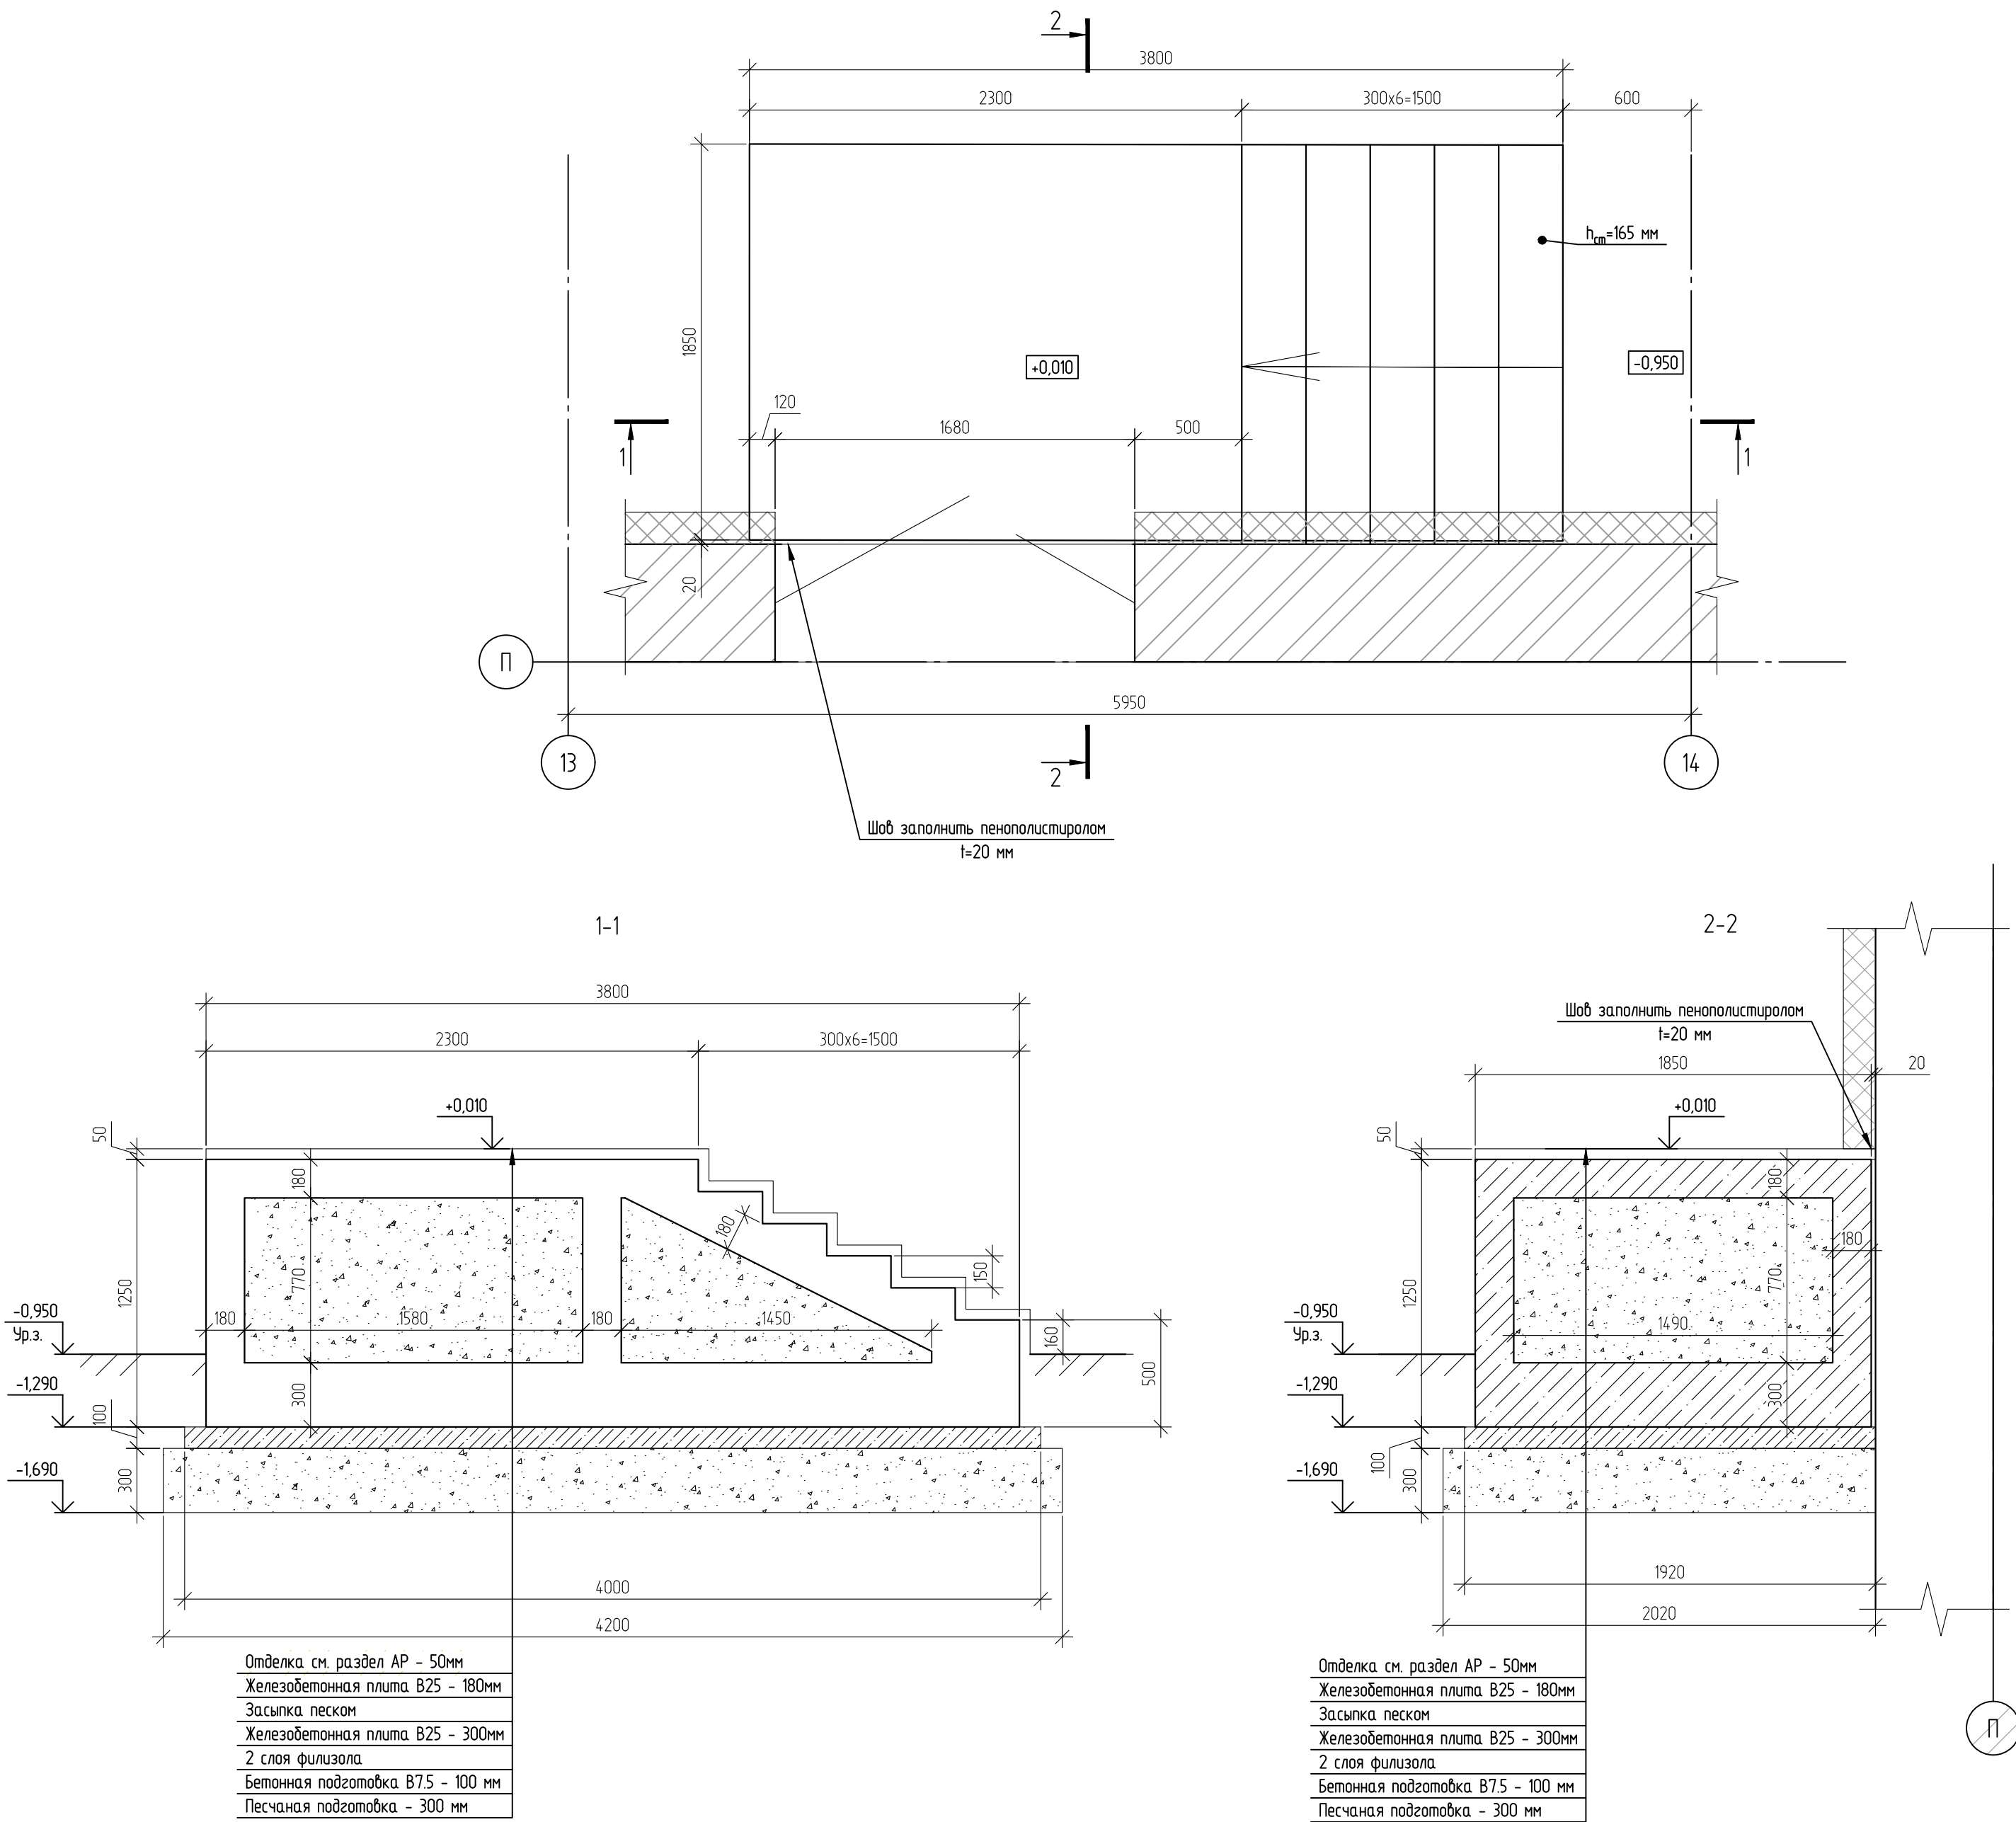

Армирование 1-1

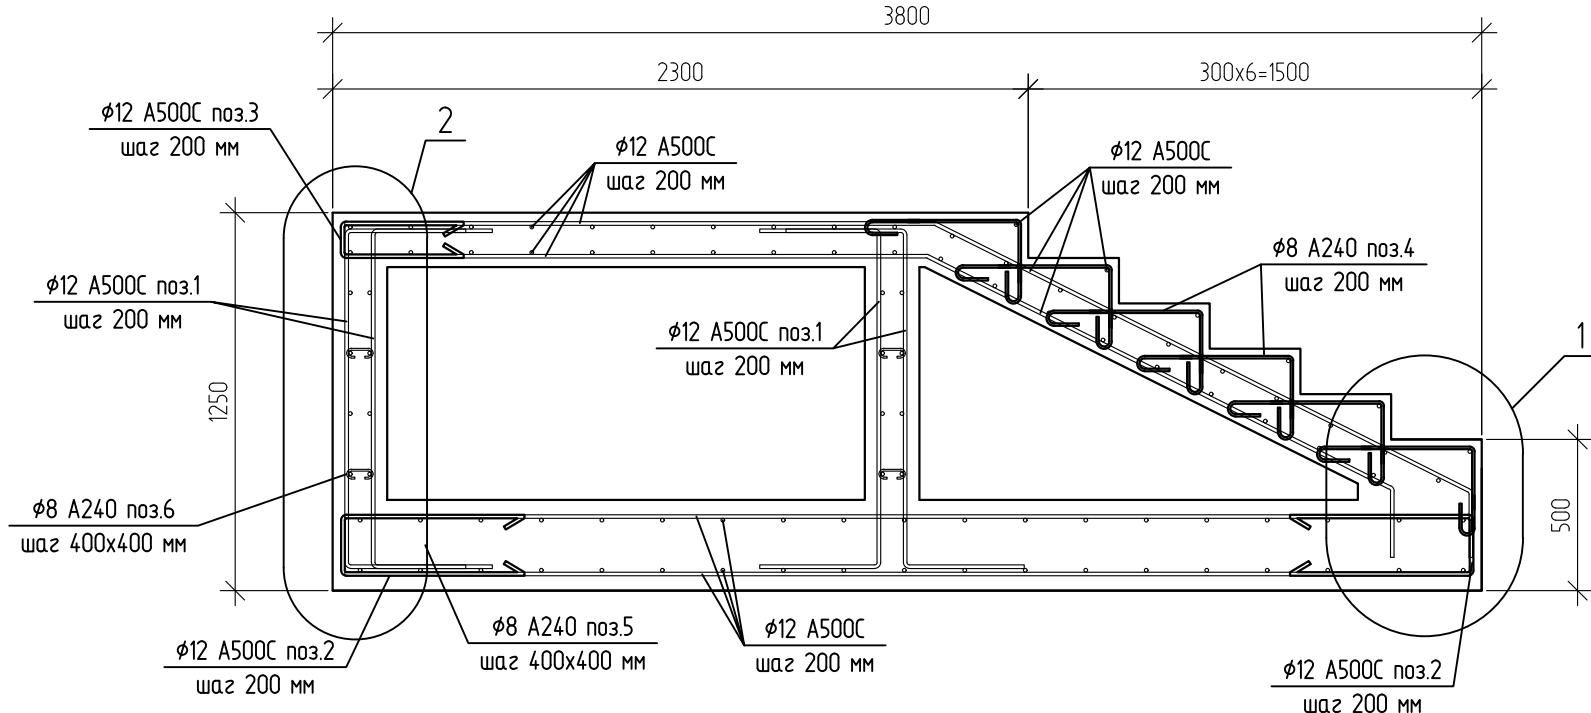

Армирование 2-2

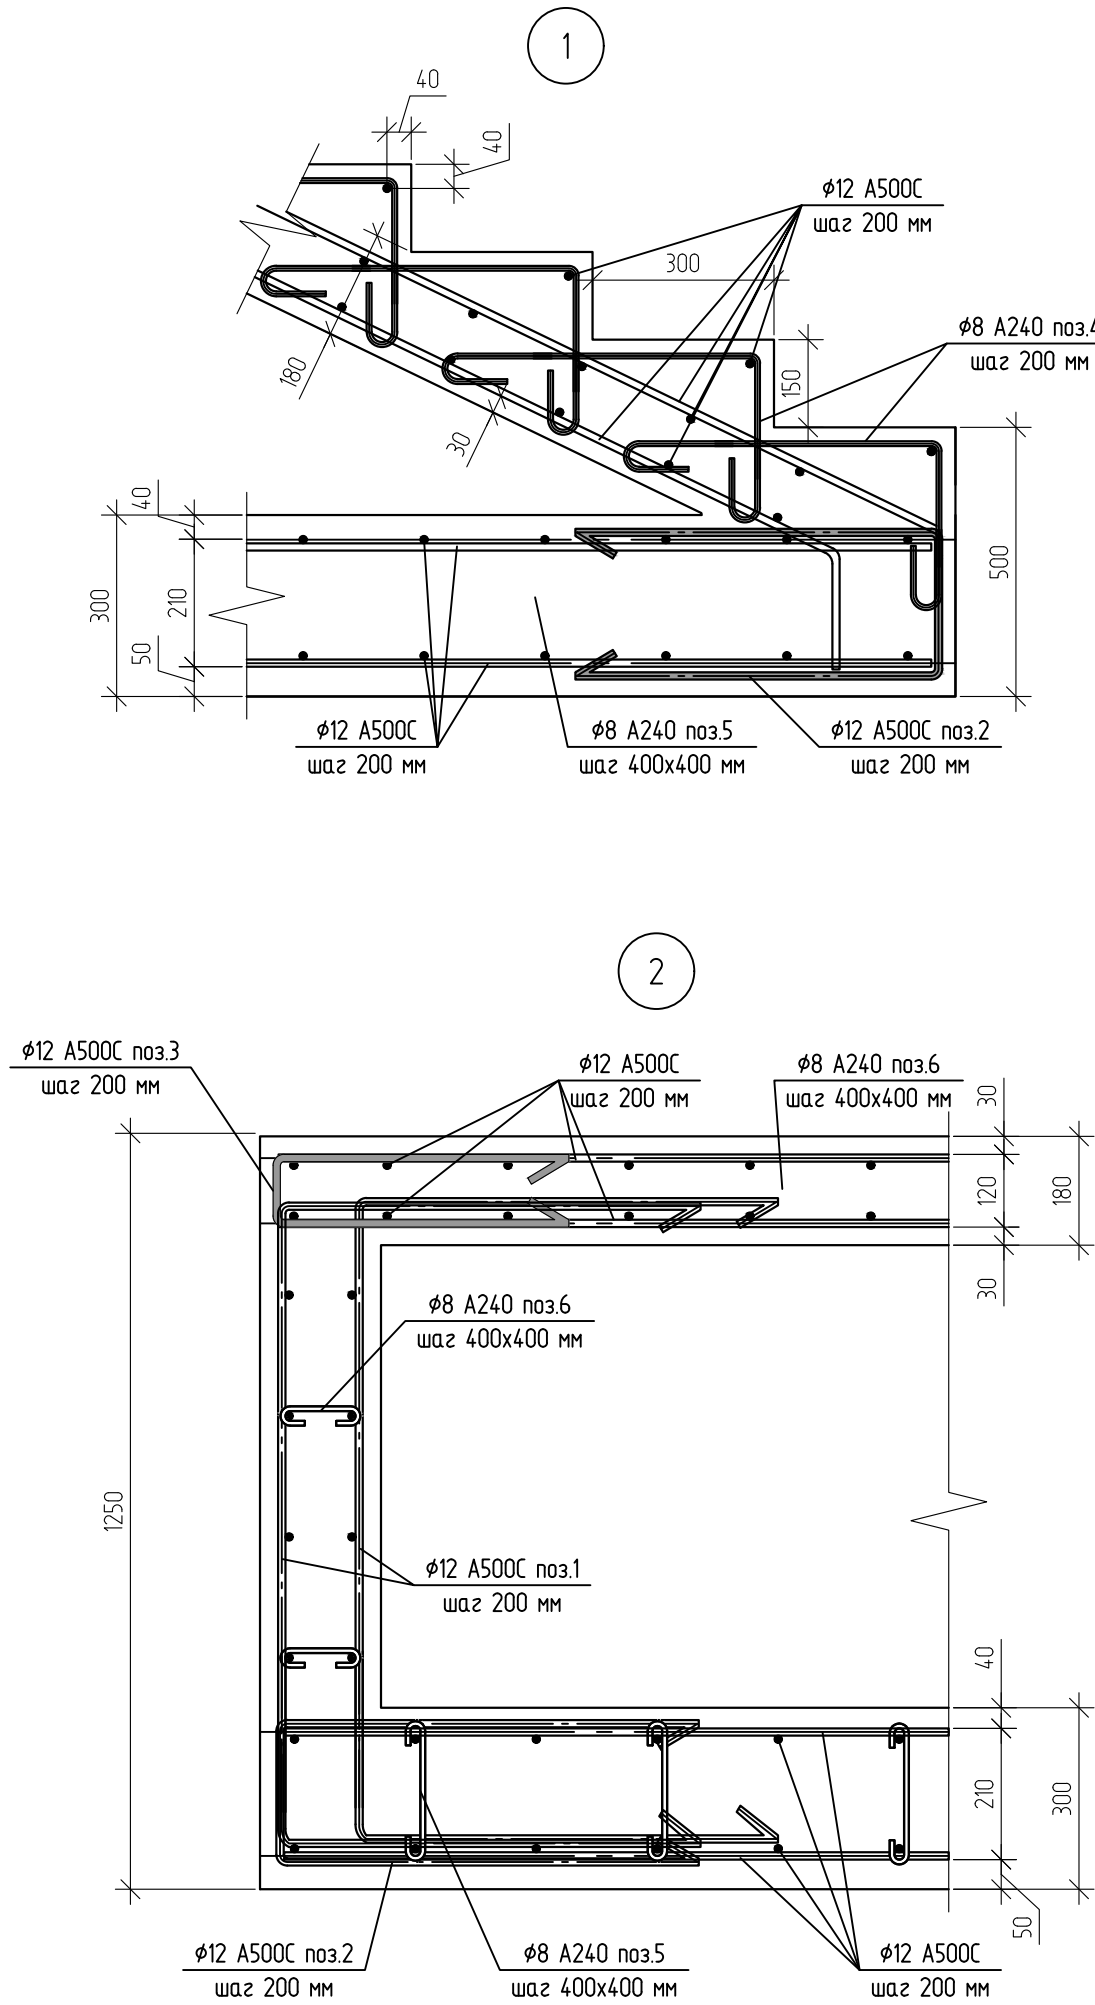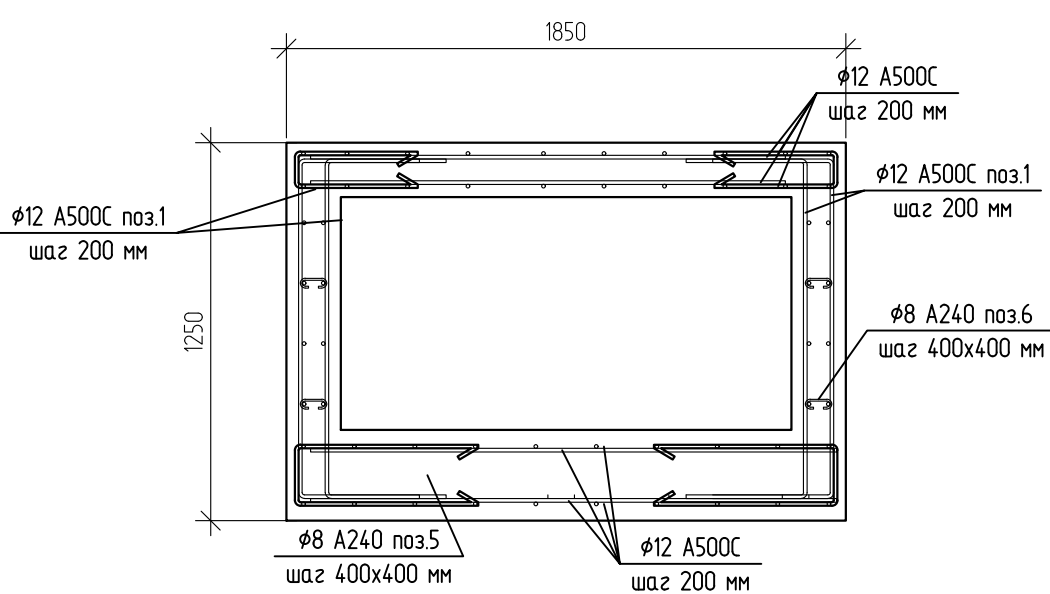

Ведомость деталей	
Поз.	Эскиз
1	
2	
3	
4	
5	
6	




Спецификация на устройство входа в осях "13-14/П"					
Поз.	Обозначение	Наименование	Кол.	Масса 1 дет., кг	Примеч. общ. вес, кг
		Конструкции выше Ур.з.			
	ГОСТ 34028-2016	Ø12 A500C, п.м	194,7	0,888	172,89
1	ГОСТ 34028-2016	Ø12 A500C, L=2120 мм, шт	76	188	142,88
3	ГОСТ 34028-2016	Ø12 A500C, L=910 мм, шт	27	0,81	21,87
4	ГОСТ 34028-2016	Ø8 A240, L=850 мм, шт	48	0,34	16,32
6	ГОСТ 34028-2016	Ø8 A240, L=200 мм, шт	162	0,08	12,96
		Фундаментная плита			
	ГОСТ 34028-2016	Ø12 A500C, п.м	138,3	0,888	122,81
2	ГОСТ 34028-2016	Ø12 A500C, L=1390 мм, шт	54	123	66,42
5	ГОСТ 34028-2016	Ø8 A240, L=300 мм, шт	30	0,12	3,6
		Материалы			
		Бетон В25, W6, F150, м³	5,3		
		Бетон В7,5, м³	0,8		
		Песок средней крупности, м³	5,3		
		Гидроизоляция, м²	10		
		Пенополистирол t=20 мм, м²	4,6		

Ведомость расхода стали, кг


Марка элемента	Изделия арматурные			
	Арматура класса		Всего	
	A500C	A240		
	ГОСТ 34028-2016	ГОСТ 34028-2016		
	Ø12	Итого	Ø8	Итого
	526,87	524,21	32,88	32,88
			559,75	

1. Фундаментную плиту, плиту площадки армировать отдельными стержнями Ø12 A500C с шагом 200x200 мм. Вся рабочая арматура соединяется в сетки с помощью вязальной проволоки. В сетках вязке подлежат пересечения стержней через одно в шахматном порядке.
2. Соединение стержней по длине производить внахлест с перелупком не менее 45 диаметров стыкуемой арматуры. В одном условном сечении не более 50% стыкуемой арматуры.
3. Размеры хомутов и гнутых деталей даны для справки. Данные размеры следует уточнять и корректировать по месту для соответствия нижней и верхней сеток проектному.
4. Стыки смежных стержней разносить в шахматном порядке.
5. Фиксаторы положения сеток (лягушки) на чертеже не показаны и в спецификации не учтены.


Схема устройства входа в осях "Ю/Л-М"

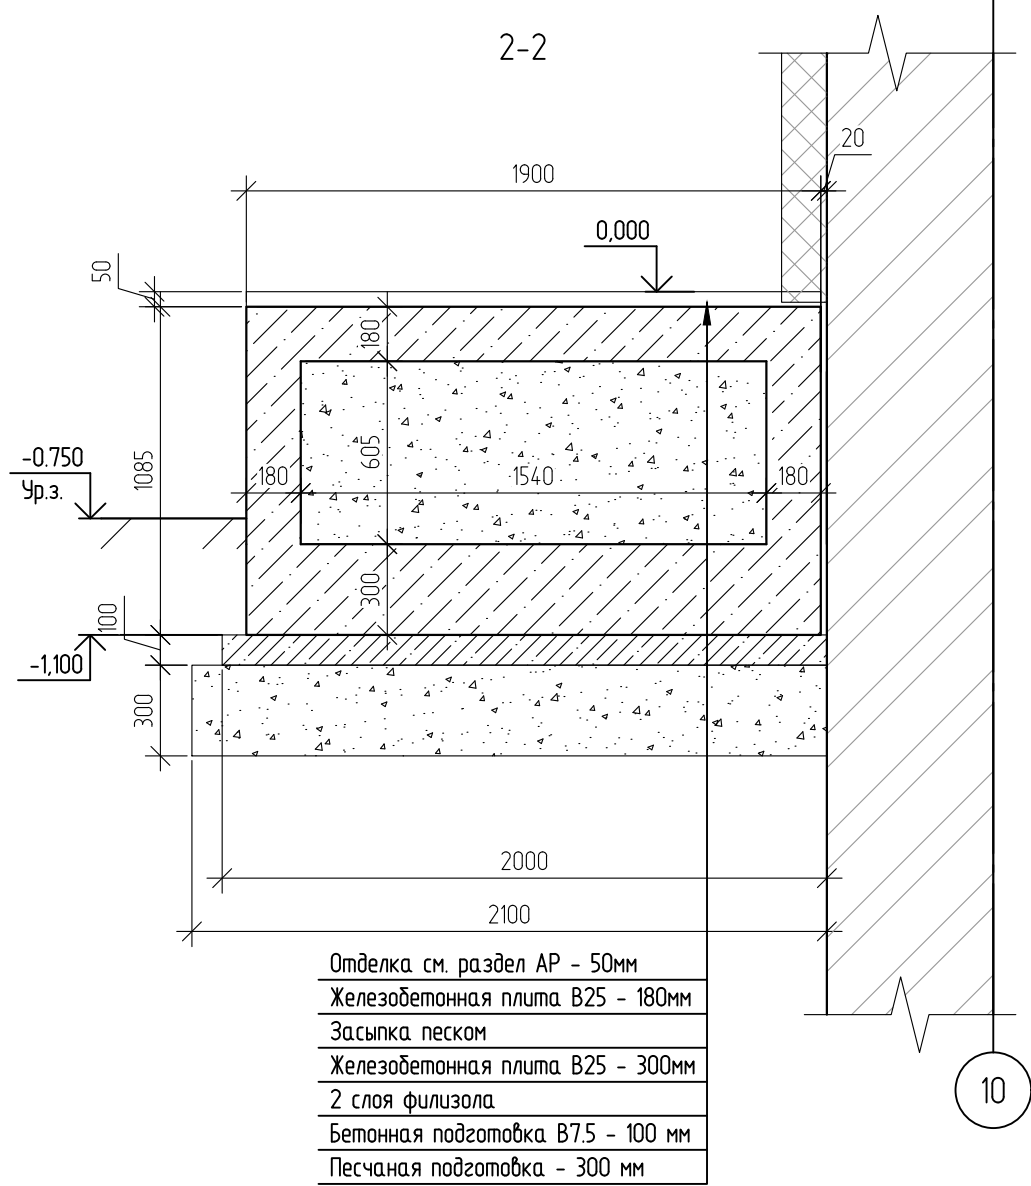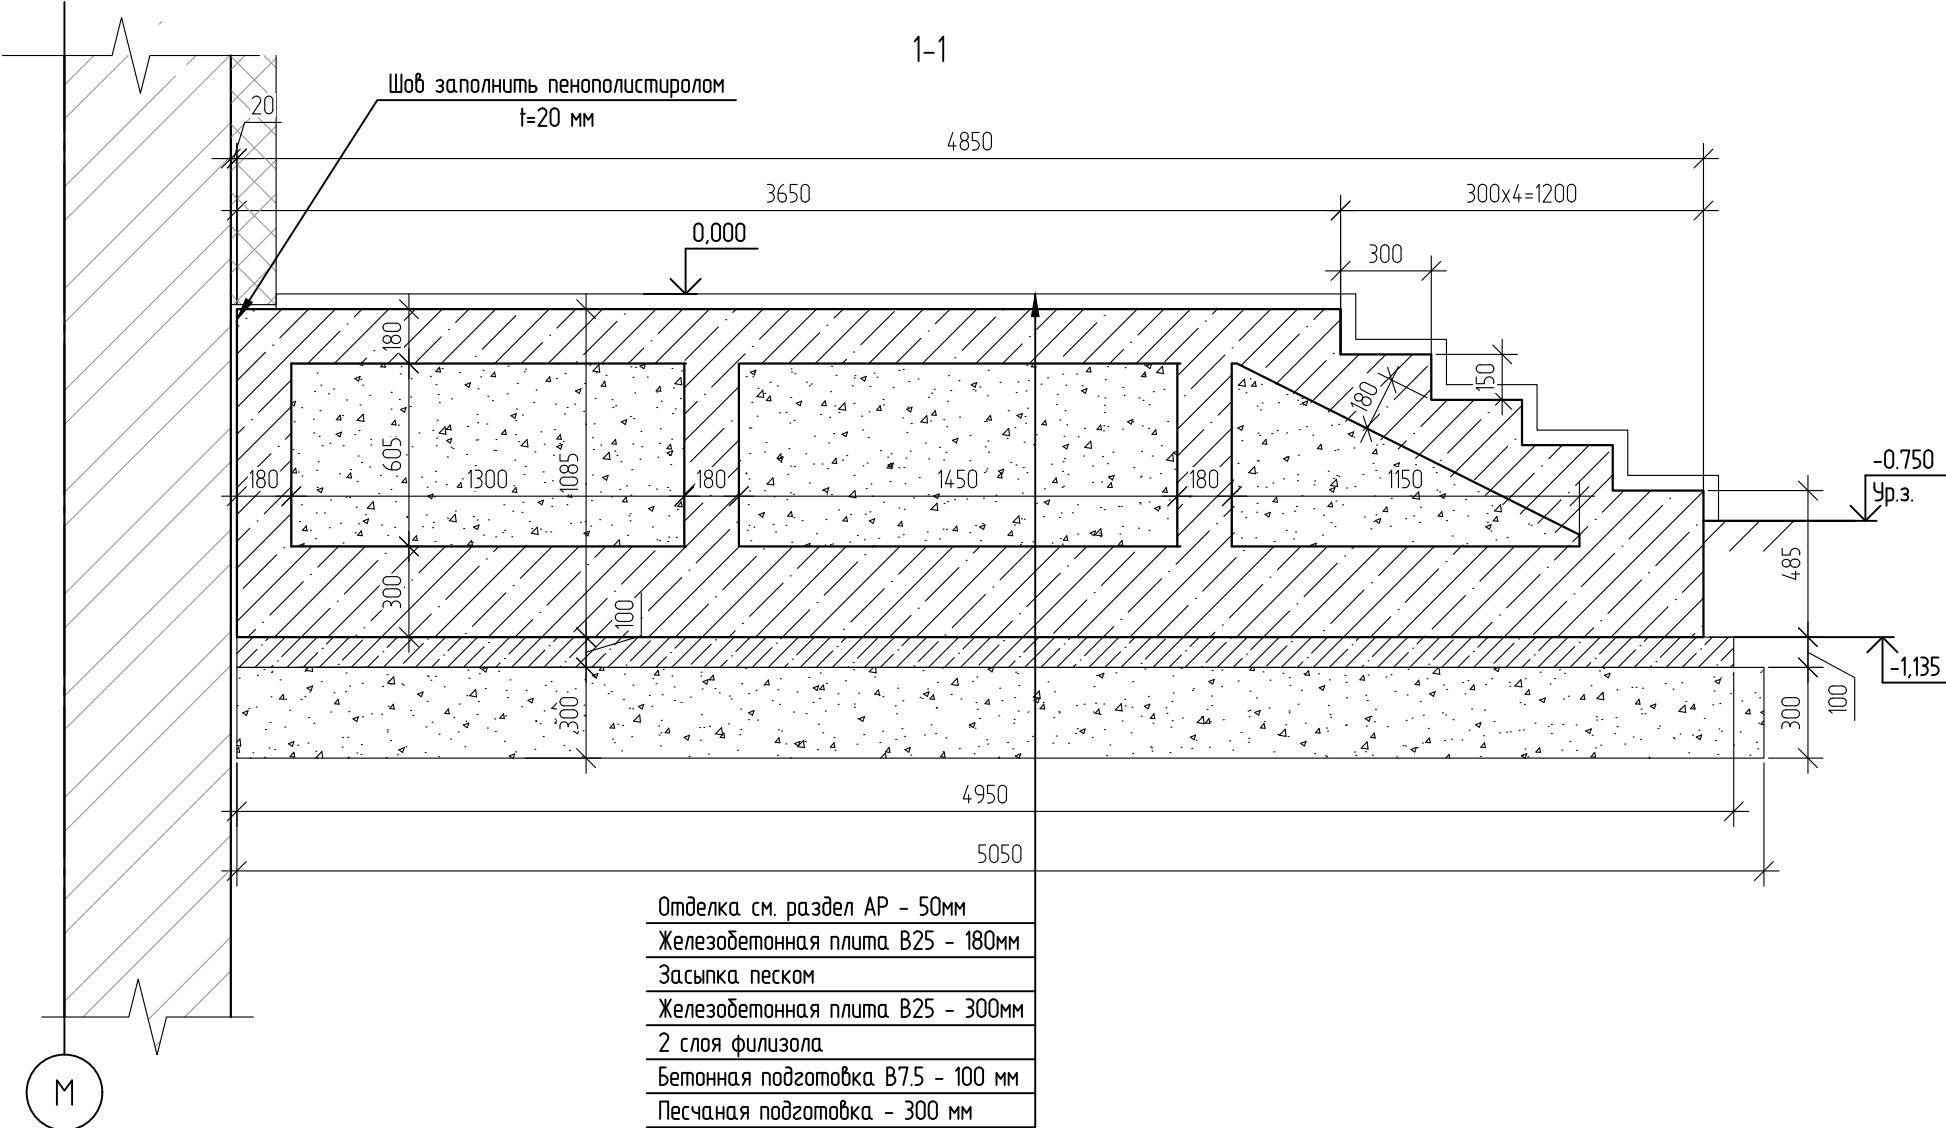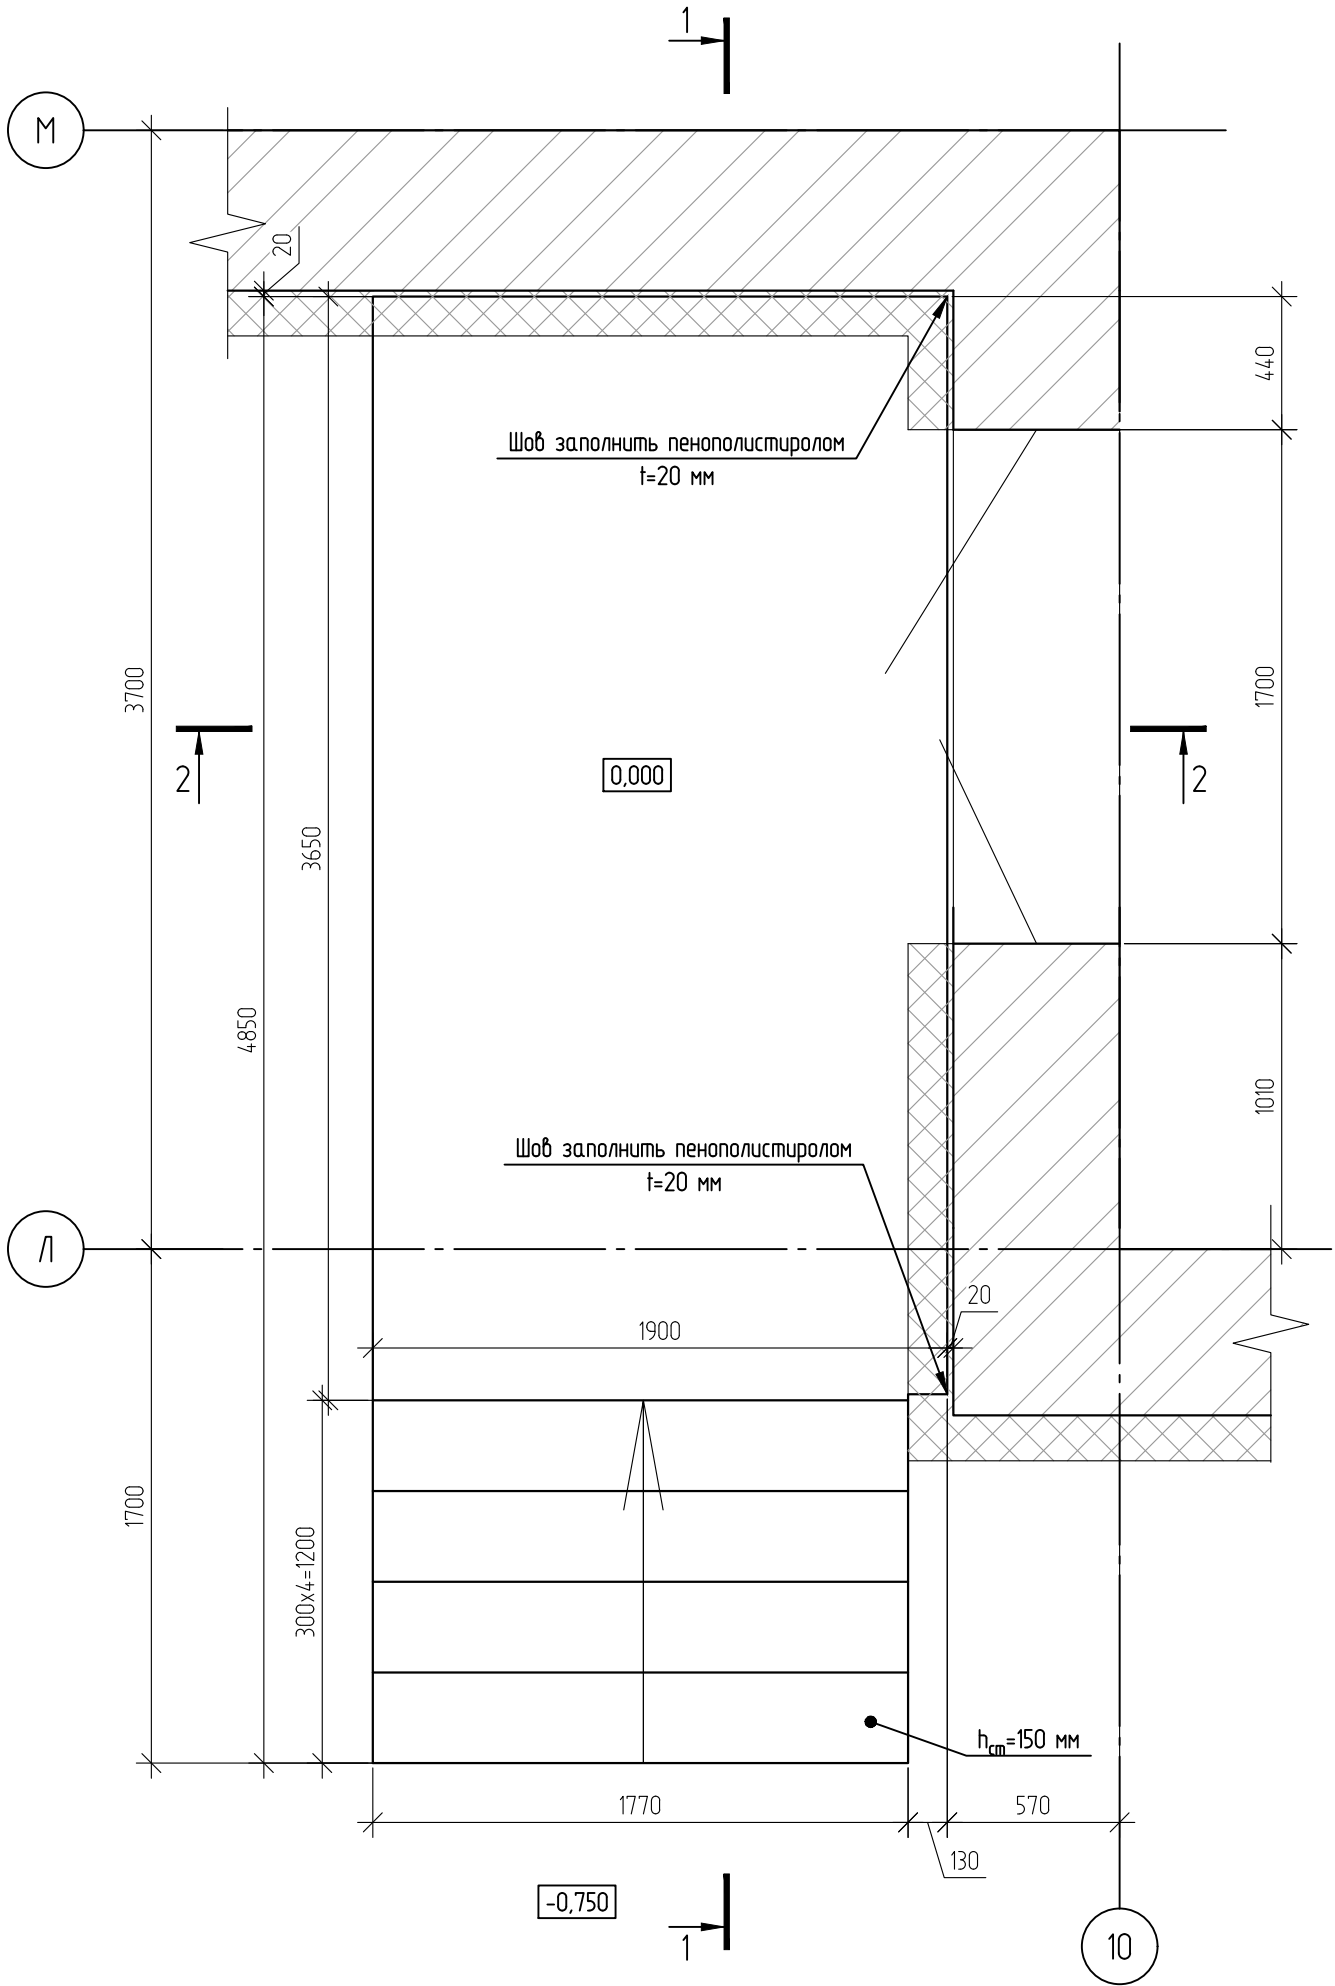


Армирование 2-2

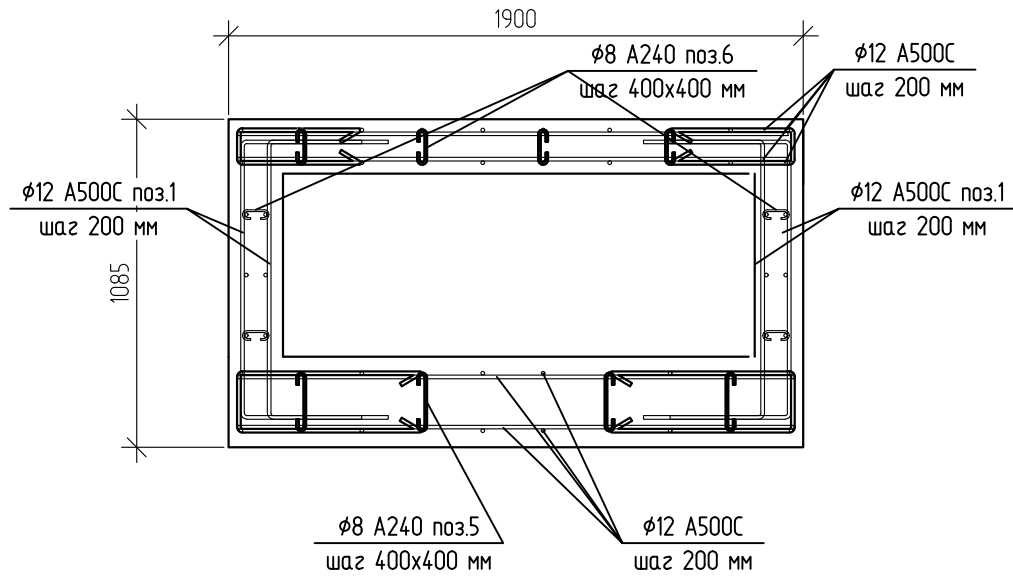


Армирование 1-1

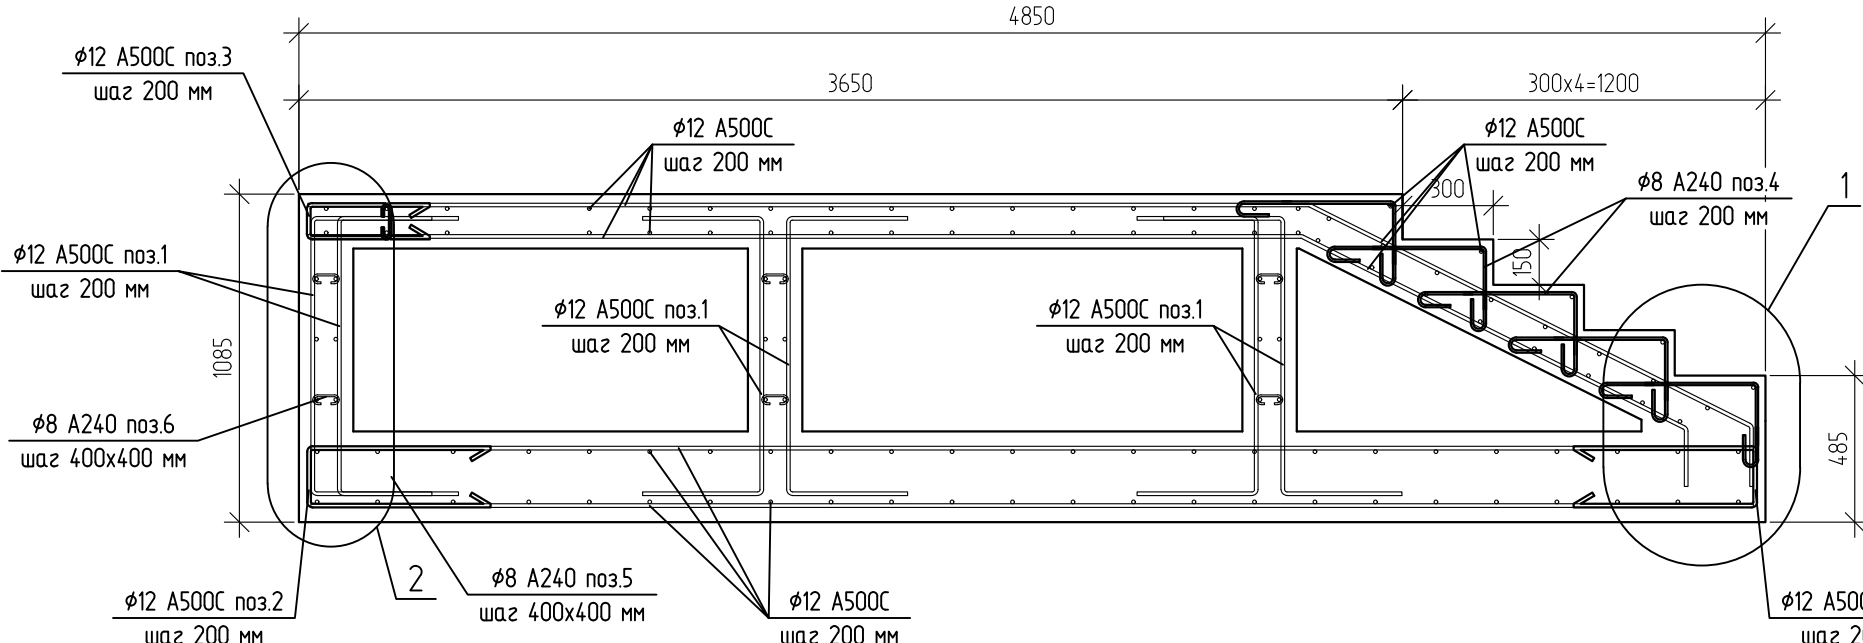

2

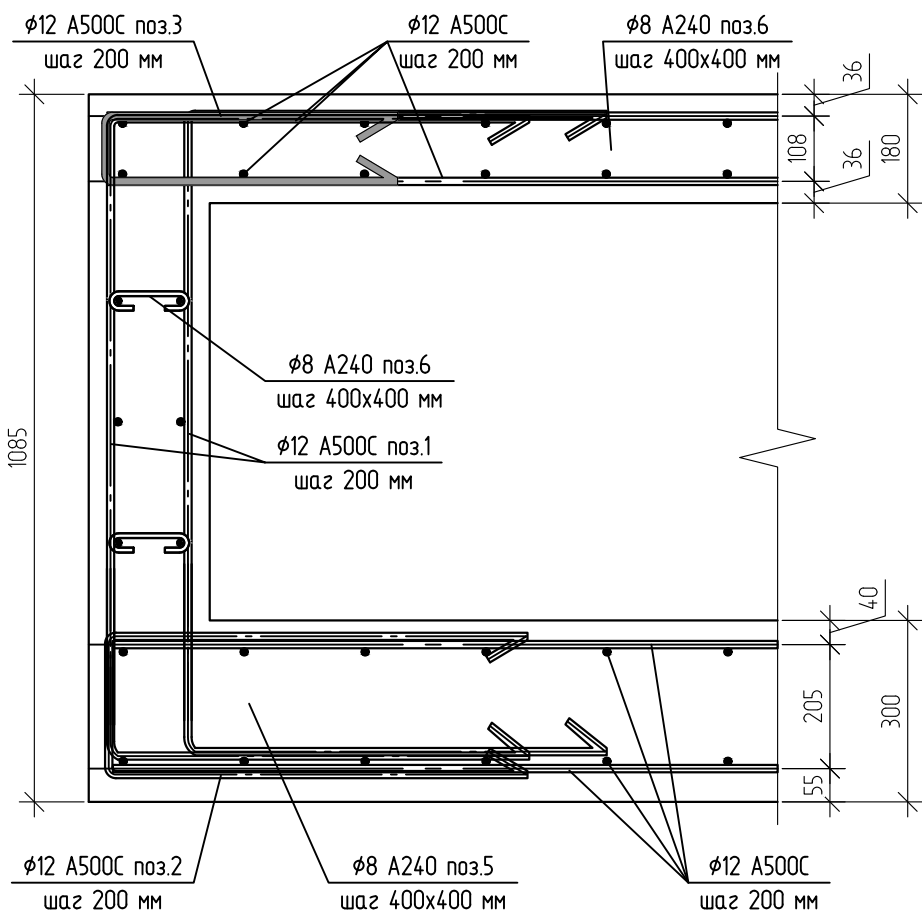

1

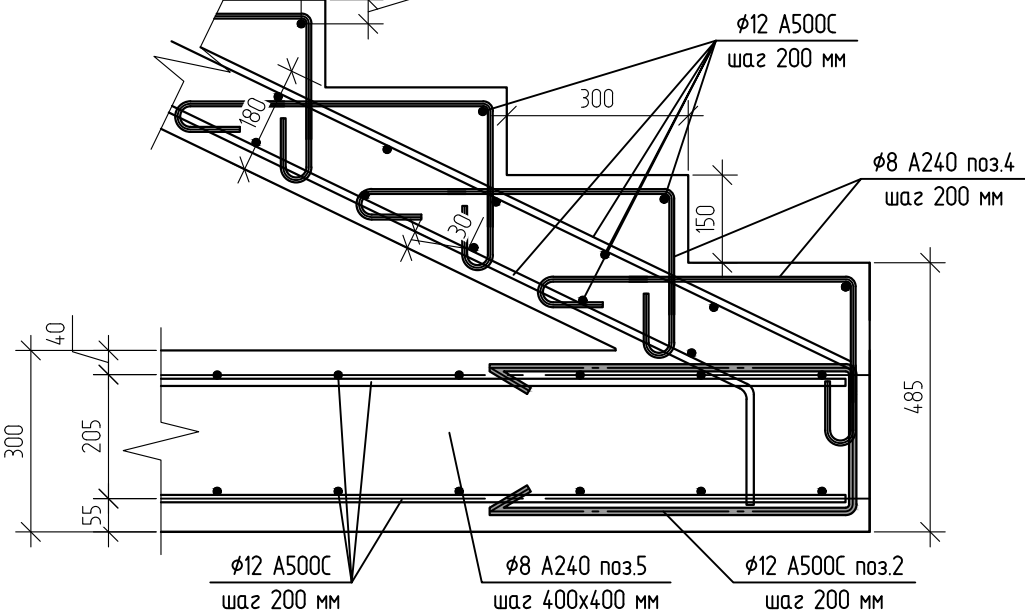

Ведомость деталей	
Поз.	Эскиз
1	
2	
3	
4	
5	
6	

Спецификация на устройство входа в осях "Ю/Л-М"






Поз.	Обозначение	Наименование	Кол.	Масса 1 дет., кг	Примеч. общ. вес кг
Конструкции выше Чр.з.					
	ГОСТ 34028-2016	Ø12 A500C, п.м	288.4	0.888	256.1
1	ГОСТ 34028-2016	Ø12 A500C, L=1680 мм, шт	126	15	189
3	ГОСТ 34028-2016	Ø12 A500C, L=910 мм, шт	27	0.81	21.87
4	ГОСТ 34028-2016	Ø8 A240, L=850 мм, шт	40	0.34	13.6
6	ГОСТ 34028-2016	Ø8 A240, L=200 мм, шт	32	0.08	2.56
Фундаментная плита					
	ГОСТ 34028-2016	Ø12 A500C, п.м	176.2	0.888	156.47
2	ГОСТ 34028-2016	Ø12 A500C, L=1390 мм, шт	33	12.3	40.59
5	ГОСТ 34028-2016	Ø8 A240, L=300 мм, шт	48	0.12	5.76
Материалы					
		Бетон В25, W6, F150, м³	6.5		
		Бетон В7.5, м³	1		
		Песок средней крупности, м³	6.2		
		Гидроизоляция, м²	16		
		Пенополистирол L=20 мм, м²	6.8		

Ведомость расхода стали, кг



Марка элемента	Изделия арматурные			
	Арматура класса		Всего	
	A500C	A240		
	ГОСТ 34028-2016	ГОСТ 34028-2016		
	Ø12	Итого	Ø8	Итого
	664.03	664.03	2192	2192
			685.95	

1. Фундаментную плиту, плиту площадки армировать отдельными стержнями Ø12 A500C с шагом 200х200 мм. Вся рабочая арматура соединяется в сетки с помощью вязальной проволоки. В сетках вязке подлежат пересечения стержней через одно в шахматном порядке.
2. Соединение стержней по длине производить внахлест с перелупком не менее 45 диаметров стержней арматуры. В одном условном сечении не более 50% стержней арматуры.
3. Размеры хомутов и гнутых деталей даны для справки. Данные размеры следует уточнять и корректировать по месту для соответствия нижней и верхней сеток проектному.
4. Стыки смежных стержней разносить в шахматном порядке.
5. Фиксаторы положения сеток (лягушки) на чертеже не показаны и в спецификации не учтены.

2

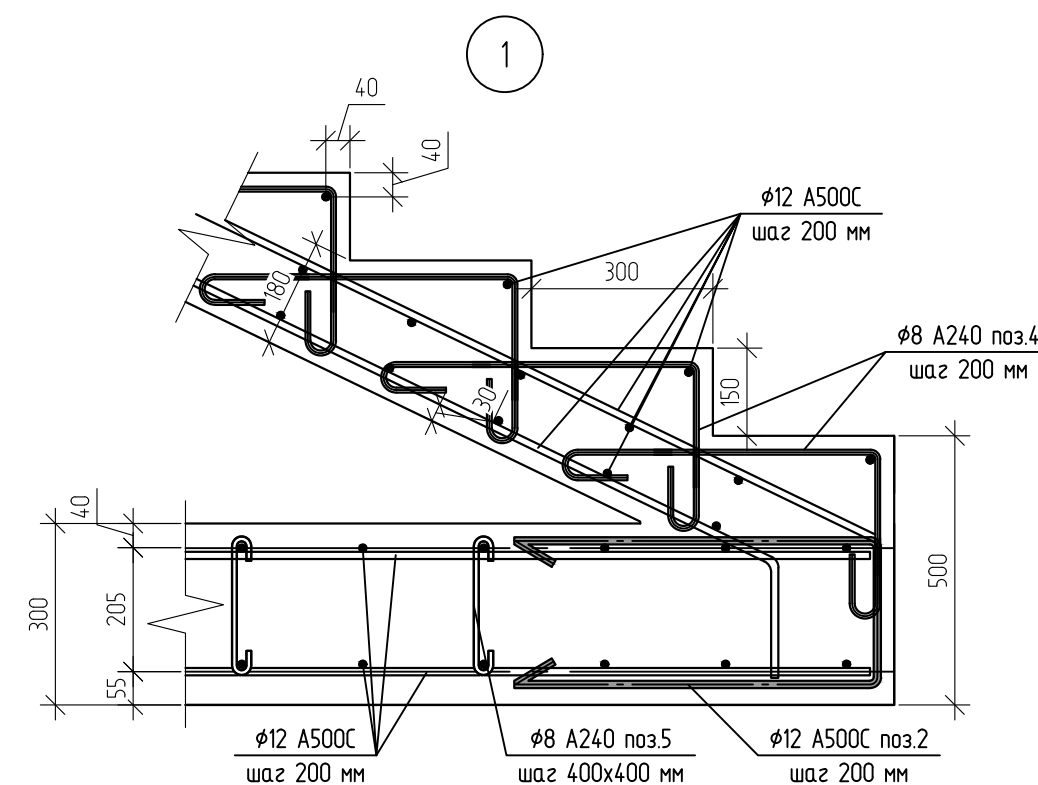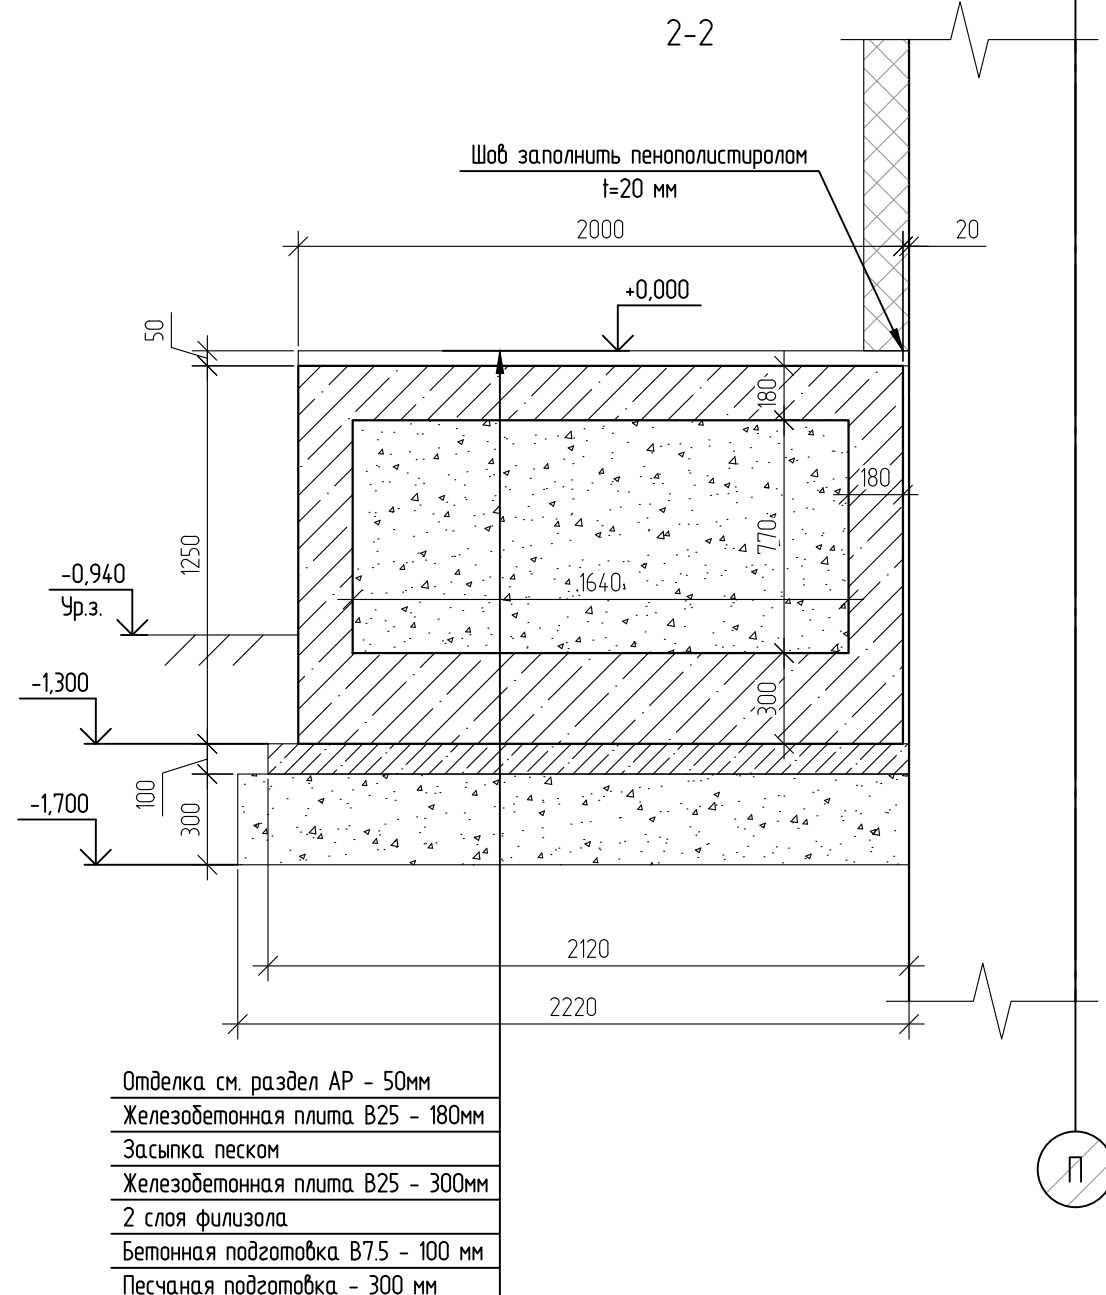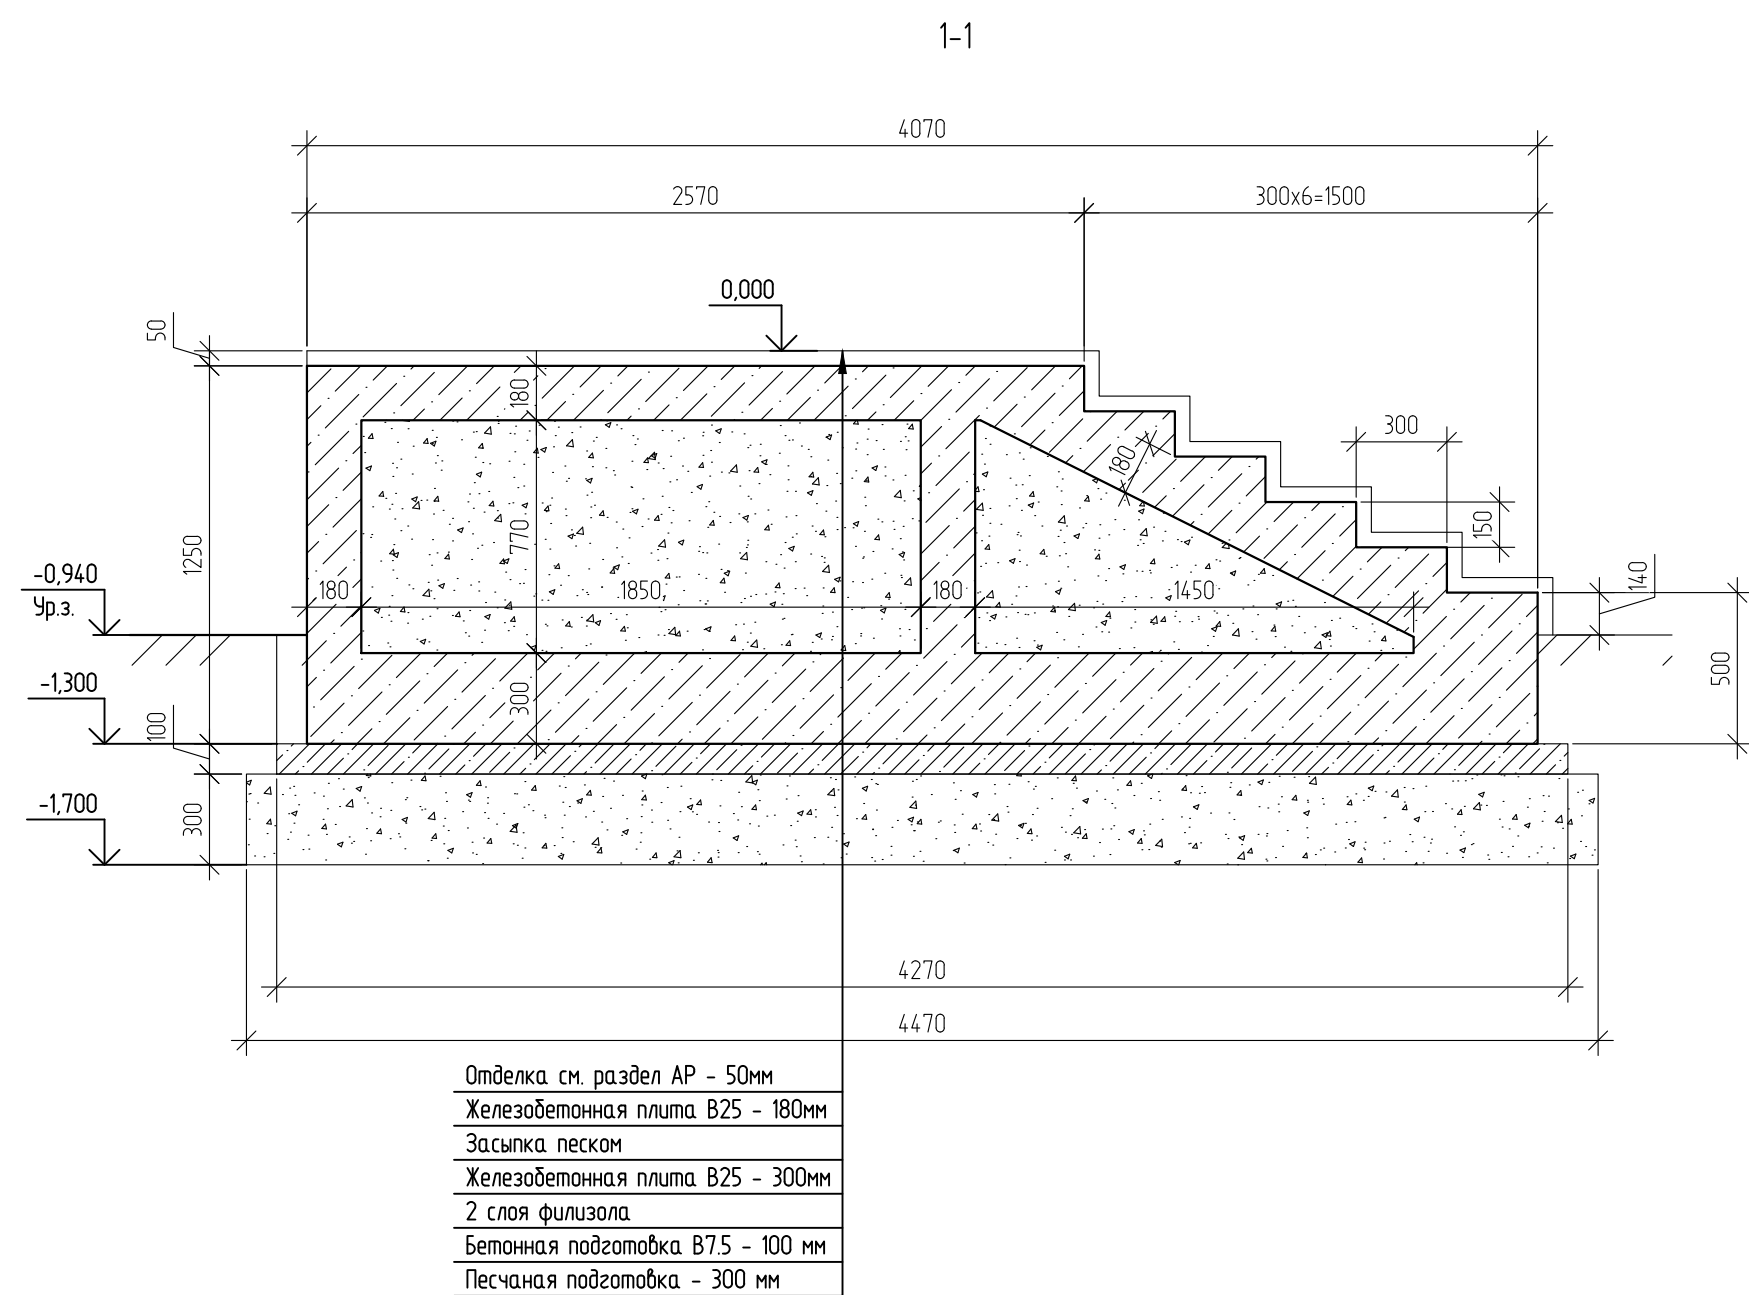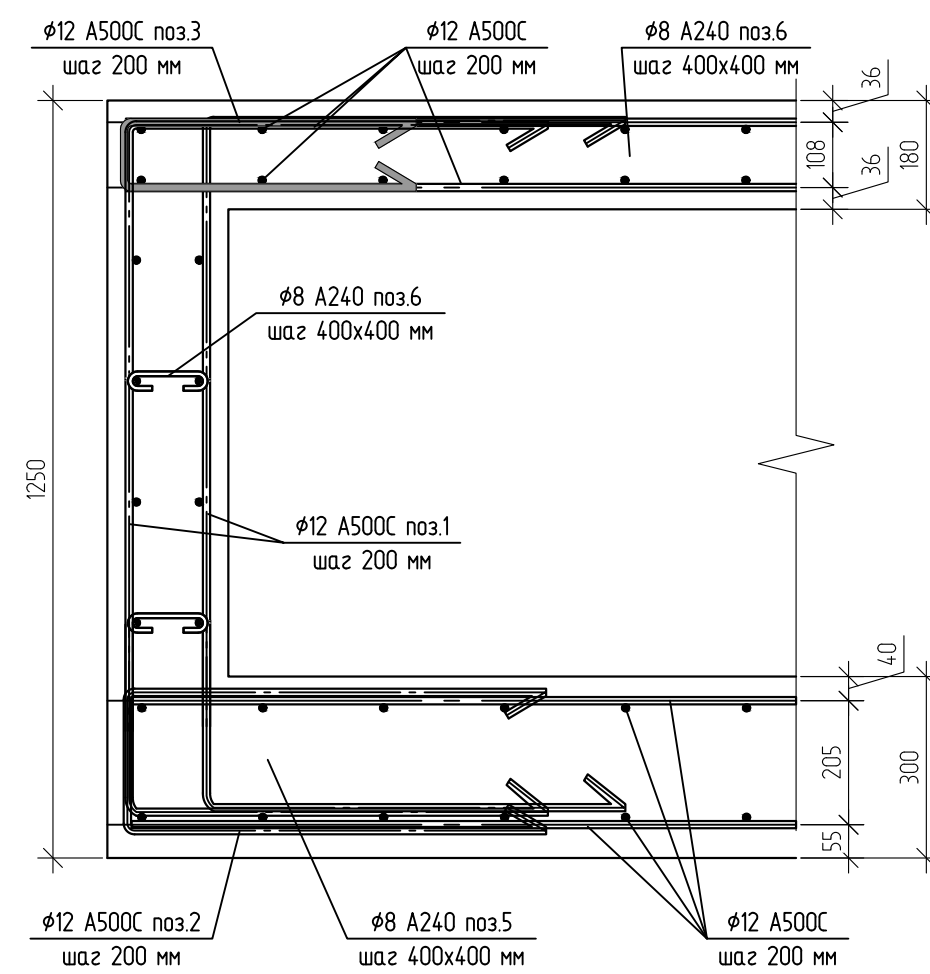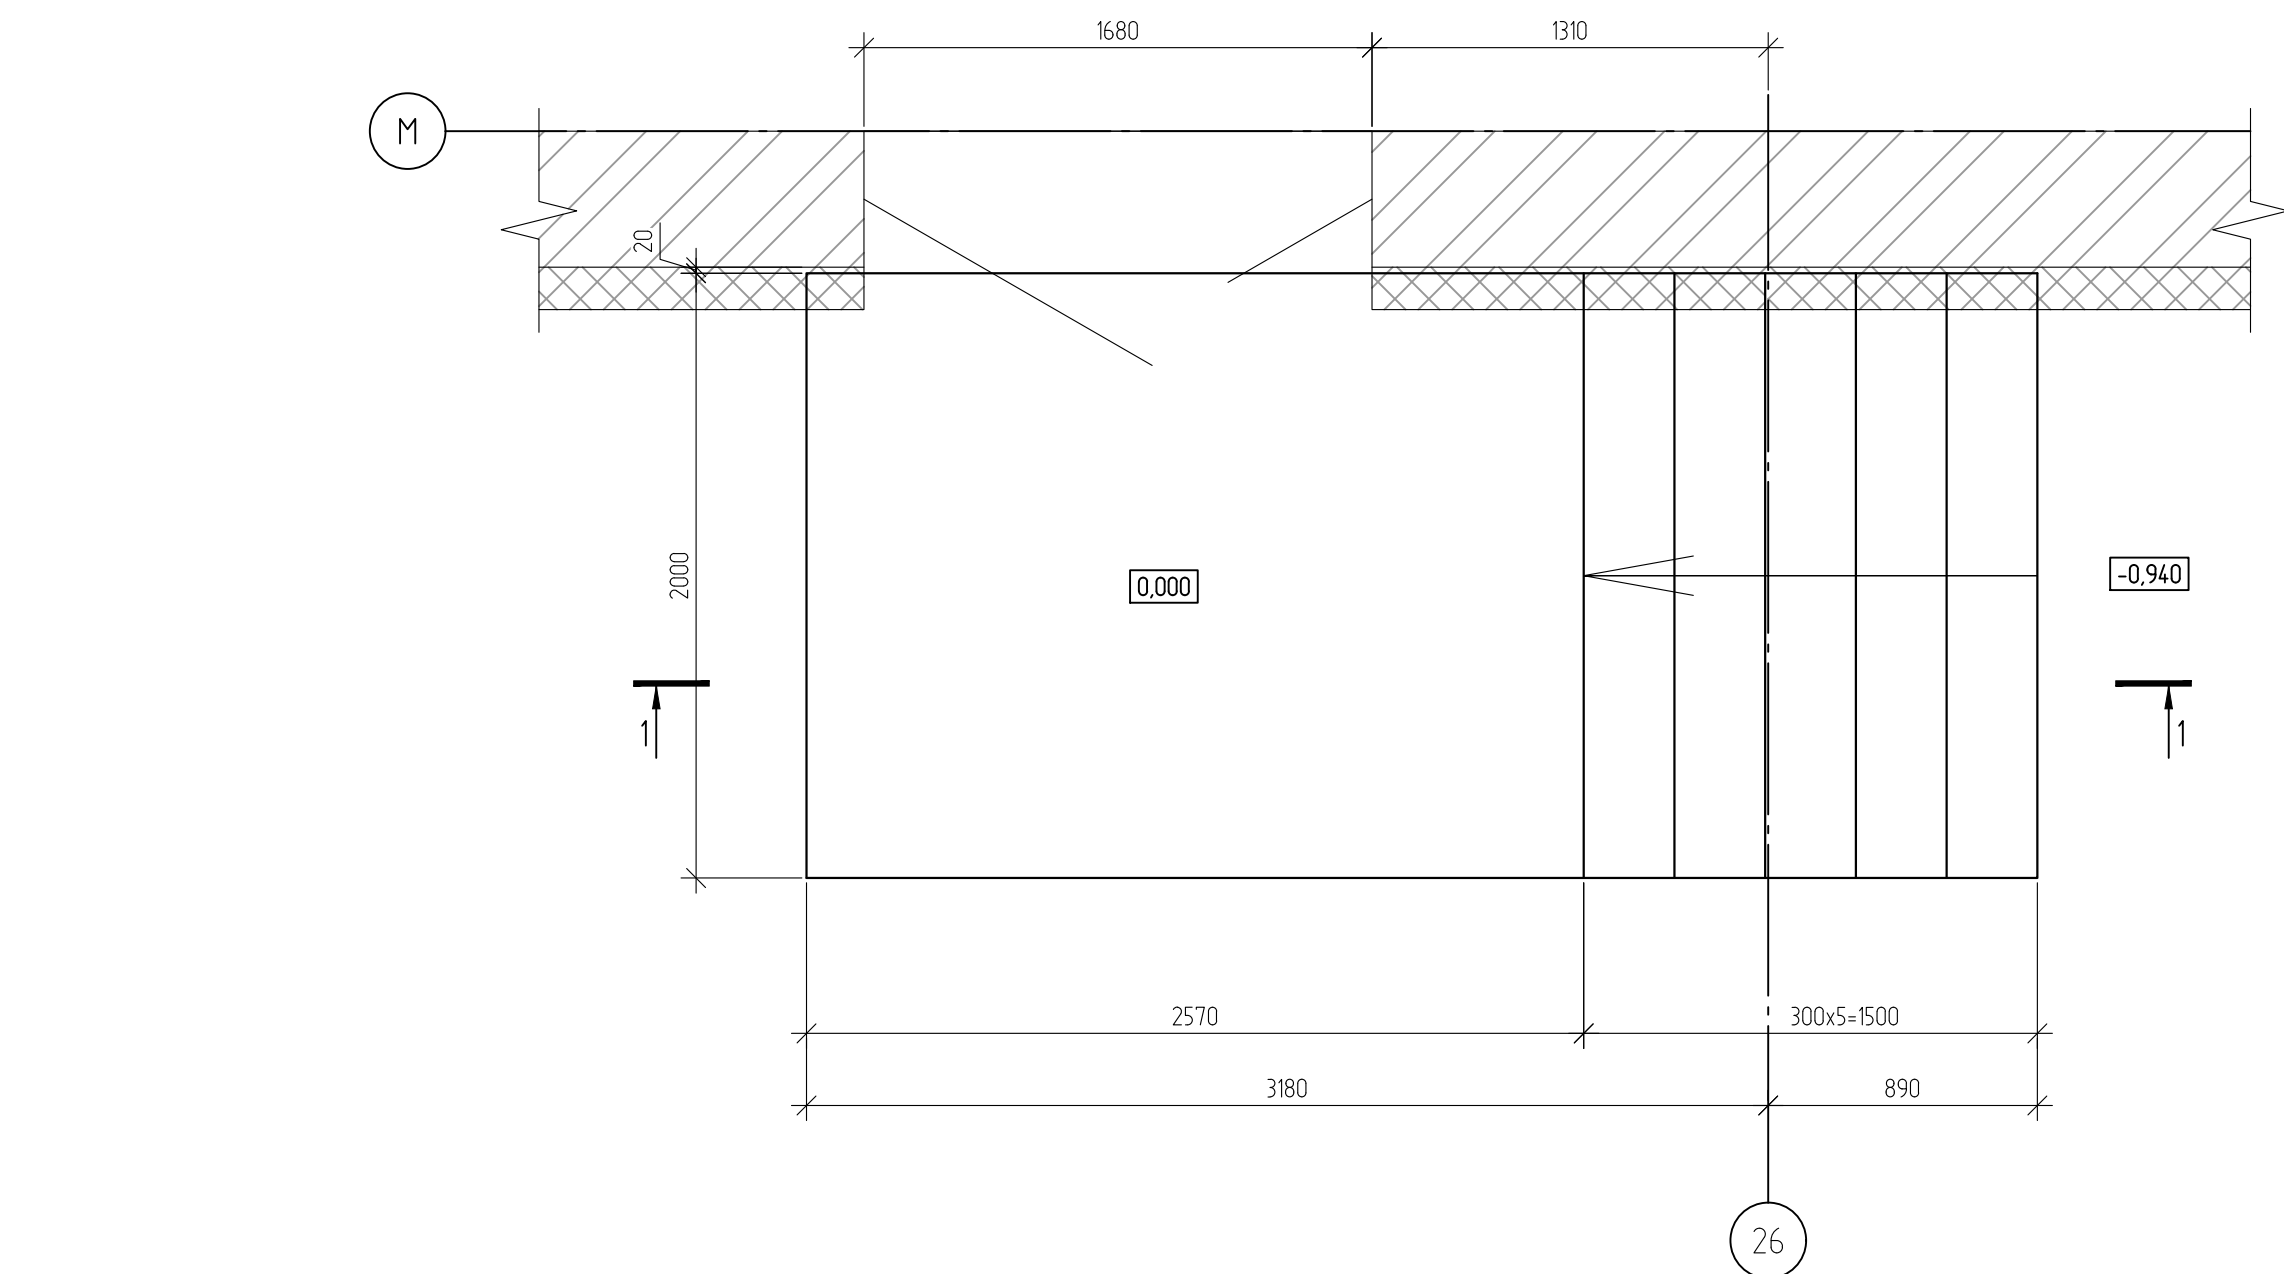

Ведомость деталей	
Поз.	Эскиз
1	
2	
3	
4	
5	
6	

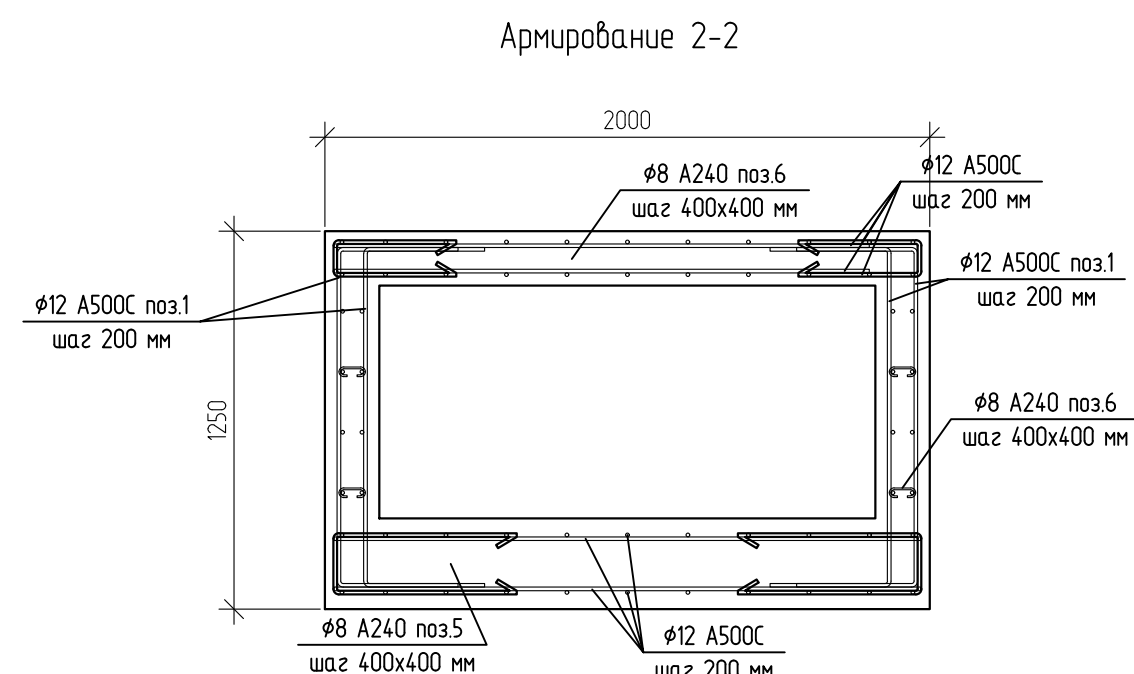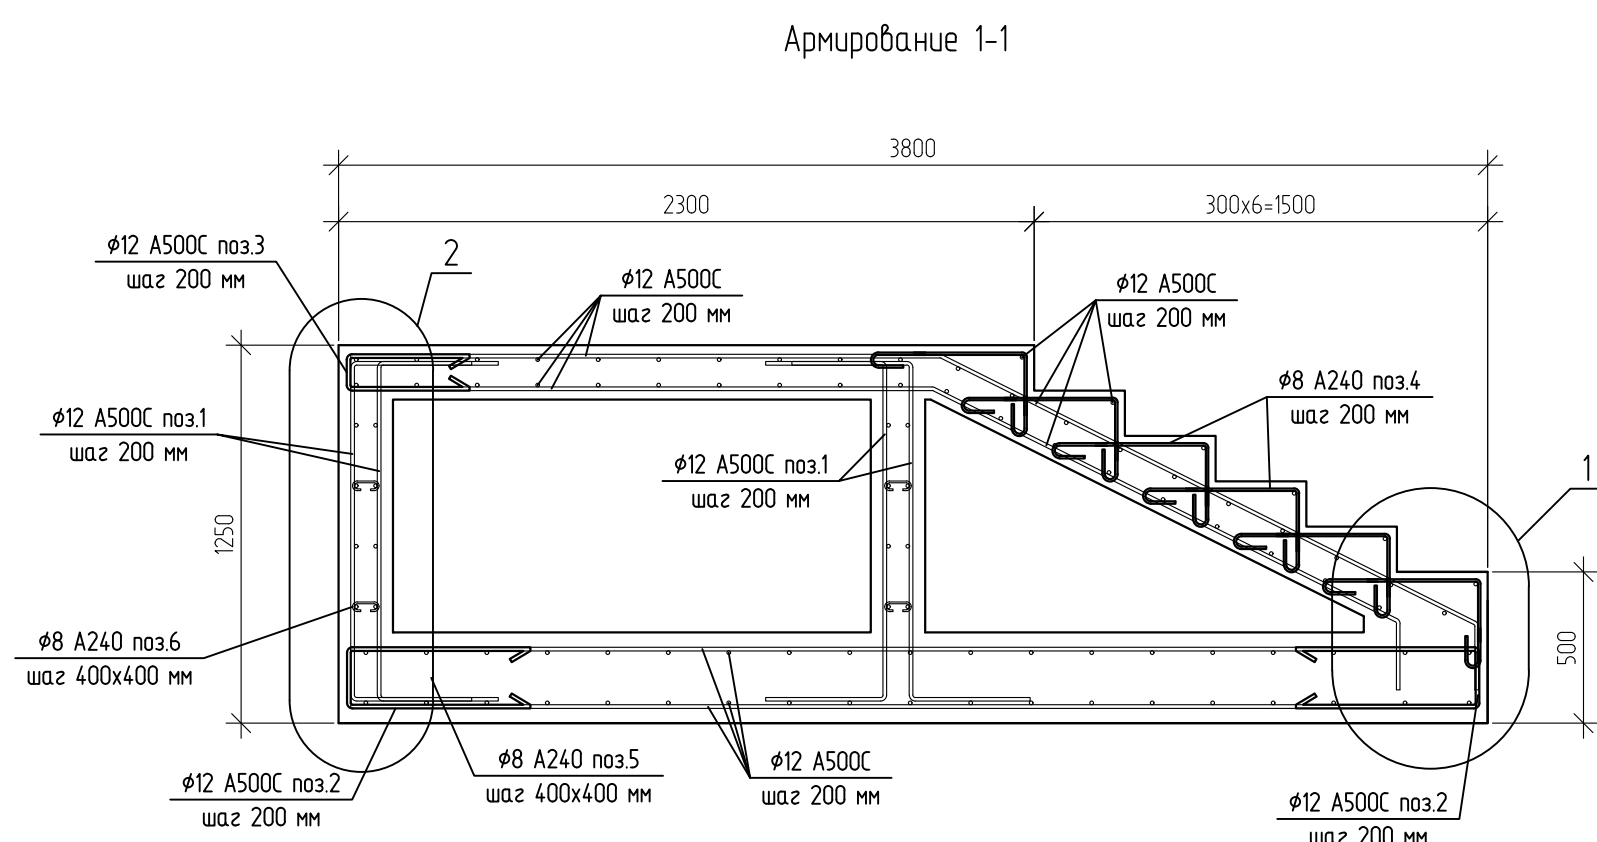

Спецификация на устройство входа в осях "26/М"

Поз.	Обозначение	Наименование	Кол.	Масса 1 дет, кг	Примеч. общ. вес кг
		Конструкции выше Ур.з			
	ГОСТ 34028-2016	Ø12 А500С, п.м.	244	0.888	216.67
1	ГОСТ 34028-2016	Ø12 А500С, L=1920 мм, шт	98	1.71	167.58
3	ГОСТ 34028-2016	Ø12 А500С, L=910 мм, шт	34	0.81	27.54
4	ГОСТ 34028-2016	Ø8 А240, L=850 мм, шт	60	0.34	20.4
6	ГОСТ 34028-2016	Ø8 А240, L=200 мм, шт	32	0.08	2.56
		Фундаментная плита			
	ГОСТ 34028-2016	Ø12 А500С, п.м.	161	0.888	142.97
2	ГОСТ 34028-2016	Ø12 А500С, L=1390 мм, шт	58	1.23	71.34
5	ГОСТ 34028-2016	Ø8 А240, L=300 мм, шт	40	0.12	4.8
		Материалы			
		Бетон В25, W6, F50, м³	5.6		
		Бетон В7.5, м³	0.85		
		Песок средней крупности, м³	6.4		
		Гидроизоляция, м²	8.2		
		Пенополистирол 1-20 мм, м²	5		



Ведомость расхода стали, кг

Марка элемента	Изделия арматурные			
	Арматура класса			Всего
	A500С		A240	
	ГОСТ 34028-2016		ГОСТ 34028-2016	
	Ø12	Итого	Ø8	Итого
	845,23	845,23	68,64	913,87




1. Фундаментную плиту, плиту площадки армировать отдельными стержнями $\Phi 12$ А500 с шагом 200х200 мм. Вся рабочая арматура соединяется в сетки с помощью вязальной проволоки. В сетках всяре подложка пересечения стержней через одну в шахматном порядке.
2. Соединение стержней по длине производить внахлест с перепуском не менее 45 диаметров стыкуемой арматуры. В одном условном сечении не более 50% стыкуемой арматуры.
3. Размеры хомутов и гнутых деталей даются для справки. Данные размеры следует уточнять и корректировать по месту для соответствия нижней и верхней сеток проектному.
4. Стыки смежных стержней разносить в шахматном порядке.
5. Фиксаторы положения сеток (лягушки) на чертеже не показаны и в спецификации не учтены.

						708/П-24 - АНО-КР			
						Капитальный ремонт общеобразовательного учреждения ГБОУ "Школа №1210" по адресу: г. Москва, ул. Хлебникова, д.32			
Изм.	Колуч.	Лист	№ док	Подп.	Дата	Конструктивные решения	Стандарт	Лист	Листов
Разработал	Торшин				04.26		Р	23	
ГАП	Фролова				04.26				
Н.Контроль	Лукашенко				04.26	Схема устройства входа в осях "26/М"			ООО "АРТИС"
ГИП	Зыкин				04.26				



Схема устройства входа в осях "27/М"

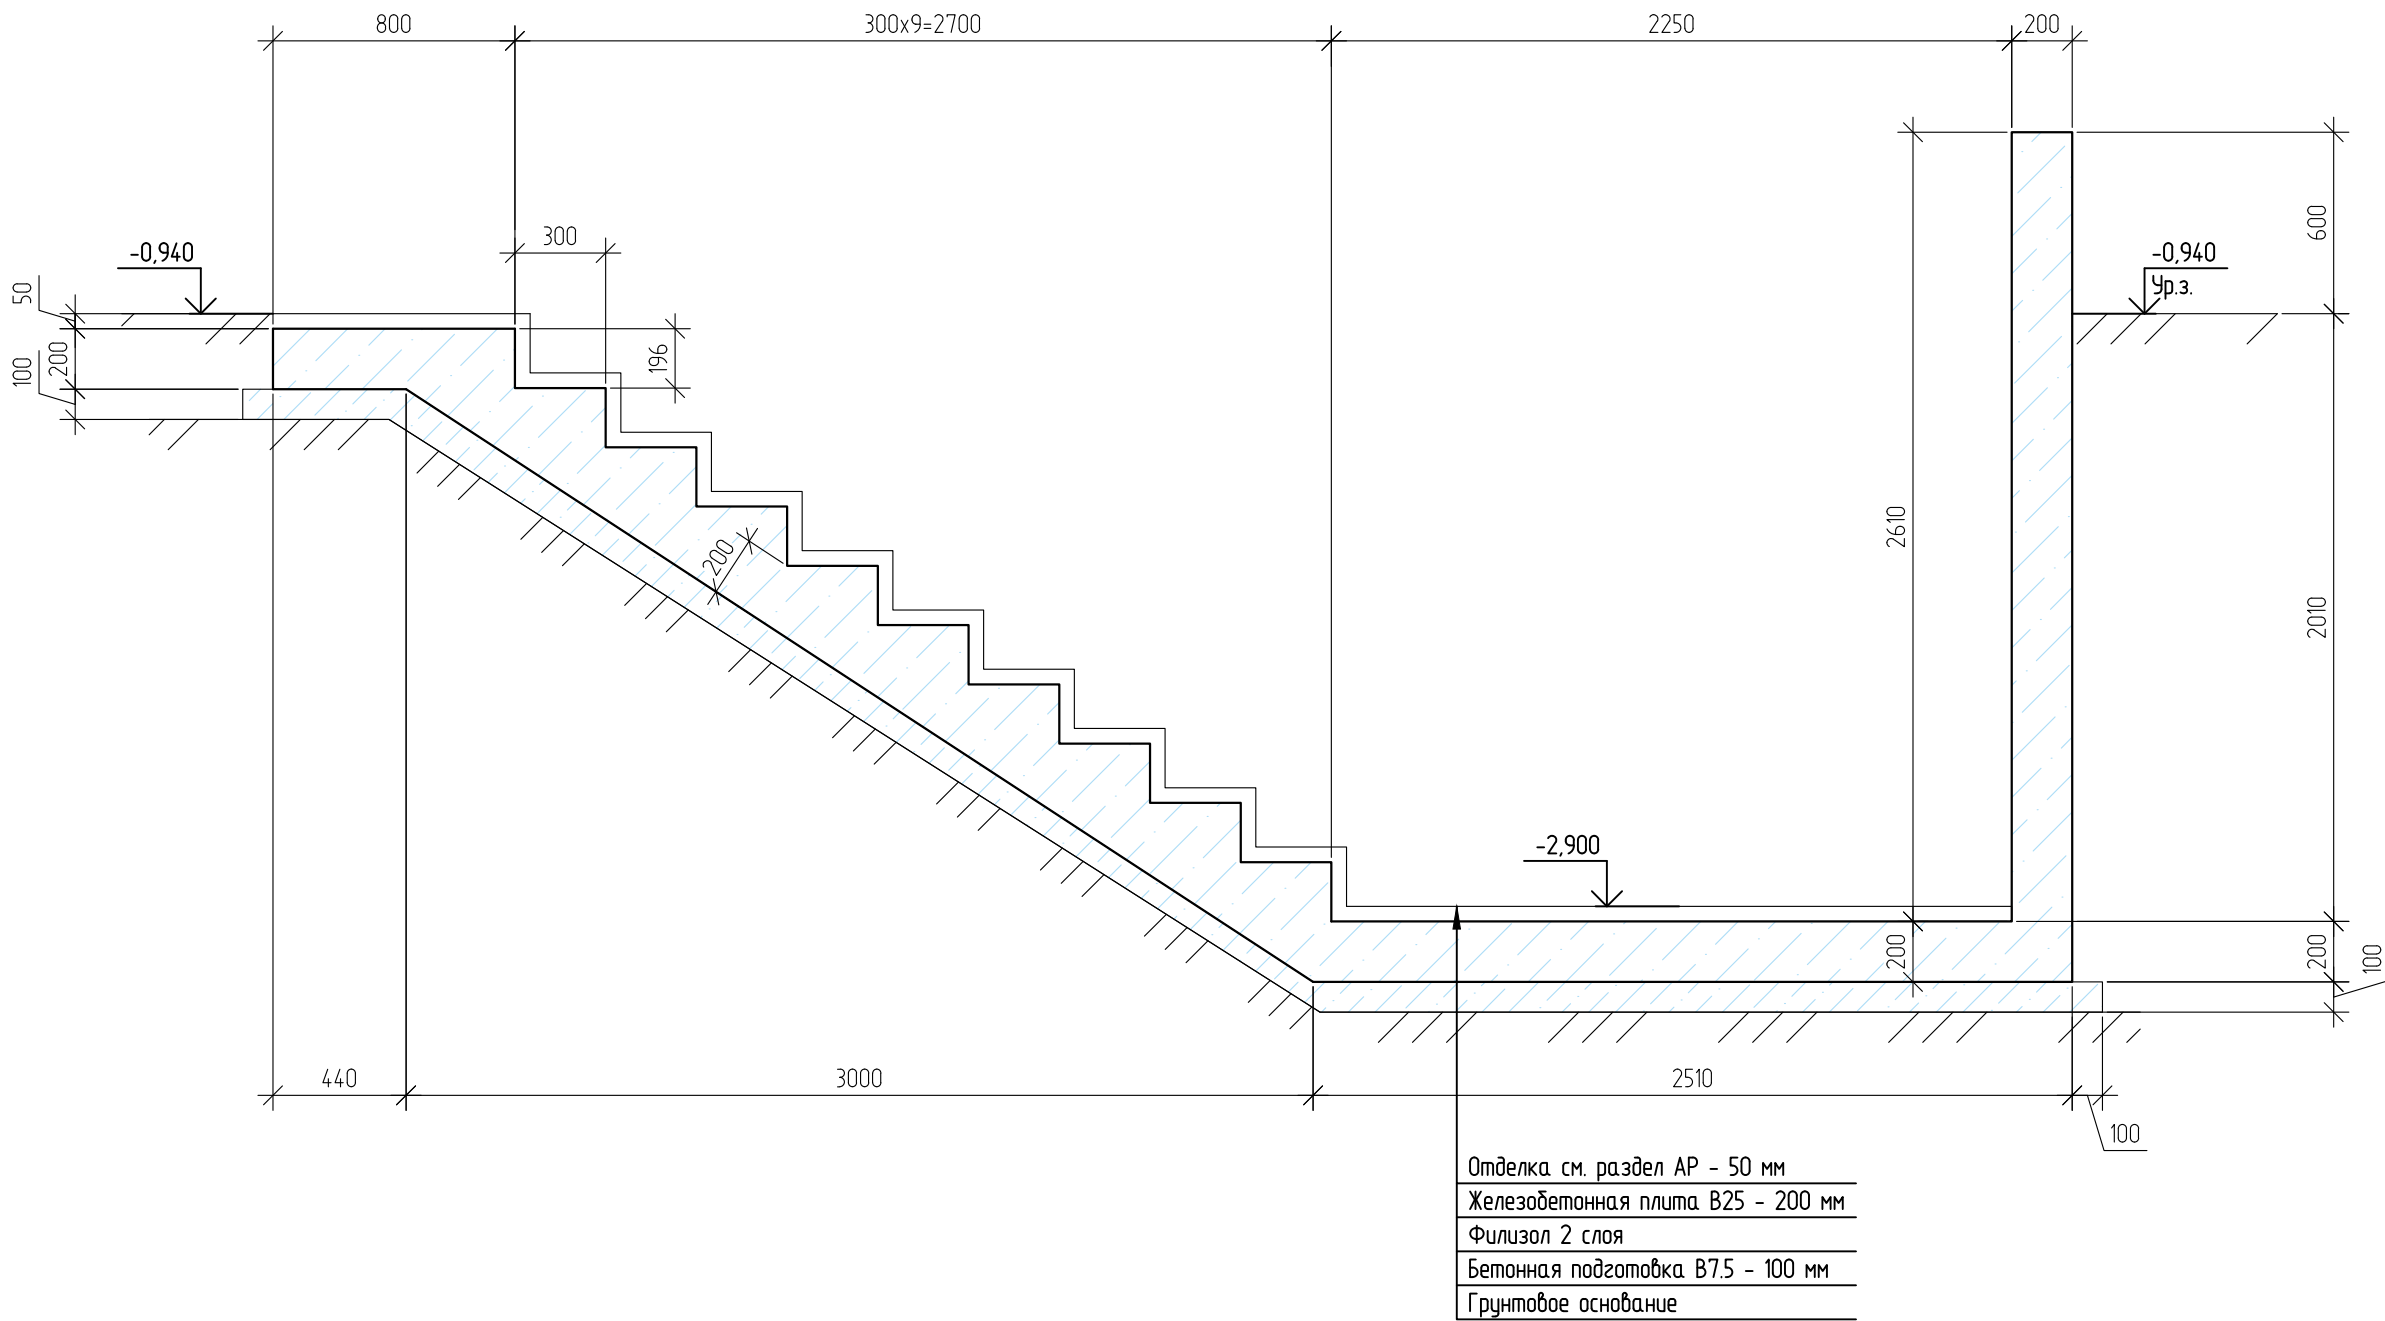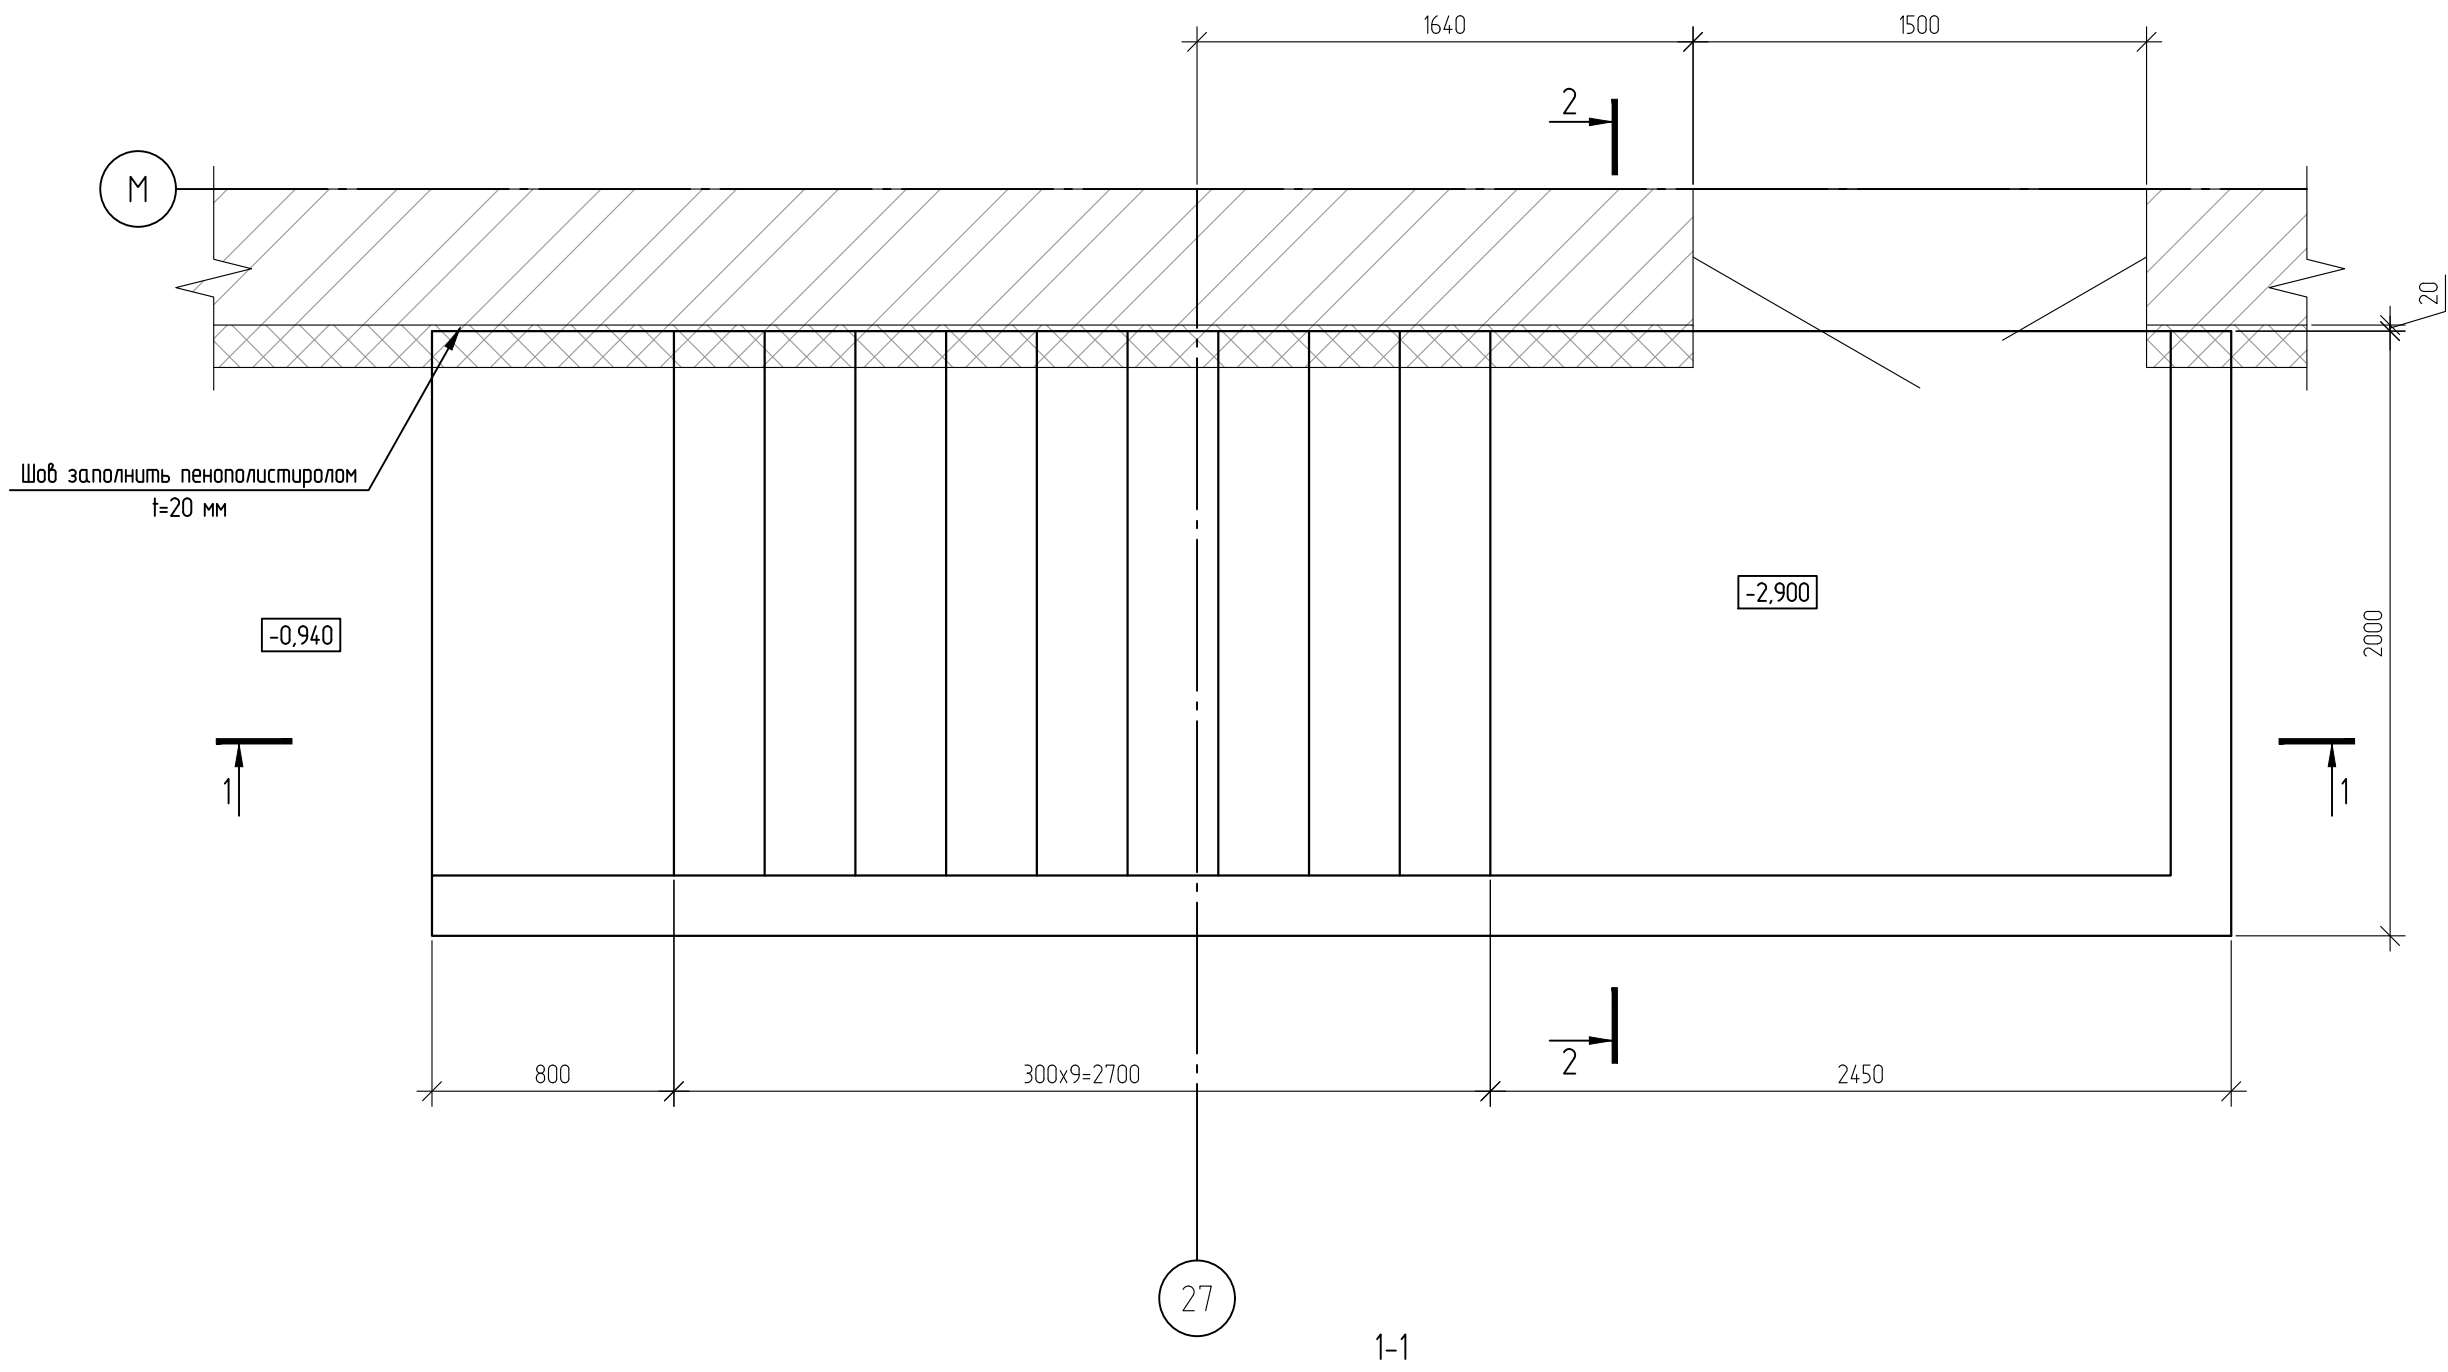

Армирование 1-1

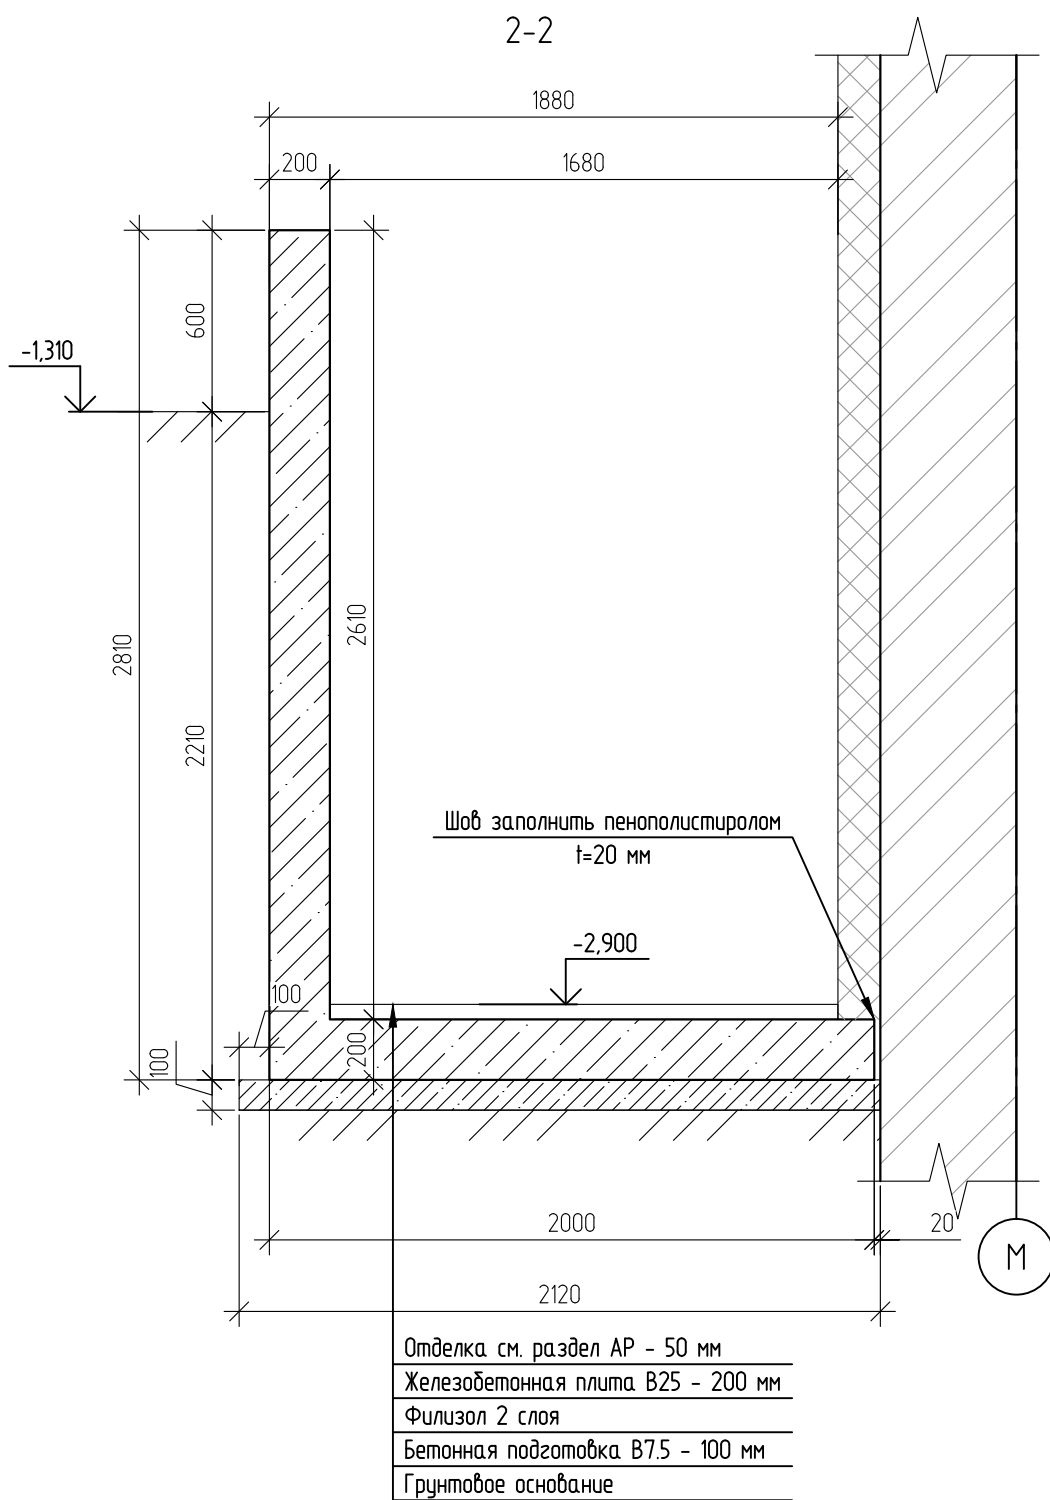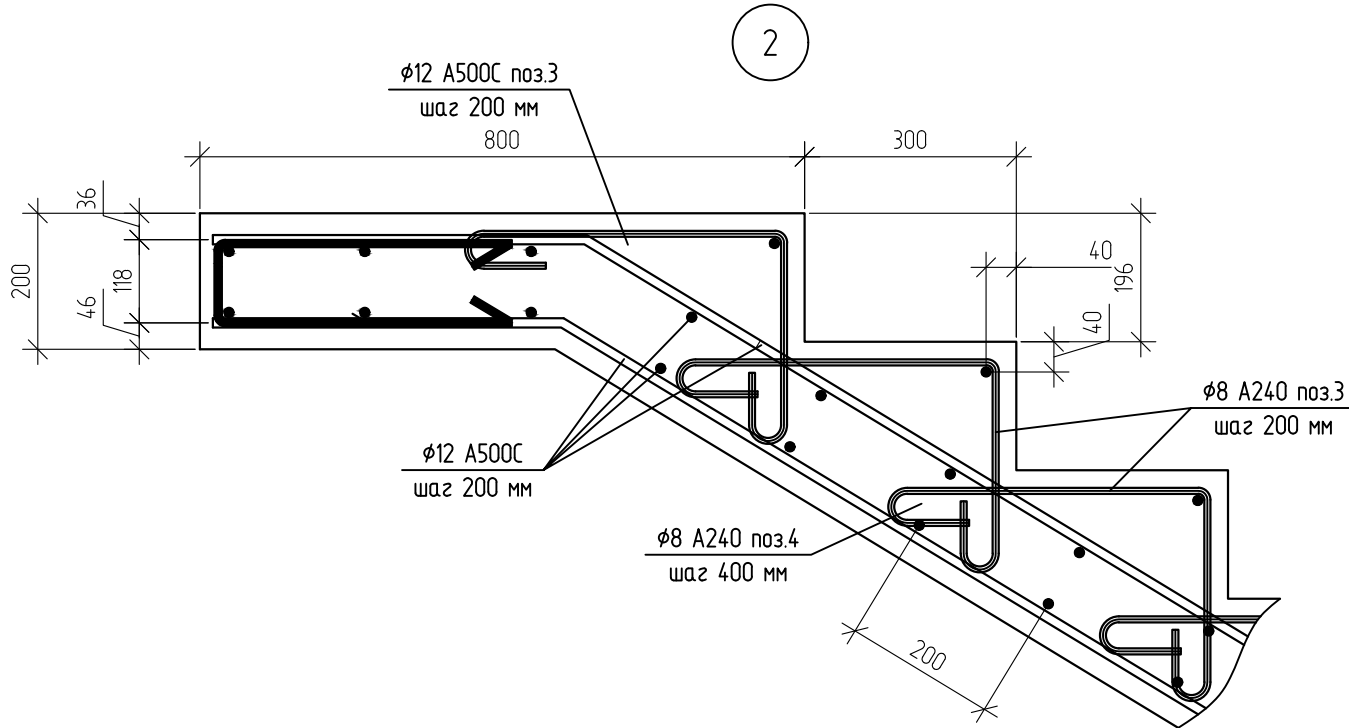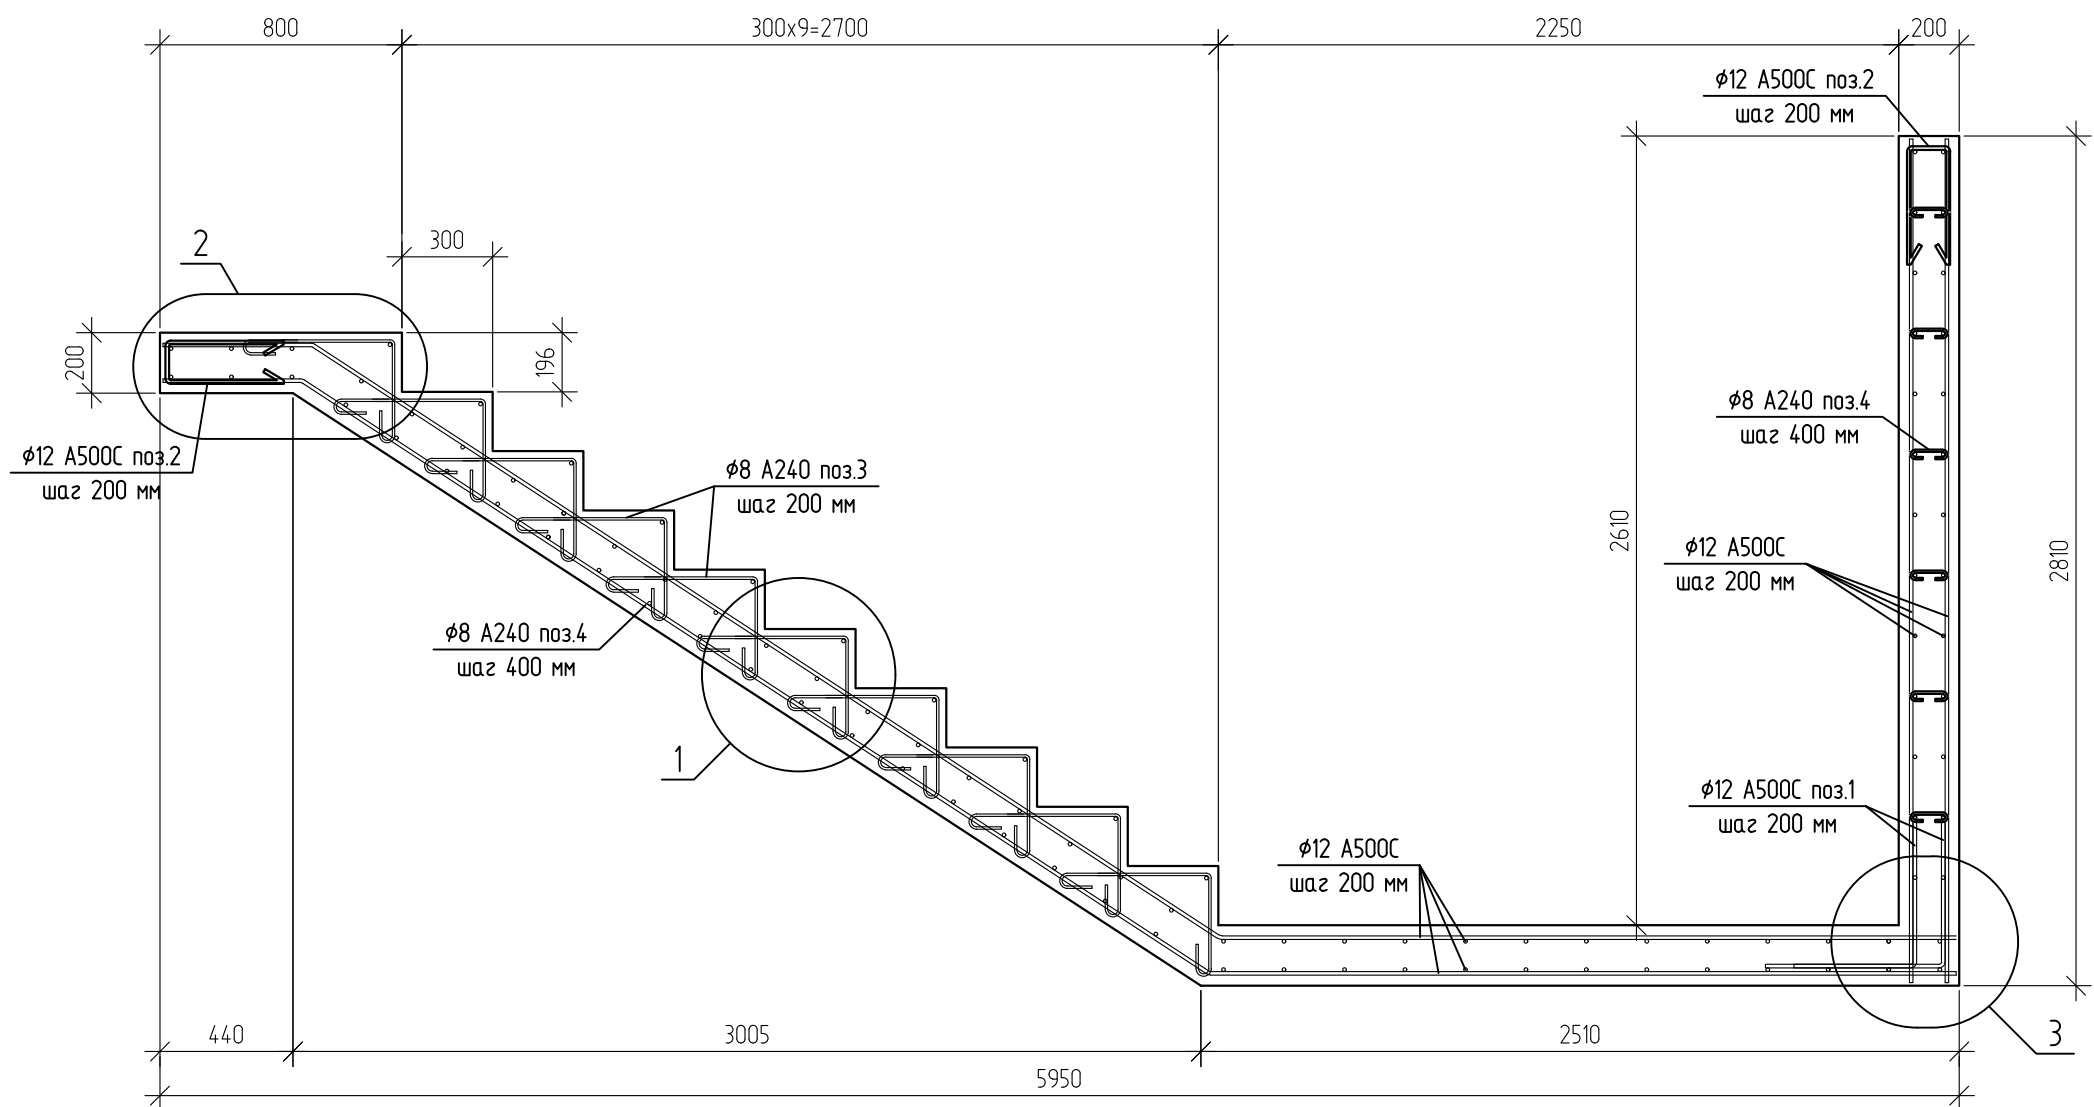

Армирование 2-2

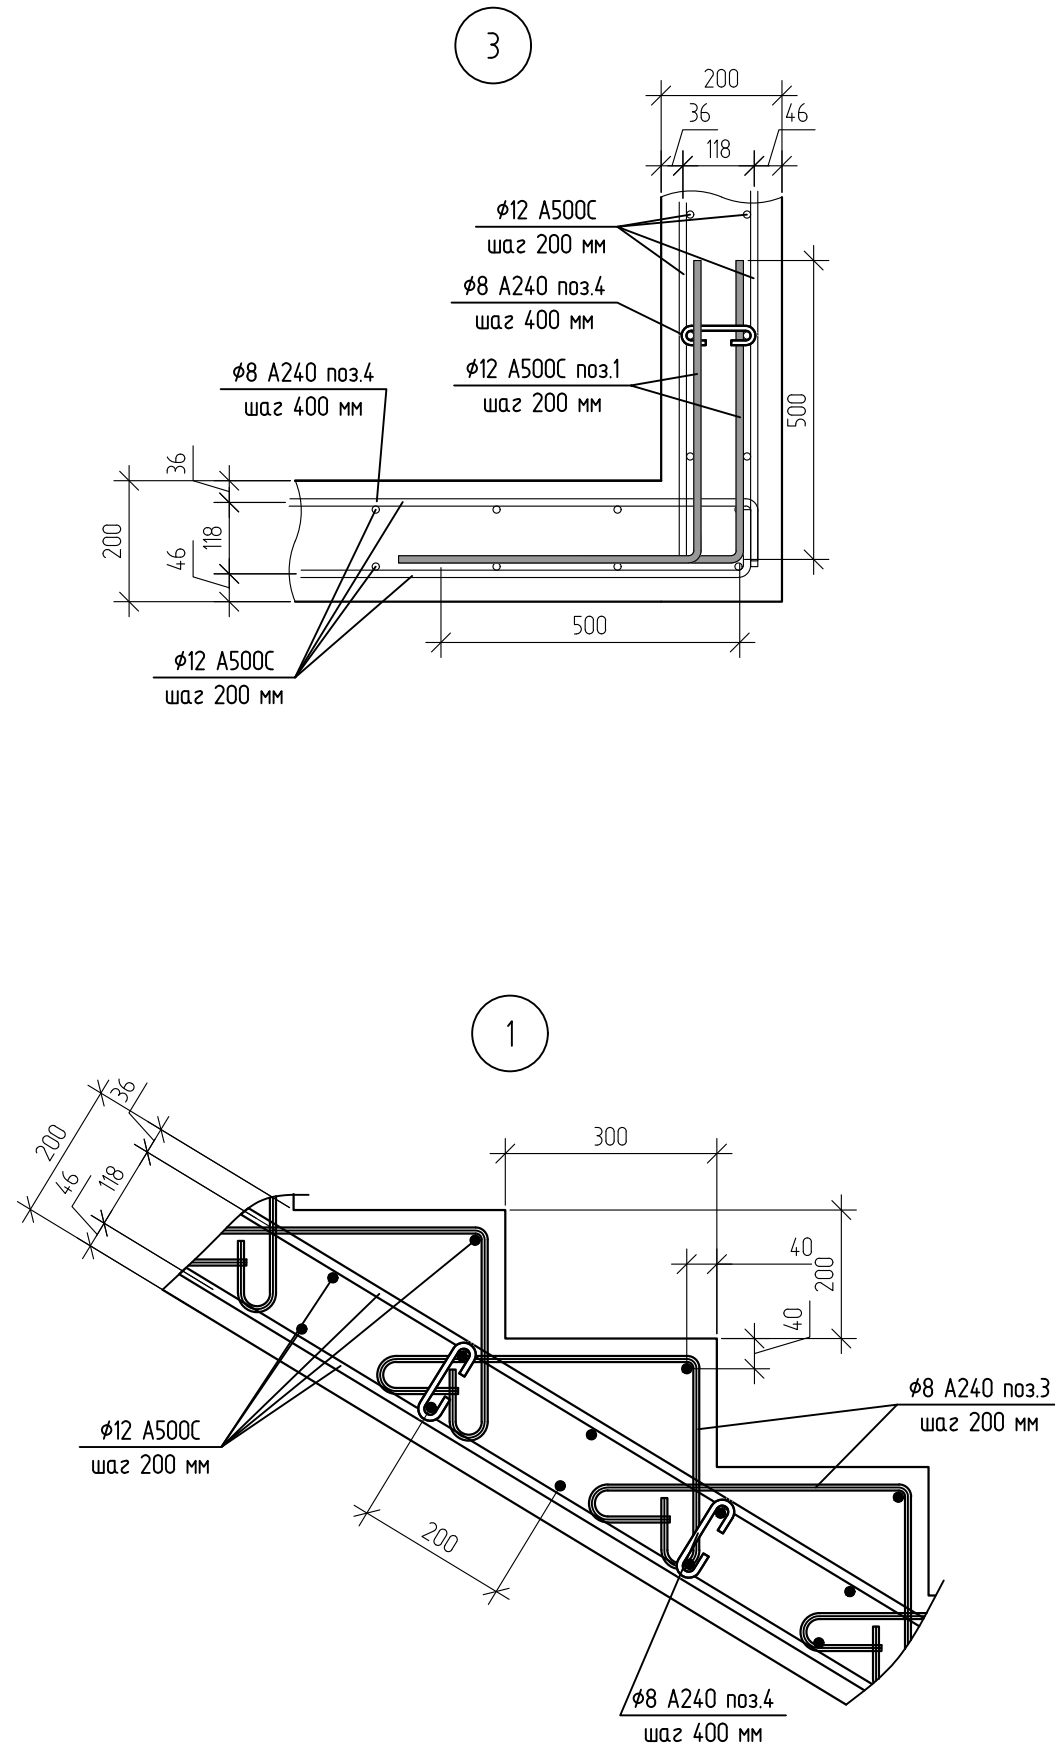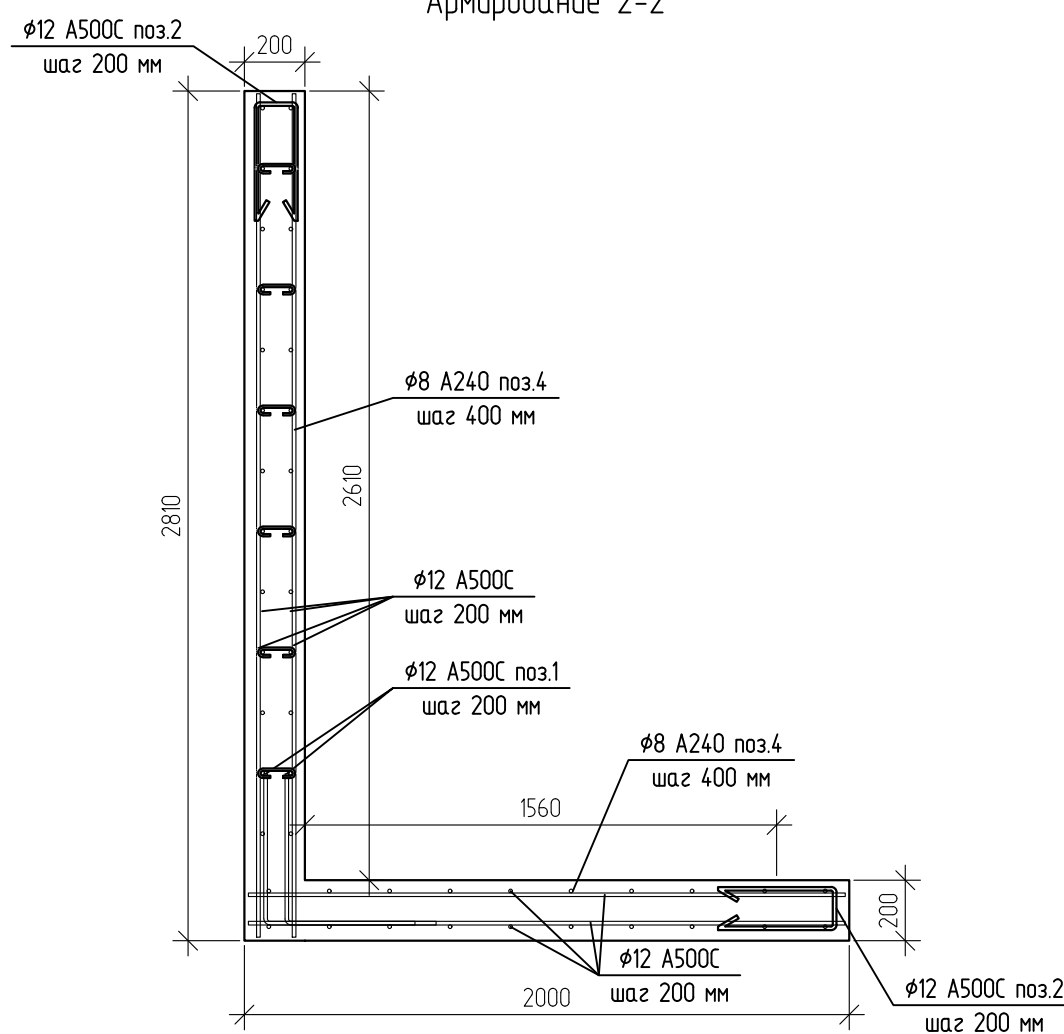

Спецификация на устройство входа в осях "27/М"

Поз.	Обозначение	Наименование	Кол.	Масса 1 дет., кг	Примеч. общ. вес, кг
	ГОСТ 34028-2016	Ø12 A500C, п.м.	660	0.888	586.08
1	ГОСТ 34028-2016	Ø12 A500C, L=1000 мм, шт	78	16	124.8
2	ГОСТ 34028-2016	Ø12 A500C, L=890 мм, шт	51	123	62.73
3	ГОСТ 34028-2016	Ø8 A240, L=920 мм, шт	100	0.36	36
4	ГОСТ 34028-2016	Ø8 A240, L=210 мм, шт	420	0.08	33.6
Материалы					
		Бетон В25, W6, F150, м³	7.21		
		Бетон В7.5, м³	15		
		Гидроизоляция, м²	14		

Ведомость деталей	
Поз.	Эскиз
1	
2	
3	
4	


Ведомость расхода стали, кг

Марка элемента	Изделия арматурные			
	Арматура класса		Всего	
	A500C	A240		
	ГОСТ 34028-2016	ГОСТ 34028-2016		
	Ø12	Ø8	Итого	
	845.23	845.23	68.64	913.87

- Фундаментную плиту, плиту площадки армировать отдельными стержнями Ø12 A500C с шагом 200x200 мм. Вся рабочая арматура соединяется в сетки с помощью вязальной проволоки. В сетках вязке подлежат пересечения стержней через одно в шахматном порядке.
- Соединение стержней по длине производить внахлест с перелупком не менее 45 диаметров стыкуемой арматуры. В одном условном сечении не более 50% стыкуемой арматуры.
- Размеры хомутов и гнутых деталей даны для справки. Данные размеры следует уточнять и корректировать по месту для соответствия нижней и верхней сеток проектному.
- Стыки смежных стержней разносить в шахматном порядке.
- Фиксаторы положения сеток (лягушки) на чертеже не показаны и в спецификации не учтены.


						708/П-24-АНО-КР					
						Капитальный ремонт общеобразовательного учреждения ГБОУ "Школа №1210" по адресу: г. Москва, ул. Хвощинская, д.32					
Изм.	Копуч	Лист	№ док.	Подп.	Дата	Конструктивные решения	Стадия	Лист	Листов	 ООО "АРТИС"	
Разработал	Горшин	4	04.26		04.26		Р	24			
Н.Контроль	Лукашова	4	04.26		04.26	Схема устройства входа в осях "27/М"					
ГИП	Зыкин	4	04.26		04.26						

Схема устройства козырька входа в осях "27/М"

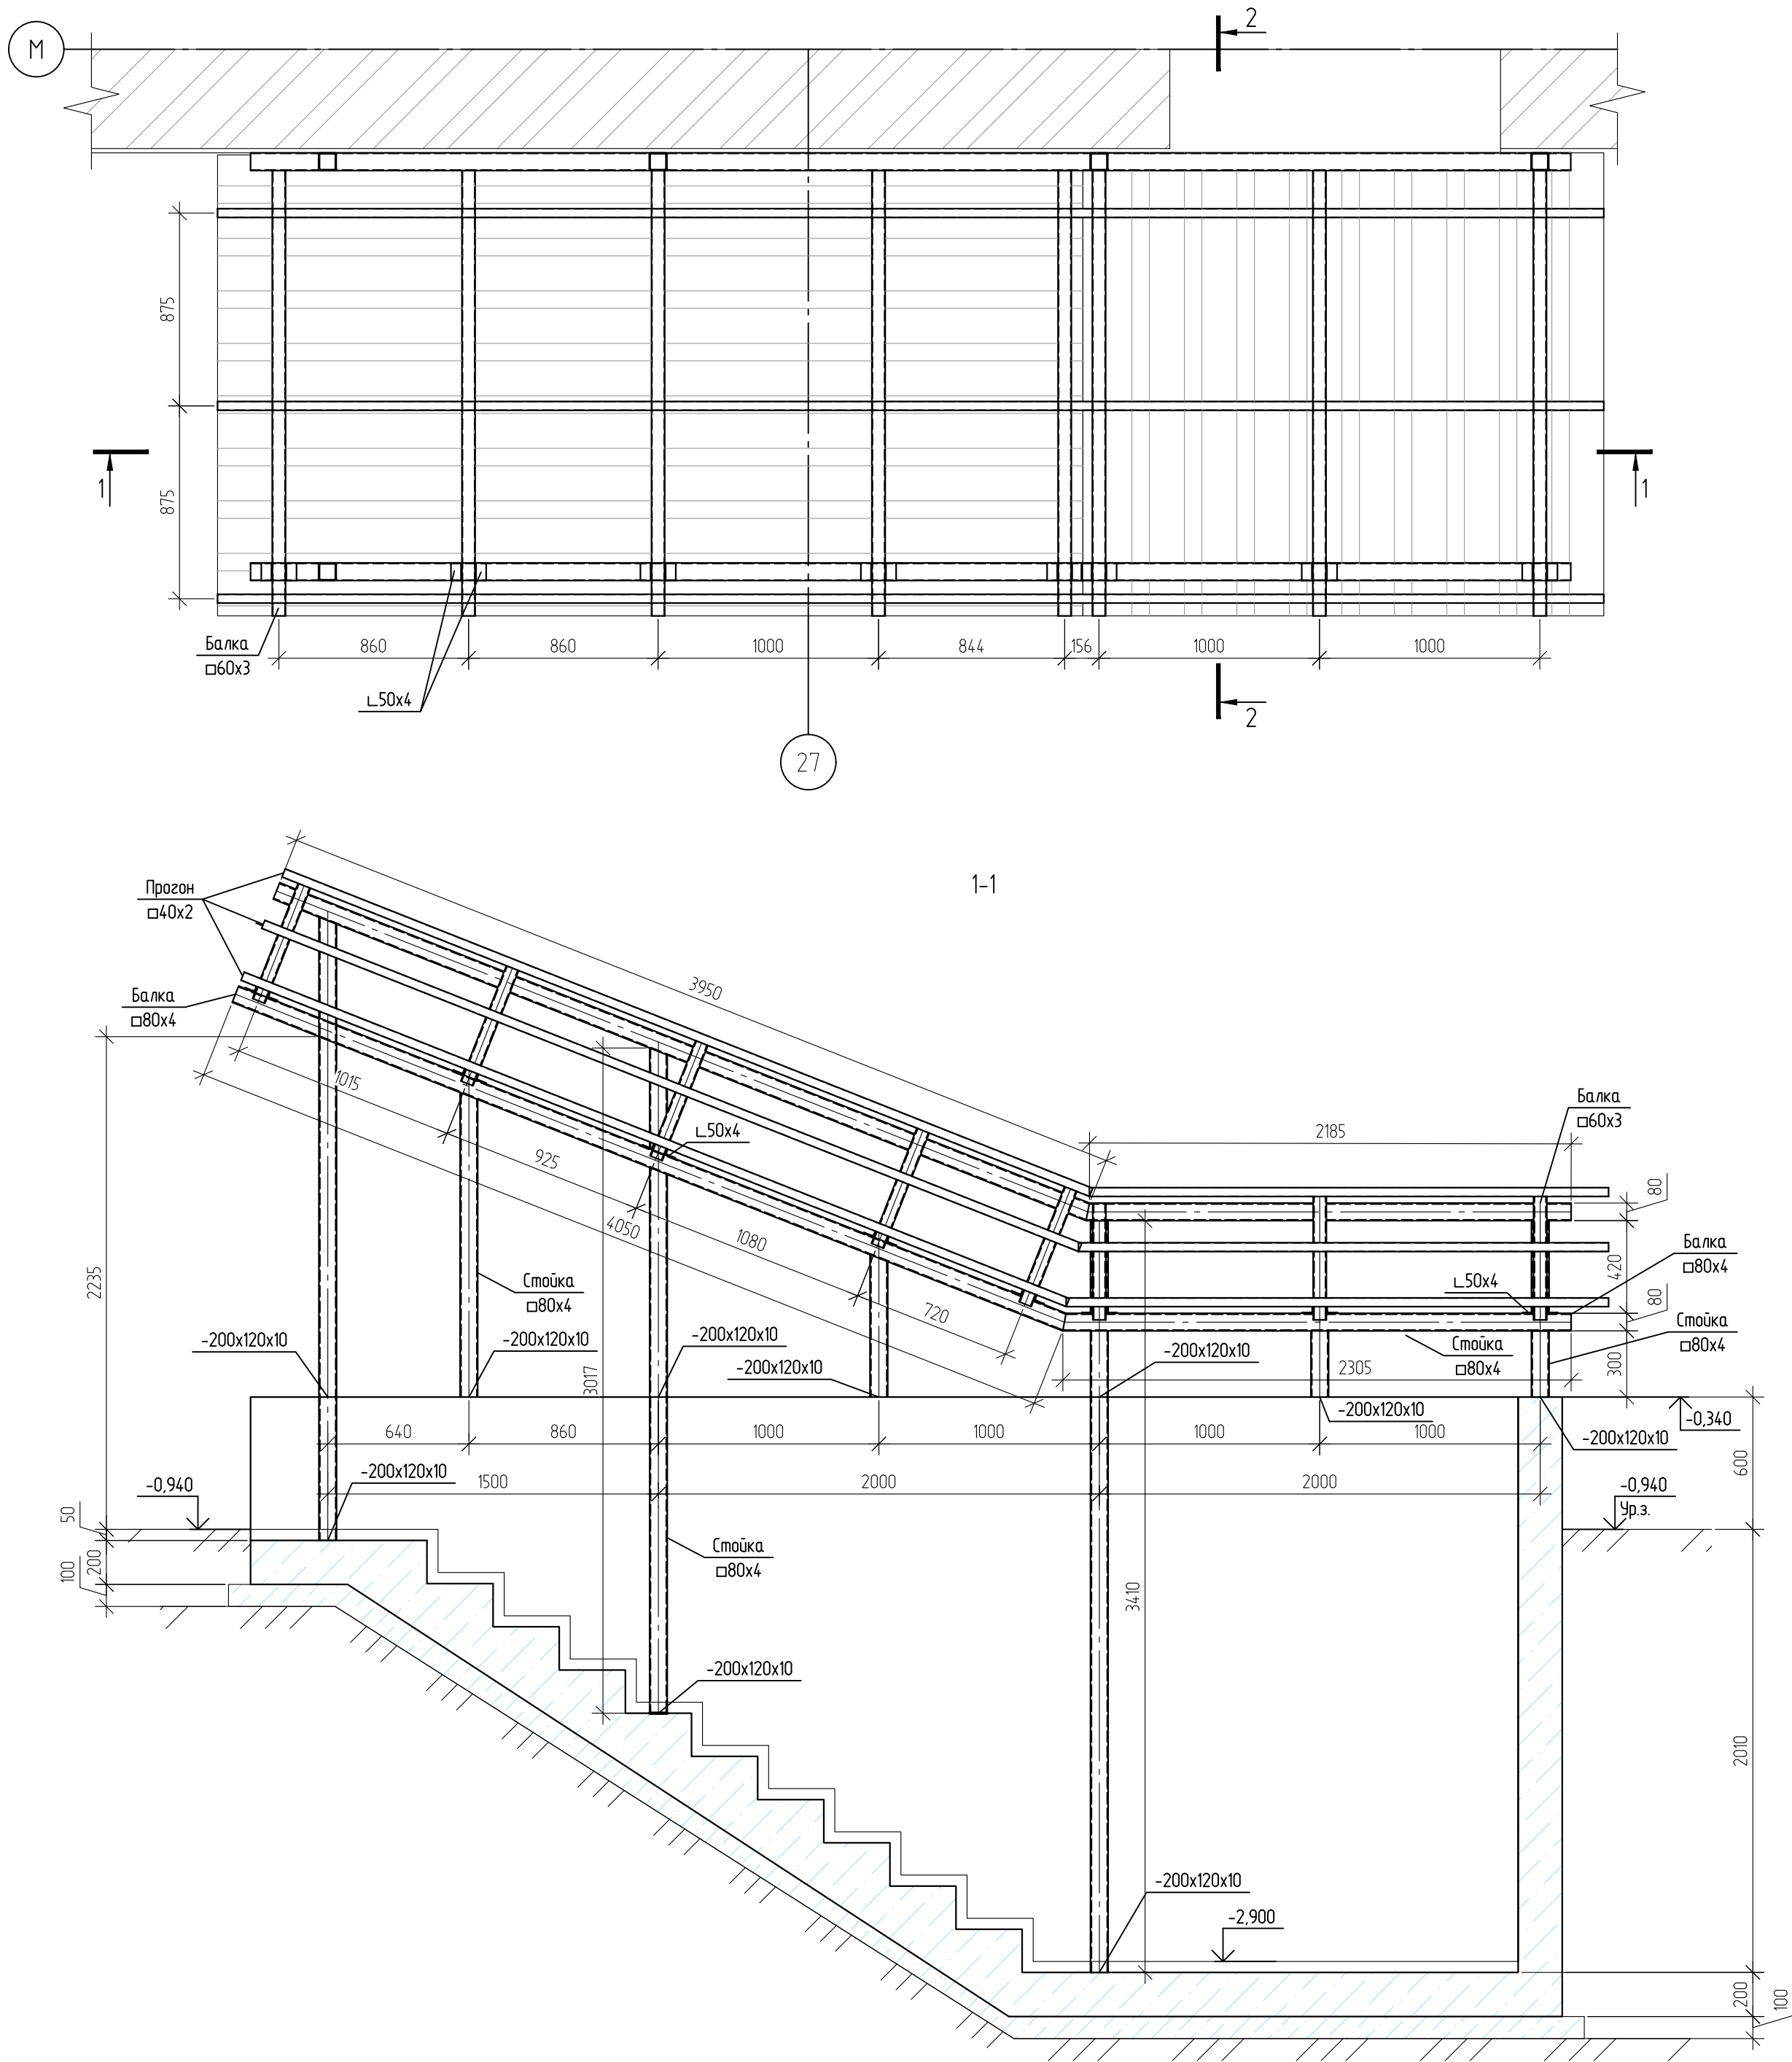

Спецификация на устройство козырька входа в осях "27/М"

Поз.	Обозначение	Наименование	Кол.	Масса 1 дет.,кг	Примеч. общ. вес кг
	ГОСТ 30245-2003	□80х4, п.м.	17	9.22	156.74
	ГОСТ 30245-2003	□60х3, п.м.	15.2	5.19	78.89
	ГОСТ 30245-2003	□40х2, п.м.	19	2.31	43.89
	ГОСТ 8509-93	Л50х4, п.м.	2	2.32	4.64
	ГОСТ 103-2006	-200х120х10, шт	12	19	22.8
		Профнастил НС-35-1000-0.6, м²	12		
		Анкер распорный М12, шт	24		







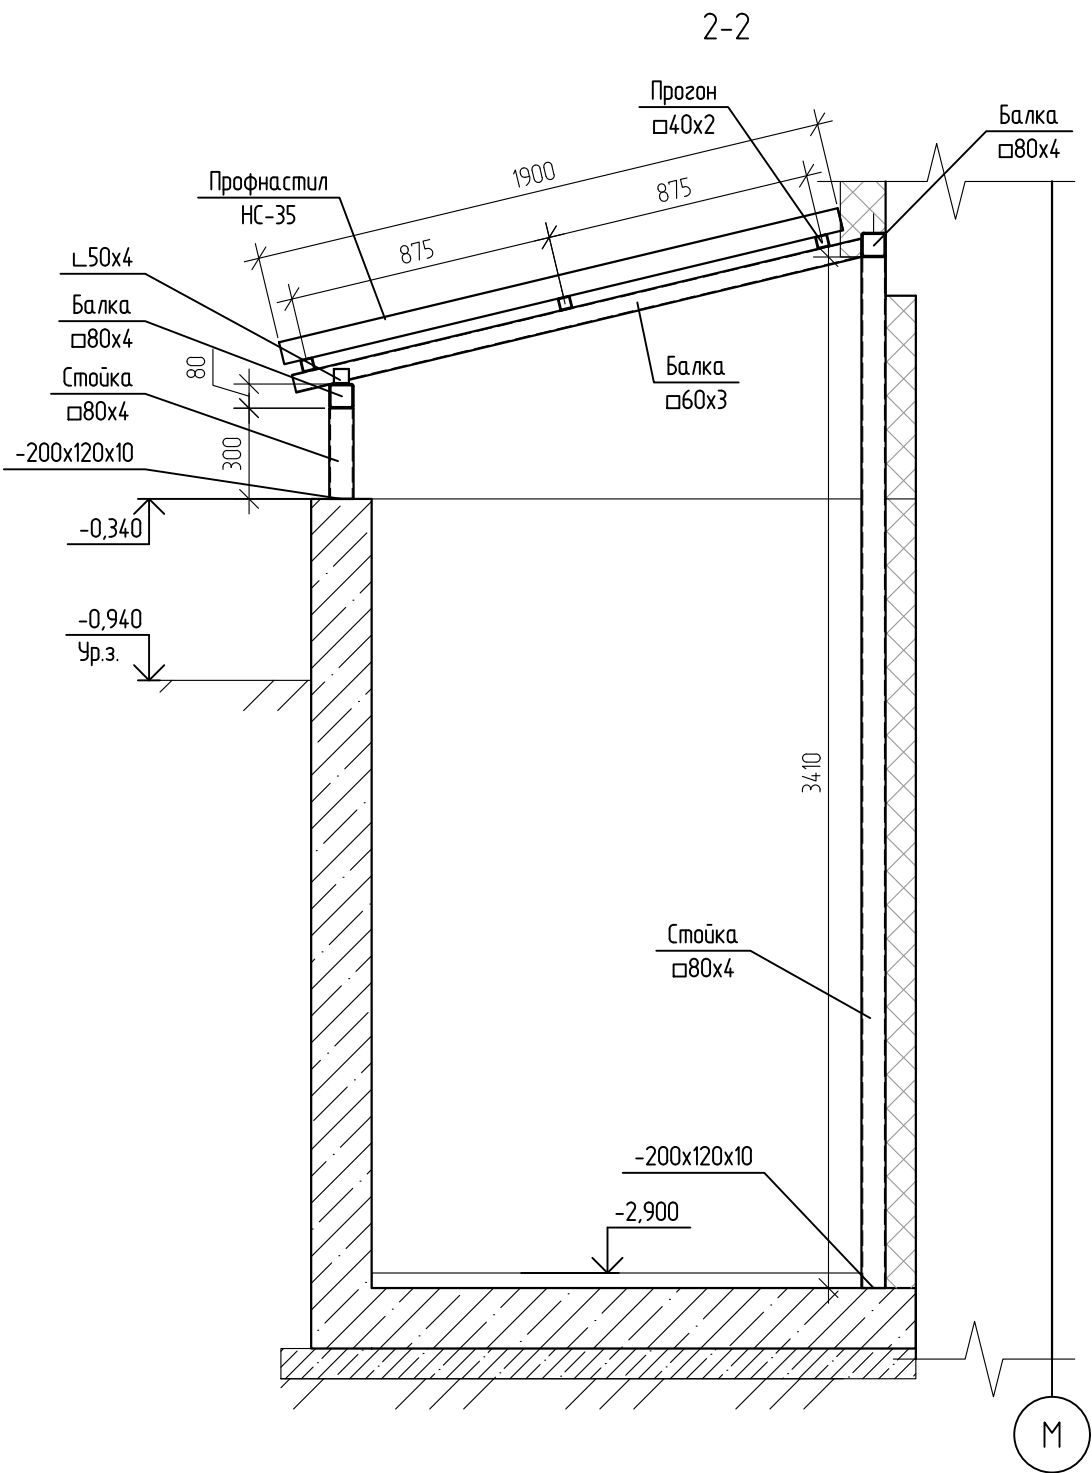


Примечание:
1. Материал для металлических конструкций - сталь С235 по ГОСТ 27772-2020;
2. Сварные соединения - по ГОСТ 5264-80. Электродом Э-42 по ГОСТ 9467-75*;
3. Минимальный катет сварного шва - по наименьшей толщине свариваемых элементов;
4. Все конструкции окрасить одним слоем эмали ПФ-115 ГОСТ 6465-76 по двум слоям грунта ГФ-021 ГОСТ 25129-82.


Согласовано	
Взам. инв. №	
Подп. и дата	
Инв. № подл.	

708/П-24-АНО-КР					
Капитальный ремонт общеобразовательного учреждения ГБОУ "Школа №1210" по адресу: г. Москва, ул. Живописная, д.32					
Изм.	Колуч.	Лист	№ док.	Подп.	Дата
Разработал	Торшин	04.26			
ГАП	Фролова	04.26			
Конструктивные решения				Стадия	Лист
				Р	25
Схема устройства козырька входа в осях "27/М"				ООО "АРТИС"	
Н.Контроль	Лукашова	04.26			
ГИП	Зыкин	04.26			

Инв. № подл.	Подп. и дата	Взам. инв. №	Согласовано

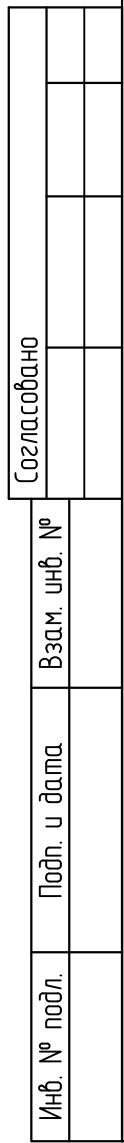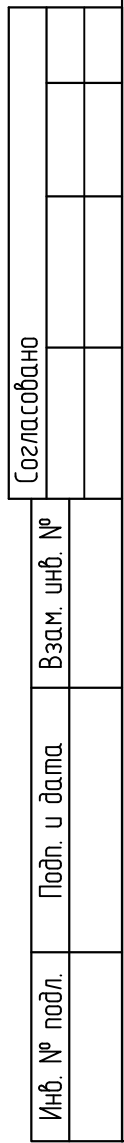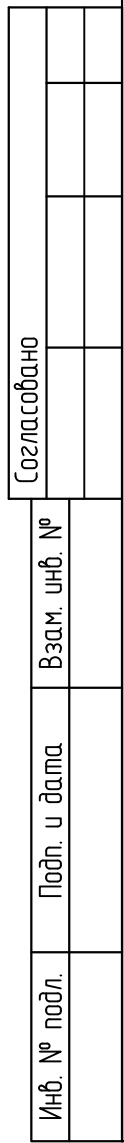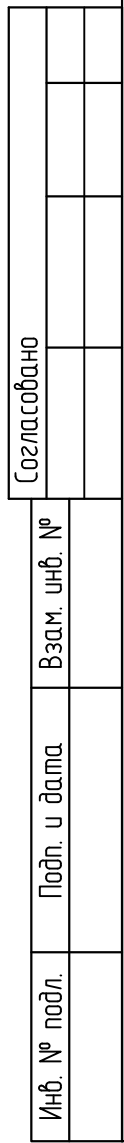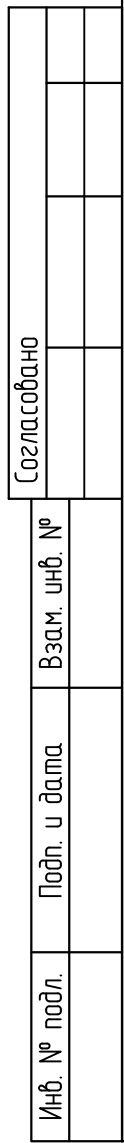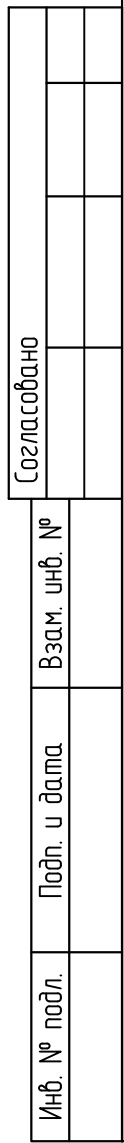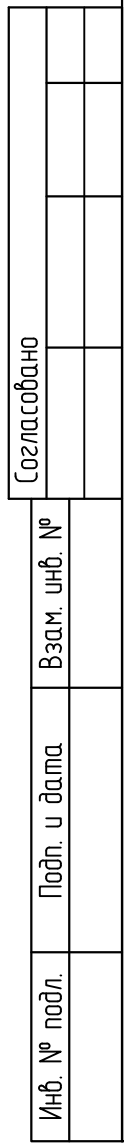

Инв. № подл.	Подп. и дата	Взам. инв. №	Согласовано

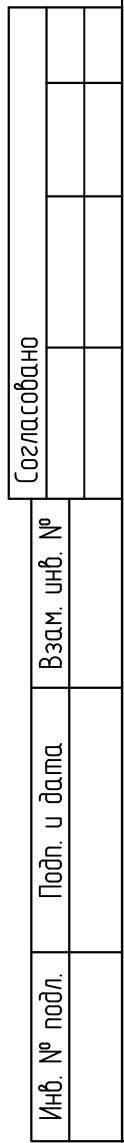

Инв. № подл.	Подп. и дата	Взам. инв. №	Согласовано




Инв. № подл.	Подп. и дата	Взам. инв. №	Согласовано

Инв. № подл.	Подп. и дата	Взам. инв. №	Согласовано

Схема устройства козырька входа в осях "1/Г-Д"



Спецификация на устройство козырька входа в осях "1-2/Г-Д"

Поз.	Обозначение	Наименование	Кол.	Масса 1 м.п. кг	Примеч. общ. вес кг
	ГОСТ 30245-2003	□80х4, п.м.	6	9.22	55.32
	ГОСТ 30245-2003	□60х3, п.м.	9.8	5.19	50.86
	ГОСТ 30245-2003	□40х2, п.м.	15.9	2.31	36.73
	ГОСТ 103-2006	-100х100х6, шт	8	0.5	4
	ГОСТ 103-2006	-200х120х10, шт	8	1.9	15.2
		Профнастил НС-35-1000-0.6, м²	11		
		Анкер распорный М12, шт	16		


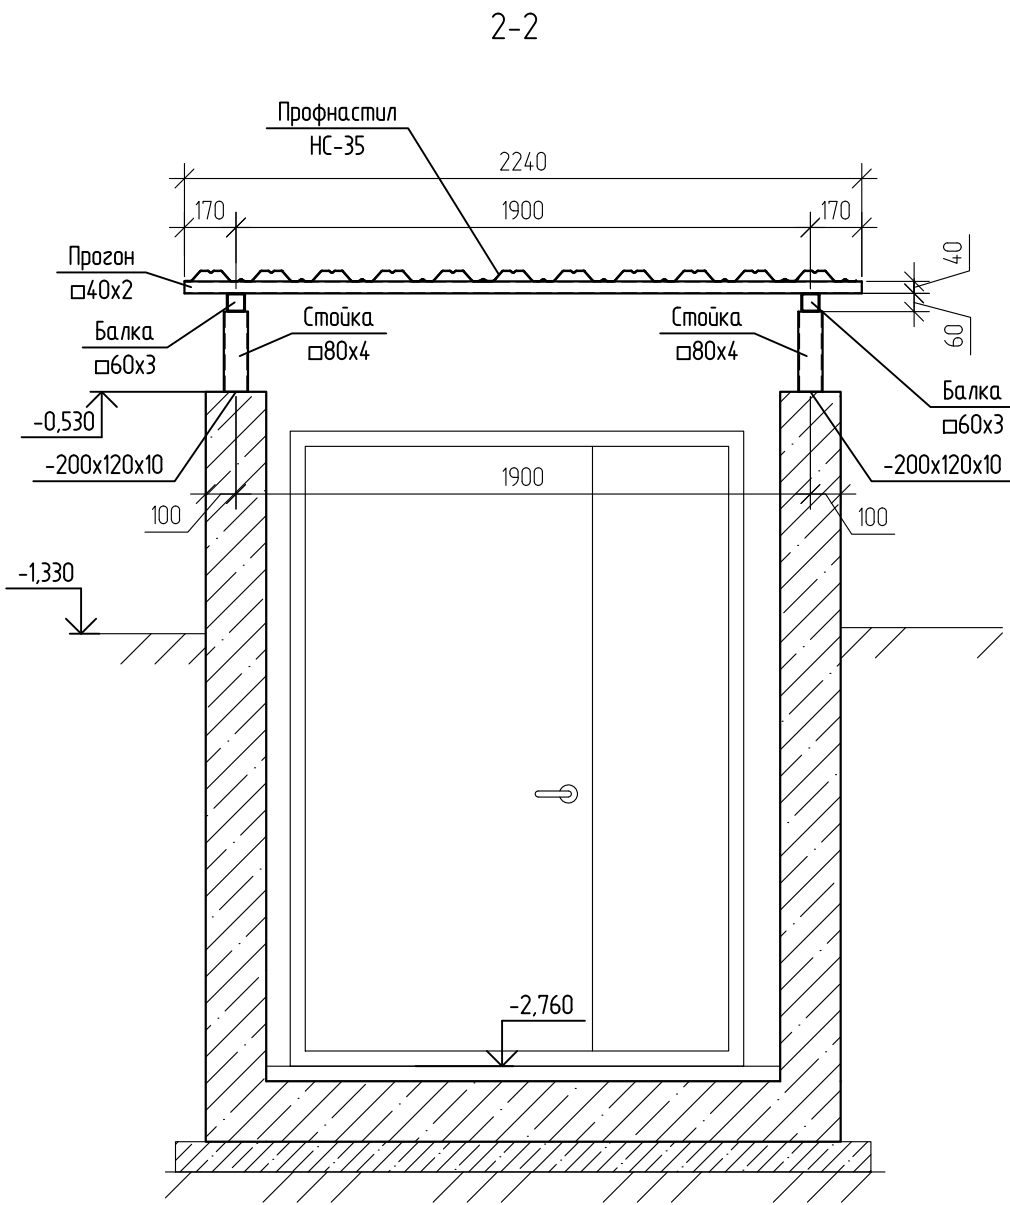
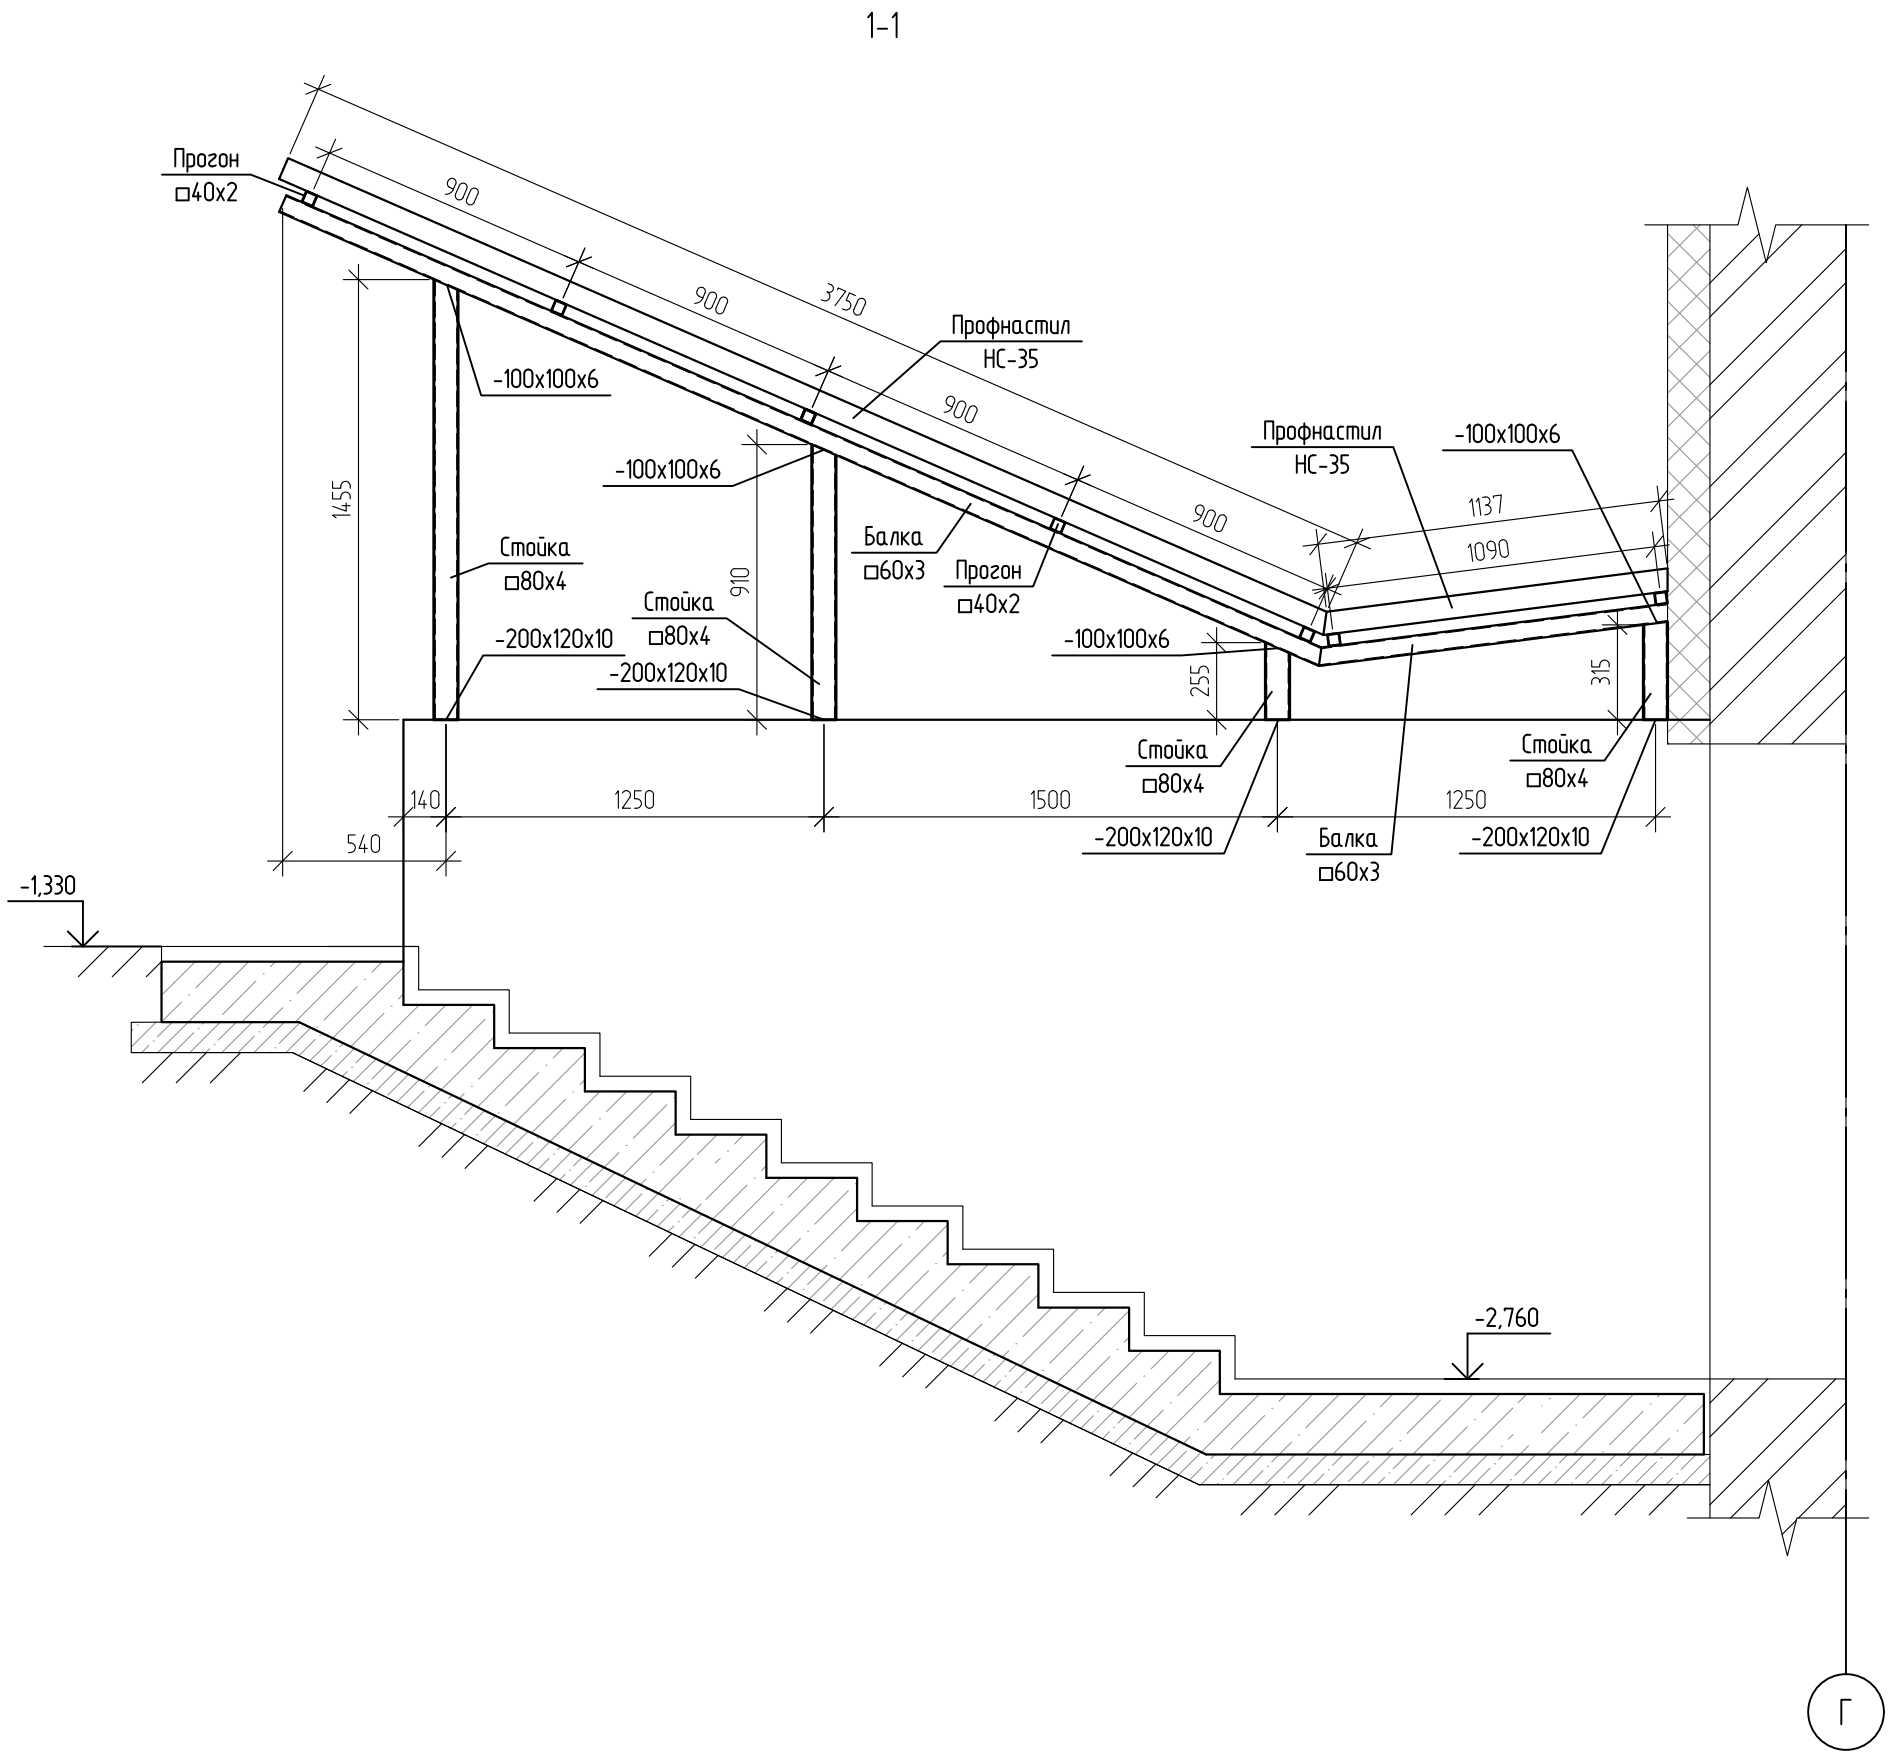
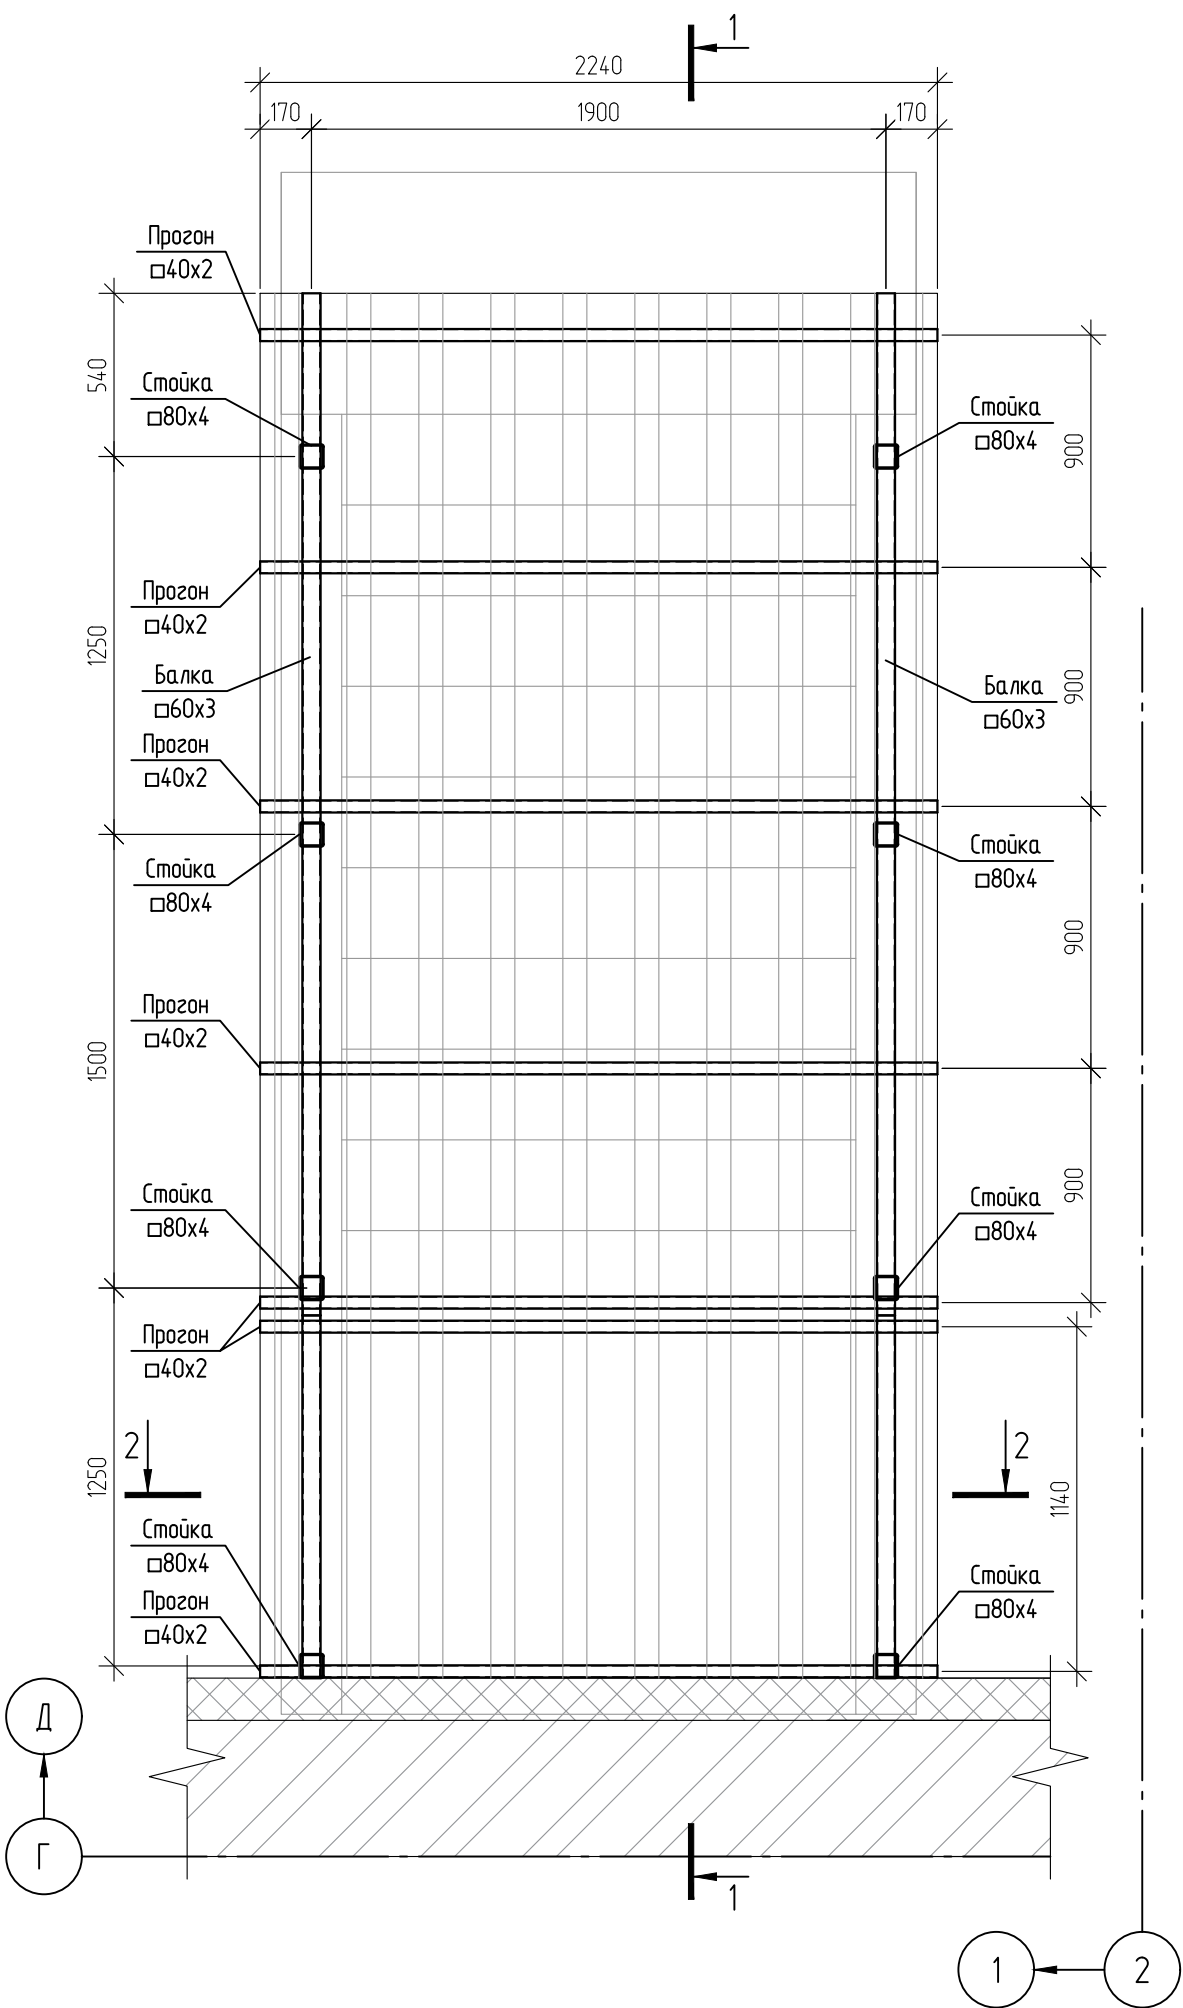


Примечание:
1. Материал для металлических конструкций - сталь С235 по ГОСТ 27772-2020;
2. Сварные соединения - по ГОСТ 5264-80. Электродам Э-42 по ГОСТ 9467-75*;
3. Минимальный катет сварного шва - по наименьшей толщине свариваемых элементов;
4. Все конструкции окрасить одним слоем эмали ПФ-115 ГОСТ 6465-76 по двум слоям грунта ГФ-021 ГОСТ 25129-82.

						708/П-24-АНО-КР			
						Капитальный ремонт общеобразовательного учреждения ГБОУ "Школа №1210" по адресу: г. Москва, ул. Живописная, д.32			
Изм.	Колуч.	Лист	№ док.	Подп.	Дата	Конструктивные решения	Стадия	Лист	Листов
Разработал	Торшин				04.26		Р	27	
ГАП	Фролова				04.26				
Н.Контроль	Лукашова				04.26	Схема устройства входа в осях "1-2/Г-Д"		комплексное проектирование промышленных и гражданских объектов ООО "АРТИС"	
ГИП	Зыкин				04.26				

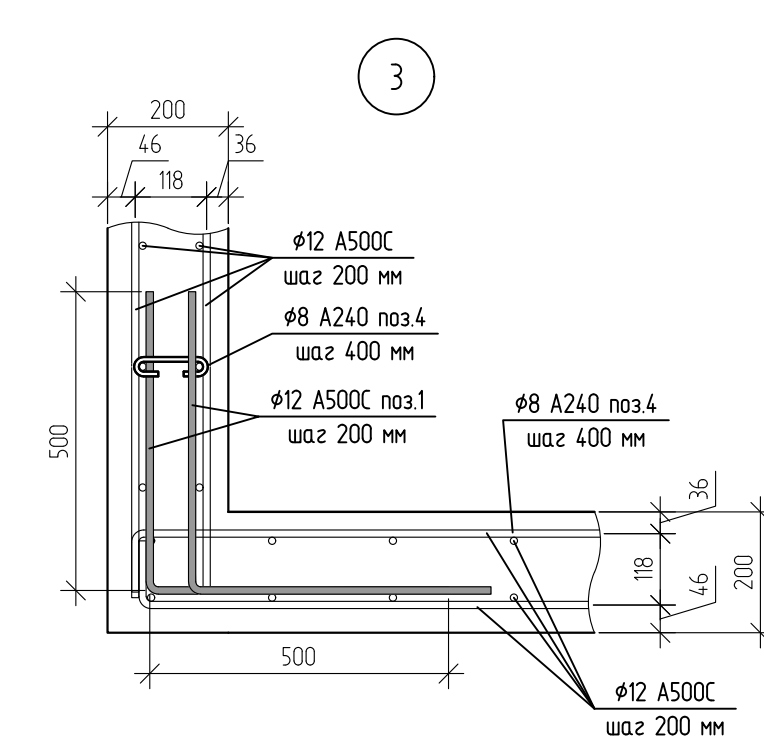
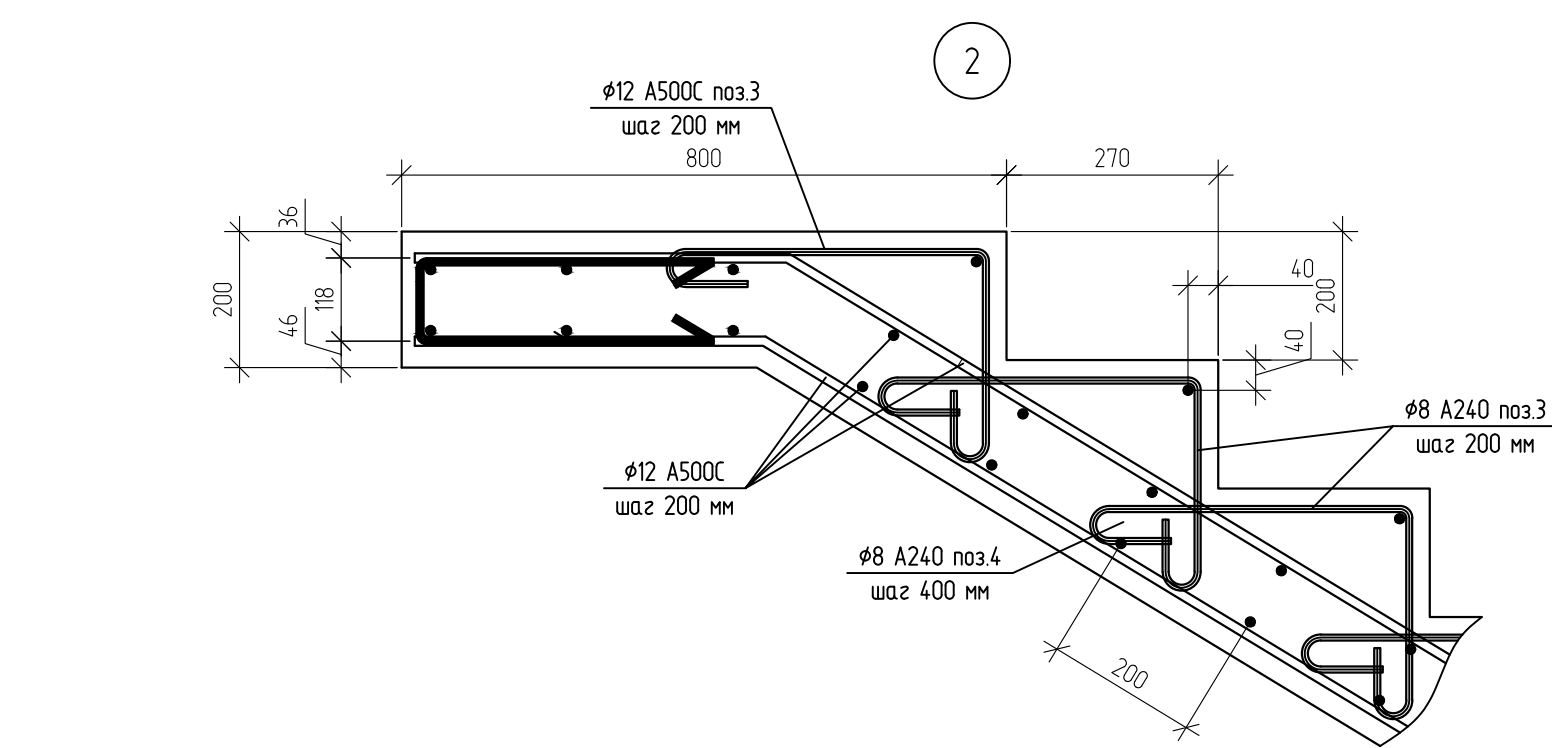


Ведомость деталей	
Поз.	Эскиз
1	
2	
3	
4	

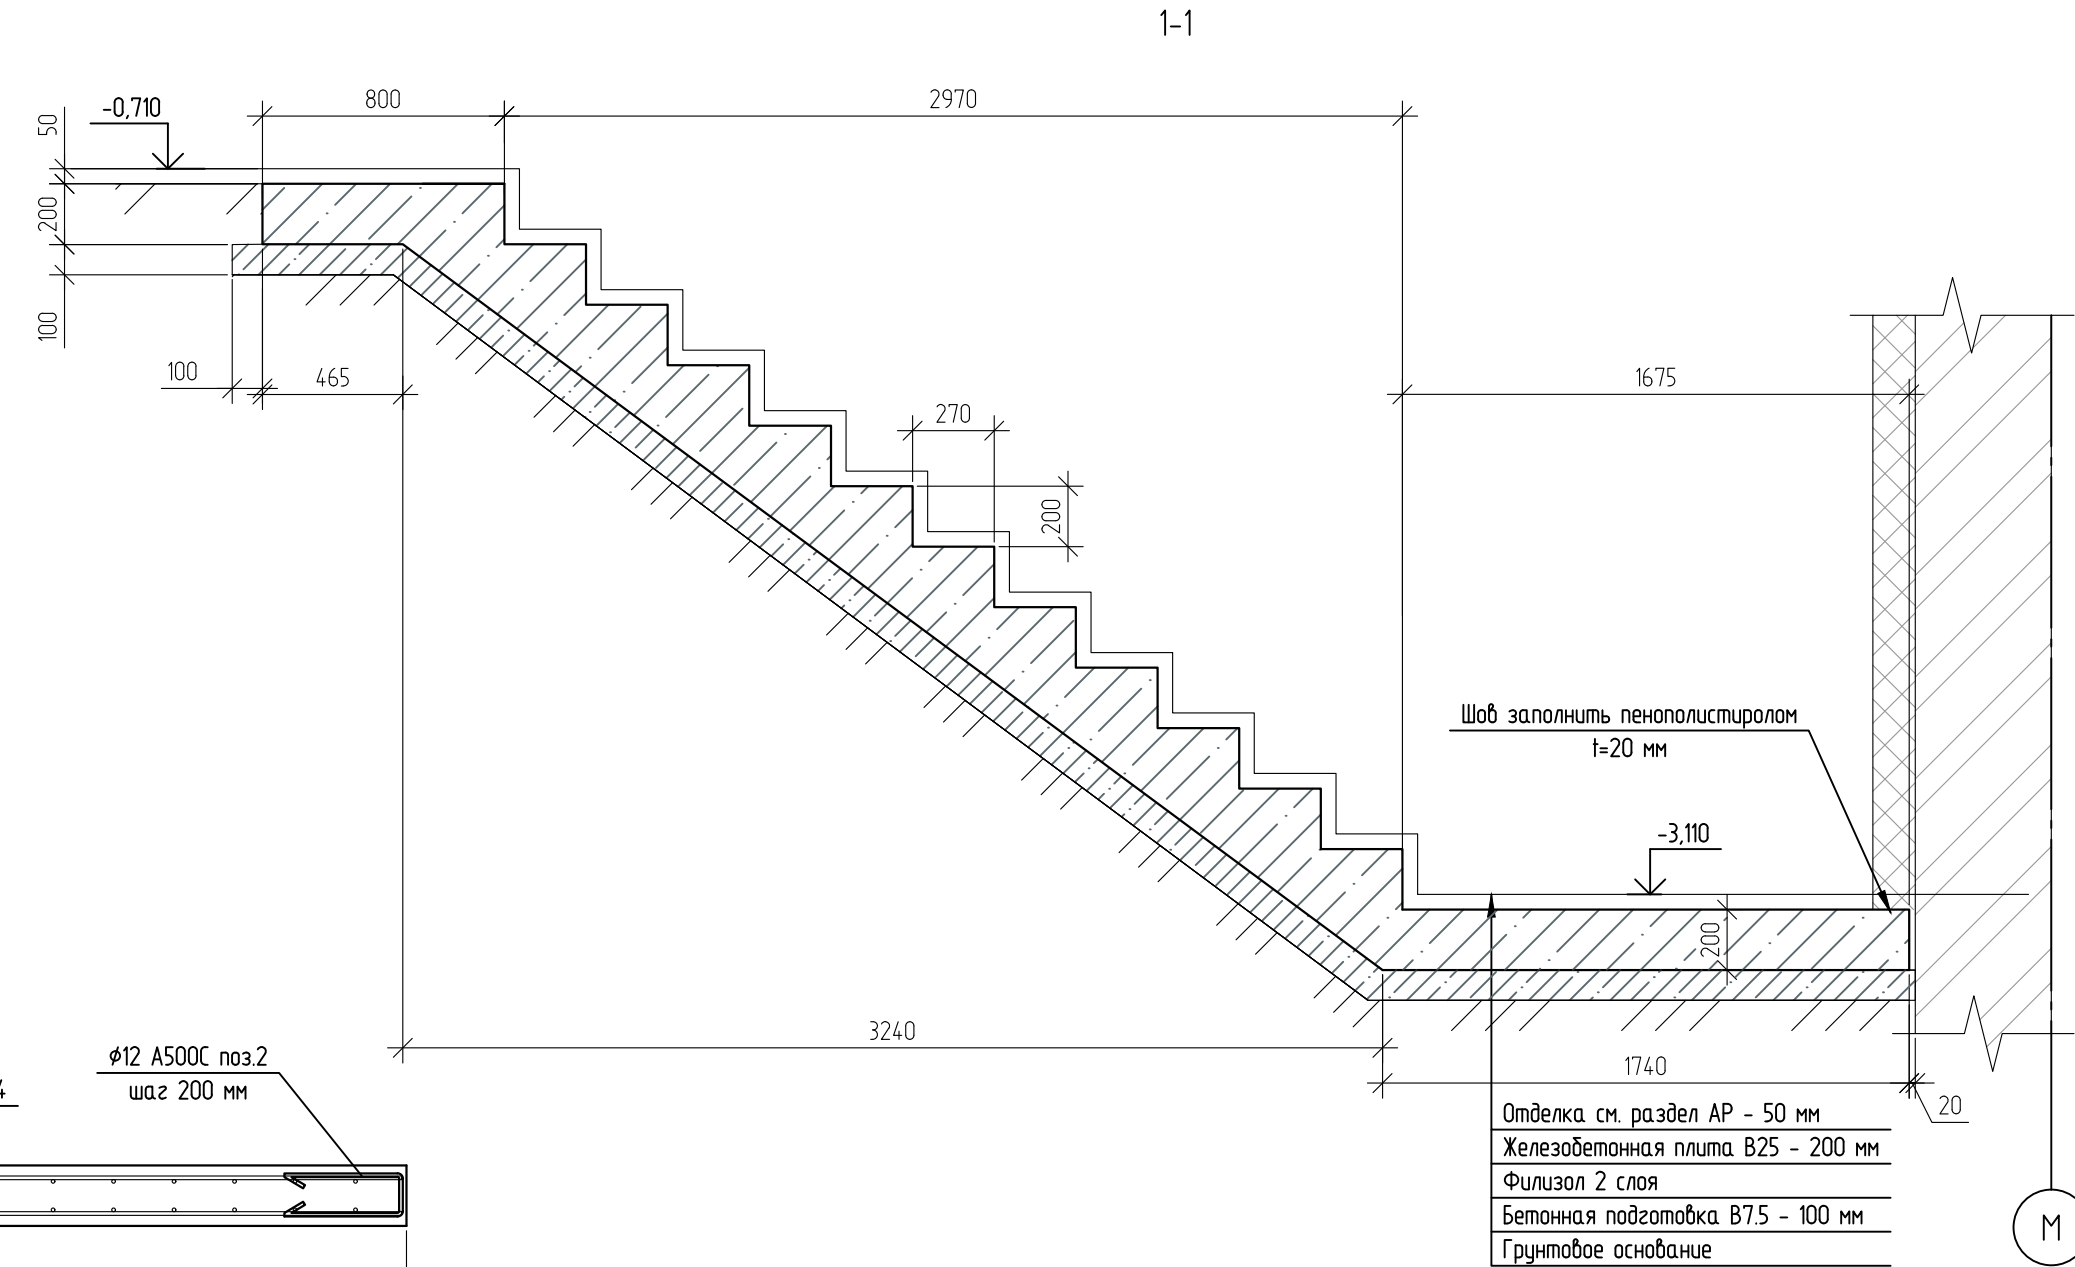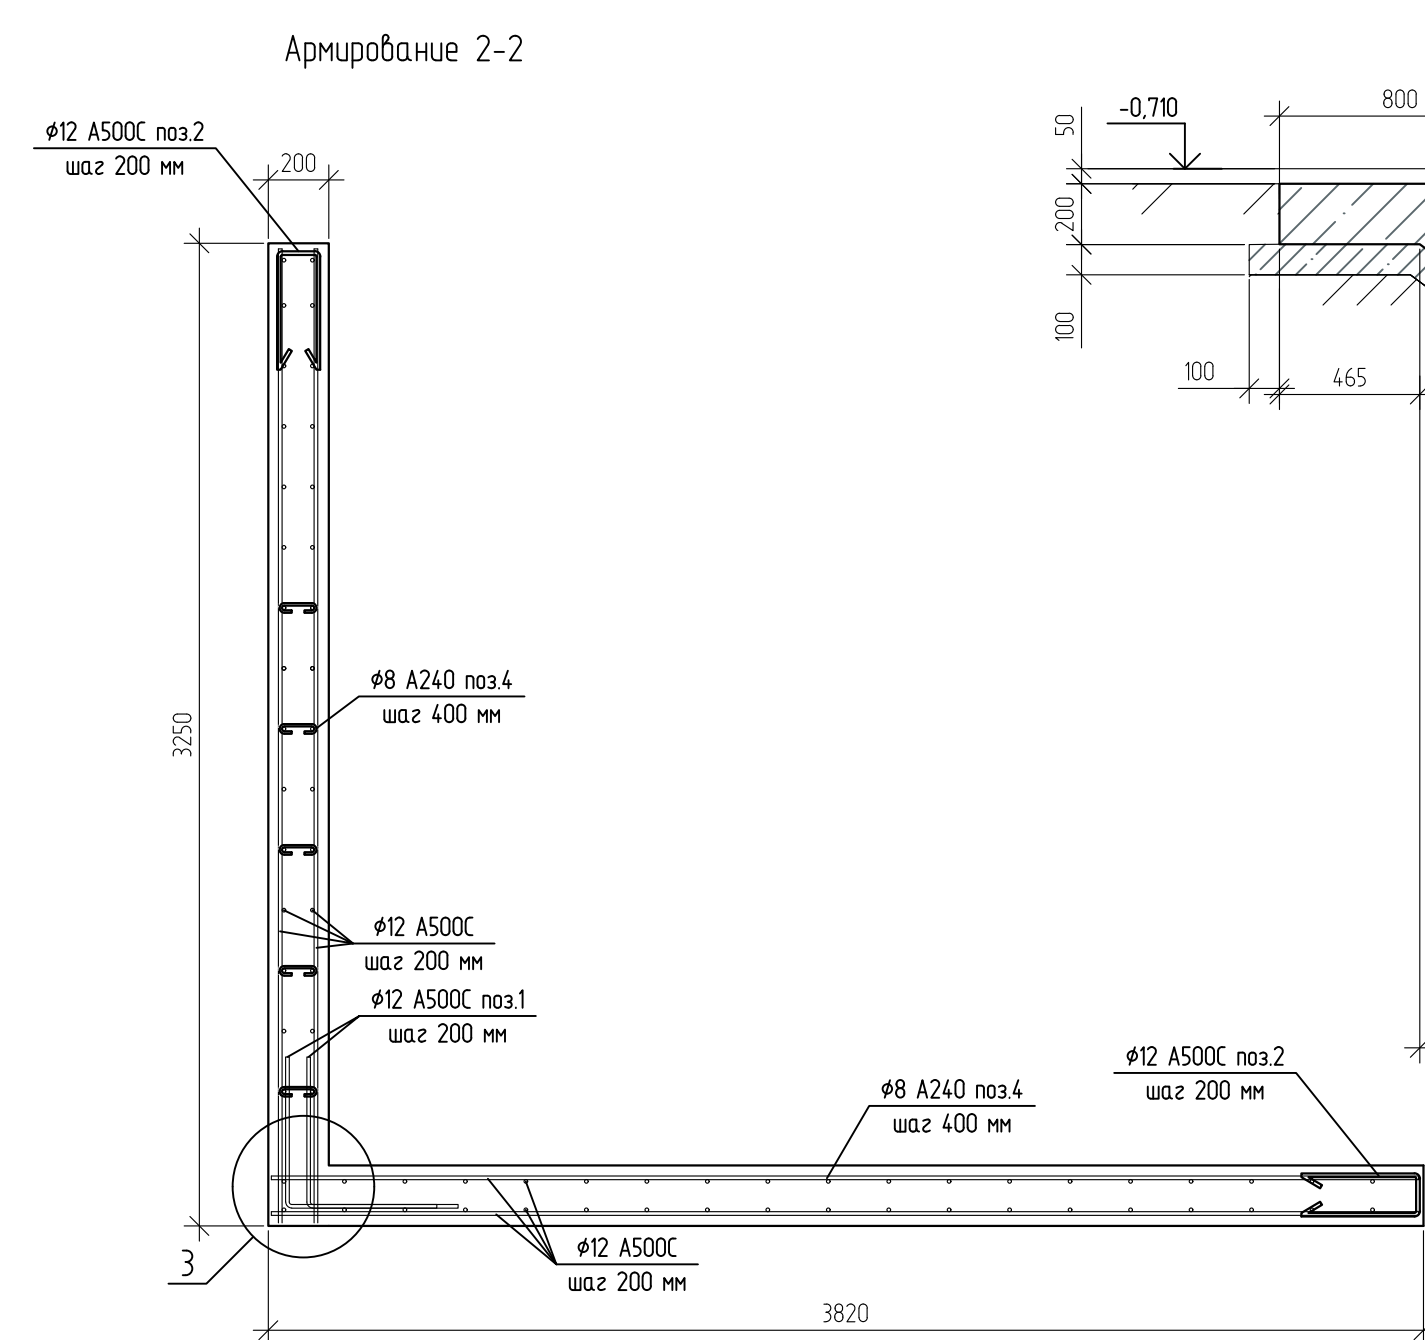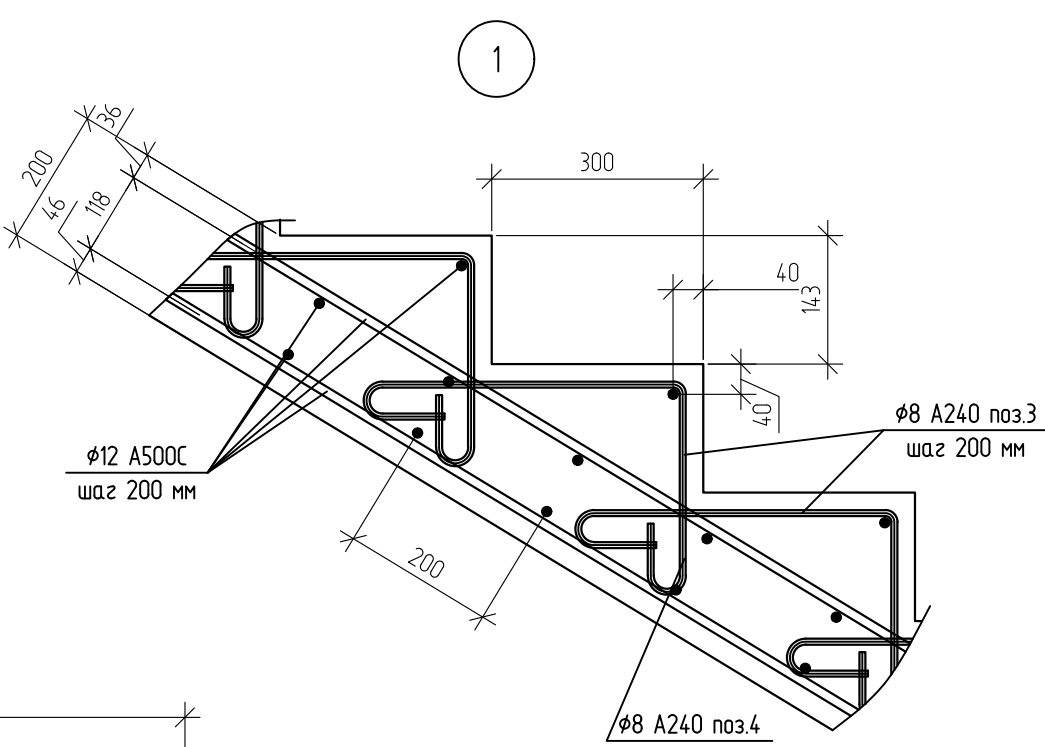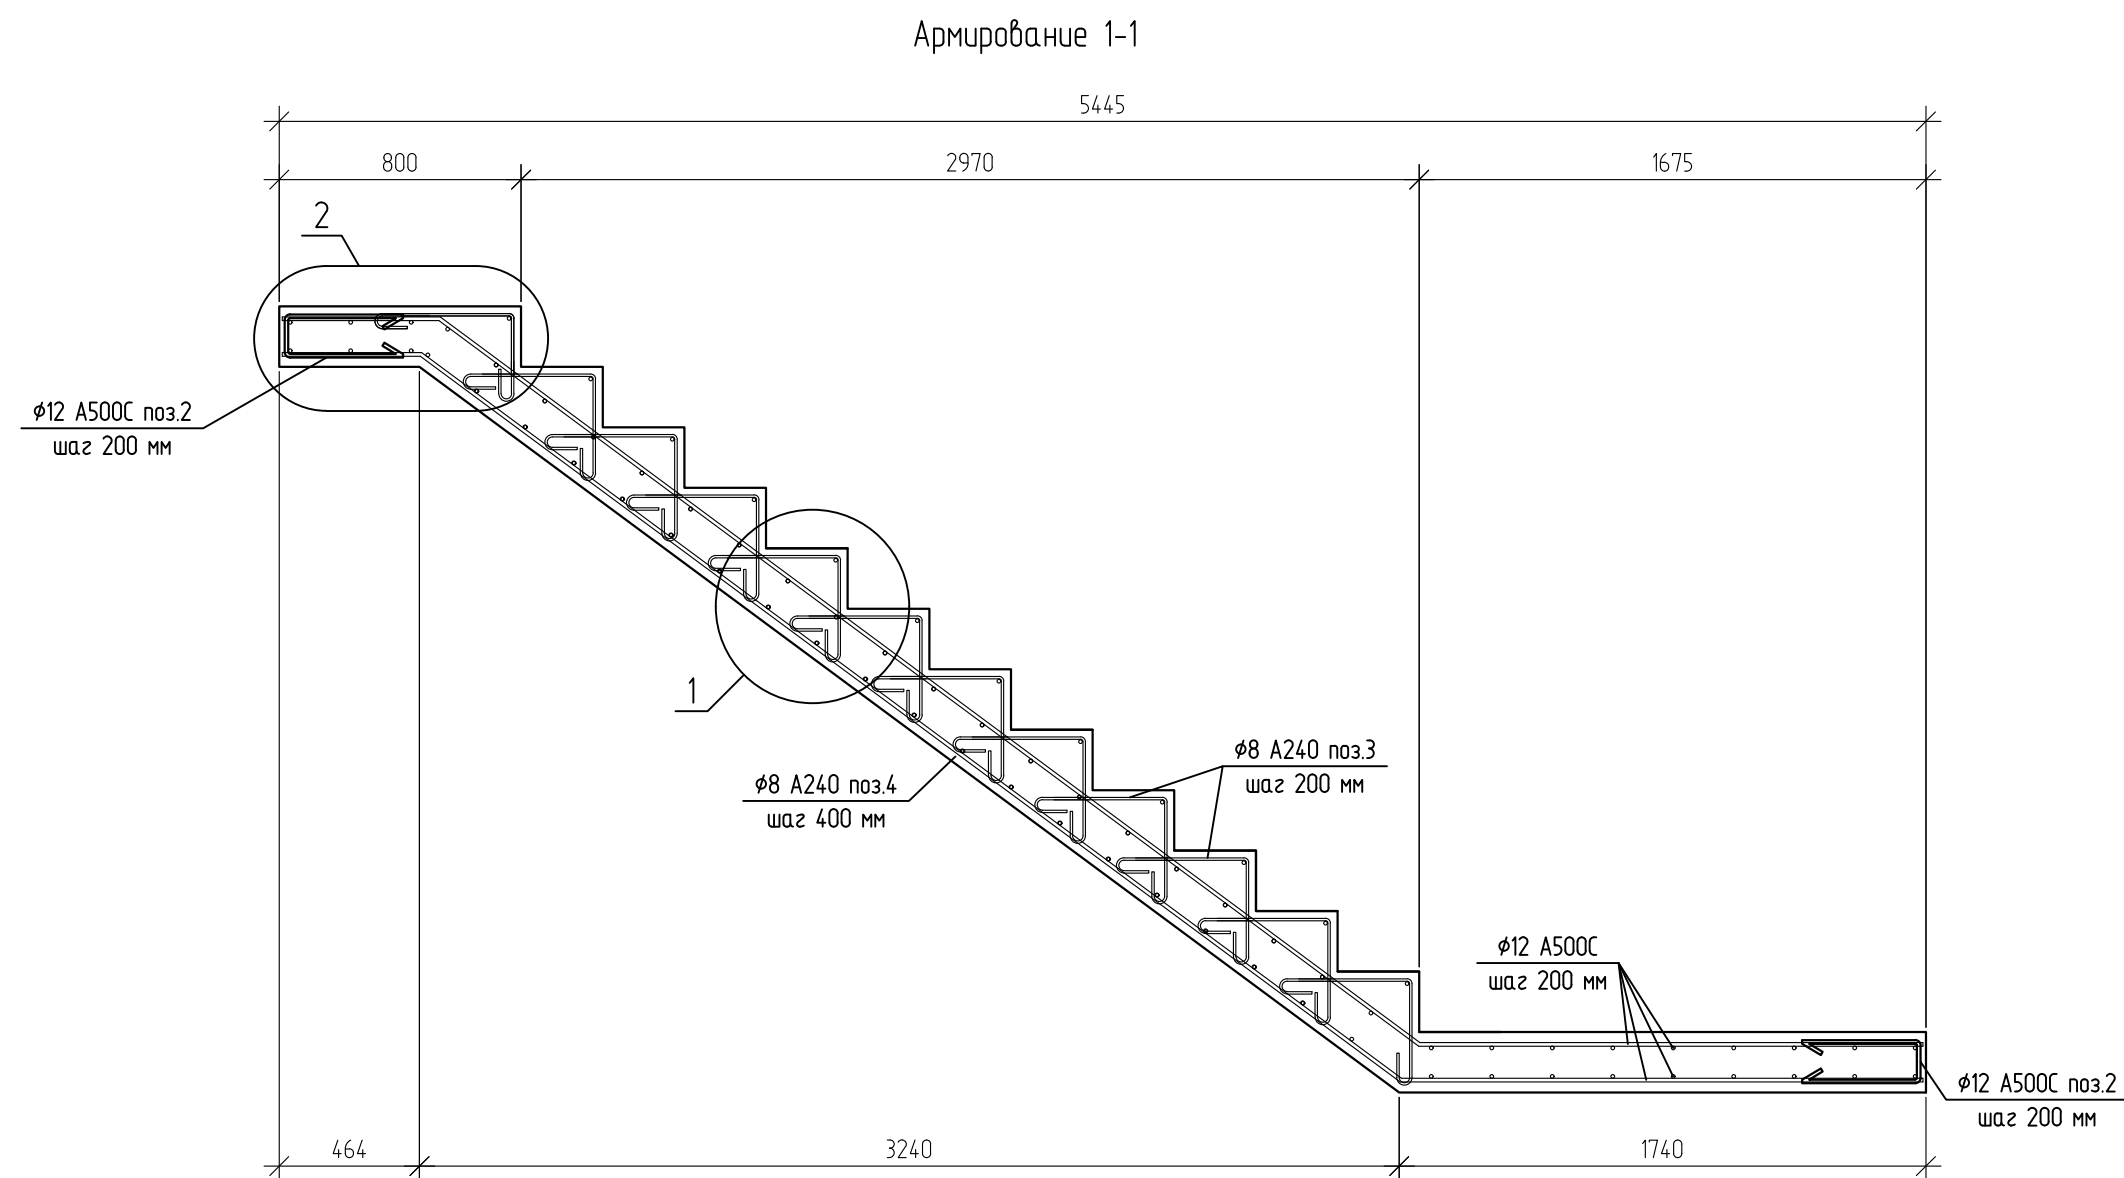

1. Фундаментную плиту, плиту площадки армировать отдельными стержнями $\Phi 12$ А500С с шагом 200х200 мм. Вся рабочая арматура соединяется в сетки с помощью вязальной проволоки. В сетках вязке подлежат пересечения стержней через одно в шахматном порядке.
2. Соединение стержней по длине производить внахлест с перелупком не менее 45 диаметров стержней арматуры. В одном условном сечении не более 50% стержней арматуры.
3. Размеры хомутов и знутых деталей даны для справки. Данные размеры следует уточнять и корректировать по месту для соответствия нижней и верхней сеток проектной.
4. Стыки смежных стержней разносить в шахматном порядке.
5. Фиксаторы положения сеток (лягушки) на чертеже не показаны и в спецификации не учтены.

						708/П-24-АНО-КР			
						Капитальный ремонт общеобразовательного учреждения ГБОУ "Школа №1210" по адресу: г. Москва, ул. Хлебная, д.32			
Изм.	Колуч.	Лист	№ док.	Подп.	Дата	Конструктивные решения	Станд.	Лист	Листов
Разработал	Горшин				04.26		Р	28	
ГАП	Фролова				04.26				
Н.Контроль	Лукашова				04.26	Схема устройства входа в оскх "21/1"		ООО "АРТИС"	
ГИП	Зыкин				04.26				

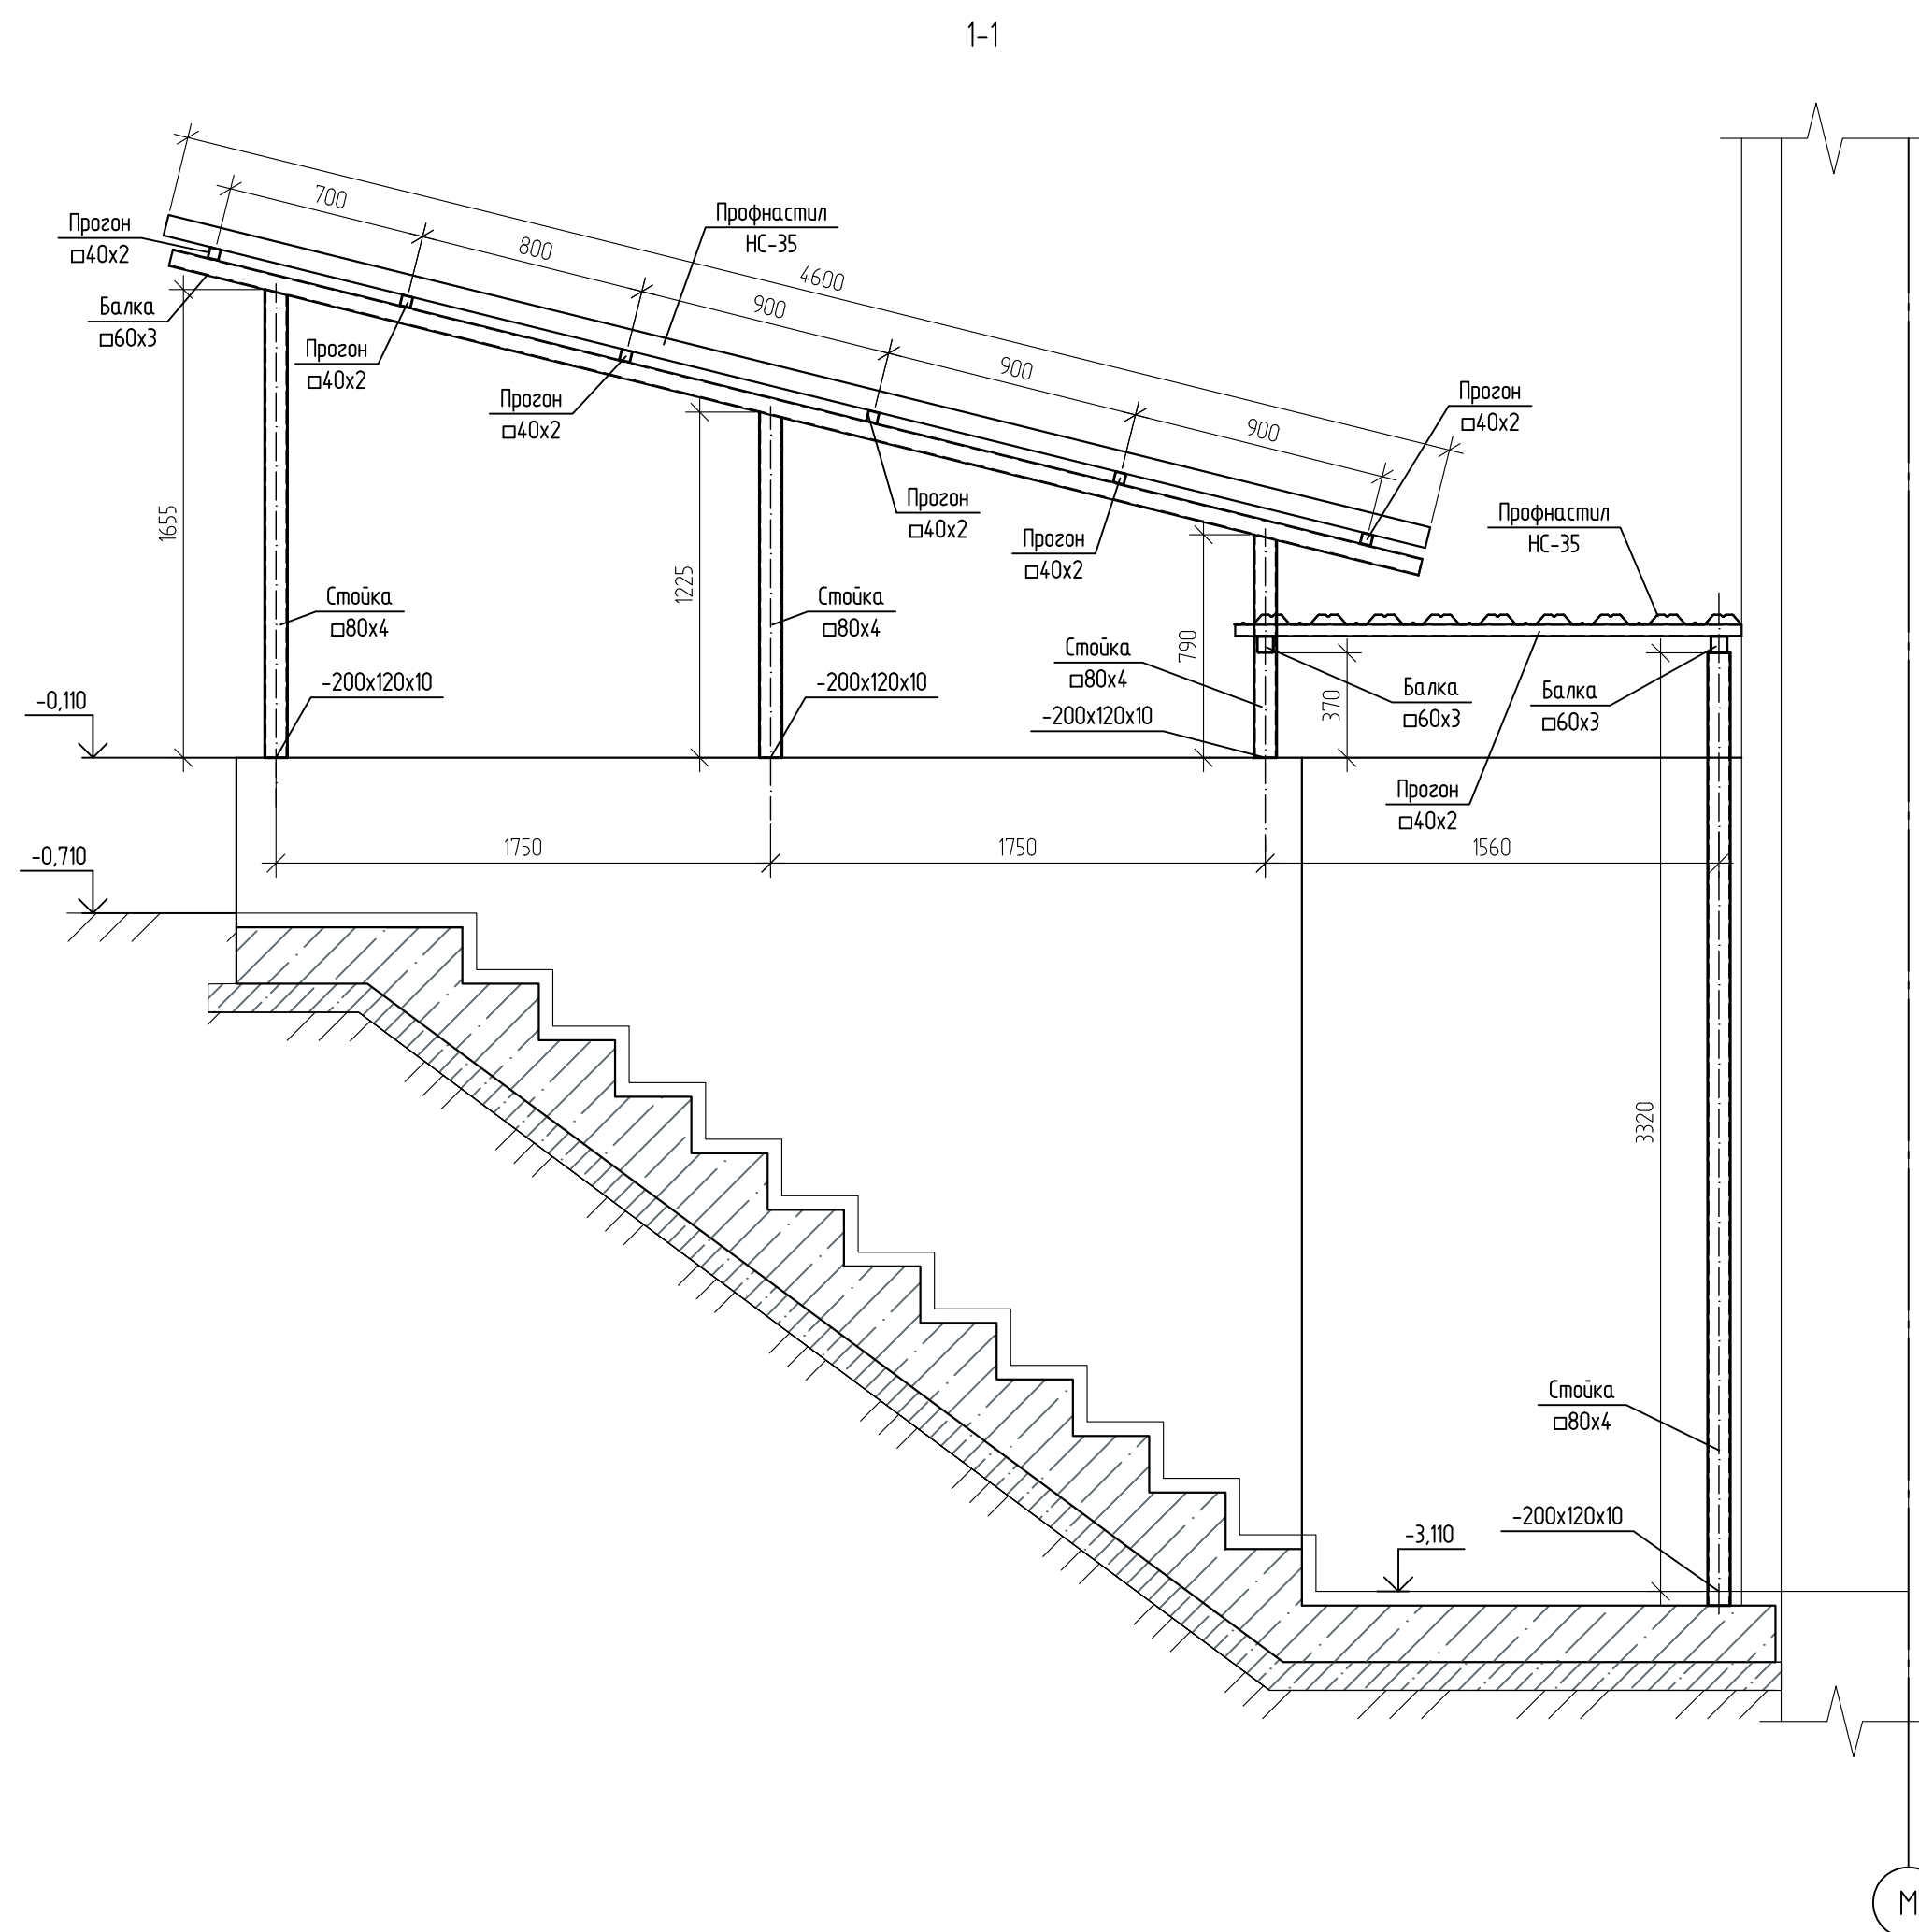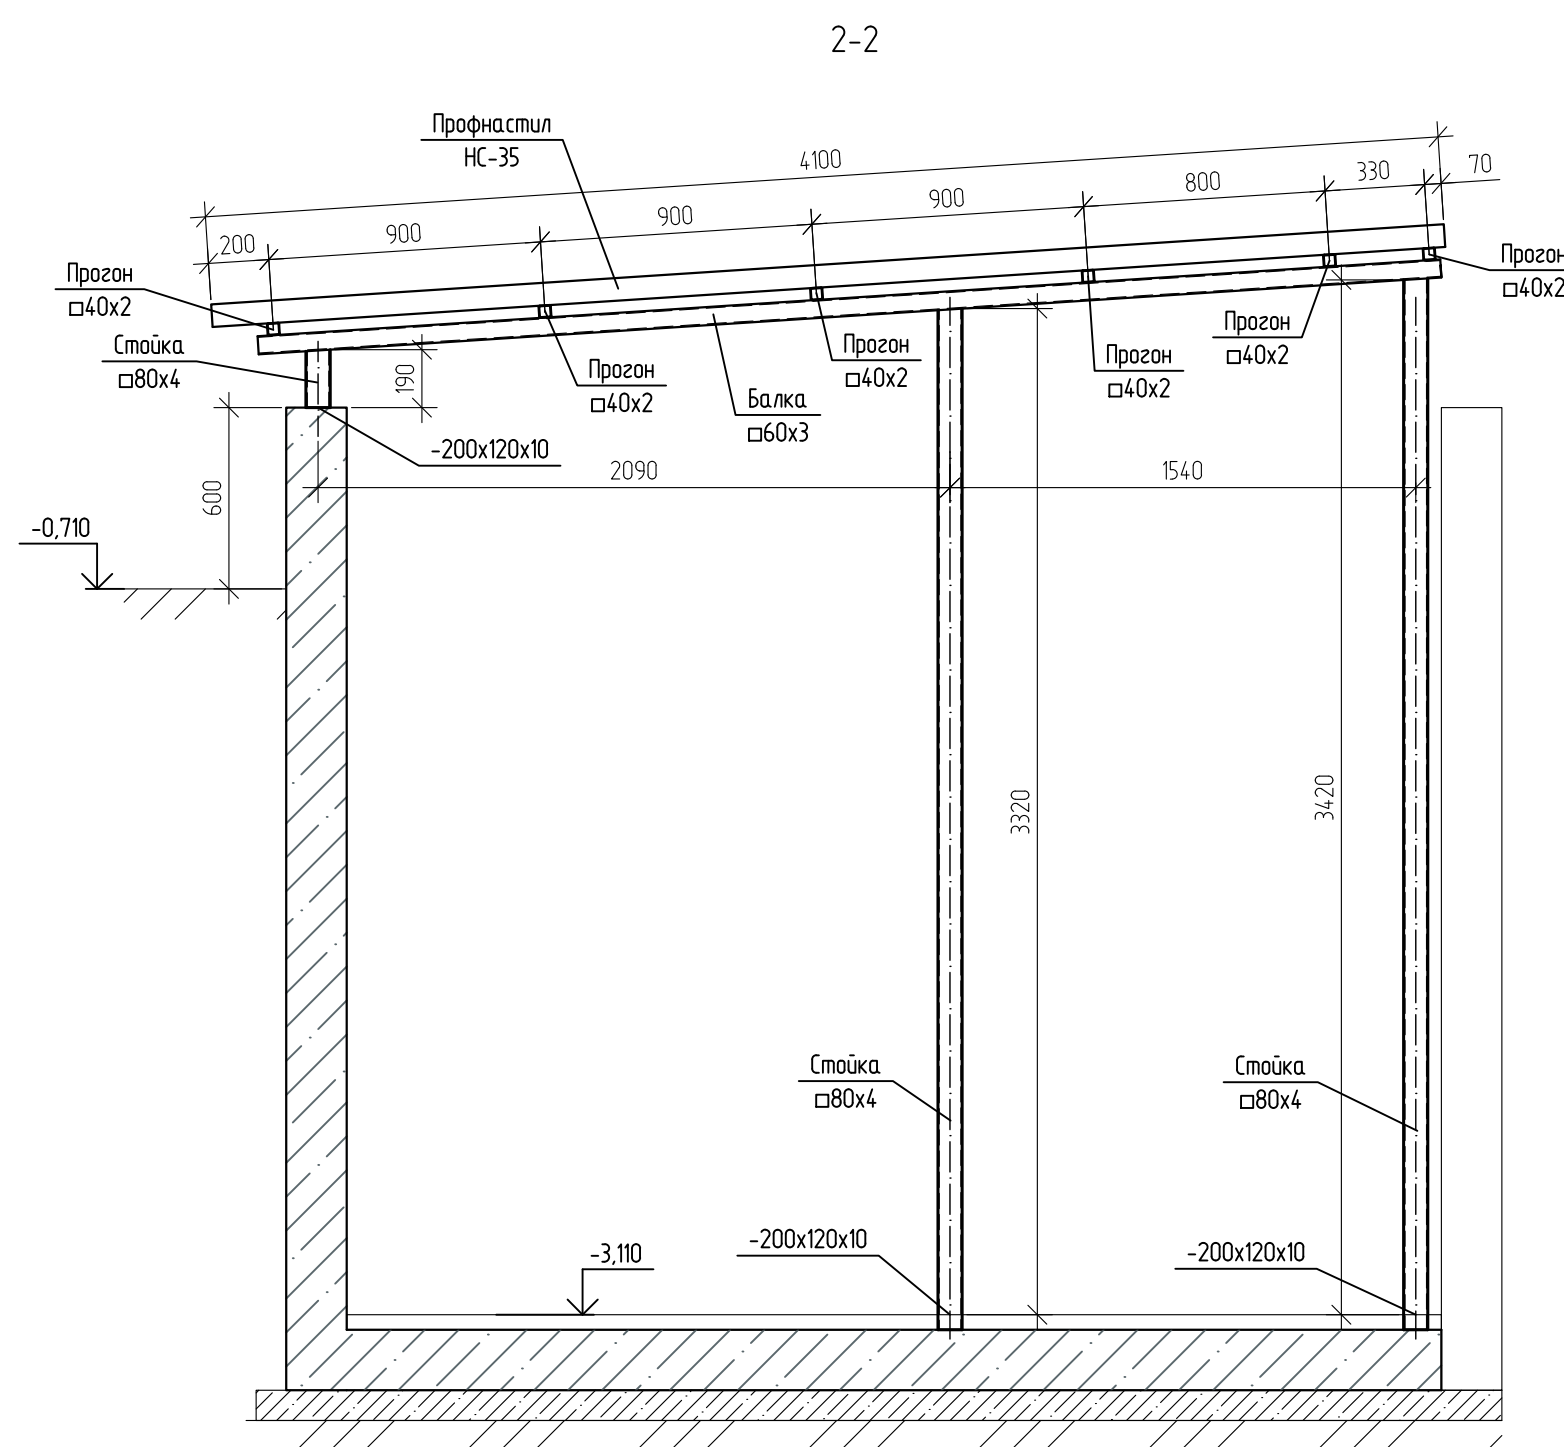


Примечание:

- 1. Материал для металлических конструкций – сталь С235 по ГОСТ 27772-2020;
- 2. Сварные соединения – по ГОСТ 5264-80. Электродом Э-42 по ГОСТ 9467-75*;
- 3. Минимальный катет сварного шва – по наименьшей толщине свариваемых элементов;
- 4. Все конструкции окрасить одним слоем эмали ПФ-115 ГОСТ 6465-76 по двум слоям грунта ПФ-021 ГОСТ 25129-82.

комплексное проектирование промышленных и гражданских объектов

ООО "АРТИС"

Опалубочный план крыльца в осях Д-Е/7-8

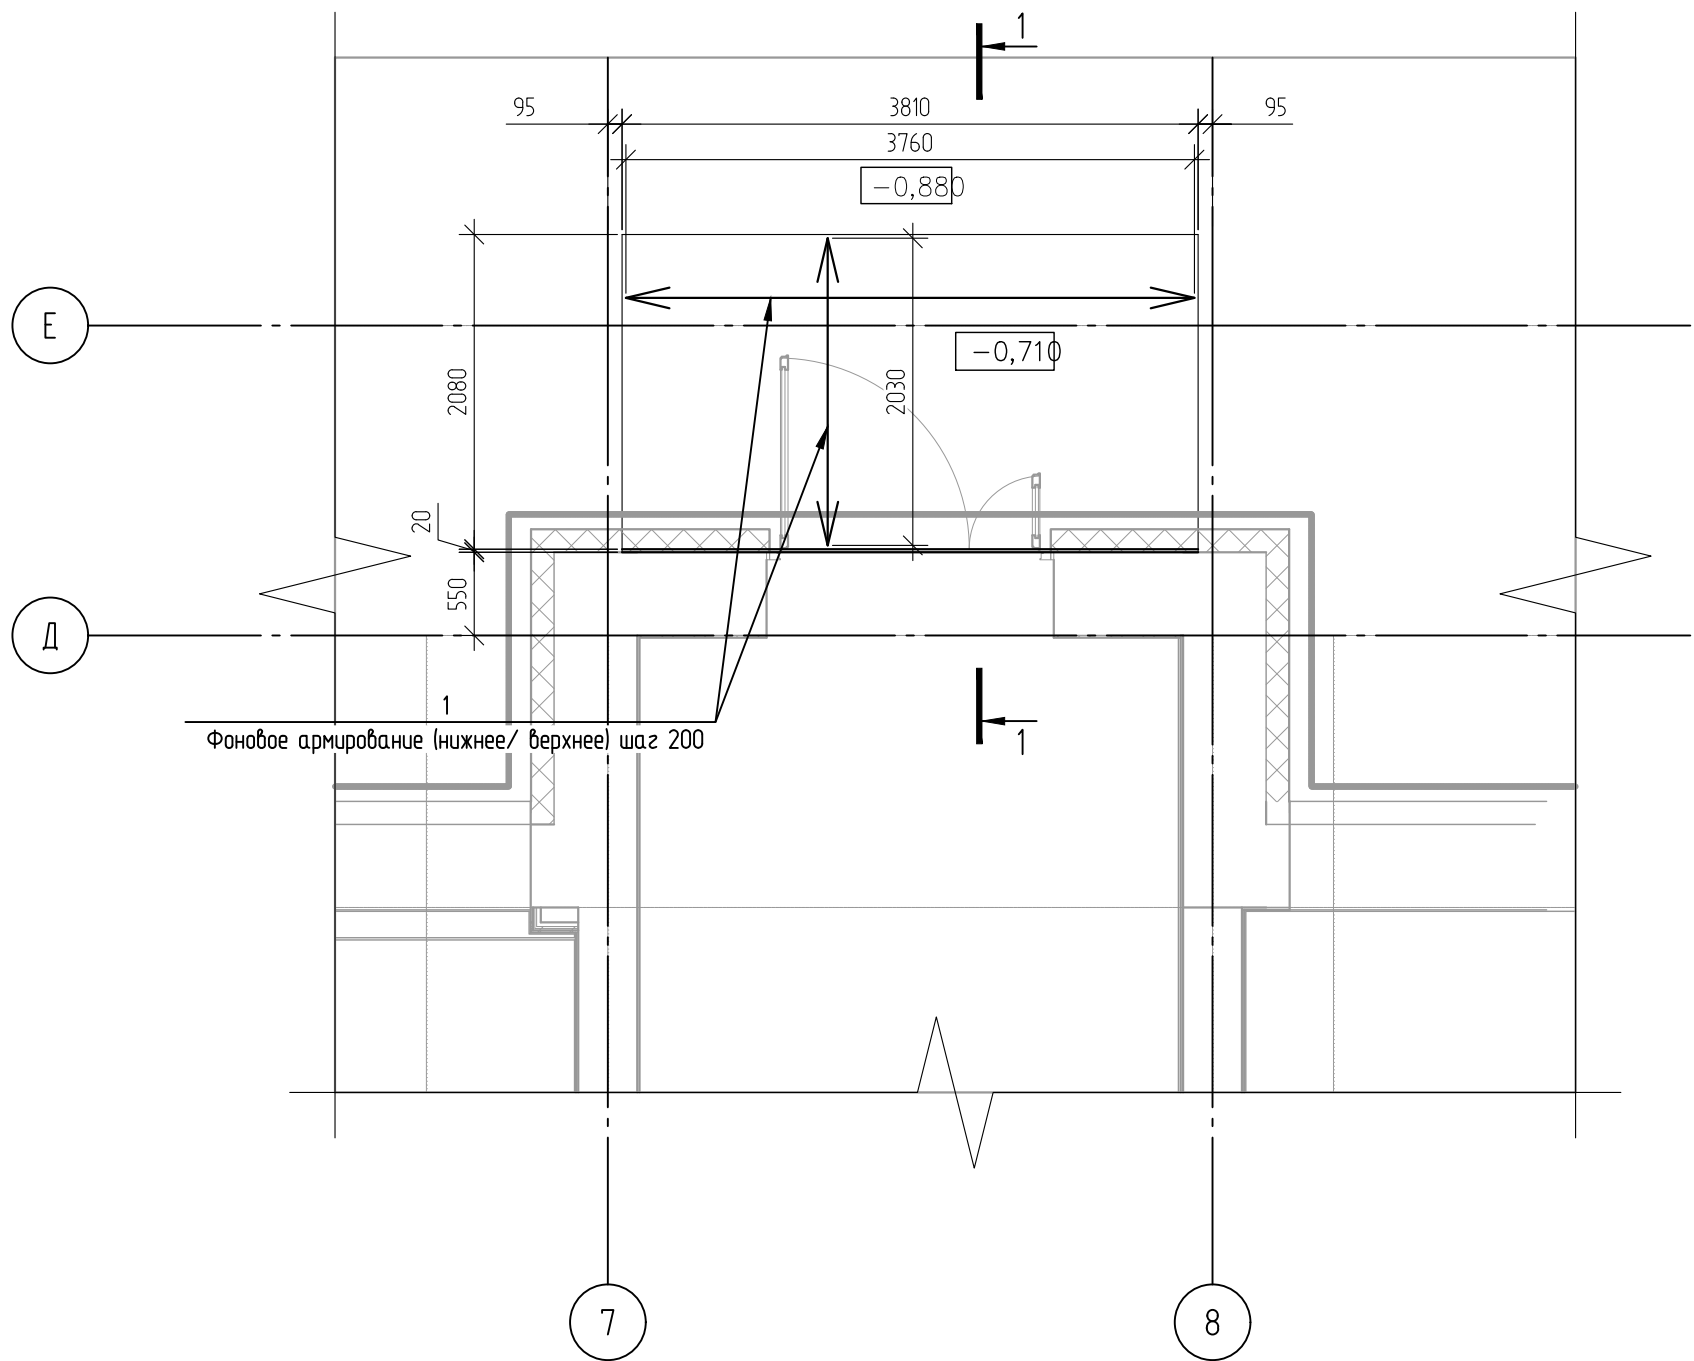


1-1

Ведомость деталей

Поз.	Эскиз
2	
3	


Спецификация на устройство крыльца в осях Д-Е/7-8

Поз.	Обозначение	Наименование	Кол.	Масса, ед. кг	Примечание
1	ГОСТ 34028-2016	Арматура 12 А500, м.п.	164	0.612	100,4
2	ГОСТ 34028-2016	Арматура 8 А240, L=970мм	59	0.38	22,4
3	ГОСТ 34028-2016	Арматура 8 А240, L=1050мм	22	0.41	9,0
Материалы					
		Пенополистирол t=20 мм, м2	0.95		
		Песок средней крупности, м3	2.75		
	ГОСТ 26633-2015	Бетон В7.5, м³	0.42		
	ГОСТ 26633-2015	Бетон В25 F150 W8, м³	1.98		

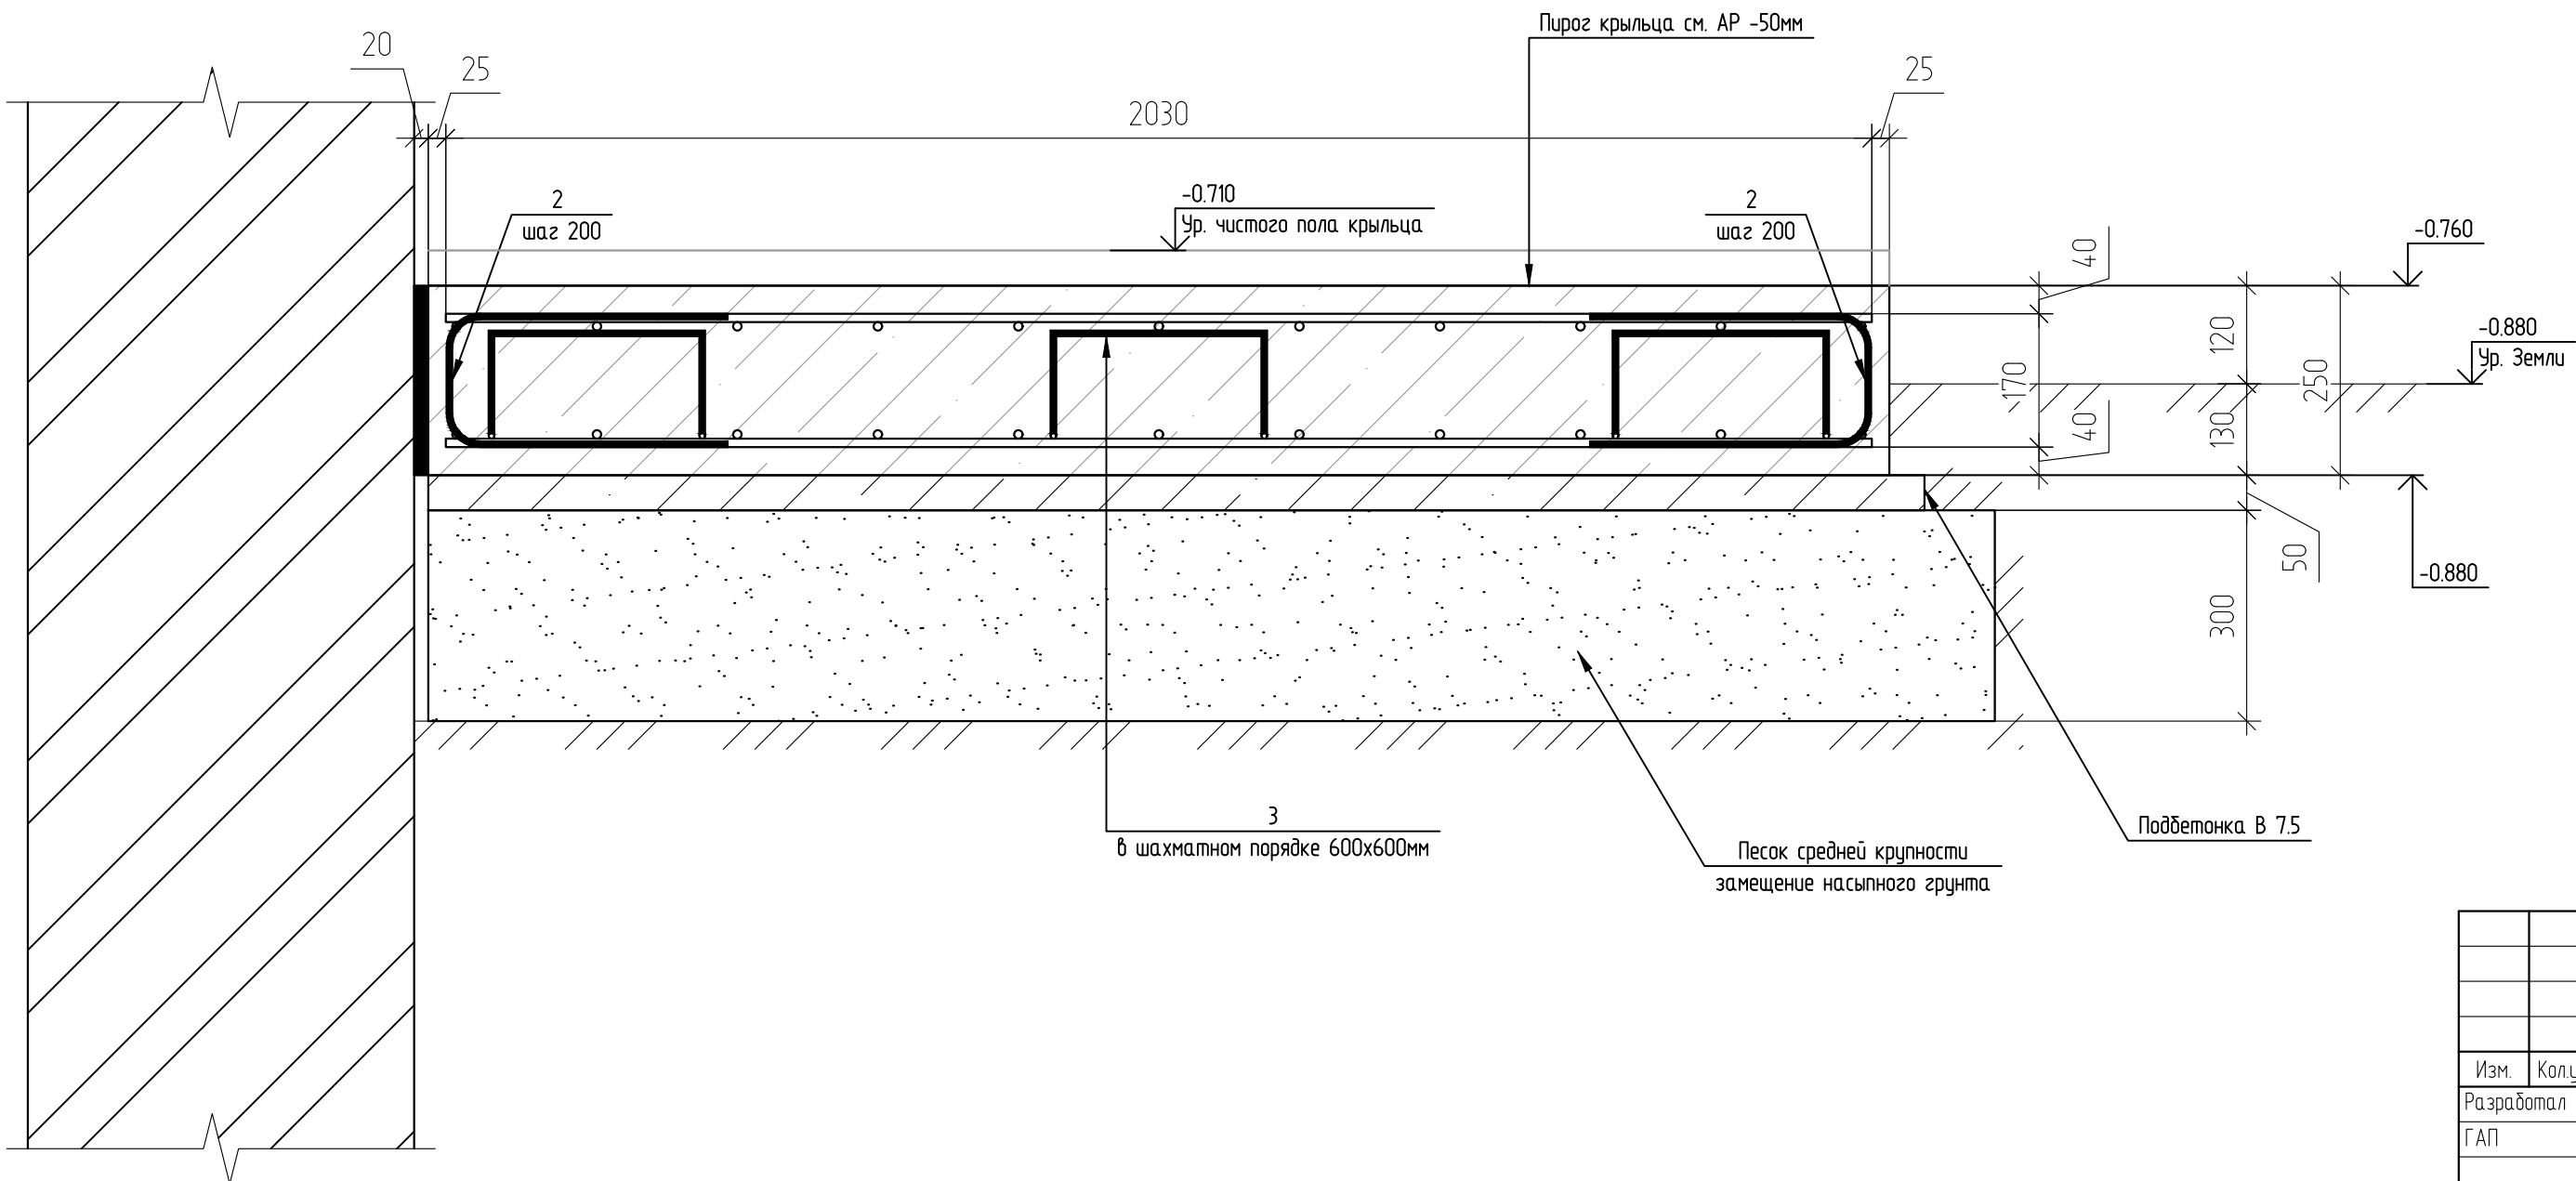

708/П-24-АНО-КР					
Капитальный ремонт общеобразовательного учреждения ГБОУ "Школа №1210" по адресу: г. Москва, ул. Живописная, д.32					
Изм.	Колуч.	Лист	№ док.	Подп.	Дата
Разработал	Торшин	04.26	04.26	04.26	04.26
ГАП	Фролова	04.26	04.26	04.26	04.26
Конструктивные решения					
Опалубочный план крыльца в осях Д-Е/7-8					
Н.Контроль	Лукашова	04.26	04.26	04.26	04.26
ГИП	Зыкин	04.26	04.26	04.26	04.26

Опалубочный план крыльца в осях Г-Е/15-16

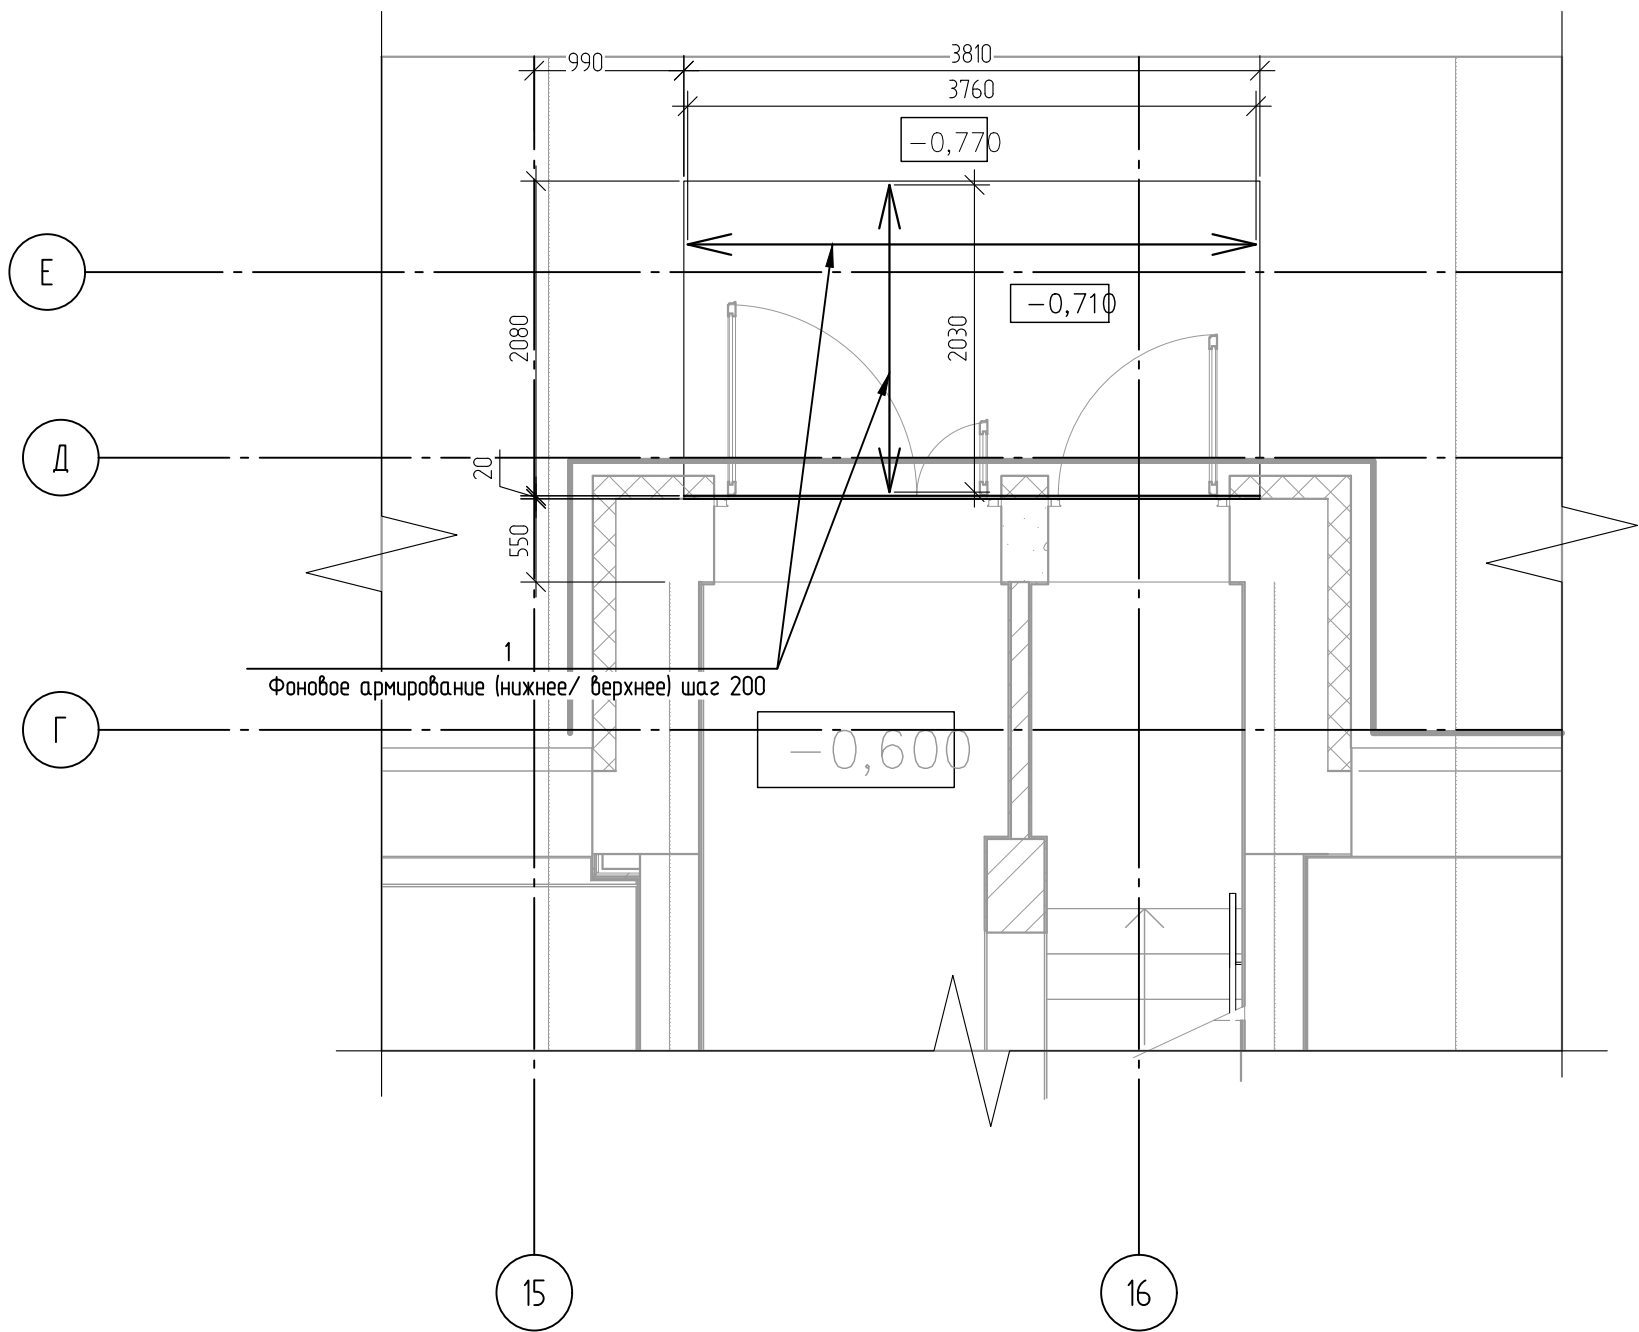


Ведомость деталей

Поз.	Эскиз
2	
3	

Спецификация на устройство крыльца в осях Г-Е/15-16

Поз.	Обозначение	Наименование	Кол.	Масса, ед. кг	Примечание
1	ГОСТ 34028-2016	Арматура 12 А500, м.п.	164	0.612	100,4
2	ГОСТ 34028-2016	Арматура 8 А240, L=1010мм	59	0.4	23,6
3	ГОСТ 34028-2016	Арматура 8 А240, L=1130мм	22	0.45	9,9
Материалы					
		Пенополистирол t=20 мм, м2	1.1		
		Песок средней крупности, м3	2.75		
	ГОСТ 26633-2015	Бетон В7.5, м³	0.42		
	ГОСТ 26633-2015	Бетон В25 F150 W8, м³	2.3		

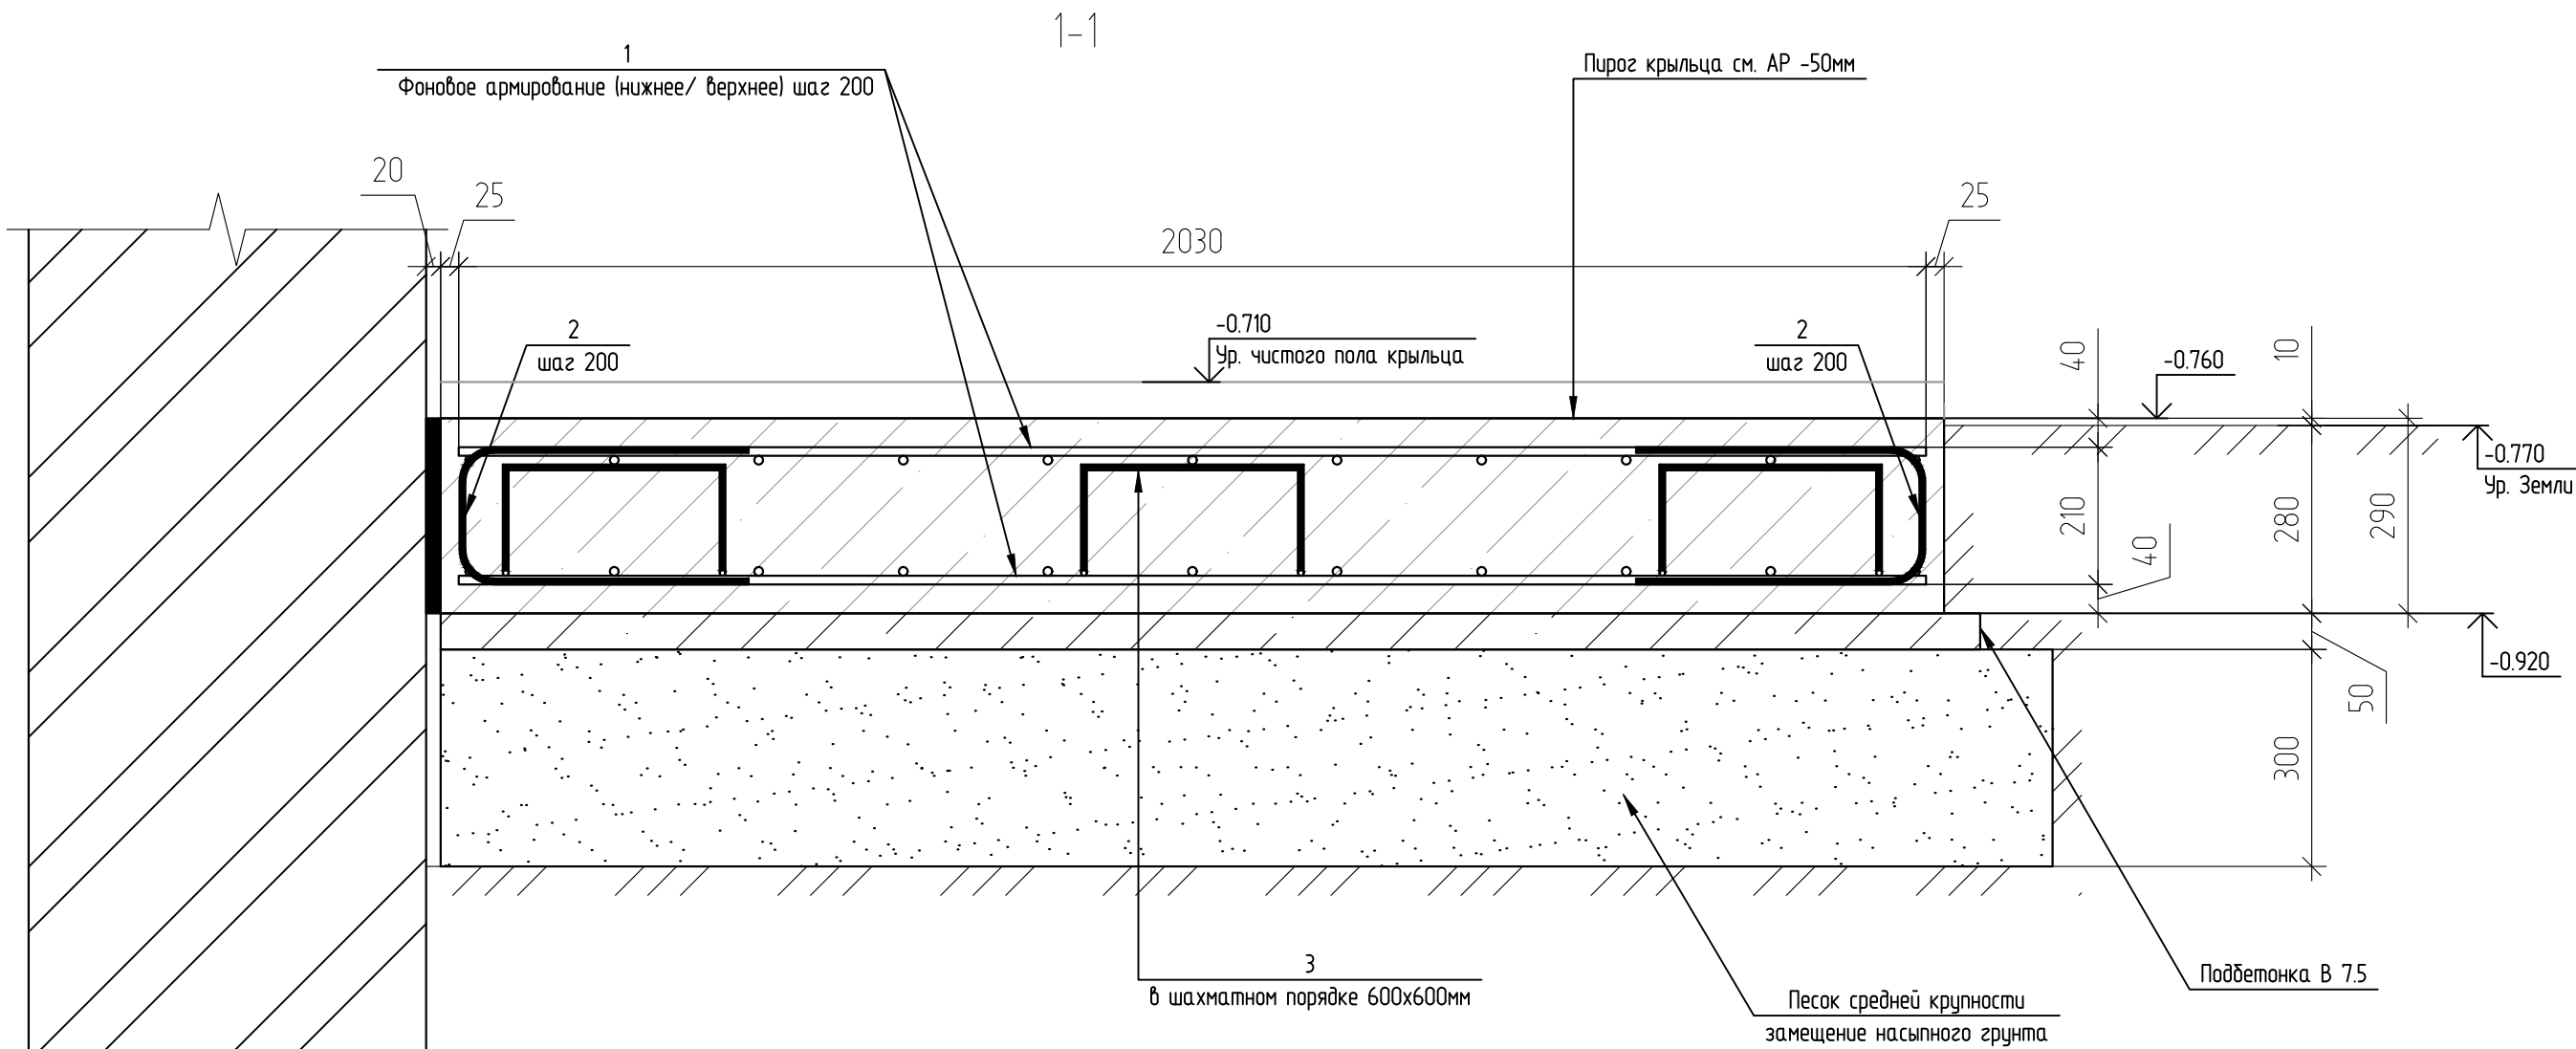


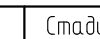
						708/П-24-АНО-КР				
						Капитальный ремонт общеобразовательного учреждения ГБОУ "Школа №1210" по адресу: г. Москва, ул. Живописная, д.32				
Изм.	Колуч.	Лист	№ док.	Подп.	Дата	Конструктивные решения		Стадия	Лист	Листов
Разработал	Торшин				04.26			Р	31	
ГАП	Фролова				04.26	Опалубочный план крыльца в осях Д-Е/15-16		 комплексное проектирование строительных и гражданских объектов ООО "АРТИС"		
Н.Контроль	Лукашова				04.26					
ГИП	Зыкин				04.26					

Схема устройства входа в осях "8-13/А"

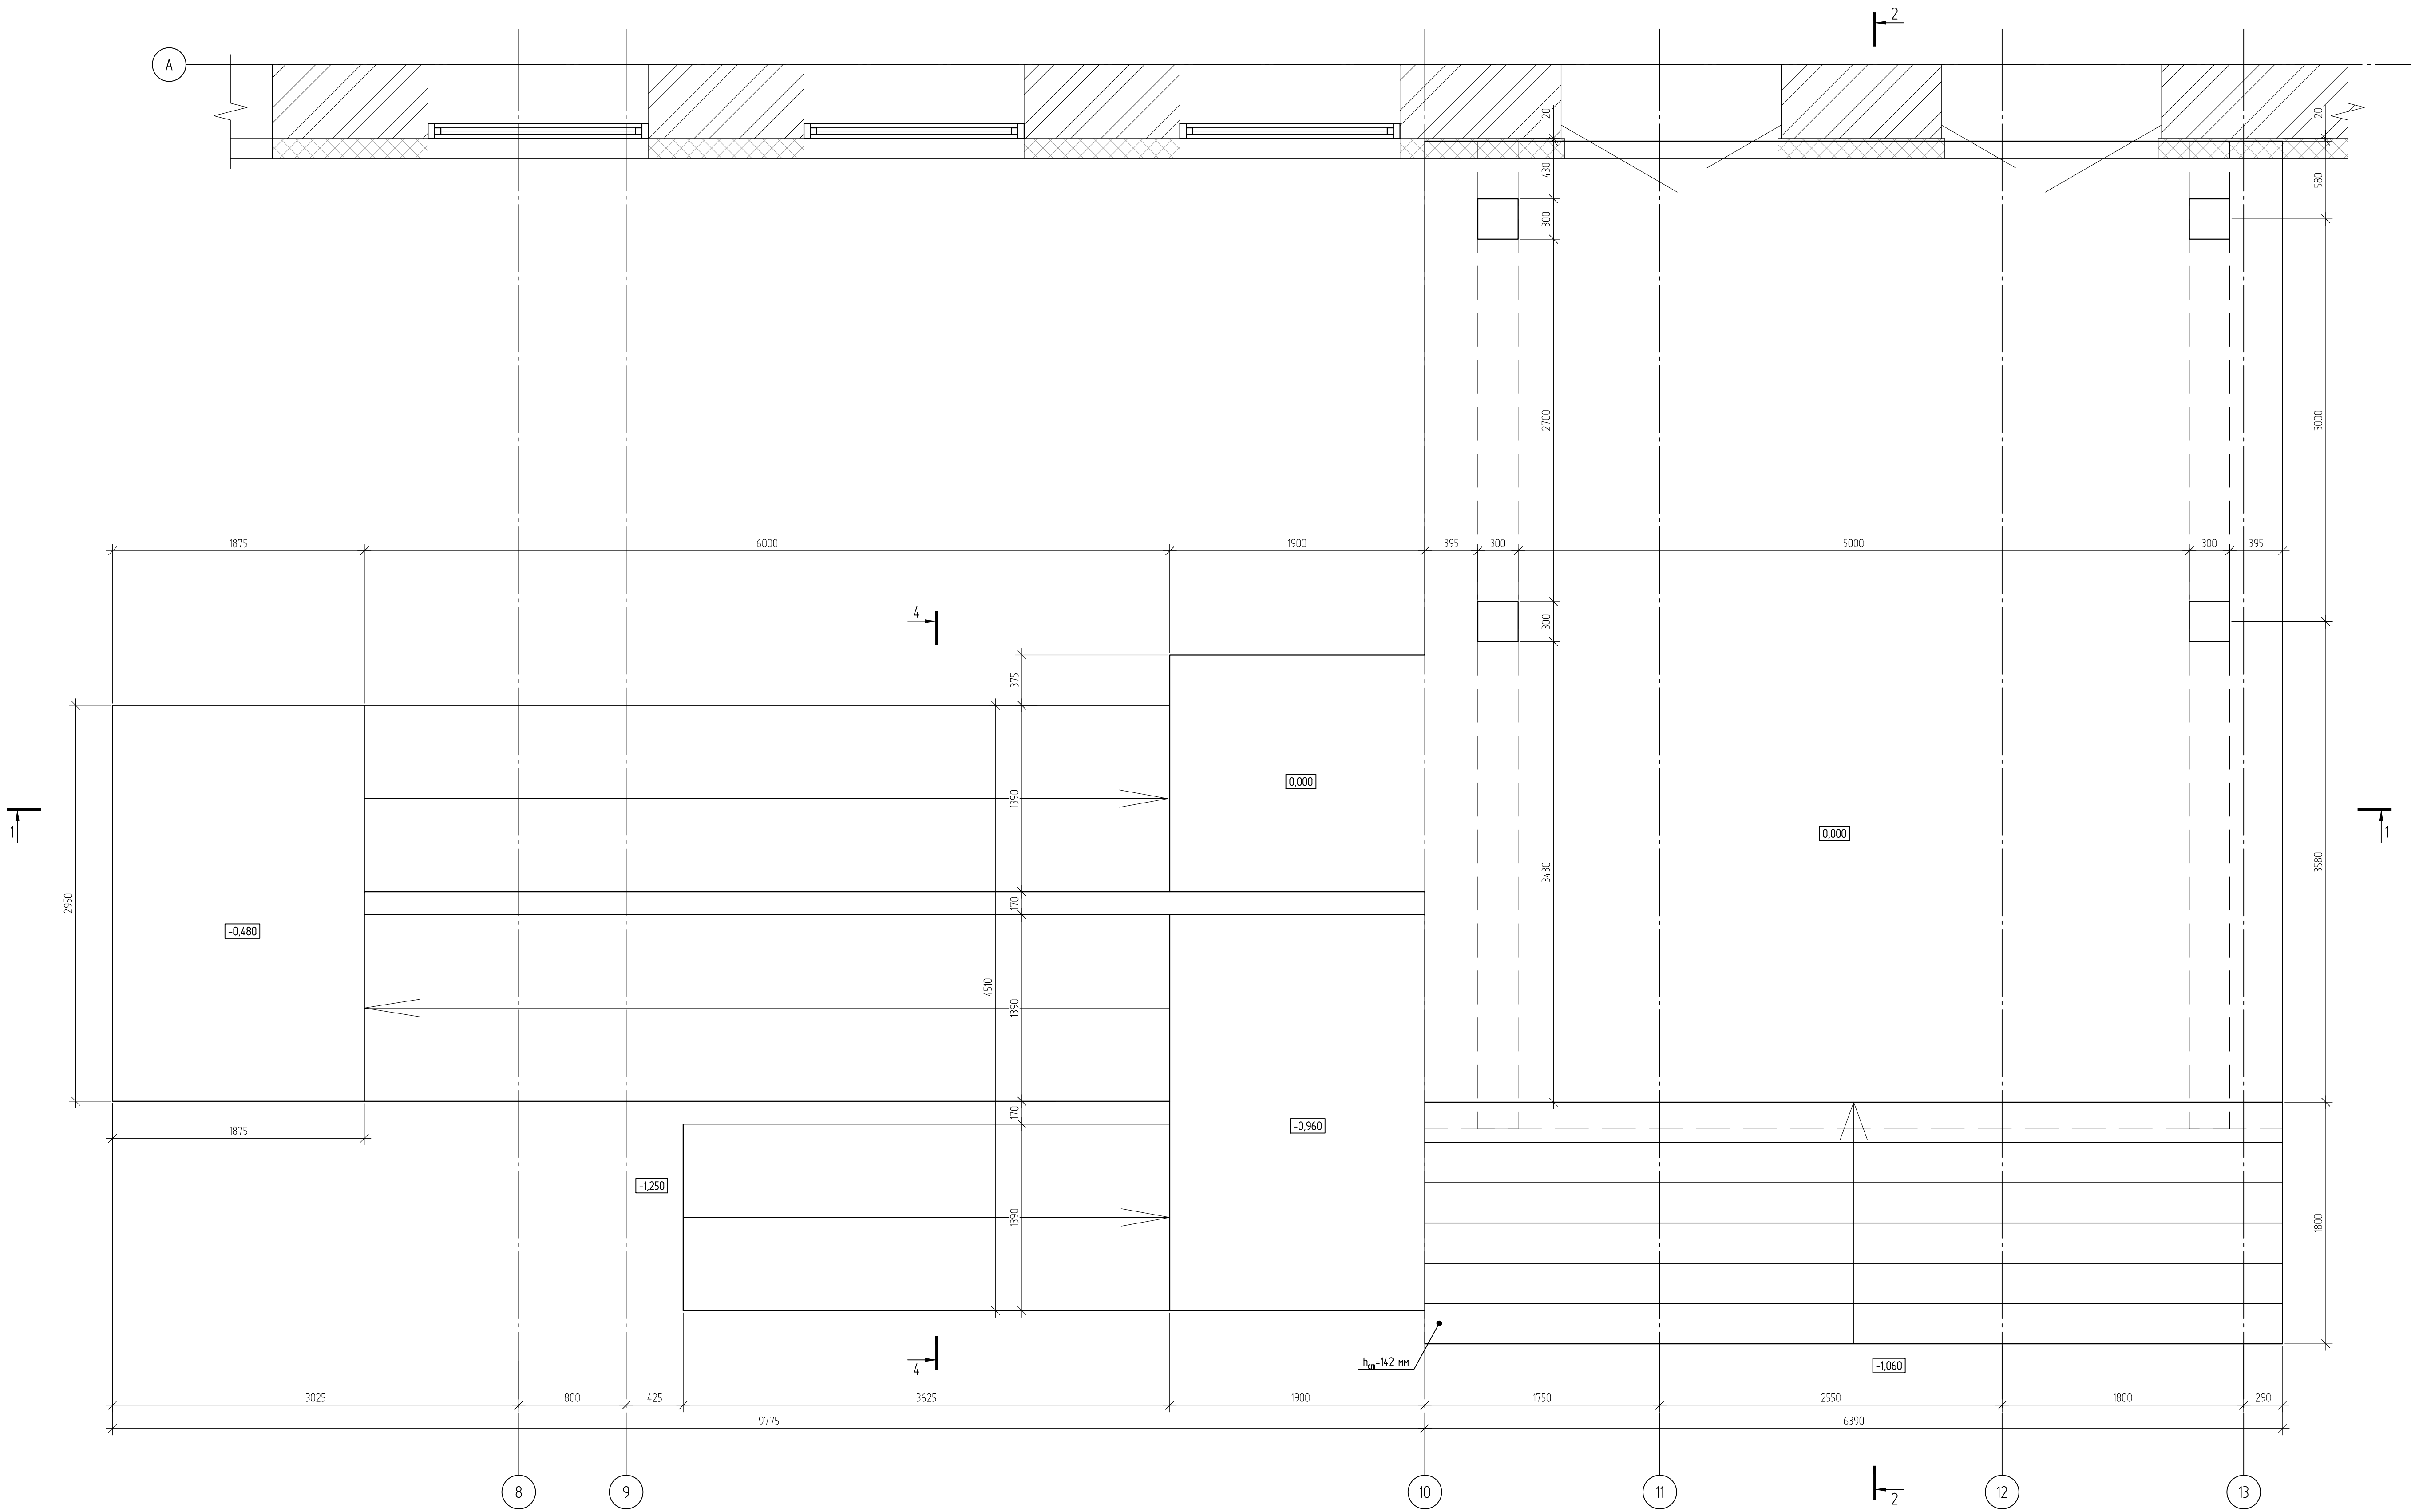


						708/П-24-АНО-КР			
						Капитальный ремонт общеобразовательного учреждения ГБОУ "Школа №1210" по адресу: г. Москва, ул. Животичная, д.32			
Изм.	Колуч.	Лист	№ док.	Подп.	Дата	Конструктивные решения	Стадия	Лист	Листов
Разработал	Горшин				04.26		Р	32	
ГАП	Фролова				04.26	Схема устройства входа в осях "8-13/А"	 ОАО "АРТИС"		
Н.Контроль	Лукашова				04.26				
ГИП	Зыкин				04.26				

Изм. № подл.	Подп. и дата	Взам. инв. №	Создана


Согласовано	
Взам. инв. №	
Подп. и дата	
Инв. № подл.	

Разрез 4-4

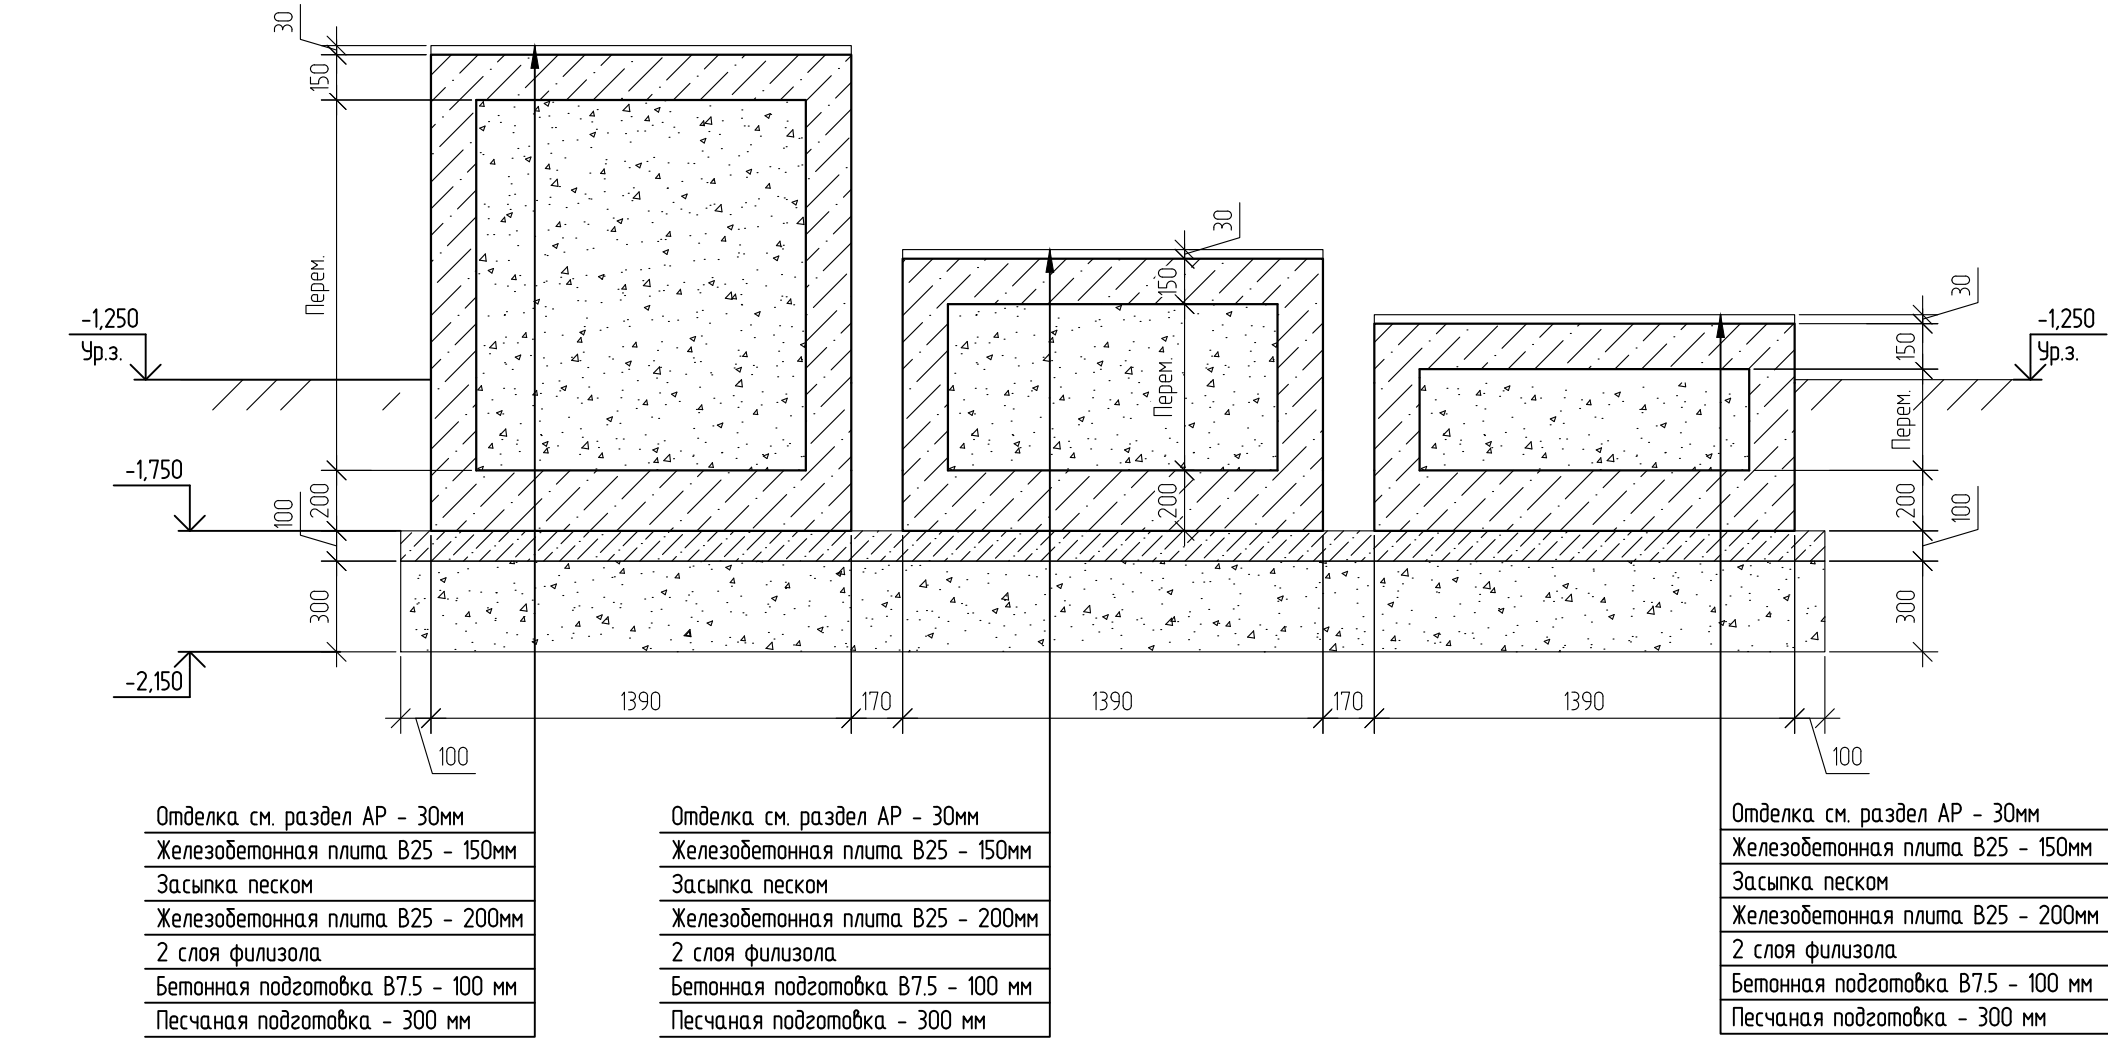

Разрез 1-1


Отделка см. раздел АР - 420мм
Основание - ж/б плита 200 мм по ж/б балкам 300х350(н) мм

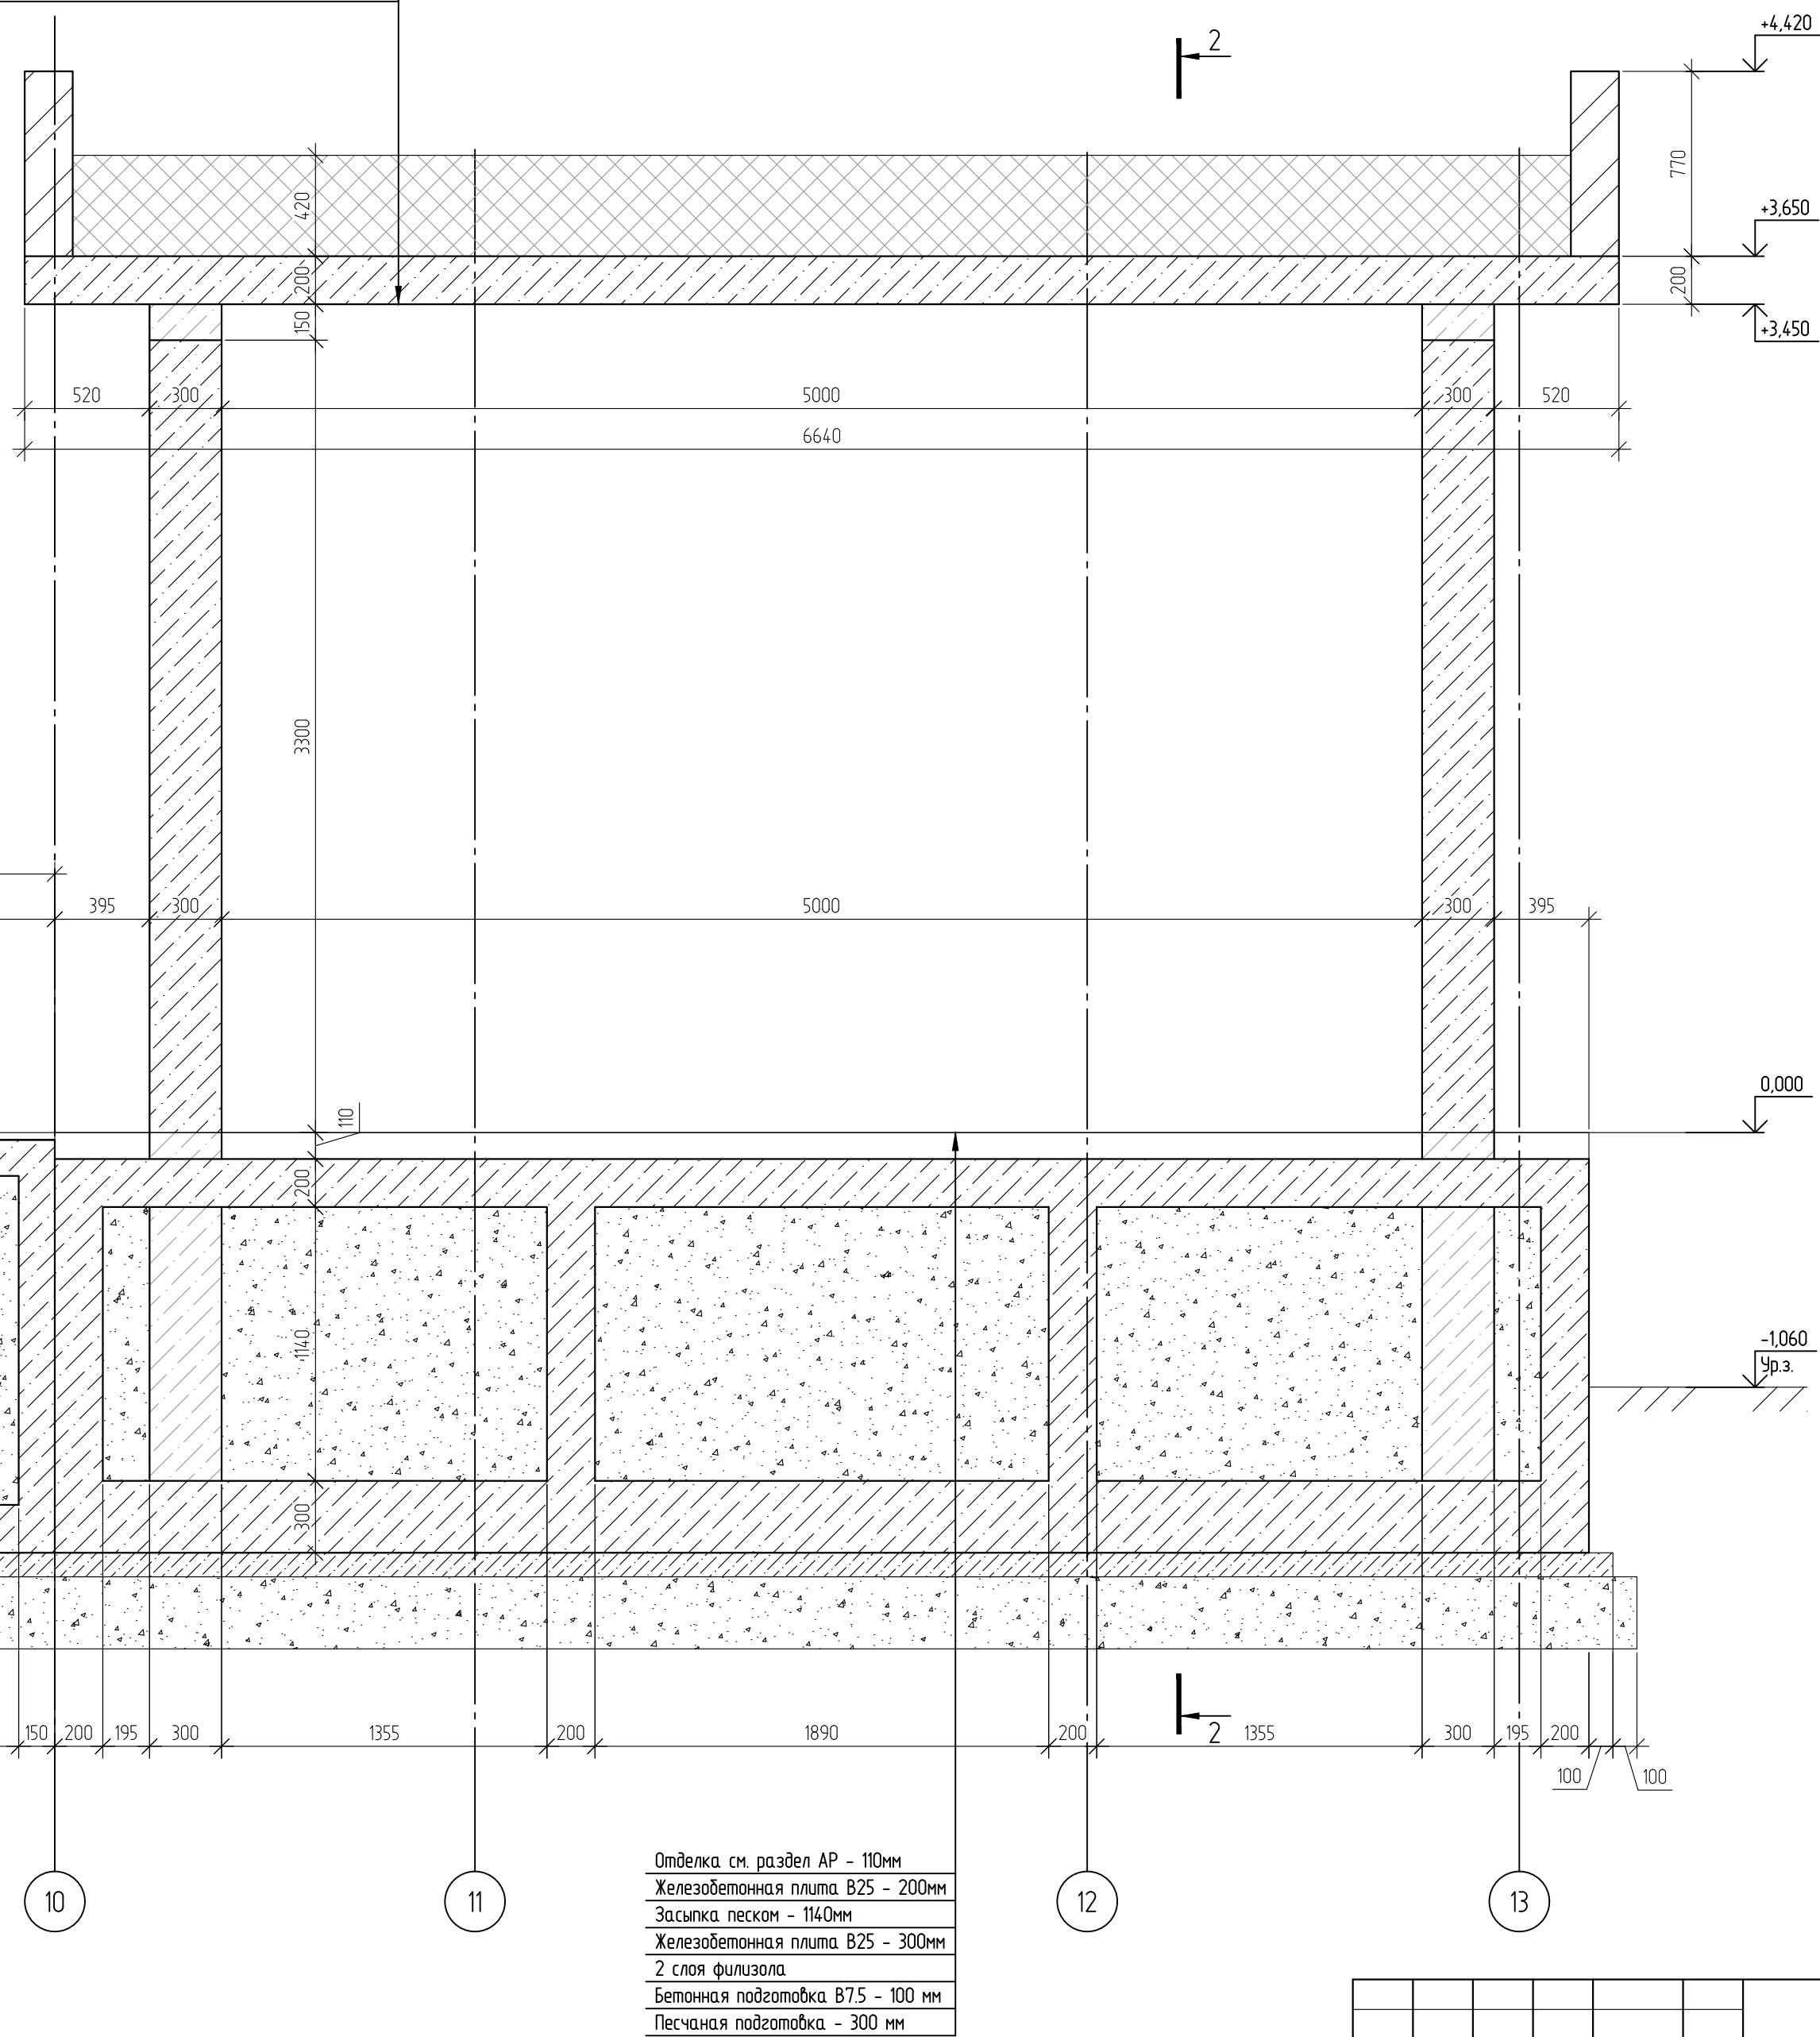


Отделка см. раздел АР - 30мм
Железобетонная плита В25 - 150мм
Засыпка песком
Железобетонная плита В25 - 200мм
2 слоя флиззола
Бетонная подготовка В7.5 - 100 мм
Песчаная подготовка - 300 мм

Отделка см. раздел АР - 110мм
Железобетонная плита В25 - 200мм
Засыпка песком - 1140мм
Железобетонная плита В25 - 300мм
2 слоя флиззола
Бетонная подготовка В7.5 - 100 мм
Песчаная подготовка - 300 мм

							708/П-24-АНО-КР
							Капитальный ремонт общеобразовательного учреждения ГБОУ "Школа №1210" по адресу: г. Москва, ул. Живописная, д.32
Изм.	Колуч.	Лист	№ док.	Подп.	Дата		
Разработал	Торшин	04.26					
Г.А.П.	Фролова	04.26				Конструктивные решения	Стадия Р
							Лист 34
							Листов
Н.Контроль	Лукашова	04.26				Разрез 1-1, 4-4	
ГИП	Зыкин	04.26					

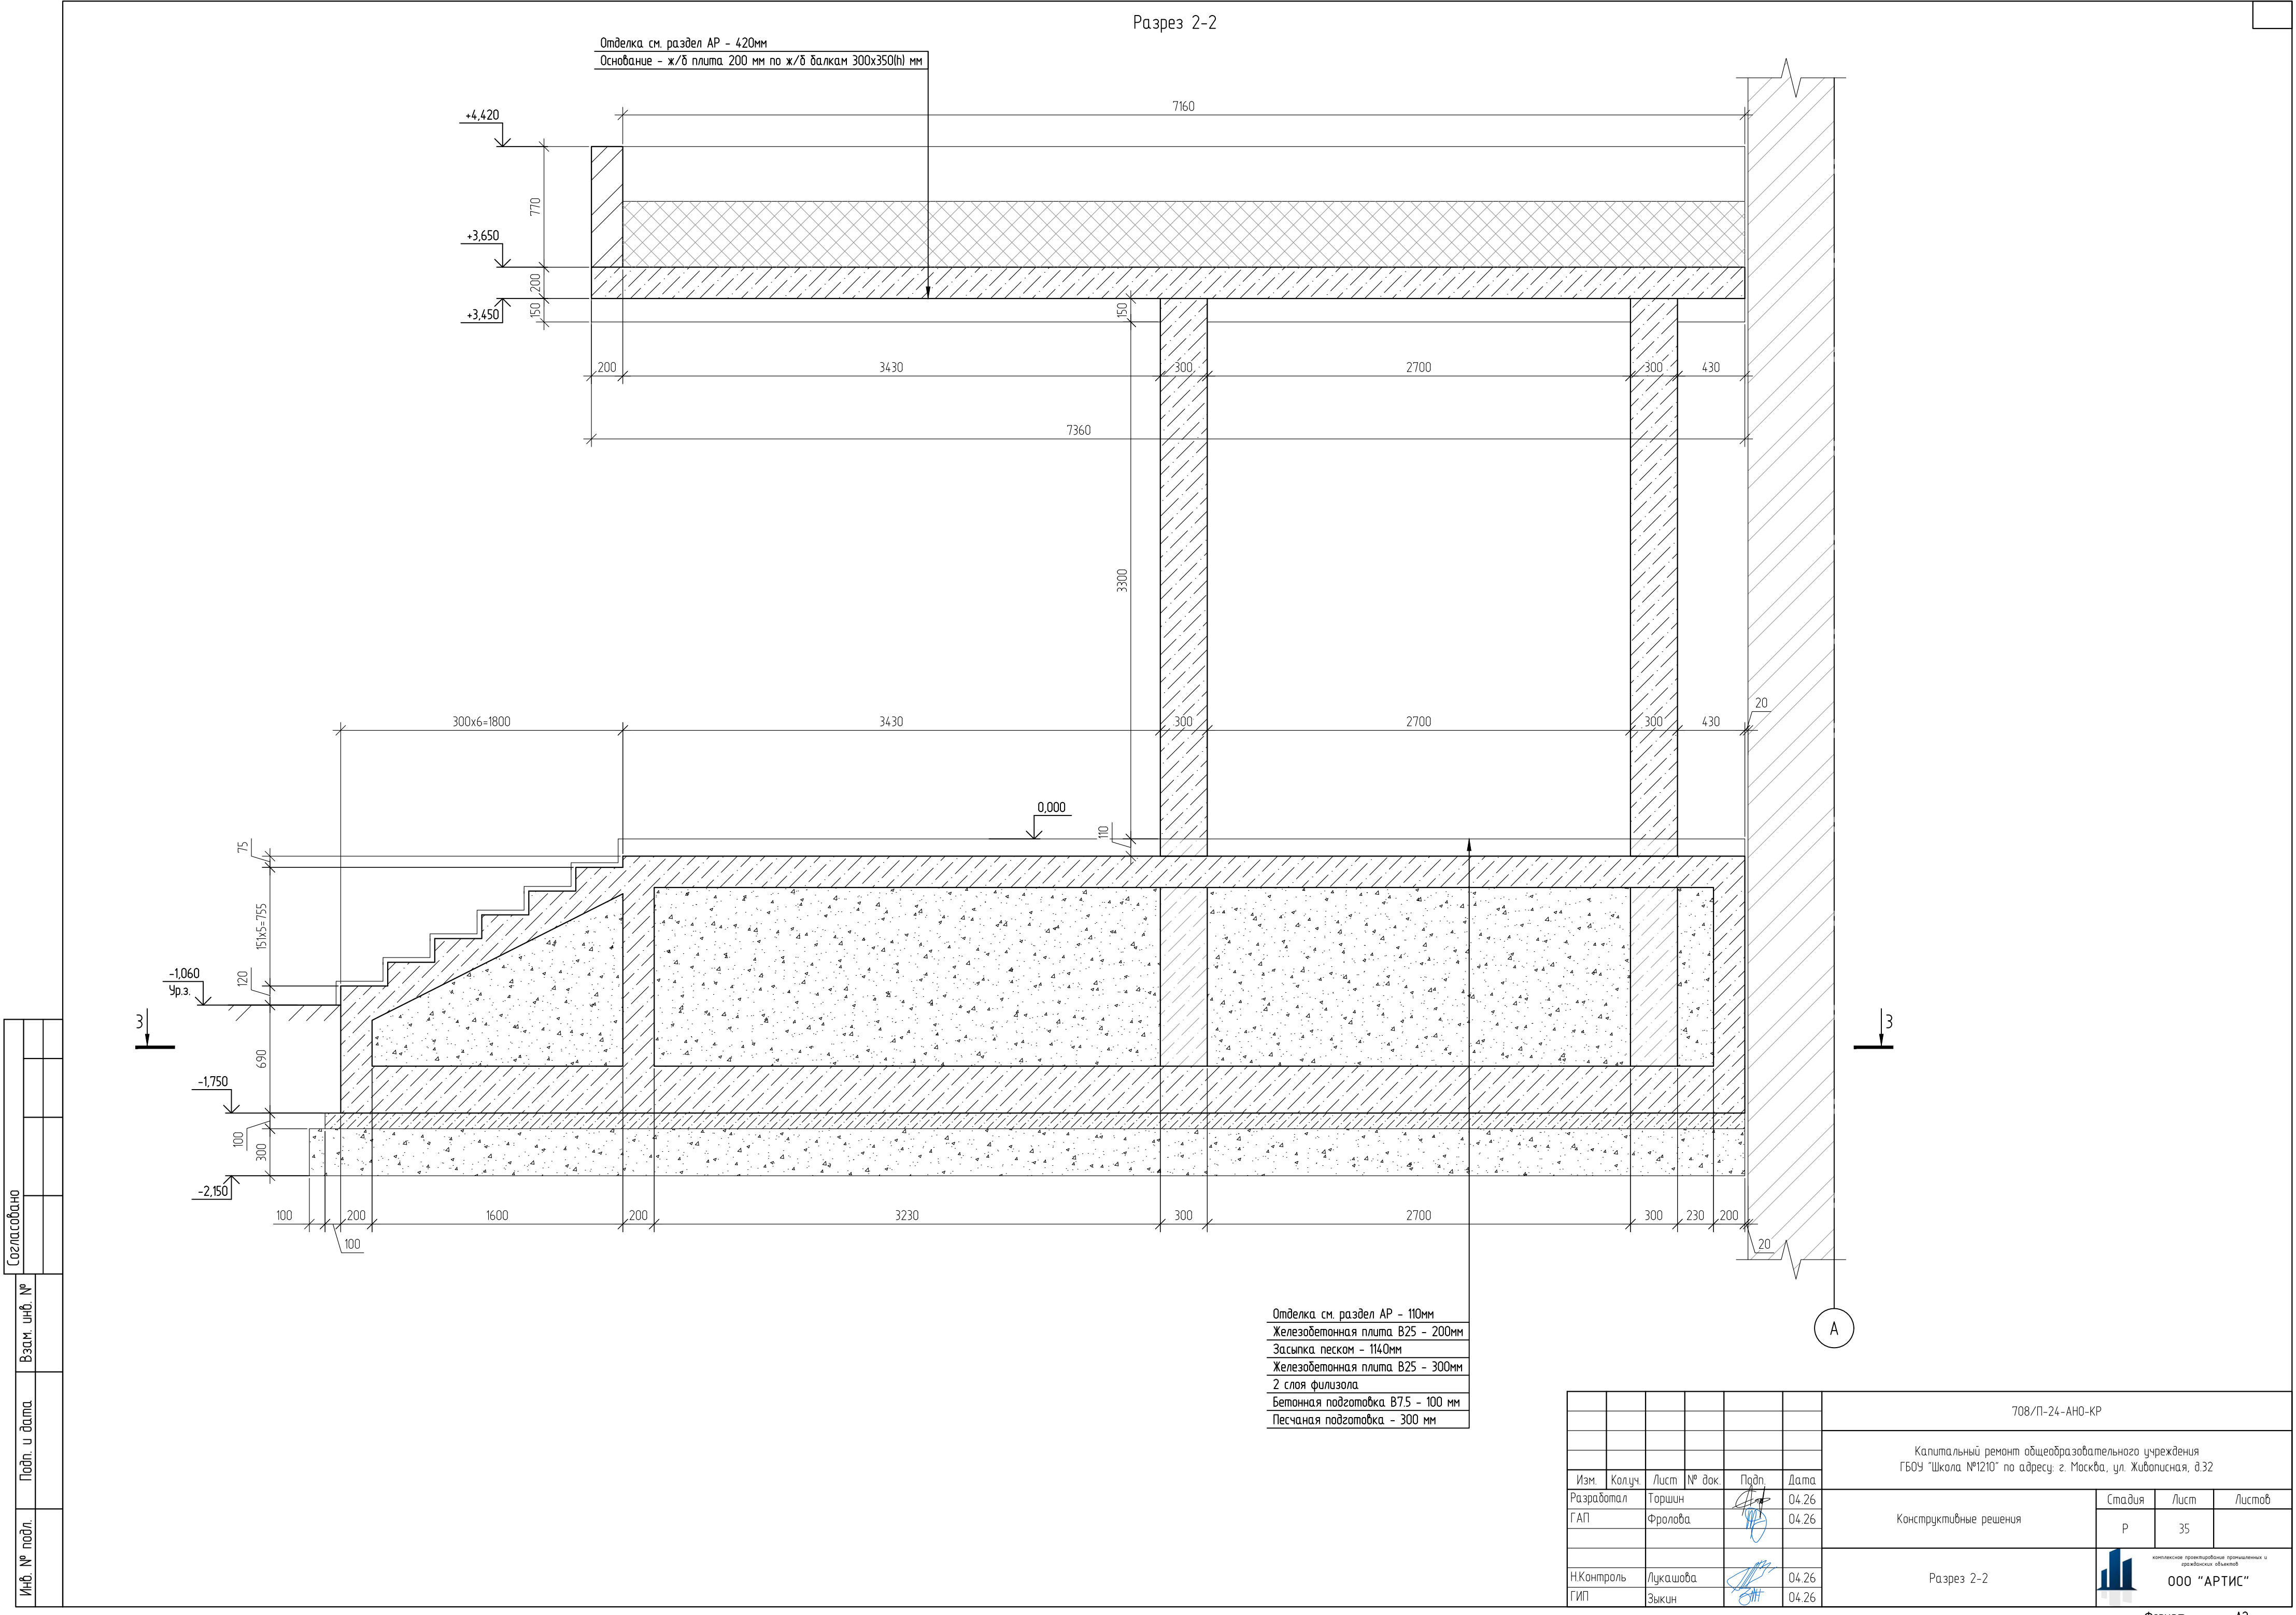


Разрез 3-3

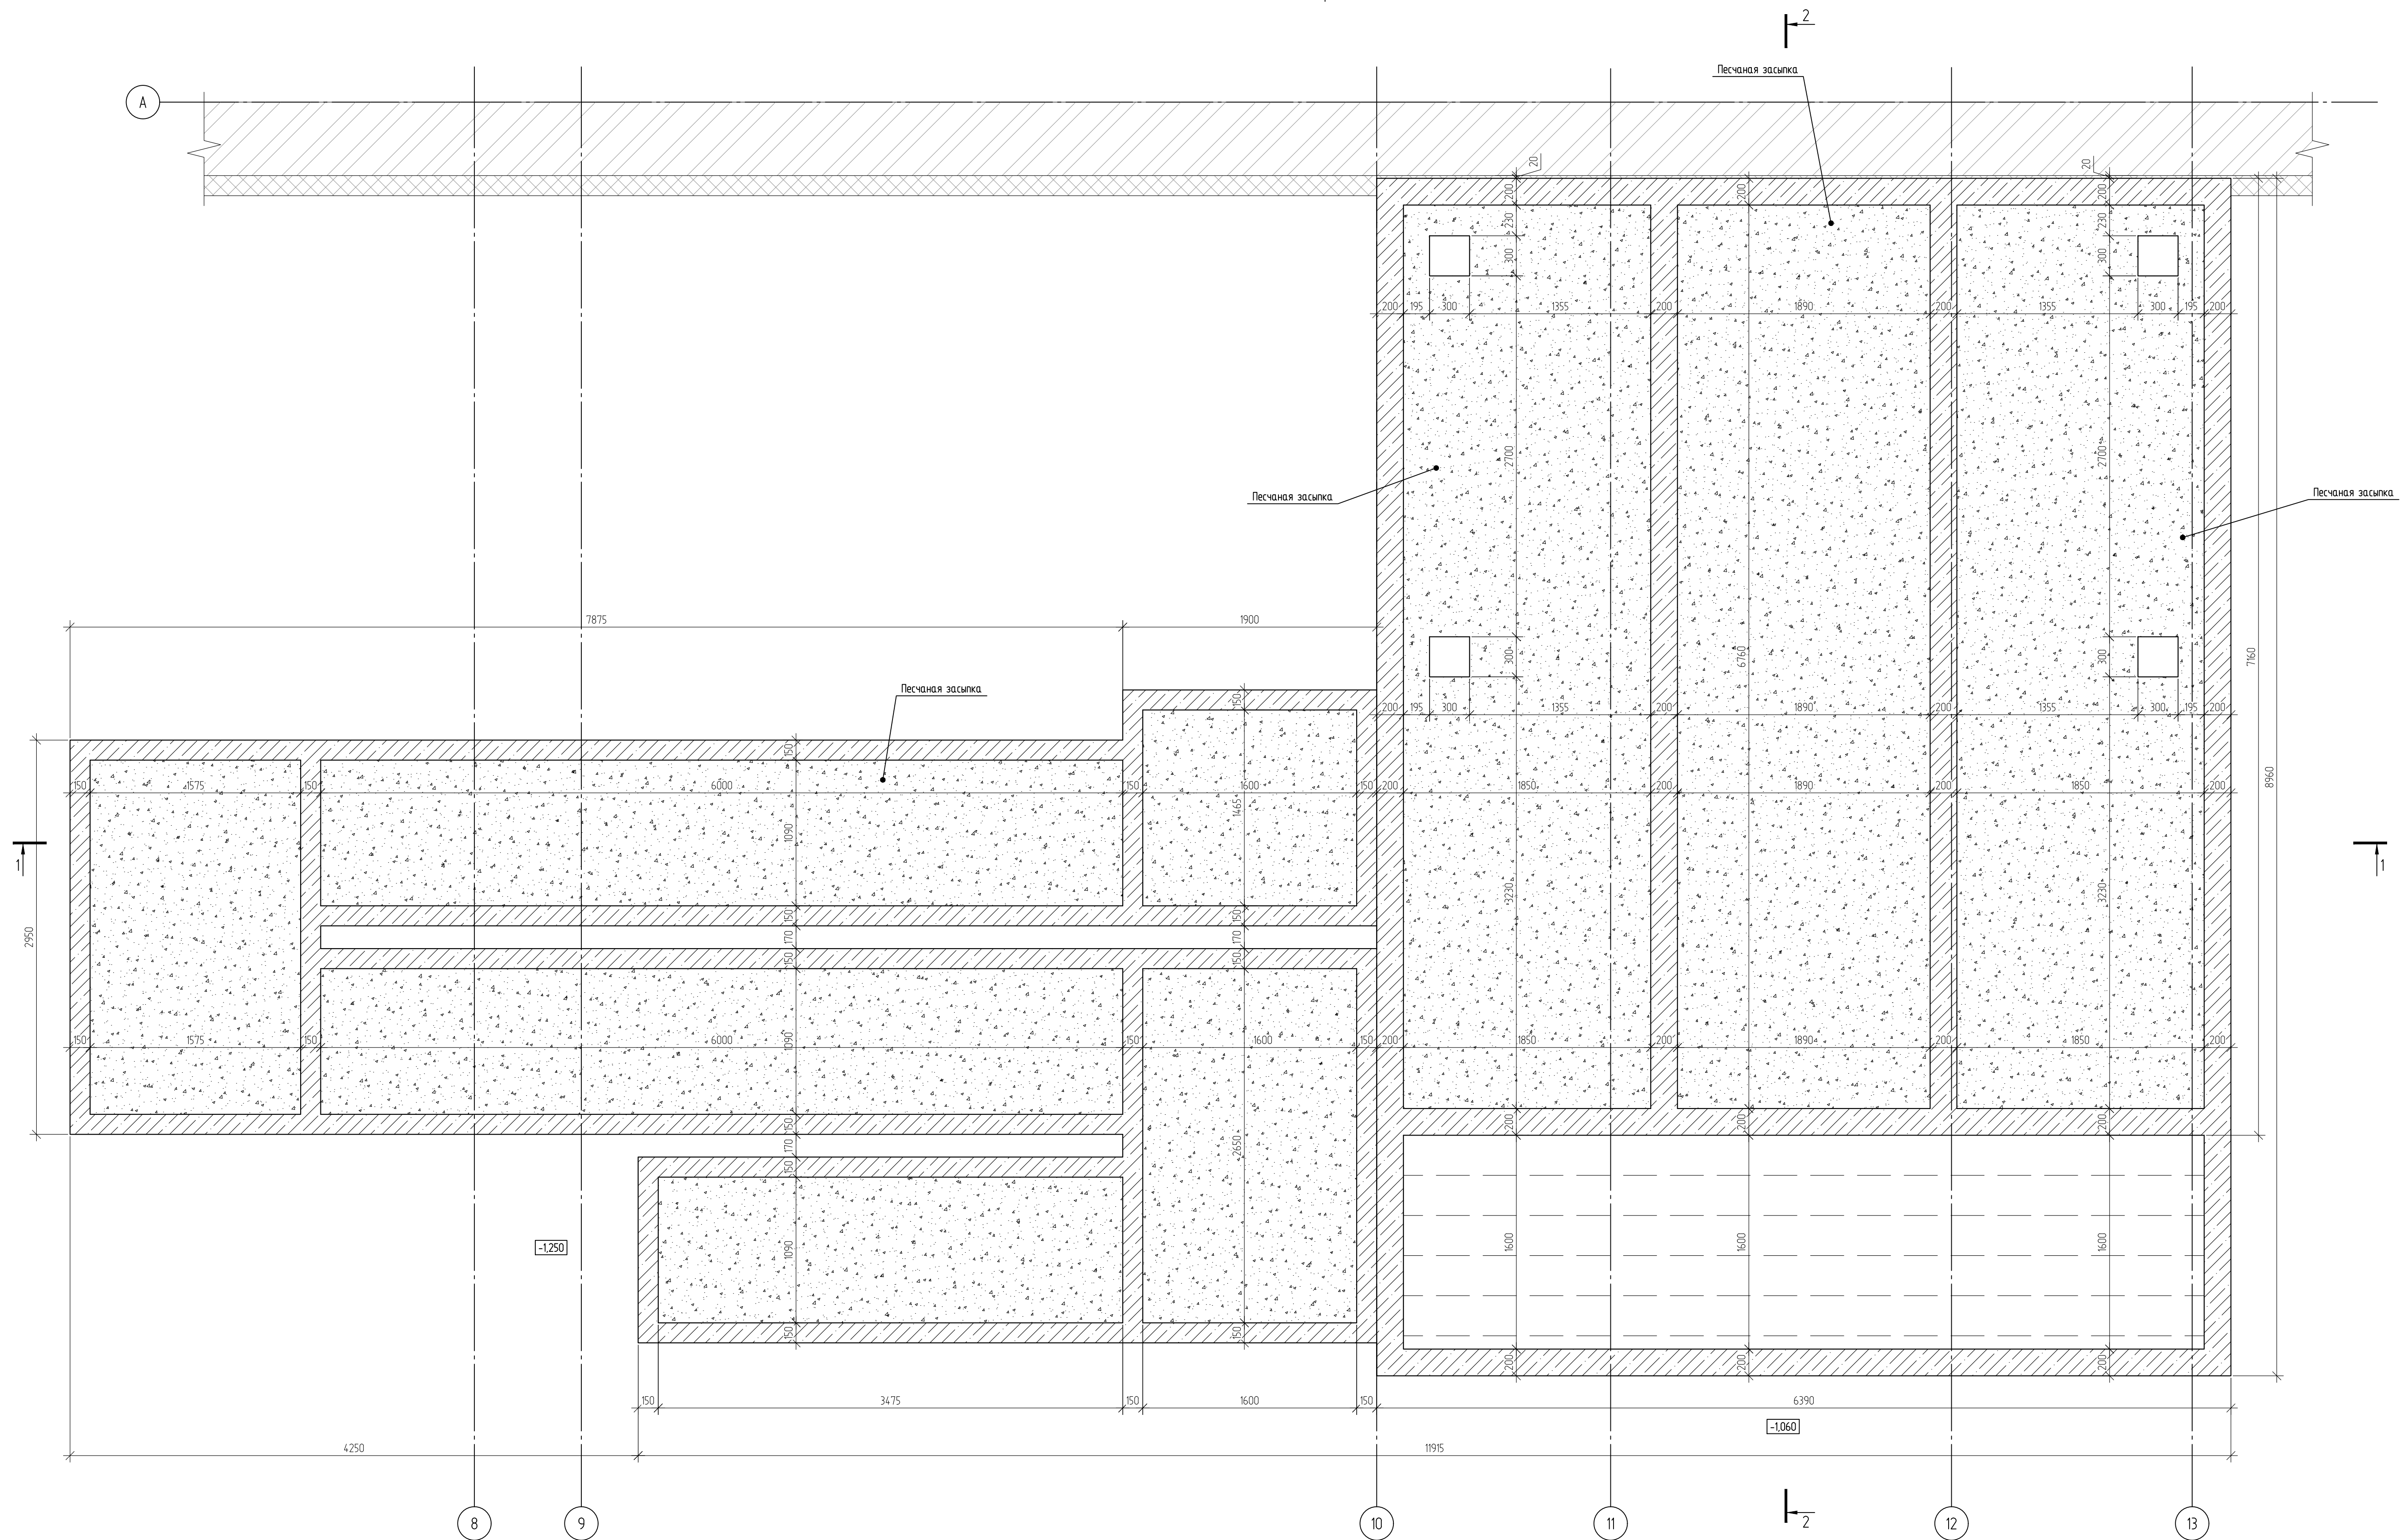

							708/П-24- АНО-КР
							Капитальный ремонт общеобразовательного учреждения ГБОУ "Школа №1210" по адресу: г. Москва, ул. Хлебническая, д.32
Изм	Колуч	Лист	№ док	Подп	Дата		Станд
Разработал	Горшин	Фралава			04.26		Лист
ГАП					04.26	Конструктивные решения	Р
							36
Н.Контроль	Лукашова				04.26	Разрез 3-3	 ООО "АРТИС"
ГИП	Эркин				04.26		






Схема армирования плиты основания входа в осях "9-13/А"

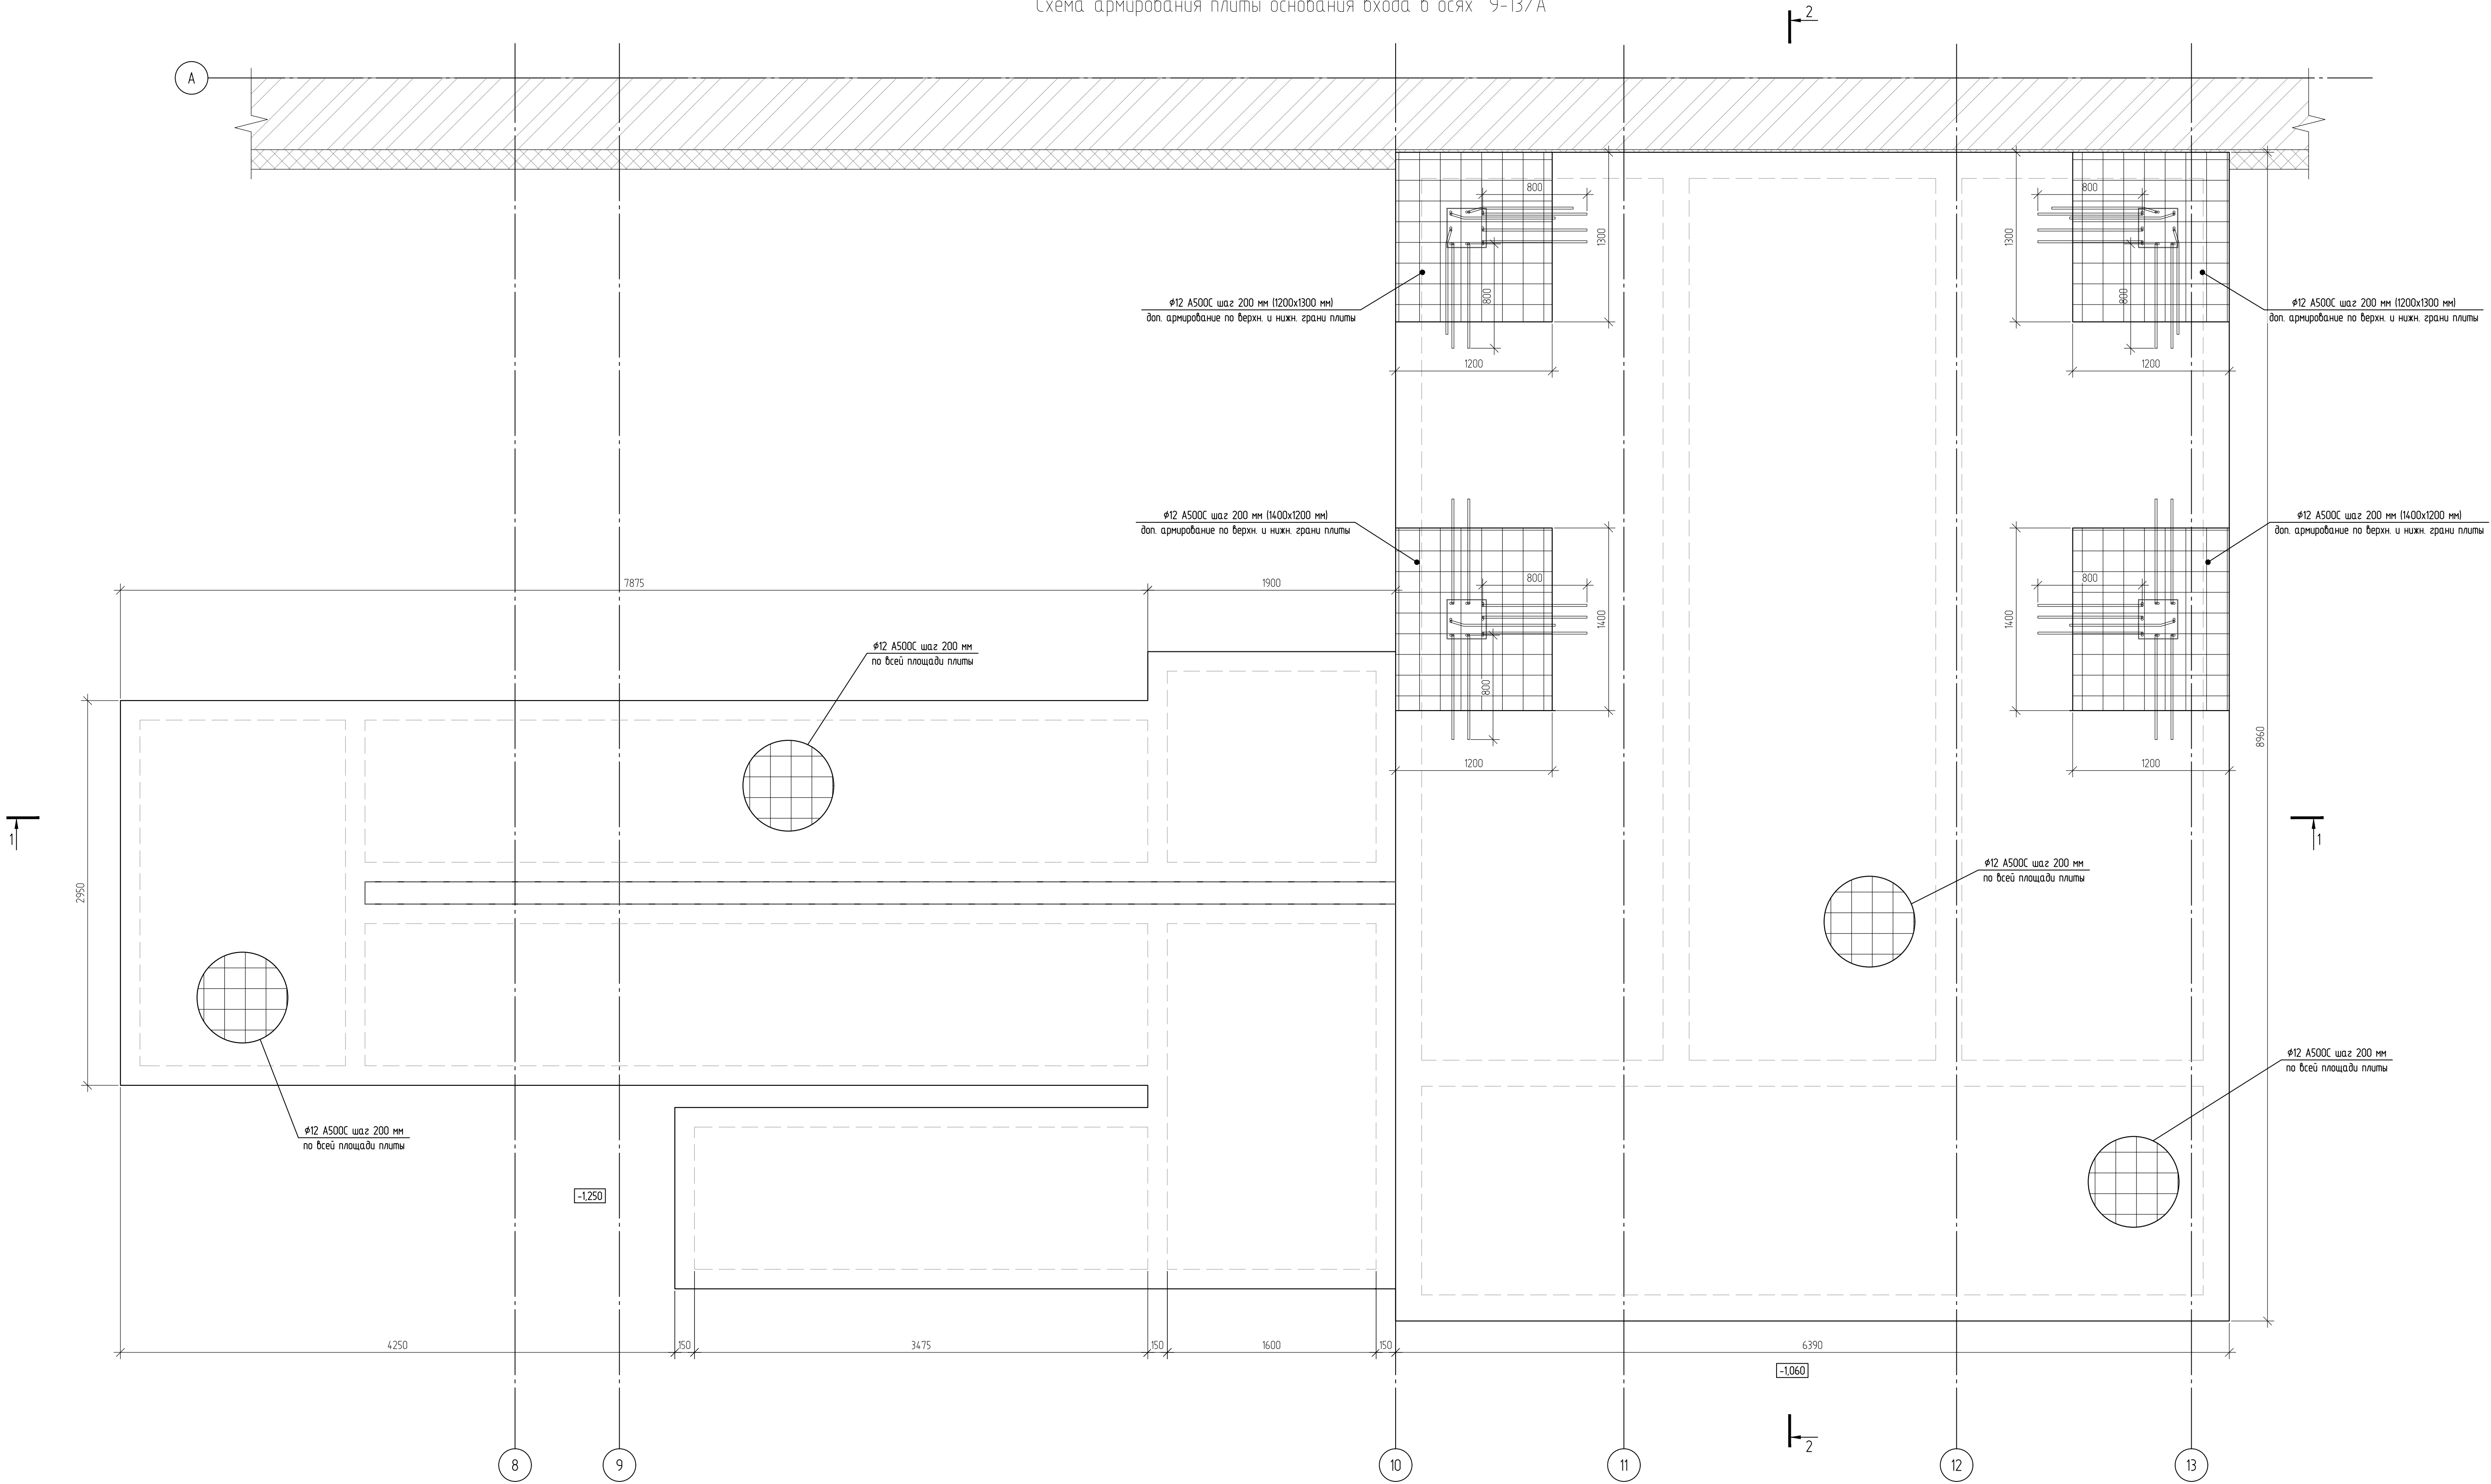

1. Фундаментную плиту, плиту площадки и козырька армировать отдельными стержнями $\phi 12$ A500C с шагом 200x200 мм. Вся рабочая арматура соединяется в сетки с помощью вязальной проволоки. В сетках вязке подлежат пересечения стержней через одно в шахматном порядке.
2. Соединение стержней по длине производить внахлест с перепуском не менее 45 диаметров стержней арматуры. В одном условном сечении не более 50% стержней арматуры.
3. Размеры хомутов и гнутых деталей даны для справки. Данные размеры следует уточнять и корректировать по месту для соответствия нижней и верхней сеток проектному.
4. Стыки смежных стержней разносить в шахматном порядке.
5. Фиксаторы положения сеток (лягушки) на чертеже не показаны и в спецификации не учтены.
6. Рабочую арматуру колонн отогнуть в плоскость верхней сетки

						708/П-24-АН0-КР			
						Капитальный ремонт общеобразовательного учреждения ГБОУ "Школа №1210" по адресу: г. Москва, ул. Жилищная, д.32			
Изм.	Копуч	Лист	№ док.	Подп.	Дата	Конструктивные решения	Стадия	Лист	Листов
Разработал	Горшин				04.26		Р	37	
ГАП	Фралова				04.26				
						Схема армирования плиты основания входа в осях "9-13/А"			
Н.Контроль	Лукашова				04.26	 ООО "АРТИС" является производителем и дистрибутором изделий	ООО "АРТИС"		
ГИП	Зыкин				04.26				


Согласовано	
Изм. № подл.	
Взам. инв. №	
Подп. и дата	

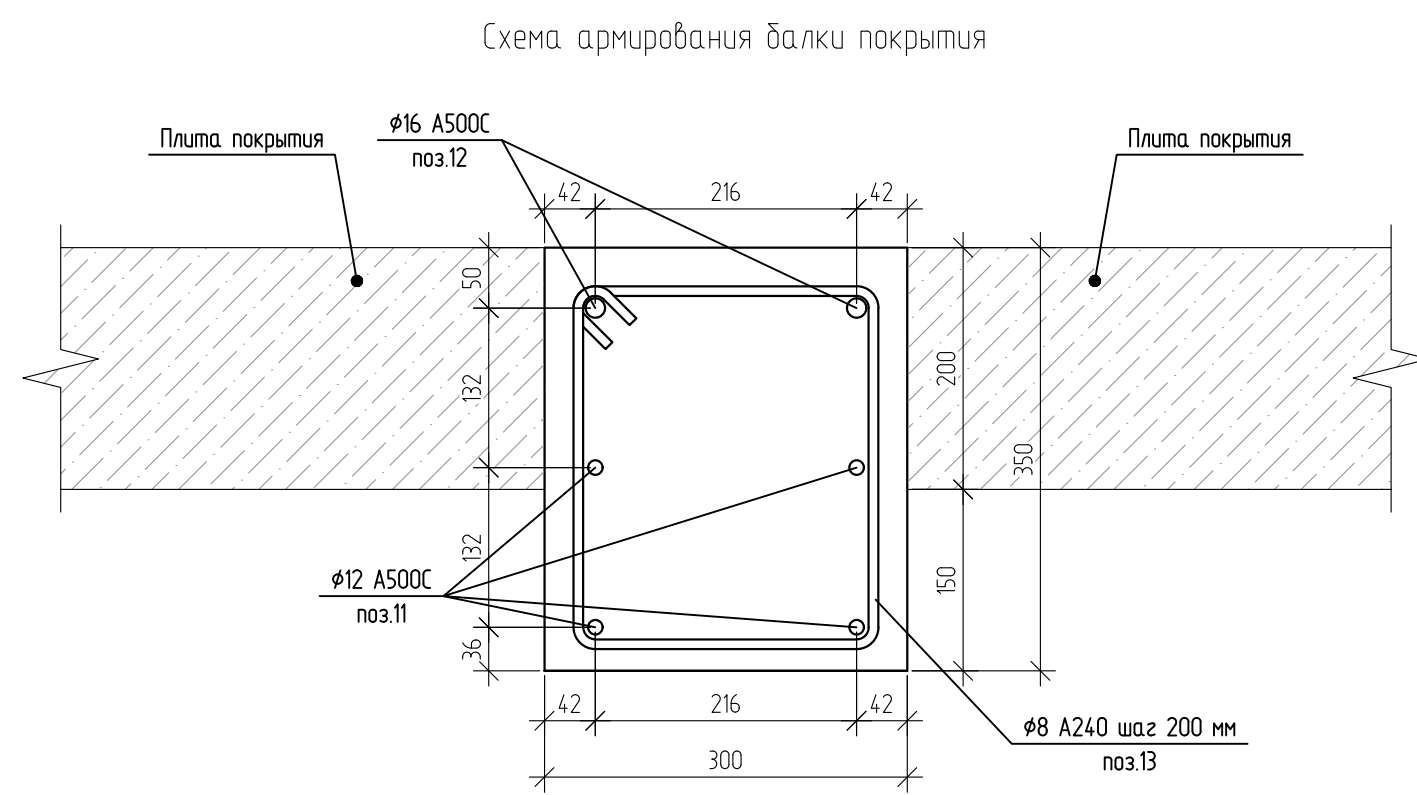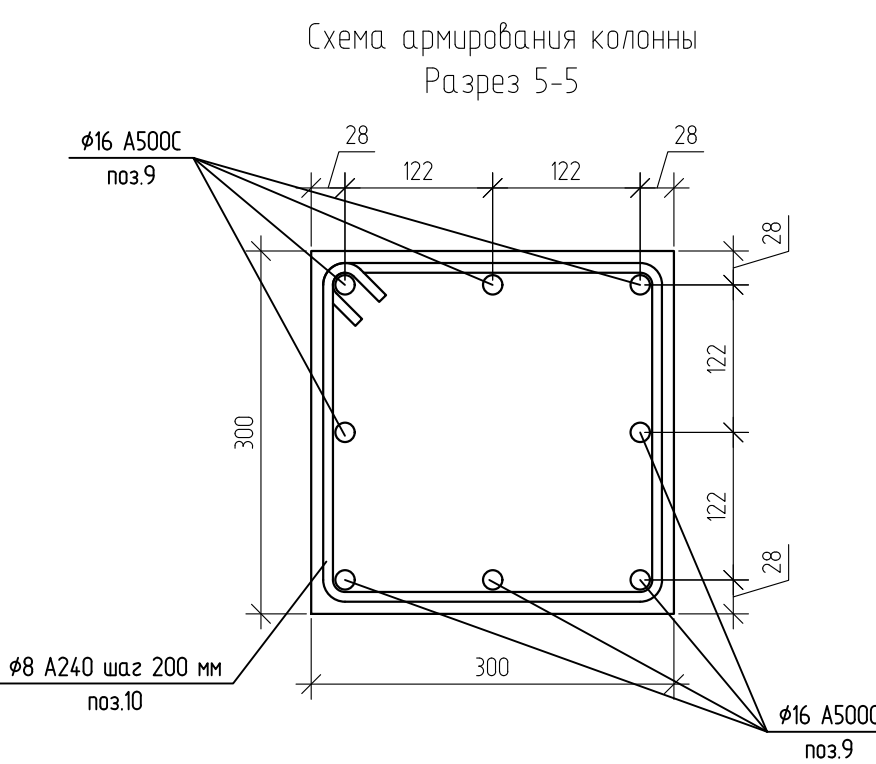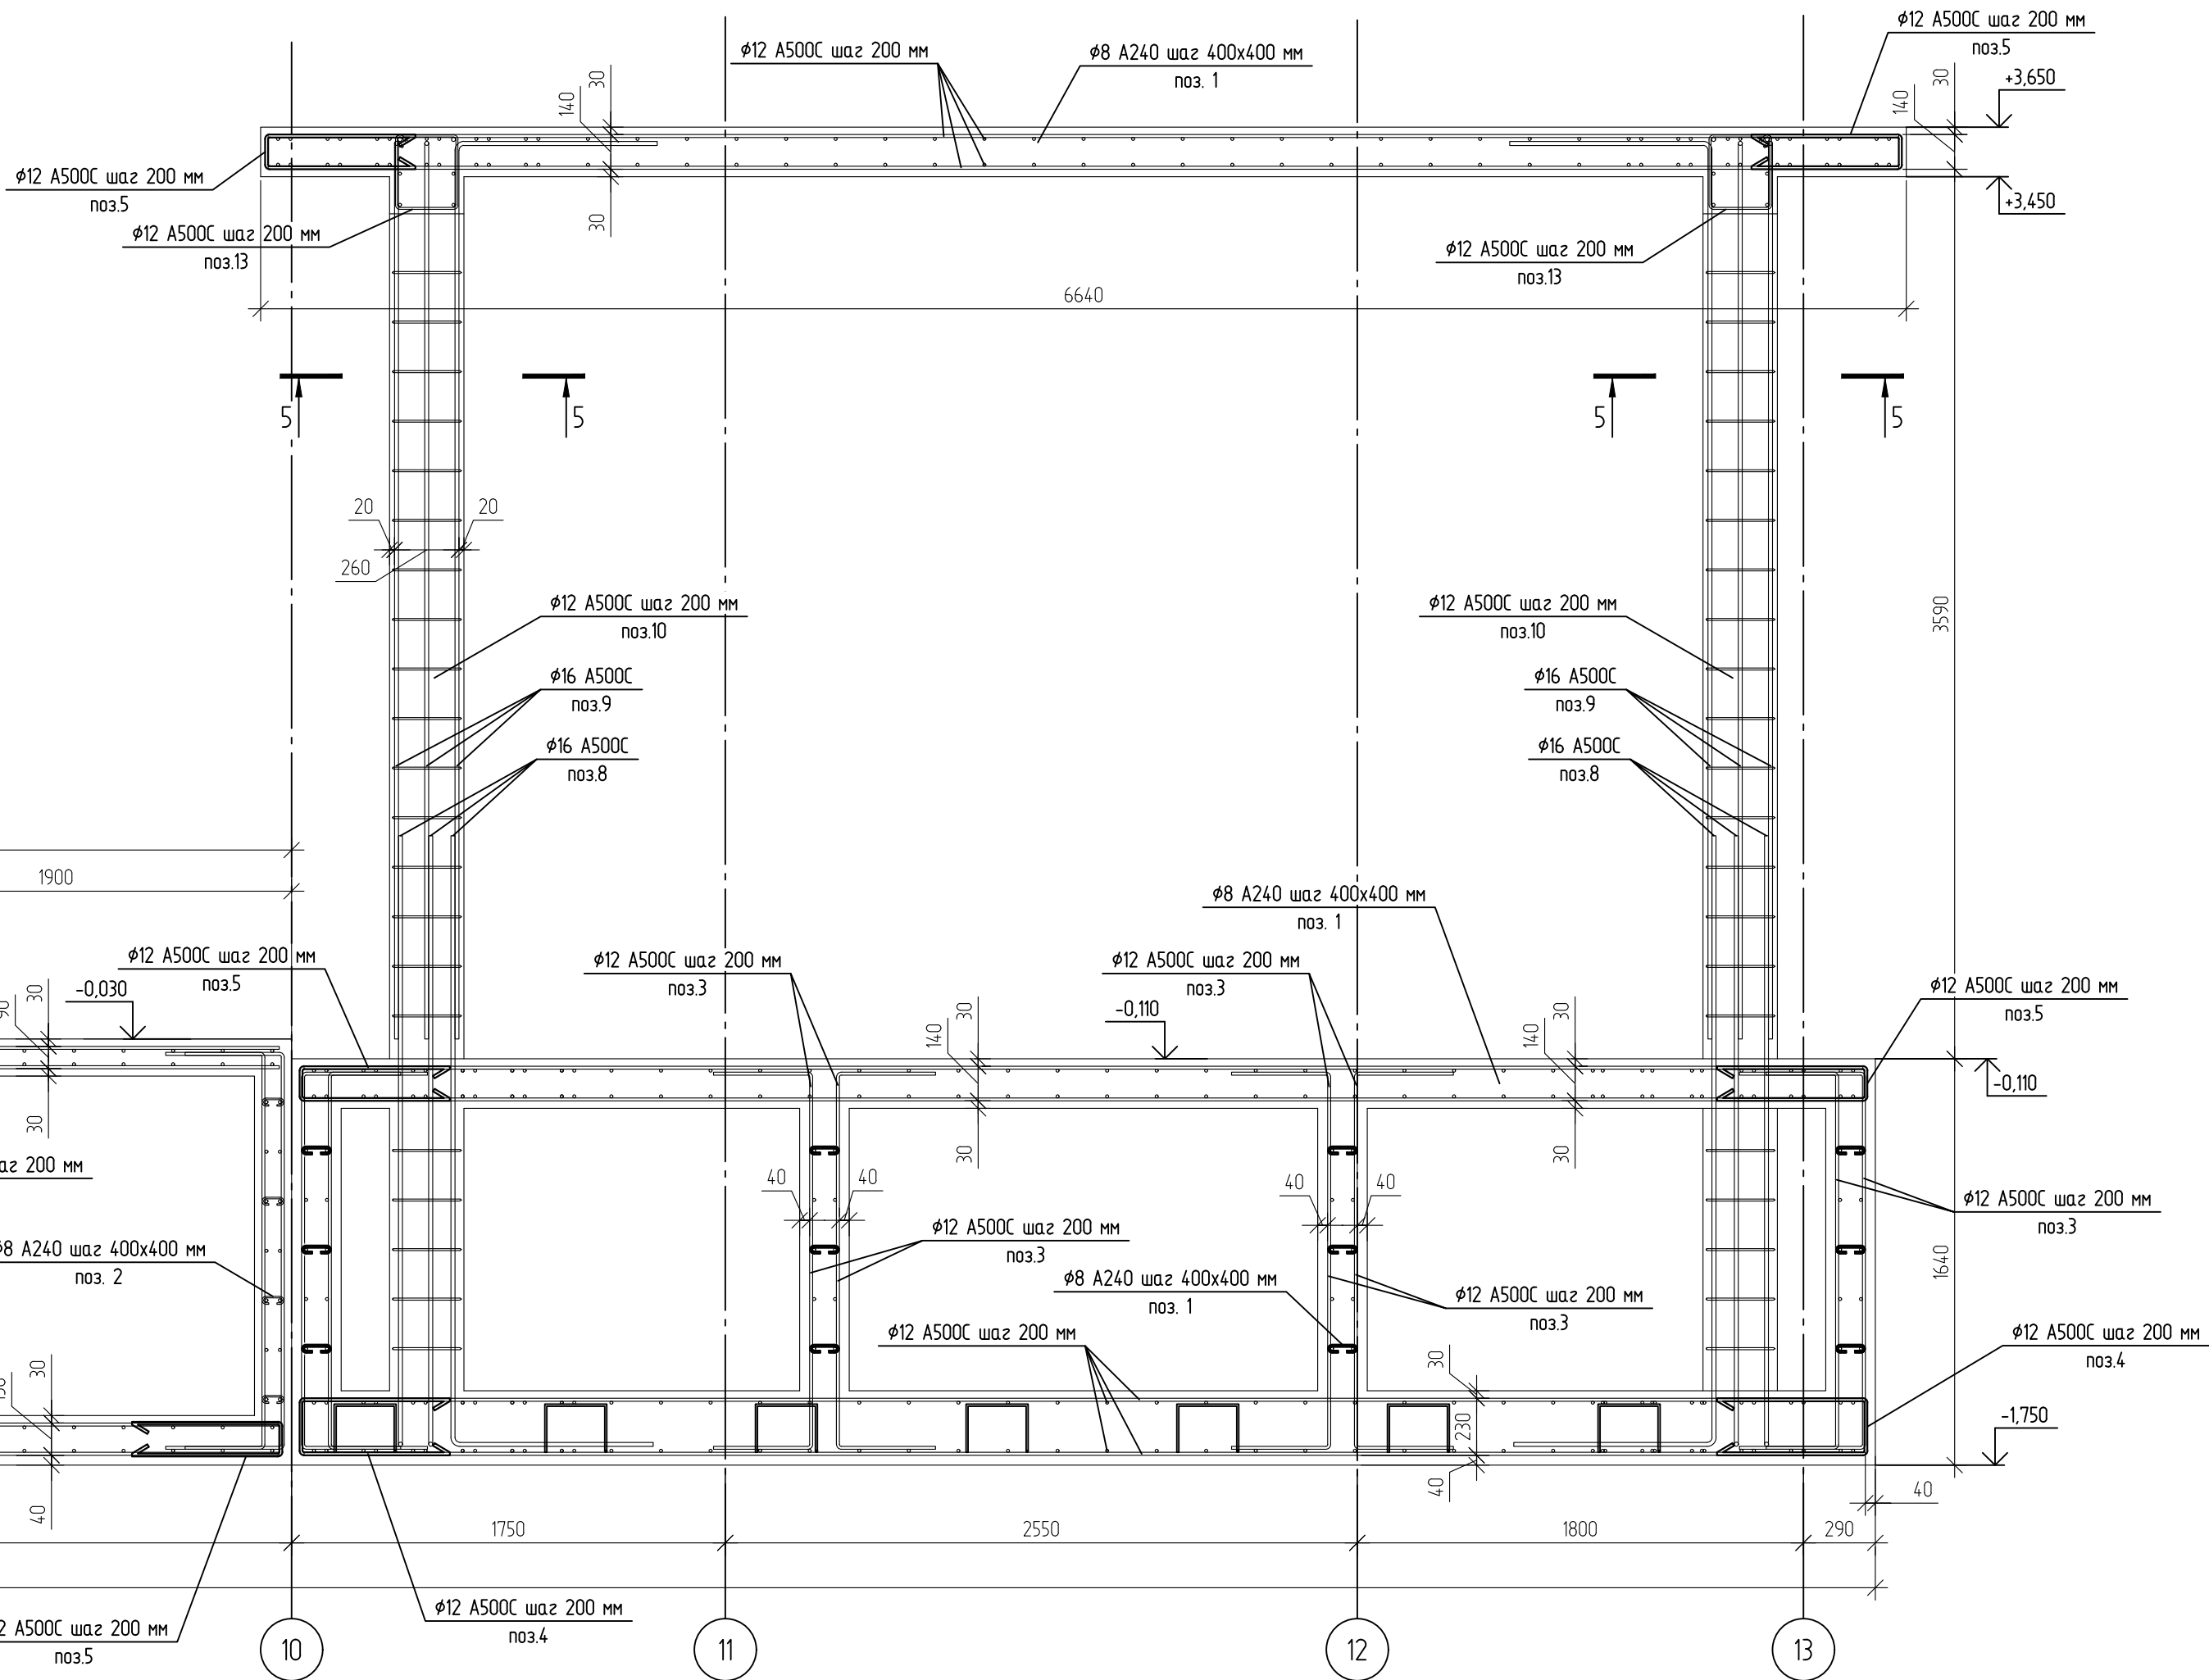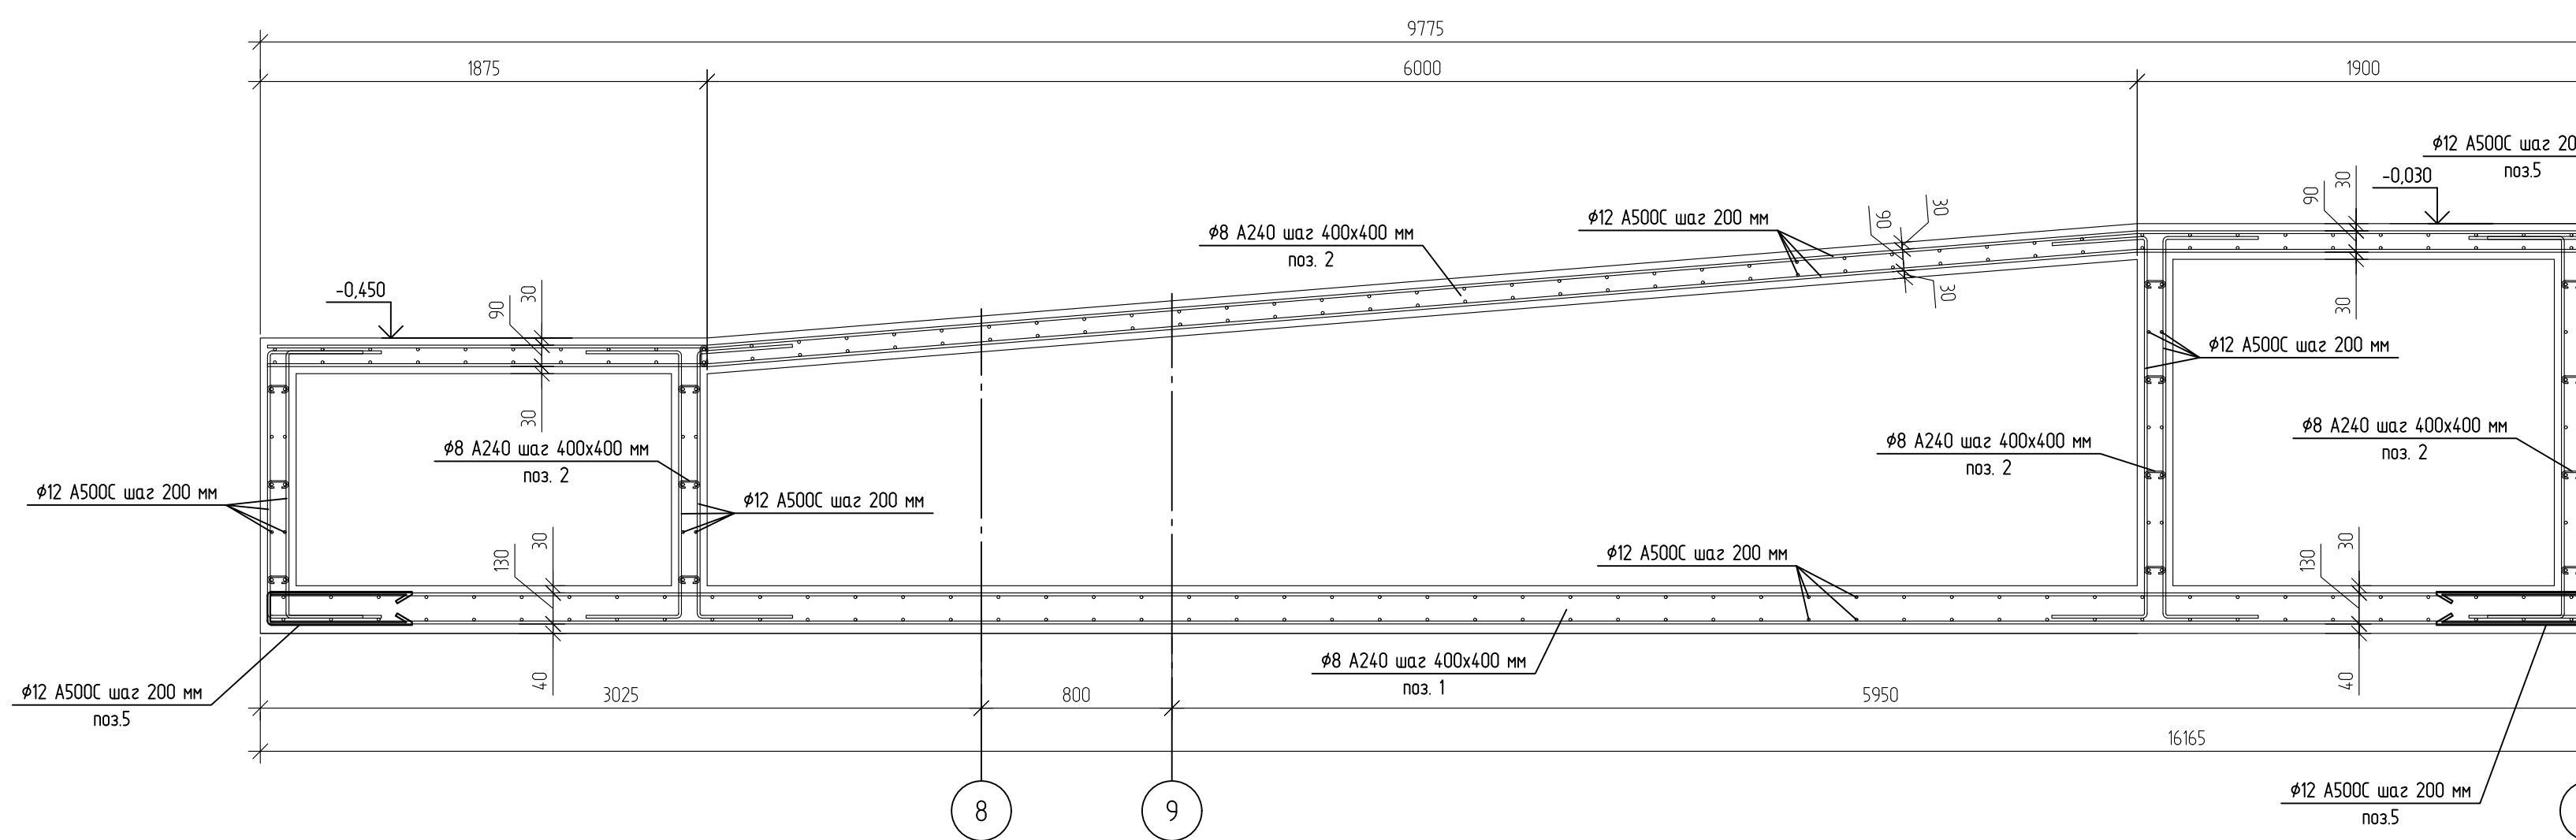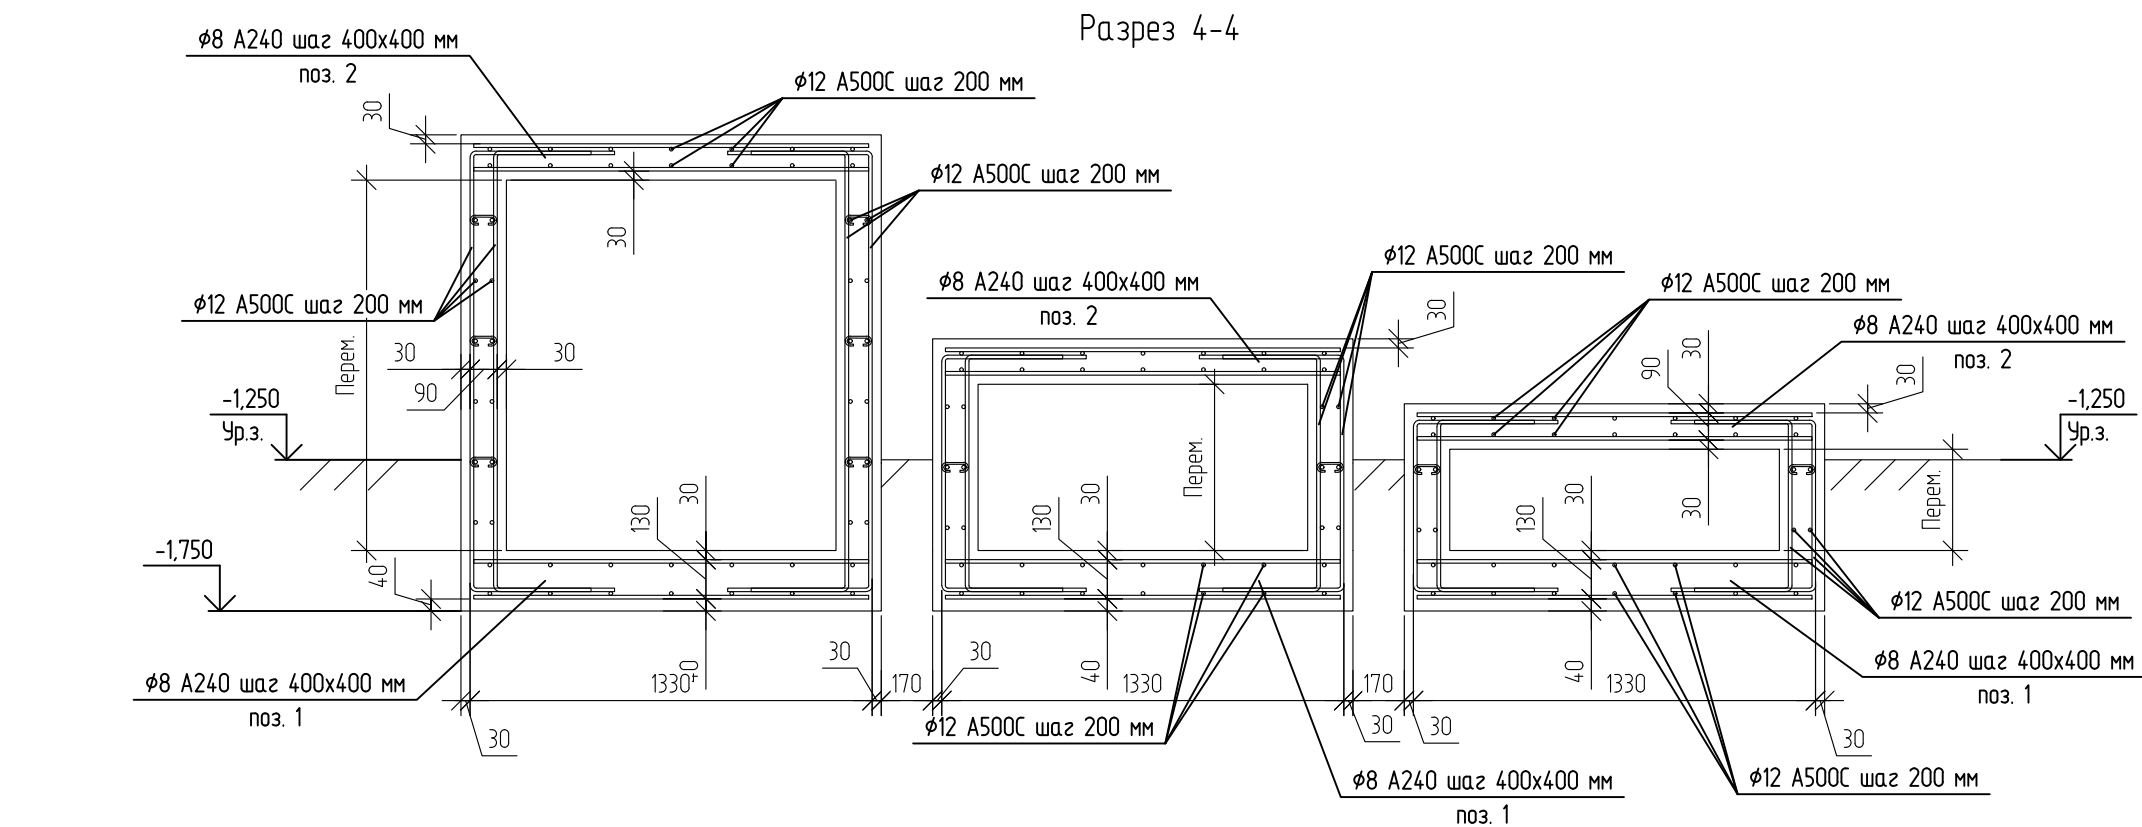

1. Фундаментную плиту, плиту площадки и козырька армировать отдельными стержнями $\phi 12$ A500C с шагом 200x200 мм. Вся рабочая арматура соединяется в сетки с помощью вязальной проволоки. В сетках вязке подлежат пересечения стержней через одно в шахматном порядке.
2. Соединение стержней по длине производить внахлест с перепуском не менее 45 диаметров стержней. В одном условном сечении не более 50% стыкуемой арматуры.
3. Размеры хомутов и гнутых деталей даны для справки. Данные размеры следует уточнять и корректировать по месту для соответствия нижней и верхней сеток проектному.
4. Стыки смежных стержней разносить в шахматном порядке.
5. Фиксаторы положения сеток (лягушки) на чертеже не показаны и в спецификации не учтены.
6. Рабочую арматуру колонн отогнуть в плоскость верхней сетки

						708/П-24-АНО-КР			
						Капитальный ремонт общеобразовательного учреждения ГБОУ "Школа №1210" по адресу: г. Москва, ул. Живописная, д.32			
Изм	Колуч	Лист	№ док	Подп	Дата	Конструктивные решения	Стадия	Лист	Листов
Разработал	Торшин				04.26		Р	38	
ГАП	Фролова				04.26				
Н.Контроль	Лукашова				04.26	Армирование. Разрез 1-1, 5-5. Схема армирования балки покрытия	 компания проектирует, строит и эксплуатирует объекты	ООО "АРТИС"	
ГИП	Зыкин				04.26				

Армирование. Разрез 2-2

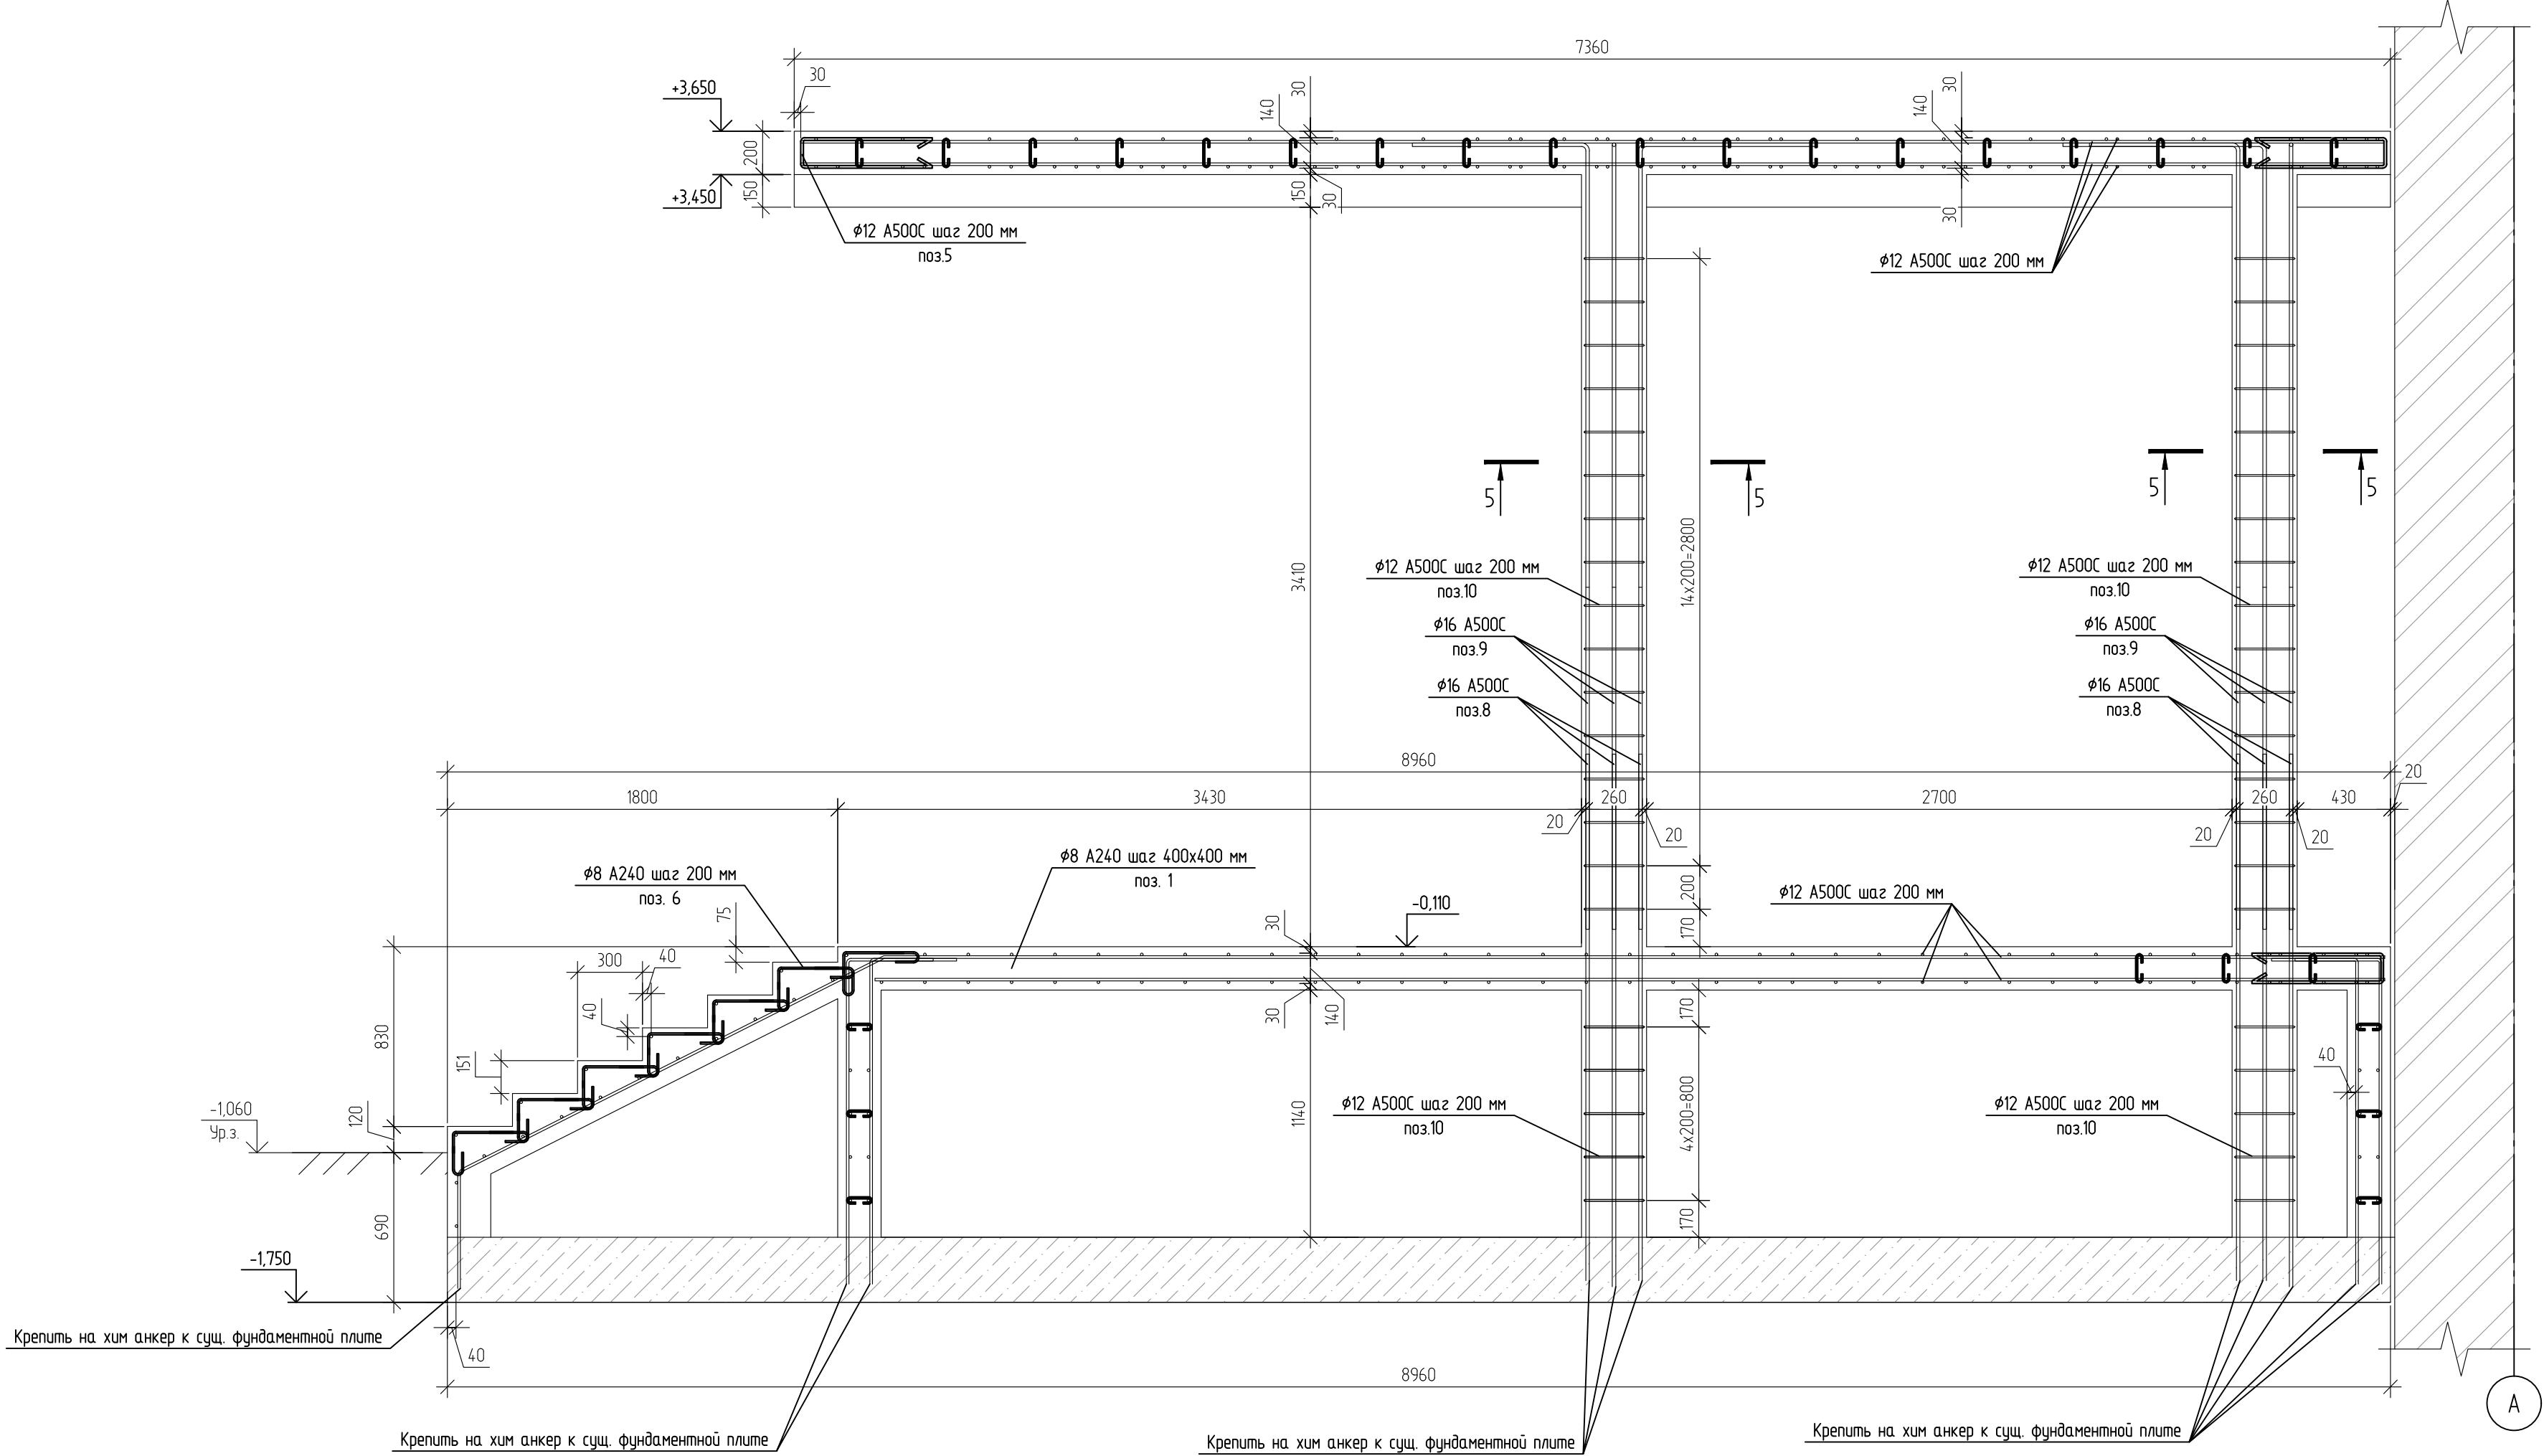

Согласовано	
Взам. инв. №	
Подп. и дата	
Инв. № подл.	

						708/П-24-АНО-КР			
						Капитальный ремонт общеобразовательного учреждения ГБОУ "Школа №1210" по адресу: г. Москва, ул. Живописная, д.32			
Изм.	Колуч.	Лист	№ док.	Подп.	Дата	Конструктивные решения	Стадия	Лист	Листов
Разработал	Торшин				04.26		Р	39	
ГАП	Фролова				04.26	Армирование. Разрез 2-2	 комплексное проектирование промышленных и гражданских объектов ООО "АРТИС"		
Н.Контроль	Лукашова				04.26				
ГИП	Зыкин				04.26				

Согласовано			
Взам. инв. №			
Подп. и дата			
Инв. № подл.			

Спецификация материалов на устройство входа в осях "8-13/А"

Поз.	Обозначение	Наименование	Кол.	Масса 1 дет.,кг	Примеч. общ. вес кг
		Пандус			
	ГОСТ 34028-2016	Ø12 А500С, п.м.	3633	0.888	3226.1
1	ГОСТ 34028-2016	Ø8 А240, L=160 мм, шт	256	0.06	15.36
2	ГОСТ 34028-2016	Ø8 А240, L=140 мм, шт	874	0.06	52.44
		Материалы			
		Бетон В25, W6, F150, м³	23.7		
		Бетон В7.5, м³	4.1		
		Песок средней крупности, м³	12.8		
		Площадка входа			
	ГОСТ 34028-2016	Ø12 А500С, п.м.	1815	0.888	1611.72
3	ГОСТ 34028-2016	Ø12 А500С, L=2522 мм, шт	418	2.25	940.5
4	ГОСТ 34028-2016	Ø12 А500С, L=1420 мм, шт	142	1.26	178.92
5	ГОСТ 34028-2016	Ø12 А500С, L=1330 мм, шт	138	1.18	162.84
6	ГОСТ 34028-2016	Ø8 А240, L=600 мм, шт	224	0.24	53.76
7	ГОСТ 34028-2016	Ø8 А240, L=1094 мм, шт	100	0.44	44
1	ГОСТ 34028-2016	Ø8 А240, L=160 мм, шт	536	0.06	32.16
		Материалы			
		Бетон В25, W6, F150, м³	39.8		
		Бетон В7.5, м³	5.9		
		Песок средней крупности, м³	18.12		
		Колонны	4		
8	ГОСТ 34028-2016	Ø16 А500С, L=3260 мм, шт	32	3.15	100.8
9	ГОСТ 34028-2016	Ø16 А500С, L=4430 мм, шт	32	7	224
10	ГОСТ 34028-2016	Ø8 А240, L=1140 мм, шт	104	0.45	46.8
		Материалы			
		Бетон В25, W6, F150, м³	1.8		

Спецификация материалов на устройство входа в осях "8-13/А"







Поз.	Обозначение	Наименование	Кол.	Масса 1 дет.,кг	Примеч. общ. вес кг
		Балки покрытия	2		
11	ГОСТ 34028-2016	Ø12 А500С, L=7360 мм, шт	8	6.55	52.4
12	ГОСТ 34028-2016	Ø16 А500С, L=7360 мм, шт	4	11.63	46.52
13	ГОСТ 34028-2016	Ø8 А240, L=1120 мм, шт	74	0.44	32.56
		Плита покрытия			
	ГОСТ 34028-2016	Ø12 А500С, п.м.	794	0.888	705.07
5	ГОСТ 34028-2016	Ø12 А500С, L=1330 мм, шт	116	1.18	136.88
1	ГОСТ 34028-2016	Ø8 А240, L=160 мм, шт	289	0.06	17.34
		Материалы			
		Бетон В25, W6, F150, м³	10.5		
		Прочие материалы			
		Гидроизоляция, м²	96		
		Кирпич керамический, м³	3.24		





Ведомость расхода стали, кг

Марка элемента	Изделия арматурные					
	Арматура класса					Всего
	A500С			A240		
	ГОСТ 34028-2016			ГОСТ 34028-2016		
	Ø16	Ø12	Итого	Ø8	Итого	
	371.32	7014.43	7385.75	294.42	294.42	7680.17





						708/П-24-АНО-КР			
						Капитальный ремонт общеобразовательного учреждения ГБОУ "Школа №1210" по адресу: г. Москва, ул. Живописная, д.32			
Изм.	Кол.уч.	Лист	№ док.	Подп.	Дата	Конструктивные решения	Стадия	Лист	Листов
Разработал	Торшин				04.26		Р	39.1	
ГАП	Фралова				04.26				
						Спецификация материалов на устройство входа в осях "8-13/А"		комплексное проектирование промышленных и гражданских объектов	
Н.Контроль	Лукашова				04.26			ООО "АРТИС"	
ГИП	Зыкин				04.26				

Согласовано			
Инв. № подл.	Подп. и дата	Взам. инв. №	

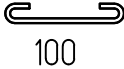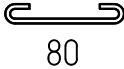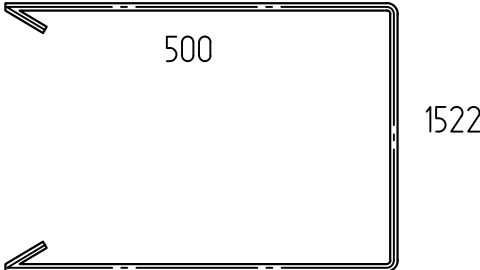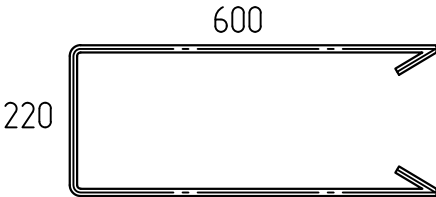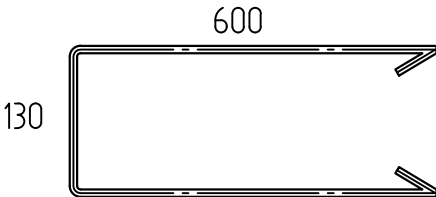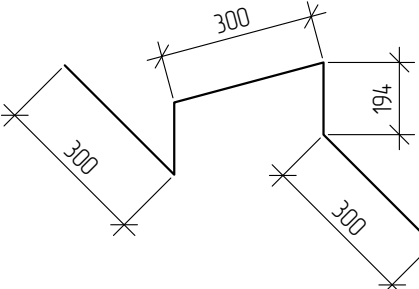
Ведомость деталей	
Поз.	Эскиз
1	
2	
3	
4	
5	
6	
7	

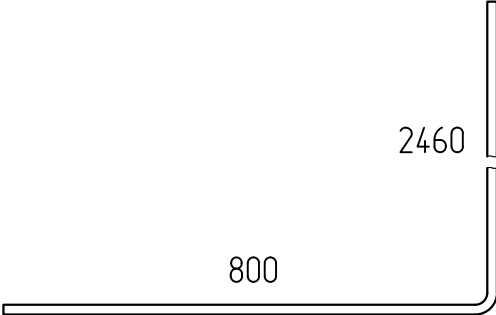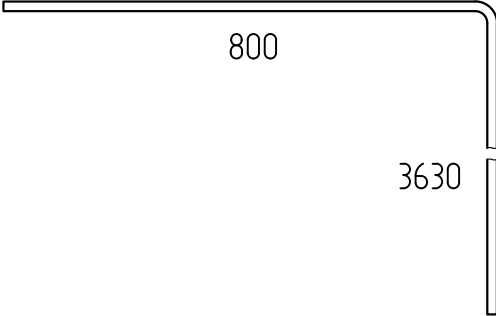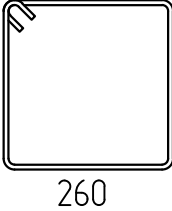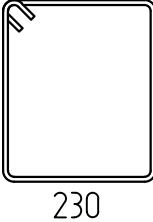Ведомость деталей	
Поз.	Эскиз
8	
9	
10	
13	


						708/П-24-АНО-КР			
						Капитальный ремонт общеобразовательного учреждения ГБОУ "Школа №1210" по адресу: г. Москва, ул. Живописная, д.32			
Изм.	Кол.уч.	Лист	№ док.	Подп.	Дата	Конструктивные решения	Стадия	Лист	Листов
Разработал	Торшин				04.26		Р	39.2	
ГАП	Фролова				04.26				
Н.Контроль	Лукашова				04.26	Ведомость деталей		комплексное проектирование промышленных и гражданских объектов ООО "АРТИС"	
ГИП	Зыкин				04.26				

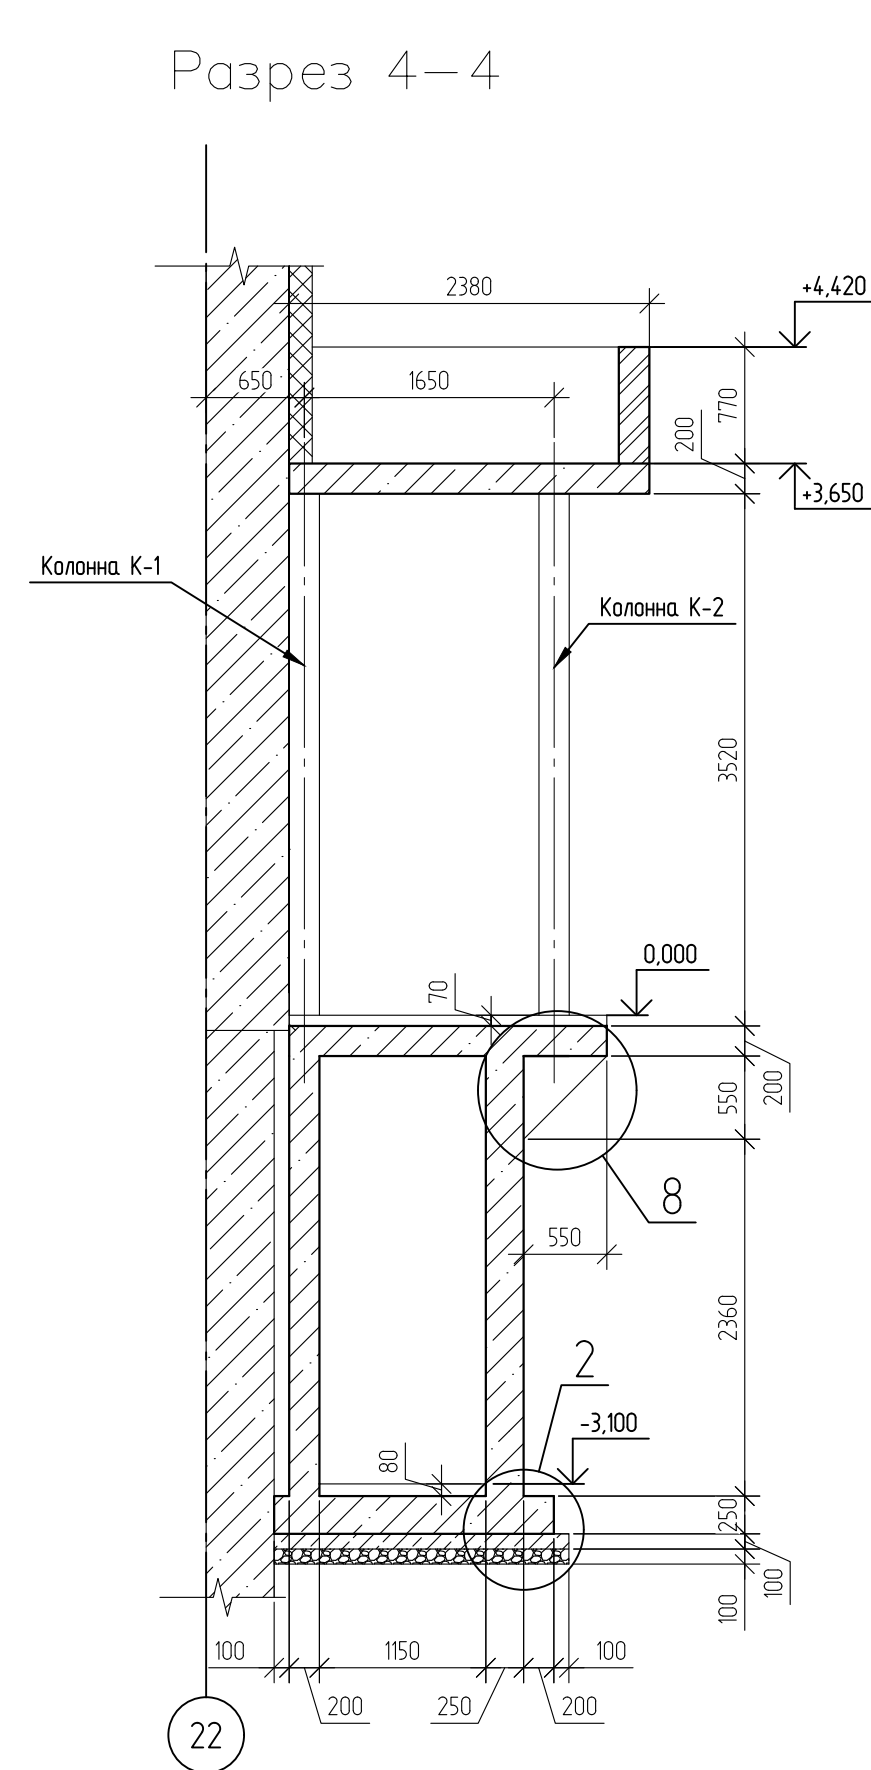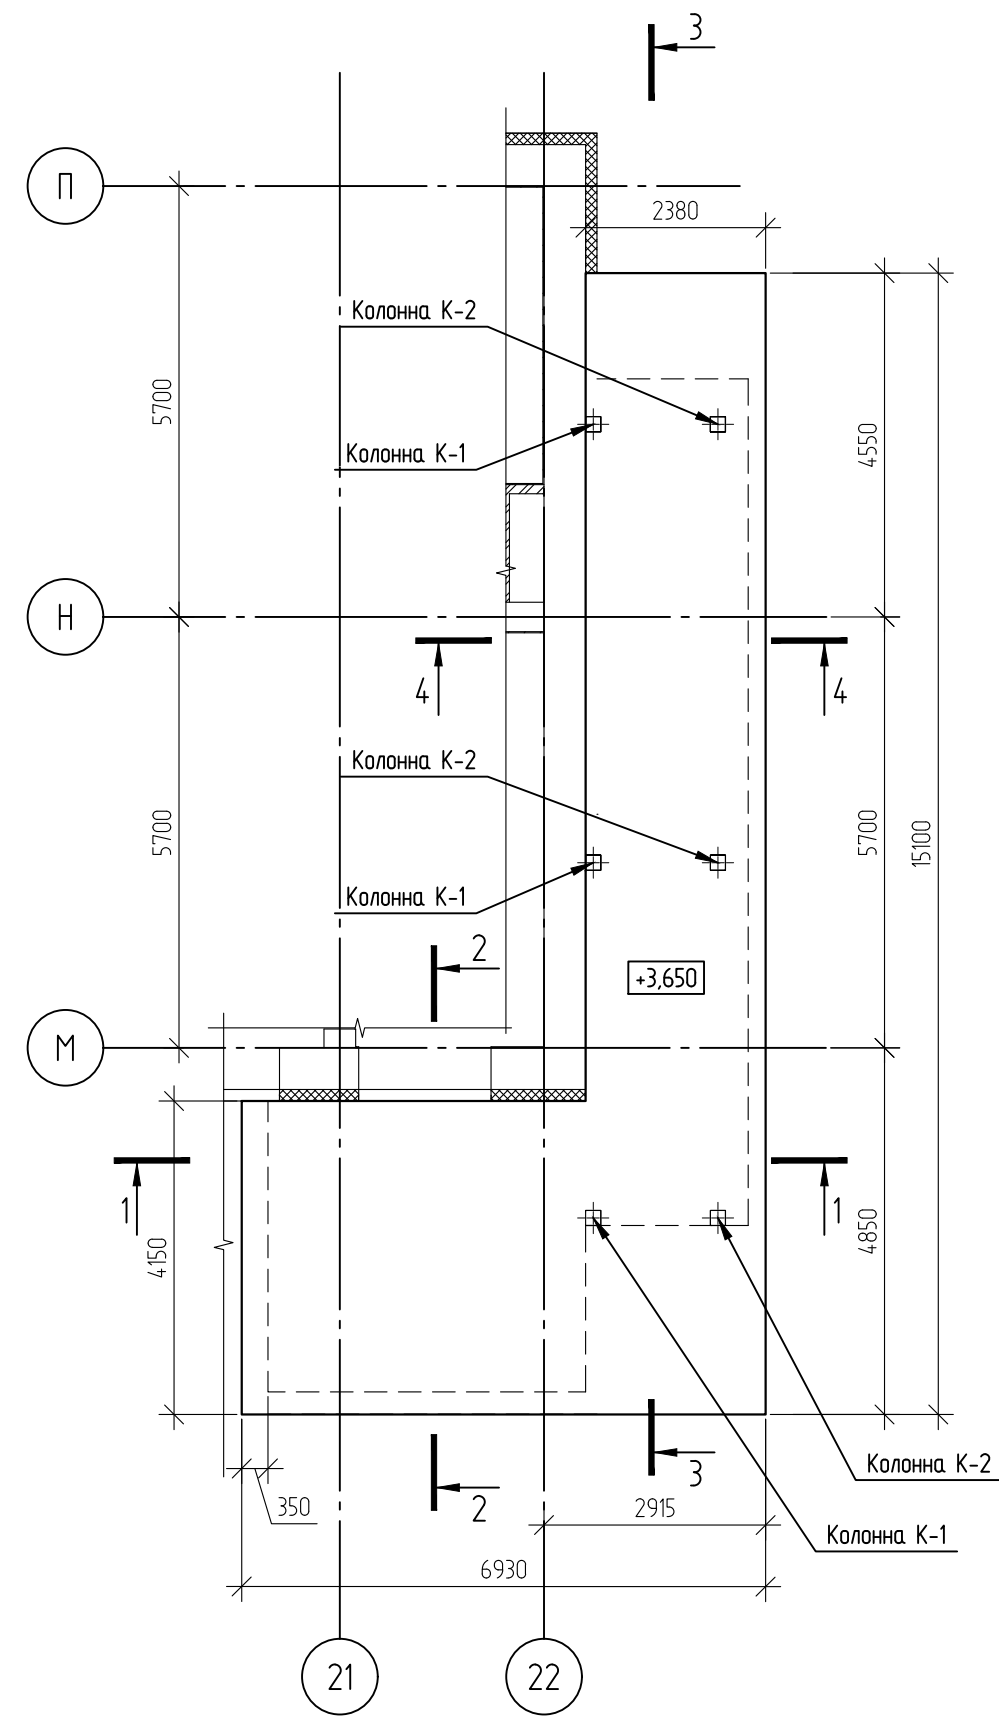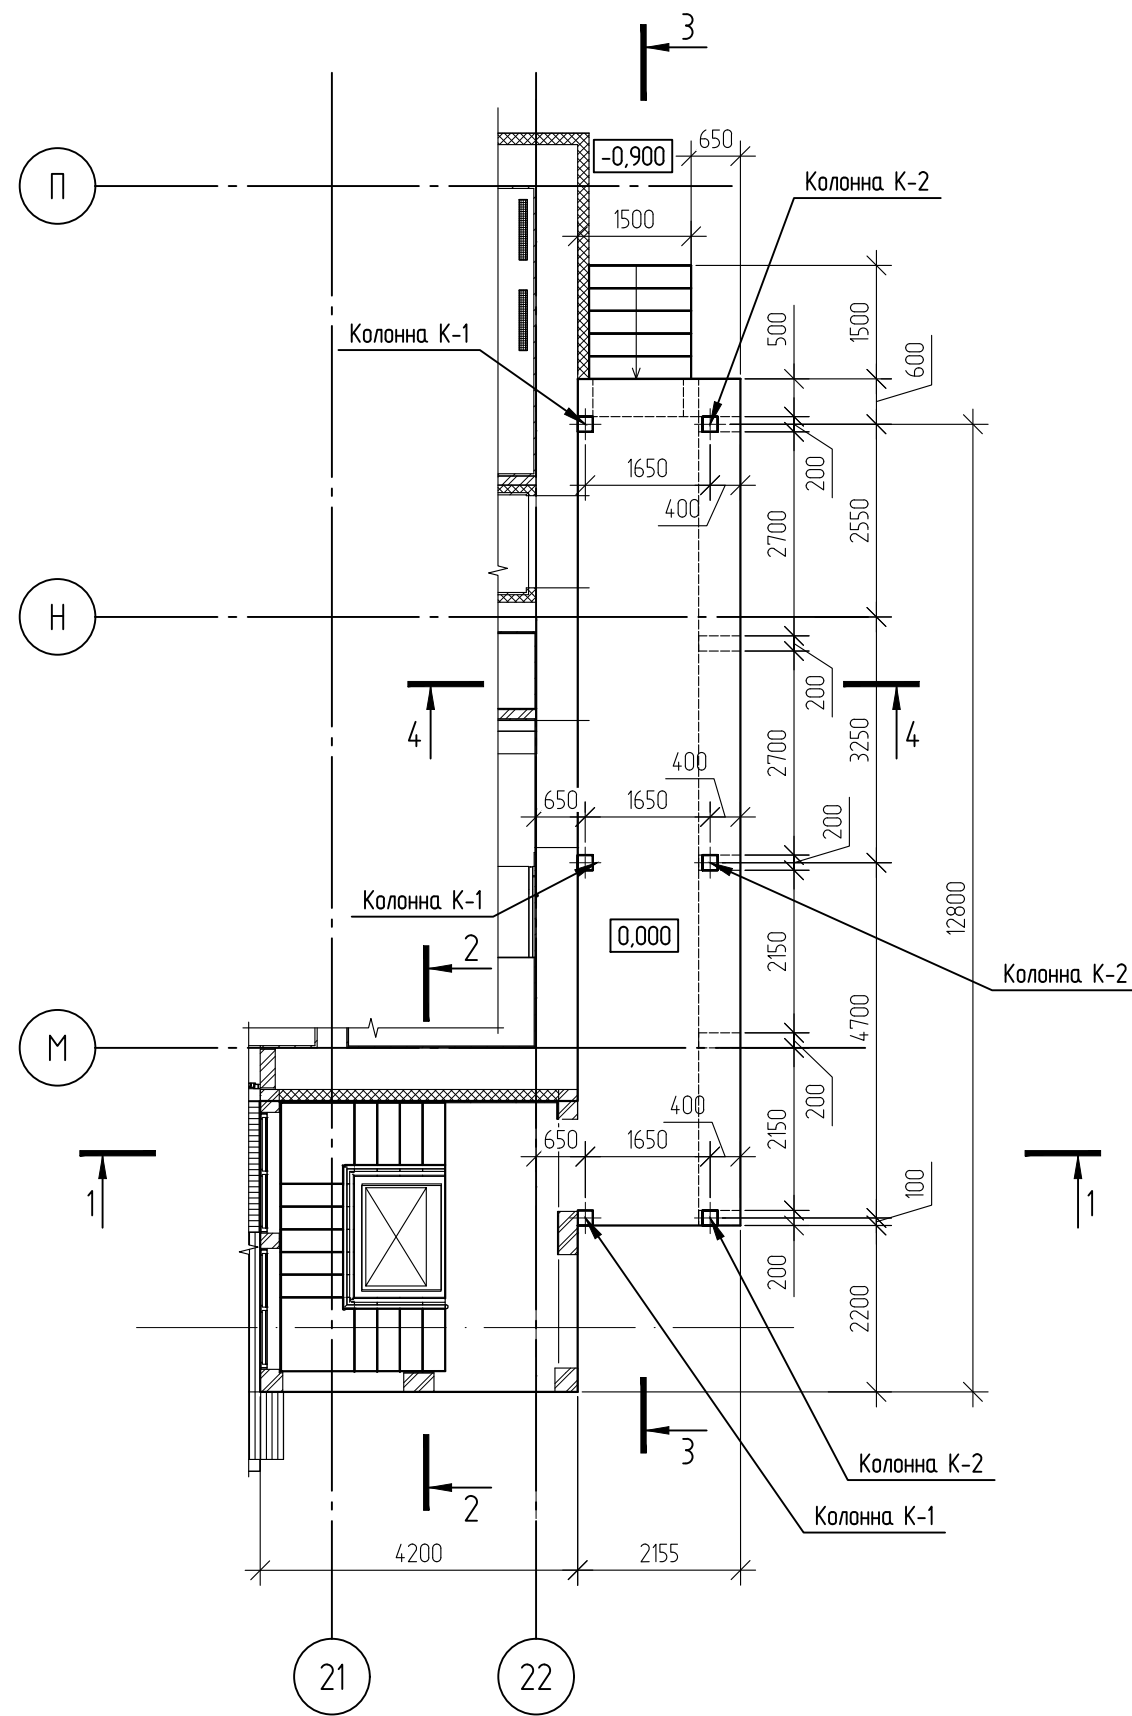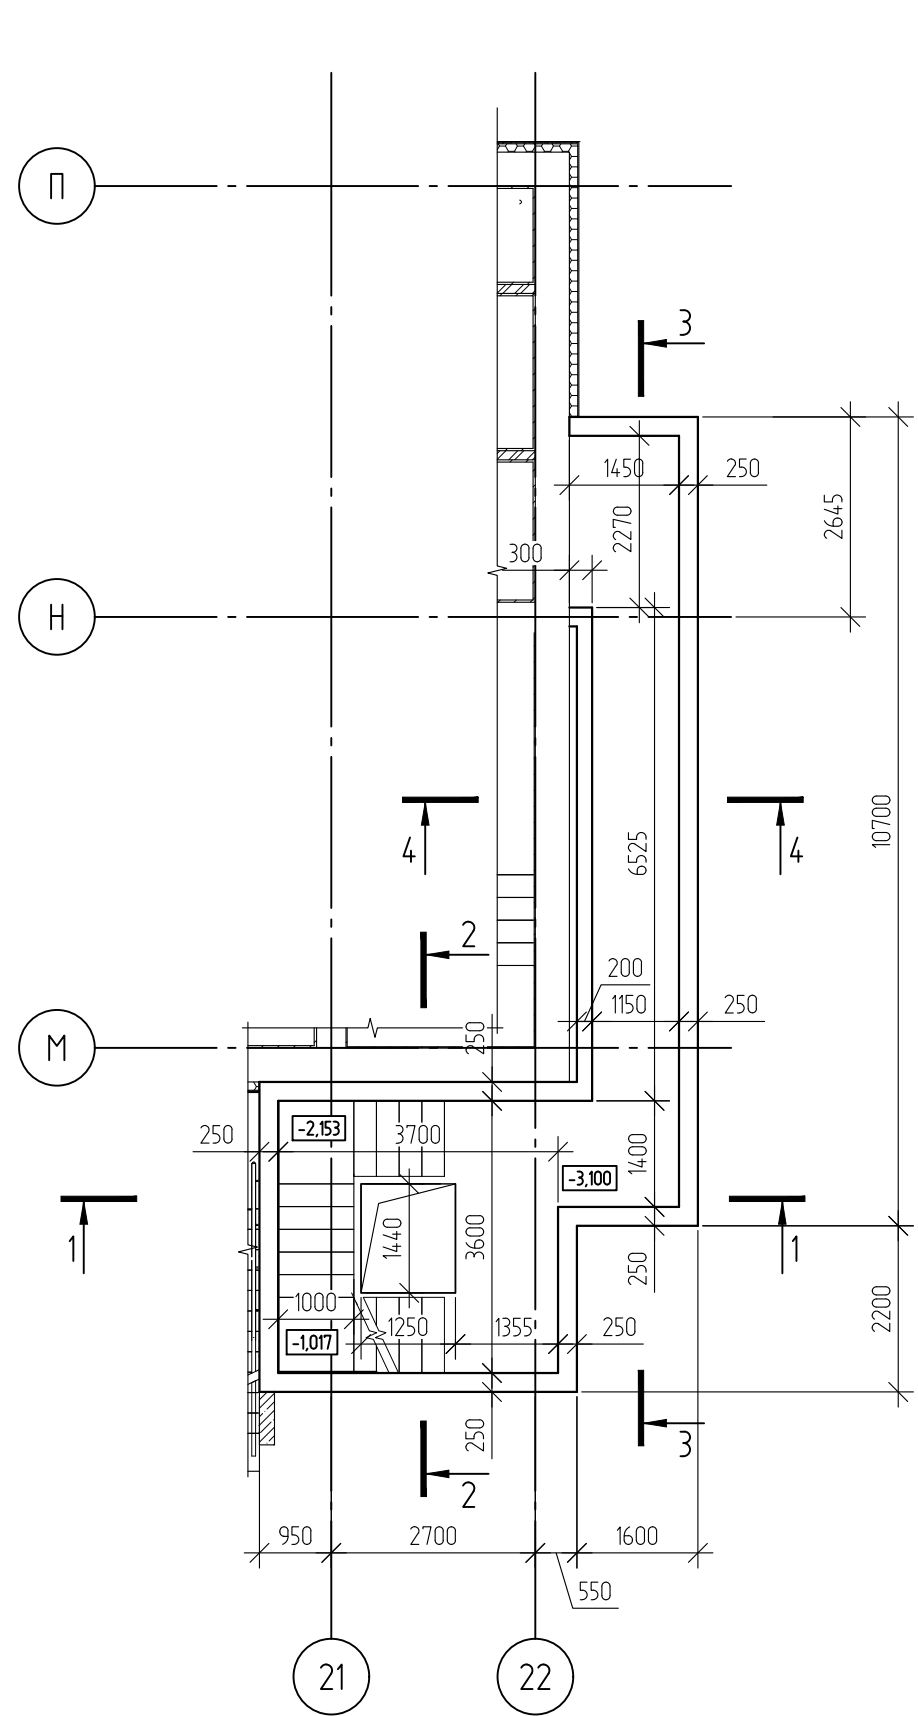


Разрез 1—1

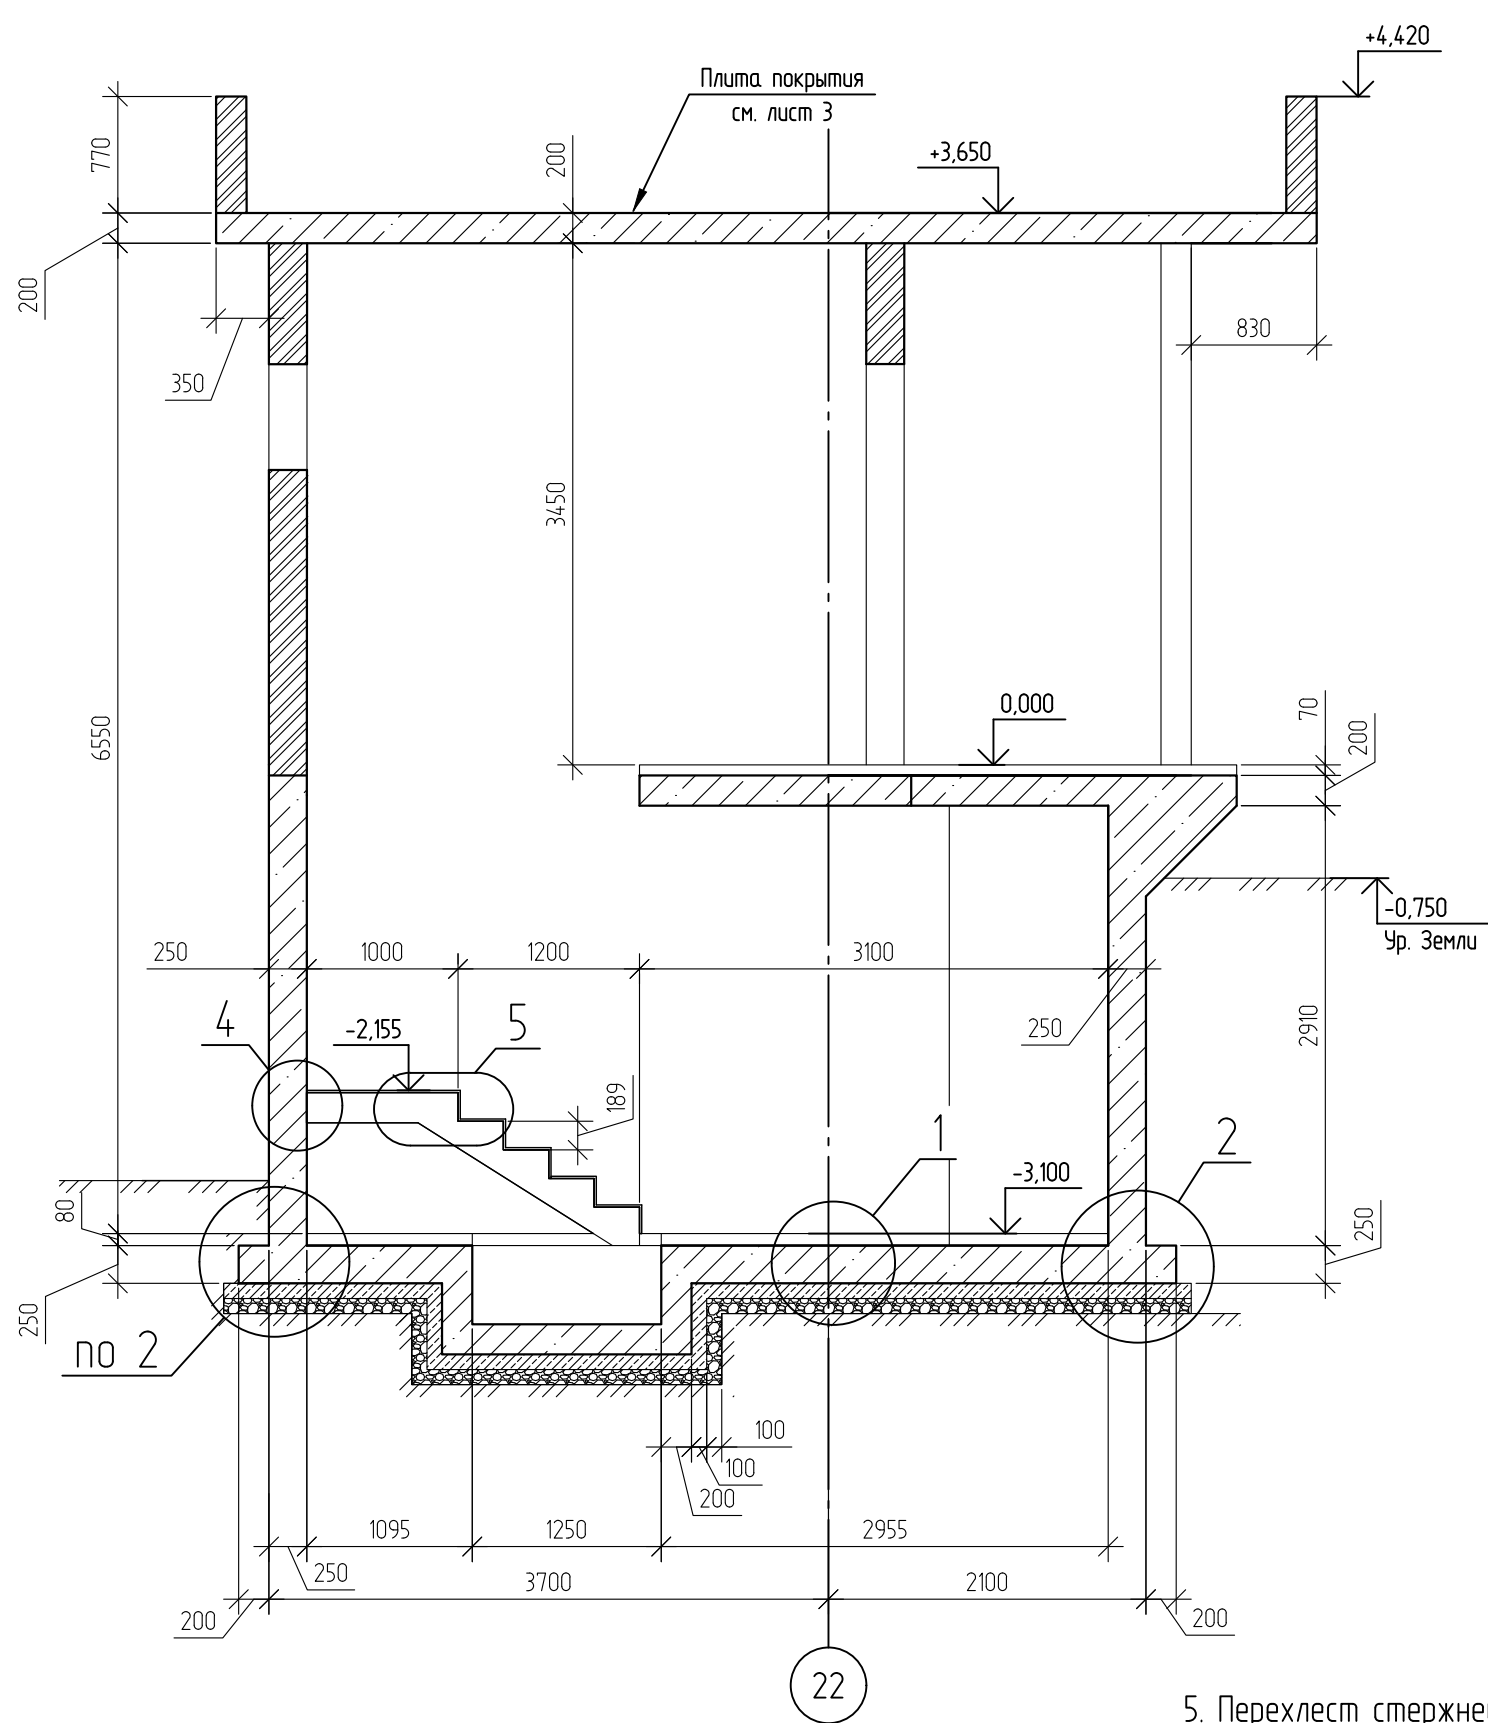

Разрез 2—2

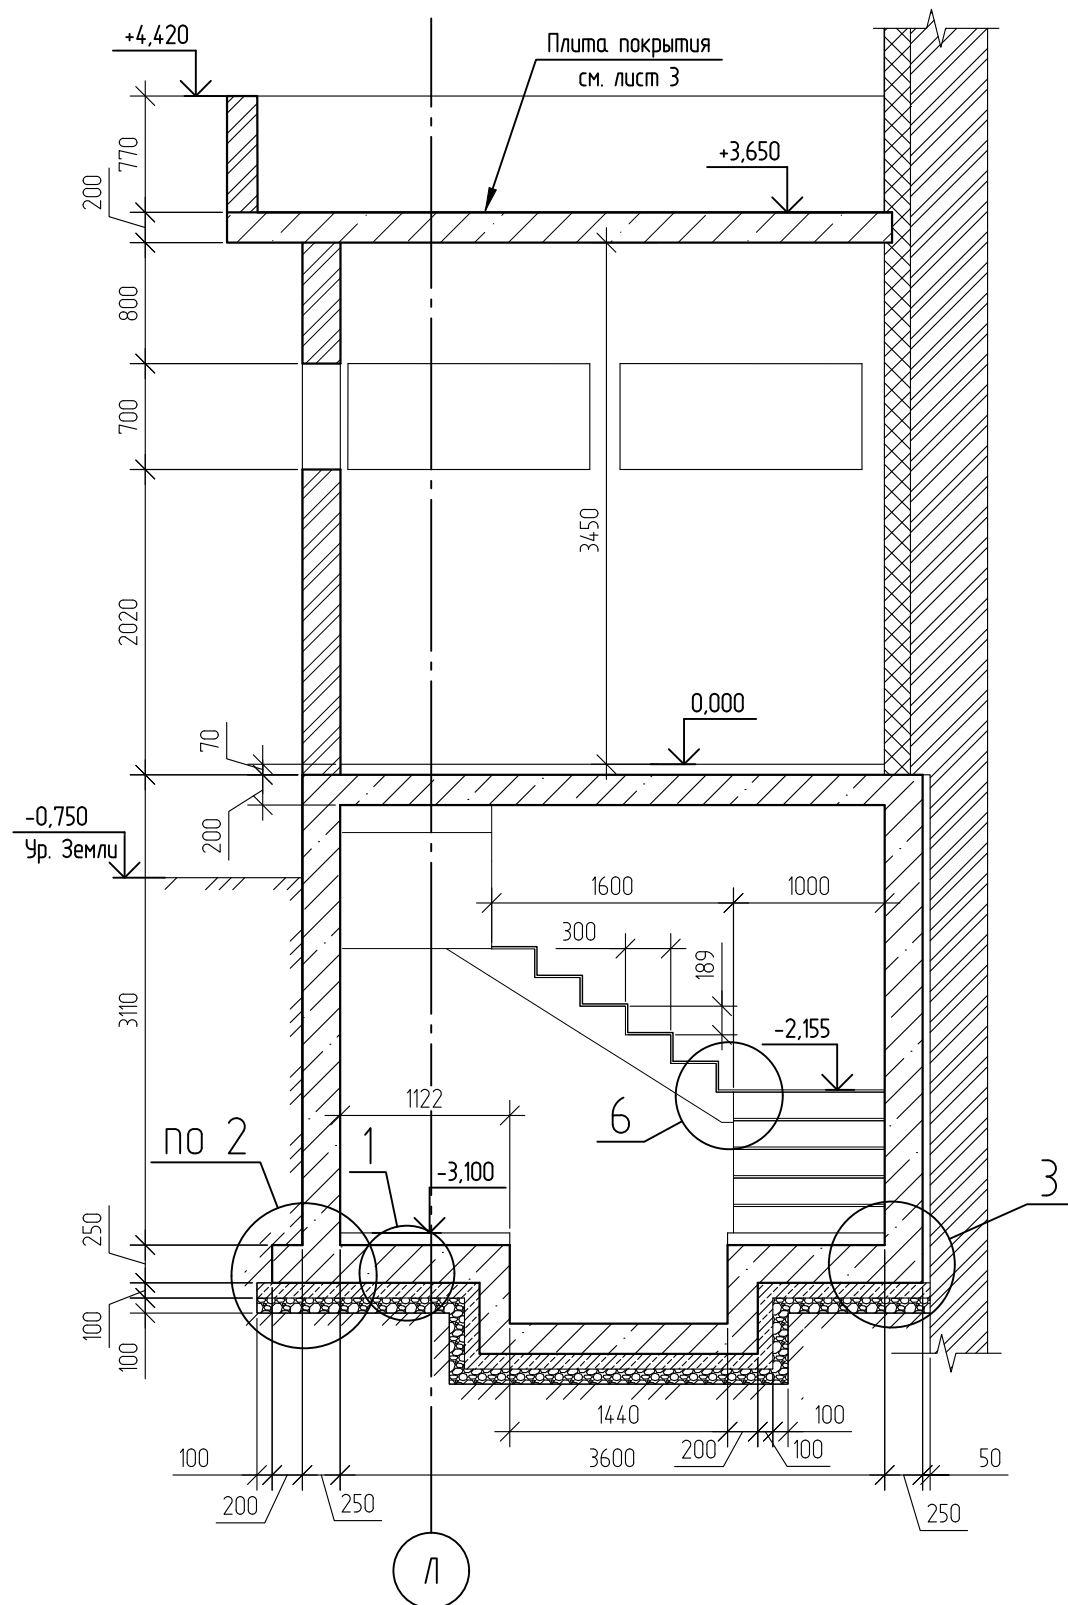

Разрез 3—3










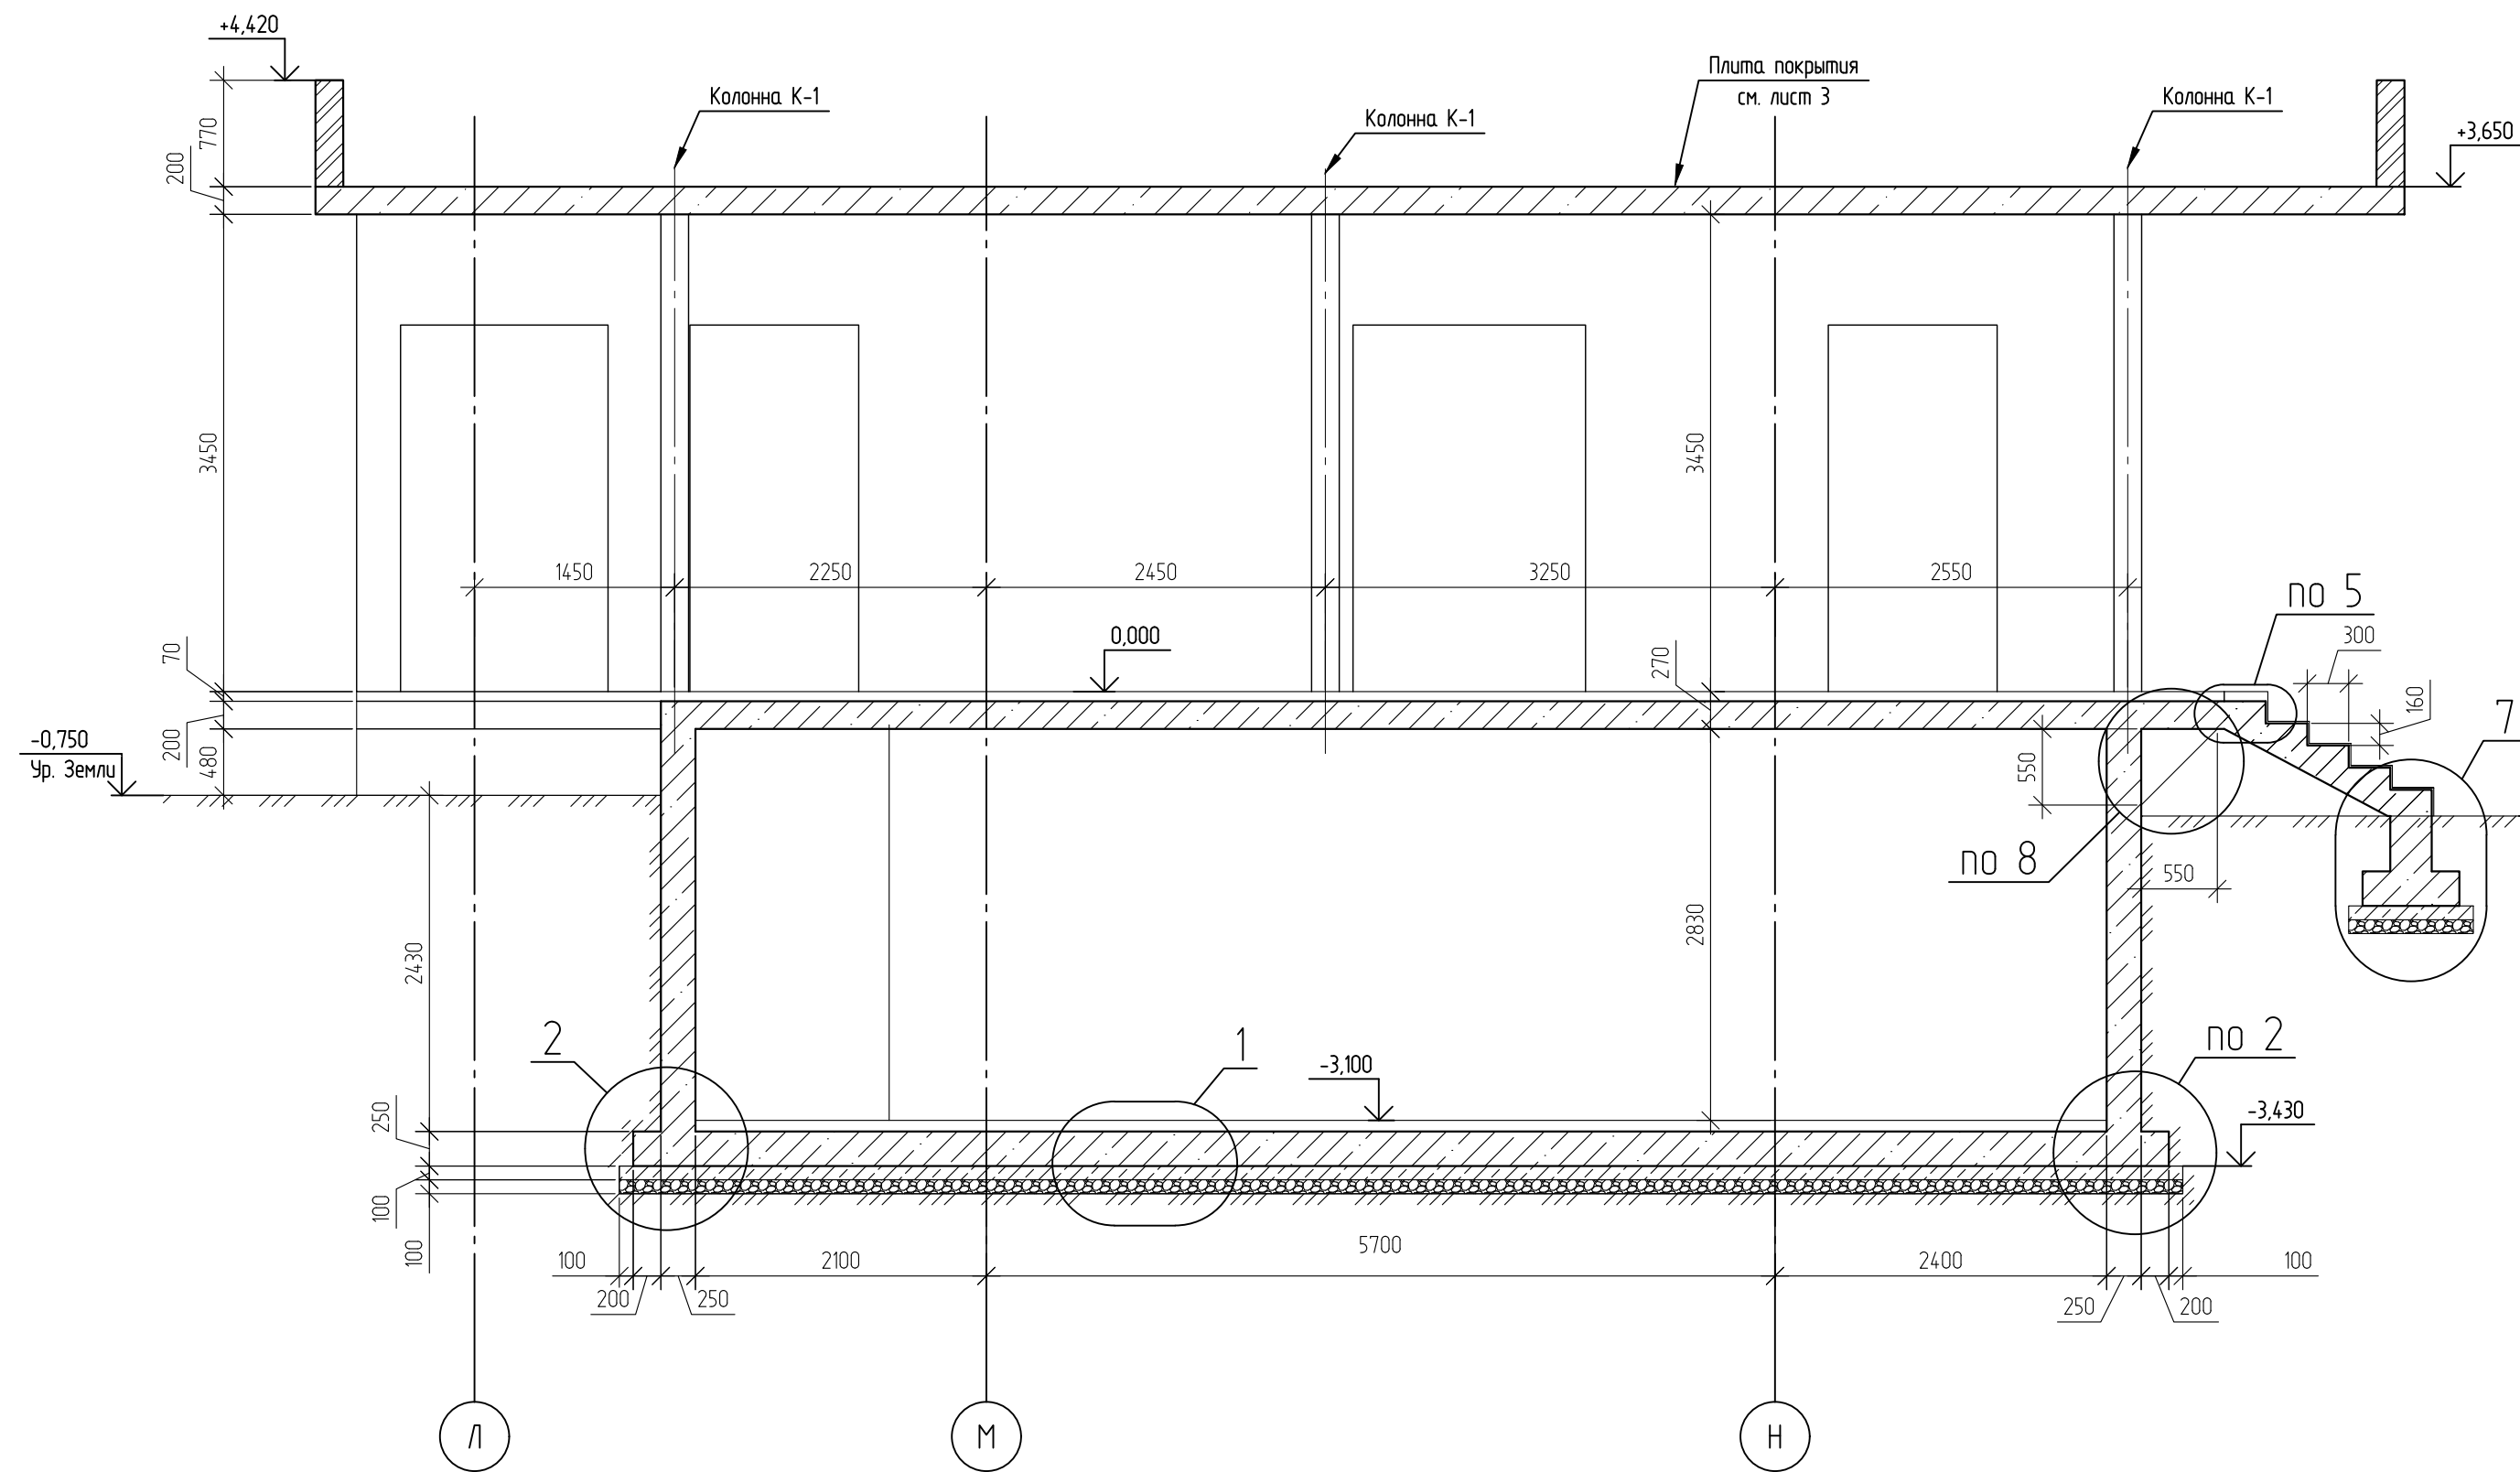


5. Перехлест стержней основного армирования должен быть не менее 40d: для стержней $\Phi 12A-400$ – 480 мм, для стержней $\Phi 10A-400$ – 400 мм. Выполнение перехлестов стержней производить бразежку. В спецификации запас на перехлест учтен в размере 6%.
6. Изготовление гнутых стержней производить в холодном состоянии на оправках диаметром 5d для стержней диаметром менее 20 мм. Величина отгиба стержней основной арматуры в уголках и Т-образных примыканиях – не менее 50d, величина отгиба для анкеровки – не менее 5d.
7. Все поверхности подпорной стены, контактирующие с землей, покрыть 2 слоями горячего битума.
8. *Размеры для справок.

1. Класс бетона по прочности на сжатие для всех монолитных конструкций – В25. Марка бетона по водонепроницаемости – не ниже W6. Марка бетона по морозостойкости – не ниже F100.
2. Арматура – А-240, А-500 по ГОСТ 34028-2016.
3. Под конструкции фундамента выполнить бетонную подготовку из бетона В7,5 толщиной 100 мм по основанию из смеси ПГС толщиной 100 мм, выступающая за габариты фундамента на 100 мм. По бетонной подготовке предусмотреть гидроизоляция – стеклоизол 2 слоя.
4. Арматурные стержни вязать в каждом пересечении, сварные соединения не допускаются. Вязальная проволока в ведомости расходов не учтена.

						708/П-24-АНД-КР		
						Капитальный ремонт общеобразовательного учреждения ГБОУ "Школа №1210" по адресу г. Москва, ул. Живительная, д.32		
Изм.	Копуч	Лист	№ док	Подп.	Дата	Конструктивные решения	Стадия	Лист
Разработал	Горшин	4	04.26				Р	40
ГАП	Фролова	5	04.26					
Н.Контроль	Лукашова	6	04.26			Декартадер. План на отм. -3.100, 0.000, +3.650. Разрез 1-1, 4-4	 ООО "АРТИС"	
ГИП	Зыкин	7	04.26					

Согласовано					
Изм. № подл.	Подп. и дата	Взам. инв. №			

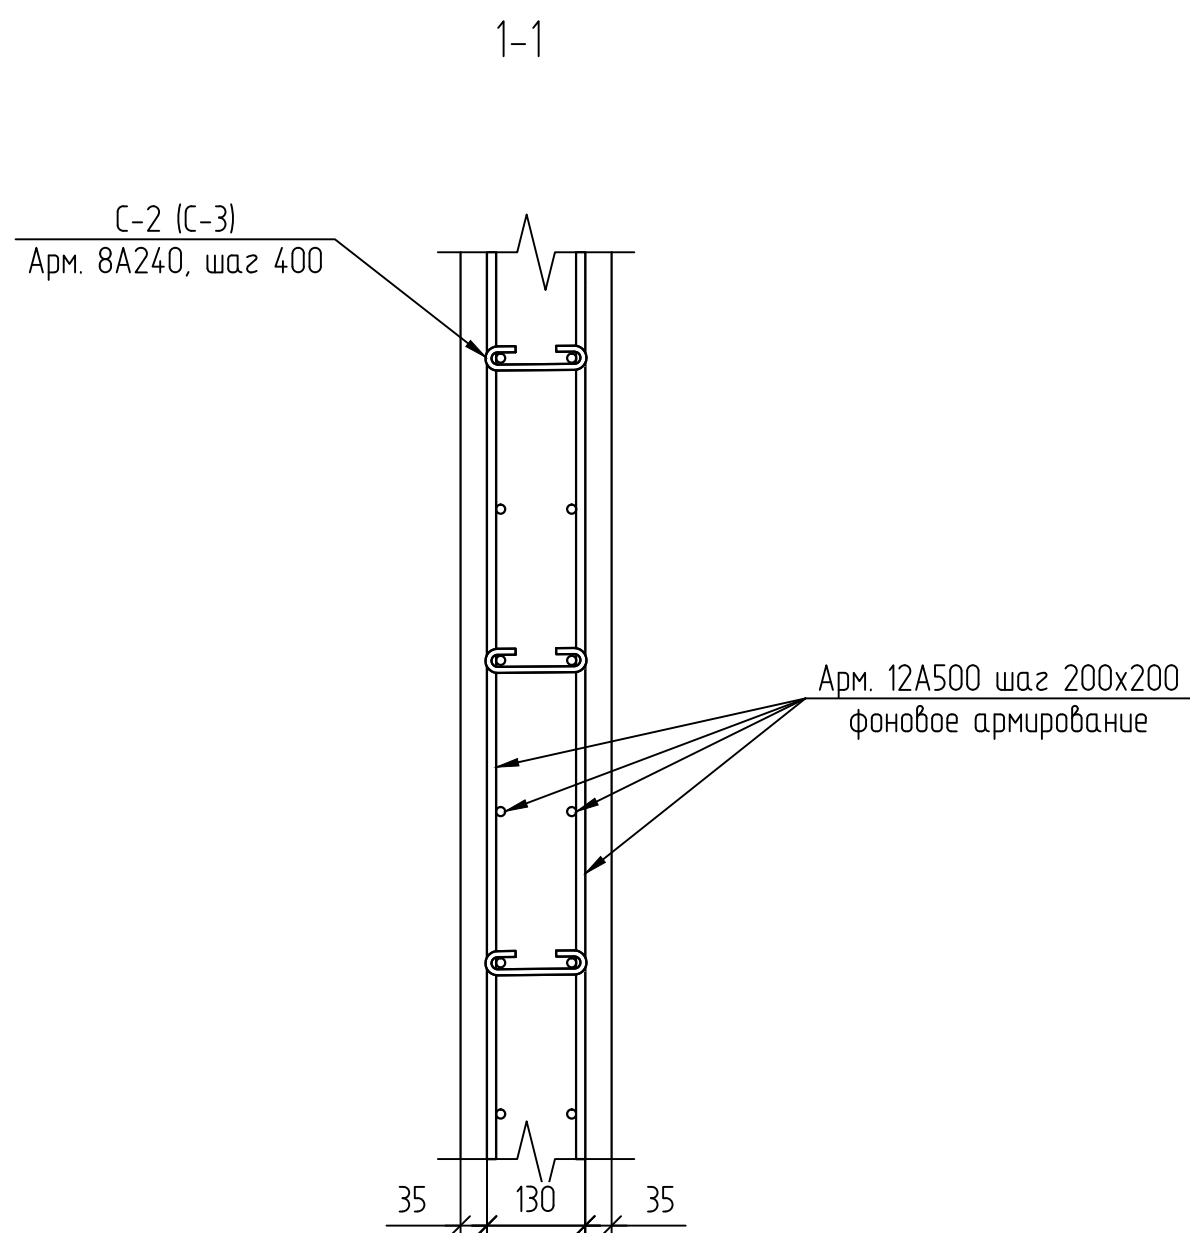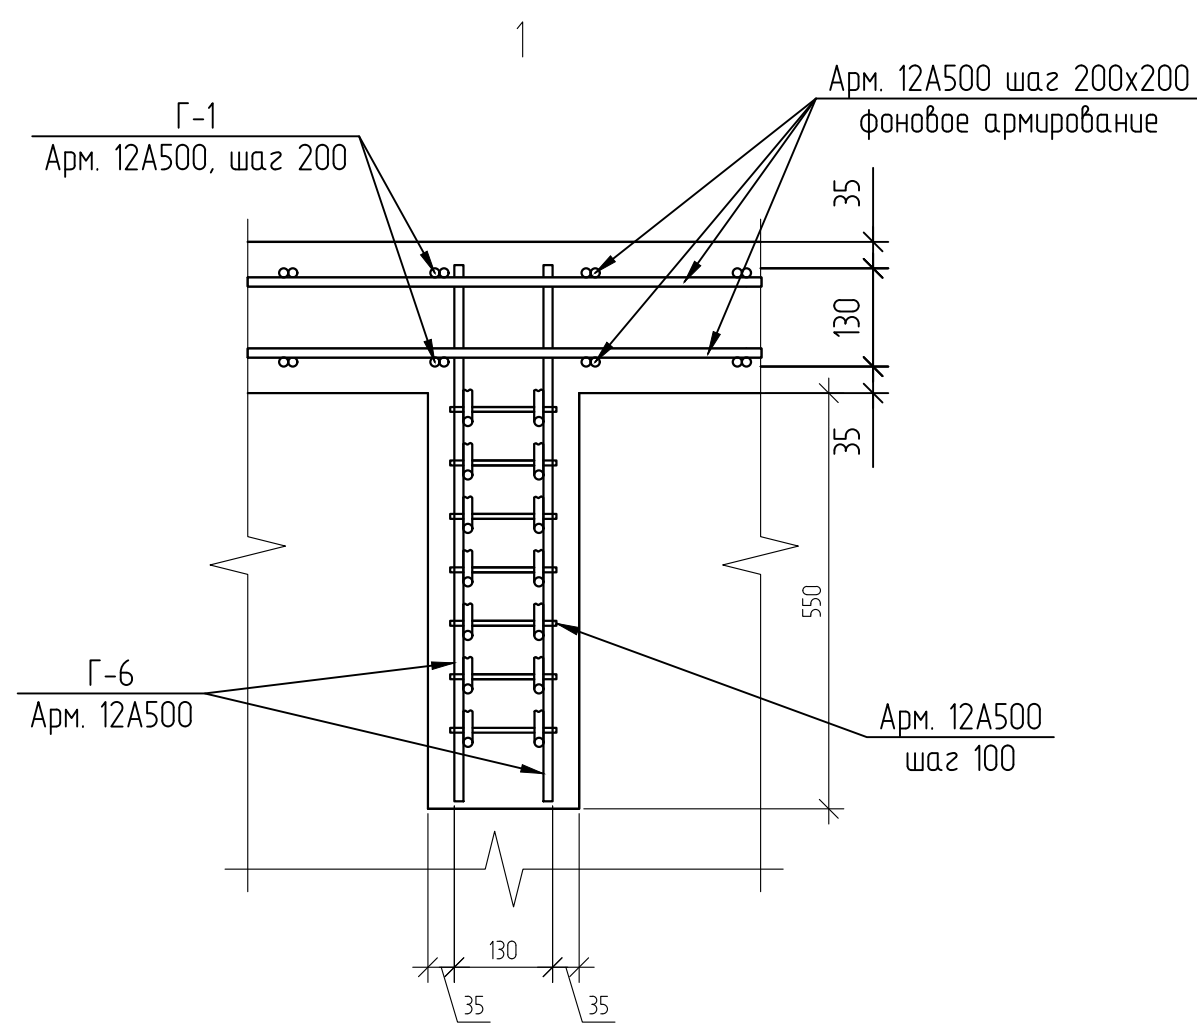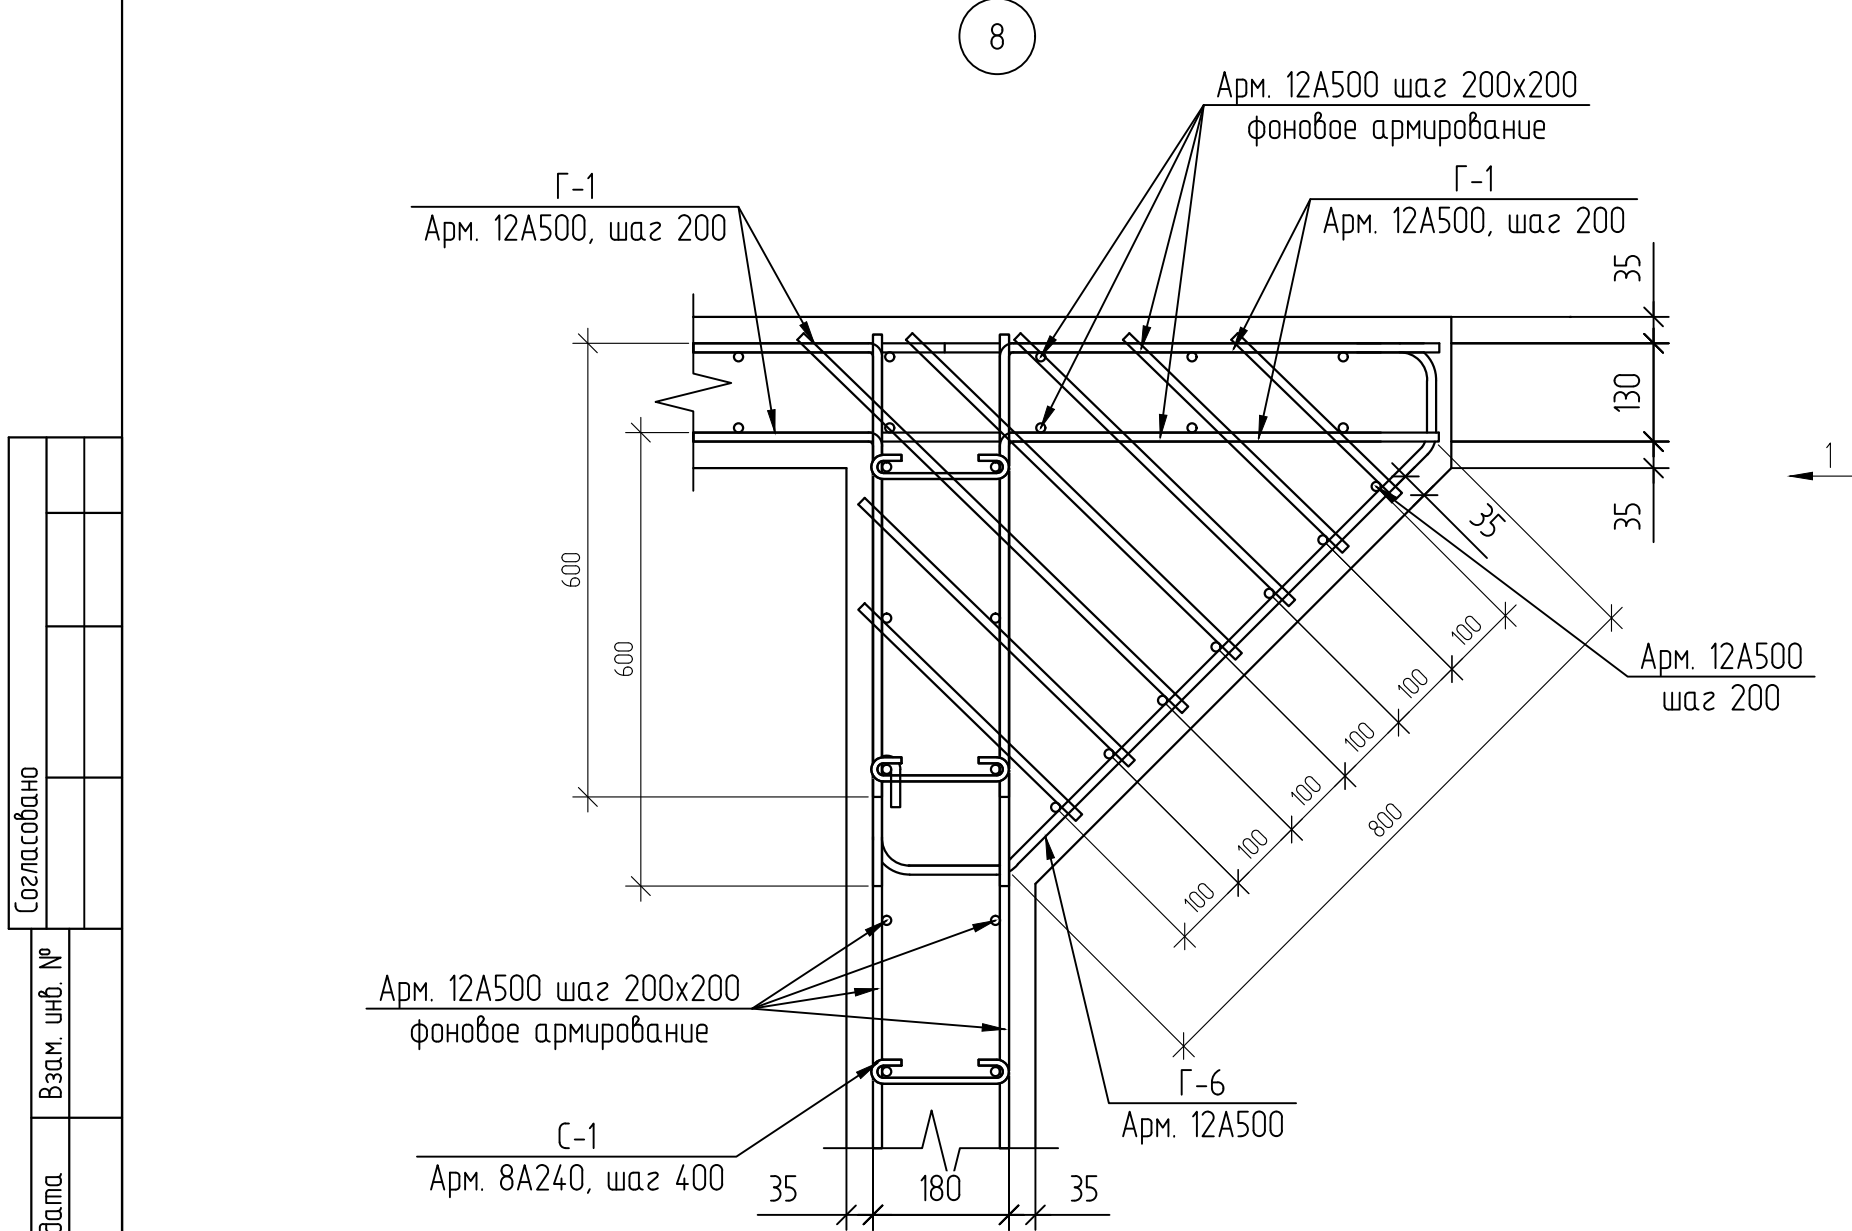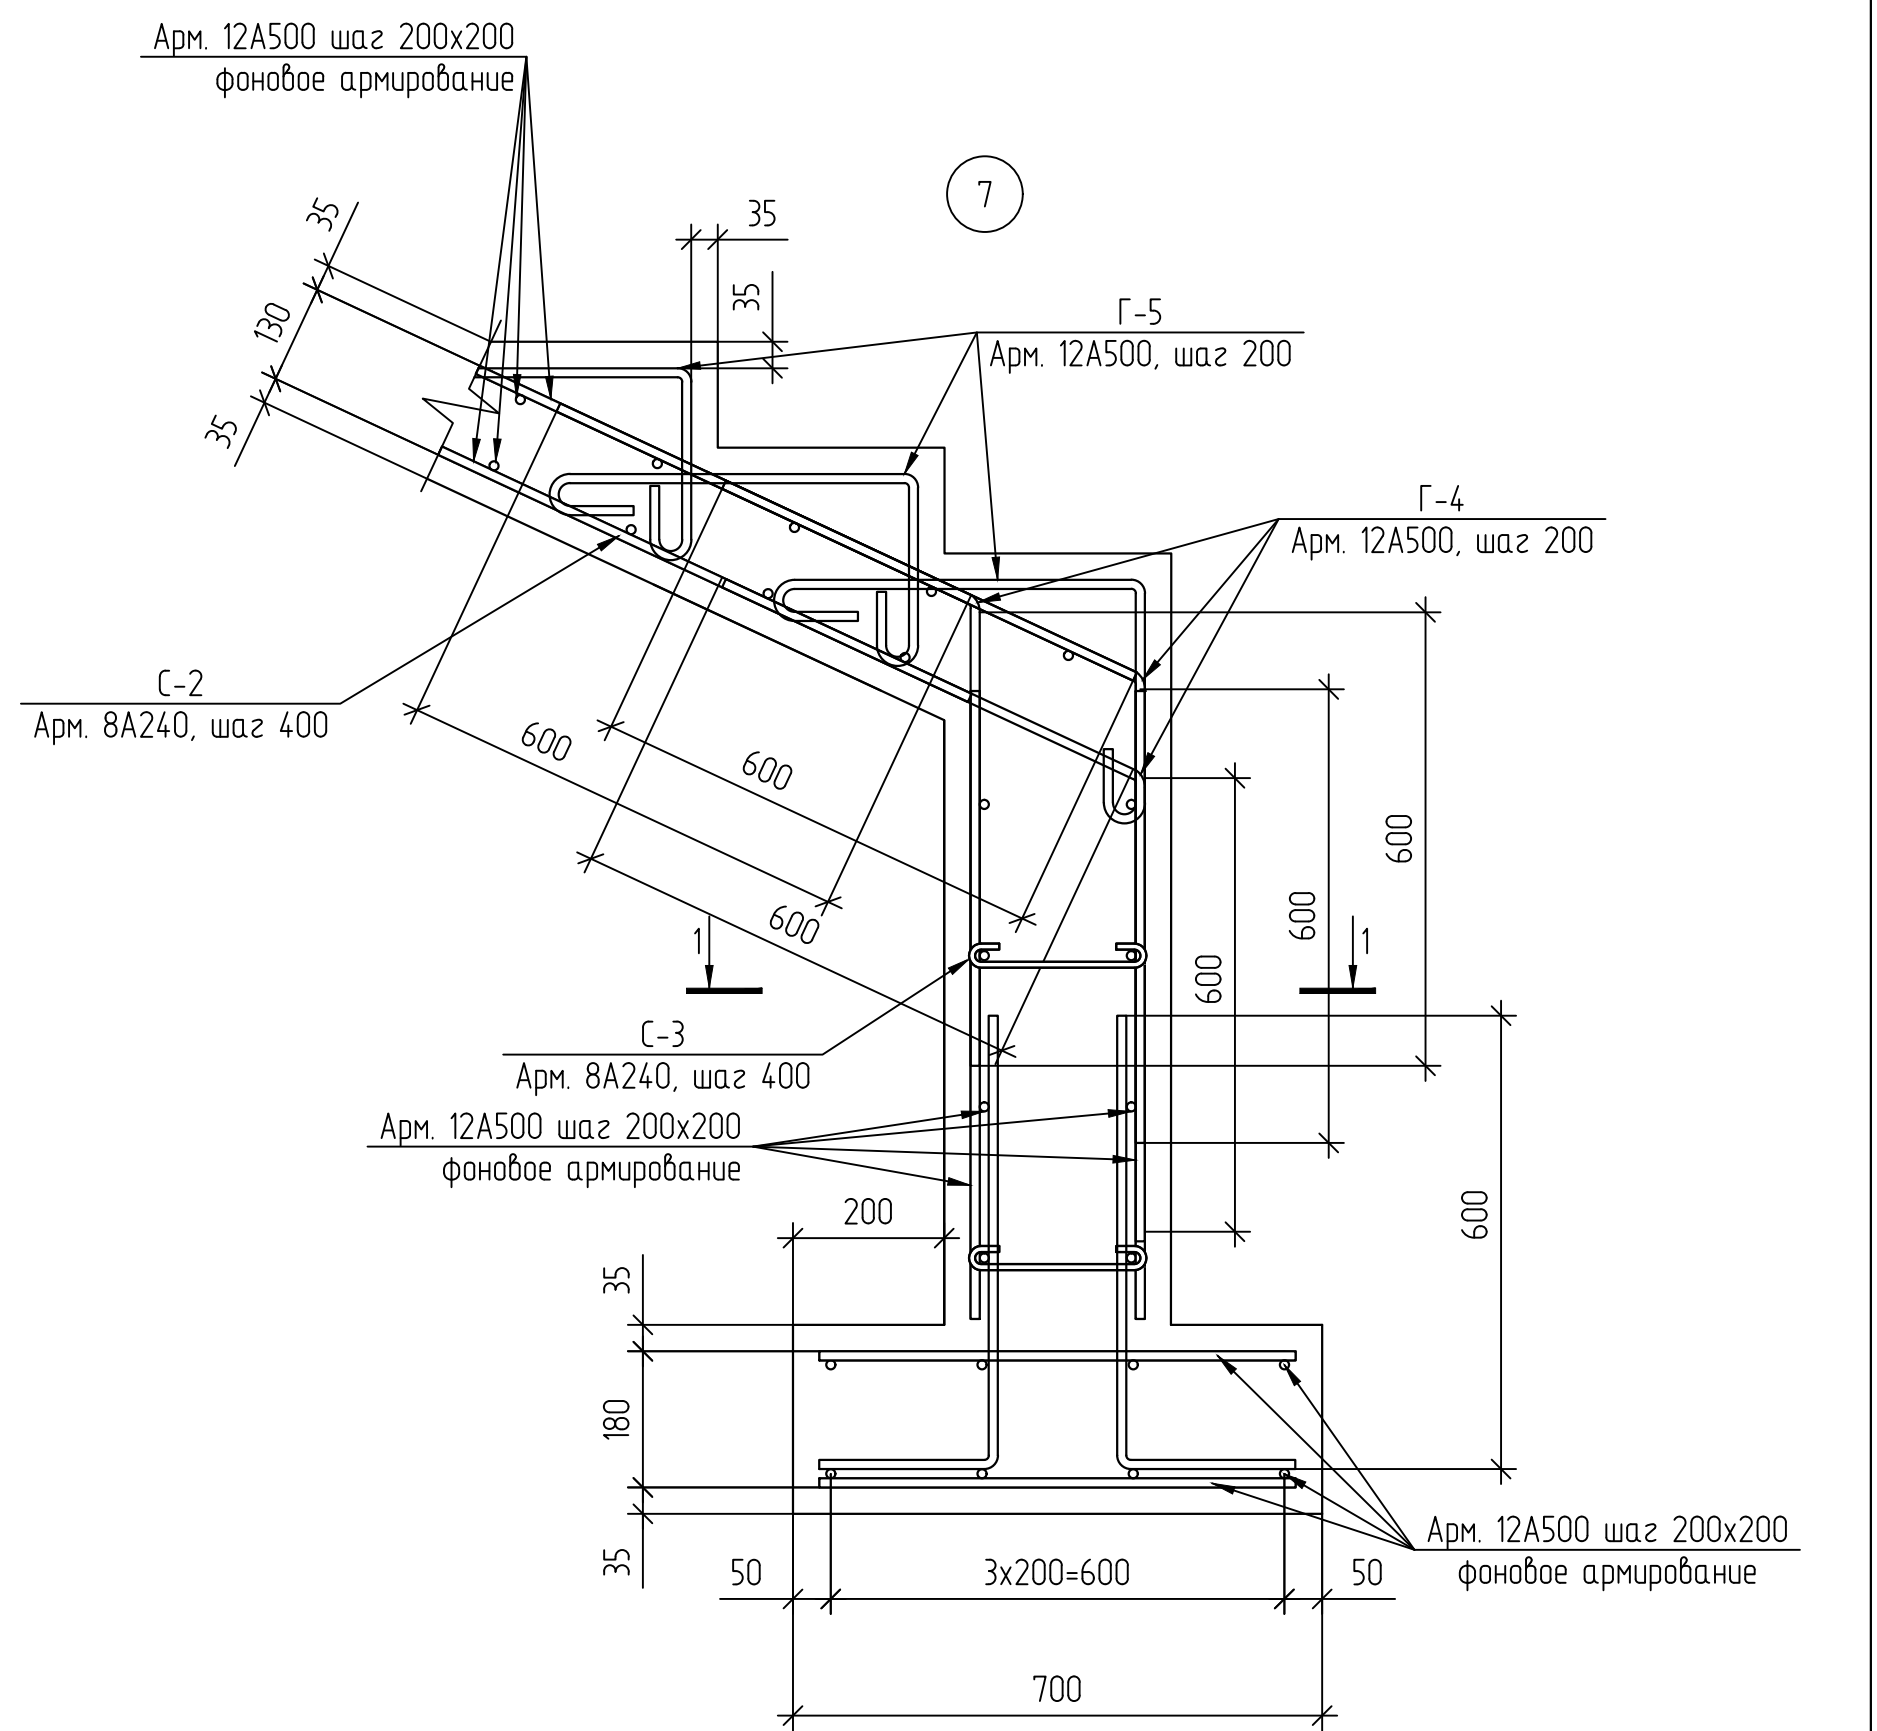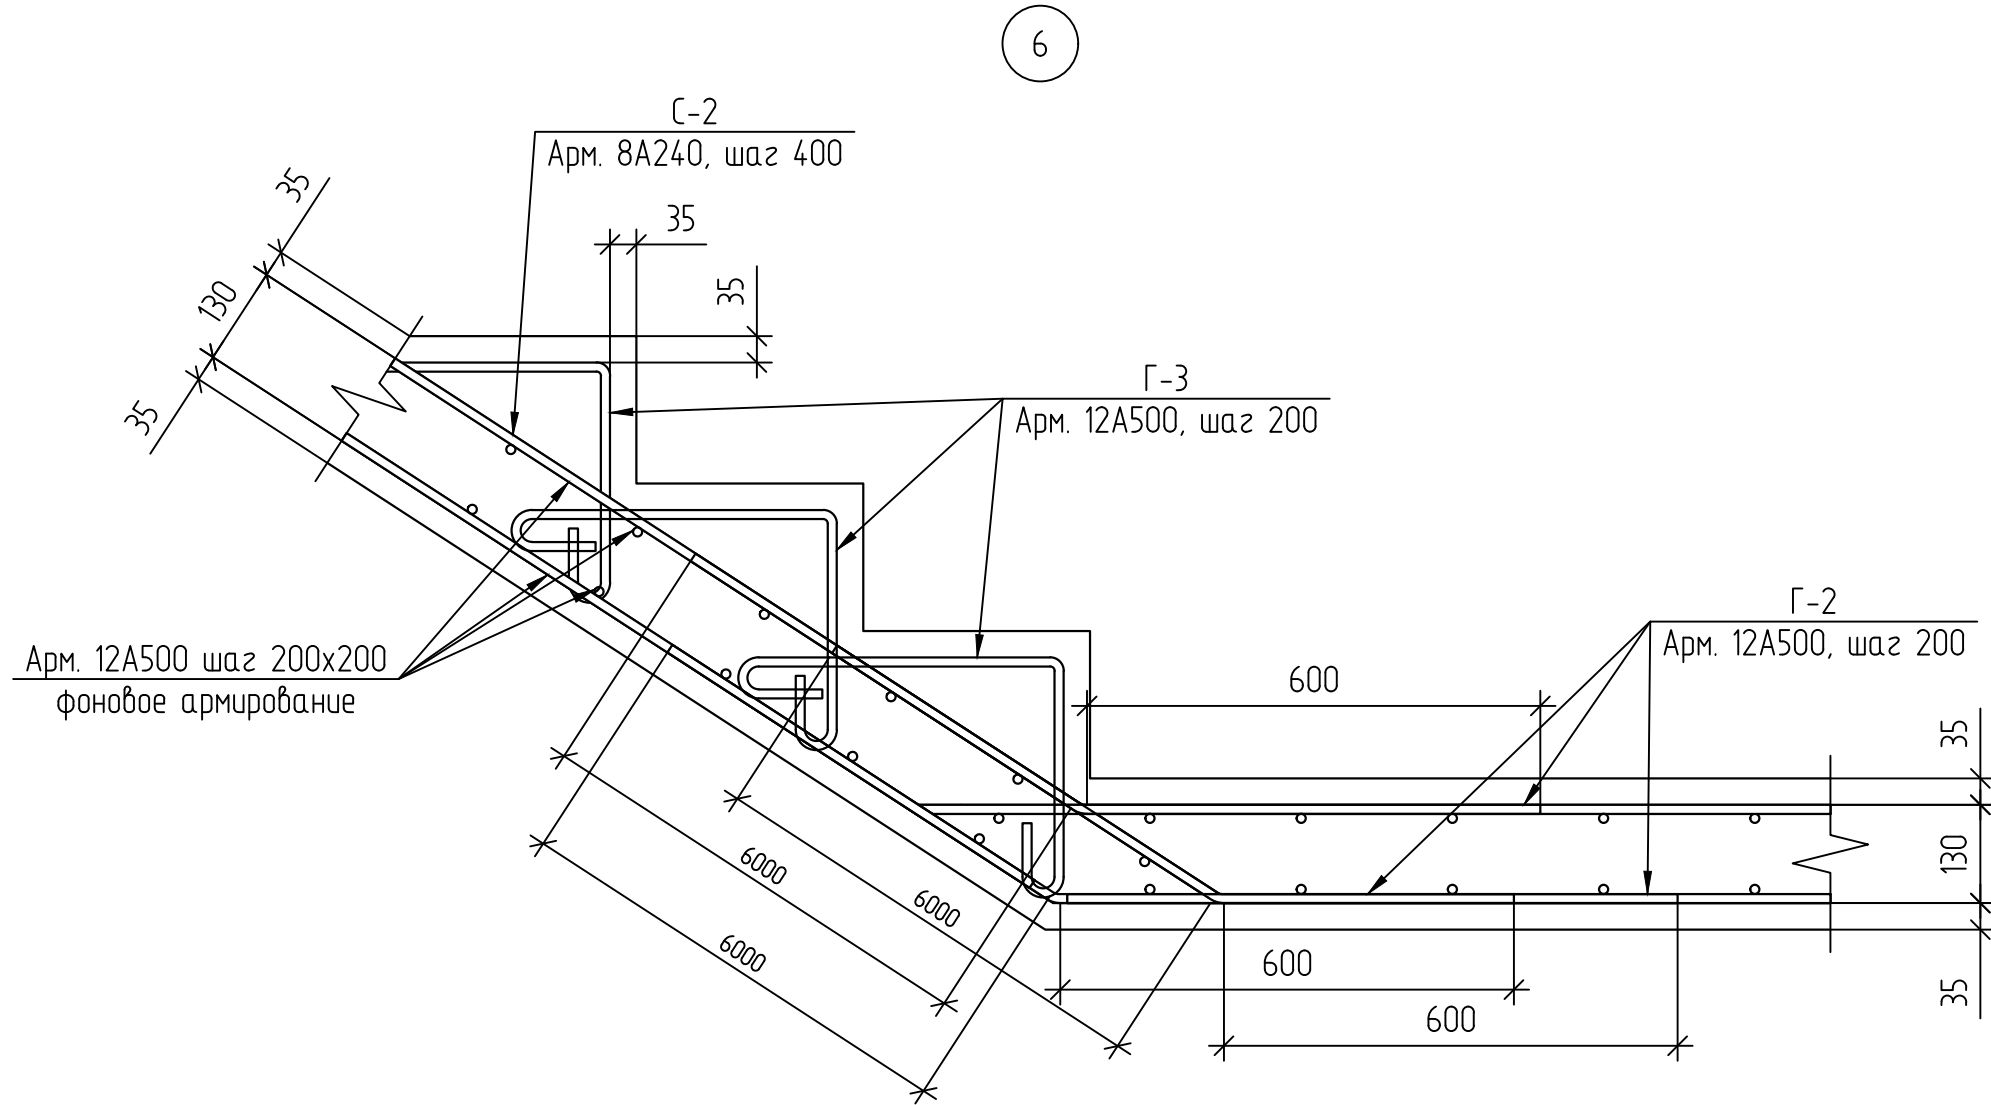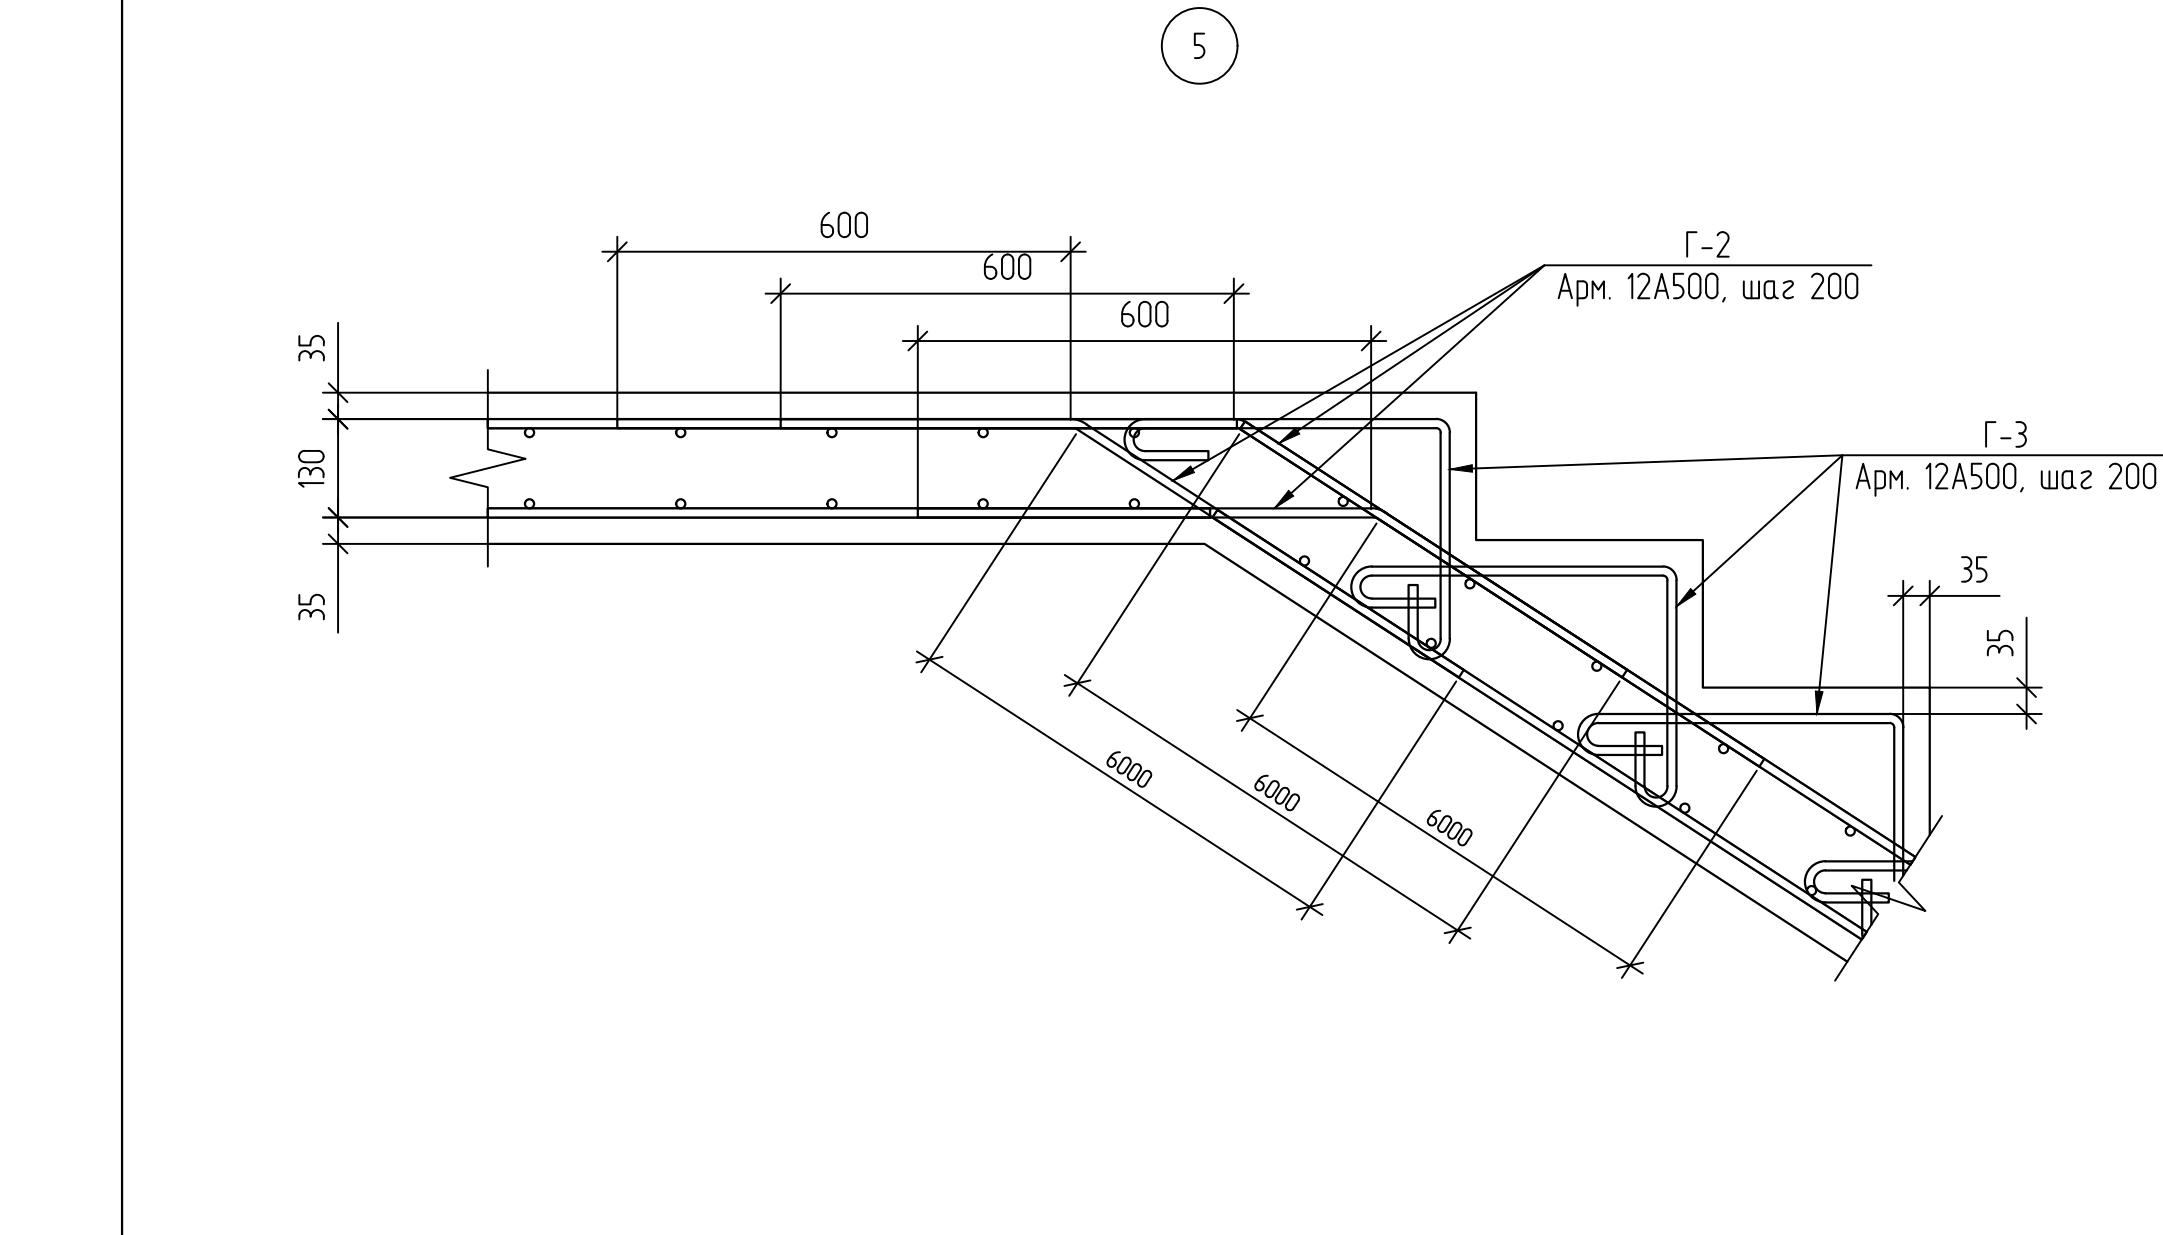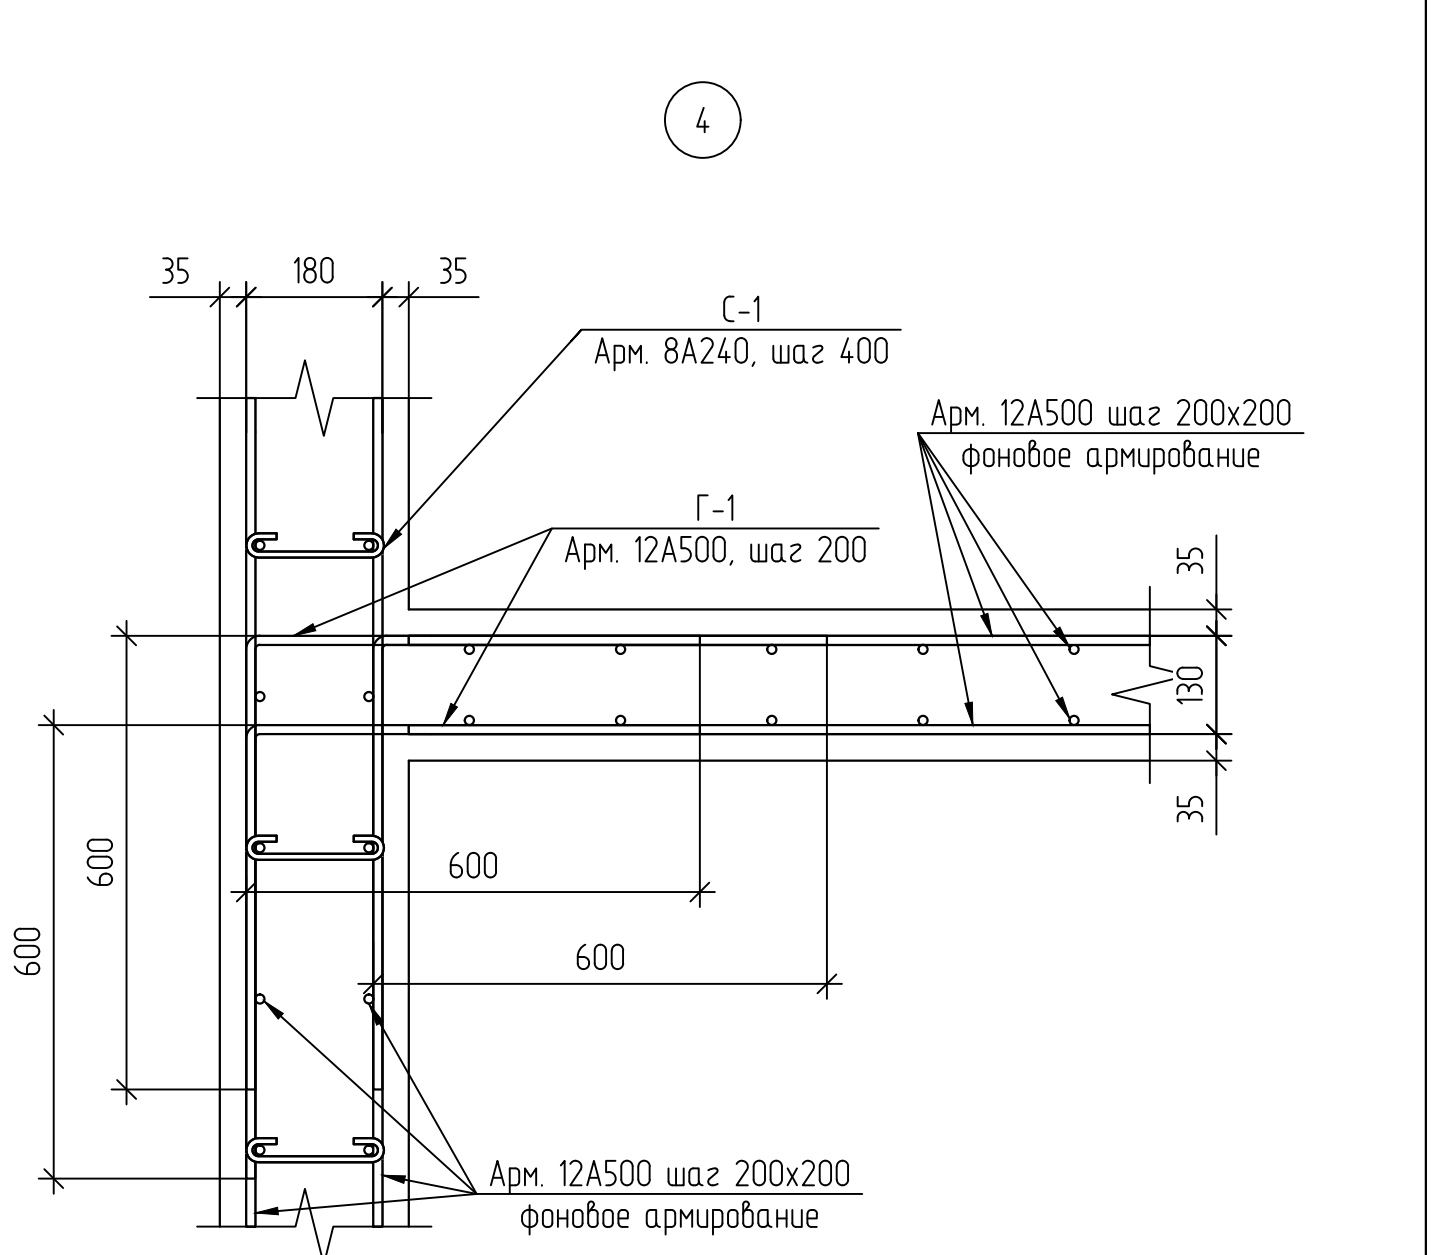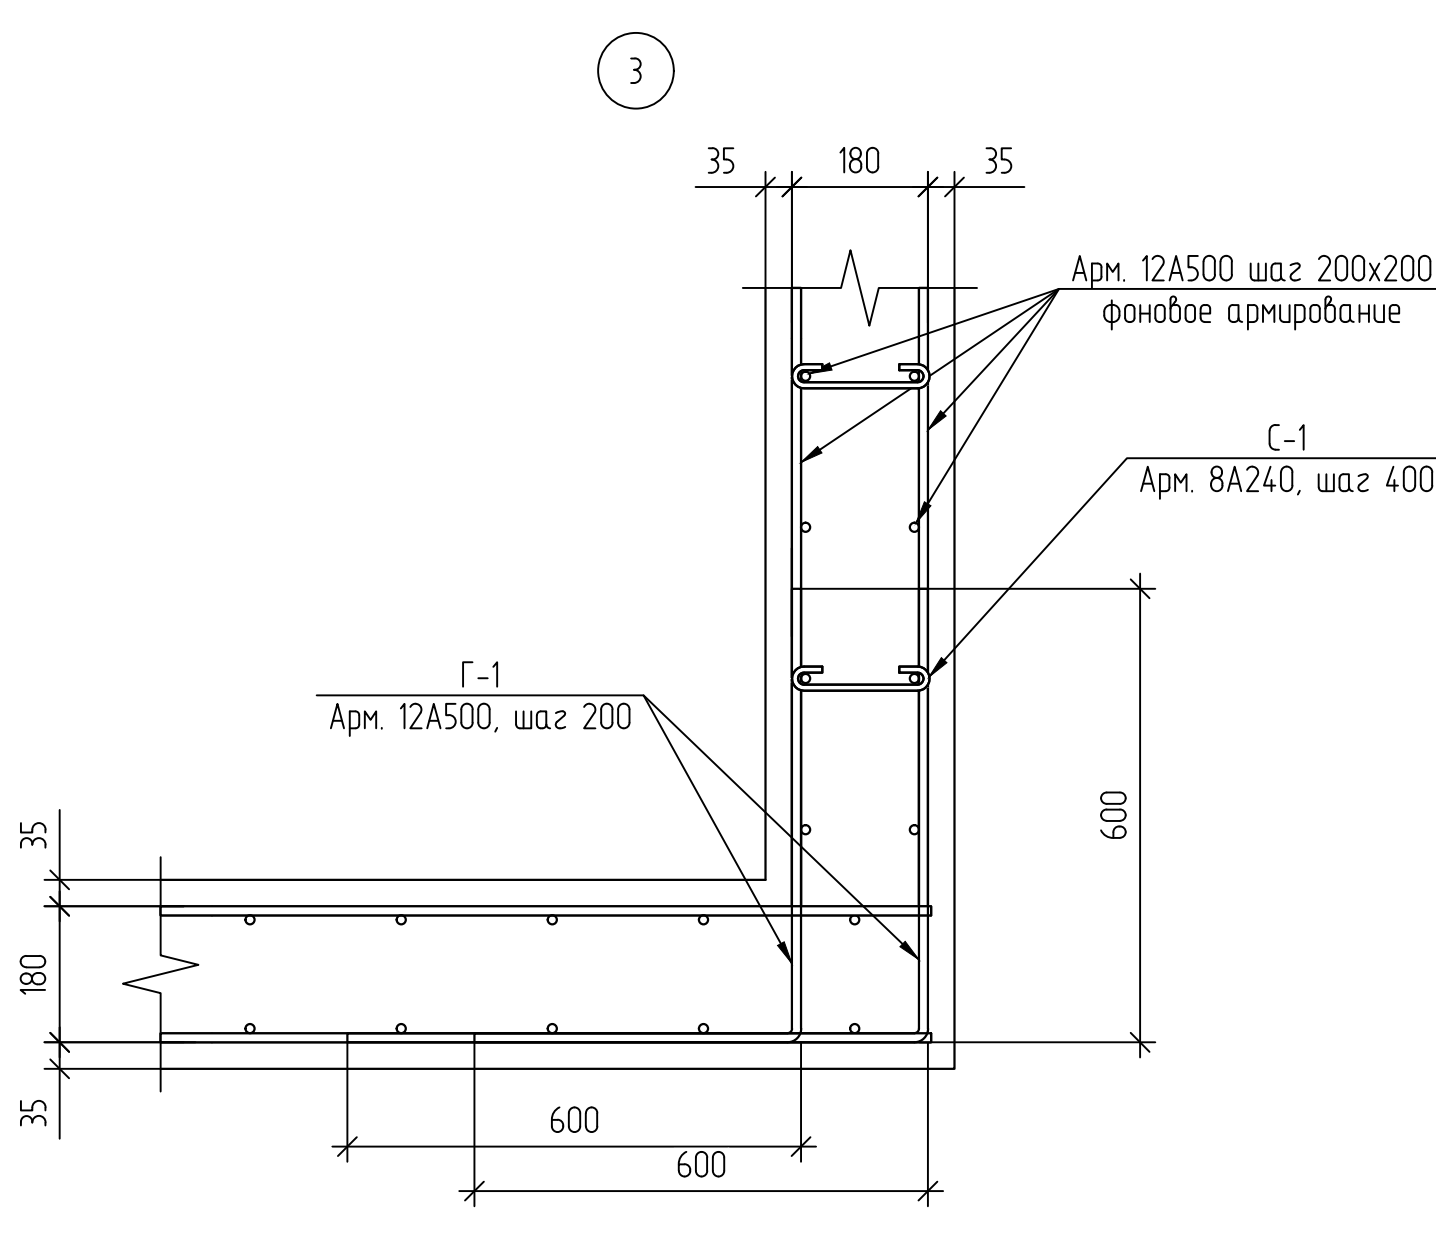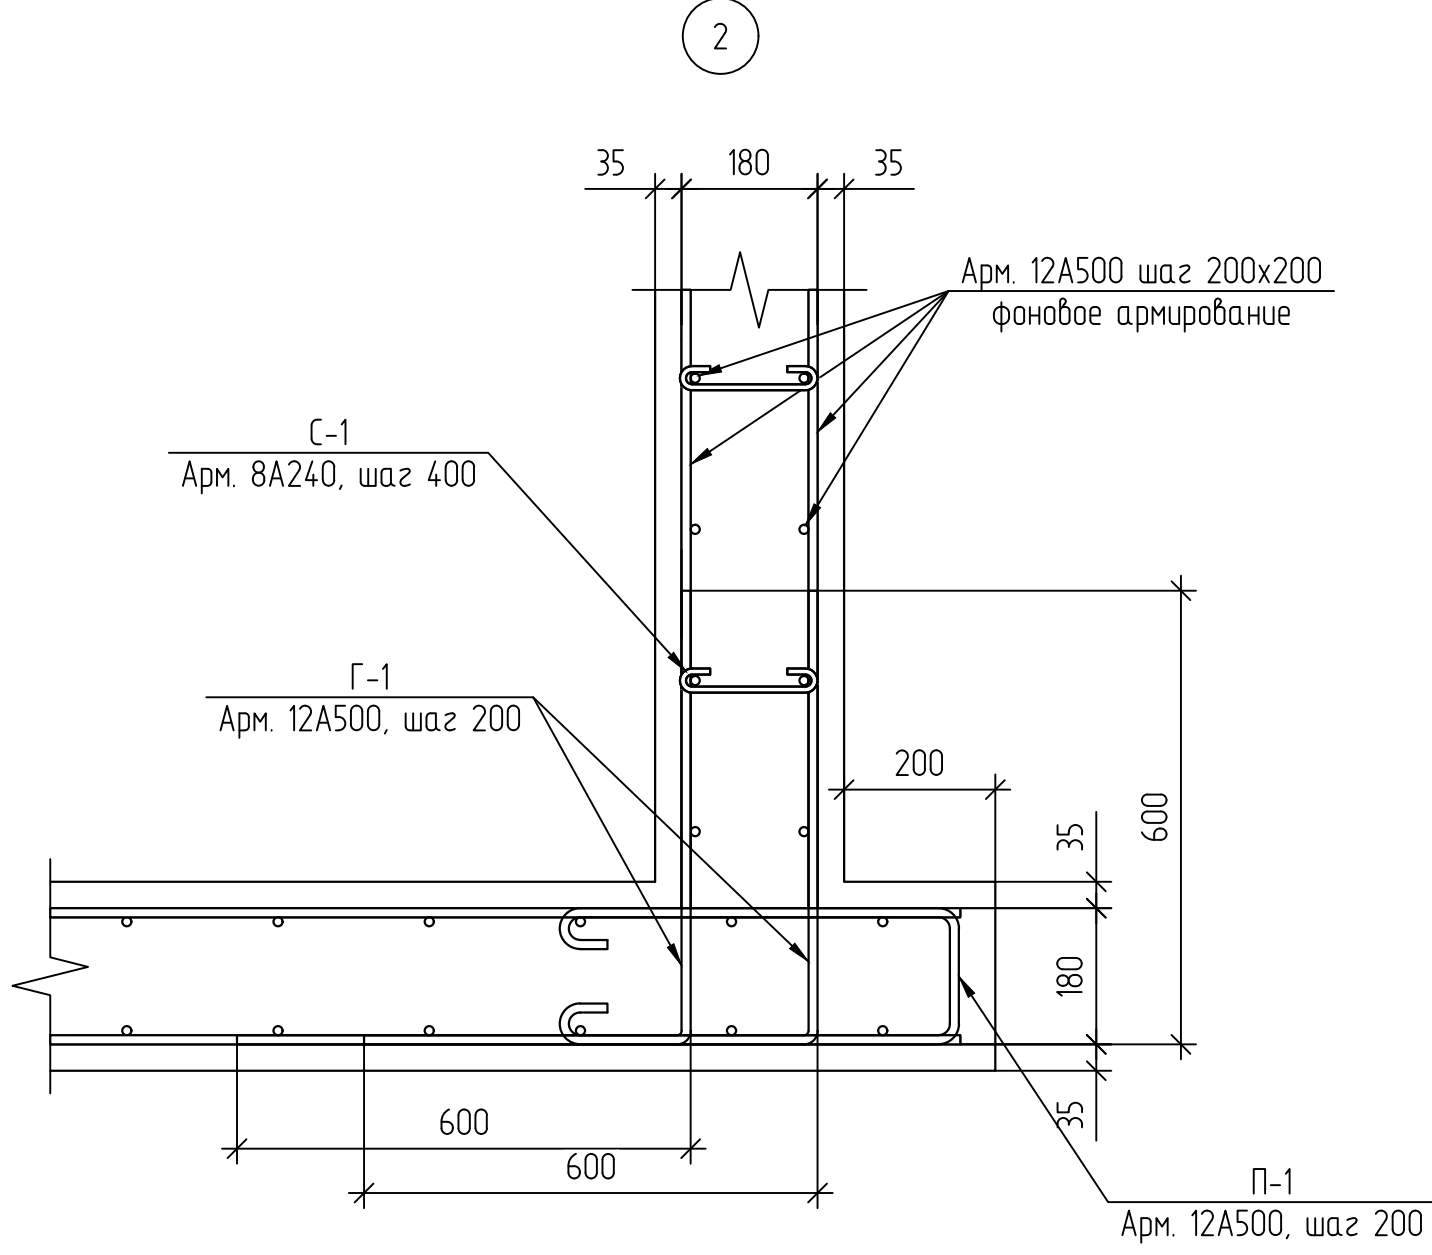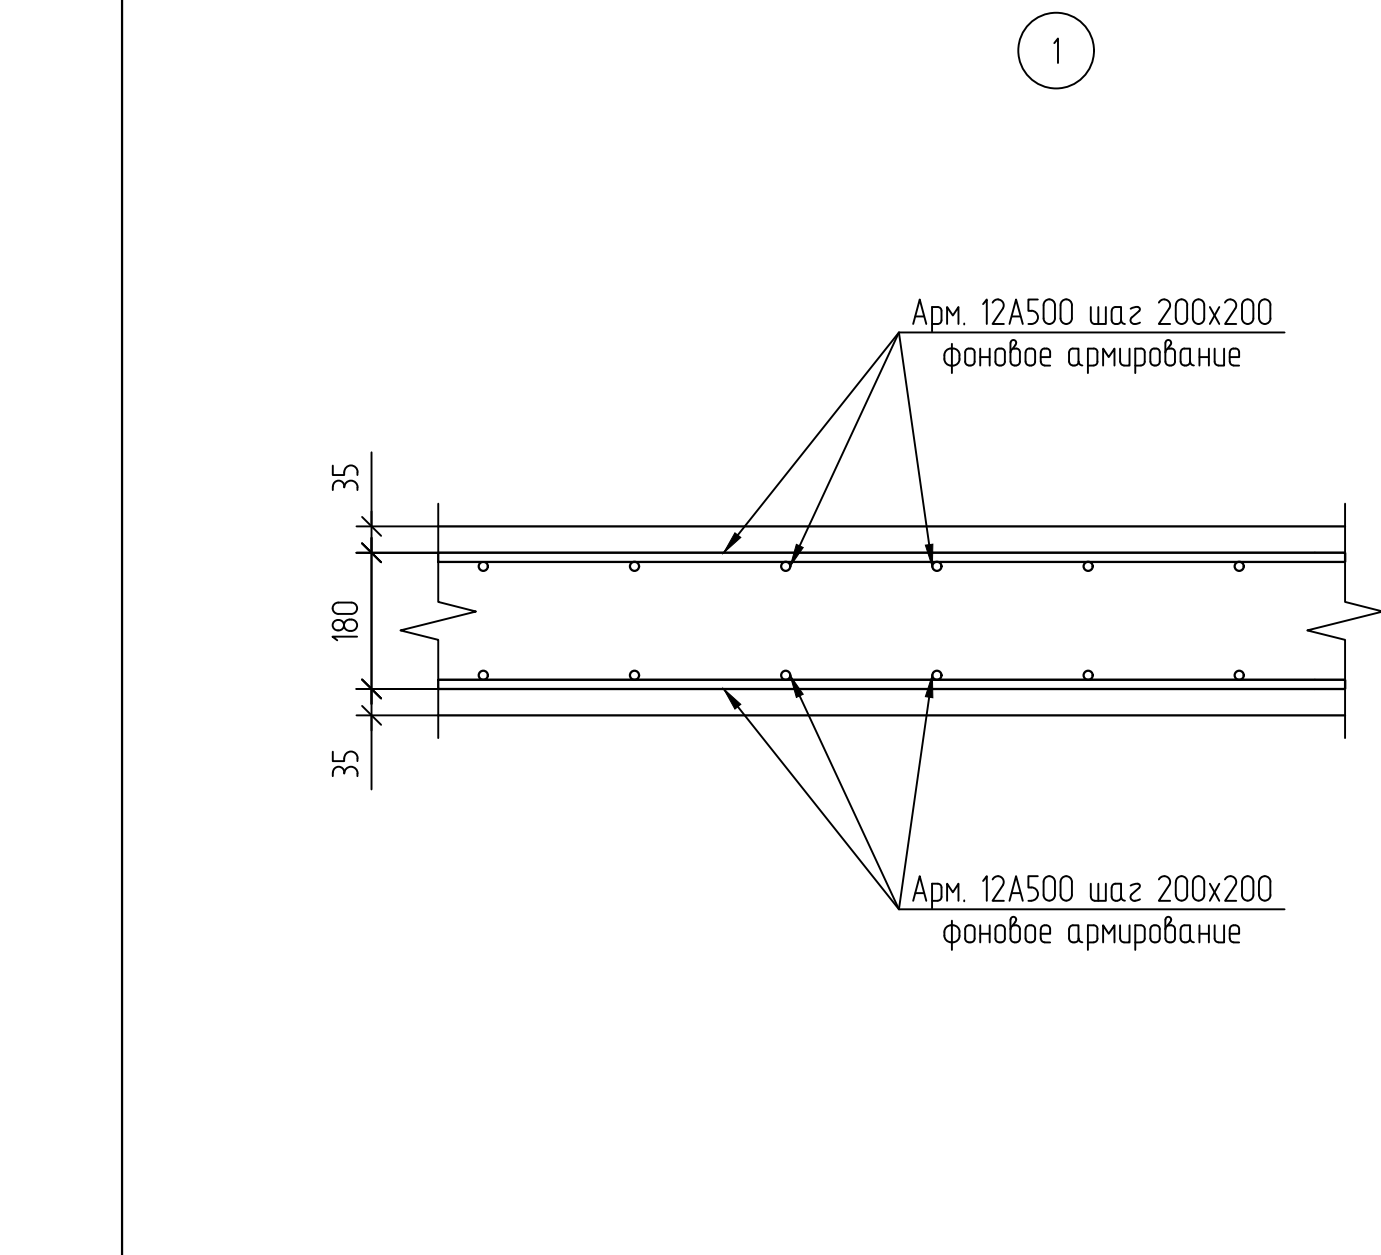





						708/П-24-АНД-КР					
						Капитальный ремонт общеобразовательного учреждения ГБОУ "Школа №1210" по адресу: г. Москва, ул. Живительная, д.32					
Изм.	Копуч	Лист	№ док.	Подп.	Дата	Конструктивные решения	Стадия	Лист	Листов		
Разработал	Горшин				04.26		Р	41			
ГАП	Фролова				04.26						
Н.Контроль	Лукашова				04.26	Деваркадер. Виды 1-8		компания проектирует, производит и устанавливает ООО "АРТИС"			
ГИП	Зыкин				04.26						

Схема плиты покрытия ПП-1 на отм. +3,650

Схема верхнего армирования плиты покрытия ПП-1





Схема нижнего армирования плиты покрытия ПП-1

Согласовано	
Инв. № подл.	Взам. инв. №
Подп. и дата	
Инв. № подл.	

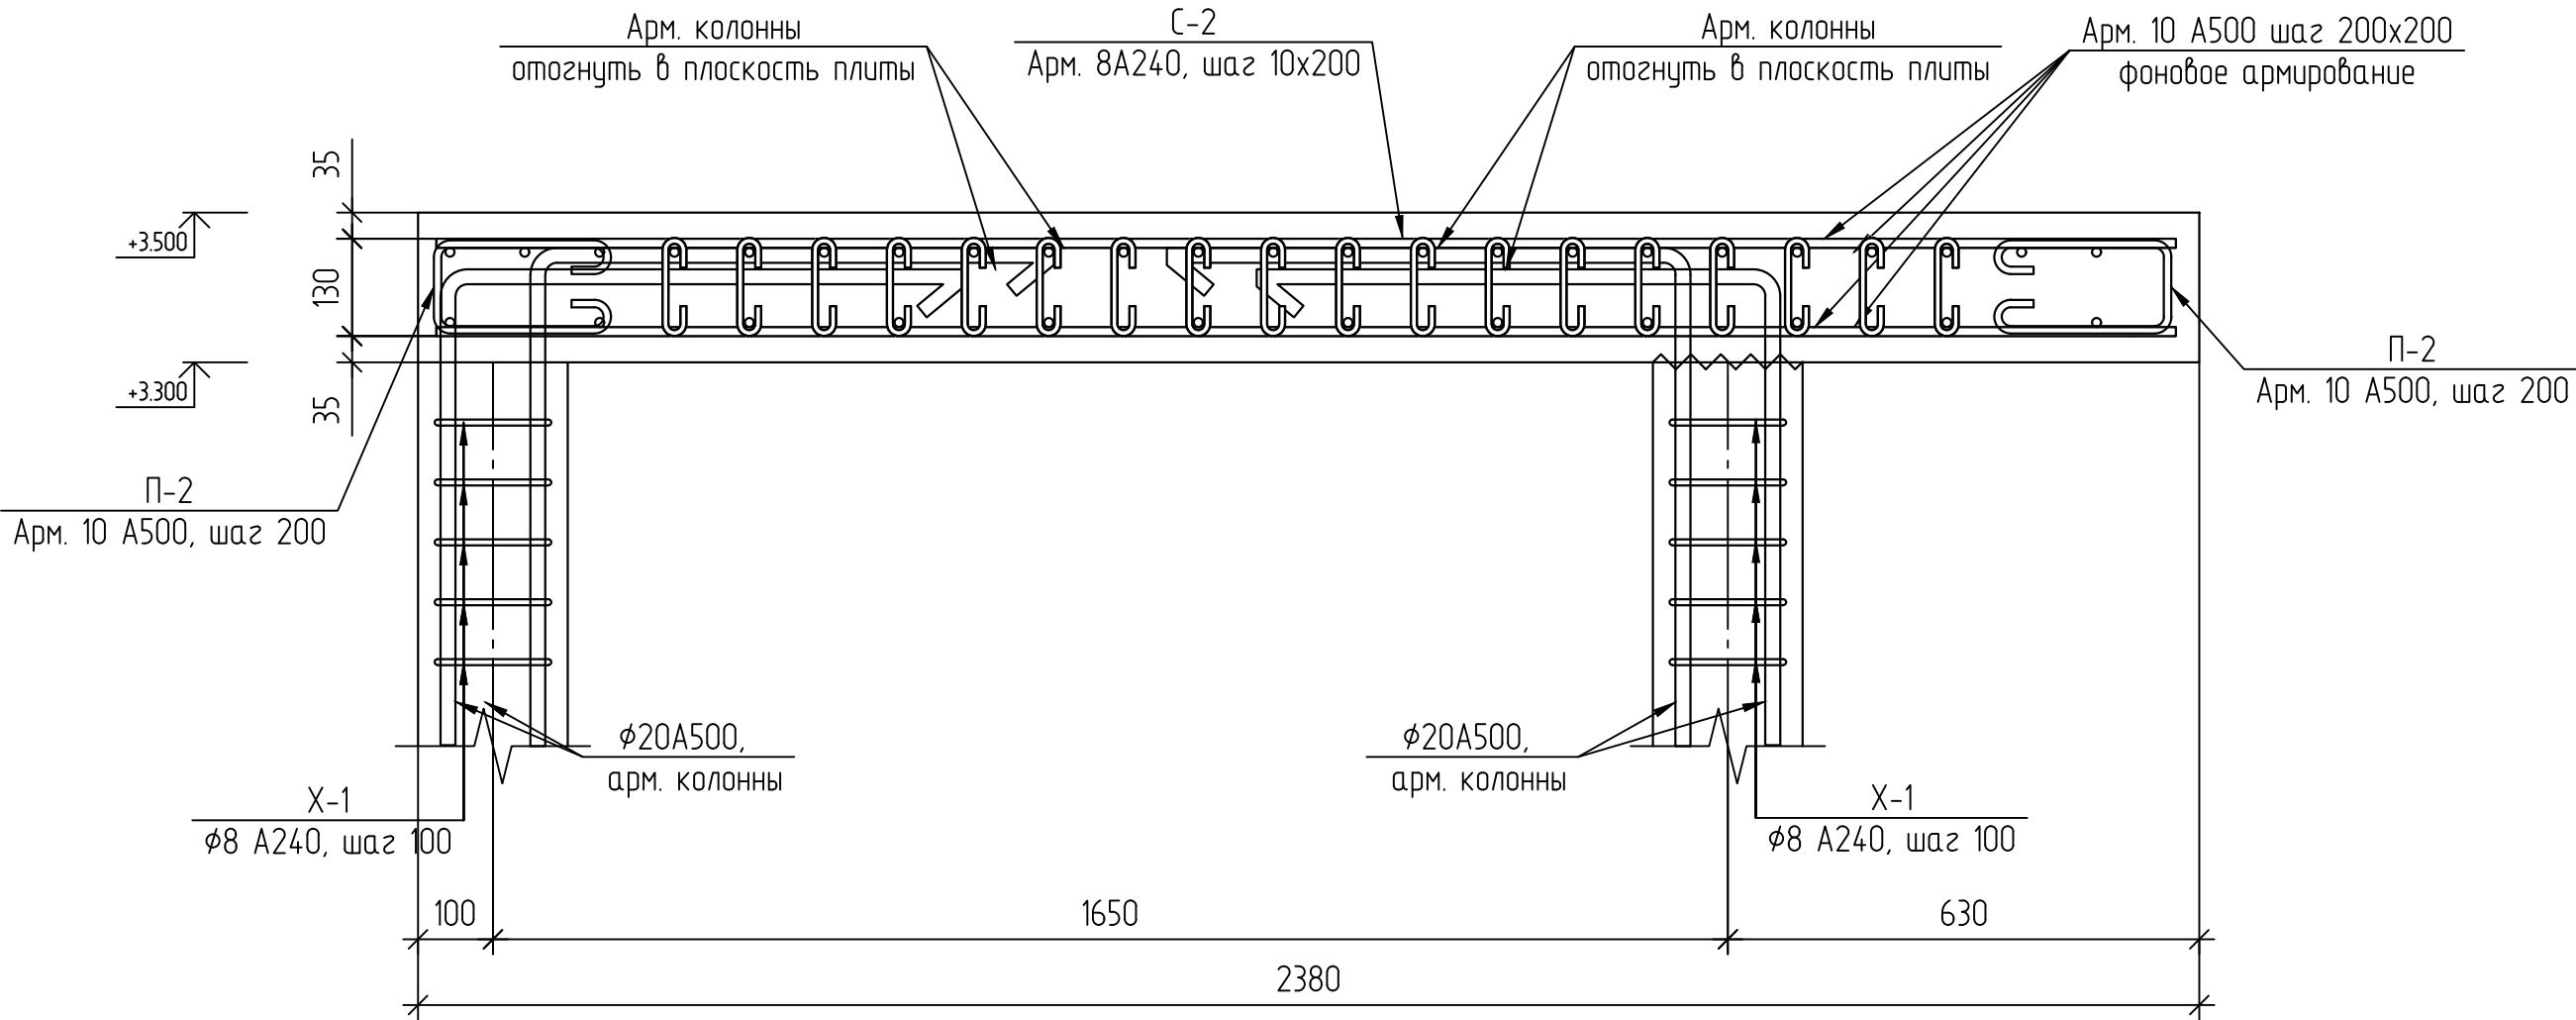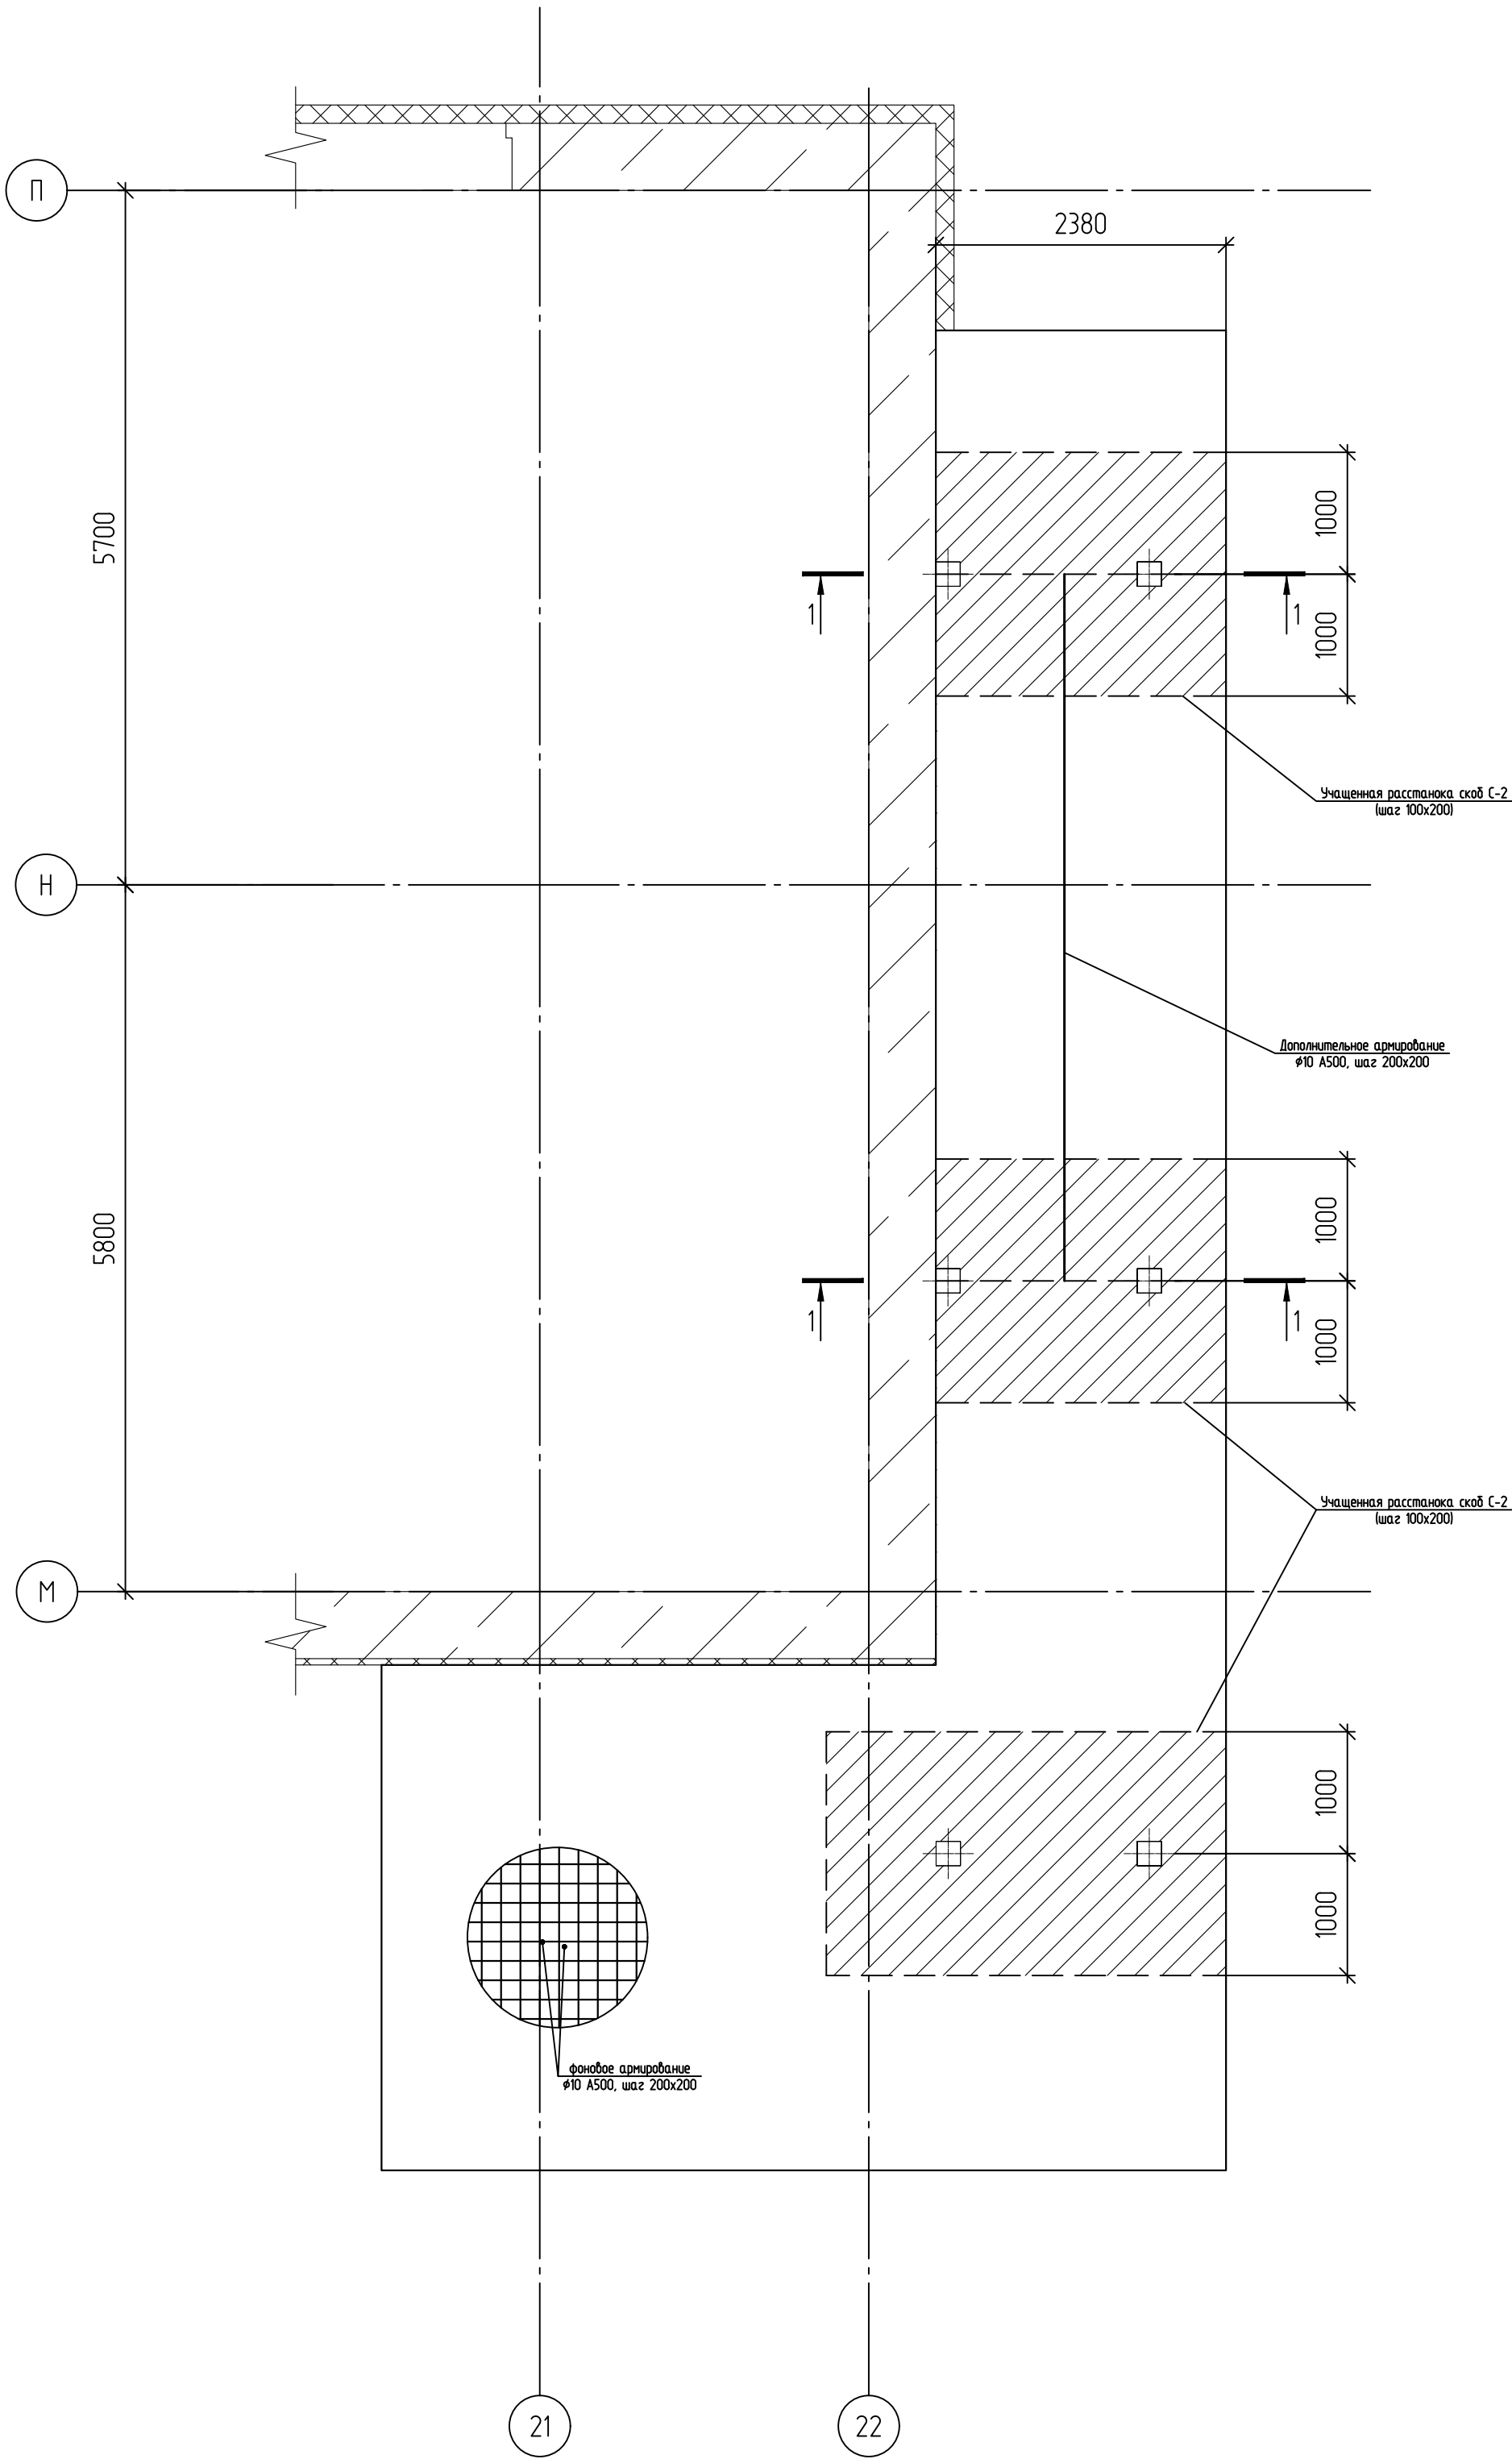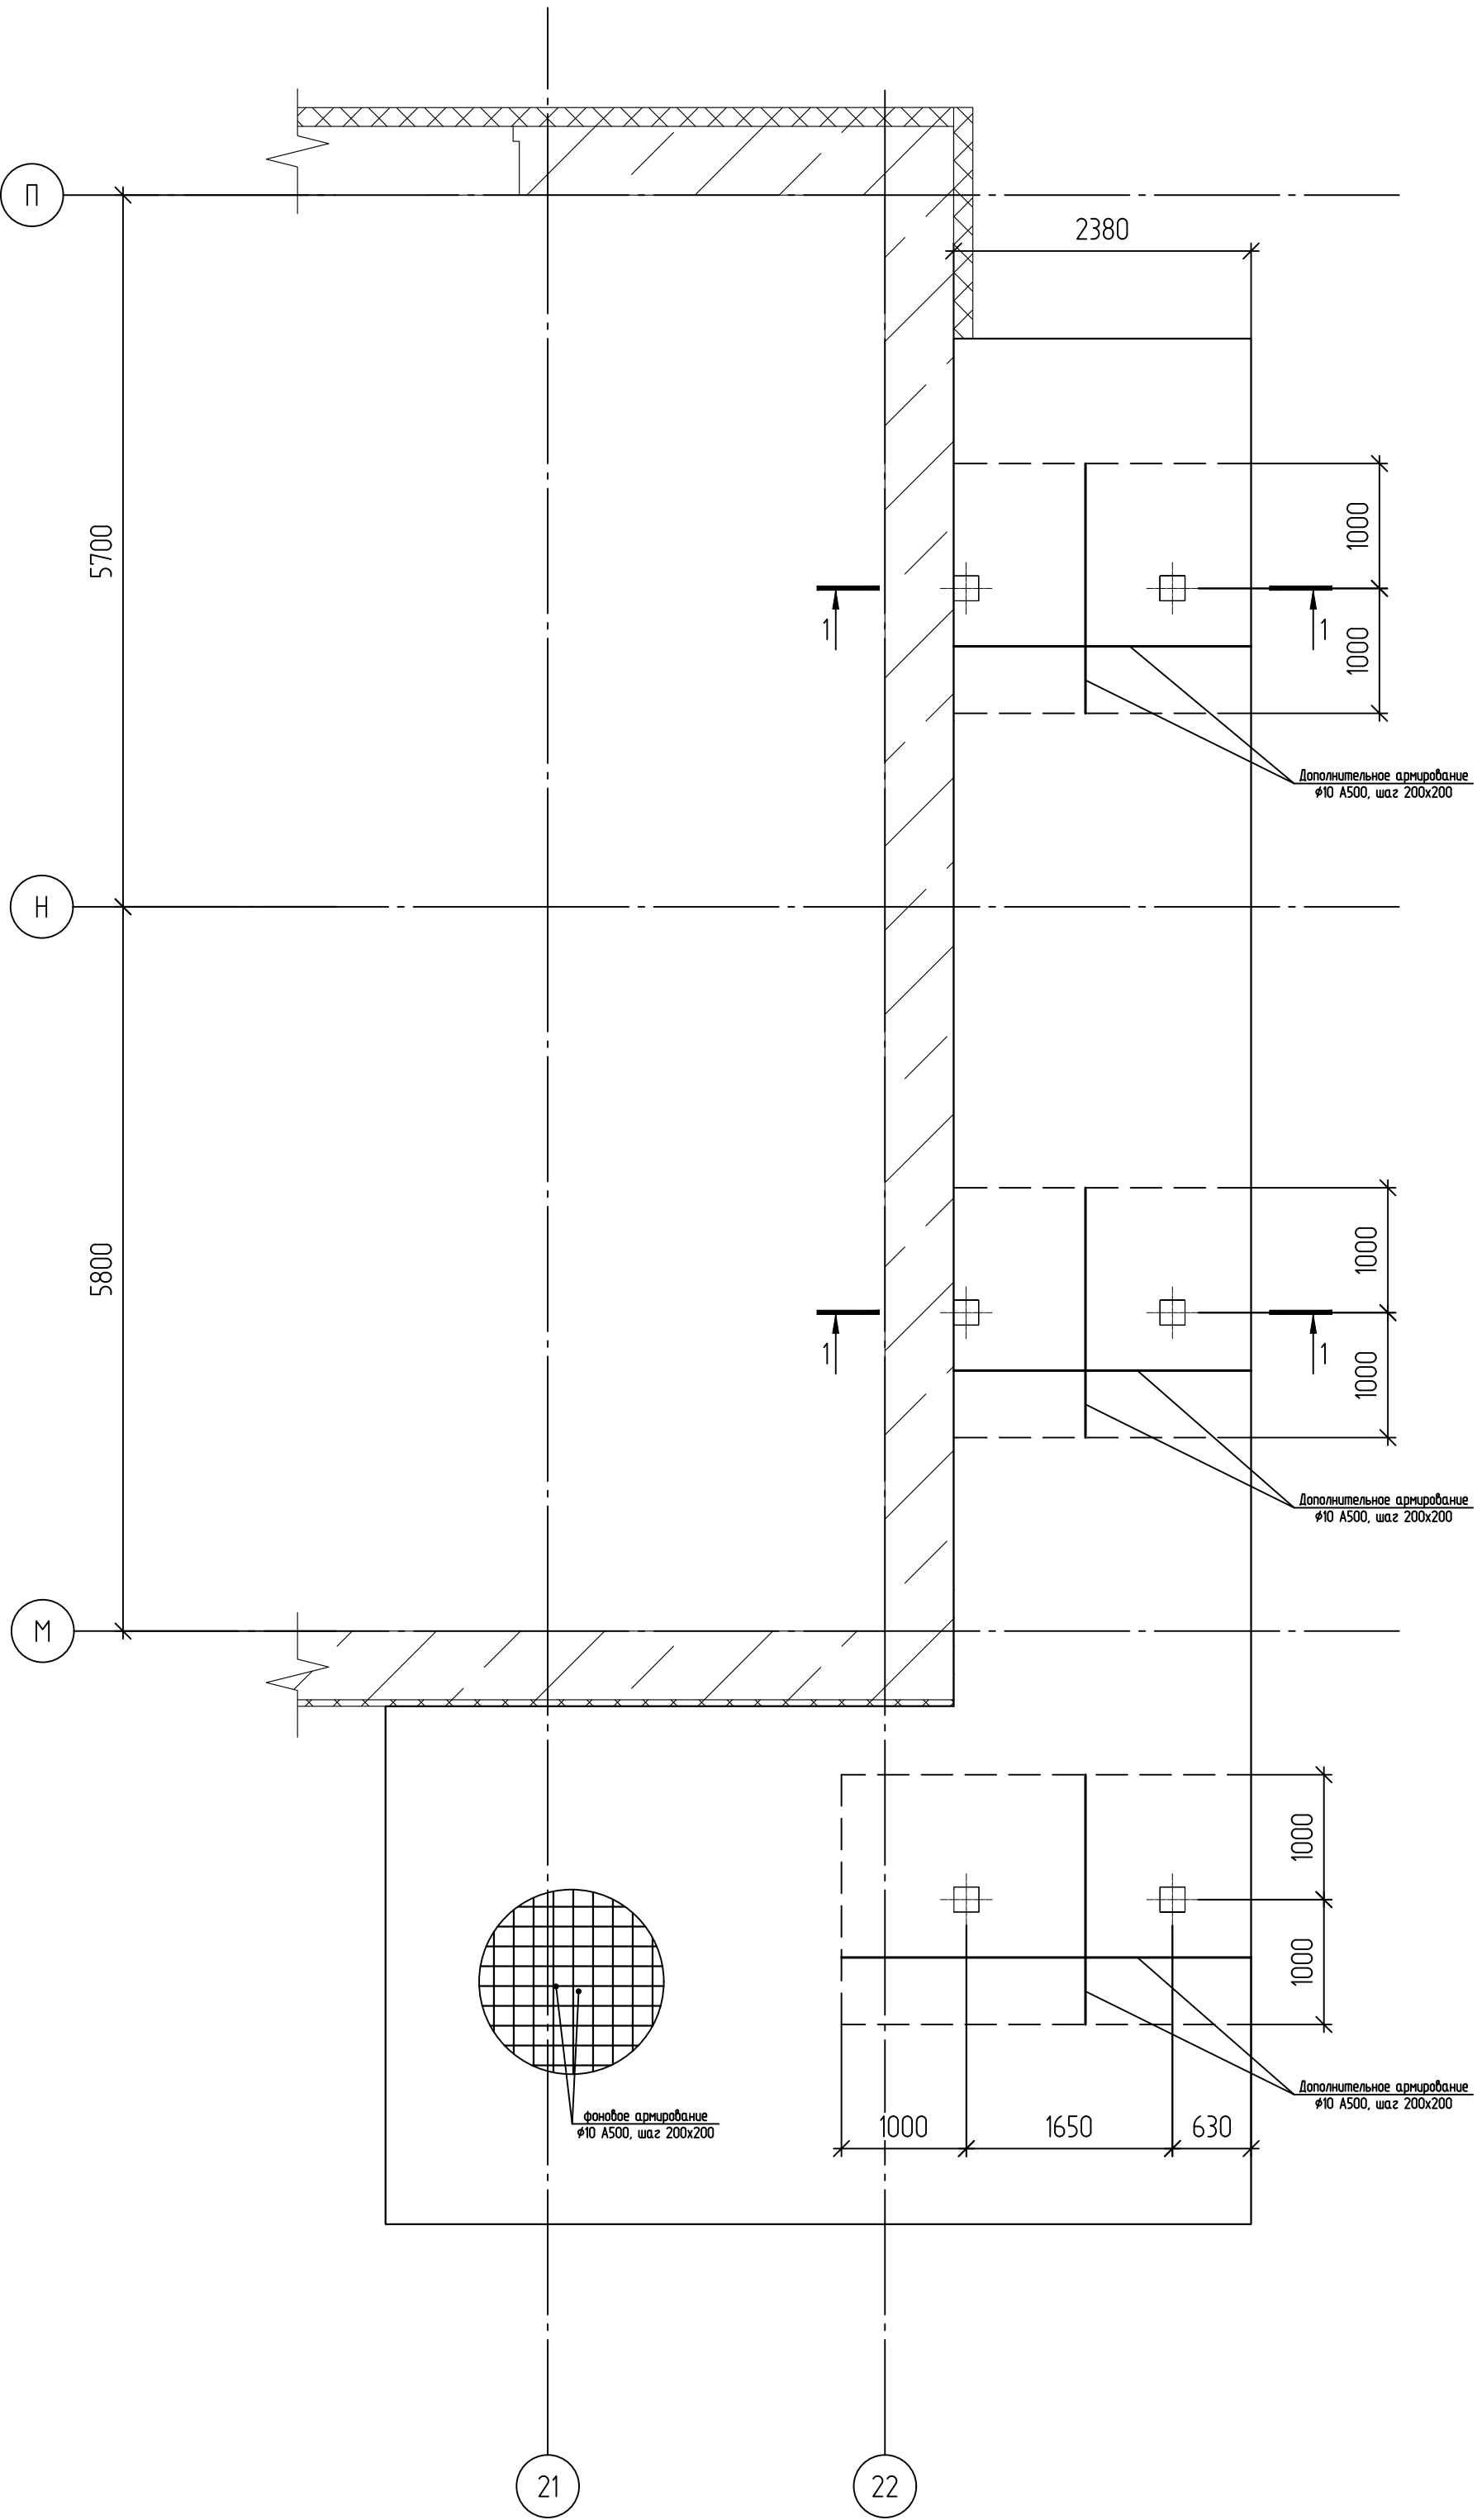
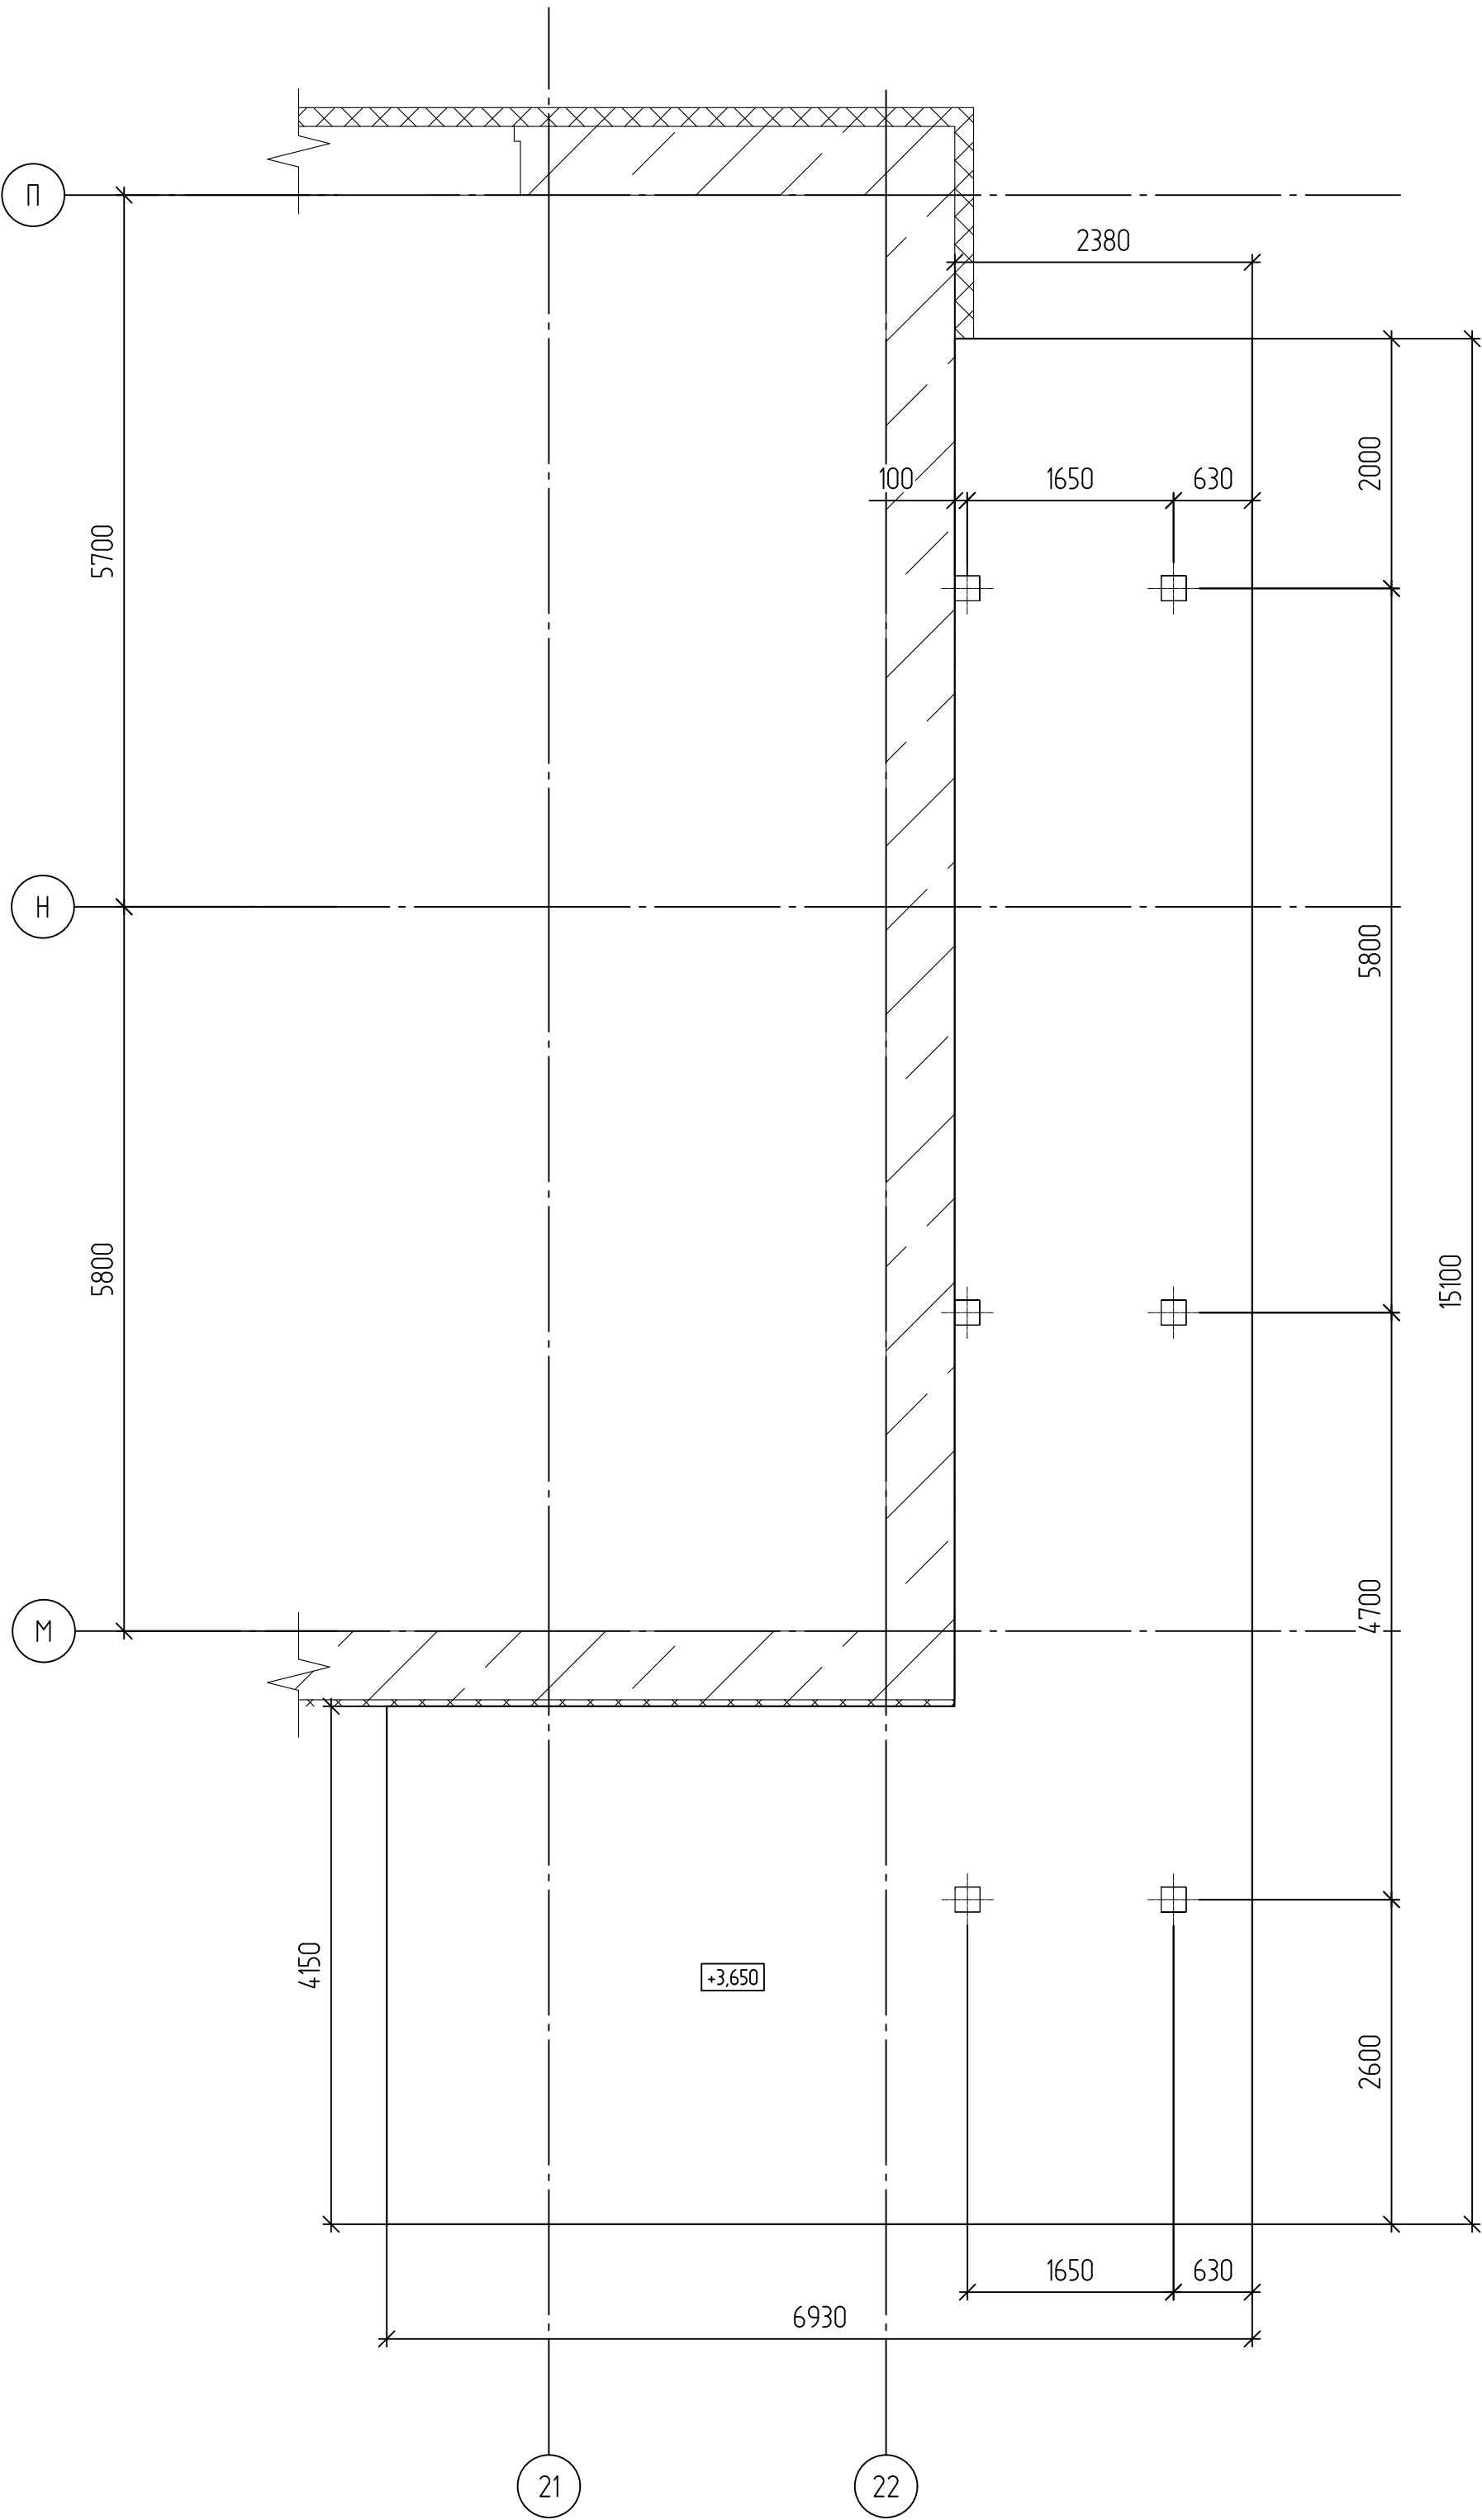


						708/П-24-АНО-КР			
						Капитальный ремонт общеобразовательного учреждения ГБОУ "Школа №1210" по адресу: г. Москва, ул. Хвостовская, д.32			
Изм.	Копию	Лист	№ док.	Подп.	Дата	Конструктивные решения	Стадия	Лист	Листов
Разработал	Горшин	04.26			04.26		Р	42	
ГАП	Фролова	04.26							
Н.Контроль	Лукашова	04.26			04.26	Дебюкадер: Плита покрытия ПП-1		исполнение проектных решений с применением BIM-технологий	ООО "АРТИС"
ГИП	Зыкин	04.26			04.26				

Колонна К-1

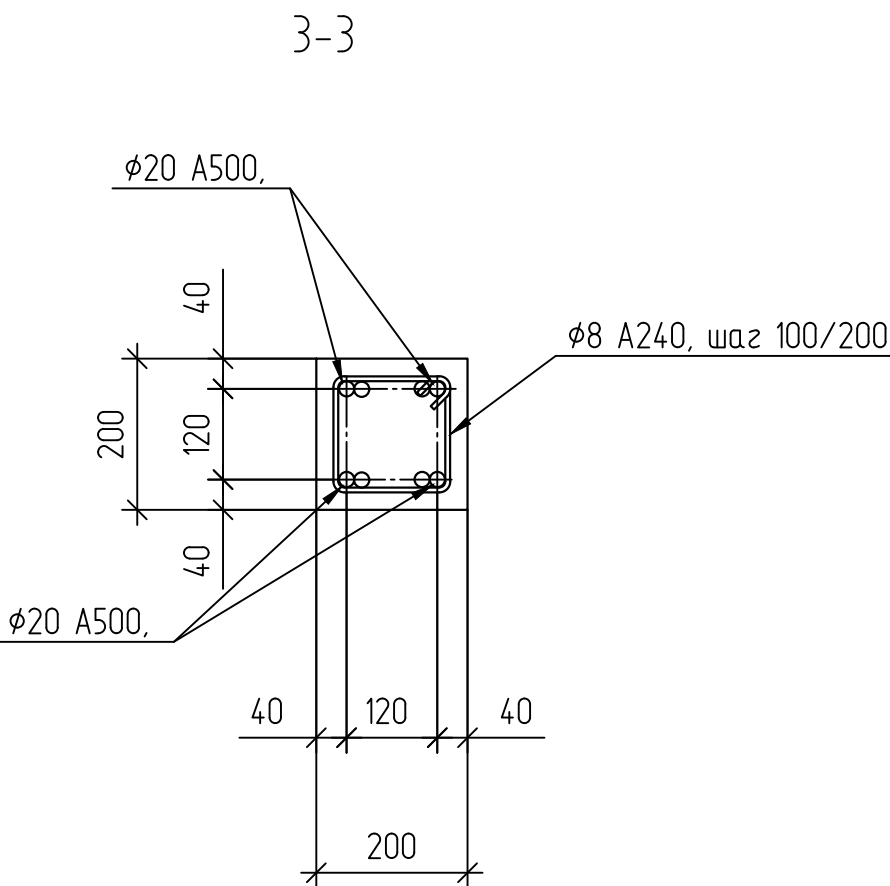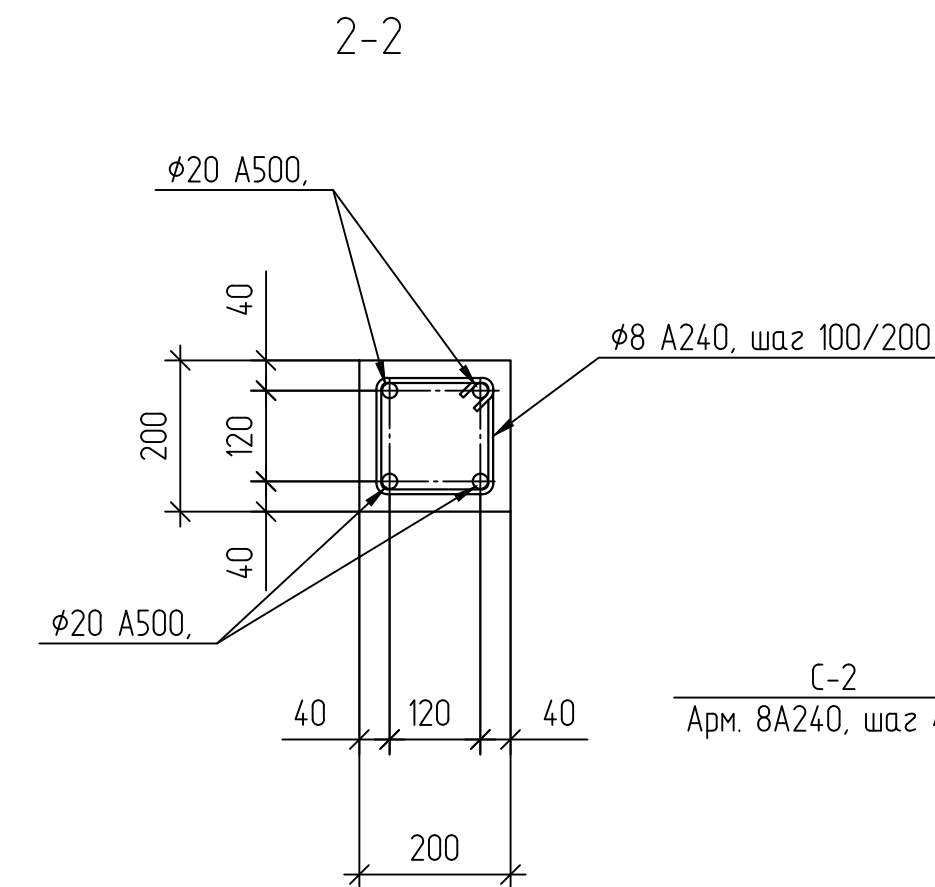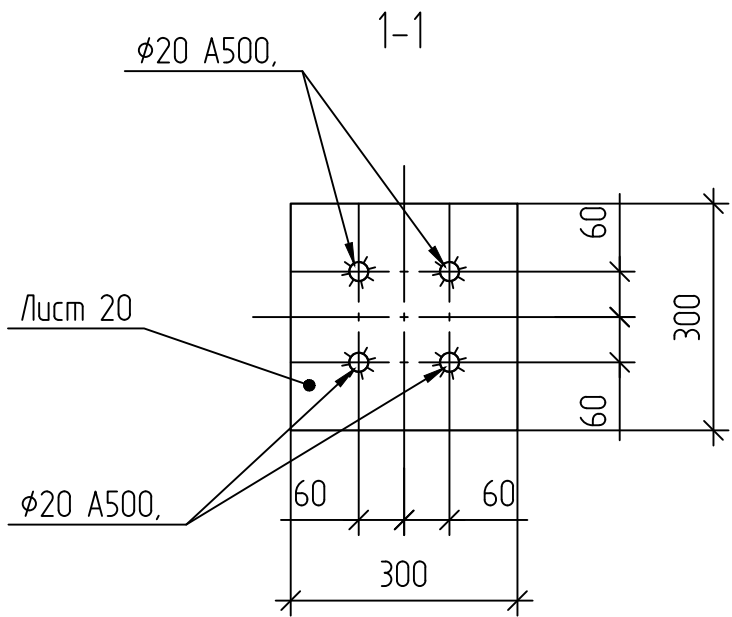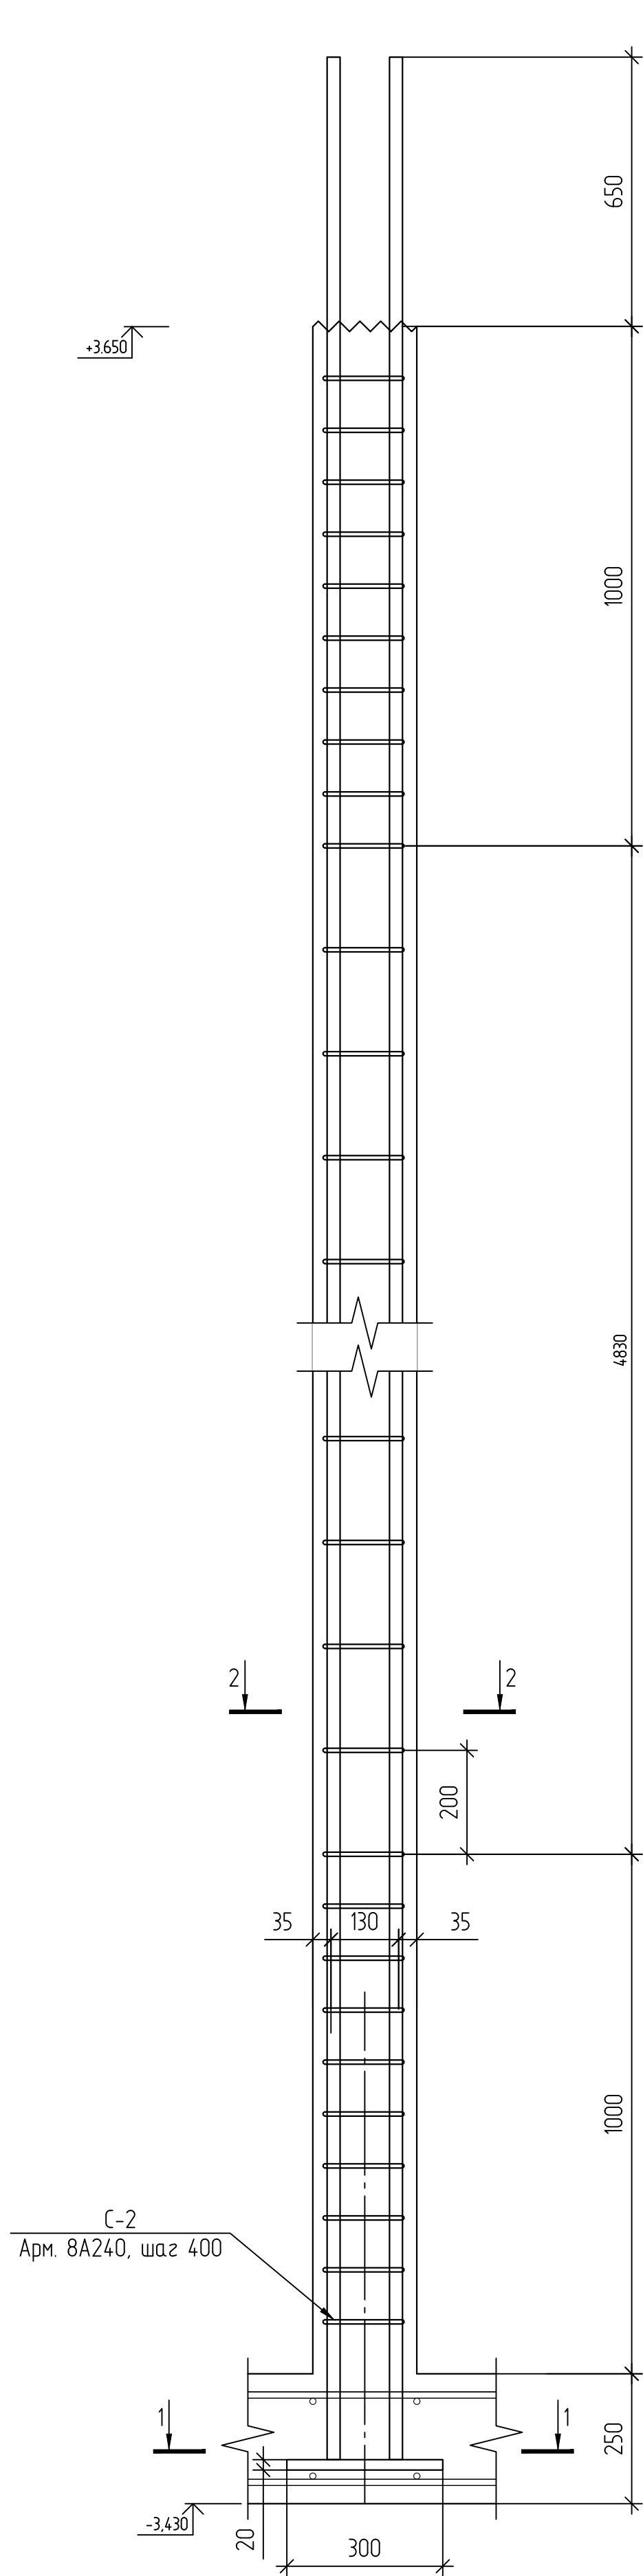


Колонна К-2

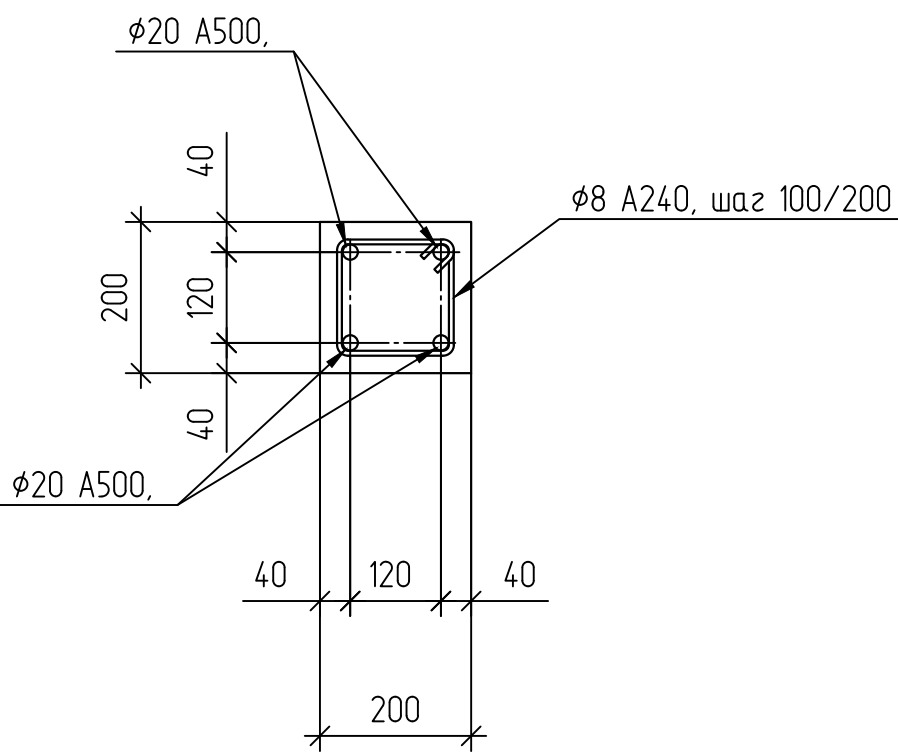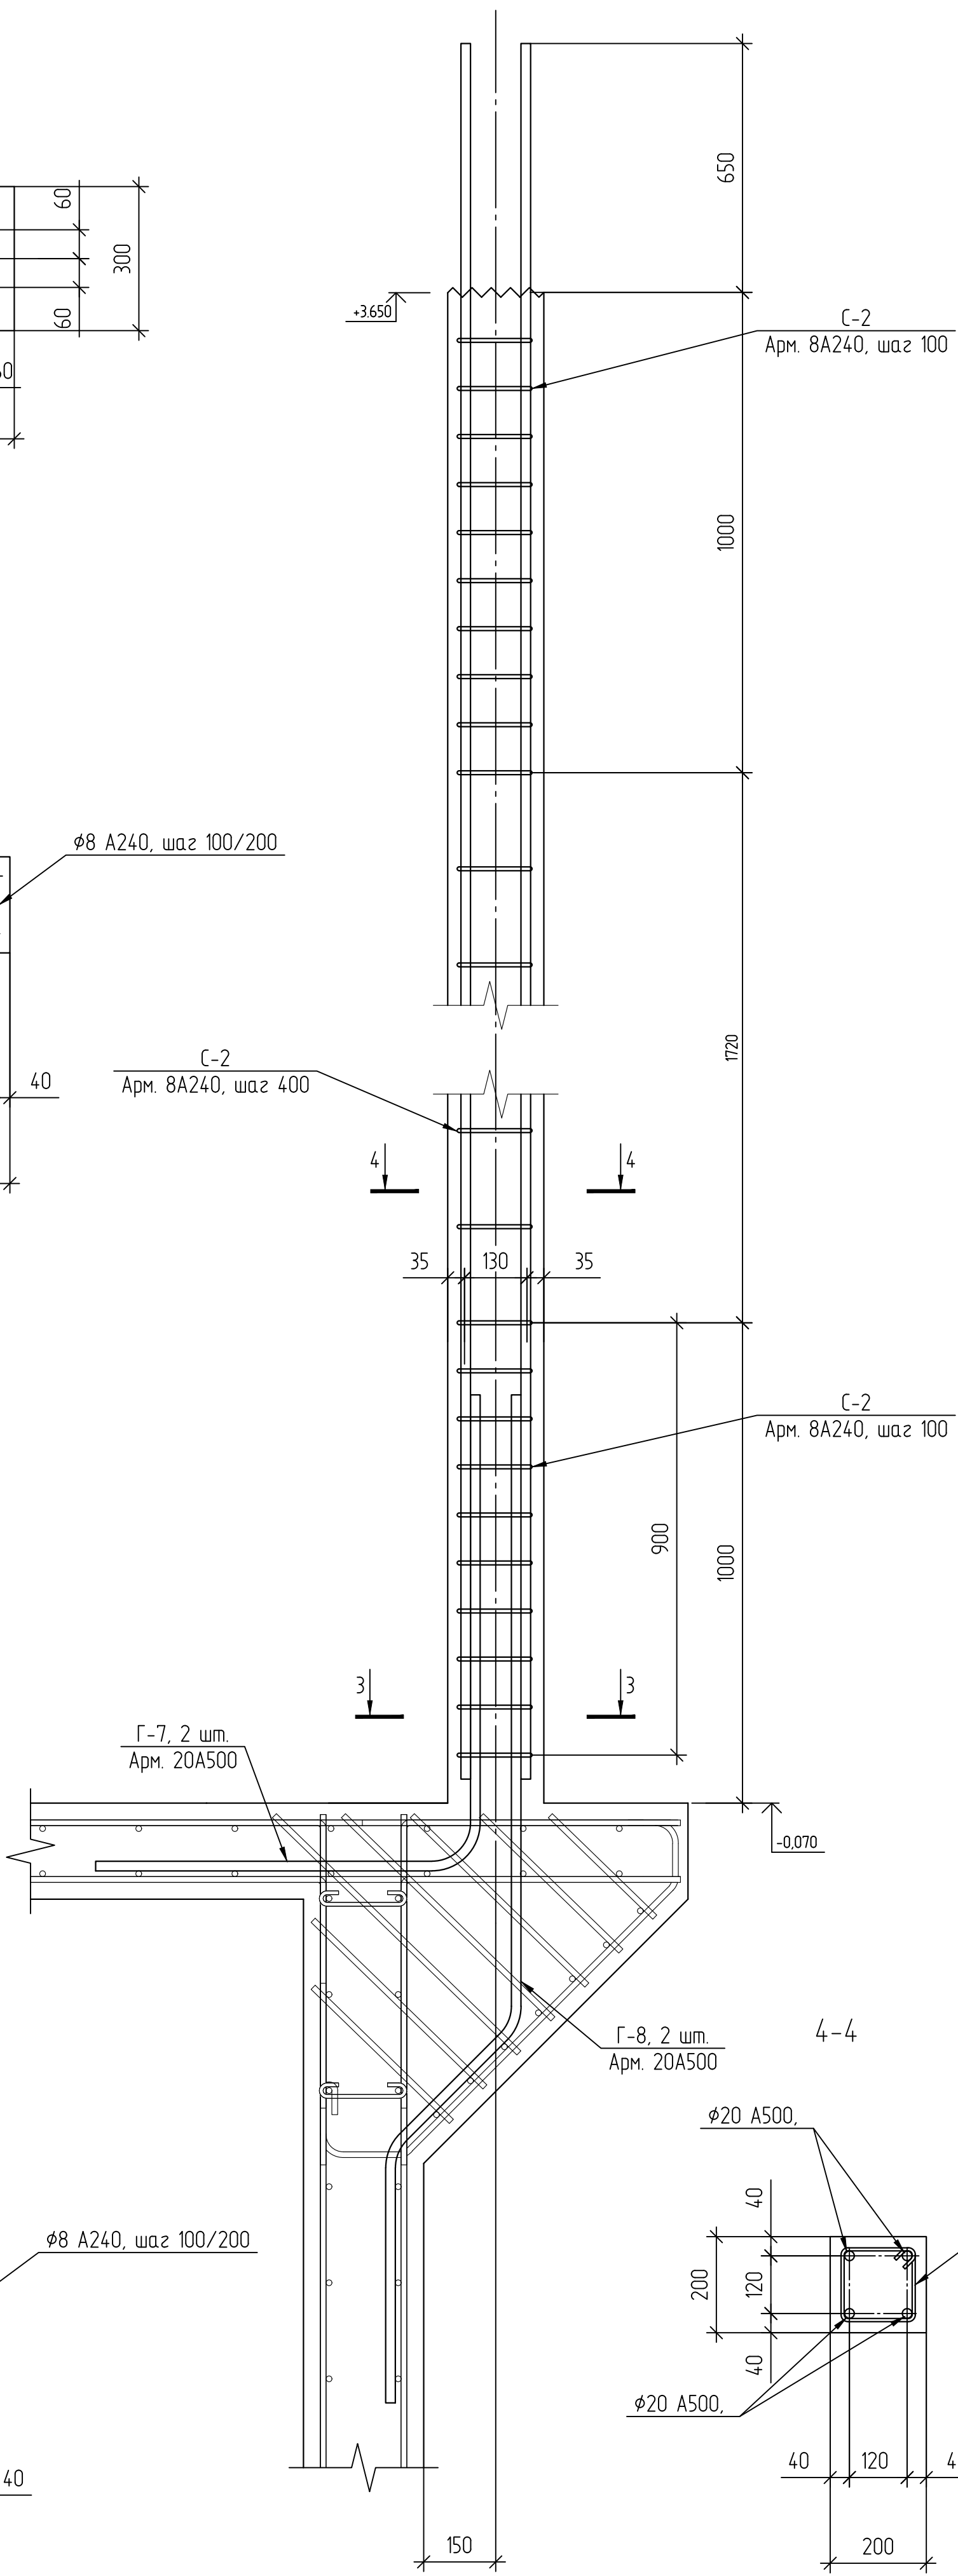


Ведомость деталей	
Поз.	Эскиз
П-1	
П-2	
С-1	
С-2	
С-3	
Г-1	
Г-2	
Г-3	
Г-4	
Г-5	
Г6	
Г-7	
Г-8	
Х-1	

Поз.	Обозначение	Наименование	Кол.	Масса, ед. кг	Примечание
		Фундаментная плита	1		
	ГОСТ 34028-2016	Арматура $\phi 12$ А500, м.п.	690	0,888	612,7
П-1	ГОСТ 34028-2016	Арматура $\phi 12$ А500, L=1350	78	1,2	93,6
Г-1	ГОСТ 34028-2016	Арматура $\phi 12$ А500, L=1200	345	1,0	345,0
	ГОСТ 26633-2012	Бетон В25 F100 W6, м.куб.	8,8		
		Стеклоизол, м.кв. (2 слоя)	80		
		Смесь ПГС, м.куб.	3,9		
		Плита дебаркадера	1		
	ГОСТ 34028-2016	Арматура $\phi 12$ А500, м.п.	870	0,888	772,6
П-2	ГОСТ 34028-2016	Арматура $\phi 12$ А500, L=700	68	1,2	81,6
Г-1	ГОСТ 34028-2016	Арматура $\phi 12$ А500, L=1200	780	1,0	780,0
Г-6	ГОСТ 34028-2016	Арматура $\phi 12$ А500, L=2160	14	1,0	14,0
	ГОСТ 26633-2012	Бетон В25 F100 W6, м.куб.	8		
		Стены дебаркадера	1		
	ГОСТ 34028-2016	Арматура $\phi 12$ А500, м.п.	2504	0,888	2223,6
С-1	ГОСТ 34028-2016	Арматура $\phi 8$ А240, L=230	120	0,15	18,0
С-2	ГОСТ 34028-2016	Арматура $\phi 8$ А240, L=280	560	0,18	100,8
С-3	ГОСТ 34028-2016	Арматура $\phi 8$ А240, L=330	6	0,21	13
	ГОСТ 26633-2012	Бетон В25F100 W6, м.куб.	26,5		
		Обмазочная гидроизоляция (битум), м.кв.	100		
		Лестницы	1		
	ГОСТ 34028-2016	Арматура $\phi 12$ А500, м.п.	210	0,888	186,5
Г-2	ГОСТ 34028-2016	Арматура $\phi 12$ А500, L=1200	28	1,0	28,0
Г-3	ГОСТ 34028-2016	Арматура $\phi 12$ А500, L=715	70	0,7	49,0
Г-4	ГОСТ 34028-2016	Арматура $\phi 12$ А500, L=1200	24	1,0	24,0
Г-5	ГОСТ 34028-2016	Арматура $\phi 12$ А500, L=760	72	0,7	50,4
С-2	ГОСТ 34028-2016	Арматура $\phi 8$ А240, L=200	128	0,1	12,8
	ГОСТ 26633-2012	Бетон В25 F100 W6, м.куб.	3,3		
		Колонна К1	3		
	ГОСТ 19903-2015	Лист 20x300x300	1	14	14,0
	ГОСТ 34028-2016	Арматура $\phi 20$ А500, L=7650	4	18,9	75,6
Х-1	ГОСТ 34028-2016	Арматура $\phi 8$ А240, L=650	44	0,26	11,4
	ГОСТ 26633-2012	Бетон В25 F100 W6, м.куб.	0,28		
		Колонна К2	3		
	ГОСТ 34028-2016	Арматура $\phi 20$ А500, L=4350	4	10,8	43,2
Г-7	ГОСТ 34028-2016	Арматура $\phi 20$ А500, L=1600	2	3,96	7,9
Г-8	ГОСТ 34028-2016	Арматура $\phi 20$ А500, L=2200	2	5,44	10,9
Х-1	ГОСТ 34028-2016	Арматура $\phi 8$ А240, L=650	29	0,26	7,5
	ГОСТ 26633-2012	Бетон В25 F100 W6, м.куб.	0,15		
		Плита навеса	1		
	ГОСТ 34028-2016	Арматура $\phi 10$ А500, м.п.	2510	0,617	1548,7
П-2	ГОСТ 34028-2016	Арматура $\phi 10$ А500, L=700	230	0,43	98,9
С-2	ГОСТ 34028-2016	Арматура $\phi 8$ А240, L=200	350	0,1	35,0
	ГОСТ 26633-2012	Бетон В25 F100 W6, м.куб.	11,3		


Разрез 4-4

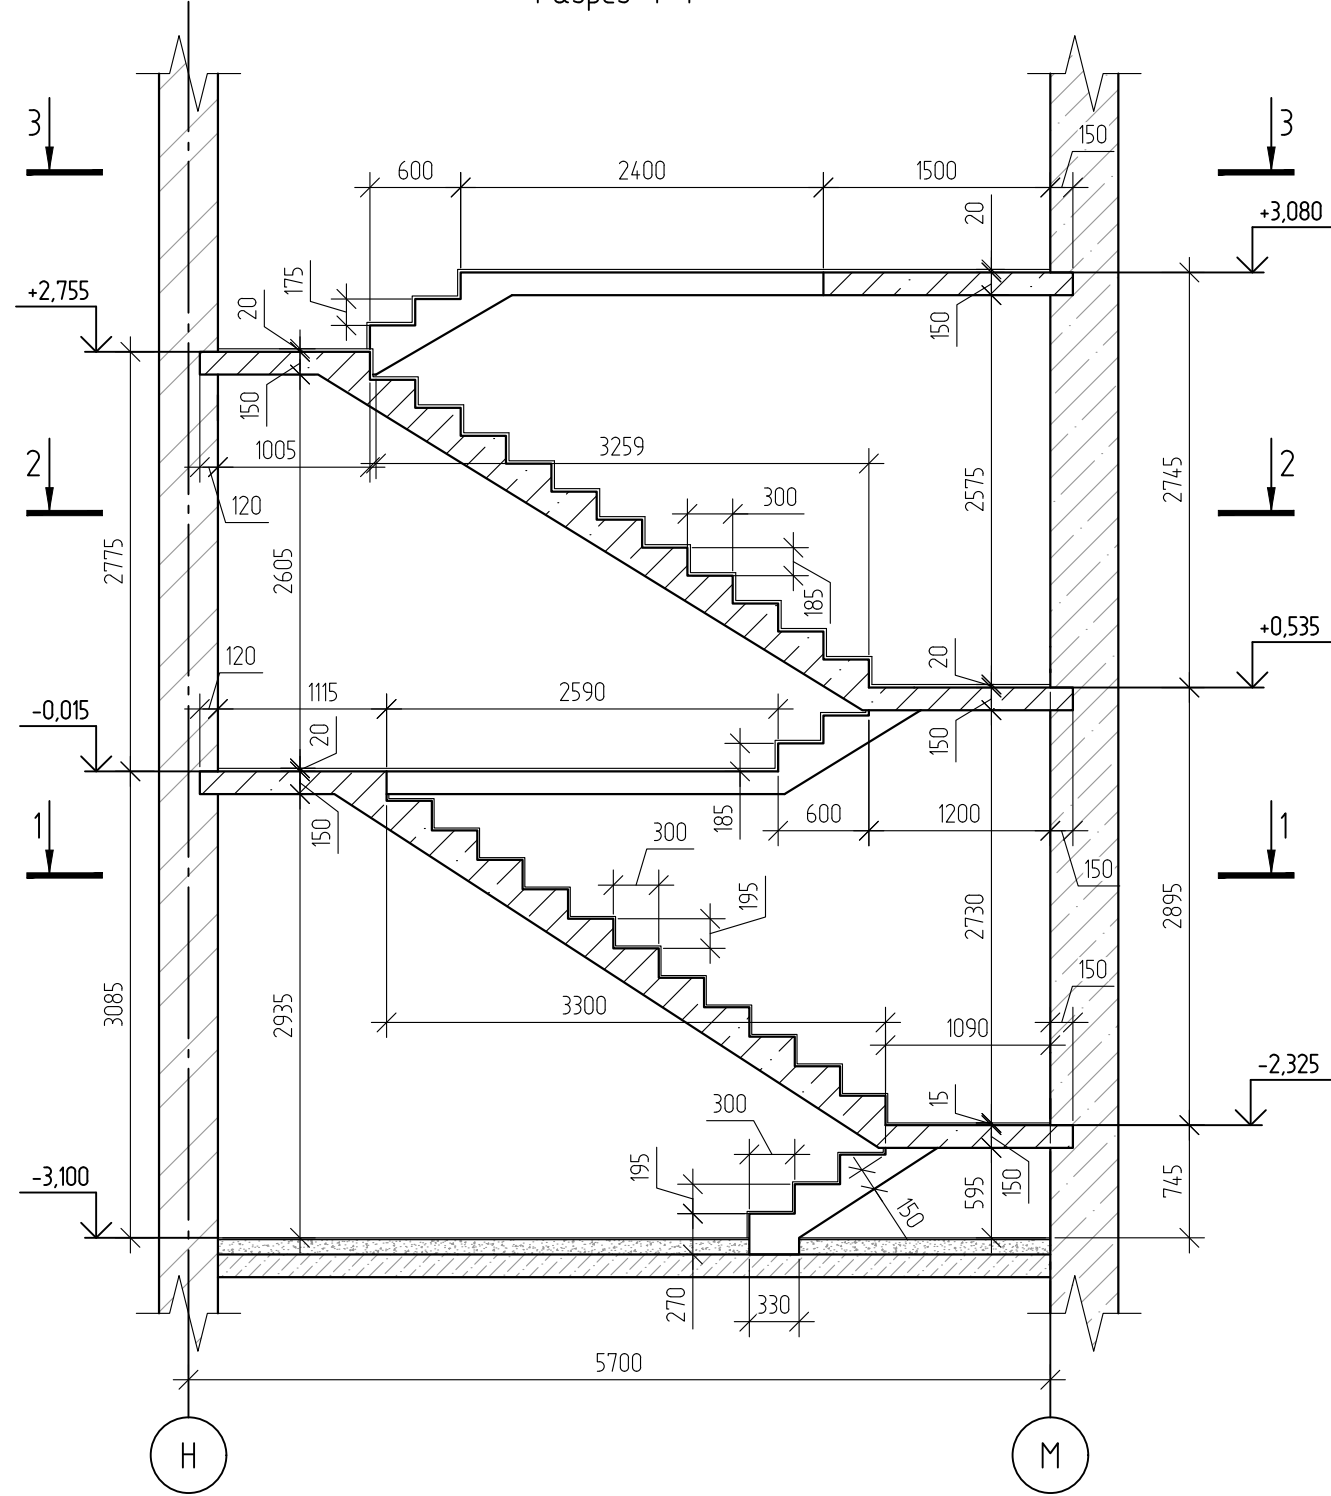


Разрез 5-5

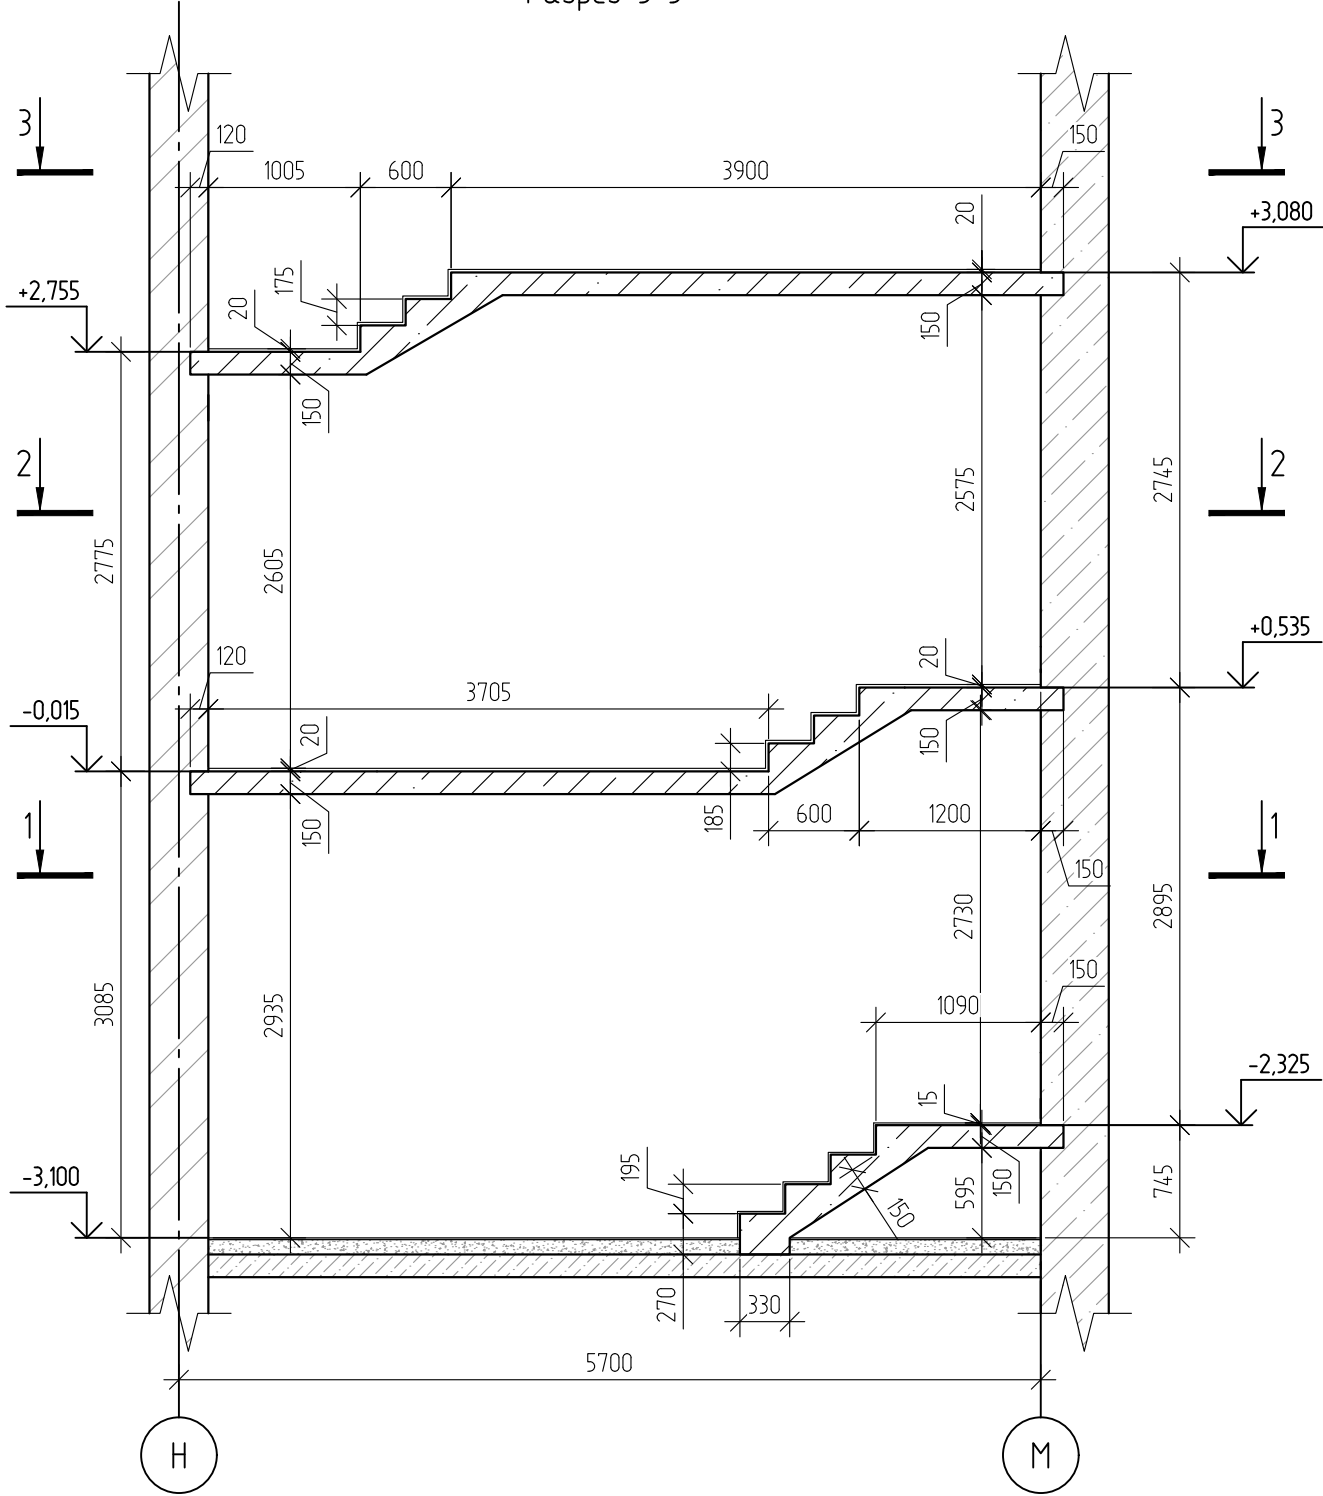


Армирование. Разрез 4-4

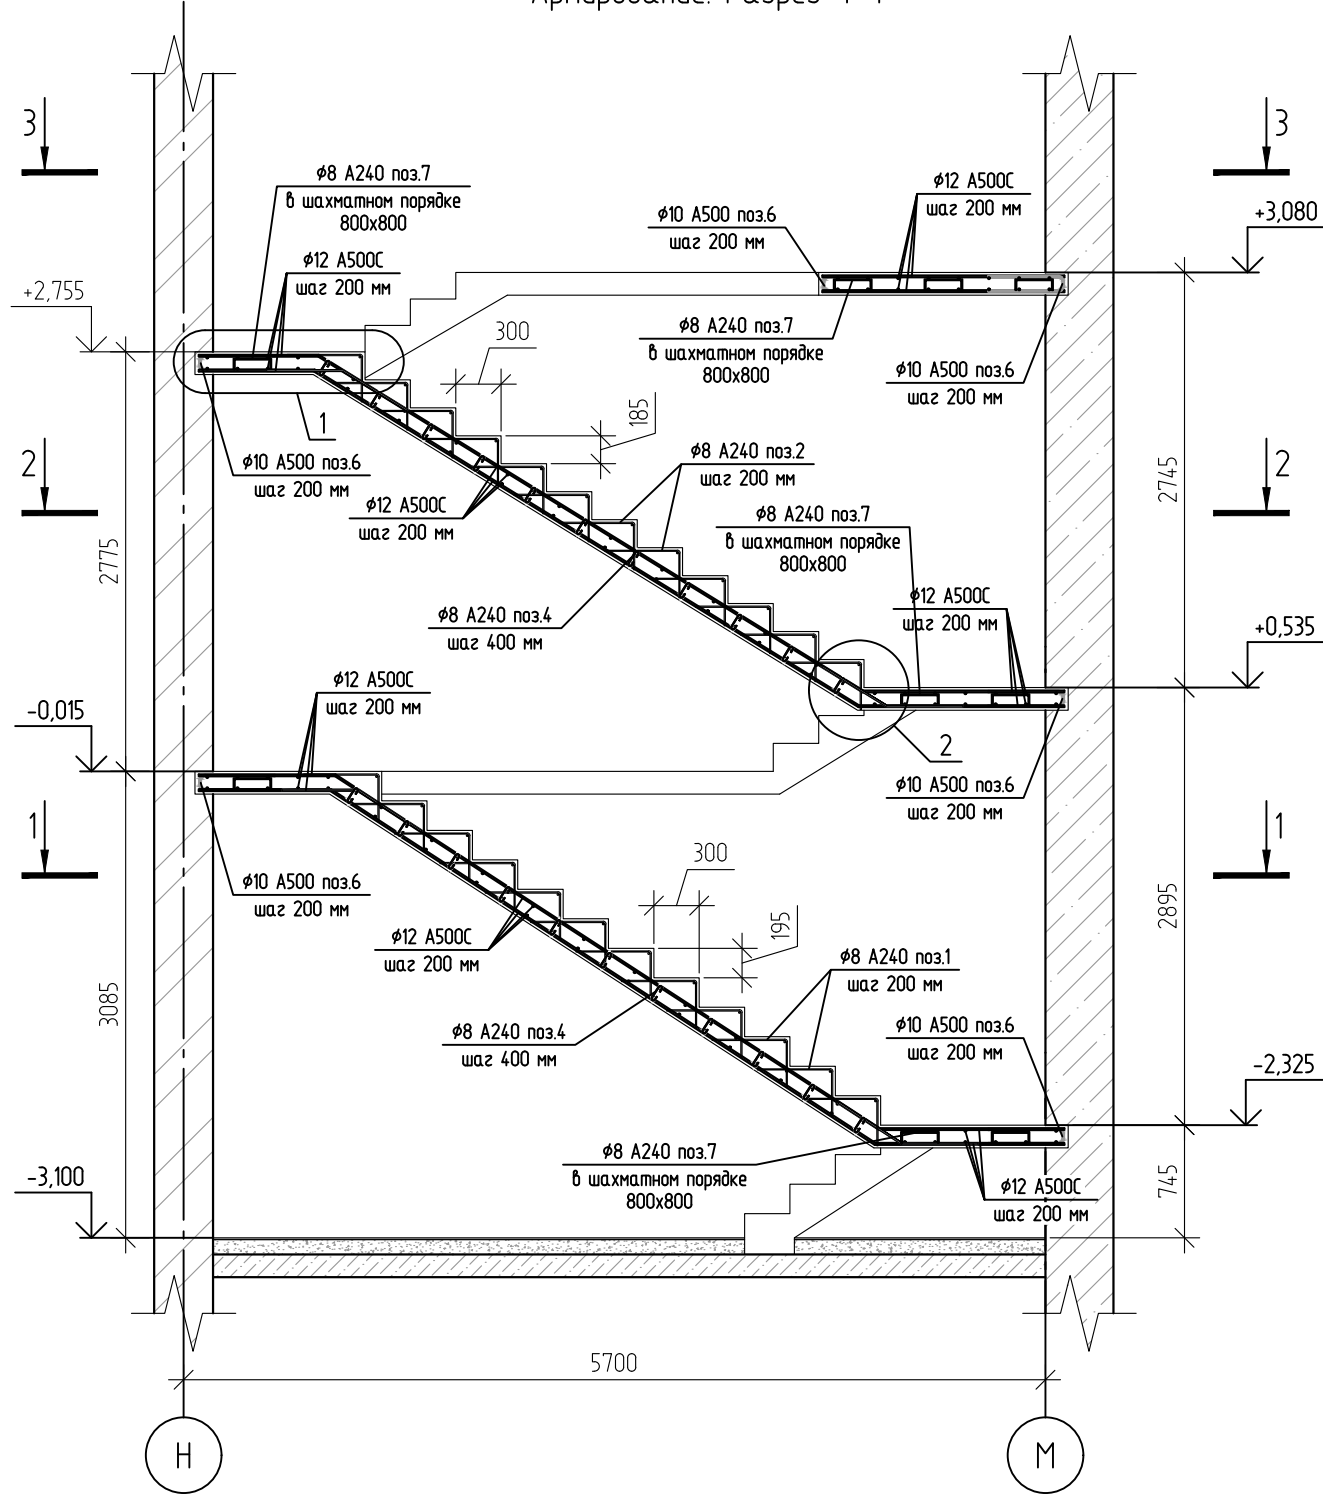


Разрез 1-1

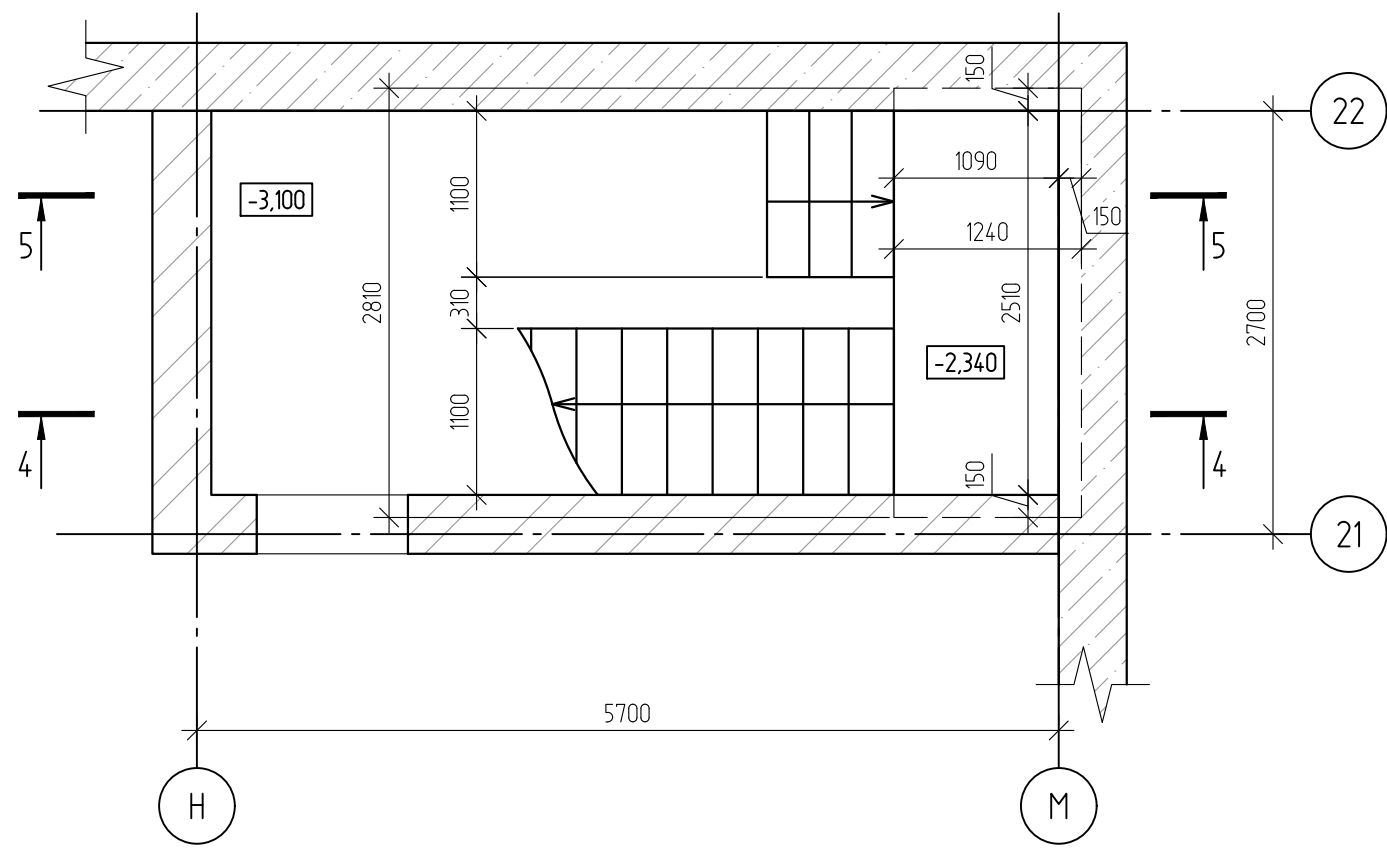





Разрез 2-2

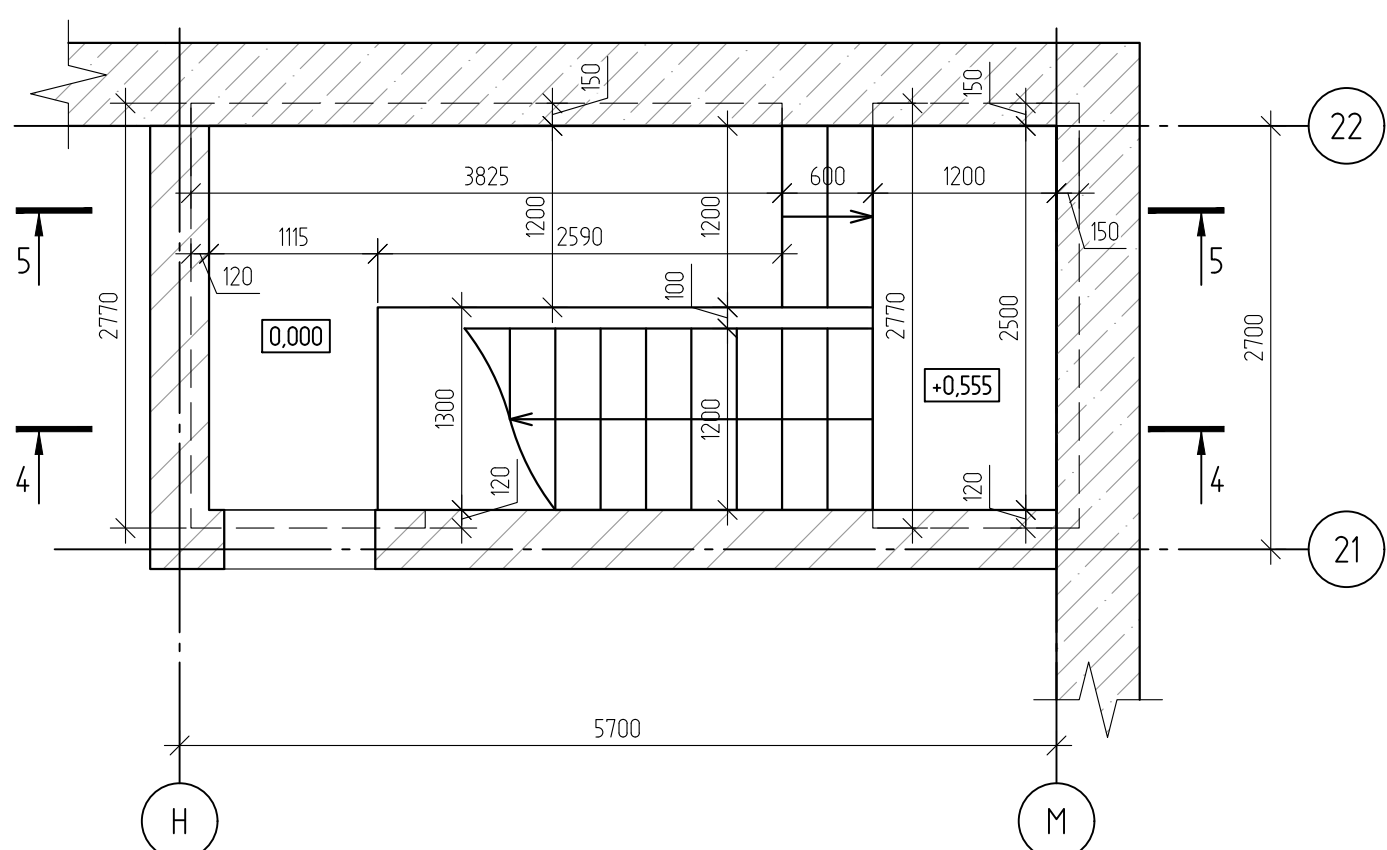


Армирование. Разрез 5-5

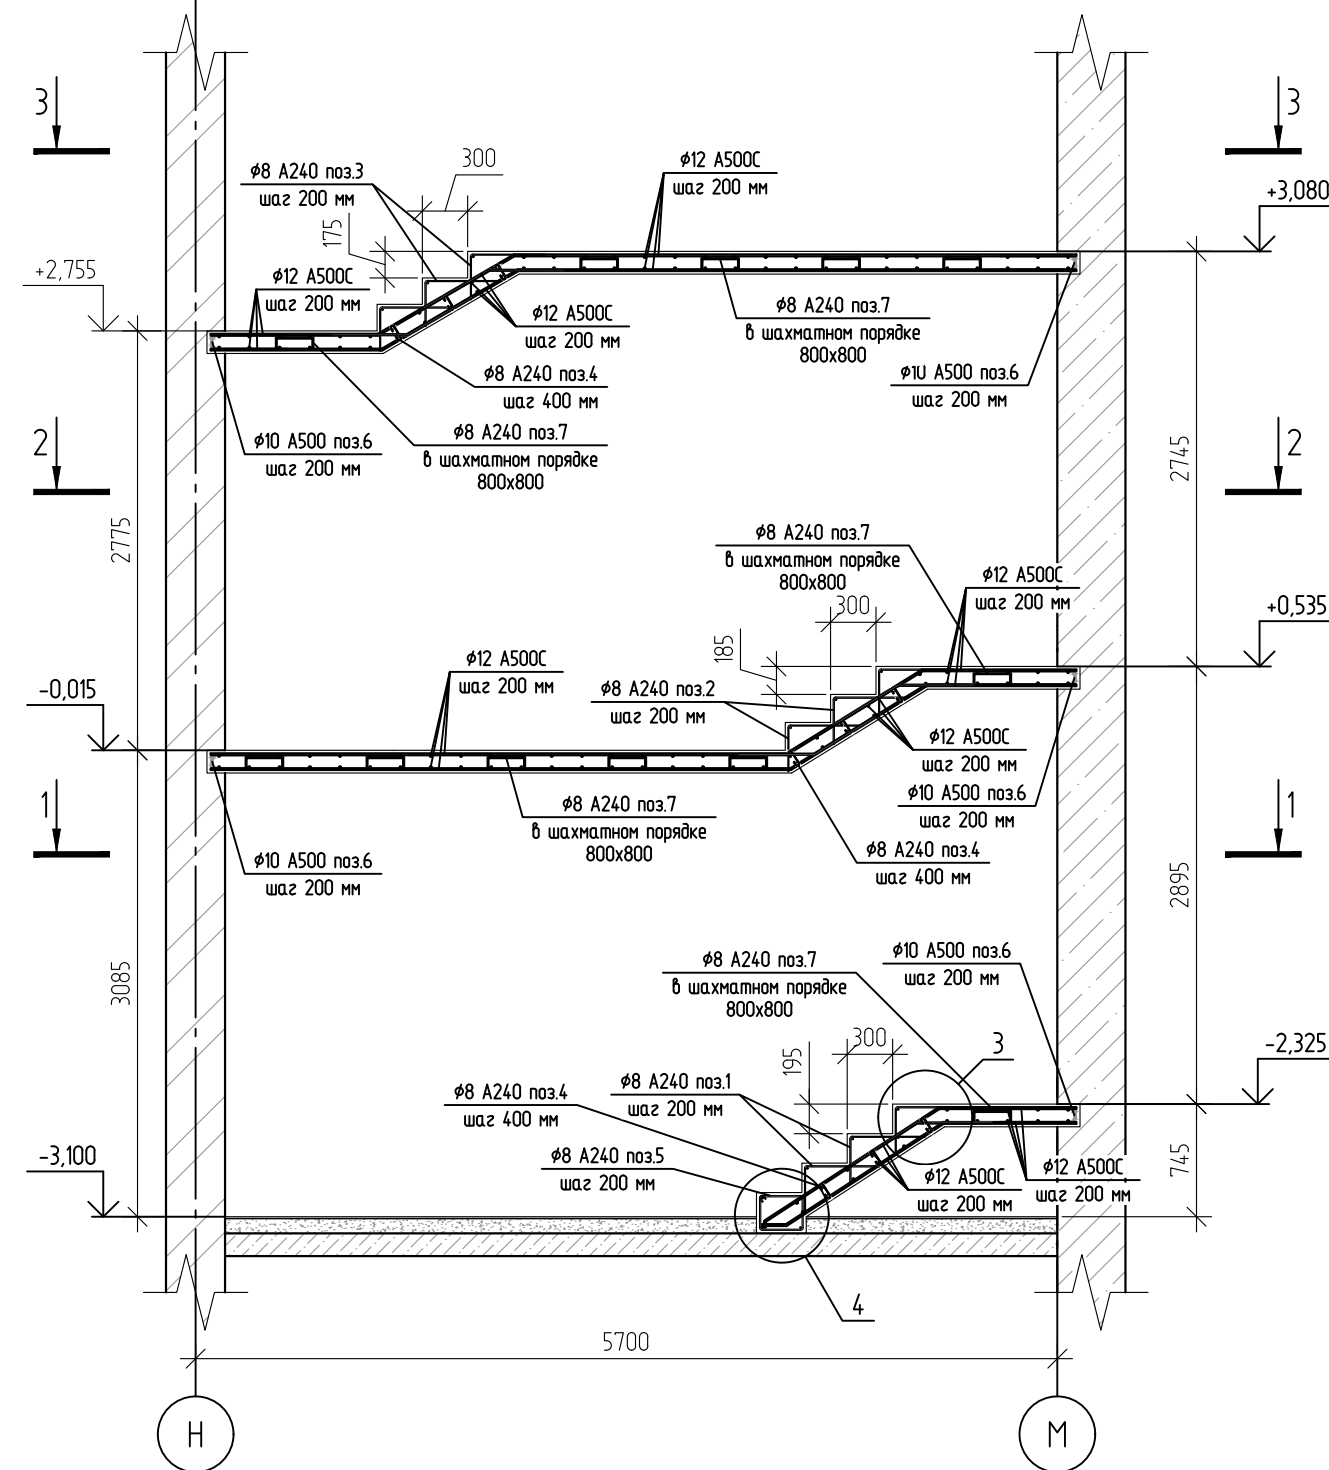

Разрез 3-3

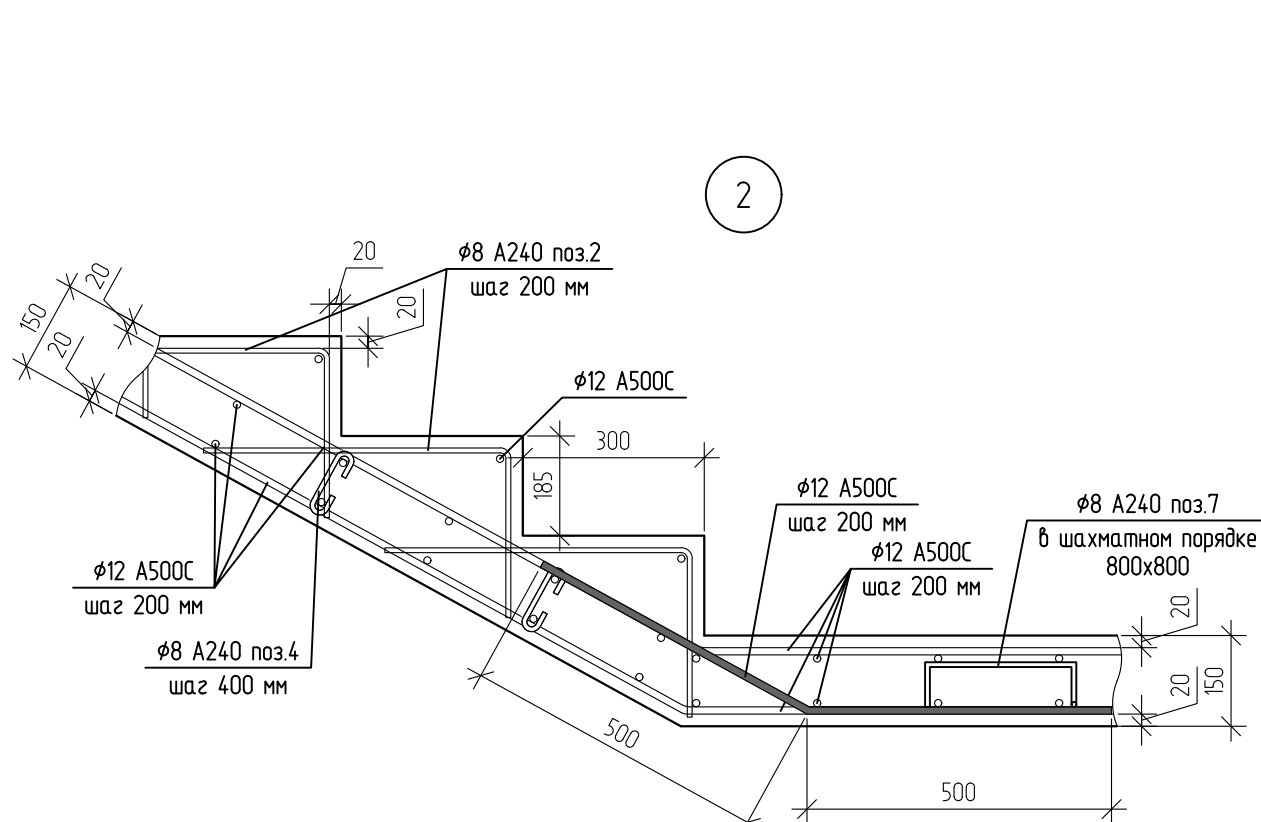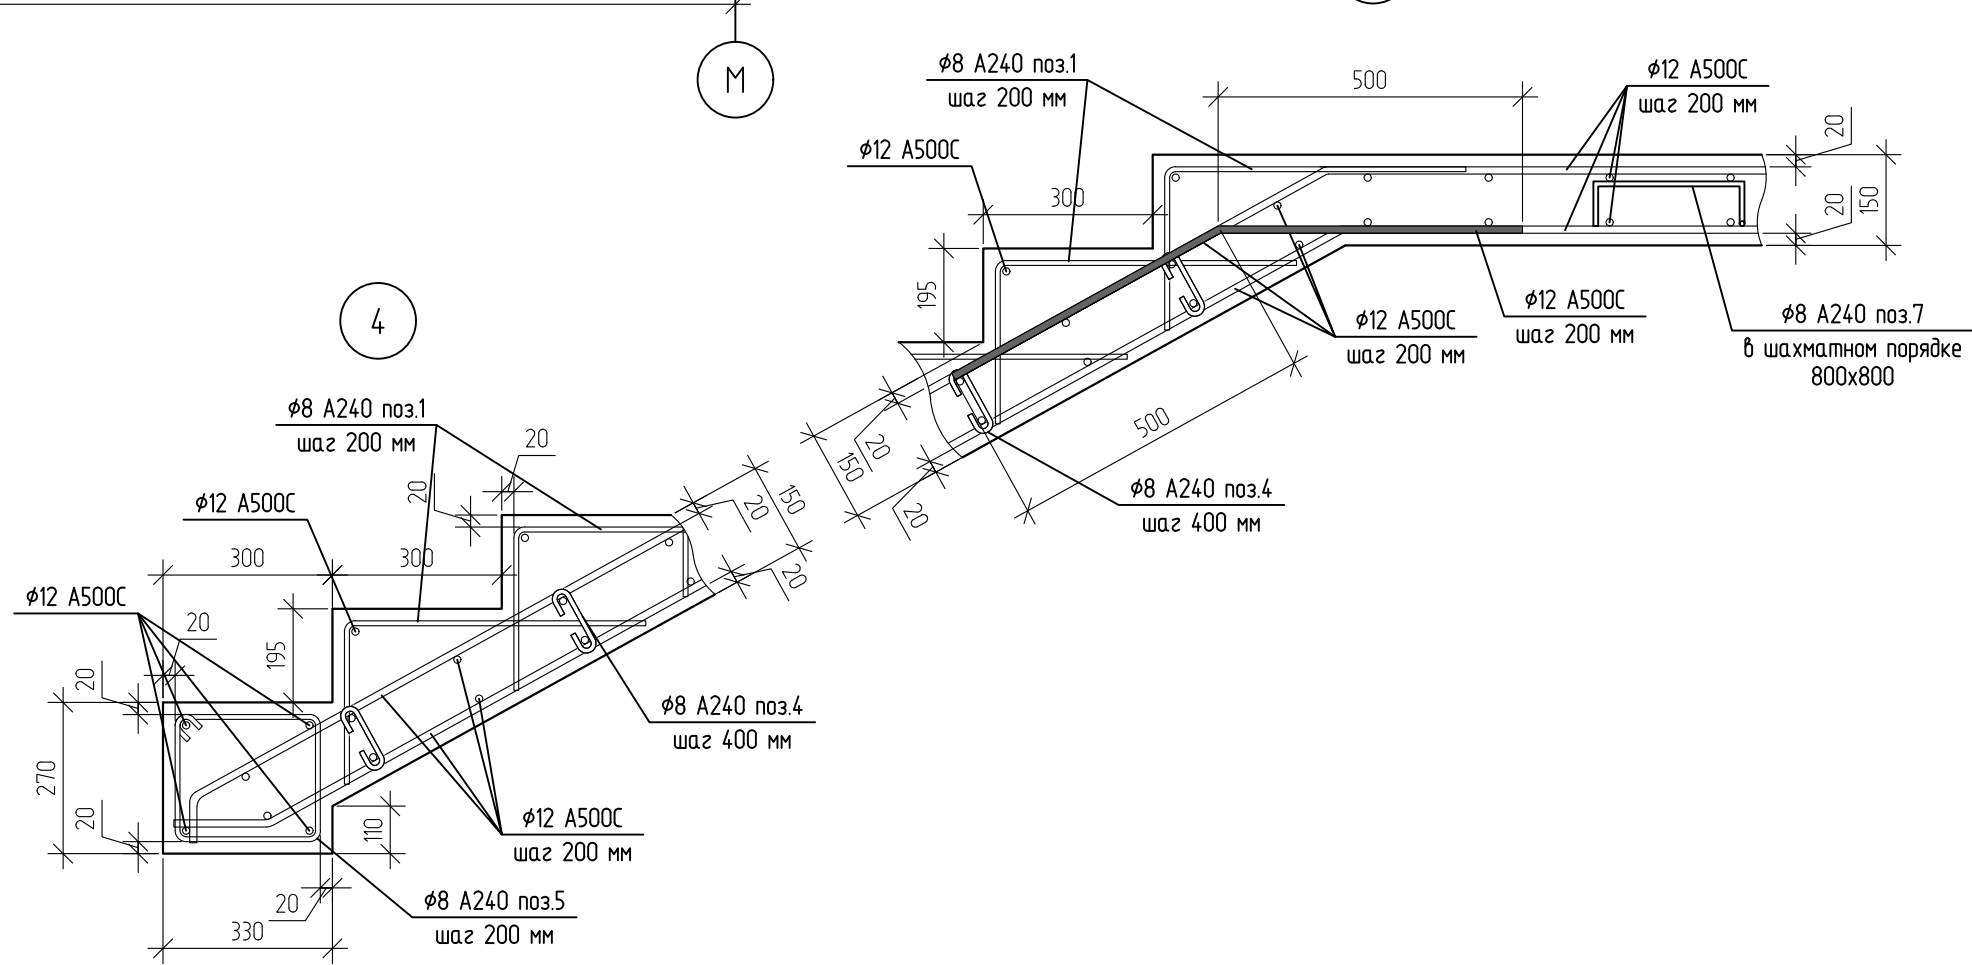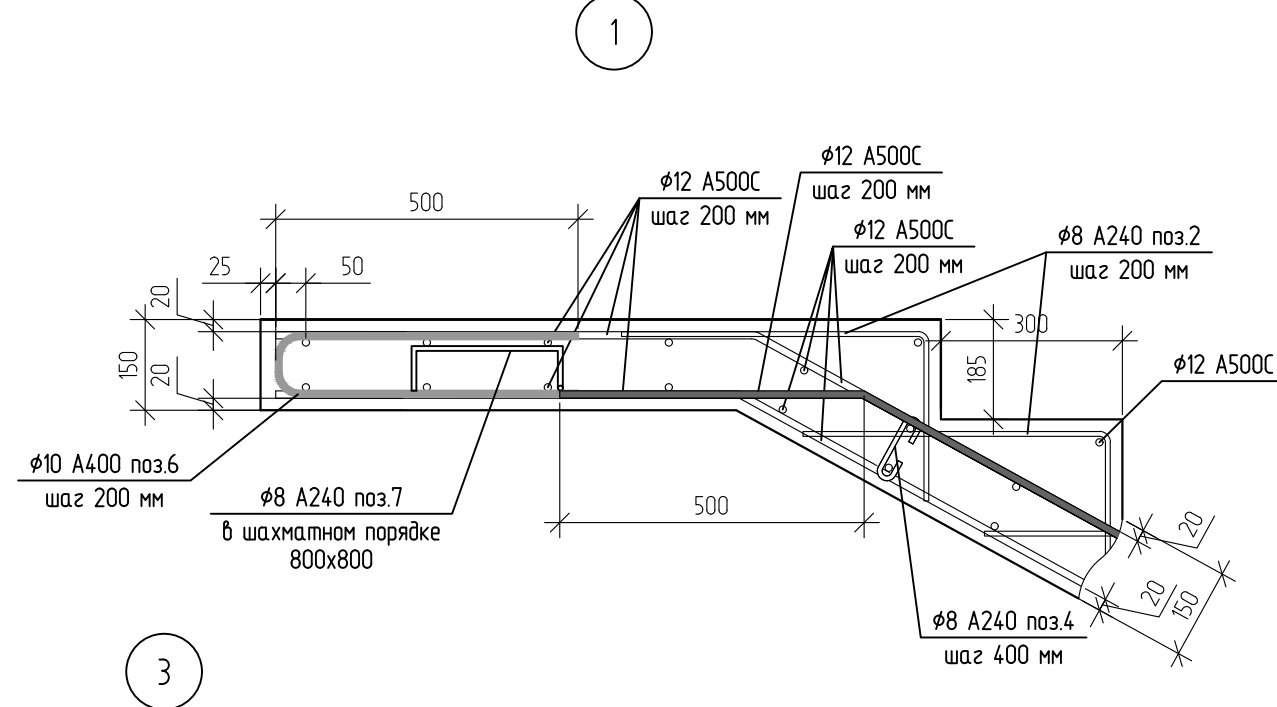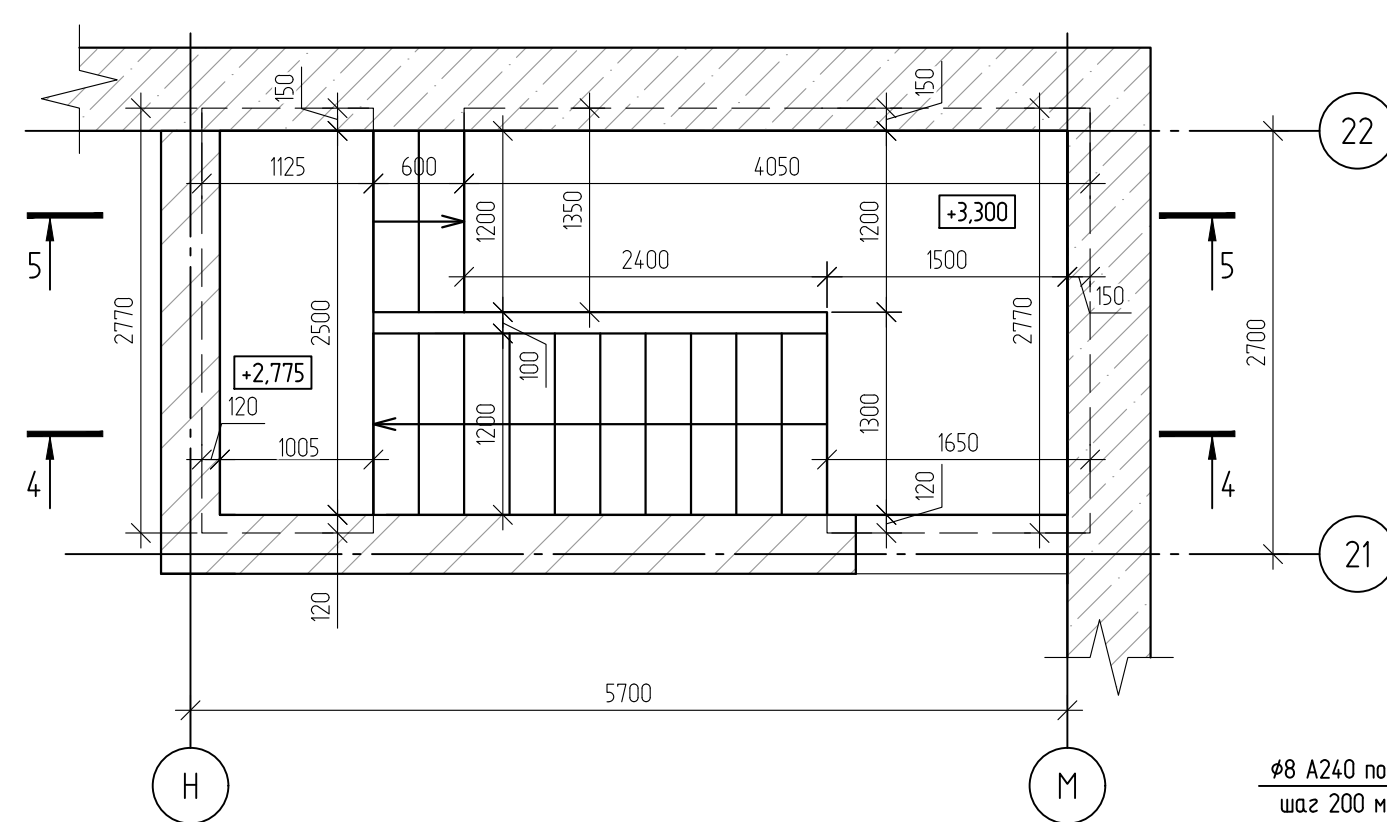

Узел крепления стойки ограждения

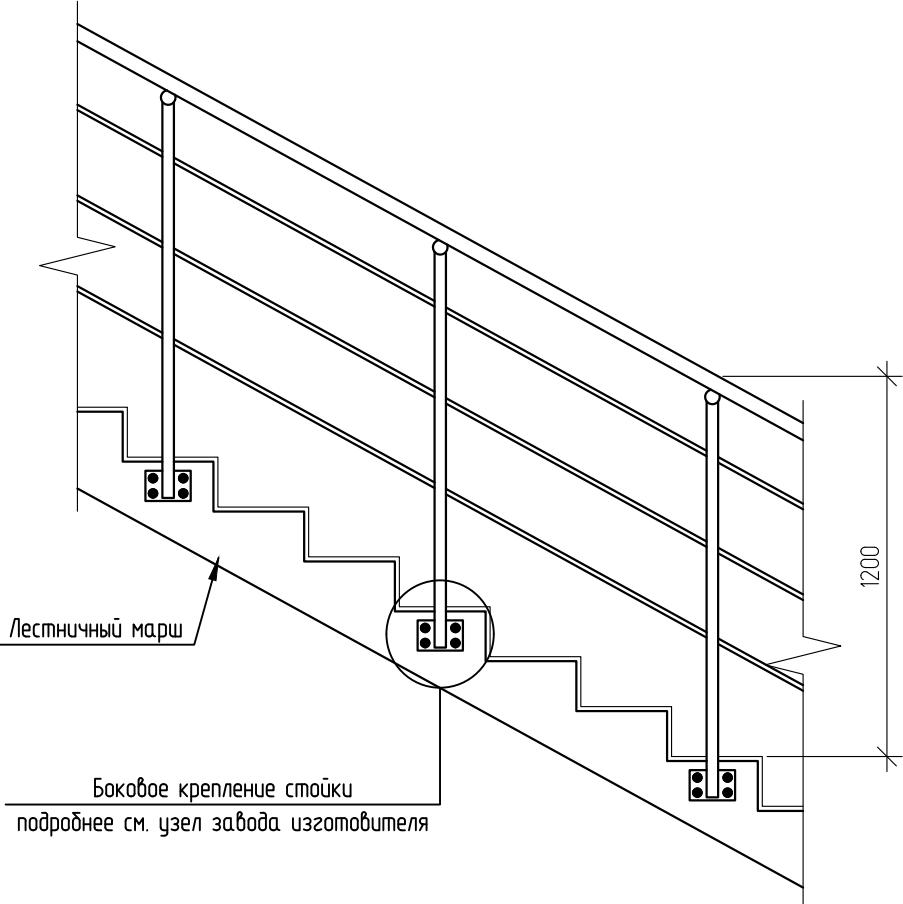

Спецификация на устройство лестниц в осях "21-22/М-Н"					
Поз.	Обозначение	Наименование	Кол.	Масса 1 дет. кг	Примеч. общ. вес кг
	ГОСТ 34028-2016	Ø12 А500С, п.м	8837	0.888	784.73
1	ГОСТ 34028-2016	Ø8 А240, L=810 мм, шт	90	0.33	29.7
2	ГОСТ 34028-2016	Ø8 А240, L=800 мм, шт	90	0.32	28.8
3	ГОСТ 34028-2016	Ø8 А240, L=790 мм, шт	18	0.32	5.76
4	ГОСТ 34028-2016	Ø8 А240, L=160 мм, шт	98	0.07	6.86
5	ГОСТ 34028-2016	Ø8 А240, L=1100 мм, шт	6	0.44	2.64
6	ГОСТ 34028-2016	Ø10 А500, L=1110 мм, шт	152	0.69	104.88
7	ГОСТ 34028-2016	Ø8 А240, L=974 мм, шт	38	0.39	14.82
Материалы					
	Бетон В25, W6, F50, м³		8.1		

Ведомость деталей	
Поз.	Эскиз
1	
2	
3	
4	
5	
6	
7	


Ведомость расхода стали, кг

Марка элемента	Изделия арматурные			
	Арматура класса		Всего	
	A500C	A240		
	ГОСТ 34028-2016	ГОСТ 34028-2016		
Ø12	1998.11	998.11	96.89	1095

- Площадки и марши армировать отдельными стержнями Ø12 А500С с шагом 200х200 мм. Вся рабочая арматура соединяется в сетки с помощью вязальной проволоки. В сетках вязке подлежат пересечения стержней через одно в шахматном порядке.
- Соединение стержней по длине производить внахлест с перекрестком не менее 45 диаметров стыкуемой арматуры. В одном условном сечении не более 50% стыкуемой арматуры.
- Размеры хомутов и гнутых деталей даны для справки. Данные размеры следует уточнять и корректировать по месту для соответствия нижней и верхней сеток проектному.
- Стыки смежных стержней разносить в шахматном порядке.
- Фиксаторы положения сеток (лягушки) на чертеже не показаны и в спецификации не учтены.

708/П-24-АНД-КР					
Капитальный ремонт общеобразовательного учреждения ГБОУ "Школа №120" по адресу г. Москва, ул. Живойкина, д.32					
Изм.	Копуч.	Лист	№ док.	Подп.	Дата
Разработал	Горшин	41			04.26
ГАП	Фролова	42			04.26
Конструктивные решения				Стация	Лист
				Р	45
Схемы устройства монолитных лестниц в осях "21-22/М-Н"				ООО "АРТИС"	
Н.Контроль	Лукашова	43			04.26
ГИП	Зыкин	44			04.26

Схема размещения подпорной стены и плиты пола подвала

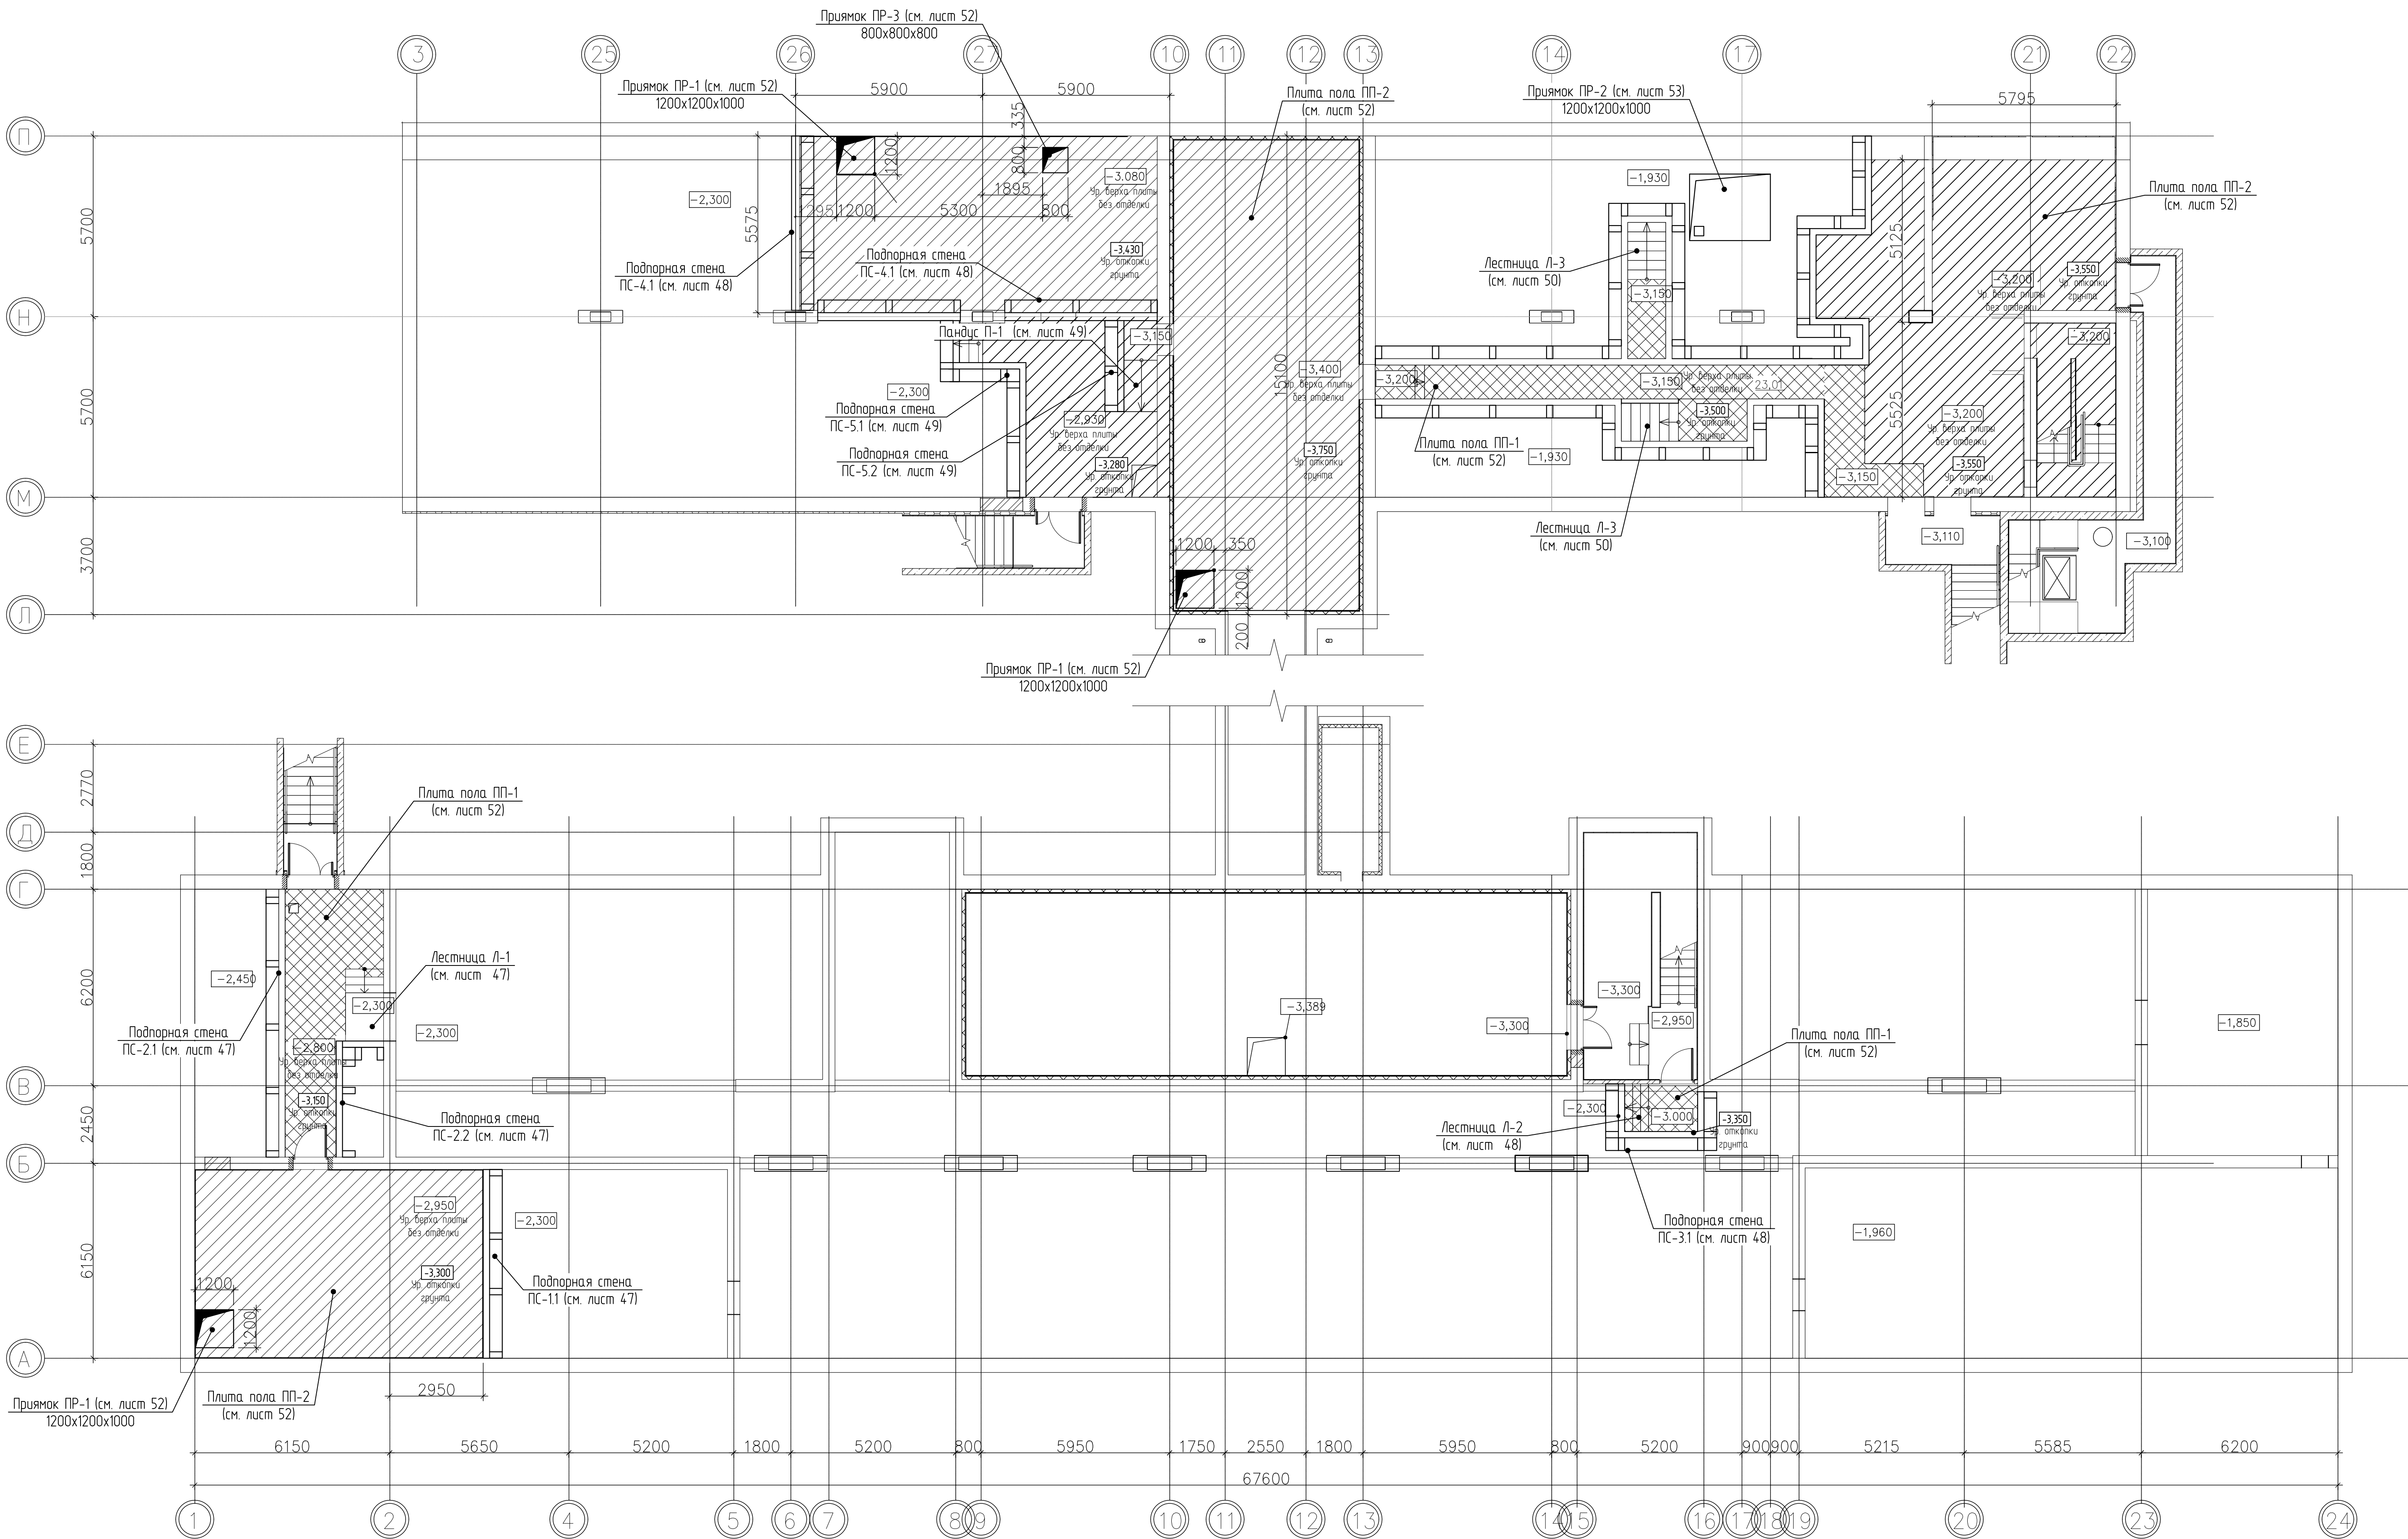

1. Объем извлеченного грунта для плит и подпорных стен составляет 425 м. куб.

2. Класс бетона по прочности на сжатие для всех монолитных конструкций - В25. Марка бетона по водонепроницаемости - не ниже W6. Марка бетона по морозостойкости - не ниже F100.

3. Арматура - А-240, А-500 по ГОСТ 34028-2016.

4. Под подпорную стену, а так же плиту пола, выполнить бетонную подготовку из бетона В7.5 толщиной 100 мм по основанию из смеси ПГС толщиной 100 мм, выступающая за габариты стены на 100 мм. Для подпорной стены по бетонной подготовке предусмотреть гидроизоляцию - стеклоизол 2 слоя.

5. Арматурные стержни вязать в каждом пересечении, сварные соединения не допускаются. Вязальная проволока в ведомости расходов не учтена.
6. Перехлест стержней основного армирования должен быть не менее 40d; для стержней $\Phi 12A-400$ - 480 мм, для стержней $\Phi 10A-400$ - 400 мм. Выполнение перехлестов стержней производить браздежку. В спецификации запас на перехлест учтен в размере 6%.

7. Изготовление гнутых стержней производить в холодном состоянии на оправках диаметром 5d для стержней диаметром менее 20 мм. Величина отгиба стержней основной арматуры в угловых и Т-образных примыканиях - не менее 50d, величина отгиба для анкеровки - не менее 5d.

8. Все поверхности подпорной стены, контактирующие с землей, покрыть 2 слоями горячего битума.

9. *Размеры для справок.

						708/П-24-АНД-КР			
						Капитальный ремонт общеобразовательного учреждения ГБОУ "Школа №1210" по адресу: г. Москва, ул. Животочная, д.32			
Изм.	Копуч.	Лист	№ док.	Подп.	Дата	Конструктивные решения	Стадия	Лист	Листов
Разработал	Горшин	4	04.26		04.26		Р	46	
ГАП	Фролова	4	04.26			Схема размещения подпорной стены и плиты пола подвала	 ООО "АРТИС"		
Н.Контроль	Лукашова	4	04.26		04.26				
ГИП	Зыкин	4	04.26						

Technical drawing of a rectangular structure, likely a foundation or wall section, showing dimensions and labels.

Dimensions:

- Overall width: 200 (left side) + 400 (right side) = 600.
- Overall height: 1800 (left side) + 1800 (right side) + 200 (top) + 200 (bottom) = 5995.
- Internal width (left): 1595.
- Internal width (right): 1595.
- Internal height (left): 1800.
- Internal height (right): 1800.
- Top offset: 200.
- Bottom offset: 200.

Labels and Symbols:

- Top left: σ (stress symbol).
- Top right: δ (delta symbol).
- Bottom left: σ (stress symbol).
- Bottom right: σ (stress symbol).
- Left side: $-2,950$ (elevation).
- Right side: $-2,300$ (elevation).
- Bottom left corner: A (label).
- Bottom right corner: 4 (label).

Подпорная стена ПС-2.1

-2.450

-2.800 (ПС-1.1)

350

850

550

300

100

600

100

800

500

[illegible]


Technical drawing of a stepped profile. The profile consists of a vertical segment of height 220, a horizontal segment of width 100, a diagonal segment of length 95, and a final horizontal segment of width 135. The total height of the profile is 30.

Technical drawing of a stepped profile. The profile consists of a horizontal base of length 100, a vertical step up of height 220, a diagonal segment of length 690, and a final horizontal segment of length 135. The total height of the profile is 30.

Technical drawing of a stepped profile. The profile consists of a vertical segment of height 220, a horizontal segment of width 100, a diagonal segment of length 820, and a horizontal segment of width 135. The total height of the profile is 30.

						708/П-24-АНО-КР			
						Капитальный ремонт общеобразовательного учреждения ГБОУ "Школа №1210" по адресу: г. Москва, ул. Жилищная, д.32			
Изм.	Колуч.	Лист	№ док.	Подп.	Дата	Конструктивные решения	Стация	Лист	Листов
Разработал	Торшин				04.26		Р	47	
ГАП	Фролова				04.26				
						Подпорная стена ПС-11, 2.1, 2.2		комплексное проектирование промышленных и гражданских объектов	
Н.Контроль	Лукашова				04.26			ООО "АРТИС"	
ГИП	Зыкин				04.26				

Подпорная стена ПС-3.1

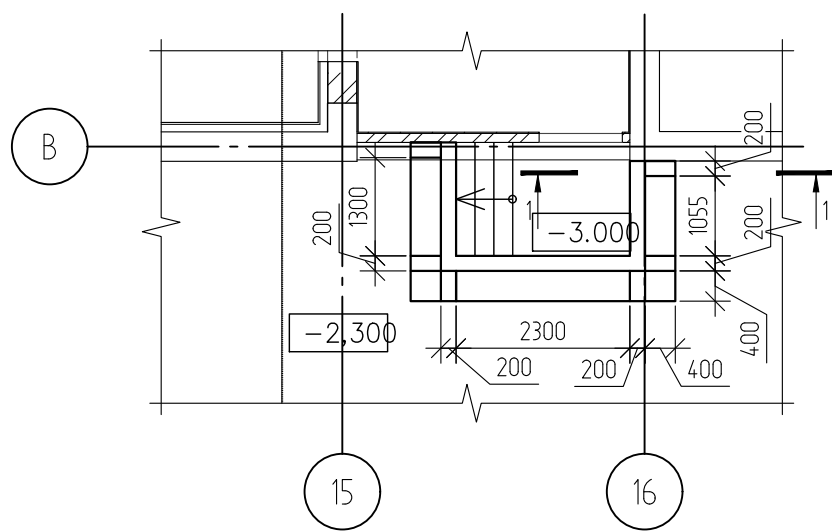

Фрагмент подпорная стена ПС-3.1



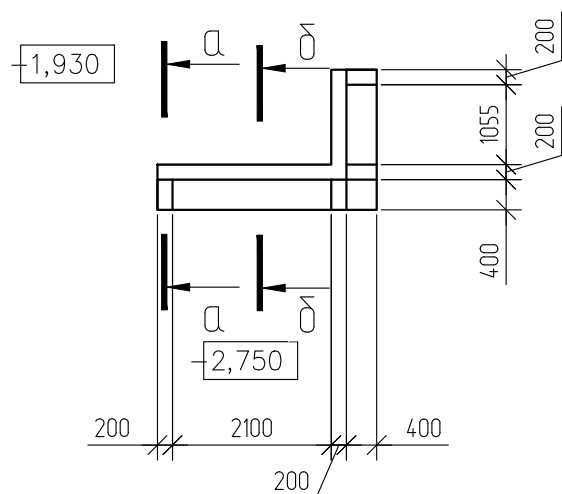



Схема расположения лестницы Л-4

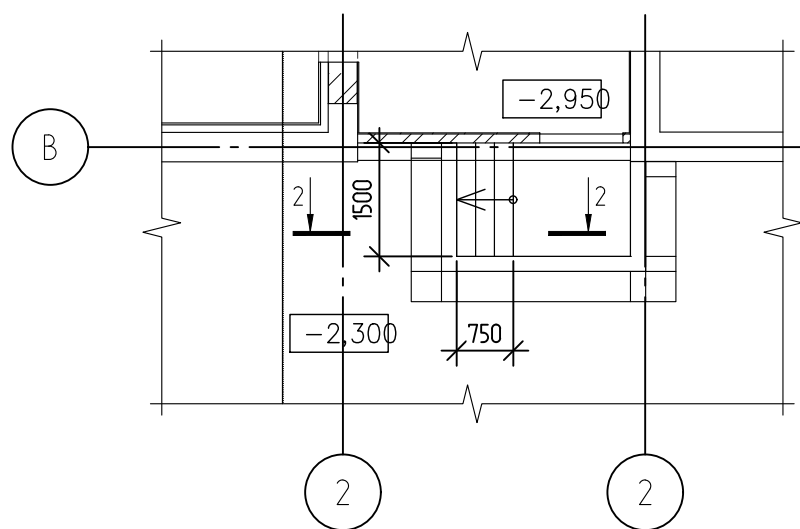


Подпорная стена ПС-4.1

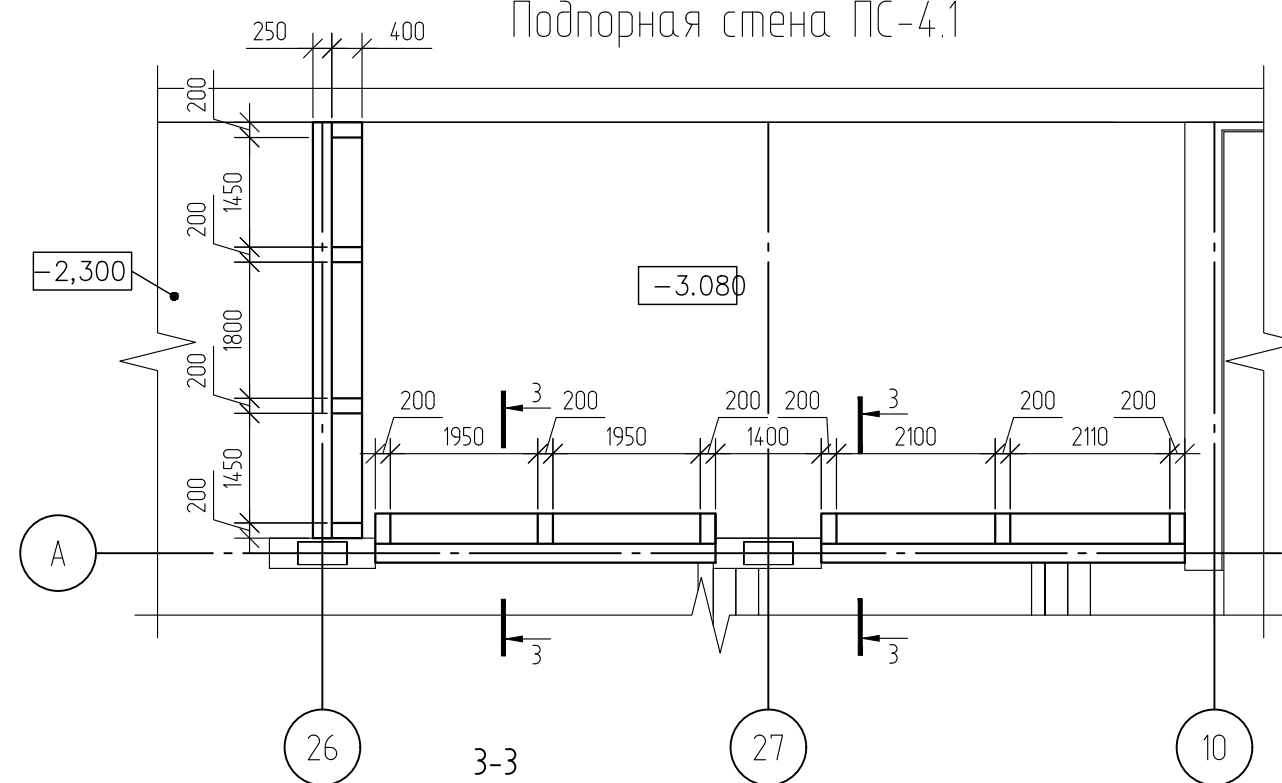


Фрагмент подпорная стена ПС-4.1

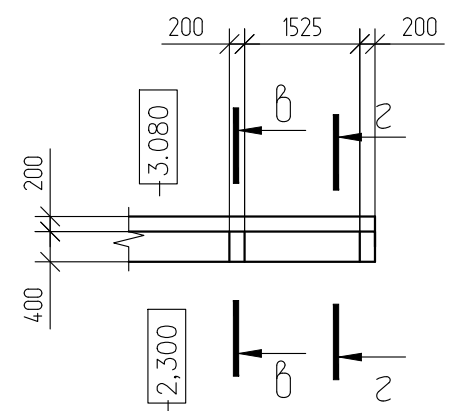


1-1

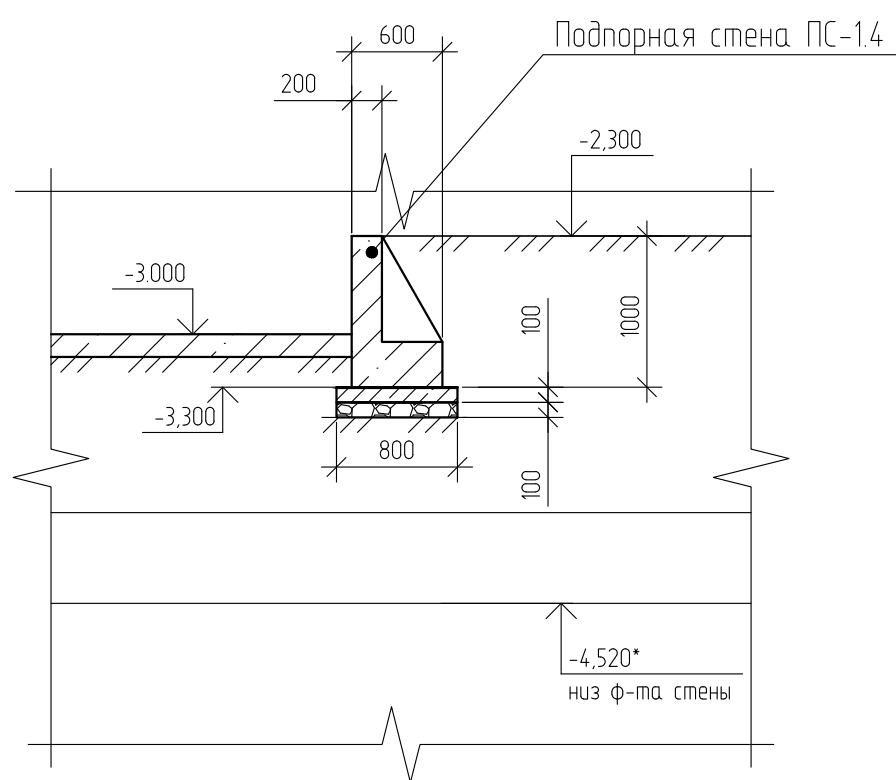


2-2 (Лестница Л-2)

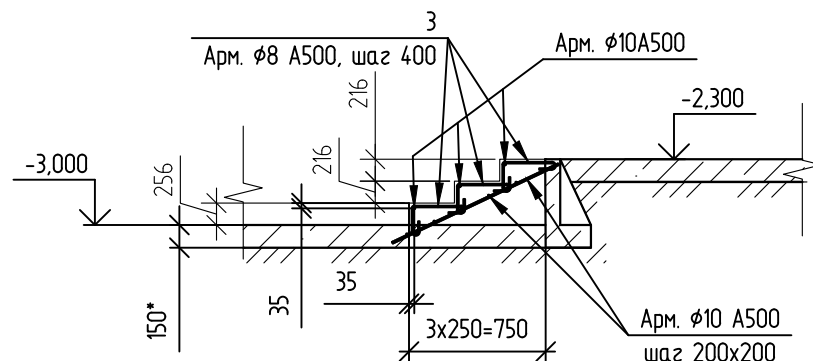


1-1

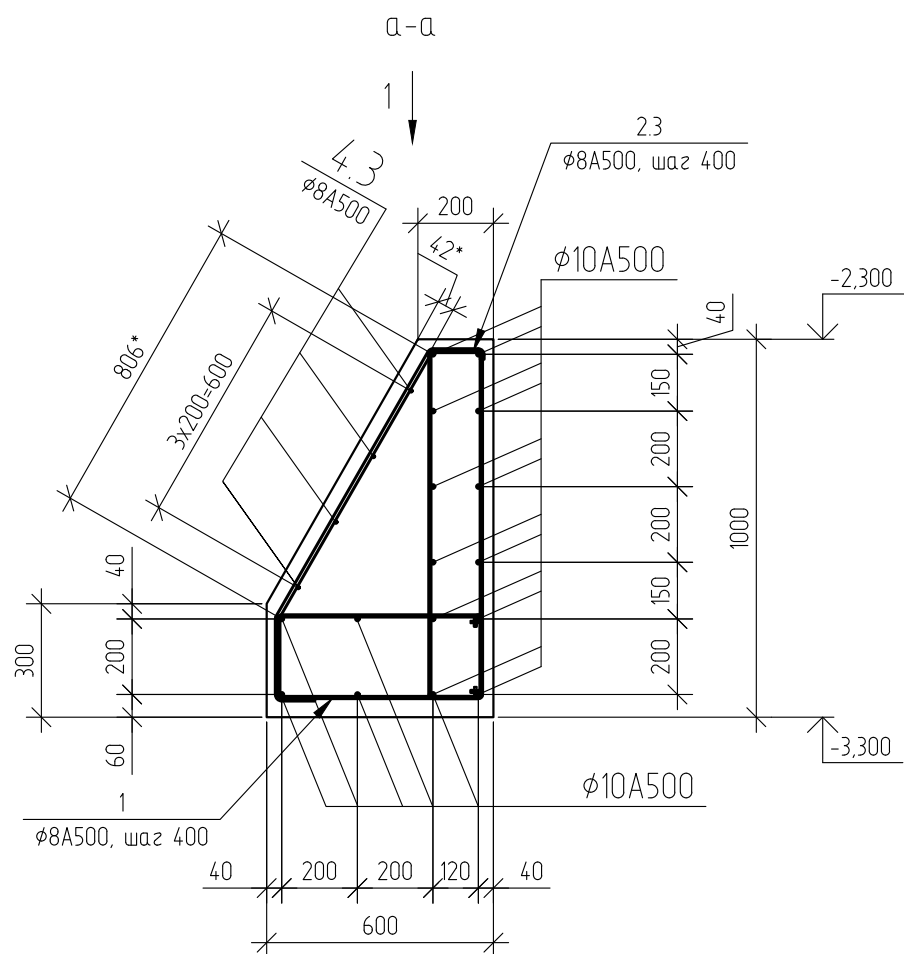


1-1

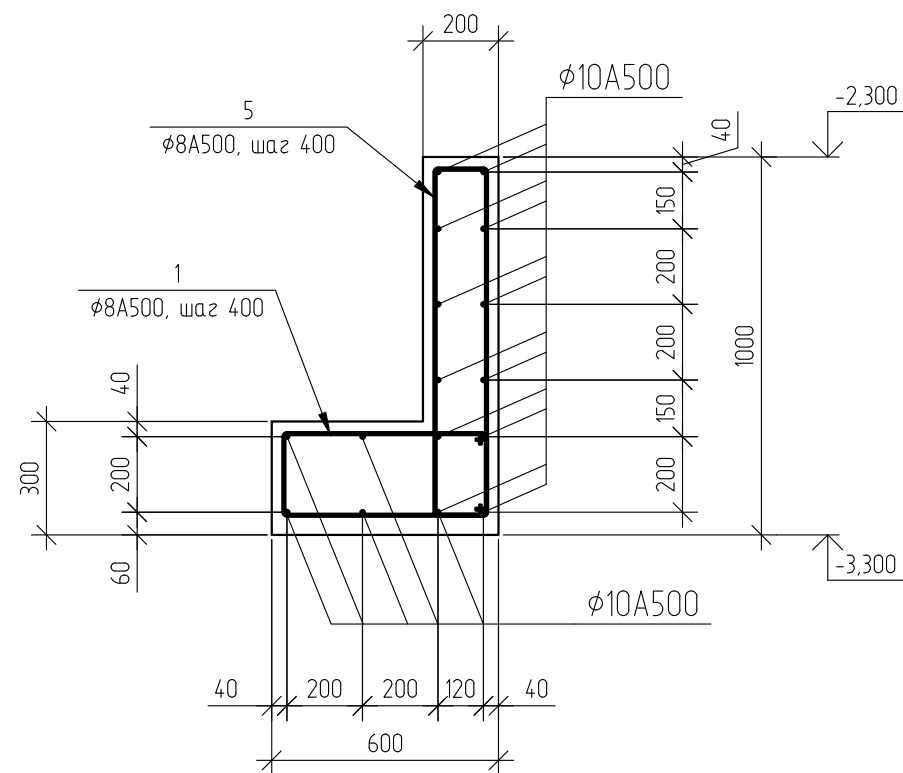

1-1

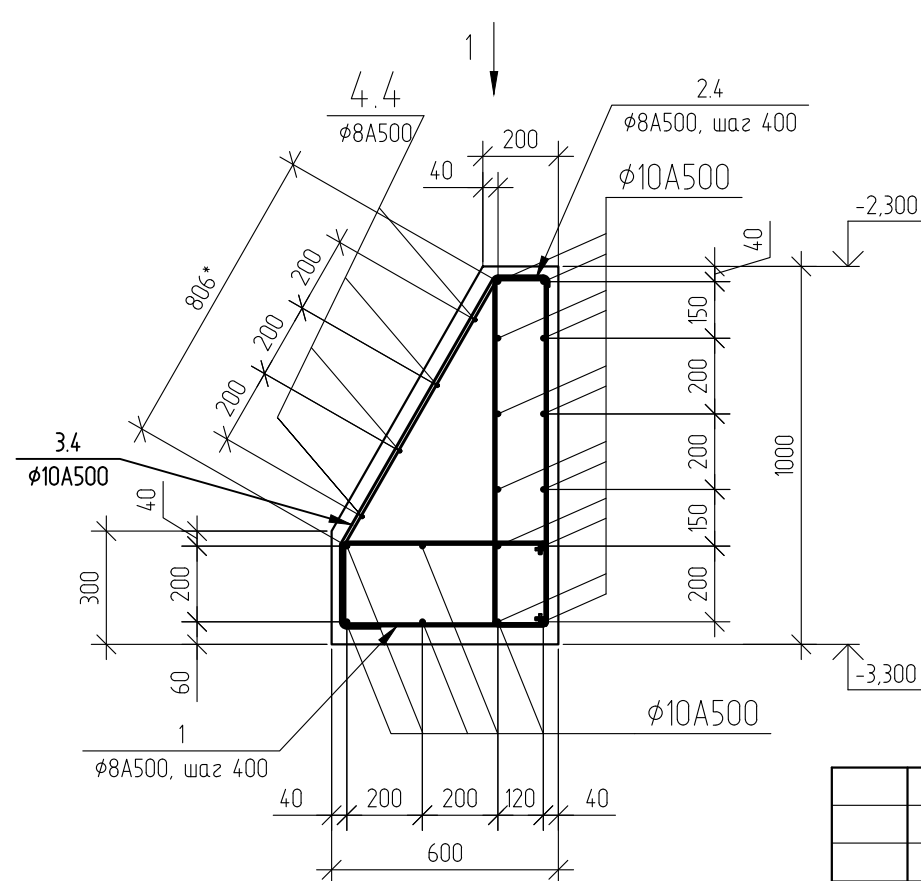



1-1

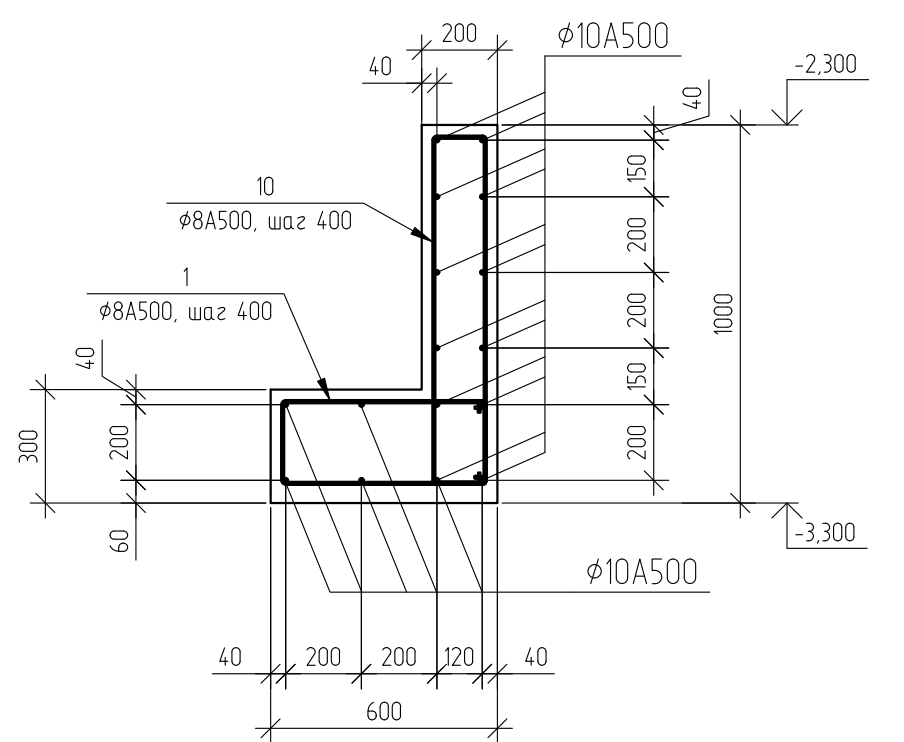

Смотреть совместно с листом 46, 51 ГЧ

					708/П-24-АНО-КР		
					Капитальный ремонт общеобразовательного учреждения ГБОУ "Школа №1210" по адресу: г. Москва, ул. Живописная, д.32		
Изм.	Колуч.	Лист	№ док.	Подп.	Дата	Конструктивные решения	Стадия
Разработал	Торшин	04.26			04.26		Лист
ГАП	Фролова					Р	48
					Подпорная стена ПС-3.1, 4.1		
Н.Контроль	Лукашова	04.26				ООО "АРТИС"	
ГИП	Зыкин	04.26					

Инв. № подл.	Подп. и дата	Взам. инв. №	Согласовано		

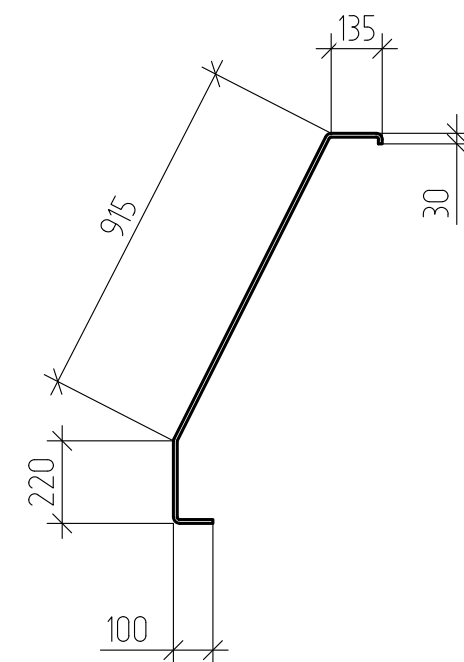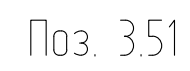


Bud A




						708/П-24-АНО-КР			
						Капитальный ремонт общеобразовательного учреждения ГБОУ "Школа №1210" по адресу: г. Москва, ул. Жилищная, д.32			
Изм.	Колуч.	Лист	№ док.	Подп.	Дата	Конструктивные решения	Стадия	Лист	Листов
Разработал	Торшин				04.26		Р	49	
ГАП	Фролова				04.26				
						Подпорная стена. ПС-5.1, 5.2	 комплексное проектирование промышленных и гражданских объектов ООО "АРТИС"		
Н.Контроль	Лукашова				04.26				
ГИП	Зыкин				04.26				


Подпорная стена ПС-6.1

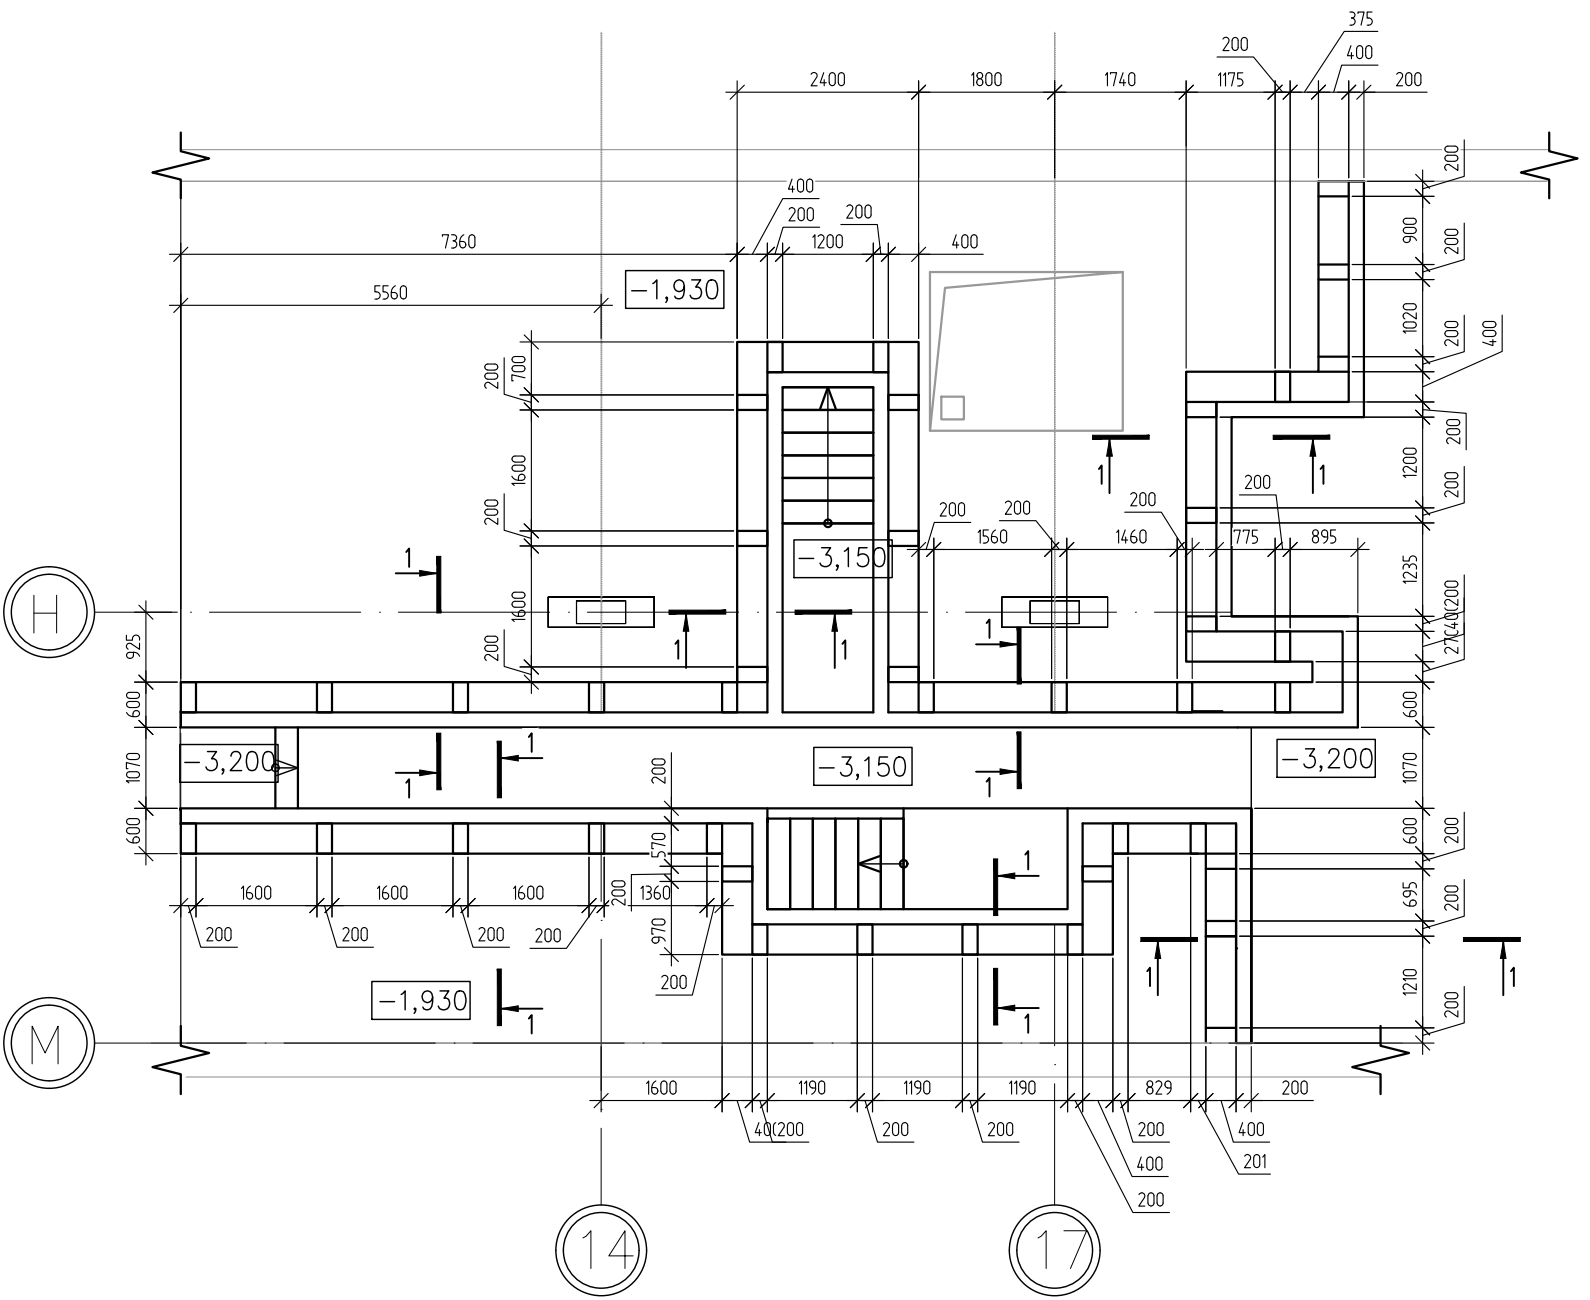


1-1 (Опалубочный)

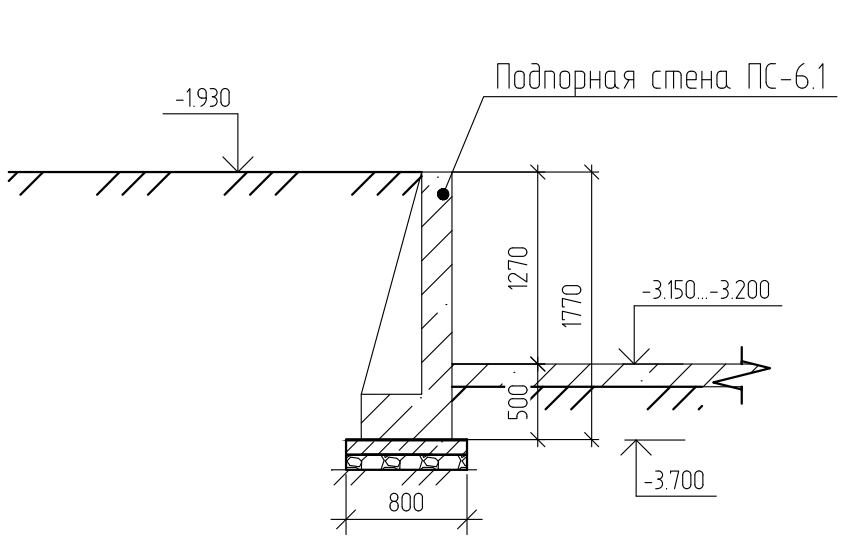


Лестница Л-3

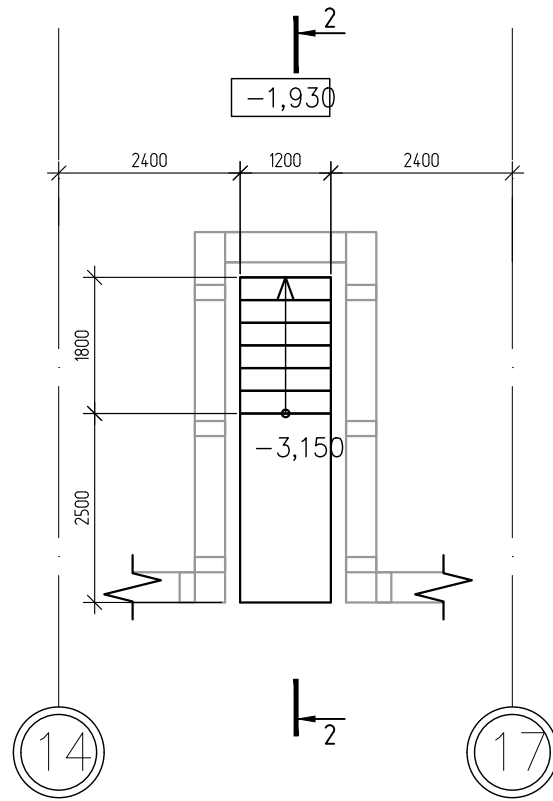




2-2 (Армирование лестницы Л-3)

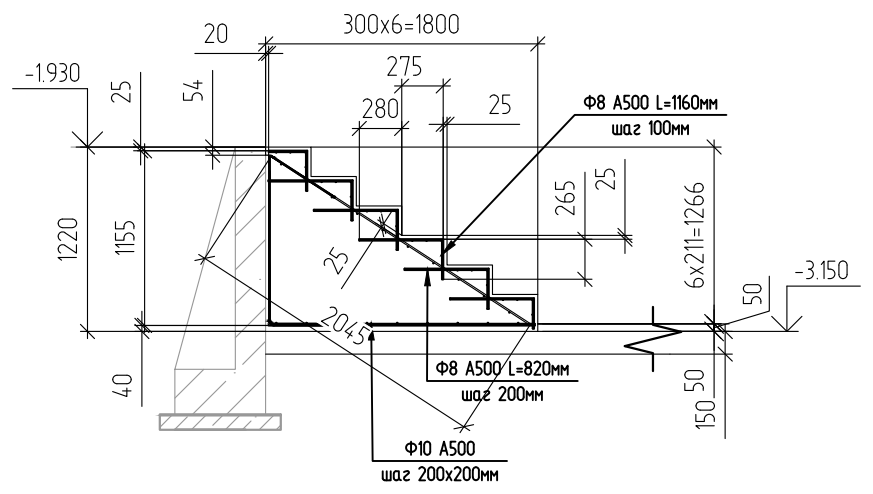

Поз. 5.3

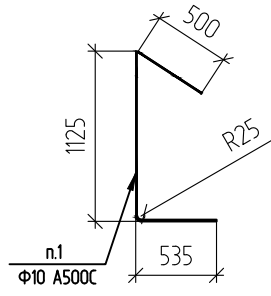

Поз. 3.6

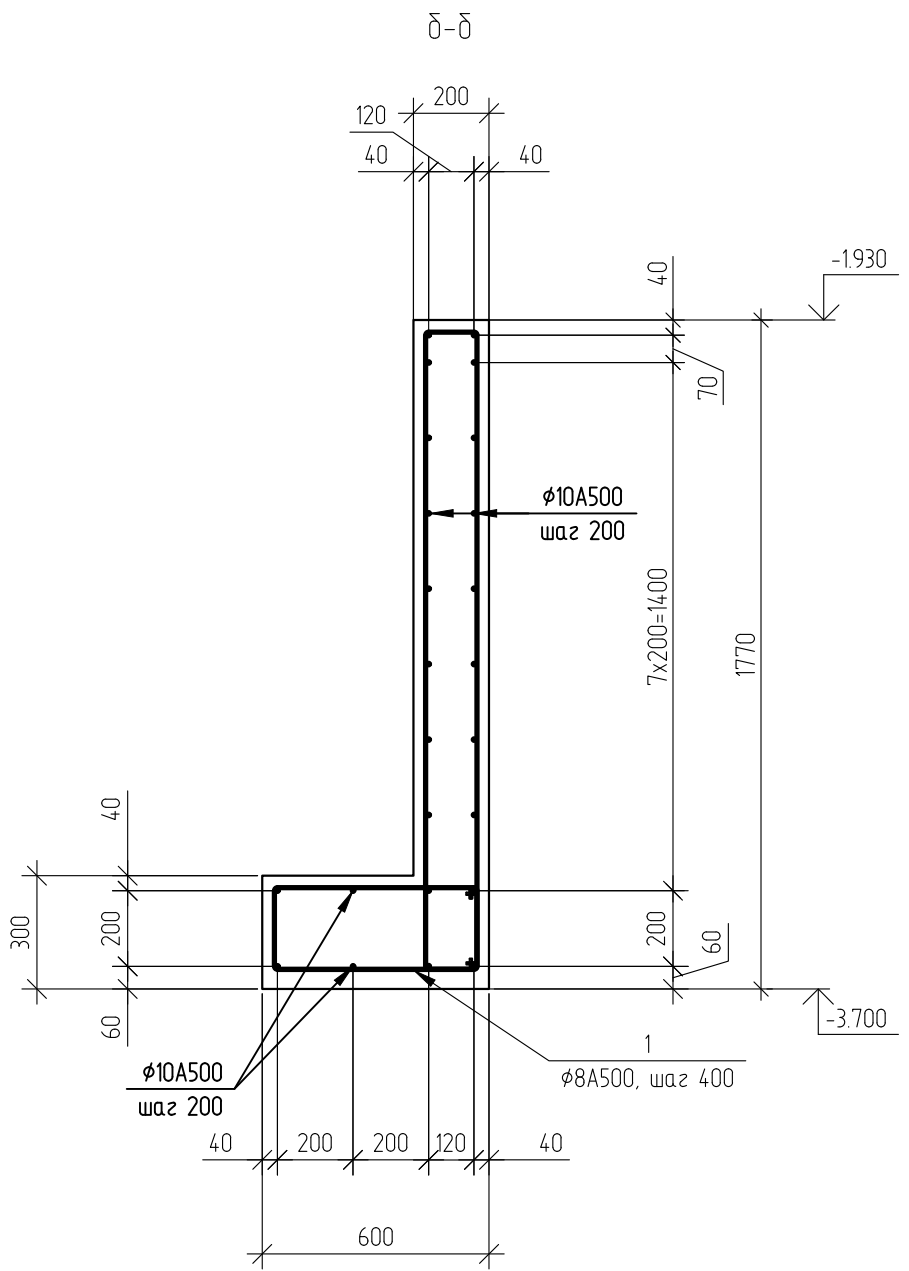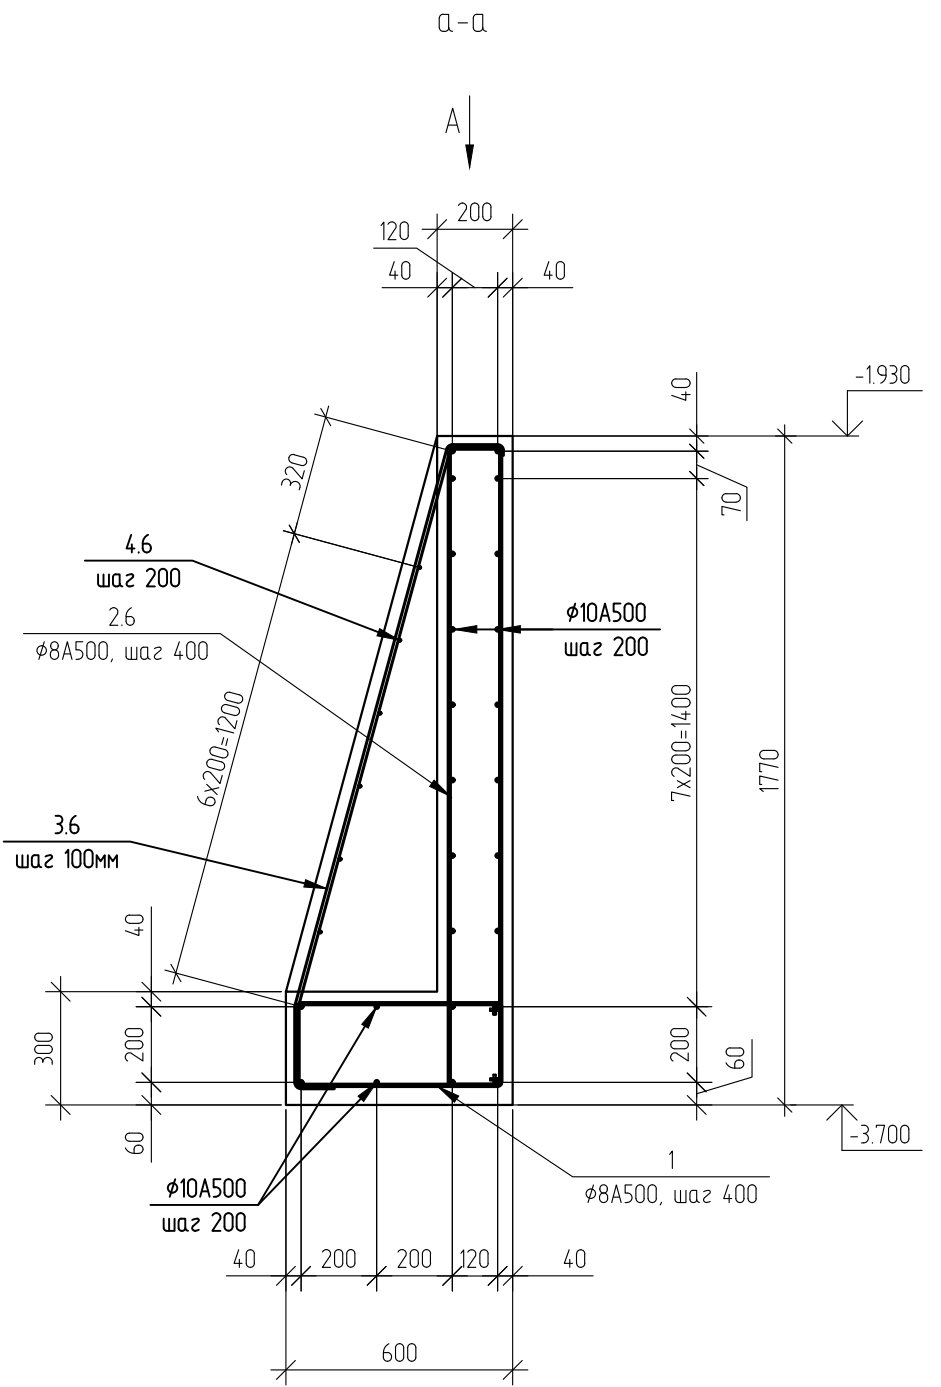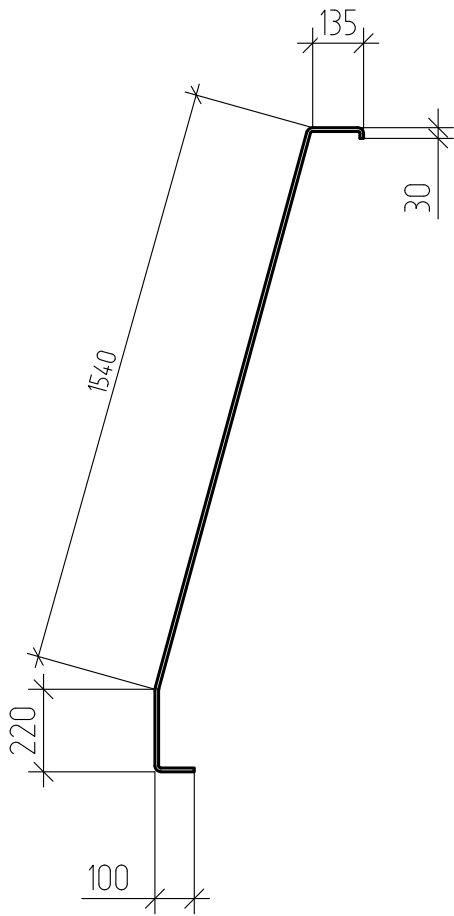

Смотреть совместно с листом 46, 51 ГЧ

						708/П-24-АНО-КР			
						Капитальный ремонт общеобразовательного учреждения ГБОУ "Школа №1210" по адресу: г. Москва, ул. Живописная, д.32			
Изм.	Колуч	Лист	№ док	Подп	Дата	Конструктивные решения	Стадия	Лист	Листов
Разработал	Торшин				04.26		Р	50	
ГАП	Фролова				04.26				
						Подпорная стена ПС-6.1	 комплексное проектирование промышленных и гражданских объектов ООО "АРТИС"		
Н Контроль	Лукашова				04.26				
ГИП	Зыкин				04.26				

Схема армирования плиты пола подвала ПП-1

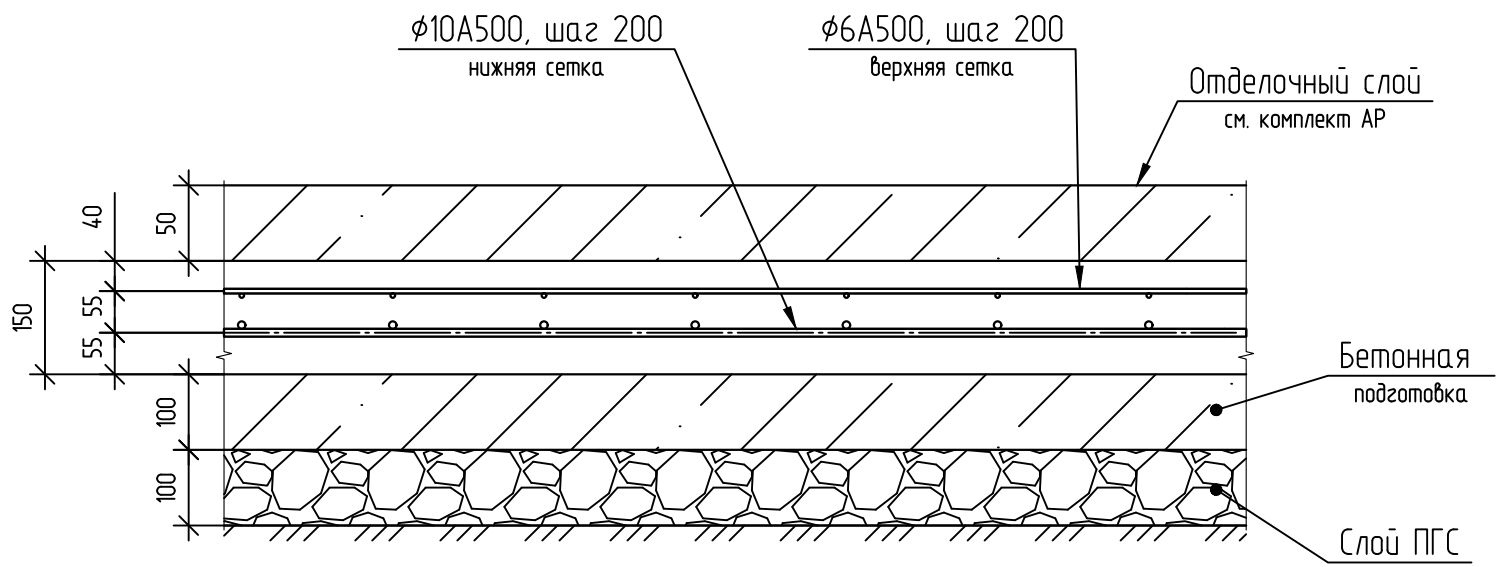


Схема армирования плиты пола подвала ПП-2


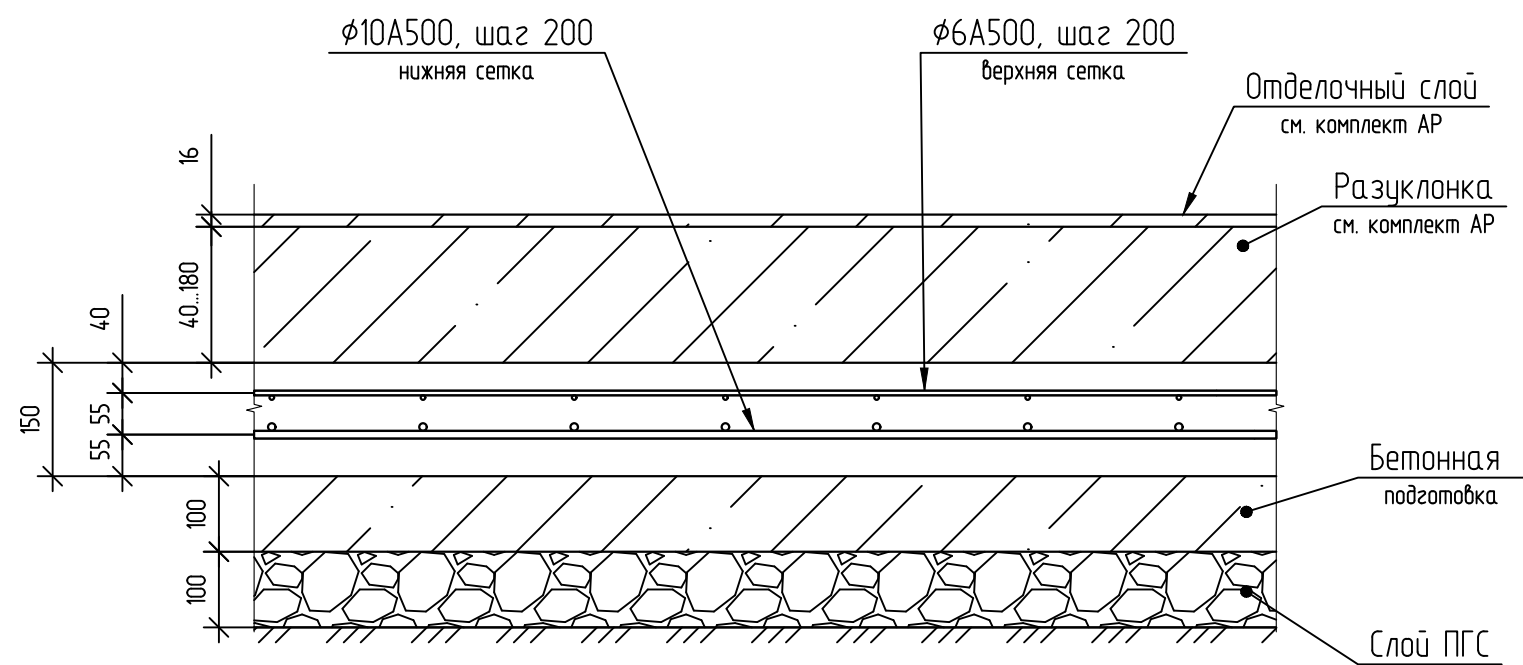


Схема прямока ПР-1 (1200x1200x1000)
ПР-3 (800x800x800)

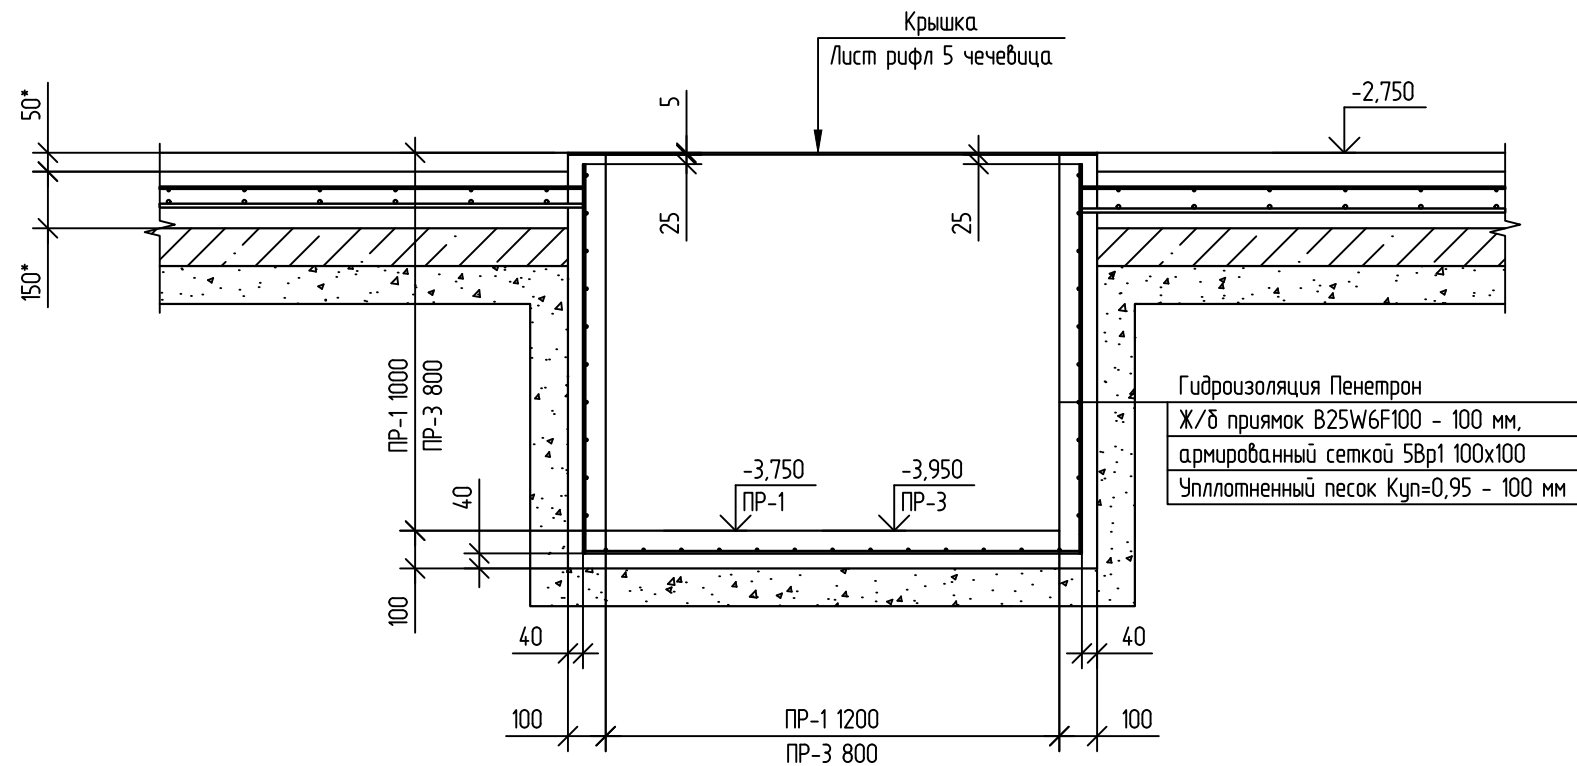

Спецификация материалов на устройство подпорной стены и плиты пола подвала

Поз.	Обозначение	Наименование	Кол.	Масса ед, кг	Примечание общ. вес кг
		Плита пола ПП-1 (S _{сум} =80,12 м.кв.)			
	ГОСТ 34028-2016	Арматура ϕ 10 A500C, м.п.	8012	0,617	494,3
	ГОСТ 34028-2016	Арматура ϕ 6 A500C, м.п.	8012	0,222	177,9
	ГОСТ 26633-2012	Бетон В25 F100 W4, м.куб.	12,0		
	ГОСТ 26633-2012	Бетон В7,5 , м.куб.	8,0		
		Смесь ПГС, м.куб.	8,0		
		Плита пола ПП-2 (S _{сум} =290 м.кв.)			
	ГОСТ 34028-2016	Арматура ϕ 10 A500C, м.п.	2900	0,617	1789,3
	ГОСТ 34028-2016	Арматура ϕ 6 A500C, м.п.	2900	0,222	643,8
	ГОСТ 26633-2012	Бетон В25 F100 W4, м.куб.	43,5		
	ГОСТ 26633-2012	Бетон В7,5 , м.куб.	29,0		
		Смесь ПГС, м.куб.	29,0		
		Прямока ПР-1	3		на 1 шт.
	ГОСТ 23279-2012	Сетка 58p-1 100x100, м ²	6,25	2,75	17,2
	ГОСТ 8568-77	Лист рифл. 5,0 чечевица, м ²	1,5	39	58,5
	ГОСТ 26633-2012	Бетон В25 F100 W6, м.куб.	0,62		
	ГОСТ 8736-93	Песок средней крупности, м.куб.	0,7		
	ТУ 5745-001-77921756-2006	Проникающая гидроизоляция "Пенетрон", кг (S= 6,24 м ²)	6,9		Расход на 2 слоя 1,1 кг,м ²
		Прямока ПР-3	1		
	ГОСТ 23279-2012	Сетка 58p-1 100x100, м ²	3,2	2,75	8,8
	ГОСТ 8568-77	Лист рифл. 5,0 чечевица, м ²	0,64	39	25,0
	ГОСТ 26633-2012	Бетон В25 F100 W6, м.куб.	0,39		
	ГОСТ 8736-93	Песок средней крупности, м.куб.	0,3		
	ТУ 5745-001-77921756-2006	Проникающая гидроизоляция "Пенетрон", кг (S= 3,2 м ²)	3,5		Расход на 2 слоя 1,1 кг,м ²


Смотреть совместно с листом 46, 51 ГЧ

						708/П-24-АНО-КР			
						Капитальный ремонт общеобразовательного учреждения ГБОУ "Школа №1210" по адресу: г. Москва, ул. Живописная, д.32			
Изм.	Колуч.	Лист	№ док.	Подп.	Дата	Конструктивные решения	Стадия	Лист	Листов
Разработал	Торшин				04.26		Р	52	
ГАП	Фролова				04.26				
						Схема армирования плит подвала. Ведомость деталей	 компания проектирования строительных и сравнительных объектов	ООО "АРТИС"	
Н.Контроль	Лукашова				04.26				
ГИП	Зыкин				04.26				




комплексное проектирование промышленных и гражданских объектов
ООО "АРТИС"

Устройство прямка ПР-2

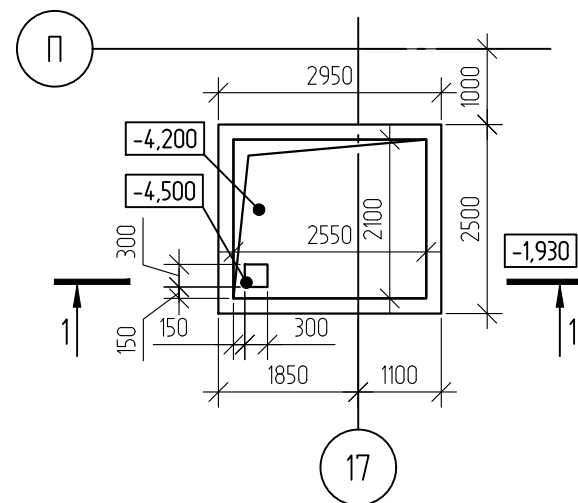

Разрез 1-1

Устройство крышки прямка

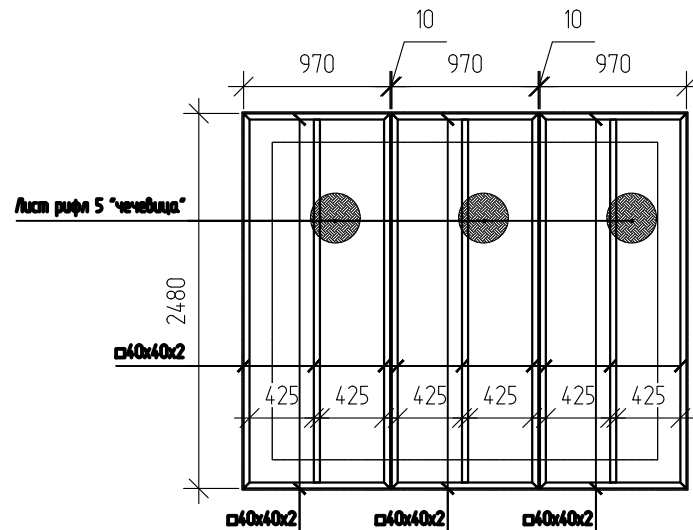

Спецификация материалов на устройство прямка

Поз.	Обозначение	Наименование	Кол.	Масса ед, кг	Примечание общ. вес кг
		Прямик ПР-1			
	ГОСТ 34028-2016	Арматура $\phi 12$ А500С, м.п.	778	0.888	690.9
1	ГОСТ 34028-2016	Арматура $\phi 12$ А500С, L=1360 мм	56	1.21	67.8
2	ГОСТ 34028-2016	Арматура $\phi 8$ А240, L=250 мм	182	0.1	18.2
		Материалы			
	ГОСТ 26633-2012	Бетон В25 F100 W6, м.куб.	6		
	ТУ 5745-001-77921756-2006	Проникающая гидроизоляция "Пенетрон", кг (S= 26.1м ²)	28.7		Расход на 2 слоя 1,1 кг/м ²

Спецификация материалов на устройство крышки прямка

Поз.	Обозначение	Наименование	Кол.	Масса ед, кг	Примечание общ. вес кг
	ГОСТ 30245-2003	$\square 40 \times 40 \times 2$, п.м.	778	0.888	690.9
	ГОСТ 8568-77	Лист рифл. 5.0 чечевица (3x2.48x0.97 м), м ²	7.22	40.5	292.4

Ведомость деталей

Поз.	Эскиз
1	
2	

Ведомость расхода стали, кг


Марка элемента	Изделия арматурные				
	Арматура класса				Всего
	А500С		А240		
	ГОСТ 34028-2016		ГОСТ 34028-2016		
	φ12	Итого	φ8	Итого	
	758.7	758.7	18.2	18.2	776.9

Примечания:

1. При устройстве прямка необходимо заложить гильзы в местах ввода коммуникаций.

						708/П-24-АНО-КР			
						Капитальный ремонт общеобразовательного учреждения ГБОУ "Школа №1210" по адресу: г. Москва, ул. Живописная, д.32			
Изм.	Кол.уч.	Лист	№ док.	Подп.	Дата	Конструктивные решения	Стадия	Лист	Листов
Разработал	Торшин				04.26		Р	53	
ГАП	Фролова				04.26				
						Прямик ПР-2. Спецификация материалов		комплексное проектирование промышленных и гражданских объектов	ООО "АРТИС"
Н.Контроль	Лукашова				04.26				
ГИП	Зыкин				04.26				

Схема демонтажа плит перекрытия подвала

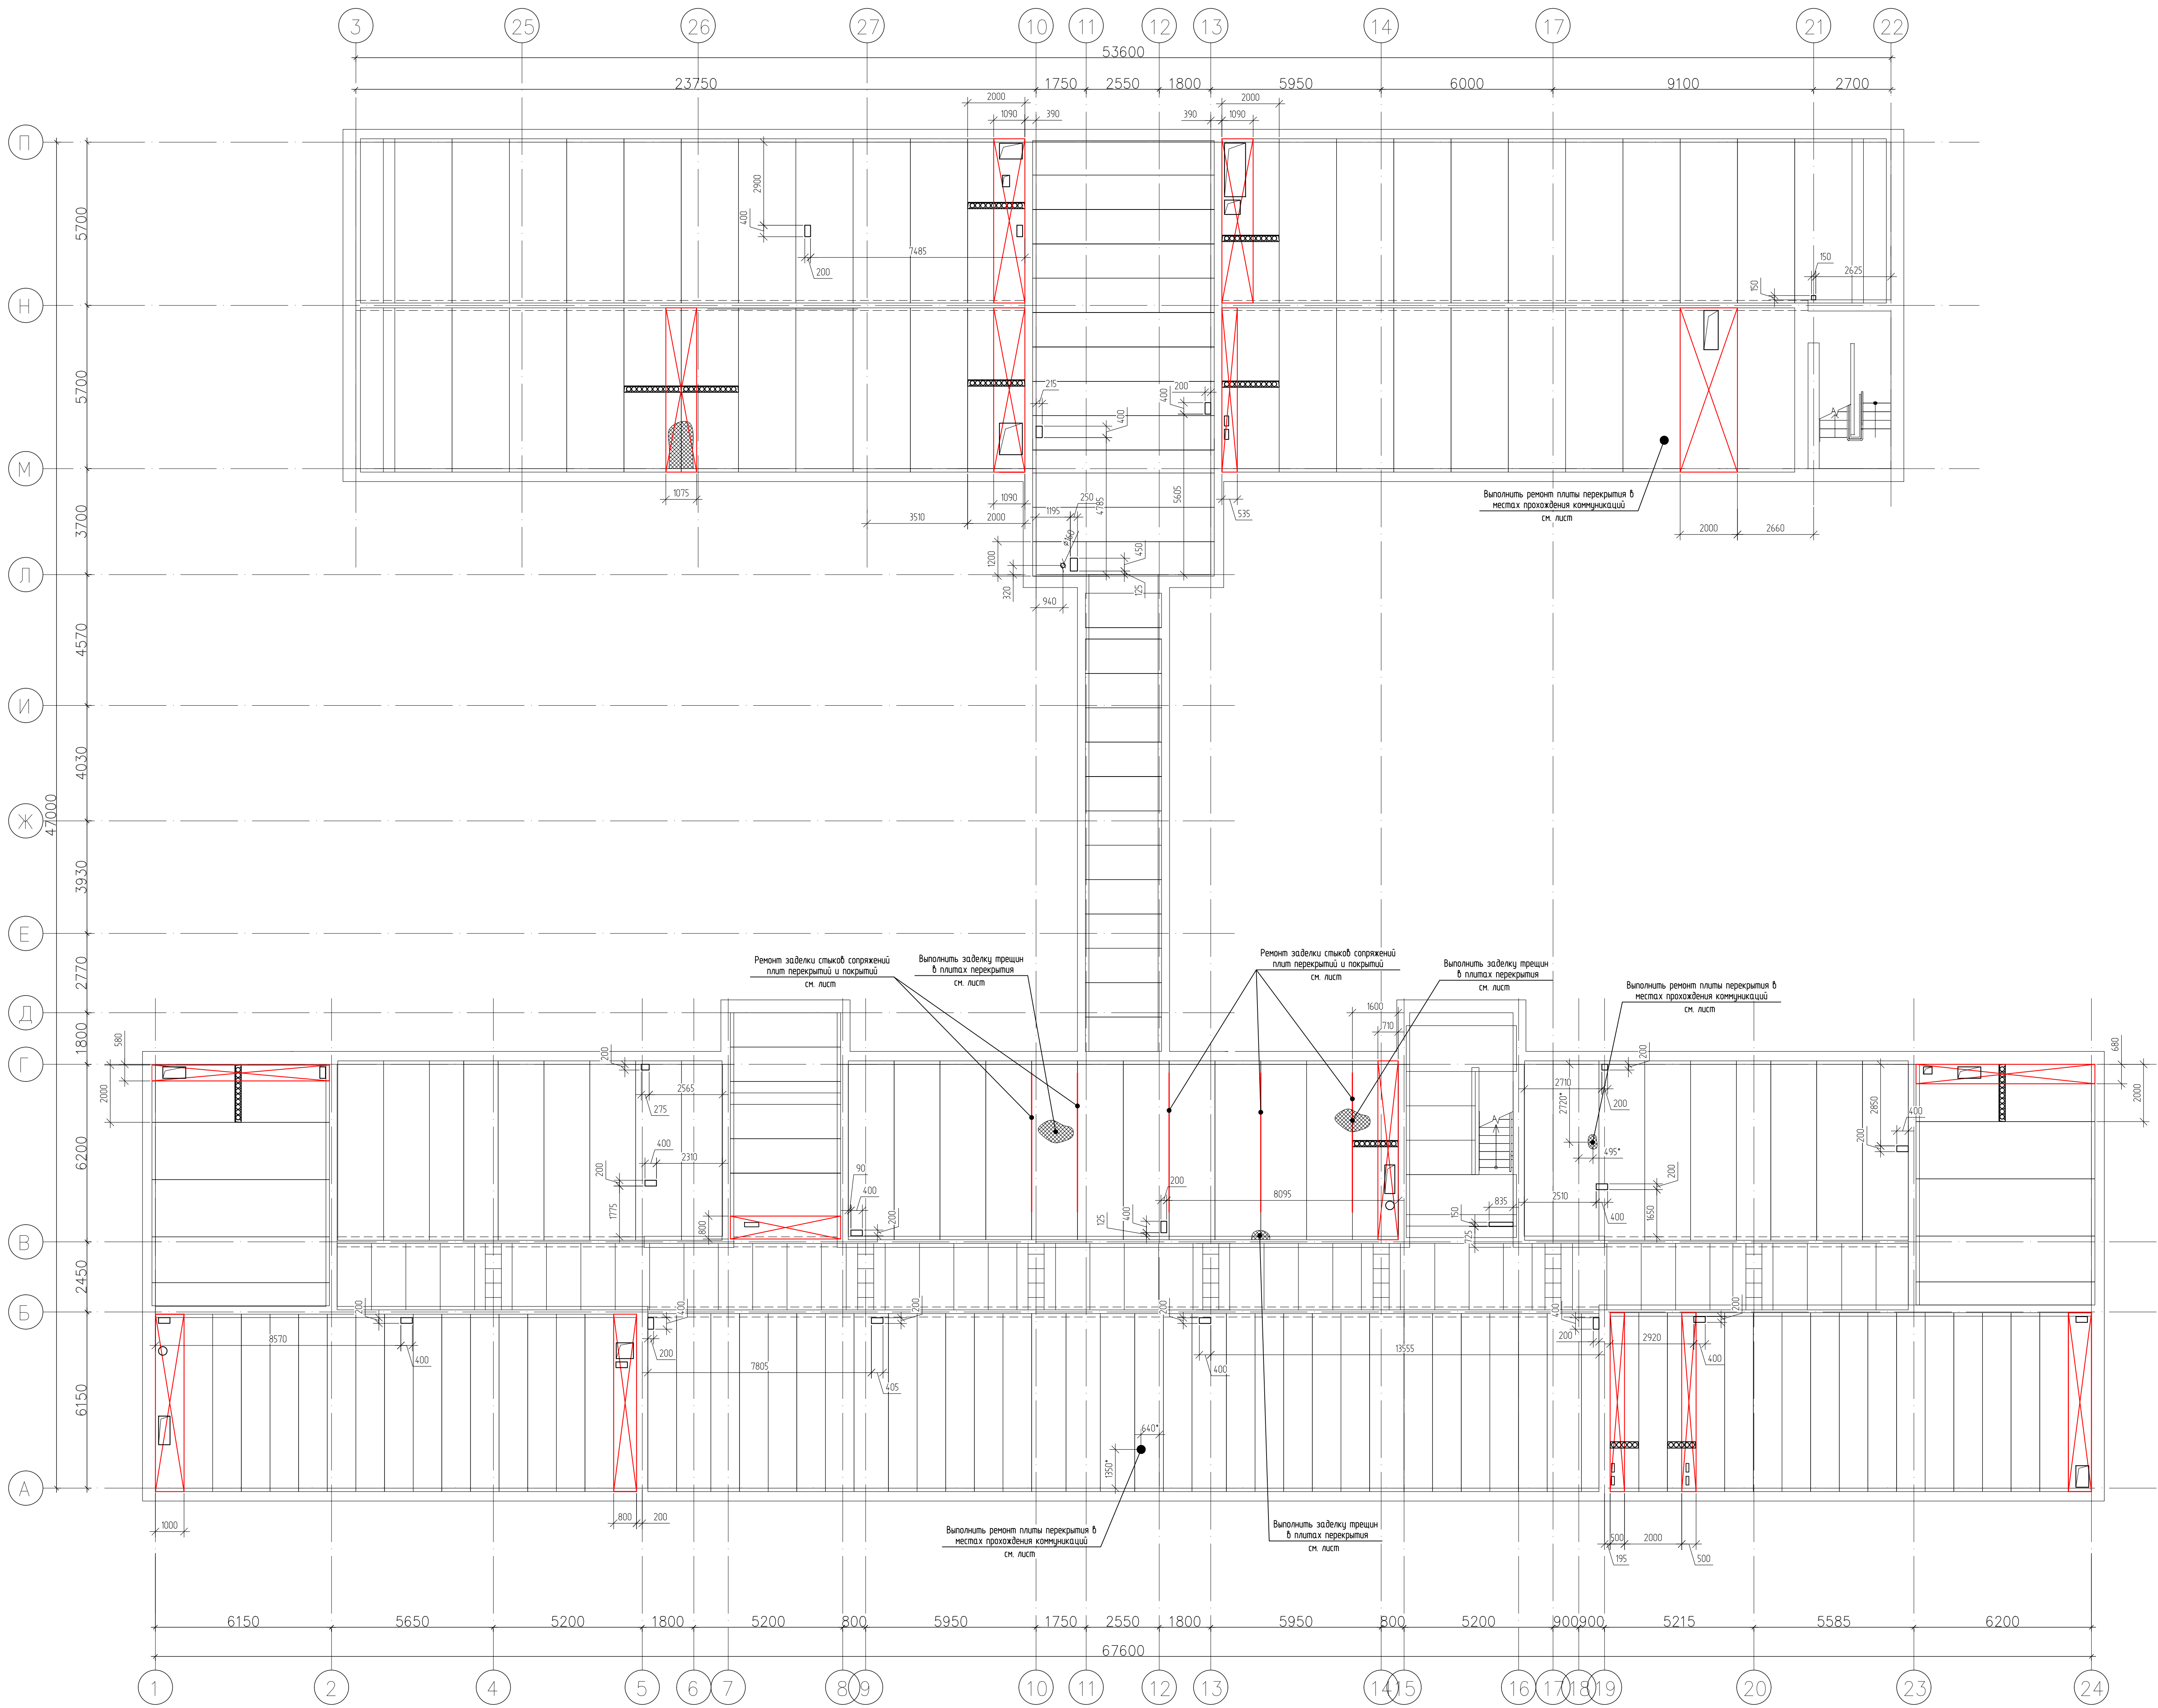

Спецификация на демонтаж плит перекрытия подвала					
Поз	Обозначение	Наименование	Кол	Масса, ед к2	Примечание
		Демонтаж сборных ж/б настилов тип УНТ Н=220мм, м. кв	771		
		Пробивка отверстий в плитах перекрытия, шт	20		

Примечания:
1. Демонтируемые плиты перекрытия разбирать полосами шириной 0,3-0,4 м в направлении рабочего пролета.
2. Первым этапом удалить бетон, а затем обрезать стержни рабочей и конструктивной арматуры.
3. *Размеры уточнить при монтаже.
4. Отверстия ВК, ЗОМ, СС выполнить без разрушения рабочей арматуры плиты перекрытия.


Таблица 1				Таблица 2		
Имя	Инициал	Лист	№ док	Подп.	Дата	
Разработчик	Павлов	1	04.25	04.25	04.25	
ГАП	Артюхов	1	04.25	04.25	04.25	
Исполнитель	Артюхов	1	04.25	04.25	04.25	
Контроль	Артюхов	1	04.25	04.25	04.25	

Схема демонтажа плит перекрытия подвала


Формат А0

Поз.	Обозначение	Наименование	Кол.	Масса, ед. к2	Примечание
		Демонтаж сборных ж/б настилов плит УНТ Н=220мм, м. кв.	92		
		Пробивка отверстий в плитах перекрытия, шт.	14		

Схема демонтажа плит перекрытия 1 этажа

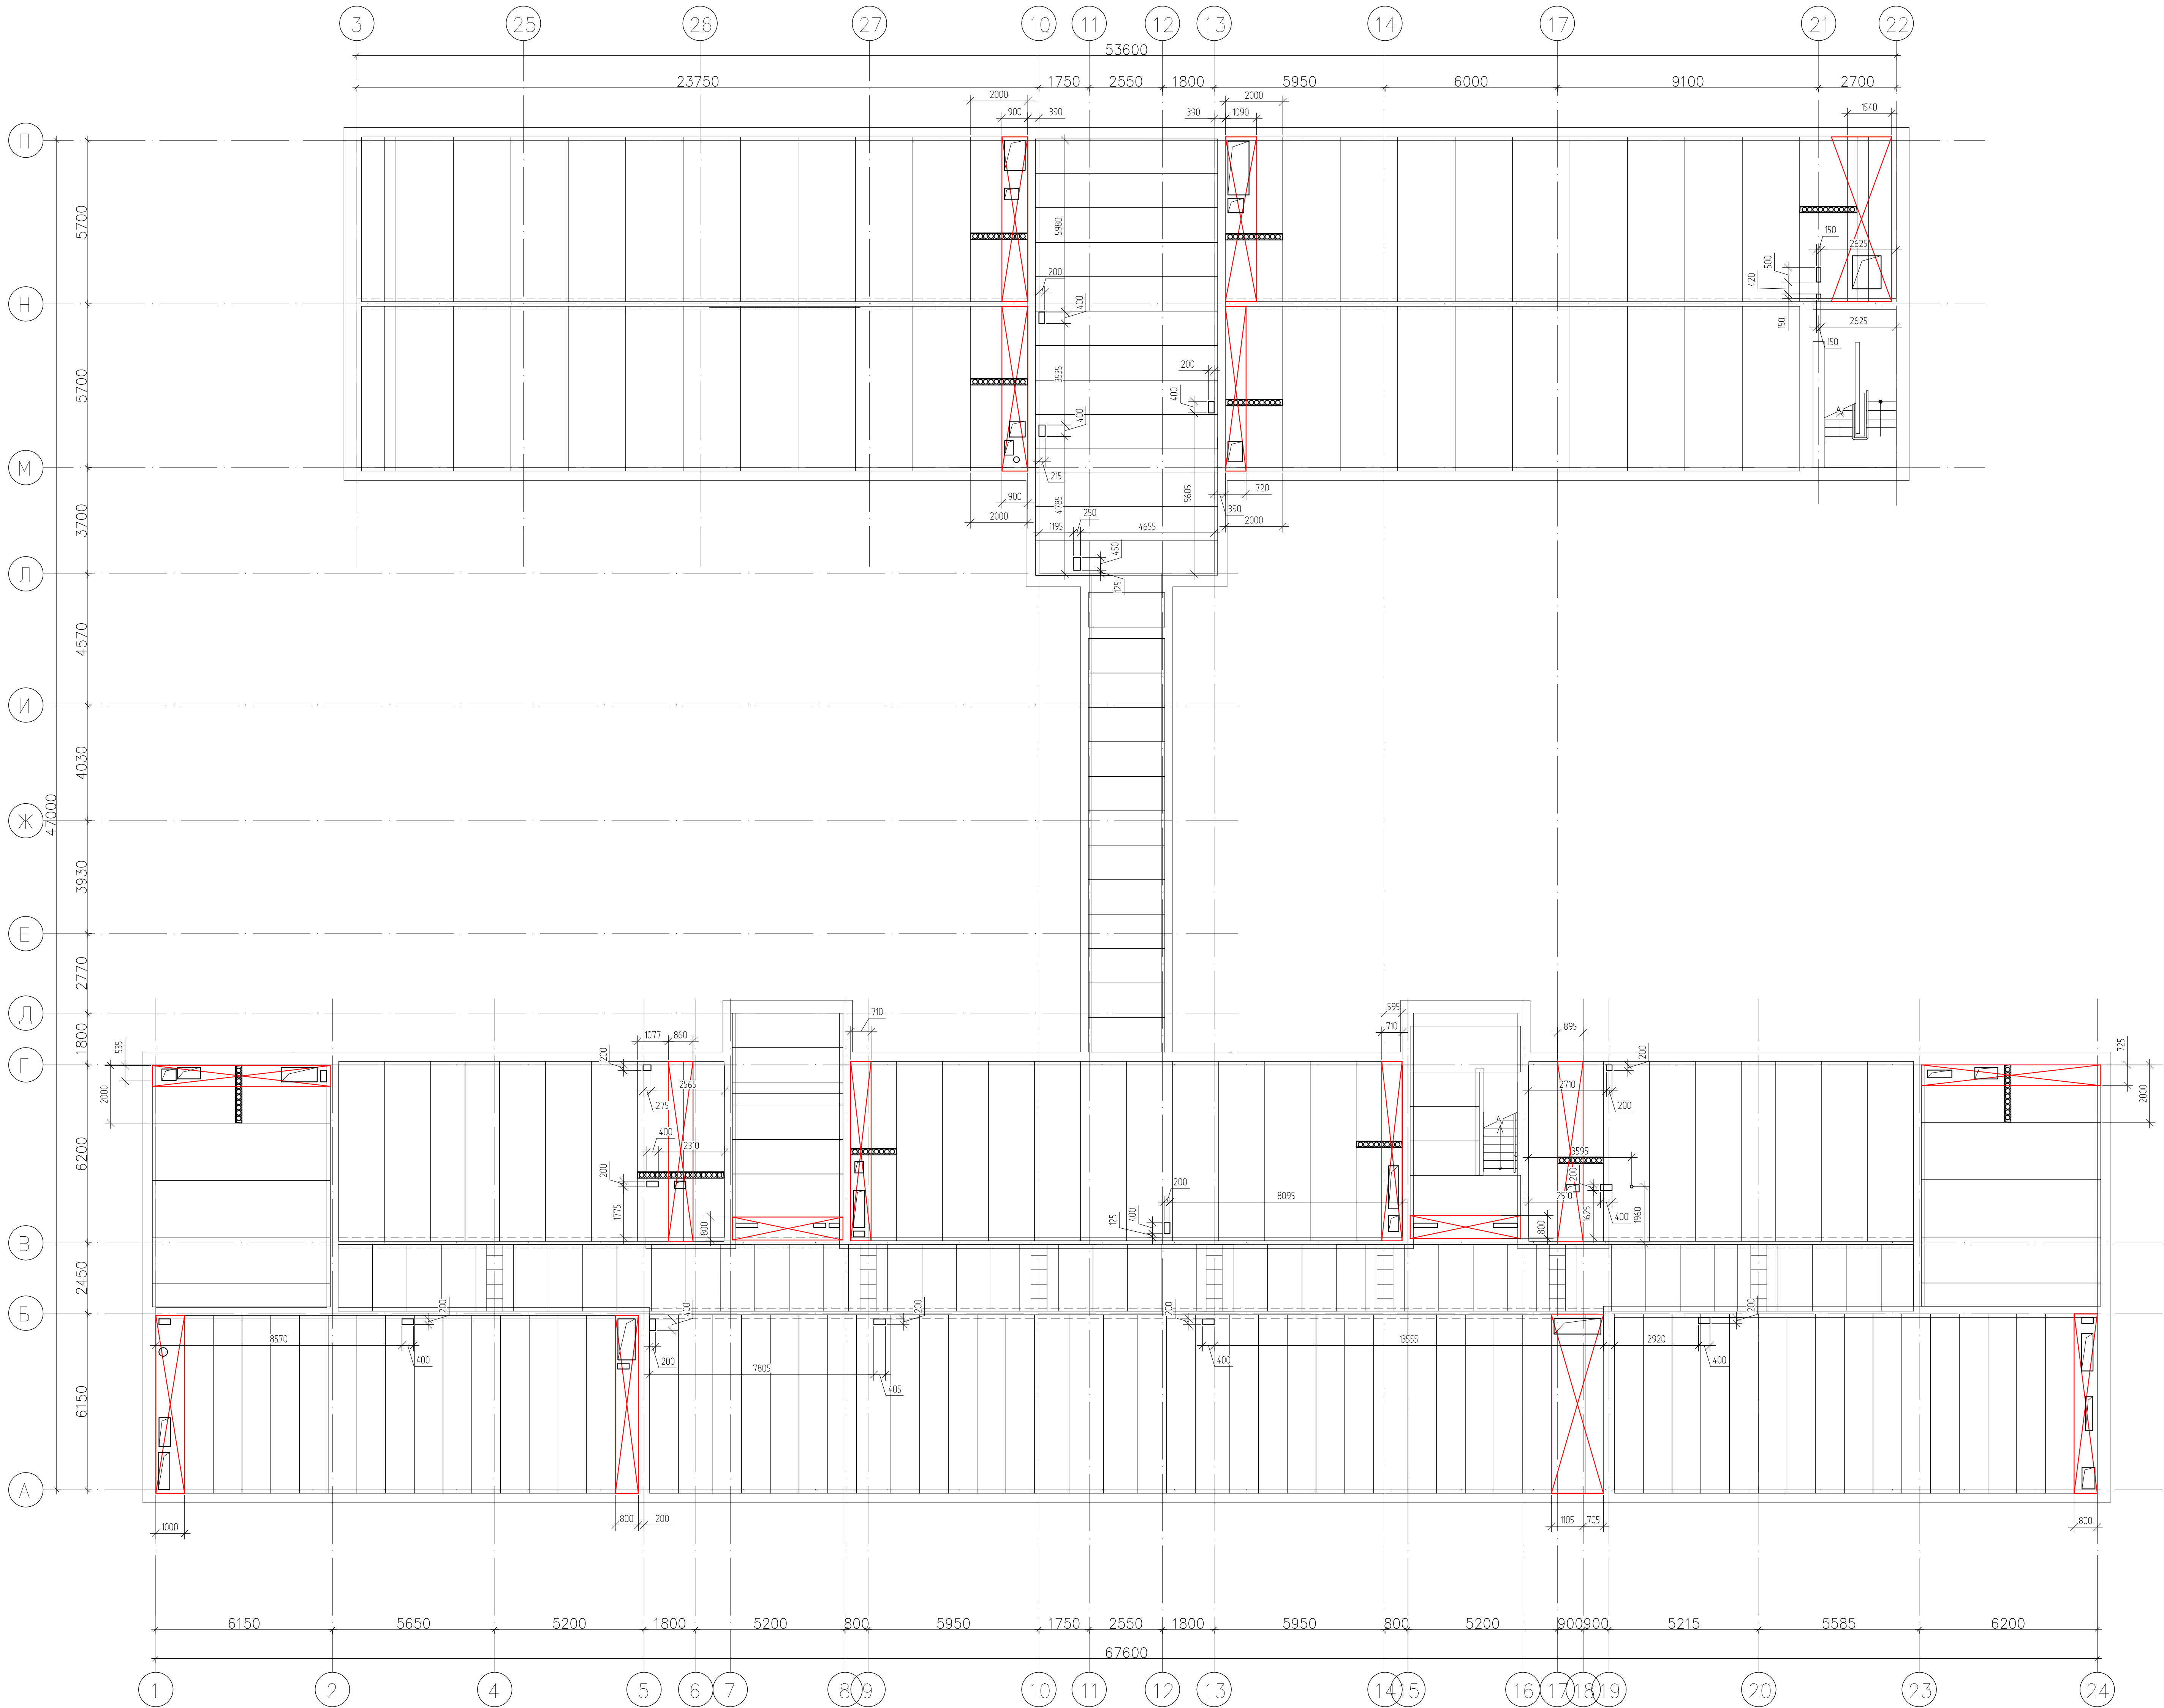

Условные обозначения

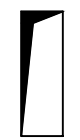 -образуемые проемы для монтажа оборудования

 -демонтируемая плита


- Примечания:
- Демонтируемые плиты перекрытия разбирать полосами шириной 0,3-0,4 м в направлении рабочего пролета.
 - Первым этапом удалить бетон, а затем обрезать стержни рабочей конструктивной арматуры.
 - Размеры уточнить при монтаже.
 - Отверстия ВК, ЗОМ, СС выполнить без разрушения рабочей арматуры плиты перекрытия.

Таблица 1-24-АНО-КР					
Капитальный ремонт общеобразовательного учреждения ГБОУ ЦОКО №2007 по адресу: г. Москва, ул. Ждановская, д.32					
Исполн.	Колосов	Лист № 001	Дата	04.25	04.25
Разработчик	Павлов	Дата	04.25	04.25	04.25
ГАП	Артюхов	Дата	04.25	04.25	04.25
Конструктивные решения				Р	56
Исполнитель	Павлов	Дата	04.25	04.25	04.25
ГАП	Артюхов	Дата	04.25	04.25	04.25
Схема демонтажа плит перекрытия 1 этажа				Формат А0	


Спецификация на демонтаж плит перекрытия 2-го этажа

Поз.	Обозначение	Наименование	Кол.	Масса, кг	Примечание
		Демонтаж сборных ж/б настилов тип 5НТ П=220см, м. кв	98,8		
		Пробивка отверстий в плитах перекрытия, шт	13		

Схема демонтажа плит перекрытия 2 этажа

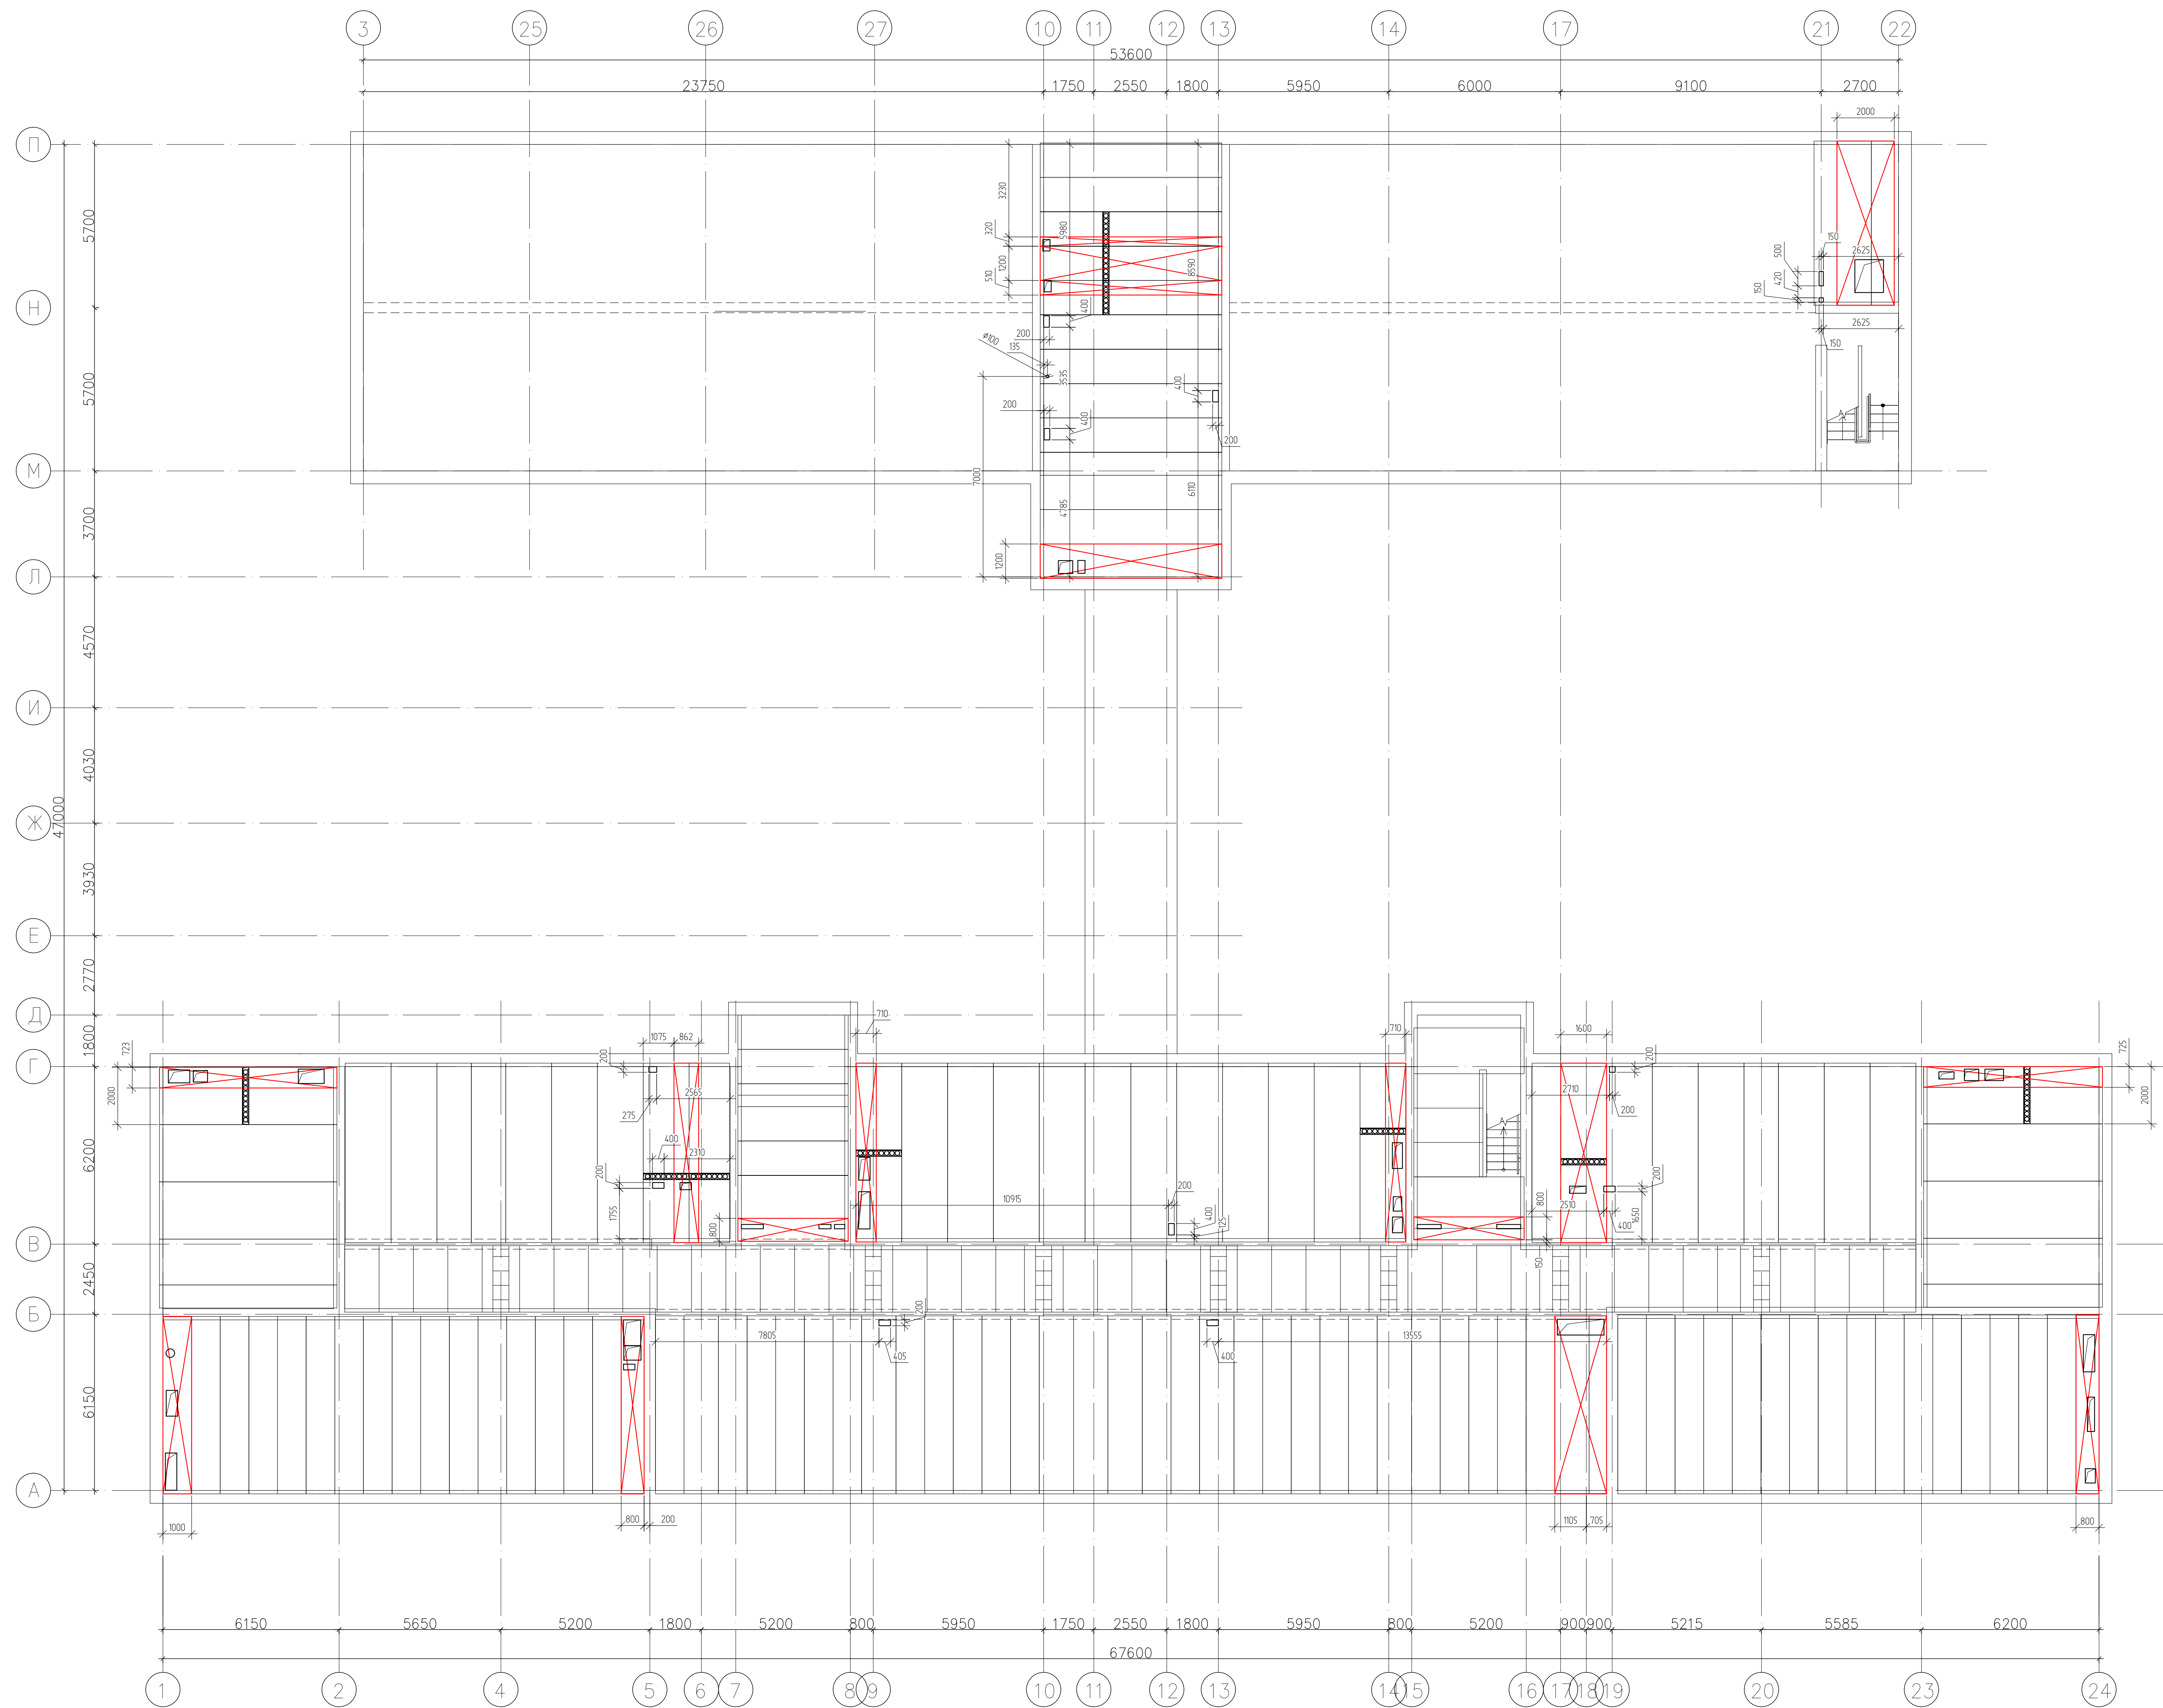

Условные обозначения

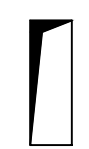

-образуемые проемы для монтажа оборудования




-демонтируемая плита

Примечания:

1. Демонтировать плиты перекрытия разбирать полосами шириной 0,3-0,4 м в направлении рабочего пролета.
2. Первым заплом удалять бетон, а затем обрезать стержни рабочей и конструктивной арматуры.
3. *Размеры уточнить при монтаже.
4. Отверстия ВК, ЗОМ, СС выполнить без разрушения рабочей арматуры плиты перекрытия.

						708/П-24-АНО-КР						
							Калькуляторы: расчеты обязательств по налогу на имущество 1659 "Искон" №232 по адресу г. Москва, ул. Ждановская, 832					
Учел.	Контекст	Листов	№ Док	Подп.	Дата							
Разработчик ГИП	Григорьев Фролов				04.26	Инструментарий расчета						
					04.26							
						Сторона	Лист	Листов				
						р	57					
НКонтроль ГИП	Лукашук Вискин				04.26	 000 "АРТИС"						
					04.26							

Схема демонтажа плит перекрытия 3 этажа

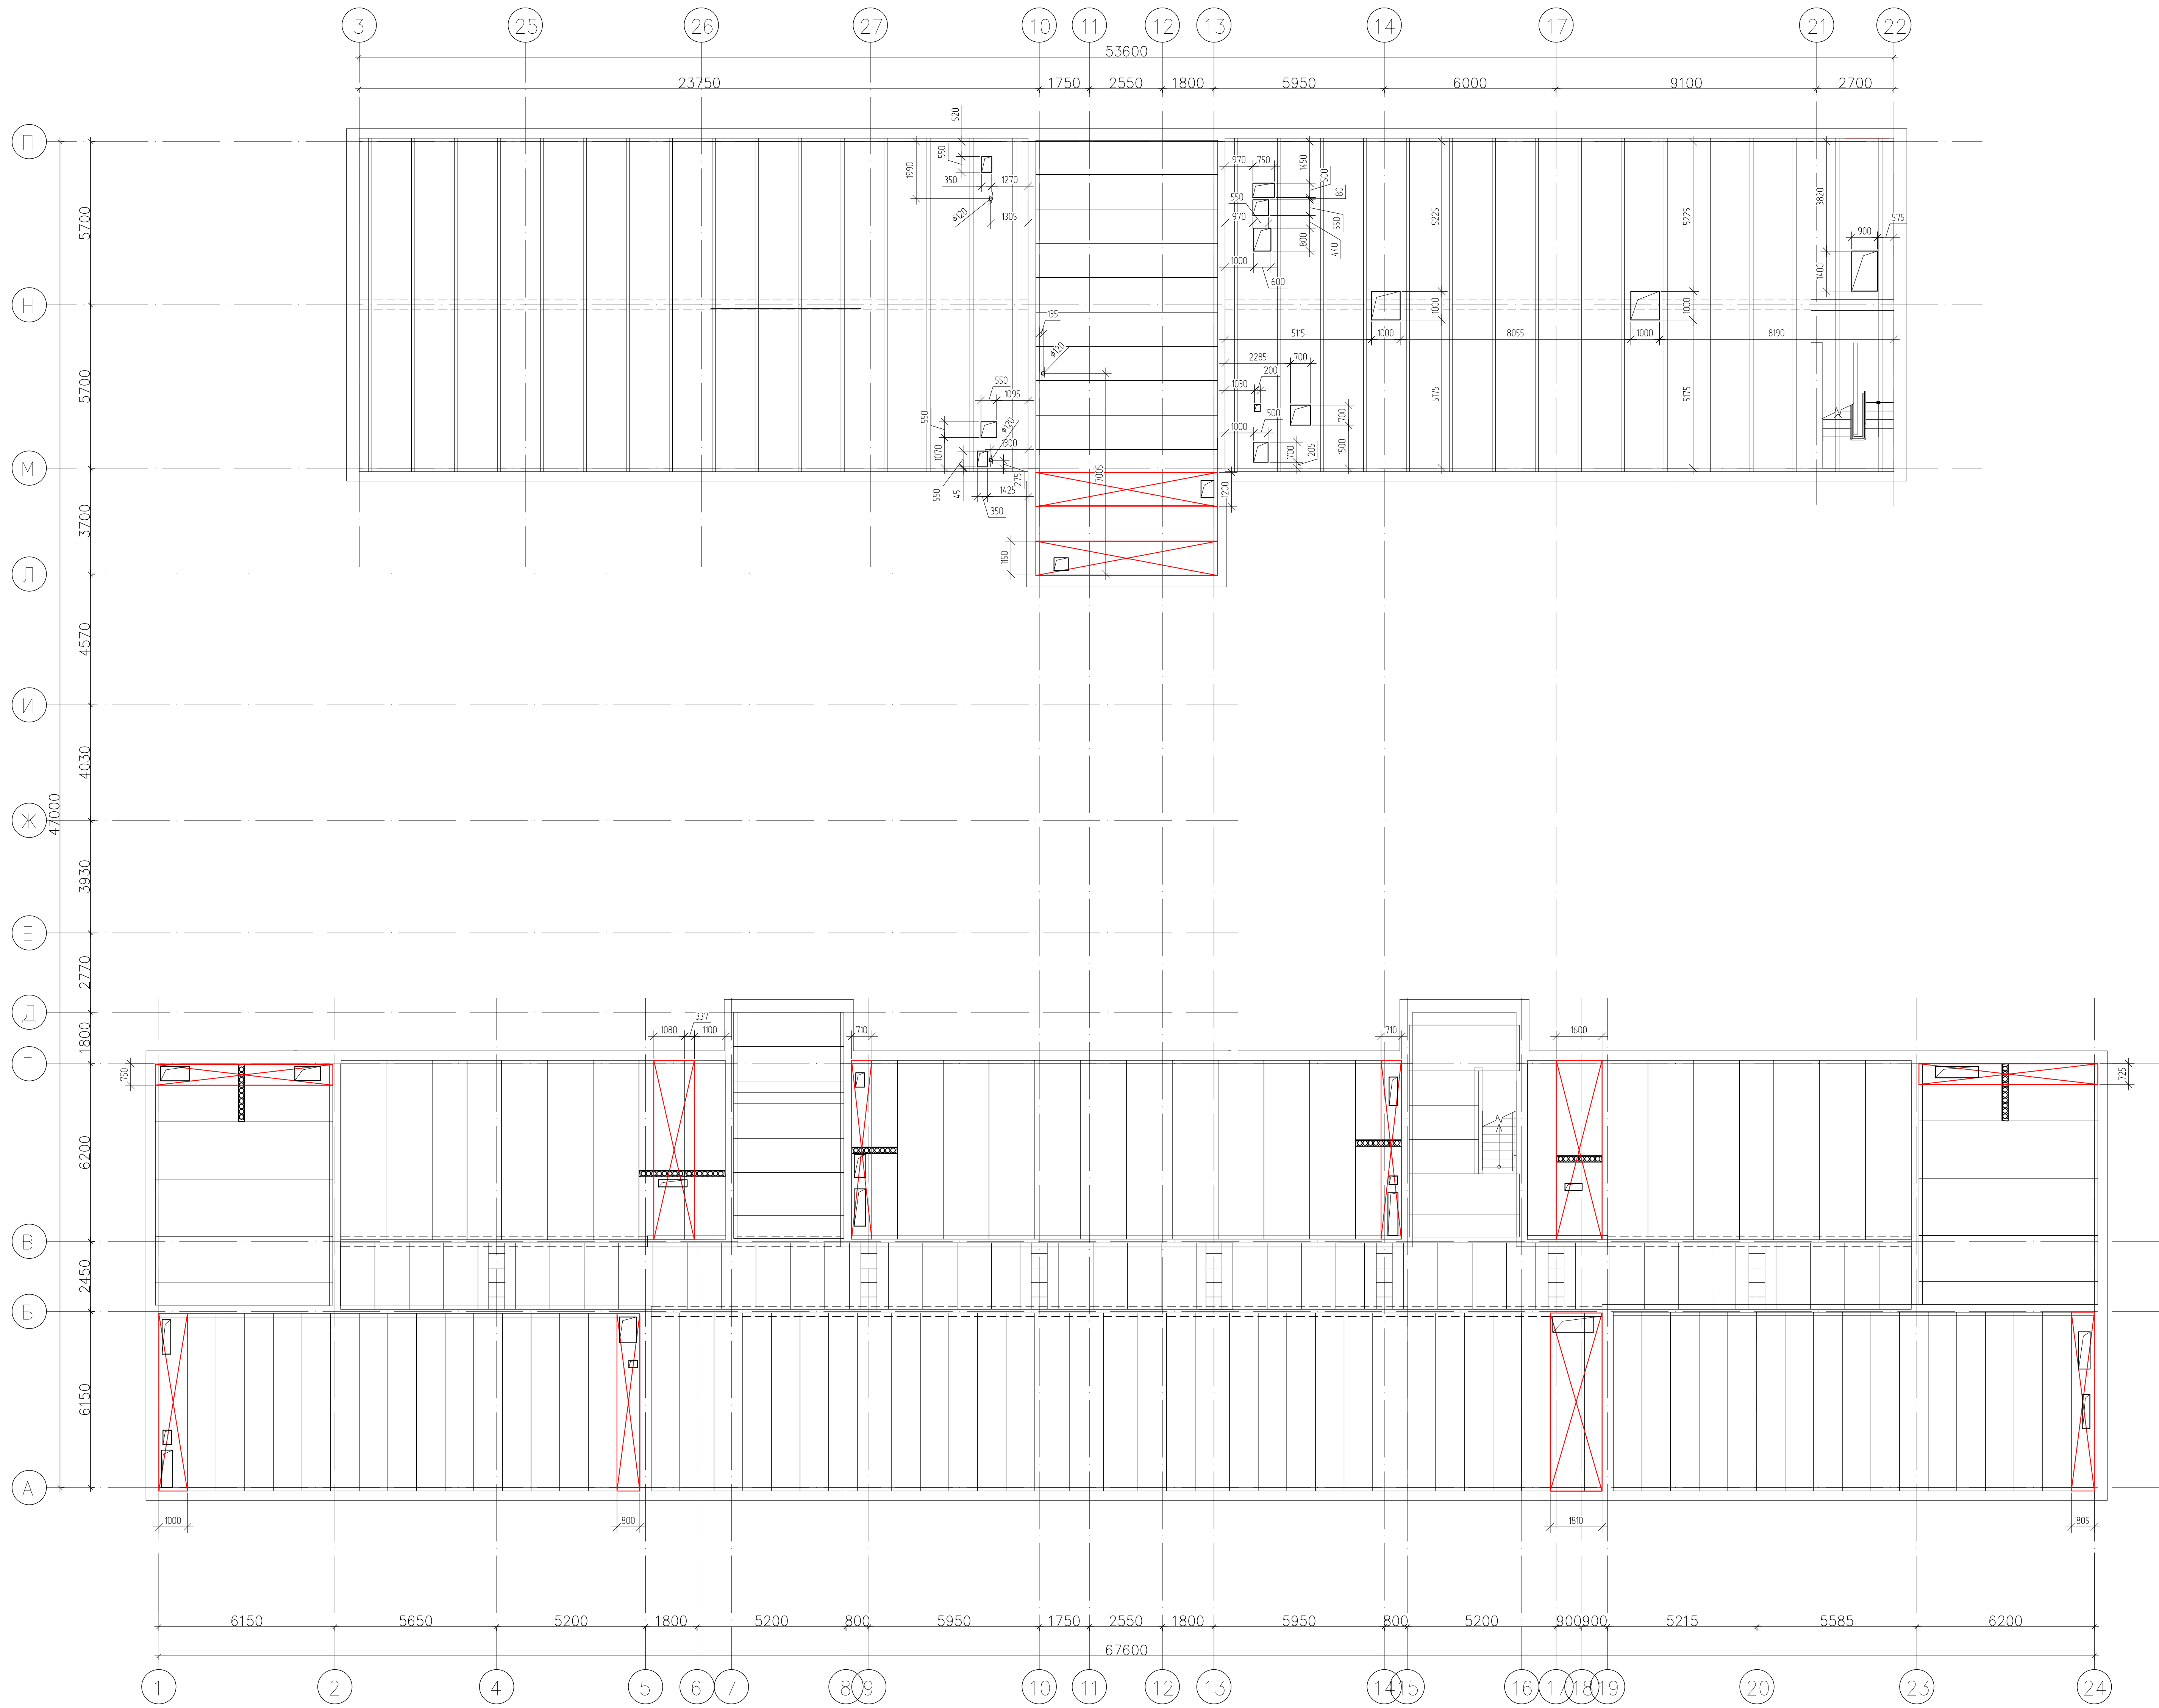

Спецификация на демонтаж плит перекрытия 3-го этажа

Поз	Обозначение	Наименование	Кол	Масса, ед. кг	Приме- чание
		Демонтах сборных ж/б настилов тип УНТ Н=220мм, м. кв.	79,4		
		Продубка отверстий в плитах перекрытия, шт	14		

Условные обозначения

-образуемые проемы для монтажа оборудования


-демонтируемая плита

Примечания

1. Демонтировать плиты перекрытия раздирать полосами шириной 0,3-0,4 м в направлении рабочего пролета.
2. Первым этапом удалить бетон, а затем обрезать стержни рабочей и конструктивной арматуры.
3. *Размеры уточнить при монтаже.
4. Отверстия ВК, ЗОМ, СОС выполнять без разрушения рабочей арматуры плиты перекрытия.

[illegible]

Схема устройства монолитных участков плит перекрытия подвала

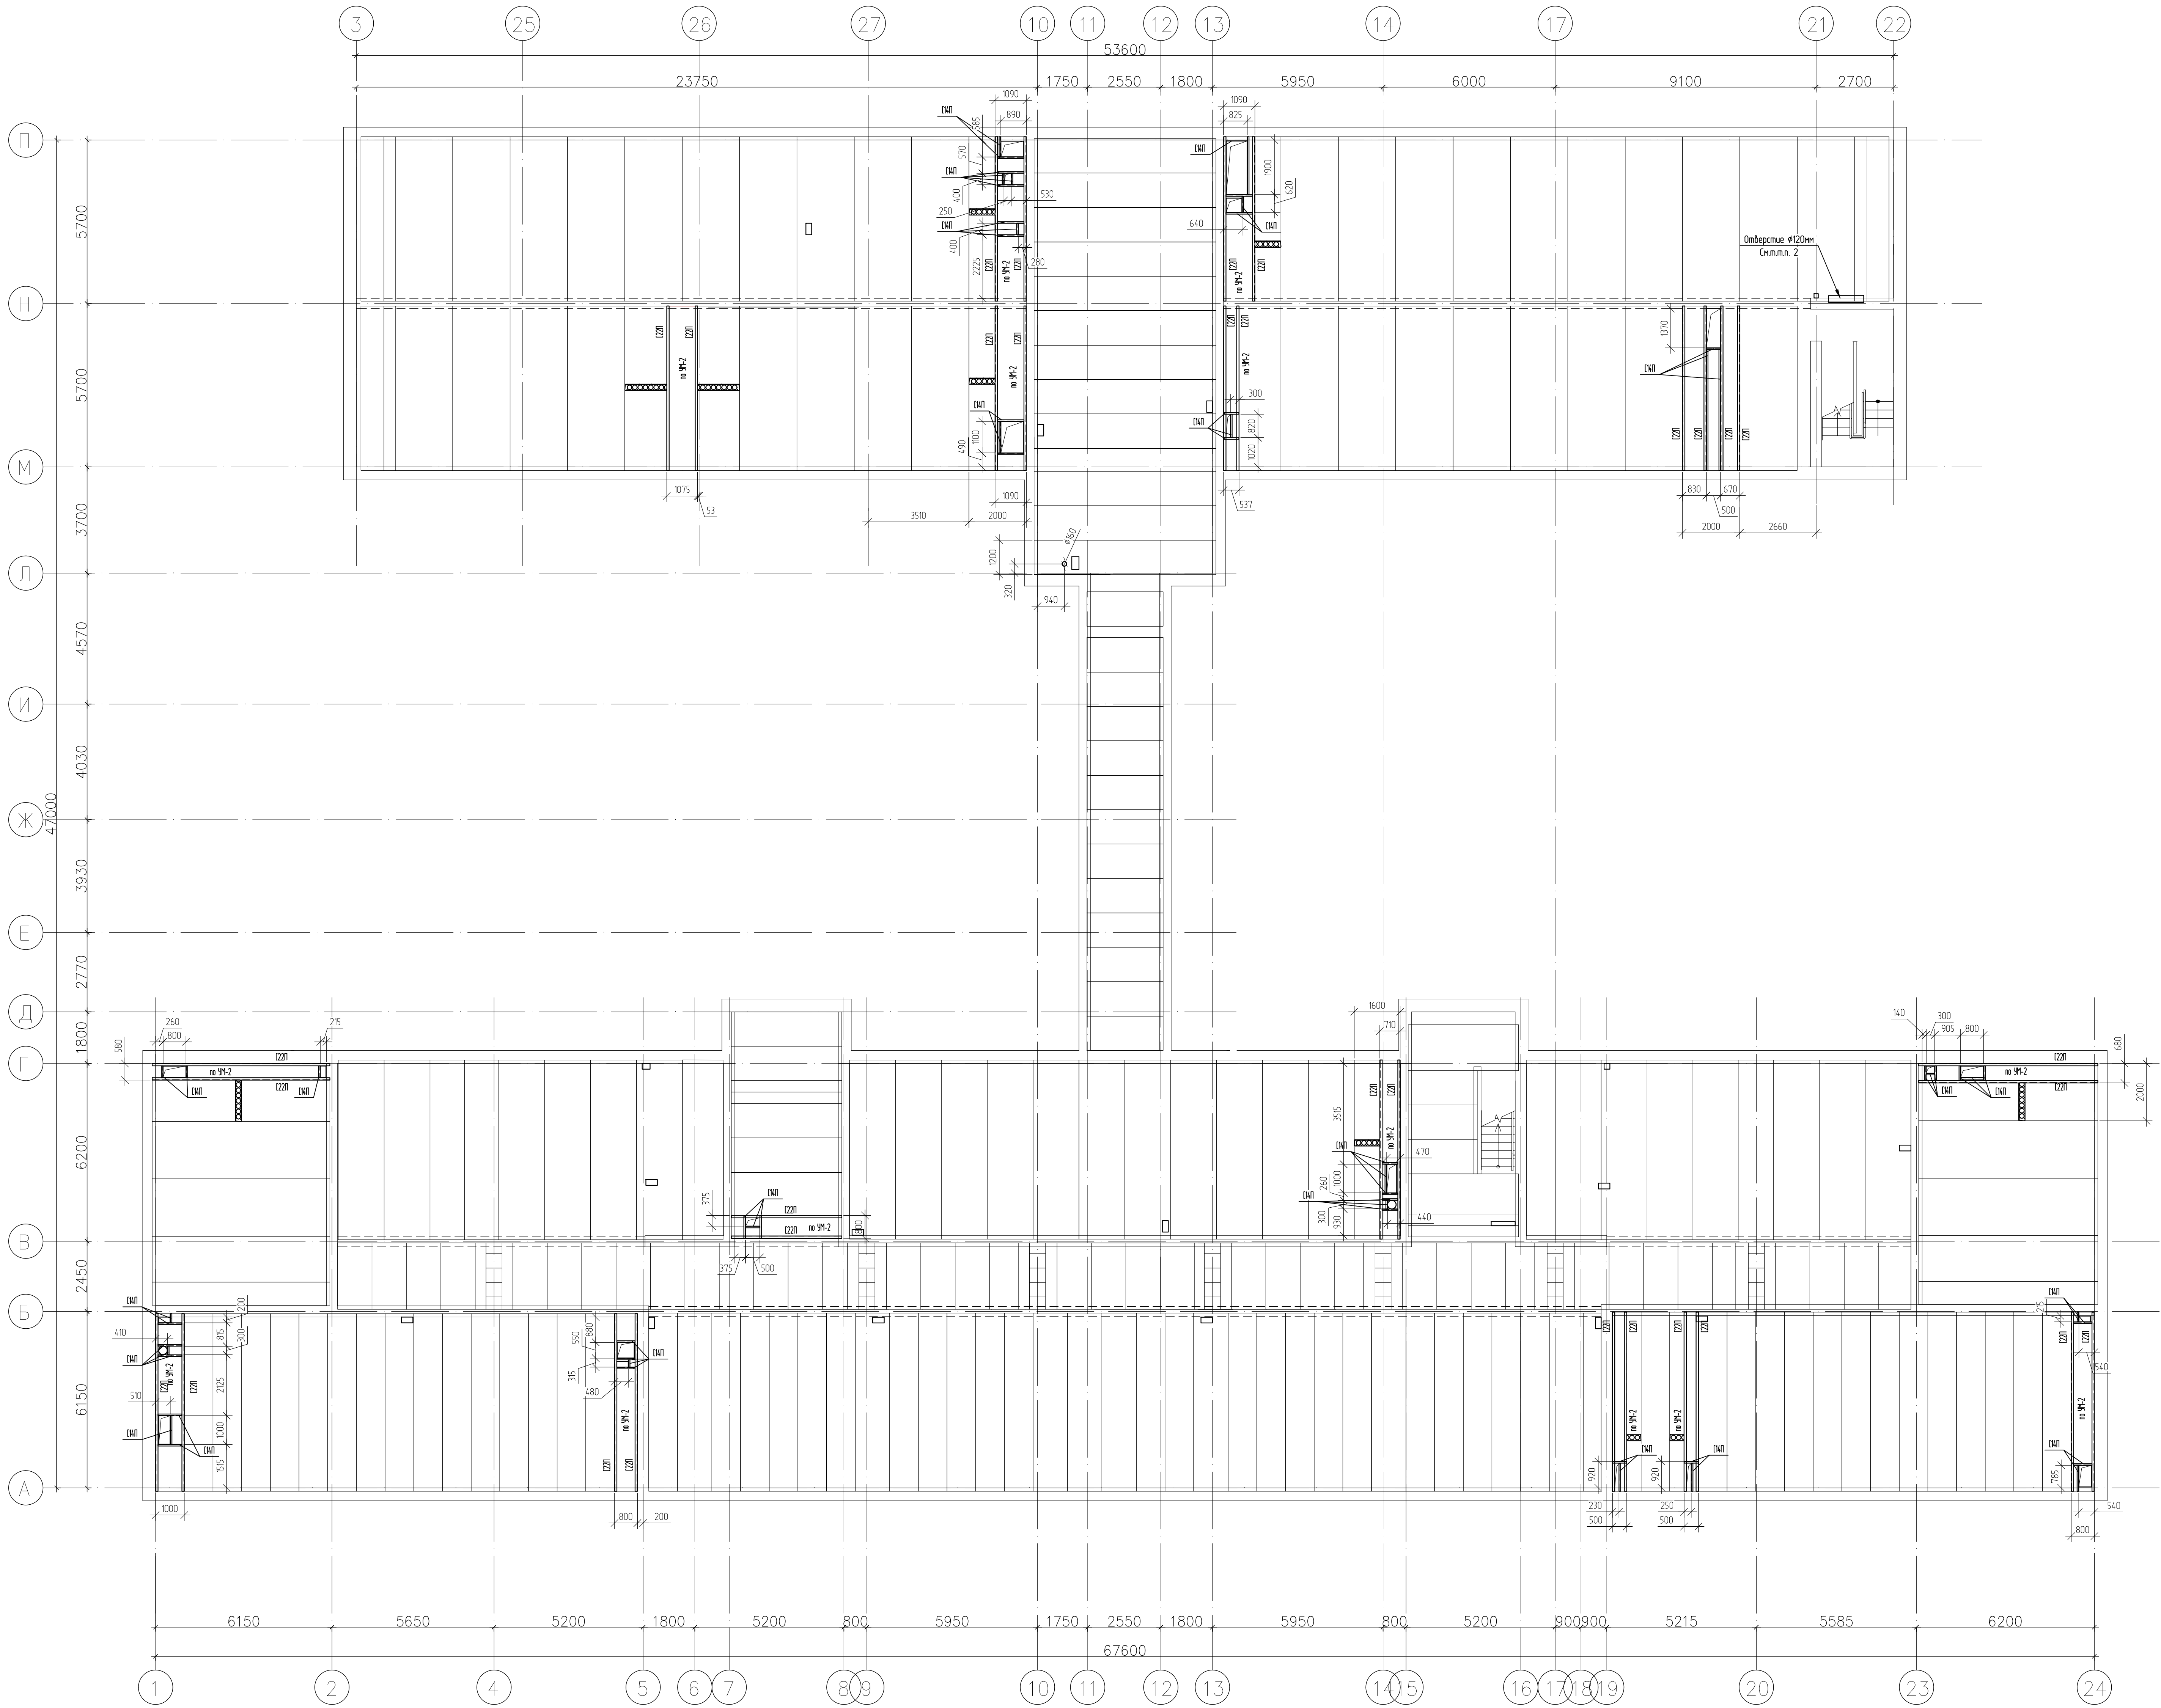

Условные обозначения

- отверстия в плите покрытия для прохождения коммуникаций
- места прохода мелкогазменных коммуникаций (СС, ЭОМ и т.п.)
- В многослойных плитах высотой 220мм отб. пробивать в пустотах (159 Ф).
- В сплошных плитах отб. пробивать, не затрагивая рабочей арматуры.

Спецификация на монолитные участки в плитах L перекрытия подвала					
Поз.	Обозначение	Наименование	Кол.	Масса, ед. кг	Приме- чание
	ГОСТ 8240-97	Швеллер 14П, Лобш. м.п.	54,6	12,3	6716
	ГОСТ 8240-97	Швеллер 22П, Лобш. м.п.	200,0	23,0	4600,0
	ГОСТ 8210-93	Уголок 200х125х12, м.п.	27,0	29,7	803,0
	ГОСТ 24045-2012	Профнастил Н75-750-0,8, м.кв.	701	12,5	876,2
	ГОСТ Р 52544-2006	Арм. #8 А500, Лобш. м.п.	707,1	0,5	355,7
	ГОСТ Р 52544-2006	Арм. #10 А500, Лобш. м.п.	361,0	0,8	283,4
	ГОСТ 23279-2012	Сетка 58р1 100х100, м.кв.	701	25,0	1752,5
	ГОСТ 22042-76	Шпилька М16х650 58 016	60		
	ГОСТ 5915-70	Гайка М16 -6Н5 016	120		
	ГОСТ 6958-70	Шайба 16 01016	120		
		Материалы			
	ГОСТ 26633-2012	Бетон В25 F100 W6, м.куб	7,5		
	ГОСТ 25129-82	Грунт ГФ-021 1б 2 слоя, расход 100г/м2, кг	36,0		

Примечания:
1. См. совместно с листом -

Т08/П-24-АНД-КР					
Калькуляционный расчет монолитного участка плиты					
ГБОУ ЦОСН №2007 по адресу: г. Москва, ул. Художественная, д.32					
Имя	Инициал	Лист	№ док.	Дата	
Разработчик	Григорьев	04.26			
ГАП	Артюхов	04.26			
Конструктивные решения				Лист	Листов
				Р	59
Исполнитель	Артюхов	04.26			
Контроль	Артюхов	04.26			
Ген.пр.	Артюхов	04.26			
Схема устройства монолитных участков плит перекрытия подвала				Формат А0	

Поз.	Обозначение	Наименование	Кол.	Масса, ед. кг	Приме- чание
	ГОСТ 8240-97	Швеллер 14П, Лодш. м.п.	73,2	12,3	900,4
	ГОСТ 8240-97	Швеллер 22П, Лодш. м.п.	186,0	23,0	4278,0
	ГОСТ 8210-93	Уголок 200х125х12, м.п.	29,0	29,7	862,5
	ГОСТ 24045-2012	Профнастил Н75-750-0,8, м.кб	80,3	12,5	1003,8
	ГОСТ Р 52544-2006	Арм. #8 А500, Лодш. м.п.	810,2	0,5	407,5
	ГОСТ Р 52544-2006	Арм. #10 А500, Лодш. м.п.	413,5	0,8	324,6
	ГОСТ 23279-2012	Сетка 5бр1 100х100 м.кб	80,3	25,0	2007,5
	ГОСТ 22042-76	Шпилька М16х6х50 58 016	6,8		
	ГОСТ 5915-70	Гайка М16 -6H5 016	136		
	ГОСТ 6958-70	Шайба 16 01016	136		
		<u>Материалы</u>			
	ГОСТ 26633-2012	Бетон В25 F100 W6, м.кбб	8,1		
	ГОСТ 25129-82	Грунт ГФ-021 1б, 2' слоя, раскод 100г/м2), кг	38,7		

Architectural floor plan of a building, showing a grid system with horizontal axis 1-24 and vertical axis A-П. The plan includes detailed dimensions for various sections and rooms.

Horizontal Dimensions (Top):

- 3 to 25: 23750
- 25 to 26: 1750
- 26 to 27: 2550
- 27 to 10: 1800
- 10 to 11: 53600
- 11 to 12: 2000
- 12 to 13: 5950
- 13 to 14: 6000
- 14 to 17: 9100
- 17 to 21: 2700
- 21 to 22: 4000

Horizontal Dimensions (Bottom):

- 1 to 2: 6150
- 2 to 4: 5650
- 4 to 5: 5200
- 5 to 6: 1800
- 6 to 7: 5200
- 7 to 8: 800
- 8 to 9: 5950
- 9 to 10: 1750
- 10 to 11: 2550
- 11 to 12: 1800
- 12 to 13: 5950
- 13 to 14: 800
- 14 to 15: 5200
- 15 to 16: 300
- 16 to 17: 300
- 17 to 18: 5215
- 18 to 19: 5585
- 19 to 20: 6200
- 20 to 23: 6200
- 23 to 24: 6200

Vertical Dimensions (Left):

- П to Н: 5700
- Н to М: 5700
- М to Л: 3700
- Л to И: 4570
- И to Ж: 4030
- Ж to Е: 3930
- Е to Д: 2770
- Д to Г: 1800
- Г to В: 6200
- В to Б: 2450
- Б to А: 6150

Vertical Dimensions (Right):

- П to Н: 5700
- Н to М: 5700
- М to Л: 3700
- Л to И: 4570
- И to Ж: 4030
- Ж to Е: 3930
- Е to Д: 2770
- Д to Г: 1800
- Г to В: 6200
- В to Б: 2450
- Б to А: 6150

Room and Section Details:

- Room 101: 101, 102, 103, 

- - отверстия в плите покрытия для прохождения коммуникаций
- - места прохода мелкокоразмерных коммуникаций (СС, ЭОМ и т.п).

В многослойных плитах высотой 220мм отв. пробивать в пустотах (159 Ф).
 В сплошных плитах отв. пробивать, не затрагивая рабочей арматуры.


Примечания:

1. См. совместно с листом -
2. Отверстия плит перекрытия выполнять безударным способом строго между рабочей арматурой в местах продольных пустот. Расположение пустот уточнить по месту проведения работ.

[illegible]

Спецификация на монолитные участки в плитах
перекрытия 2-го этажа

Схема устройства монолитных участков плит перекрытия 2 этажа.

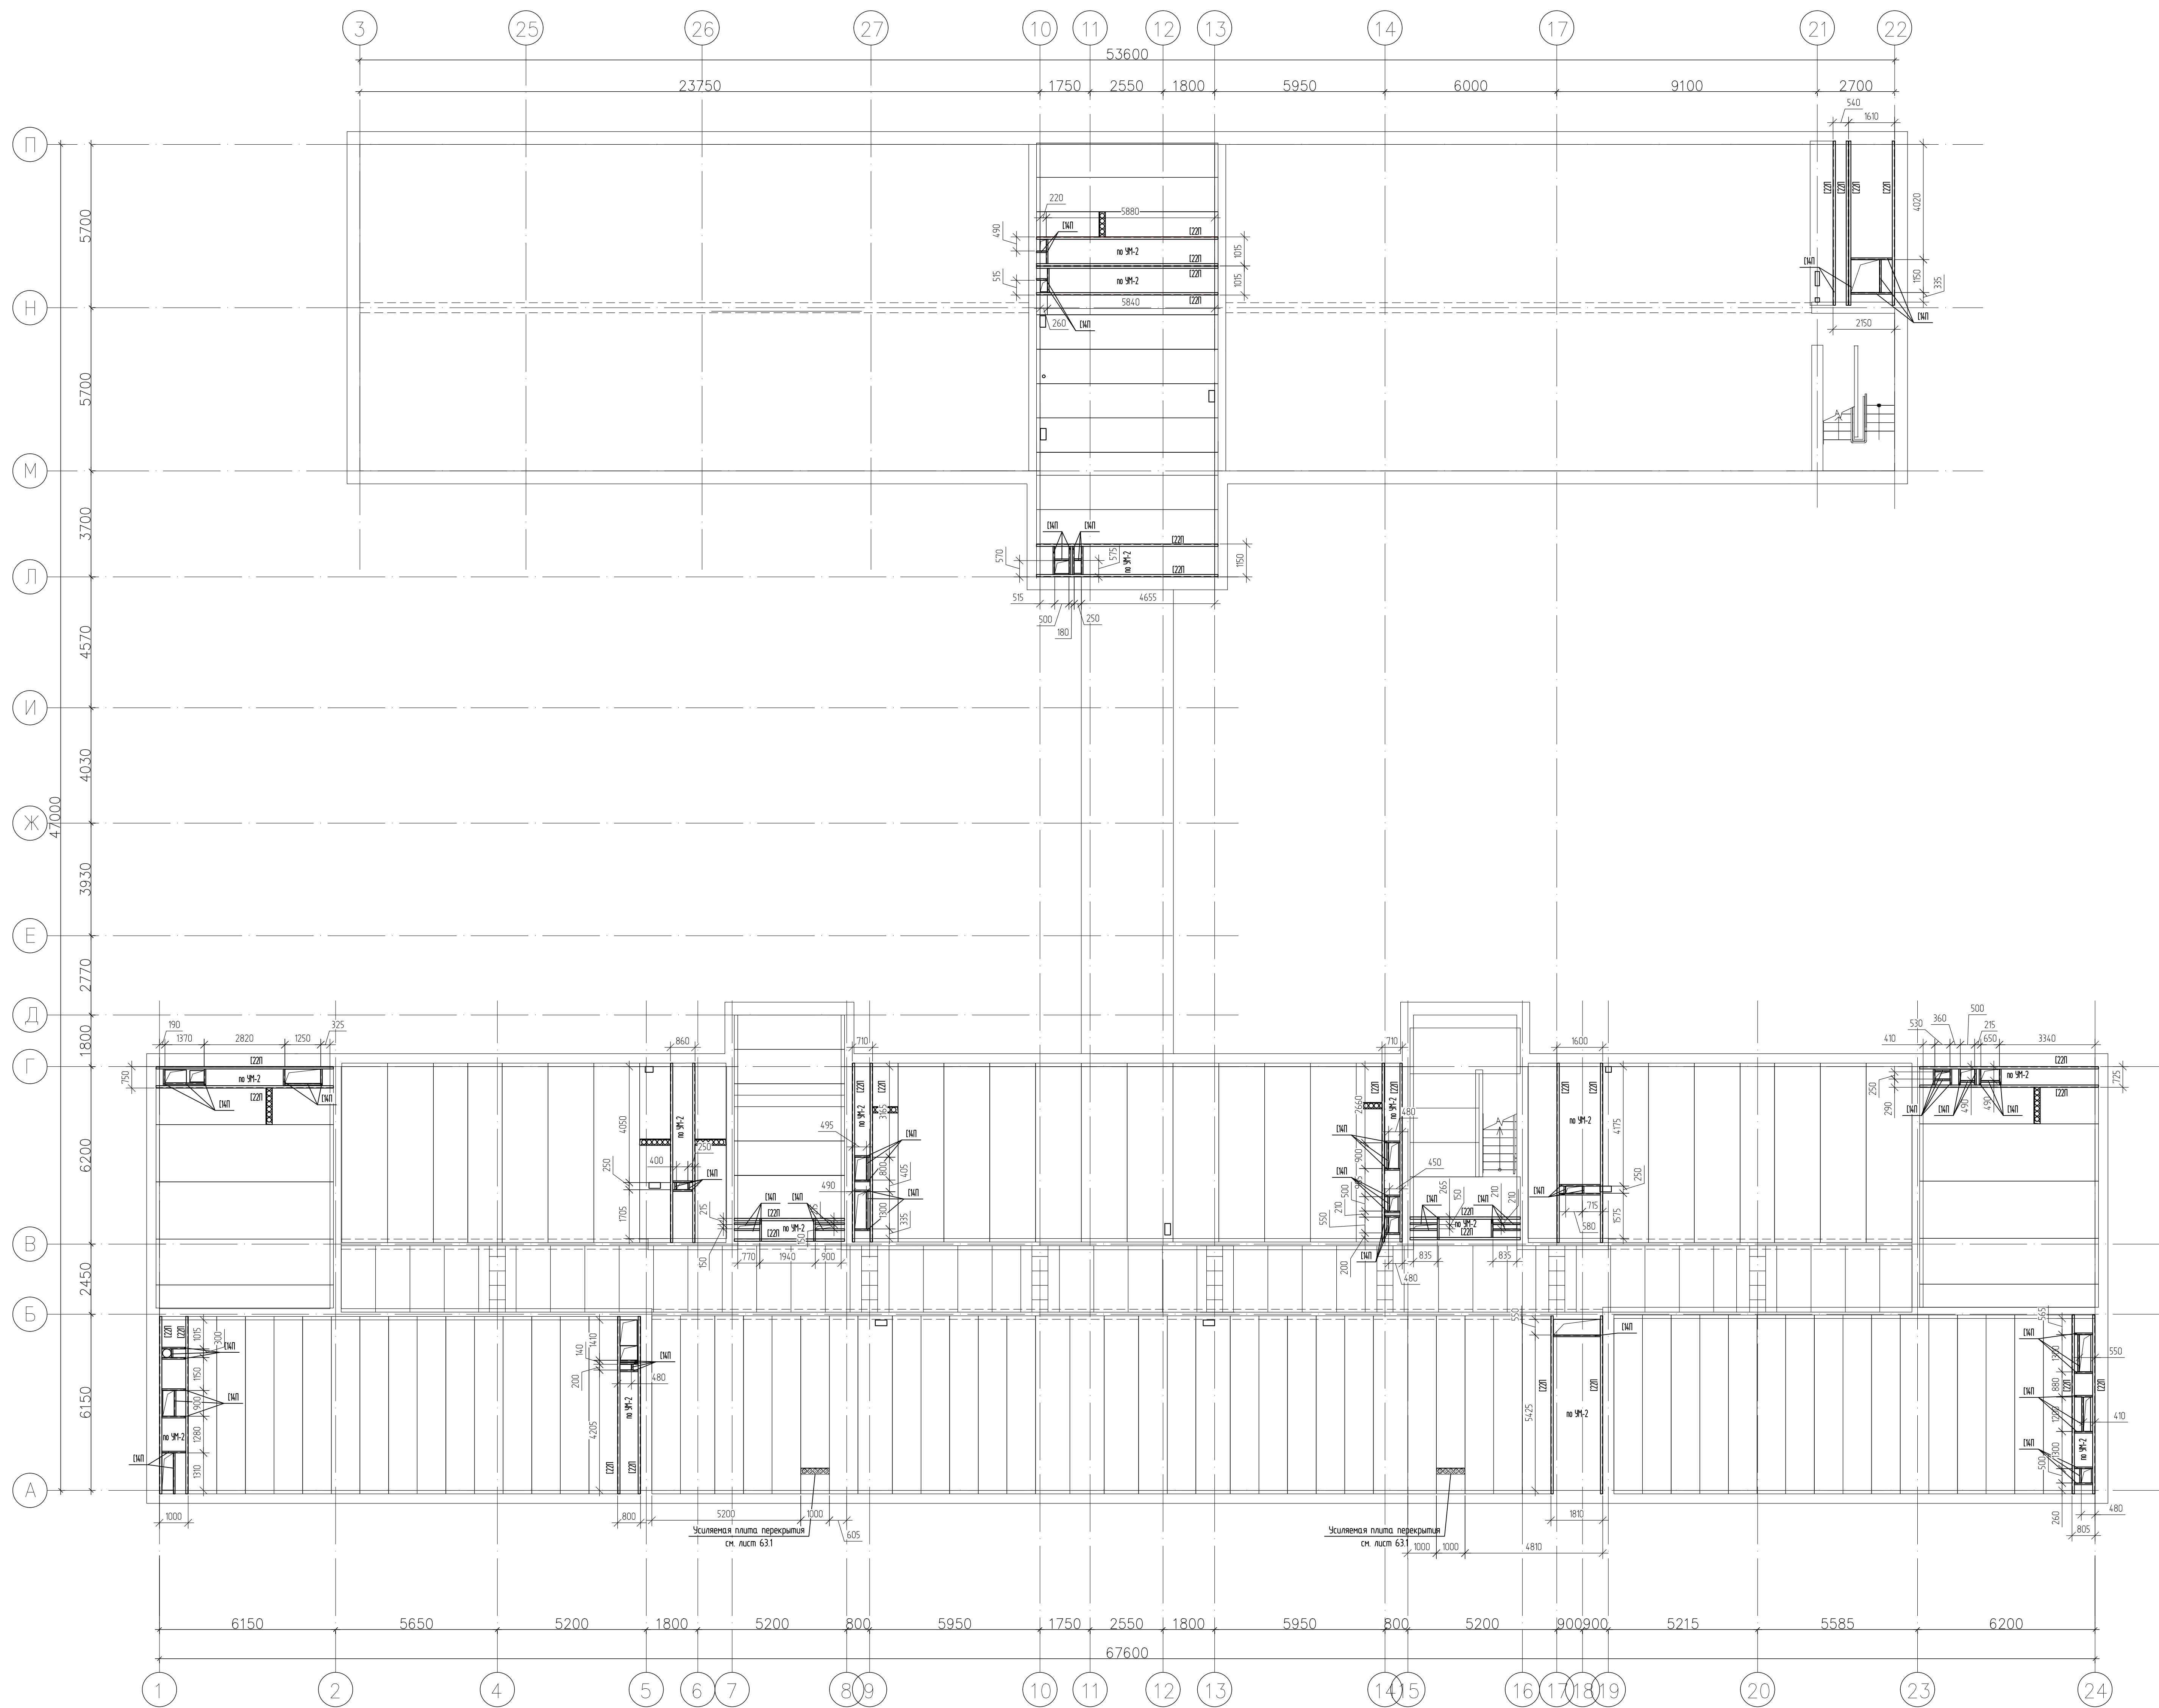

Условные обозначения


- отверстия в плите покрытия для прохождения коммуникаций
 - места прохода мелкокоразмерных коммуникаций (СС, ЭОМ и т.п).
- В многослойных плитах высотой 220мм отв. пробивать в пустотах (159 Ф).
 В сплошных плитах отв. пробивать, не затрагивая рабочей арматуры.

Примечания:


1. См. совместно с листом -
2. Отверстия плит перекрытия выполнять безударным способом строго между рабочей арматурой в местах продольных пустот. Расположение пустот уточнить по месту проведения работ.

[illegible]

Схема устройства монолитных участков плит перекрытия 3 этажа

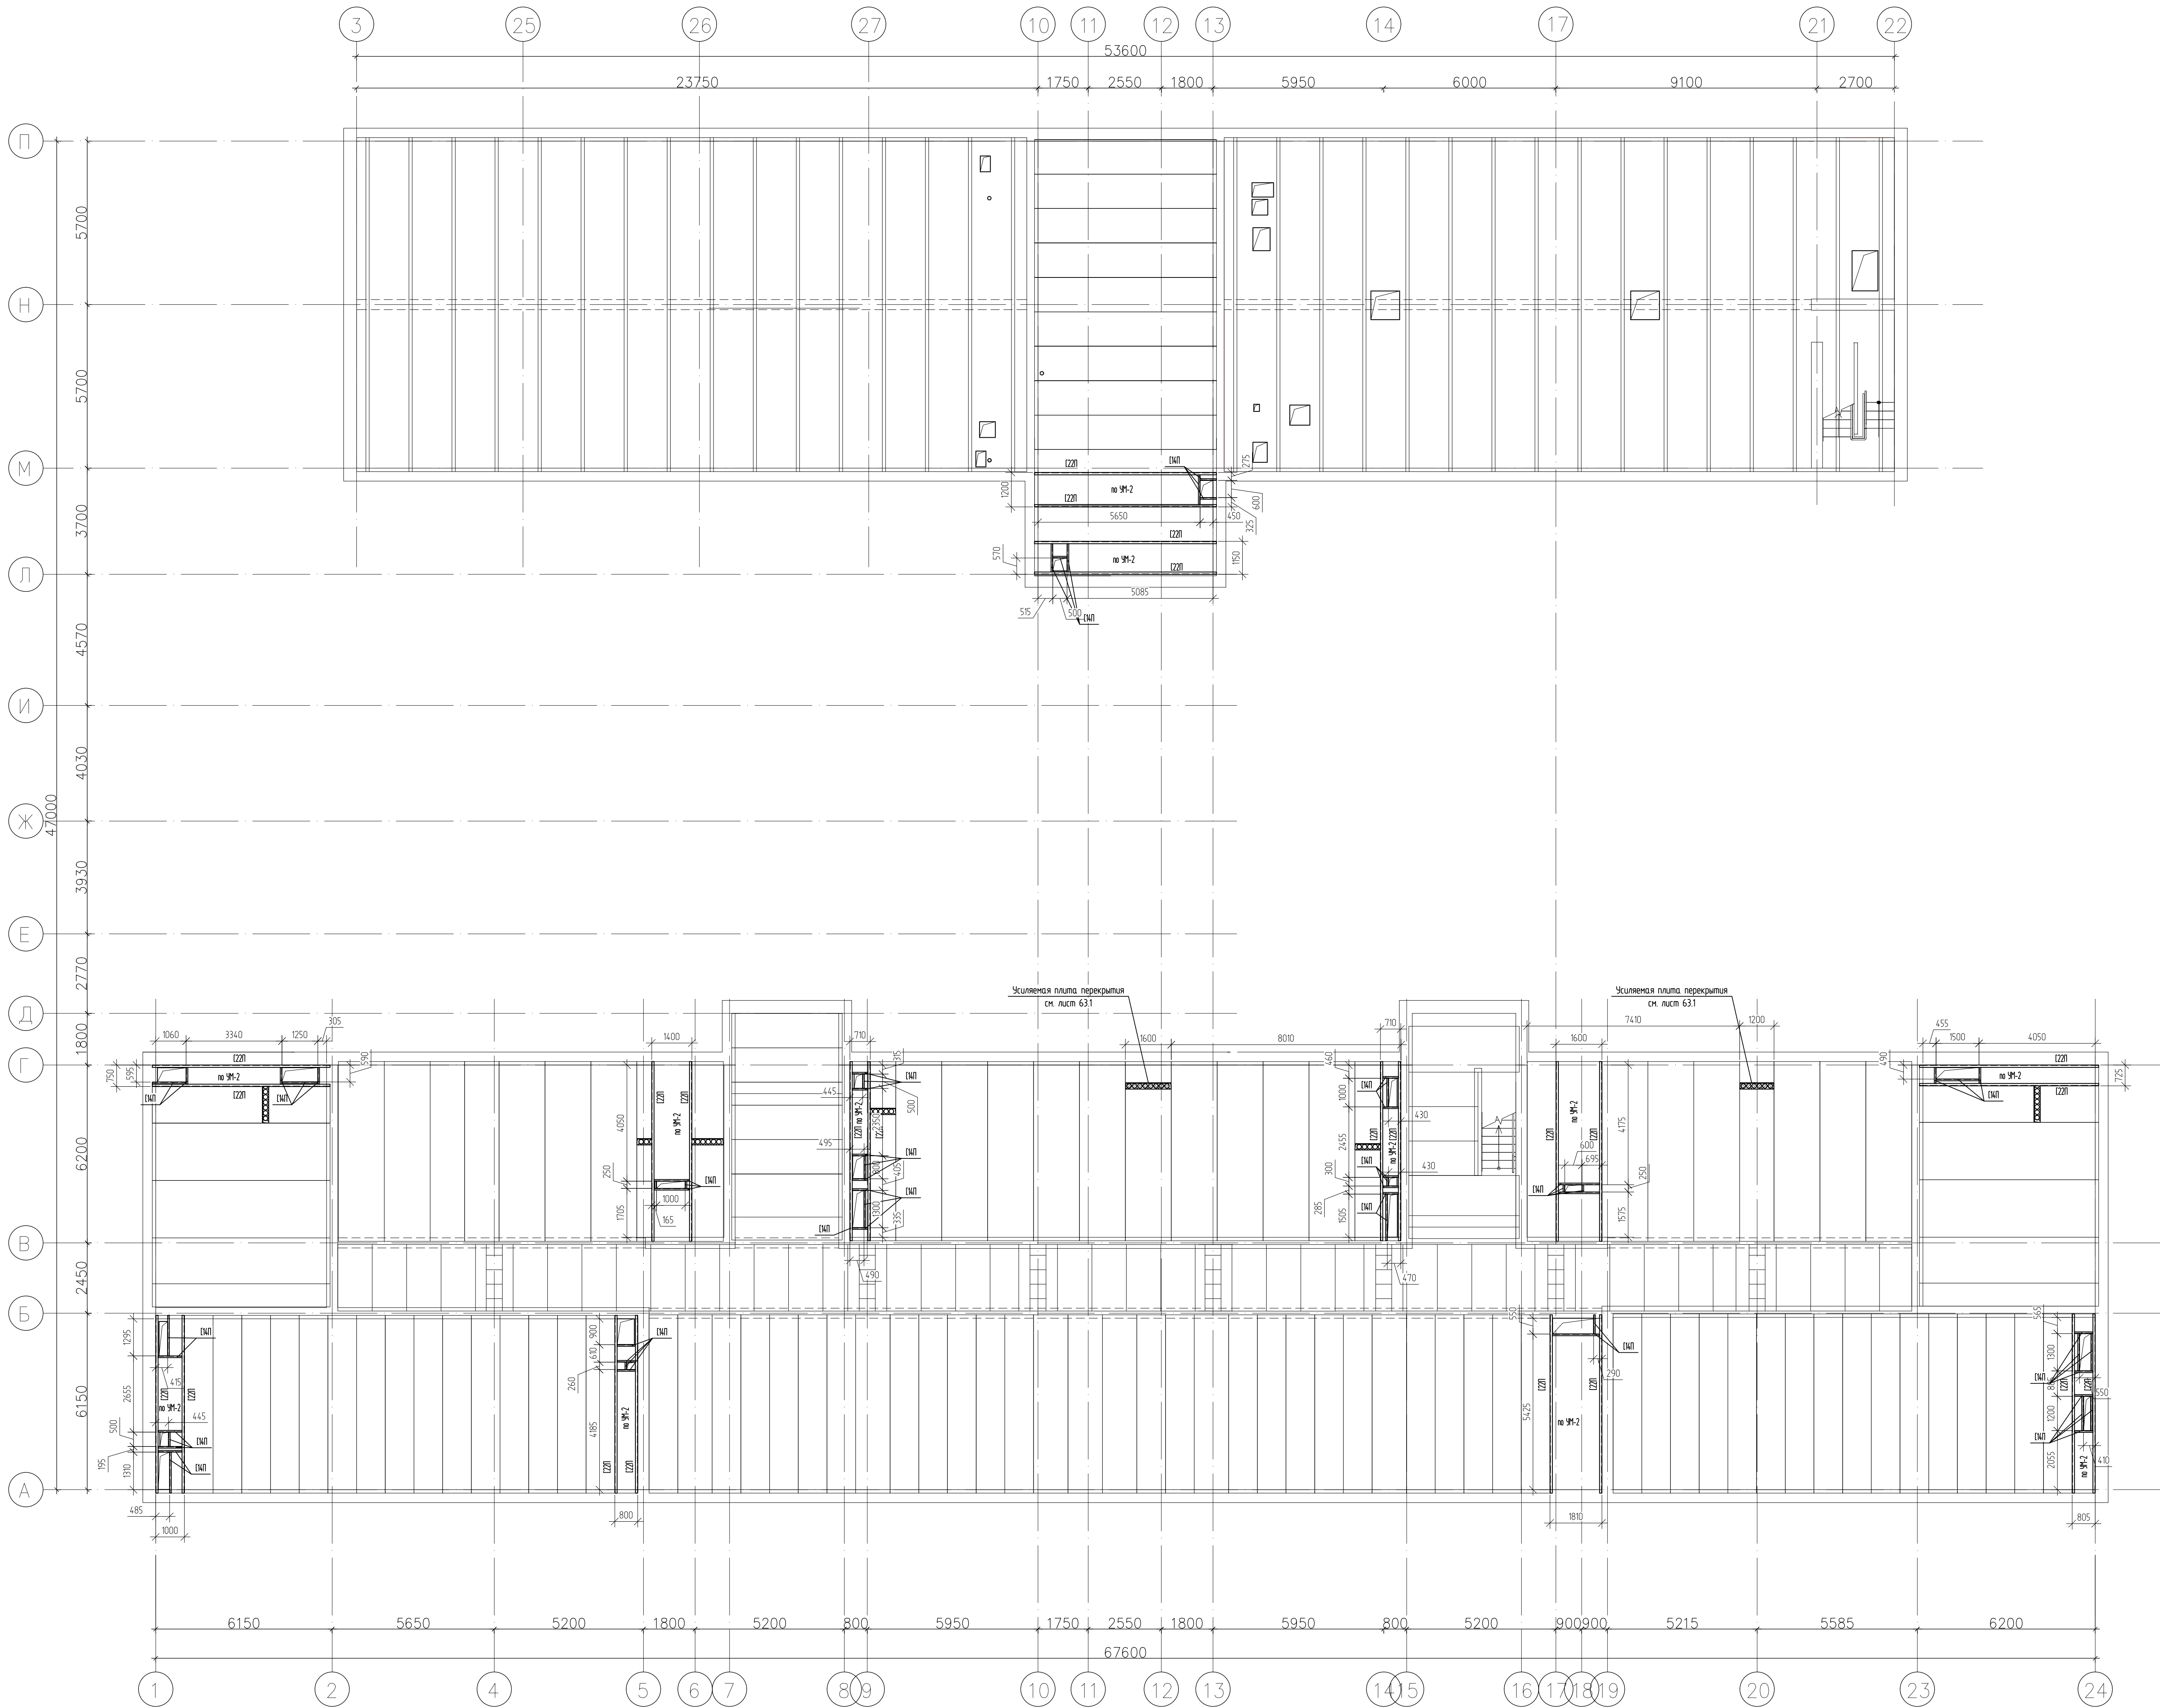

Условные обозначения

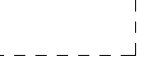-  - отверстия в плите покрытия для прохождения коммуникаций
-  - места прохода мелкогабаритных коммуникаций (СС, ЭОМ и т.п.).
В многослойных плитах высотой 220мм отв. пробивать в пустотах (159 Ф).
В сплошных плитах отв. пробивать, не затрагивая рабочей арматуры.


Спецификация на монолитные участки в плитах перекрытия 3-го этажа					
Поз.	Обозначение	Наименование	Кол.	Масса, ед. кг	Примечание
	ГОСТ 8240-97	Швеллер 14П, Лобш. м.п.	52,5	12,3	645,8
	ГОСТ 8240-97	Швеллер 22П, Лобш. м.п.	148,8	23,0	3422,4
	ГОСТ 8210-93	Уголок 200х125х12, м.п.	25,5	29,7	758,4
	ГОСТ 24045-2012	Профнастил Н75-750-0,8, м.кв.	71,8	12,5	897,5
	ГОСТ Р 52544-2006	Арм. #8 А500, Лобш. м.п.	724,5	0,5	364,4
	ГОСТ Р 52544-2006	Арм. #10 А500, Лобш. м.п.	370,0	0,8	290,5
	ГОСТ 23279-2012	Сетка 58р1 100х100, м.кв.	71,8	25,0	1795,0
	ГОСТ 22042-76	Шпилька М166х65058016	4,8		
	ГОСТ 5915-70	Гайка М16 -6Н5016	96		
	ГОСТ 6958-70	Шайба 16.01016	96		
		Материалы			
	ГОСТ 26633-2012	Бетон В25 F100 W6, м.куб	7,2		
	ГОСТ 25129-82	Грунт ГФ-021 (б. 2 слоя, расход 100гр/м2), кг	28,0		

- Примечания:
- См. совместно с листом -
 - Выполнить отверстия безударным способом, не повреждая несущие балки плиты ТТ-12.


Таблица 1-24-АИО-КР					
Калькуляция работ и материалов на устройство монолитных участков плит перекрытия 3-го этажа №1017 по адресу: г. Москва, ул. Ждановская, д.32					
Изм.	Исполн.	Лист № док.	Дата	Лист	Листов
Разработчик	Получен	04.26	04.26	Р	62
ГАП	Проектировщик	04.26	04.26	К	62
Исполнитель	Листов	04.26	04.26	С	62
Контроль	Листов	04.26	04.26	С	62
ГАП	Листов	04.26	04.26	С	62
Схема устройства монолитных участков плит перекрытия 3 этажа					
Формат А0					

Согласовано					
Инв. № подл.	Подп. и дата	Взам. инв. №			


Монолитный участок УМ-1

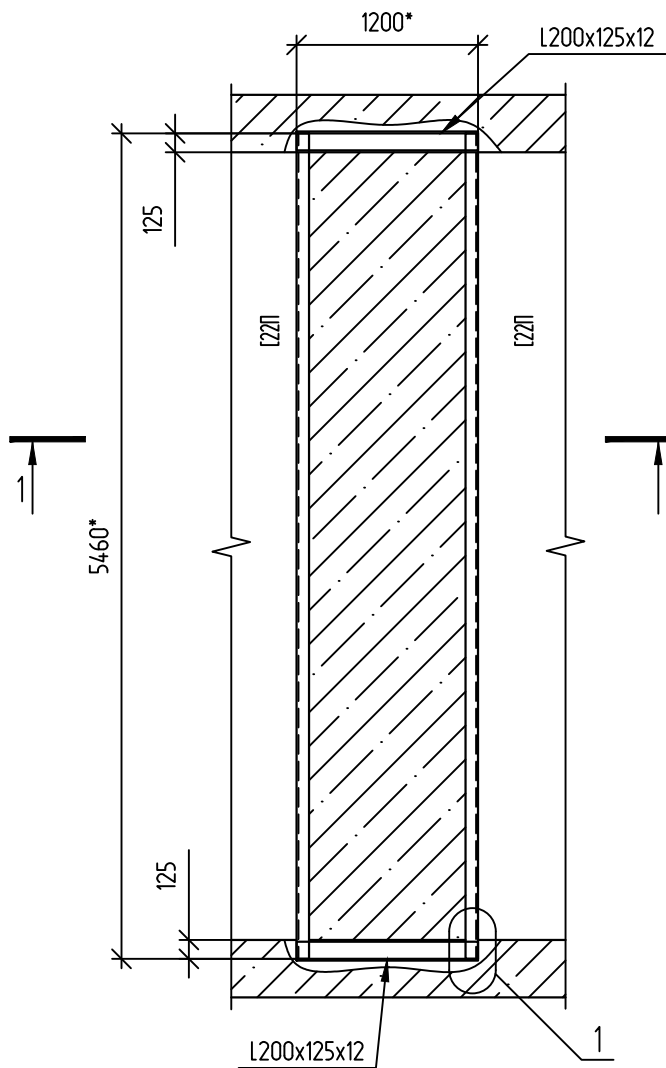


1-1

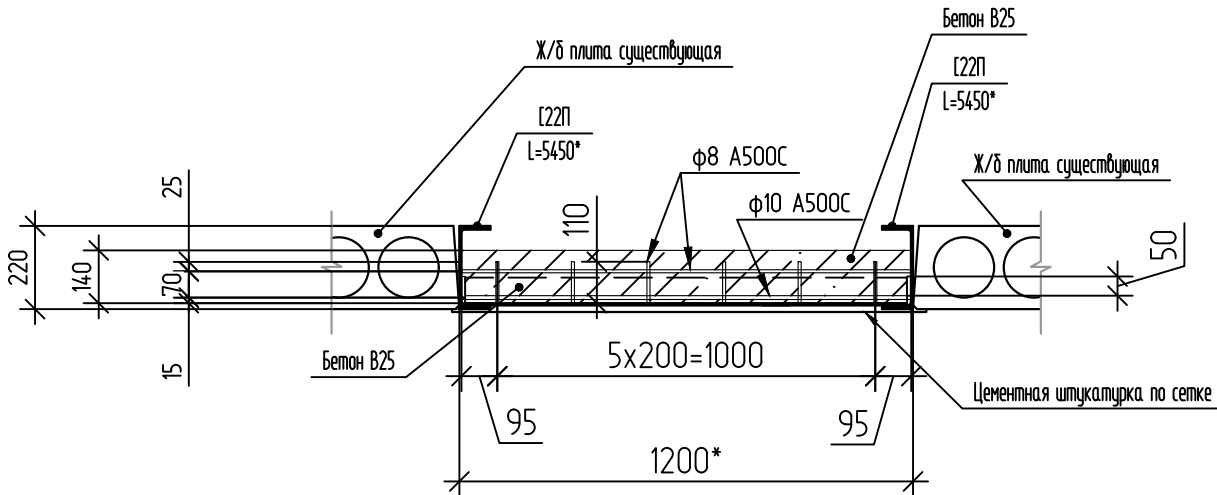


2-2

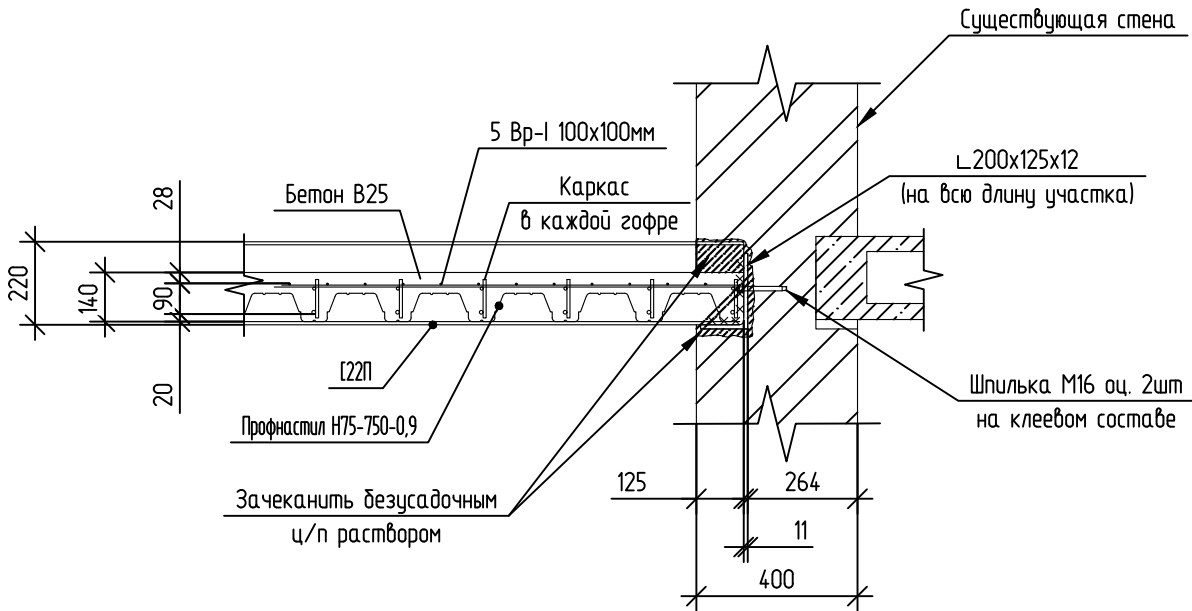


Монолитный участок УМ-2

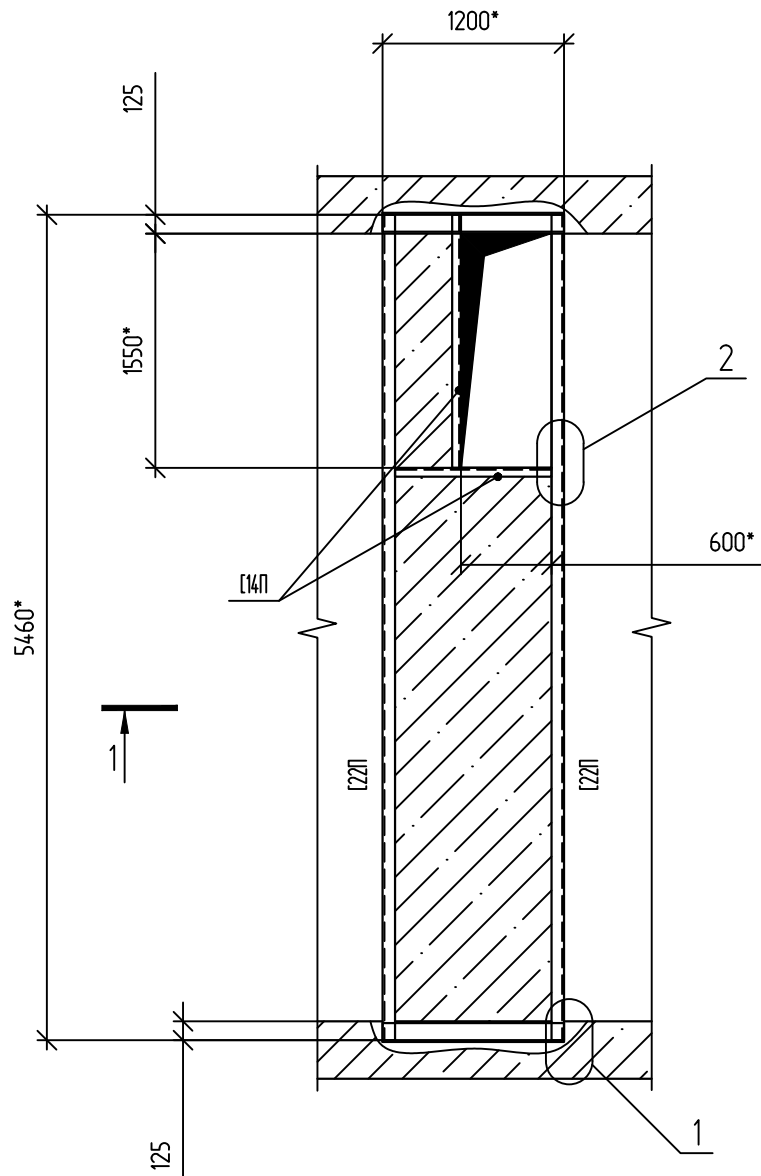


2

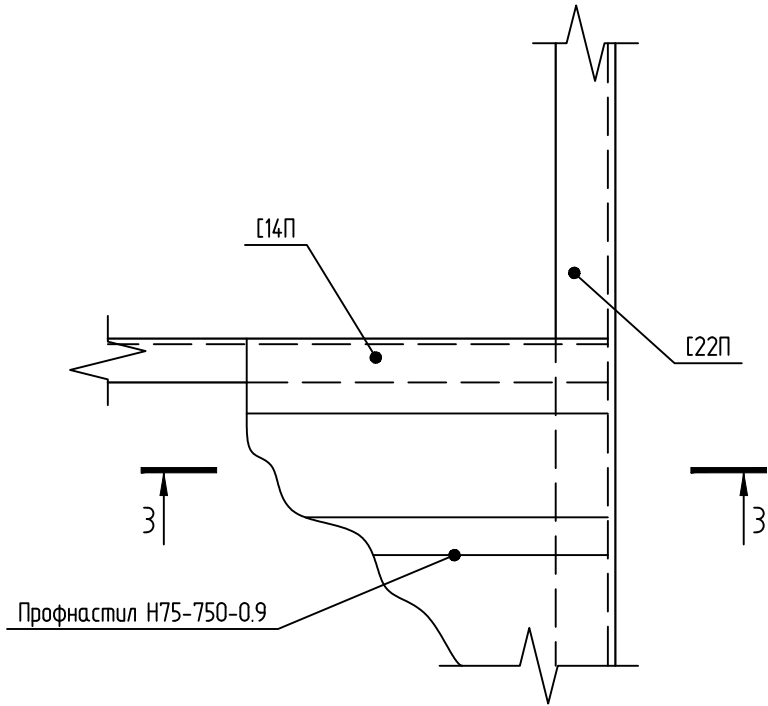

3-3

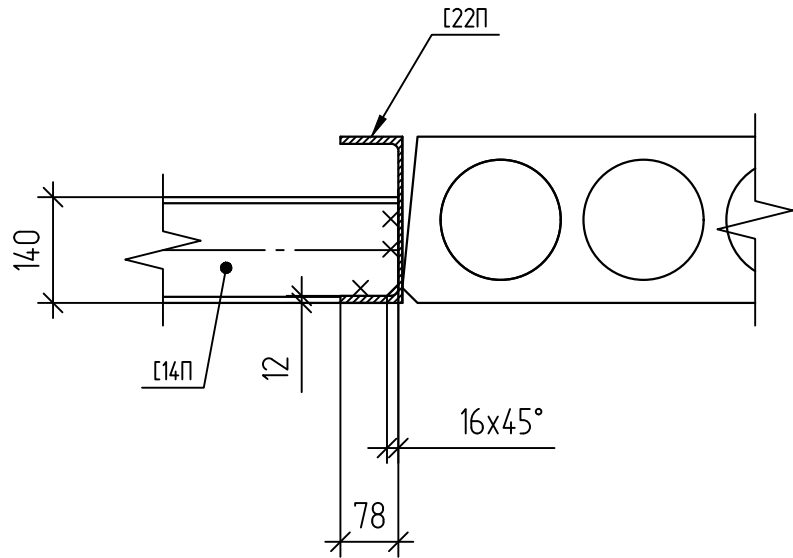

1

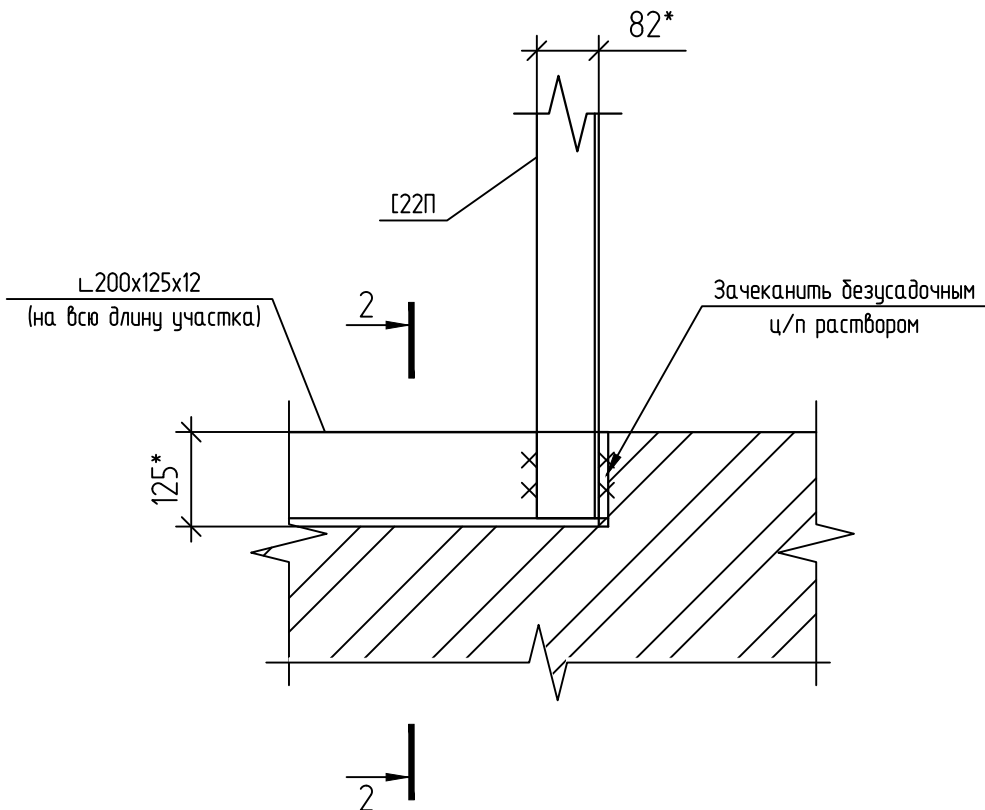

						708/П-24-АНО-КР			
						Капитальный ремонт общеобразовательного учреждения ГБОУ "Школа №1210" по адресу: г. Москва, ул. Живописная, д.32			
Изм.	Колуч.	Лист	№ док.	Подп.	Дата	Конструктивные решения	Стадия	Лист	Листов
Разработал	Торшин	1	Фролова	04.26	04.26		Р	63	
Н.Контроль	Лукашова			04.26	04.26	Монолитные участки УМ-1, УМ-2	 ООО "АРТИС"		
ГИП	Зыкин			04.26	04.26				

Схема устройства усиления плит перекрытия в местах повышенных нагрузок



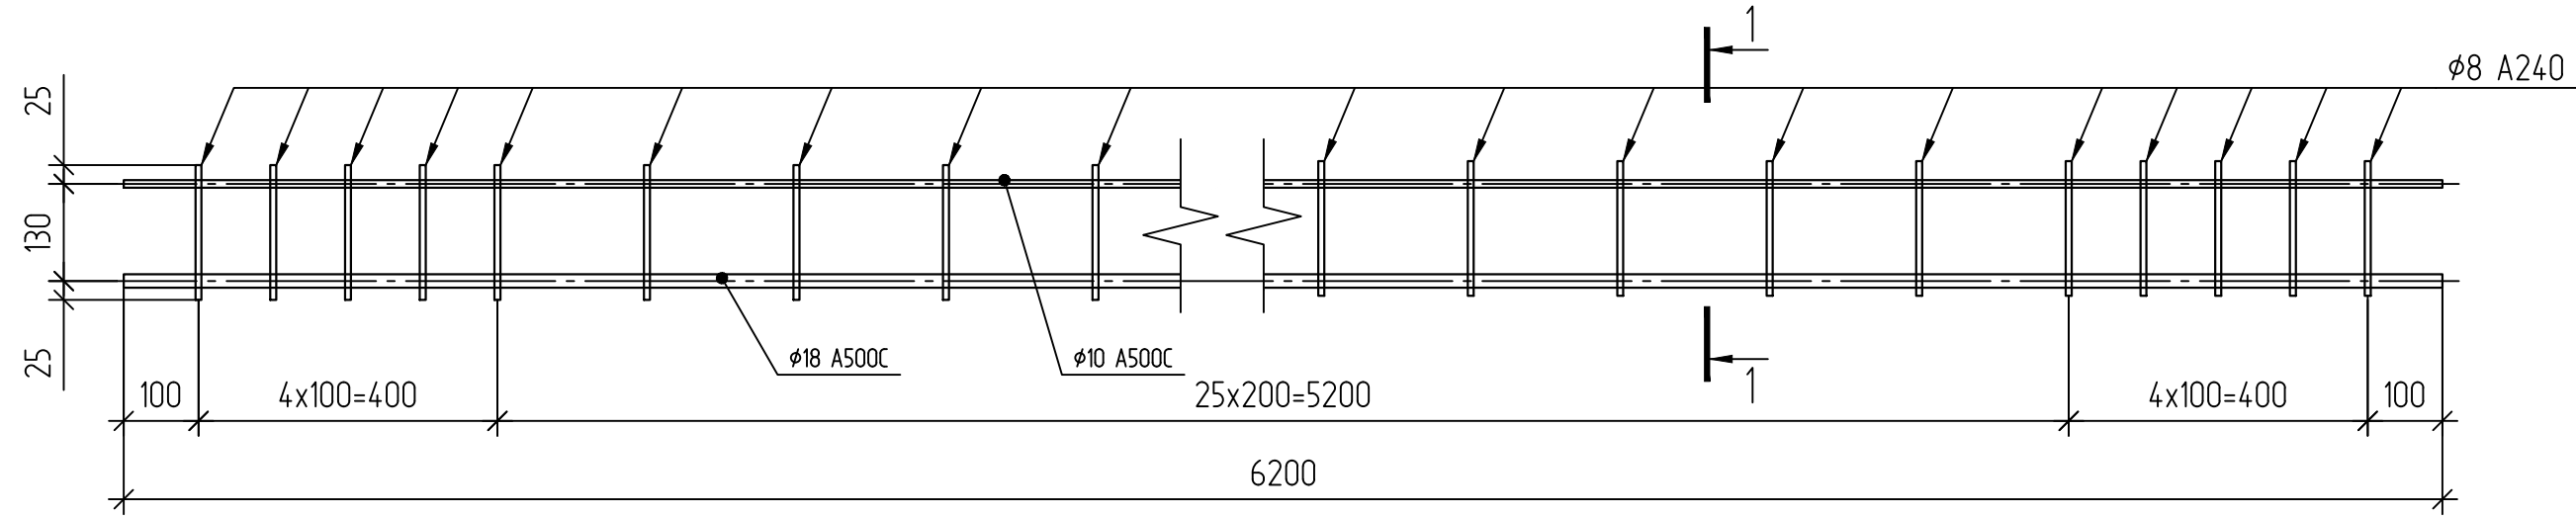


Схема усиления плиты перекрытия




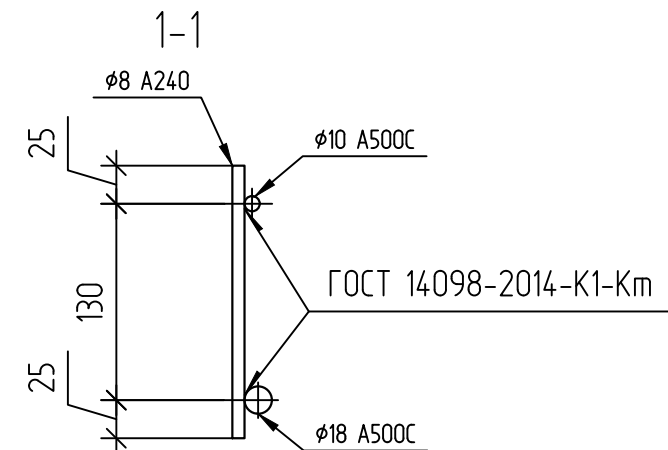
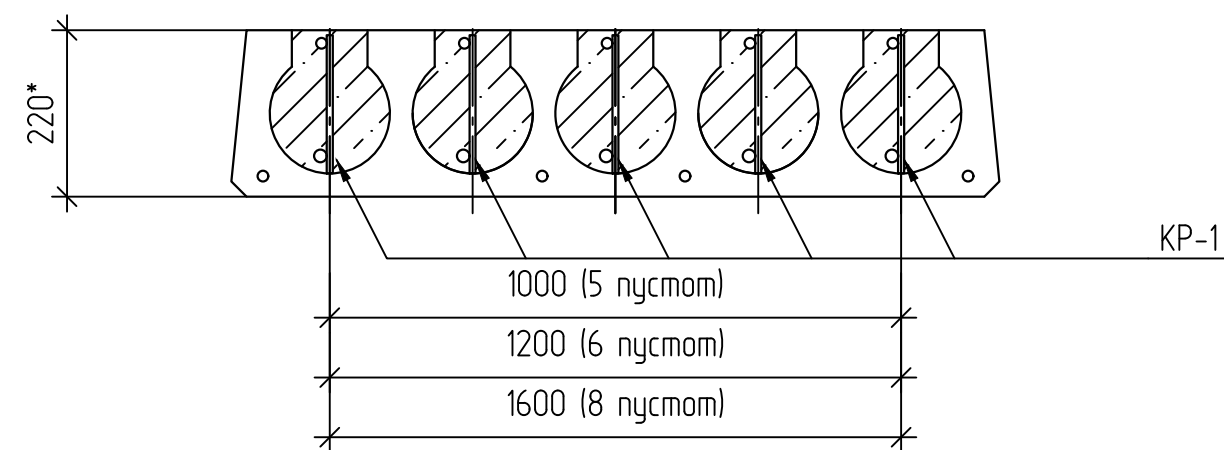


Спецификация материалов на устройство усилений плит перекрытий



Поз.	Обозначение	Наименование	Кол.	Масса, ед. кг	Примечание
		Каркас арматурный КР-1	24	18.74	449,76
1	ГОСТ 34028-2016	Арматура 18 А500С, L=6200	1	12.4	
2	ГОСТ 34028-2016	Арматура 10 А500С, L=6200	1	3.82	
3	ГОСТ 34028-2016	Арматура 8 А240, L=180	36	0,07	2,52
		Материалы			
	ГОСТ 26633-2015	Бетон В25 F150 W6, м³	0.14	24	3,36

1. Усиление плиты производится после ее полной разгрузки - удаляется вся временная нагрузка и конструктивный слой пола.
2. После очистки поверхности плиты пробивают верхнюю полку плиты вдоль пустот шириной 80-100 мм на всю длину плиты. Удаляют разрушенный бетон с поверхности и из пустот. Промывают поверхность плиты и вскрытых пустот водой.
3. Устанавливают в пустоты арматурные каркасы, после этого производят заполнение пустот бетоном класса В25 с последующим виброуплотнением бетонной смеси.
4. Дальнейшие работы производить после набора бетоном усиления прочности 100% от проектной.
5. * Размеры для справок.




708/П-24-АНО-КР					
Капитальный ремонт общеобразовательного учреждения ГБОУ "Школа №1210" по адресу: г. Москва, ул. Живописная, д.32					
Изм.	Кол.уч.	Лист	№ док.	Подп.	Дата
Разработал	Торшин				04.26
ГАП	Фралова				04.26
Н.Контроль	Лукашова				04.26
ГИП	Зыкин				04.26
Конструктивные решения				Стадия	Лист
				Р	63.1
Схема устройства усиления плит перекрытия в местах повышенных нагрузок				ООО "АРТИС"	

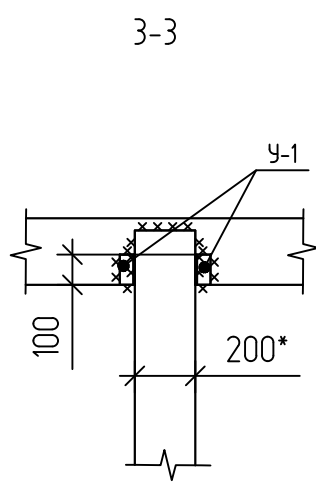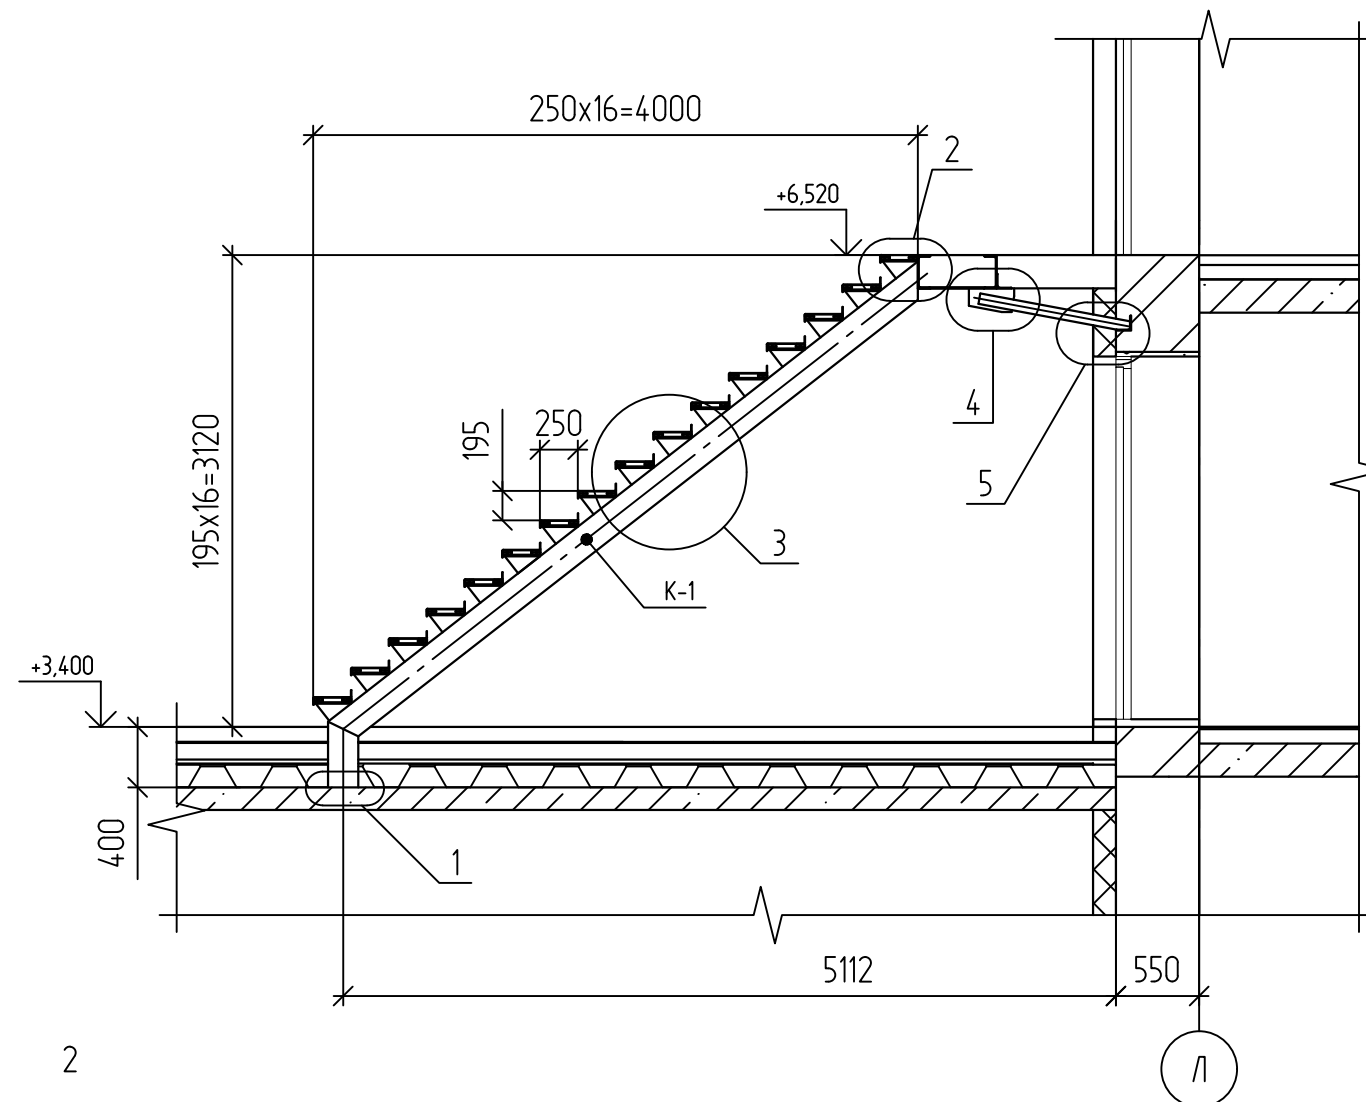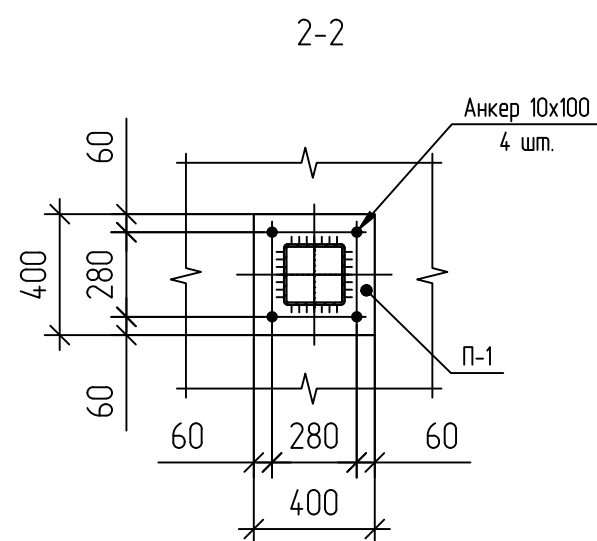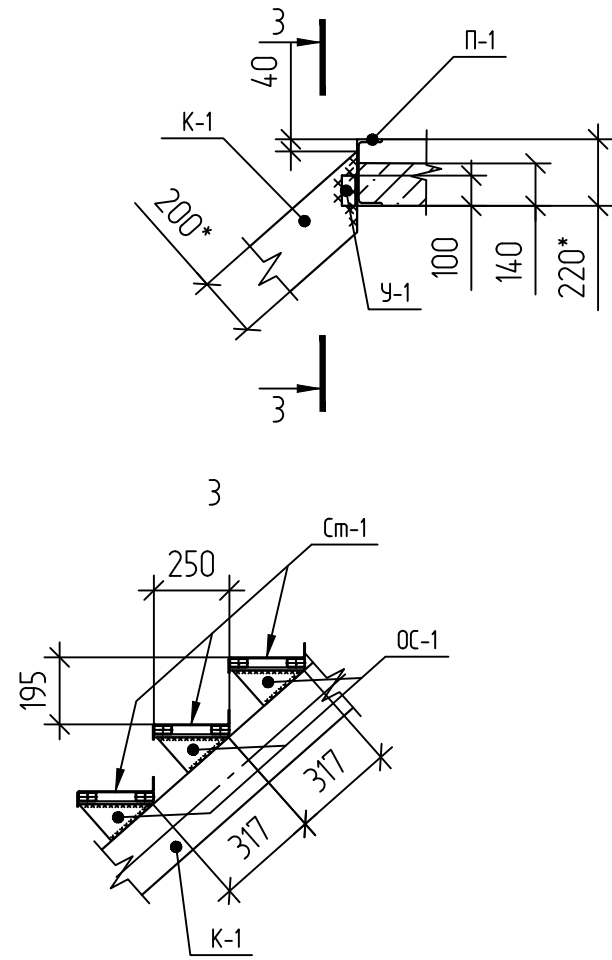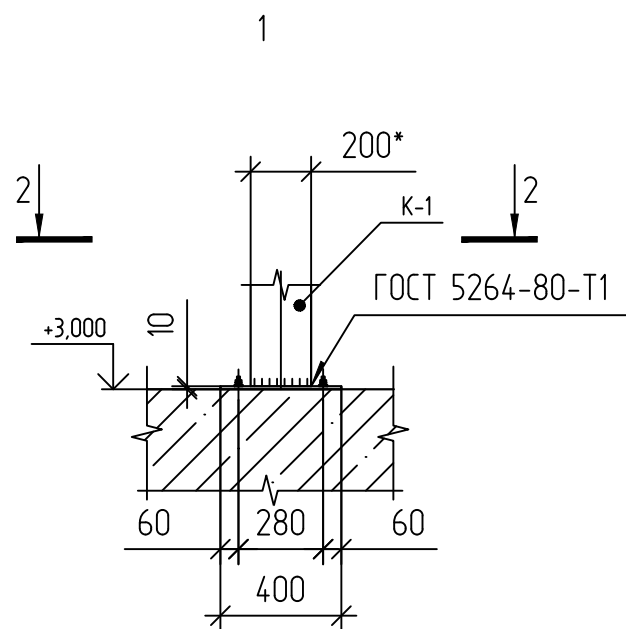[illegible]

Technical drawing of a roof structure showing a gable roof. The roof slope is 15.6 degrees. The horizontal distance is 3902. The vertical distance is 98. The roof length is 4948. The roof width is 200*.

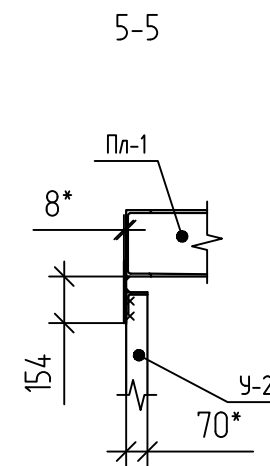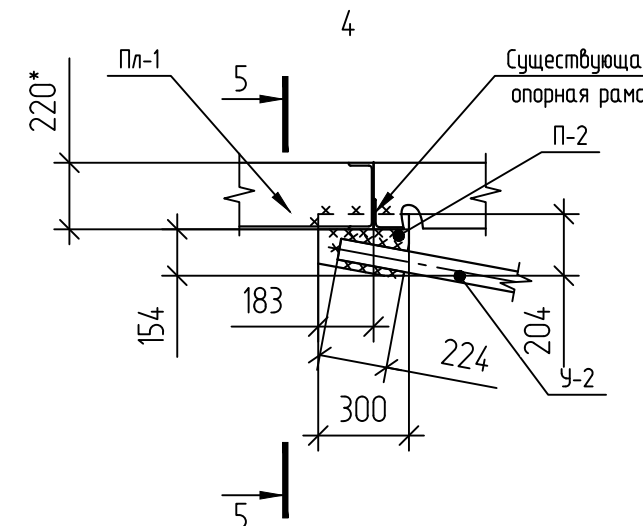

Поз.	Обозначение	Наименование	Кол.	Масса, ед. кг	Приме- чание
К-1	ГОСТ 30245-2003	Профиль 200х200х10, L=5390	1	308	308
ОС-1	ГОСТ 30245-2003	Профиль 200х200х10, L=143	16	8.2	131,2
СТ-1	ГОСТ 30245-2003	Профиль 60х30х4, L=2700	16	13	208
	ГОСТ 19903-2015	Лист 10х250х250	16	5	80
	ГОСТ 8568-77	Лист чечевица 3х350х1100	16	9	144
Пл-1	ГОСТ 8240-97	Швеллер 22, L=3740	1	78	78.0
	ГОСТ 8568-77	Лист чечевица 3х550х1620	1	21	21
У-1	ГОСТ 8509-93	Уголок 50х5, L=100	2	0,5	1.0
У-2	ГОСТ 8509-93	Уголок 70х6, L=1000	2	6,5	13.0
У-3	ГОСТ 8509-93	Уголок 100х7, L=200	2	2	4.0
П-1	ГОСТ 19903-2015	Лист 10х400х400	1	12	12
П-2	ГОСТ 19903-2015	Лист 8х300х204	2	4	8

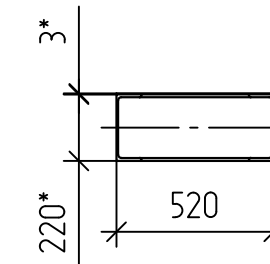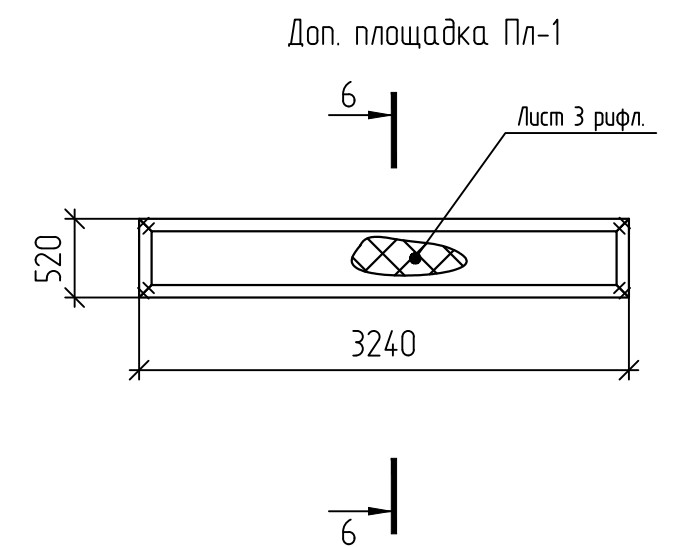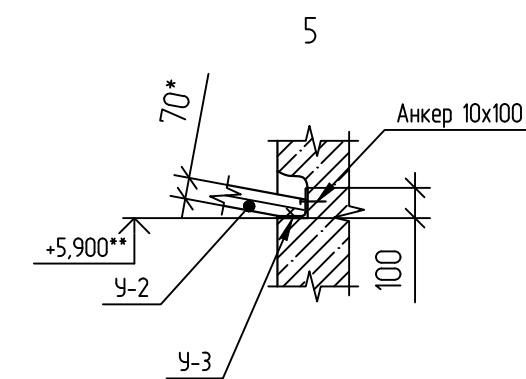

1. Материал конструкции - сталь С-245 ГОСТ
2. Неуказанные предельные отклонения формы и расположения - по ГОСТ 23118-2012.
3. Сварные соединения - по ГОСТ 5264-80. Электроды - Э-42 по ГОСТ 9467-75.
Величина катета шва - по минимальной толщине детали.
4. * Размеры для справок.
5. **Размеры уточнить по месту
6. Готовую лестницу окрасить двумя слоями эмали ПФ-115 ГОСТ 6465-76 по одному слою грунта ГФ-021 ГОСТ 25129-82.

						708/П-24-АНО-КР			
						Капитальный ремонт общеобразовательного учреждения ГБОУ "Школа №1210" по адресу: г. Москва, ул. Жилищная, д.32			
Изм.	Колуч.	Лист	№ док.	Подп.	Дата	Конструктивные решения	Стадия	Лист	Листов
Разработал	Торшин				04.26		Р	64	
ГАП	Фролова				04.26				
						Лестница 1 л в осях 11-12/М-Л на отм. +6.400		комплексное проектирование промышленных и гражданских объектов	ООО "АРТИС"
НКонтроль	Лукашова				04.26				
ГИП	Зыкин				04.26				

Лестница Л-1 в осях 10-11/Д-Ж на отм. +3.460



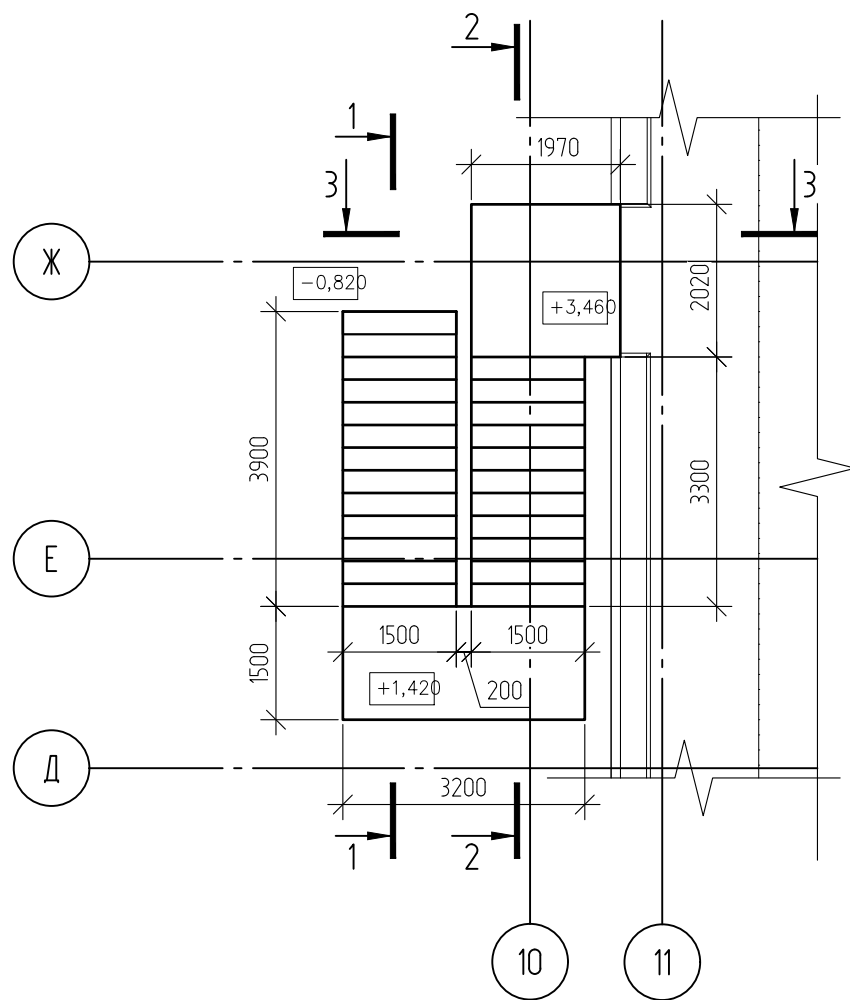


Схема несущих косоуров лестница Л-1 в осях 10-11/Д-Ж

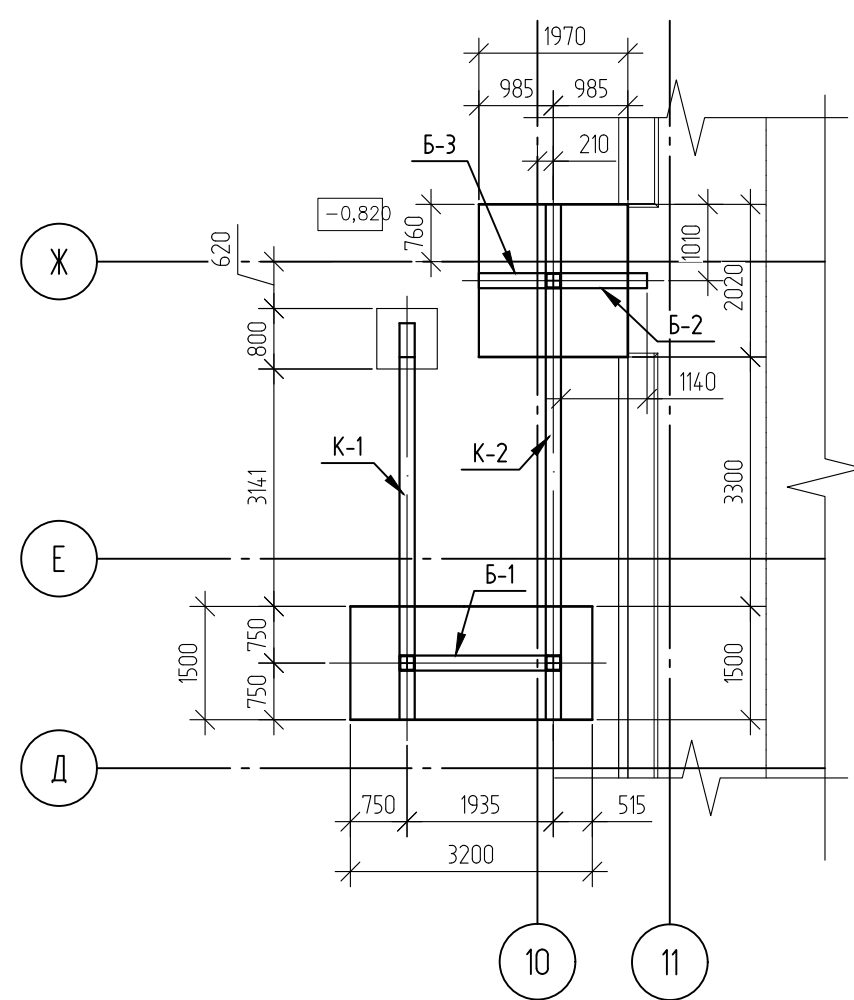


План фундаментов на отм. -0.850

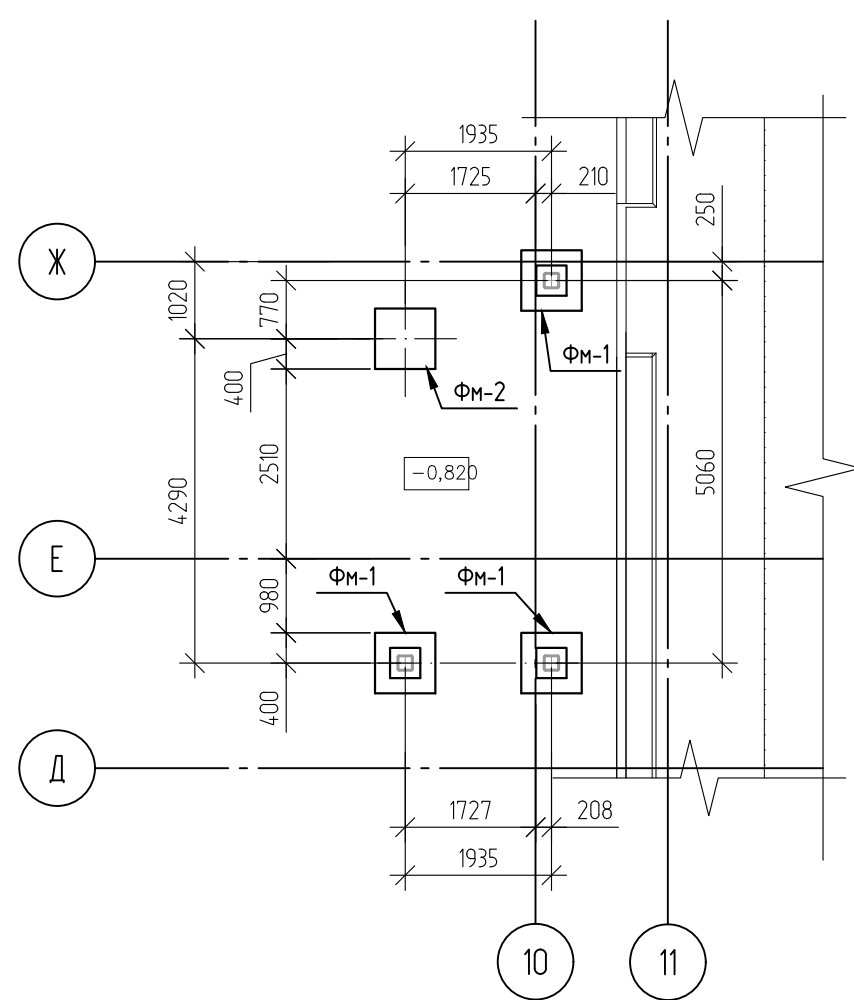

Лист чечевица -5 мм
Рама ступени из трубы 70x50x5 ГОСТ 30245-2003
Косоур из трубы 200x10 ГОСТ 30245-2003


1-1

Лист чечевица -5 мм
Рама из трубы 80x60x5 ГОСТ 30245-2003
Косоур из трубы 200x10 ГОСТ 30245-2003

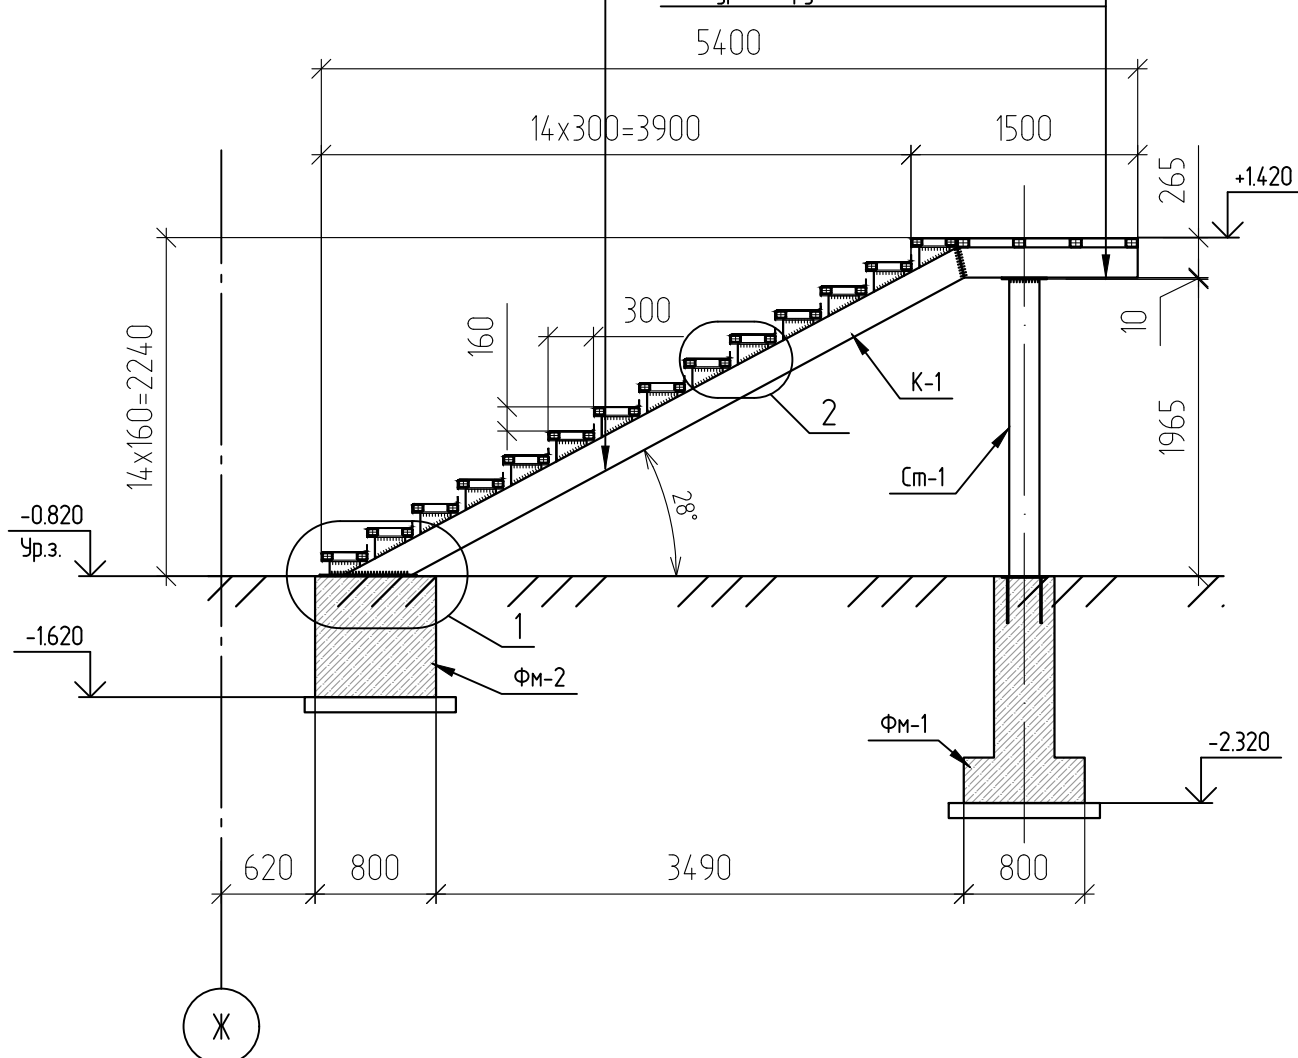


Лист чечевица -5 мм
Рама из трубы 80x60x5 ГОСТ 30245-2003
Косоур из трубы 200x10 ГОСТ 30245-2003

2-2

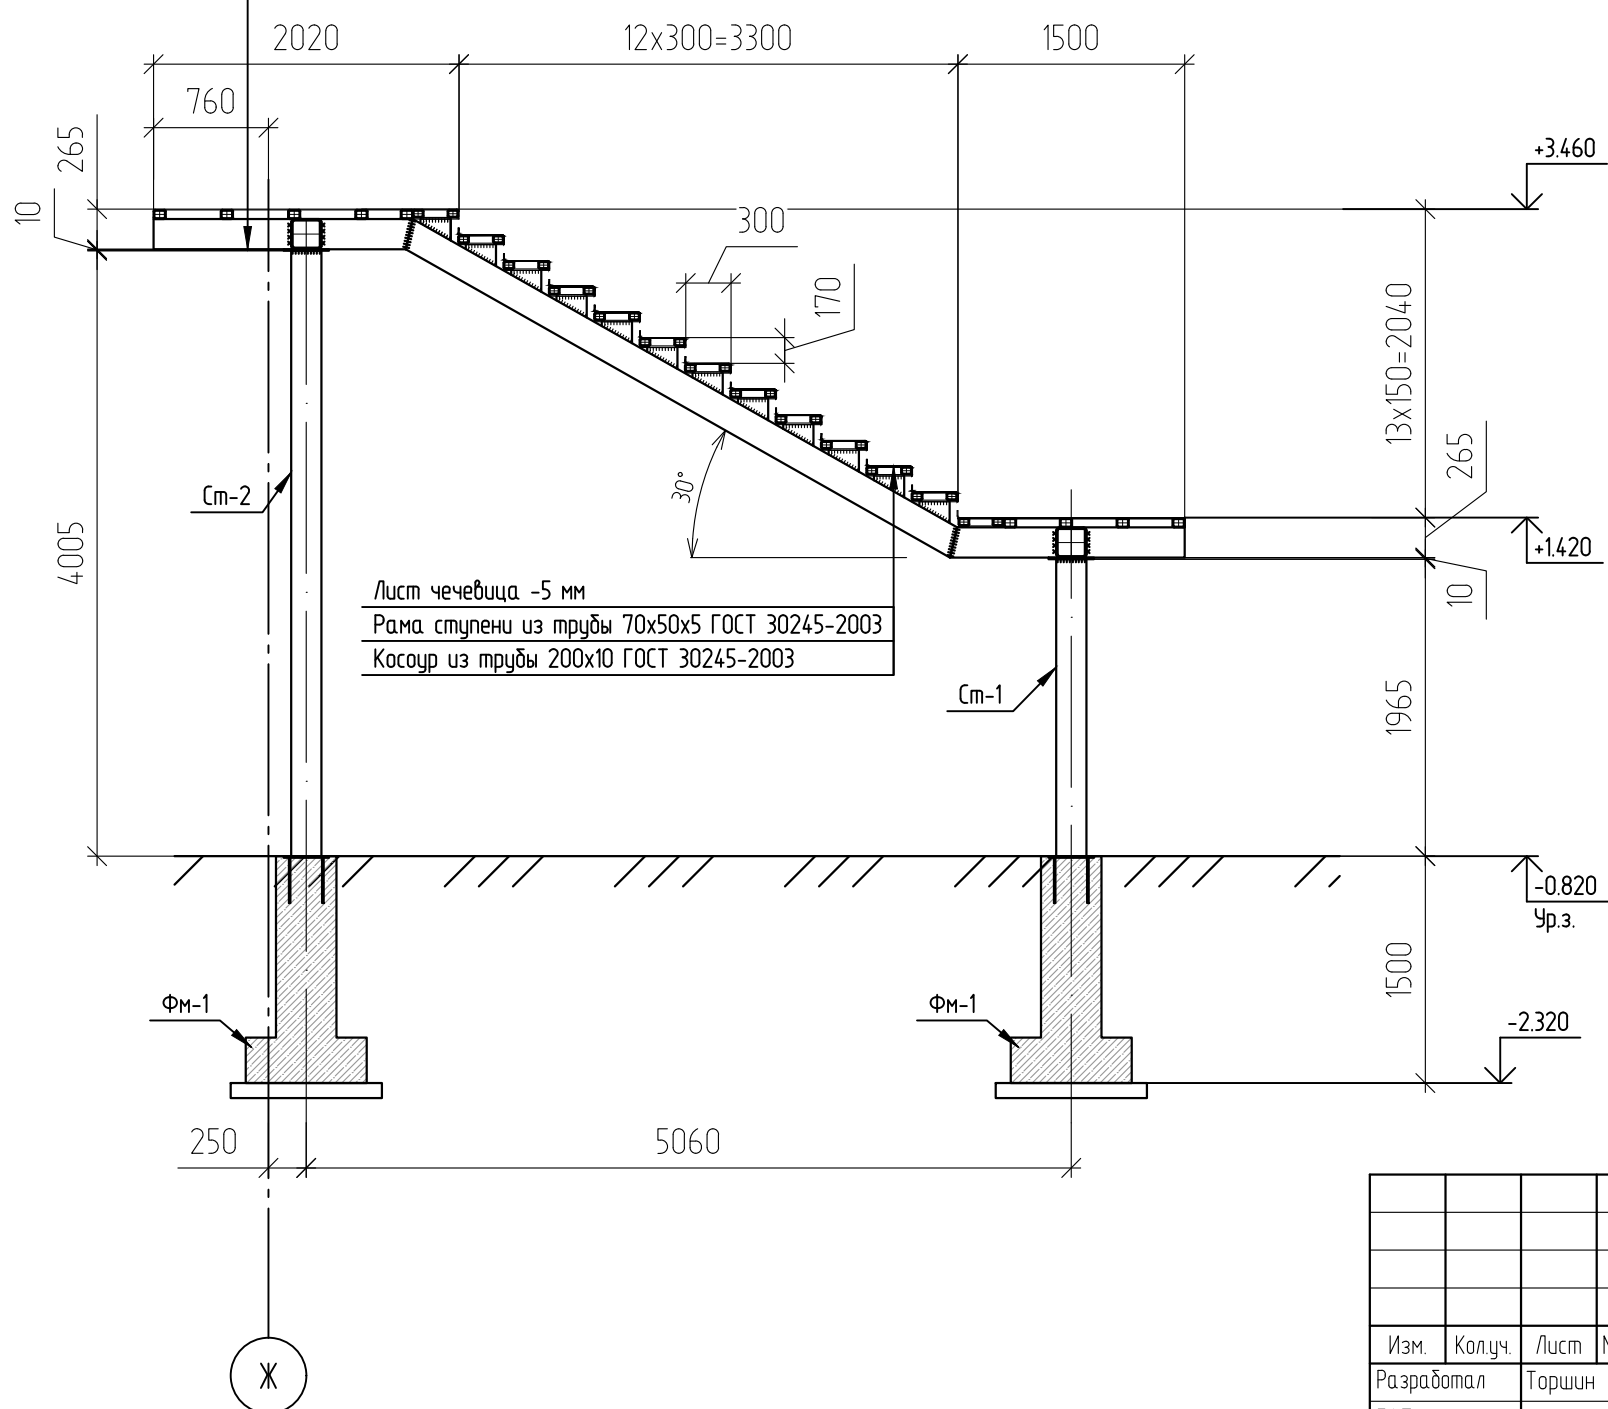





Лист чечевица -5 мм
Рама ступени из трубы 70x50x5 ГОСТ 30245-2003
Косоур из трубы 200x10 ГОСТ 30245-2003

3-3

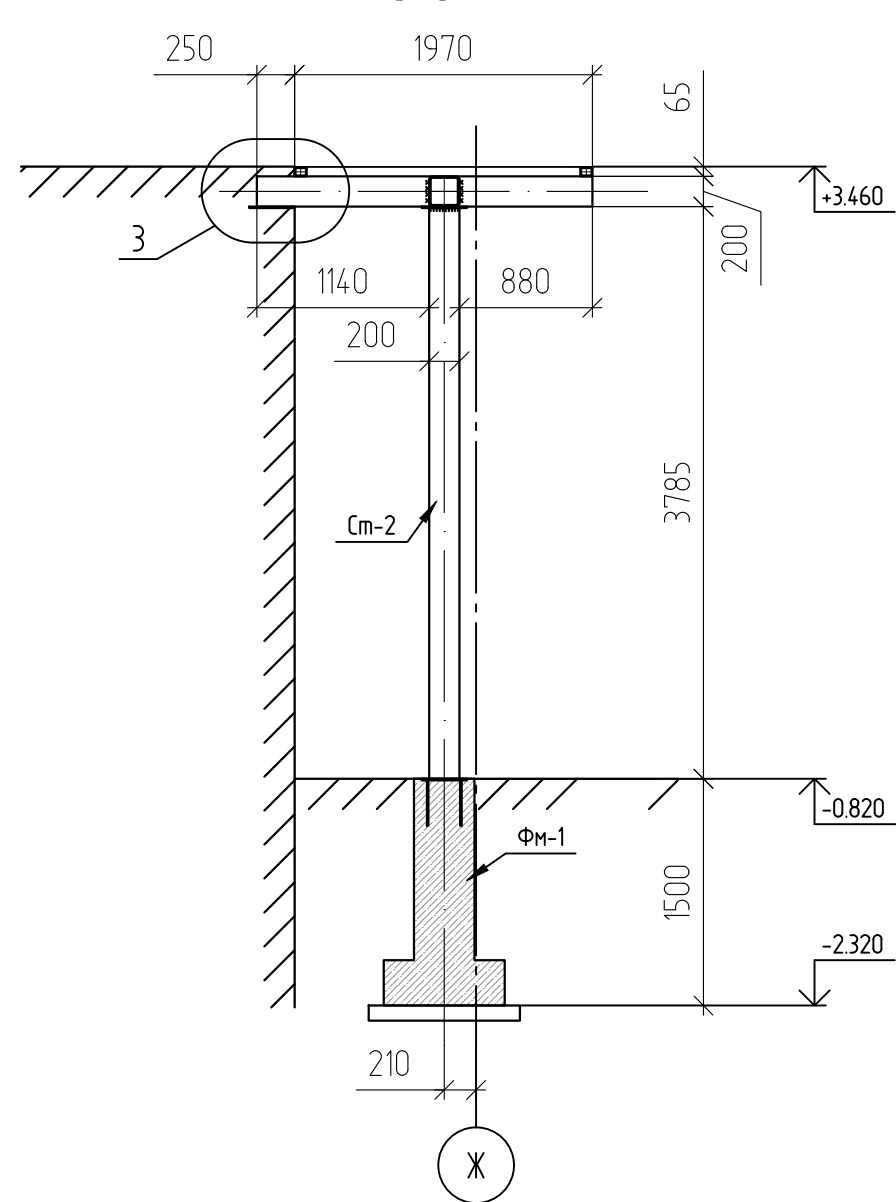

						708/П-24-АНО-КР			
						Капитальный ремонт общеобразовательного учреждения ГБОУ "Школа №1210" по адресу: г. Москва, ул. Живописная, д.32			
Изм.	Колуч.	Лист	№ док.	Подп.	Дата	Конструктивные решения	Стадия	Лист	Листов
Разработал	Торшин				04.26		Р	65	
ГАП	Фролова				04.26				
						Лестница Л-1 в осях 10-11/Д-Ж на отм. +3.460		ООО "АРТИС"	
Н.Контроль	Лукашова				04.26				
ГИП	Зыкин				04.26				

Согласовано			
Инф. № подл.	Подп. и дата	Взам. инф. №	

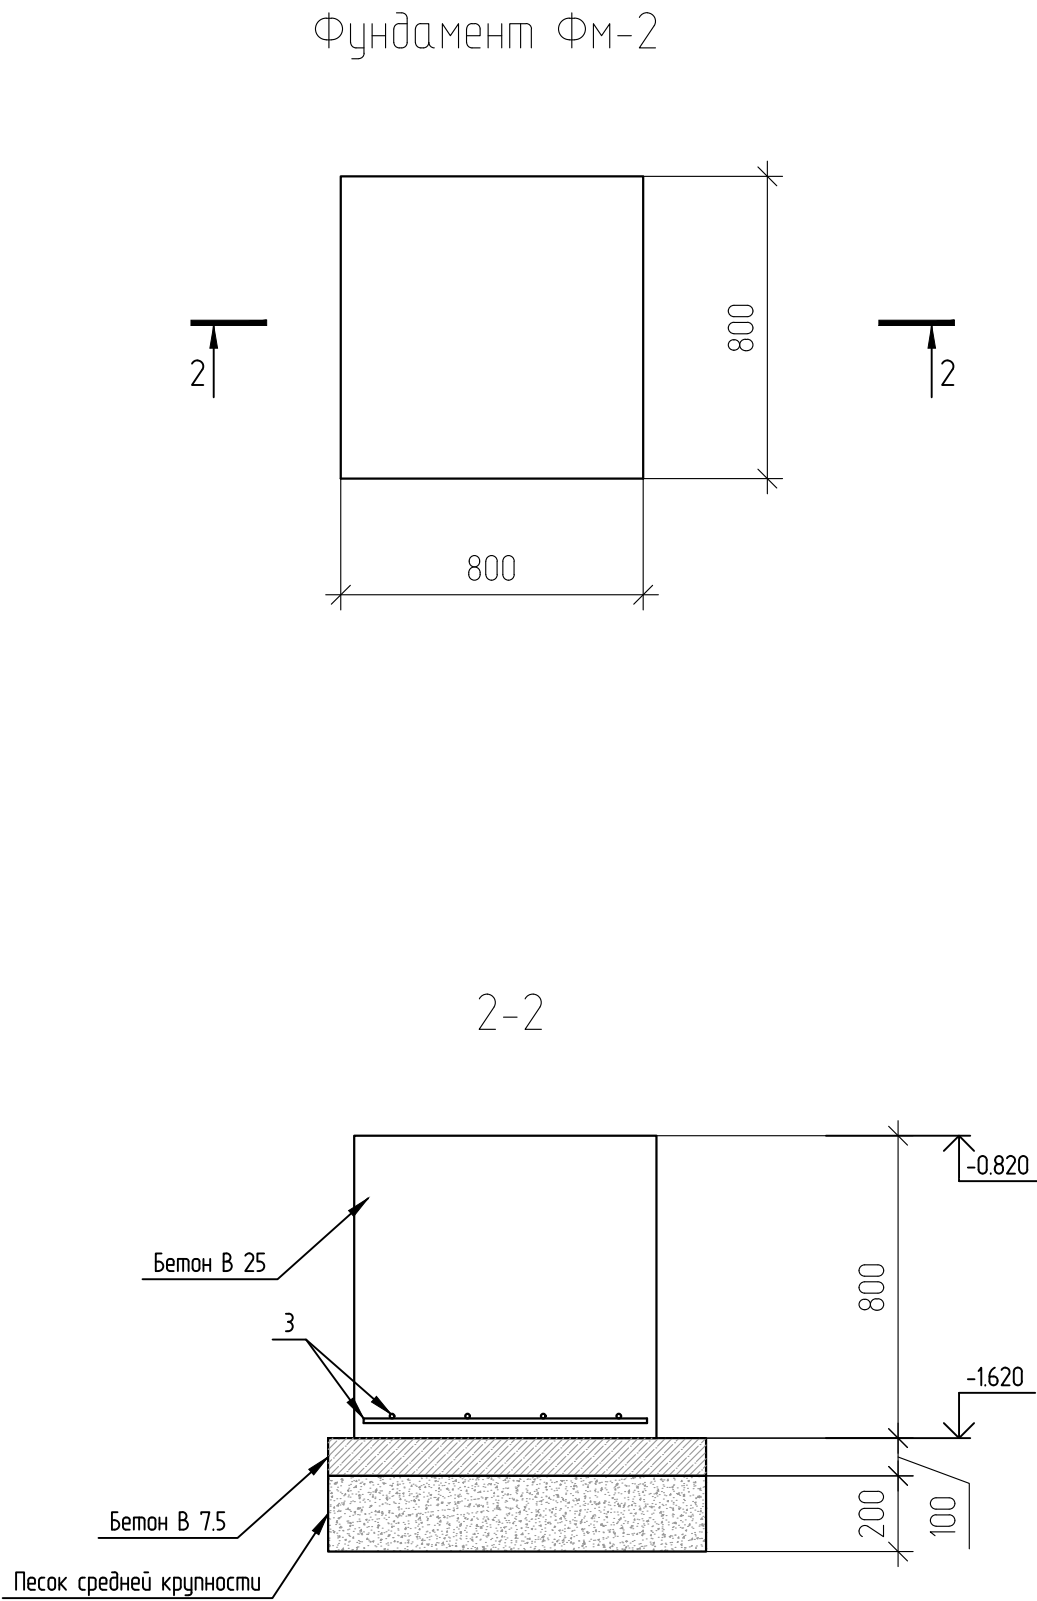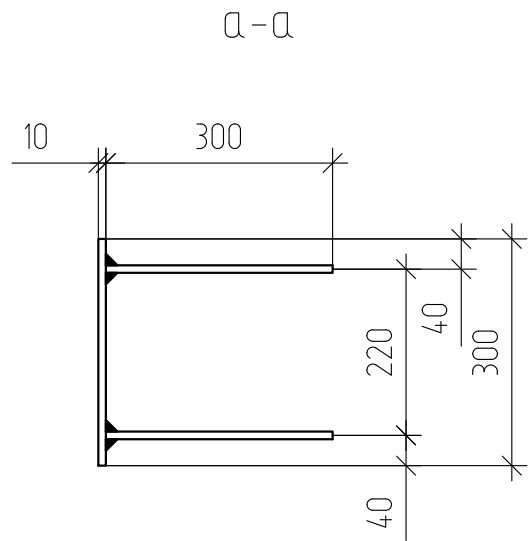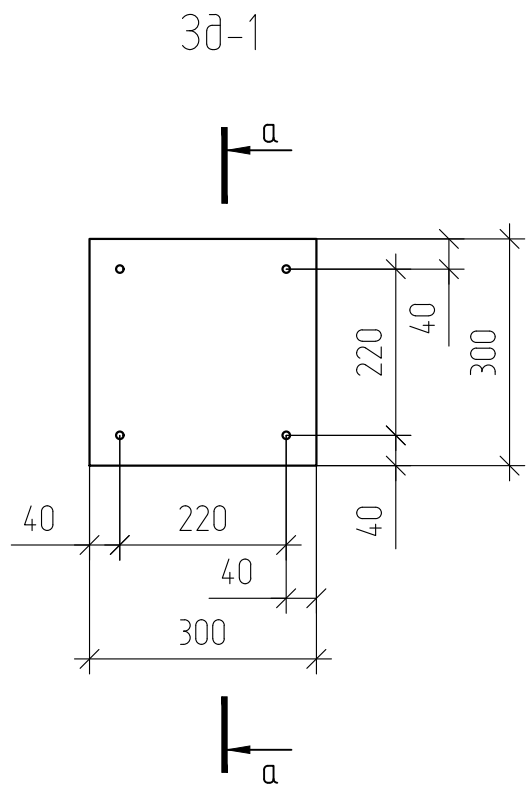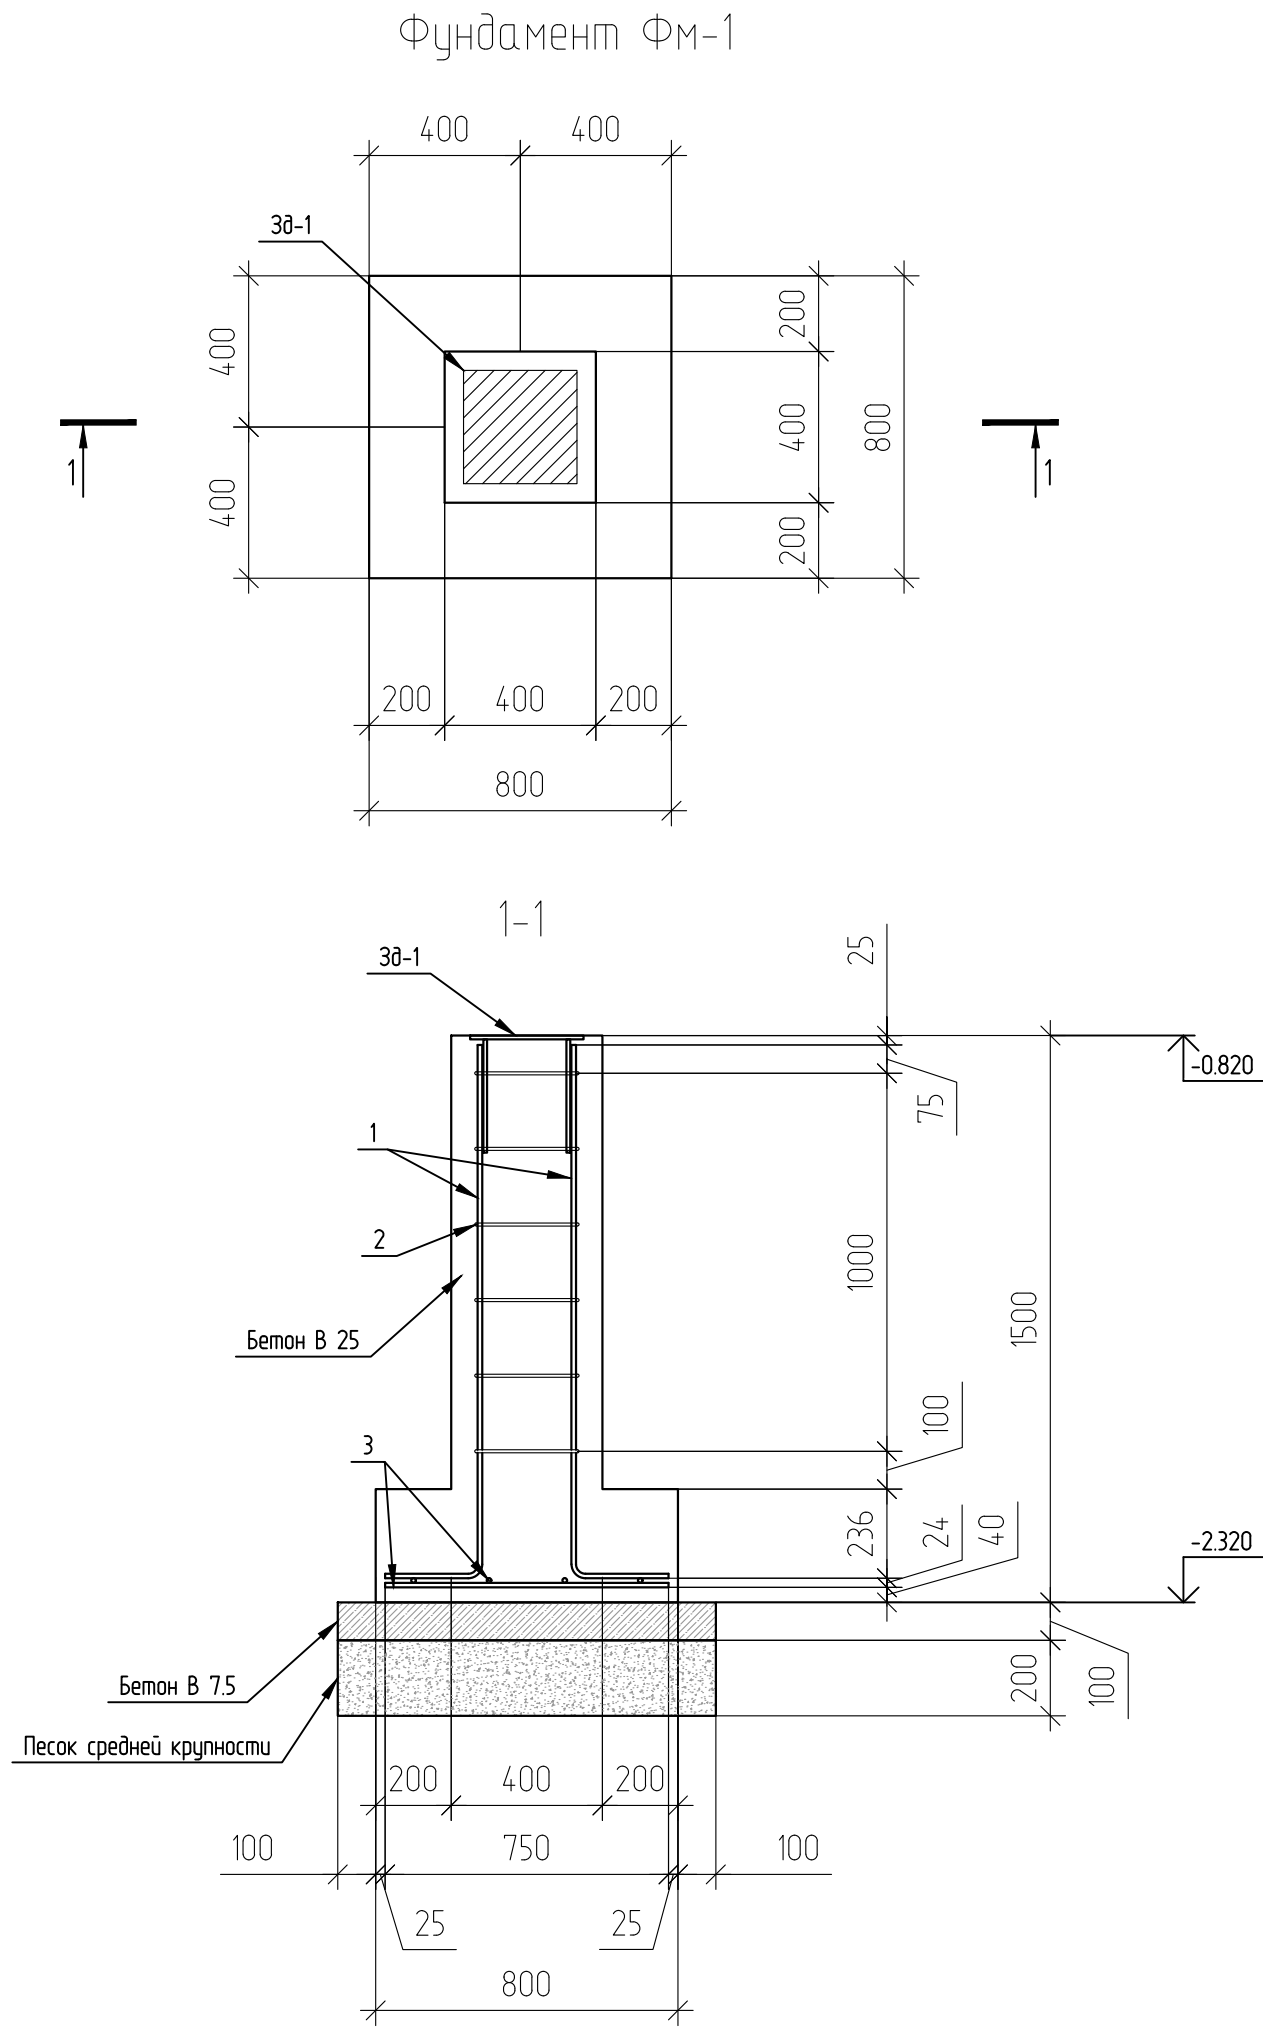


Поз.	Обозначение	Наименование	Кол.	Масса, ед. кг	Примечание
ФМ-1		Фундамент ФМ-1	3		
1	ГОСТ 34028-2016	Пруток МД-12-А500С L=1630мм	4	1,44	5,76
2	ГОСТ 34028-2016	Пруток МД-8-А240 L=1220мм	6	0,48	2,88
3	ГОСТ 34028-2016	Пруток МД-12-А500С L=750мм	8	0,67	5,36
		Материалы			
	ГОСТ 26633-2012	Бетон В25 F200 W6, м.куб.	0,4		
	ГОСТ 26633-2012	Подбетонка Бетон В7,5 , м.куб.	0,1		
		Праймер битумный Технониколь №01, м2.	3,6		
		Мастика Технониколь AquaMast, м2.	3,6		
ФМ-2		Фундамент ФМ-2	1		
3	ГОСТ 34028-2016	Пруток МД-12-А500С L=750мм	8	0,67	5,36
		Материалы			
	ГОСТ 26633-2012	Бетон В25 F200 W6, м.куб.	0,51		
	ГОСТ 26633-2012	Подбетонка Бетон В7,5 , м.куб.	0,1		
		Праймер битумный Технониколь №01, м2.	2,6		
		Мастика Технониколь AquaMast, м2.	2,6		
3d-1		Закладная 3d-1			
1а	ГОСТ 103-2006	Полоса 10х300, С245 ГОСТ 27772-2015. L=250мм	1	4,71	
2а	ГОСТ 34028-2016	Пруток МД-10-А500С L=300мм	4	0,19	0,76

						708/П-24-АНО-КР			
						Капитальный ремонт общеобразовательного учреждения ГБОУ "Школа №1210" по адресу: г. Москва, ул. Живописная, д.32			
Изм.	Колуч.	Лист	№ док.	Подп.	Дата	Конструктивные решения	Стадия	Лист	Листов
Разработал	Торшин				04.26		Р	66	
ГАП	Фролова				04.26				
						Фундамент ФМ-1, ФМ-2		комплексное проектирование промышленных и гражданских объектов ООО "АРТИС"	
Н.Контроль	Лукашова				04.26				
ГИП	Зыкин				04.26				



A bar chart with four bars representing different age groups. The first bar is the tallest, followed by the second, third, and fourth bars in descending order of height.

Согласовано			
Изм.	Кол.	Лист	№ док.
Разработал	Торшин	Подп.	Дата
ГАП	Фралова	Подп.	Дата
Н.Контроль	Лукашова	Подп.	Дата
ГИП	Зыкин	Подп.	Дата

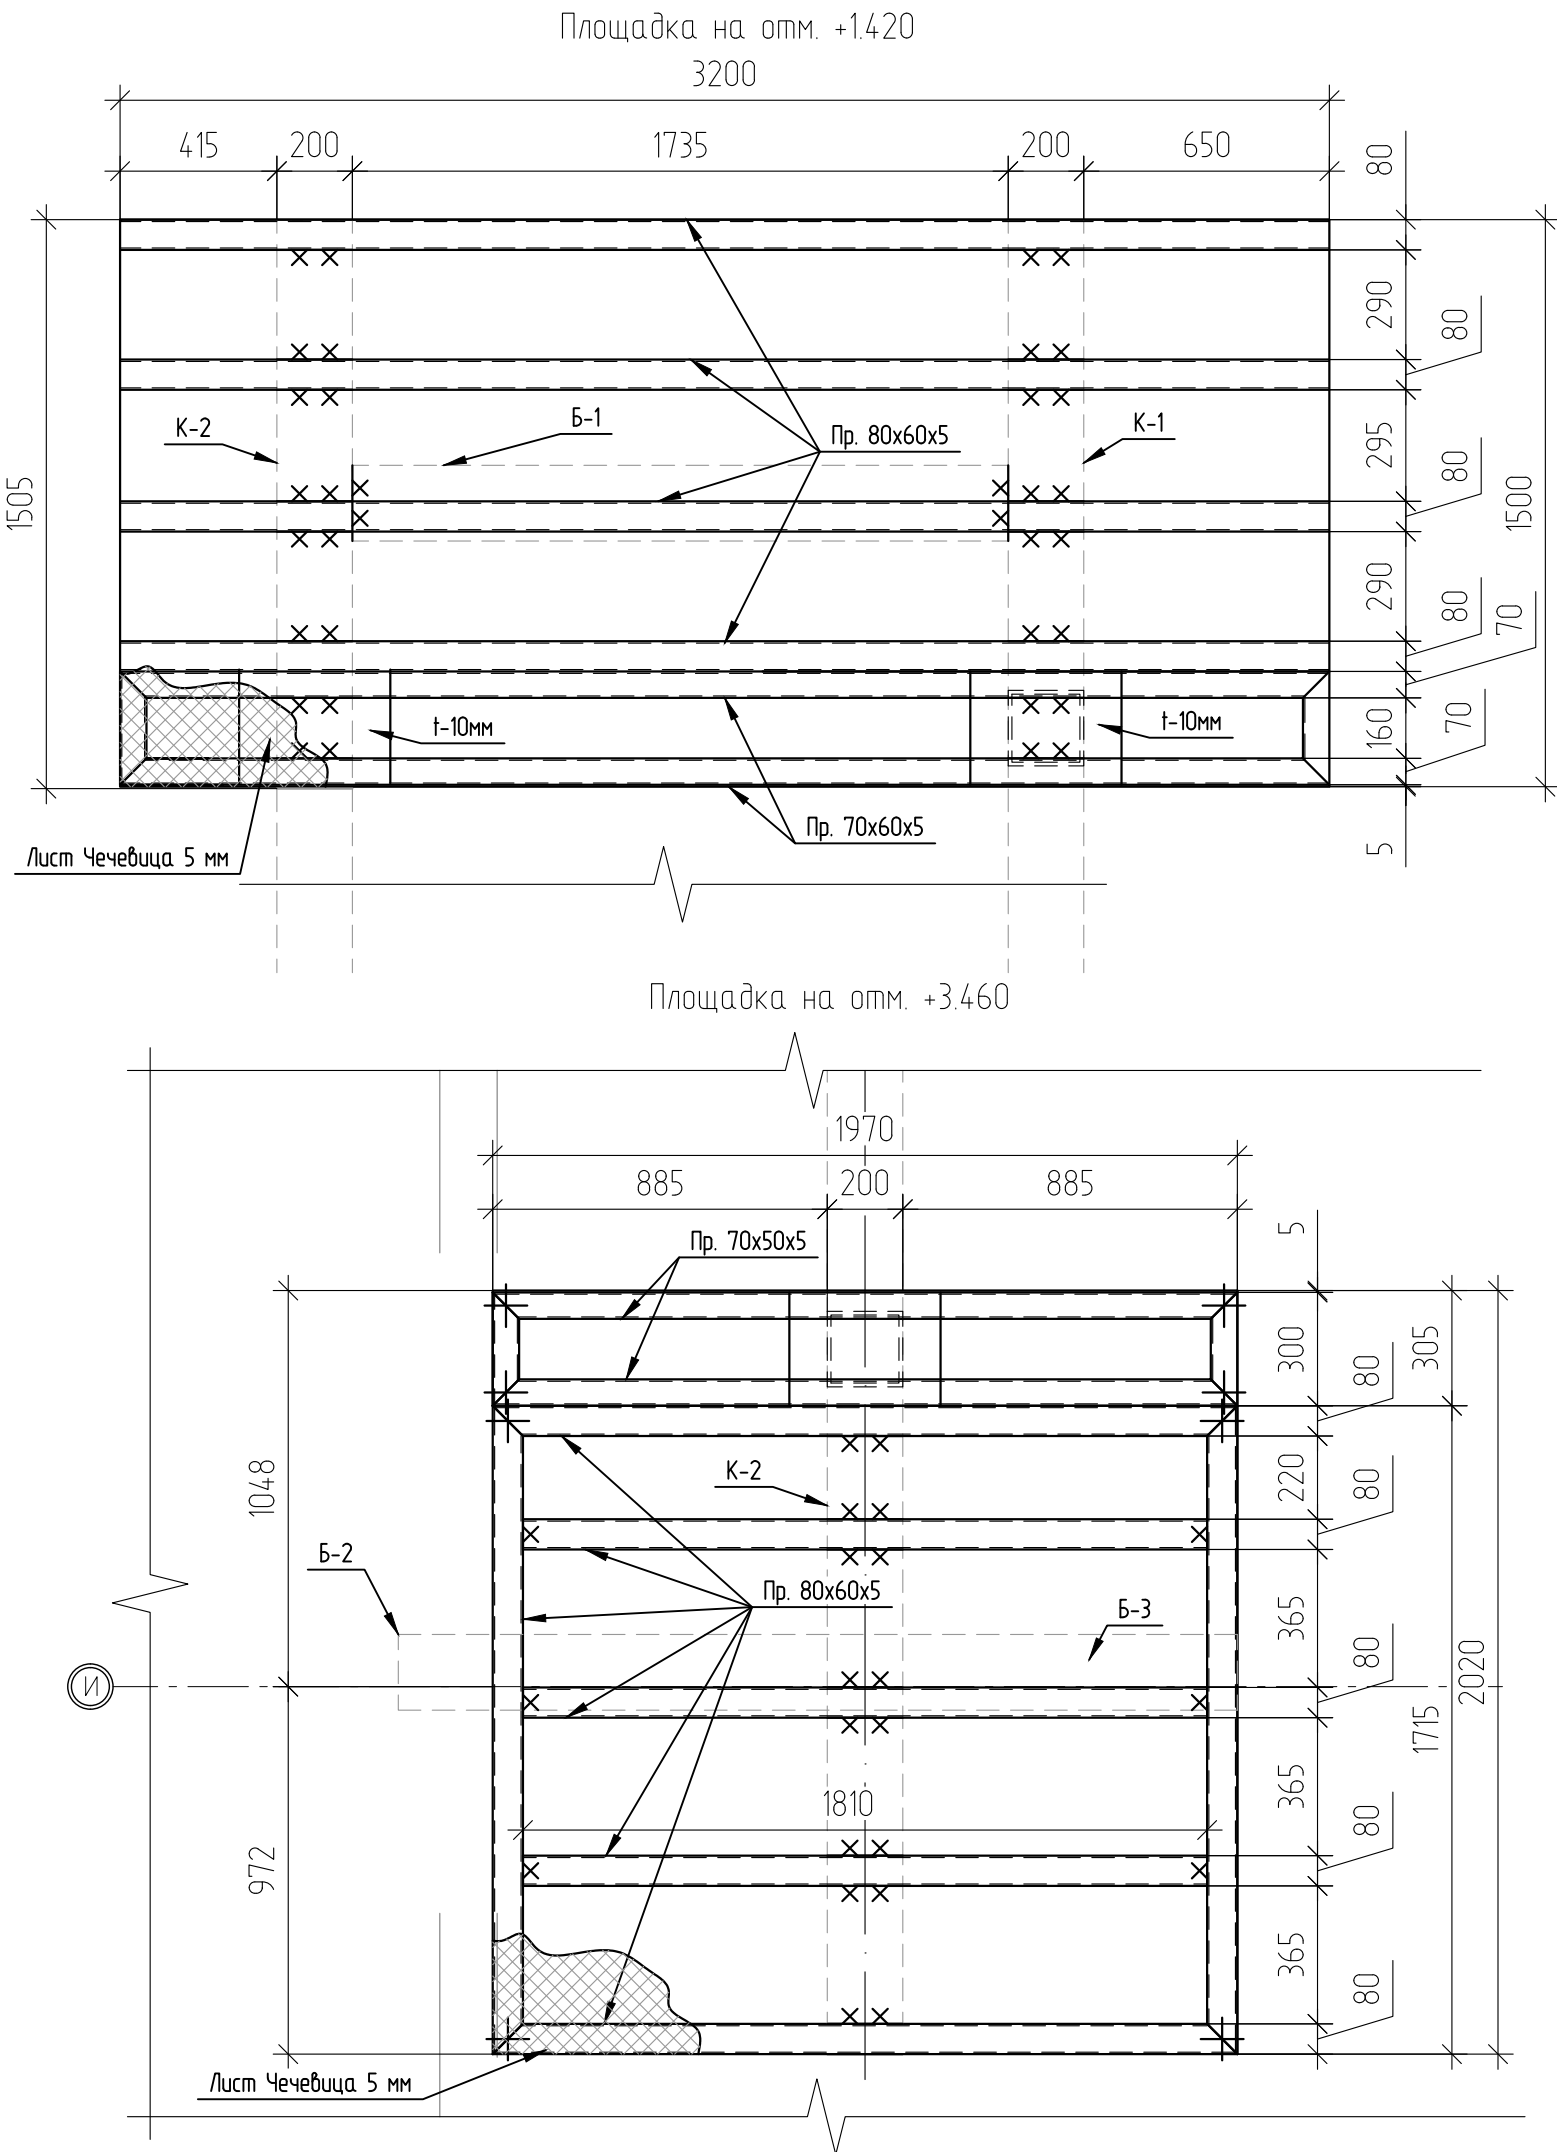

Поз.	Обозначение	Наименование	Кол.	Масса, ед. кг	Примечание
		Косоур К-1	1		
		Полоса 5x200 ГОСТ 103-2006 L=200 мм	1	157	
		Полоса 10x400 ГОСТ 103-2006 L=645 мм	1	20.2	
		Профиль 10x200 ГОСТ 103-2006 L=5.787 м.п		57.0	330
		Косоур К-2	1		
		Полоса 5x200 ГОСТ 103-2006 L=200 мм	2	157	3.14
		Профиль 10x200 ГОСТ 103-2006 L=7.353 м.п		57.0	420
		Балка Б-1, Б-2, Б-3			
		Профиль 10x200 ГОСТ 103-2006 L=3.76 м.п		57.0	214.5
		Полоса 10x300 ГОСТ 103-2006 L=300 мм	1	7.1	
		Стойка Ст-1, Ст-2			
Ст-1		Профиль 10x200 ГОСТ 103-2006 L=1.965 м.п	2	57.0	104.0
		Полоса 10x220 ГОСТ 103-2006 L=220 мм	2	3.8	7.6
Ст-2		Профиль 10x200 ГОСТ 103-2006 L=4.005 м.п	1	57.0	215.2
		Полоса 10x220 ГОСТ 103-2006 L=220 мм	1	3.8	
		Ступень металлическая СТ-1			
		Профиль 5x70x50 ГОСТ 30245-2012 L=3.6 м.п	27	8.13	791.1
		Полоса 10x400 ГОСТ 103-2006 L=300 мм	27	9.42	254.4
ОС-1		Профиль 10x200 ГОСТ 103-2006 L=0.136 м.п	14	57.0	100
ОС-1		Профиль 10x200 ГОСТ 103-2006 L=0.142 м.п	12	57.0	85.6
		Площадка на отм. +1.420, +3.460			
		Профиль 5x70x50 ГОСТ 30245-2012 L=11.6 м.п		8.13	94.4
		Профиль 5x80x60 ГОСТ 30245-2012 L=26.5 м.п		9.7	257.1
		Полоса 10x400 ГОСТ 103-2006 L=300 мм	2	9.42	18.9
	ГОСТ 8568-77	Лист Чечевица В-К-ПУ-5.0 Ст3сп, м2	24.1	40.5	976.1

708/П-24-АНО-КР					
Капитальный ремонт общеобразовательного учреждения ГБОУ "Школа №1210" по адресу: г. Москва, ул. Живописная, д.32					
Изм.	Кол.	Лист	№ док.	Подп.	Дата
Разработал	Торшин			Подп.	04.26
ГАП	Фралова			Подп.	04.26
Конструктивные решения				Стадия	Лист
				Р	68
Площадка на отм. +1.250, +3.200				ООО "АРТИС"	

Лестница Л-3 в осях 3-25/Н-П на отм. +3.300



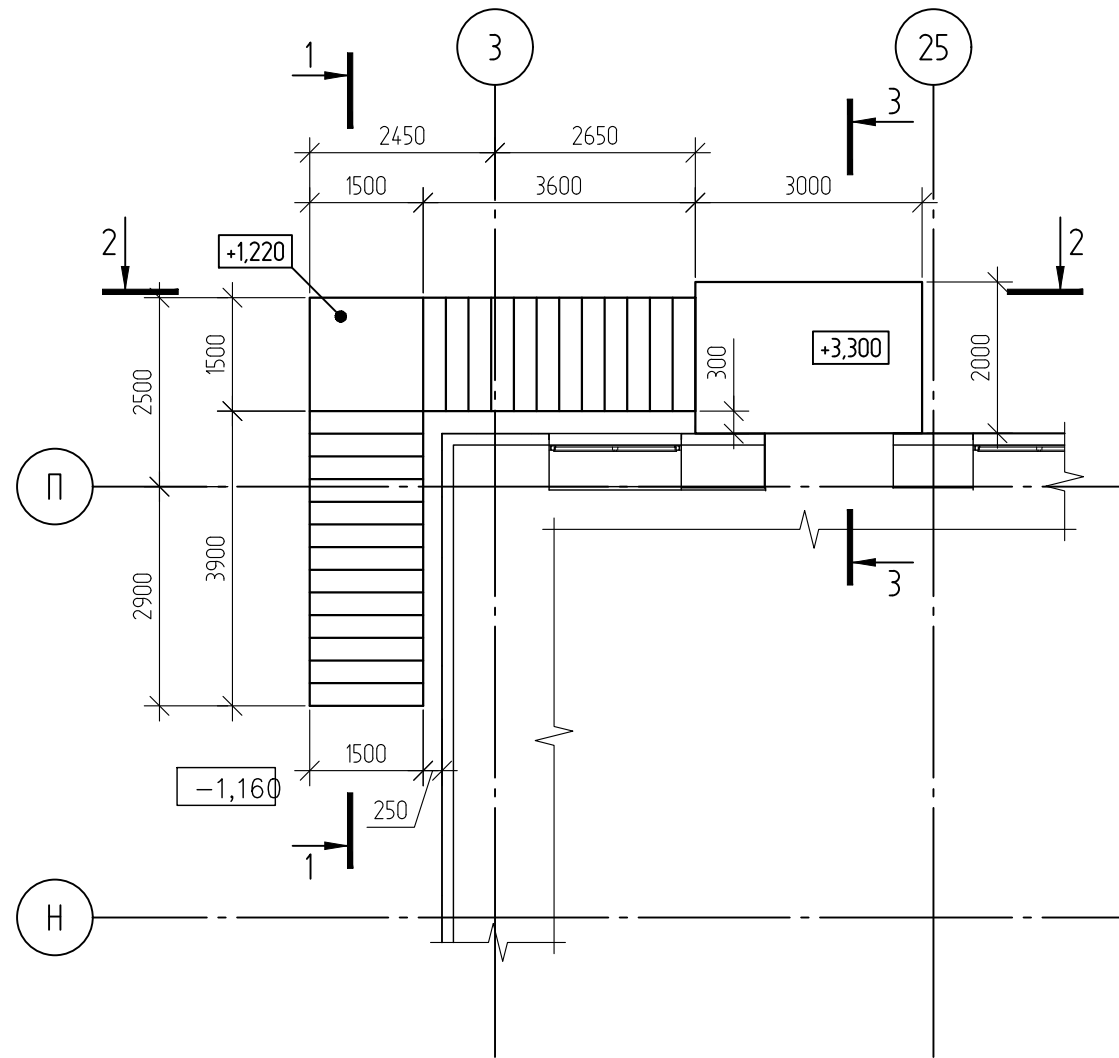


Схема расположения элементов лестницы Л-3 в осях 3-25/Н-П

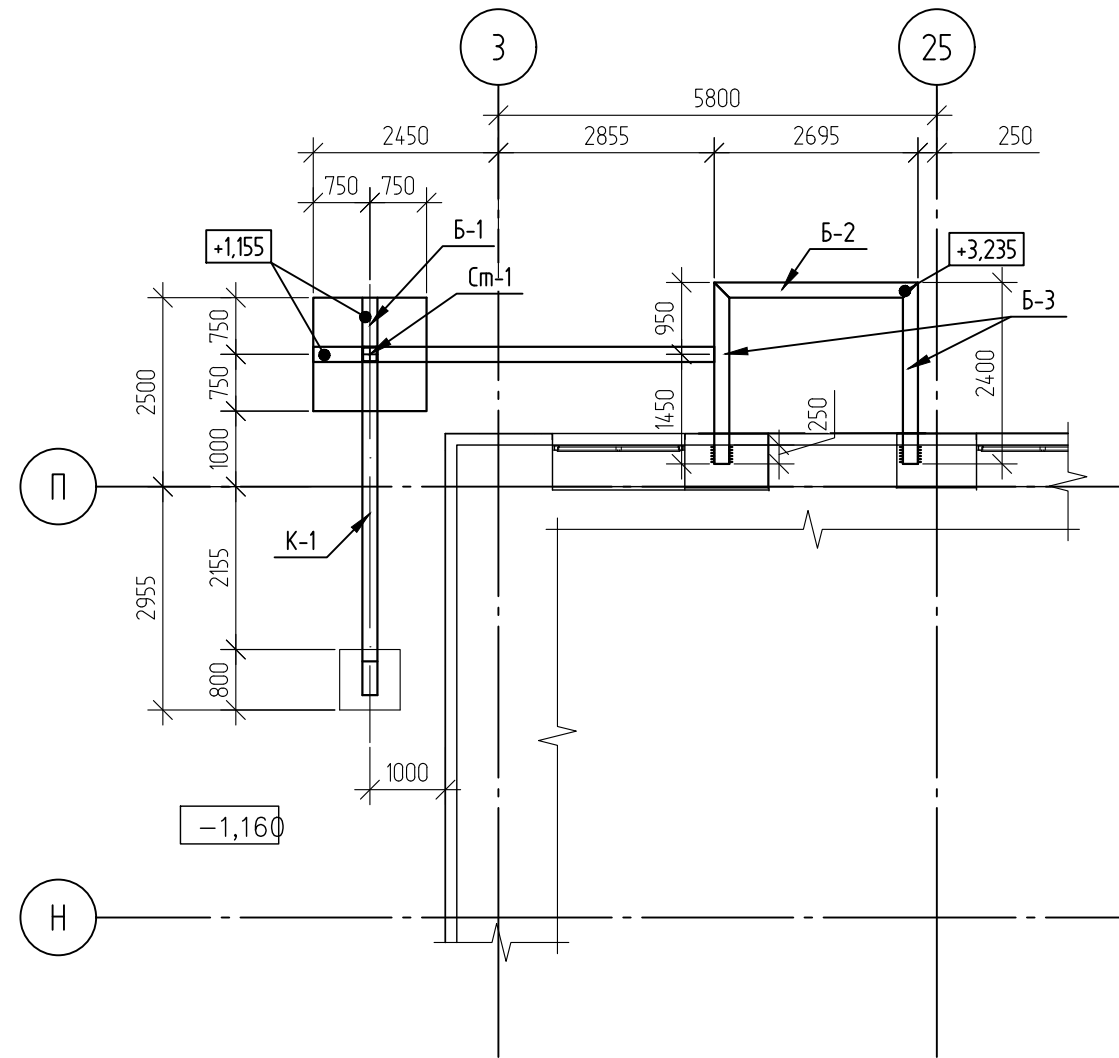


План фундаментов на отм. -1.160

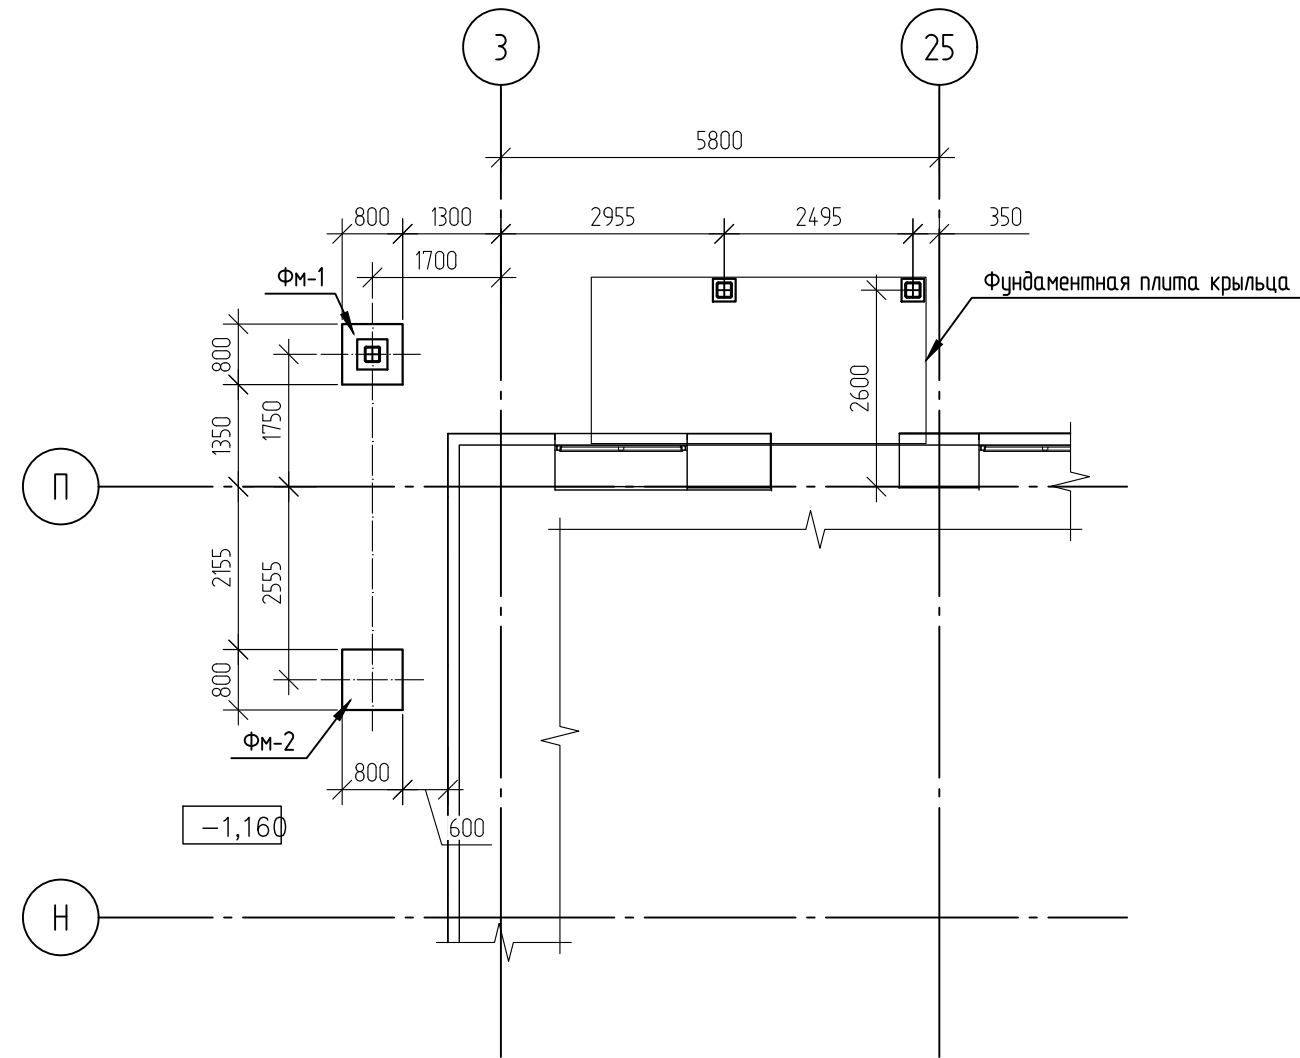


Лист чечевица -5 мм
Рама из трубы 80x60x5 ГОСТ 30245-2003
Рама из трубы 200x10 ГОСТ 30245-2003

2-2

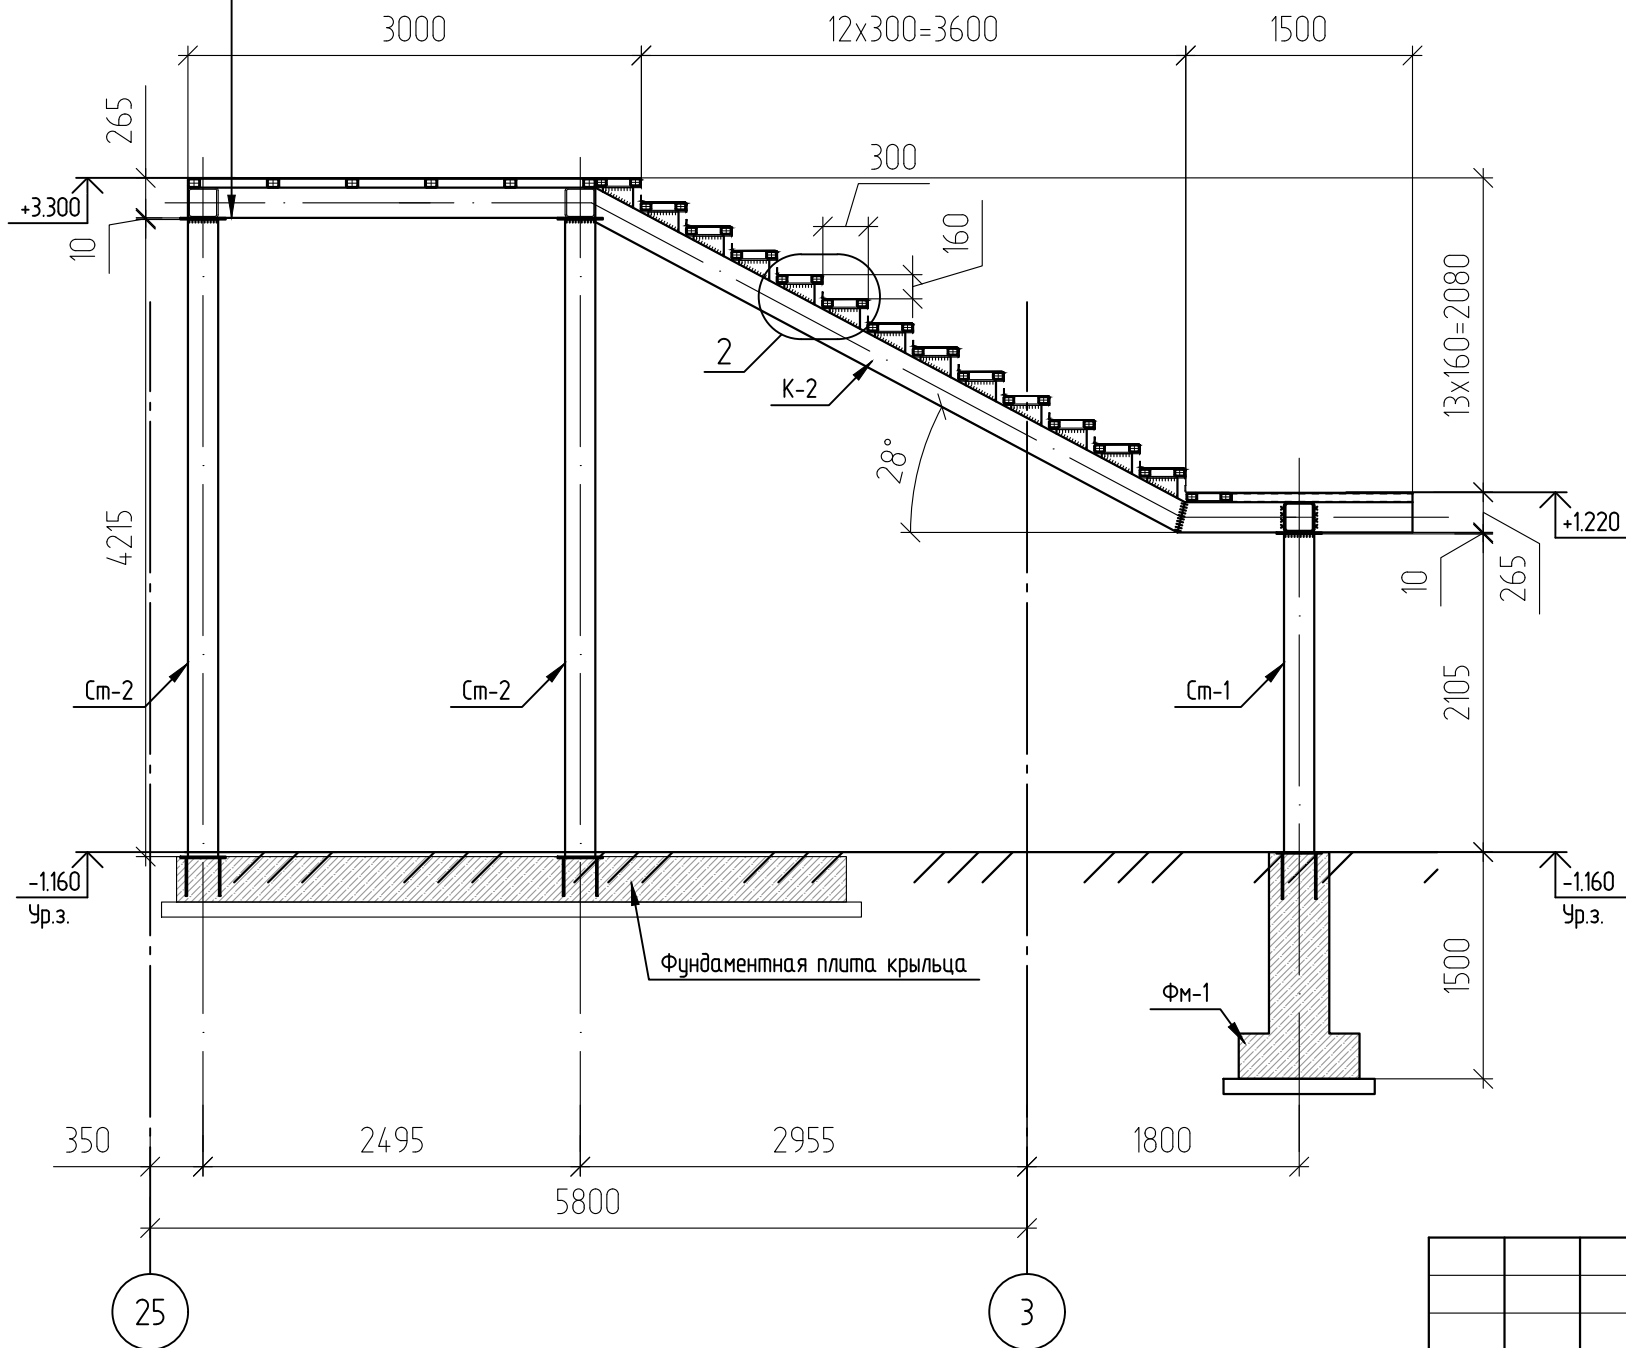


Лист чечевица -5 мм
Рама из трубы 80x60x5 ГОСТ 30245-2003
Рама из трубы 200x10 ГОСТ 30245-2003

3-3

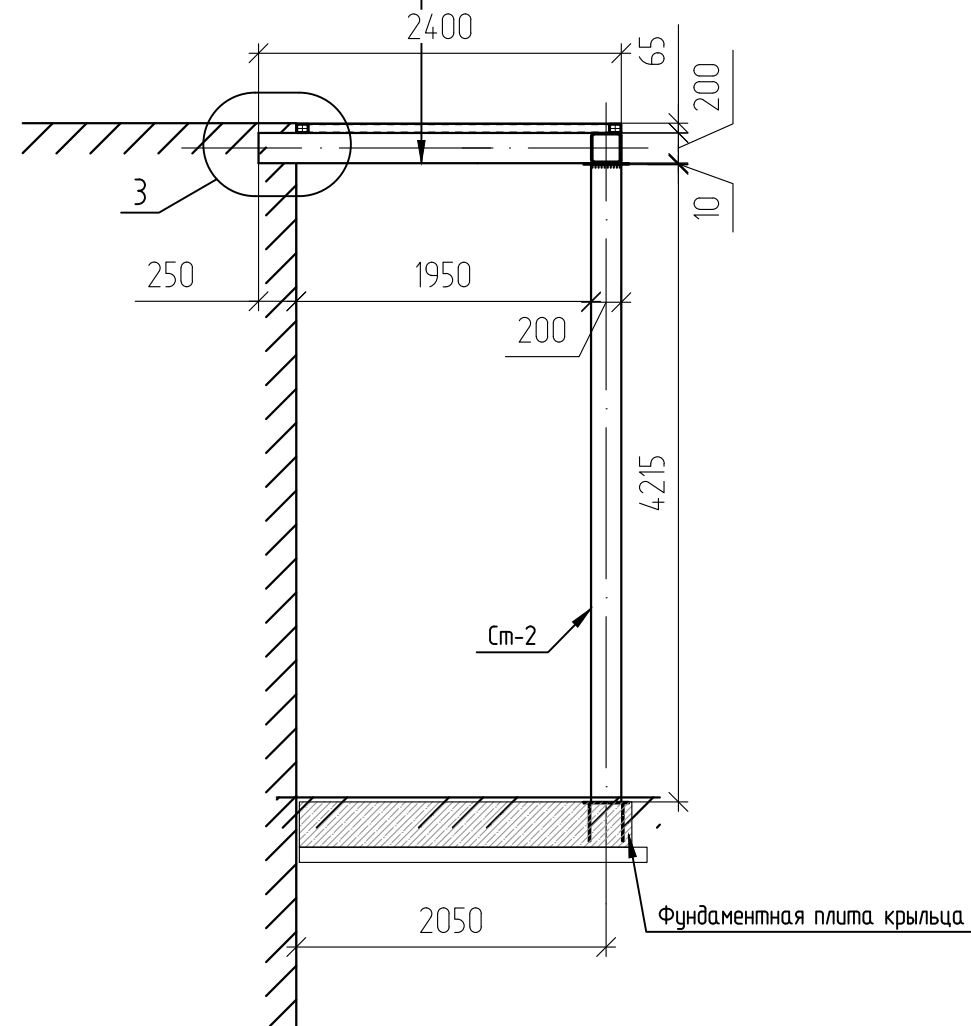





Лист чечевица -5 мм
Рама из трубы 80x60x5 ГОСТ 30245-2003
Косоур из трубы 200x10 ГОСТ 30245-2003

Лист чечевица -5 мм
Рама ступени из трубы 70x50x5 ГОСТ 30245-2003
Косоур из трубы 200x10 ГОСТ 30245-2003

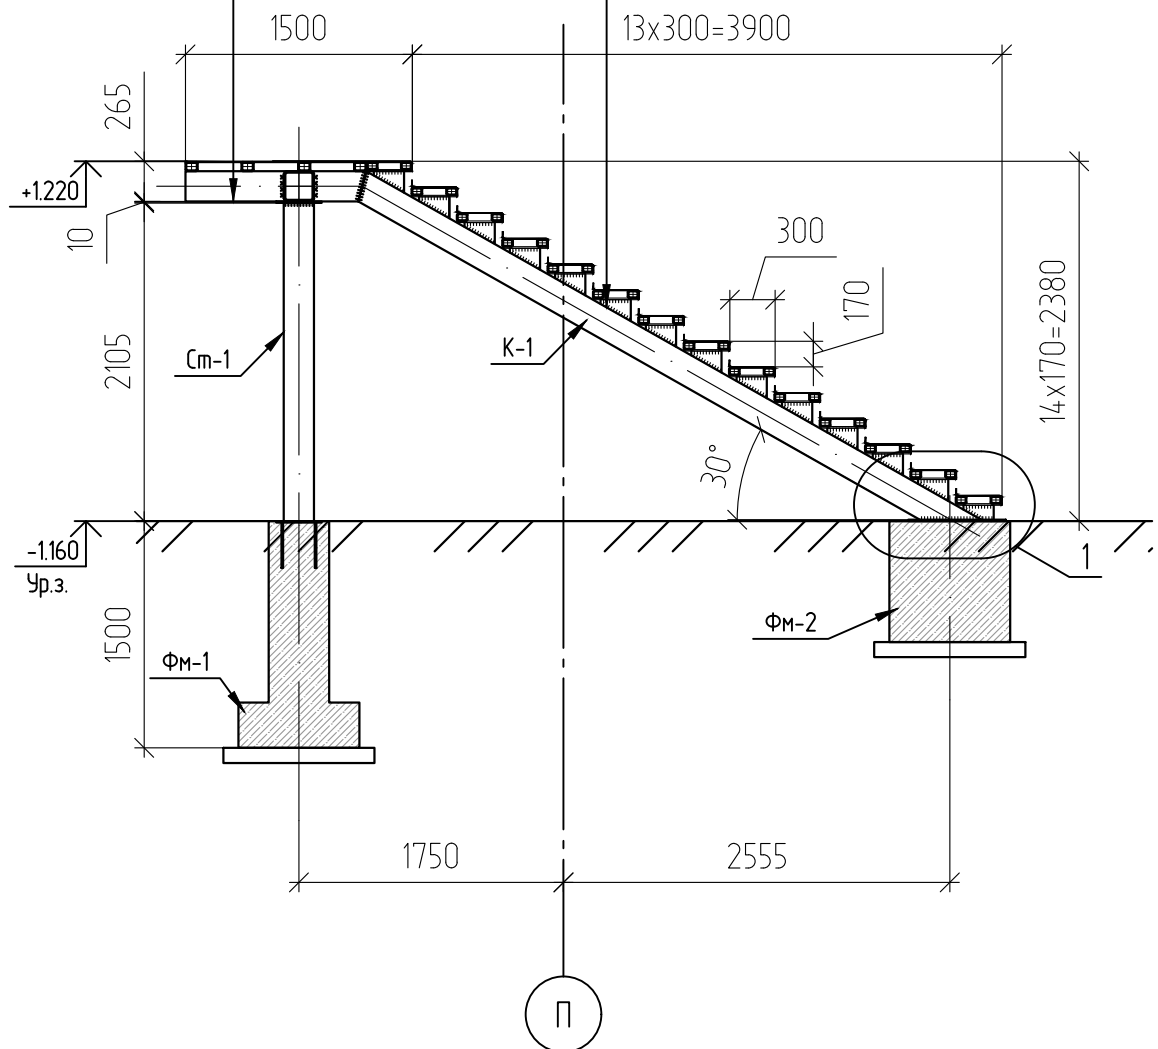

						708/П-24-АНО-КР			
						Капитальный ремонт общеобразовательного учреждения ГБОУ "Школа №1210" по адресу: г. Москва, ул. Живописная, д.32			
Изм.	Колуч.	Лист	№ док.	Подп.	Дата	Конструктивные решения	Стадия	Лист	Листов
Разработал	Торшин				04.26		Р	69	
ГАП	Фролова				04.26				
						Лестница Л-3 в осях 3-25/Н-П на отм. +3.300		институт проектных решений и градских объектов ООО "АРТИС"	
Н.Контроль	Лукашова				04.26				
ГИП	Зыкин				04.26				







Согласовано			
Инф. № подл.	Подп. и дата	Взам. инф. №	

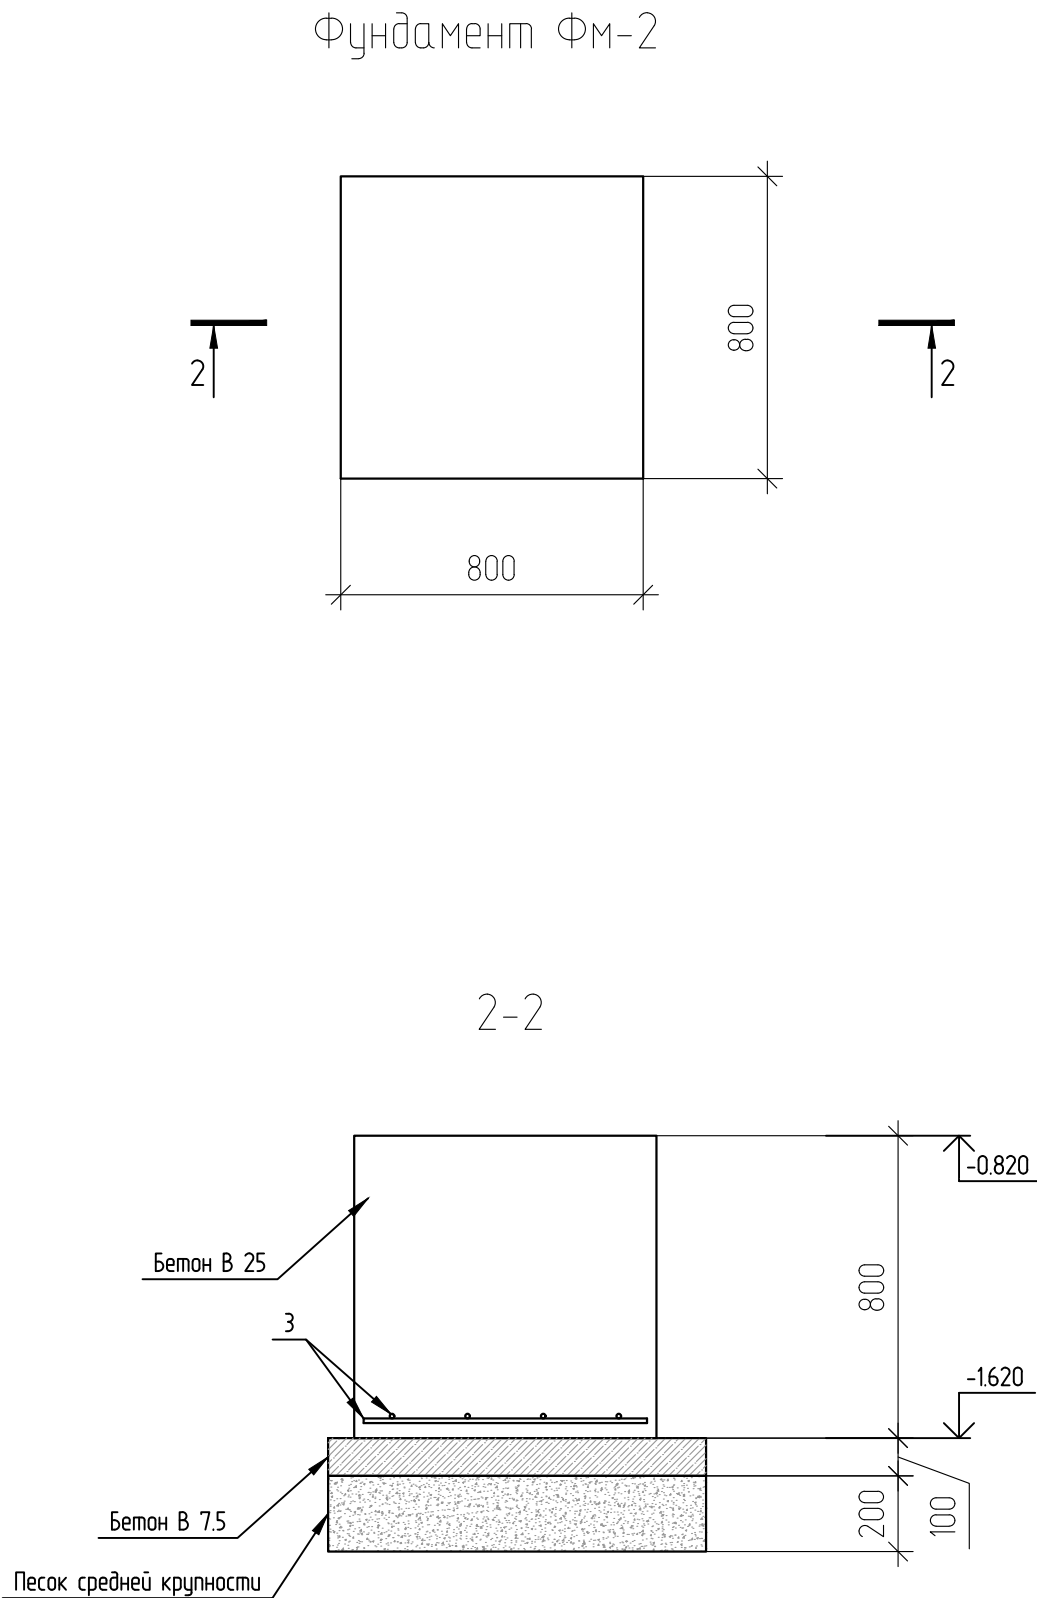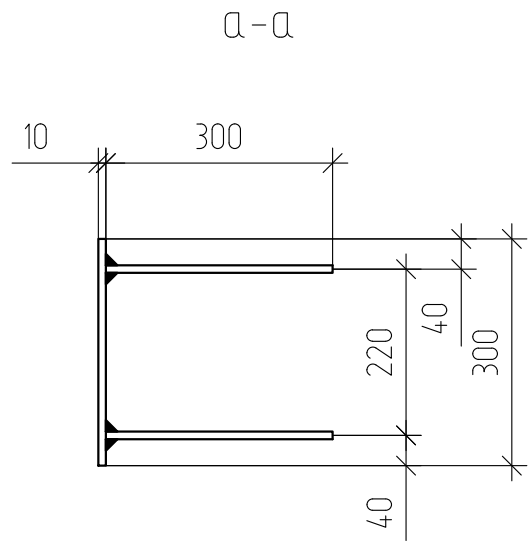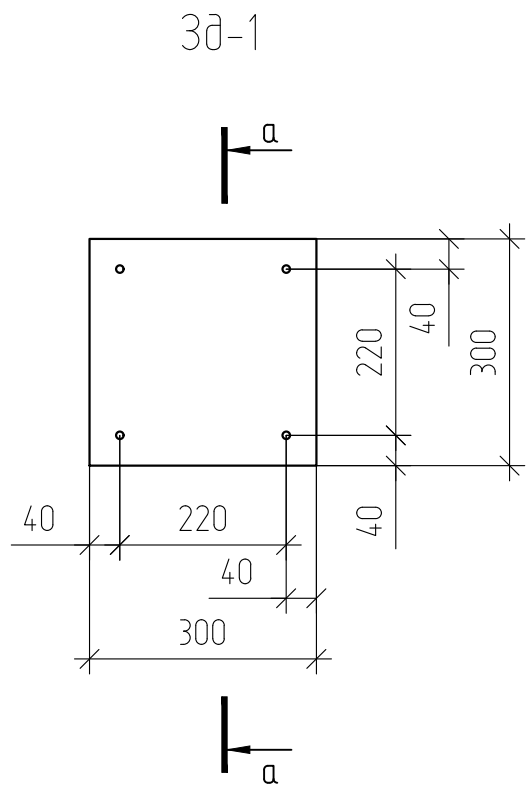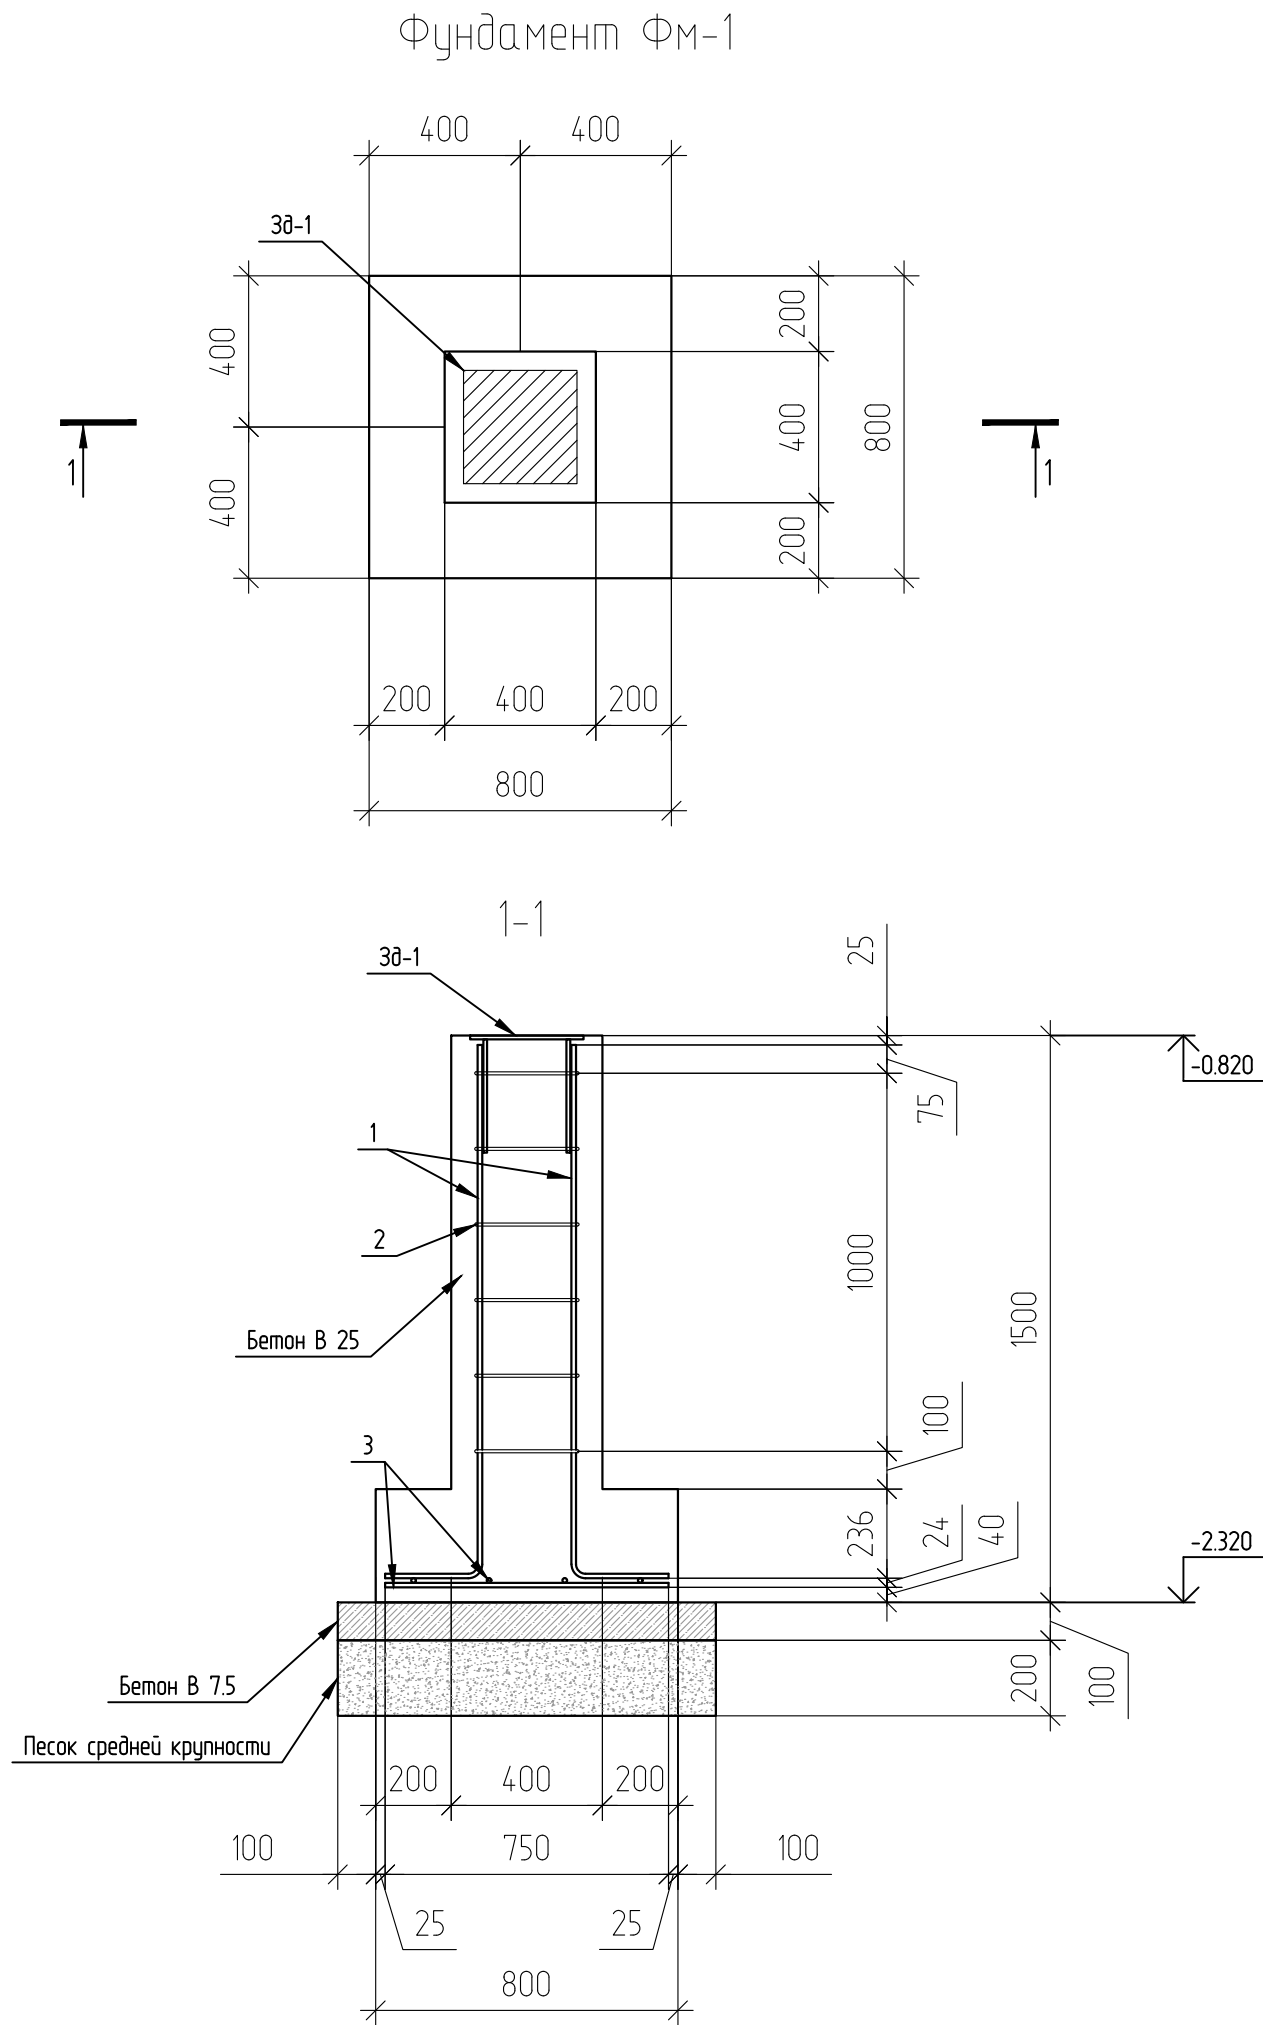



Поз.	Обозначение	Наименование	Кол.	Масса, ед. кг	Примечание
ФМ-1		Фундамент ФМ-1	1		
1	ГОСТ 34028-2016	Пруток МД-12-А500С L=1630мм	4	1,44	5,76
2	ГОСТ 34028-2016	Пруток МД-8-А240 L=1220мм	6	0,48	2,88
3	ГОСТ 34028-2016	Пруток МД-12-А500С L=750мм	8	0,67	5,36
		Материалы			
	ГОСТ 26633-2012	Бетон В25 F200 W6, м.куб.	0,4		
	ГОСТ 26633-2012	Подбетонка Бетон В7,5 , м.куб.	0,1		
		Праймер битумный Технониколь №01, м2.	3,6		
		Мастика Технониколь AquaMast, м2.	3,6		
ФМ-2		Фундамент ФМ-2	1		
3	ГОСТ 34028-2016	Пруток МД-12-А500С L=750мм	8	0,67	5,36
		Материалы			
	ГОСТ 26633-2012	Бетон В25 F200 W6, м.куб.	0,51		
	ГОСТ 26633-2012	Подбетонка Бетон В7,5 , м.куб.	0,1		
		Праймер битумный Технониколь №01, м2.	2,6		
		Мастика Технониколь AquaMast, м2.	2,6		
30-1		Закладная 30-1			
1а	ГОСТ 103-2006	Полоса 10х300, С245 ГОСТ 27772-2015. L=250мм	1	4,71	
2а	ГОСТ 34028-2016	Пруток МД-10-А500С L=300мм	4	0,19	0,76

						708/П-24-АНО-КР			
						Капитальный ремонт общеобразовательного учреждения ГБОУ "Школа №1210" по адресу: г. Москва, ул. Живописная, д.32			
Изм.	Колуч.	Лист	№ док.	Подп.	Дата	Конструктивные решения	Стадия	Лист	Листов
Разработал	Торшин				04.26		Р	70	
ГАП	Фролова				04.26				
						Фундамент ФМ-1, ФМ-2		комплексное проектирование промышленных и гражданских объектов ООО "АРТИС"	
Н.Контроль	Лукашова				04.26				
ГИП	Зыкин				04.26				

Согласовано	
Инв. № подл.	Взам. инв. №
	Подп. и дата
Инв. № подл.	

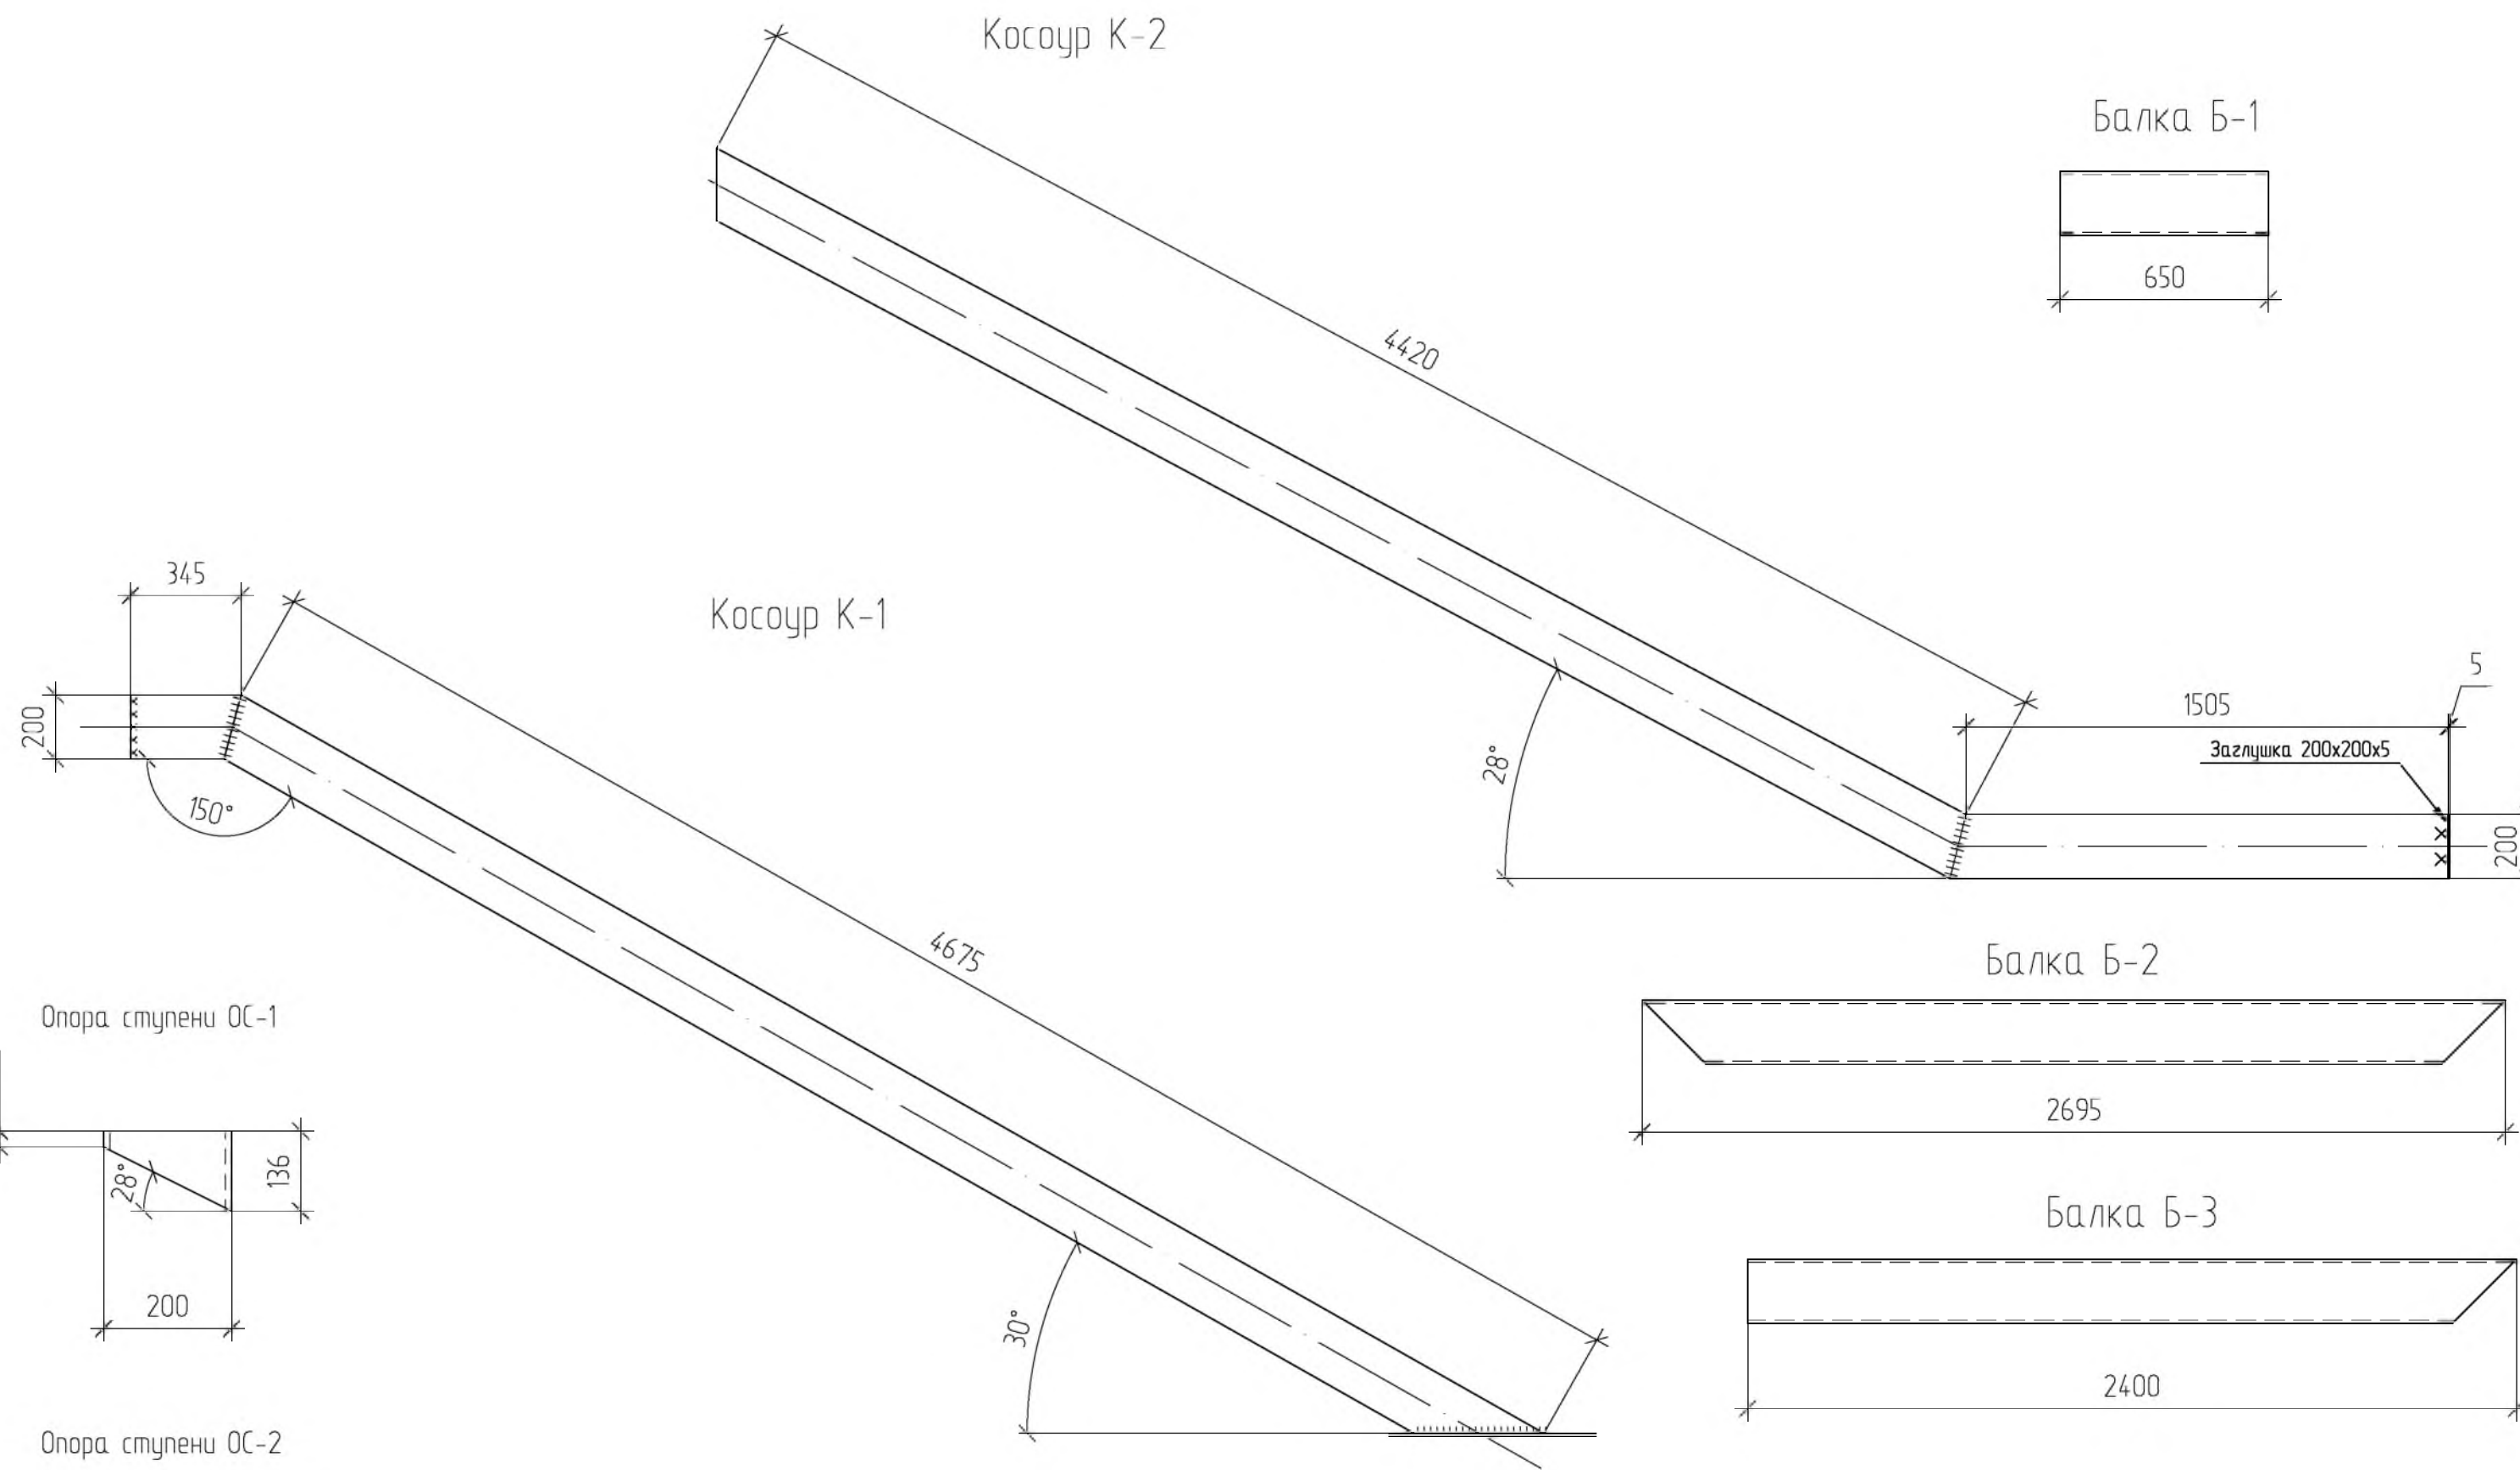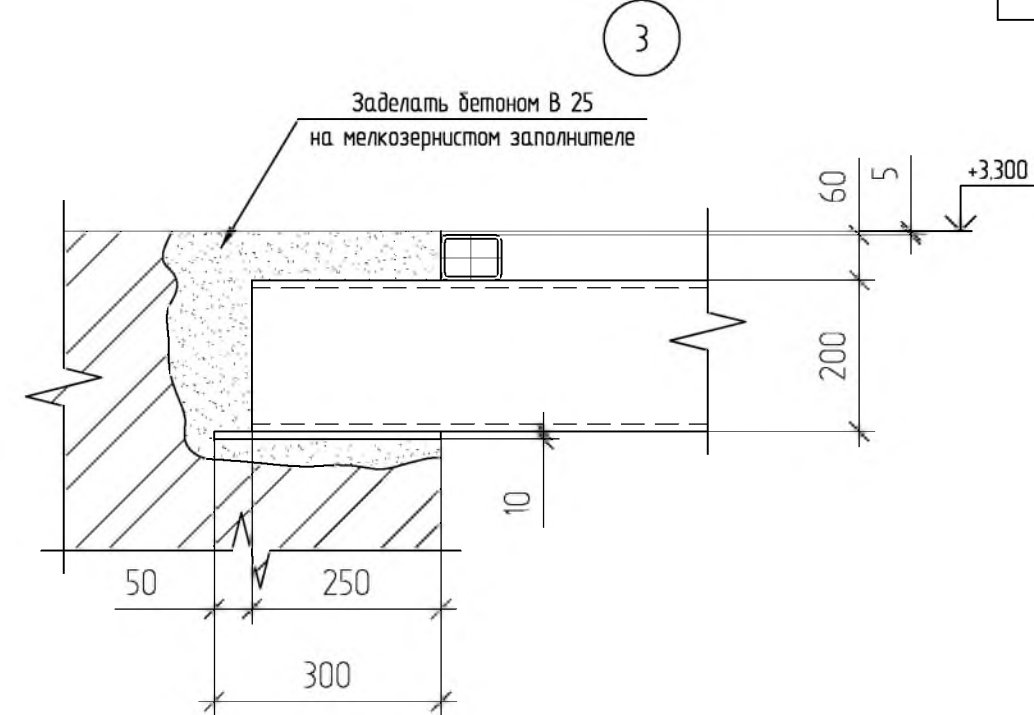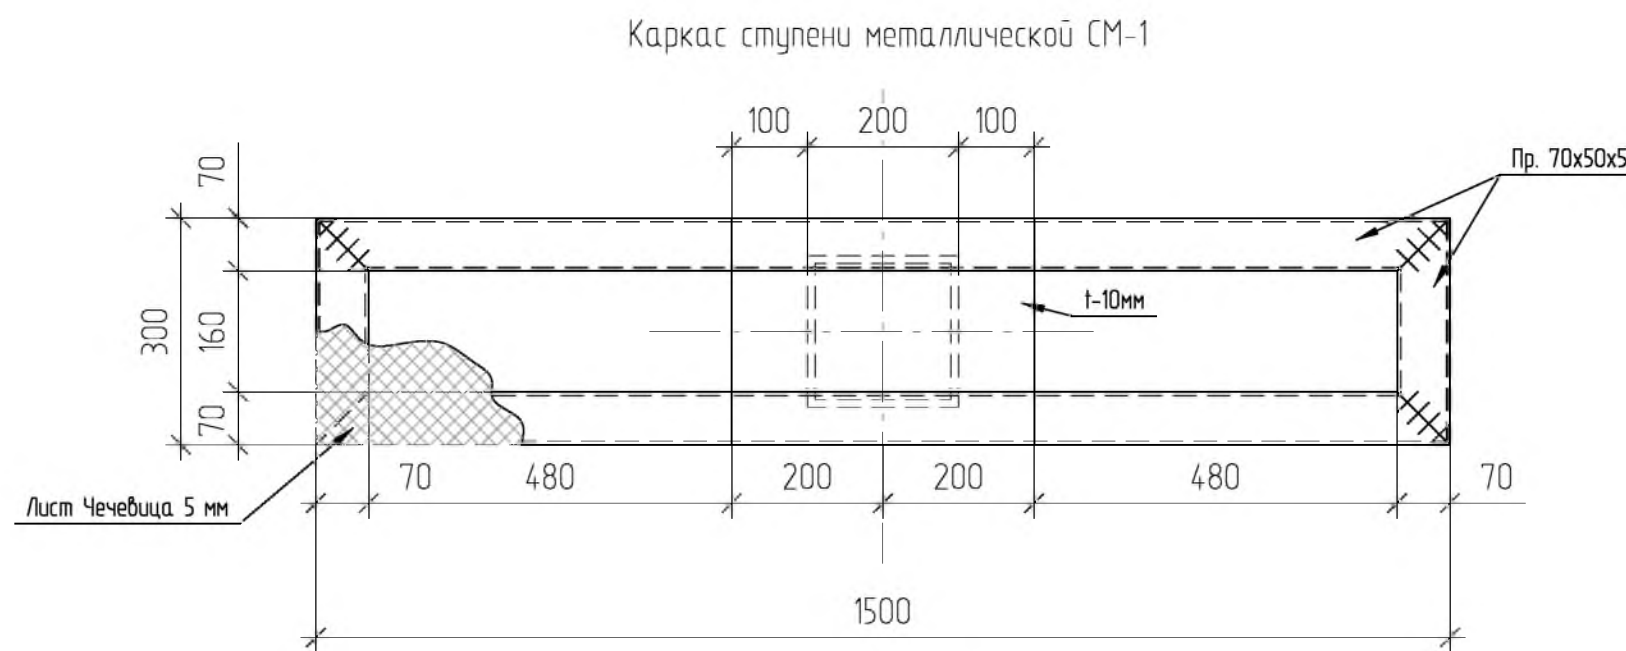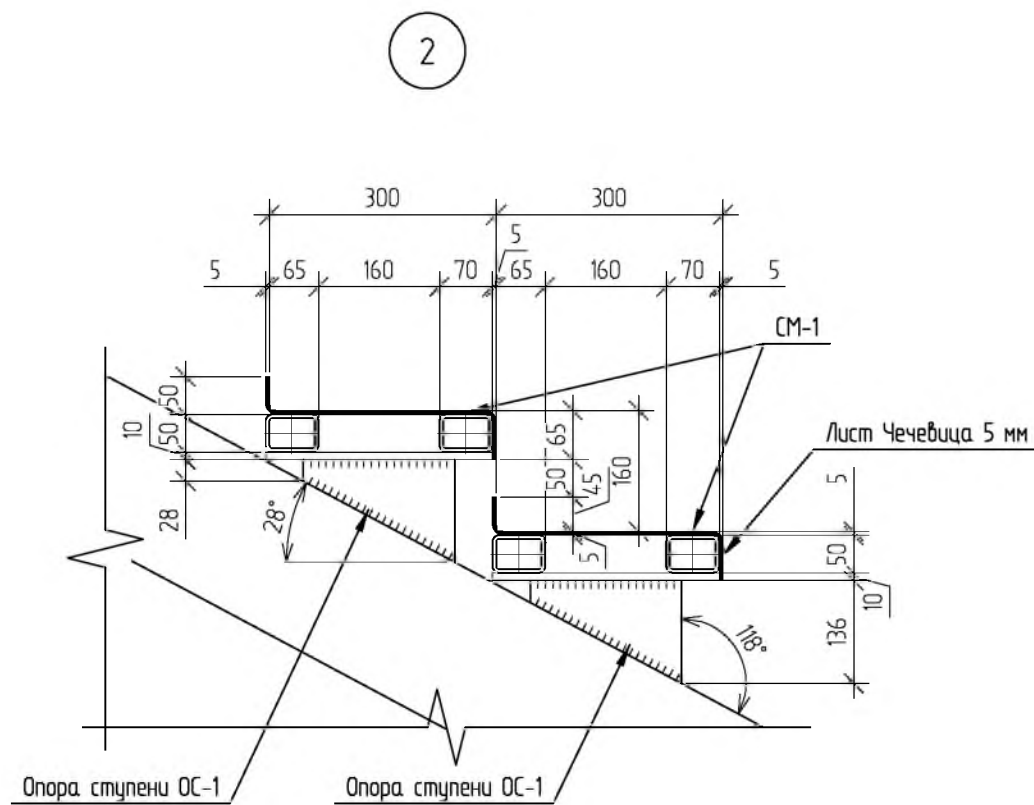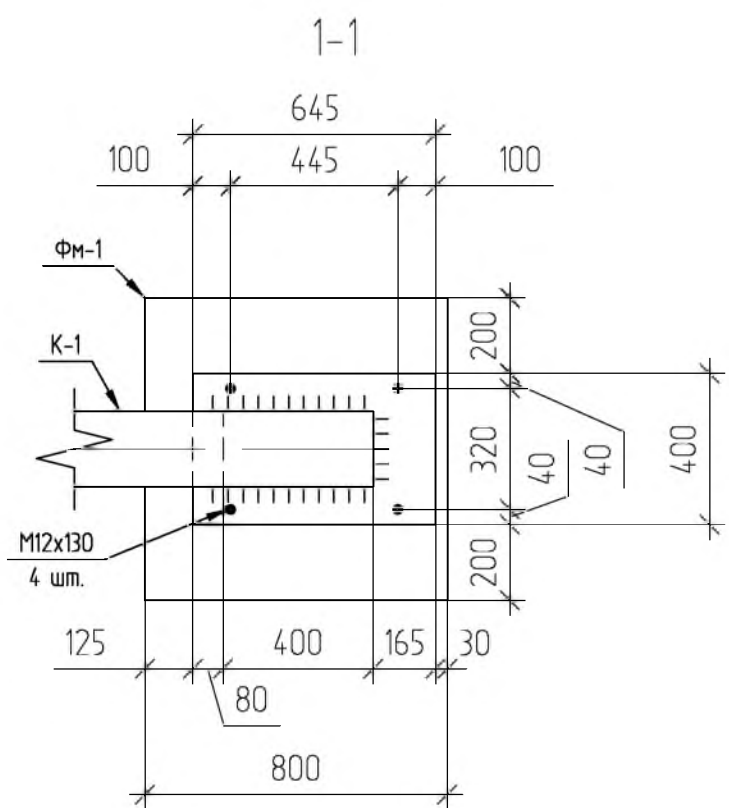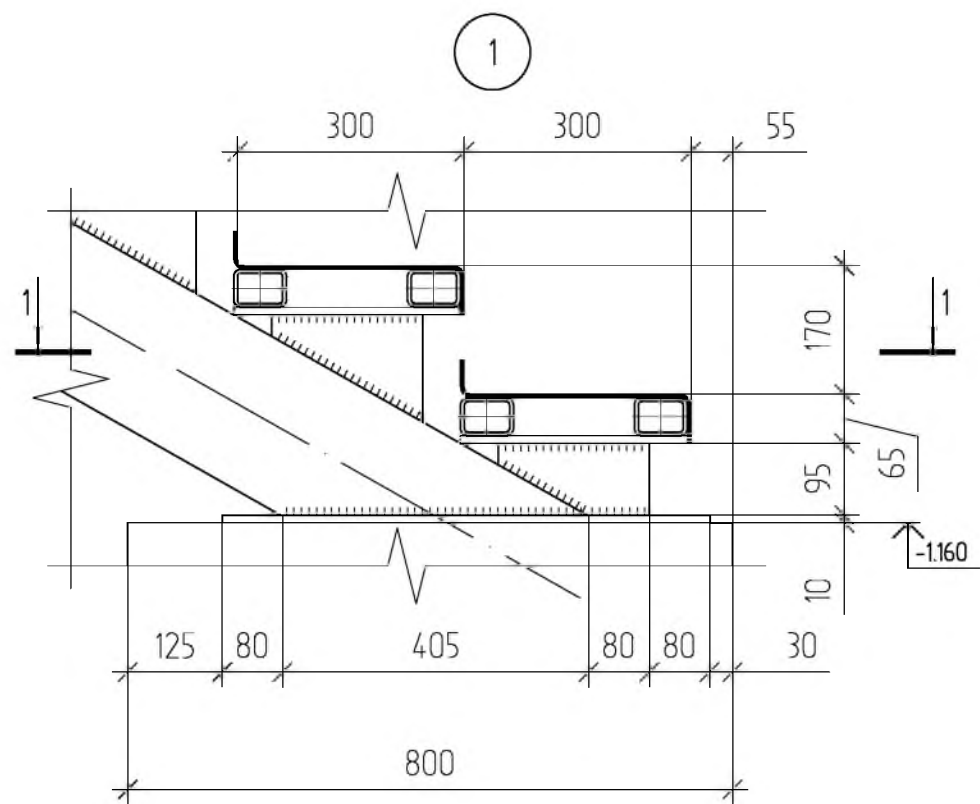

						708/П-24-АНО-КР			
						Капитальный ремонт общеобразовательного учреждения ГБОУ "Школа №1210" по адресу: г. Москва, ул. Живописная, д 32			
Изм.	Колуч.	Лист	№ док.	Подп.	Дата	Конструктивные решения	Стадия	Лист	Листов
Разработал	ГАП	Торшин	Фролова	С.И.	04.26		Р	71	
						Косоур К-1, К-2. Узел 1, 2, 3	 ООО "АРТИС"		
Н.Контроль	ГИП	Лукашова	Зыкин	С.И.	04.26				

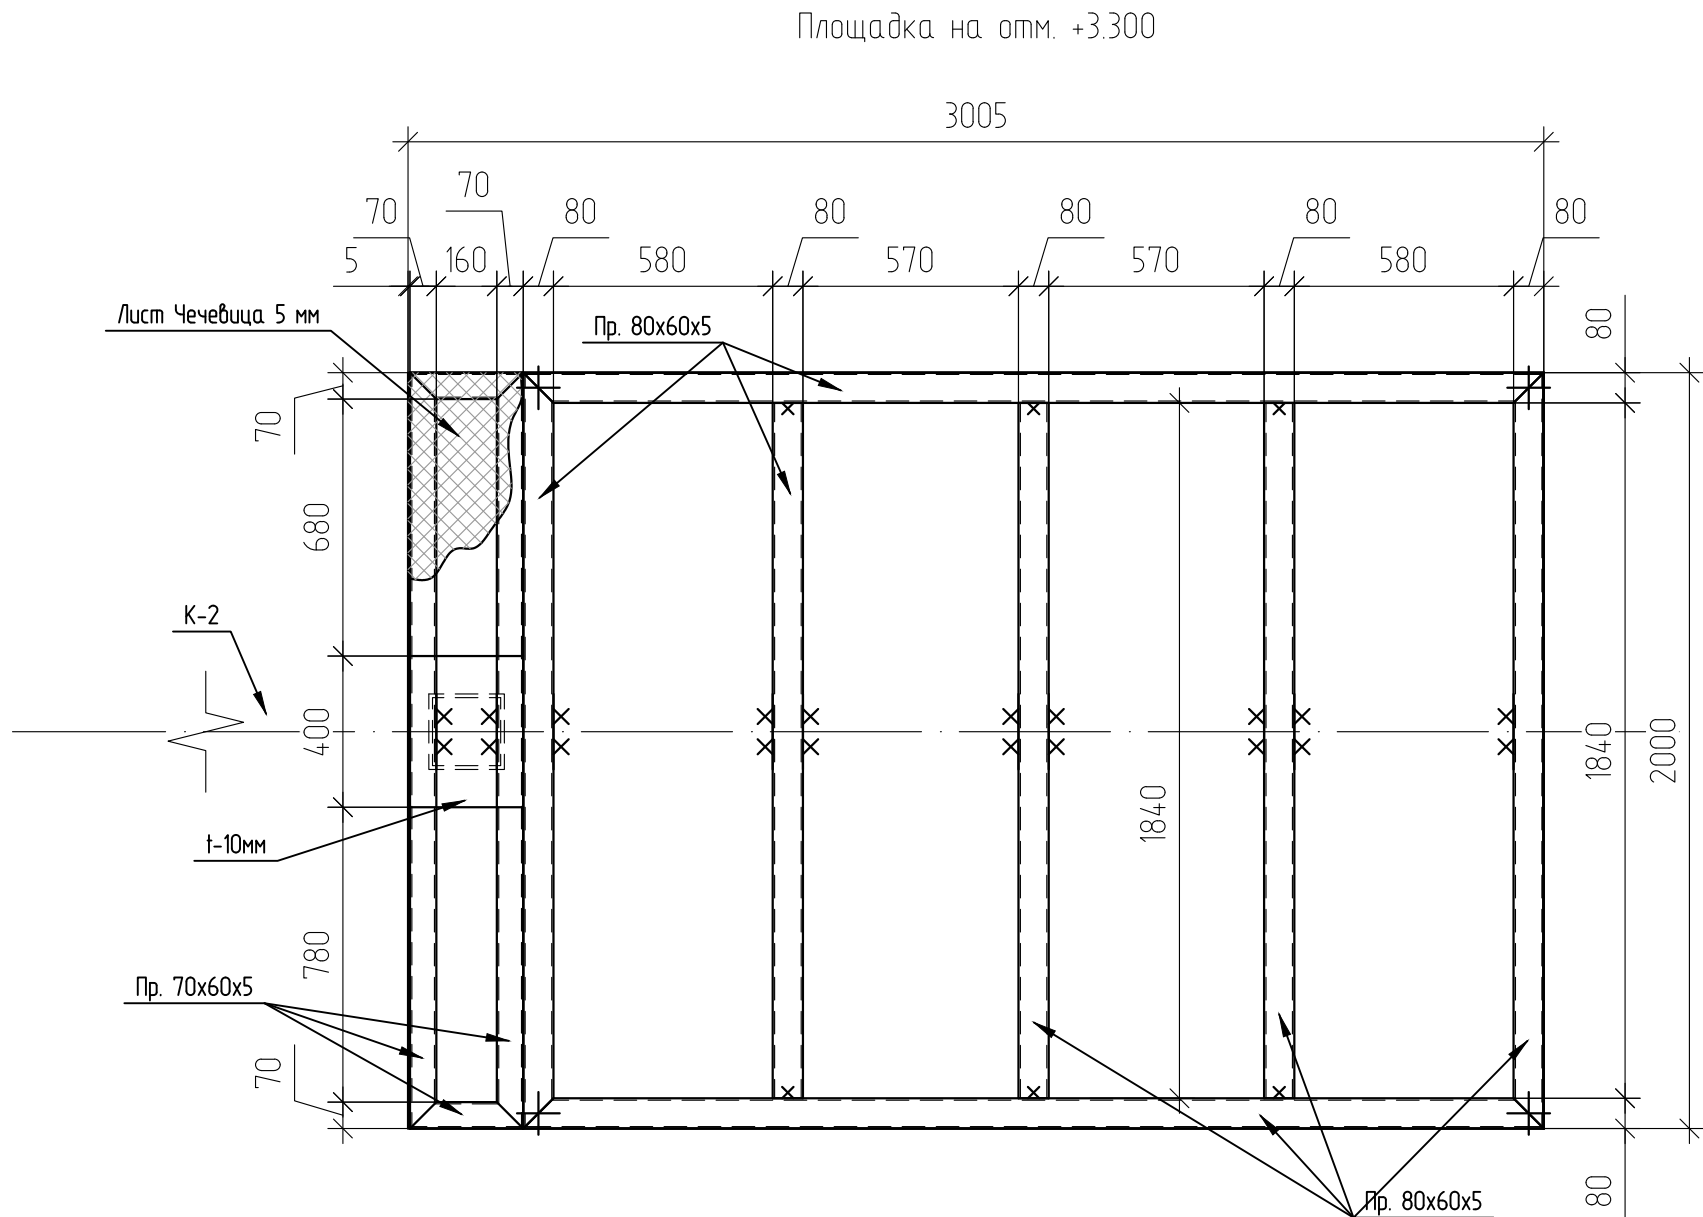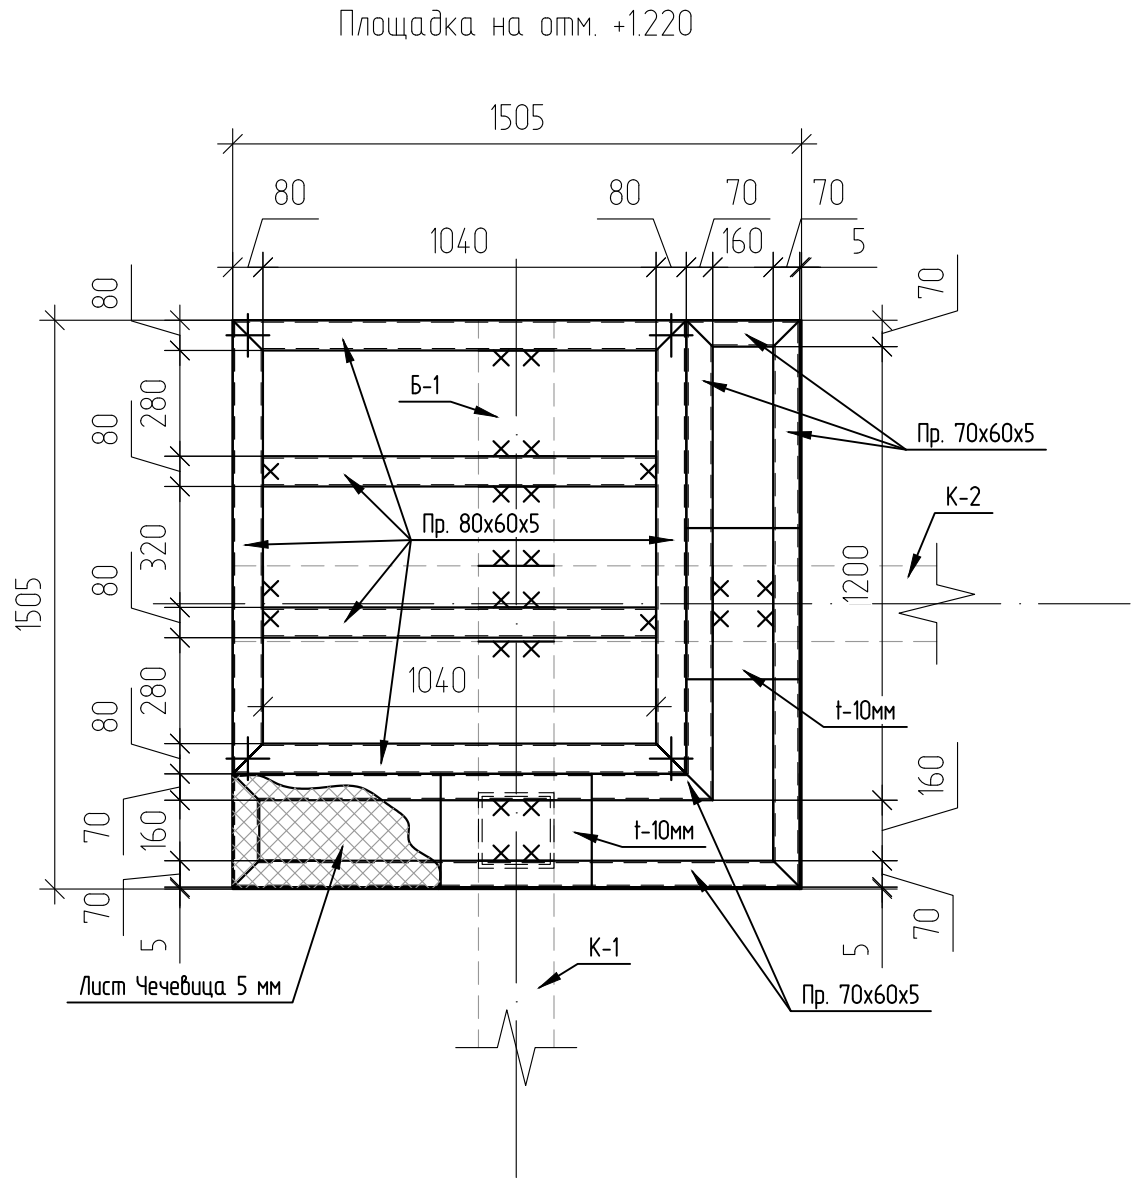

Поз.	Обозначение	Наименование	Кол.	Масса, ед. кг	Приме- чание
		Косоур К-1	1		
		Полоса 10x400 ГОСТ 103-2006 L=645 мм	1	20.2	
		Профиль 10x200 ГОСТ 103-2006 L=5.020 м.л		57.0	286.2
		Косоур К-2	1		
		Полоса 5x200 ГОСТ 103-2006 L=200 мм	1	157	
		Профиль 10x200 ГОСТ 103-2006 L=5.93 м.л		57.0	338.01
		Балка Б-1, Б-2, Б-3			
		Профиль 10x200 ГОСТ 103-2006 L=8.25 м.л		57.0	470.25
		Полоса 10x300 ГОСТ 103-2006 L=300 мм	2	7.1	14.2
		Стойка Ст-1, Ст-2			
Ст-1		Профиль 10x200 ГОСТ 103-2006 L=2.105 м.л	1	57.0	120
		Полоса 10x220 ГОСТ 103-2006 L=220 мм	1	3.8	
Ст-2		Профиль 10x200 ГОСТ 103-2006 L=4.215 м.л	2	57.0	477.09
		Полоса 10x220 ГОСТ 103-2006 L=220 мм	1	3.8	
		Ступень металлическая СТ-1			
		Профиль 5x70x50 ГОСТ 30245-2012 L=36 м.л	27	8.13	219.6
		Полоса 10x400 ГОСТ 103-2006 L=300 мм	27	9.42	254.4
ОС-1		Профиль 10x200 ГОСТ 103-2006 L=0.136 м.л	14	57.0	100
ОС-1		Профиль 10x200 ГОСТ 103-2006 L=0.142 м.л	12	57.0	85.6
		Площадка на отм. +1.420, +3.460			
		Профиль 5x70x50 ГОСТ 30245-2012 L=10.14 м.л		8.13	82.5
		Профиль 5x80x60 ГОСТ 30245-2012 L=218 м.л		9.7	211.5
		Полоса 10x400 ГОСТ 103-2006 L=300 мм	2	9.42	5.88
	ГОСТ 8568-77	Лист Чечевица В-К-ПУ-5.0 Ст3сп, м2	19.8	40.5	802

						708/П-24-АНО-КР
						Капитальный ремонт общеобразовательного учреждения ГБОУ "Школа №1210" по адресу: г. Москва, ул. Живописная, д.32
Изм.	Колуч.	Лист	№ док.	Подп.	Дата	
Разработал	Торшин				04.26	
ГАП	Фролова				04.26	Конструктивные решения
Н.Контроль	Лукашова				04.26	Площадки на отм. +1.220, +3.300
ГИП	Зыкин				04.26	

комплексное проектирование промышленных и гражданских объектов
ООО "АРТИС"

Формат A2

Согласовано				
Взам. инв. №				
Подп. и дата				
Инв. № подл.				

Схема рамы на кровле для
оборудования кондиционирования
в осях М/17

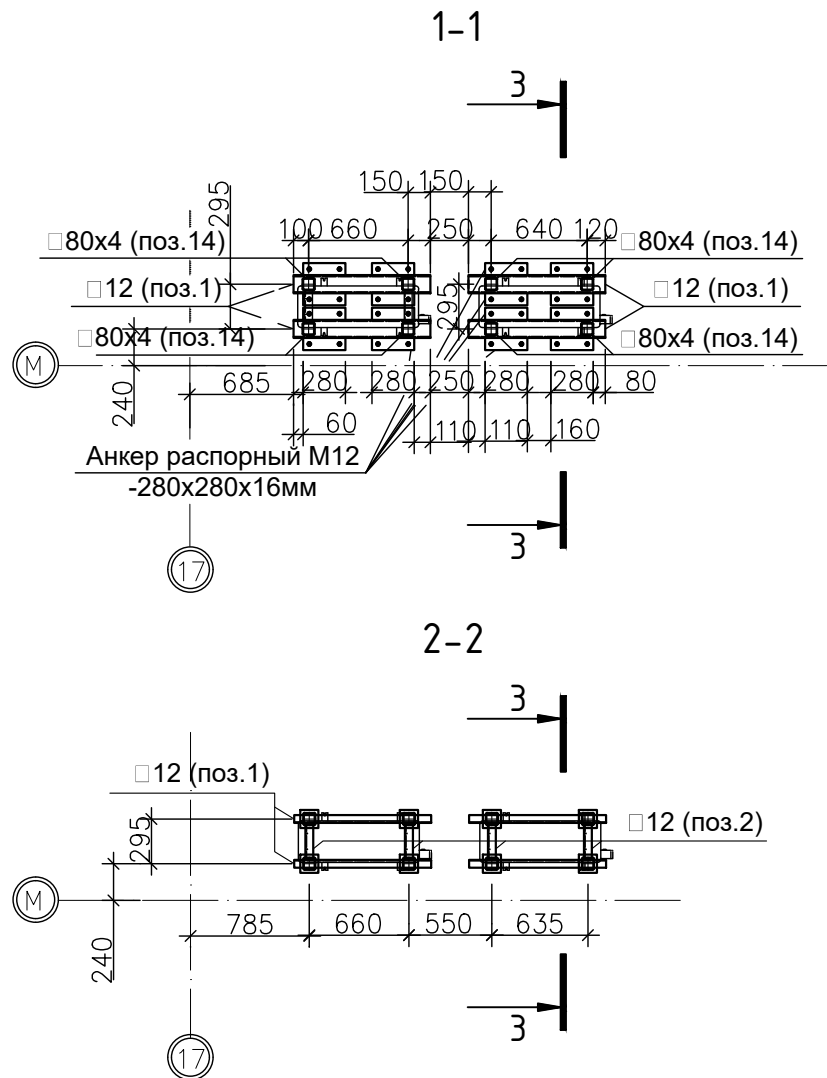


Схема рамы на кровле для
оборудования кондиционирования
в осях М/21





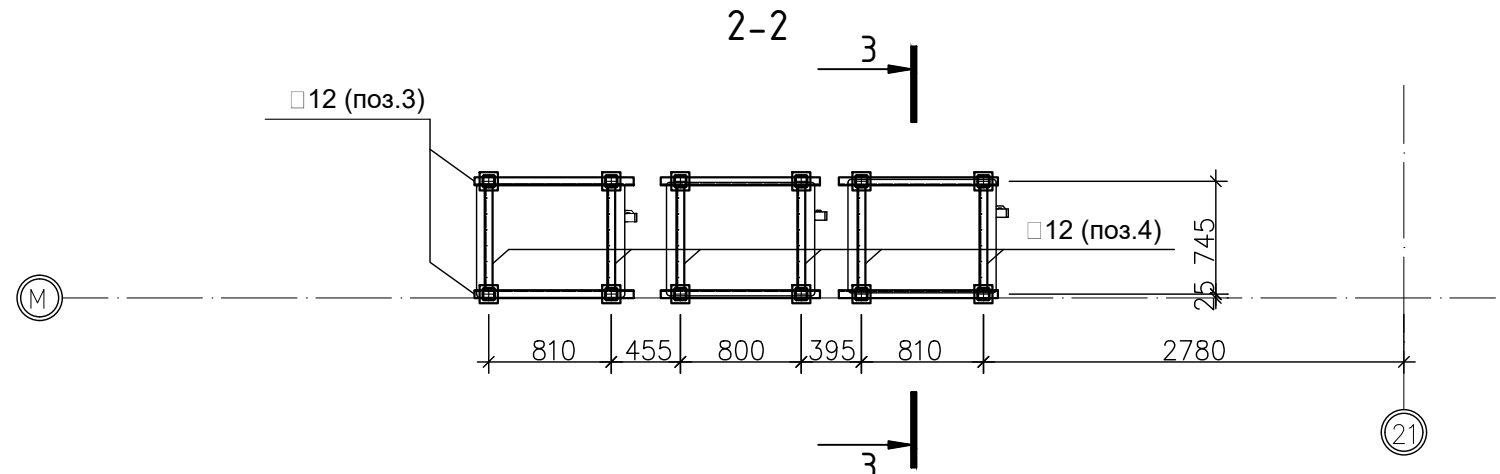


Схема рамы на кровле для
оборудования кондиционирования
в осях В/7

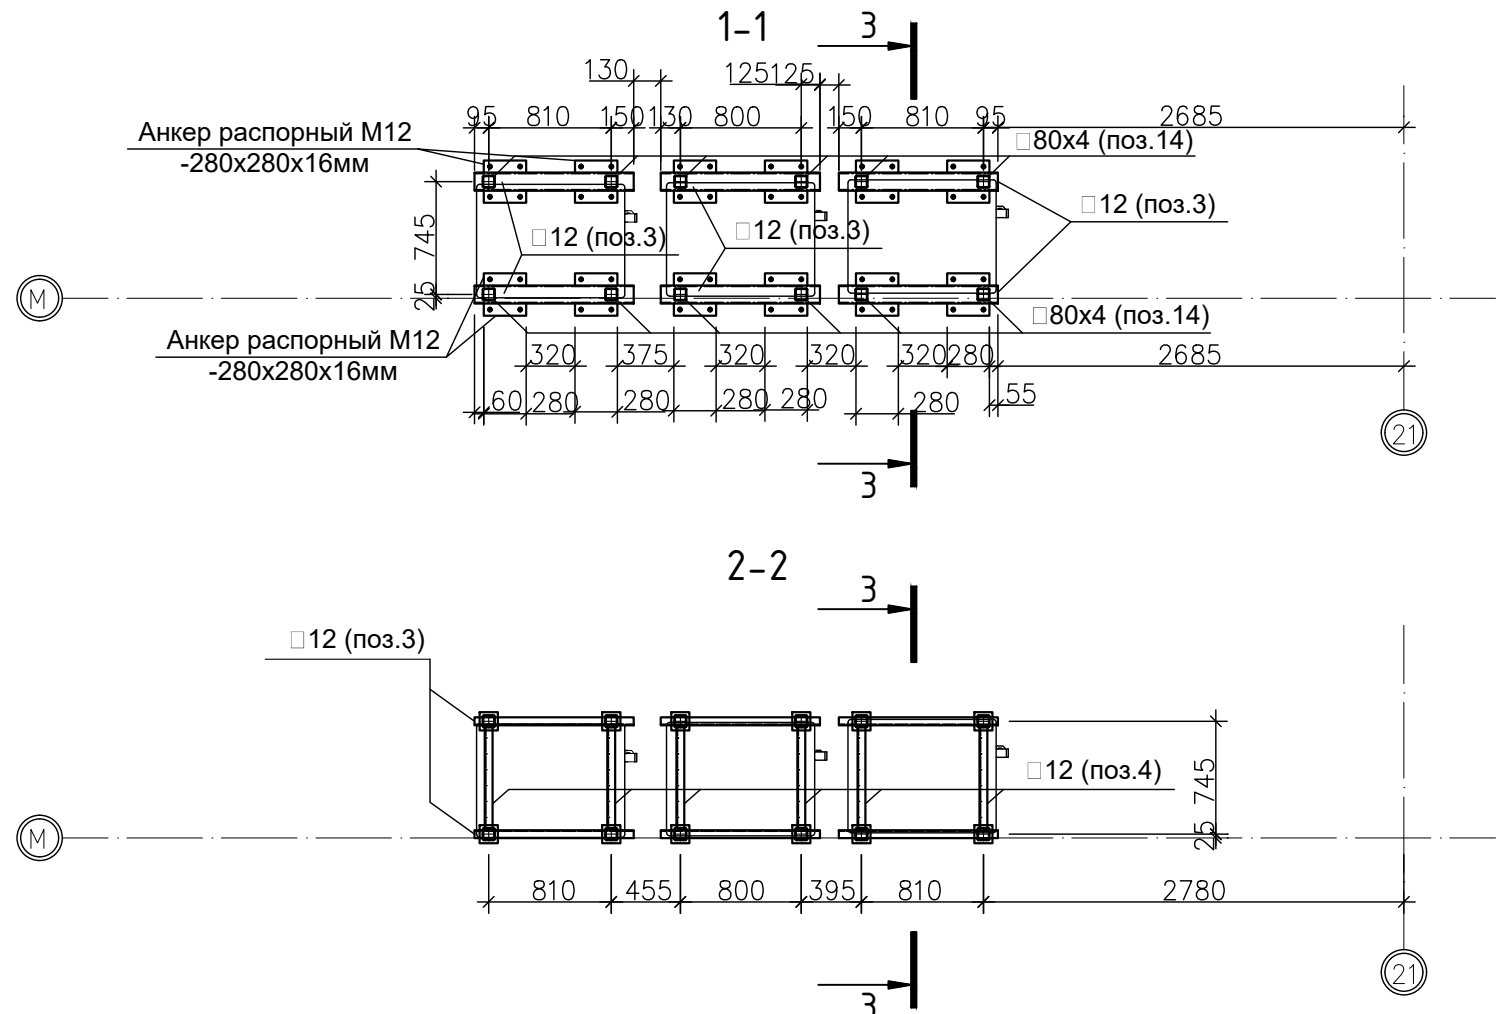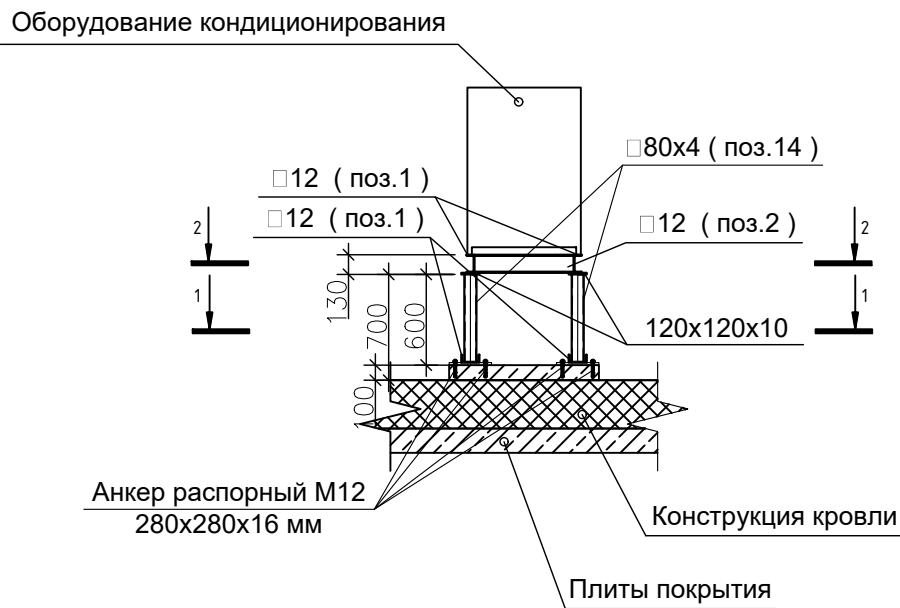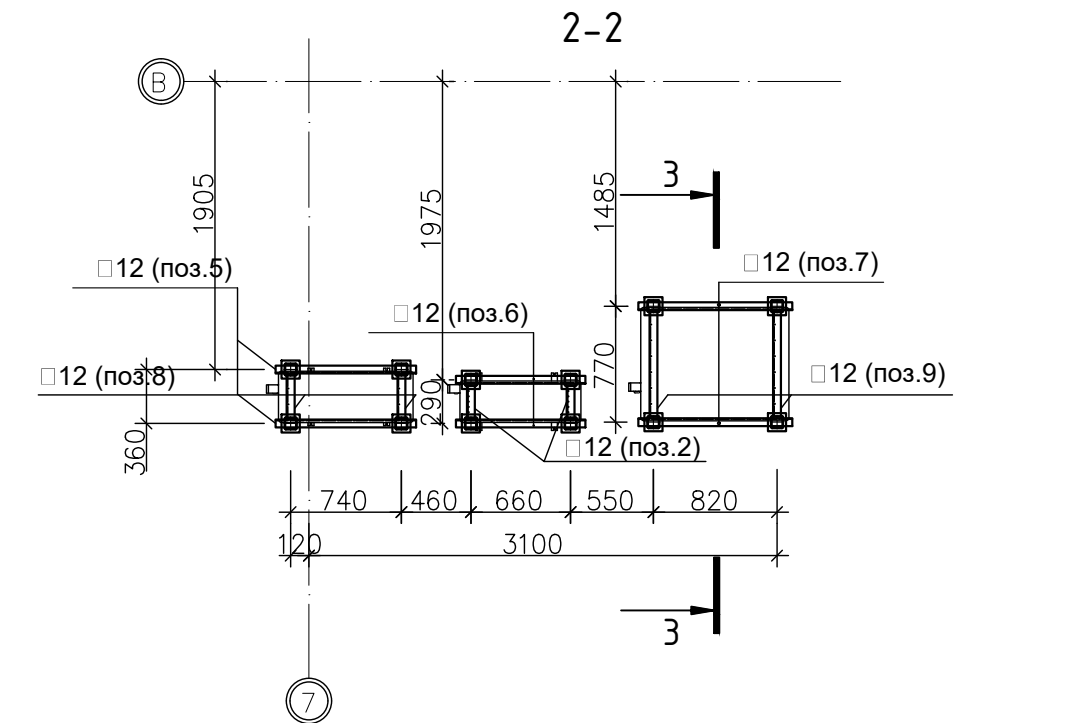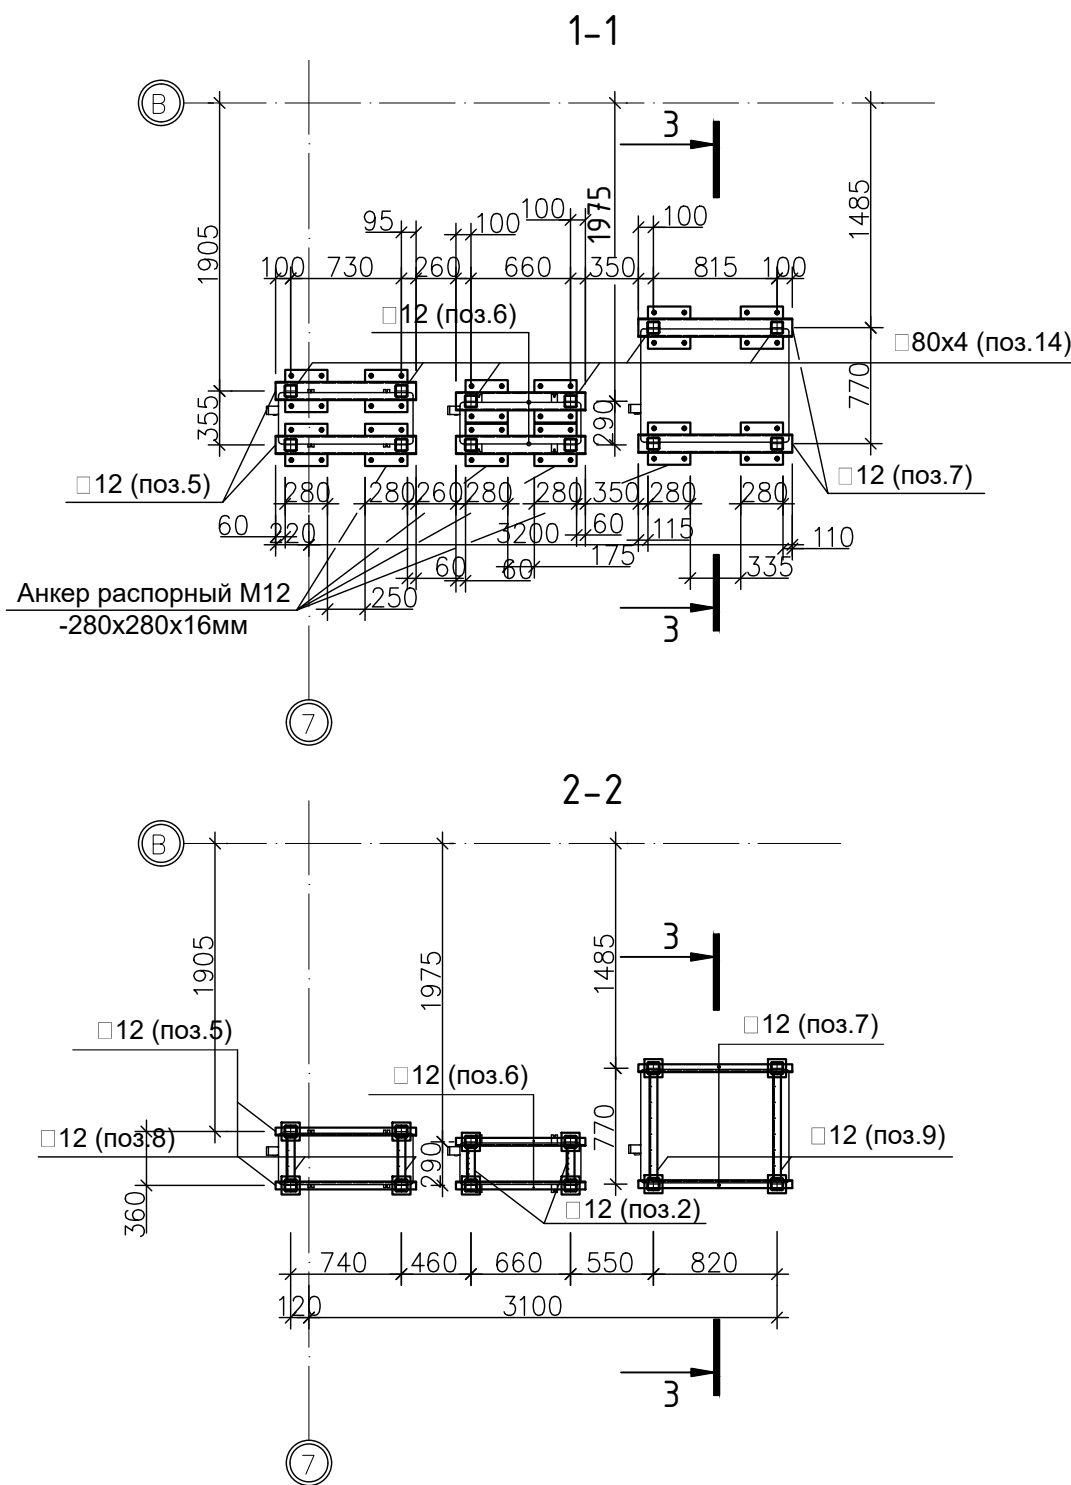

Примечание:
1. Материал для металлических конструкций – сталь С245 по ГОСТ 27772-2021;
2. Сварные соединения – по ГОСТ 5264-80. Электродом Э-42 по ГОСТ 9467-75*;
3. * Размеры уточнить при монтаже
4. Минимальный катет сварного шва – по наименьшей толщине свариваемых элементов;
5. Все конструкции окрасить одним слоем эмали ПФ-115 ГОСТ 6465-76 по двум слоям грунта ГФ-021 ГОСТ 25129-82.

						708/П-24-АНО-КР			
						Капитальный ремонт общеобразовательного учреждения ГБОУ "Школа №1210" по адресу: г. Москва, ул. Живописная, д.32			
Изм.	Колуч.	Лист	№ док.	Подп.	Дата	Конструктивные решения	Стадия	Лист	Листов
Разработал	Торшин				04.26		Р	74	
ГАП	Фролова				04.26				
						Схема рамы на кровле для оборудования кондиционирования в осях М/17, М/21, В/7		комплексное проектирование промышленных и гражданских объектов ООО "АРТИС"	
Н.Контроль	Лукашова				04.26				
ГИП	Зыкин				04.26				

Схема рамы на кровле для
оборудования кондиционирования
в осях В/7




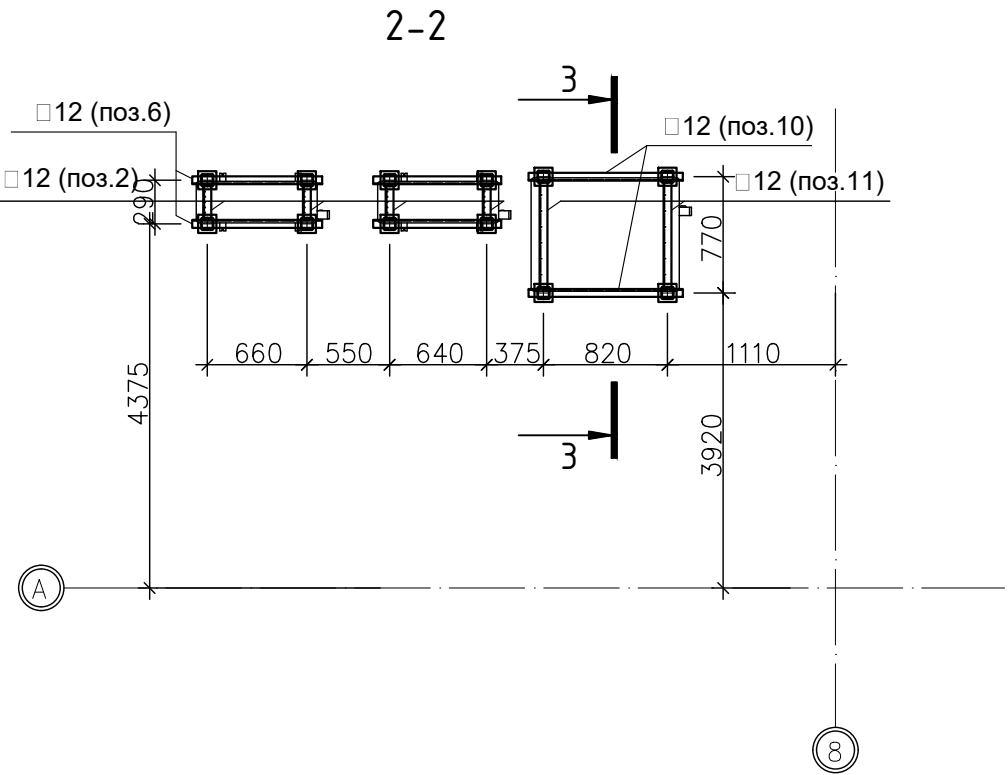


Схема рамы на кровле для
оборудования кондиционирования
в осях А/14-16

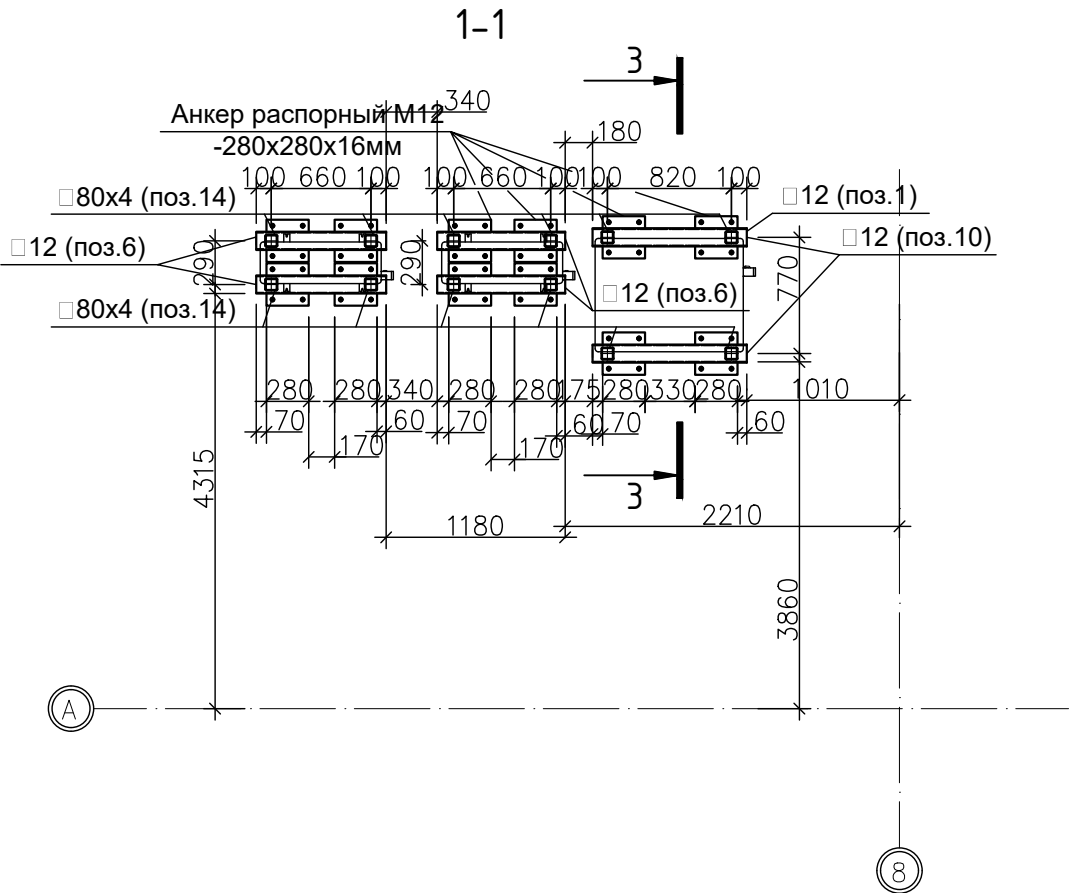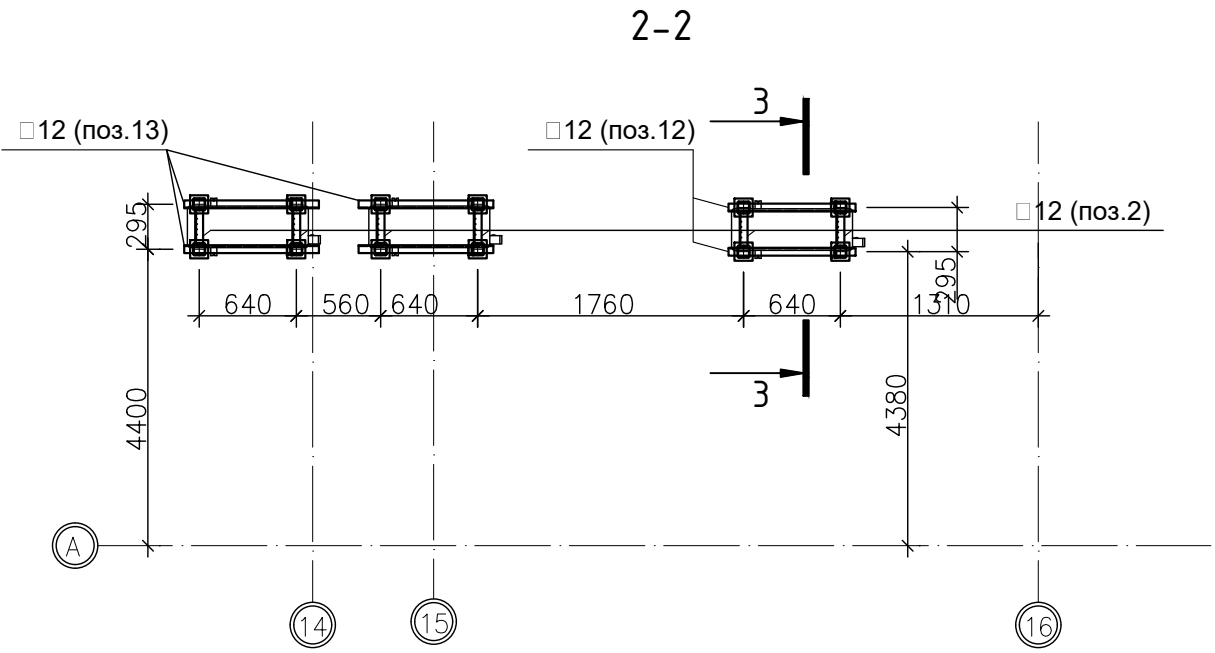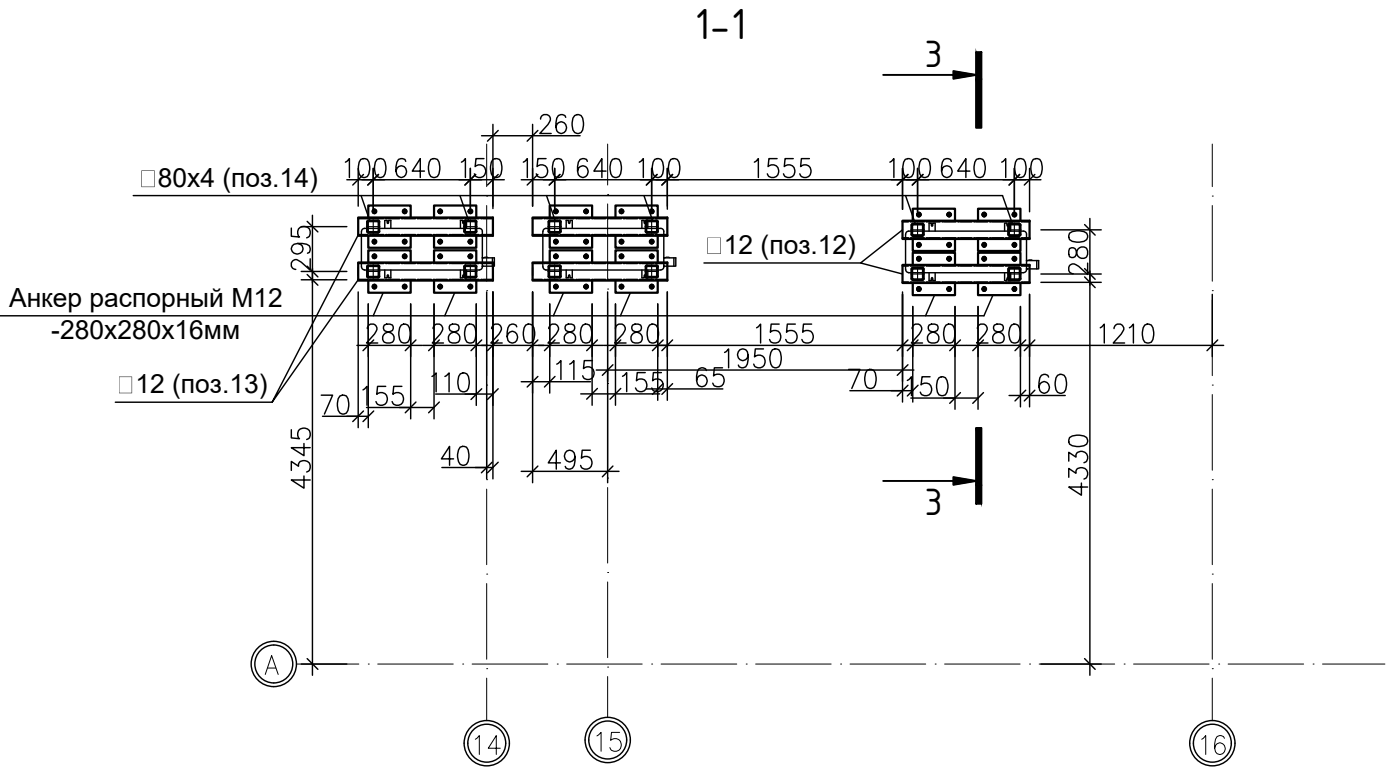

Согласовано				
Взам. инв. №				
Подп. и дата				
Инв. № подл.				

						708/П-24-АНО-КР			
						Капитальный ремонт общеобразовательного учреждения ГБОУ "Школа №1210" по адресу: г. Москва, ул. Живописная, д.32			
Изм.	Кол.уч.	Лист	№ док.	Подп.	Дата	Конструктивные решения	Стадия	Лист	Листов
Разработал	Торшин				04.26		Р	75	
ГАП	Фролова				04.26				
						Схема рамы на кровле для оборудования кондиционирования в осях В/7, А/14-16		комплексное проектирование промышленных и гражданских объектов ООО "АРТИС"	
Н.Контроль	Лукашова				04.26				
ГИП	Зыкин				04.26				

Спецификация материалов на изготовление рамы для оборудования кондиционирования

Поз.	Обозначение	Наименование	Кол.	Масса ед, кг	Примечание общ. вес кг
1	ГОСТ 8240-89	Швеллер 12 L=910 мм	8	9,46	75.7
2	ГОСТ 8240-89	Швеллер 12 L=240 мм	14	2,50	35.0
3	ГОСТ 8240-89	Швеллер 12 L=1055 мм	12	10,97	131.6
4	ГОСТ 8240-89	Швеллер 12 L=690 мм	6	7,18	43.1
5	ГОСТ 8240-89	Швеллер 12 L=925 мм	4	9,62	38.5
6	ГОСТ 8240-89	Швеллер 12 L=860 мм	12	8,94	107.3
7	ГОСТ 8240-89	Швеллер 12 L=1015 мм	4	10,56	42.2
8	ГОСТ 8240-89	Швеллер 12 L=310 мм	2	3,22	6.4
9	ГОСТ 8240-89	Швеллер 12 L=770 мм	2	8,01	16.0
10	ГОСТ 8240-89	Швеллер 12 L=1020 мм	4	10,61	42.4
11	ГОСТ 8240-89	Швеллер 12 L=720 мм	2	7,49	15.0
12	ГОСТ 8240-89	Швеллер 12 L=840 мм	4	8,74	35.0
13	ГОСТ 8240-89	Швеллер 12 L=890 мм	8	9,26	74.1
14	ГОСТ 30245-2003	Профиль 80x80x4 L=580 мм	56	5.4	302.4
15	ГОСТ 19903-2015	Лист 280x280x6	56	3,67	205.5
16		Анкер распорный M12x100	224		

Согласовано		



Взам. инв. №	
Подп. и дата	
Инв. № подл.	

						708/П-24-АНО-КР
						Капитальный ремонт общеобразовательного учреждения ГБОУ "Школа №1210" по адресу: г. Москва, ул. Живописная, д.32
Изм.	Кол.уч.	Лист	№ док.	Подп.	Дата	
Разработал	Торшин				04.26	
ГАП	Фролова				04.26	Конструктивные решения
Н.Контроль	Лукашова				04.26	Спецификация материалов на изготовление рамы для оборудования кондиционирования
ГИП	Зыкин				04.26	



комплексное проектирование промышленных и
гражданских объектов
ООО "АРТИС"

Согласовано		Взам. инв. №	Подп. и дата	Инв. № подл.

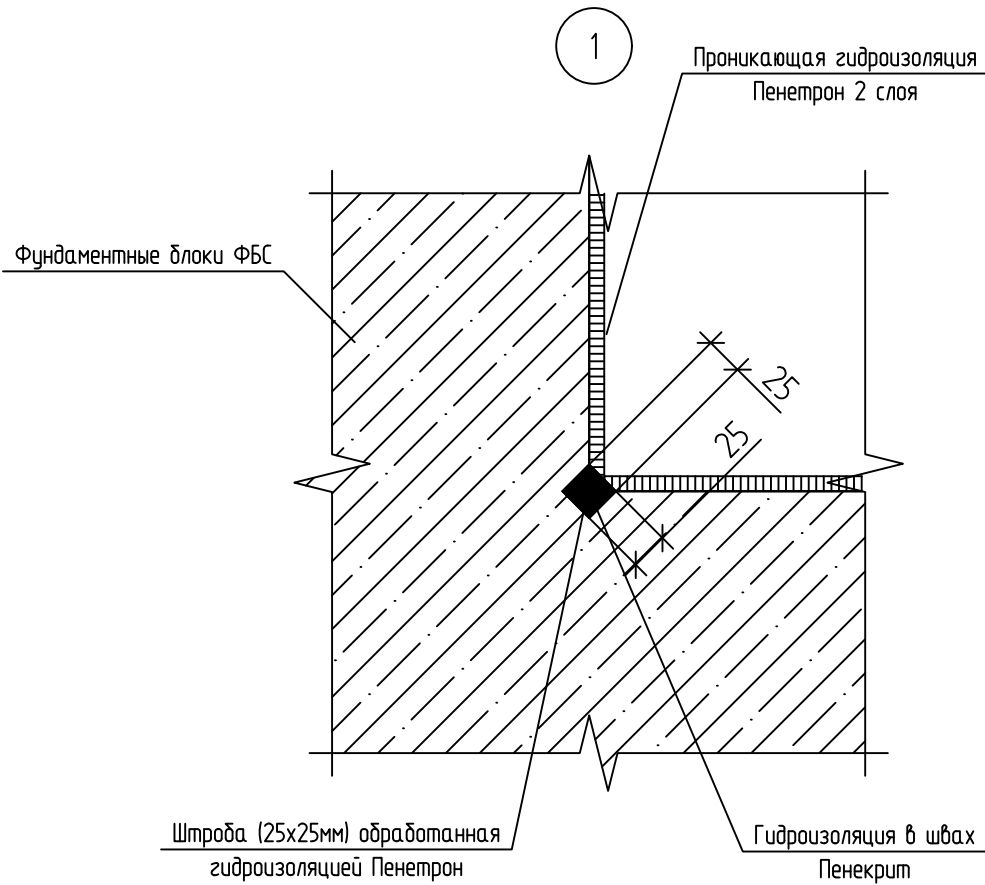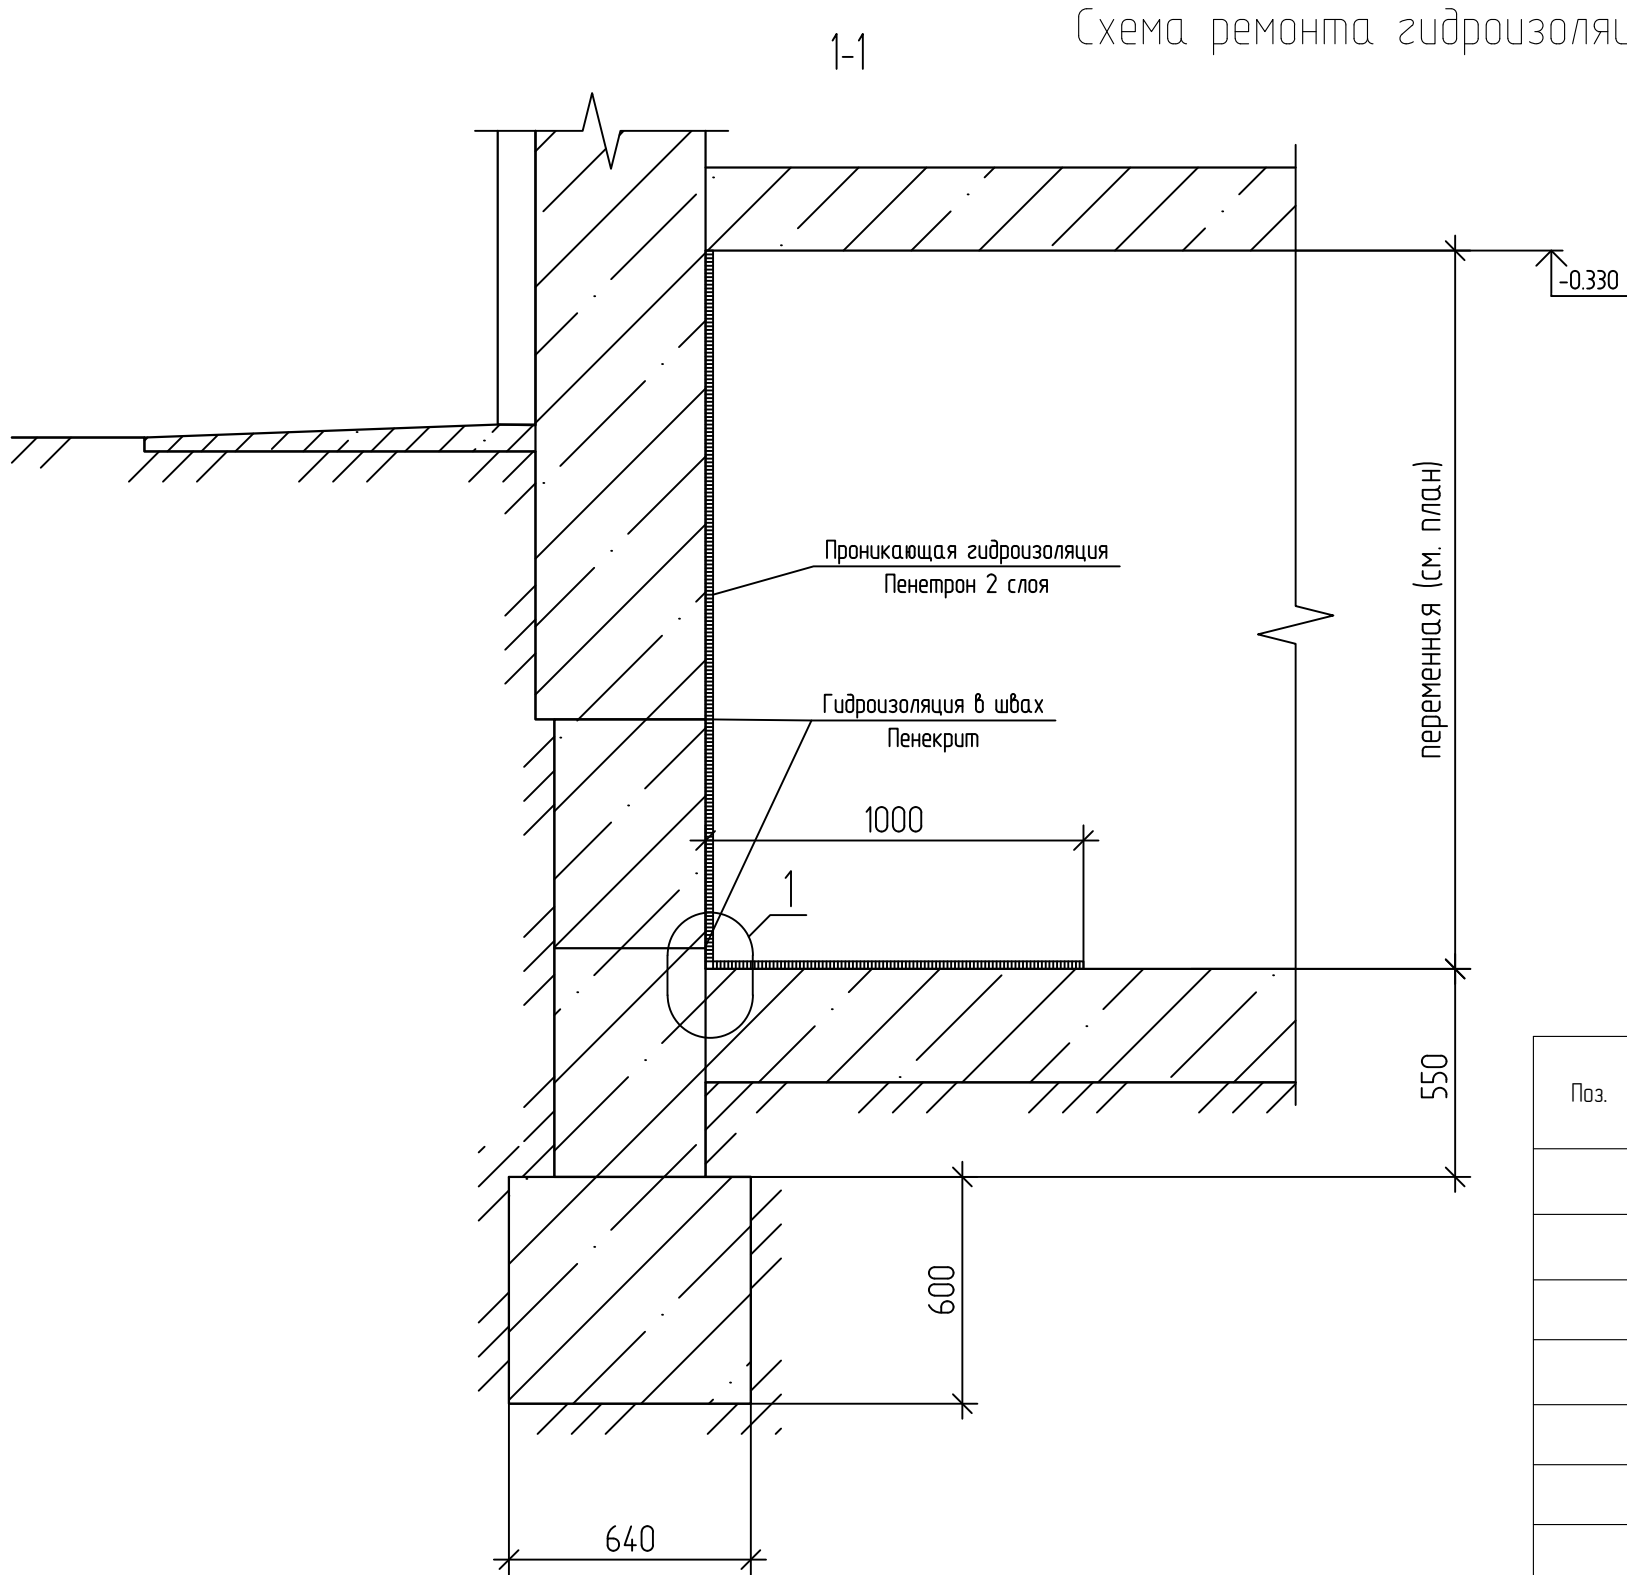

Спецификация материалов на устройство гидроизоляции стен подвала


Поз.	Обозначение	Наименование	Кол.	Масса ед, кг	Примечание общ. вес кг
		Подготовка поверхности стен (очистка), м ²	1081		
		Гидроизоляция стен стен (2 раза) , м ²	2120		
		Устройство штробы в швах бетонных элементов 25х25мм, п.м.	1020		
		Материалы			
	ТУ 5745-001-77921756-2006	Шовный состав Пенекрит, кг.	1530	1,5 кг/м.п.	
	ТУ 5745-001-77921756-2006	Проникающая гидроизоляция Пенетрон, кг	2332	1,1 кг/м ²	

- Порядок выполнения работ:
1. Стены очистить от грязи, пыли, осушить.
 2. Выполнить штробу размерами 25х25мм вдоль всех швов.
 3. Штробу обработать раствором смеси Пенетрон.
 4. Заполнить швы составом Пенекрит. Так же составом Пенекрит обработать трещины, сколы и ямки шириной более 0.4мм
 5. Обработать поверхности проникающей гидроизоляцией Пенетрон в 2 слоя.
 6. Выполнить отделку стен подвала не ранее 28 дней после устройства гидроизоляции.
 7. Все работы вести в соответствии с техкартой фирмы Пенетрон.

						708/П-24-АНО-КР			
						Капитальный ремонт общеобразовательного учреждения ГБОУ "Школа №1210" по адресу: г. Москва, ул. Живописная, д.32			
Изм.	Кол.уч.	Лист	№ док.	Подп.	Дата	Конструктивные решения	Стадия	Лист	Листов
Разработал	Торшин				04.26		Р	76	
ГАП	Фролова				04.26				
						Схема ремонта гидроизоляции стен подвала		комплексное проектирование промышленных и гражданских объектов ООО "АРТИС"	
Н.Контроль	Лукашова				04.26				
ГИП	Зыкин				04.26				

Согласовано			
Взам. инв. №			
Подп. и дата			
Инв. № подл.			

Инъектирование трещин в межблочных стеновых швах

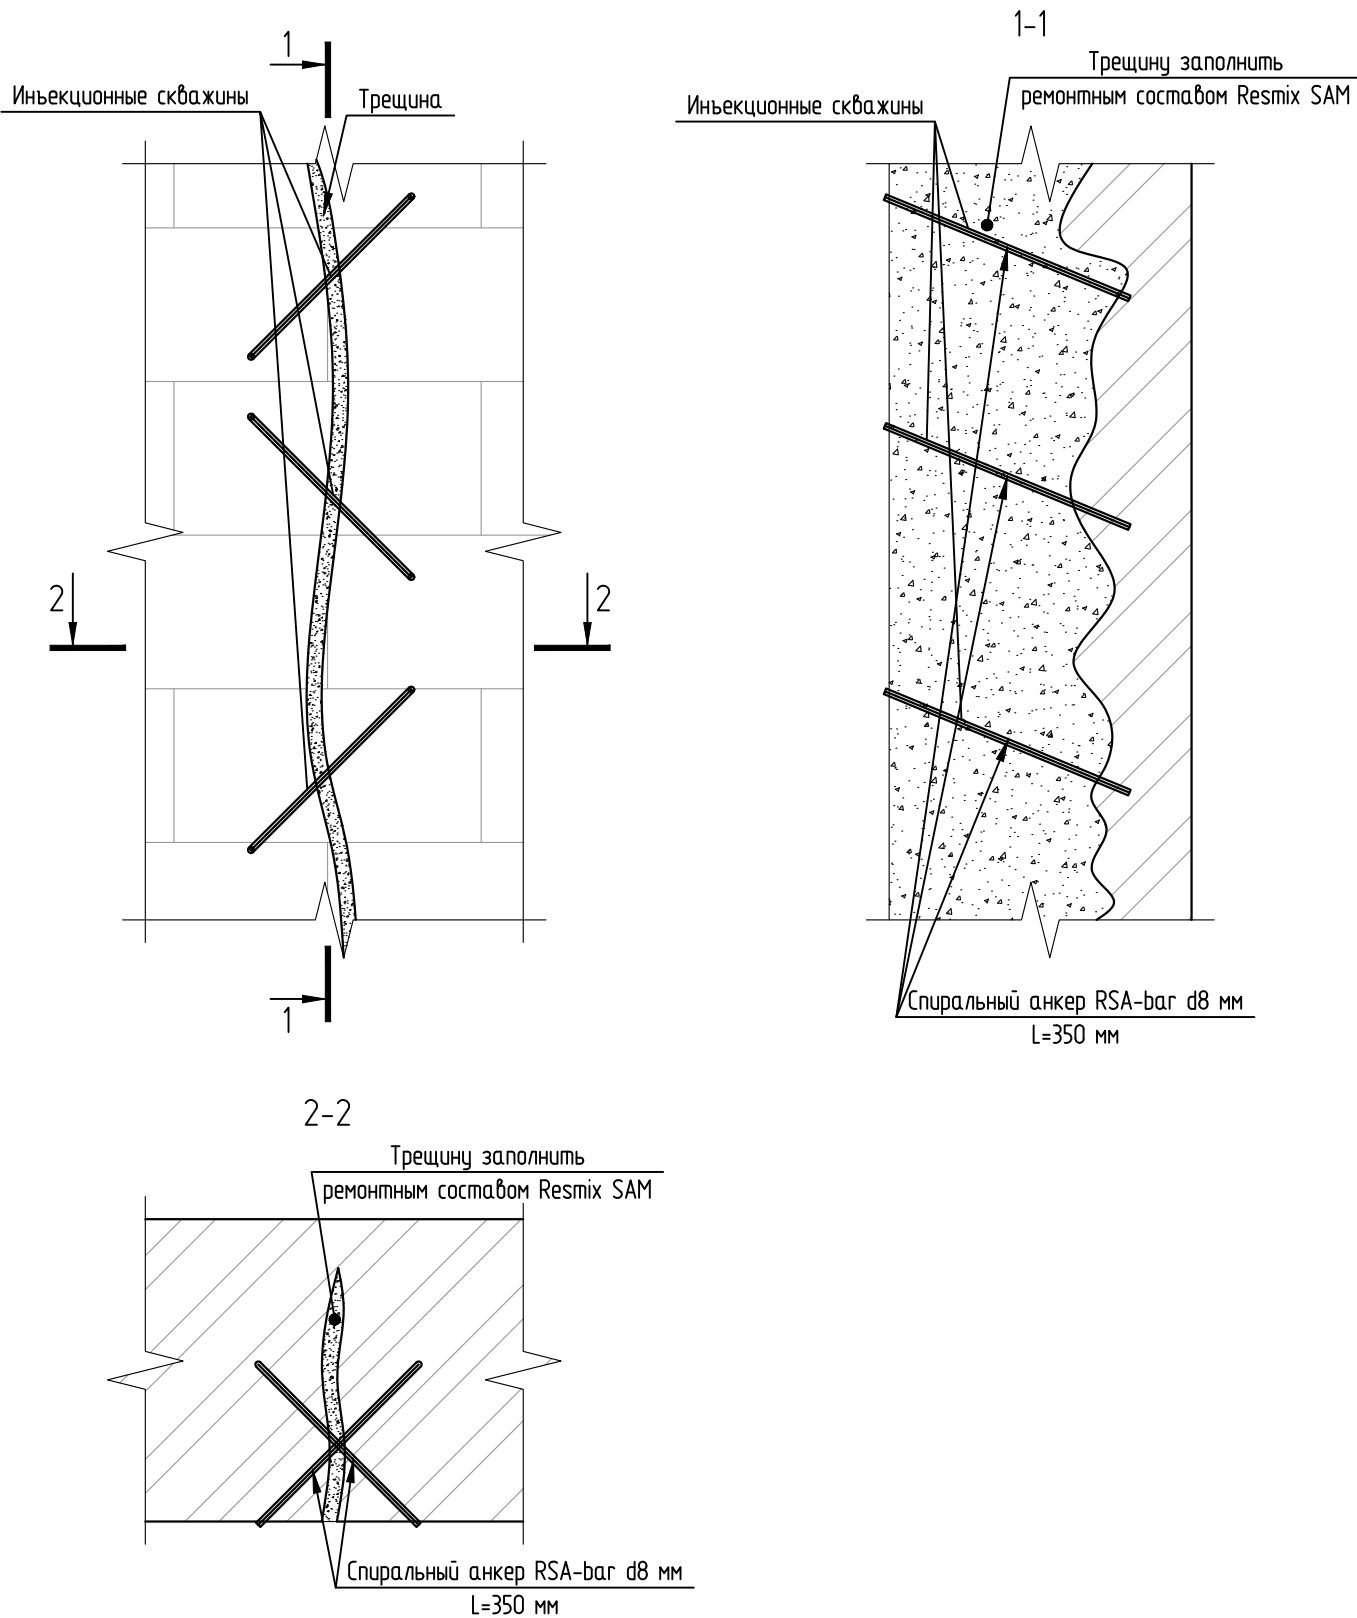


Спецификация к ремонту стен

Поз.	Обозначение	Наименование	Кол.	Масса, ед., кг	Примечание
		Работы по инъектированию трещин в блочной кладке, п.м.	14		
		Бурения шпуров 18 мм и расположения пакеров для инъектирования на расстоянии L=500мм, шт	56		
		Спиральный анкер RSA-bar d8 мм, L=350 мм, шт	56		
		Заполнение ремонтным составом Resmix SAM (h трещины=5мм), м³	0.03	48	Расход 1.6м³/м³

- Порядок производства работ:
1. Бурение отверстий (шпуров) $\phi 26$ с шагом 500 мм под углом 30° - 40° .
 2. Очистка поверхностей трещин.
 3. Инъекции скважин ремонтным составом Resmix SAM. Инъекция скрепляющего раствора производится под давлением до 0.6 МПа.
 4. Установка спиральных анкеров RSA-bar d8 мм с шагом 500 мм.
 5. Затирка трещин и пустых швов цементным раствором.




						708/П-24-АНО-КР			
						Капитальный ремонт общеобразовательного учреждения ГБОУ "Школа №1210" по адресу: г. Москва, ул. Живописная, д.32			
Изм.	Кол.уч.	Лист	№ док.	Подп.	Дата	Конструктивные решения	Стадия	Лист	Листов
Разработал	Торшин				04.26		Р	77	
ГАП	Фролова				04.26				
						Инъектирование трещин в межблочных стеновых швах		комплексное проектирование промышленных и гражданских объектов	
Н.Контроль	Лукашова				04.26			ООО "АРТИС"	
ГИП	Зыкин				04.26				

Инв. № подл.	Подп. и дата	Взам. инв. №	Согласовано		

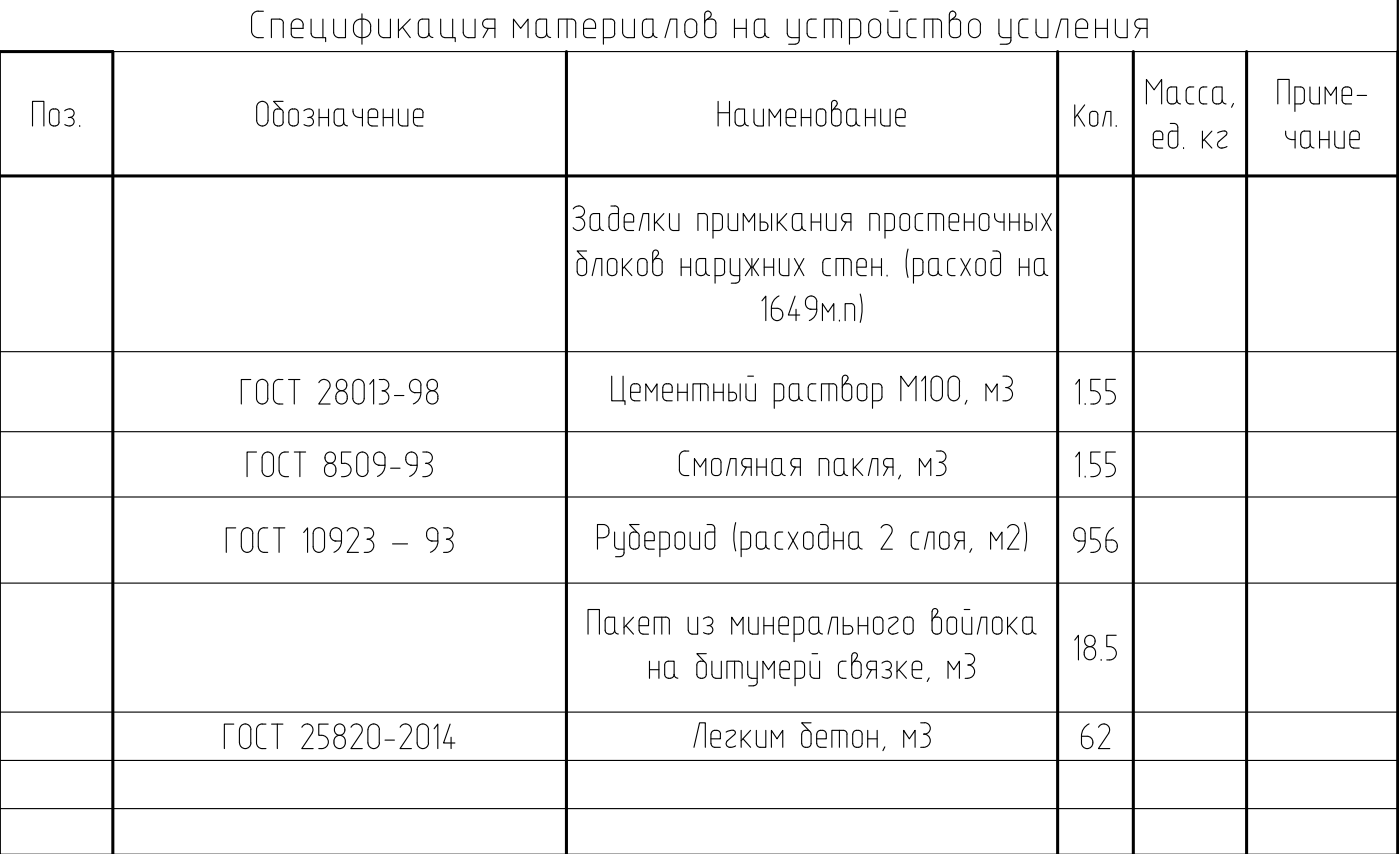


- | | | | | | | | | | |
|------------|----------|------|--------|---|-------|---|---|---|-------------|
| | | | | | | 708/П-24-АНО-КР | | | |
| | | | | | | Капитальный ремонт общеобразовательного учреждения
ГБОУ "Школа №1210" по адресу: г. Москва, ул. Живописная, д.32 | | | |
| Изм. | Кол.уч. | Лист | № док. | Подп. | Дата | Конструктивные решения | Стадия | Лист | Листов |
| Разработал | Торшин | | |  | 04.26 | | Р | 78 | |
| ГАП | Фролова | | |  | 04.26 | | | | |
| | | | | | | Узел заделки примыкания простеночных блоков
наружных стен из крупноблочных
керамзитобетонных блоков |  | комплексное проектирование промышленных и
гражданских объектов | ООО "АРТИС" |
| Н.Контроль | Лукашова | | |  | 04.26 | | | | |
| ГИП | Зыкин | | |  | 04.26 | | | | |

Схемы устройства рам для установки баскетбольных щитов

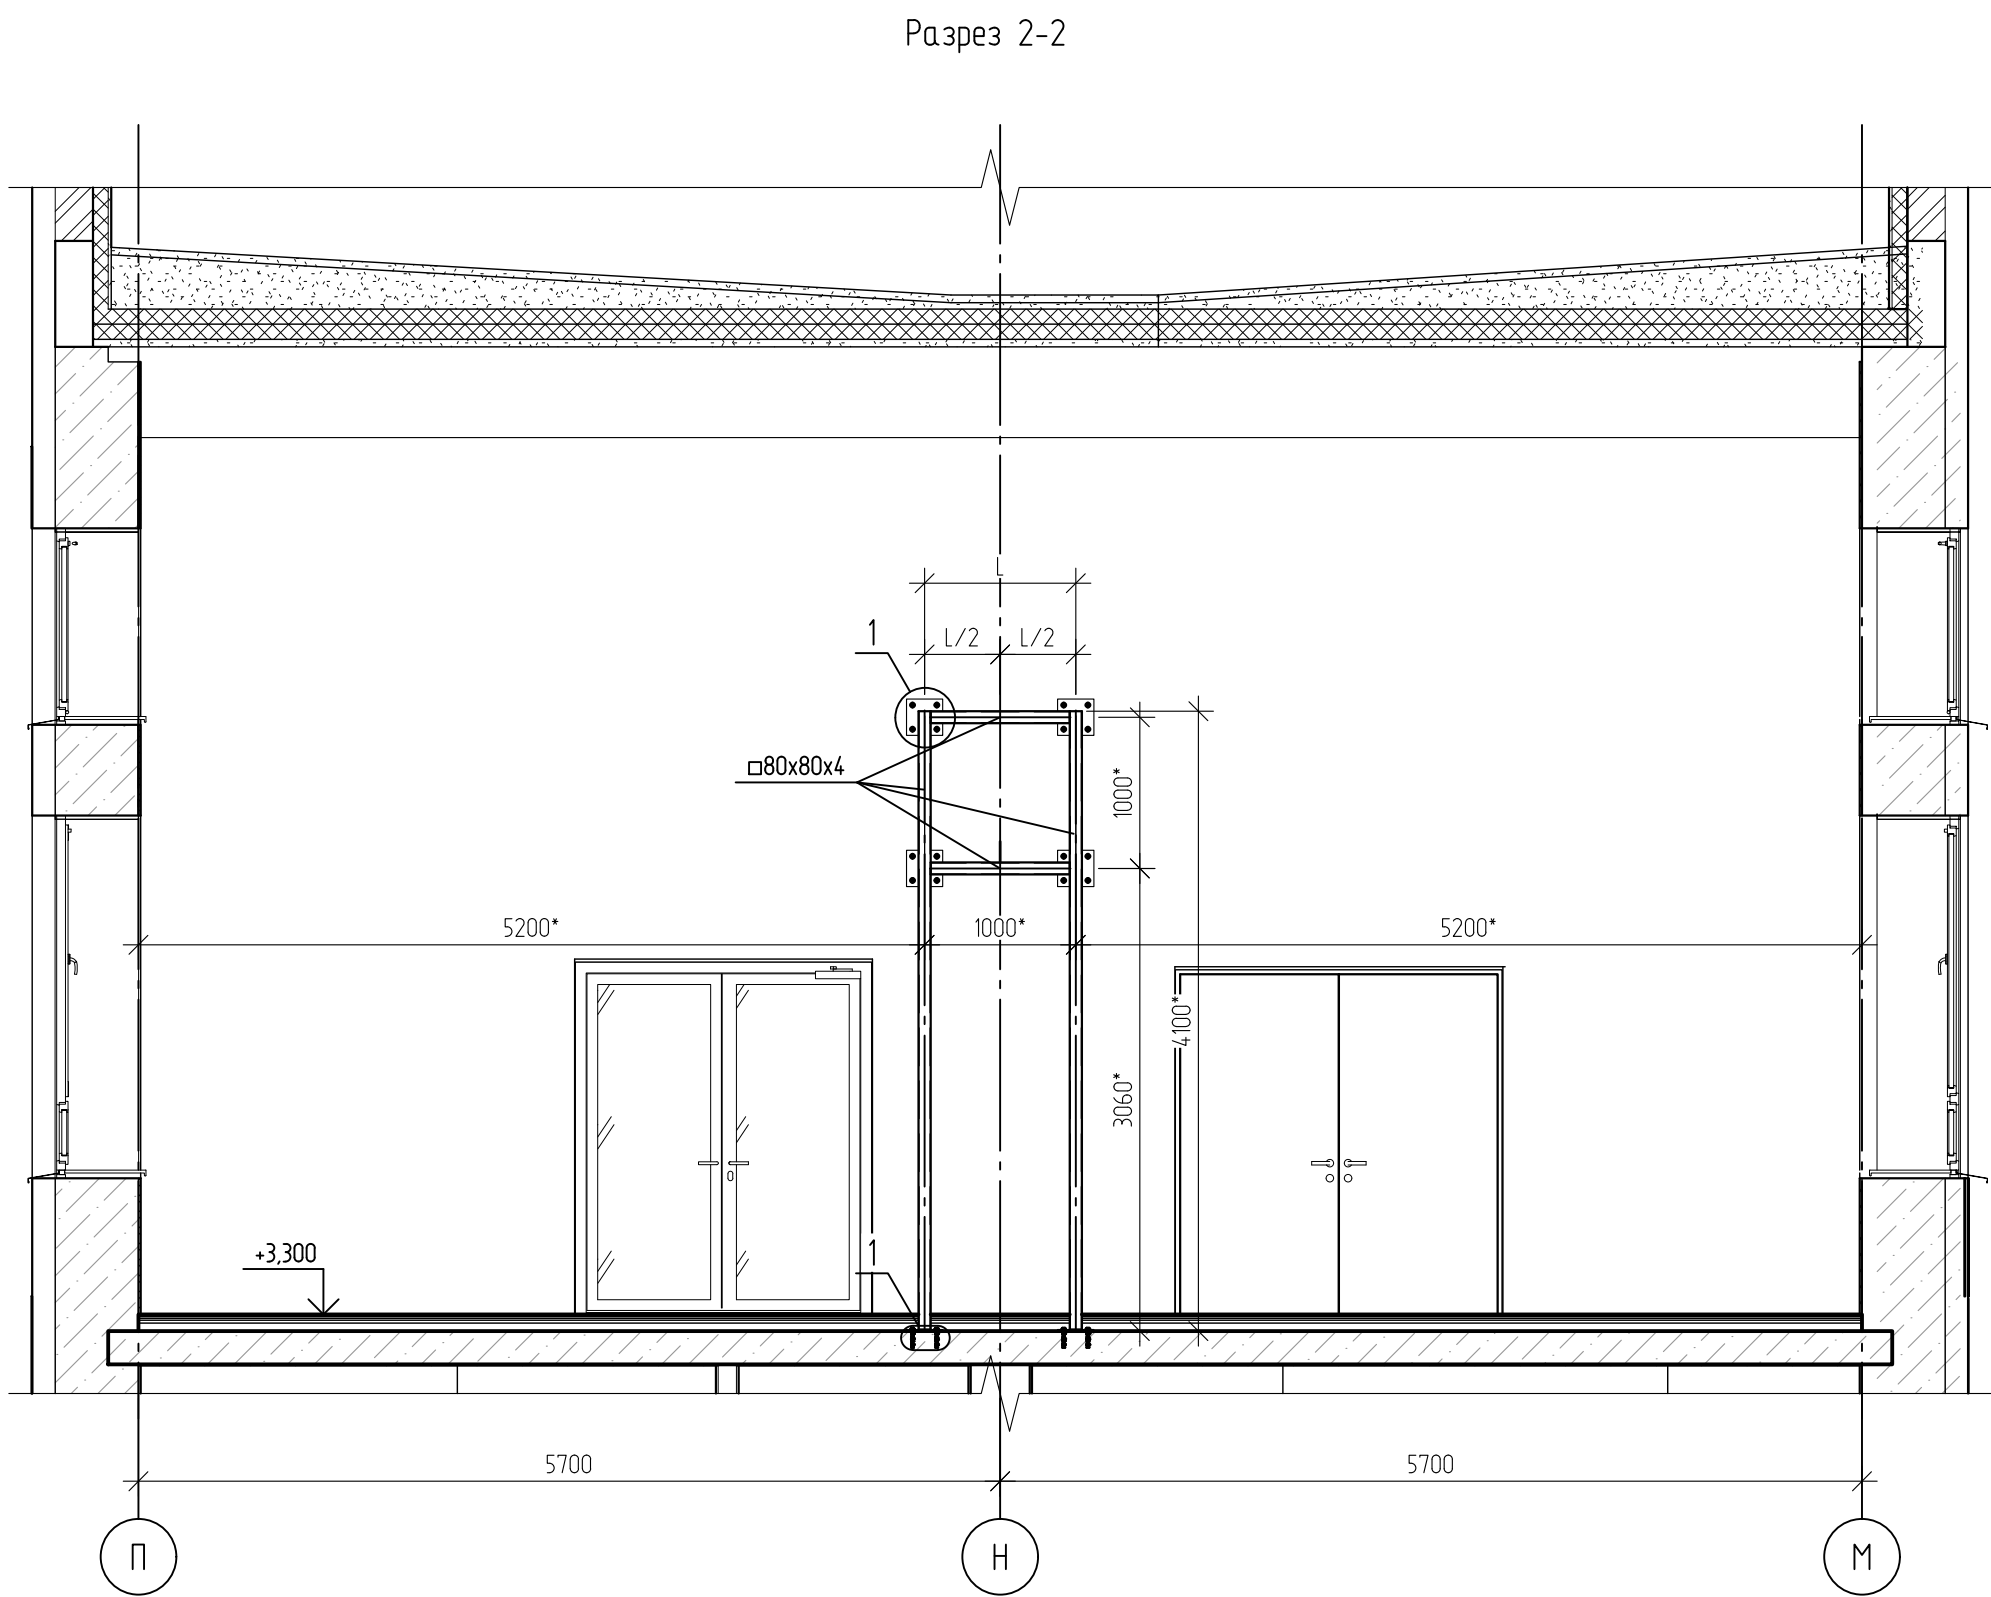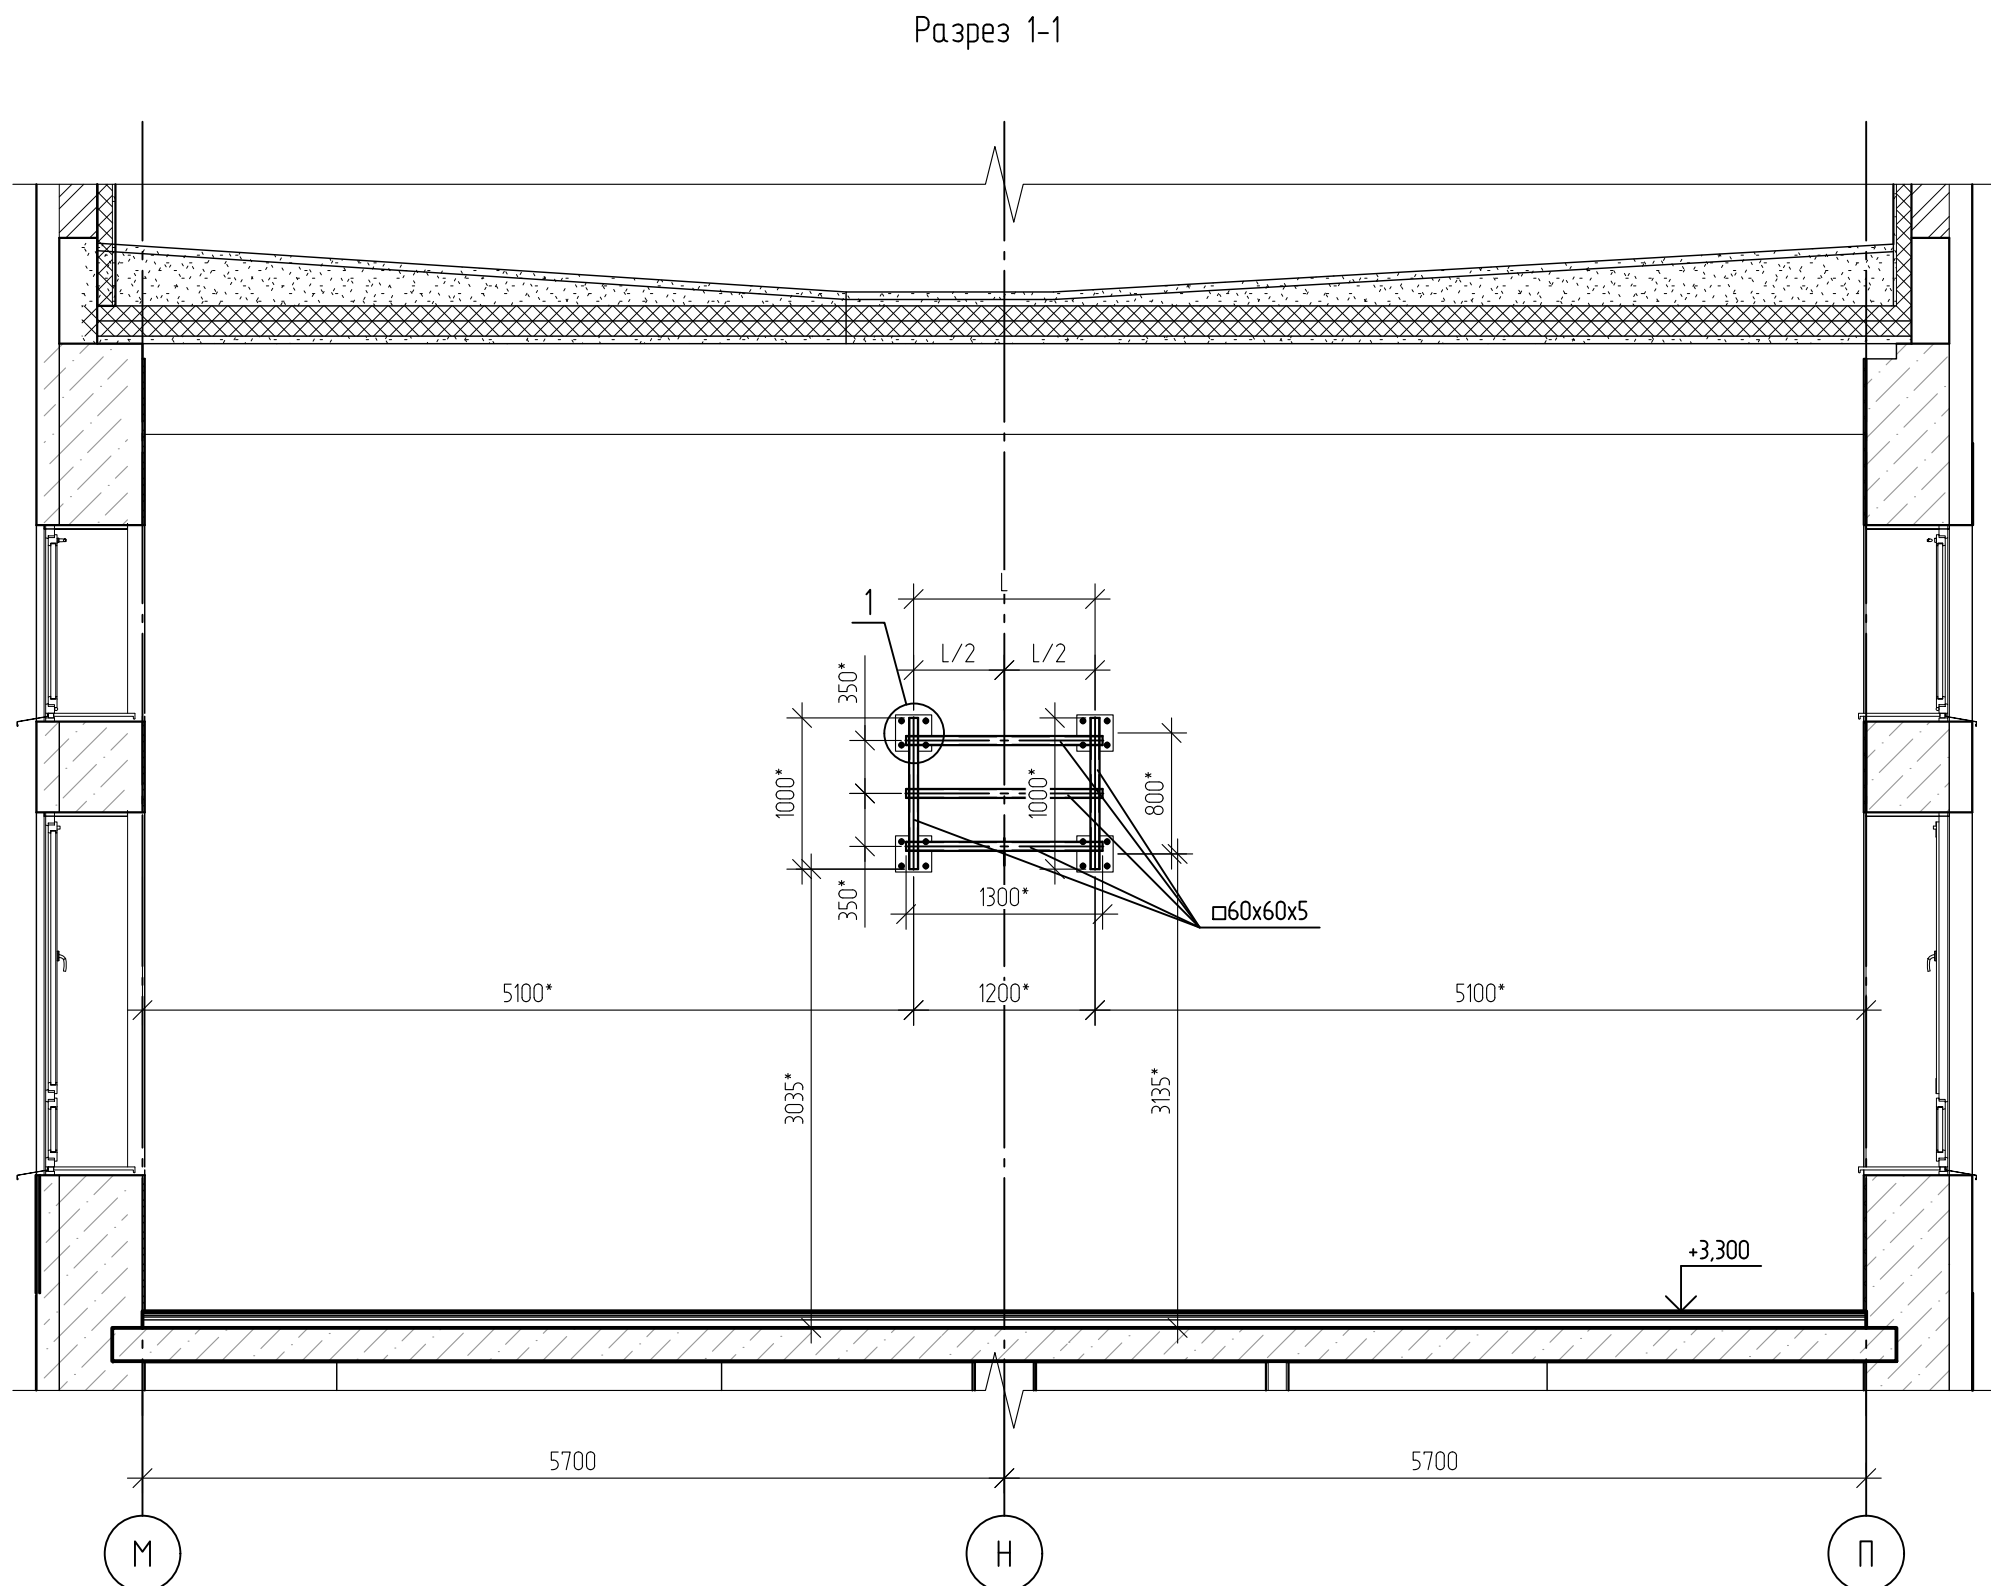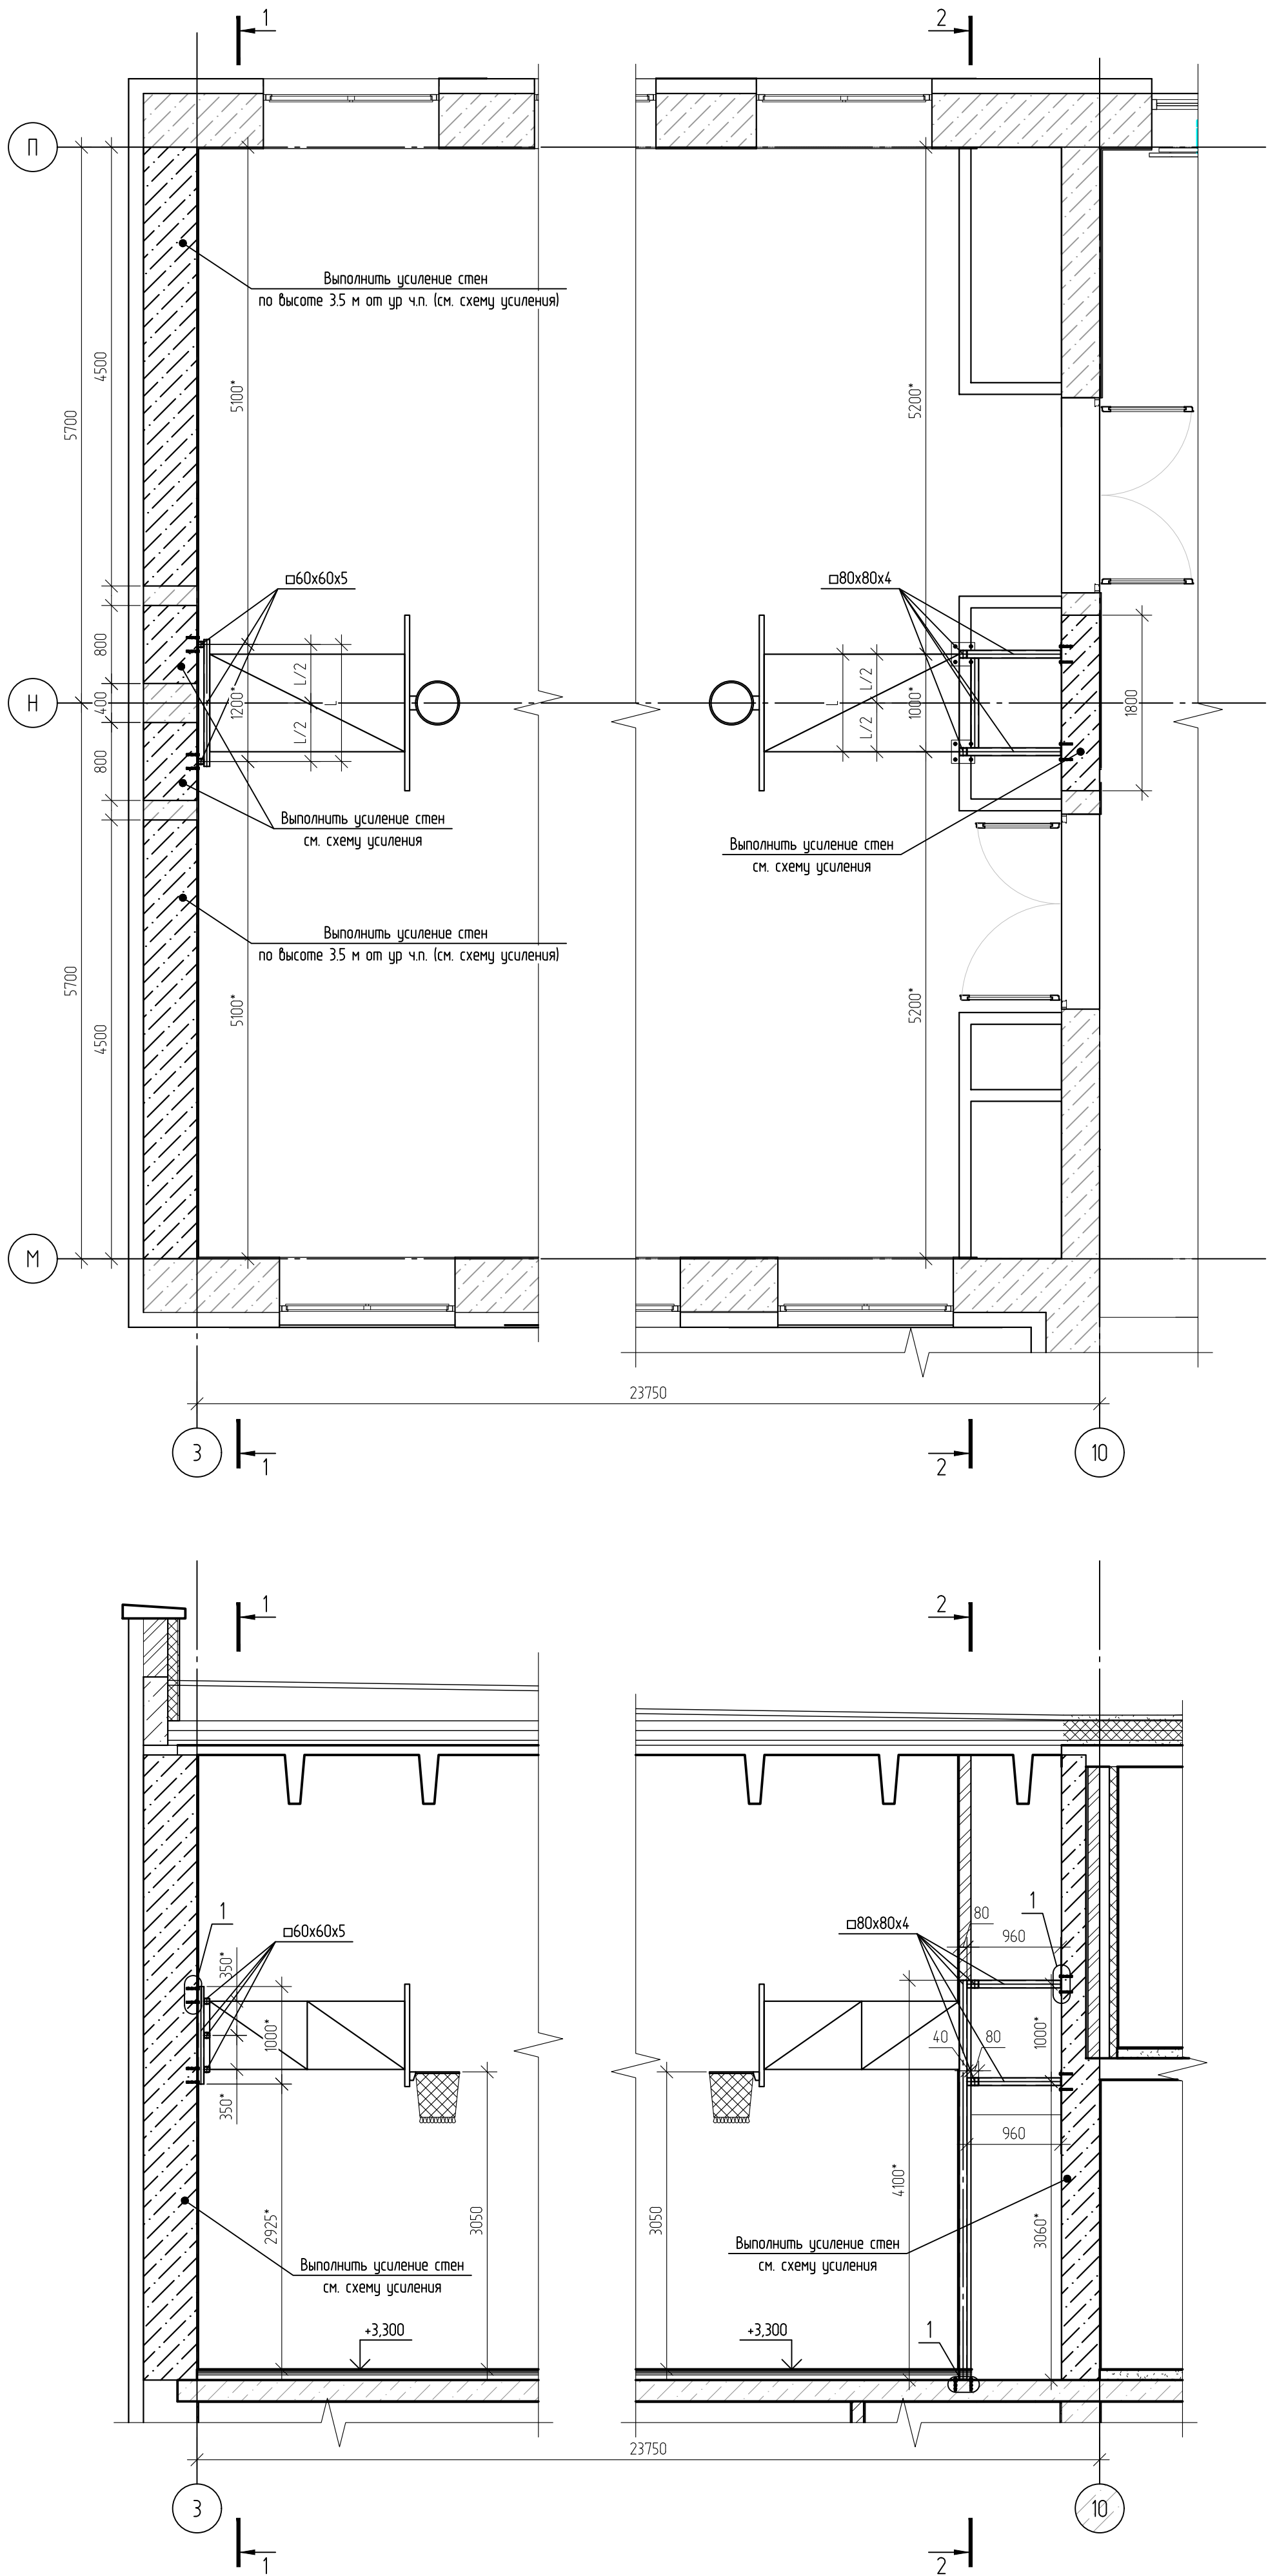


Спецификация материалов на устройство рам для закрепления баскетбольных щитов					
Поз.	Обозначение	Наименование	Кол.	Масса 1 дет.,кг	Примеч. общ. вес кг
		Рама по оси "З"	1		
	ГОСТ 30245-2003	с60х60х5, п.м.	6,1	8,13	4959
	ГОСТ 19903-2015	-240х240х10 мм, шт	4	4,5	18
		Химический анкер на шпильке М18, шт	16		
	ГОСТ 6958-70	Шайба 18, шт	16		
	ГОСТ 5915-70	Гайка М18, шт	16		
		Рама по оси "Ю"	1		
	ГОСТ 30245-2003	с80х80х4, п.м.	13,6	9,8	13328
	ГОСТ 19903-2015	-240х240х10 мм, шт	6	4,5	27
		Химический анкер на шпильке М18, шт	24		
	ГОСТ 6958-70	Шайба 18, шт	24		
	ГОСТ 5915-70	Гайка М18, шт	24		

Спецификация материалов на устройство усиления стен					
Поз.	Обозначение	Наименование	Кол.	Масса 1 дет.,кг	Примеч. общ. вес кг
	ГОСТ 28013-98	Цементно-песчаный раствор М300, м³	13,3		

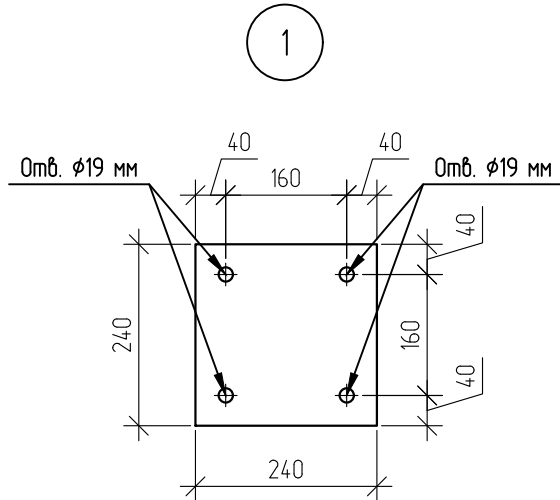

Схемы усиления стен в местах крепления спортивного инвентаря

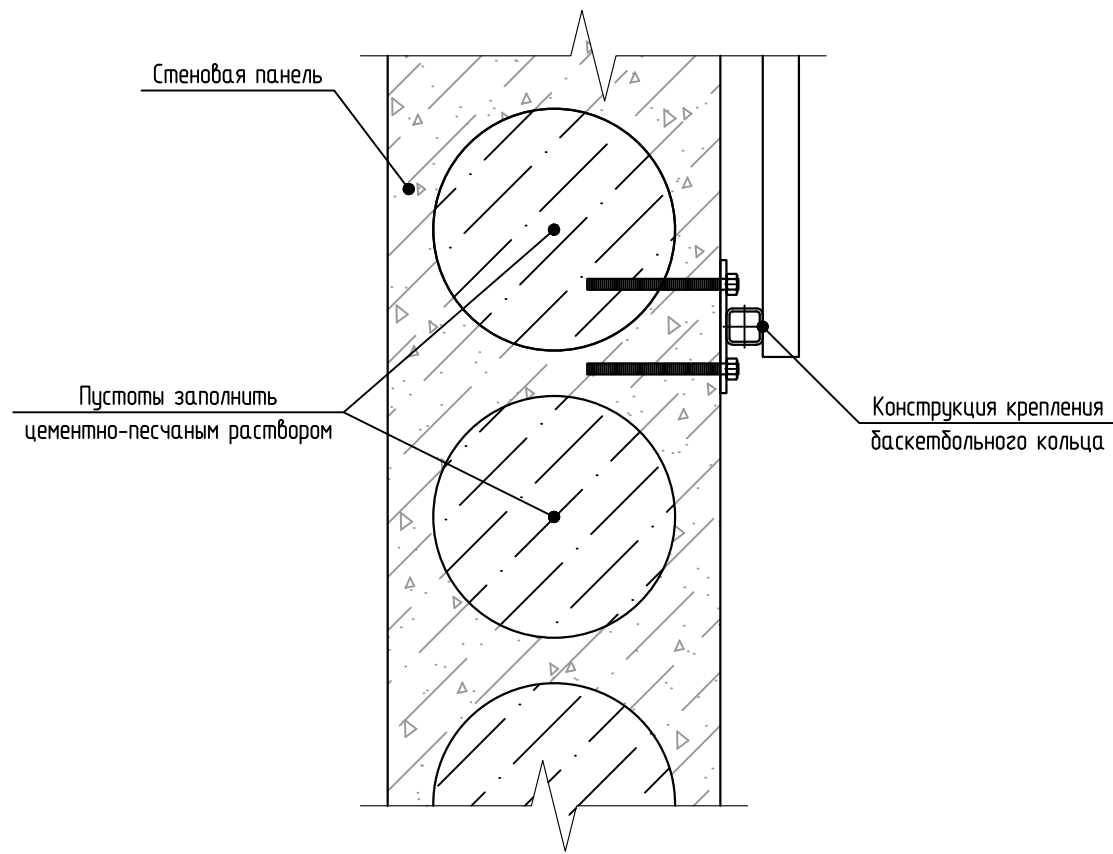

Примечание:
1. Рекомендуемый к установке спортивный инвентарь от производителя "Спортивные технологии".
Наименование товара: "Баскетбольный щит из закаленного стекла 10 мм, со складной фермой 2000-3200 мм, амортизационным кольцом и протектором СТ-200". Код товара: sp10019025.
2. Вылет баскетбольного щита согласовать с производителем.
3. На чертеже конструкция баскетбольного кольца показана условно.
4. Размеры с обозначением "*" уточнить по месту после поставки инвентаря на объект.
5. Материал для металлических конструкций - сталь С235 по ГОСТ 27772-2020.
6. Сварные соединения - по ГОСТ 5264-80. Электродами Э-42 по ГОСТ 9467-75*.
7. Минимальный катет сварного шва - по наименьшей толщине свариваемых элементов.
8. Все конструкции окрасить одним слоем эмали ПФ-115 ГОСТ 6465-76 по двум слоям грунта ГФ-021 ГОСТ 25129-82.
9. В границах закрепления баскетбольных колец выполнить усиление стен путем заполнения пустот цементно-песчаным раствором на всю их высоту.

708/П-24-АНД-КР					
Капитальный ремонт общеобразовательного учреждения ГБОУ "Школа №1210" по адресу: г. Москва, ул. Животочная, д.32					
Изм.	Копуч	Лист	№ док	Подп.	Дата
Разработал	Горшин	79	04.26	04.26	04.26
ГАП	Фролова	Р	79	04.26	04.26
Конструктивные решения					
Схемы устройства рам для установки баскетбольных щитов					
Н.Контроль	Лукашова	04.26	04.26	04.26	04.26
ГИП	Зыкин	04.26	04.26	04.26	04.26

Technical drawing of a building section showing a staircase and a curved wall. The drawing includes dimensions, elevations, and section markers.

Dimensions:

- Staircase height: 1200
- Horizontal distance from staircase to curved wall: 12905.2965
- Vertical distance from staircase to curved wall: 900
- Vertical distance from staircase to curved wall: 1200

Elevations:

- +3,450
- +3,600
- +3,300
- +3,750
- +4,200
- +3,750
- +3,600
- +3,450

Section Markers:

- 1
- 2

Curved Wall Details:

- Radii: R900, R1200, R1500, R1800
- Angle: 28°35'

Other Labels:

- M
- 14
- 17

Technical drawing of a building section, showing a long, low structure with a curved end. The drawing includes dimensions in millimeters and meters, and labels for structural elements like 'Стойка' (post) and 'П856', 'R1738', 'R1438', 'R856'. The section is labeled 'М' and '1'.

Technical drawing of a metal structure detail, likely a staircase or platform, showing dimensions and components. The drawing includes labels for materials like "Лист стальной 5 мм" (5 mm steel sheet) and "Покрытие см. АР" (coating see AR). Dimensions are given in millimeters and meters. A section line "П" is indicated at the bottom right.

Key dimensions and components shown:

- Overall width: 968 mm
- Overall height: 900 mm
- Material: Лист стальной 5 мм (5 mm steel sheet)
- Coating: Покрытие см. АР (coating see AR)
- Section line: П
- Other dimensions: 200, 29, 80, 32, 900, 475, 560, 32, 62, 900, 908, 230, 1, 925, 80x60x4, 60x4, 60x4, 4.200, 3.750, 3.300, 3.190.

2

80x60x4

80

ГОСТ 5264-80-T1-Б4

Ступица

60

Спецификация материалов и изделий на устройство зрительной трибуны на отм. +3.320 в осях 15-21/К								
Поз.	Обозначение	Наименование	Ед. изм.	Кол.	Масса, ед. кг		Примечание	Обоснование
					ед.	всего		
	ГОСТ 30245-2012	□80x60x4 (С245 ГОСТ 27772-2021)	пог.м.	133,8	7,97	1066,39		
		□60x60x4 (С245 ГОСТ 27772-2021)	пог.м.	48,9	6,71	328,12		
	ГОСТ 103-2006	-260x260x10 (С245 ГОСТ 27772-2021)	шт.	63	5,27	332,2		
		Дюбель-шпилька М12х130	шт.	252				
		Всего:				1726,7		
		Материалы						
	ГОСТ 103-2006	Лист стальной 5 мм (С245 ГОСТ 27772-2021)	м²	37,3				
	ГОСТ 25129-82	Грунтовка ГФ-021	м²	129,32				
	ТУ 5768-005-30642285-2016	Термобарьер Т	м²	129,32				
	ТУ 20.30.22-007-30642285-2017	Термобарьер 2	м²	129,32				
Демонтаж принимать в объеме монтажа								

а-а

Стойка
60x4

260x260x10

260

50

160

50

Дюбель-шпилька
M12x130

50

160


50

260

						708/П-24 - АНО-КР			
						Капитальный ремонт общеобразовательного учреждения ГБОУ "Школа №1210" по адресу: г. Москва, ул. Живописная, д.32			
Изм.	Колуч.	Лист	№ док.	Подп.	Дата	Конструктивные решения	Стадия	Лист	Листов
Разработал	Торшин				04.26		Р	80	
ГАП	Фролова				04.26				
						Схемы устройства зрительной трибуны		консалтинговое проектирование проектные и проектные работы ООО "АРТИС"	
НКонтроль	Лукашова				04.26				
ГИП	Зыкин				04.26				
							ООО "АРТИС"		

Согласовано					
Взам. инв. №					
Подп. и дата					
Инв. № подл.					

Схема устройства лестницы ПЛ-1

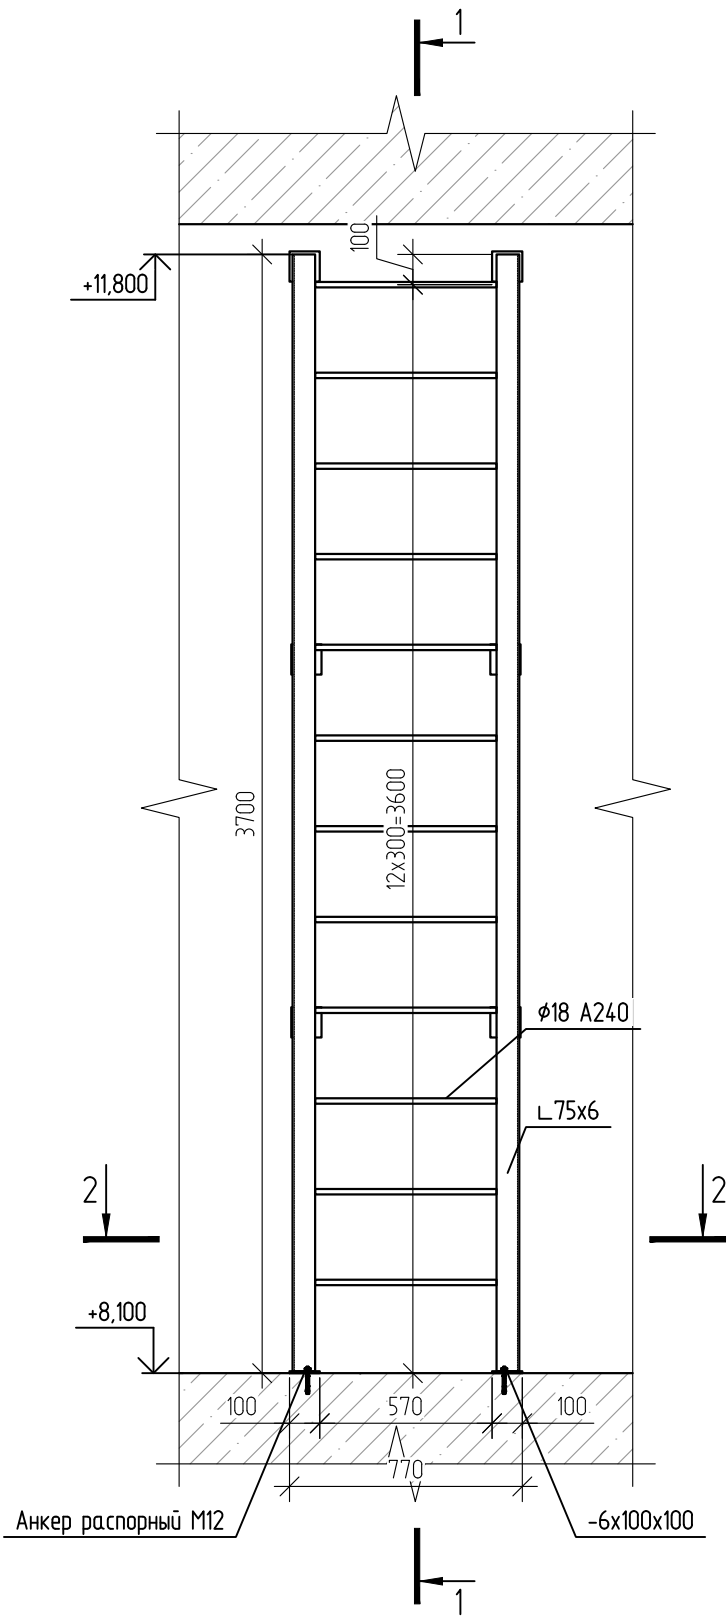

Разрез 1-1


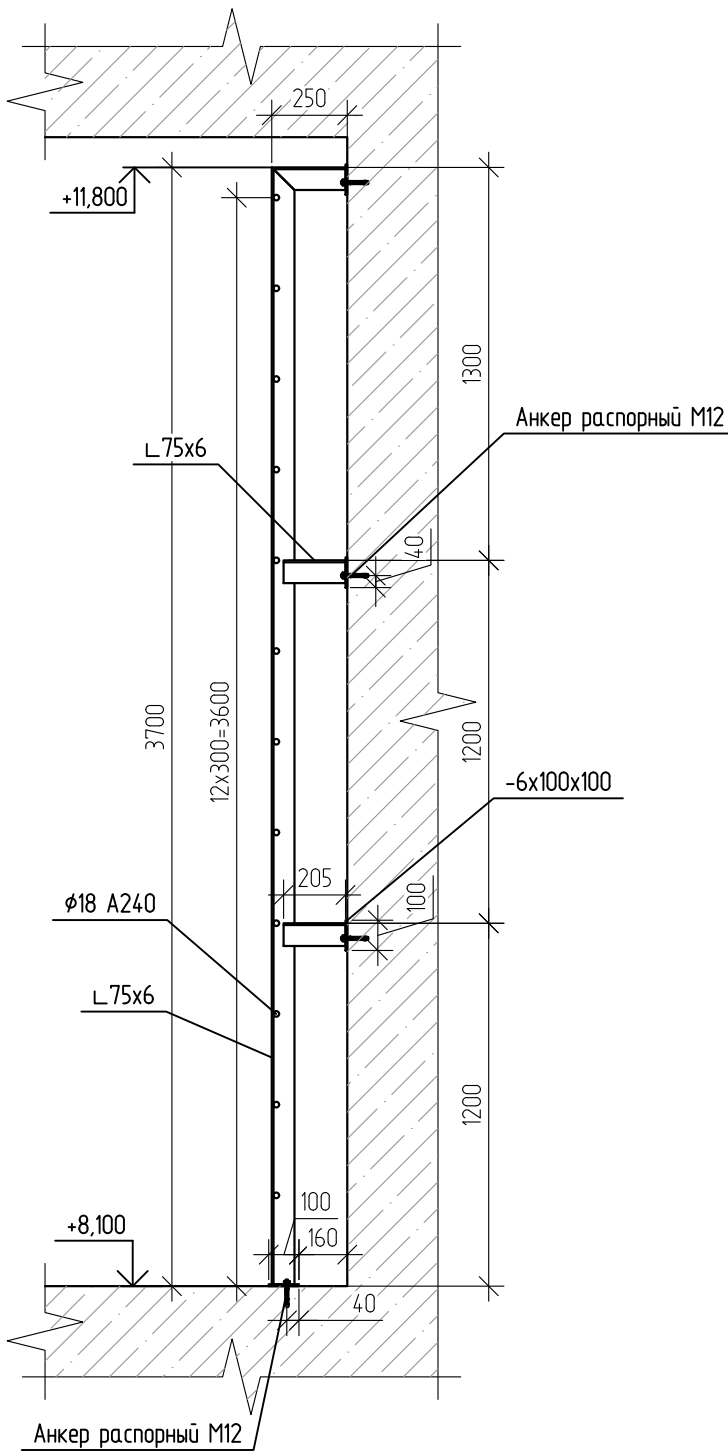


Схема устройства лестницы ПЛ-2

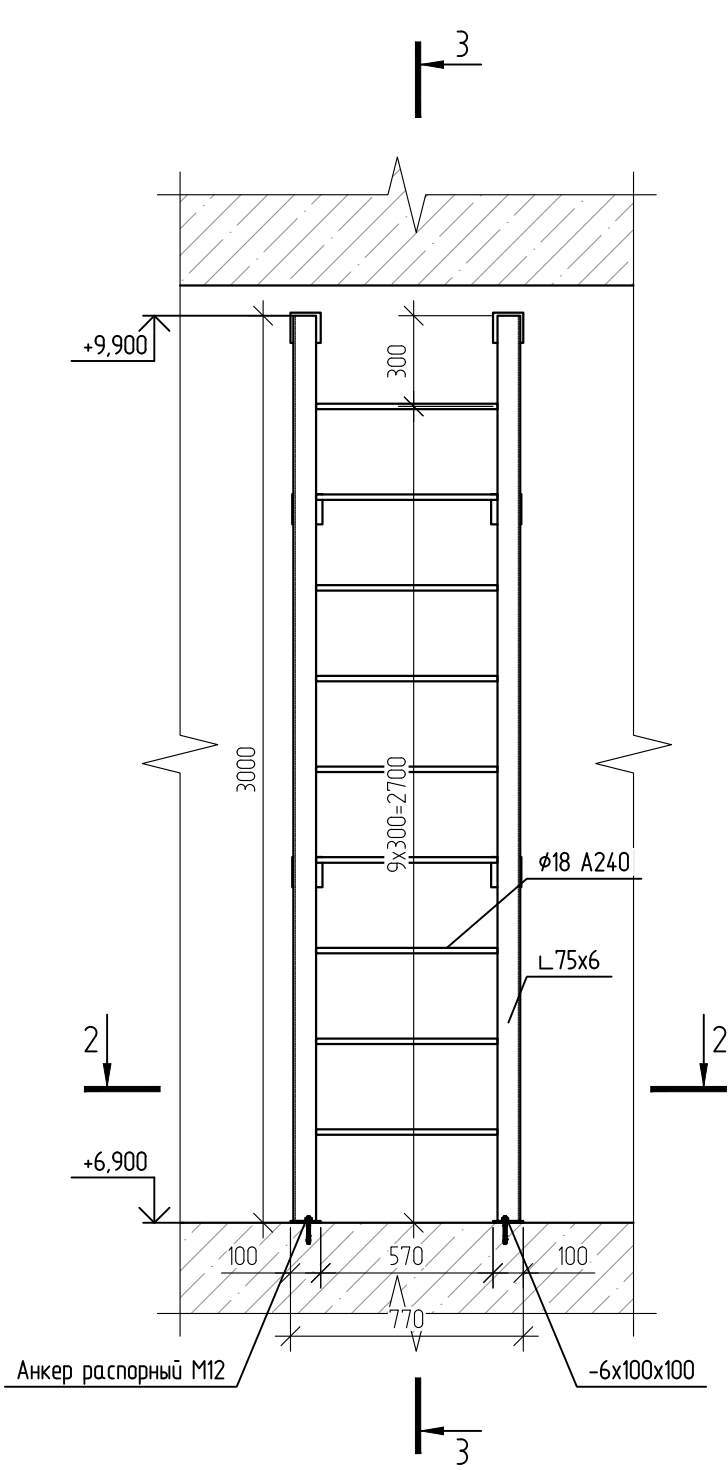

Разрез 3-3



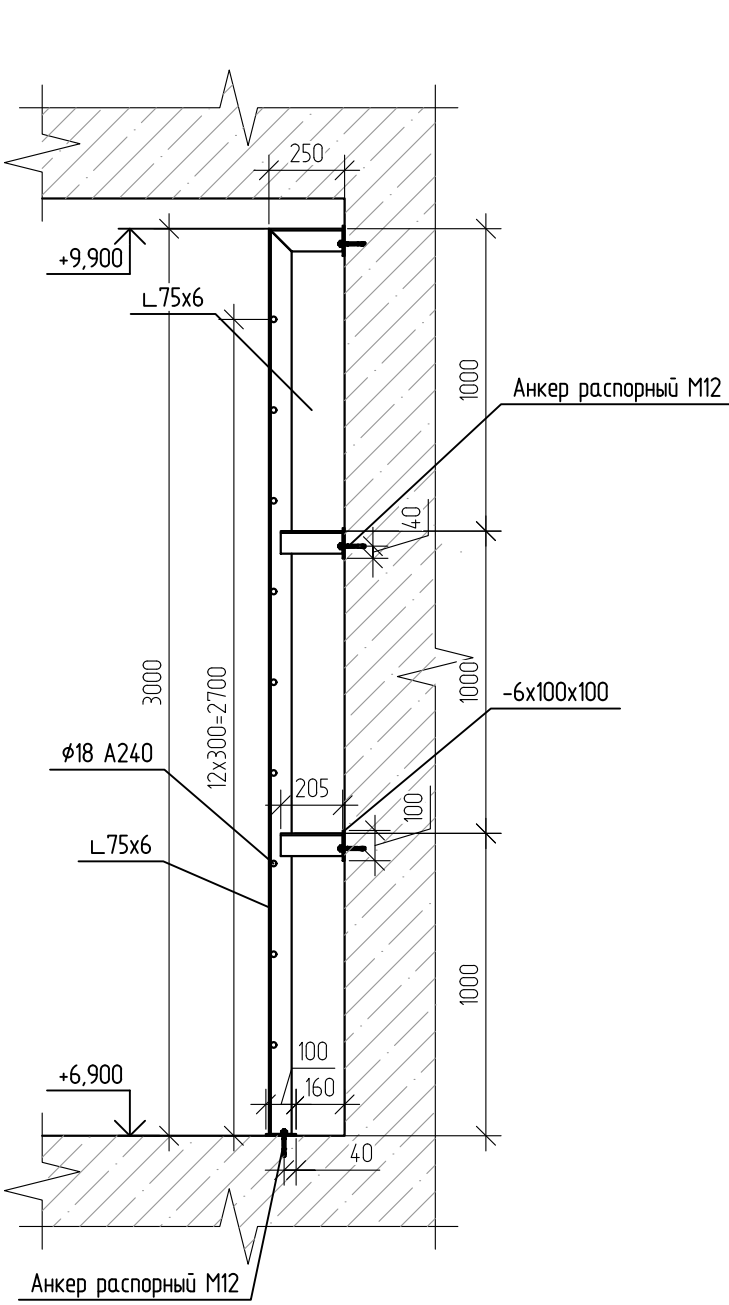



Схема устройства лестницы ПЛ-3

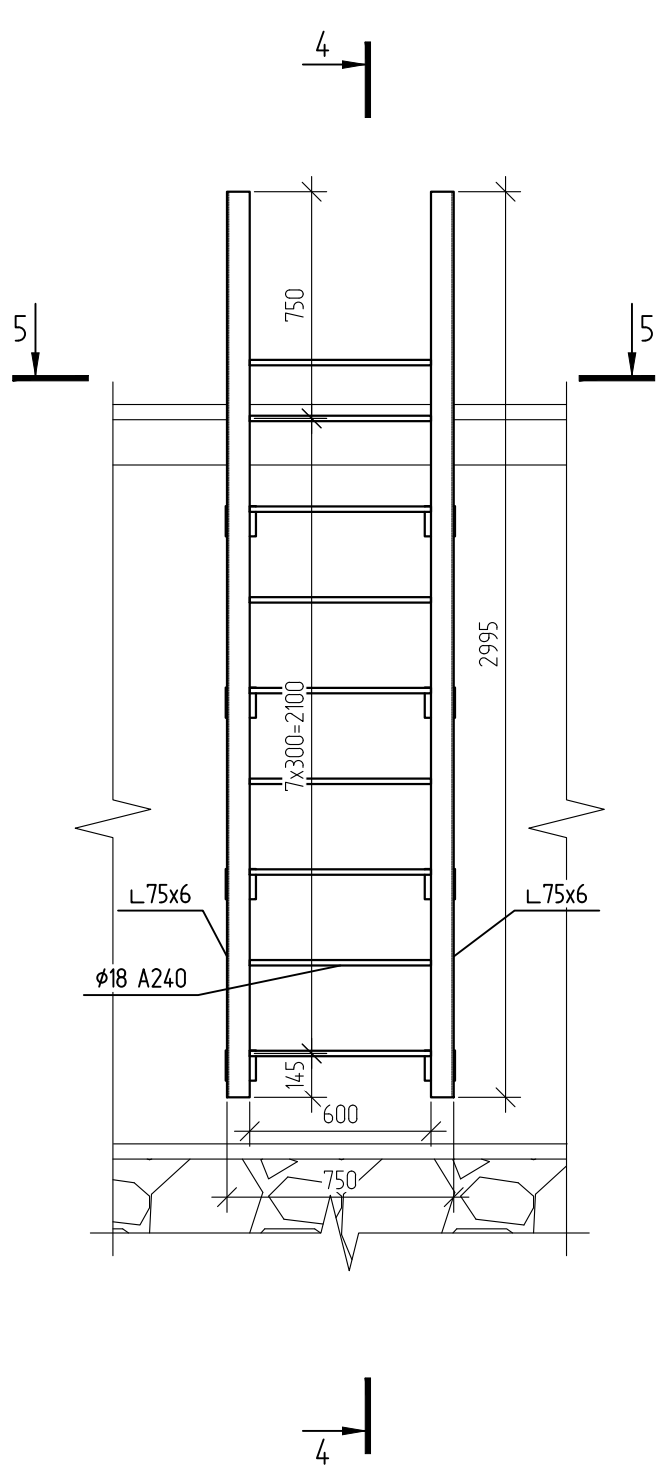

Разрез 4-4

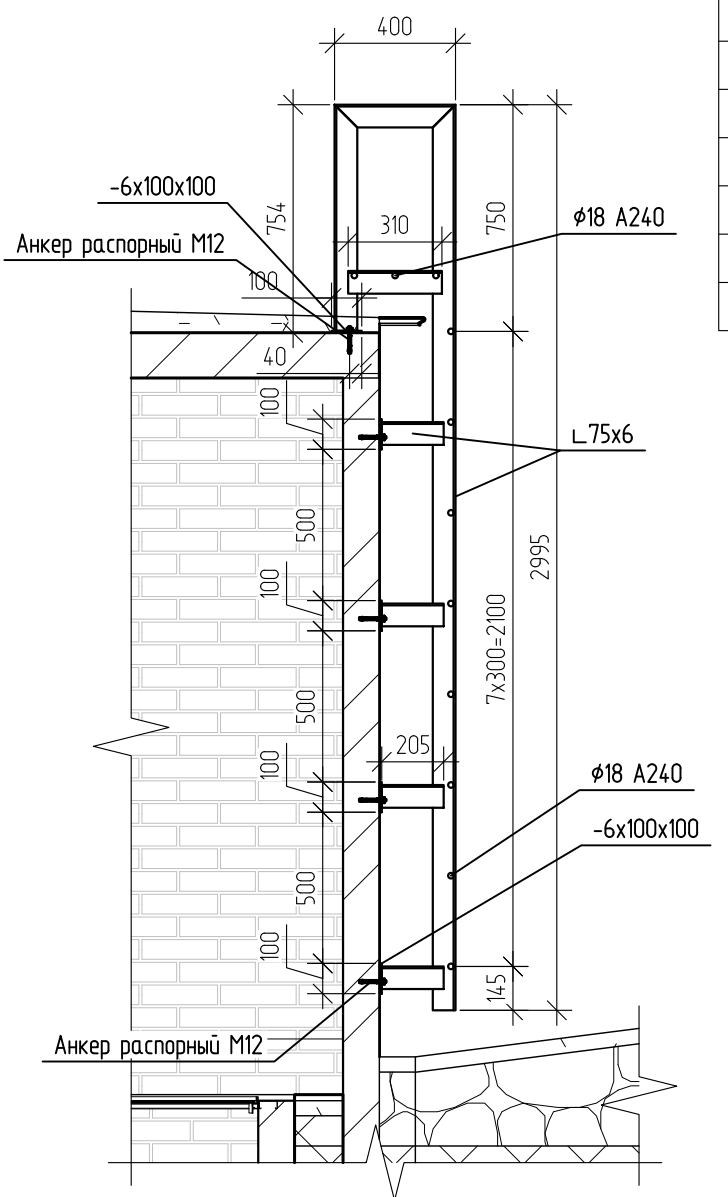

Разрез 5-5

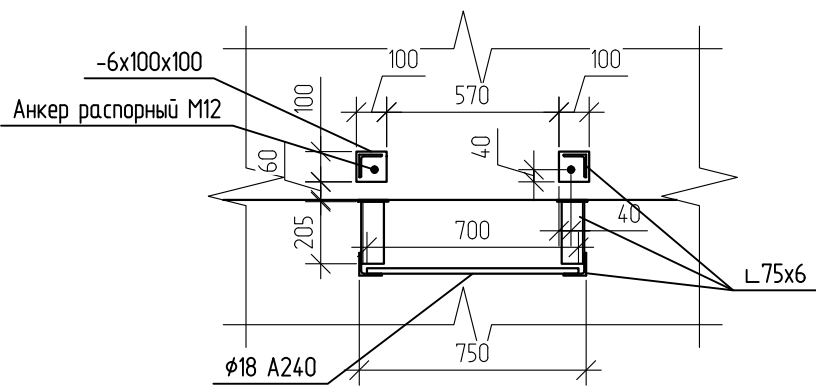

Спецификация материалов на устройство пожарных лестниц ПЛ-1...ПЛ-3

Поз.	Обозначение	Наименование	Кол.	Масса, ед. кз	Примечание
		Лестница ПЛ-1	1		
	ГОСТ 8509-93	Уголок 75х6, м.п.	872	6.89	60.1
	ГОСТ 34028-2016	Арматура ϕ 18 A240, м.п.	8.4	2	16.8
	ГОСТ 19903-2015	Лист 6х100х100, шт	8	0.47	3.8
		Анкер распорный M12	8		
		Лестница ПЛ-2	1		
	ГОСТ 8509-93	Уголок 75х6, м.п.	732	6.89	50.4
	ГОСТ 34028-2016	Арматура ϕ 18 A240, м.п.	6.3	2	12.6
	ГОСТ 19903-2015	Лист 6х100х100, шт	8	0.47	3.8
		Анкер распорный M12	8		
		Лестница ПЛ-3	2		
	ГОСТ 8509-93	Уголок 75х6, м.п.	1058	6.89	72.9
	ГОСТ 34028-2016	Арматура ϕ 18 A240, м.п.	7	2	14.0
	ГОСТ 19903-2015	Лист 6х100х100, шт	10	0.47	4.7
		Анкер распорный M12	10		

Примечание:
1. Материал для металлических конструкций - сталь С235 по ГОСТ 27772-2020;
2. Сварные соединения - по ГОСТ 5264-80. Электродом Э-42 по ГОСТ 9467-75*;
3. Минимальный катет сварного шва - по наименьшей толщине свариваемых элементов;
4. Все конструкции окрасить одним слоем эмали ПФ-115 ГОСТ 6465-76 по двум слоям грунта ГФ-021 ГОСТ 25129-82.

							708/П-24-АНО-КР			
							Капитальный ремонт общеобразовательного учреждения ГБОУ "Школа №1210" по адресу: г. Москва, ул. Живописная, д.32			
Изм.	Колуч.	Лист	№ док.	Подп.	Дата					
Разработал	Торшин	04.26								
Г.АП	Фролова	04.26					Конструктивные решения	Стадия	Лист	Листов
								Р	81	
Н.Контроль	Лукашова	04.26					Схема устройства пожарных лестниц ПЛ-1, ПЛ-3			
ГИП	Зыкин	04.26					Спецификация материалов			