


Узел устройства связей паранета

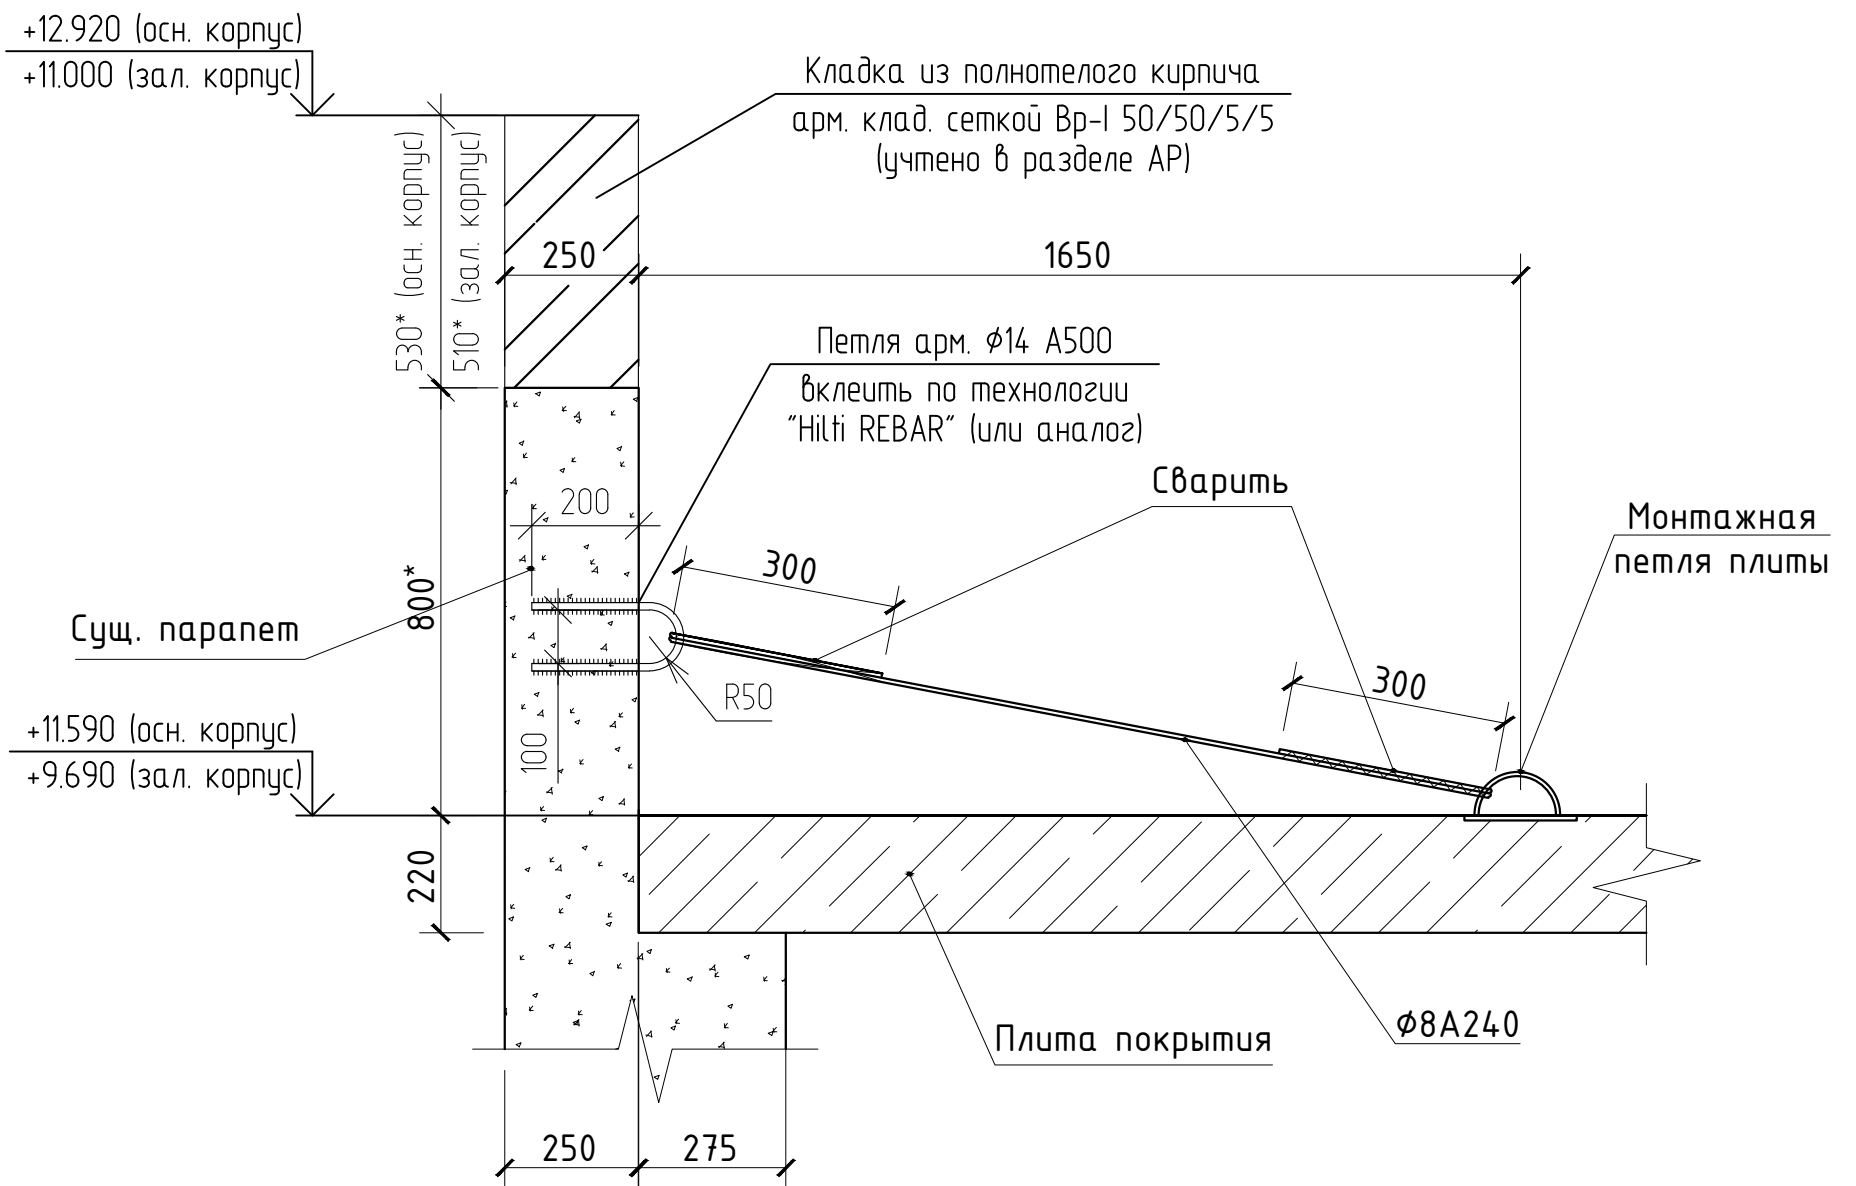

Примечание:

1. Новые петли вклеить по технологии "Hilti REBAR" (или аналог).
2. Кладку парапета выполнить из полнотелого кирпича керамического толщиной 250 мм марки М150, армированного кладочной сеткой Вр-1 50/50/5/5 по ГОСТ 23279-2012 через 3 ряда на растворе марки М75. Расход материалов учтен в разделе АР.
3. Размеры с "*" уточнить по месту.
4. Все металлические элементы окрасить одним слоем эмали ПФ-115 ГОСТ 6465-2023 по двум слоям грунта ГФ-021 ГОСТ 25129-2020.

Согласовано

Примечание:

1. Новые петли клеить по технологии "Hilti REBAR" (или аналог).

2. Кладку парапета выполнить из полнотелого кирпича керамического толщиной 250 мм марки М150, армированного кладочной сеткой Вр-I 50/50/5/5 по ГОСТ 23279-2012 через 3 ряда на растворе марки М75. Расход материалов учтен в разделе АР.

3. Размеры с "*" уточнить по месту.

4. Все металлические элементы окрасить одним слоем эмали ПФ-115 ГОСТ 6465-2023 по двум слоям грунта ГФ-021 ГОСТ 25129-2020.

Взам. инв. №		Поз.	Наименование				Обозначение				Кол.	Масса ед., кг	Приме- чание	
		1	ГОСТ 34028-2016				Арматура Ø8А240				440	0.395	м.п.	
Подп. и дата							708/П-24-АНО-КР							
								Капитальный ремонт общеобразовательного учреждения ГБОУ "Школа №1210" по адресу: г. Москва, ул. Живописная, д.32						
		Изм.	Кол.уч.	Лист	№ док.	Подп.	Дата							
		Разработал		Торшин			04.26	Конструктивные решения	Стадия	Лист	Листов			
		ГАП		Фролова			04.26		Р	82				
						Узел устройства связей парапета		комплексное проектирование промышленных и гражданских объектов ООО "АРТИС"						
Н.Контроль		Лукашова			04.26									
ГИП		Зыкин			04.26									