

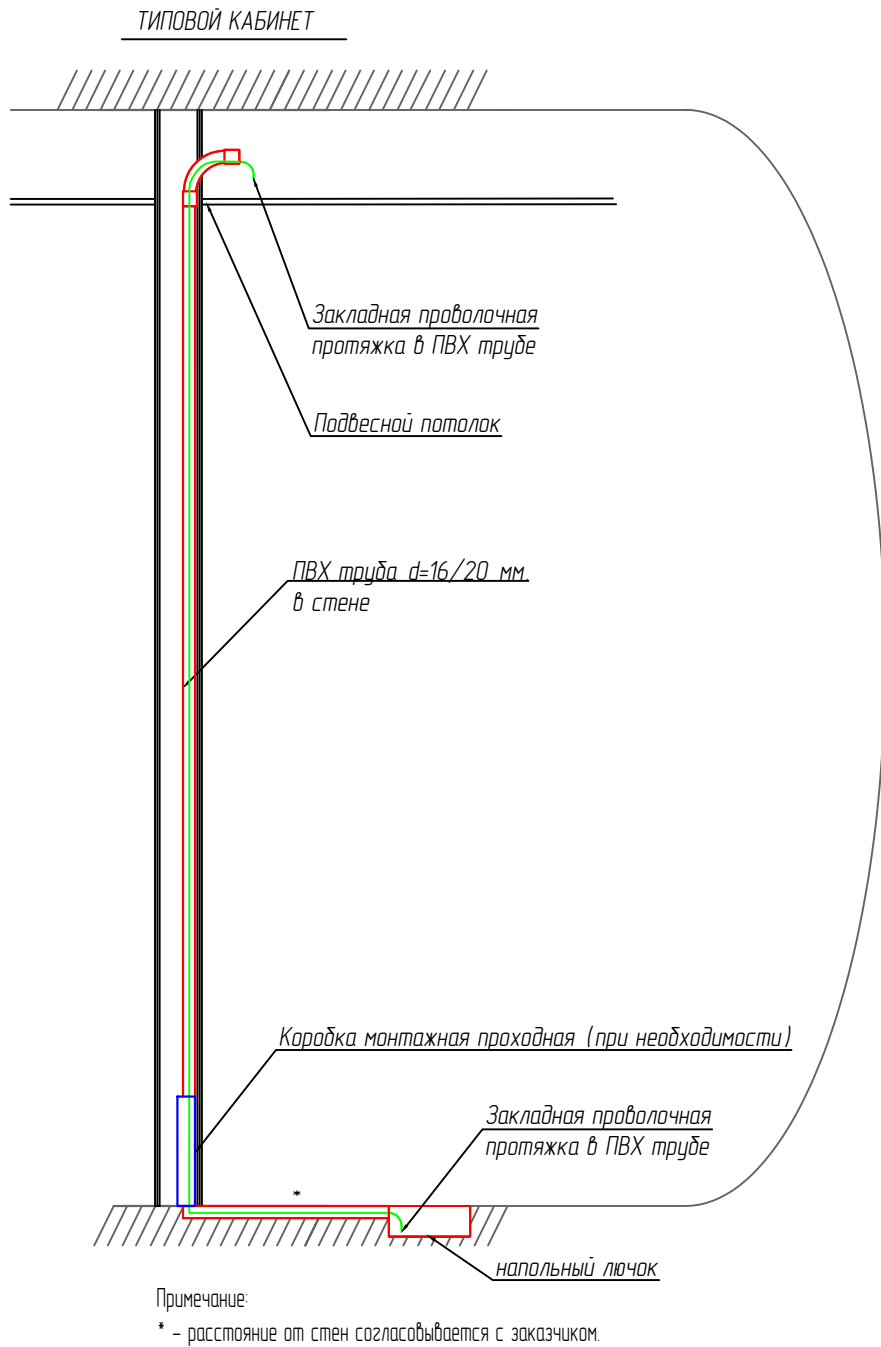
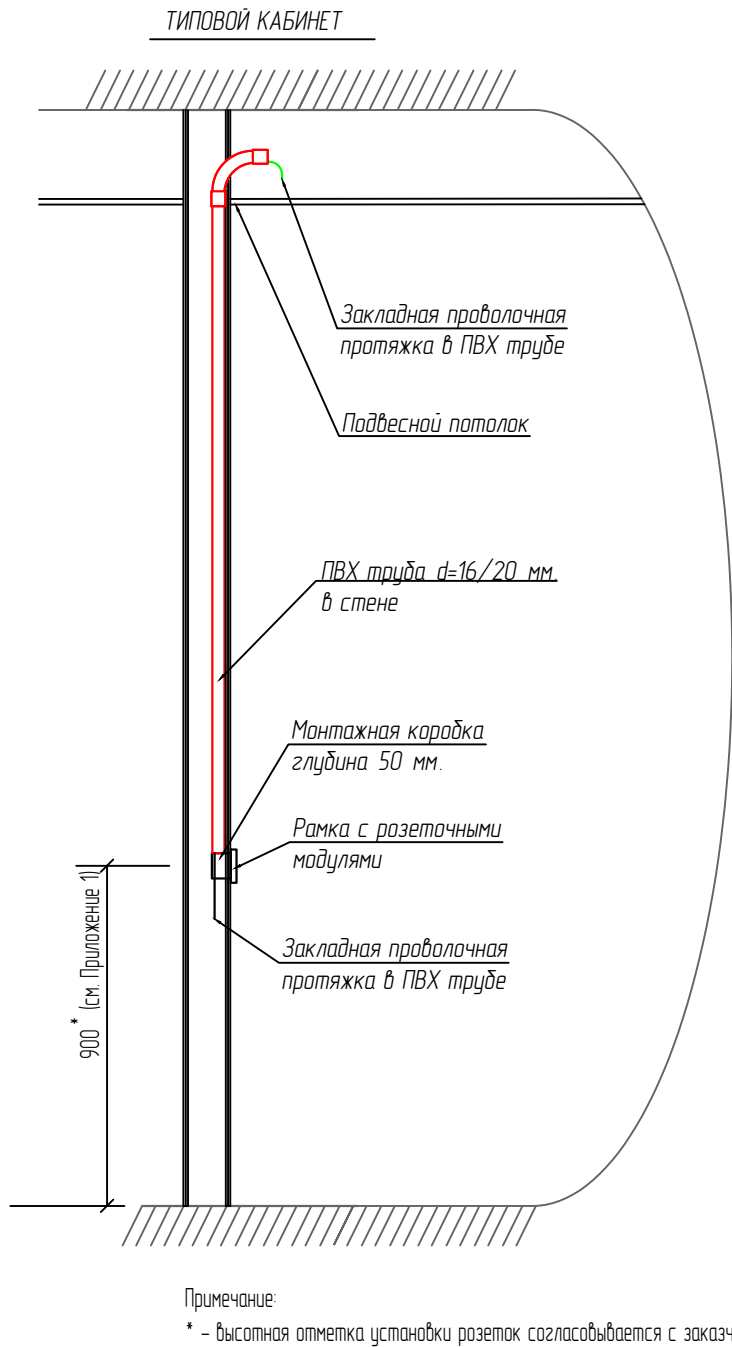


Согласовано				
Взам. инв. №				
Подп. и дата				
Инв. № подл.				

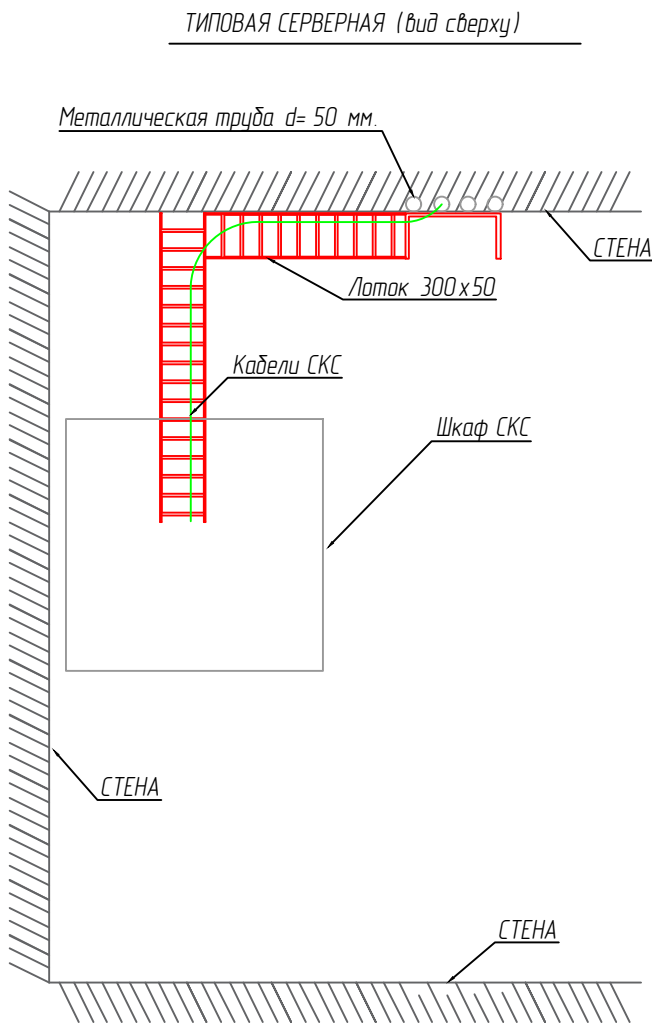

Допускается прокладка кабелей до напольных лючков через нижележащие этажи (кроме помещения актового зала).

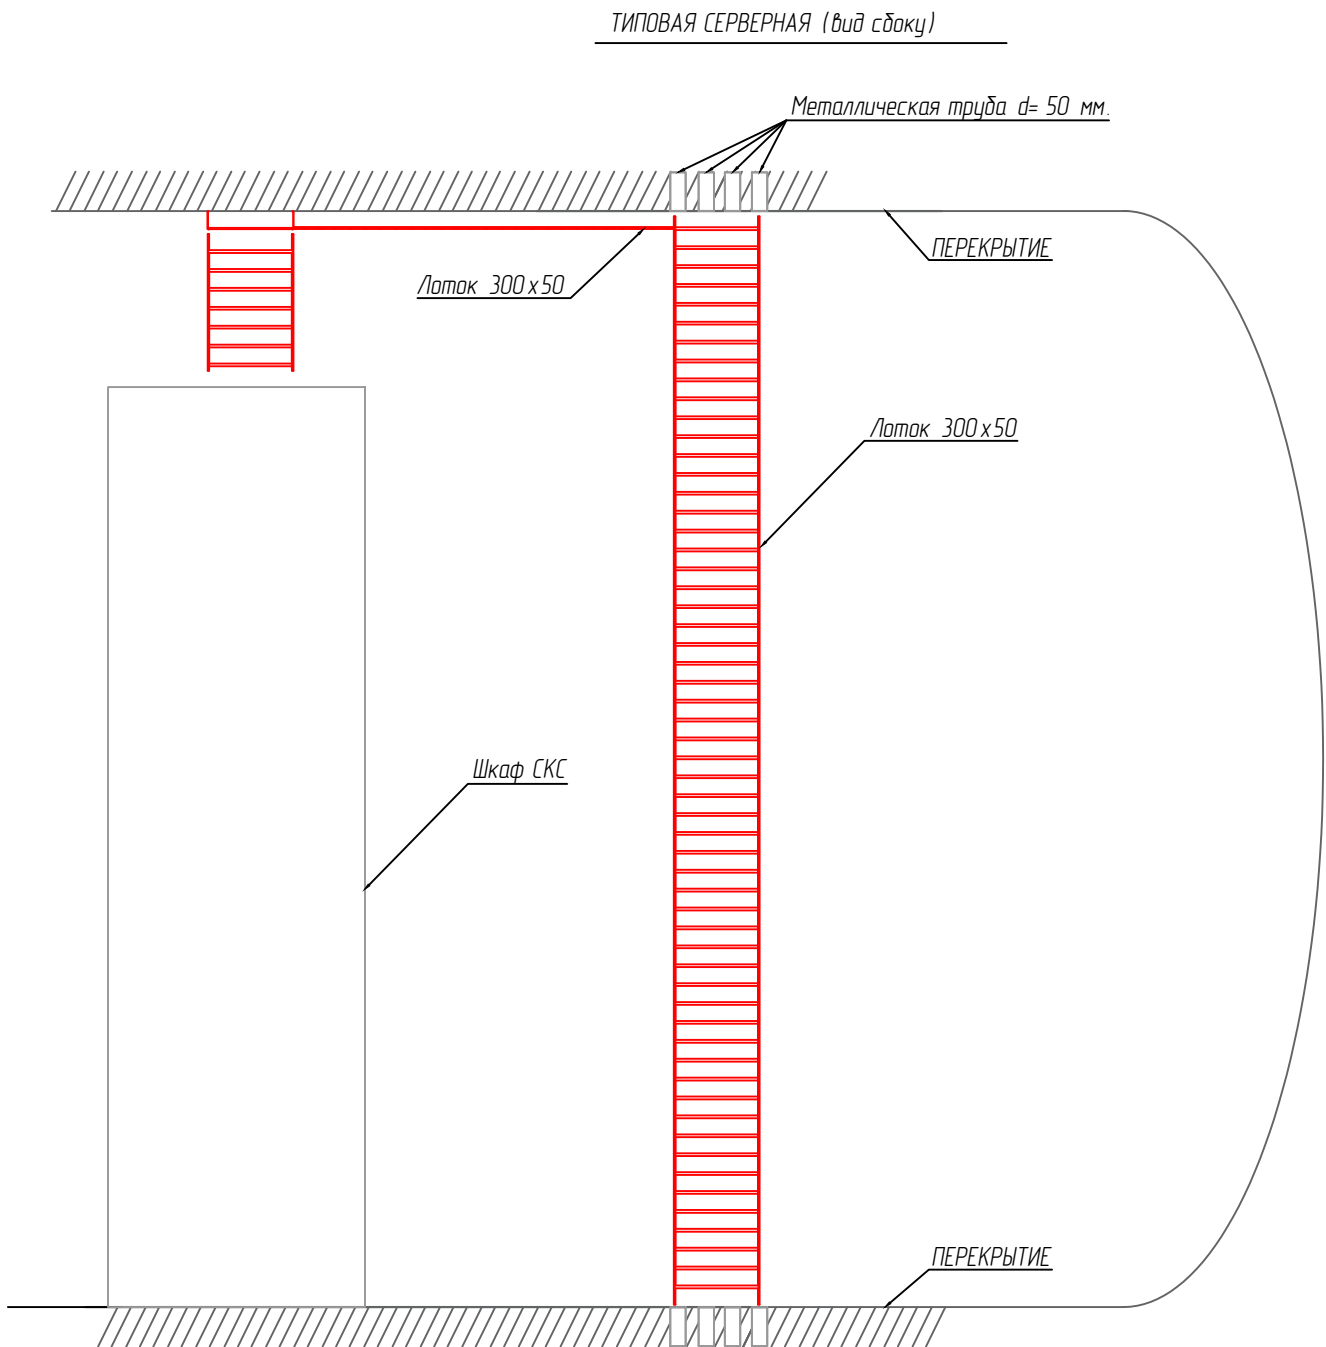

- Примечания:
- В соответствии с письмом ДИОМ Иск-14665/25 от 10.06.2025, проектом предусмотрены резервные закладные трубы во все учебные классы для обеспечения возможности последующей прокладки кабелей камер видеонаблюдения проведения единого государственного экзамена (не менее 1-ой трубы на каждый учебный класс, позволяющей проложить в ней не менее 3-х кабелей типа UTP). Предусмотрена труба гладкая ПВХ, d=32мм.
 - Приведенные схемы являются типовыми, точное месторасположение стояков, телекоммуникационных шкафов, рабочих мест приведены на планах размещения оборудования

						708/П-24-АНО-СКС			
						Капитальный ремонт общеобразовательного учреждения ГБОУ Школа № 1210 по адресу: г. Москва, ул. Живописная д. 32			
Изм.	Колуч.	Лист	№Док	Подп.	Дата				
Разработал	Ляля	Шен	03.26			Стадия	Лист	Листов	
						Р	15		
ГИП	Лукашова	Шен	03.26			Типовые схемы прокладки кабелей			
Н. Контр.	Зыкин	Шен	03.26						
						комплексное проектирование промышленных и гражданских объектов ООО "АРТИС"			