



Экз. № _____

Заказчик: АНО «РГТ»

**Капитальный ремонт общеобразовательного
учреждения (ГБОУ Школа № 1210) по адресу:
г. Москва, ул. Живописная, д. 32**

ПРОЕКТНАЯ ДОКУМЕНТАЦИЯ

Раздел 6. Технологические решения

Часть 3. Пищеблок

708/П-24-АНО-ТХ1.2

Том 6.3



Экз. № _____

Заказчик: АНО «РГТ»

**Капитальный ремонт общеобразовательного
учреждения (ГБОУ Школа № 1210) по адресу:
г. Москва, ул. Живописная, д. 32**

ПРОЕКТНАЯ ДОКУМЕНТАЦИЯ

Раздел 6. Технологические решения

Часть 2. Пищеблок

708/П-24-АНО-ТХ1.2


Том 6.1.2

Генеральный директор:



Цибизов В.В.

План расстановки технологического оборудования и мебели
Подвал

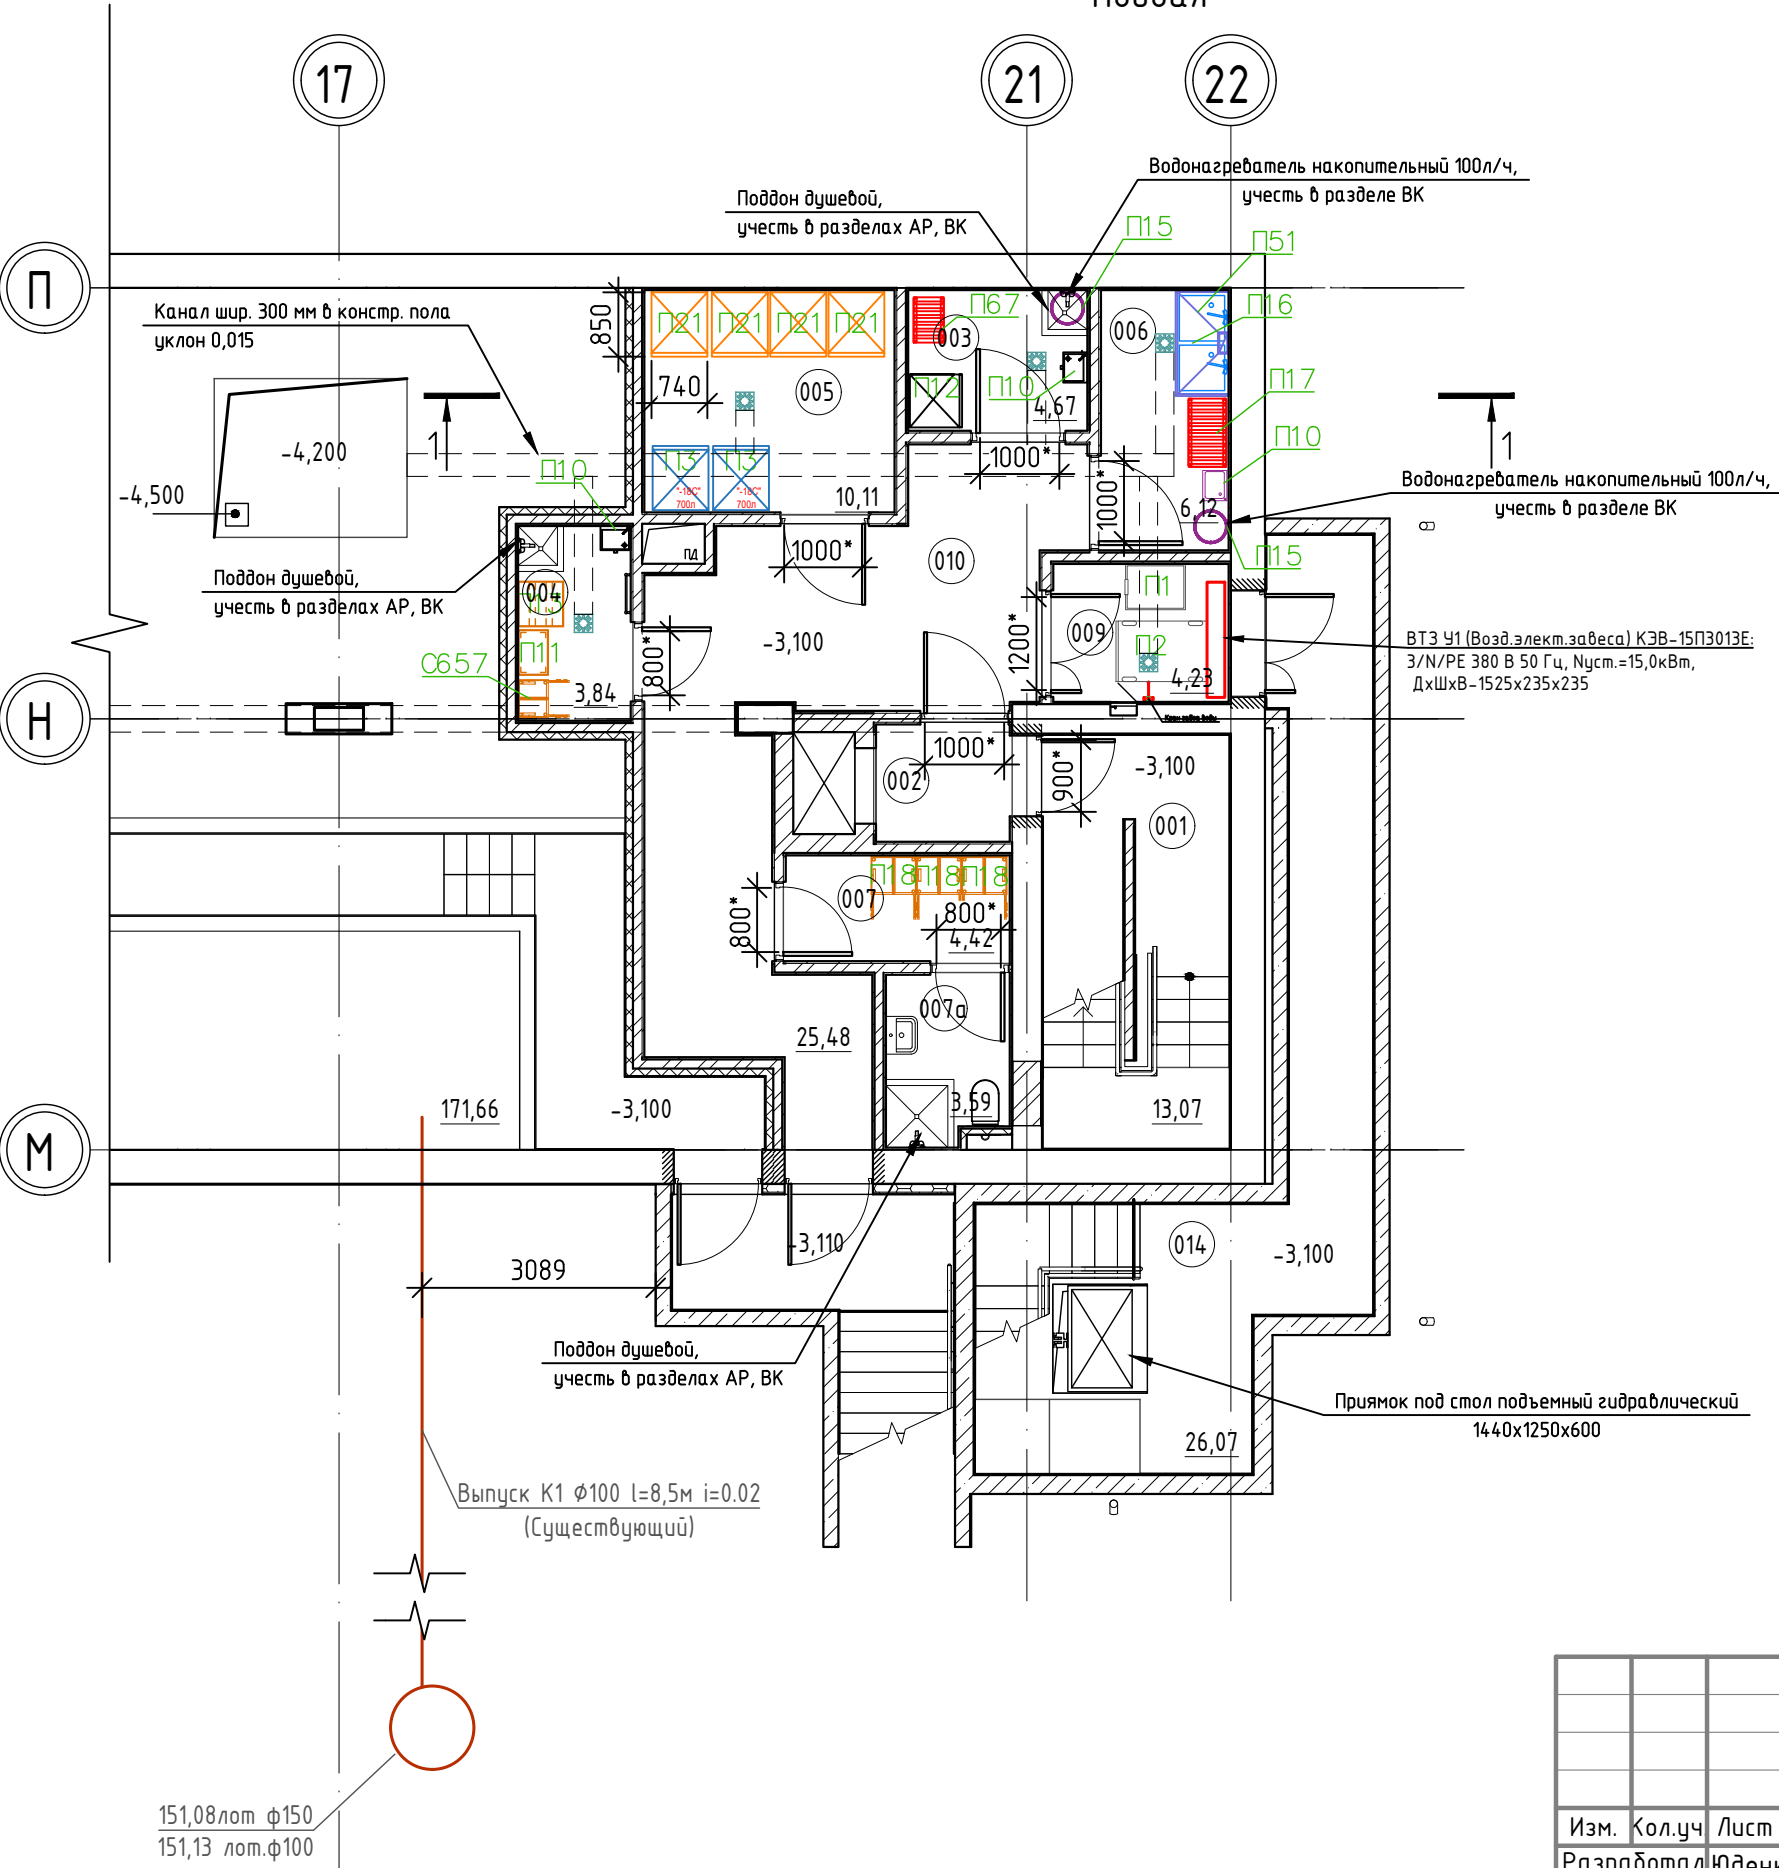

Экспликация помещений подвала

Номер помеще-ния	Наименование	Площадь, м²	Кат. поме-ще-ния
001	Технологическая лестница	13,07	
002	Тамбур-шлюз	2,74	
003	Помещения для временного хранения пищевых отходов	4,67	B4
004	Помещение для хранения уборочного инвентаря (Пищеблок)	3,49	B4
005	Коридор с местом установки холодильного оборудования	10,11	B3
006	Кладовая и моечная оборотной тары	6,12	B4
007	Помещение для персонала (включая душевую и санузел)	4,42	
007а	Помещение	2,89	
009	Загрузочный цех	4,23	B4
010	Коридор	26,81	
014	Зона загрузки	24,54	B3

Условные обозначения:

- трап Ø100
- лотковый трап Ø100, с гидрозатвором по задней стенке, размером 300*300, разрыв струи
- сливной лоток с трапом со съёмной решеткой из нерж стали, размером 800x100, размер ячеек 33x33 мм

Согласовано
Взам. инв. №
Подп. и дата
Инв. № подл.

						708/П-24-АНО-ТХ1.2			
						Капитальный ремонт общеобразовательного учреждения (ГБОУ Школа № 1210) по адресу: г. Москва, ул. Живописная, д. 32			
Изм.	Кол.уч	Лист	№ док.	Подп.	Дата	Пищеблок	Стадия	Лист	Листов
Разработал	Юденкова	Юденкова	12.24				П	1	4
ГАП	Фролова		12.24						
						План расстановки технологического оборудования и мебели Подвал		комплексное проектирование промышленных и гражданских объектов ООО "АРТИС"	
Н.Контроль	Лукашова		12.24						
ГИП	Зыкин		12.24						

[illegible]

Номер помещения	Наименование	Площадь, м²	Кат. помещения
136	Обеденный зал		
137	Маечная столовой посуды		B4
138	Коридор пищеблока		
139	Лестничная клетка (типа /11)		
140	Коридор		
141	Помещение подготовки блюд к реализации с участком кухонной посуды		B4


-  – трап Ø100
-  – лотковый трап Ø100, с гидрозатвором по задней стенке, размером 300*300, разрыв струи
-  – слибный лоток с трапом со съемной решеткой из нерж стали, размером 800x100, размер ячеек 33x33 мм

На выпуске производственной канализации на улице предусматривается установка жируловителя.

						708/П-24-АНО-ТХ1.2
						Капитальный ремонт общеобразовательного учреждения (ГБОУ Школа № 1210) по адресу: г. Москва, ул. Живописная, д. 32
Изм.	Кол.уч	Лист	№ док.	Подп.	Дата	
Разработал	Юденкова	Юденкова			12.24	
ГАП	Фролова				12.24	
						Пищеблок
						Стадия
						Лист
						Листов
						П
						2
						2
Н.Контроль	Лукашова	Лукашова			12.24	
ГИП	Зыкин	Зыкин			12.24	
						План расстановки технологического оборудования и мебели 1 этаж
						 комплексное проектирование промышленных и гражданских объектов ООО "АРТИС"

Инв. № подл.	Подп. и дата	Взам. инв. №
--------------	--------------	--------------

Инв. № подл.	Подп. и дата	Взам. инв. №	Согласовано	

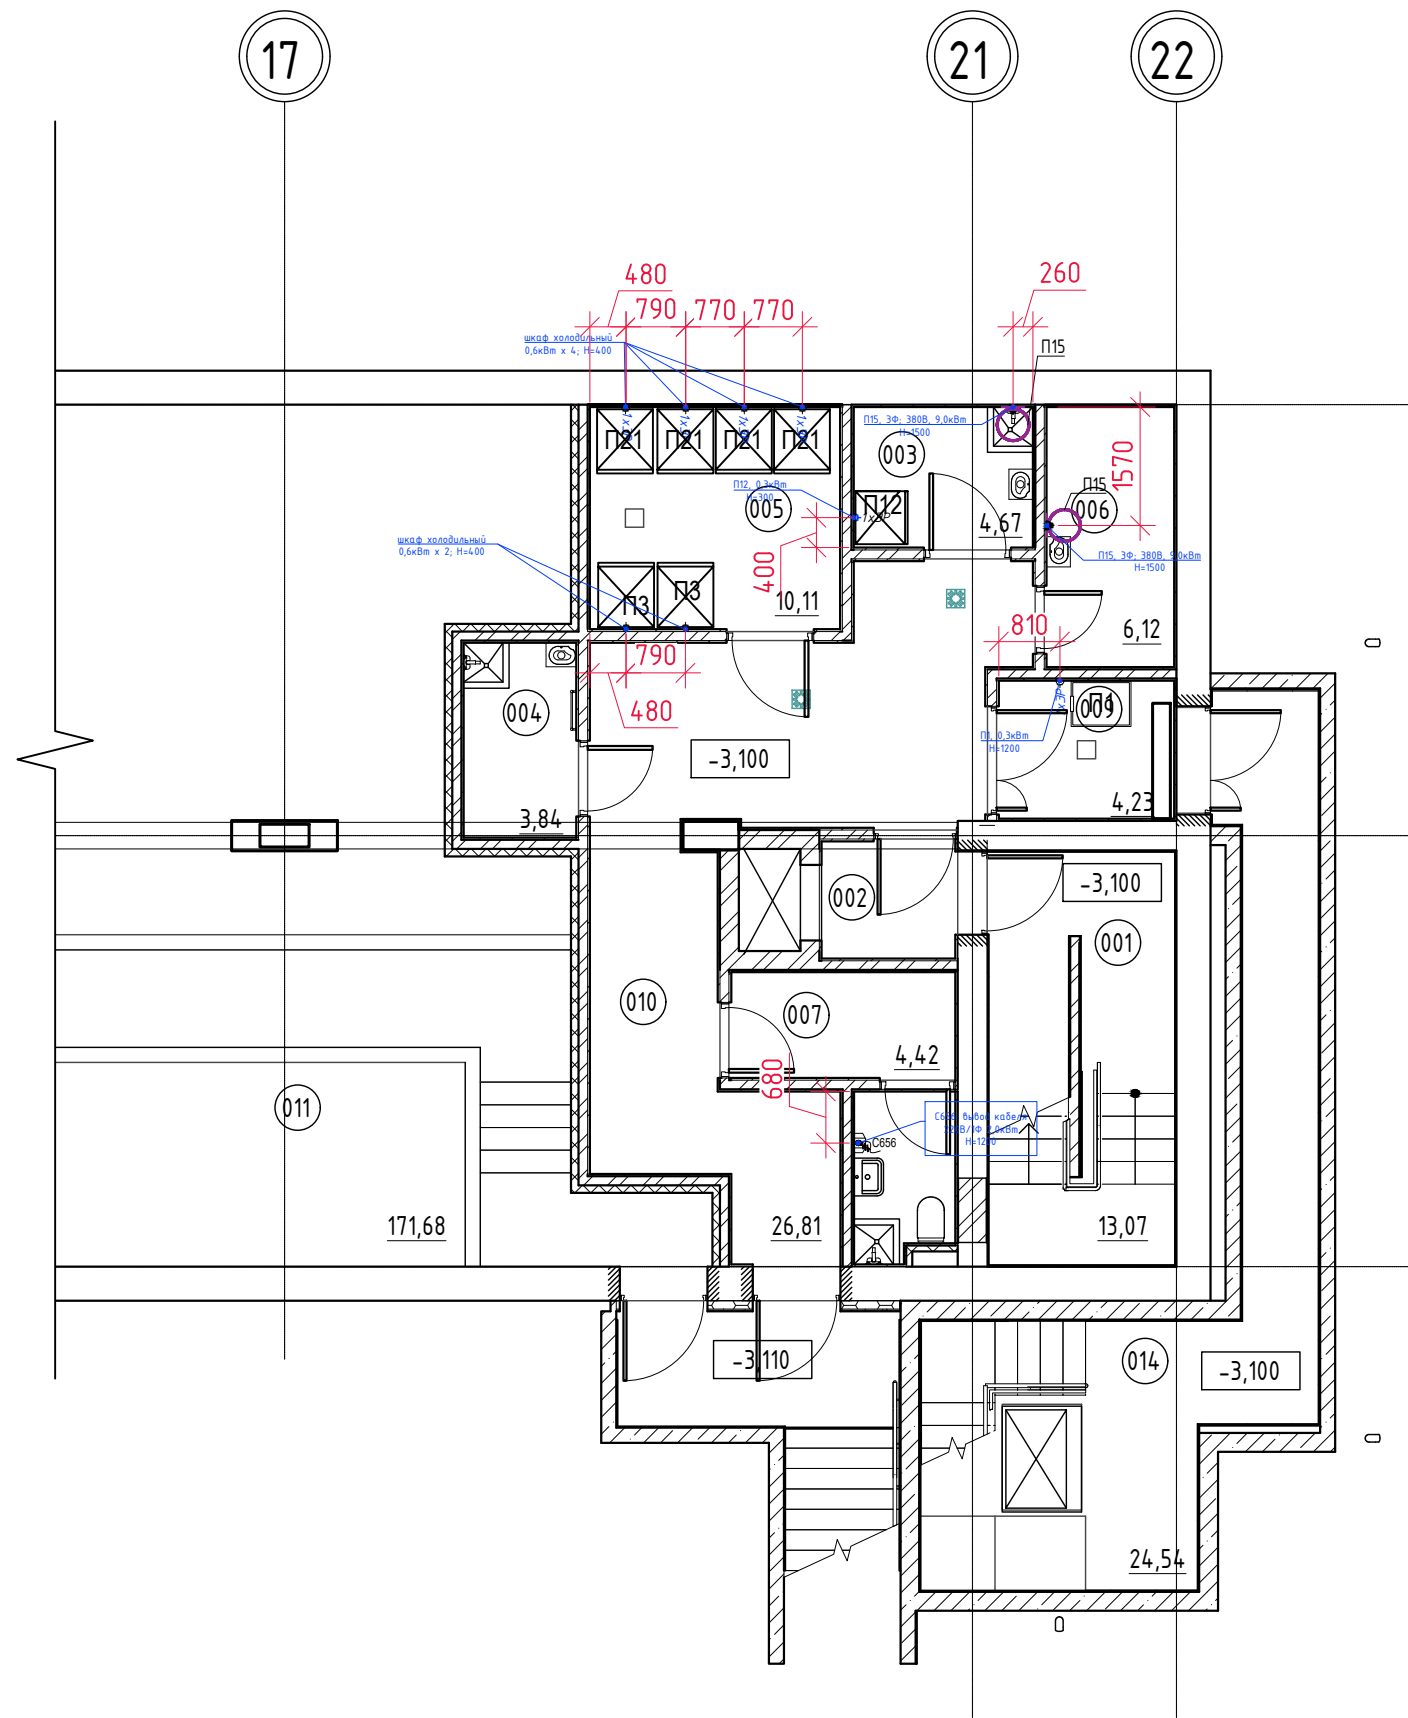


Экспликация помещений подвала

Номер помеще-ния	Наименование	Площадь, м²	Кат. поме-ще-ния
001	Технологическая лестница	13,07	
002	Тамбур-шлюз	2,74	
003	Помещения для временного хранения пищевых отходов	4,67	В4
004	Помещение для хранения уборочного инвентаря (Пищеблок)	3,49	В4
005	Коридор с местом установки холодильного оборудования	10,11	В3
006	Кладовая и моечная оборотной тары	6,12	В4
007	Помещение для персонала (включая душевую и санузел)	4,42	
007а	Помещение	2,89	
009	Загрузочный цех	4,23	В4
010	Коридор	26,81	
014	Зона загрузки	24,54	В3

Примечание
1. Условные обозначения подводимых коммуникаций см. л. 4 "План расстановки технологического оборудования и мебели. 1 этаж"

						708/П-24-АНО-АР			
						Капитальный ремонт общеобразовательного учреждения (ГБОУ Школа № 1210) по адресу: г. Москва, ул. Живописная, д. 32			
Изм.	Кол.уч.	Лист	№ док.	Подп.	Дата	Архитектурные решения	Стадия	Лист	Листов
Разработал		Юденкова			12.24		П	3	
						Подключения розеток и оконечных устройств. Подвал	 комплексное проектирование промышленных и гражданских объектов ООО "АРТИС"		
Н.Контроль		Трудииков			12.24				
ГИП		Фролова			12.24				

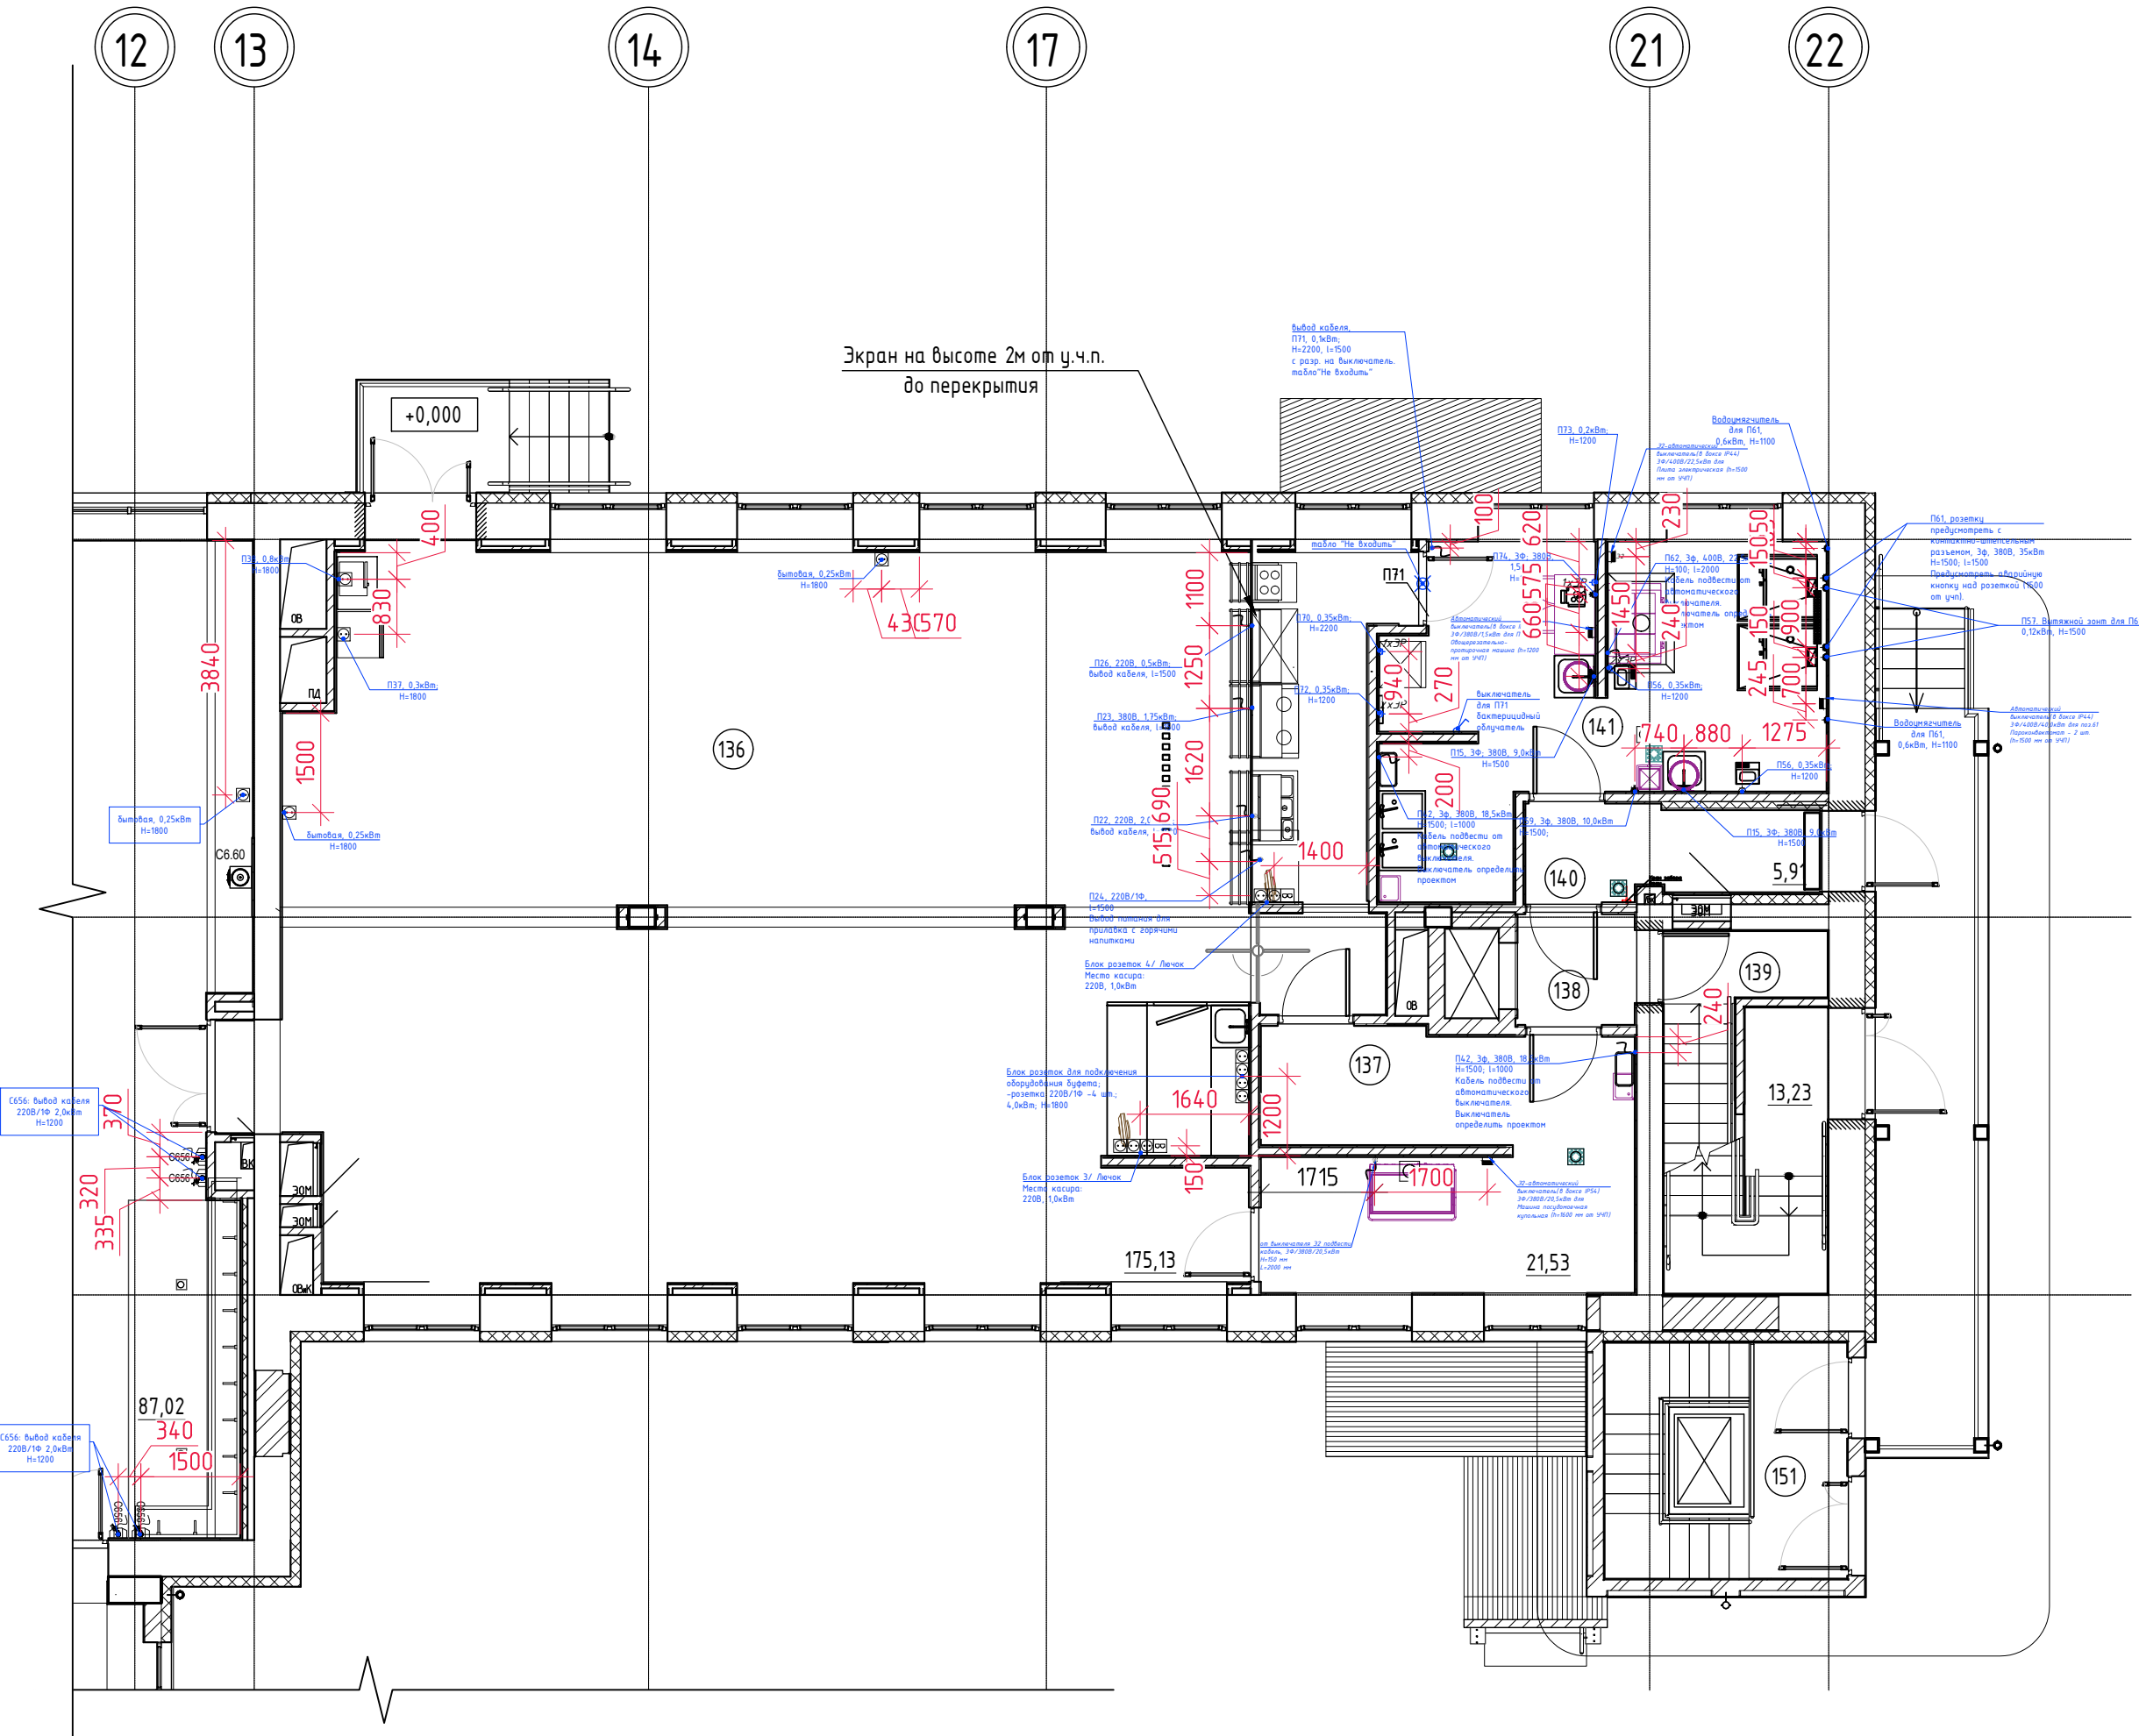

Экспликация помещений 1 этажа			
Номер помеще-ния	Наименование	Площадь, м²	Кат. поме-ще-ния
136	Обеденный зал		
137	Моечная столовой посуды		B4
138	Коридор пищеблока		
139	Лестничная клетка (типа /11)		
140	Коридор		
141	Помещение подготовки блюд к реализации с участком кухонной посуды		B4


УСЛОВНЫЕ ОБОЗНАЧЕНИЯ ПОДВОДИМЫХ КОММУНИКАЦИЙ

	выводы RJ45 и 220В кабелей под НТР часы (уточняется в СС и ЭОМ соответственно); h=2200
	розетка 220В бытовая сеть h=300 (если не указано иное)
	Блок розеток 1: розетка 220В/1Ф - 2 шт.; RJ45 - 2 шт.; HDMI - 1 шт.; USB - 1 шт.
	Блок розеток 2: розетка 220В/1Ф - 4 шт.; RJ45 - 1 шт.;
	Блок розеток 3: розетка 220В/1Ф - 4 шт.; RJ45 - 2 шт.;
	Блок розеток 4: розетка 220В/1Ф - 2 шт.; RJ45 - 2 шт.;
	Лючок в полу для рабочего места: розетка 220В/1Ф - 4 шт.; RJ45 - 4 шт.;
	Лючок в полу для рабочего места учителя (защита не менее IP 34/44) : розетка 220В/1Ф - 4 шт.; RJ45 - 2 шт.; HDMI - 1 шт.; USB - 1 шт.
	Лючок в полу для рабочего места ученика(защита не менее IP 34/44): розетка 220В/1Ф - 2 шт.;
	Лючок в полу для интерактивного устройства на мобильной стойке: розетка 220В/1Ф - 2 шт.; RJ45 - 2 шт.; HDMI - 1 шт.; USB - 1 шт.
	Блок МФУ: розетка 220В/1Ф - 1 шт.; RJ45 - 1 шт.;
	вывод кабеля 380В; запас не менее 2,5м.
	табло "НЕ ВХОДИТЬ/ВХОДИТЕ"; над входом или не менее 2м
	Вывод ВК: холодная, горячая вода 1/2" h=350мм; канализация Ø50мм h=100мм
	вывод кабеля 220В; запас не менее 1,5м.
	кнопка аварийного отключения питания

						708/П-24-АНО-АР			
						Капитальный ремонт общеобразовательного учреждения (ГБОУ Школа № 1210) по адресу: г. Москва, ул. Живописная, д. 32			
Изм.	Кол.уч	Лист	№ док.	Подп.	Дата	Архитектурные решения	Стадия	Лист	Листов
Разработал	Юденкова				12.24		П	4	
						Подключения розеток и оконечных устройств. 1 этаж	 комплексное проектирование промышленных и гражданских объектов ООО "АРТИС"		
Н.Контроль	Трубников				12.24				
ГИП	Фролова				12.24				


Экспликация помещений подвала

Номер помеще-ния	Наименование	Площадь, м ²	Кат. поме-ще-ния
001	Технологическая лестница	13,07	
002	Тамбур-шлюз	2,74	
003	Помещения для временного хранения пищевых отходов	4,67	B4
004	Помещение для хранения уборочного инвентаря (Пищеблок)	3,49	B4
005	Коридор с местом установки холодильного оборудования	10,11	B3
006	Кладовая и моечная оборотной тары	6,12	B4
007	Помещение для персонала(включая душевую и санузел)	4,42	
007а	Помещение	2,89	
009	Загрузочный цех	4,23	B4
010	Коридор	26,81	
014	Зона загрузки	24,54	B3

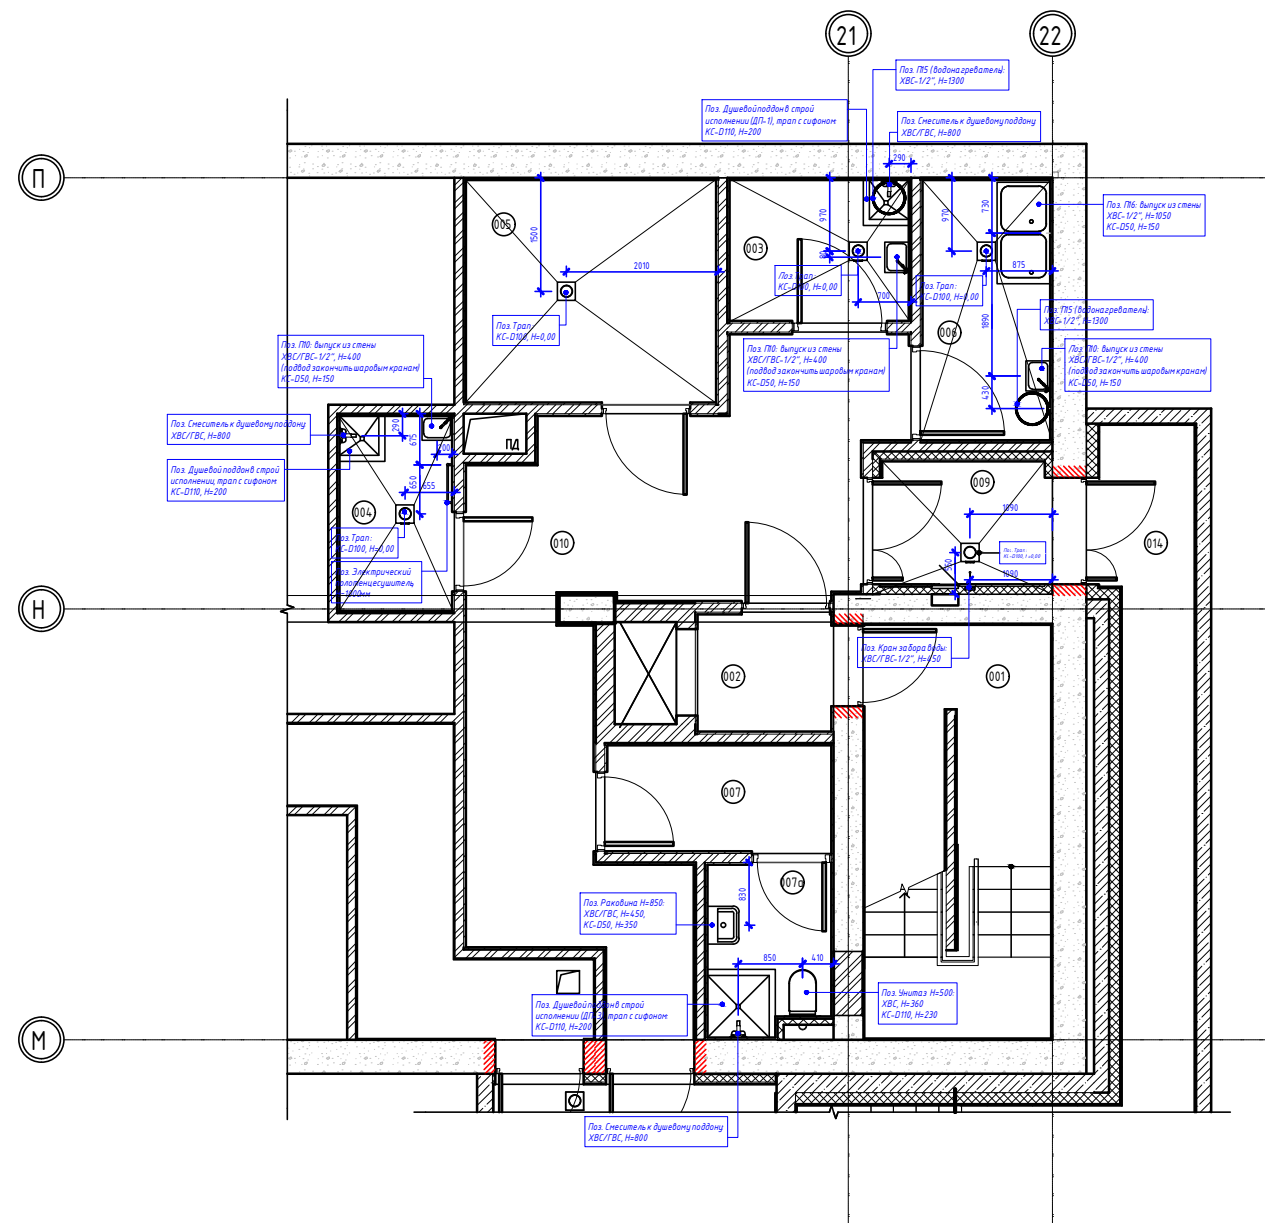

						708/П-24-АНО-АР				
						Капитальный ремонт общеобразовательного учреждения (ГБОУ Школа № 1210) по адресу: г. Москва, ул. Живописная, д. 32				
Изм.	Кол.уч	Лист	№ док.	Подп.	Дата			Стадия	Лист	Листов
Разработал	Юденкова				12.24	Архитектурные решения		П	5	
Н.Контроль	Трубников				12.24	Привязка мокрых точек. Подвал		 комплексное проектирование промышленных и гражданских объектов ООО "АРТИС"		
ГИП	Фролова				12.24					

Инв. № подл.	Подп. и дата	Взам. инв. №	Согласовано	

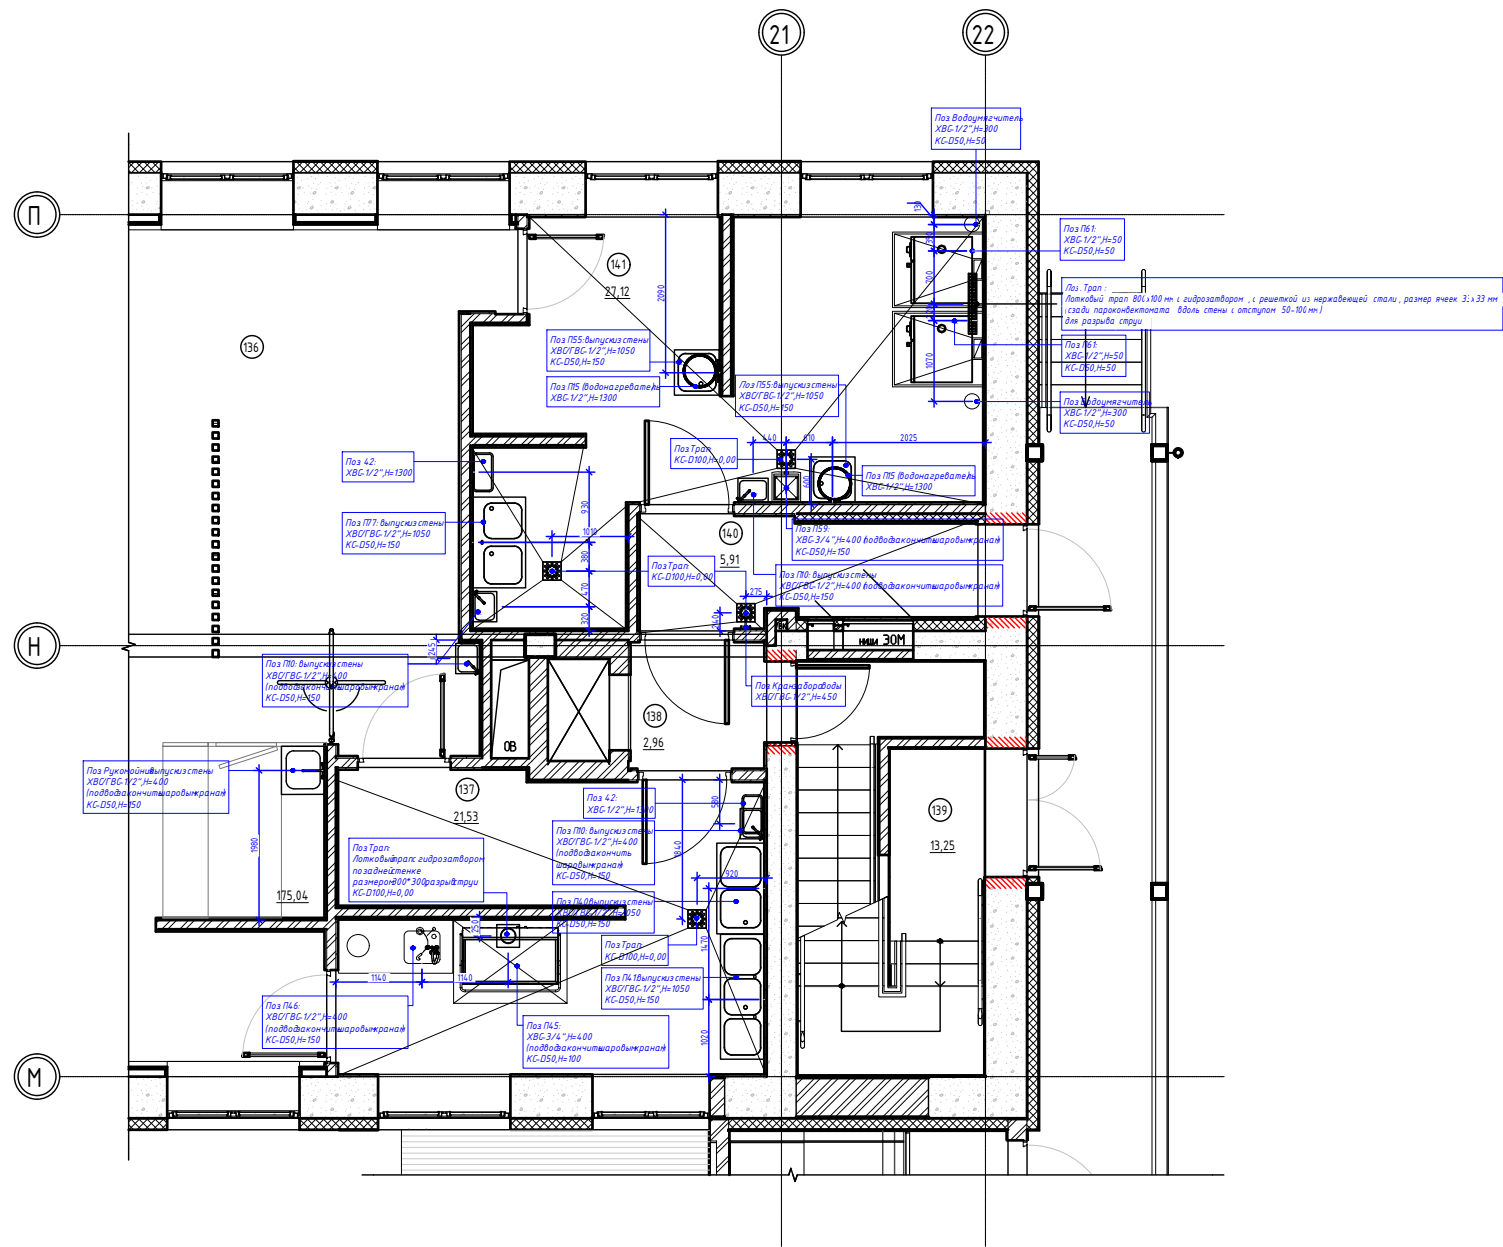

Экспликация помещений 1 этажа


Номер помеще-ния	Наименование	Площадь, м²	Кат. поме-ще-ния
136	Обеденный зал		
137	Моечная столовой посуды		В4
138	Коридор пищеблока		
139	Лестничная клетка (типа /Л1/)		
140	Коридор		
141	Помещение подготовки блюд к реализации с участком кухонной посуды		В4

						708/П-24-АНО-АР			
						Капитальный ремонт общеобразовательного учреждения (ГБОУ Школа № 1210) по адресу: г. Москва, ул. Живописная, д. 32			
Изм.	Кол.уч	Лист	№ док.	Подп.	Дата	Архитектурные решения	Стадия	Лист	Листов
Разработал		Юденкова			12.24		П	6	
Н.Контроль		Трудников			12.24	Привязка мокрых точек. 1 этаж	 комплексное проектирование промышленных и гражданских объектов ООО "АРТИС"		
ГИП		Фролова			12.24				

Приложение к Графической части

Инв. № подл.	Подп. и дата	Взам. инв. №	Согласовано			

Разрез 1-1

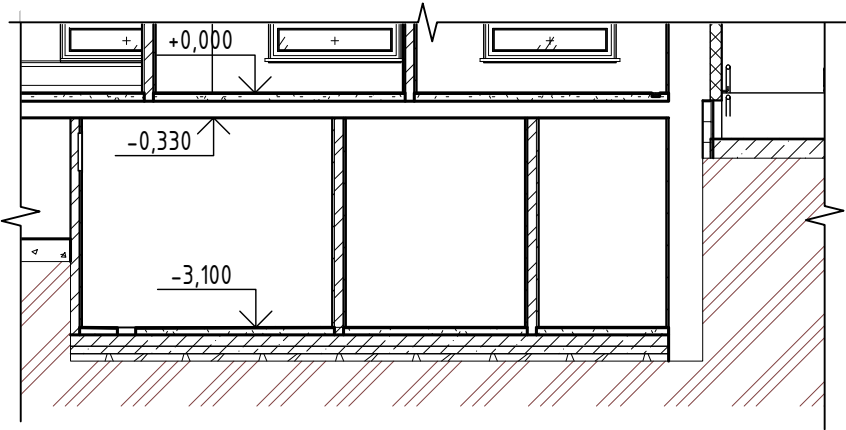

						708/П-24-АНО-ТХ1.2		
						Капитальный ремонт общеобразовательного учреждения (ГБОУ Школа № 1210) по адресу: г. Москва, ул. Живописная, д. 32		
Изм.	Кол.уч	Лист	№ док.	Подп.	Дата	Пищеблок	Стадия	Лист
Разработал		Юденкова		Юденкова	12.24			
ГАП		Фролова			12.24	Разрез 1-1	П	1
								2
Н.Контроль		Лукашова			12.24			ООО "АРТИС"
ГИП		Зыкин			12.24			

Приложение 3

№	Раздел	Помещение	Кол-во пом.	Наименование	Технические характеристики	Ед. изм.	Кол-во	Дополнительное пояснение	№ пом. в ГЧ	№ поз. в ГЧ	Марка оборудования	Кол-во, отличное от Перечня	Комментарии проектировщика	Комментарий ГКУ ДИОМ на письмо от 29.07.2025 № 07-10-3057/25-1	Ответ на замечания ГКУ ДИОМ от 01.08.2025	Комментарий ГКУ ДИОМ на письмо от 07.08.2025 № 07-03-1708/25-2	Ответ на замечания ГКУ ДИОМ от 20.08.2025
1	Мебель	Обеденный зал	1	Стол обеденный школьный № 4, 1000х600	Ростовая группа - №4 Высота - Не менее 640 и не более 700 мм Наличие регулировки высоты (640/700 мм) Соответствие требованиям ГОСТ 20902-95 "Столы обеденные школьные. Функциональные размеры" - Наличие Каркас изделия - Сварной или разборный металлокаркас Материал каркаса - Нержавеющая сталь или металл, окрашенный методом порошкового напыления Цвет каркаса - Белый и/или	шт.	19		136	П27		10		Принято.			
2	Мебель	Обеденный зал	1	Стол обеденный школьный № 4, 1500х600	Ростовая группа - №4 Высота - Не менее 640 и не более 700 мм	шт.	16	Кол-во может быть отличным от Перечня	136	П28		9					
2	Мебель	Обеденный зал	1	Стол обеденный школьный № 5, 1800х600	Ростовая группа - №5 Высота - Не менее 700 и не более 760 мм	шт.	6		136	П29		2		Принято.			
3	Мебель	Обеденный зал	1	Стол обеденный школьный № 5, 1200х600	Ростовая группа - №5 Высота - Не менее 700 и не более 760 мм	шт.	0		136	П29.1		14	Новая позиция	Принято.			
4	Мебель	Обеденный зал	1	Табурет №4	Соответствие требованиям ГОСТ 19917-2014 "Мебель для сидения и лежания"	шт.	167	Кол-во может быть отличным от Перечня	136	б/п		90					
5	Мебель	Обеденный зал	1	Табурет №5	Соответствие требованиям ГОСТ 19917-2014 "Мебель для сидения и лежания". Вид табурета - школьный к	шт.	36		136	б/п		67		Принято.			
6	Мебель	Обеденный зал	1	Стол высокий (обеденный зал)	Соответствие требованиям ГОСТ 16371-2014 "Мебель. Общие технические условия" -	к-т	1		136	П30			Габаритные размеры: 11000х500х900 мм	Принято.			
7	Мебель	Обеденный зал	1	Стул высокий (обеденный зал)	Соответствие требованиям ГОСТ 19917-2014 "Мебель для сидения и лежания. Общие	шт.	18	РАЗМЕЩЕНИЕ: вдоль линии окна НЕОБХОДИМО	136	П31			Габаритные размеры: 400х620/900 мм				
8	Занавески, жалюзи и прочие	Обеденный зал	1	Шторы рулонные тип 1	Штора рулонная из негорючего пожаробезопасного материала. Светозащитная категория	к-т	1		136	б/п			Размер : 1850х2250 (ШкВ) - 10 шт Тип крепления:				
9	Торгово-технологическое оборудование	Обеденный зал	1	Тележка-шпилька для подносов	Конструкция каркаса: сварная. Габаритный размер в мм, не менее 380х300х1680 и не более 420х340х1720. Количество уровней не менее 10. Расстояние между уровнями	шт.	5	Кол-во может быть отличным от Перечня	136	П32		3	Тележка-шпилька предназначена для временного хранения и транспортировки подносов. Количество уровней - 12 шт. Размер	Принято.			
10	Торгово-технологическое	Обеденный зал	1	Тележка для сбора посуды	Конструкция неразборная - поставляется в сборе (сварная). Габаритные размеры в мм, не	шт.	2	УДАЛИТЬ если школа 5-11	136	б/п	Техно-ТТ ТПР-320/905 или аналог		Габаритные размеры: 800х500х850 мм	Принято.			
11	Торгово-технологическое оборудование	Обеденный зал	1	Мармит для вторых блюд тип 1	Материал изготовления: нержавеющая сталь. Напряжение: Э1ф, 220В. Мощность: в соответствии с типом и маркой оборудования. Поддержание температуры готовых вторых блюд и гарниров в соответствии с требованиями СанПиН 2.3/2.4.3590-20. Количество гастророек не менее 5. Регулируемые по высоте ножки. Габаритные размеры в	шт.	1	НЕОБХОДИМО указать габаритные размеры и количество полотен, тип крепления (потолочное/настенное)	136	П22	ЭМК-70Е или аналог		Температурный режим теплового отсека - 85 °С; В комплект поставки входят 1 гастрорейка GN 1/1 глубиной 150 мм, 2 гастрорейки GN 1/2 глубиной 150 мм и 3 гастрорейки GN 1/3 глубиной 150 мм; Электрическое подключение: 220В, 1~N/PE, 2,02 кВт.	Принято.			

№	Раздел	Помещение	Кол-во пом.	Наименование	Технические характеристики	Ед. изм.	Кол-во	Дополнительное пояснение	№ пом. в ГЧ	№ поз. в ГЧ	Марка оборудования	Кол-во, отличное от Перечня	Комментарии проектировщика	Комментарий ГКУ ДНОМ на письмо от 29.07.2025 № 07-10-3057/25-1	Ответ на замечания ГКУ ДНОМ от 01.08.2025	Комментарий ГКУ ДНОМ на письмо от 07.08.2025 № 07-03-1708/25-2	Ответ на замечания ГКУ ДНОМ от 20.08.2025
12	Торгово-технологическое оборудование	Обеденный зал	1	Мармит для первых блюд тип 1	Материал изготовления: нержавеющая сталь. Напряжение: 3ф, 220В. Мощность: в соответствии с типом и маркой оборудования. Поддержание температуры готовых первых блюд в соответствии с требованиями СанПиН 2.3/2.4.3590-20.	шт.	1		136	П23	ПМЭС-70Е или аналог		Температурный режим теплового отсека - 85 °С; Модель оснащена 2 конфорками (Диаметр конфорки: 220 мм); Электрическое подключение: 380В, 1,75 кВт. Габаритные размеры: 1120x717(1022)x1217	Принято.			
13	Торгово-технологическое оборудование	Обеденный зал	1	Прилавок-витрина холодильный тип 1	Материал изготовления корпуса, столешницы: нержавеющая сталь. Напряжение: 3ф, 220В. Мощность: в соответствии с типом и маркой оборудования. Поддержание температуры готовых холодных блюд и закусок в соответствии с требованиями СанПиН	шт.	1		136	П26	ПВВ(Н)-70Е-С-02-НШ или аналог		Температурный режим холодильного отсека от 5 до 15 °С; Демонстрационная площадь полок витрины: 1,36 м2 (3 полки); Электрическое подключение: 220В, 1, 2/0Е, 0,5 кВт.	Принято.			
14	Торгово-технологическое оборудование	Обеденный зал	1	Прилавок для столовых приборов и подносов тип 1	Материал: нержавеющая сталь. Ножи должны регулироваться по высоте. В комплекте: элементы хранения для столовых приборов, направляющие для подносов. Габаритные размеры в мм, не менее: 630x710(1060)x1410.	шт.	1	Кол-во может быть отличным от Перечня	136	П25	ПСРХ-70Е или аналог		В комплект поставки входят 6 гастроремкостей GN 1/6 глубиной 150 мм Габаритные размеры: 600x689x870(1487) мм	Принято.			
15	Торгово-технологическое оборудование	Обеденный зал	1	Прилавок нейтральный тип 1	Материал изготовления: нержавеющая сталь. Регулируемые по высоте полки. Материал изготовления: нержавеющая сталь.	шт.	1	Кол-во может быть отличным от Перечня	136	П24	ПГН-70Е или аналог		Нейтральный прилавок Габаритные размеры: 1120x717(1032)x870 мм	Принято.			
16	Торгово-технологическое оборудование	Обеденный зал	1	Рукомойник	Материал: нержавеющая сталь. Крепление: настенное. Условия монтажа: согласно паспорту	шт.	1	Кол-во может быть отличным от Перечня	136	П10	Техно-ТТ ВМ-12/301 или аналог		Рукомойник коленный, емкость цельнотянутая 355x255x150 из	Принято.			
17	Торгово-технологическое оборудование	Обеденный зал	1	Сифон для рукомойника	Сифон для рукомойника в сборе. Условия монтажа: согласно паспорту завода -	шт.	1	Кол-во может быть отличным от Перечня	136	б/п							
18	Торгово-технологическое оборудование	Обеденный зал	1	Смеситель для рукомойника	Смеситель для рукомойника одноручковый. Крепление к рукомойнику. Габаритные	шт.	1	Кол-во может быть отличным от Перечня	136	б/п							
19	Мебель	Обеденный зал	1	Шкаф-стол рабочий двухдверный тип 1	Соответствие требованиям ГОСТ 16371-2014 "Мебель. Общие технические условия", а	шт.	1	Кол-во может быть отличным от Перечня	136	П39			Габаритные размеры: 800x600x850 мм	Принято.			
20	Торгово-технологическое оборудование	Обеденный зал	1	Микроволновая печь	Печь микроволновая; Вид микроволновой печи: отдельностоящая. Внутреннее	шт.	1	Кол-во может быть отличным от Перечня	136	П38	Samsung ME83KRW-1/BW или		Микроволновая печь. Объем 23 л. Диаметр поворотного стола 288	Принято.			
21	Торгово-технологическое оборудование	Обеденный зал	1	Ограждение с калиткой	Материал трубы: нержавеющая сталь. Тип исполнения: горизонтальная створка	шт.	1	Кол-во может быть отличным от Перечня	136	б/п							
22	Торгово-технологическое оборудование	Обеденный зал	1	Стол производственный 900x600	Столешница и каркас должны быть изготовлены из нержавеющей стали. Конструкция стола разборная.	к-т	0		136	П66	SIMECO 001.6ER.04839 или аналог	1	Новая позиция	Принято.			
23	Торгово-технологическое оборудование	Помещение подготовки блюд к реализации с участком мойки	1	Ванна котломоечная двухсекционная тип 2	Комплект состоит из ванны моечной и сифона(ов). Ванна моечная двухсекционная: -конструкция неразборная /	шт.	1	Кол-во может быть отличным от Перечня	141	П76		0	Две сварные емкости размером 600x600x450 из нержавеющей стали марки AISI 304 толщиной 0,8мм. Конструкция не разборная.	Принято.			
	Торгово-технологическое оборудование	Помещение подготовки блюд к реализации с участком мойки	1	Ванна котломоечная двухсекционная	Конструкция не разборная - поставляется в сборе (сварная). Каркас под моеющей ванной должен быть усилен ребром жесткости шириной в мм, не	шт.	0		141	П77	iRon BM2 или аналог	1	Ванна моечная. Размеры раковины (ДхШхВ): 500x500x300. Габаритные размеры: 1200x700x850 мм	Принято.			

№	Раздел	Помещение	Кол-во пом.	Наименование	Технические характеристики	Ед. изм.	Кол-во	Дополнительное пояснение	№ пом. в ГЧ	№ поз. в ГЧ	Марка оборудования	Кол-во, отличное от Перечня	Комментарии проектировщика	Комментарий ГКУ ДНОМ на письмо от 29.07.2025 № 07-10-3057/25-1	Ответ на замечания ГКУ ДНОМ от 01.08.2025	Комментарий ГКУ ДНОМ на письмо от 07.08.2025 № 07-03-1708/25-2	Ответ на замечания ГКУ ДНОМ от 20.08.2025
24	Торгово-технологическое	Помещение подготовки блюд к	1	Сифон для ванны моечной	Сифон для моечной ванны с разрывом струи в сборе. Условия монтажа: согласно	шт.	2	Кол-во может быть отличным от Перечня	141	б/п							
25	Торгово-технологическое	Помещение подготовки блюд к	1	Смеситель с душирующим устройством	Душирующее устройство со встроенным локтевым смесителем, длина излива не	шт.	2	Кол-во может быть отличным от Перечня	141	б/п		1		Принято.			
	Торгово-технологическое	Помещение подготовки блюд к реализации с участком мойки	1	Смеситель для ванны моечной.	Смеситель для ванны моечной. Крепление настенное или к борту ванны. Габаритные размеры и длина излива в соответствии с моделью	шт.	0		141	б/п		1		Принято.			
26	Торгово-технологическое	Помещение подготовки блюд к	1	Ванна моечная односекционная тип 1	Конструкция не разборная - поставляется в сборе (сварная). Без бортика. Габаритные	шт.	2	Кол-во может быть отличным от Перечня	141	П55			Ванна моечная сварная, размер емкости 569x569x400мм	Принято.			
27	Торгово-технологическое	Помещение подготовки блюд к	1	Сифон для ванны моечной	Сифон для моечной ванны с разрывом струи в сборе. Условия монтажа: согласно	шт.	2	Кол-во может быть отличным от Перечня	141	б/п							
28	Торгово-технологическое	Помещение подготовки блюд к	1	Смеситель с душирующим устройством	Душирующее устройство со встроенным локтевым смесителем, длина излива не	шт.	2	Кол-во может быть отличным от Перечня	141	б/п		0		Принято.			
	Торгово-технологическое	Помещение подготовки блюд к	1	Смеситель для ванны моечной.	Смеситель для ванны моечной. Крепление настенное или к борту ванны. Габаритные	шт.	0		141	б/п		2		Принято.			
29	Торгово-технологическое	Помещение подготовки блюд к	1	Весы настольные	Автоматическая установка нуля и автоматическая регулировка коэффициента усиления	шт.	2	Кол-во может быть отличным от Перечня	141	П56			Весы торговые. Наибольший предел взвешивания 32 кг.	Принято.			
30	Торгово-технологическое	Помещение подготовки блюд к реализации с участком мойки кухонной	1	Зонт вытяжной	Материал: нержавеющая сталь. Принцип работы: вытяжной. Тип конструкции: пристенный. В комплекте: жиротрапливающие фильтры, сливной кран. Габаритные размеры в соответствии с	шт.	1	Кол-во может быть отличным от Перечня	141	П51	МВО-1,2МСВ-0,7П или аналог		Зонт вытяжной пристенный. Бескаркасный. Изготовлен из нержавеющей стали марки AISI 430 толщиной 0,8мм. С	Принято.			
31	Торгово-технологическое	Помещение подготовки блюд к	1	Зонт вытяжной пристенный	Материал: нержавеющая сталь. Принцип работы: вытяжной. Тип конструкции:	шт.	2	Кол-во может быть отличным от Перечня	141	П57			Зонт вытяжной пристенный. Бескаркасный.				
32	Торгово-технологическое	Помещение подготовки блюд к	1	Зонт приточно-вытяжной	Конструкция не разборная - поставляется в сборе (клепаная). Материал: коробка	к-т	1	Кол-во может быть отличным от Перечня	141	П58			Зонт вытяжной пристенный. Бескаркасный.				
33	Торгово-технологическое	Помещение подготовки блюд к	1	Кипятильник электрический	Электрический, непрерывного действия. Материал корпуса: нержавеющая сталь.	шт.	1	Кол-во может быть отличным от Перечня	141	П59	ЭКГ-100 или аналог		Электрокипятильник. Производительность 100 л/ч.	Принято.			
34	Торгово-технологическое	Помещение подготовки блюд к	1	Магнитный держатель для ножей	Материал корпуса: пластик. Крепление: настенное. Вставки из ферромагнитного материала.	шт.	1	Кол-во может быть отличным от Перечня	141	П60			Магнитный держатель для ножей. Материал: пластик.				
35	Торгово-технологическое	Помещение подготовки блюд к	1	Набор гастроемкостей с крышками для пароконвектомата 20	Материал: нержавеющая сталь толщиной не менее: 0,8 мм. Тип гастроемкости: GN 1/1.	набор	2	Кол-во может быть отличным от Перечня	141	б/п			Набор гастроемкостей с крышками. Материал:				
36	Торгово-технологическое	Помещение подготовки блюд к реализации с участком	1	Облучатель бактерицидный	Облучатель бактерицидный ультрафиолетовый настенный комбинированного типа. Использование в помещении с отсутствием людей (с	шт.	1	Кол-во может быть отличным от Перечня	141	П71	ОБРН-150 или аналог		Облучатель бактерицидный. Количество бактерицидных ламп 2 шт.	Заменить на модель ОБРН-150 либо аналог.	Откорректировано	Принято.	
37	Торгово-технологическое	Помещение подготовки блюд к	1	Овощерезательно-протирочная машина	Материал корпуса: нержавеющая сталь. Производительность не менее:	шт.	1		141	П74	УКМ-11 или аналог		Машина кухонная универсальная. Механизм	Принято.			
38	Торгово-технологическое	Помещение подготовки блюд к	1	Пароконвектомат 20 уровней	Электрический. Тип: бойлерный. Материал: нержавеющая сталь.	шт.	2		141	П61	ПКА 20-1/ПМ2-01 или аналог		Пароварочный конвективный аппарат, электрический.	Принято.			
39	Торгово-технологическое	Помещение подготовки блюд к	1	Плита электрическая 6 конфорок	Материал: нержавеющая сталь. Должна быть оснащена жарочным шкафом. Площадь	шт.	1		141	П62	6ЖКШ-01 или аналог		Шестиконфорочная плита. Кол-во комфорок - 6 шт.	Принято.			
40	Торгово-технологическое	Помещение подготовки блюд к	1	Подставка под кухонный инвентарь	Конструкция неразборная - поставляется в сборе (сварная). Габаритные размеры в мм, не	шт.	1		141	П63	030.0ES.05837 или аналог		Подставка под кухонный инвентарь, нержавеющая сталь.	Принято.			

№	Раздел	Помещение	Кол-во пом.	Наименование	Технические характеристики	Ед. изм.	Кол-во	Дополнительное пояснение	№ пом. в ГЧ	№ поз. в ГЧ	Марка оборудования	Кол-во, отличное от Перечня	Комментарии проектировщика	Комментарий ГКУ ДНОМ на письмо от 29.07.2025 № 07-10-3057/25-1	Ответ на замечания ГКУ ДНОМ от 01.08.2025	Комментарий ГКУ ДНОМ на письмо от 07.08.2025 № 07-03-1708/25-2	Ответ на замечания ГКУ ДНОМ от 20.08.2025
41	Торгово-технологическое	Помещение подготовки блюд к	1	Подставка под электрокипятильник	Материал: нержавеющая сталь, толщиной не менее 0,8 мм. В столешнице должны быть	шт.	1		141	П64			Подставка под электрокипятильник. Материал:				
42	Торгово-технологическое	Помещение подготовки блюд к	1	Полка для хранения разделочных досок	Тип монтажа: настенный. Для хранения не менее 6 разделочных досок на "ребре".	шт.	2		141	П65	Техно-ТТ ПН-117/600 или аналог		Полка для хранения разделочных досок Габаритные размеры:	Принято.			
43	Торгово-технологическое	Помещение подготовки блюд к	1	Рукомойник	Материал: нержавеющая сталь. Крепление: настенное. Условия монтажа: согласно паспорту	шт.	2		141	П10	Техно-ТТ ВМ-12/301 или аналог		Рукомойник коленный, емкость цельнотянутая 355х255х150 из	Принято.			
44	Торгово-технологическое	Помещение подготовки блюд к	1	Сифон для рукомойника.	Сифон для рукомойника в сборе. Условия монтажа: согласно паспорту завода -	шт.	2		141	б/п							
45	Торгово-технологическое	Помещение подготовки блюд к	1	Смеситель для рукомойника	Смеситель для рукомойника одноручковый. Крепление к рукомойнику. Габаритные	шт.	2		141	б/п							
46	Торгово-технологическое	Помещение подготовки блюд к	1	Стеллаж 900х500	Конструкция: сборно - разборная. Не менее 4 полок. Материал каркаса и полок:	шт.	1		141	П52		0	Стеллаж Габаритные размеры: 900х500х1800 мм	Принято.			
47	Торгово-технологическое	Помещение подготовки блюд к	1	Стеллаж 600х500	Конструкция: сборно - разборная. Не менее 4 полок. Материал каркаса и полок:	шт.	1		141	П44		0	Стеллаж Габаритные размеры: 600х500х1800 мм	Принято.			
	Торгово-технологическое оборудование	Помещение подготовки блюд к реализации с участком мойки кухонной посуды	1	Стеллаж с перфорированными полками 900х400	Конструкция: сборно - разборная. Не менее 4 полок. Материал каркаса и полок: нержавеющая сталь. Полки должны быть перфорированные. Ножки должны быть с регуляторами	шт.			141	П53	СТР-414/904 или аналог	1	Стеллаж технологический разборный, стойки из уголка 40х40 толщиной 2мм, покрытого порошковой краской серого цвета. Четыре	Принято.			
	Торгово-технологическое оборудование	Помещение подготовки блюд к реализации с участком мойки	1	Стеллаж с перфорированными полками 600х400	Конструкция неразборная/разборная. Габаритные размеры в мм, не менее: 580х380х1580 и не более: 620х420х1850. Количество полок, не менее 4 шт. Материал	шт.			141	П67	СТР-414/604 или аналог	1	Стеллаж технологический разборный, стойки из уголка 40х40 толщиной 2мм, покрытого порошковой краской	Принято.			
47	Торгово-технологическое оборудование	Помещение подготовки блюд к реализации с участком	1	Стерилизатор для ножей ультрафиолетовый	Материал каркаса: нержавеющая сталь. Крепление: настенное. Ртутная лампа низкого/высокого давления. Номинальная	шт.	1		141	П72	SK-15 или аналог		Стерилизатор для ножей ультрафиолетовый Электрическое подключение: 220В	Принято.			
48	Торгово-технологическое оборудование	Помещение подготовки блюд к реализации с участком мойки кухонной посуды	1	Стол производственный 600х700	Столешница и каркас должны быть изготовлены из нержавеющей стали. Конструкция стола разборная. Возможно наличие борта. В комплект должна входить сплошная/решетчатая полка из нержавеющей стали. Ножки	к-т	0		141	П78	SIMECO 001.7ER.05840 или аналог	1	Стол производственный из нержавеющей стали. Конструкция разборная, сплошная полка, борт. Габаритные размеры: 600х700х850 мм	Откорректировано согласно Приложению 2 л.1 пункт 3 "Увеличена глубина производственного стола", глубина принята 700 мм, согласно марки оборудования	Принято.		
49	Торгово-технологическое оборудование	Помещение подготовки блюд к реализации с участком мойки кухонной посуды	1	Стол производственный 600х600	Столешница и каркас должны быть изготовлены из нержавеющей стали. Конструкция стола разборная. Возможно наличие борта. В комплект должна входить сплошная/решетчатая полка из нержавеющей стали. Ножки	к-т	3		141	П54	SIMECO 001.6ER.04840 или аналог	2	Стол производственный из нержавеющей стали. Конструкция разборная, сплошная полка, борт. Габаритные размеры: 600х600х850 мм	Принято.	Откорректирована 1 поз. согласно Приложению 2 л.1 пункт 3 "Увеличена глубина производственного стола", глубина принята 700 мм, изменена марка оборудования на П78	Принять 2 шт. согласно Приложения 2. Откорректировать нумерацию на плане.	Откорректировано

№	Раздел	Помещение	Кол-во пом.	Наименование	Технические характеристики	Ед. изм.	Кол-во	Дополнительное пояснение	№ пом. в ГЧ	№ поз. в ГЧ	Марка оборудования	Кол-во, отличное от Перечня	Комментарии проектировщика	Комментарий ГКУ ДНОМ на письмо от 29.07.2025 № 07-10-3057/25-1	Ответ на замечания ГКУ ДНОМ от 01.08.2025	Комментарий ГКУ ДНОМ на письмо от 07.08.2025 № 07-03-1708/25-2	Ответ на замечания ГКУ ДНОМ от 20.08.2025
	Торгово-технологическое оборудование	Помещение подготовки блюда к реализации с участком мойки кухонной посуды	1	Стол производственный 600x700	Столешница и каркас должны быть изготовлены из нержавеющей стали. Конструкция стола разборная. Возможно наличие борта. В комплект должна входить сплошная/решётчатая полка из нержавеющей стали. Ножки должны быть оснащены регулируемыми по высоте опорами, позволяющими компенсировать неровности пола. Габаритные размеры в мм, не менее 580x680x830 и не более 620x720x870.	к-т	0		141	П79	SIMECO 001.6ER.04454 или аналог	0	Стол производственный из нержавеющей стали. Конструкция разборная, сплошная полка, борт. Габаритные размеры: 600x700x850 мм	Принять 1 шт. согласно Приложения 2.	Откорректировано	Исключить оборудование.	Исключено
49	Торгово-технологическое оборудование	Помещение подготовки блюда к реализации с участком мойки кухонной посуды	1	Стол производственный 900x600	Столешница и каркас должны быть изготовлены из нержавеющей стали. Конструкция стола разборная. Возможно наличие борта. В комплект должна входить сплошная/решётчатая полка из нержавеющей стали. Ножки должны быть оснащены регулируемыми по высоте опорами, позволяющими компенсировать неровности пола. Габаритные размеры в мм, не менее 880x580x830 и не более 920x620x870.	к-т	2		141	П66	SIMECO 001.6ER.04839 или аналог	2	Стол производственный из нержавеющей стали. Конструкция разборная, сплошная полка, борт. Габаритные размеры: 900x600x850 мм	Принять 2 шт. согласно Приложения 2.	Откорректировано	Принято.	
50	Торгово-технологическое оборудование	Помещение подготовки блюда к реализации с участком мойки кухонной посуды	1	Стол-вставка нейтральная тип 1	Конструкция неразборная - поставляется в сборе (сварная), без борта. Габаритные размеры в мм, не менее: 280x580x830 и не более: 320x620x870. Материал столешницы нержавеющая сталь. Толщина металла столешницы в мм, не менее 2-х дверей. Наличие	шт.	2		141	П68	СП-114/408 или аналог		Стол-вставка нейтральная. Материал столешницы	Принято.			
51	Торгово-технологическое оборудование	Помещение подготовки блюда к реализации с участком мойки кухонной посуды	1	Стол-вставка нейтральная тип 3	Конструкция неразборная - поставляется в сборе (сварная), без борта. Габаритные размеры в мм, не менее: 280x580x830 и не более: 320x620x870. Материал столешницы нержавеющая сталь. Толщина металла столешницы в мм, не менее 2-х дверей. Наличие	шт.	1		141	П75	Финист СПП-300*600*850 Эконом или аналог		Стол-вставка нейтральная. Материал столешницы нержавеющая сталь. Сварная конструкция. Габаритные размеры: 300x600x850 мм	Откорректировать марку оборудования согласно графе "Технические характеристики".	Откорректировано	Принято.	
52	Торгово-технологическое оборудование	Помещение подготовки блюда к реализации с участком мойки кухонной посуды	1	Тележка с баком для отходов	Материал бака: полипропилен. Объем бака не менее: 50 л. В комплекте с крышкой.	шт.	3		141	б/п			Тележка с баком для отходов. Материал бака: полипропилен.				
53	Торгово-технологическое оборудование	Помещение подготовки блюда к реализации с участком мойки кухонной посуды	1	Тележка-шпилька для гастробюджетов	Материал каркаса: нержавеющая сталь. Конструкция каркаса	шт.	1	Кол-во может быть отличным от Перечня	141	П69	ТППГ-14-1/1 или аналог		Тележка-шпилька для гастробюджетов. Количество уровней	Принято.			
54	Торгово-технологическое оборудование	Помещение подготовки блюда к реализации с участком мойки кухонной посуды	1	Холодильный стол тип 2	Материал: нержавеющая сталь. Среднетемпературный. Диапазон рабочих температур - 2...+10°C. Боковое расположение агрегата. Не менее 2-х дверей. Наличие	шт.	1	Кол-во может быть отличным от Перечня	141	П73	ТМ2-G или аналог		Холодильный стол. Объем 270 л. Двери - 2 шт. Диапазон рабочих температур от -2 до 10 °C	Принято.			
55	Торгово-технологическое оборудование	Помещение подготовки блюда к реализации с участком мойки кухонной посуды	1	Водоумягчитель	Материал: нержавеющая сталь. Среднетемпературный. Диапазон рабочих температур - 2...+10°C. Боковое расположение агрегата. Не менее 2-х дверей. Наличие	шт.	3		141	б/п			Новая позиция				
56	Торгово-технологическое оборудование	Помещение подготовки блюда к реализации с участком мойки кухонной посуды	1	Шкаф холодильный 500	Материал: сталь с полимерным покрытием. Дверь металлическая. Однодверный	шт.	1		141	П70	ПХ-0,5 или аналог		Шкаф холодильный. Объем 520 л. Температурный режим от -5 до 5 °C	Принято.			

№	Раздел	Помещение	Кол-во пом.	Наименование	Технические характеристики	Ед. изм.	Кол-во	Дополнительное пояснение	№ пом. в ГЧ	№ поз. в ГЧ	Марка оборудования	Кол-во, отличное от Перечня	Комментарии проектировщика	Комментарий ГКУ ДНОМ на письмо от 29.07.2025 № 07-10-3057/25-1	Ответ на замечания ГКУ ДНОМ от 01.08.2025	Комментарий ГКУ ДНОМ на письмо от 07.08.2025 № 07-03-1708/25-2	Ответ на замечания ГКУ ДНОМ от 20.08.2025
56	Торгово-технологическое оборудование	Кладовая и моечная оборотной тары	1	Ванна котломоечная двухсекционная	Конструкция не разборная - поставляется в сборе (сварная). Каркас под мойшей ванной должен быть усилен ребром жесткости шириной в мм, не менее: 170, материал нержавеющей сталь, толщина металла в мм, не менее: 0,8	шт.	1		006	П14	Проммаш 2ВМ-12/6/2,5 или аналог	0	Ванна котломоечная из нержавеющей стали. Объем 2х50 л. Борт Габаритные размеры: 1200х700х850 мм	Исключить.	Исключено	Принято.	
	Торгово-технологическое оборудование	Кладовая и моечная оборотной тары	1	Ванна котломоечная двухсекционная тип 2	Комплект состоит из ванны моечной и сифона(ов). Ванна моечная двухсекционная: -конструкция неразборная / разборная; -материал — нержавеющая сталь, толщина металла в мм: не менее 0,8; -габаритные размеры в мм, не менее: 1320х680х830 и не более: 1360х720х870; -количество емкостей - 2, глубина каждой емкости в мм: не менее 440 и не более 460; -диаметр сливного отверстия в мм, не более 50;	шт.	0		006	П16	ВМ-21/600 или аналог	1	Две сварные емкости размером 600х600х450 из нержавеющей стали марки AISI 304 толщиной 0,8мм. Каркас сварной из уголка 40х40 толщиной 2мм, покрытого порошковой краской серого цвета, внизу по периметру обвязка. Ванна комплектуется выпуском с нержавеющей решеткой и механическим запорным клапаном	Принять 1 шт. согласно Приложения 2.	Откорректировано	Принято.	
57	Торгово-технологическое	Кладовая и моечная оборотной	1	Сифон для ванны моечной	Сифон для моечной ванны с разрывом струи в сборе. Условия монтажа: согласно	шт.	2		006	б/п							
58	Торгово-технологическое	Кладовая и моечная оборотной	1	Смеситель с душирующим устройством	Душирующее устройство со встроенным локтевым смесителем, линия излива не	шт.	1	Окончательное кол-во и тип определяются	006	б/п							
	Торгово-технологическое	Кладовая и моечная оборотной	1	Смеситель для ванны моечной.	Смеситель для ванны моечной. Крепление настенное или к борту ванны. Габаритные	шт.	0		006	б/п		1					
59	Торгово-технологическое оборудование тары	Кладовая и моечная оборотной	1	Зонт вытяжной	Материал: нержавеющая сталь. Принцип работы: вытяжной. Тип конструкции: пристенный. В комплекте:	шт.	1	Окончательное кол-во и тип определяются	006	П51	МВО-1,4МСВ-0,7П или аналог		Зонт вытяжной пристенный. Бескаркасный. Изготовлен из	Принять габаритные размеры зонта 1400х700 мм согласно Приложения 2.	Откорректировано	Принято.	
60	Торгово-технологическое	Кладовая и моечная оборотной	1	Рукомойник	Материал: нержавеющая сталь. Крепление: настенное. Условия монтажа: согласно паспорту	шт.	1	Окончательное кол-во и тип определяются	006	П10	Техно-ТТ ВМ-12/301 или аналог		Рукомойник коленный, емкость цельнотянутая 355х255х150 из	Принято.			
61	Торгово-технологическое	Кладовая и моечная оборотной	1	Сифон для рукомойника.	Сифон для рукомойника в сборе. Условия монтажа: согласно паспорту завода -	шт.	1		006	б/п							
62	Торгово-технологическое	Кладовая и моечная оборотной	1	Смеситель для рукомойника	Смеситель для рукомойника одноручковый. Крепление к рукомойнику. Габаритные	шт.	1		006	б/п							
63	Торгово-технологическое оборудование тары	Кладовая и моечная оборотной тары	1	Стеллаж с перфорированными полками 900х500	Конструкция: сборно - разборная. Не менее 4 полок. Материал каркаса и полок: нержавеющая сталь. Полки должны быть перфорированные. Ножки должны быть с регуляторами	шт.	1		006	П17	СТР-524/900 или аналог		Стеллаж с перфорированными полками. Количество полок, не менее 4 шт. Материал каркаса и полок: нержавеющая сталь. Полки	Принять 1 шт. согласно Приложения 2.	Откорректировано	Принять откорректированные габаритные размеры в ГЧ согласно тех. характеристик подобранной марки оборудования.	Откорректировано
	Торгово-технологическое оборудование тары	Кладовая и моечная оборотной тары	1	Стеллаж с перфорированными полками 900х400	Конструкция: сборно - разборная. Не менее 4 полок. Материал каркаса и полок: нержавеющая сталь. Полки должны быть	шт.	0		006	П53	СТР-414/904 или аналог		технологический разборный, стойки из уголка 40х40 толщиной 2мм, покрытого	Исключить.	Исключено	Принято.	

№	Раздел	Помещение	Кол-во пом.	Наименование	Технические характеристики	Ед. изм.	Кол-во	Дополнительное пояснение	№ пом. в ГЧ	№ поз. в ГЧ	Марка оборудования	Кол-во, отличное от Перечня	Комментарии проектировщика	Комментарий ГКУ ДНОМ на письмо от 29.07.2025 № 07-10-3057/25-1	Ответ на замечания ГКУ ДНОМ от 01.08.2025	Комментарий ГКУ ДНОМ на письмо от 07.08.2025 № 07-03-1708/25-2	Ответ на замечания ГКУ ДНОМ от 20.08.2025
64	Торгово-технологическое оборудование	Моечная для столовой посуды	1	Ванна моечная двухсекционная тип 1	Конструкция не разборная - поставляется в сборе (сварная). Без бортика. Габаритные размеры в мм, не менее: 1180x580x830 и не более: 1220x620x870. Количество емкостей - 2, глубина каждой емкости в мм, не менее: 400. Материал ванны: нержавеющая сталь, толщиной в мм, не менее 0,7 и не более 0,8. Каркас под мойщей ванной: материал нержавеющая сталь. Профиль ножек - квадратная или круглая труба, размером профиля в мм, не менее 20. Опорные ножки	шт.	1		137	П40	ВМО2-530ЧНК-М		Ванна моечная двухсекционная. Материал нержавеющая сталь. Размеры раковины 530x530 мм. Габаритные размеры: 1200x630x870 мм			Заполнить графу "Марка оборудования". Габариты оборудования привести в соответствие с графой "Технические характеристики".	Откорректировано
65	Торгово-технологическое	Моечная для столовой посуды	1	Сифон для ванны моечной	Сифон для моечной ванны с разрывом струи в сборе. Условия монтажа: согласно	шт.	2		137	б/п							
66	Торгово-технологическое	Моечная для столовой посуды	1	Смеситель с душирующим устройством	Душирующее устройство со встроенным локтевым смесителем, длина излива не	шт.	2		137	б/п							
67	Торгово-технологическое оборудование	Моечная для столовой посуды	1	Ванна моечная трехсекционная тип 2	Конструкция не разборная - поставляется в сборе (сварная). Без бортика. Габаритные размеры в мм, не менее: 1680x580x830 и не более: 1720x620x870. Количество емкостей - 3, глубина каждой емкости в мм, не менее: 400. Материал ванны: нержавеющая сталь, толщиной в мм, не менее 0,7 и не более 0,8. Каркас под мойщей ванной: материал нержавеющая сталь. Профиль ножек - квадратная или круглая труба, размером профиля в мм, не менее 20. Опорные ножки	шт.	1		137	П41	ВМО3-480ЧНК-М или аналог		Ванна моечная трехсекционная. Материал нержавеющая сталь. Размеры раковины 480x480 мм. Габаритные размеры: 1650x580x870 мм	Заполнить графу "Марка оборудования".	Откорректировано	Принято.	
68	Торгово-технологическое	Моечная для столовой посуды	1	Сифон для ванны моечной	Сифон для моечной ванны с разрывом струи в сборе. Условия монтажа: согласно	шт.	3		137	б/п							
69	Торгово-технологическое	Моечная для столовой посуды	1	Смеситель с душирующим устройством	Душирующее устройство со встроенным локтевым смесителем, длина излива не	шт.	3		137	б/п		0					
	Торгово-технологическое	Моечная для столовой посуды	1	Смеситель для ванны моечной.	Смеситель для ванны моечной. Крепление настенное или к борту ванны. Габаритные	шт.	0		137	б/п		3		Принять 3 шт. согласно Приложения 2.	Откорректировано	Принято.	
70	Торгово-технологическое	Моечная для столовой посуды	1	Зонт вытяжной	Материал: нержавеющая сталь. Принцип работы: вытяжной. Тип конструкции: пристенный.	шт.	1		137	П43	МВО-1,5МСВ-1,П или аналог		Зонт вытяжной пристенный. Бескаркасный.	Заполнить графу "Марка оборудования".	Откорректировано	Принято.	
71	Торгово-технологическое	Моечная для столовой посуды	1	Зонт вытяжной	Материал: нержавеющая сталь. Принцип работы: вытяжной. Тип конструкции: пристенный.	шт.	1	Кол-во может быть отличным от Перечня	141	П42	МВО-1,7МСВ-0,П или аналог		Зонт вытяжной пристенный. Бескаркасный.	Заполнить графу "Марка оборудования".	Откорректировано	Принято.	
72	Торгово-технологическое	Моечная для столовой посуды	1	Зонт вытяжной	Материал: нержавеющая сталь. Принцип работы: вытяжной. Тип конструкции: пристенный.	шт.	1	Кол-во может быть отличным от Перечня	141	П48	МВО-1,2МСВ-0,П или аналог		Зонт вытяжной пристенный. Бескаркасный.	Заполнить графу "Марка оборудования".	Откорректировано	Принято.	
71	Торгово-технологическое оборудование	Моечная для столовой посуды	1	Машина посудомоечная купольная 1400	Для мытья столовой посуды и приборов, стаканов и т.д. Материал корпуса: нержавеющая сталь. Производительность не менее 1400 тар/час. Напряжение: 3ф, 380-400В. Мощность: в соответствии с типом и маркой оборудования. Автоматическая полка и поддержания уровня	к-т	1		137	П45	LM-C-1400 или аналог		Машина посудомоечная купольная. Производительность 1400 шт./ч. Количество программ мытья 2 шт. Электрическое подключение: 380В, 3~N/PE, 22,5 кВт. Габаритные размеры:	Не исправлено. Указать модель.	Откорректировано	Принято.	

№	Раздел	Помещение	Кол-во пом.	Наименование	Технические характеристики	Ед. изм.	Кол-во	Дополнительное пояснение	№ пом. в ГЧ	№ поз. в ГЧ	Марка оборудования	Кол-во, отличное от Перечня	Комментарии проектировщика	Комментарий ГКУ ДНОМ на письмо от 29.07.2025 № 07-10-3057/25-1	Ответ на замечания ГКУ ДНОМ от 01.08.2025	Комментарий ГКУ ДНОМ на письмо от 07.08.2025 № 07-03-1708/25-2	Ответ на замечания ГКУ ДНОМ от 20.08.2025
72	Торгово-технологическое	Моечная для столовой посуды	1	Рукомойник	Материал: нержавеющая сталь. Крепление: настенное. Условия монтажа: согласно паспорту	шт.	1		137	П10	Техно-ТТ ВМ-12/301 или аналог		Рукомойник коленный, емкость цельнотянутая 355х255х150 из	Принято.			
73	Торгово-технологическое	Моечная для столовой посуды	1	Сифон для рукомойника.	Сифон для рукомойника в сборе. Условия монтажа: согласно паспорту завода -	шт.	1		137	б/ч							
74	Торгово-технологическое	Моечная для столовой посуды	1	Смеситель для рукомойника	Смеситель для рукомойника одноручковый. Крепление к рукомойнику. Габаритные	шт.	1	Окончательное кол-во и тип определяются	137	б/ч							
75	Торгово-технологическое	Моечная для столовой посуды	1	Стеллаж для сушки посуды	Стеллаж для сушки тарелок и стаканов (комбинированный). Конструкция неразборная -	шт.	4	Окончательное кол-во и тип определяются	137	П50	СПП-02 или аналог		Стеллаж мобильный для столовой посуды, нержавеющая сталь.	Принято.			
76	Торгово-технологическое	Моечная для столовой посуды	1	Стеллаж для хранения столовой посуды	Конструкция: сборно - разборная. Материал изготовления: нержавеющая	шт.	2	Окончательное кол-во и тип определяются	137	П49	СКТК-4КЭ-2М или аналог		Стеллаж для сушки столовой посуды, нержавеющая сталь.	Принято.			
77	Торгово-технологическое	Моечная для столовой посуды	1	Стол предмоечный для купольных посудомоечных машин	Стол предмоечный - материал: нержавеющая сталь, цельнотянутая ванна для	шт.	1		137	П46	СПМП-6-5 или аналог		Стол предмоечный с душем. Материал: нержавеющая сталь.	Принято.			
78	Торгово-технологическое	Моечная для столовой посуды	1	Стол раздаточный для купольных посудомоечных машин	Каркас и столешница должны быть изготовлены из нержавеющей стали. Возможно	шт.	1		137	П47	СПМП-6-1 или аналог		Стол раздаточный. Материал: нержавеющая сталь.	Принято.			
79	Торгово-технологическое	Моечная для столовой посуды	1	Тележка с баком для отходов	Материал бака: полипропилен. Объем бака не менее: 50 л. В комплекте с крышкой.	шт.	1		137	б/ч			Тележка с баком для отходов. Материал бака: полипропилен.				
80	Торгово-технологическое	Моечная для столовой посуды	1	Водоумягчитель		шт.	1		137	б/ч			Новая позиция				
80	Торгово-технологическое	Загрузочный цех	1	Весы напольные тип 1	Автоматическая установка нуля и автоматическая регулировка коэффициента усиления.	шт.	1		009	П1	Масса ТВ-М-300.2-А3 или аналог		Весы напольные. Максимальный предел взвешивания 300 кг.	Принято.			
81	Торгово-технологическое оборудование	Загрузочный цех	1	Тележка грузовая платформенная	Платформенная тележка, четырехколесная, грузоподъемность не менее 150 кг. Материал каркаса и платформы: полимерно-	шт.	1		009	П2	КПО-500Т-125-К или аналог		Тележка грузовая платформенная, грузоподъемность 300 кг. Размер платформы: 1200х800 мм.	Принято.			
82	Торгово-технологическое оборудование	Помещение с холодильным оборудованием	1	Шкаф холодильный 700 с нижним агрегатом	Материал: сталь с полимерным покрытием. Дверь металлическая. Одностворчатый. Среднетемпературный. Диапазон рабочих температур - 5...+5°C. Нижнее расположение агрегата. Не менее 4-х полок. Напряжение: 220В. Мощность: 0,3 кВт. Габаритные размеры в мм, не менее: 730х840х2040. Должен соответствовать требованиям	шт.	4		005	П21	ШХс-0,7-0,2 или аналог		Шкаф холодильный среднетемпературный с нижним агрегатом. Объем 700л. Температурный режим от 0 до +5 °С. Электрическое подключение: 220В, ~/N/PE, 0,3 кВт.	Откорректировать марку оборудования согласно графе "Технические характеристики" и габаритных размеров в ГЧ.	Откорректировано	Принято.	
83	Торгово-технологическое оборудование	Помещение с холодильным оборудованием	1	Шкаф холодильный низкотемпературный 700 с нижним агрегатом	Материал: сталь с полимерным покрытием. Дверь металлическая. Одностворчатый. Низкотемпературный. Температура воздуха полезного объема, не выше -18°C. Нижнее расположение агрегата. Не менее 4-х полок. Напряжение: 21ф, 220В. Мощность: в соответствии с типом и маркой оборудования. Охлаждаемый объем: не менее 700 л. Габаритные размеры в мм, не менее: 730х840х2040. Должен соответствовать требованиям	шт.	2		005	П3	ШХн-0,7-02 или аналог		Шкаф холодильный низкотемпературный с нижним агрегатом. Объем 700л. Температурный режим не выше -18 °С. Электрическое подключение: 220В, ~/N/PE, 0,3 кВт. Габаритные размеры: 740х850х2050 мм	Откорректировать марку оборудования согласно графе "Технические характеристики" и габаритных размеров в ГЧ.	Откорректировано	Принято.	
84	Торгово-технологическое	Помещение для временного	1	Рукомойник	Материал: нержавеющая сталь. Крепление: настенное. Условия монтажа: согласно паспорту	шт.	1		003	П10	Техно-ТТ ВМ-12/301 или аналог		Рукомойник коленный, емкость цельнотянутая 355х255х150 из	Принято.			
85	Торгово-технологическое	Помещение для временного	1	Сифон для рукомойника.	Сифон для рукомойника в сборе. Условия монтажа: согласно паспорту завода -	шт.	1		003	б/ч							

№	Раздел	Помещение	Кол-во пом.	Наименование	Технические характеристики	Ед. изм.	Кол-во	Дополнительное пояснение	№ пом. в ГЧ	№ поз. в ГЧ	Марка оборудования	Кол-во, отличное от Перечня	Комментарии проектировщика	Комментарий ГКУ ДНОМ на письмо от 29.07.2025 № 07-10-3057/25-1	Ответ на замечания ГКУ ДНОМ от 01.08.2025	Комментарий ГКУ ДНОМ на письмо от 07.08.2025 № 07-03-1708/25-2	Ответ на замечания ГКУ ДНОМ от 20.08.2025
86	Торгово-технологическое	Помещение для временного	1	Смеситель для раковины	Смеситель для раковины одноручковый. Крепление к раковине. Габаритные	шт.	1		003	б/п							
87	Торгово-технологическое	Помещение для временного	1	Стеллаж с перфорированными полками 600x400	Конструкция: сборно - разборная. Не менее 4 полок. Материал каркаса и полок:	шт.	1		003	П67	СТР-414/604 или аналог		Стеллаж технологический разборный, стойки из	Принято.			
88	Торгово-технологическое	Помещение для временного	1	Шкаф холодильный 500 с нижним агрегатом	Материал: сталь с полимерным покрытием. Дверь металлическая.	шт.	1		003	П12	ШХ-0,5-02 или аналог		Шкаф холодильный. Объем 520 л. Температурный режим	Принято.			
89	Торгово-технологическое	Помещение для хранения уборочного	1	Раковина	Материал: нержавеющая сталь. Крепление: настенное. Условия монтажа: согласно паспорту	шт.	1		004	П10	Техно-ТТ ВМ-12/301 или аналог		Раковина коленная, емкость цельнотянутая 355x255x150 из	Принято.			
90	Торгово-технологическое	Помещение для хранения уборочного	1	Сифон для раковины.	Сифон для раковины в сборе. Условия монтажа: согласно паспорту завода -	шт.	1		004	б/п							
91	Торгово-технологическое	Помещение для хранения уборочного	1	Смеситель для раковины	Смеситель для раковины одноручковый. Крепление к раковине. Габаритные	шт.	1		004	б/п							
92	Торгово-технологическое	Помещение для хранения уборочного	1	Стеллаж 600x400	Конструкция: сборно - разборная. Не менее 4 полок. Материал каркаса и полок:	шт.	1		004	П11	С-4-0,4/0,4/1,8 или аналог		Стеллаж. Материал каркаса и полок: нержавеющая сталь.	Принято.			
93	Торгово-технологическое	Помещение для хранения уборочного	1	Подтоварник 600x600	Конструкция неразборная - поставляется в сборе (сварная). Габаритные размеры в мм, не	шт.	1		004	П13	Техно-ТТ ПТ-606/3 или аналог			Принято.			
94	Мебель	Помещение для хранения уборочного инвентаря (Помещение)	1	Шкаф для хозяйственного инвентаря одностворчатый металлический	Изделие должно соответствовать требованиям ГОСТ 16371-2014 "Мебель. Общие технические условия". Материал изделия - металл. Толщина материала изделия не менее 0,7 мм.	шт.	1		004	С657	ПУ-500 или аналог		Шкаф для уборочного инвентаря. Габаритные размеры: 500x400x1860	Принято.			
95	Мебель	Помещение для персонала (включая)	1	Шкаф для одежды металлический двухуровневый на 4	Изделие должно соответствовать требованиям ГОСТ Р 56422-2015 "Шкафы	шт.	3		007	П18	LS-22 или аналог		Шкаф для одежды с выдвижной скамейкой-подставкой.	Принято.			
96	Инвентарь хозяйственный	Помещение для персонала (включая)	1	Зеркало тип 1	Травмобезопасное. Торцы зеркального полотна должны быть зашлифованы и	шт.	1		007	б/п			Позиция из общего перечня оснащения				
97	Кухонный инвентарь	Кухонный инвентарь	1	Венчик	Материал: нержавеющая сталь. Длина не менее 450 мм, не более 650 мм	шт.	2		141	б/п							
98	Кухонный инвентарь	Кухонный инвентарь	1	Доска разделочная	Материал: дерево твердых пород без дефектов (зазоров, щелей и др.). Размер в мм, не	шт.	24		141	б/п							
99	Кухонный инвентарь	Кухонный инвентарь	1	Кассета для столовых приборов	Для хранения столовых приборов. Материал: нержавеющая сталь. Не менее 4	шт.	3	Кол-во может быть отличным от Перечня	141	б/п		2					
100	Кухонный инвентарь	Кухонный инвентарь	1	Кастриля с крышкой, 3 л	Изделие должно соответствовать ГОСТ Р 54156-2010 "Посуда и приборы	шт.	3	Кол-во может быть отличным от Перечня	141	б/п							
101	Кухонный инвентарь	Кухонный инвентарь	1	Кастриля с крышкой, 5 л	Изделие должно соответствовать ГОСТ Р 54156-2010 "Посуда и приборы	шт.	3	Кол-во может быть отличным от Перечня	141	б/п							
102	Кухонный инвентарь	Кухонный инвентарь	1	Котел с крышкой, 10 л	Материал: нержавеющая сталь. Дно с теплораспределительным слоем. Объем - 10 л.	шт.	5	Кол-во может быть отличным от Перечня	141	б/п							
103	Кухонный инвентарь	Кухонный инвентарь	1	Котел с крышкой, 20 л	Материал: нержавеющая сталь. Дно с теплораспределительным слоем. Объем - 20 л.	шт.	5		141	б/п							
104	Кухонный инвентарь	Кухонный инвентарь	1	Котел с крышкой, 30 л	Материал: нержавеющая сталь. Дно с теплораспределительным слоем. Объем - 30 л.	шт.	5	Окончательное кол-во и тип определяются	141	б/п							
105	Кухонный инвентарь	Кухонный инвентарь	1	Котел с крышкой, 40 л	Материал: нержавеющая сталь. Дно с теплораспределительным слоем. Объем - 40 л.	шт.	2	Окончательное кол-во и тип определяются	141	б/п							
106	Кухонный инвентарь	Кухонный инвентарь	1	Котел с крышкой, 50 л	Материал: нержавеющая сталь. Дно с теплораспределительным слоем. Объем - 50 л.	шт.	2	Окончательное кол-во и тип определяются	141	б/п							

№	Раздел	Помещение	Кол-во пом.	Наименование	Технические характеристики	Ед. изм.	Кол-во	Дополнительное пояснение	№ пом. в ГЧ	№ поз. в ГЧ	Марка оборудования	Кол-во, отличное от Перечня	Комментарии проектировщика	Комментарий ГКУ ДНОМ на письмо от 29.07.2025 № 07-10-3057/25-1	Ответ на замечания ГКУ ДНОМ от 01.08.2025	Комментарий ГКУ ДНОМ на письмо от 07.08.2025 № 07-03-1708/25-2	Ответ на замечания ГКУ ДНОМ от 20.08.2025
107	Кухонный инвентарь	Кухонный инвентарь	1	Ложка разливательная 0,25 л	Изделие должно соответствовать ГОСТ 51687-2000 "Приборы столовые и	шт.	5	Окончательное кол-во и тип определяются	141	б/п							
108	Кухонный инвентарь	Кухонный инвентарь	1	Ложка соусная	Изделие должно соответствовать ГОСТ 51687-2000 "Приборы столовые и	шт.	5	Окончательное кол-во и тип определяются	141	б/п							
109	Кухонный инвентарь	Кухонный инвентарь	1	Лопатка кулинарная	Изделие должно соответствовать ГОСТ 51687-2000 "Приборы столовые и	шт.	5	Окончательное кол-во и тип определяются	141	б/п							
110	Кухонный инвентарь	Кухонный инвентарь	1	Миска металлическая	Изделие должно соответствовать ГОСТ 27002-86 "Посуда из коррозионно-	шт.	30		141	б/п							
111	Кухонный инвентарь	Кухонный инвентарь	1	Набор дуршлагов	Изделие должно соответствовать ГОСТ 27002-86 "Посуда из коррозионно-	набор	2		141	б/п							
112	Кухонный инвентарь	Кухонный инвентарь	1	Нож консервный настольный	Тип: механический. Материал: металл, пластик. Максимальная высота вскрытия не менее 300	шт.	2		141	б/п							
113	Кухонный инвентарь	Кухонный инвентарь	1	Нож универсальный большой	Изделие должно соответствовать ГОСТ 51687-2000 "Приборы столовые и	шт.	12		141	б/п							
114	Кухонный инвентарь	Кухонный инвентарь	1	Нож универсальный малый	Изделие должно соответствовать ГОСТ 51687-2000 "Приборы столовые и	шт.	12		141	б/п							
115	Кухонный инвентарь	Кухонный инвентарь	1	Нож универсальный средний	Изделия должны соответствовать ГОСТ 51687-2000 "Приборы столовые и	шт.	12		141	б/п							
116	Кухонный инвентарь	Кухонный инвентарь	1	Поднос пластмассовый (для школьной столовой)	Изделие должно соответствовать ГОСТ Р 50962-96 "Посуда и изделия	шт.	221		141	б/п		175				Принять 175 шт. по кол-ву посадочных мест.	Откорректировано
117	Кухонный инвентарь	Кухонный инвентарь	1	Сито	Материал: нержавеющая сталь. Диаметр не менее 180 и не более 200 мм. с размерами	шт.	2		141	б/п							
118	Кухонный инвентарь	Кухонный инвентарь	1	Скалка тип 2	Материал: дерево. Размер: длина 500 мм, диаметр не менее 40 мм.	шт.	2		141	б/п							
119	Кухонный инвентарь	Кухонный инвентарь	1	Сковорода с крышкой	Изделие должно соответствовать ГОСТ Р 52116-2022 "Посуда чугунная черная.	шт.	5		141	б/п							
120	Кухонный инвентарь	Кухонный инвентарь	1	Сушарница	Изделие должно соответствовать ГОСТ Р 50962-96 "Посуда и изделия	шт.	47	Габаритные размеры и кол-во определяются	141	б/п		44					
121	Кухонный инвентарь	Кухонный инвентарь	1	Терка овощная универсальная	Материал: нержавеющая сталь. Ручка из пластика. Имеет от 4 до 6 граней для разных	шт.	2		141	б/п							
122	Кухонный инвентарь	Кухонный инвентарь	1	Чайник	Изделие должно соответствовать ГОСТ Р 54156-2010 "Посуда и приборы	шт.	9		141	б/п		7					
123	Кухонный инвентарь	Кухонный инвентарь	1	Шумовка	Изделие должно соответствовать ГОСТ 51687-2000 "Приборы столовые и	шт.	5		141	б/п							

Приложение 3											
При проведении проектных работ по формированию раздела 5 «Сведения об инженерном оборудовании, о сетях инженерно-технического обеспечения, перечень инженерно-технических мероприятий, содержание технологических решений» (далее-Раздел) необходимо предусмотреть размещение и подключение указанного оборудования к инженерным сетям. Оборудование данного раздела закупается, оснащается и монтируется силами Департамента капитального ремонта города Москвы в рамках строительно-монтажных работ капитального ремонта.											
Наименование помещения	Кол-во ном.	Наименование	Технические характеристики	Ед. изм.	Кол-во	Раздел	№ пом. в ГЧ	№ поз. в ГЧ	Марка оборудования	Кол-во, отличное от Перечня	Комментарии проектировщика
Помещение подготовки блоч к реализации с участком мойки кухонной посуды (зона подготовки горячих блюд)	1	Водонагреватель	Тип работы: проточный/накопительный. Тип монтажа: настенный. Способ подачи воды: напорный. Напряжение: 31ф/3ф; 220В/380В. Мощность: в соответствии с	шт.	1	Торгово-технологическое оборудование	141	П15			
Помещение подготовки блоч к реализации с участком мойки кухонной посуды (зона подготовки холодных блюд)	1	Водонагреватель	Тип работы: проточный/накопительный. Тип монтажа: настенный. Способ подачи воды: напорный. Напряжение: 31ф/3ф; 220В/380В. Мощность: в соответствии с	шт.	1	Торгово-технологическое оборудование	141	П15			
Помещение подготовки блоч к реализации с участком мойки кухонной посуды (участок мойки кухонной посуды)	1	Водонагреватель	Тип работы: проточный. Тип монтажа: настенный. Способ подачи воды: напорный. Напряжение: 3ф; 380В. Мощность не менее: 12 кВт.	шт.	1	Торгово-технологическое оборудование	141	П42			
Кладовая и моечная оборотной тары	1	Водонагреватель	Тип работы: проточный/накопительный. Тип монтажа: настенный. Способ подачи воды: напорный. Напряжение: 31ф/3ф; 220В/380В. Мощность: в соответствии с	шт.	1	Торгово-технологическое оборудование	003	П15			
Моечная для столовой посуды	1	Водонагреватель проточный	Тип работы: проточный. Тип монтажа: настенный. Способ подачи воды: напорный. Напряжение: 3ф; 380В. Мощность не менее: 12 кВт.	шт.	1	Торгово-технологическое оборудование	137	П42			
Помещение для временного хранения пищевых отходов	1	Водонагреватель	Тип работы: проточный/накопительный. Тип монтажа: настенный. Способ подачи воды: напорный. Напряжение: 31ф/3ф; 220В/380В. Мощность: в соответствии с	шт.	1	Торгово-технологическое оборудование	006	П15			