Департамент капитального ремонта города Москвы Государственное автономное учреждение города Москвы Московский научно-исследовательский и проектный институт жилищного хозяйства «МосжилНИИпроект» (ГАУ «МосжилНИИпроект»)

mgnp@mgnp.mos.ru +7 495 624 40 65 107078, г. Москва,ул.Каланчевская, д. 4/2, стр. 1

Арх. №

Капитальный ремонт здания Государственного бюджетного общеобразовательного учреждения города Москвы "Школа № 236", расположенного по адресу: г. Москва, ул. Клязьминская, д. 7, корп. 4

ПРОЕКТНАЯ ДОКУМЕНТАЦИЯ

Раздел 5. Сведения об инженерном оборудовании, о сетях инженерно-технологического обеспечения, перечень инженерно-технических мероприятий, содержание технологических решений.
Подраздел 5. Сети связи
Часть 6. Электрочасофикация.
2024-00272-01-0-ИОС5.6
Том 5.5.6
I Этап

2025

Департамент капитального ремонта города Москвы Государственное автономное учреждение города Москвы Московский научно-исследовательский и проектный институт жилищного хозяйства «МосжилНИИпроект» (ГАУ «МосжилНИИпроект»)

mgnp@mgnp.mos.ru +7 495 624 40 65 107078, г. Москва,ул.Каланчевская, д. 4/2, стр. 1

Капитальный ремонт здания Государственного бюджетного общеобразовательного учреждения города Москвы "Школа № 236", расположенного по адресу: г. Москва, ул. Клязьминская, д. 7, корп. 4

ПРОЕКТНАЯ ДОКУМЕНТАЦИЯ

Раздел 5. Сведения об инженерном оборудовании, о сетях инженерно-технологического обеспечения, перечень инженерно-технических мероприятий, содержание технологических решений.
Подраздел 5. Сети связи
Часть 6. Электрочасофикация.
2024-00272-01-0-ИОС5.6
Том 5.5.6
I Этап

Начальник отдела проектирования Инженерных систем №1 — Д.П.Белоусова

06.05.25

2025

СОДЕРЖАНИЕ РАЗДЕЛА

№п/п	Наименование	стр.
1	Содержание раздела	2
2	Состав проектной документации	3
3	Пояснительная записка	4
4	Принципиальная схема системы ЭЧ	5
5	План 1-го этажа. М1:100. Расположение оконечного оборудования системы ЭЧ.	6
6	Спецификация оборудования, изделий и материалов	7

Взам. инв. N

Подпись и дата

Инв. N док.

Изм.	Кол.уч.	Лист	Nдок.	Подпись	Дата
Разработал		Целин С.Р.			05.2025
Зав.сектор.		Роянцева А.А.			05.2025
Н.Контроль		Роянцева А.А.			05.2025
Нач. ОПИС №1		Белоусова Д.П.			05.2025

2024-00272-01-0-ИОС5.6

Содержание раздела

Стадия	Лист	Листов
П	1	1

МОСЖИЛ НИИПРОЕКТ

Состав проектной документации

Смотри том 1, 2024-00272-01-0-СП , Часть 1. Раздел 1. Состав проектной документации.

Согласовано

Взам. Инв. №

Подп. И дата

Инв. № подл.

Изм.	Кол.уч	Лист	№док.	Подп.	Дата	2024-00272-01-0-ИОС5.6		
Разработал		Целин С.Р.			05.2025	Капитальный ремонт	Стадия	Лист	Листов
Зав.сектор.		Роянцева А.А.			05.2025		П	1	1
Н.контр.		Роянцева А.А.			05.2025		МОСЖИЛ НИИПРОЕКТ		
Нач. ОПИС №1		Белоусова Д.П.			05.2025				

Пояснительная записка.

Капитальный ремонт здания Государственного бюджетного общеобразовательного учреждения города Москвы "Школа № 236", расположенного по адресу: г. Москва, ул. Клязьминская, д. 7, корп. 4

Система Электрочасофикации (ЭЧ).

Данным проектом выполняются расстановка оконечного оборудования системы ЭЧ. Проект разработан на основании архитектурных чертежей стадии проектной документации.

Раздел соответствует требованиям действующих нормативных документов:

- СП 2.13130.2009 «Системы противопожарной защиты. Обеспечение огнестойкости объектов защиты»;
- СП 3.13130.2009 «Системы оповещения и управления эвакуацией людей при пожаре»;
- СП 6.13130.2013 «Системы противопожарной защиты. Электрооборудование. Требования пожарной безопасности»;
- СП 12.13130.2009 «Определение категорий помещений, зданий и наружных установок по взрывопожарной и пожарной опасности»;
- СП 134.13330.2022 «Системы электросвязи зданий и сооружений. Основные положения проектирования»;
- ГОСТ 31565-2012 Межгосударственный стандарт «Кабельные изделия. Требования пожарной безопасности»;
- ПУЭ «Правила устройства электроустановок».

Система Электрочасофикации.

Для отображения текущего времени в здании поликлинике предусматривается организация системы электрочасофикации.

Систему электрочасофикации строится на базе оборудования производства НИИЧАСПРОМ.

Часовая станция позволяет подключить 4 двухпроводных линий связи с нагрузкой 1А.

Проектом предусматривается установка оборудования электрочасофикации в следующих помещениях:

- Часовая станция ПИК-2М-4002 установить в комнате охраны (104);
- Подключение часовой станции к сети радиовещания, для синхронизации времени (см. проект РФ);
- Вторичные часы установить в вестибюле, обеденном зале.

ниже 2-х метров от уровня чистого пола (точное место установки уточнить по месту).

Для обеспечения возможности расширения системы, предусмотрен резерв двух выделенных линий связи на часовой станции ПИК.

Монтаж системы электрочасофикации выполнить кабелем КПСВВнг(А)-LSLTx 1х2х1.0. Соединения и ответвления кабелей производиться в распаячных коробках способом пайки.

Электропитание и заземление

По степени надежности электроснабжения сети связи относятся ко 2-ой категории потребителей. Для оборудования предусмотрены источники бесперебойного питания.

Защита электрических цепей должна быть выполнена в соответствии с ПУЭ.

Защитное заземление электрооборудования, металлических каркасов и конструкций следует выполнить в соответствии с ПУЭ и технической документацией на оборудование.

Взам. инв. N

Подпись и дата

Инв. N док.


Изм.	Кол.уч.	Лист	Nдок.	Подпись	Дата
Разработал		Целин С.Р.			05.2025
Зав.сектор.		Роянцева А.А.			05.2025
Н.Контроль		Роянцева А.А.			05.2025
Нач. ОПИС №1		Белоусова Д.П.			05.2025

2024-00272-01-0-ИОС5.6

Пояснительная записка.

Стадия	Лист	Листов
П	2	3

МОСЖИЛ НИИПРОЕКТ

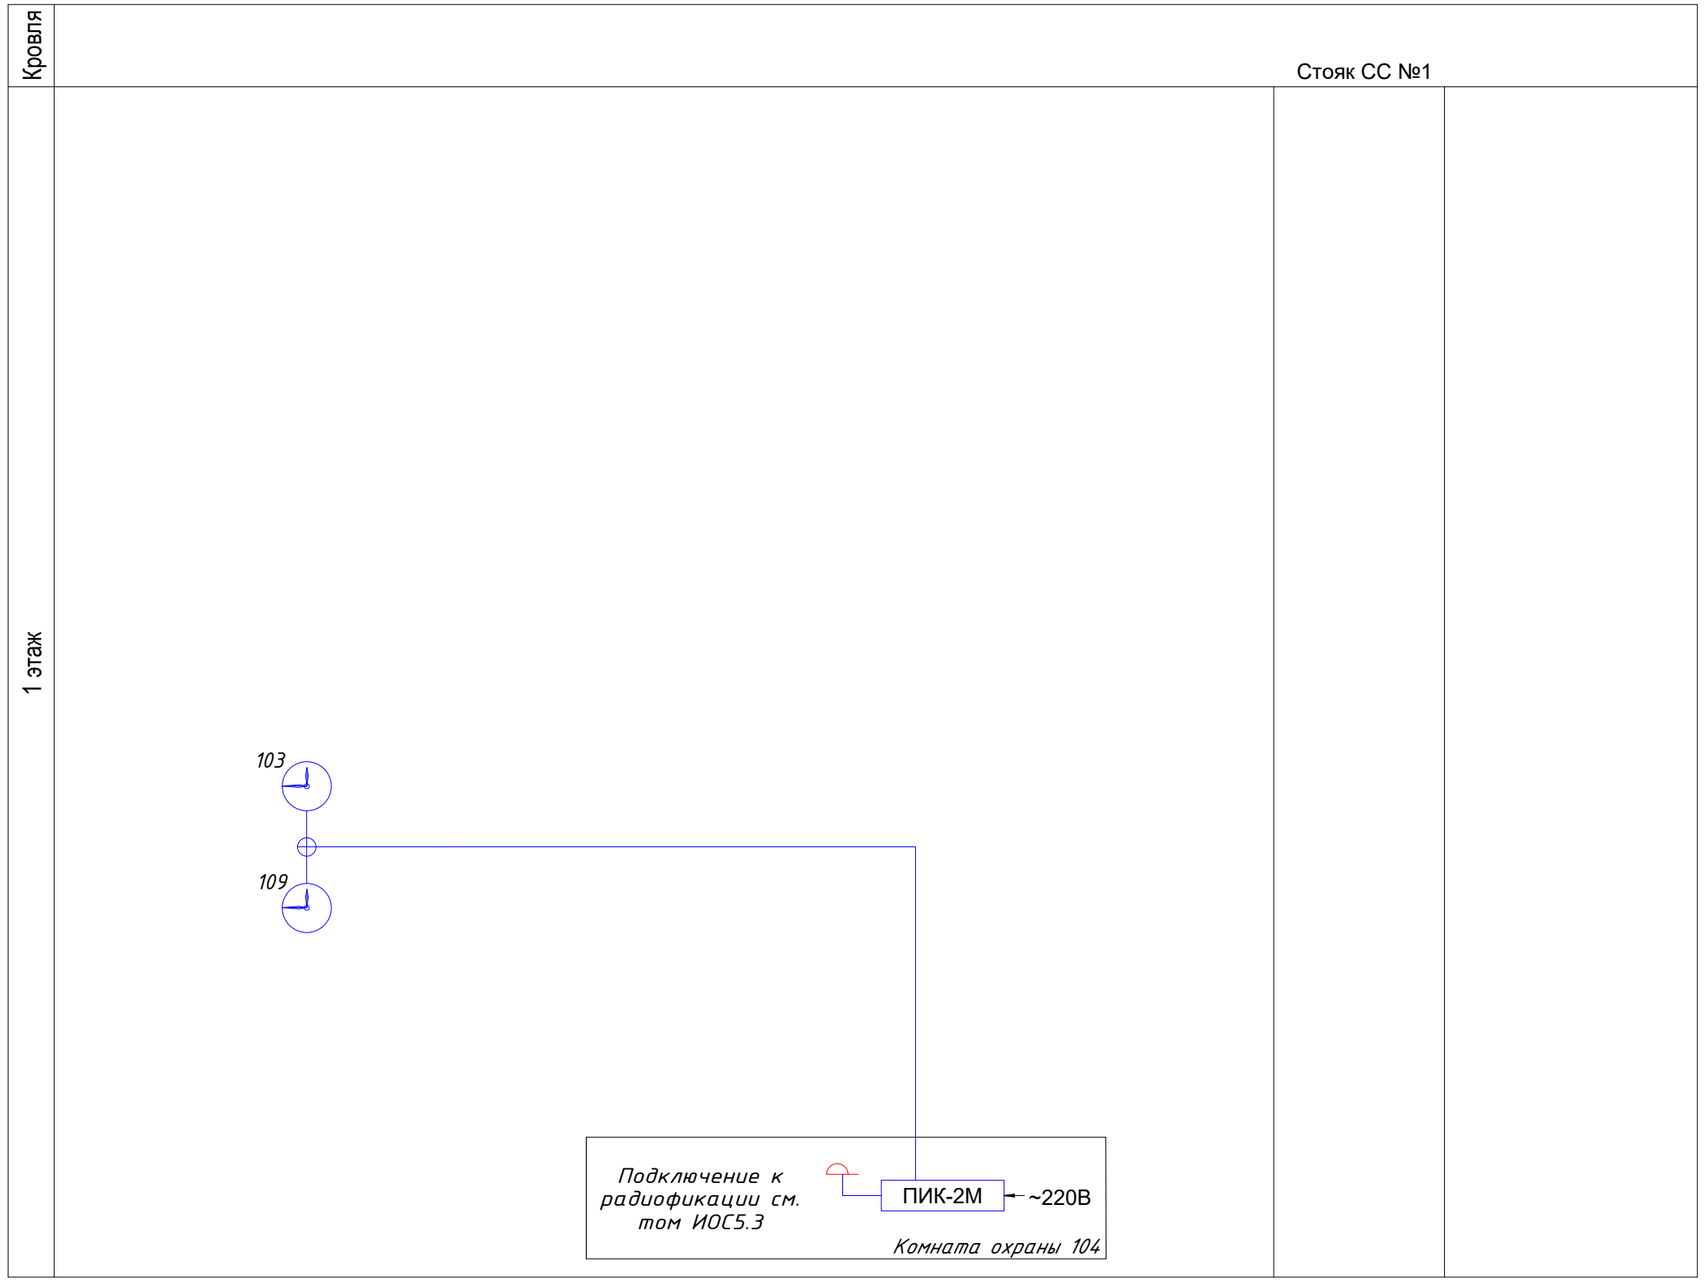

Условные обозначения:

ПИК-2М – Станция часовая ПИК (первичные часы)

– Коробка распаечная

115 – Вторичные часы ВЧС, с указанием номера помещения (115)

– Кабель КПСВВнг(А)-LSLTx 1х2х1,0

						2024-00272-01-0-ИОС5.6
						Капитальный ремонт ГБОУ «Школа №1236 имени Героя Советского Союза Г.И.Щедрина» по адресу: г. Москва, ул. Клязьминская. д.7, корп.4
Изм.	Кол.уч.	Лист	№ док.	Подпись	Дата	
Разработал		Целин С.Р.			05.2025	Капитальный ремонт
Зав. сектор		Роянцева А.А.			05.2025	
Н. Контроль		Роянцева А.А.			05.2025	Принципиальная схема системы ЭЧ
Нач.ОПИС№1		Белоусова Д.П.			05.2025	

Стадия	Лист	Листов
П	1	2

МОСЖИЛ НИИПРОЕКТ


Формат А3

Согласовано:

Инв. N подл. | Подпись и дата | Взам. инв. N

Здание Государственного бюджетного общеобразовательного
учреждения города Москвы "Школа № 236 имени Героя Советского Союза
Г.И.Щедрина", расположенное по адресу: г. Москва, ул.Клязьминская, д. 7,корп.4"

План 1-го этажа
М 1:100

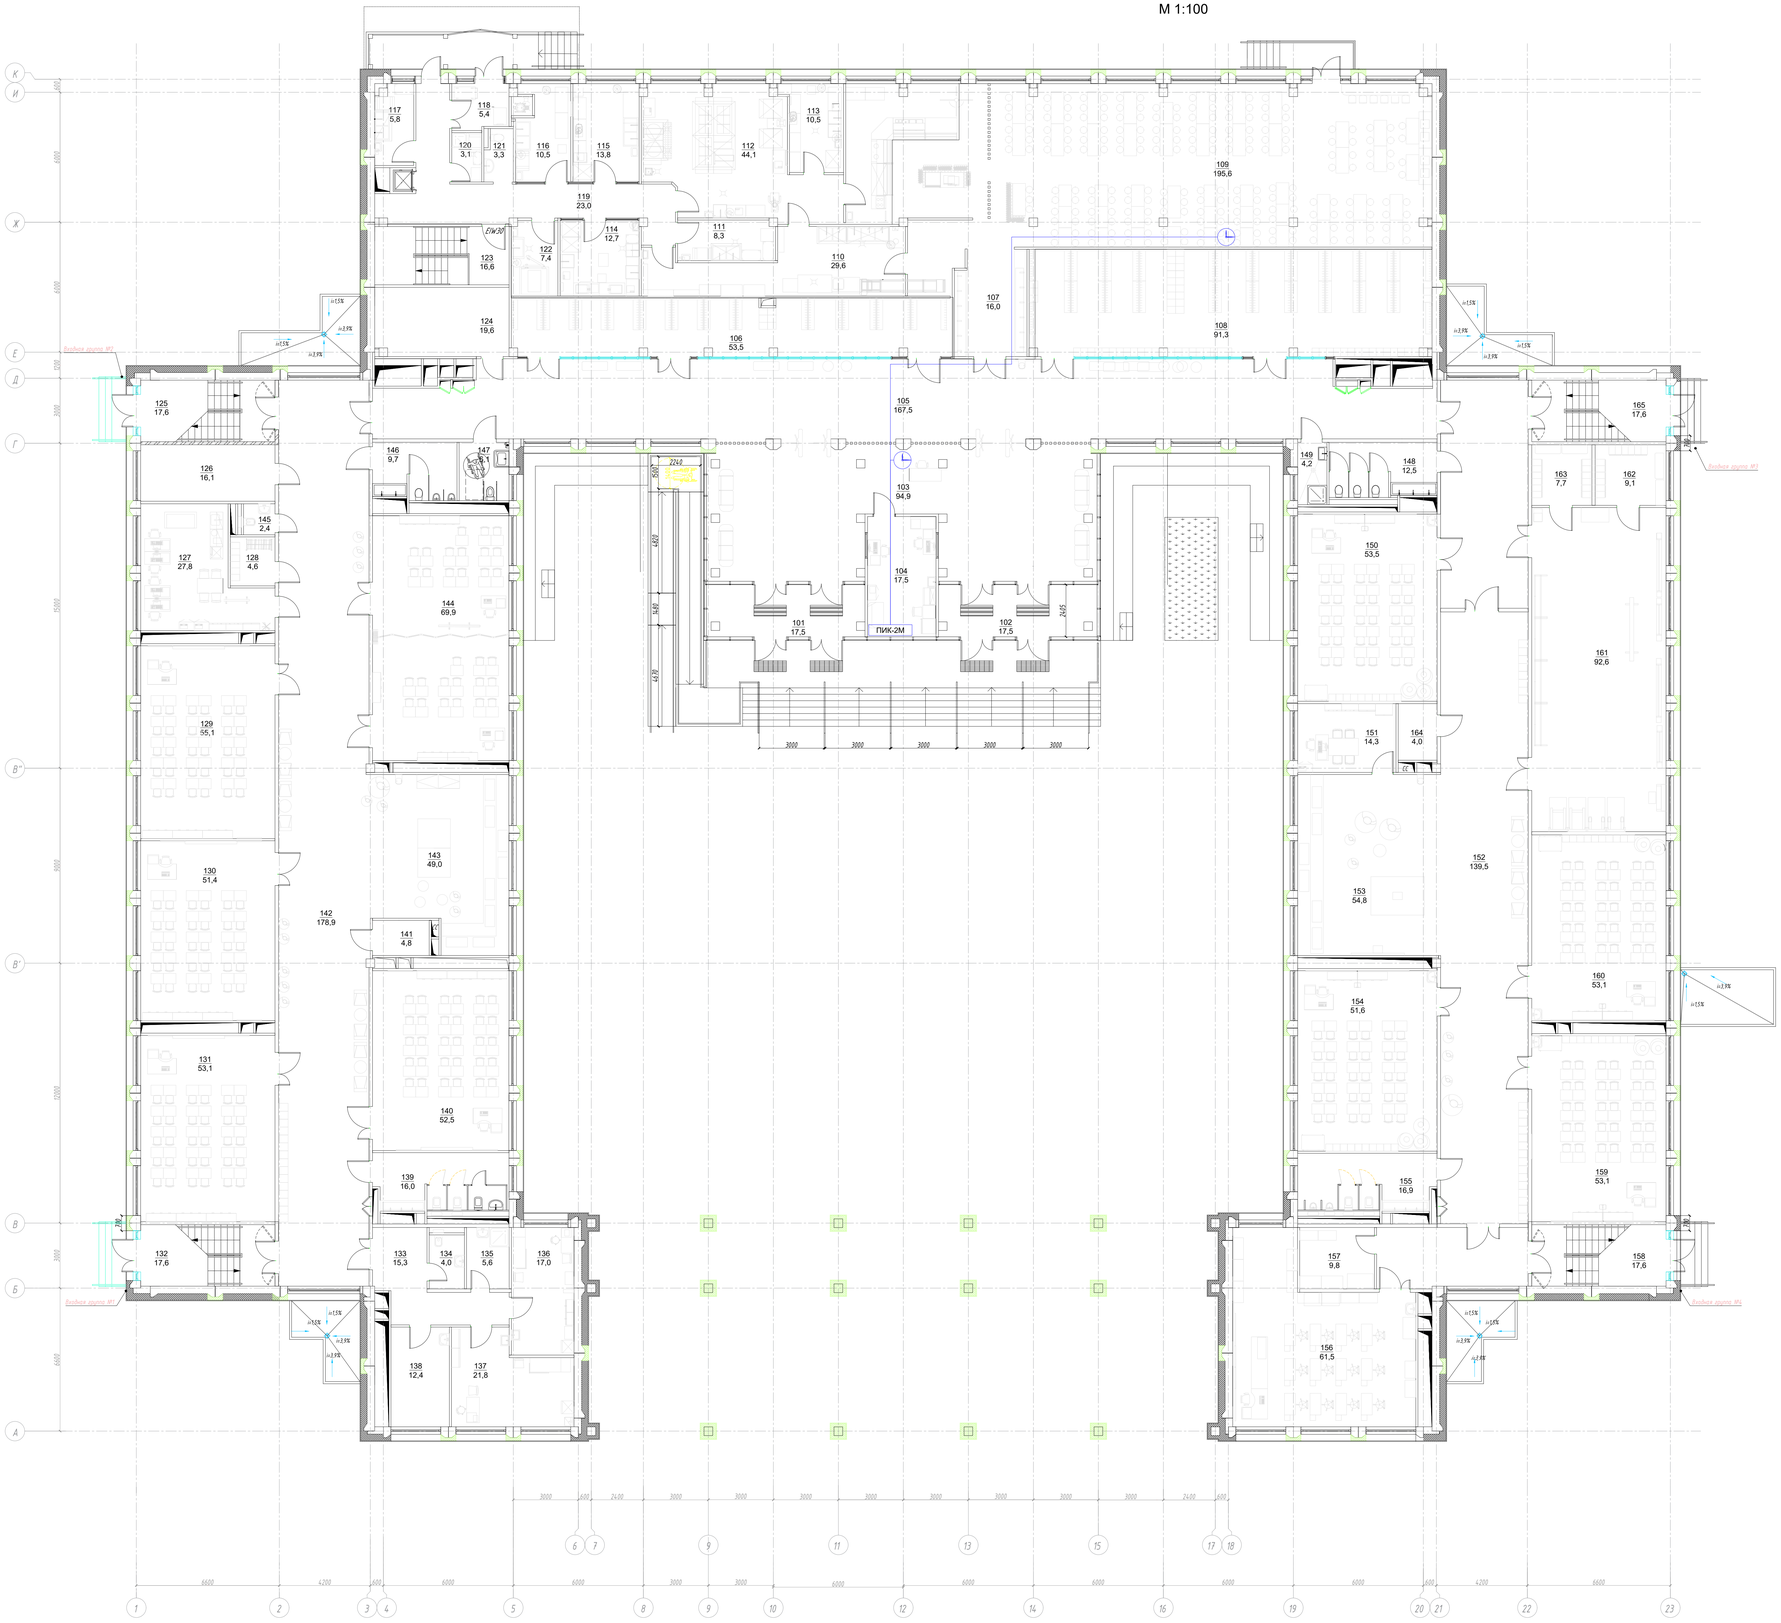

Экспликация помещений 1-го этажа

N п/п	Наименование помещений	Пл-дь м²	Кат. пом.
101	Тамбур	17,5	
102	Тамбур	17,5	
103	Зона ожидания для посетителей	94,9	
104	Комната охраны с диспетчерским пунктом	17,5	
105	Коридор с зоной ожидания	167,5	
106	Гардеробная для обучающихся (начальная школа)	53,5	
107	Умывальная	16,0	
108	Гардеробная для обучающихся (основная школа)	91,3	
109	Обеденный зал	195,6	*
110	Моечная для столовой посуды	29,6	*
111	Моечная для кухонной посуды	8,3	*
112	Горячий цех	44,1	*
113	Холодный цех	10,5	*
114	Мясо-рыбный цех	12,7	*
115	Цех вторичной обработки овощей	13,8	*
116	Цех первичной обработки овощей	10,5	*
117	Кладовая и моечная оборотной тары	5,8	*
118	Загрузочный цех	5,4	*
119	Коридор	23,0	*
120	ПЗМ	3,1	*
121	Санузел персонала	3,3	*
122	Помещение для временного хранения пищевых отходов	7,4	В4
123	Технологическая лестница типа Н2	16,6	
124	Серверная	19,6	В3
125	Лестничная клетка "А" типа Н2	17,6	
126	Электрощитовая	16,1	В3
127	Кабинет с рабочим пространством для учителей 1-го типа	27,8	
128	Гардеробная комната (для учителей)	4,6	
129	Кабинет математики	55,1	
130	Кабинет математики	51,4	
131	Кабинет математики	53,1	
132	Лестничная клетка "Б" типа Л1	17,6	
133	Коридор теплоузла	15,3	
134	Туалет теплоузла	4,0	
135	Помещение приготовления дезинфицирующих растворов и хранения уборочного инвентаря, предназначенных для помещений медицинского назначения	5,6	В4
136	Процедурный кабинет	17,0	
137	Кабинет врача	21,8	
138	Прививочный кабинет	12,4	
139	Санузел для девочек с комнатой личной гигиены (основная школа)	16,0	
140	Кабинет русского языка и литературы	52,5	
141	Кроссовая	4,8	В4
142	Коридор с рекреацией	178,9	
143	Коридор с рекреацией	4,9	
144	Кабинет иностранного языка с возможностью деления трансформируемой перегородкой на два помещения (основная и старшая школа)	69,9	
145	Санузел для персонала	2,4	
146	Санузел для мальчиков начальной школы	9,7	
147	Санузел для МГН	6,3	
148	Санузел для девочек (начальная школа)	12,5	
149	ПЗМ	4,2	В4
150	Учебный кабинет (1 класс)	53,5	
151	Административный кабинет 1-го типа	14,3	
152	Коридор с рекреацией	139,5	
153	Коридор с рекреацией	54,8	
154	Учебный кабинет (1 класс)	51,6	
155	Санузел для мальчиков (начальная школа)	16,9	
156	Кабинет материальной технологии 2-го типа	61,5	
157	Лаборантская при кабинете технологии	9,8	В3
158	Лестничная клетка "В" типа Л1	17,6	
159	Учебный кабинет (1 класс)	53,1	
160	Учебный кабинет (2 класс)	53,1	
161	Гимнастического зала (хореография)	92,6	
162	Раздевальная	9,1	
163	Раздевальная	7,7	
164	Кроссовая	4,0	В4
165	Лестничная клетка "Г" типа Н2	17,6	
	ИТОГО:	2260,7	

Условные обозначения:

ПИК-2М – Станция часовая ПИК (первичные часы)

115 – Вторичные часы ВЧС, с указанием номера помещения (115)

– Кабель КПКВВнг(А)-LSLTx 1х2х1,0

Согласовано

Взамен инв. №

Подпись и дата

Инв. № подл.

					2024-00272-01-0-ИОС5.6
Изм.	Кол.уч.	Лист	№ док.	Подпись	Дата
Разработал	Цвелик С.Р.				05.2025
Зав. сектор	Ровнейка А.А.				05.2025
Н. Контроль	Ровнейка А.А.				05.2025
Нач. ОПИС №1	Белоусова Д.П.				05.2025

Капитальный ремонт ГБОУ «Школа №1236 имени Героя Советского Союза Г.И.Щедрина» по адресу: г. Москва, ул. Клязьминская, д.7, корп.4

Капитальный ремонт

План 1-го этажа
М 1:100

Стадия	Лист	Листов
П	2	2

МОСЖИЛ НИИПРОЕКТ

Копировал

Формат А0

Позиция	Наименование и техническая характеристика	Тип, марка, обозначение документа, опросного листа	Код оборудования, изделия, материала	Завод-изготовитель	Единица измерения	Количество	Масса, единицы, кг	Примечание
1	2	3	4	5	6	7	8	9
	Оборудование:							
1	Часовая станция "Первичные часы"	ПИК-2М-4002		АО "НИИЧаспром"	компл.	1		
2	Часы вторичные стрелочные	ВЧС-03		АО "НИИЧаспром"	шт.	2		
	Кабельные изделия:							
1	Кабель электрочасофикации	КПСВВнг(А)-LSLTx 1х2х1.0		ООО "НПП Спецкабель"	м.	100		
	Материалы:							
1	Коробка распаечная				шт.	1		
2	Труба гофрированная из самозатухающего ПВХ-пластиката, Ø 20 мм	91920		ДКС	м.	50		

Инв. N док. | Подпись и дата | Взам. инв. N

Изм.	Кол.уч.	Лист	Nдок.	Подпись	Дата
Разработал		Целин С.Р.			05.2025
Зав.сектор.		Роянцева А.А.			05.2025
Н.Контроль		Роянцева А.А.			05.2025
Нач. ОПИС №1		Белоусова Д.П.			05.2025

2024-00272-01-0-ИОС5.6.СО

Спецификация оборудования, изделий и материалов

Стадия	Лист	Листов
П	1	1

МОСЖИЛ НИИПРОЕКТ