Департамент капитального ремонта города Москвы Государственное автономное учреждение города Москвы Московский научно-исследовательский и проектный институт жилищного хозяйства «МосжилНИИпроект» (ГАУ «МосжилНИИпроект»)

mgnp@mgnp.mos.ru +7 495 624 40 65 107078, г. Москва,ул.Каланчевская, д. 4/2, стр. 1

Арх. №

Капитальный ремонт здания Государственного бюджетного общеобразовательного учреждения города Москвы "Школа № 236", расположенного по адресу: г. Москва, ул. Клязьминская, д. 7, корп. 4

ПРОЕКТНАЯ ДОКУМЕНТАЦИЯ

Сведения об инженерном оборудовании, о сетях инженерно-технического обеспечения, перечень инженерно-технических мероприятий, содержание технологических решений. Подраздел 5. Сети связи

Часть 8. Система контроля и управления доступом

2024-00272-00-ИОС5.8

Том 5.5.8

I этап

2025

Департамент капитального ремонта города Москвы Государственное автономное учреждение города Москвы Московский научно-исследовательский и проектный институт жилищного хозяйства «МосжилНИИпроект» (ГАУ «МосжилНИИпроект»)

mgnp@mgnp.mos.ru +7 495 624 40 65 107078, г. Москва, ул. Каланчевская, д. 4/2, стр. 1

Арх. №

Капитальный ремонт здания Государственного бюджетного общеобразовательного учреждения города Москвы "Школа № 236", расположенного по адресу: г. Москва, ул. Клязьминская, д. 7, корп. 4

ПРОЕКТНАЯ ДОКУМЕНТАЦИЯ

Сведения об инженерном оборудовании, о сетях инженерно-технического обеспечения, перечень инженерно-технических мероприятий, содержание технологических решений. Подраздел 5. Сети связи

Часть 8. Система контроля и управления доступом

2024-00272-00-ИОС5.8

Том 5.5.8

I этап

Начальник ОПИС №1 Д.П. Белоусова

29.04.2025

2025

Содержание раздела

№п/п	Наименование проектных материалов	Марка листа	Стр.
1	Содержание раздела		2
2	Состав проектной документации		3
3	Текстовая часть		4-6
4	Принципиальная схема СКУД	ИОС5.8-1	7
5	Принципиальная схема видеодомофона	ИОС5.8-2	8
6	План подвала. СКУД.	ИОС5.8-3	9
7	План 1-го этажа. СКУД	ИОС5.8-4	10
8	План 2-го этажа. СКУД	ИОС5.8-5	11
9	План 3-го этажа. СКУД	ИОС5.8-6	12
10	Спецификация оборудования и материалов	ИОС5.8-СО	13-15

Согласовано

Взам. Инв. №

Подп. И дата

Инв. № подл.

Изм.	Кол.уч	Лист	№док.	Подп.	Дата	2024-00272-01-0-ИОС5.8		
Разработал		Роянцева А.А				Капитальный ремонт ГБОУ г. Москвы. Школа №1236 имени Героя Советского Союза Г.И. Щедрина, по адресу г. Москва, ул. Клязьминская , д.7, корп.4	Стадия	Лист	Листов
Зав.сектора		Роянцева А.А					П	1	1
							МОСЖИЛ НИИПРОЕКТ		
Норм.контр		Роянцева А.А							
Нач.ОПИС№1		Белоусова Д.П.							

Формат А4

СОСТАВ ПРОЕКТНОЙ ДОКУМЕНТАЦИИ

Смотри том 1, 2024-00272-00-СП , Часть 1. Раздел 1. Состав проектной документации.

Взам. инв. N

Подпись и дата

Инв. N док.

Изм.	Кол.уч.	Лист	Nдок.	Подпись	Дата
Разработал		Короткова К.Н			12.2024
Зав.сектор.		Роянцева А.А.			12.2024
Н.Контроль		Белоусова Д.П.			12.2024
Нач. ОПИС №1		Белоусова Д.П.			12.2024

2024-00272-00-ИОС5.12

Состав проектной документации

Стадия	Лист	Листов
П	1	1

МОСЖИЛ НИИПРОЕКТ

Текстовая часть.

1. *Краткая характеристика объекта*

Капитальный ремонт здания ГБОУ «Школа №1236 имени Героя Советского Союза Г.И. Щедрина», расположенное по адресу: г. Москва, ул. Клязьминская, д.7, корп.4.

Здание оборудовано центральным отоплением; холодным и горячим водоснабжением; канализацией; электроснабжением; городским телефонным вводом, который при капитальном ремонте сохраняется.

Для обеспечения устойчивого функционирования сетей связи, в том числе при чрезвычайных ситуациях, проектом выполнены мероприятия по обеспечению здания:городским радио-вводом;

- городским телефонным вводом;

- цифровым телевидением.

Для защиты информационных сетей применяются антивирусные программы.

2. Система контроля и управления доступом

Система контроля и управления доступом (СКУД) принадлежит к техническим средствам высокого уровня и предназначена для ограничения несанкционированного доступа в охраняемые помещения с помощью электронных идентификаторов.

Системой контроля и управления доступом оборудовать входы в подвал и 1-й этаж, технические помещения в подвале, кабинет для учительей, серверные, посты охраны, медицинские кабинеты, процедурные, входы в пищеблок с цехами приготовления пищи.

Система СКУД интегрирована с системой охранно-пожарной сигнализации и имеет общую базу данных на основе системы "Рубеж" и собрана на сетевые контроллеры STR20-IP которые подключаются на коммутаторы, расположенные в телекоммуникационных шкафах. К каждому сетевому контроллеру можно подключить до 8-ми модулей доступа "STR-1AP-M". Смотри схему на л.1 Гр.части. Каждый из модулей доступа устанавливаются на стене у контролируемой двери и подключаются к сетевому контроллеру кабелем КПСВВнг(А)LSLTx -2х0.75. Сетевые контролеры включается в линию интерфейса и питания RS-485 кабель U/UTPнг(А) LSLTx -4х2х0.52. Питание контроллеров осуществляется от ИВЭПР-12/3.5.

Система обеспечивает возможность управления доступом несколькими способами: децентрализованно (с помощью считывателя электронных идентификаторов и централизованно (с помощью пульта АПС). Для ручной разблокировки устанавливаются кнопки УДП 513-10 исп.01. Автоматическая разблокировка предусматривается при помощи релейных блоков системы пожарной сигнализации, которые подключаются к модулям доступа кабелем ЛОУТОКС 20нг(А)-FRLSLTx -1х2х0.5.

На контролируемых дверях устанавливаются электромагнитные замки,

Согласовано | Взам. Инв. № | Подп. И дата | Инв. № подл.

Изм.	Кол.уч	Лист	№док.	Подп.	Дата	2024-00272-01-0-ИОС5.8		
Разработал		Роянцева А.А				Капитальный ремонт ГБОУ г. Москвы. Школа №1236 имени Героя Советского Союза Г.И. Щедрина, по адресу г. Москва, ул. Клязьминская , д.7, корп.4	Стадия	Лист	Листов
Зав.сектора		Роянцева А.А					П	1	3
							МОСЖИЛ НИИПРОЕКТ		
Норм.контр		Роянцева А.А							
Нач.ОПИС№1		Белоусова Д.П.							

Формат А4

магнито-контактные извещатели типа ИО 102 -26 и дверные доводчики. Доводчики учитываются в разделе АР в комплекте с дверьми. В помещениях изнутри рядом с дверью монтируется считыватель STR-RM-A01. Со стороны входа у двери монтируется считыватель электронных идентификаторов. Карточки выдаются сотрудникам учреждения.

Система доступа объедена в локально вычислительную сеть с подключением к коммутаторам через патч-панели. Патч-панели, коммутаторы устанавливаются в телекоммуникационных шкафах, которые учтены в разделе СКС. Смотри схему на листе №1

3. Видеодомофон

У входных дверей главного и дополнительного входа, запасных входах, вход в пищеблок на стене здания устанавливаются комплект видеодомофона SM-400W на 9 вызывных панелей DS06AP. Монитор устанавливается на посту охраны, пом. №104. Видеодомофоны являются одним из вариантов решения для организации системы контроля и управления доступом, состоящей из видеомонитора с вызывной панелью.

Видеомонитор предназначен для просмотра изображения от внешней видеокамеры (вызывной панели) и звукового вызова при входе посетителя и состоит из переговорной трубки с динамиком и монитора 4.3", индикатором питания, кнопками "монитор", вызова и открытия двери.

Антивандальная вызывная панель имеет встроенные микрофон и динамическую головку, кнопку вызова и монохромную видеокамеру 1/3" (400ТВЛ, 0Лк) с ИК -подсветкой (60см).

Монитор видеодомофона устанавливается на стене на посту охраны, вызывные панели монтируются снаружи у входной двери. Также рядом с вызывной панелью монтируется считыватель ключей. Ключи выдаются сотрудникам учреждения.

Питание видеомонитора осуществляется от сети (100 -240В, 50/60Гц), питание вызывной панели - от видеомонитора (12В). Сеть выполняется кабелем марки КПСВВнг(А)-LSLTx -4х2х0, 75.


По степени надежности электроснабжения сети связи относятся к 1-ой категории потребителей. Для оборудования предусмотрены источники бесперебойного питания.

Защита электрических цепей должна быть выполнена в соответствии с ПУЭ. Защитное заземление электрооборудования, металлических каркасов и конструкций следует выполнить в соответствии с ПУЭ и технической документацией на оборудование.

5. Перечень нормативных документов

- ***ГОСТ Р 21.101-2020*** *«Система проектной документации для строительства (СПДС). Основные требования к проектной и рабочей документации». Постановление №87 от 16.02.2008 «О составе разделов проектной документации и требования к их содержанию» (с изменениями на 23 января 2016г.)*
- ***СП 118.13330.2022*** *«Общественные здания и сооружения».*
- ***ГОСТ 21.406-88*** *«Проводные средства связи. Обозначения условные графические на схемах и планах»*
- ***Пособие 431 от 12.04.2010*** *«Инструкция по проектированию систем связи информатизации и диспетчеризации объектов жилищного строительства»*
- ***ГОСТ 53246-2008*** *«Информационные технологии. Системы кабельные структурированные. Проектирование основных узлов системы. Общие требования».*
- ***ГОСТ 29099-91*** *«Сети вычислительные локальные. Термины и определения».*
- ***ГОСТ Р 21.703-2000*** *«Правила выполнения рабочей документации проводных систем связи».*
- ***СП 76.13130-2016*** *«Электротехнические устройства».*
- ***ПУЭ*** *«Правила устройства электроустановок».*
- ***ГОСТ 28601.2-90*** *«Система несущих конструкций серии 482,6мм. Шкафы и стоечные конструкции. Основные рекомендации».*
- ***СП 158.13330-2014*** *«Здания и помещения медицинских организаций. Правила проектирования»*
- ***СП 134.13330.2022*** *«Система электросвязи зданий и сооружений. Основные положения проектирования».*
- ***МИ-ИТ-001*** *«Методическая инструкция. Требования проектирования ЛВС. Москва 2019»*

Принципиальная схема СКУД

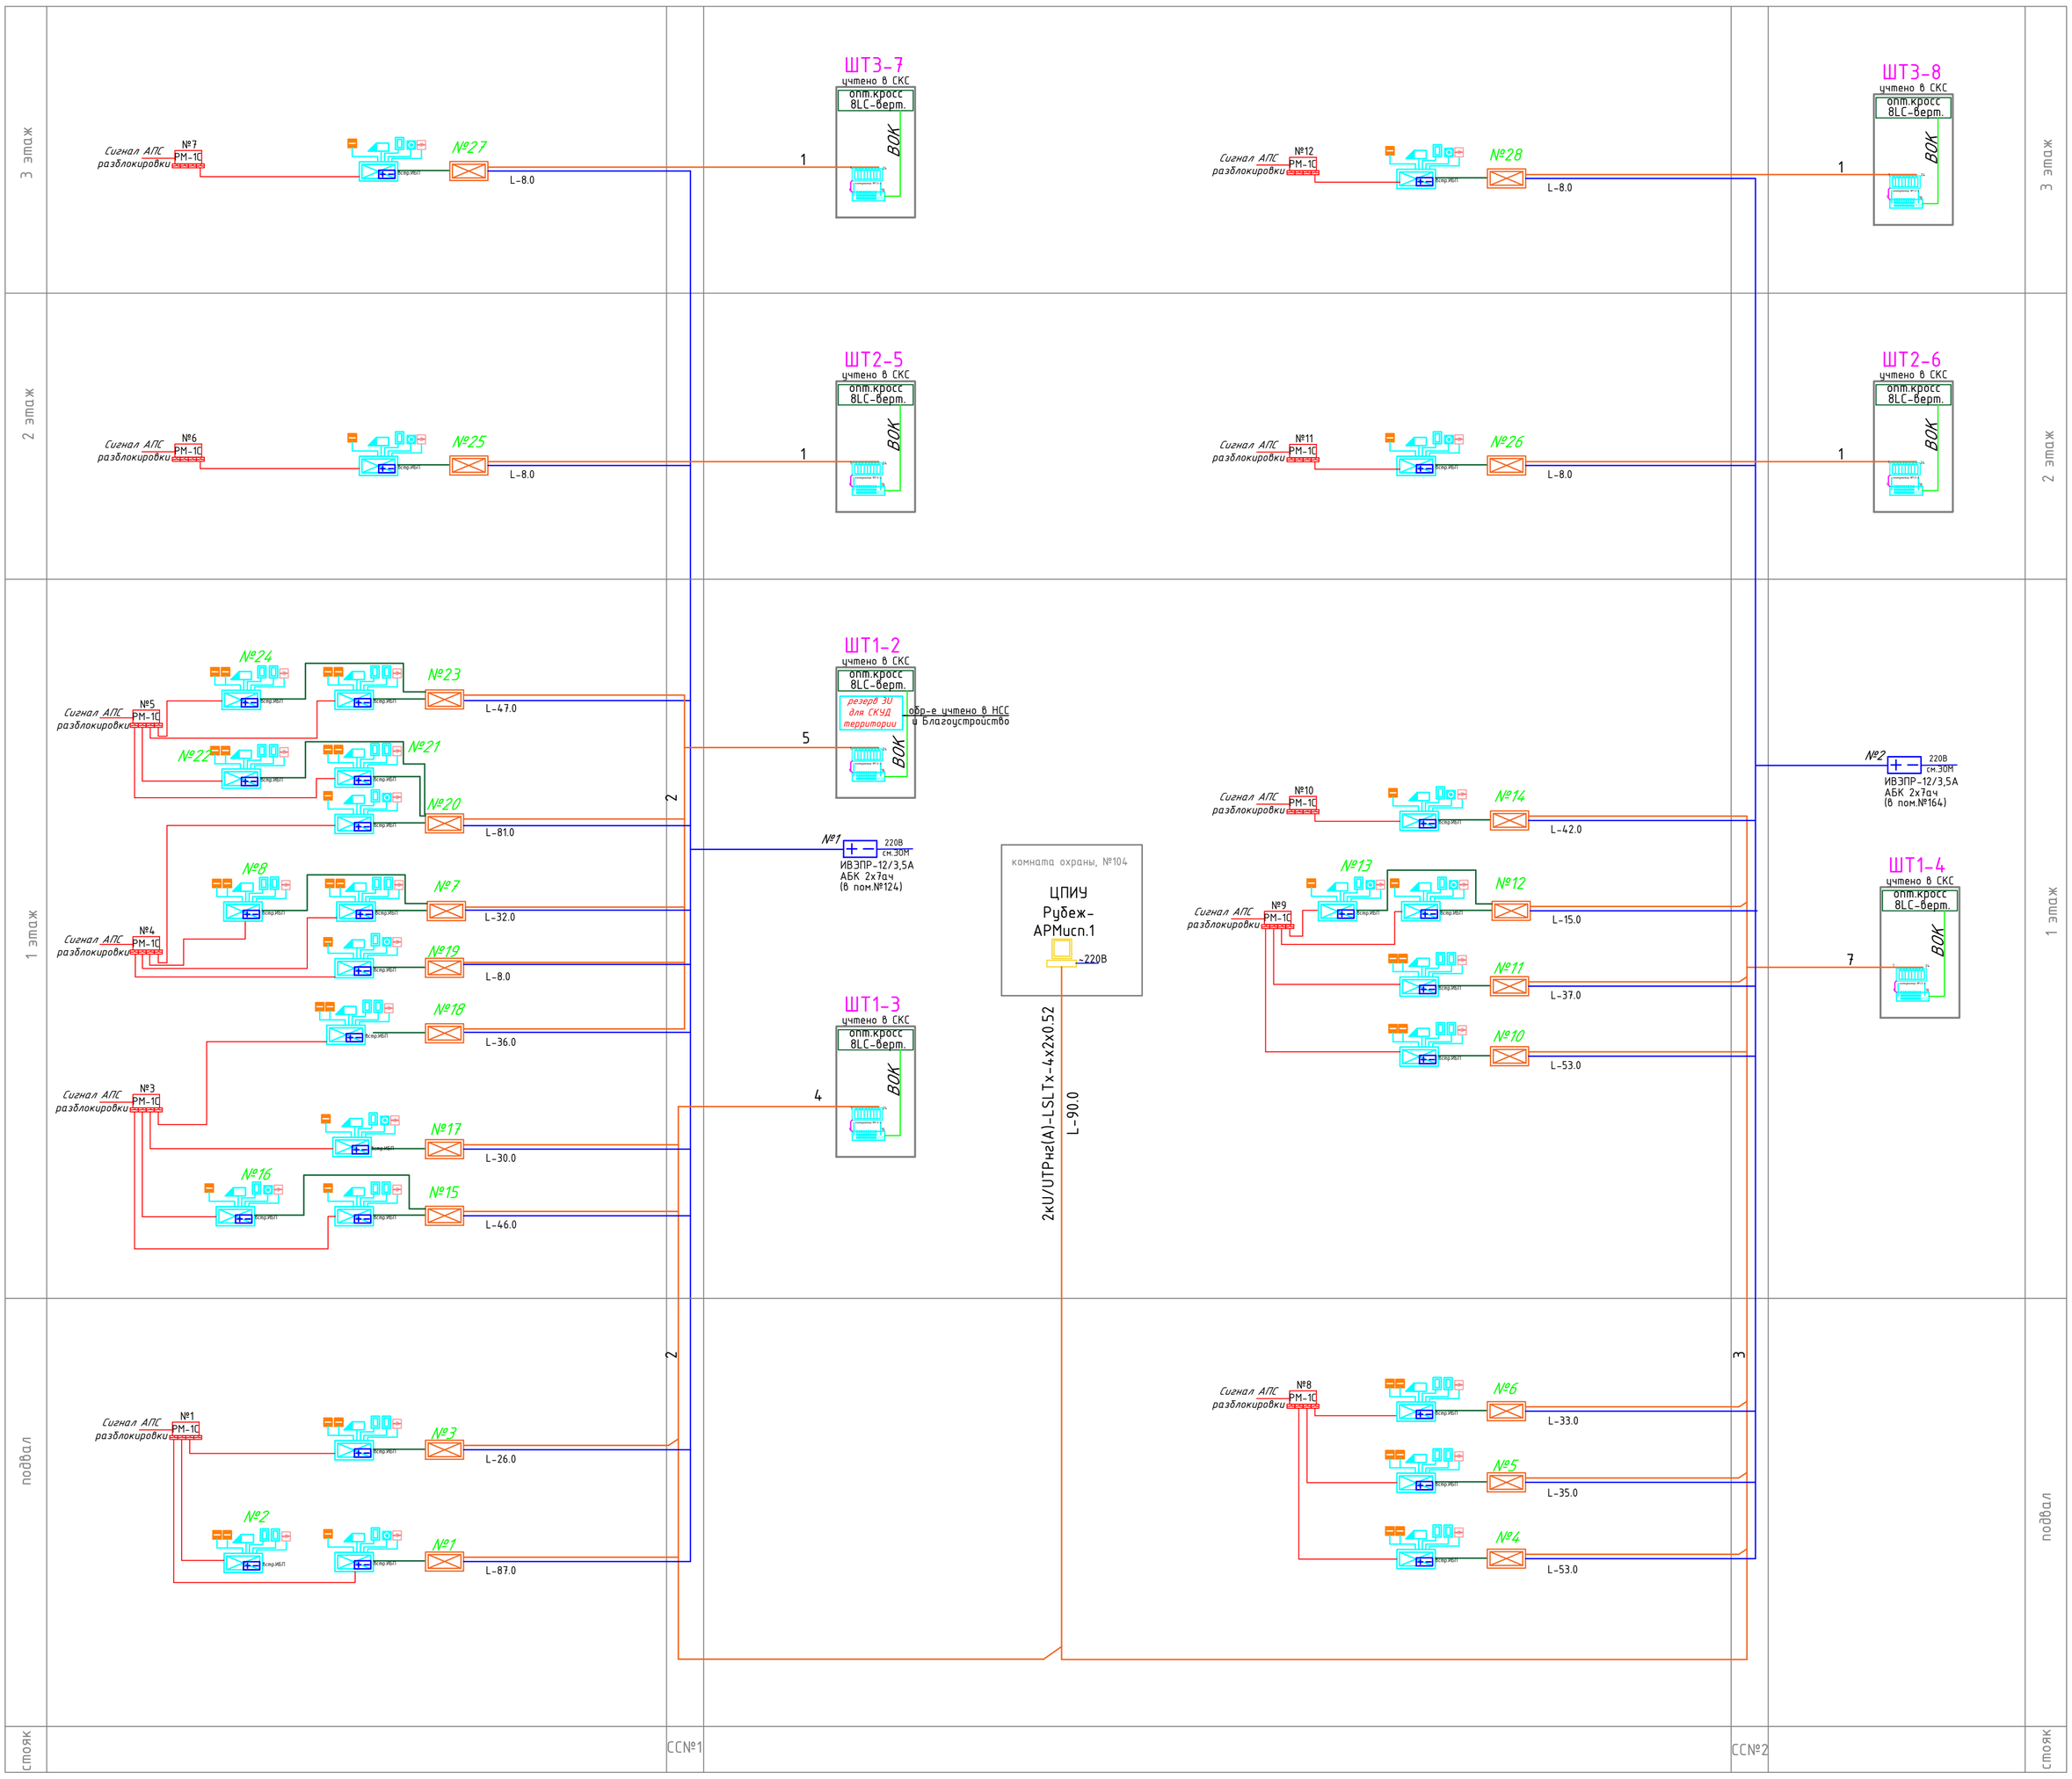

Условные обозначения

ШТ-1.4 — Телекоммуникационный шкаф 19" 42U напольный с указанием номера

П-п №8.1-1 — Патч -панель с указанием номера

Коммутатор на 16 портов с PoE

Источник электропитания 12В

Контроллер доступа "STR20-IP"

Модуль доступа "STR-1AP-M",встроенным ИБП

Замок электромагнитный

Извещатель охранный точечный магнитоконтактный

Считыватель электронных идентификаторов

Бесконтактная кнопка выхода

Аварийная кнопка выхода

№13 РМ-1С — Адресная метка на 4 точки с указанием номера

Кабели:

U/UTPнг(A)-LSLTx-4x2x0.52

КПСВВнг(A)-LSLTx-1x2x0.75

ВВГнг(A)-LSLTx-1x2x1.5мм

ЛОУТОКС 20нг(A)-FRLSLTx -1x2x0.5


ПРИМЕЧАНИЯ:

1. *Шкафы телекоммуникационные, оптические кроссовые панели, оптические кабели ВОК,металлические лотки учтены в части СКС-2024-00272-01-0-ИОС5.5*
2. *Адресные релейные модули РМ-1С включаются в шлейф пожарной сигнализации и учтены в части АПС -2024-00272-01-0-ИОС5.5.1. Подключение к контроллерам и модулям выполняется кабелем ЛОУТОКС 20нг(A)-FRLSLTx -1x2x0.5 и учитывается в части СКУД.*
3. *Элементы СКУД расположенные на территории школы (ворота и калитки), смотри проект "Благоустройство" и "Наружные сети связи".*
4. *В разделе СКС учтен телекоммуникационный шкаф ШТ.1-01, в котором расположен резерв ЗИ для оборудования СКУД территории.*

Взам.инв.N | Подпись и дата | Инв.N

Изм.	Кол.уч.	Лист	Nдок.	Подпись	Дата	2024-00272-00-ИОС5.8			
						Капитальный ремонт ГБОУ «Школа №1236 имени Героя Советского Союза Г.И.Щедрина» по адресу: г. Москва, ул. Клязьминская. д.7, корп.4			
Разработал		Роянцева А.А			12.2024	Капитальный ремонт	Стадия	Лист	Листов
Зав.сектора		Роянцева А.А			12.2024		П	1	6
Н. Контроль		Роянцева А.А.			12.2024	Принципиальная схема СКУД	МОСЖИЛ НИИПРОЕКТ		
Нач.ОПИС№1		Белоусова Д.П.			12.2024				

Принципиальная схема видеодомофона

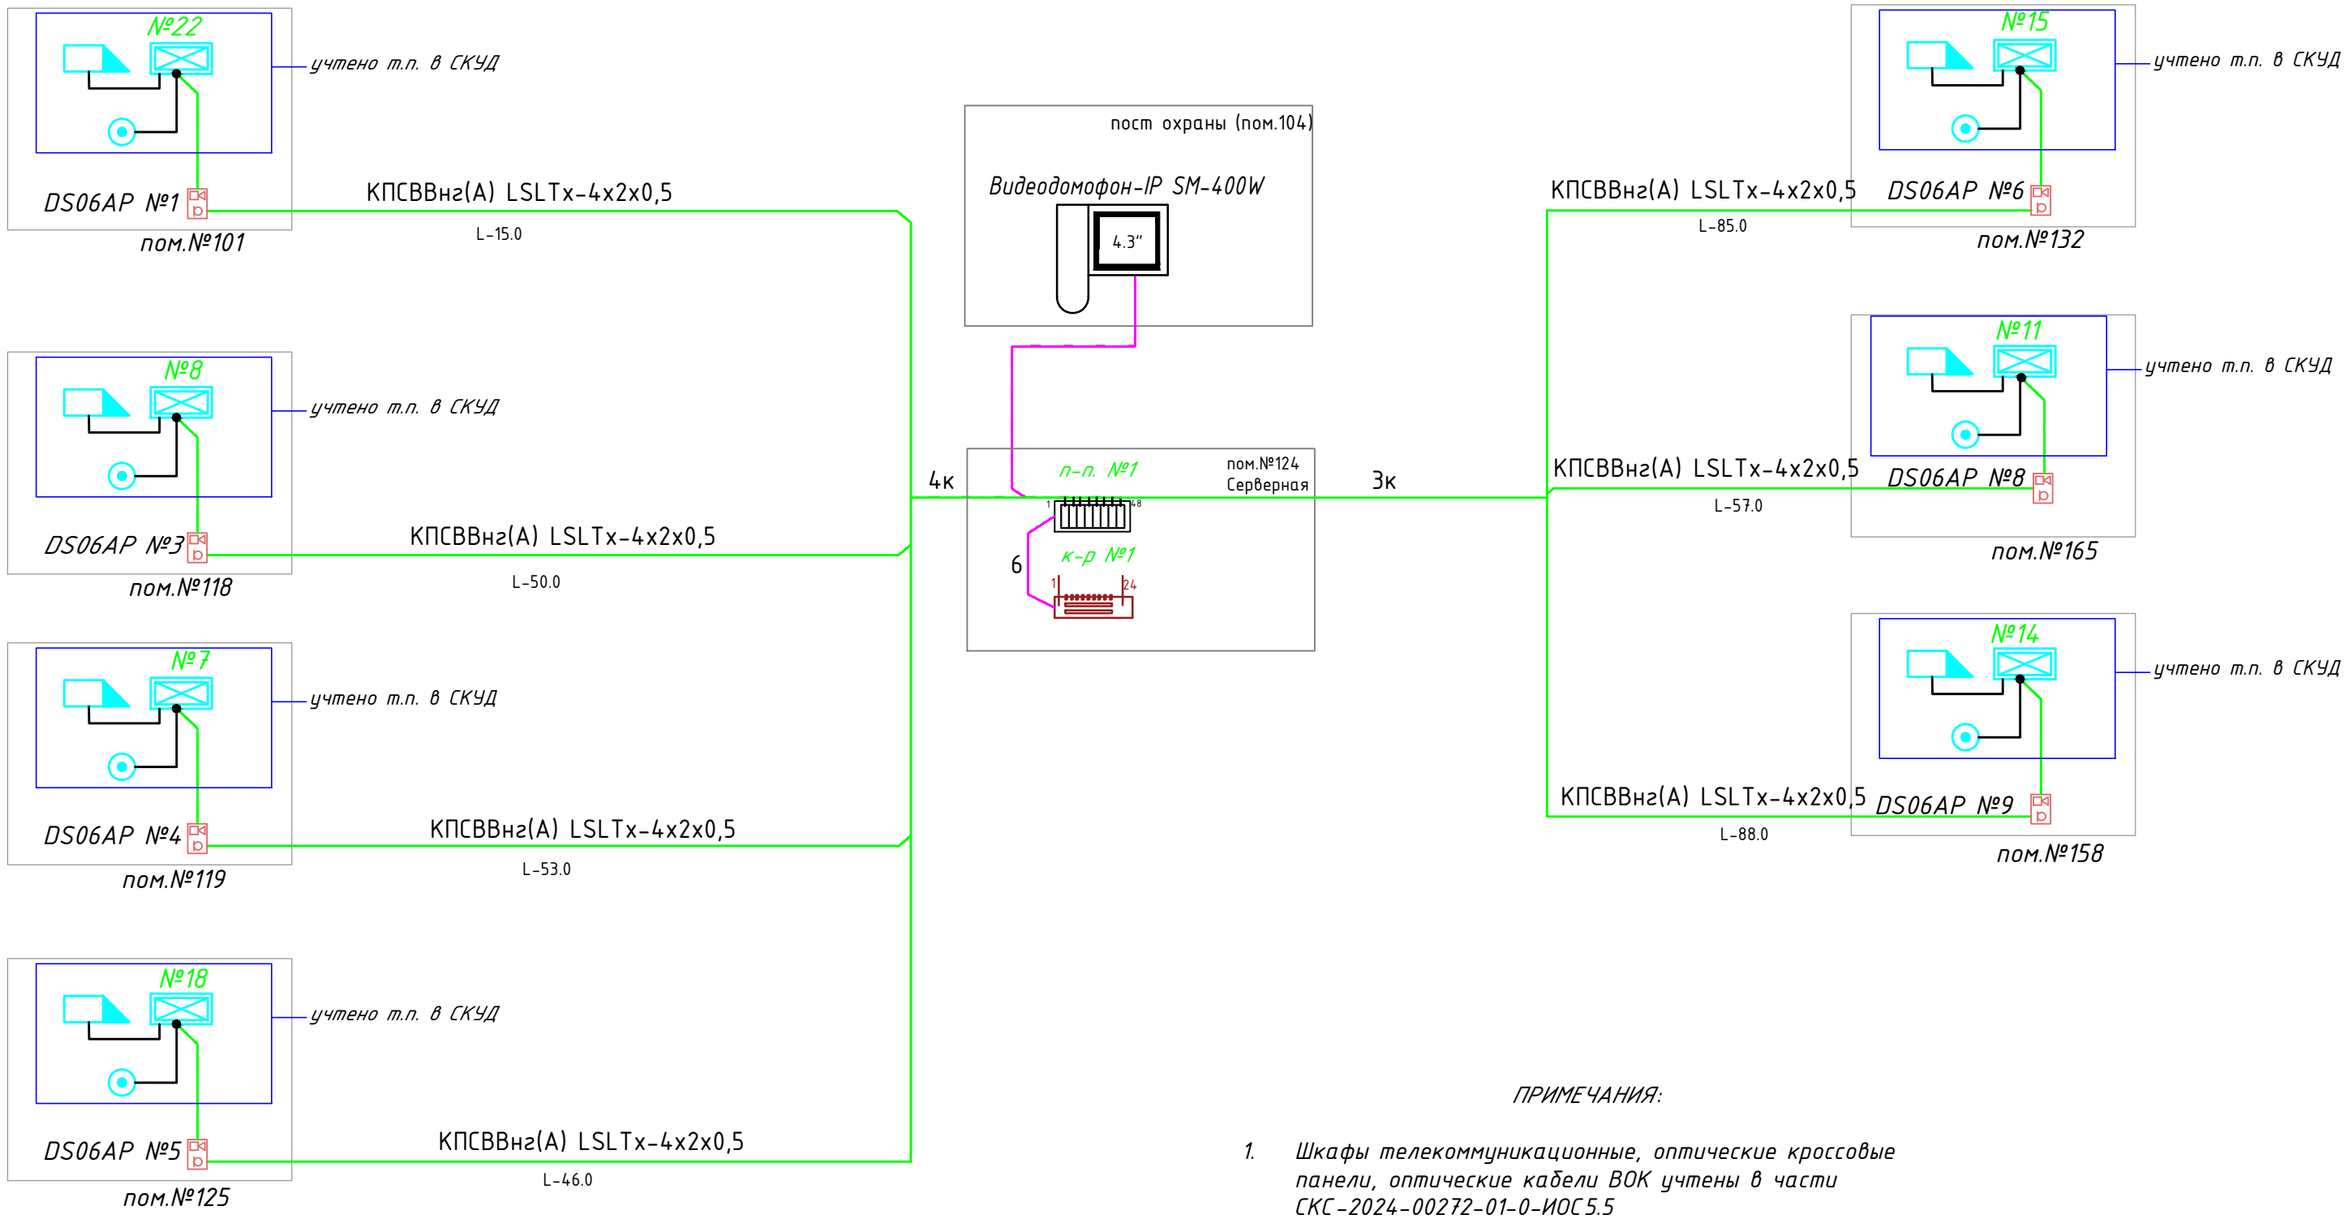

Условные обозначения

видеомонитор

вызывная панель

Патч-панель

Коммутатор доступа

ВВГнг(А)-LSLTх-1х2х1.5мм

U/UTPнг(А)-LSLTх-4х2х0.52

КПСВВнг(А) LSLTх-4х2х0,5

ПРИМЕЧАНИЯ:

1. *Шкафы телекоммуникационные, оптические кроссовые панели, оптические кабели ВОК учтены в части СКС-2024-00272-01-0-ИОС5.5*

Изм.	Кол.уч	Лист	Nдок.	Подпись	Дата	2024-00272-00-ИОС5.8		
						Капитальный ремонт ГБОУ «Школа №1236 имени Героя Советского Союза Г.И.Щедрина» по адресу: г. Москва, ул. Клязьминская. д.7, корп.4		
Разработал		Роянцева А.А			12.2024	Капитальный ремонт	Стадия	Лист	Листов
Зав.сектора		Роянцева А.А			12.2024		П	2	6
Н. Контроль		Роянцева А.А.			12.2024	Принципиальная схема видеодомофона	МОСЖИЛ НИИПРОЕКТ		
Нач.ОПИС№1		Белоусова Д.П.			12.2024				

Согласовано


Взамен инв. N°

Подпись и дата

Инв. N° подл.

Здание Государственного бюджетного общеобразовательного
учреждения города Москвы "Школа № 236 имени Героя Советского Союза
Г.И.Щедрина", расположенное по адресу: г. Москва, ул.Клязьминская, д. 7,корп.4"

План подвала
М 1:100

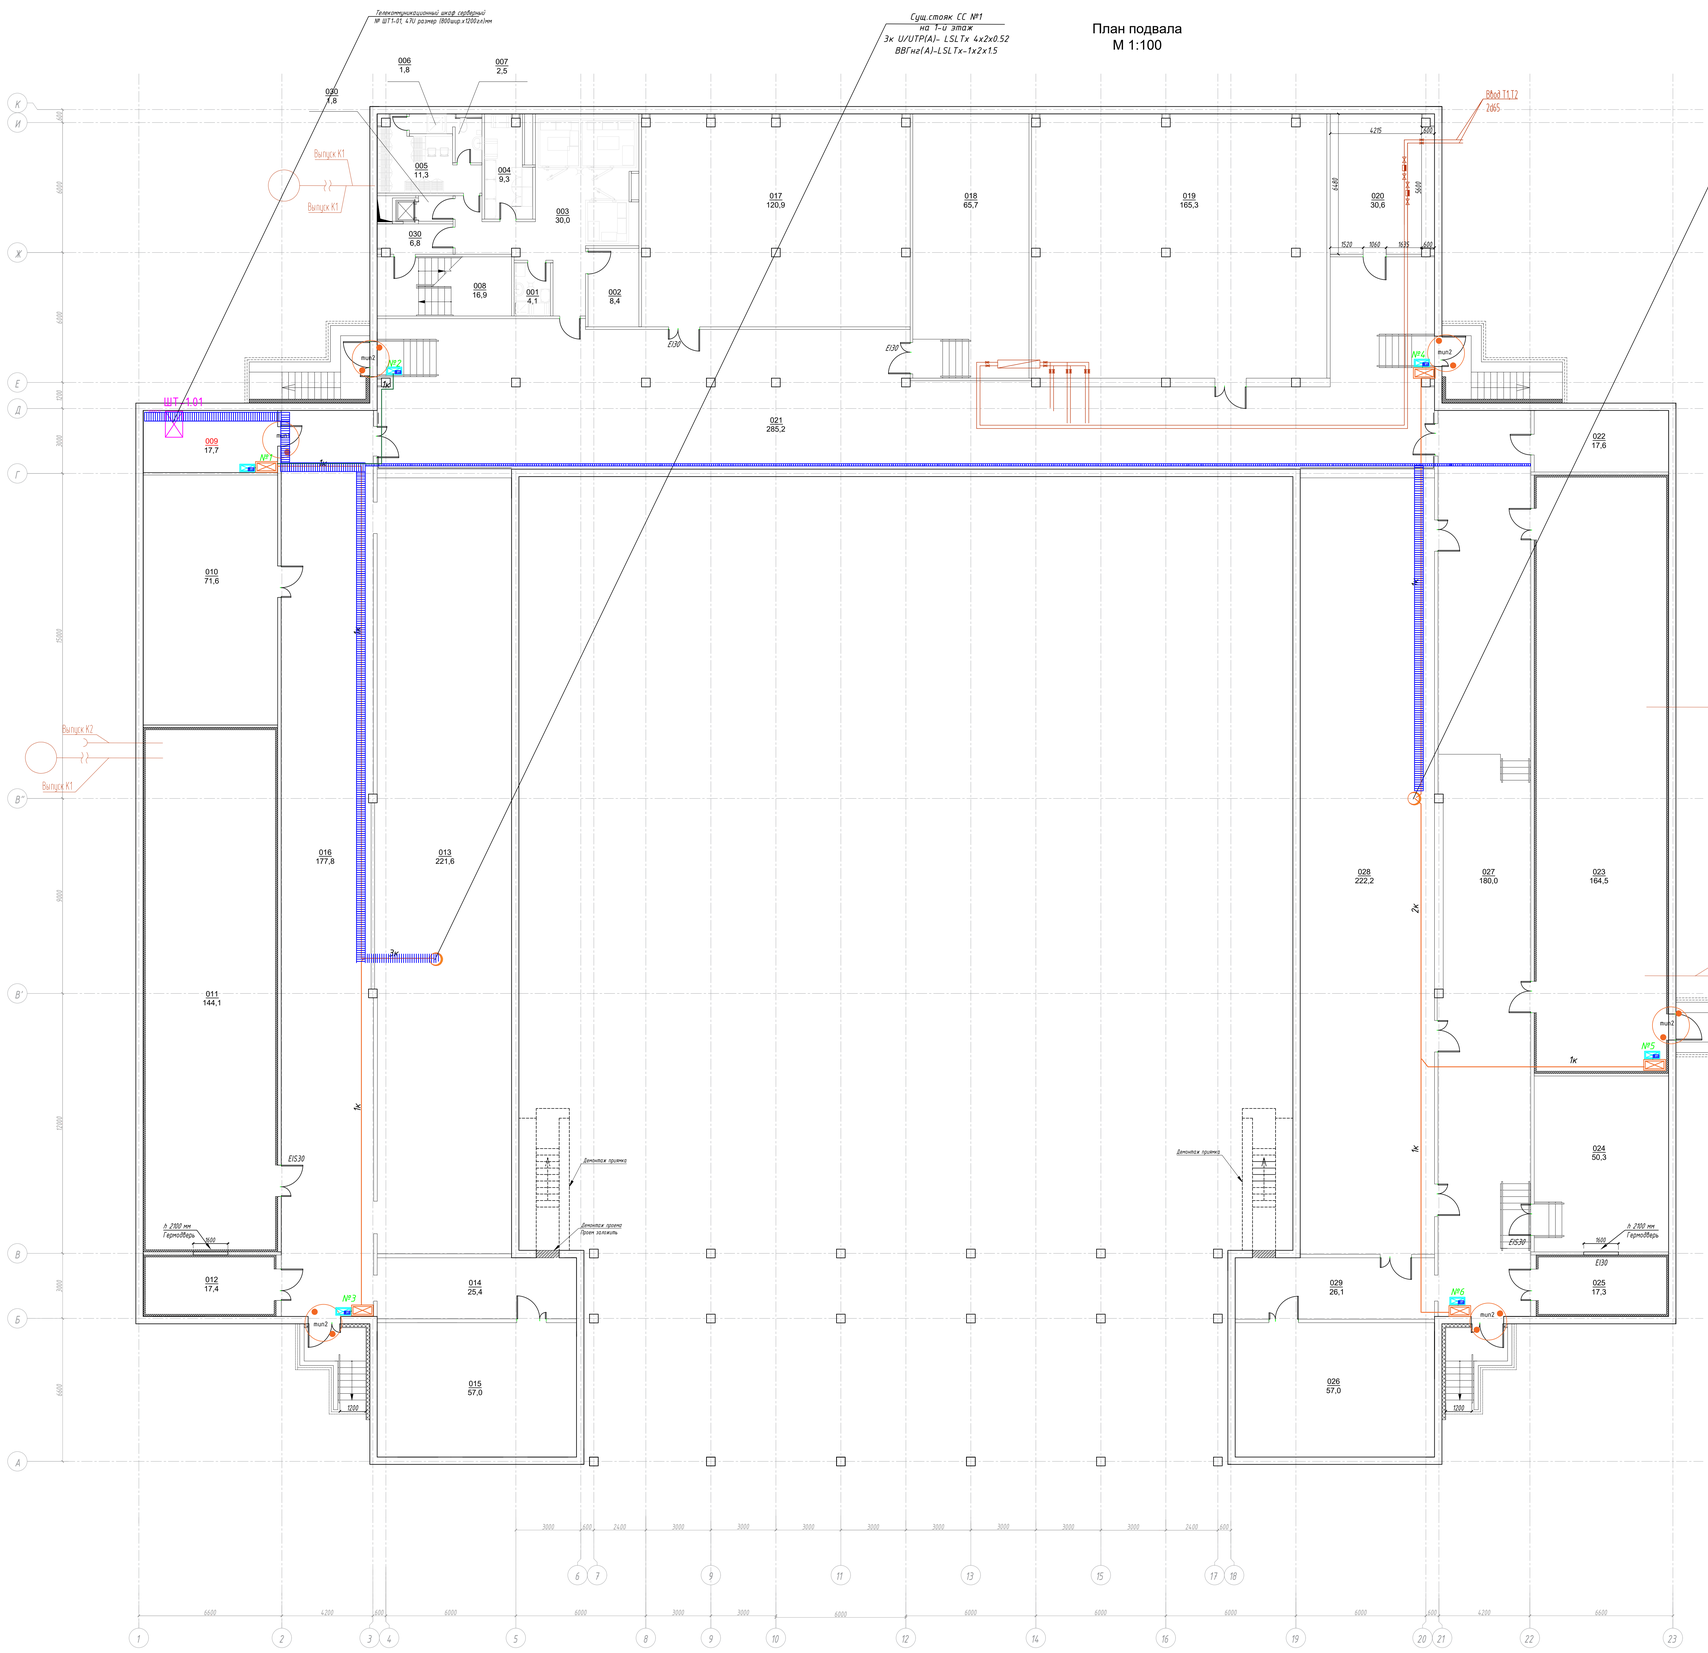


Экспликация помещений подвала

N п/п	Наименование помещений	Пл-дь м²	Кат. пом.
001	ПУИ	4,1	*
002	Кладовая овощей	8,4	*
003	Коридор	30,0	*
004	Кладовая сухих продуктов	9,3	*
005	Помещение для персонала (раздевалка с душевой)	11,3	
006	Душевая	1,8	
007	Санузел персонала	2,5	
008	Технологическая лестница типа Н2	16,9	
009	Серверная	17,7	В3
010	Электрощитовая /ВРУ	71,6	В3
011	Венткамера	144,1	Д
012	Венткамера	17,4	Д
013	Теплотрасса	221,6	
014	Коридор	25,4	
015	Теплотрасса	57,0	
016	Коридор	177,8	
017	Теплотрасса	120,9	
018	Теплотрасса	65,7	
019	Водомерный узел	165,3	В4
020	ИТП	30,6	В4
021	Коридор	285,2	
022	Теплотрасса	17,6	
023	Венткамера	164,5	Д
024	Теплотрасса	50,3	
025	Венткамера	17,3	Д
026	Теплотрасса	57,0	
027	Коридор	180,0	
028	Теплотрасса	222,2	
029	Коридор	26,1	
030	Тамбур-шлюз	6,8	
	ИТОГО:	2286,2	

Условные обозначения

- ШТ-1.4 — Телекоммуникационный шкаф 19" 42U напольный с указанием номера
- П-п №8.1-1 — Патч-панель с указанием номера
- Коммутатор на 16 портов с PoE
- Источник электропитания 12В
- Контроллер доступа "STR20-IP"
- Модуль доступа "STR-1AP-M",встроенным ИБП
- Замок электромагнитный
- Извещатель охранный точечный магнитоконтактный
- Считыватель электронных идентификаторов
- Бесконтактная кнопка выхода
- Аварийная кнопка выхода
- №13 РМ-1С — Адресная метка на 4 точки с указанием номера
- mun1 — - односторонняя точка прохода считыватель - кнопка "Выход"
- mun2 — - двухсторонняя точка прохода считыватель - считыватель

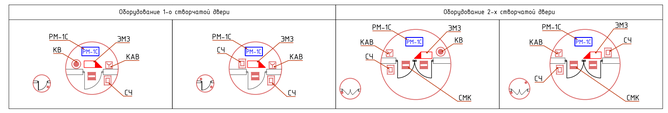


						2024-00272-00-ИОС5.8	
Изм.	Кол.уч.	Лист	N док.	Подпись	Дата	Капитальный ремонт ГБОУ «Школа №1236 имени Героя Советского Союза Г.И.Щедрина» по адресу: г. Москва, ул. Клязьминская. д.7, корп.4	
Разработал		Ровицова А.А.			12.2024		
Зав.сектора		Ровицова А.А.			12.2024	Капитальный ремонт	Стадия: П; Лист: 3; Листов: 6
Н. Контроль		Ровицова А.А.			12.2024	План подвала. М 1:100. Расположение оборудования и кабельных трасс СКУД.	МОСЖИЛ НИИПРОЕКТ
Нач.ОПИСиТ		Белоусова Д.П.			12.2024		

Согласовано | Взам.инв. N° | Подпись и дата | Инв. N° подл.

Копировал | Формат А0

Здание Государственного бюджетного общеобразовательного учреждения города Москвы "Школа № 236 имени Героя Советского Союза Г.И.Щедрина", расположенное по адресу: г. Москва, ул.Клязьминская, д. 7,корп.4

План 1-го этажа
М 1:100

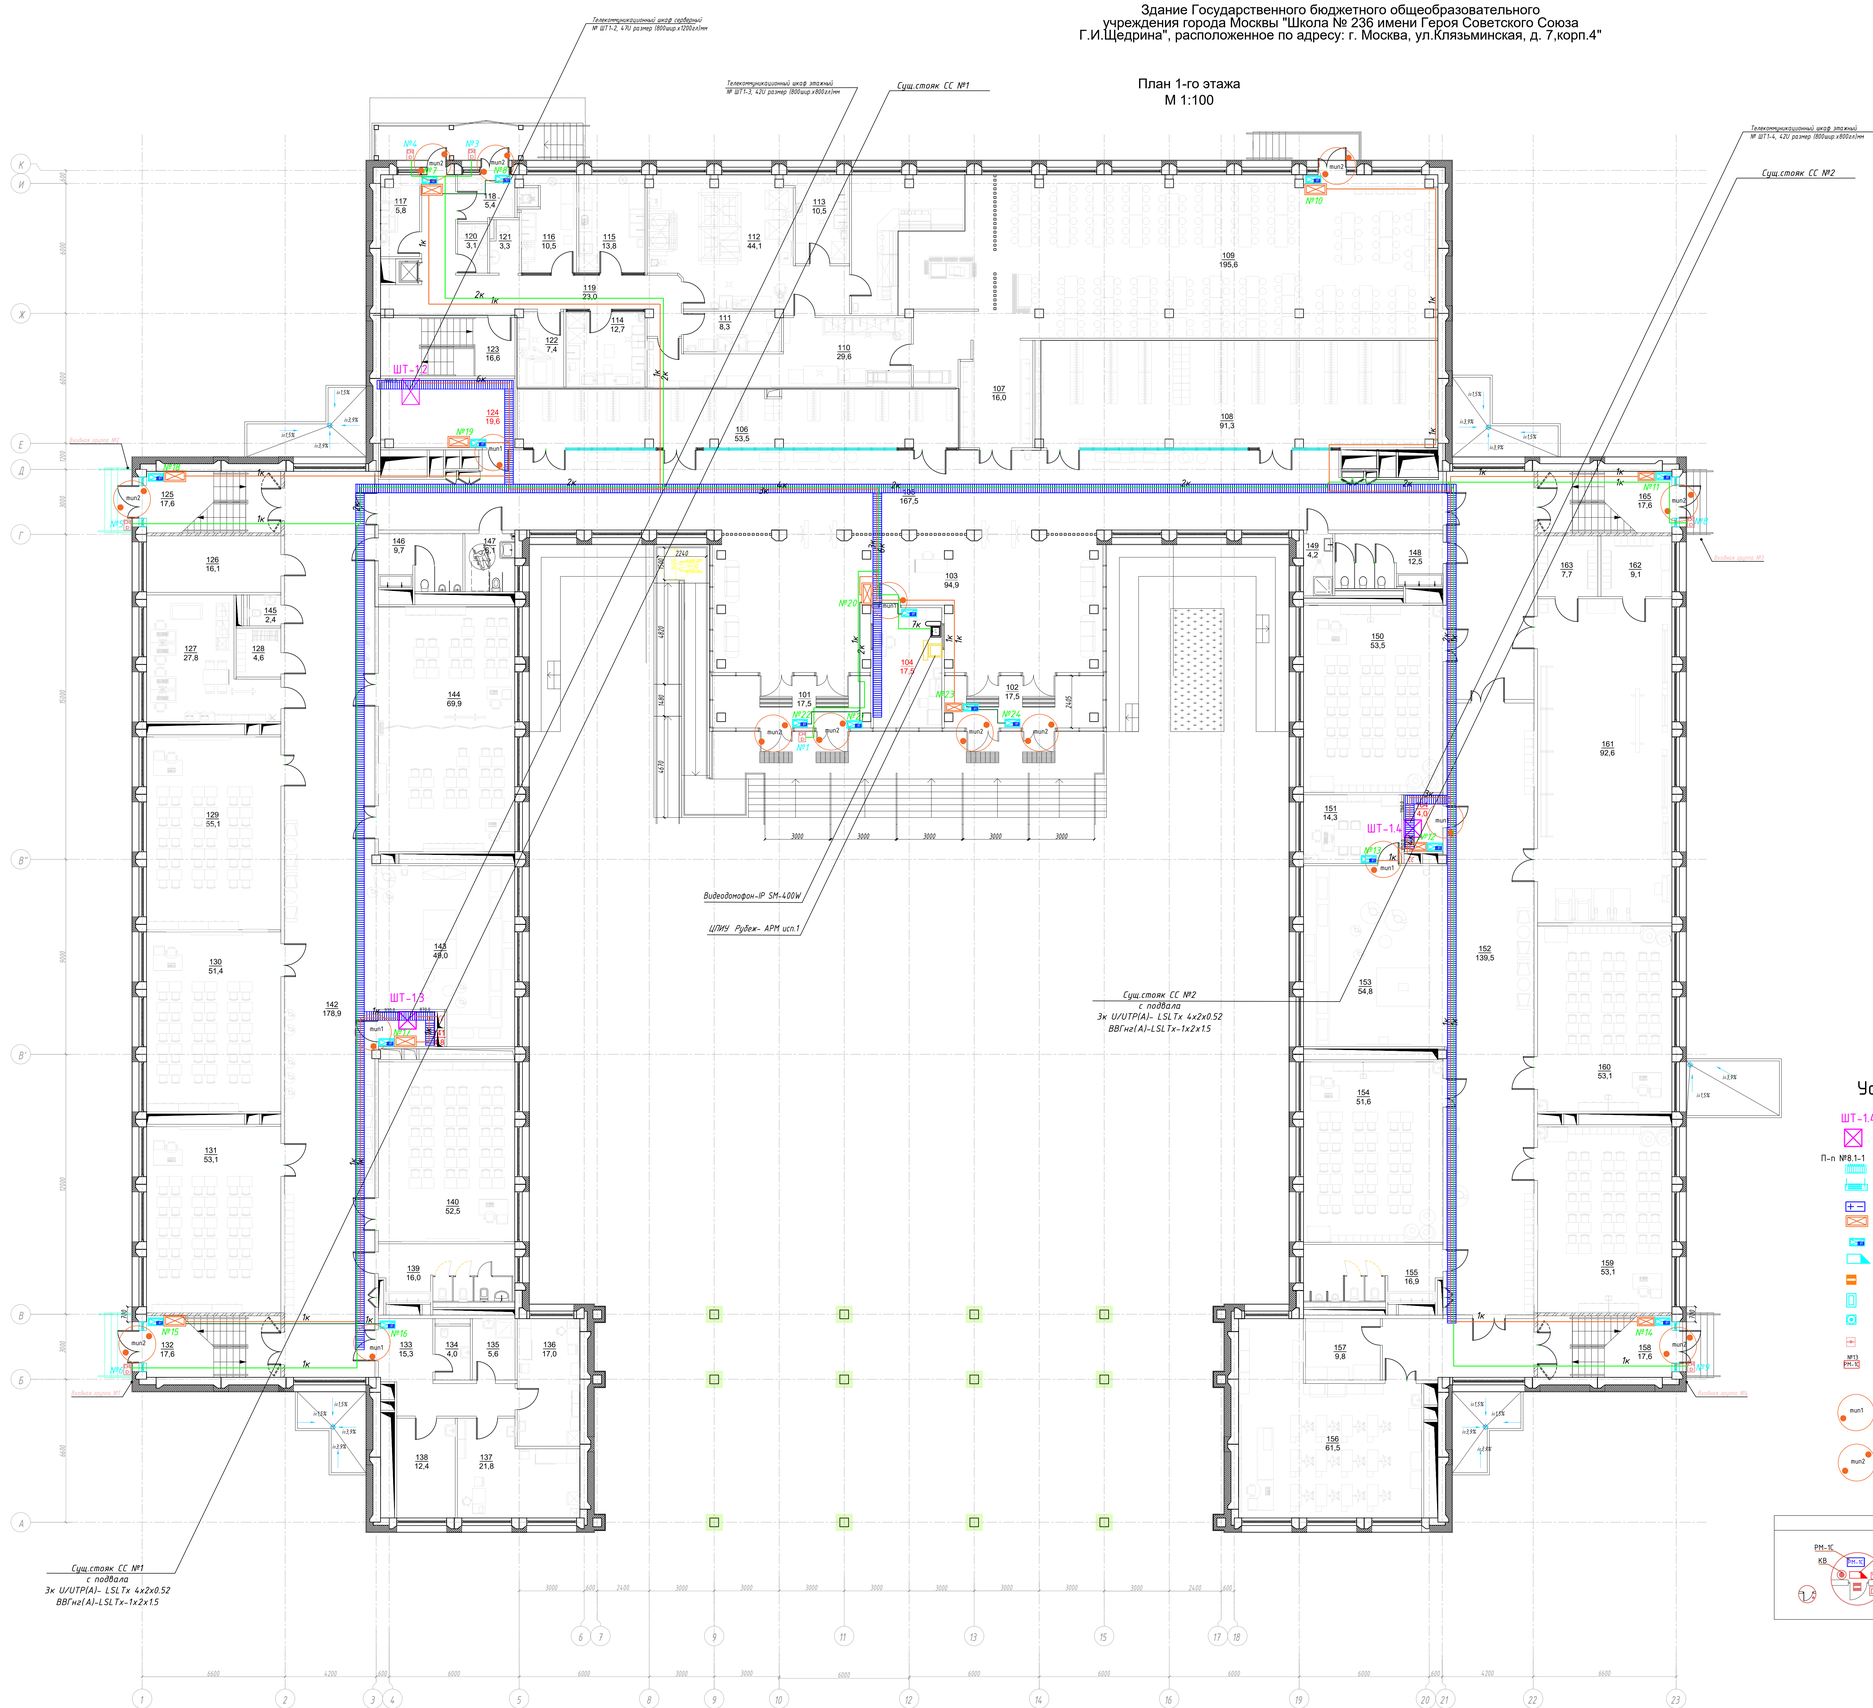

Условные обозначения

ШТ-1.4	Телекоммуникационный шкаф 19" 42U напольный с указанием номера
П-п №8.1-1	Патч -панель с указанием номера
	Коммутатор на 16 портов с PoE
	Источник электропитания 12В
	Контроллер доступа "STR20-IP"
	Модуль доступа "STR-1AP-M",встроенным ИБП
	Замок электромагнитный
	Извещатель охранный точечный магнитоконтактный
	Считыватель электронных идентификаторов
	Бесконтактная кнопка выхода
	Аварийная кнопка выхода
№13 РМ-1С	Адресная метка на 4 точки с указанием номера
mun1	- односторонняя точка прохода считыватель - кнопка "Выход"
mun2	- двухсторонняя точка прохода считыватель - считыватель

Оборудование 1-о створчатой двери		Оборудование 2-х створчатой двери	
РМ-1С, КВ, ЭМЗ, КАВ, СЧ	РМ-1С, ЭМЗ, КАВ, СЧ	РМ-1С, КАВ, СЧ, ЭМЗ, КВ, СМК	РМ-1С, КАВ, ЭМЗ, СЧ, СМК

Экспликация помещений 1-го этажа

N п/п	Наименование помещений	Пл-дь м²	Кат. пом.
101	Тамбур	17,5	
102	Тамбур	17,5	
103	Зона ожидания для посетителей	94,9	
104	Комната охраны с диспетчерским пунктом	17,5	
105	Коридор с зоной ожидания	167,5	
106	Гардеробная для обучающихся (начальная школа)	53,5	
107	Умывальная	16,0	
108	Гардеробная для обучающихся (основная школа)	91,3	
109	Обеденный зал	195,6	*
110	Моечная для столовой посуды	29,6	*
111	Моечная для кухонной посуды	8,3	*
112	Горячий цех	44,1	*
113	Холодный цех	10,5	*
114	Мясо-рыбный цех	12,7	*
115	Цех вторичной обработки овощей	13,8	*
116	Цех первичной обработки овощей	10,5	*
117	Кладовая и моечная оборотной тары	5,8	*
118	Загрузочный цех	5,4	*
119	Коридор	23,0	*
120	ПДМ	3,1	*
121	Санузел персонала	3,3	*
122	Помещение для временного хранения пищевых отходов	7,4	В4
123	Технологическая лестница типа Н2	16,6	
124	Серверная	19,6	В3
125	Лестничная клетка "А" типа Н2	17,6	
126	Электрощитовая	16,1	В3
127	Кабинет с рабочим пространством для учителей 1-го типа	27,8	
128	Гардеробная комната (для учителей)	4,6	
129	Кабинет математики	55,1	
130	Кабинет математики	51,4	
131	Кабинет математики	53,1	
132	Лестничная клетка "Б" типа Л1	17,6	
133	Коридор тех.блока	15,3	
134	Гуалет тех.блока	4,0	
135	Помещение приготовления дезинфицирующих растворов и хранения уборочного инвентаря, предназначенных для помещений медицинского назначения	5,6	В4
136	Процедурный кабинет	17,0	
137	Кабинет врача	21,8	
138	Прививочный кабинет	12,4	
139	Санузел для девочек с комнатой личной гигиены (основная школа)	16,0	
140	Кабинет русского языка и литературы	52,5	
141	Кроссовая	4,8	В4
142	Коридор с рекреацией	178,9	
143	Коридор с рекреацией	4,9	
144	Кабинет иностранного языка с возможностью деления трансформируемой перегородкой на два помещения (основная и старшая школа)	69,9	
145	Санузел для персонала	2,4	
146	Санузел для мальчиков начальной школы	9,7	
147	Санузел для МГН	6,3	
148	Санузел для девочек (начальная школа)	12,5	
149	ПэМ	4,2	В4
150	Учебный кабинет (1 класс)	53,5	
151	Административный кабинет 1-го типа	14,3	
152	Коридор с рекреацией	139,5	
153	Коридор с рекреацией	54,8	
154	Учебный кабинет (1 класс)	51,6	
155	Санузел для мальчиков (начальная школа)	16,9	
156	Кабинет материальной технологии 2-го типа	61,5	
157	Лаборантская при кабинете технологии	9,8	В3
158	Лестничная клетка "В" типа Л1	17,6	
159	Учебный кабинет (1 класс)	53,1	
160	Учебный кабинет (2 класс)	53,1	
161	Гимнастического зала (хореография)	92,6	
162	Раздевальная	9,1	
163	Раздевальная	7,7	
164	Кроссовая	4,0	В4
165	Лестничная клетка "Г" типа Н2	17,6	
	ИТОГО:	2260,1	

Изм.	Кол.уч.	Лист	№док.	Подпись	Дата
Разработал		Ровнейко А.А.			12.2024
Зав.сектором		Ровнейко А.А.			12.2024
Н. Контроль		Ровнейко А.А.			12.2024
Нач.ОПИСМП		Белоусова Д.П.			12.2024

2024-00272-00-ИОСЗ.В

Капитальный ремонт ГБОУ «Школа №1236 имени Героя Советского Союза Г.И.Щедрина» по адресу: г. Москва, ул. Клязьминская, д.7, корп.4

Капитальный ремонт

План 1-го этажа. М 1:100. Расположение оборудования и кабельных трасс СКУД.

Стадия	Лист	Листов
П	4	6

МОСЖИЛ НИИПРОЕКТ

Копировал

Формат А0

Согласовано


Взамен инв. №

Подпись и дата

Инв. № подл.

Здание Государственного бюджетного общеобразовательного
учреждения города Москвы "Школа № 236 имени Героя Советского Союза
Г.И.Щедрина", расположенное по адресу: г. Москва, ул.Клязьминская, д. 7,корп.4"

План 2-го этажа
М 1:100

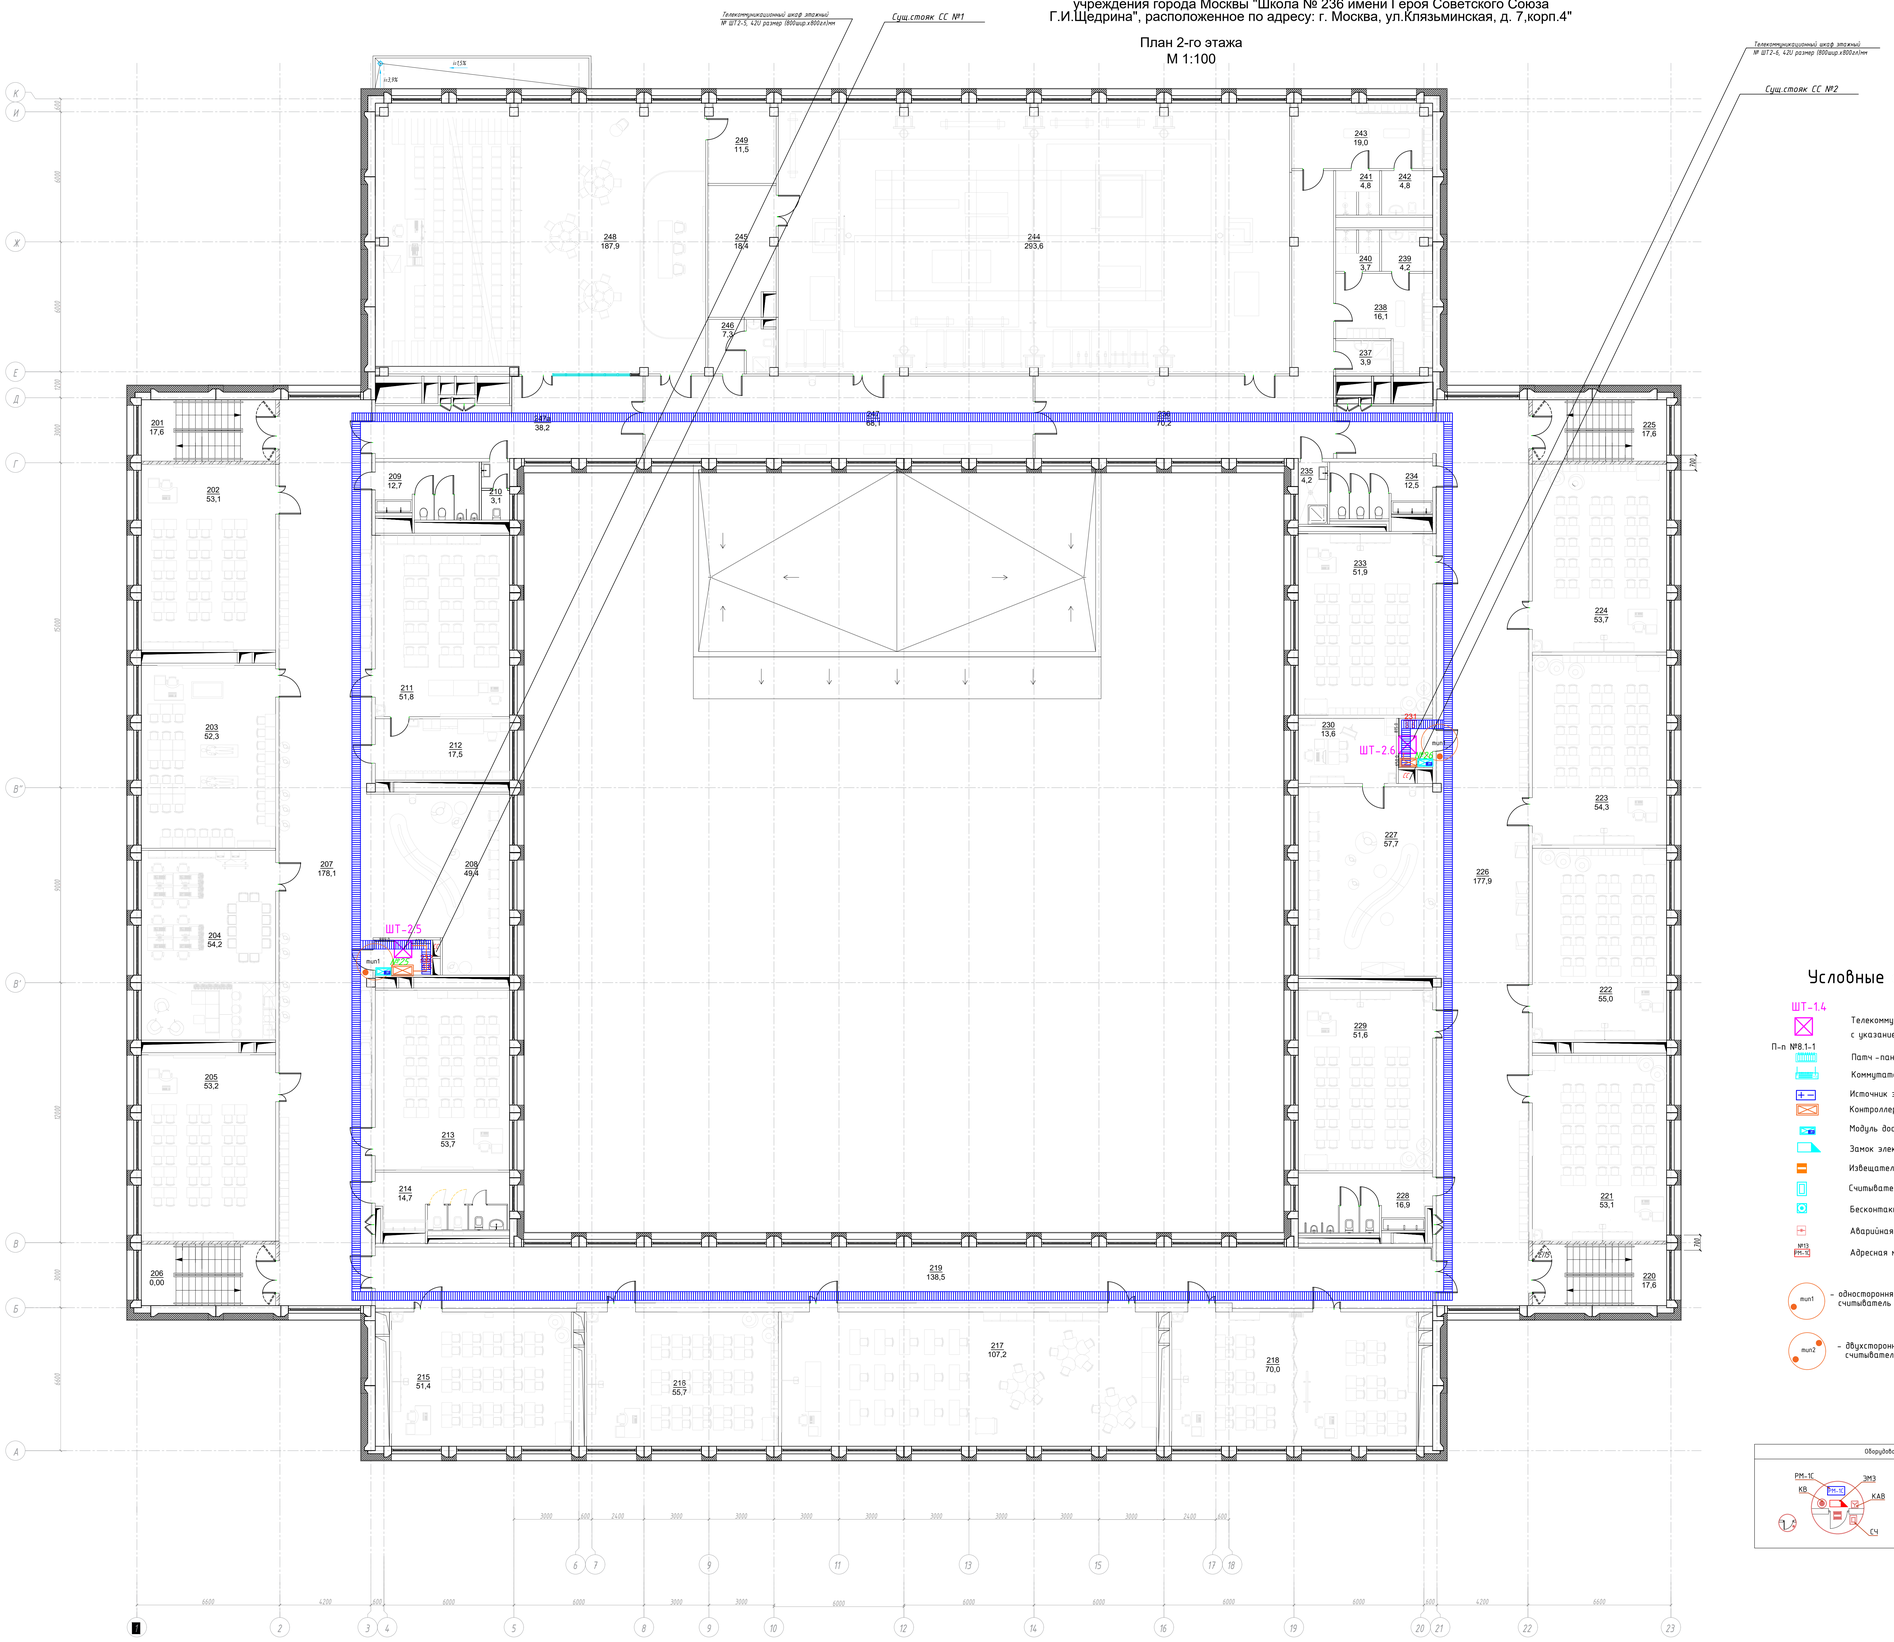

Экспликация помещений 2-го этажа

N п/п	Наименование помещений	Пл-дь м²	Кат. пом.
201	Лестничная клетка "А" типа Н2	17,6	
202	Кабинет русского языка и литературы	53,1	
203	Кабинет ОБЗР	52,3	
204	Кабинет с рабочим пространством для учителей 2-го типа	54,2	
205	Кабинет математики	53,2	
206	Лестничная клетка "Б" типа Л1	17,6	
207	Коридор с зоной ожидания	178,1	
208	Коридор с зоной ожидания	49,4	
209	Санузел для мальчиков (начальная школа)	12,7	
210	Санузел для персонала	3,1	
211	Учебный кабинет для изучения естествознания: биология, тип 1	51,8	
212	Лаборантская кабинета биологии	17,5	В3
213	Кабинет математики	53,7	
214	Санузел для девочек с комнатой личной гигиены (основная школа)	14,7	
215	Учебный кабинет (2-4 класс)	51,4	
216	Учебный кабинет (2-4 класс)	55,6	
217	Лабораторно-исследовательский комплекс для изучения естествознания 2-го типа	107,2	
218	Кабинет иностранного языка с возможностью деления трансформируемой перегородкой на два помещения (начальная школа)	107,0	
219	Коридор	138,5	
220	Лестничная клетка "В" типа Л1	17,6	
221	Учебный кабинет (2-4 класс)	53,1	
222	Учебный кабинет (2-4 класс)	55,0	
223	Учебный кабинет (2-4 класс)	54,3	
224	Учебный кабинет (2-4 класс)	53,7	
225	Лестничная клетка "Г" типа Н2	17,6	
226	Коридор с зоной ожидания	177,9	
227	Коридор с зоной ожидания	57,7	
228	Санузел для мальчиков (начальная школа)	16,9	
229	Учебный кабинет (2-4 класс)	51,6	
230	Кабинет индивидуальных занятий, в т.ч. с учителем-логопедом	13,6	
231	Кроссовая	3,5	
232	Кроссовая	4,8	
233	Учебный кабинет (2-4 класс)	51,9	
234	Санузел для девочек (начальная школа)	12,5	
235	ПЗИ	4,2	В4
236	Коридор	70,2	
237	ПЗИ	3,9	
238	Раздевальные	16,1	
239	Санузел	4,2	
240	Душевые	3,7	
241	Душевые	4,8	
242	Санузел	4,8	
243	Раздевальные	19,0	
244	Спортивный зал	239,6	
245	Снарядная	18,4	В4
246	Комната инструктора (с душем и санузлом)	7,3	
247	Коридор	68,1	
247а	Коридор	38,2	
248	Актовый зал (с эстрадой в уровне пола)	187,9	
249	Кладовая инвентаря	11,5	В4
	ИТОГО:	2423,3	

Условные обозначения

ШТ-1.4 — Телекоммуникационный шкаф 19" 42U напольный с указанием номера

П-п №8.1-1 — Патч-панель с указанием номера

Коммутатор на 16 портов с PoE

Источник электропитания 12В

Контроллер доступа "STR20-IP"

Модуль доступа "STR-1AP-M",встроенным ИБП

Замок электромагнитный

Извещатель охранный точечный магнитоконтактный

Считыватель электронных идентификаторов


Бесконтактная кнопка выхода

Аварийная кнопка выхода

№13 РМ-1С — Адресная метка на 4 точки с указанием номера

mun1 – односторонняя точка прохода
считыватель - кнопка "Выход"

mun2 – двухсторонняя точка прохода
считыватель - считыватель

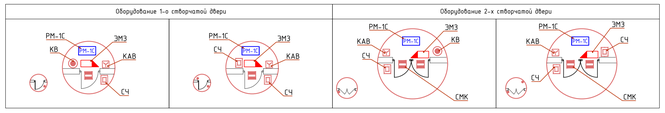

						2024-00272-00-ИОС5.8	
						Капитальный ремонт ГБОУ «Школа №1236 имени Героя Советского Союза Г.И.Щедрина» по адресу: г. Москва, ул. Клязьминская. д.7, корп.4	
Изм.	Кол.уч.	Лист	№док.	Подпись	Дата		
Разработал		Ромицова А.А.			12.2024	Капитальный ремонт	Стадия: П; Лист: 5; Листов: 6
Зав.сектора		Ромицова А.А.			12.2024		
Н. Контроль		Ромицова А.А.			12.2024	План 2-го этажа. М 1:100. Расположение оборудования и кабельных трасс СКУД.	МОСЖИЛ НИИПРОЕКТ
Нач.ОПЭСМП		Белусова Д.П.			12.2024		

Копировал

Формат А0

Согласовано


Взам.инв. №

Подпись и дата

Инв. № подл.

Здание Государственного бюджетного общеобразовательного
учреждения города Москвы "Школа № 236 имени Героя Советского Союза
Г.И.Щедрина", расположенное по адресу: г. Москва, ул.Клязьминская, д. 7,корп.4"

План 3-го этажа
М 1:100

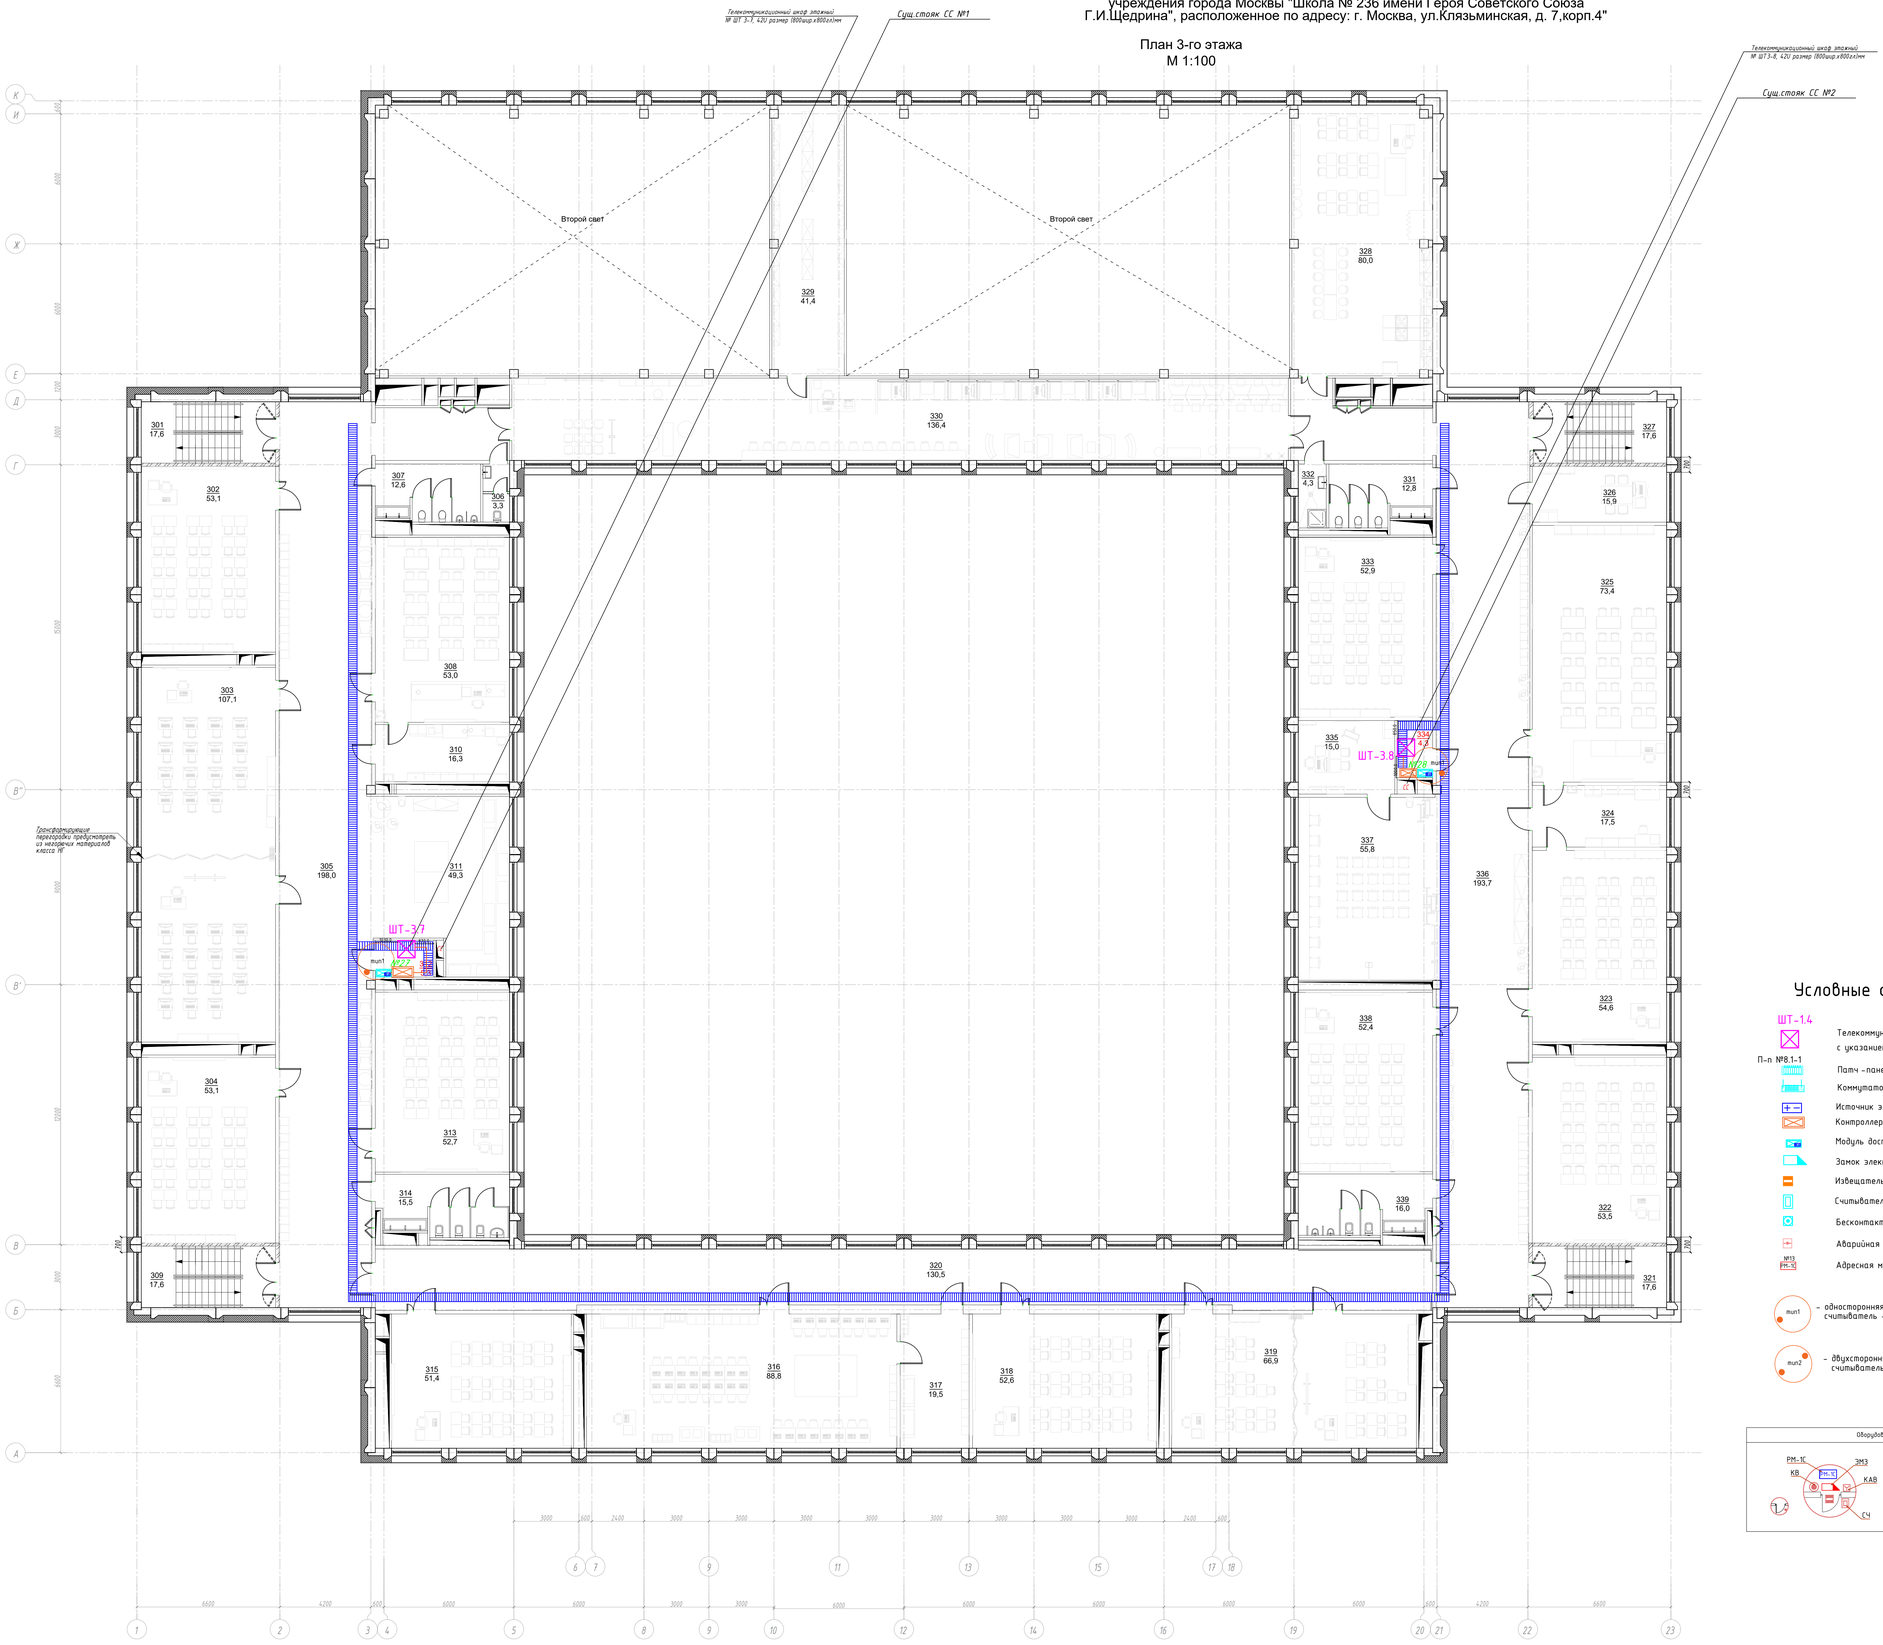

Экспликация помещений 3-го этажа

N п/п	Наименование помещений	Пл-дь м²	Кат. пом.
301	Лестничная клетка "А" типа Н2	17,6	
302	Кабинет химии (универсальный)	53,1	
303	Кабинет информатики с возможностью деления трансформируемой перегородкой на два помещения	107,1	
304	Кабинет русского языка и литературы	53,1	
305	Коридор	198,5	
306	Санузел для персонала	3,3	
307	Санузел для мальчиков (основная школа)	12,6	
308	Учебный кабинет для изучения естествознания: химия	53,0	
309	Лестничная клетка "Б" типа Л1	17,6	
310	Лаборантская кабинета химии	16,3	В3
311	Рекреация	49,3	
312	Кроссовая	53,3	В4
313	Кабинет русского языка и литературы	52,7	
314	Санузел для девочек (основная школа)	15,5	
315	Кабинет русского языка и литературы	51,4	
316	Кабинет информационных технологий	88,8	
317	Лаборантская при кабинете информационных технологий	19,5	
318	Кабинет русского языка и литературы	52,6	
319	Кабинет иностранного языка с возможностью деления трансформируемой перегородкой на два помещения (основная школа)	66,9	
320	Зона ожидания	130,5	
321	Лестничная клетка "В" типа Л1	17,6	
322	Кабинет истории 1-го типа	53,5	
323	Кабинет физики (универсальный)	54,6	
324	Лаборантская кабинета физики	17,5	
325	Учебный кабинет для изучения естествознания	73,4	
326	Административный кабинет 1-го типа	15,9	
327	Лестничная клетка "Г" типа Н2	17,6	
328	Кабинет материальной технологии 1-го типа	80,0	
329	Библиотечный центр, хранение: закрытый фонд с выдачей книг	41,4	В3
330	Библиотечный центр, хранение: закрытый фонд с выдачей книг	136,4	
331	Санузел для девочек (начальная школа)	12,8	
332	ПУИ	4,3	В4
333	Кабинет истории 1-го типа	52,9	
334	Кроссовая	3,9	В4
335	Кабинет индивидуальных занятий, в т.ч. с педагогом-психологом	15,0	В4
336	Коридор с зоной ожидания	193,7	
337	Коридор с зоной ожидания	55,8	
338	Кабинет географии	52,4	
339	Санузел для мальчиков (основная школа)	16,0	
	ИТОГО:	1974,4	

Условные обозначения

ШТ-1.4 — Телекоммуникационный шкаф 19" 42U напольный с указанием номера

П-п №8.1-1 — Патч-панель с указанием номера

Коммутатор на 16 портов с PoE

Источник электропитания 12В

Контроллер доступа "STR20-IP"

Модуль доступа "STR-1AP-M",встроенным ИБП

Замок электромагнитный

Извещатель охранный точечный магнитоконтактный

Считыватель электронных идентификаторов


Бесконтактная кнопка выхода

Аварийная кнопка выхода

№13 РМ-1С — Адресная метка на 4 точки с указанием номера

mun1 – одностороняя точка прохода
считыватель - кнопка "Выход"

mun2 – двухсторонняя точка прохода
считыватель - считыватель

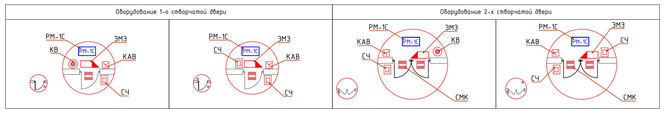

Изм.	Кол.уч.	Лист	N док.	Подпись	Дата
Разработал		Ромашов А.А.			12.2024
Зав.сектора		Ромашов А.А.			12.2024
Н. Контроль		Ромашов А.А.			12.2024
Нач.ОПиСМТ		Белоусов Д.П.			12.2024

2024-00272-00-ИОС5.8

Капитальный ремонт ГБОУ «Школа №1236 имени Героя Советского Союза Г.И.Щедрина» по адресу: г. Москва, ул. Клязьминская. д.7, корп.4

Капитальный ремонт

План 3-го этажа. М 1:100
Расположение оборудования и кабельных трасс СКУД.

Стадия	Лист	Листов
П	6	6

МОСЖИЛ НИИПРОЕКТ

Согласовано

Взам.инв. N°

Подпись и дата

Инв. N° подл.

Копировал

Формат А0

Позиция	Наименование и техническая характеристика	Тип, марка, обозначение документа, опросного листа	Код оборудования, изделия, материала	Завод-изготовитель	Единица измерения	Коли-чество	Масса единицы кг	Примечания
1	2	3	4	5	6	7	8	9
	СИСТЕМА КОНТРОЛЯ И УПРАВЛЕНИЯ ДОСТУПОМ							
	Оборудование							
1	Сетевой контроллер доступа "STR20-IP" до 8 точек, встроенное ПО	"STR20-IP"	apm.RBZ-269656	RUBEZH STRAZH	ком	20		
2	Модуль доступа-контроллер доступа STR-1AP-M на 2точки	STR 1AP-M	apm.RBZ-269662	RUBEZH STRAZH	ком	12		
	прохода, встроенный источник питания и место под АБК							
3	Модуль доступа-контроллер доступа STR-2AP-M на 4 точки	STR 2AP-M	apm.RBZ-269664	RUBEZH STRAZH	ком	15		
	прохода, встроенный источник питания и место под АБК							
4	Электромагнитный замок с монтажным комплектом	"AL-400 Premium "		Aler	ком	27		
5	Извещатель охр. магнито-контактный для металлических дверей	ИО 102-26 исп. Аякс		Магнито-Контакт	шт	38		
6	Извещатель охр. магнито-контактный для неметалл. поверхностей	ИО 102-2 СМК		Магнито-Контакт	шт	4		
7	Считыватель для установке на улице и в помещение,-40....+55гр интерфейс Wiegand 26-58, формат карт Mifare, EM-Marin,HID Prox II	RusGuard R-15 multi	код.35015	RusGuard	шт	42		
8	Кнопка экстренного выхода	ST-FR115		Телеинформсеть	шт	12		
9	Кнопка разблокировки дверей "ИПР 513-10" "АВАРИЙНЫЙ ВЫХОД"	SB 1		Рубеж	шт	27		
10	Резервный источник питания,12В	ИВЭПР 12/3,5 2х7 -Р		Рубеж	комп	2		
11	Аккумуляторная батарея 12В, 7 А/ч			Дельта	шт	22		
12	Коммутационная панель категории 5е UTP19",1U,24xRj45,п-корды	PLHD-24 Dual IDC-1U		ITK	шт.	7		
13	Горизонтальный органайзер, слотовый с крышкой, белый, 1U	MX-CMC-1U-45-B		Maxus	шт.	7		
14	Центральный прибор индикации и управления с ПО FireSec	ЦПИУ Рубеж-АРМ исп.1		Рубеж	шт.	1		
	в составе: блок системный, монитор- размер 21.5 дюйм, пульт							
	индикации и управления, блок АВР							

Согласовано:

Взам. инв. N

Подпись и дата

Инв. N подл.

Изм.	Кол.уч.	Лист	Nдок.	Подпись	Дата
Разработал		Роянцева А.А			12.2024
Зав.сектора		Роянцева А.А			12.2024
Н. Контроль		Роянцева А.А.			12.2024
Нач.ОПИС№1		Белоусова Д.П.			12.2024

2024-00272-00-ИОС5.8.СО

Капитальный ремонт ГБОУ «Школа №1236 им. Героя Советского Союза Г.И.Щедрина» по адресу: г. Москва, ул. Клязьминская. д.7, к.4
Капитальный ремонт
Спецификация оборудования, изделий и материалов

Стадия	Лист	Листов
П	1	3

МОСЖИЛ НИИПРОЕКТ

Копировал А

Позиция	Наименование и техническая характеристика	Тип, марка, обозначение документа, опросного листа	Код оборудования, изделия, материала	Завод-изготовитель	Единица измерения	Коли-чество	Масса единицы кг	Примечания
1	2	3	4	5	6	7	8	9
15	Источник бесперебойного питания	Rapan-USB 3000		ЗАО "Бастион"	шт.	1		
16	Сетевой коммутатор RVI-1NSM16G-4H 16 портов	RVI-1NSM 16G-4H	арт.2310007	RVI	комп.	7		
17	Карта Mifare стандартная	ST-PC010MF		Smartec	шт.	50		
	Кабельные изделия и материалы							
1	Кабель	КПСВВнг(А)-LSLTx -1х2х0.75мм		"Спецкабель"г.Подольск	м	290.0		
2	Кабель	КПСВВнг(А)-LSLTx -1х2х1.0мм		"Спецкабель"г.Подольск	м	80.0		
3	Кабель	ЛОУТОКС 20нг(А)-FRLSLTx -1х2х0.5		"Спецкабель"г.Подольск	м	100.0		
4	Кабель	U/UTPнг(А)-LSLTx-4х2х0.52 кат.5е		ПТД "Паритет"	м	900.0		
5	Кабель	ВВГнг(А)-LSLTx -1х2х1.5мм		"Спецкабель"г.Подольск	м	450.0		
6	Труба гофрированная гибкая ПВХ-20мм			ДКС	м	870,0		
7	Труба гофрированная гибкая ПВХ-16мм			ДКС	м	470,0		
8	Гидроизоляционная огнеупорная мастика	АМ-05		Россия	кг	1,0		

Согласовано:

Взам. инв. N

Подпись и дата

Инв. N подл.

Изм.	Кол.уч.	Лист	N док.	Подпись	Дата	2024-00272-00-ИОС5.8.СО	лист 2

Формат А3

Позиция	Наименование и техническая характеристика	Тип, марка, обозначение документа, опросного листа	Код оборудования, изделия, материала	Завод-изготовитель	Единица измерения	Коли-чество	Масса единицы кг	Примечания
1	2	3	4	5	6	7	8	9
	ВИДЕОДОМОФОН							
	Оборудование							
1	Монитор IP-видеодомофона 4.3" SIP протокол ,PoE, ОС Linux	SM-400W		ПП Бевард	шт	1		
	с поддержкой подключения IP-вызывных панелей и IP-камер.							
2	Вызывная Full HD IP-панель для видеодомофонов	DS06AP		ПП Бевард	шт	7		
	с углом обзора 146° врезной установки.							
	Кабельные изделия и материалы							
3	Кабель "витая пара" негорючий с низким выделением газа,дыма.	КПСВВнг(А)-LSLTx -4х2х0.5мм		"Спецкабель"г.Подольск	м	420.0		
4	Кабель электрический негорючий с низким выделением газа,дыма.	ВВГнг(А)-LSLTx -1х2х1.5мм		"Спецкабель"г.Подольск	м	20.0		
5	Труба гофрированная самозатухающая «ТГ ПВХ» 20 мм		RTK-2-5-02	RTK	м	440,0		
6	Патч-корд RJ45, cat.5e, 1.0м					9		

НОПРИЗ
НАЦИОНАЛЬНОЕ ОБЪЕДИНЕНИЕ ИЗЫСКАТЕЛЕЙ И ПРОЕКТИРОВЩИКОВ

АССОЦИАЦИЯ САМОРЕГУЛИРУЕМЫХ ОРГАНИЗАЦИЙ ОБЩЕРОССИЙСКАЯ НЕГОСУДАРСТВЕННАЯ НЕКОММЕРЧЕСКАЯ ОРГАНИЗАЦИЯ – ОБЩЕРОССИЙСКОЕ МЕЖОТРАСЛЕВОЕ ОБЪЕДИНЕНИЕ РАБОТОДАТЕЛЕЙ «НАЦИОНАЛЬНОЕ ОБЪЕДИНЕНИЕ САМОРЕГУЛИРУЕМЫХ ОРГАНИЗАЦИЙ, ОСНОВАННЫХ НА ЧЛЕНСТВЕ ЛИЦ, ВЫПОЛНЯЮЩИХ ИНЖЕНЕРНЫЕ ИЗЫСКАНИЯ, И САМОРЕГУЛИРУЕМЫХ ОРГАНИЗАЦИЙ, ОСНОВАННЫХ НА ЧЛЕНСТВЕ ЛИЦ, ОСУЩЕСТВЛЯЮЩИХ ПОДГОТОВКУ ПРОЕКТНОЙ ДОКУМЕНТАЦИИ»

9710075487-20241024-1105
(регистрационный номер выписки)

24.10.2024
(дата формирования выписки)

ВЫПИСКА
из единого реестра сведений о членах саморегулируемых организаций в области инженерных изысканий и в области архитектурно-строительного проектирования и их обязательствах

Настоящая выписка содержит сведения о юридическом лице (индивидуальном предпринимателе), осуществляющем подготовку проектной документации:

Государственное автономное учреждение города Москвы Московский научно-исследовательский и проектный институт жилищного хозяйства «МосжилНИИпроект»
(полное наименование юридического лица/ФИО индивидуального предпринимателя)

1197746303204
(основной государственный регистрационный номер)

1. Сведения о члене саморегулируемой организации:		
1.1	Идентификационный номер налогоплательщика	9710075487
1.2	Полное наименование юридического лица (Фамилия Имя Отчество индивидуального предпринимателя)	Государственное автономное учреждение города Москвы Московский научно-исследовательский и проектный институт жилищного хозяйства «МосжилНИИпроект»
1.3	Сокращенное наименование юридического лица	ГАУ «МосжилНИИпроект»
1.4	Адрес юридического лица Место фактического осуществления деятельности (для индивидуального предпринимателя)	107078, Россия, Москва, г. Москва, Каланчевская, 4/2, 1, -
1.5	Является членом саморегулируемой организации	Ассоциация проектировщиков инженерной инфраструктуры «Инфрадизайн» (СРО-П-218-15012021)
1.6	Регистрационный номер члена саморегулируемой организации	П-218-009710075487-0095
1.7	Дата вступления в силу решения о приеме в члены саморегулируемой организации	18.06.2021
1.8	Дата и номер решения об исключении из членов саморегулируемой организации, основания исключения	

2. Сведения о наличии у члена саморегулируемой организации права осуществлять подготовку проектной документации:		
2.1 в отношении объектов капитального строительства (кроме особо опасных, технически сложных и уникальных объектов, объектов использования атомной энергии) (дата возникновения/изменения права)	2.2 в отношении особо опасных, технически сложных и уникальных объектов капитального строительства (кроме объектов использования атомной энергии) (дата возникновения/изменения права)	2.3 в отношении объектов использования атомной энергии (дата возникновения/изменения права)
Да, 18.06.2021	Нет	Нет

3. Компенсационный фонд возмещения вреда		
3.1	Уровень ответственности члена саморегулируемой организации по обязательствам по договору подряда на подготовку проектной документации, в соответствии с которым указанным членом внесен взнос в компенсационный фонд возмещения вреда	**Третий уровень ответственности (не превышает триста миллионов рублей)**
3.2	Сведения о приостановлении / прекращении права осуществлять подготовку проектной документации объектов капитального строительства	
4. Компенсационный фонд обеспечения договорных обязательств		
4.1	Дата, с которой член саморегулируемой организации имеет право осуществлять подготовку проектной документации по договорам подряда, заключаемым с использованием конкурентных способов заключения договоров, в соответствии с которым указанным членом внесен взнос в компенсационный фонд обеспечения договорных обязательств	**18.06.2021**
4.2	Уровень ответственности члена саморегулируемой организации по обязательствам по договорам подряда на подготовку проектной документации, заключаемым с использованием конкурентных способов заключения договоров, в соответствии с которым указанным членом внесен взнос в компенсационный фонд обеспечения договорных обязательств	**Четвертый уровень ответственности (составляет триста миллионов рублей и более)**
4.3	Дата уплаты дополнительного взноса	**Нет**
4.4	Сведения о приостановлении / прекращении права осуществлять подготовку проектной документации по договорам подряда, заключаемым с использованием конкурентных способов заключения договоров	
5. Фактический совокупный размер обязательств		
5.1	Фактический совокупный размер обязательств по договорам подряда на подготовку проектной документации, заключаемым с использованием конкурентных способов заключения договоров на дату выдачи выписки	**Нет**

Руководитель аппарата

НОПРИЗ

ДОКУМЕНТ ПОДПИСАН УСИЛЕННОЙ КВАЛИФИЦИРОВАННОЙ ЭЛЕКТРОННОЙ ПОДПИСЬЮ

Владелец: Кожуховский Алексей Олегович

123056, г. Москва, ул. 2-я Брестская, д. 5

СЕРТИФИКАТ 0402FE9100C0B0148D4019113D8DEA876F

ДЕЙСТВИТЕЛЕН: С 20.11.2023 ПО 20.11.2024

А.О. Кожуховский

НОПРИЗ
НАЦИОНАЛЬНОЕ ОБЪЕДИНЕНИЕ ИЗЫСКАТЕЛЕЙ И ПРОЕКТИРОВЩИКОВ

АССОЦИАЦИЯ САМОРЕГУЛИРУЕМЫХ ОРГАНИЗАЦИЙ ОБЩЕРОССИЙСКАЯ НЕГОСУДАРСТВЕННАЯ НЕКОММЕРЧЕСКАЯ ОРГАНИЗАЦИЯ – ОБЩЕРОССИЙСКОЕ МЕЖОТРАСЛЕВОЕ ОБЪЕДИНЕНИЕ РАБОТОДАТЕЛЕЙ «НАЦИОНАЛЬНОЕ ОБЪЕДИНЕНИЕ САМОРЕГУЛИРУЕМЫХ ОРГАНИЗАЦИЙ, ОСНОВАННЫХ НА ЧЛЕНСТВЕ ЛИЦ, ВЫПОЛНЯЮЩИХ ИНЖЕНЕРНЫЕ ИЗЫСКАНИЯ, И САМОРЕГУЛИРУЕМЫХ ОРГАНИЗАЦИЙ, ОСНОВАННЫХ НА ЧЛЕНСТВЕ ЛИЦ, ОСУЩЕСТВЛЯЮЩИХ ПОДГОТОВКУ ПРОЕКТНОЙ ДОКУМЕНТАЦИИ»

9710075487-20241024-1103
(регистрационный номер выписки)

24.10.2024
(дата формирования выписки)

ВЫПИСКА
из единого реестра сведений о членах саморегулируемых организаций в области инженерных изысканий и в области архитектурно-строительного проектирования и их обязательствах

Настоящая выписка содержит сведения о юридическом лице (индивидуальном предпринимателе), выполняющем инженерные изыскания:

Государственное автономное учреждение города Москвы Московский научно-исследовательский и проектный институт жилищного хозяйства "МосжилНИИпроект"
(полное наименование юридического лица/ФИО индивидуального предпринимателя)

1197746303204
(основной государственный регистрационный номер)

1. Сведения о члене саморегулируемой организации:		
1.1	Идентификационный номер налогоплательщика	9710075487
1.2	Полное наименование юридического лица (Фамилия Имя Отчество индивидуального предпринимателя)	Государственное автономное учреждение города Москвы Московский научно-исследовательский и проектный институт жилищного хозяйства "МосжилНИИпроект"
1.3	Сокращенное наименование юридического лица	ГАУ "МосжилНИИпроект"
1.4	Адрес юридического лица Место фактического осуществления деятельности (для индивидуального предпринимателя)	107078, Россия, Москва, вн.тер.г. муниципальный округ Красносельский, ул. Каланчевская, д. 4/2, стр. 1
1.5	Является членом саморегулируемой организации	Ассоциация саморегулируемая организация «Центральное объединение организаций по инженерным изысканиям для строительства «Центризыскания» (СРО-И-003-14092009)
1.6	Регистрационный номер члена саморегулируемой организации	И-003-009710075487-0097
1.7	Дата вступления в силу решения о приеме в члены саморегулируемой организации	14.10.2009
1.8	Дата и номер решения об исключении из членов саморегулируемой организации, основания исключения	

2. Сведения о наличии у члена саморегулируемой организации права выполнять инженерные изыскания:		
2.1 в отношении объектов капитального строительства (кроме особо опасных, технически сложных и уникальных объектов, объектов использования атомной энергии) (дата возникновения/изменения права)	2.2 в отношении особо опасных, технически сложных и уникальных объектов капитального строительства (кроме объектов использования атомной энергии) (дата возникновения/изменения права)	2.3 в отношении объектов использования атомной энергии (дата возникновения/изменения права)
Да, 14.10.2009	Да, 28.06.2023	Нет

3. Компенсационный фонд возмещения вреда		
3.1	Уровень ответственности члена саморегулируемой организации по обязательствам по договору подряда на выполнение инженерных изысканий, в соответствии с которым указанным членом внесен взнос в компенсационный фонд возмещения вреда	**Третий уровень ответственности (не превышает триста миллионов рублей)**
3.2	Сведения о приостановлении права выполнять инженерные изыскания объектов капитального строительства	
4. Компенсационный фонд обеспечения договорных обязательств		
4.1	Дата, с которой член саморегулируемой организации имеет право выполнять инженерные изыскания по договорам подряда, заключаемым с использованием конкурентных способов заключения договоров, в соответствии с которым указанным членом внесен взнос в компенсационный фонд обеспечения договорных обязательств	**01.07.2017**
4.2	Уровень ответственности члена саморегулируемой организации по обязательствам по договорам подряда на выполнение инженерных изысканий, заключаемым с использованием конкурентных способов заключения договоров, в соответствии с которым указанным членом внесен взнос в компенсационный фонд обеспечения договорных обязательств	**Третий уровень ответственности (не превышает триста миллионов рублей)**
4.3	Дата уплаты дополнительного взноса	**07.03.2019**
4.4	Сведения о приостановлении права выполнять инженерные изыскания по договорам подряда, заключаемым с использованием конкурентных способов заключения договоров	
5. Фактический совокупный размер обязательств		
5.1	Фактический совокупный размер обязательств по договорам подряда на выполнение инженерных изысканий, заключаемым с использованием конкурентных способов заключения договоров на дату выдачи выписки	**Нет**

Руководитель аппарата

НОПРИЗ

ДОКУМЕНТ ПОДПИСАН УСИЛЕННОЙ КВАЛИФИЦИРОВАННОЙ ЭЛЕКТРОННОЙ ПОДПИСЬЮ

Владелец: Кожуховский Алексей Олегович

123056, г. Москва, ул. 2-я Брестская, д. 5

СЕРТИФИКАТ 0402FE9100C0B0148D4019113D8DEA876F

ДЕЙСТВИТЕЛЕН: С 20.11.2023 ПО 20.11.2024

А.О. Кожуховский