Департамент капитального ремонта города Москвы Государственное автономное учреждение города Москвы Московский научно-исследовательский и проектный институт жилищного хозяйства «МосжилНИИпроект» (ГАУ «МосжилНИИпроект»)

mgnp@mgnp.mos.ru +7 495 624 40 65 107078, г. Москва, ул. Каланчевская, д. 4/2, стр. 1

Арх. №

Капитальный ремонт объекта Государственного бюджетного общеобразовательного учреждения города Москвы «Школа № 1574 по адресу: г. Москва, пер. Старопименовский, д. 5»

ПРОЕКТНАЯ ДОКУМЕНТАЦИЯ

Раздел 5. «Сведения об инженерном оборудовании, о сетях и системах инженерно-технического обеспечения»
Подраздел 5. «Сети связи»
Часть 10. Система двусторонней связи

2024-00375-01-0-ИОС5.10

Том 5.5.10

2024

Департамент капитального ремонта города Москвы Государственное автономное учреждение города Москвы Московский научно-исследовательский и проектный институт жилищного хозяйства «МосжилНИИпроект» (ГАУ «МосжилНИИпроект»)

mgnp@mgnp.mos.ru +7 495 624 40 65 107078, г. Москва,ул.Каланчевская, д. 4/2, стр. 1

Арх. №

Капитальный ремонт объекта Государственного бюджетного общеобразовательного учреждения города Москвы «Школа № 1574 по адресу: г. Москва, пер. Старопименовский, д. 5»

ПРОЕКТНАЯ ДОКУМЕНТАЦИЯ

Раздел 5. «Сведения об инженерном оборудовании, о сетях и системах инженерно-технического обеспечения»
Подраздел 5. «Сети связи»
Часть 10. Система двусторонней связи

2024-00375-01-0-ИОС5.10

Том 5.5.10

1 этап

Заместитель директора Н.Р. Нигматулин

30.11.24

Главный инженер проекта Н.М. Пильгуй

30.11.24

2024

СОДЕРЖАНИЕ ТОМА

Обозначение	Наименование	Примечание
	Текстовая часть	
2024-00375-01-0-ИОС5.10.С	Содержание тома	2
2024-00375-01-0-ИОС5.10	Справка ГИПа	3
2024-00375-01-0-ИОС5.10.ПЗ	Пояснительная записка	4-8
	Графическая часть	
2024-00375-01-0-ИОС5.10	Условные обозначения	9
2024-00375-01-0-ИОС5.10	Принципиальная схема	10
2024-00375-01-0-ИОС5.10	План расположения оборудования и прокладки кабельных трасс. Подвал.	11
2024-00375-01-0-ИОС5.10	План расположения оборудования и прокладки кабельных трасс. Первый этаж.	12
2024-00375-01-0-ИОС5.10	План расположения оборудования и прокладки кабельных трасс. Второй этаж.	13
2024-00375-01-0-ИОС5.10	План расположения оборудования и прокладки кабельных трасс. Третий этаж.	14
2024-00375-01-0-ИОС5.10	План расположения оборудования и прокладки кабельных трасс. Четвертый этаж.	15
2024-00375-01-0-ИОС5.10	План расположения оборудования и прокладки кабельных трасс. Пятый этаж.	16
	Прилагаемые документы	
2024-00375-01-0-ИОС5.10.С1	Спецификация оборудования и материалов	17-18
2024-00375-01-0-ИОС5.10.ТЗ-ЭОМ	Задание на электроснабжение	19

СПРАВКА ГИПа

Проектная документация разработана в соответствии с заданием на проектирование, градостроительным регламентом, техническими регламентами, требованиями экологических, санитарно-гигиенических, противопожарных и других норм, действующих на территории Российской Федерации, и обеспечивают безопасную для жизни и здоровья людей эксплуатацию объекта при соблюдении предусмотренных проектом мероприятий.

Главный инженер проекта  Н.М. Пильгуй

						2024-00375-01-0-ИОС5.10		
Изм.	Кол.	Лист	№док	Подп.	Дата			
Разработал		Ветлицкая			11.24	Справка ГИПа	Стадия	Лист	Листов
Проверил		Щипин			11.24		П		1
							МОСЖИЛ НИИПРОЕКТ	
Н. контрол.		Исаев			11.24				
ГИП		Пильгуй			11.24				

ПОЯСНИТЕЛЬНАЯ ЗАПИСКА

1. ОБЩАЯ ЧАСТЬ

1.1. Наименование работ

Капитальный ремонт здания Государственного бюджетного общеобразовательного учреждения города Москвы «Школа № 1574 по адресу: г. Москва, пер. Старопименовский, д. 5»

1.2 Основание для разработки

Основаниями для разработки проектной документации являются:

– задание на проектирование;

– архитектурно-строительные чертежи.

При разработке раздела учтены требования следующих нормативных документов:

Обозначение	Наименование	Примечание
Ссылочные документы		
Постановление № 87 от 16.02.2008	О составе разделов проектной документации и требованиях к их содержанию.	
ГОСТ Р 21.101-2020	Система проектной документации для строительства. Основные требования к проектной и рабочей документации.	
ГОСТ 21.406-88 (2002)	Проводные средства связи. Обозначения условные графические на схемах и планах.	
СП 3.13130.2009	Свод правил. Системы противопожарной защиты. Система оповещения и управления эвакуацией людей при пожаре. Требования пожарной безопасности"	
СП 59.13330.2020	Доступность зданий и сооружений для маломобильных групп населения. Актуализированная редакция СНиП 35-01-2001	
СП 132.13330.2020	Свод правил. Обеспечение антитеррористической защищенности зданий и сооружений. Общие требования проектирования"	
ПУЭ (издание 7)	Правила устройства электроустановок.	

Правила	Правила строительства и ремонта воздушных линий связи и радиотрансляционных сетей.	

2. ХАРАКТЕРИСТИКА ОБЪЕКТА

Пятиэтажное здание школы с подвалом. На объекте предусмотрено:

– один пост охраны с двумя диспетчерскими пультами, расположенными в пом. 122;

– один въездной пандус для маломобильных групп населения (МГН);

– санузел для МГН, расположенный в пом. № 121.

На объекте имеются помещения с массовым пребыванием людей (50 человек и более): зал ЛФК (пом. 010), гардероб (пом.103), обеденный зал (пом. 131), спортивный зал (пом. 220), актовый зал (пом. 206), многофункциональный информационный библиотечный центр (пом. 312).

3. СИСТЕМА ДВУСТОРОННЕЙ СВЯЗИ

3.1. Назначение системы

Проектируемая система двусторонней связи предназначена для решения следующих задач.

1. Обеспечение обратной связи зон пожарного оповещения с помещением пожарного поста (диспетчерской) во исполнение выполнения требований табл.1 СП 3.13130.2009 к СОУЭ 4-го типа, которая принята в разделе проекта 2024-00375-01-0-ИОС5.2.
2. Организация двусторонней связи для маломобильных групп населения (МГН) в соответствии с требованиями СП 59.13330.2020.
3. Обеспечение системой экстренной связи с постом охраны всех входов в здание и мест пребывания людей численностью более 50 человек в одном из помещений в соответствии с требованиями СП 132.13330.2020.

3.2. Мероприятия по обеспечению здания двусторонней связью

Для обеспечения обратной связи зон пожарного оповещения предусмотрена:

– установка абонентских переговорных устройств на путях эвакуации (подвал, 1-5 этажи);

– вывод сигналов с абонентских переговорных устройств в ближайшую комнату охраны с диспетчерским пунктом (пом. 122).

Для обеспечения двусторонней связи МГН проектом предусмотрена двусторонняя связь между комнатой охраны с диспетчерскими пунктами, расположенной в пом. 122, и следующими местами:

– специализированным сан. узлом для МГН в пом. 121;

– пандусом для МГН.

Сан. узел для МГН (пом. 121) оборудован абонентским переговорным устройством, а также устройством вызова со шнуром. В нижней и в верхней части пандусов для МГН предусмотрены абонентские переговорные устройства.

Для организации системы экстренной связи проектом принята:

– установка рядом со всеми входами в здание абонентских переговорных устройств;

– установка абонентских переговорных устройств в помещениях с массовым пребыванием людей;

– вывод сигналов с упомянутых выше абонентских переговорных устройств в ближайшую комнату охраны с диспетчерскими пунктами (пом.122).

Все виды двусторонней связи в здании выводятся на единые пульты, расположенные в комнате охраны с диспетчерскими пунктами (пом. 122).

3.3. Оборудование, применяемое в системе

В системе используется следующее основное оборудование:

– пульт диспетчера AN-CO32;

– блок коммутации AN-X8 и AN-X8MGN;

– абонентское переговорное устройство AN-BR1, AN-BG-WP, AN-BG1;

– устройство вызова AL-RB;

– устройство отмены вызова AL-CB;

– светозвуковой сигнализатор AL-DI;

– резервированный источник питания РИП-24 исп. 01.

3.4. Размещение оборудования

На первом этаже в помещении № 122 устанавливается пульт диспетчера AN-CO32, блоки коммутации AN-X8, AN-X8MGN и резервированный источники питания РИП-24 исп. 01.

Абонентские переговорные устройства модели AN-BR1 установить на путях эвакуации и в с.у. МГН. В местах массового пребывания людей установить модели AN-BG1,

на стойках около въездного пандуса установить модели AN-BG-WP. С/у для МГН дополнительно оборудовать устройством вызова AL-RB, устройством отмены вызова AL-CB и светозвуковым сигнализатором AL-DI (с внешней стороны в коридоре).

Переговорные устройства AN-BG-WP (для МГН) установить на высоте 1 метр.

Переговорные устройства AN-BR1, AN-BG1 установить на высоте 1,4 метра.

Переговорные устройства AN-BR1 (в с/у МГН) установить на высоте 1 метр.

Переговорные устройства AN-BR1 установить на высоте 1,4 метра.

Проводные кнопки вызова со шнуром AL-RB установить на высоте 0,6-0,8 метр.

Устройство отмены вызова AL-CB установить на высоте 1,1 метр.

4. ПРОКЛАДКА КАБЕЛЬНЫХ ТРАСС

Кабели связи для обеспечения обратной связи зон пожарного оповещения прокладывать отдельно от прочих систем, и крепить при помощи металлических держателей.


Организация кабельных линий связи предусматривается с использованием огнестойких кабелей, не распространяющих горение при групповой прокладке, с низкими показателями дымо и газовыделениями при горении и тлении, с низкими показателями токсичности продуктов горения (исполнение - нг(А)-FRLSLTx). Кабели выбраны с учетом требования табл. 2 ГОСТ31565-2012.

Кабельные линии систем противопожарной защиты и способы их прокладки, в соответствии с требованиями ч. 2 ст. 82 123-ФЗ, обеспечивают работоспособность в условиях пожара в течение времени, необходимого для выполнения их функций, посредством:

– применения кабелей исполнения нг(А)-FRLSLTx (ГОСТ 31565-2012 Кабельные изделия. Требования пожарной безопасности);

– применения сертифицированных решений (ГОСТ Р 53316-2021 Кабельные линии. Сохранение работоспособности в условиях пожара).

В соответствии с требованиями п.5.2.4 СП 2.13130.2020, места пересечения кабелей, кабеленесущих конструкций со строительными конструкциями с нормируемыми пределами огнестойкости, обеспечиваются проходками не ниже пределов огнестойкости, установленных для пересекаемых конструкций посредством заполнения пеной однокомпонентной огнезащитной в соответствии с ГОСТ 30247.1, ГОСТ Р 53306, ГОСТ Р 53310.

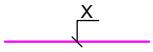Условные обозначения	
Обозначение	Наименование
	Пульт диспетчера AN-CO32 + комплектный кросс-блок
	Блок коммутации AN-X8
	Блок коммутации AN-X8MGN
	Абонентское переговорное устройство AN-BG1, с лицевой панелью зеленого цвета для встроенного монтажа (для СЭС)
	Абонентское переговорное устройство AN-BG-WP, с лицевой панелью зеленого цвета для поверхностного монтажа и защитой IP65 (для МГН)
	Абонентское переговорное устройство AN-BR1, с лицевой панелью красного цвета для встроенного монтажа (для СОУЭ, с/у МГН, СЭС)
	Светозвуковой сигнализатор AL-DI
	Устройство отмены вызова AL-CB
	Устройство вызова AL-RB
	Резервированный источник питания РИП-24 исп. 01
	Витая пара ParLan F/UTP Cat5e PVCLS нг(A)-FRLSLTx 4x2x0,52
	Витая пара ParLan F/UTP Cat5e PVCLS нг(A)-FRLSLTx 4x2x0,52 (групповая прокладка с указанием количества)
	Кабель КСРВнг(A)-FRLSLTx 1x2x0,97
	Места соединения кабелей
	Переход кабельной трассы вверх
	Подъем кабельной трассы снизу
	Опуск кабельной трассы сверху
	Опуск кабельной трассы вниз

Согласовано

Взам. инв. №


Подп. и дата

Инв. № подл.

						2024-00375-01-0-ИОС5.10		
						Здание государственного бюджетного общеобразовательного учреждения города Москвы "Школа № № 1574", расположенное по адресу: г. Москва, пер. Старопименовский, д. 5		
Изм.	Кол. уч	Лист	N док.	Подп.	Дата			
Разработал		Ветлицкая			11.24	Капитальный ремонт	Стадия	Лист	Листов
Проверил		Щипин			11.24		П		1
Н. Контр.		Исаев			11.24	Условные обозначения	МОСЖИЛ НИИПРОЕКТ		
ГИП		Пильгуй			11.24				

Копировал

Формат А4

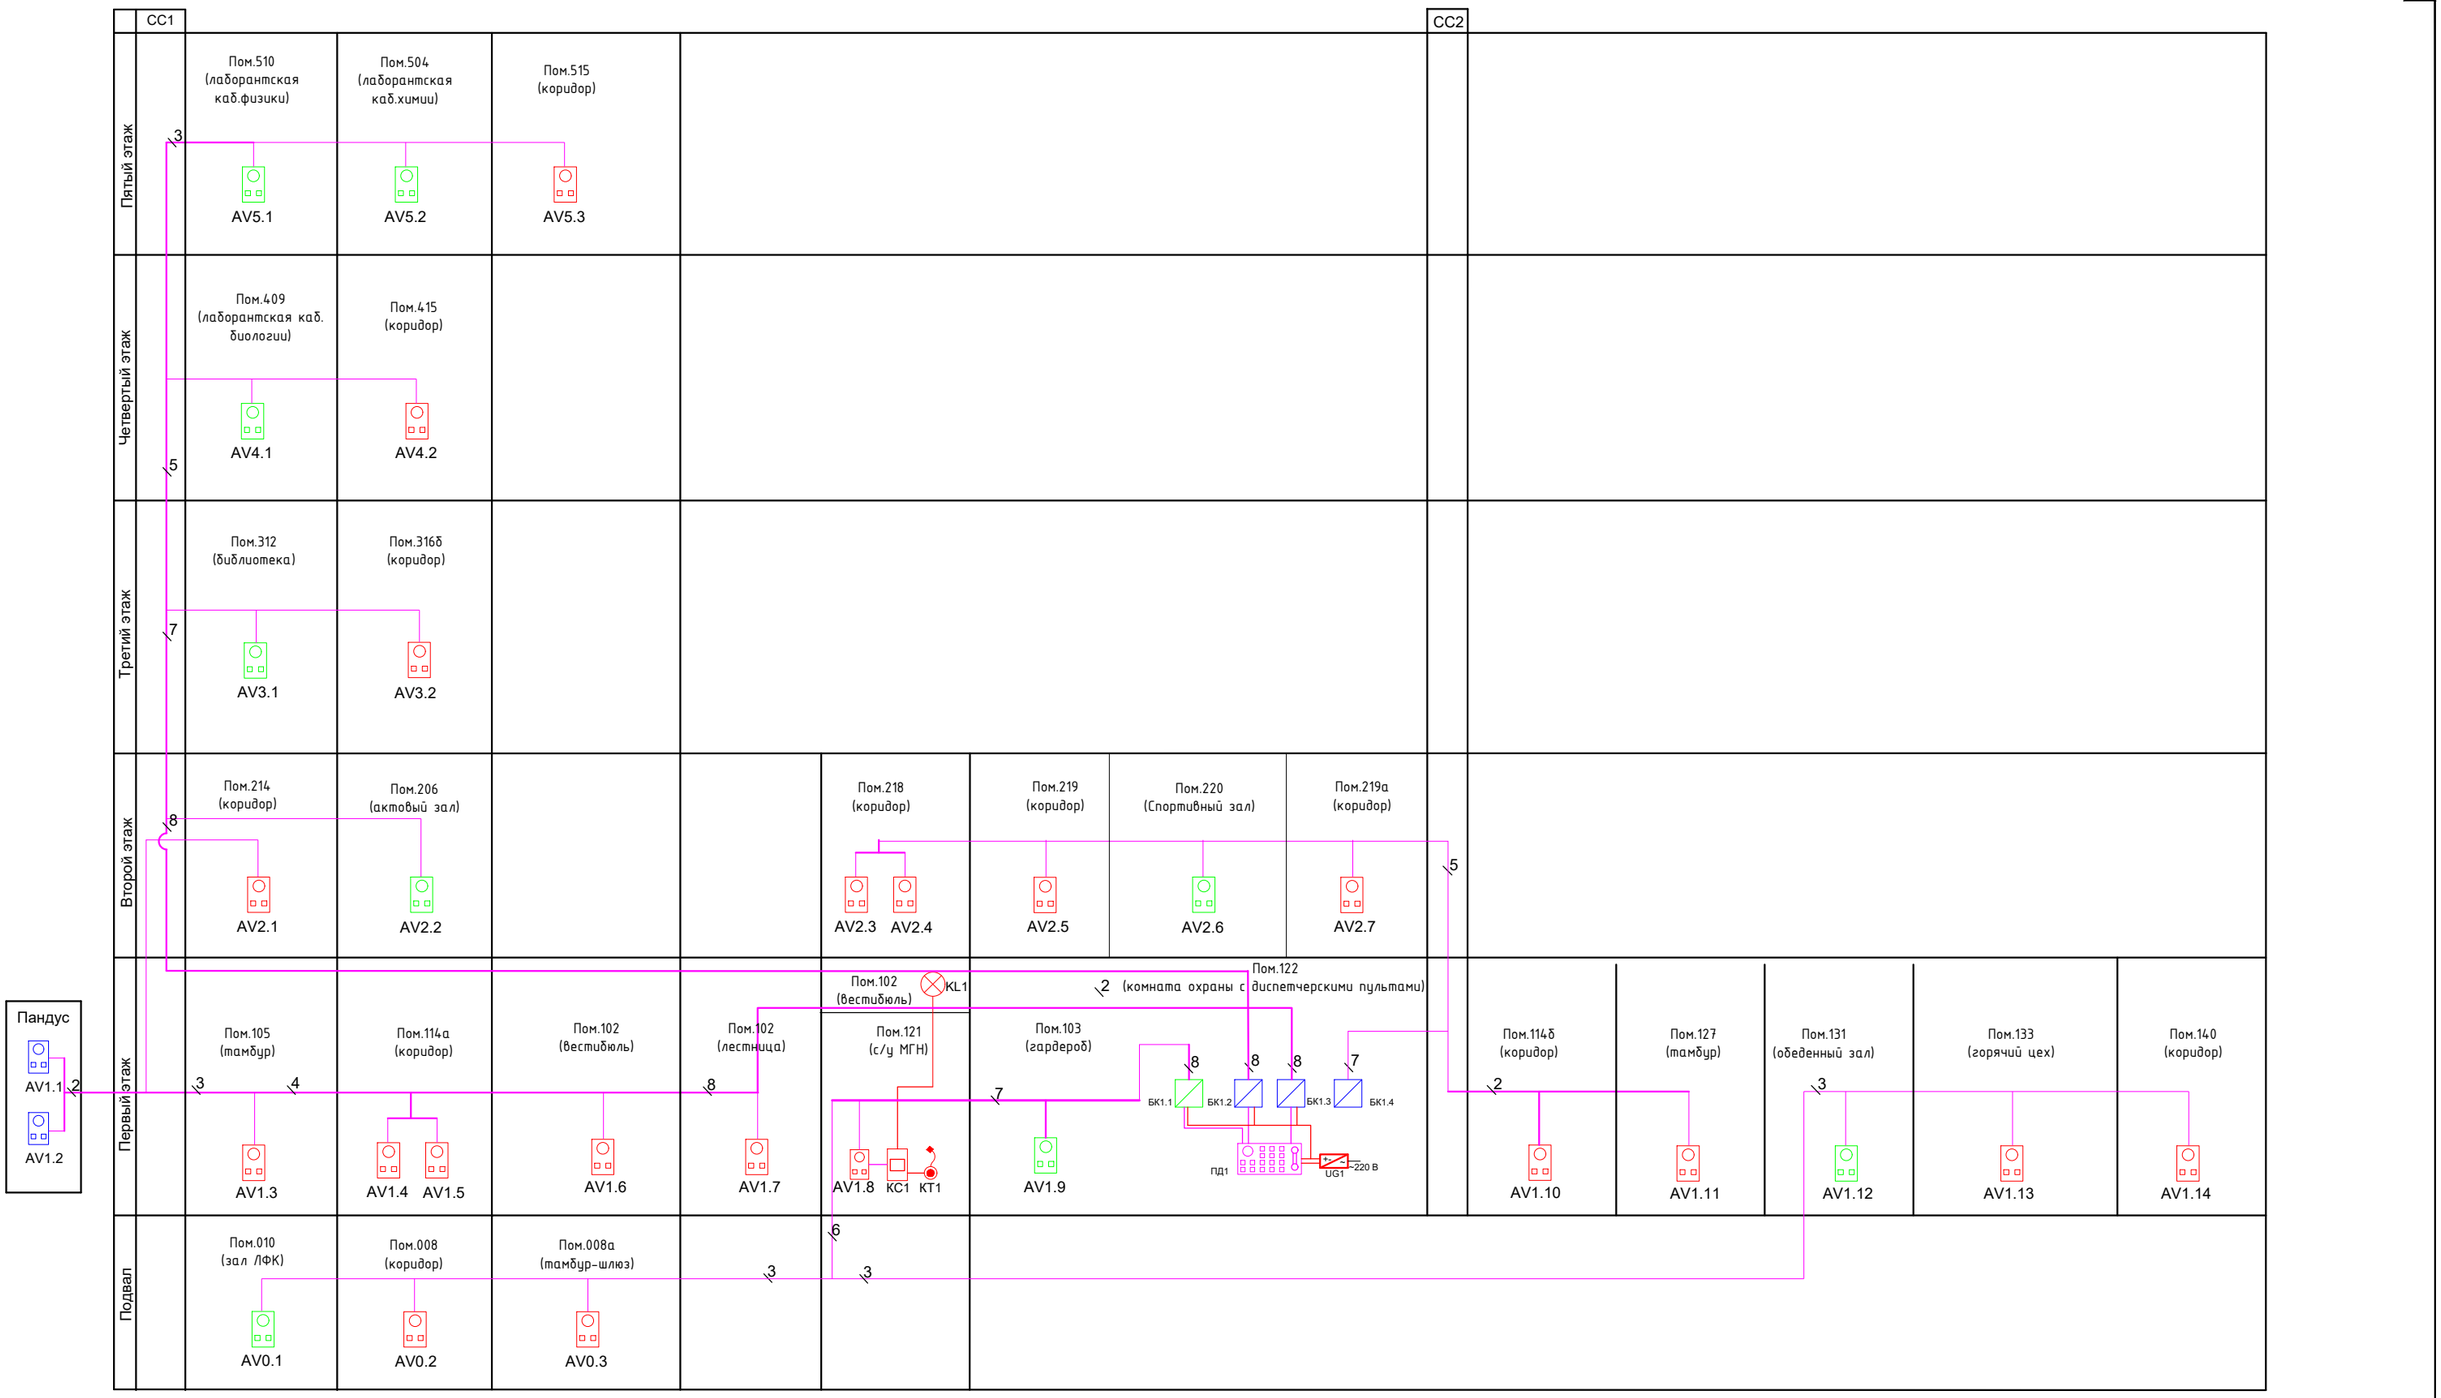

Согласовано

Взам. инв. №

Подп. и дата

Инв. № подл.

Изм.	Кол. уч	Лист	N док.	Подп.	Дата
Разработал		Ветлицкая			11.24
Проверил		Щипин			11.24
Н. Контр.		Исаев			11.24
ГИП		Пильгуй			11.24

2024-00375-01-0-ИОС 5.10

Здание государственного бюджетного общеобразовательного учреждения города Москвы "Школа № № 1574", расположенное по адресу: г. Москва, пер. Старопименовский, д. 5

Капитальный ремонт


Стадия	Лист	Листов
П		1

Принципиальная схема

МОСЖИЛ НИИПРОЕКТ

Копировал

Формат А3 альбомный

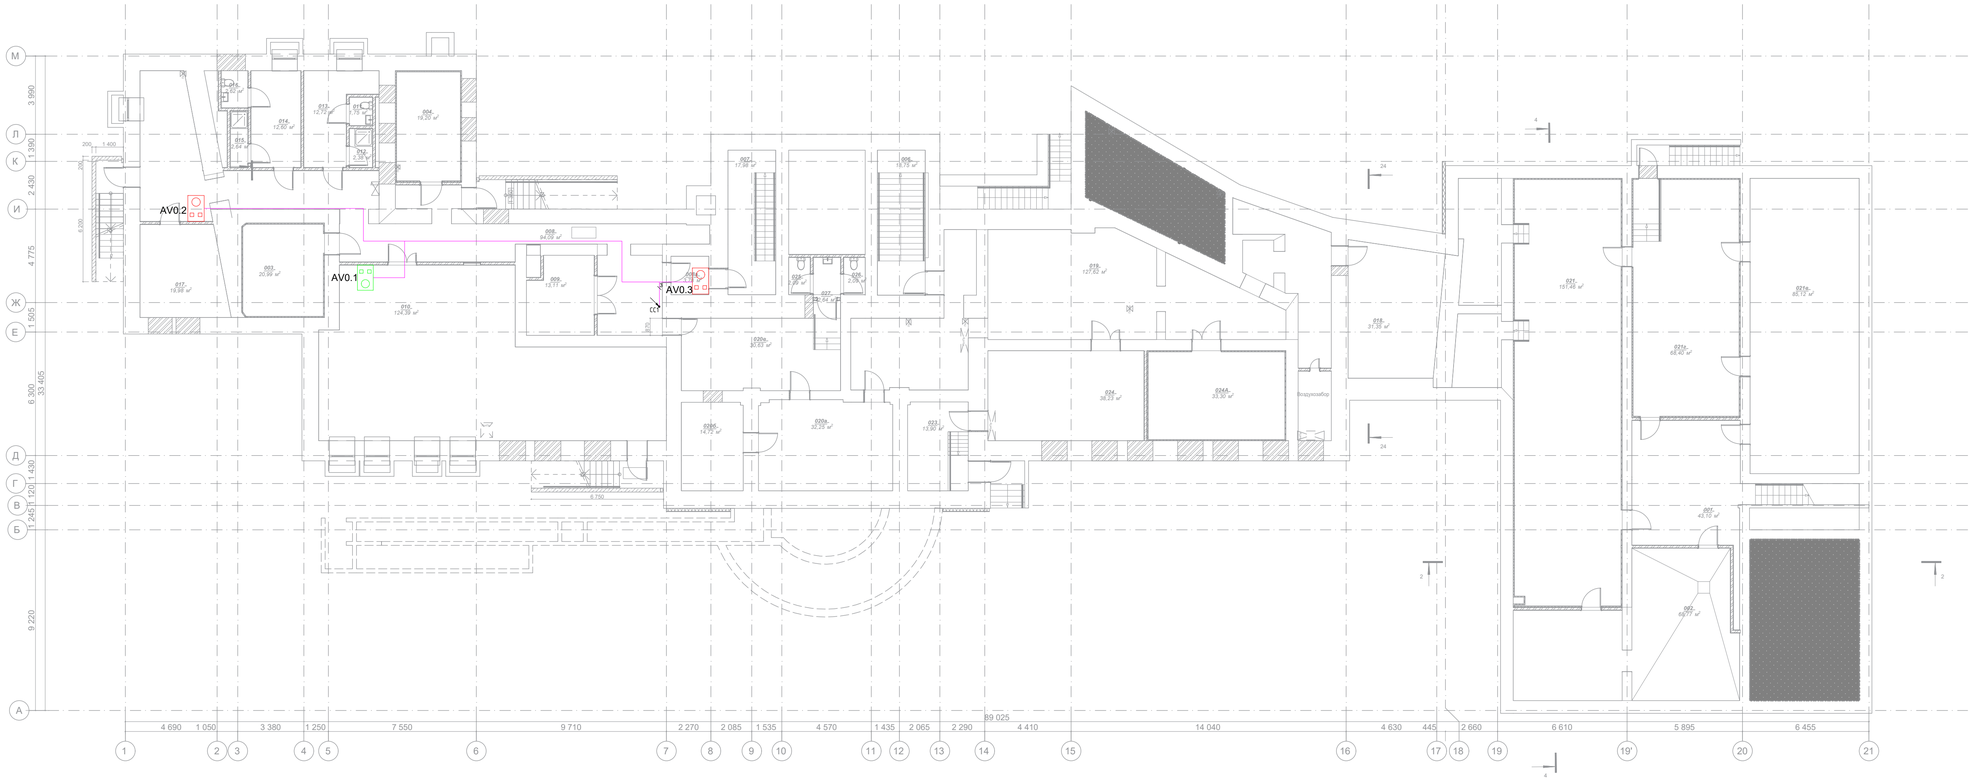

Экспликация помещений подвального этажа

Номер помещения	Наименование	Площадь, м2	Кат. помещения
001	Лестничная клетка	43,10	
002	ИТП	68,77	В4
003	Венткамера	20,99	В4
004	Венткамера	19,20	В4
006	Лестничная клетка тип Л1	18,75	
007	Технологическая лестница	17,98	
008	Коридор	94,09	
008а	Тамбур-шлюз	3,78	
009	Снарядная	13,11	В3
010	Зал ЛФК	124,39	
011	Санузел	1,75	
012	Душевая	2,38	
013	Раздевальная (не более 5 чел)	12,72	
014	Раздевальная (не более 5 чел)	12,60	
015	Душевая	2,64	
016	Санузел	2,62	
017	Электрощитовая	19,98	В3
018	Подсобное помещение	31,35	В3
019	Коридор	127,62	
020а	Коридор	32,25	
020б	Помещение для прокладки коммуникаций	14,72	В4
020в	Коридор	30,63	
021	Венткамера	151,46	В4
021в	Помещение для прокладки коммуникаций	85,12	В4
021г	Венткамера	68,40	В3
023	Узел ввода	13,90	Д
024	Насосная	38,23	Д
024А	Венткамера	33,30	В4
025	Санузел	2,09	
026	Санузел	2,09	
027	Умывальная	2,64	
		1 112,65 м²	

Согласовано

Взам. инв. №

Подп. и дата

Инв. № подл.

Изм.	Кол. уч.	Лист	N док.	Подп.	Дата
Разработал		Ветлицкая			11.24
Проверил		Щипин			11.24
Н. Контр.		Исаев			11.24
ГИП		Пильгуй			11.24

2024-00375-01-0-ИОС5.10

Здание государственного бюджетного общеобразовательного учреждения города Москвы "Школа № № 1574", расположенное по адресу: г. Москва, пер. Старопименовский, д. 5

Капитальный ремонт


Стадия	Лист	Листов
П		1

План расположения оборудования и прокладки кабельных трасс. Подвал

МОСЖИЛ НИИПРОЕКТ

Копировал

Формат А1

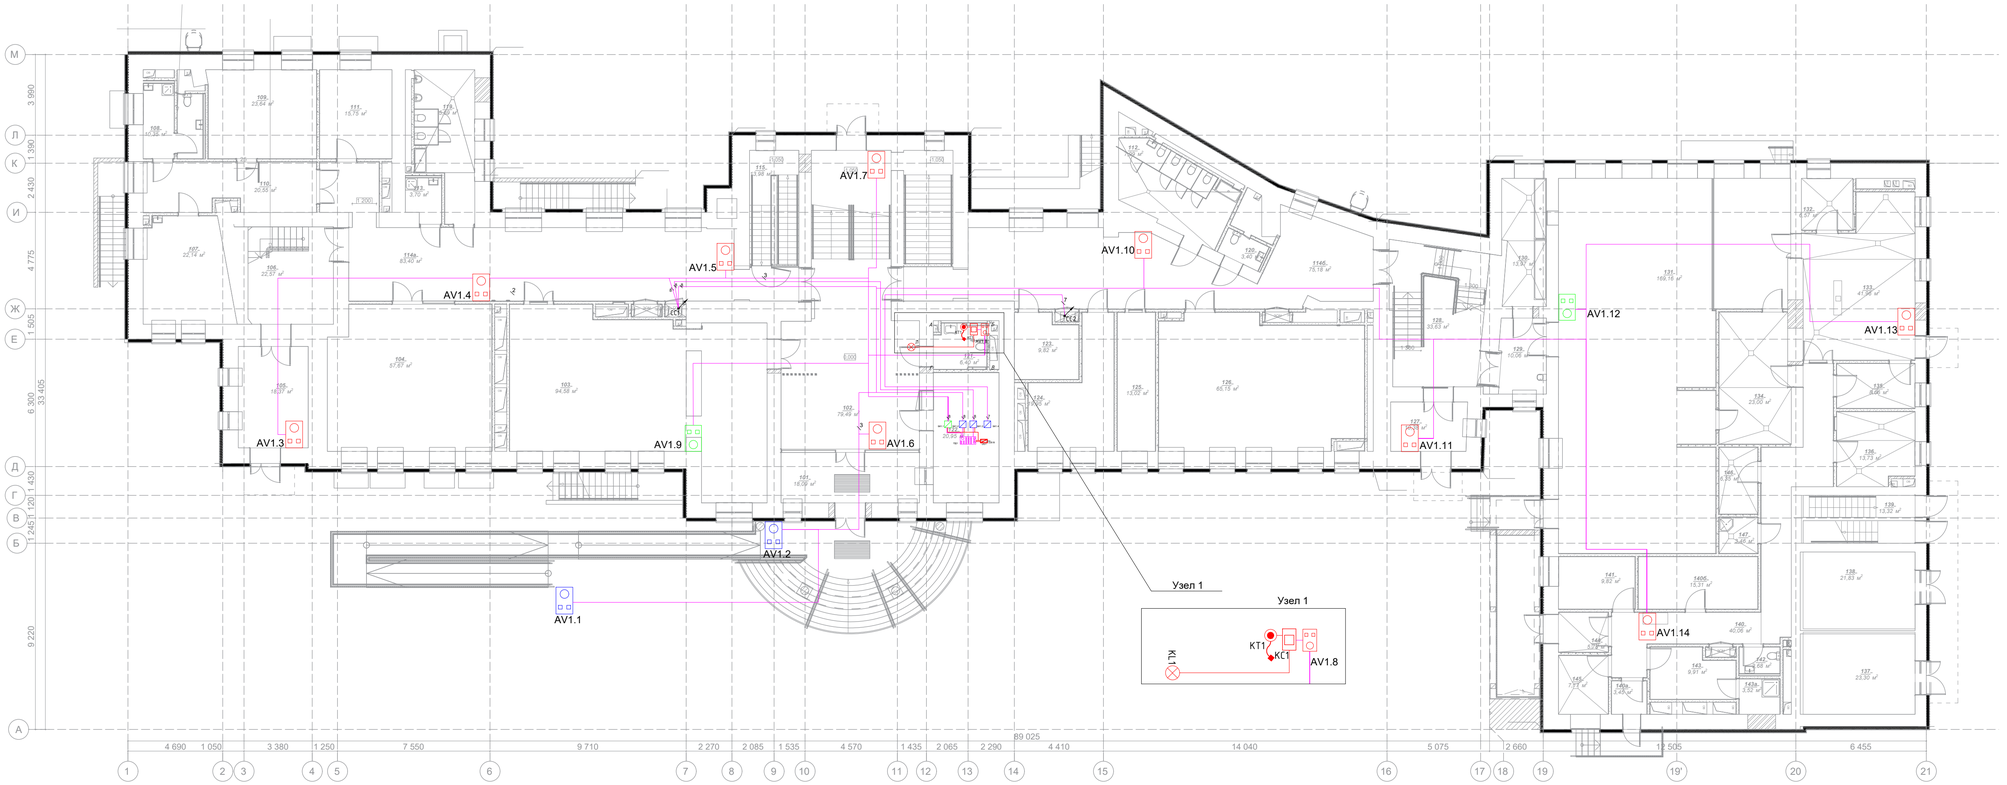

Экспликация помещений 1 этажа			
Номер помещения	Наименование	Площадь, м2	Кат. помещения
101	Тамбур	18,09	
102	Вестибюль	79,49	
103	Гардеробная для обучающихся	94,58	
104	Учебный кабинет	57,67	
105	Тамбур	18,37	
106	Лестничная клетка тип Н2	22,57	
107	Процедурный (прививочный) кабинет	22,14	
108	Место для приготовления дезинфицирующих растворов и хранения уборочного инвентаря	10,35	В4
109	Кабинет врача	23,64	
110	Зона ожидания посетителей	20,55	
111	Кладовая	15,75	В3
112	Санузел для девочек с комнатой личной гигиены	7,99	
113	ПУИ	3,70	В4
114а	Коридор	83,40	
114б	Коридор	75,18	
115	Технологическая лестница	13,98	
119	Санузел для мальчиков	5,69	
120	Санузел для персонала	3,40	
121	Санузел для МГН	6,40	
122	Комната охраны	20,95	
123	Кроссовая	9,82	В4
124	Административный кабинет тип 1	19,95	
125	Гардеробная комната для учителей	13,02	
126	Учебный кабинет	65,15	
127	Тамбур	10,38	
128	Лестничная клетка тип Л1	33,63	
129	Коридор	10,06	
130	Умывальная	13,97	
131	Обеденный зал	169,16	
132	Холодный цех	6,57	В4
133	Горячий цех	41,96	В3
134	Моечная столовой посуды	23,00	В4
135	Моечная кухонной посуды	8,66	В4
136	Доготовочный цех	13,73	В3
137	Техническое помещение (электрощитовая)	23,30	В3
138	Техническое помещение (электрощитовая)	21,83	В3
139	Лестничная клетка лип Л1	13,32	
140	Коридор	40,06	
140а	Тамбур	3,45	
140б	помещение холодильного оборудования	15,31	В3
141	Кладовая сухих продуктов	9,82	В4
142	Санузел	2,68	
143	Помещение для персонала	9,91	
143а	Душ	3,52	
144	Загрузочный цех	5,78	В4
145	Кладовая и моечная оборотной тары	7,17	В4
146	Помещение для временного хранения пищевых отходов	6,35	В4
147	ПУИ	3,46	В4
		1 208,91 м²	

Согласовано

Взам. инв. №

Подп. и дата

Инв. № подл.

Изм.	Кол. уч.	Лист	N док.	Подп.	Дата
Разработал		Ветлицкая			11.24
Проверил		Щипин			11.24
Н. Контр.		Исаев			11.24
ГИП		Пильгуй			11.24

2024-00375-01-0-ИОС5.10

Здание государственного бюджетного общеобразовательного учреждения города Москвы "Школа № № 1574", расположенное по адресу: г. Москва, пер. Старопименовский, д. 5

Капитальный ремонт


Стадия	Лист	Листов
П		1

План расположения оборудования и прокладки кабельных трасс. Первый этаж

МОСЖИЛ НИИПРОЕКТ

Копировал

Формат А1

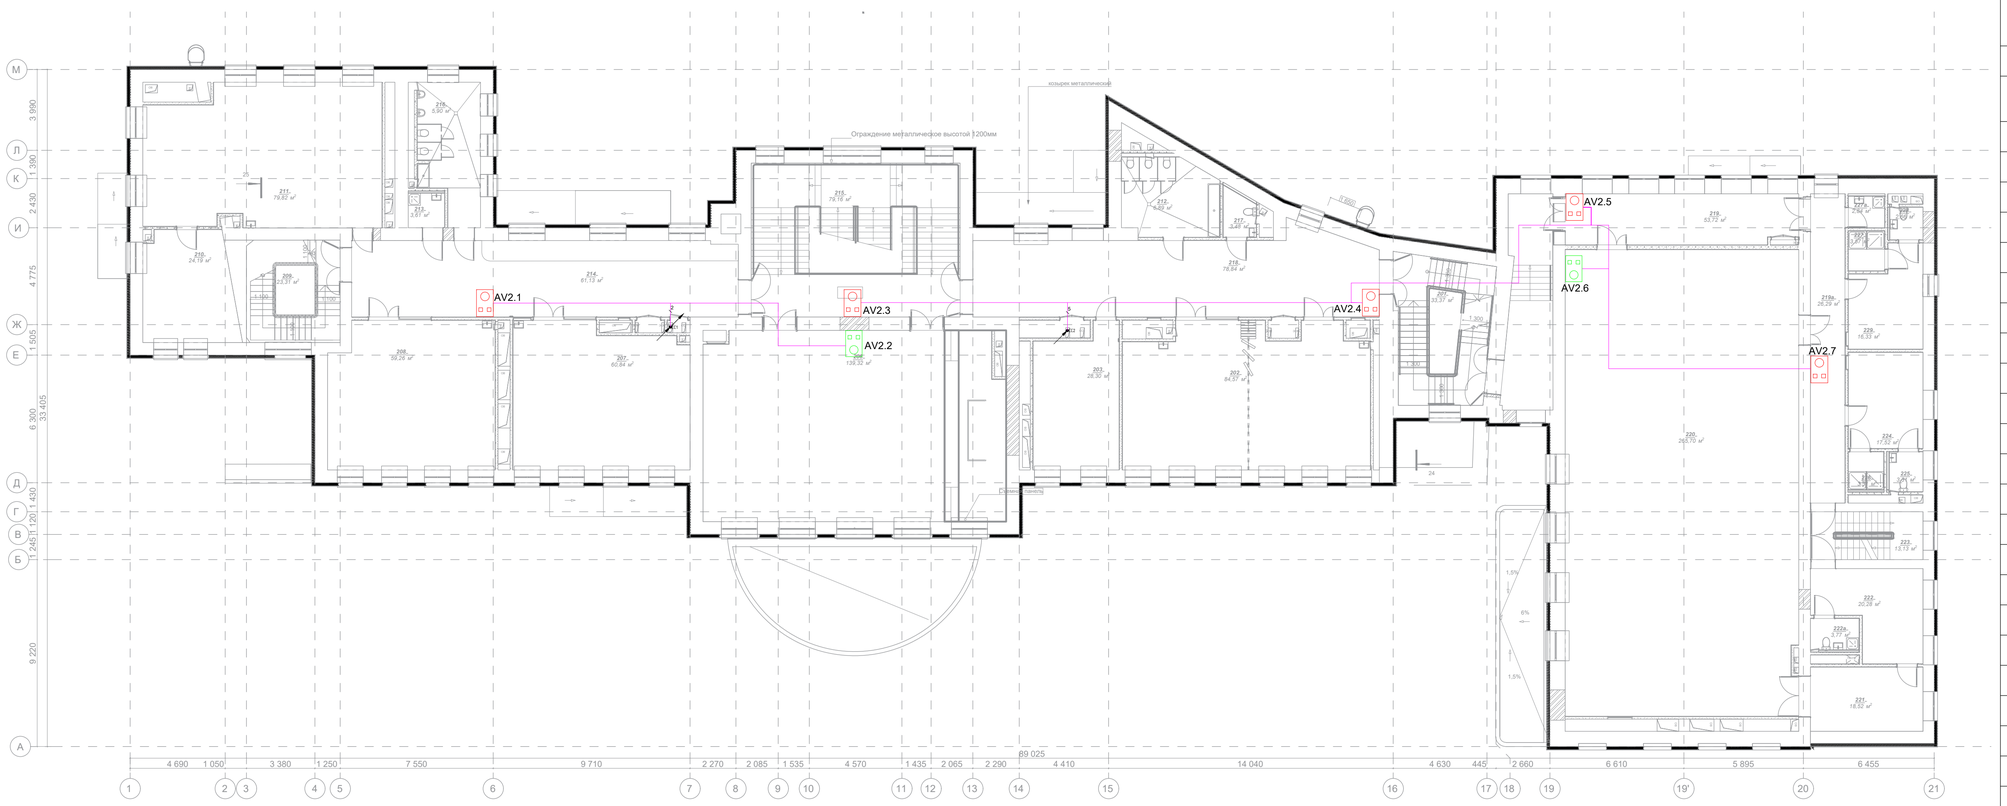

Экспликация помещений 2 этажа			
Номер поме-щения	Наименование	Площадь, м2	Кат. поме-щения
201	Лестничная клетка тип Л1	33,37	
202	Кабинет иностранного языка	84,57	
203	Рабочее пространство для учителей тип 2	28,30	
206	Актовый зал	139,32	
207	Учебный кабинет	60,84	
208	Учебный кабинет	59,26	
209	Лестничная клетка Л1	23,31	
210	Кладовая инвентаря творческой мастерской	24,19	В3
211	Кабинет ИЗО	79,82	
212	Санузел для девочек	6,89	
213	ПУИ	3,61	В4
214	Коридор	61,13	
215	Вестибюль	79,16	
216	Санузел для мальчиков	5,90	
217	Санузел для персонала	3,48	
218	Коридор	78,84	
219	Коридор	53,72	
219а	Коридор	26,29	
220	Спортивный зал	265,70	
221	Снарядная	18,52	В3
222	Комната инструктора	20,28	
222а	Душ с санузлом	3,77	
223	Лестничная клетка тип Л1	13,13	
224	Раздевальная	17,52	
225	Санузел	3,31	
226	Душевая	3,31	
227	Душевая	3,57	
227а	ПУИ	2,84	В4
228	Санузел	2,66	
229	Раздевальная	16,33	
		1 222,94 м²	

Согласовано

Взам. инв. №


Подп. и дата

Инв. № подл.

						2024-00375-01-0-ИОС5.10	
						Здание государственного бюджетного общеобразовательного учреждения города Москвы "Школа № № 1574", расположенное по адресу: г. Москва, пер. Старопименовский, д. 5	
Изм.	Кол. уч.	Лист	N док.	Подп.	Дата		
Разработал		Ветлицкая			11.24	Капитальный ремонт	Стадия: П; Лист: ; Листов: 1
Проверил		Щипин			11.24		
Н. Контр.		Исаев			11.24	План расположения оборудования и прокладки кабельных трасс. Второй этаж	МОСЖИЛ НИИПРОЕКТ
ГИП		Пильгуй			11.24		

Копировал

Формат А1

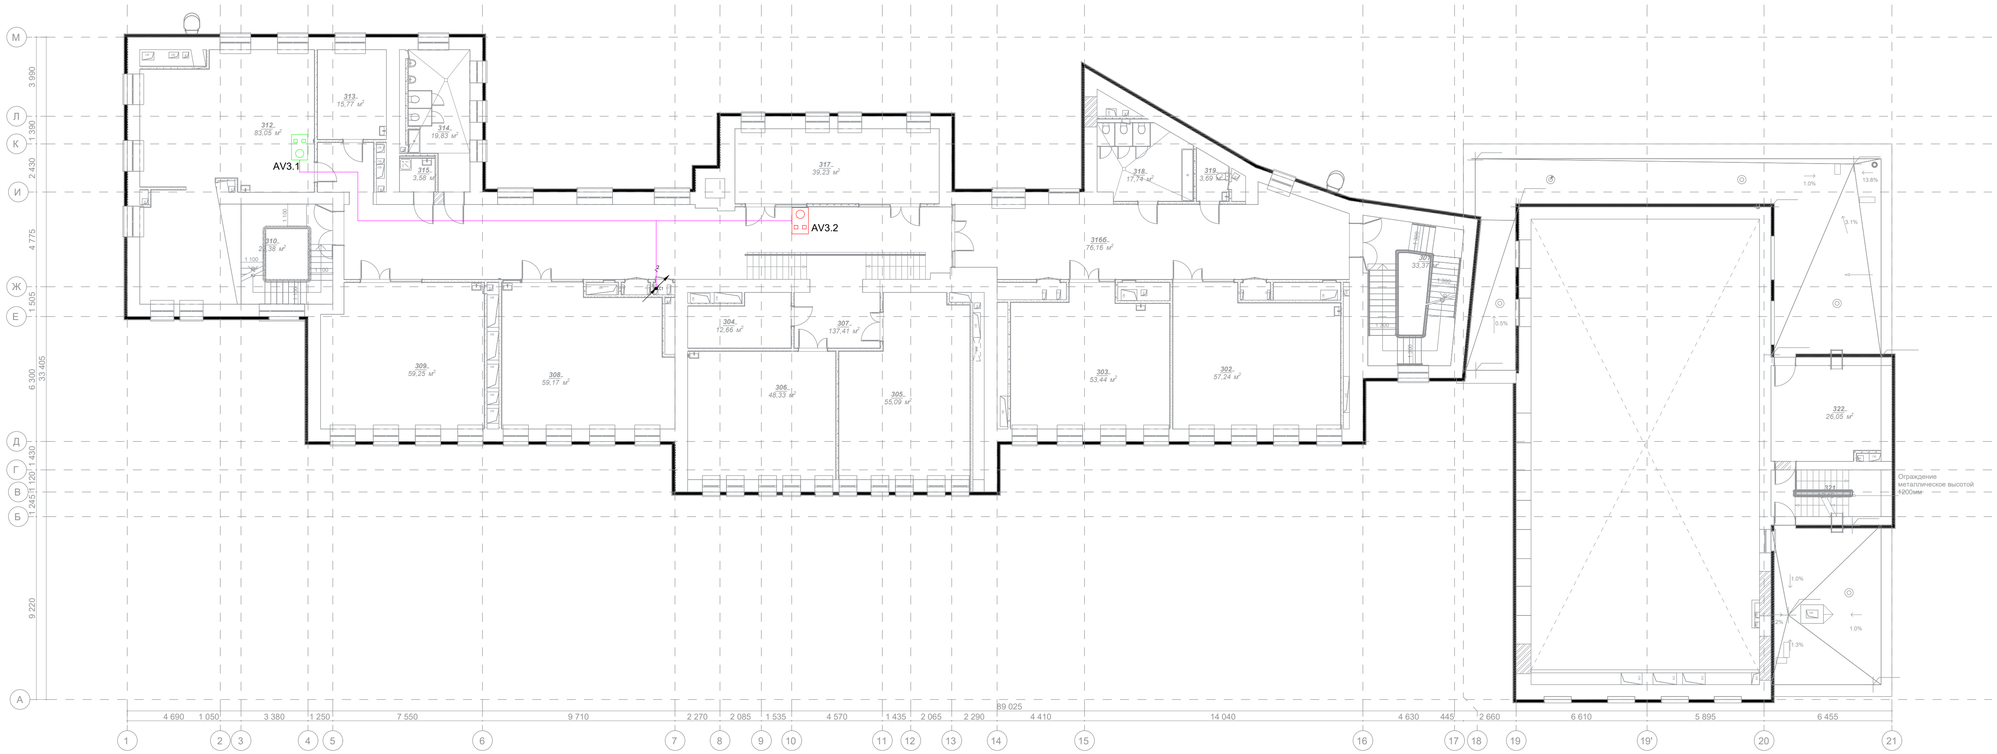

Экспликация помещений 3 этажа			
Номер поме-щения	Наименование	Площадь, м2	Кат. поме-щения
301	Лестничная клетка тип Л1	33,37	
302	Учебный кабинет	57,24	
303	Учебный кабинет	53,44	
304	Серверная	12,66	В3
305	Учебный кабинет	55,09	
306	Учебный кабинет	48,33	
307	Коридор	137,41	
308	Учебный кабинет	59,17	
309	Учебный кабинет	59,25	
310	Лестничная клетка тип Н2	23,38	
312	Библиотека	83,05	В3
313	Кабинет для индивидуальных занятий в тч с учителем -логопедом	15,77	
314	Санузел для мальчиков	19,83	
315	ПУИ	3,58	В4
316б	Коридор	76,16	
317	Кабинет иностранного языка	39,23	
318	Санузел для девочек	17,74	
319	Санузел для персонала	3,69	
321	Лестничная клетка тип Л1	13,13	
322	Техническое помещение	26,05	В3
		837,57 м²	

Согласовано

Взам. инв. №

Подп. и дата

Инв. № подл.

Изм.	Кол. уч.	Лист	N док.	Подп.	Дата
Разработал		Ветлицкая			11.24
Проверил		Щипин			11.24
Н. Контр.		Исаев			11.24
ГИП		Пильгуй			11.24

2024-00375-01-0-ИОС5.10

Здание государственного бюджетного общеобразовательного учреждения города Москвы "Школа № № 1574", расположенное по адресу: г. Москва, пер. Старопименовский, д. 5

Капитальный ремонт


Стадия	Лист	Листов
П		1

План расположения оборудования и прокладки кабельных трасс. Третий этаж

МОСЖИЛ НИИПРОЕКТ

Копировал

Формат А1

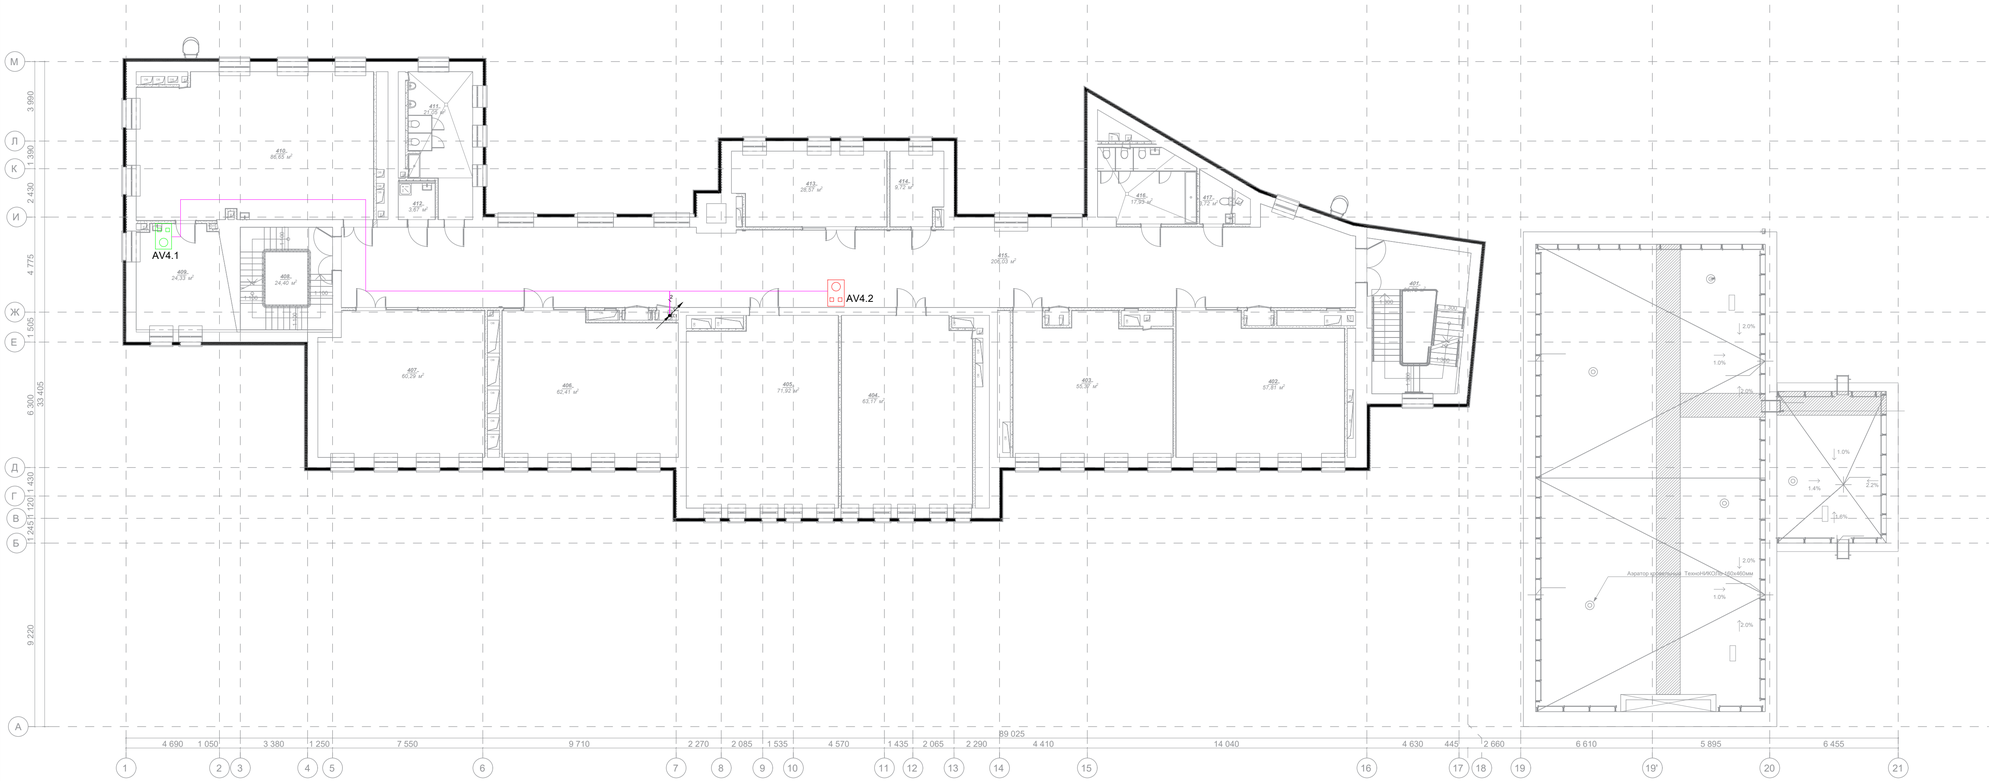

Экспликация помещений 4 этажа			
Номер поме-щения	Наименование	Площадь, м2	Кат. поме-щения
401	Лестничная клетка тип Л1	35,72	
402	Кабинет русского языка и литературы	57,81	
403	Кабинет русского языка и литературы	55,37	
404	Кабинет истории тип 1	63,17	
405	Кабинет математики	71,92	
406	Кабинет математики	62,41	
407	ОБЗР	60,29	
408	Лестничная клетка тип Н2	24,40	
409	Лаборантская кабинета биологии	24,33	В3
410	Учебные кабинеты для изучения естествознания: биология/ЛИК	86,65	
411	Санузел для мальчиков	21,05	
412	ПУИ	3,67	В4
413	Административный кабинет тип 1	28,57	
414	Кабинет для индивидуальных занятий в тч с педагогом-психологом	9,72	
415	Коридор	206,03	
416	Санузел для девочек с комнатой личной гигиены	17,93	
417	Санузел для персонала	3,72	
		832,76 м²	

Согласовано

Взам. инв. №

Подп. и дата

Инв. № подл.

						2024-00375-01-0-ИОС5.10	
						Здание государственного бюджетного общеобразовательного учреждения города Москвы "Школа № 1574", расположенное по адресу: г. Москва, пер. Старопименовский, д. 5	
Изм.	Кол. уч.	Лист	N док.	Подп.	Дата		
Разработал		Ветлицкая			11.24	Капитальный ремонт	Стадия: П; Лист: ; Листов: 1
Проверил		Щипин			11.24		
Н. Контр.		Исаев			11.24	План расположения оборудования и прокладки кабельных трасс. Четвертый этаж	МОСЖИЛ НИИПРОЕКТ
ГИП		Пильгуй			11.24		

Копировал

Формат А1



Экспликация помещений 5 этажа			
Номер поме-щения	Наименование	Площадь, м2	Кат. поме-щения
501	Лестничная клетка тип Л1	35,72	
502	Кабинет иностранного языка для подгруппы	28,66	
503	Учебный кабинет для изучения естествознания (химия)	73,11	
504	Лаборантская кабинета химии	19,17	В3
505	Серверная	8,77	В4
506	Кабинет информационных технологий	131,15	
507	Кабинет географии	62,36	
508	Кабинет русского и литературы	60,13	
509	Лестничная клетка тип Н2	23,94	
510	Лаборантская кабинета физики	25,30	В3
511	Учебные кабинеты для изучения естествознания: физика	86,65	
512	ПУИ	4,50	В4
513	Санузел для мальчиков	20,87	
514	Кабинет иностранного языка для подгруппы	37,15	
515	Коридор	205,54	
516	Санузел для девочек с комнатой личной гигиены	17,88	
517	Санузел для персонала	3,67	
		844,57 м²	

Согласовано

Взам. инв. №

Подп. и дата

Инв. № подл.

						2024-00375-01-0-ИОС5.10	
						Здание государственного бюджетного общеобразовательного учреждения города Москвы "Школа № № 1574", расположенное по адресу: г. Москва, пер. Старопименовский, д. 5	
Изм.	Кол. уч.	Лист	N док.	Подп.	Дата		
Разработал		Ветлицкая			11.24	Капитальный ремонт	Стадия: П; Лист: ; Листов: 1
Проверил		Шипин			11.24		
Н. Контр.		Исаев			11.24	План расположения оборудования и прокладки кабельных трасс. Пятый этаж	МОСЖИЛ НИИПРОЕКТ
ГИП		Пильгуй			11.24		

Копировал

Формат А1

Поз.	Наименование и техническая характеристика	Тип, марка, обозначение документа, опросного листа	Код продукции	Поставщик	Ед. измерения	Количество	Масса 1 ед., кг	Примечание
	ОБОРУДОВАНИЕ СИСТЕМЫ ДВУСТОРОННЕЙ СВЯЗИ							
	1. Пульт диспетчера (32 абонента)	AN-CO32		Омега Саунд	шт	1		
	2. Блок коммутации (не более 4-х для одного пульта AN-CO32, 8 линий)	AN-X8		Омега Саунд	шт	4		
	3. Блок коммутации абонентских линий	AN-X8 MGN		Омега Саунд	шт	1		
	4. Стойка для считывателя Stolz (Штольц) 150х150 мм		237228	Штольц Групп	шт	2		
	5. Устройство вызова	AL-RB		Омега Саунд	шт	1		
	6. Устройство отмены вызова	AL-CB		Омега Саунд	шт	1		
	7. Светозвуковой сигнализатор	AL-DI		Омега Саунд	шт	1		
	8. Абонентское переговорное устроство с лицевой поверхностью зелёного цвета для поверхностного монтажа и защитой IP65	AN-BG-WP		Омега Саунд	шт	2		
	9. Абонентское переговорное устроство с лицевой панелью красного цвета для встроенного монтажа	AN-BR1		Омега Саунд	шт	20		
	10. Абонентское переговорное устроство с лицевой панелью зеленого цвета для встроенного монтажа	AN-BG1		Омега Саунд	шт	9		
	ЭЛЕКТРООБОРУДОВАНИЕ							
	1. Резервированный источник питания, 24 Вт, 3 А (под 2 АКБ 1207)		РИП-24 ИСП.01 (РИП-24-3/7М4)	Болид	шт	2		
	2. Аккумуляторная батарея, 12В, 26Ач	АБ 1226С		Болид	шт	4		
	ОГНЕСТОЙКАЯ КАБЕЛЬНАЯ ЛИНИЯ "ПАРЛАЙН+ДКС ОКЛ-15"							
	1. Огнестойкий низкотоксичный кабель парной скрутки	ParLan F/UTP Cat5e PVCLS нг(A)-FRLSLTx 4x2x0.52	110222	Паритет	м	4200	0,088	
	2. Кабель сигнальный, огнестойкий, низкотоксичный	КСРВнг(A)-FRLSLTx 1x2x0.97	102489	Паритет	м	20	0,0463	
	3. Гибкая гофрированная ПЛЛ труба без содержания галогенов, ДУ20, Ø 19.7 / 14.8 мм, протяжка, цвет белый, бухта 100 м		81820	DKC	м	4220	0,048	

Согласовано

Взам. инв. №

Подп. и дата

Инв. № подл.

Изм.	Кол.уч.	Лист	№ док.	Подп.	Дата
Разраб.		Ветлицкая			11.2024
Проверил		Щипин			11.2024
Н.контр.		Исаев			11.2024
ГИП		Пильгуй			11.2024

2024-00375-01-0-СДС.ИОС5.10.С1

Спецификация оборудования и материалов

Стадия	Лист	Листов
П	1	2

МОСЖИЛ НИИПРОЕКТ

Формат А3

Поз.	Наименование и техническая характеристика	Тип, марка, обозначение документа, опросного листа	Код продукции	Поставщик	Ед. изме-ре-ния	Кол.	Масса 1 ед., кг	Примечание
	4. Держатель оцинкованный двусторонний, д.22мм		53356	DKC	шт	10550	0,008	с аксессуарами
	5. Мастика герметизирующая		МГКП	ООО "НПЛ-38080"	кг	1		

Взам. инв. №

Подп. и дата

Инв. № подл.

Изм.	Кол.уч.	Лист	№ док.	Подп.	Дата	2024-00375-01-0-СДС.ИОС5.10.С1	Лист 2

ТЕХНИЧЕСКОЕ ЗАДАНИЕ НА ЭЛЕКТРОСНАБЖЕНИЕ

№ п/п	Наименование потребителя	Место расположения потребителя	Категория надёжности согласно ПУЭ	Напряжение, В	Потребляемая мощность
1	РИП-24 исп. 01	Пом. 122	II	220 АС	20 Вт
2	РИП-24 исп. 01	Пом. 122	II	220 АС	20 Вт

Защита от поражения электрическим током обеспечивается использованием подключения электрооборудования по системе TN-S (TN-C-S). Оборудование должно быть заземлено с помощью защитного PE проводника кабеля питания, либо отдельным медным проводником сечением 6,0 мм2. Заземляющий проводник присоединяется болтовым соединением непосредственно к главной заземляющей шине.