Департамент капитального ремонта города Москвы Государственное автономное учреждение города Москвы Московский научно-исследовательский и проектный институт жилищного хозяйства «МосжилНИИпроект» (ГАУ «МосжилНИИпроект»)

mgnp@mgnp.mos.ru +7 495 624 40 65 107078, г. Москва,ул.Каланчевская, д. 4/2, стр. 1

Капитальный ремонт здания Государственного бюджетного общеобразовательного учреждения города Москвы "Школа № 1 574", расположенного по адресу: г. Москва, пер. Старопименовский, д. 5

ПРОЕКТНАЯ ДОКУМЕНТАЦИЯ

Система электроснабжения

2024-00375-01-0-ИОС1

1 этап

2025

Департамент капитального ремонта города Москвы Государственное автономное учреждение города Москвы Московский научно-исследовательский и проектный институт жилищного хозяйства «МосжилНИИпроект» (ГАУ «МосжилНИИпроект»)

mgnp@mgnp.mos.ru +7 495 624 40 65 107078, г. Москва,ул.Каланчевская, д. 4/2, стр. 1

Капитальный ремонт здания Государственного бюджетного общеобразовательного учреждения города Москвы " Школа № 1574", расположенного по адресу: г. Москва, пер. Старопименовский, д. 5

ПРОЕКТНАЯ ДОКУМЕНТАЦИЯ

Система электроснабжения

2024-00375-01-0-ИОС1

1 этап

Заместитель директора Н.Р. Нигматулин 18.02.25

Главный инженер проекта Н.Р. Нигматулин 18.02.25

2025

Обозначение	Наименование	Приме-чание
2024-00375-01-0-ИОС1-С	Содержание тома	2-4
2024-00375-01-0-ИОС1-СП	Состав проектной документации	5
2024-00375-01-0-ИОС1.ТЧ	Текстовая часть	6-23
	Графическая часть в составе:	
	Однолинейная схема ГРЩ	24
	Однолинейная схема ПЭСПЗ	25
	Щит ЩО-0.1. Схема электрическая принципиальная	26
	Щит ЩО-0.2. Схема электрическая принципиальная	27
	Щит ЩО-1.1. Схема электрическая принципиальная	28
	Щит ЩО-1.2. Схема электрическая принципиальная	29
	Щит ЩО-1.3. Схема электрическая принципиальная	30
	Щит ЩО-2.1. Схема электрическая принципиальная	31
	Щит ЩО-2.2. Схема электрическая принципиальная	32
	Щит ЩО-2.3. Схема электрическая принципиальная	33
	Щит ЩО-3.1. Схема электрическая принципиальная	34
	Щит ЩО-3.2. Схема электрическая принципиальная	35
	Щит ЩО-4.1. Схема электрическая принципиальная	36
	Щит ЩО-4.2. Схема электрическая принципиальная	37
	Щит ЩО-5.1. Схема электрическая принципиальная	38
	Щит ЩО-5.2. Схема электрическая принципиальная	39
	Щит ЩАО-0.1. Схема электрическая принципиальная	40
	Щит ЩАО-0.2. Схема электрическая принципиальная	41
	Щит ЩАО-1.1. Схема электрическая принципиальная	42
	Щит ЩАО-1.2. Схема электрическая принципиальная	43
	Щит ЩАО-1.3. Схема электрическая принципиальная	44
	Щит ЩАО-2.1. Схема электрическая принципиальная	45

Согласовано

Взам. инв.№

Подп. и дата

Инв. №подл.

Изм.	Кол.уч.	Лист	№ док	Подпись	Дата	2024-00375-01-0-ИОС1-С		
Разраб.		Семенов Д.Ф			02.2025	Содержание тома 5.1	Стадия	Лист	Листов
Проверил		Пильгуй Н.М			02.2025		П	1	3
Н.контр.		Пильгуй Н.М			02.2025		МОСЖИЛ НИИПРОЕКТ		
Нач.отдела		Белоусова Д.П			02.2025				

Обозначение	Наименование	Приме-чание
	Щит ЩАО-2.2. Схема электрическая принципиальная	46
	Щит ЩАО-3.1. Схема электрическая принципиальная	47
	Щит ЩАО-4.1. Схема электрическая принципиальная	48
	Щит ЩАО-5.1. Схема электрическая принципиальная	49
	Щит ЩР-0.1. Схема электрическая принципиальная	50
	Щит ЩР-104. Схема электрическая принципиальная	51
	Щит ЩР-126. Схема электрическая принципиальная	52
	Щит ЩР-1.1. Схема электрическая принципиальная	53
	Щит ЩР-1.2. Схема электрическая принципиальная	54
	Щит ЩР-2.1. Схема электрическая принципиальная	55
	Щит ЩР-2.2. Схема электрическая принципиальная	56
	Щит ЩР-2.3. Схема электрическая принципиальная	57
	Щит ЩР-3.1. Схема электрическая принципиальная	58
	Щит ЩР-3.2. Схема электрическая принципиальная	59
	Щит ЩР-4.1. Схема электрическая принципиальная	60
	Щит ЩР-4.2. Схема электрическая принципиальная	61
	Щит ЩР-5.1. Схема электрическая принципиальная	62
	Щит ЩР-5.2. Схема электрическая принципиальная	63
	Щит ЩВ-0.1. Схема электрическая принципиальная	64
	Щит ЩВ-0.2. Схема электрическая принципиальная	65
	Щит ЩВ-2. Схема электрическая принципиальная	66
	Щит ЩК. Схема электрическая принципиальная	67
	Щит ЩКс. Схема электрическая принципиальная	68
	Щит ЩКПБ. Схема электрическая принципиальная	69
	Щит ЩПБ1. Схема электрическая принципиальная	70
	Щит ЩПБ2. Схема электрическая принципиальная	71
	План освещения подвала	72
	План освещения 1 этажа	73

Обозначение	Наименование	Приме-чание
	План освещения 2 этажа	74
	План освещения 3 этажа	75
	План освещения 4 этажа	76
	План освещения 5 этажа	77
	Силовое электрооборудование. План подвала	78
	Силовое электрооборудование. План 1 этажа	79
	Силовое электрооборудование. План 2 этажа	80
	Силовое электрооборудование. План 3 этажа	81
	Силовое электрооборудование. План 4 этажа	82
	Силовое электрооборудование. План 5 этажа	83
	Силовое электрооборудование. План пищеблока	84
	План молниезащиты и заземления	85
	Расчет зон защиты стержневых молниеотводов	86
	План подвала с трубными проводками ОЗДС	87
	План 1 этажа с трубными проводками ОЗДС	88
	Схема уравнивания потенциалов	89
	Прилагаемые документы:	
2024-00375-01-0-ИОС1.СО	Спецификация оборудования, изделий и материалов	90-127

Взам. инв.№

Подп. и дата

Инв. №подл.

Состав проектной документации*

№ тома	Обозначение	Наименование	Примечание

* Состав проектной документации смотри том «Состав проектной документации».

Согласовано

Взам. инв.№

Подп. и дата

Инв. № подл.

						2024-00000-01-0-ИОС1-С	
Изм.	Кол.уч.	Лист	№ док	Подпись	Дата		
Разраб.		Семенов Д.Ф			02.2025	Состав проектной документации	Стадия: П; Лист: ; Листов: 1
Проверил		Пильгуй Н.М			02.2025		
Н.контр.		Пильгуй Н.М			02.2025		МОСЖИЛ НИИПРОЕКТ
Нач.отдела		Белоусова Д.П			02.2025		

Содержание

Стр.

Общая часть 2

а) Характеристика источников электроснабжения 2

б) Обоснование принятой схемы электроснабжения 3

в) Сведения о количестве электроприемников, их установленной и расчетной мощности 3

г) Требования к надёжности электроснабжения и качеству электроэнергии 5

д) Описание решений по обеспечению электроэнергией электроприемников в соответствии с установленной классификацией в рабочем и аварийном режимах..... 6

е) Описание проектных решений по компенсации реактивной мощности, релейной защите, управлению, автоматизации и диспетчеризации системы электроснабжения 7

е_1) Проектные решения по релейной защите и автоматике, включая противоаварийную и режимную автоматику 8

ж) Перечень мероприятий по обеспечению соблюдения установленных требований энергетической эффективности и устройствам, технологиям и материалам, используемым в системе электроснабжения, позволяющих исключить нерациональный расход электрической энергии. 8

ж_1) Описание мест расположения приборов учета используемой электрической энергии и устройств сбора и передачи данных от таких приборов, а так же технических решений включения приборов учета электрической энергии в интеллектуальную систему учета электрической энергии (мощности) 8

з) Сведения о мощности сетевых и трансформаторных объектов..... 8

и) Решения по организации масляного и ремонтного хозяйства – для объектов производственного назначения..... 9

к) Перечень мероприятий по заземлению (занулению) и молниезащите..... 9

л) Сведения о типе, классе проводов и осветительной арматуры, которые подлежат применению при строительстве объекта капитального строительства 10

м) Описание системы рабочего, дежурного и аварийного освещения..... 11

о) Перечень мероприятий по резервированию электроэнергии 13

о_1) Перечень энергопринимающих устройств аварийной и технологической брони и его обоснование..... 13

о_2) Сведения о типе и количестве установок, потребляющих электрическую энергию, параметрах и режимах их работы..... 14

Согласовано

Гл.спец.

Гл.спец.

Взам. инв.№

Подп. и дата

Инв. №подл.

Изм.	Кол.уч.	Лист	№ док	Подпись	Дата
Разраб.		Семенов Д.Ф			02.2025
Проверил		Пильгуй Н.М			02.2025
Н.контр.		Пильгуй Н.М			02.2025
Нач.отдела		Белоусова Д.П			02.2025

2024-00375-01-0-ИОС1.ТЧ

Текстовая часть

Стадия	Лист	Листов
П	1	12

МОСЖИЛ НИИПРОЕКТ

Общая часть

В настоящем томе проекта выполнена проектная документация системы силового электрооборудования, молниезащиты и электроосвещения объекта: «ГБОУ Школа №1574 по адресу: г. Москва, пер. Старопименовский, д. 5».

Вид строительства: капитальный ремонт.

Проектная документация разработана в соответствии с требованиями:

- Постановления Правительства РФ от 16.02.2008 №87 (ред. от 06.05.2023) "О составе разделов проектной документации и требованиях к их содержанию";
- ПУЭ «Правила устройства электроустановок»;
- № 123-ФЗ "Технический регламент о требованиях пожарной безопасности"
- № 384-ФЗ "Технический регламент о безопасности зданий и сооружений";
- ГОСТ 21.210-2014 Условные графические изображения электрооборудования и проводок на планах;
- ГОСТ Р 21.101-2020 Национальный стандарт Российской Федерации «Система проектной документации для строительства. Основные требования к проектной и рабочей документации»;
- СП 76.13330.2016 Электротехнические устройства. Актуализированная редакция СНиП 3.05.06-85;
- ГОСТ 31996-2012 Кабели силовые с пластмассовой изоляцией на номинальное напряжение 0,66; 1 и 3 кВ. Общие технические условия;
- СП 256.1325800.2016 Электроустановки жилых и общественных зданий правила проектирования и монтажа;
- СП 52.13330.2016 Естественное и искусственное освещение;
- РД 34.21.122-87 Инструкция по устройству молниезащиты зданий и сооружений;
- СО 153-34.21.122-2003 Инструкция по устройству молниезащиты зданий, сооружений и промышленных предприятий;
- ГОСТ Р 50571 Национальный стандарт российской федерации. Электроустановки низковольтные. (комплекс стандартов).

а) Характеристика источников электроснабжения

Для осуществления приема и распределения электроэнергии для электропотребителей школы в помещении электрощитовой № 017, расположенной в подвале, предусматривается установка ГРЩ.

Электроснабжение здания осуществляется от РУ-0,4кВ ТП-10/0,4кВ № новая по двум независимым взаиморезервирующим кабельными линиям. Прокладка питающих кабелей выполняется по отдельному проекту.

Коммерческий учёт электрической энергии (мощности) предусматривается трёхфазными счетчиками полукосвенного включения в количестве 2 шт в помещении электрощитовой в щитах ЩУ1 и ЩУ2. Мероприятия по коммерческому учету осуществляет сетевая организация (в соответствии с п.10.3 Технических условий № И-25-00-145945/102/МС выданные ПАО «Россети Московский регион» - Московские кабельные сети).

б) Обоснование принятой схемы электроснабжения

Электроснабжение объекта предусмотрено по второй категории надёжности. Для электропитания потребителей 1-ой категории электроснабжения предусмотрено устройство автоматического ввода резерва (АВР).

Напряжение питающих сетей ~ 400/230 В (ГОСТ29322—2014).

Сети электроснабжения объекта приняты с глухозаземленной нейтралью (система TN-C-S).

Распределительные сети выполняются кабелем марки ВВГнг(А)-LSLTx и прокладываются от распределительных панелей до групповых щитов и потребителей. Распределительные сети систем противопожарной защиты, а также для других электроприемников, которые должны сохранять работоспособность в условиях пожара выполняются кабелем марки ВВГнг(А)-FRLSLTx и прокладываются от распределительной панели противопожарных устройств до групповых щитов и потребителей. Структура внутреннего электроснабжения имеет радиальную схему. Схема внутреннего электроснабжения оптимизирована с целью снижения капитальных затрат (стоимость материалов, удобства монтажа), снижения эксплуатационных затрат (потери электроэнергии, удобство обслуживания), имеет возможность расширения и изменения (в процессе эксплуатации).

в) Сведения о количестве электроприемников, их установленной и расчетной мощности

Суммарная расчетная мощность электроприёмников объекта составляет: 221,43 кВт. Основными электроприёмниками являются:

- оборудование учебных классов;
- оборудование пищеблока;
- компьютеры и оргтехника;
- освещение;
- система кондиционирования;
- системы приточной и вытяжной вентиляции;
- системы подпора воздуха и дымоудаления.

Расчет нагрузок приведен в таблицах:

Таблица 1. Расчет нагрузок в рабочем режиме

Наименование потребителей	Кат.	Руст. кВт.	cos φ	tgφ	Кс	Ррасч. кВт	Q, кВАр	S, кВА	Ip А
РП1:									
Электроприемники бытового назначения	II	19.55	0.90	0.45	0.20	3.91	1.76	4.29	
Оборудование кабинетов материальной технологии	II	33.00	0.90	0.45	0.20	6.60	2.98	7.24	
Лабораторное оборудование для школьных классов	II	13.50	0.90	0.45	0.20	2.70	1.22	2.96	
Рукосушители	II	18.00	0.95	0.32	0.15	2.70	0.86	2.83	
Электроприемники вычислительных машин	II	13.20	0.65	0.86	0.40	5.28	4.56	6.98	
Рабочее освещение	II	22.70	0.92	0.40	0.84	19.07	7.68	20.56	
Технологическое оборудование пищеблока	II	100.60	0.95	0.32	0.43	42.76	13.58	44.86	
Оборудование актового зала	II	15.60	0.92	0.40	0.77	12.01	4.84	12.95	
Тепловые завесы	II	12.00	0.97	0.25	0.75	9.00	2.21	9.27	
Калориферы	II	3.00	0.97	0.25	0.75	2.25	0.55	2.32	
Водонагреватели	II	26.50	0.97	0.25	0.30	7.95	1.95	8.19	
Вентиляция	II	25.38	0.80	0.64	0.60	15.23	9.80	18.11	
Итого РП1:						129.45	51.98	140.54	213.54
РП2:									
Электроприемники бытового назначения	II	13.74	0.90	0.45	0.20	2.75	1.24	3.01	
Оборудование кабинетов материальной технологии	II	24.81	0.90	0.45	0.20	4.96	2.24	5.44	
Лабораторное оборудование для школьных классов	II	4.50	0.90	0.45	0.20	0.90	0.41	0.99	
Рукосушители	II	19.50	0.95	0.32	0.15	2.93	0.93	3.07	
Электроприемники вычислительных машин	II	10.40	0.65	0.86	0.40	4.16	3.59	5.50	
Кондиционирование	II	39.26	0.85	0.55	0.55	21.59	11.98	24.69	
Рабочее освещение	II	10.19	0.92	0.40	0.84	8.56	3.45	9.23	
Технологическое оборудование пищеблока	II	101.40	0.95	0.32	0.43	43.10	13.69	45.22	
Тепловые завесы	II	12.00	0.97	0.25	0.75	9.00	2.21	9.27	
Калориферы	II	6.00	0.97	0.25	0.75	4.50	1.11	4.63	
Водонагреватели	II	26.50	0.97	0.25	0.30	7.95	1.95	8.19	
Вентиляция	II	8.82	0.80	0.64	0.60	5.29	3.41	6.29	
Оборудование ОЗДС	II	1.00	0.95	0.32	0.43	1.00	0.32	1.05	
Итого РП2:						116.68	46.51	126.58	192.32
РП3:									
Электроприемники вычислительных машин	I	11.70	0.65	0.86	0.40	4.68	4.04	6.18	
Блоки питания СКУД, ОС, турникетов, розетки медблока	I	5.63	0.65	0.86	0.40	2.25	1.94	2.97	
Кондиционирование серверных	I	10.54	0.80	0.64	0.80	8.43	5.43	10.03	
Итого РП3:						15.36	11.41	19.18	29.15
ПЭСП3:									
Аварийное освещение	I	8.72	0.92	0.40	1.00	8.72	3.51	9.40	
Установки противодымной вентиляции	I	114.87	0.80	0.64	0.00	0.00	0.00	0.00	
Пожарная насосная станция	I	15.75	0.80	0.64	0.00	0.00	0.00	0.00	
Клапаны огнезащитные	I	0.10	0.85	0.55	0.00	0.00	0.00	0.00	
Охранно-пожарная сигнализация	I	0.50	0.90	0.45	1.00	0.50	0.23	0.55	
Система оповещения и управления эвакуацией	I	1.49	0.90	0.45	1.00	1.49	0.67	1.63	
Итого ПЭСП3:						10.71	4.41	11.58	17.60
Итого ВВОД 1 (РП1+РП3):						**144.82**	**63.39**	**159.73**	**242.69**
Итого ВВОД 2 (РП2+ПЭСП3):						**127.39**	**50.92**	**138.16**	**209.92**
Итого в Раб. Режиме:						**272.21**	**114.31**	**297.89**	**452.61**

Таблица 2. Расчет нагрузок в режиме пожара

Наименование потребителей	Кат.	Руст. кВт.	cos φ	tgφ	Кс	Ррасч. кВт	Q, кВАр	S, кВА	Ip А
РП1:									
Электроприемники бытового назначения	II	19.55	0.90	0.45	0.20	3.91	1.76	4.29	
Оборудование кабинетов материальной технологии	II	33.00	0.90	0.45	0.20	6.60	2.98	7.24	
Лабораторное оборудование для школьных классов	II	13.50	0.90	0.45	0.20	2.70	1.22	2.96	

Рукосушители	II	18.00	0.95	0.32	0.15	2.70	0.86	2.83	
Электроприемники вычислительных машин	II	13.20	0.65	0.86	0.40	5.28	4.56	6.98	
Рабочее освещение	II	22.70	0.92	0.40	0.84	19.07	7.68	20.56	
Технологическое оборудование пищеблока	II	100.60	0.95	0.32	0.43	42.76	13.58	44.86	
Оборудование актового зала	II	15.60	0.92	0.40	0.77	12.01	4.84	12.95	
Тепловые завесы	II	12.00	0.97	0.25	0.00	0.00	0.00	0.00	
Калориферы	II	3.00	0.97	0.25	0.75	2.25	0.55	2.32	
Водонагреватели	II	26.50	0.97	0.25	0.30	7.95	1.95	8.19	
Вентиляция	II	25.38	0.80	0.64	0.00	0.00	0.00	0.00	
Итого РП1:						105.23	39.97	113.17	171.94
РП2:									
Электроприемники бытового назначения		13.74	0.90	0.45	0.20	2.75	1.24	3.01	
Оборудование кабинетов материальной технологии	II	24.81	0.90	0.45	0.20	4.96	2.24	5.44	
Лабораторное оборудование для школьных классов	II	4.50	0.90	0.45	0.20	0.90	0.41	0.99	
Рукосушители	II	19.50	0.95	0.32	0.15	2.93	0.93	3.07	
Электроприемники вычислительных машин	II	10.40	0.65	0.86	0.40	4.16	3.59	5.50	
Кондиционирование	II	39.26	0.85	0.55	0.00	0.00	0.00	0.00	
Рабочее освещение	II	10.19	0.92	0.40	0.84	8.56	3.45	9.23	
Технологическое оборудование пищеблока	II	101.40	0.95	0.32	0.43	43.10	13.69	45.22	
Тепловые завесы	II	12.00	0.97	0.25	0.00	0.00	0.00	0.00	
Калориферы	II	6.00	0.97	0.25	0.75	4.50	1.11	4.63	
Водонагреватели	II	26.50	0.97	0.25	0.30	7.95	1.95	8.19	
Вентиляция	II	8.82	0.80	0.64	0.00	0.00	0.00	0.00	
Оборудование ОЗДС	II	1.00	0.95	0.32	0.43	1.00	0.32	1.05	
Итого РП2:						80.80	28.91	86.32	131.16
РП3:									
Электроприемники вычислительных машин	I	11.70	0.65	0.86	0.40	4.68	4.04	6.18	
Блоки питания СКУД, ОС, турникетов, розетки медблока	I	5.63	0.65	0.86	0.40	2.25	1.94	2.97	
Кондиционирование серверных		10.54	0.80	0.64	0.00	0.00	0.00	0.00	
Итого РП3:						6.93	5.98	9.16	13.91
ПЭСПЗ:									
Аварийное освещение	I	8.72	0.92	0.40	1.00	8.72	3.51	9.40	
Установки противодымной вентиляции	I	114.87	0.80	0.64	1.00	114.87	73.92	136.60	
Пожарная насосная станция	I	15.75	0.80	0.64	1.00	15.75	10.14	18.73	
Клапаны огнезащитные	I	0.10	0.85	0.55	1.00	0.10	0.06	0.11	
Охранно-пожарная сигнализация	I	0.50	0.90	0.45	1.00	0.50	0.23	0.55	
Система оповещения и управления эвакуацией	I	1.49	0.90	0.45	1.00	1.49	0.67	1.63	
Итого ПЭСПЗ:						141.43	88.52	167.03	253.78
Итого ВВОД 1 (РП1+РП3):						**112.16**	**45.96**	**122.32**	**185.86**
Итого ВВОД 2 (РП2+ПЭСПЗ):						**222.23**	**117.43**	**253.35**	**384.93**
Итого в Пож. Режиме:						**334.39**	**163.38**	**375.67**	**570.79**

г) Требования к надёжности электроснабжения и качеству электроэнергии

Электропотребители относятся к потребителям первой и второй категории надежности электроснабжения (по классификации ПУЭ) согласно табл. 6.1 СП256.1325800.2016.

К нагрузкам первой категории и относятся:

— Пожарно-охранная сигнализация;

— Системы оповещения о пожаре;

— Системы противодымной защиты;

— Система видеонаблюдения;

— Указатели пожарных гидрантов и номера здания;

— Система контроля доступа;

— Информационная система «Проход и питание»;

— Аварийное (эвакуационное и резервное) освещение;

— Система управления эвакуацией;

— Система пожаротушения;

— Лабораторные холодильники медицинского блока;

— Телекоммуникационные шкафы серверных.

К нагрузкам второй категории относятся все остальные электропотребители здания. Требуемая надежность электроснабжения обеспечивается применений следующих мероприятий:

- секционированием шин в РУ-0,4кВ трансформаторной подстанции с включением секционного выключателя при отключении одного из силовых трансформаторов и перевод нагрузки на оставшийся в работе силовой трансформатор;
- электроснабжение потребителей I и II категории производится от двух независимых источников питания;
- для электроснабжения электроприемников СПЗ предусмотрена отдельная панель с блоком АВР для электроснабжения в аварийном режиме (потеря напряжения на одном из вводов);

Качество электроэнергии, потребляемое зданием, соответствует ГОСТ 13109-97

д) Описание решений по обеспечению электроэнергией электроприемников в соответствии с установленной классификацией в рабочем и аварийном режимах

Для распределения электроэнергии по объекту проектом предусматривается организация ГРЩ.

ГРЩ состоит из вводных (ВП1, ВП2) и распределительных панелей РП1, РП2, РП3, ПЭСПЗ.

В рабочем режиме питание всех потребителей осуществляется по двум вводам от электросети. При пропадании напряжения на одном из вводов АВР автоматически переводит питание потребителей I категории на второй ввод. Перевод остальных потребителей на второй ввод осуществляется в ручном режиме перекидными рубильниками на вводных панелях.

При восстановлении напряжения на вводах, потребители первой категории переходят на рабочий ввод автоматически, перевод остальных потребителей осуществляется вручную.

ГРЩ устанавливается в электрощитовой, расположенной в подвале. Над помещением электрощитовой есть помещения с мокрыми технологическими процессами, разделом АР предусматривается надежная гидроизоляция данных помещений.

Аварийное отключение приточно-вытяжной вентиляции при пожаре выполняется по вторичным цепям с использованием управляющих сигналов на отключение от системы противопожарной защиты (предусмотрено в разделе автоматики). Щиты управления приточно- вытяжными вент. системами предусмотрены в разделе автоматики. Импульсы на их отключение подаются от системы противопожарной автоматики.

Магистральные кабельные трассы выполняются преимущественно вертикальными стояками по лоткам. Проход через этажные перекрытия осуществляется в стальных гильзах. Электрические и слаботочные кабели прокладываются по разным лоткам.

Питающие кабели (до распределительных и групповых щитов) имеют запас по пропускной способности 10-15%.

Проектом предусмотрены следующие мероприятия для маломобильных групп населения в соответствии с п.п.5.5.2, 5.5.7 СП59,12220,2012:

-Аварийное электроосвещение в зонах безопасности МГН;

-Аварийное освещение в помещениях санузлов для МГН;

-Повышение уровня освещенности на одну ступень;

-Выключатели освещения размещаются на высоте 0,8м от уровня пола.

Проектом применяется охранно-дератизационная система на базе электрического дератизатора «ИССАН-ОХРА-Д-333. Система рекомендована к применению Минздравом РФ, соответствует требованиям ГОСТ-Р 50940-96 «Устройства электрошоковые». Система прошла медико-биологические испытания, подтверждающие безопасность воздействия на человека и животных. Эффективность работы системы подтверждена НИИ Дезинфектологии, а радиопомехи, создаваемые в ходе работы, соответствуют ГОСТ-Р 51318.14.1-99.

е) Описание проектных решений по компенсации реактивной мощности, релейной защите, управлению, автоматизации и диспетчеризации системы электроснабжения

Согласно Приказу Минэнерго России от 23.06.2015 N 380 "О Порядке расчета значений соотношения потребления активной и реактивной мощности для отдельных энергопринимающих устройств (групп энергопринимающих устройств) потребителей электрической энергии" максимальное значение коэффициента реактивной мощности, потребляемой в часы больших суточных нагрузок электрической сети, не должно превышать tgφ= 0,35 для напряжения 0,4 кВ.

Применение автоматической конденсаторной установки не требуется.

е_1) Проектные решения по релейной защите и автоматике, включая противоаварийную и режимную автоматику

Данным проектом не предусматривается релейная защита, противоаварийная и режимная автоматика.

ж) Перечень мероприятий по обеспечению соблюдения установленных требований энергетической эффективности и устройствам, технологиям и материалам, используемым в системе электроснабжения, позволяющих исключить нерациональный расход электрической энергии.

Проектом предусмотрены следующие мероприятия по энергосбережению:

- для освещения помещений применены энергоэффективные светодиодные источники света и светильники;

- применены системы автоматизации, позволяющие оптимизировать работу технологических систем;

- предусмотрено устройство включения резервного питания (АВР).

ж_1) Описание мест расположения приборов учета используемой электрической энергии и устройств сбора и передачи данных от таких приборов, а так же технических решений включения приборов учета электрической энергии в интеллектуальную систему учета электрической энергии (мощности)

Коммерческий учёт электрической энергии (мощности) предусматривается трёхфазными счетчиками полукосвенного включения в количестве 2 шт в помещении электрощитовой в щитах ЩУ1 и ЩУ2. Подключение измерительных трансформаторов тока предусматривается до точек подключения панели ППУ (ПЭСПЗ), таким образом обеспечивается учет потребления электроэнергии потребителями первой категории. Мероприятия по коммерческому учету осуществляет сетевая организация (в соответствии с п.10.3 Технических условий № И-25-00-145945/102/МС выданные ПАО «Россети Московский регион» - Московские кабельные сети).

з) Сведения о мощности сетевых и трансформаторных объектов

Трансформаторная подстанция в объем проектирования не входит и в данном разделе не рассматривается.

и) Решения по организации масляного и ремонтного хозяйства – для объектов производственного назначения.

Организация масляного и ремонтного хозяйства не требуется.

к) Перечень мероприятий по заземлению (занулению) и молниезащите

В соответствии с требованиями ПУЭ п.1.7.50 и п. 1.7.57, комплекса стандартов ГОСТ Р 50571 "Электроустановки зданий" для защиты людей от поражения электрическим током при повреждении изоляции все металлические нетоковедущие части электроустановки подлежат заземлению.

Сети электроснабжения объекта приняты с глухозаземленной нейтралью (система TN-C-S).

Организация пятипроводной трехфазной (3 фазы, N и PE) и трехпроводной однофазной (1 фаза, N, PE) системы электропитания предусмотрена в ГРЩ-0,4кВ. Функцию ГЗШ выполняет PE шина вводно-распределительного устройства. Защитные проводники PE используются для заземления только непосредственно потребителей электропитания.

На вводе в здание выполнена система уравнивания потенциалов согласно ПУЭ 7.1.82 путём объединения проводящих частей на шине (PE) и присоединенная в двух местах к существующему наружному контуру заземления. Дополнительная мера для уравнивания потенциала проводится в помещениях, где отдельными одножильными проводниками с системой заземления соединяются все металлические части неэлектрического оборудования (трубопроводы, вентиляционные каналы, кабельные лотки и пр.) К этой системе подключаются все доступные прикосновению открытые проводящие электрооборудования (в том числе штепсельные розетки).

Защищаемое сооружение относится к III категории молниезащиты в соответствии с СО. Защита зданий от разрядов молнии осуществляется с помощью молниеотводов. На всех вентшахтах необходимо предусмотреть металлические колпаки, которые будут выполнять роль естественных молниеприёмников. В качестве токоотвода применяется стальная проволока d8 мм. Для соединения проката по длине и в узлах используется универсальные зажимы. Все металлические элементы, размещенные на кровле, необходимо присоединить к токоотводу при помощи зажимов. Подключение токоотводов осуществляется к существующему контуру заземления. Контур заземления данным разделом не разрабатывается.

Для защиты людей от поражения электрическим током при повреждении изоляции предусматриваются следующие защитные меры:

- заземление электроустановок;

- система уравнивания потенциалов путем присоединения всех металлических трубопроводов, коробов вентиляции, кабельных лотков, и другого оборудования, которое может оказаться под напряжением при повреждении изоляции электрооборудования к заземлителю;

- установка устройств защитного отключения (УЗО);

- автоматическое отключение питания;

- применение электрооборудования, работающего на сверхнизком напряжении. Заземление и защитные меры безопасности электроустановок здания выполняются согласно требованиям, приведенным в разделе 1, гл.1.7 ПУЭ, изд.7-е.

Электропроводка по всей длине электрооборудования должна обеспечивать возможность легкого распознания по цветам ПУЭ изд. 7, п. 1.1.29.

Все электрооборудование и материалы, применяемые при монтаже, должны иметь сертификат соответствия стандартам РФ. Сопротивление заземляющего устройства, в соответствии с требованиями ПУЭ не нормируется.

Сопротивление заземляющего устройства, в соответствии с требованиями ПУЭ не нормируется.

л) Сведения о типе, классе проводов и осветительной арматуры, которые подлежат применению при строительстве объекта капитального строительства

Магистральные и групповые сети выполнены трех- и пяти- проводными, кабелями марки ВВГнг(А)-LSLTx и ВВГнг(А)-FRLSLTx, (противопожарное оборудование) с медными жилами, проложенными:

- для распределительных линий осветительных и силовых нагрузок на горизонтальных участках - скрыто в трубах ПВХ, на перфорированных лотках по коридору;
- в подвальных помещениях – открыто в гофротрубах на скобах;
- для групповых сетей общего и аварийного освещения, силового оборудования и розеток – за подвесным потолком на лотках, опуски к выключателям или розеткам - скрыто в штробе в гофротрубе;

Гофрированные трубы из ПВХ должны иметь сертификат пожарной безопасности.

Прокладку и монтаж кабельных линий вести в соответствии со СНиП 3.05.06-85 и ПУЭ (изд.7).

Электропроводки противопожарных систем прокладываются отдельно от основных электросетей.

Проходы кабелей через стены и перегородки выполняются в строительных проемах с последующей заделкой легкосменяемым составом с огнестойкостью не менее

предела огнестойкости стен и перекрытия в которых они выполняются. Одиночных кабелей – в отрезках труб с герметизацией огнестойким материалом.

Сечение жил кабелей выбрано с учетом длительно допустимой токовой нагрузки в нормальном/аварийном режимах, и проверено по допустимым потерям напряжения.

Сечение жил кабелей выбрано по длительно допустимой токовой нагрузке и проверено по потерям напряжения.

Выбор световой арматуры выполнен в зависимости от назначения помещения, характеристики среды, величины требуемой освещенности и высоты подвеса светильников.

Провода, кабели, осветительная арматура, электрощитовое оборудование, электроустановочные изделия, используемые в проекте, должны иметь необходимые сертификаты соответствия и пожарной безопасности.

Вторичные распределительные щиты на этажах расположены в этажных технических помещениях, нишах по коридорам

Для освещения помещений здания применяются светодиодные светильники. Степень защиты светильников выбрана с учетом среды помещения.

м) Описание системы рабочего, дежурного и аварийного освещения

Согласно СП 158.13330.2014 и 256.1325800.2016 проект предусматривает следующие виды освещения:

- Рабочее освещение
- Аварийное освещение
- Эвакуационное освещение

Управление освещением коридоров, зон ожидания, тамбура главного входа и лестниц предусматривается дистанционно с поста охраны, для остальных помещений предусматривается управление освещением местное ручное с помощью выключателей.

Все светильники, соответствуют Российским стандартам. При выборе светильников учитывались следующие критерии:

- Спектр светоизлучения: от 3500К до 5000К (4000 К);
- Коэффициент пульсации: не более 10%, не более 5% при работе на ПК;
- Индекс цветопередачи Ra: не менее 80;
- Тип рассеивателя: опаловый, матовый.

Освещение спортивного зала обеспечивается светильниками с широким углом рассеивания. Для защиты от механических повреждений светильники оснащены металлическими решётками.

Обслуживание светильников в двусветных помещениях предусмотреть в следующем порядке:

- обеспечить безопасный доступ к светильникам с лестницы или подмости;
- при необходимости временно отключить отдельные группы светильников;
- очистить оптику и рассеиватели от пыли и загрязнений;
- проверить исправность встроенных световых модулей и блоков питания, при необходимости заменить неисправные модули;
- проверить крепления и электрические соединения;

Подключение встроенных и подвесных светильников производится через распаячную коробку. Все светильники подключаются к системе заземления.

Уровень освещенности помещений рассчитан на основании требований СП 52.13330.2016.Степень защиты светильников выбрана с учетом среды помещения. В качестве источников освещения выбраны светодиодные светильники.

Аварийное эвакуационное освещение предусматривается в коридорах, на лестничных клетках, по линиям основных проходов и обеспечивают нормируемую освещенность в любой точке на путях эвакуации не менее 0,5Лк. Аварийные светильники для путей эвакуации предусмотрены со встроенными блоками аварийного питания (БАП) с продолжительностью работы не менее 1ч . Светильники аварийного освещения должны быть отмечены «А». Согласно заданию на проектирование в учебных классах предусмотрено аварийное освещение.

Светильники аварийного освещения выбраны по аналогии со светильниками рабочего освещения, и соответствуют по внешнему виду. Освещенность на путях эвакуации (в том числе в начале и конце пути) и в местах оказания (предоставления) услуг для маломобильных групп - 100лк. Перепад освещенности между соседними помещениями и зонами предусмотрен не более 1:4.

В замкнутых пространствах здания (помещения различного функционального назначения, кабины уборной,), где инвалид, в том числе с дефектами слуха, может оказаться один, а также лифтовых холлах и зонах безопасности предусмотрено аварийное освещение. Эвакуационное освещение выполнено в соответствии с нормативами.

Нормы освещённости помещений приведены в таблице 3.

Таблица 3

№ п/п	Тип помещения	Нормы освещенности согласно СП 52.13330.2016, САНПИН 1.2.3685-21, СП 2.4.3648-20, Лк
1	Учебные кабинеты	300
2	Кабинеты информационных технологий	400
3	Кабинеты ИЗО	500
4	Лаборантские при учебных кабинетах	400
5	Мастерские трудового обучения	400

6	Комнаты инструкторов; кабинеты и комнаты преподавателей; кабинеты врачей	300
7	Процедурные	500
8	Места приготовления дезинфицирующих растворов	300
9	Залы ожидания мед.пункта	200
10	Тамбуры, вестибюли, гардеробы, коридоры, лестничные клетки	100
11	Санузлы (в т.ч. санузлы для девочек с комнатой личной гигиены)	75
12	Санузлы для МГН	100
13	Спортивные залы	200
14	Снарядные, инвентарные, кладовые	50
15	Актовый зал	200
16	Обеденный зал	200
17	Технические помещения (электрощитовые, венткамеры, насосные, водомерные узлы)	200
18	Серверные, кроссовые	400
19	Раздевальные, душевые	100
20	Горячие, холодные, заготовочные цехи	300
21	Доготовочный цех, моечные посуды	200
22	Загрузочный цех	100

н) Описание дополнительных и резервных источников электроэнергии

Данным проектом не предусматриваются резервные источники электроэнергии.

о) Перечень мероприятий по резервированию электроэнергии

По степени надежности электроснабжения электроприемники объекта относятся к потребителям II категории электроснабжения. Для электроприемников I категории предусматривается установка устройства автоматического ввода резерва – АВР.

о_1) Перечень энергопринимающих устройств аварийной и технологической брони и его обоснование

Данным проектом решения по аварийной и технологической брони не рассматриваются.

о_2) Сведения о типе и количестве установок, потребляющих электрическую энергию, параметрах и режимах их работы

Основным оборудованием объекта являются:

Работа в рабочее время: технологическое оборудование учебных классов (рабочие столы учащихся, учителей, лабораторное оборудование), оборудование пищеблока, оборудование актового зала.

Непрерывная работа: оборудование слаботочных сетей (серверное оборудование, блоки питания устройств безопасности здания), оборудование водоснабжения и водоотведения.

Работа в летнем режиме: оборудование кондиционирования, вентиляция.

Работа в зимнем режиме оборудование отопления, вентиляция.

Работа в пожарном режиме: оборудование дымоудаления, пожаротушения.

Приложение 1. Технические условия на технологическое присоединение к электрическим сетям ПАО «Россети Московский регион» энергопринимающих устройств

Приложение № _____
к договору ТП № _____
от "____" _____ 20___ г.

6 Район

№ И-25-00-145945/102/МС «_____»_____ 20 ___ г.

Технические условия
на технологическое присоединение к электрическим сетям
ПАО «Россети Московский регион» энергопринимающих устройств

Автономная некоммерческая организация "Развитие Городских Технологий"

1. Наименование энергопринимающих устройств заявителя: энергопринимающие устройства **Школы (пл. 6 314,9 кв.м.)**
2. Наименование и место нахождения объектов, в целях электроснабжения которых осуществляется технологическое присоединение энергопринимающих устройств заявителя: **Школа (пл. 6 314,9 кв.м.), 127006, г. Москва, пер. Старопименовский, д.5; 77:01:0001099:1064**.
3. Максимальная мощность присоединяемых энергопринимающих устройств заявителя составляет: **440 кВт.**

4. Категория надежности: **вторая.**
5. Класс напряжения электрических сетей, к которым осуществляется технологическое присоединение: **0,4 кВ**.
6. Год ввода в эксплуатацию энергопринимающих устройств заявителя: в сроки, устанавливаемые Договором об осуществлении технологического присоединения, но не позднее окончания срока действия настоящих технических условий.

7. Точка (точки) присоединения и распределение максимальной мощности по каждой точке присоединения (указанное распределение максимальной мощности по точкам присоединения является условным, фактическое распределение максимальной мощности может отличаться от указанного в зависимости от режима работы энергосистемы):
7.1. 1-4 точки - вновь сооружаемые КЛ-0,4 кВ, отходящие от секции РУ-0,4кВ ТП-10/0,4кВ № новая – 440 кВт.
8. Основной источник питания: **ПС 220 кВ Центральная № 378 220/10/10/6/ кВ.**
9. Резервный источник питания: **Отсутствует.**
10. ПАО «Россети Московский регион» выполнить:
10.1. Мероприятия по строительству объектов электросетевого хозяйства ПАО «Россети Московский регион» от существующих объектов электросетевого хозяйства ПАО «Россети Московский регион» до присоединяемых энергопринимающих устройств и (или) объектов электросетевого хозяйства Заявителя:
10.1.1. Строительство блочной комплектной двухтрансформаторной подстанции 10/0,4 кВ, 1 шт. (ТП-10/0,4 кВ №нов.). Для присоединения Заявителя установить 2 трансформатора мощностью по 400 кВА. РазмещениеТП выполнить на территории земельного участка Заявителя. Предусмотреть возможность круглогодичного подъезда персонала к ТП.
10.1.2. Установить 2 комбинированные сборки н/н с защитой в части МКС на трехполюсных автоматических выключателях и электронным расцепителем, имеющим две ступени защиты регулируемых как по току, так и по времени.
10.1.3. Выполнить телемеханизацию и АИИС КУЭ ТП-10/0,4кВ № новая в соответствии с типовыми техническими решениями, утвержденными в МКС – филиале ПАО «Россети Московский регион», и в объеме ТС, ТИ, ТУ, согласованными стехническими службами

МКС –филиала ПАО «Россети Московский регион». Организовать основной и резервный каналы связи, арендованные у операторов связи, имеющих подключение к технологической сети передачи данных МКС – филиала ПАО «Россети Московский регион». Тип и эксплуатационные характеристики необходимо согласовать с техническими службами МКС – филиала ПАО «Россети Московский регион».

10.1.4. Строительство КЛ-10кВ, 2 шт., от РУ-10 кВ новой ТП-10/0,4кВ до врезки в КЛ направления ТП-10/0,4кВ № 11701– РП-10кВ № 11086. Ориентировочная протяженность каждой КЛ – 0,300 км, сечение кабеля 185 кв. мм.:

- протяженность каждой КЛ в траншее с благоустройством– 0,100 км;

- протяженность каждой КЛ в закрытых переходах методом ГНБ, выполняемых тремя трубами ПНД диаметром 160 мм– 0,200 км.

10.1.5. Строительство КЛ-10кВ, 2 шт., от РУ-10 кВ новой ТП-10/0,4кВ до врезки в КЛ направления ТП-10/0,4кВ № 11701– РП-10кВ № 11086 . Ориентировочная протяженность каждой КЛ – 0,300 км, сечение кабеля 185 кв. мм.:

- протяженность каждой КЛ в траншее с благоустройством– 0,100 км;

- протяженность каждой КЛ в закрытых переходах методом ГНБ, выполняемых тремя трубами ПНД диаметром 160 мм– 0,200 км.

10.1.6. Строительство КЛ-0,4кВ, 2 шт., от сборок НН с.ш. РУ-0,4кВ ТП-10/0,4кВ № новая до ГРЩ-0,4кВ. Ориентировочная протяженность каждой многожильной КЛ сечением 240 кв.мм. с пластмассовой изоляцией – 0,1 км, из них:

- протяженность каждой КЛ в траншее с благоустройством – 0,07 км;

- протяженность каждой КЛ в закрытых переходах методом ГНБ, выполняемых тремя трубами ПНД диаметром 160 мм– 0,03 км.

10.1.7. Строительство КЛ-0,4кВ, 2 шт., от сборок НН с.ш. РУ-0,4кВ ТП-10/0,4кВ № новая до ГРЩ-0,4кВ. Ориентировочная протяженность каждой многожильной КЛ сечением 240 кв.мм. с пластмассовой изоляцией – 0,1 км, из них: - протяженность каждой КЛ в траншее с благоустройством – 0,07 км; - протяженность каждой КЛ в закрытых переходах методом ГНБ, выполняемых тремя трубами ПНД диаметром 160 мм– 0,03 км.

10.2. Мероприятия по развитию существующей инфраструктуры ПАО «Россети Московский регион» в целях создания технической возможности технологического присоединения энергопринимающих устройств и (или) объектов электросетевого хозяйства Заявителя:

10.2.1. Существующие КЛ-0,4 кВ направлением ТП-10/0,4кВ № 17601 – ВРЩ-0,4 кВ № 90416 вывести из эксплуатации.

10.3. Мероприятия, выполняемые ПАО «Россети Московский регион» по обеспечению учета электрической энергии (мощности) с использованием приборов учета электрической энергии, в том числе включенных в состав измерительных комплексов:

10.3.1. Установка средств коммерческого учёта электрической энергии (мощности) трёхфазных полукосвенного включения в количестве 2 шт в ГРЩ заявителя (место установки согласовать с 6 ремонтно-эксплуатационным районом). Параметры установки определить в соответствии с типовыми техническими решениями по организации учёта электроэнергии.

11. Заявителю выполнить:

11.1. Мероприятия, выполняемые Заявителем и необходимые для осуществления технологического присоединения:

11.1.1. Строительство нов. ГРЩ-0,4кВ Заявителя по 2 категории надежности (ГРЩ установить не далее стены фасада здания).

11.1.2. Предоставить земельный участок для размещения ТП-10/0,4 кВ № нов. ПАО «Россети Московский регион» на свободной от инженерных коммуникаций площадке.

11.1.3. Обеспечить предоставление сетевой организации мест установки приборов учета электрической энергии.

11.1.4. Нагрузку распределить равномерно (в рамках границ балансовой принадлежности).

11.1.5. Запрещается замыкание в транзит элементов электрической сети 0,4 кВ Заявителя, работающих раздельно от разных источников электроснабжения при нормальном режиме эксплуатации.
11.1.6. Установку защиты на вводе заявителя для питания ЭПУ трехполюсный автоматический выключатель и электронным расцепителем, имеющим две ступени защиты, регулируемых как по току, так и по времени, обеспечив селективность работы защит выбранного автоматического выключателя и автоматического выключателя в части ПАО «Россети Московский регион».
11.1.7. Существующий ВРЩ-0,4 кВ № 90416 вывести из эксплуатации.

В случае, если размещение приборов учета электрической энергии и (или) иного оборудования, необходимого для обеспечения коммерческого учета электрической энергии, возможно только на объектах Заявителя, Заявитель обязан на безвозмездной основе обеспечить предоставление сетевой организации мест размещения приборов учета электрической энергии и (или) иного оборудования, необходимого для обеспечения коммерческого учета электрической энергии, и доступа к таким местам размещения приборов учета и указанного оборудования для их установки.
11.2. Разработать проектную (рабочую) документацию внутреннего электроснабжения объекта на основе Градостроительного кодекса, ПУЭ и НТД (предусмотреть мероприятия по установке приборов учета электроэнергии, устройств релейной защиты и автоматики, телемеханики и коммутационных аппаратов), в случае, если в соответствии с законодательством РФ о градостроительной деятельности разработка проектной документации является обязательной.
11.3. Проектом определить необходимость установки устройств компенсации реактивной мощности, их вид, количество, номинальные данные и места подключения. Устройства компенсации реактивной мощности должны обеспечивать степень компенсации реактивной мощности в точках присоединения энергопринимающих устройств Заявителя напряжением 0,4 кВ не выше 0,35 (tg φ меньше или равно 0,35)
11.4. В случае необходимости разработки проекта в соответствии с требованиями, указанными в пункте 11.2 настоящих технических условий, принимаемые на стадии проектирования технические решения, а так же сам проект внутреннего электроснабжения Заявителя, согласовать с филиалом ПАО «Россети Московский регион»
11.5. В случае наличия нагрузок, искажающих форму кривой электрического тока и вызывающих несимметрию напряжения в точках присоединения, установить в электрических сетях Заявителя фильтрокомпенсирующие устройства, исключающие ухудшение качества электроэнергии в соответствии с ГОСТ 32144-2013, а также средства измерения и регистрации качества электроэнергии и соотношения потребления активной и реактивной мощности с передачей указанной информации в ПАО «Россети Московский регион».
11.6. Для электроснабжения электроприемников, относящихся к первой категории надежности, внезапный перерыв снабжения электрической энергией которых может повлечь угрозу жизни и здоровью людей, экологической безопасности либо безопасности государства, Заявитель обеспечивает установку автономных резервных источников питания или резервирование вышеуказанных электроприемников по внутренней сети Заявителя. При установке автономных резервных источников питания Заявитель обязан поддерживать устанавливаемые автономные резервные источники питания в состоянии готовности к использованию при возникновении внерегламентных отключений, введении аварийных ограничений режима потребления электрической энергии (мощности) или использовании противоаварийной автоматики.
12. Общие требования:
12.1. Присоединение энергопринимающих устройств осуществляется к сетям общего назначения, обеспечивающим качество электроэнергии в соответствии с ГОСТ 32144-2013.

12.2. В случае если в ходе проектирования возникает необходимость частичного отступления от технических условий, такие отступления подлежат согласованию с ПАО «Россети Московский регион», с корректировкой утвержденных технических условий.
12.3. Фактическое присоединение энергопринимающих устройств будет произведено после осмотра (обследования) присоединяемых энергопринимающих устройств должностным лицом ПАО «Россети Московский регион» при участии Заявителя и после подписания акта осмотра (обследования).
12.4. Настоящий документ является неотъемлемой частью Договора № _____ от **"_____" _____ 20___ г.** об осуществлении технологического присоединения энергопринимающих устройств к электрической сети и без заключения Договора является недействительным и не создает никаких прав и/или обязанностей.
12.5. Вариант цены (тарифа): **одноставочный тариф без дифференц. по зонам суток.**
12.6. Условия учета потребления электрической энергии: **однотарифный учет в целом за расчетный период.**
12.7. Вид деятельности: **Для бытовых нужд**.
12.8. Срок действия настоящих технических условий составляет **2 года** со дня заключения **договора** об осуществлении технологического присоединения к электрическим сетям.

ПОДПИСАНО
ЭЛЕКТРОННОЙ ПОДПИСЬЮ
a853f171
Директор департамента инженерного обеспечения технологического присоединения филиала ПАО «Россети Московский регион» - Московские кабельные сети
С.С.Горностаев

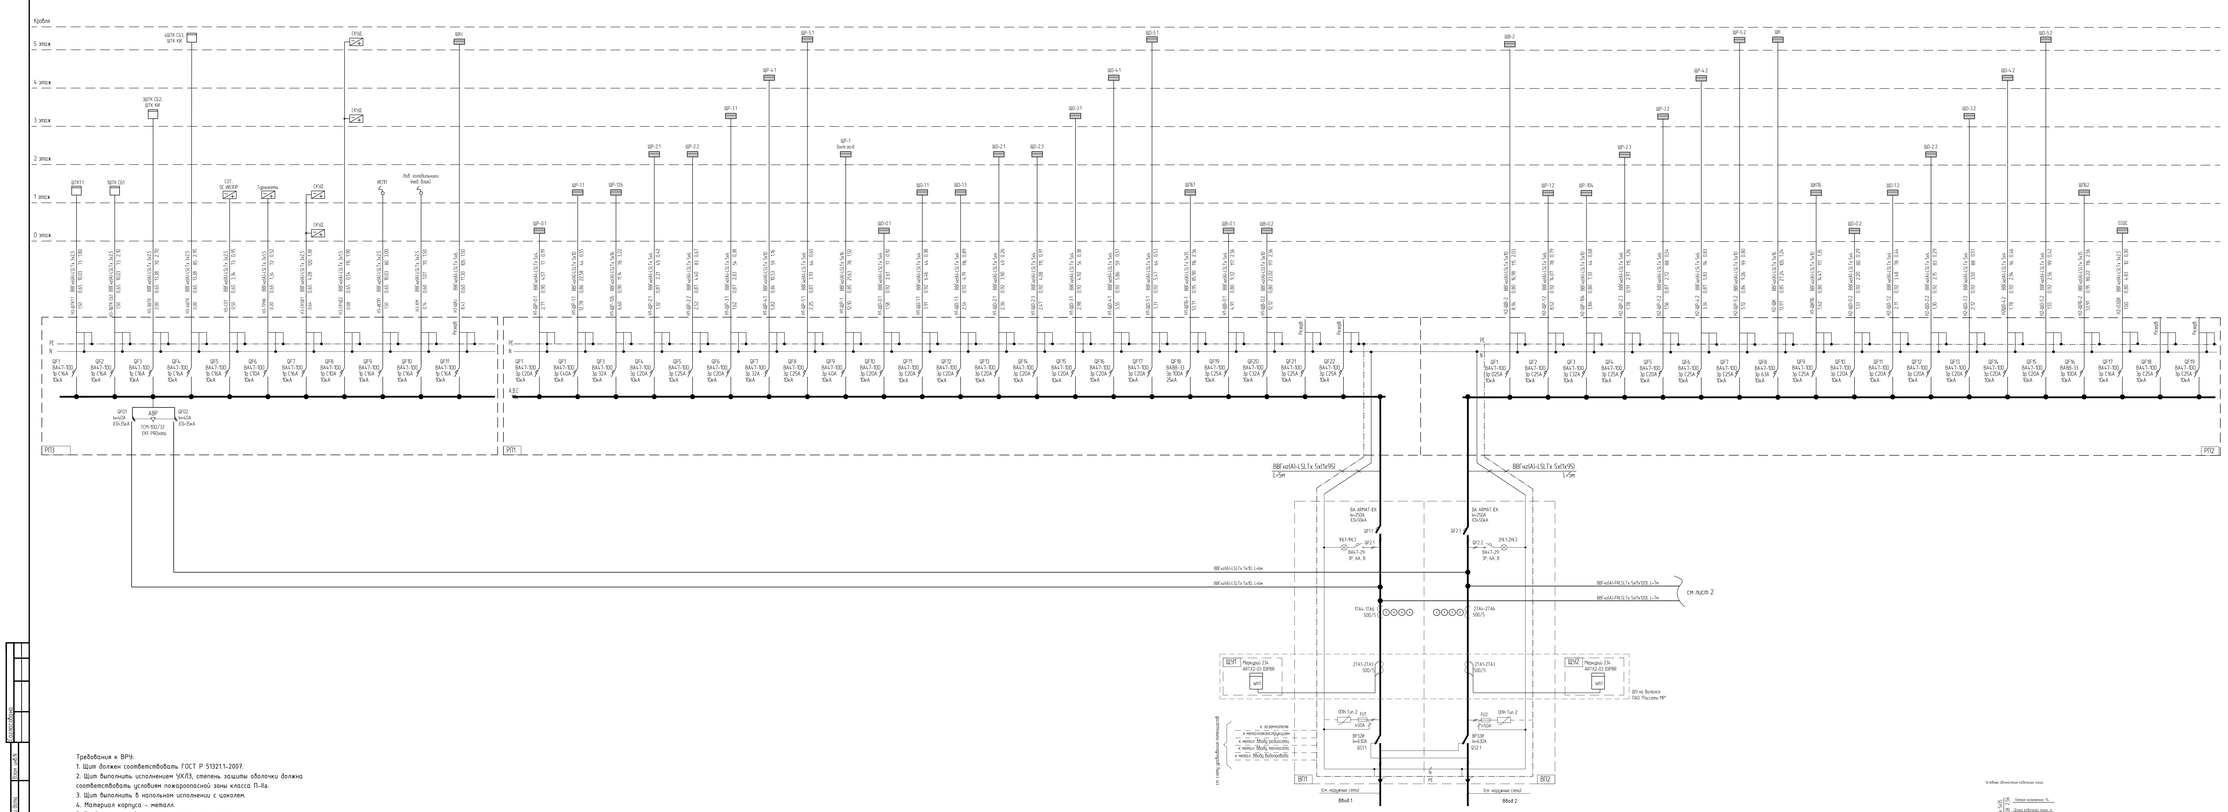
Кровля
5 этаж
4 этаж
3 этаж
2 этаж
1 этаж
0 этаж
ЩПТ11
ЩПТ4 СП1
ЩПТ4 СП2
ЩПТ4 ПР
СПЕ ОС ИВЭПР
Турникеты
ОУОЛ
ИОЛ
Лоб кожухотроп (нет Взо)
ЩР-0.1
ЩР-0.2
ЩР-1.1
ЩР-1.2
ЩР-2.1
ЩР-2.2
ЩР-3.1
ЩР-3.2
ЩР-4.1
ЩР-4.2
ЩР-5.1
ЩР-5.2
ЩР-6
ЩР-7
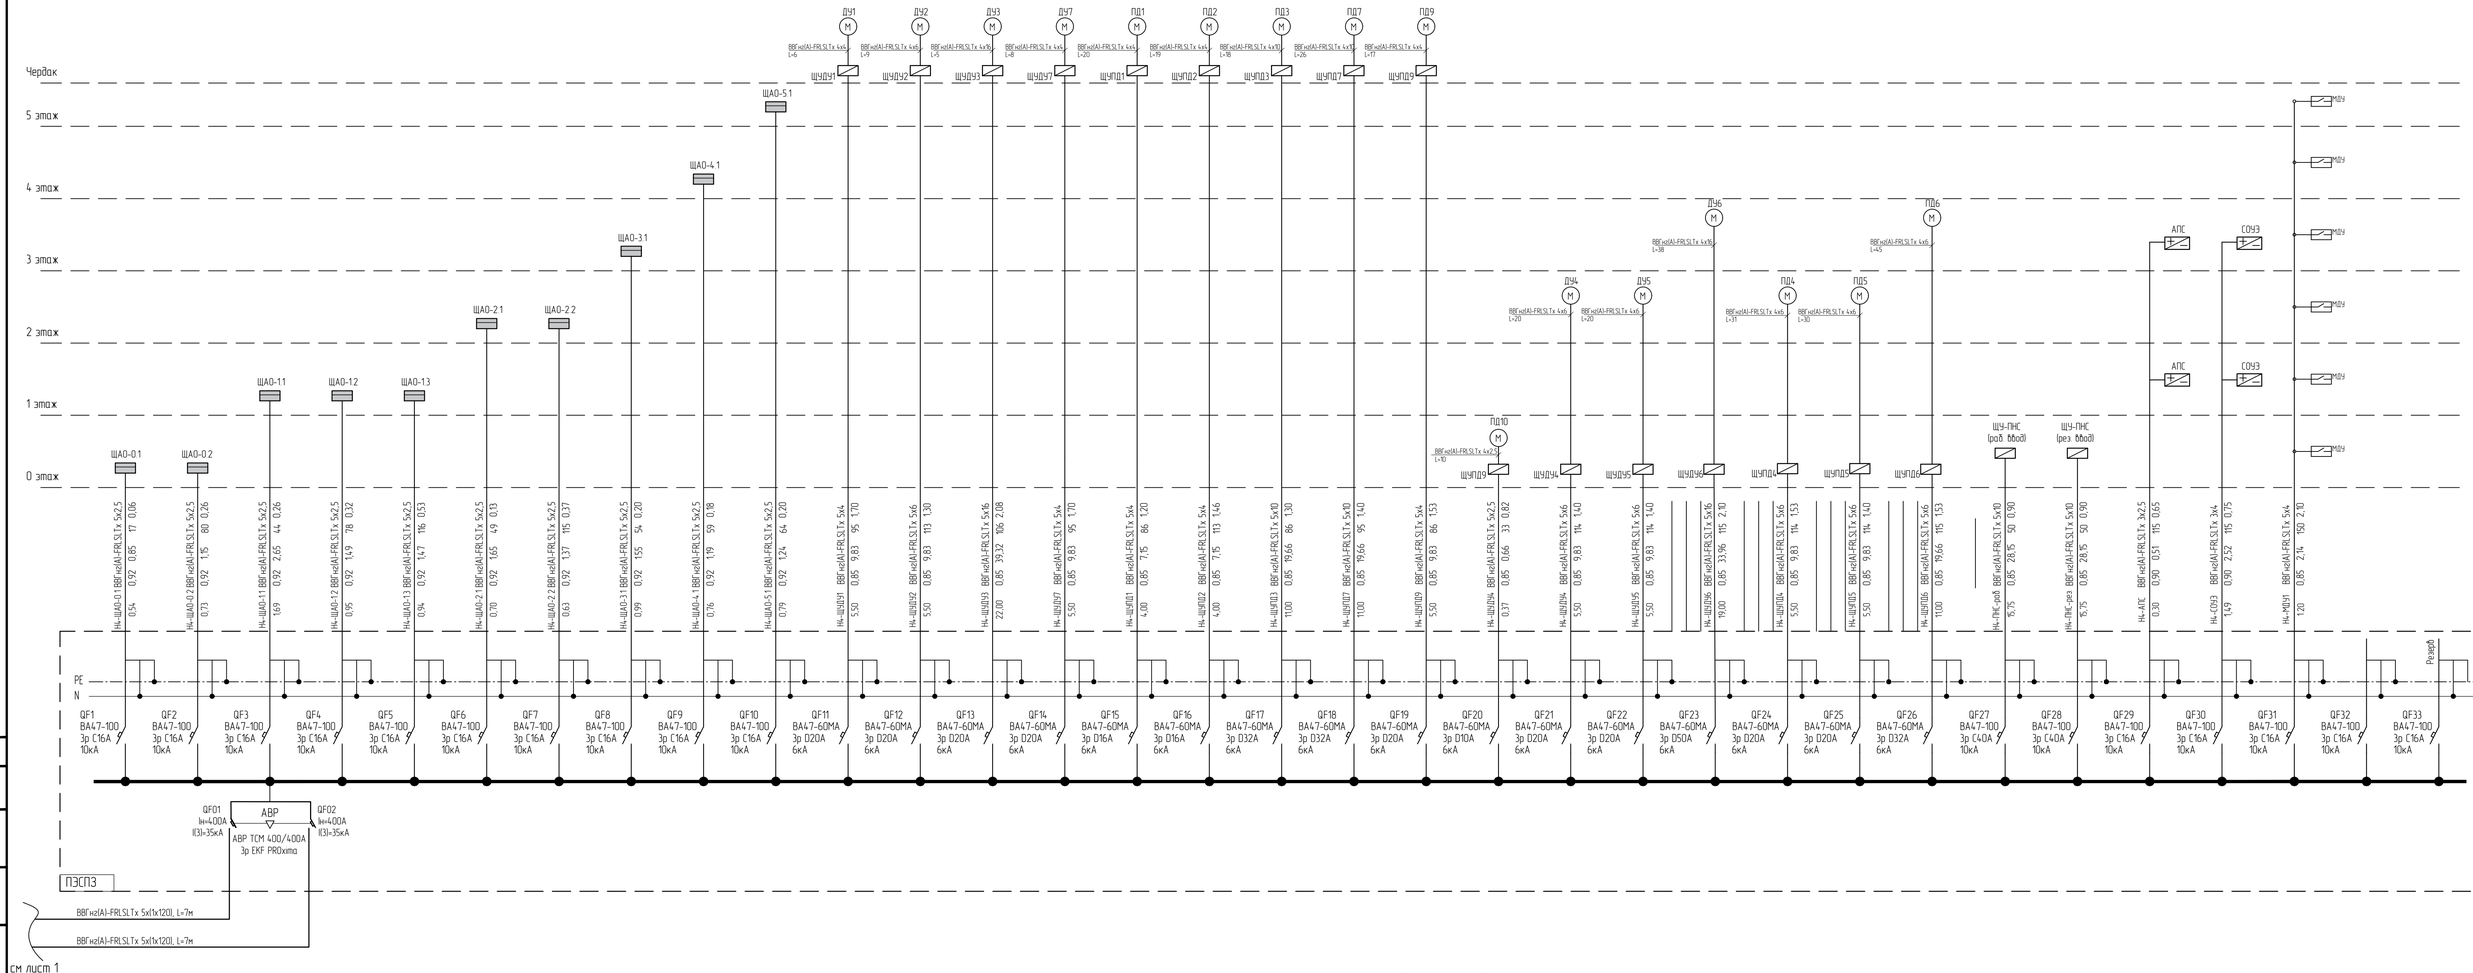

Требования к ПЭСПЗ:

1. Щит должен соответствовать ГОСТ Р 51321.1-2007.
2. Щит выполнить исполнением УХЛ3, степень защиты оболочки должна соответствовать условиям пожароопасной зоны класса П-IIа.
3. Щит выполнить в напольном исполнении с цоколем.
4. Материал корпуса – металл.
5. Предусмотреть возможность запирания на ключ.
6. Предусмотреть ввод питающего кабеля снизу через мембранные фланцы.
7. Предусмотреть вывод отходящих линий сверху через мембранные фланцы.
8. Коммутационно-защитная аппаратура производства «IEK».

						2024-00375-01-0-ИОС1	
						Капитальный ремонт здания Государственного бюджетного общеобразовательного учреждения города Москвы «Школа № 1574» по адресу г. Москва, Старопименовский пер., д №5	
Изм.	Колич.	Лист	№док.	Подп.	Дата		
Разраб.		Семенов			02.2025	Система электроснабжения	Стадия: П; Лист: 2; Листов:
Провер.		Пильгуй Н.М.			02.2025		
Н. контр.		Пильгуй Н.М.			02.2025	Однолинейная схема ПЭСПЗ	МОСЖИЛ НИИПРОЕКТ
Нач. ОПИС №1		Белоусова Д.П.			02.2025		

Согласовано

Взам. инв.№

Подпись и дата

Инв.№ подл.

Формат А3 х 3

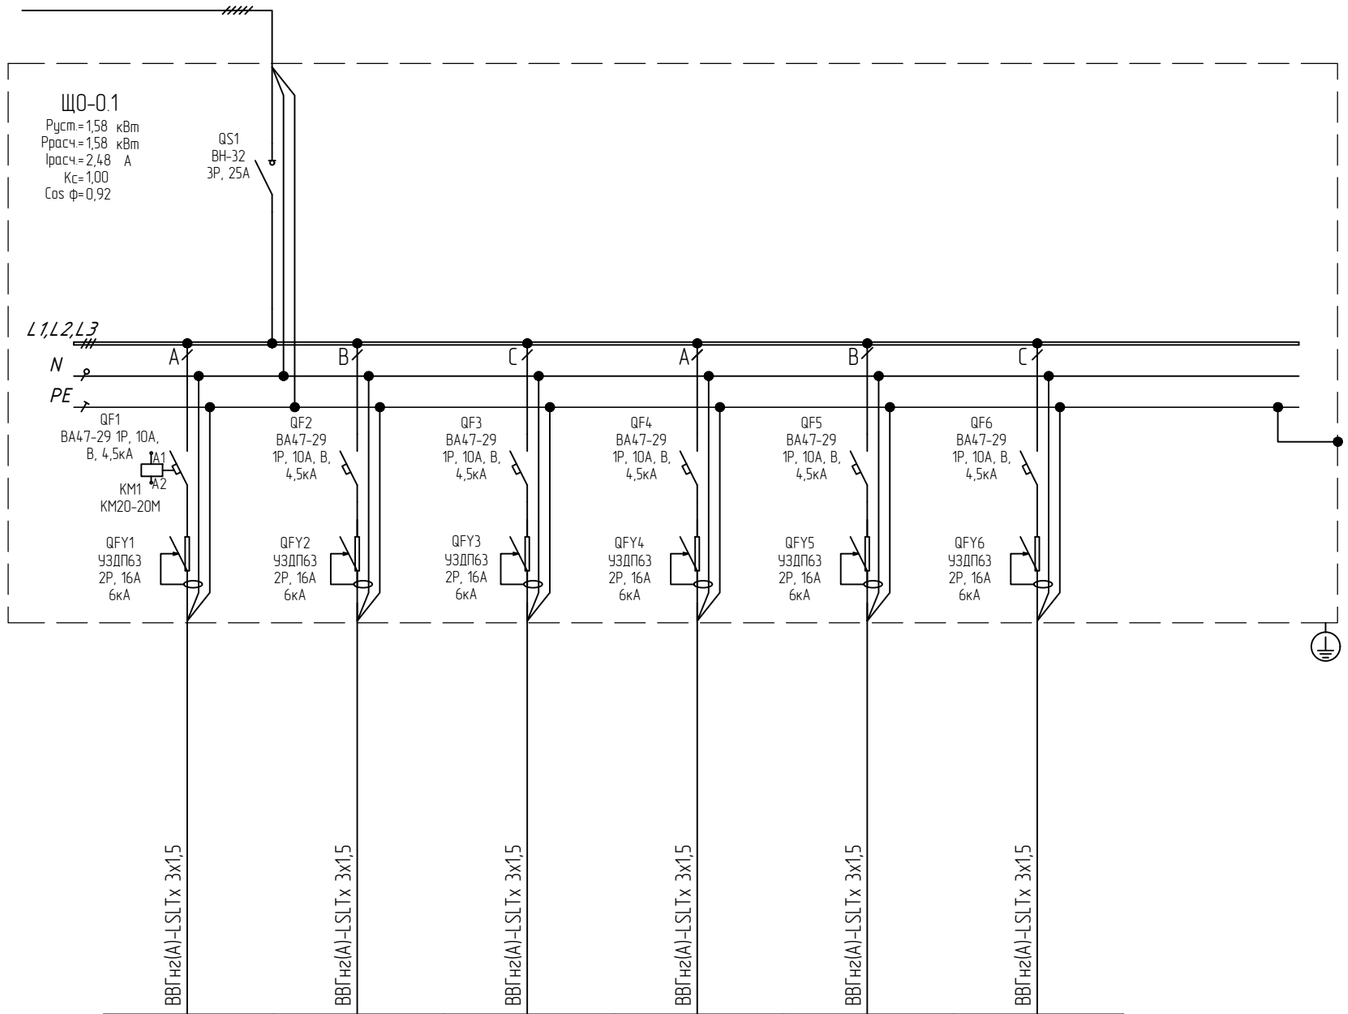

Электроприёмники						
	номер группы	0-0.1-1	0-0.1-2	0-0.1-3	0-0.1-4	0-0.1-5	
	Руст. (кВт)	0,22	0,31	0,64	0,34	0,06	
	Iр. (А)	1,03	1,43	2,93	1,57	0,26	
	Наименование	Рабочее освещение	Рабочее освещение	Рабочее освещение	Рабочее освещение	Рабочее освещение	Резерв
	Помещения	008	011-017, 004	010	008, 009, 020.б, 020.а, 020.б, 025-027	017	
	Марка и сечение кабелей	ВВГнг(А)-LSLTx 3х1,5	ВВГнг(А)-LSLTx 3х1,5	ВВГнг(А)-LSLTx 3х1,5	ВВГнг(А)-LSLTx 3х1,5	ВВГнг(А)-LSLTx 3х1,5	ВВГнг(А)-LSLTx 3х1,5
	Длина участка сети						

Согласовано

Взам. инв.N

Подпись и дата

Инв.N подл.

Изм.	Кол.уч.	Лист	N°док.	Подп.	Дата
Разраб.		Семенов			02.2025
Провер.		Пильгуй М.Н.			02.2025
Н. контр.		Пильгуй Н.М			02.2025
Нач. ОПИС N°1		Белоусова Д.П.			02.2025

2024-00375-01-0-ИОС1

Капитальный ремонт здания Государственного бюджетного общеобразовательного учреждения города Москвы «Школа № 1574» по адресу: г. Москва, Старопименовский пер., д. №5

Система электроснабжения

Стадия	Лист	Листов
П	3	

Щит ЩО-0.1. Схема электрическая принципиальная

МОСЖИЛ НИИПРОЕКТ

Формат А3 х 1

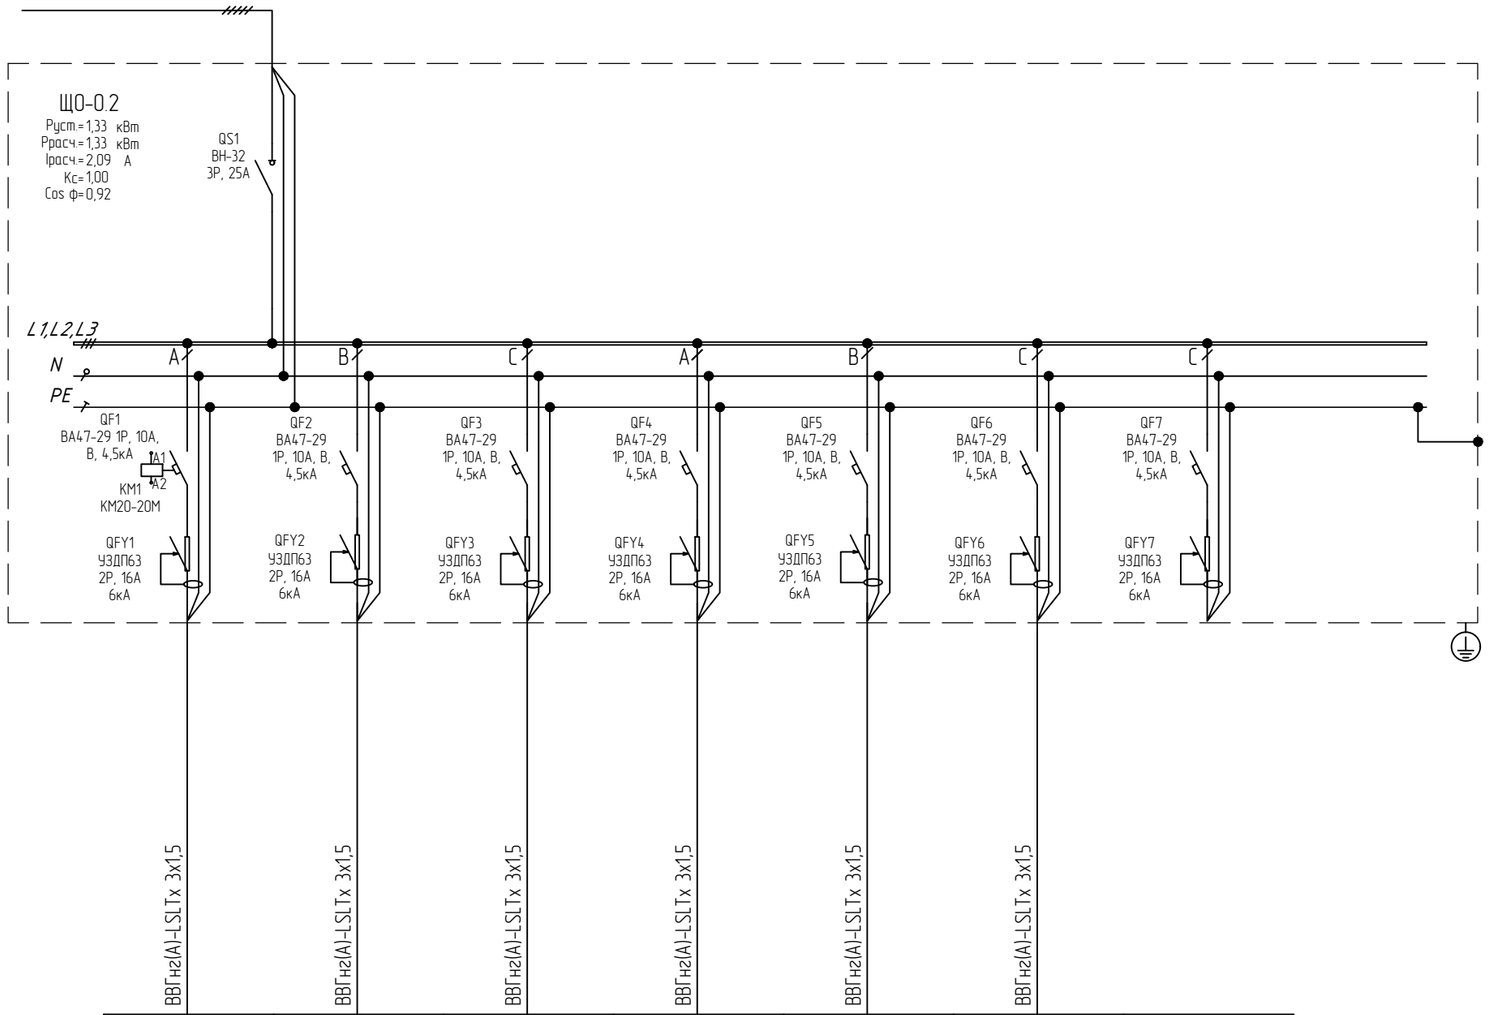

Электроприёмники	номер группы	0-0.2-1	0-0.2-2	0-0.2-3	0-0.2-4	0-0.2-5	0-0.2-6	
	Руст. (кВт)	0,25	0,25	0,28	0,21	0,28	0,18	
	Ip. (А)	1,12	1,12	1,28	0,96	1,28	0,80	
	Наименование	Рабочее освещение	Рабочее освещение	Рабочее освещение	Рабочее освещение	Рабочее освещение	Рабочее освещение	Резерв
	Помещения	005, 006, 019, 020	024, 024а, 023, 018, 024б, 022	021, 021б, 021а,	001, 002	021г, 021в	02, 03, 04	
	Марка и сечения кабелей	ВВГнг(А)-LSLTx 3х1,5	ВВГнг(А)-LSLTx 3х1,5	ВВГнг(А)-LSLTx 3х1,5	ВВГнг(А)-LSLTx 3х1,5	ВВГнг(А)-LSLTx 3х1,5	ВВГнг(А)-LSLTx 3х1,5	
	Длина участка сети							

Согласовано

Взам. инв.N

Подпись и дата

Инв.N подл.

Изм.	Кол.уч.	Лист	№док.	Подп.	Дата
Разраб.		Семенов			02.2025
Провер.		Пильгуй М.Н.			02.2025
Н. контр.		Пильгуй Н.М			02.2025
Нач. ОПИС №1		Белоусова Д.П.			02.2025

2024-00375-01-0-ИОС1

Капитальный ремонт здания Государственного бюджетного общеобразовательного учреждения города Москвы «Школа № 1574» по адресу: г. Москва, Старопименовский пер., д. №5

Система электроснабжения

Стадия	Лист	Листов
П	4	

Щит ЩО-0.2. Схема электрическая принципиальная

МОСЖИЛ НИИПРОЕКТ

Формат А3 х 1

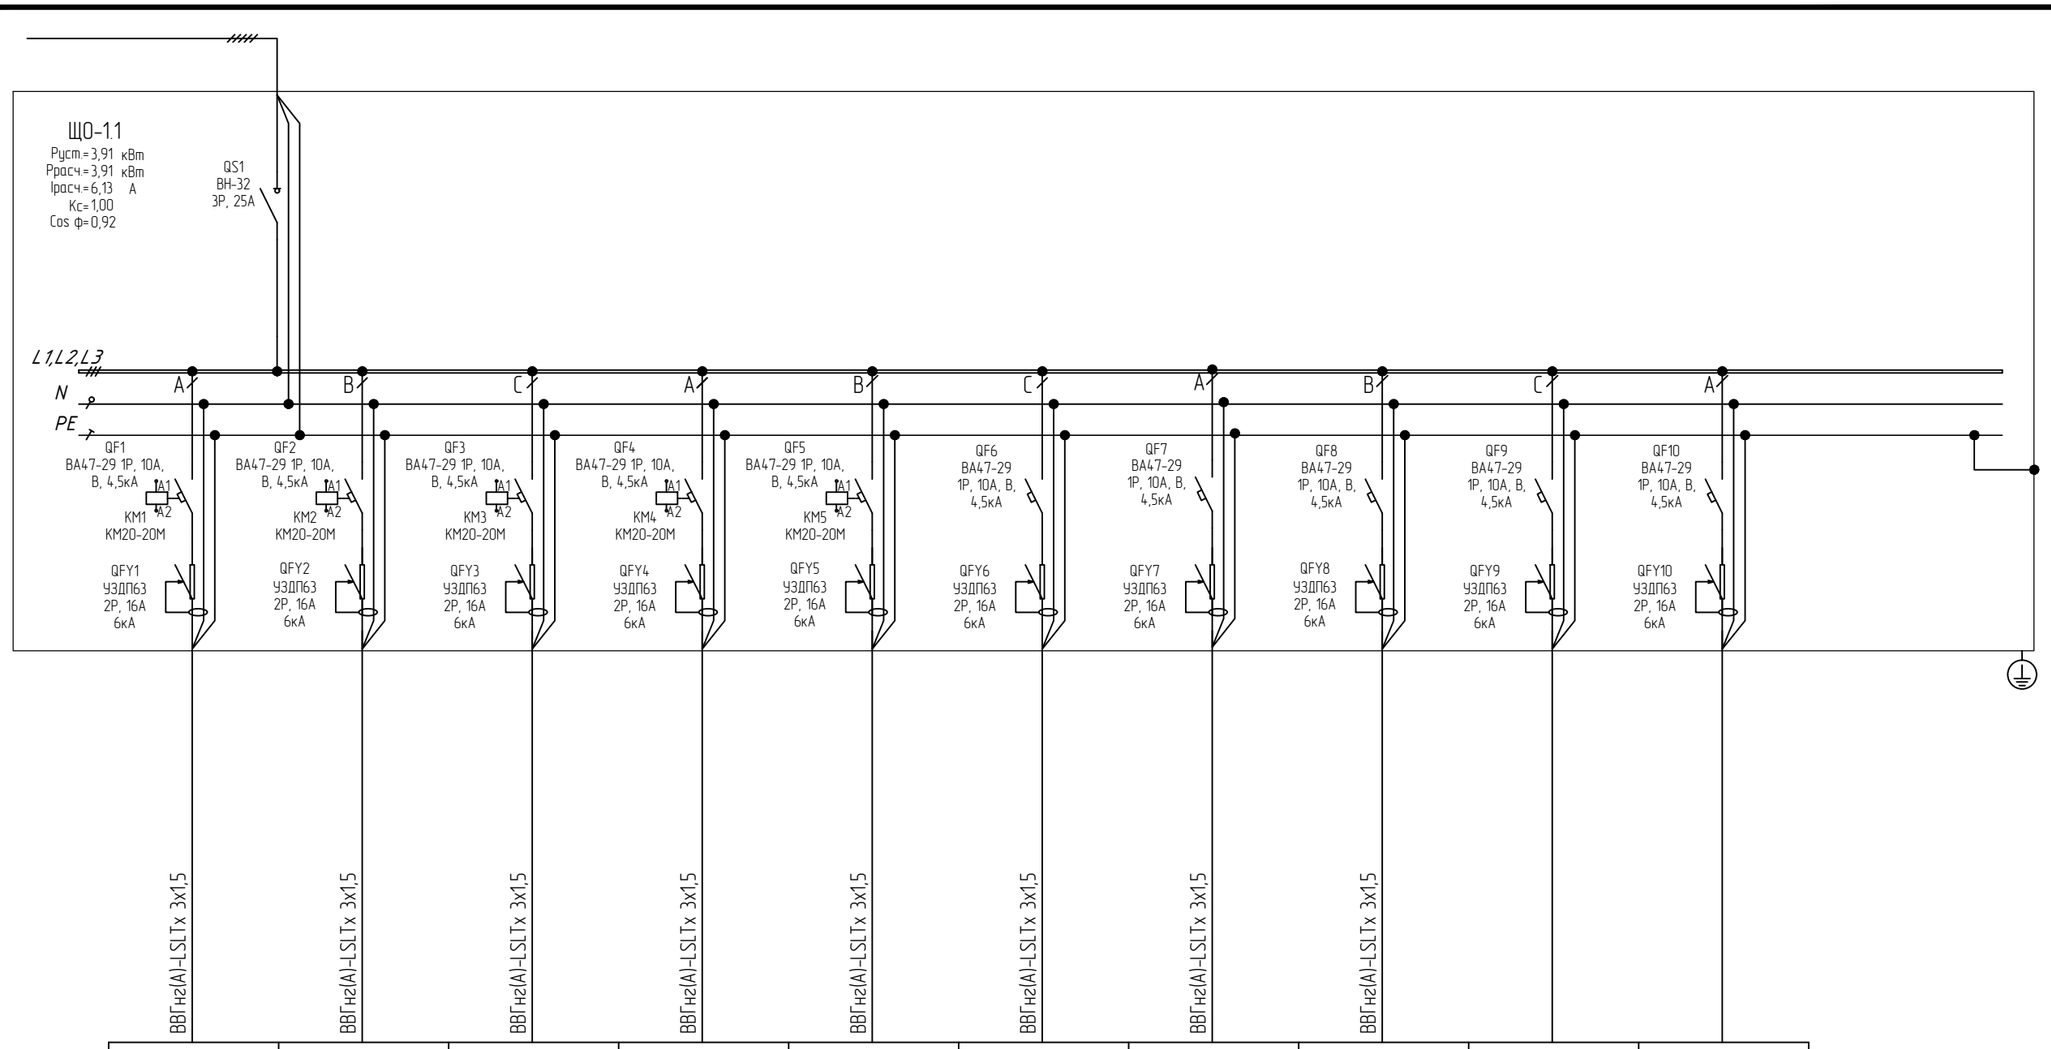

Щит распределительный		
	Аппараты ввода	Тип Iном. (А) Iу. (мА)
	Аппараты отходящих линий	Тип Iном. (А) Iу. (мА)
Марка и сечения кабелей		ВВГнг(А)-LSLTx 3х1,5
Длина участка сети		

Электроприёмники									
номер группы	0-1.1-1	0-1.1-2	0-1.1-3	0-1.1-4	0-1.1-5	0-1.1-6	0-1.1-7	0-1.1-8		
Руст. (кВт)	0,25	0,60	0,36	0,30	0,42	1,12	0,50	0,36		
Ip. (А)	1,15	2,75	1,62	1,37	1,92	5,14	2,31	1,67		
Наименование	Рабочее освещение	Рабочее освещение	Рабочее освещение	Рабочее освещение	Рабочее освещение	Рабочее освещение	Рабочее освещение	Рабочее освещение	Резерв	Резерв
Помещения	110, 114	106, 105, 209, 310, 408, 509	101, 102, 116	115, 118, 215	107, 108, 109	111, 113, 119	104	103		

Согласовано

Взам. инв.N

Подпись и дата

Инв.N подл.

Изм.	Кол.уч.	Лист	N°док.	Подп.	Дата
Разраб.		Семенов			02.2025
Провер.		Пильгуй М.Н.			02.2025
Н. контр.		Пильгуй Н.М			02.2025
Нач. ОПИС №1		Белоусова Д.П.			02.2025

2024-00375-01-0-ИОС1

Капитальный ремонт здания Государственного бюджетного общеобразовательного учреждения города Москвы «Школа № 1574» по адресу: г. Москва, Старопименовский пер., д. №5

Система электроснабжения

Стадия	Лист	Листов
П	5	

Щит ЩО-1.1. Схема электрическая принципиальная

МОСЖИЛ НИИПРОЕКТ

Формат А3 х 1

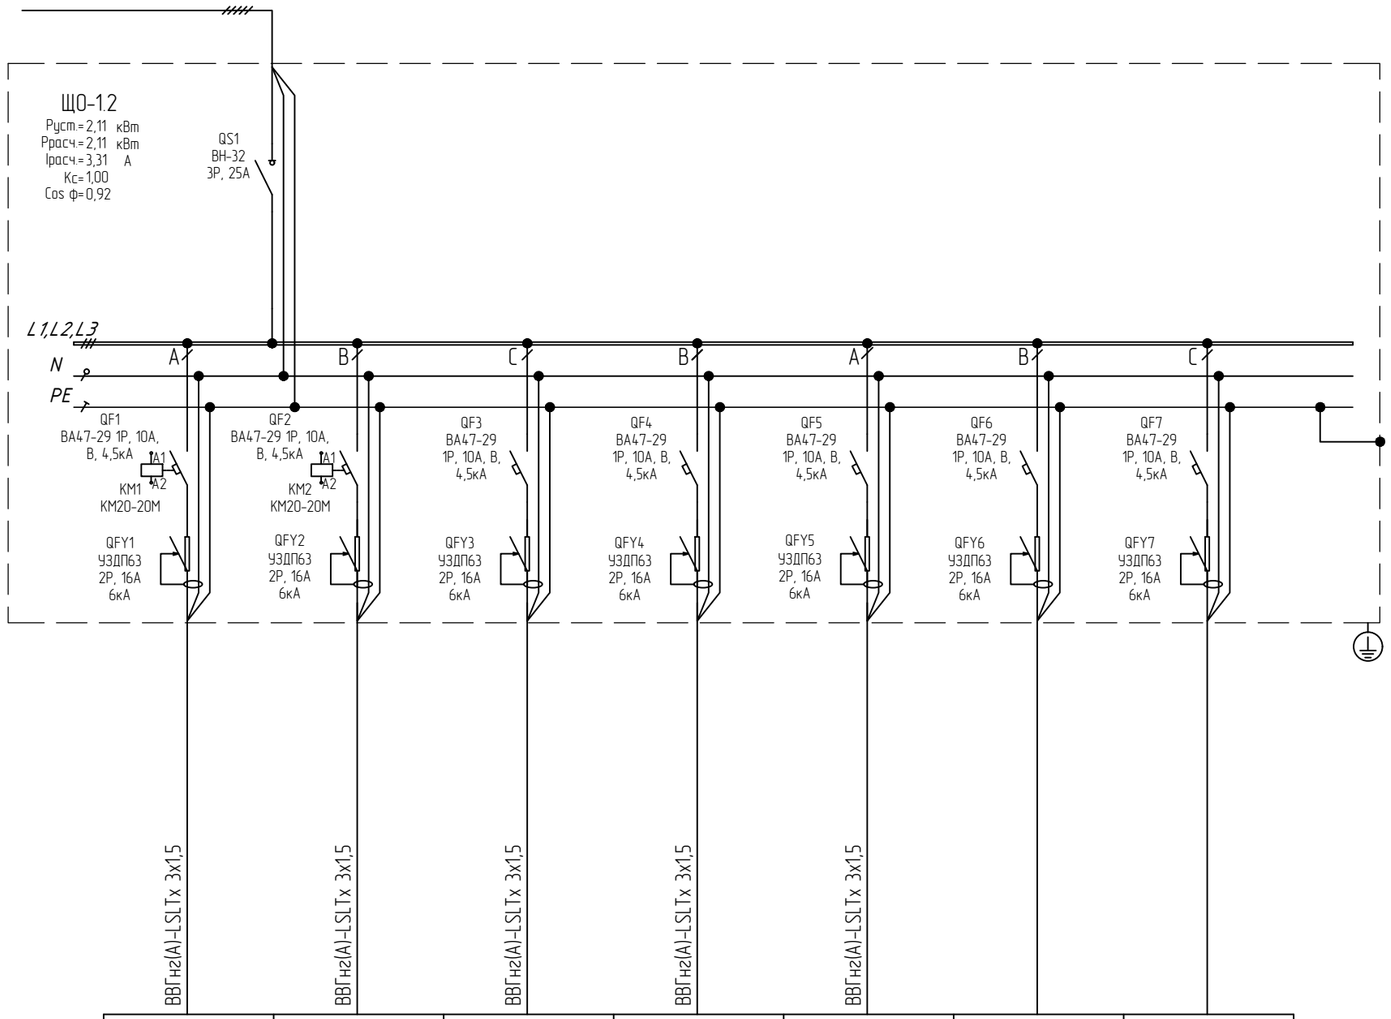

Электроприёмники	номер группы	0-1.2-1	0-1.2-2	0-1.2-3	0-1.2-4	0-1.2-5	0-1.2-6	
	Руст. (кВт)	0,14	0,63	0,77	0,13	0,32	0,14	
	Iр. (А)	0,64	2,89	3,54	0,60	1,47	0,66	
	Наименование	Рабочее освещение	Рабочее освещение	Рабочее освещение	Рабочее освещение	Рабочее освещение	Рабочее освещение	Резерв
	Помещения	128	128, 201, 301, 401, 501	126	112, 120	126	123-125	
Марка и сечение кабелей		ВВГнг(А)-LSLTx 3х1,5	ВВГнг(А)-LSLTx 3х1,5	ВВГнг(А)-LSLTx 3х1,5	ВВГнг(А)-LSLTx 3х1,5	ВВГнг(А)-LSLTx 3х1,5		
Длина участка сети								

Согласовано

Взам. инв.N

Подпись и дата

Инв.N подл.

Изм.	Кол.уч.	Лист	N°док.	Подп.	Дата
Разраб.		Семенов			02.2025
Провер.		Пильгуй М.Н.			02.2025
Н. контр.		Пильгуй Н.М			02.2025
Нач. ОПИС N°1		Белоусова Д.П.			02.2025

2024-00375-01-0-ИОС1

Капитальный ремонт здания Государственного бюджетного общеобразовательного учреждения города Москвы «Школа № 1574» по адресу: г. Москва, Старопименовский пер., д. №5

Система электроснабжения

Стадия	Лист	Листов
П	6	

Щит ЩО-1.2. Схема электрическая принципиальная

МОСЖИЛ НИИПРОЕКТ

Формат А3 х 1

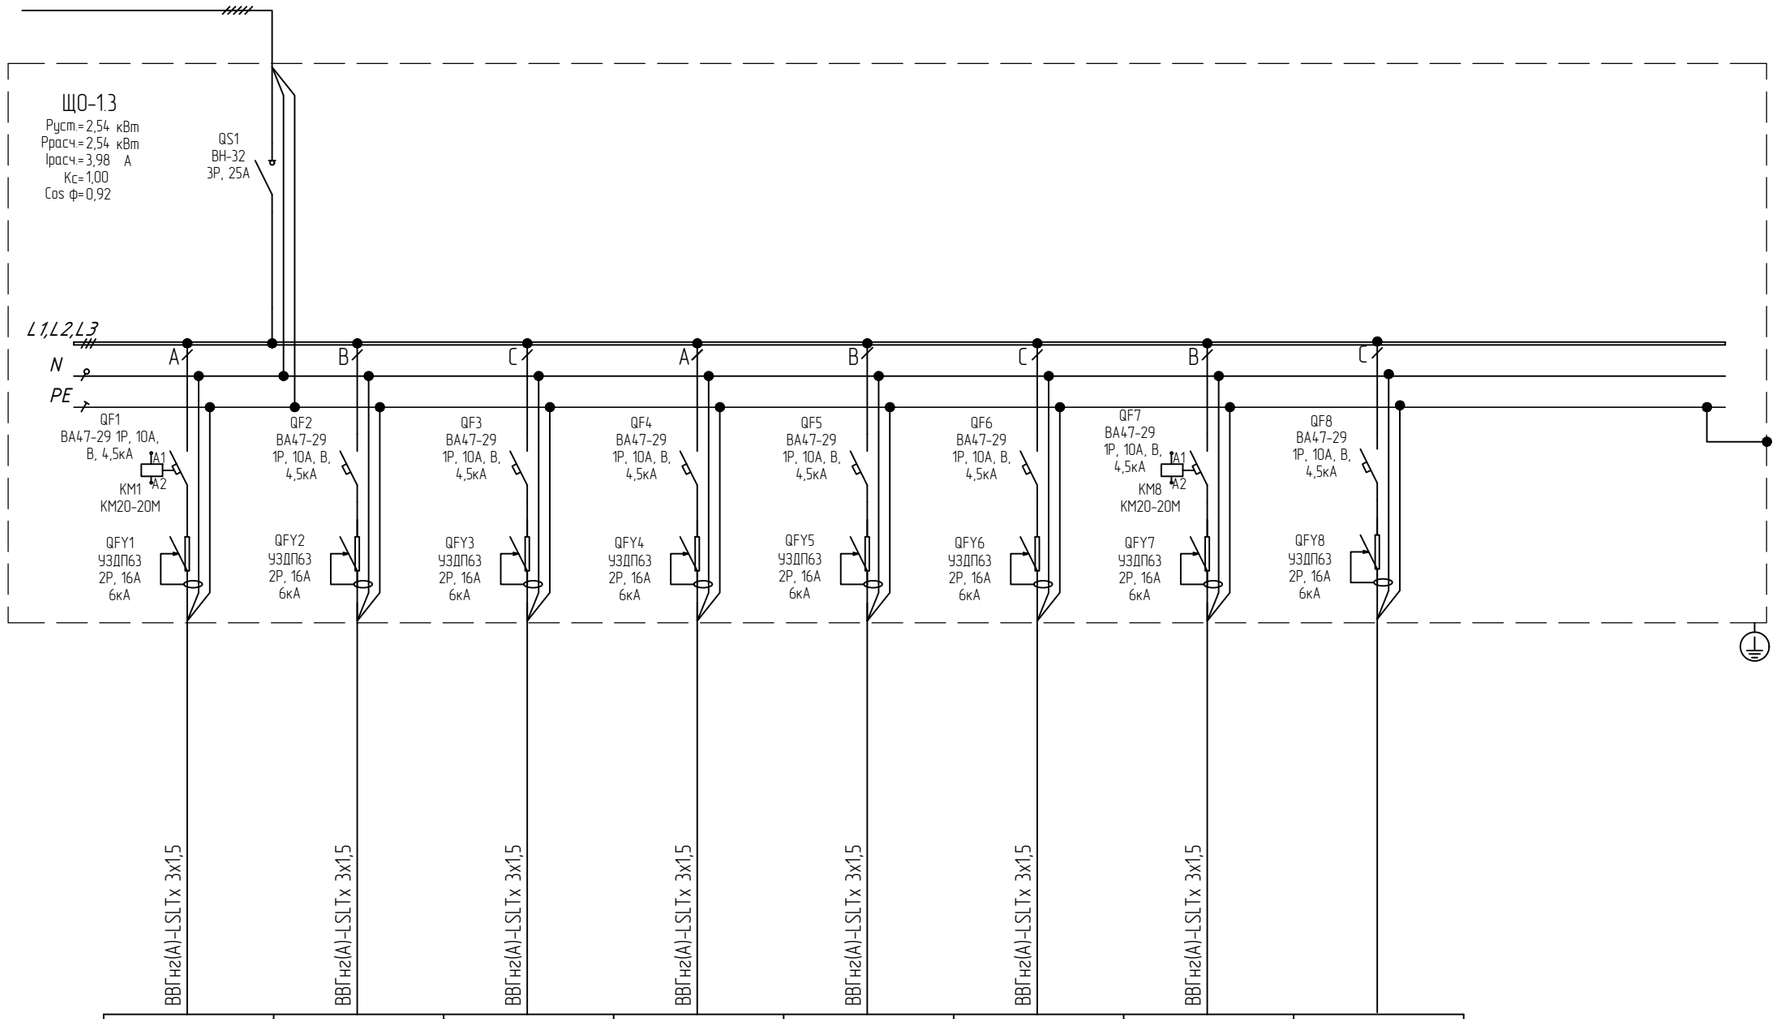

Марка и сечение кабелей	Длина участка сети	Электроприёмники								
		номер группы	0-1.3-1	0-1.3-2	0-1.3-3	0-1.3-4	0-1.3-5	0-1.3-6	0-1.3-7	
		Руст. (кВт)	0,18	0,42	0,29	0,67	0,50	0,26	0,23	
		Ip. (А)	0,80	1,92	1,31	3,08	2,31	1,19	7,88	
ВВГнг(А)-LSLTx 3х1,5		Наименование	Рабочее освещение	Рабочее освещение	Рабочее освещение	Рабочее освещение	Рабочее освещение	Рабочее освещение	Рабочее освещение	Резерв
		Помещения	140, 141, 140а	141, 143а, 143, 145, 142	146, 147, 134, 131	131	131	132, 133, 135, 136	139, 223, 321	

Согласовано

Взам. инв.N

Подпись и дата

Инв.N подл.

Изм.	Кол.уч.	Лист	N°док.	Подп.	Дата
Разраб.		Семенов			02.2025
Провер.		Пильгуй М.Н.			02.2025
Н. контр.		Пильгуй Н.М			02.2025
Нач. ОПИС №1		Белоусова Д.П.			02.2025

2024-00375-01-0-ИОС1

Капитальный ремонт здания Государственного бюджетного общеобразовательного учреждения города Москвы «Школа № 1574» по адресу: г. Москва, Старопименовский пер., д. №5

Система электроснабжения

Стадия	Лист	Листов
П	7	

Щит ЩО-1.3. Схема электрическая принципиальная

МОСЖИЛ НИИПРОЕКТ

Формат А3 х 1

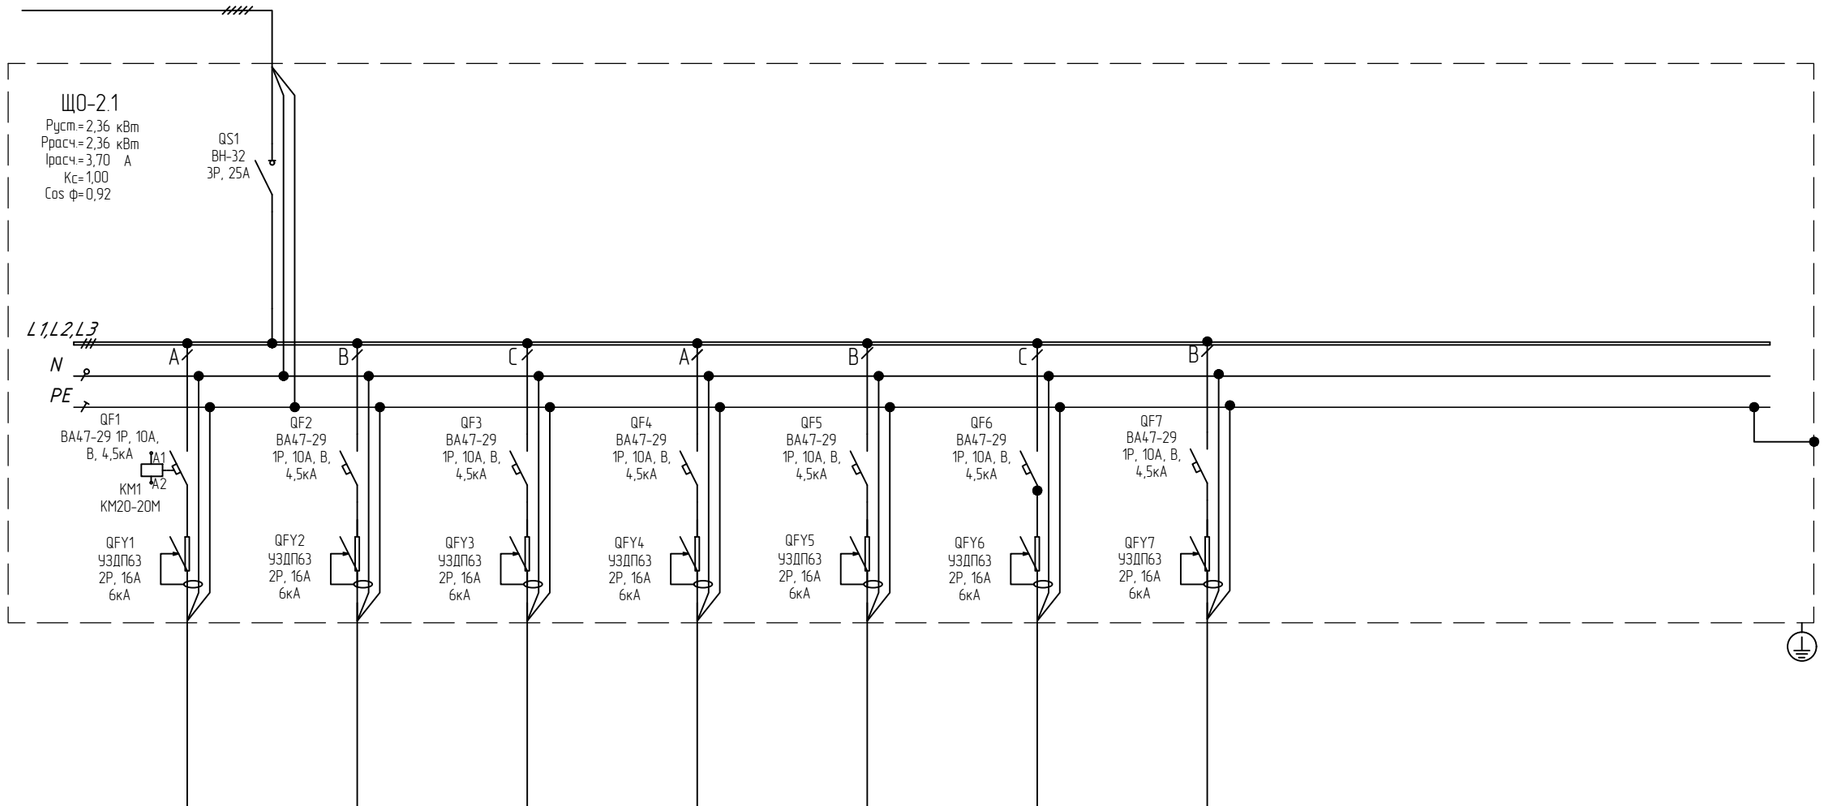

Питающая сеть, марка, сечение кабеля			ВВГнг(А)-LSLTx 3х1,5	ВВГнг(А)-LSLTx 3х1,5	ВВГнг(А)-LSLTx 3х1,5	ВВГнг(А)-LSLTx 3х1,5	ВВГнг(А)-LSLTx 3х1,5	ВВГнг(А)-LSLTx 3х1,5		
Щит распределительный	Аппараты ввода	Тип Iном. (А) Iу. (мА)								
	Аппараты отходящих линий	Тип Iном. (А) Iу. (мА)								
	Марка и сечения кабелей									
	Длина участка сети									
Электроприёмники	номер группы		0-2.1-1	0-2.1-2	0-2.1-3	0-2.1-4	0-2.1-5	0-2.1-6		
	Руст. (кВт)		0,18	0,48	0,12	0,33	0,33	0,80		
	Ip. (А)		0,82	2,20	0,57	1,51	1,51	3,66		
	Наименование		Рабочее освещение	Рабочее освещение	Рабочее освещение	Рабочее освещение	Рабочее освещение	Рабочее освещение	Резерв	
	Помещения		214	211	213, 216	208	207	206		

Согласовано

Взам. инв.N

Подпись и дата

Инв.N подл.

Изм.	Кол.уч.	Лист	N°док.	Подп.	Дата
Разраб.		Семенов			02.2025
Провер.		Пильгуй М.Н.			02.2025
Н. контр.		Пильгуй Н.М			02.2025
Нач. ОПИС N°1		Белоусова Д.П.			02.2025

2024-00375-01-0-ИОС1

Капитальный ремонт здания Государственного бюджетного общеобразовательного учреждения города Москвы «Школа № 1574» по адресу: г. Москва, Старопименовский пер., д. №5

Система электроснабжения

Стадия	Лист	Листов
П	8	

Щит ЩО-2.1. Схема электрическая принципиальная

МОСЖИЛ НИИПРОЕКТ

Формат А3 х 1

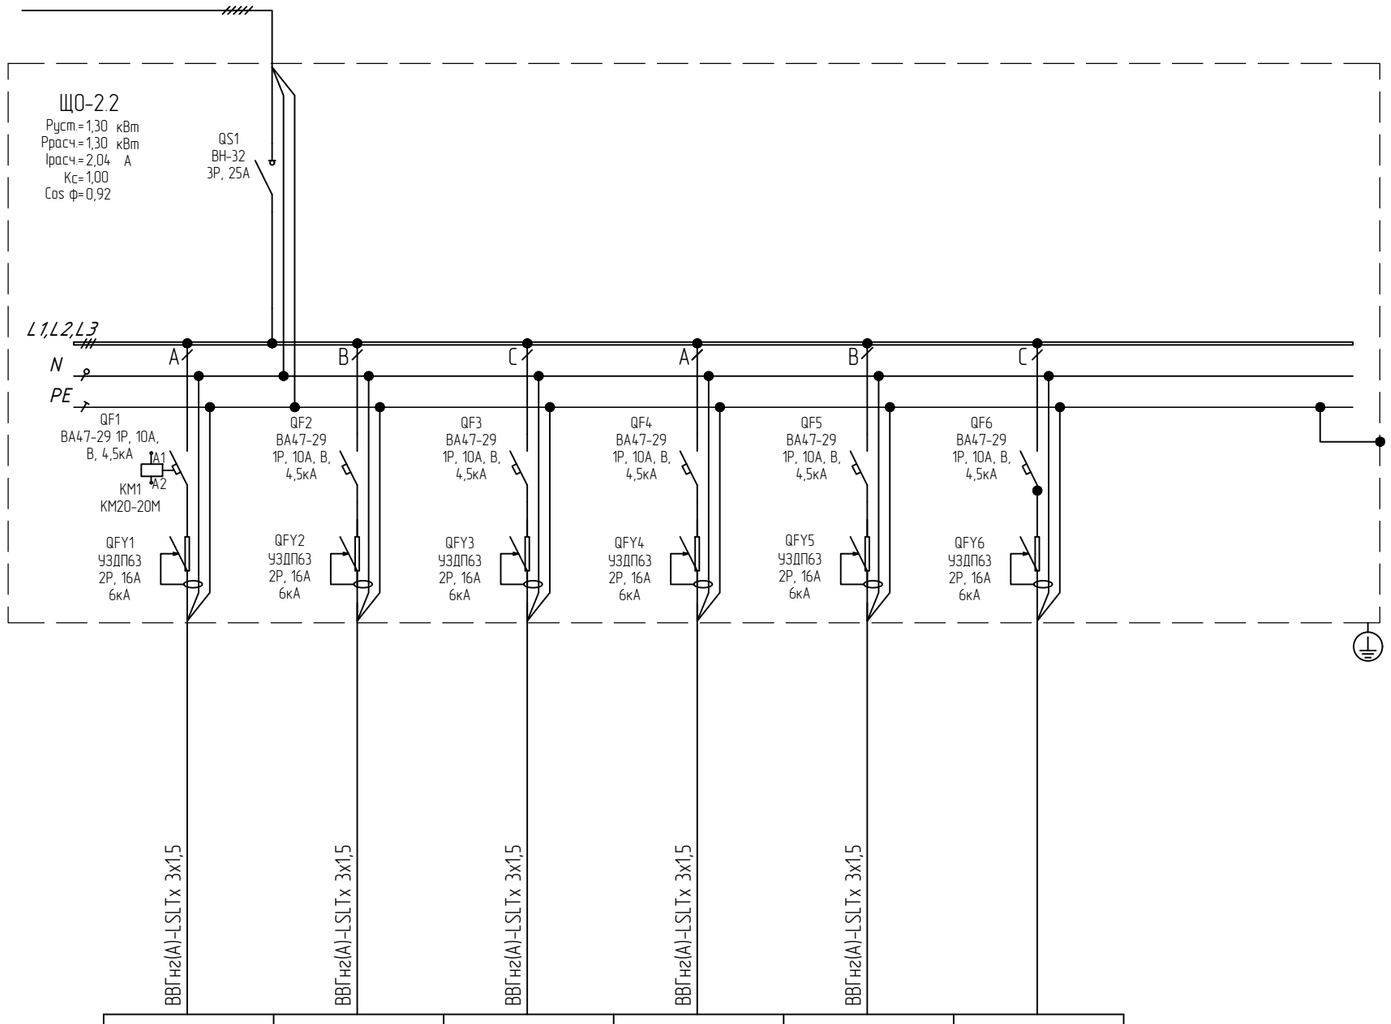

Щит распределительный	Аппараты ввода	Тип Iном. (А) Iу. (мА)						
	Аппараты отходящих линий	Тип Iном. (А) Iу. (мА)						
	Марка и сечения кабелей		ВВГнг(А)-LSLTx 3х1,5	ВВГнг(А)-LSLTx 3х1,5	ВВГнг(А)-LSLTx 3х1,5	ВВГнг(А)-LSLTx 3х1,5	ВВГнг(А)-LSLTx 3х1,5	
	Длина участка сети							
Электроприёмники	номер группы		0-2.2-1	0-2.2-2	0-2.2-3	0-2.2-4	0-2.2-5	
	Руст. (кВт)		0,18	0,32	0,38	0,30	0,12	
	Ip. (А)		0,82	1,46	1,76	1,37	0,54	
	Наименование		Рабочее освещение	Рабочее освещение	Рабочее освещение	Рабочее освещение	Рабочее освещение	Резерв
	Помещения		218	203-205	202	202	212, 217	хх

Согласовано

Взам. инв.N

Подпись и дата

Инв.N подл.

Изм.	Кол.уч.	Лист	N°док.	Подп.	Дата
Разраб.		Семенов			02.2025
Провер.		Пильгуй М.Н.			02.2025
Н. контр.		Пильгуй Н.М			02.2025
Нач. ОПИС N°1		Белоусова Д.П.			02.2025

2024-00375-01-0-ИОС1

Капитальный ремонт здания Государственного бюджетного общеобразовательного учреждения города Москвы «Школа № 1574» по адресу: г. Москва, Старопименовский пер., д. №5

Система электроснабжения

Стадия	Лист	Листов
П	9	

Щит ЩО-2.2. Схема электрическая принципиальная

МОСЖИЛ НИИПРОЕКТ

Формат А3 х 1

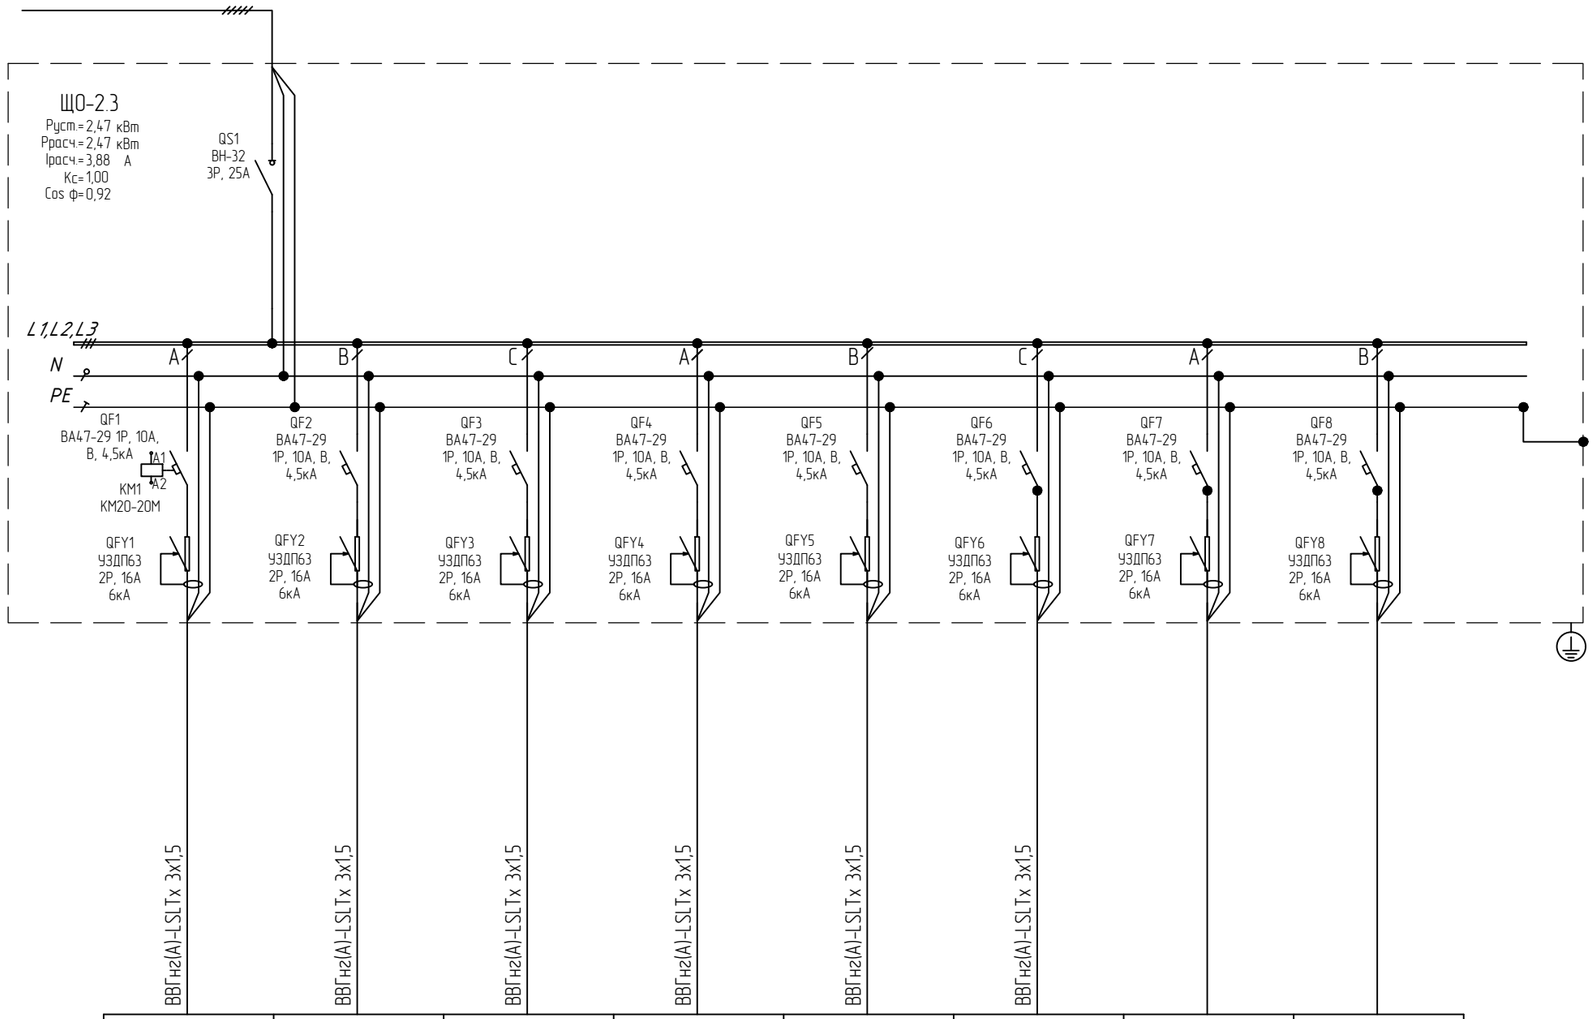

Электроприёмники	номер группы	0-2.3-1	0-2.3-2	0-2.3-3	0-2.3-4	0-2.3-5	0-2.3-6		
	Руст. (кВт)	0,42	0,60	0,60	0,15	0,23	0,40		
	Ip. (А)	1,92	2,75	2,75	0,70	1,06	1,83		
	Наименование	Рабочее освещение	Рабочее освещение	Рабочее освещение	Рабочее освещение	Рабочее освещение	Рабочее освещение	Резерв	Резерв
	Помещения	219	220	220	227-229	224-226, 322	221, 222		
	Марка и сечения кабелей	ВВГнг(А)-LSLTx 3х1,5	ВВГнг(А)-LSLTx 3х1,5	ВВГнг(А)-LSLTx 3х1,5	ВВГнг(А)-LSLTx 3х1,5	ВВГнг(А)-LSLTx 3х1,5	ВВГнг(А)-LSLTx 3х1,5		
	Длина участка сети								

Согласовано

Взам. инв.N

Подпись и дата

Инв.N подл.

Изм.	Кол.уч.	Лист	N°док.	Подп.	Дата
Разраб.		Семенов			02.2025
Провер.		Пильгуй М.Н.			02.2025
Н. контр.		Пильгуй Н.М			02.2025
Нач. ОПИС N°1		Белоусова Д.П.			02.2025

2024-00375-01-0-ИОС1

Капитальный ремонт здания Государственного бюджетного общеобразовательного учреждения города Москвы «Школа № 1574» по адресу: г. Москва, Старопименовский пер., д. №5

Система электроснабжения

Стадия	Лист	Листов
П	10	

Щит ЩО-2.3. Схема электрическая принципиальная

МОСЖИЛ НИИПРОЕКТ

Формат А3 х 1

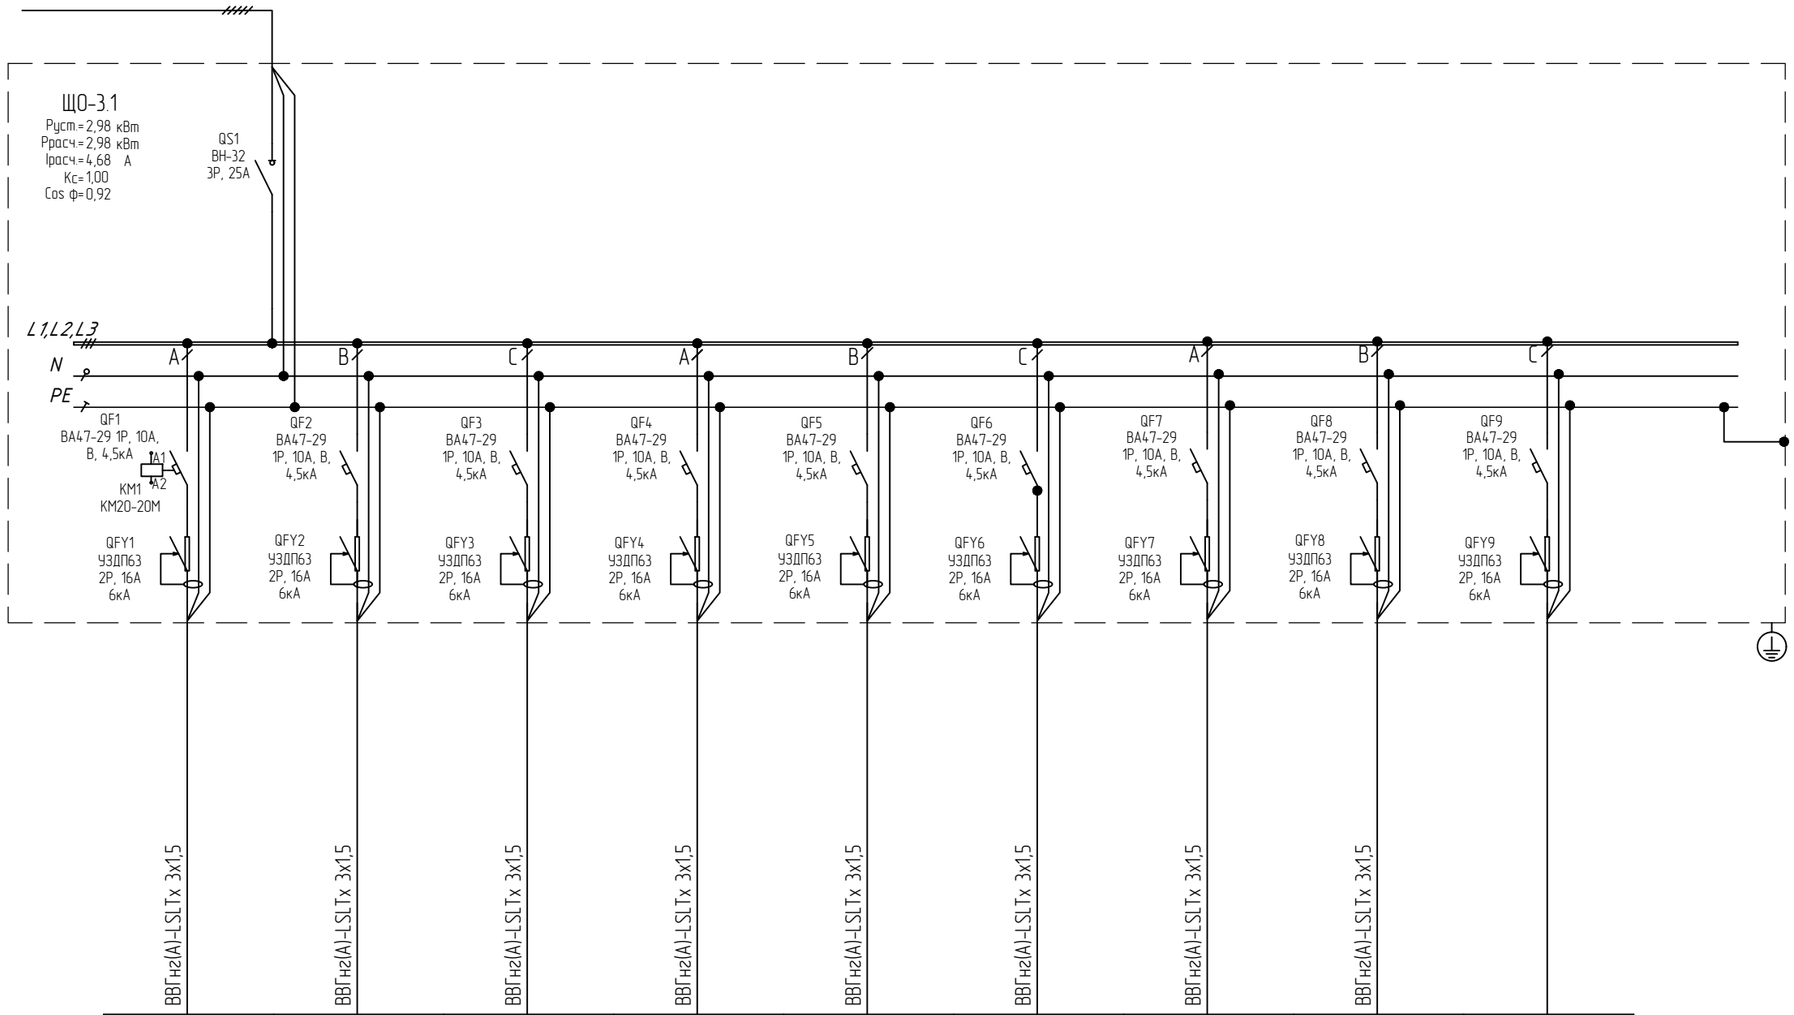

Питающая сеть, марка, сечение кабеля			ВВГнг(А)-LSLTx 3х1,5	ВВГнг(А)-LSLTx 3х1,5	ВВГнг(А)-LSLTx 3х1,5	ВВГнг(А)-LSLTx 3х1,5	ВВГнг(А)-LSLTx 3х1,5	ВВГнг(А)-LSLTx 3х1,5	ВВГнг(А)-LSLTx 3х1,5	ВВГнг(А)-LSLTx 3х1,5	ВВГнг(А)-LSLTx 3х1,5
Щит распределительный	Аппараты ввода	Тип Iном. (А) Iу. (мА)									
	Аппараты отходящих линий	Тип Iном. (А) Iу. (мА)									
	Марка и сечения кабелей										
	Длина участка сети										
Электроприёмники	номер группы		0-3.1-1	0-3.1-2	0-3.1-3	0-3.1-4	0-3.1-5	0-3.1-6	0-3.1-7	0-3.1-8	0-3.1-9
	Руст. (кВт)		0,36	0,60	0,17	0,18	0,16	0,50	0,50	0,50	0,12
	Ip. (А)		1,65	2,75	0,77	0,82	0,73	2,31	2,31	2,31	0,55
	Наименование		Рабочее освещение	Рабочее освещение	Рабочее освещение	Рабочее освещение	Рабочее освещение	Рабочее освещение	Рабочее освещение	Рабочее освещение	Рабочее освещение
	Помещения		317	312	311	313	314, 315	309	309	309	309

Согласовано

Взам. инв.N

Подпись и дата

Инв.N подл.

Изм.	Кол.уч.	Лист	N°док.	Подп.	Дата
Разраб.		Семенов			02.2025
Провер.		Пильгуй М.Н.			02.2025
Н. контр.		Пильгуй Н.М			02.2025
Нач. ОПИС №1		Белоусова Д.П.			02.2025

2024-00375-01-0-ИОС1

Капитальный ремонт здания Государственного бюджетного общеобразовательного учреждения города Москвы «Школа № 1574» по адресу: г. Москва, Старопименовский пер., д. №5

Система электроснабжения

Стадия	Лист	Листов
П	11	

Щит ЩО-3.1. Схема электрическая принципиальная

МОСЖИЛ НИИПРОЕКТ

Формат А3 х 1

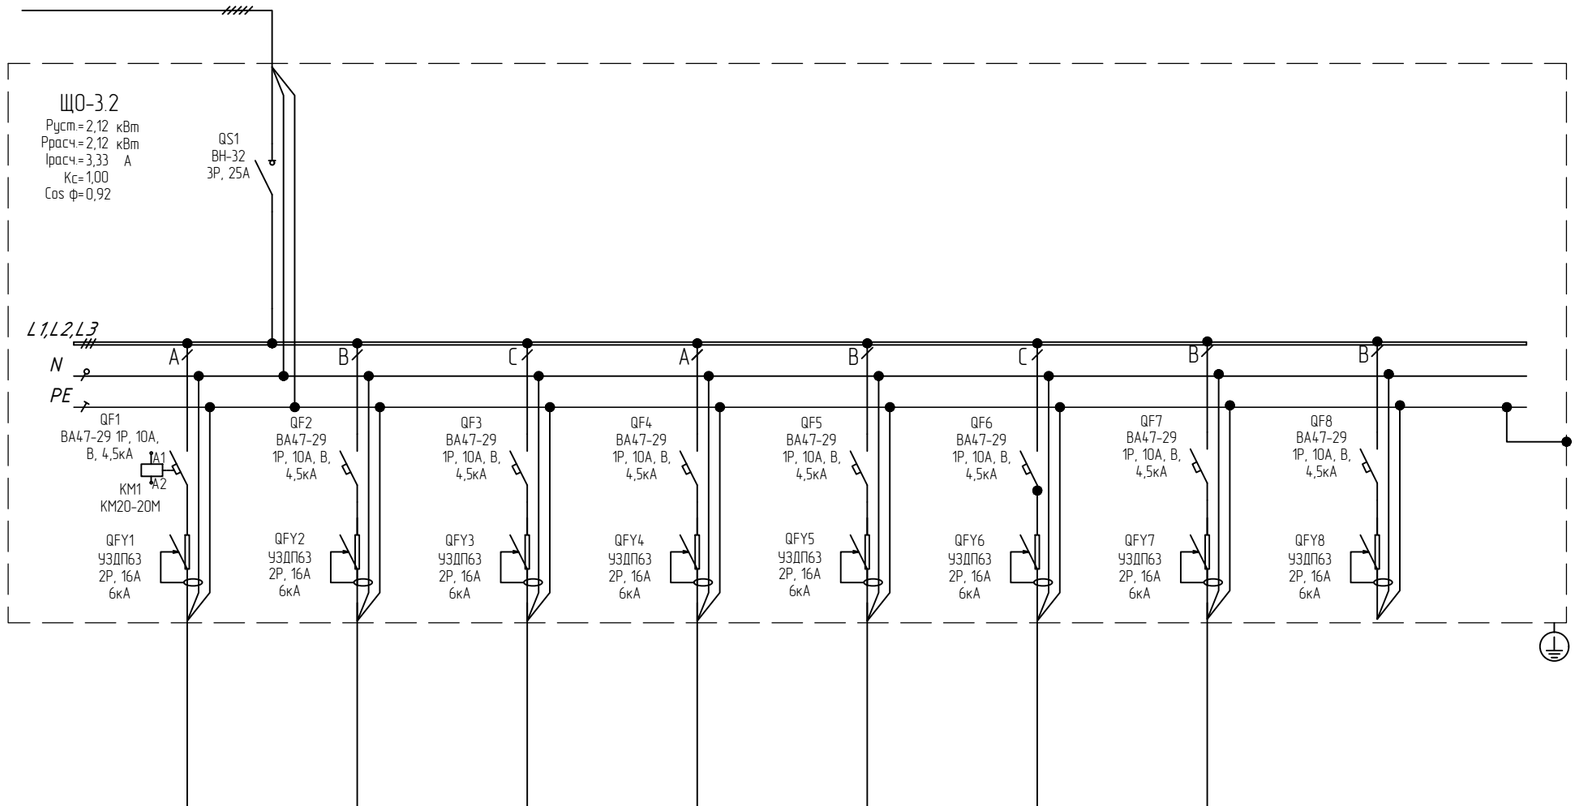

Щит распределительный		Питающая сеть, марка, сечение кабеля							
	Аппараты ввода	Тип Iном. (А) Iу. (мА)							
	Аппараты отходящих линий	Тип Iном. (А) Iу. (мА)							
	Марка и сечения кабелей		ВВГнг(А)-LSLTx 3х1,5	ВВГнг(А)-LSLTx 3х1,5	ВВГнг(А)-LSLTx 3х1,5	ВВГнг(А)-LSLTx 3х1,5	ВВГнг(А)-LSLTx 3х1,5	ВВГнг(А)-LSLTx 3х1,5	ВВГнг(А)-LSLTx 3х1,5
	Длина участка сети								
Электроприёмники	номер группы		0-3.2-1	0-3.2-2	0-3.2-3		0-3.2-5	0-3.2-6	0-3.2-7	
	Руст. (кВт)		0,42	0,50	0,50		0,44	0,13	0,44	
	Ip. (А)		1,92	2,31	2,31		2,03	0,59	2,01	
	Наименование		Рабочее освещение	Рабочее освещение	Рабочее освещение	Резерв	Рабочее освещение	Рабочее освещение	Рабочее освещение	Резерв
	Помещения		317.1	302	303		305	318, 319	318, 319	

Согласовано

Взам. инв.N

Подпись и дата

Инв.N подл.

Изм.	Кол.уч.	Лист	N°док.	Подп.	Дата
Разраб.		Семенов			02.2025
Провер.		Пильгуй М.Н.			02.2025
Н. контр.		Пильгуй Н.М			02.2025
Нач. ОПИС №1		Белоусова Д.П.			02.2025

2024-00375-01-0-ИОС1

Капитальный ремонт здания Государственного бюджетного общеобразовательного учреждения города Москвы «Школа № 1574» по адресу: г. Москва, Старопименовский пер., д. №5

Система электроснабжения

Стадия	Лист	Листов
П	12	

Щит ЩО-3.2. Схема электрическая принципиальная

МОСЖИЛ НИИПРОЕКТ

Формат А3 х 1

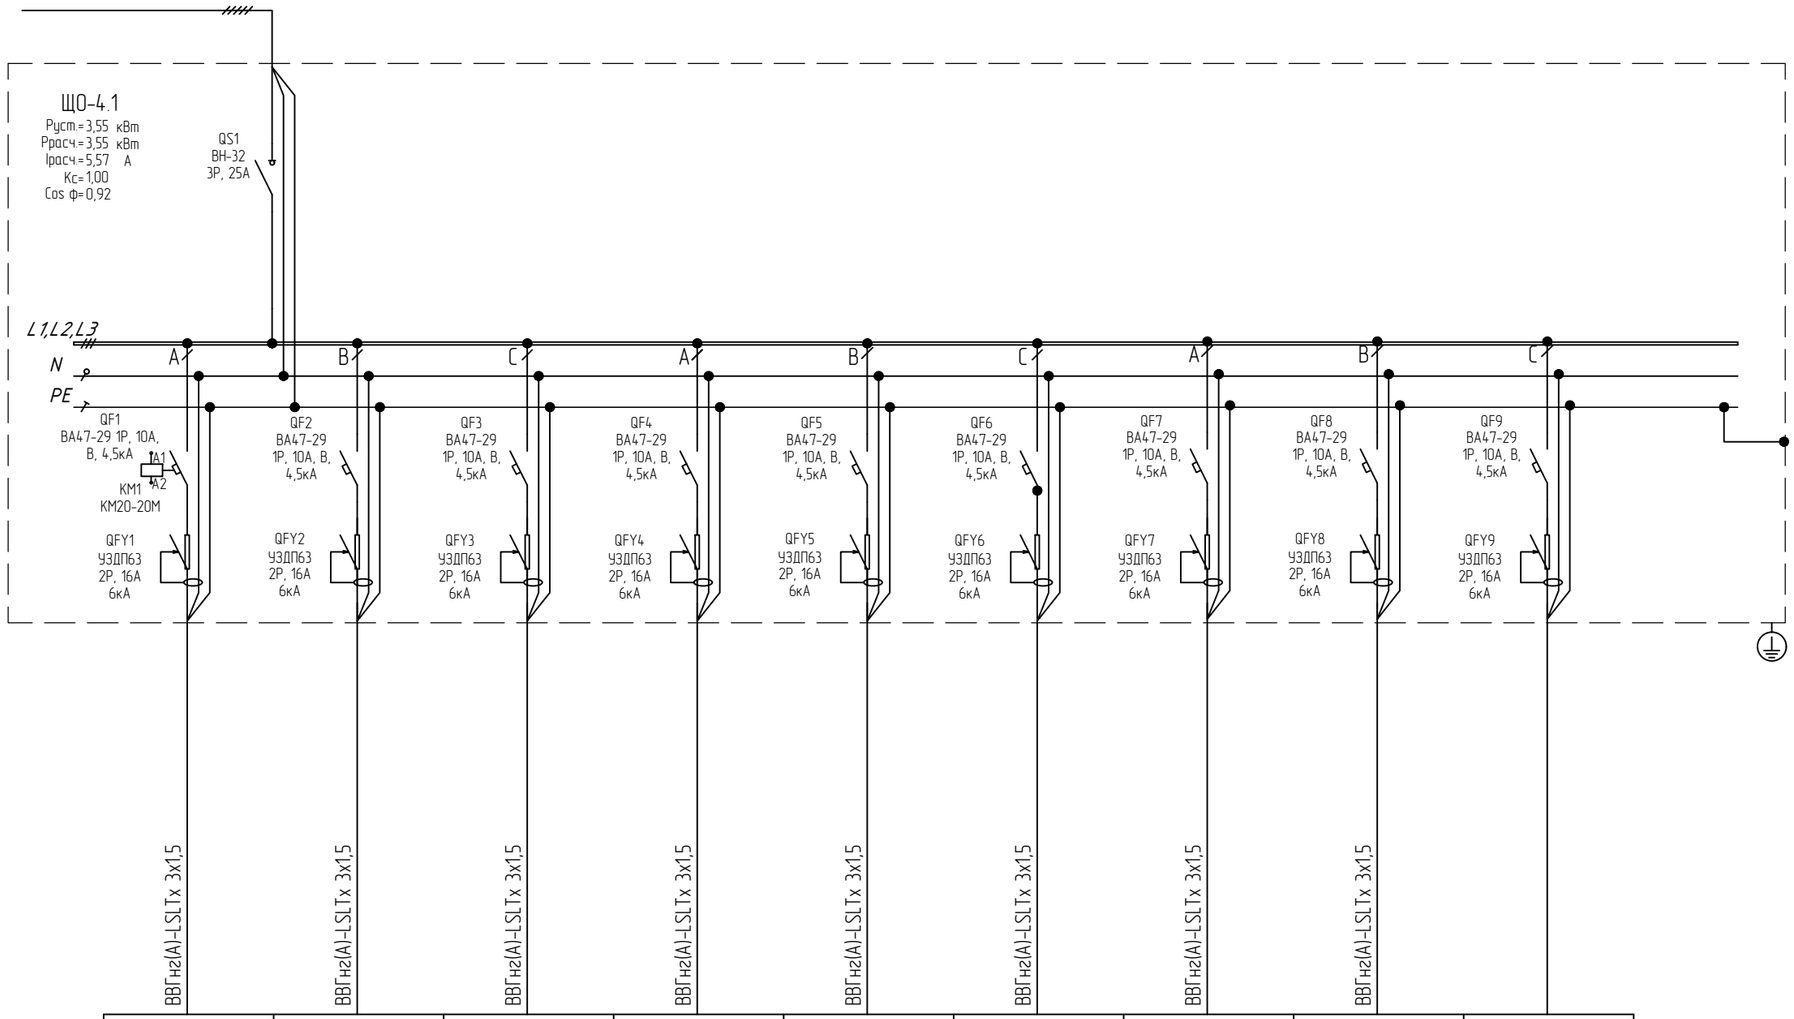

Щит распределительный	Аппараты ввода	Тип								
		Iном. (А)								
		Iу. (мА)								
	Аппараты отходящих линий	Тип								
		Iном. (А)								
		Iу. (мА)								
	Марка и сечения кабелей		ВВГнг(А)-LSLTx 3х1,5	ВВГнг(А)-LSLTx 3х1,5	ВВГнг(А)-LSLTx 3х1,5	ВВГнг(А)-LSLTx 3х1,5	ВВГнг(А)-LSLTx 3х1,5	ВВГнг(А)-LSLTx 3х1,5	ВВГнг(А)-LSLTx 3х1,5	ВВГнг(А)-LSLTx 3х1,5	
	Длина участка сети										
Электроприёмники	номер группы		0-4.1-1	0-4.1-2	0-4.1-3	0-4.1-4	0-4.1-5	0-4.1-6	0-4.1-7	0-4.1-8	
	Руст. (кВт)		0,66	0,60	0,18	0,14	0,48	0,50	0,62	0,36	
	Ip. (А)		3,02	2,75	0,82	0,66	2,20	2,31	2,86	1,65	
	Наименование		Рабочее освещение	Рабочее освещение	Рабочее освещение	Рабочее освещение	Рабочее освещение	Рабочее освещение	Рабочее освещение	Рабочее освещение	Резерв
	Помещения		415	410	409	411, 412	407	406	405	413, 414	

Согласовано

Взам. инв.N

Подпись и дата

Инв.N подл.

Изм.	Кол.уч.	Лист	N°док.	Подп.	Дата
Разраб.		Семенов			02.2025
Провер.		Пильгуй М.Н.			02.2025
Н. контр.		Пильгуй Н.М			02.2025
Нач. ОПИС №1		Белоусова Д.П.			02.2025

2024-00375-01-0-ИОС1

Капитальный ремонт здания Государственного бюджетного общеобразовательного учреждения города Москвы «Школа № 1574» по адресу: г. Москва, Старопименовский пер., д. №5

Система электроснабжения

Стадия	Лист	Листов
П	13	

Щит ЩО-4.1. Схема электрическая принципиальная

МОСЖИЛ НИИПРОЕКТ

Формат А3 х 1

Питающая сеть, марка, сечение кабеля

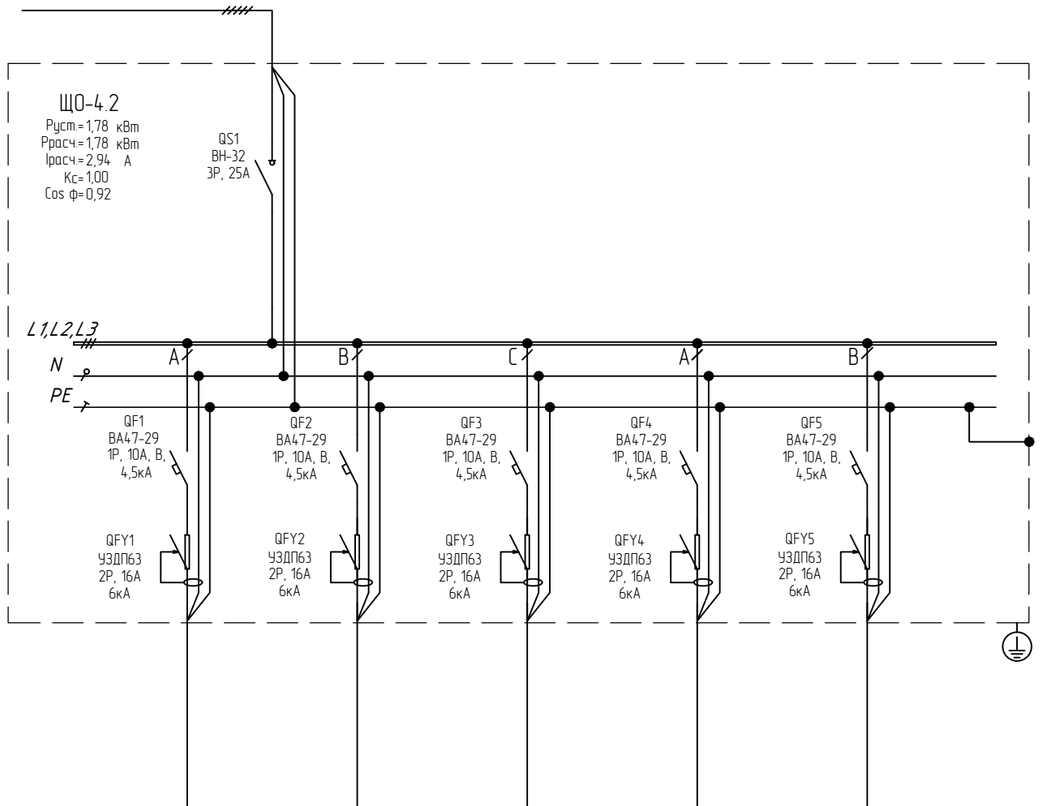

Щит распределительный	Аппараты ввода	Тип Iном. (А) Iу. (мА)				
	Аппараты отходящих линий	Тип Iном. (А) Iу. (мА)				
Марка и сечение кабелей			ВВГнг(А)-LSLTx 3х1,5	ВВГнг(А)-LSLTx 3х1,5	ВВГнг(А)-LSLTx 3х1,5	ВВГнг(А)-LSLTx 3х1,5
Длина участка сети						
Электроприёмники	номер группы		0-4.2-1	0-4.2-2	0-4.2-3	0-4.2-4
	Руст. (кВт)		0,50	0,50	0,62	0,15
	Ip. (А)		2,31	2,31	2,86	0,70
	Наименование		Рабочее освещение	Рабочее освещение	Рабочее освещение	Рабочее освещение
	Помещения		402	403	404	416, 417

Резерв

Согласовано

Взам. инв.N

Подпись и дата

Инв.N подл.

Изм.	Кол.уч.	Лист	N°док.	Подп.	Дата
Разраб.		Семенов			02.2025
Провер.		Пильгуй М.Н.			02.2025
Н. контр.		Пильгуй Н.М			02.2025
Нач. ОПИС №1		Белоусова Д.П.			02.2025

2024-00375-01-0-ИОС1

Капитальный ремонт здания Государственного бюджетного общеобразовательного учреждения города Москвы «Школа № 1574» по адресу: г. Москва, Старопименовский пер., д. №5

Система электроснабжения

Стадия	Лист	Листов
П	14	

Щит ЩО-4.2. Схема электрическая принципиальная

МОСЖИЛ НИИПРОЕКТ

Формат А3 х 1

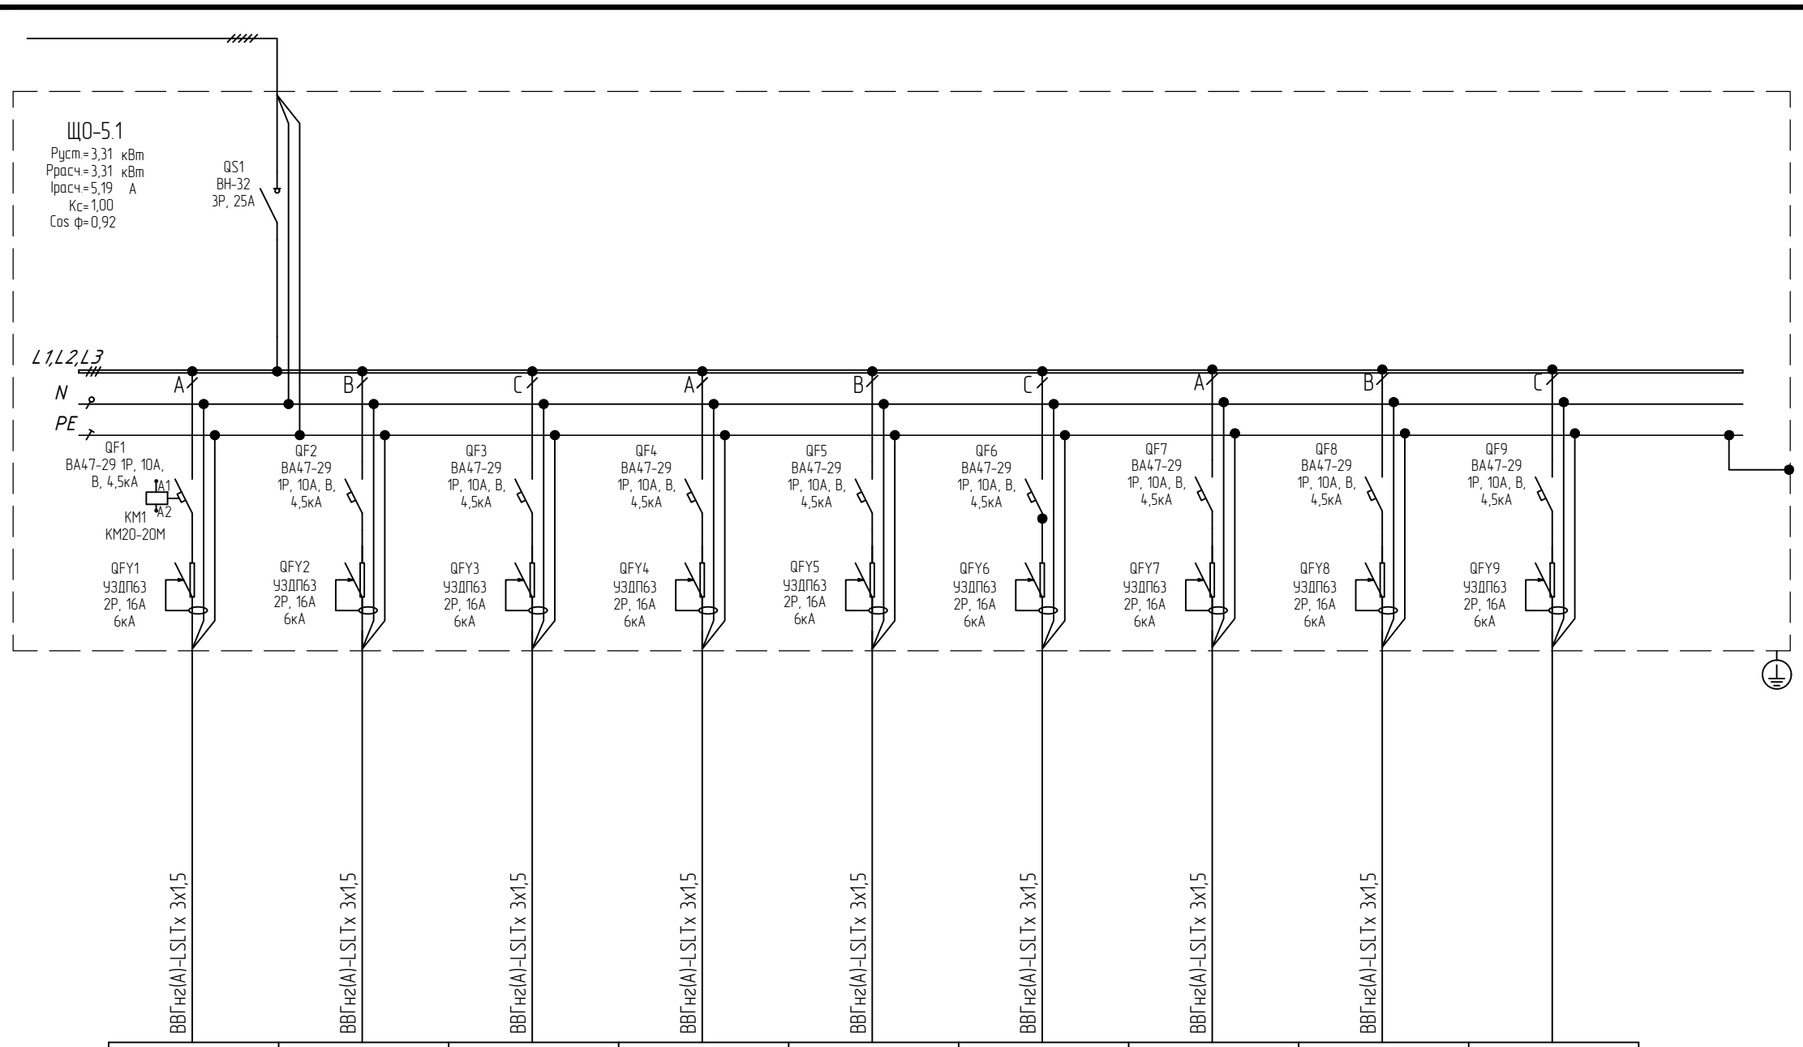

Щит распределительный	Аппараты ввода	Тип								
		Iном. (А)								
		Iу. (мА)								
	Аппараты отходящих линий	Тип								
		Iном. (А)								
		Iу. (мА)								
Марка и сечения кабелей			ВВГнг(А)-LSLTx 3х1,5	ВВГнг(А)-LSLTx 3х1,5	ВВГнг(А)-LSLTx 3х1,5	ВВГнг(А)-LSLTx 3х1,5	ВВГнг(А)-LSLTx 3х1,5	ВВГнг(А)-LSLTx 3х1,5	ВВГнг(А)-LSLTx 3х1,5	ВВГнг(А)-LSLTx 3х1,5	
Длина участка сети											
Электроприёмники	номер группы		0-5.1-1	0-5.1-2	0-5.1-3	0-5.1-4	0-5.1-5	0-5.1-6	0-5.1-7	0-5.1-8	
	Руст. (кВт)		0,66	0,60	0,18	0,14	0,48	0,50	0,50	0,24	
	Ip. (А)		3,02	2,75	0,82	0,66	2,20	2,31	2,31	1,10	
	Наименование		Рабочее освещение	Рабочее освещение	Рабочее освещение	Рабочее освещение	Рабочее освещение	Рабочее освещение	Рабочее освещение	Рабочее освещение	Резерв
	Помещения		515	511	510	512, 513	508	507	506	506	

Согласовано

Взам. инв.N

Подпись и дата

Инв.N подл.

Изм.	Кол.уч.	Лист	N°док.	Подп.	Дата
Разраб.		Семенов			02.2025
Провер.		Пильгуй М.Н.			02.2025
Н. контр.		Пильгуй Н.М			02.2025
Нач. ОПИС N°1		Белоусова Д.П.			02.2025

2024-00375-01-0-ИОС1

Капитальный ремонт здания Государственного бюджетного общеобразовательного учреждения города Москвы «Школа № 1574» по адресу: г. Москва, Старопименовский пер., д. №5

Система электроснабжения

Стадия	Лист	Листов
П	15	

Щит ЩО-5.1. Схема электрическая принципиальная

МОСЖИЛ НИИПРОЕКТ

Формат А3 х 1

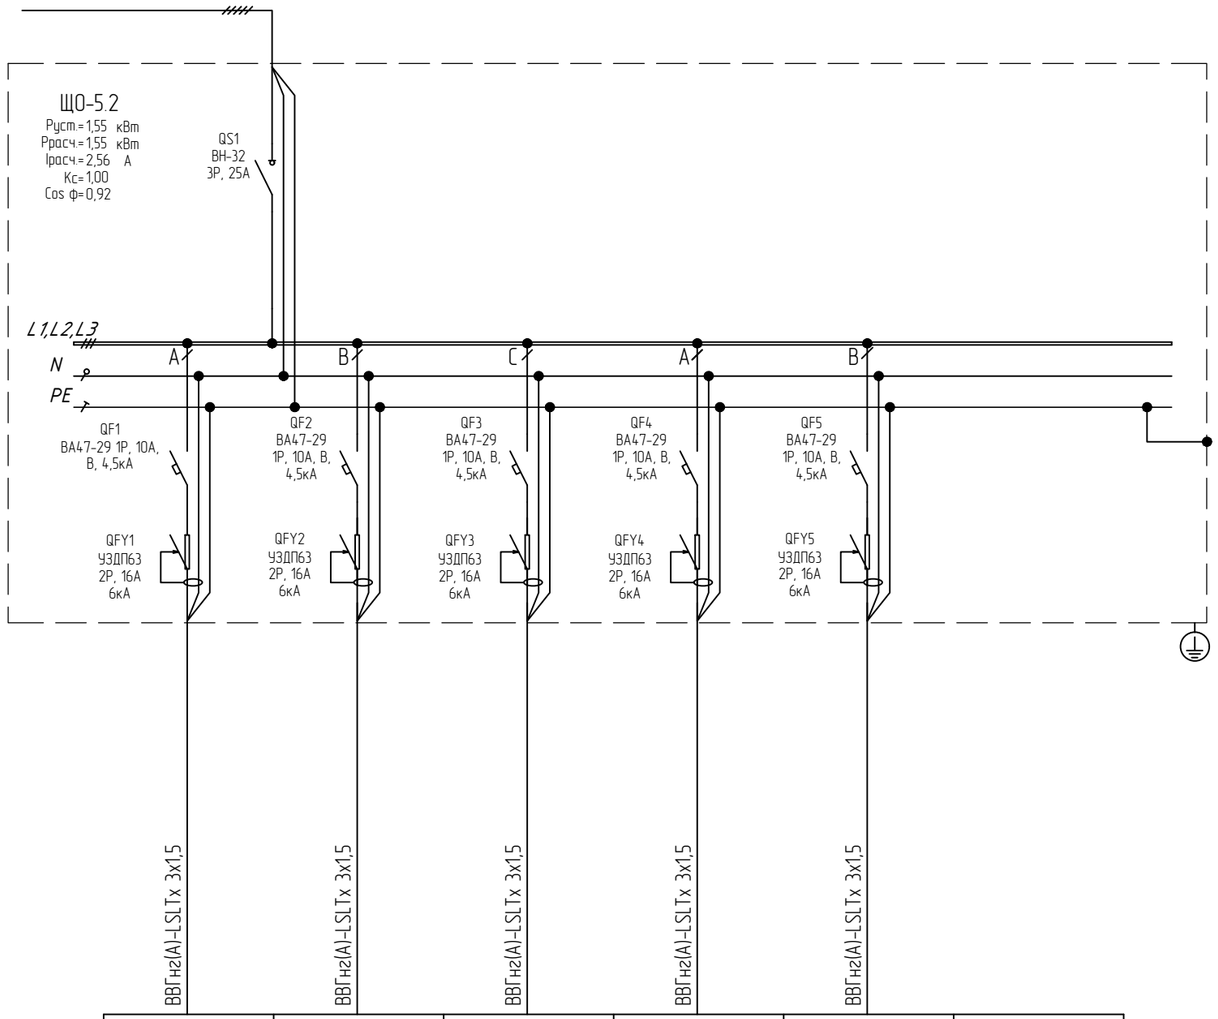

Питающая сеть, марка, сечение кабеля

Щит распределительный

Аппараты ввода: Тип, Iном. (А), Iу. (мА)

Аппараты отходящих линий: Тип, Iном. (А), Iу. (мА)

Марка и сечения кабелей

Длина участка сети

Электроприёмники	номер группы	0-5.2-1	0-5.2-2	0-5.2-3	0-5.2-4	0-5.2-5	
	Руст. (кВт)	0,21	0,62	0,29	0,15	0,27	
	Ip. (А)	0,96	2,86	1,35	0,70	1,24	
	Наименование	Рабочее освещение	Рабочее освещение	Рабочее освещение	Рабочее освещение	Рабочее освещение	Резерв
	Помещения	502	503	504	516, 517	514	
Марка и сечения кабелей		ВВГнг(А)-LSLTx 3х1,5	ВВГнг(А)-LSLTx 3х1,5	ВВГнг(А)-LSLTx 3х1,5	ВВГнг(А)-LSLTx 3х1,5	ВВГнг(А)-LSLTx 3х1,5	
Длина участка сети							

Согласовано

Взам. инв.N

Подпись и дата

Инв.N подл.

Изм.	Кол.уч.	Лист	N°док.	Подп.	Дата
Разраб.		Семенов			02.2025
Провер.		Пильгуй М.Н.			02.2025
Н. контр.		Пильгуй Н.М			02.2025
Нач. ОПИС N°1		Белоусова Д.П.			02.2025

2024-00375-01-0-ИОС1

Капитальный ремонт здания Государственного бюджетного общеобразовательного учреждения города Москвы «Школа № 1574» по адресу: г. Москва, Старопименовский пер., д. №5

Система электроснабжения

Стадия	Лист	Листов
П	16	

Щит ЩО-5.2. Схема электрическая принципиальная

МОСЖИЛ НИИПРОЕКТ

Формат А3 х 1

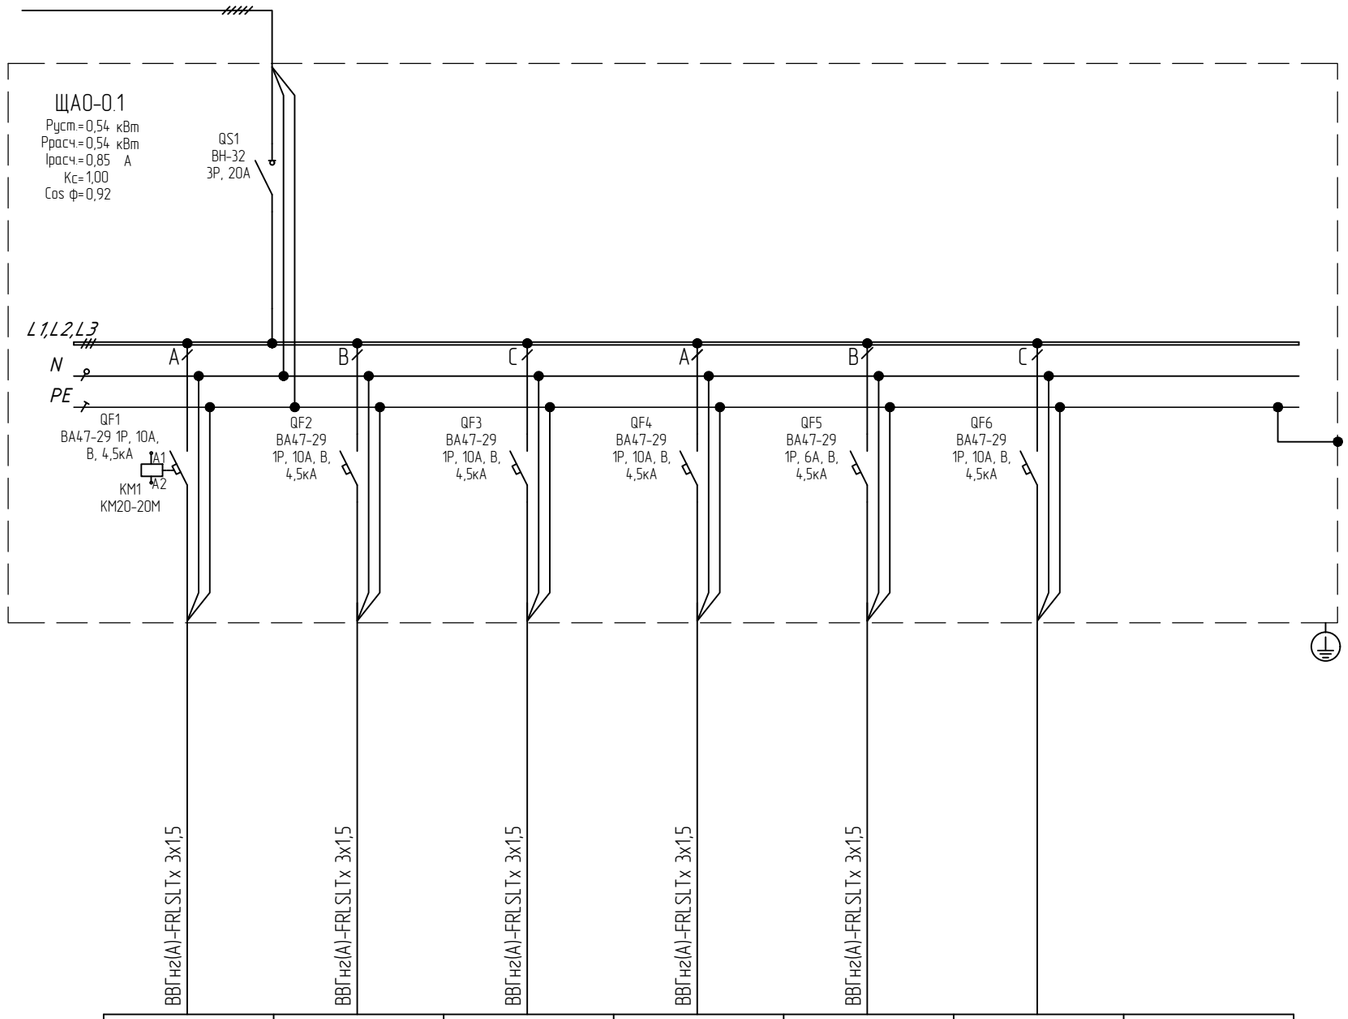

Электроприёмники							
номер группы	АО-0.1-1	АО-0.1-2	АО-0.1-3	АО-0.1-4	АО-0.1-5	АО-0.1-6	
Руст. (кВт)	0,11	0,07	0,15	0,14	0,14	0,01	
Ip. (А)	0,51	0,32	0,66	0,64	0,64	0,05	
Наименование	Аварийное освещение	Аварийное освещение	Аварийное освещение	Аварийное освещение	Аварийное освещение	Световые указатели "Выход"	Резерв
Помещения	007, 008	003, 004, 013, 017	010	020б, 020в, 020а	Входы в здание	008, 010, 020в	

Согласовано

Взам. инв.N

Подпись и дата

Инв.N подл.

Изм.	Кол.уч.	Лист	N°док.	Подп.	Дата
Разраб.		Семенов			02.2025
Провер.		Пильгуй М.Н.			02.2025
Н. контр.		Пильгуй Н.М			02.2025
Нач. ОПИС №1		Белоусова Д.П.			02.2025

2024-00375-01-0-ИОС1

Капитальный ремонт здания Государственного бюджетного общеобразовательного учреждения города Москвы «Школа № 1574» по адресу: г. Москва, Старопименовский пер., д. №5

Система электроснабжения

Стадия	Лист	Листов
П	17	

Щит ЩАО-0.1. Схема электрическая принципиальная

МОСЖИЛ НИИПРОЕКТ

Формат А3 х 1

Питающая сеть, марка, сечение кабеля

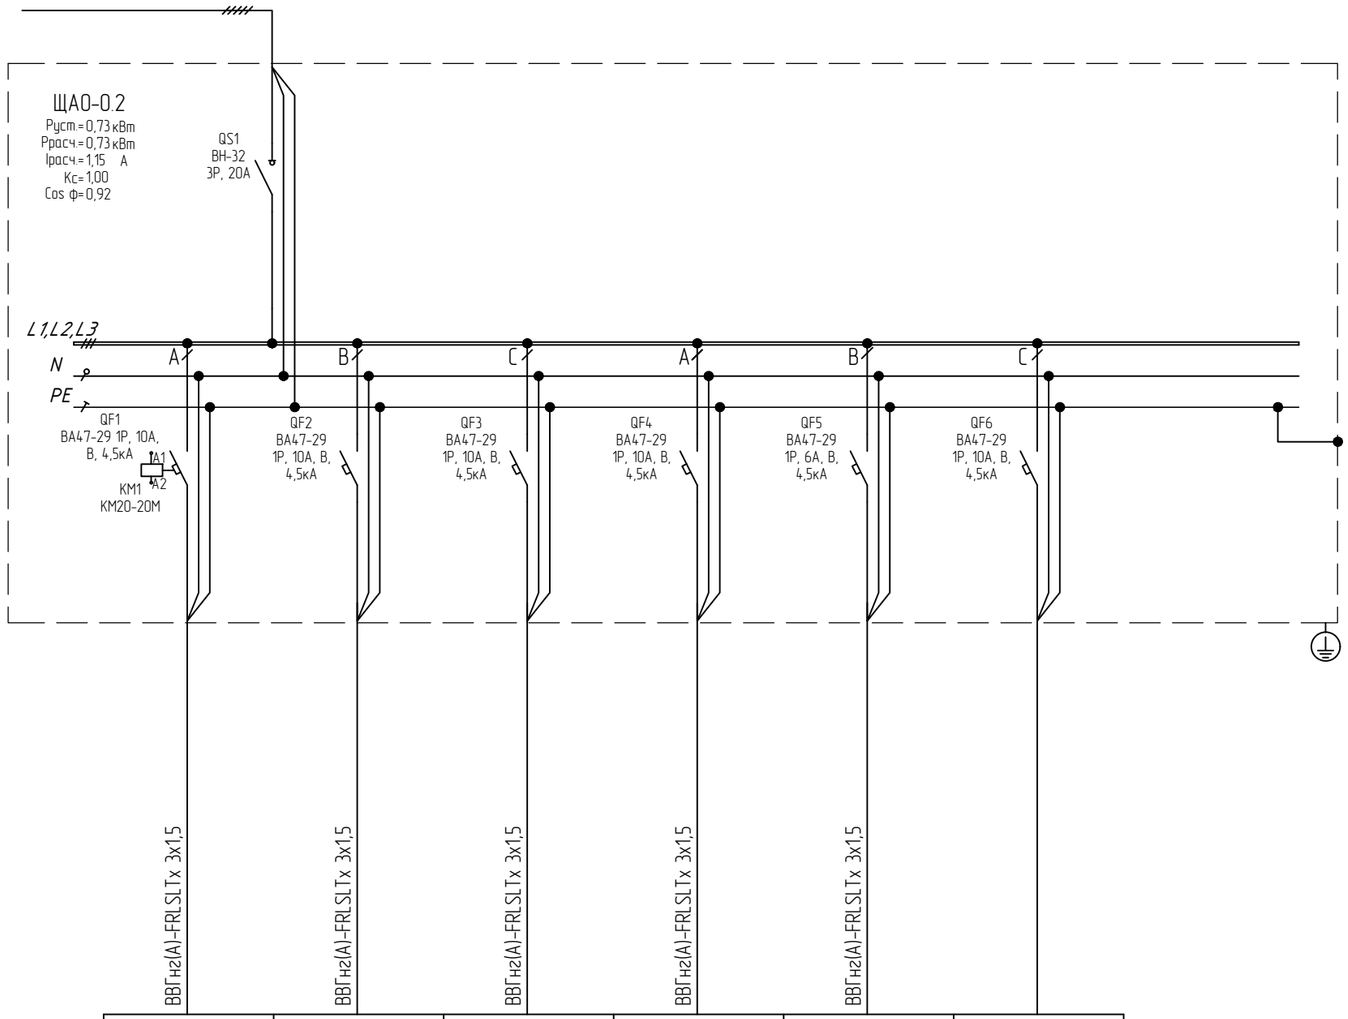

Щит распределительный	Аппараты ввода	Тип Iном. (А) Iу. (мА)					
	Аппараты отходящих линий	Тип Iном. (А) Iу. (мА)					
	Марка и сечения кабелей		ВВГнг(А)-FRLSLTx 3х1,5	ВВГнг(А)-FRLSLTx 3х1,5	ВВГнг(А)-FRLSLTx 3х1,5	ВВГнг(А)-FRLSLTx 3х1,5	ВВГнг(А)-FRLSLTx 3х1,5	
	Длина участка сети							
Электроприёмники	номер группы		АО-0.2-1	АО-0.2-2	АО-0.2-3	АО-0.2-4	АО-0.2-5	
	Руст. (кВт)		0,23	0,21	0,21	0,07	0,01	
	Iр. (А)		1,03	0,96	0,96	0,32	0,05	
	Наименование		Аварийное освещение	Аварийное освещение	Аварийное освещение	Аварийное освещение	Световые указатели "Выход"	Резерв
	Помещения		005, 006, 020, 01	019, 023, 024	001, 002, 021, 021г	Входы в здании	005, 023, 024, 021г, 019б	

Согласовано

Взам. инв.N

Подпись и дата

Инв.N подл.

Изм.	Кол.уч.	Лист	N°док.	Подп.	Дата
Разраб.		Семенов			02.2025
Провер.		Пильгуй М.Н.			02.2025
Н. контр.		Пильгуй Н.М			02.2025
Нач. ОПИС N°1		Белоусова Д.П.			02.2025

2024-00375-01-0-ИОС1

Капитальный ремонт здания Государственного бюджетного общеобразовательного учреждения города Москвы «Школа № 1574» по адресу: г. Москва, Старопименовский пер., д. №5

Система электроснабжения

Стадия	Лист	Листов
П	18	

Щит ЩАО-0.2. Схема электрическая принципиальная

МОСЖИЛ НИИПРОЕКТ

Формат А3 х 1

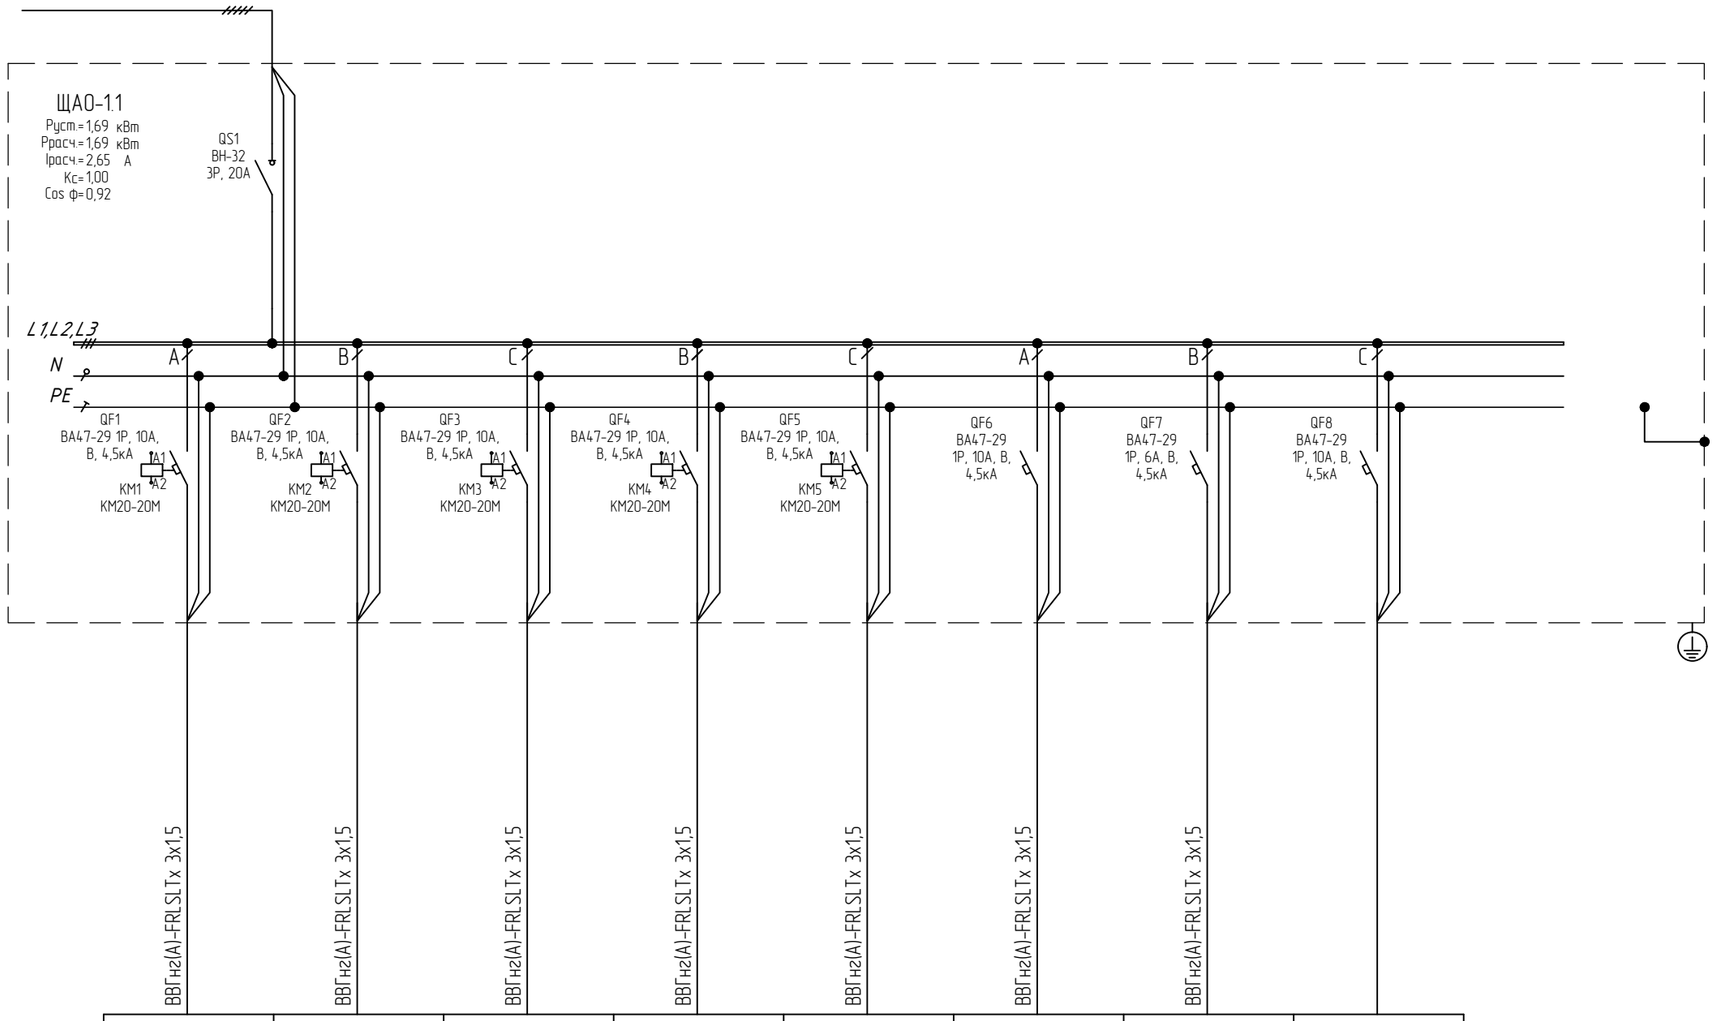

Щит распределительный

Аппараты ввода: Тип, Iном. (А), Iу. (мА)

Аппараты отходящих линий: Тип, Iном. (А), Iу. (мА)

Марка и сечения кабелей

Длина участка сети

Электроприёмники								
номер группы	АО-1.1-1	АО-1.1-2	АО-1.1-3	АО-1.1-4	АО-1.1-5	АО-1.1-6	АО-1.1-7	
Руст. (кВт)	0,17	0,60	0,16	0,24	0,20	0,32	0,01	
Ip. (А)	0,77	2,75	0,73	1,10	0,89	6,24	0,05	
Наименование	Аварийное освещение	Аварийное освещение	Аварийное освещение	Аварийное освещение	Аварийное освещение	Аварийное освещение	Световые указатели "Выход"	Резерв
Помещения	114, 110	106, 105, 209, 310, 408, 509	101, 102, 116	115, 118, 215	Входы в здание	103, 104, 107, 108, 109	101-106, 115, 118	
Марка и сечения кабелей	ВВГнг(А)-FRLSLTx 3х1,5	ВВГнг(А)-FRLSLTx 3х1,5	ВВГнг(А)-FRLSLTx 3х1,5	ВВГнг(А)-FRLSLTx 3х1,5	ВВГнг(А)-FRLSLTx 3х1,5	ВВГнг(А)-FRLSLTx 3х1,5	ВВГнг(А)-FRLSLTx 3х1,5	
Длина участка сети								

Согласовано

Взам. инв.N

Подпись и дата

Инв.N подл.

Изм.	Кол.уч.	Лист	№док.	Подп.	Дата
Разраб.		Семенов			02.2025
Провер.		Пильгуй М.Н.			02.2025
Н. контр.		Пильгуй Н.М			02.2025
Нач. ОПИС №1		Белоусова Д.П.			02.2025

2024-00375-01-0-ИОС1

Капитальный ремонт здания Государственного бюджетного общеобразовательного учреждения города Москвы «Школа № 1574» по адресу: г. Москва, Старопименовский пер., д. №5

Система электроснабжения

Стадия	Лист	Листов
П	19	

Щит ЩАО-1.1. Схема электрическая принципиальная

МОСЖИЛ НИИПРОЕКТ

Формат А3 х 1

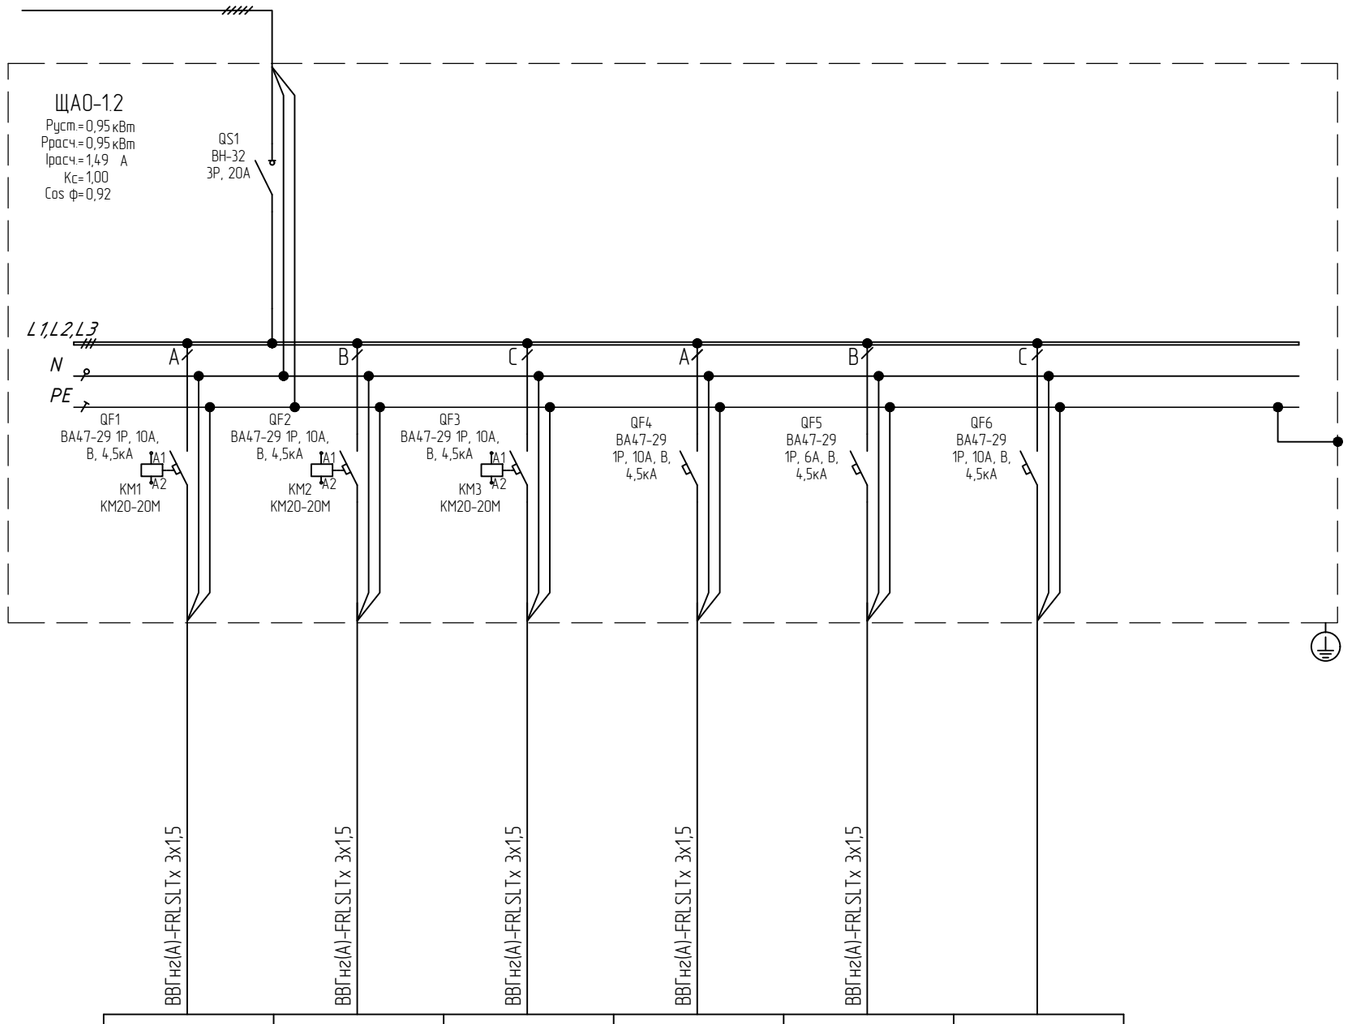

Щит распределительный	Аппараты ввода	Тип				
		Iном. (А)				
		Iу. (мА)				
	Аппараты отходящих линий	Тип				
		Iном. (А)				
		Iу. (мА)				
	Марка и сечения кабелей		ВВГнг(А)-FRLSLTx 3х1,5	ВВГнг(А)-FRLSLTx 3х1,5	ВВГнг(А)-FRLSLTx 3х1,5	ВВГнг(А)-FRLSLTx 3х1,5	ВВГнг(А)-FRLSLTx 3х1,5	
	Длина участка сети							
Электроприёмники	номер группы		АО-1.2-1	АО-1.2-2	АО-1.2-3	АО-1.2-4	АО-1.2-5	
	Руст. (кВт)		0,12	0,60	0,05	0,16	0,01	
	Iр. (А)		0,55	2,75	0,23	0,73	0,05	
	Наименование		Аварийное освещение	Аварийное освещение	Аварийное освещение	Аварийное освещение	Световые указатели "Выход"	Резерв
	Помещения		128	128, 201, 301, 401, 501	Входы в здание	121-123, 125, 126	127, 128	

Согласовано

Взам. инв.N

Подпись и дата

Инв.N подл.

Изм.	Кол.уч.	Лист	N°док.	Подп.	Дата
Разраб.		Семенов			02.2025
Провер.		Пильгуй М.Н.			02.2025
Н. контр.		Пильгуй Н.М			02.2025
Нач. ОПИС №1		Белоусова Д.П.			02.2025

2024-00375-01-0-ИОС1

Капитальный ремонт здания Государственного бюджетного общеобразовательного учреждения города Москвы «Школа № 1574» по адресу: г. Москва, Старопименовский пер., д. №5

Система электроснабжения

Стадия	Лист	Листов
П	20	

Щит ЩАО-1.2. Схема электрическая принципиальная

МОСЖИЛ НИИПРОЕКТ

Формат А3 х 1

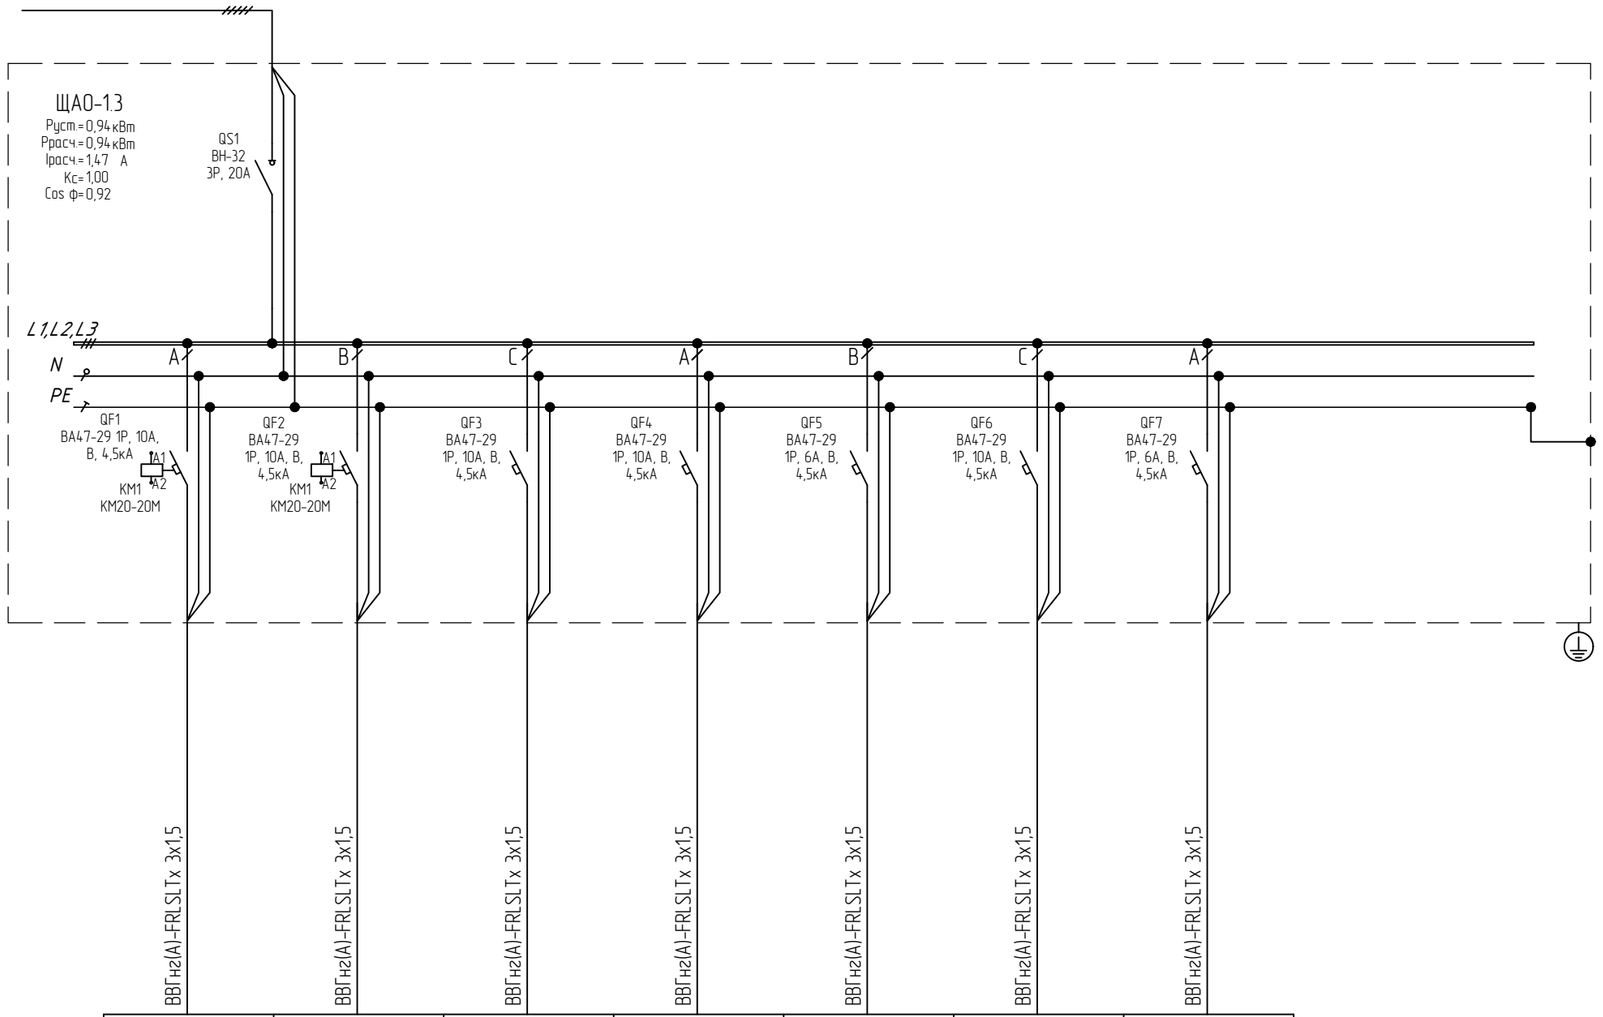

Щит распределительный		
	Аппараты ввода	Тип Iном. (А) Iу. (мА)
	Аппараты отходящих линий	Тип Iном. (А) Iу. (мА)
Марка и сечения кабелей		ВВГнг(А)-FRLSLTx 3х1,5	ВВГнг(А)-FRLSLTx 3х1,5	ВВГнг(А)-FRLSLTx 3х1,5	ВВГнг(А)-FRLSLTx 3х1,5	ВВГнг(А)-FRLSLTx 3х1,5	ВВГнг(А)-FRLSLTx 3х1,5	ВВГнг(А)-FRLSLTx 3х1,5
Длина участка сети								
Электроприёмники	номер группы	АО-1.3-1	АО-1.3-2	АО-1.3-3	АО-1.3-4	АО-1.3-5	АО-1.3-7	
	Руст. (кВт)	0,18	0,13	0,15	0,18	0,18	0,01	
	Ip. (А)	0,80	0,59	0,69	0,80	0,83	0,05	
	Наименование	Аварийное освещение	Аварийное освещение	Аварийное освещение	Аварийное освещение	Аварийное освещение	Световые указатели "Выход"	Резерв
	Помещения	140	223, 321	Входы в здание	132-136	131, 134	140, 140.1, 139, 138, 322	

Согласовано

Взам. инв.N

Подпись и дата

Инв.N подл.

Изм.	Кол.уч.	Лист	№док.	Подп.	Дата
Разраб.		Семенов			02.2025
Провер.		Пильгуй М.Н.			02.2025
Н. контр.		Пильгуй Н.М			02.2025
Нач. ОПИС №1		Белоусова Д.П.			02.2025

2024-00375-01-0-ИОС1

Капитальный ремонт здания Государственного бюджетного общеобразовательного учреждения города Москвы «Школа № 1574» по адресу: г. Москва, Старопименовский пер., д. №5

Система электроснабжения

Стадия	Лист	Листов
П	21	

Щит ЩАО-1.3. Схема электрическая принципиальная

МОСЖИЛ НИИПРОЕКТ

Формат А3 х 1

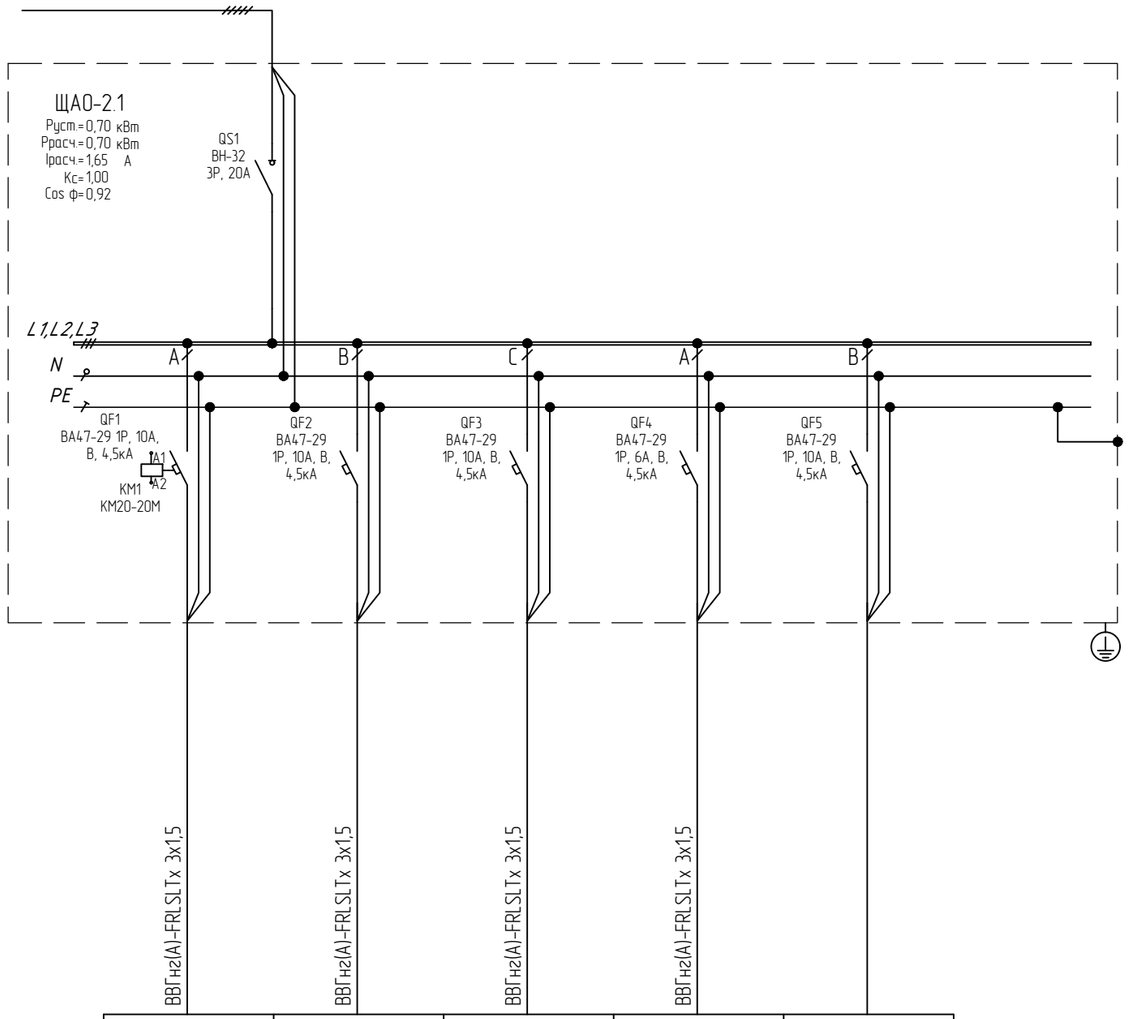

Питающая сеть, марка, сечение кабеля			ВВГнг(А)-FRLSLTx 3х1,5	ВВГнг(А)-FRLSLTx 3х1,5	ВВГнг(А)-FRLSLTx 3х1,5	ВВГнг(А)-FRLSLTx 3х1,5	
Щит распределительный	Аппараты ввода	Тип Iном. (А) Iу. (мА)					
	Аппараты отходящих линий	Тип Iном. (А) Iу. (мА)					
Марка и сечения кабелей							
Длина участка сети							
Электроприёмники	номер группы		АО-2.1-1	АО-2.1-2	АО-2.1-3	АО-2.1-4	
	Руст. (кВт)		0,36	0,21	0,12	0,01	
	Ip. (А)		1,65	0,96	0,55	0,05	
	Наименование		Аварийное освещение	Аварийное освещение	Аварийное освещение	Световые указатели "Выход"	Резерв
	Помещения		214, 218	207, 208, 211	202, 203	206, 214, 218	

Согласовано

Взам. инв.N

Подпись и дата

Инв.N подл.

Изм.	Кол.уч.	Лист	N°док.	Подп.	Дата
Разраб.		Семенов			02.2025
Провер.		Пильгуй М.Н.			02.2025
Н. контр.		Пильгуй Н.М			02.2025
Нач. ОПИС №1		Белоусова Д.П.			02.2025

2024-00375-01-0-ИОС1

Капитальный ремонт здания Государственного бюджетного общеобразовательного учреждения города Москвы «Школа № 1574» по адресу: г. Москва, Старопименовский пер., д. №5

Система электроснабжения

Стадия	Лист	Листов
П	22	

Щит ЩАО-2.1. Схема электрическая принципиальная

МОСЖИЛ НИИПРОЕКТ

Формат А3 х 1

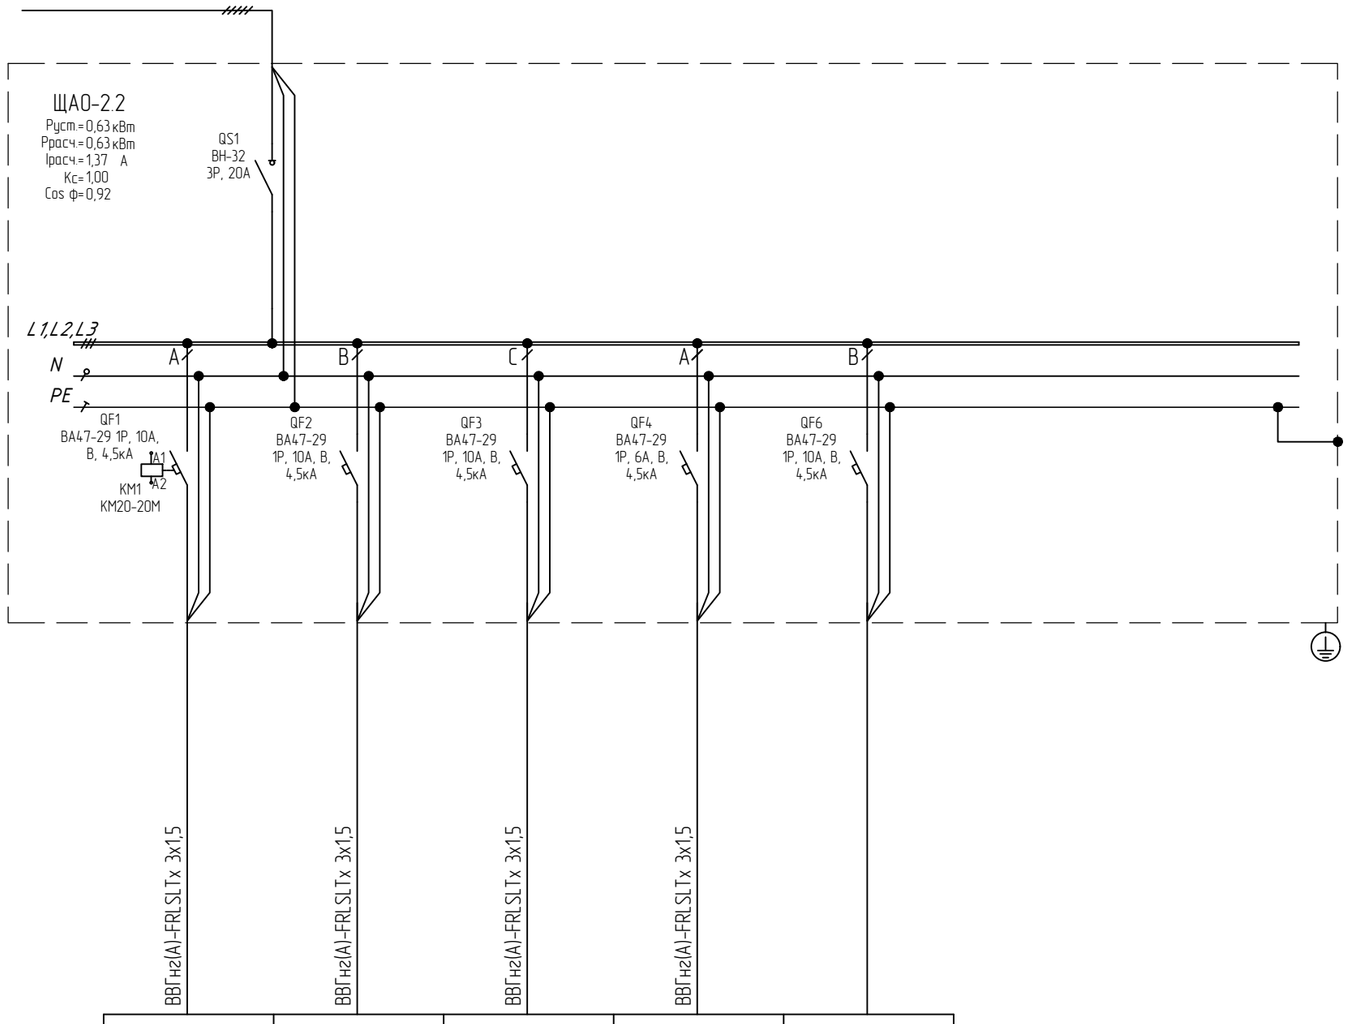

Щит распределительный	Аппараты ввода	Тип			
		Iном. (А)			
		Iу. (мА)			
	Аппараты отходящих линий	Тип			
		Iном. (А)			
		Iу. (мА)			
Марка и сечения кабелей			ВВГнг(А)-FRLSLTx 3х1,5	ВВГнг(А)-FRLSLTx 3х1,5	ВВГнг(А)-FRLSLTx 3х1,5	ВВГнг(А)-FRLSLTx 3х1,5	
Длина участка сети							
Электроприёмники	номер группы		АО-2.2-1	АО-2.2-2	АО-2.2-3	АО-2.2-4	
	Руст. (кВт)		0,30	0,24	0,08	0,01	
	Iр. (А)		1,37	1,10	0,37	0,05	
	Наименование		Аварийное освещение	Аварийное освещение	Аварийное освещение	Световые указатели "Выход"	Резерв
	Помещения		219	220	224, 229, 322	219, 220, 322	

Согласовано

Взам. инв.N

Подпись и дата

Инв.N подл.

Изм.	Кол.уч.	Лист	N°док.	Подп.	Дата
Разраб.		Семенов			02.2025
Провер.		Пильгуй М.Н.			02.2025
Н. контр.		Пильгуй Н.М			02.2025
Нач. ОПИС №1		Белоусова Д.П.			02.2025

2024-00375-01-0-ИОС1

Капитальный ремонт здания Государственного бюджетного общеобразовательного учреждения города Москвы «Школа № 1574» по адресу: г. Москва, Старопименовский пер., д. №5

Система электроснабжения

Стадия	Лист	Листов
П	23	

Щит ЩАО-2.2. Схема электрическая принципиальная

МОСЖИЛ НИИПРОЕКТ

Формат А3 х 1

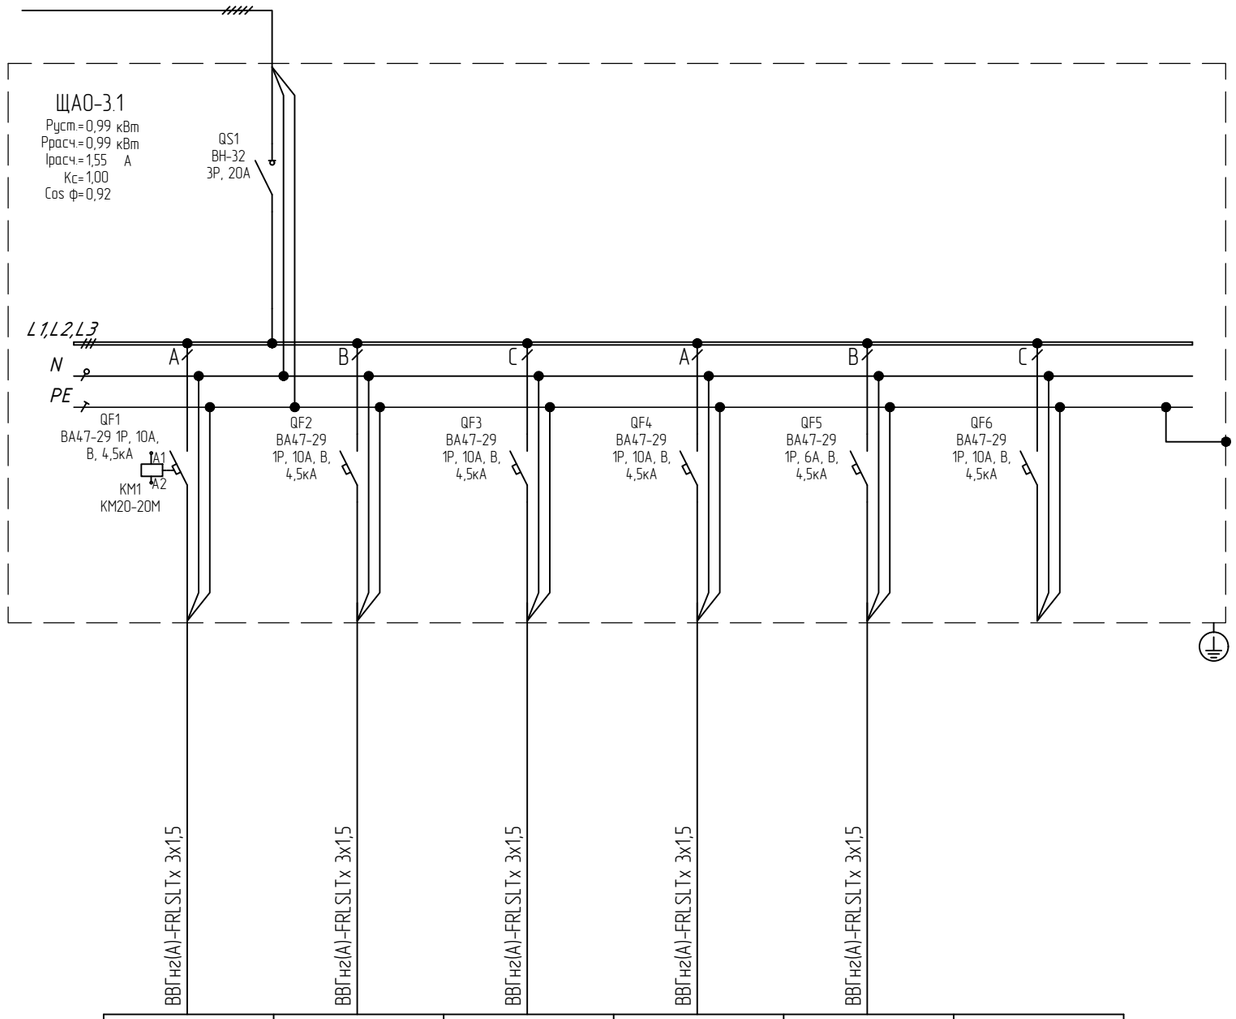

Щит распределительный	Аппараты ввода	Тип Iном. (А) Iу. (мА)					
	Аппараты отходящих линий	Тип Iном. (А) Iу. (мА)					
Марка и сечения кабелей			ВВГнг(А)-FRLSLTx 3х1,5	ВВГнг(А)-FRLSLTx 3х1,5	ВВГнг(А)-FRLSLTx 3х1,5	ВВГнг(А)-FRLSLTx 3х1,5	ВВГнг(А)-FRLSLTx 3х1,5	
Длина участка сети								
Электроприёмники	номер группы		АО-3.1-1	АО-3.1-2	АО-3.1-3	АО-3.1-4	АО-3.1-5	
	Руст. (кВт)		0,24	0,24	0,26	0,24	0,01	
	Iр. (А)		1,10	1,10	1,19	1,08	0,05	
	Наименование		Аварийное освещение	Аварийное освещение	Аварийное освещение	Аварийное освещение	Световые указатели "Выход"	Резерв
	Помещения		316	316а	312, 305, 307, 308	302, 303, 317	312, 316	

Согласовано

Взам. инв.N

Подпись и дата

Инв.N подл.

Изм.	Кол.уч.	Лист	N°док.	Подп.	Дата
Разраб.		Семенов			02.2025
Провер.		Пильгуй М.Н.			02.2025
Н. контр.		Пильгуй Н.М			02.2025
Нач. ОПИС №1		Белоусова Д.П.			02.2025

2024-00375-01-0-ИОС1

Капитальный ремонт здания Государственного бюджетного общеобразовательного учреждения города Москвы «Школа № 1574» по адресу: г. Москва, Старопименовский пер., д. №5

Система электроснабжения

Стадия	Лист	Листов
П	24	

Щит ЩАО-3.1. Схема электрическая принципиальная

МОСЖИЛ НИИПРОЕКТ

Формат А3 х 1

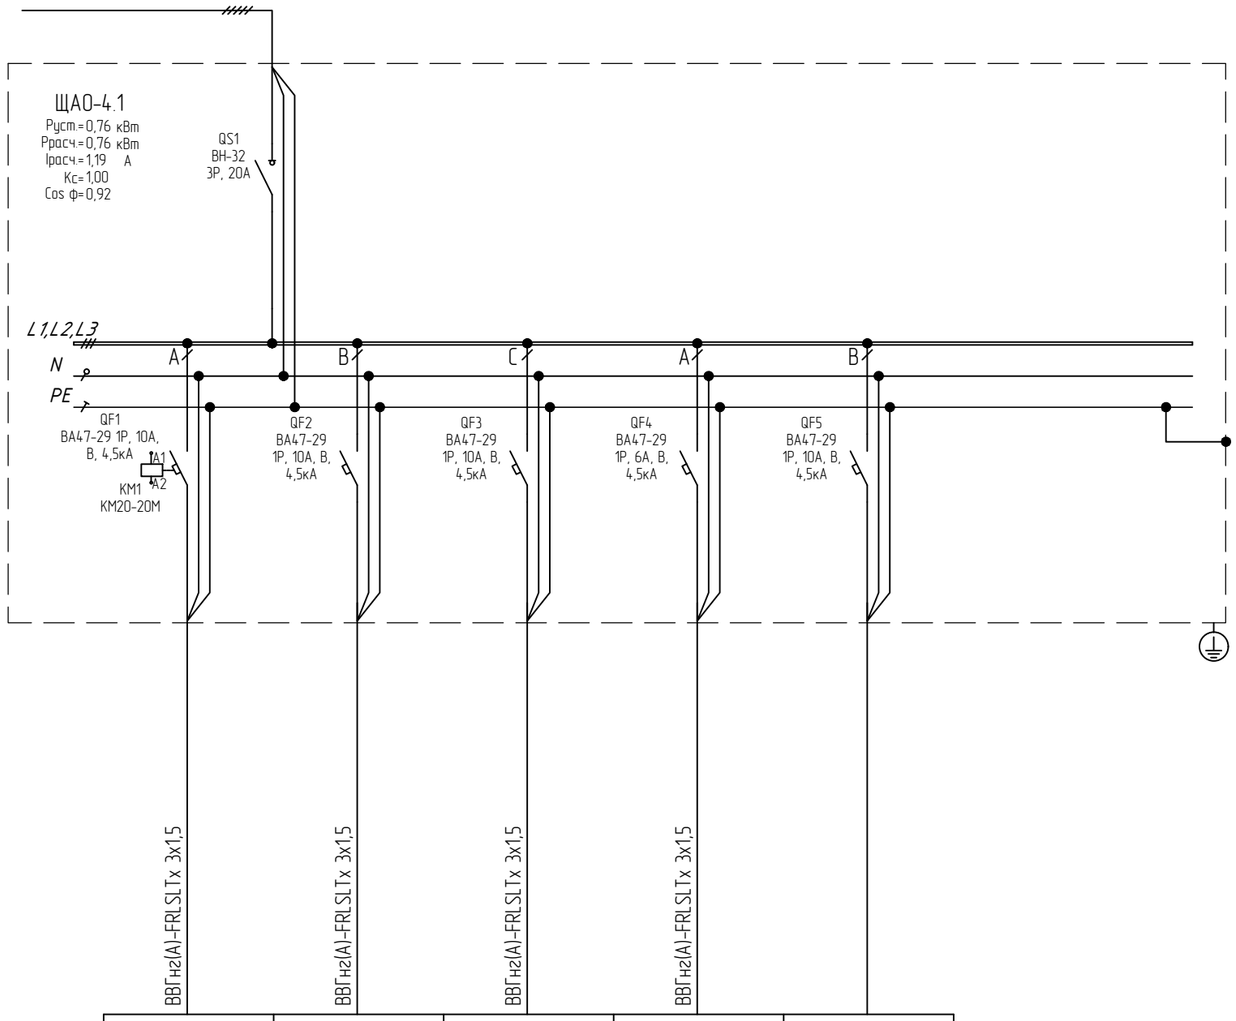

Щит распределительный	Аппараты ввода	Тип Iном. (А) Iу. (мА)				
	Аппараты отходящих линий	Тип Iном. (А) Iу. (мА)				
	Марка и сечения кабелей		ВВГнг(А)-FRLSLTx 3х1,5	ВВГнг(А)-FRLSLTx 3х1,5	ВВГнг(А)-FRLSLTx 3х1,5	ВВГнг(А)-FRLSLTx 3х1,5	
	Длина участка сети						
Электроприёмники	номер группы		АО-4.1-1	АО-4.1-2	АО-4.1-3	АО-4.1-4	
	Руст. (кВт)		0,36	0,21	0,18	0,01	
	Ip. (А)		1,65	0,96	0,82	0,05	
	Наименование		Аварийное освещение	Аварийное освещение	Аварийное освещение	Световые указатели "Выход"	Резерв
	Помещения		415	405, 406, 407 410	402, 403, 404	415	

Согласовано

Взам. инв.N

Подпись и дата

Инв.N подл.

Изм.	Кол.уч.	Лист	N°док.	Подп.	Дата
Разраб.		Семенов			02.2025
Провер.		Пильгуй М.Н.			02.2025
Н. контр.		Пильгуй Н.М			02.2025
Нач. ОПИС №1		Белоусова Д.П.			02.2025

2024-00375-01-0-ИОС1

Капитальный ремонт здания Государственного бюджетного общеобразовательного учреждения города Москвы «Школа № 1574» по адресу: г. Москва, Старопименовский пер., д. №5

Система электроснабжения

Стадия	Лист	Листов
П	25	

Щит ЩАО-4.1. Схема электрическая принципиальная

МОСЖИЛ НИИПРОЕКТ

Формат А3 х 1

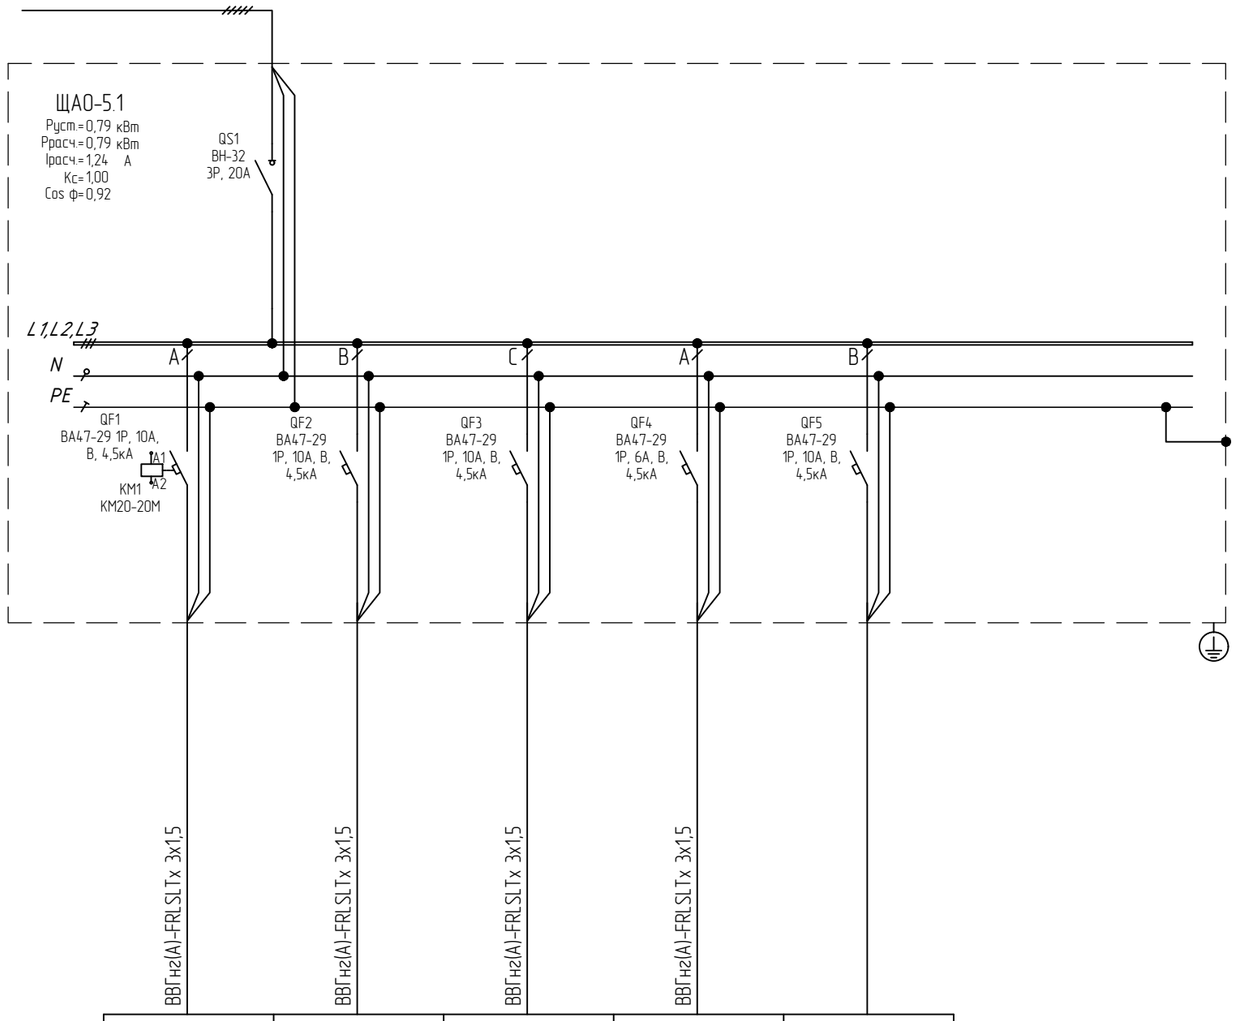

Питающая сеть, марка, сечение кабеля			ВВГнг(А)-FRLSLTx 3х1,5	ВВГнг(А)-FRLSLTx 3х1,5	ВВГнг(А)-FRLSLTx 3х1,5	ВВГнг(А)-FRLSLTx 3х1,5	
Щит распределительный	Аппараты ввода	Тип Iном. (А) Iу. (мА)					
	Аппараты отходящих линий	Тип Iном. (А) Iу. (мА)					
Марка и сечения кабелей							
Длина участка сети							
Электроприёмники	номер группы		АО-5.1-1	АО-5.1-2	АО-5.1-3	АО-5.1-4	
	Руст. (кВт)		0,36	0,24	0,18	0,01	
	Ip. (А)		1,65	1,10	0,82	0,05	
	Наименование		Аварийное освещение	Аварийное освещение	Аварийное освещение	Световые указатели "Выход"	Резерв
	Помещения		515	506, 507, 508, 511	502, 503, 505, 514	515	

Согласовано

Взам. инв.N

Подпись и дата

Инв.N подл.

Изм.	Кол.уч.	Лист	N°док.	Подп.	Дата
Разраб.		Семенов			02.2025
Провер.		Пильгуй М.Н.			02.2025
Н. контр.		Пильгуй Н.М			02.2025
Нач. ОПИС №1		Белоусова Д.П.			02.2025

2024-00375-01-0-ИОС1

Капитальный ремонт здания Государственного бюджетного общеобразовательного учреждения города Москвы «Школа № 1574» по адресу: г. Москва, Старопименовский пер., д. №5

Система электроснабжения

Стадия	Лист	Листов
П	26	

Щит ЩАО-5.1. Схема электрическая принципиальная

МОСЖИЛ НИИПРОЕКТ

Формат А3 х 1

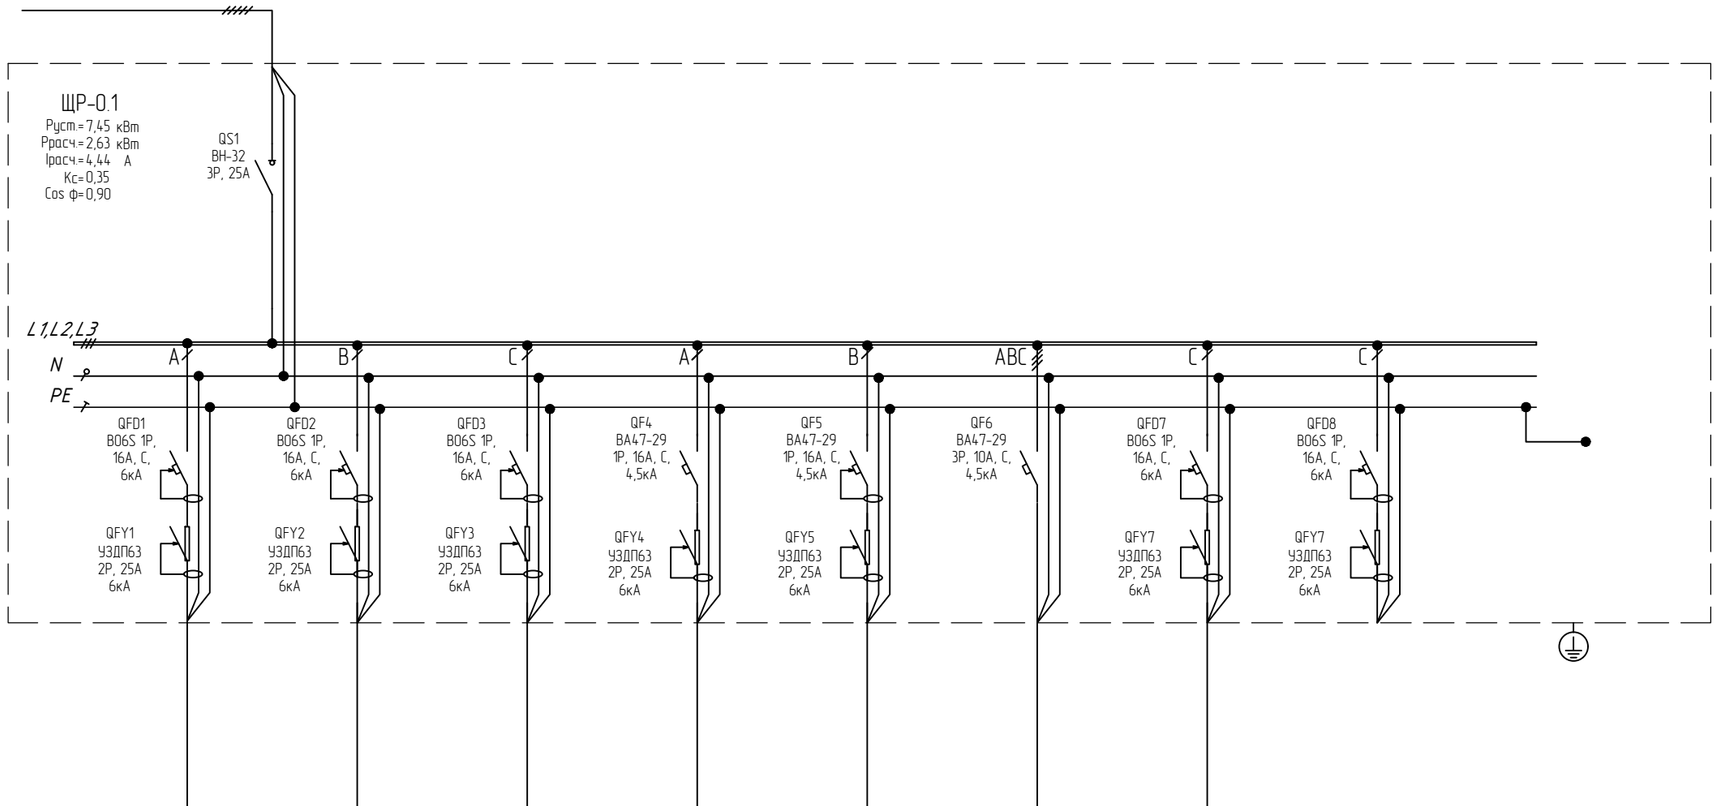

Щит распределительный			Питающая сеть, марка, сечение кабеля								
	Аппараты ввода	Тип Iном. (А) Iу. (мА)									
	Аппараты отходящих линий	Тип Iном. (А) Iу. (мА)									
	Марка и сечения кабелей		ВВГнг(А)-LSLTx 3х2,5	ВВГнг(А)-LSLTx 3х2,5	ВВГнг(А)-LSLTx 3х2,5	ВВГнг(А)-LSLTx 3х2,5	ВВГнг(А)-LSLTx 3х2,5	ВВГнг(А)-LSLTx 5х2,5	ВВГнг(А)-LSLTx 3х2,5		
	Длина участка сети										
Электроприёмники	номер группы		Р-0.1-1	Р-0.1-2	Р-0.1-3	Р-0.1-4	Р-0.1-5	Р-0.1-6	Р-0.1-7		
	Руст. (кВт)		1,70	1,70	1,70	0,25	1,00	1,10	0,40		
	Ip. (А)		7,78	7,78	7,78	1,14	24,49	2,31	1,83		
	Наименование		Бытовые розетки, рукосушитель	Бытовые розетки, рукосушитель	Бытовые розетки, рукосушитель	ЯТП	Электроконвектор в электрощитовой	Повысительная станция ANTARUS 2 MLV6-6/01/GPRS	Бытовые розетки	Резерв	
	Помещения		011, 013	014, 015	009, 020.4	017	017	017	010		

Согласовано

Взам. инв.N

Подпись и дата

Инв.N подл.

Изм.	Кол.уч.	Лист	№док.	Подп.	Дата
Разраб.		Семенов			02.2025
Провер.		Пильгуй М.Н.			02.2025
Н. контр.		Пильгуй Н.М			02.2025
Нач. ОПИС №1		Белоусова Д.П.			02.2025

2024-00375-01-0-ИОС1

Капитальный ремонт здания Государственного бюджетного общеобразовательного учреждения города Москвы «Школа № 1574» по адресу: г. Москва, Старопименовский пер., д. №5

Система электроснабжения

Стадия	Лист	Листов
П	27	

Щит ЩР-0.1. Схема электрическая принципиальная

МОСЖИЛ НИИПРОЕКТ

Формат А3 х 1

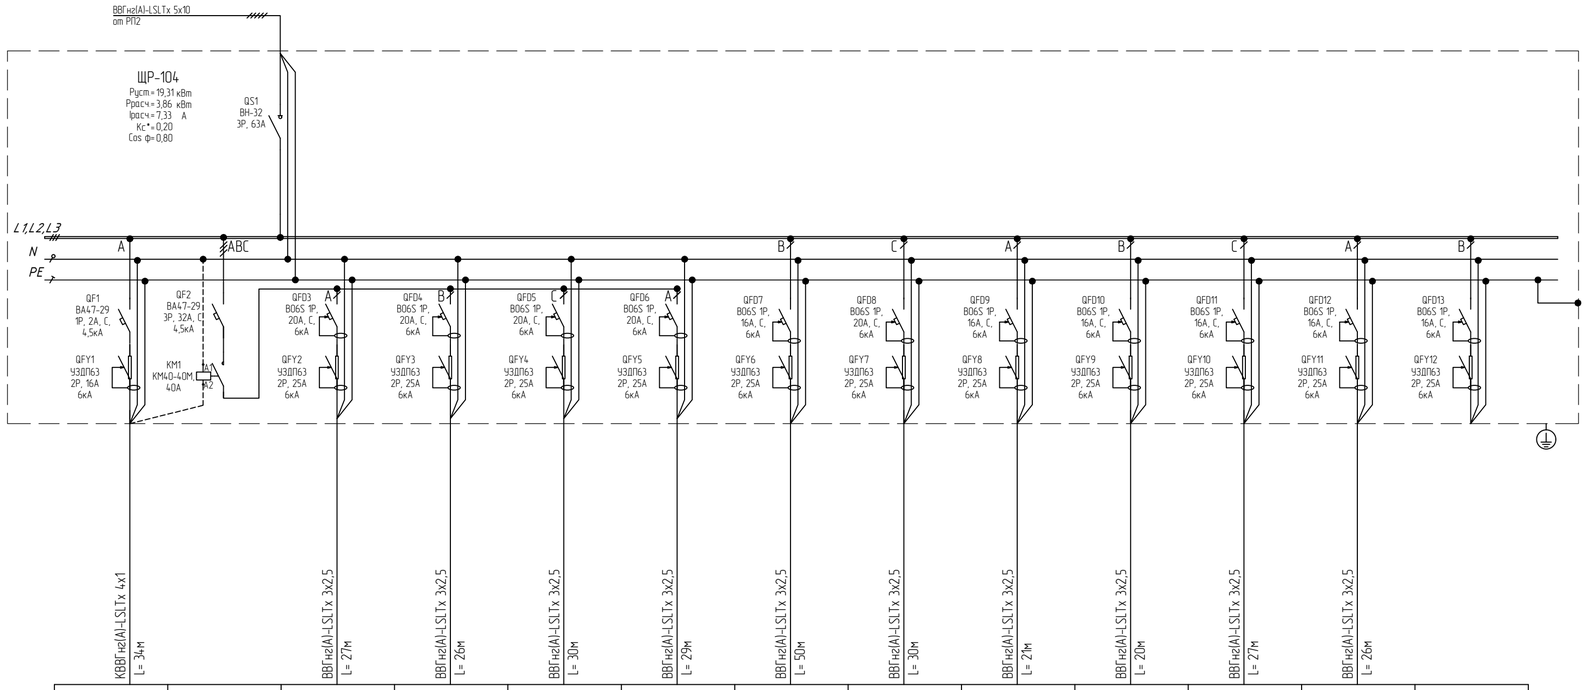

Питающая сеть, марка, сечение кабеля													
Щит распределительный	Аппараты ввода	Тип Iном. (А) Iу. (мА)											
	Аппараты отходящих линий	Тип Iном. (А) Iу. (мА)											
Марка и сечения кабелей	Длина участка сети												
Электроприёмники	номер группы		P-104.1		P-104.2	P-104.3	P-104.4	P-104.5	P-104.6	P-104.7	P-104.8	P-104.9	P-104.10	P-104.11	
	Pуст. (кВт)		0,01		3,00	3,00	3,00	3,00	0,80	0,50	1,50	1,50	1,50	1,50	
	Ip. (А)		0,02		13,73	13,73	13,73	13,73	3,66	2,29	6,86	6,86	6,86	6,86	
	Наименование		Кнопка с подсветкой для стола преподавателя**		Лючки в полу учеников	Лючки в полу учеников	Лючки в полу учеников	Лючки в полу учеников	Бытовые розетки	Машина заточная (поз.187)	Токарный станок по металлу (поз.183) Машина заточная (поз.187)	Станок сверлильный (поз.186)	Станок лазерной резки и гравировки (поз.181), Токарный станок по дереву (поз.185)	Фрезерный станок (поз.182) Вытяжная система (поз. 184)	Резерв
	Помещения		104		104	104	104	104	104	104	104	104	104	104	

* — Расчёт нагрузок выполнен согласно СП 256.1325800.2016.
- оборудование учебно-производственных мастерских — табл. 7.8;

** — Кнопка управления питанием размещается на столе преподавателя

Согласовано

Взам. инв.N

Подпись и дата

Инв.N подл.

Изм.	Кол.уч.	Лист	N°док.	Подп.	Дата
Разраб.		Семенов			02.2025
Провер.		Пильгуй М.Н.			02.2025
Н. контр.		Пильгуй Н.М.			02.2025
Нач. ОПИС №1		Белоусова Д.П.			02.2025

2024-00375-01-0-ИОС1

Капитальный ремонт здания Государственного бюджетного общеобразовательного учреждения города Москвы «Школа № 1574» по адресу: г. Москва, Старопименовский пер., д. №5

Система электроснабжения

Стадия	Лист	Листов
П	28	

Щит ЩР-104. Схема электрическая принципиальная

МОСЖИЛ НИИПРОЕКТ

Формат А4 х 3

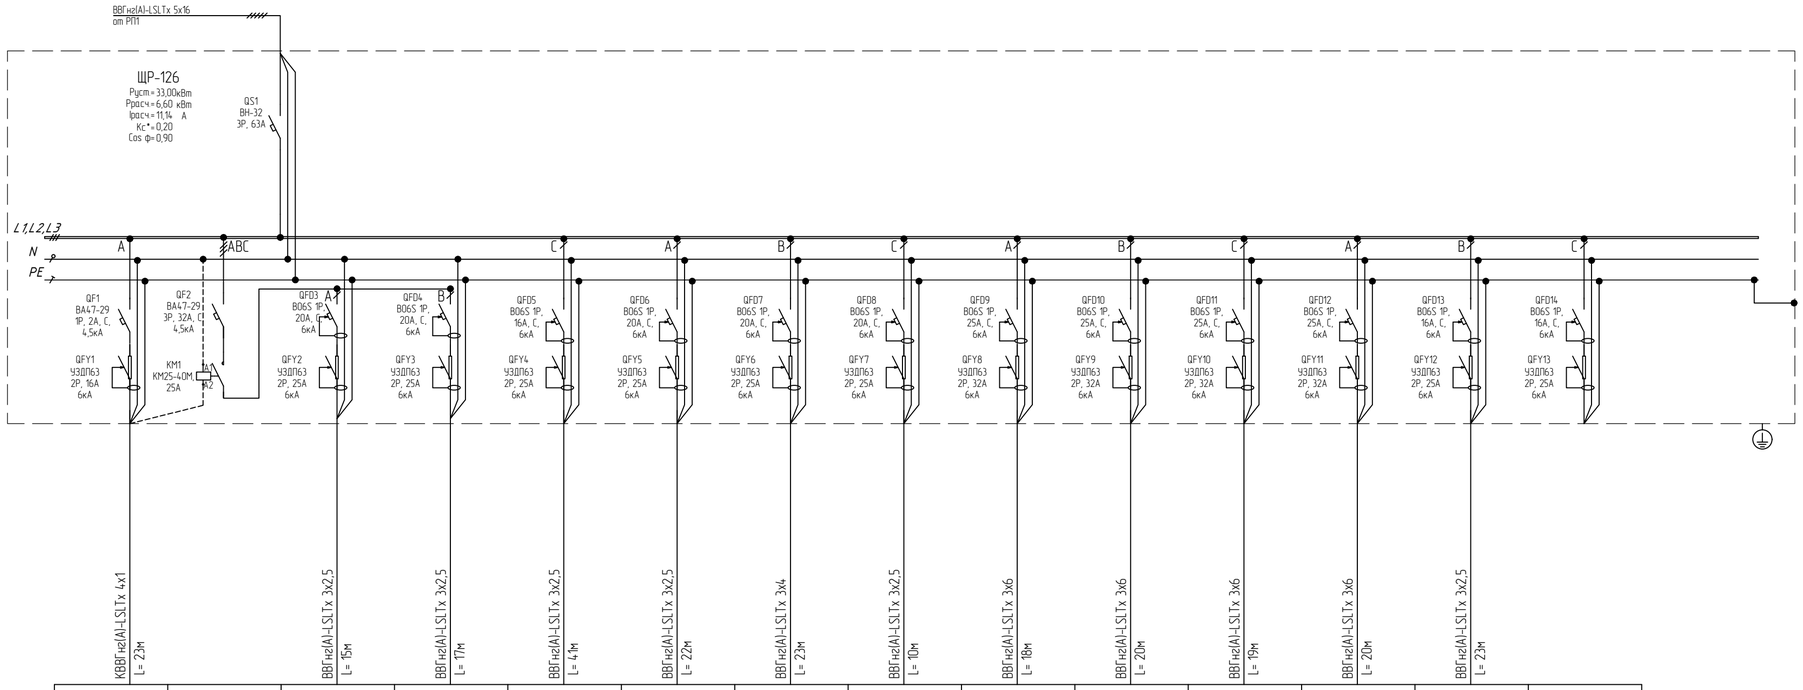

Электроприёмники														
номер группы	P-126.1		P-126.2	P-126.3	P-126.4	P-126.5	P-126.6	P-126.7	P-126.8	P-126.9	P-126.10	P-126.11	P-126.12	
Pуст. (кВт)	0,01		1,20	1,20	0,80	2,00	4,00	3,60	5,00	5,00	5,00	5,00	0,20	
Ip. (А)	0,02		5,49	5,49	3,66	9,15	19,32	16,48	22,88	22,88	22,88	22,88	0,92	
Наименование	Кнопка с подсветкой для стола преподавателя**		Лючки в полу учеников	Лючки в полу учеников	Бытовые розетки	Посудомоечная машина, 2 шт (поз. 85)	Микроволновая печь, чайник	Утюг, 2 шт	Варочная панель (поз. 87)	Варочная панель, тип 1 (поз. 87)	Варочная панель тип 2, 2 шт (поз. 87.1)	Духовой шкаф тип 2, 2 шт (поз. 87.2)	Вытяжка, 2 шт	Резерв
Помещения	126		126	126	126	126	126	126	126	126	126	126	126	

* — Расчёт нагрузок выполнен согласно СП 256.1325800.2016:
- оборудование учебно-производственных мастерских — табл. 7.8.

** - Кнопка управления питанием размещается на столе преподавателя

Согласовано

Взам. инв.N

Подпись и дата

Инв.N подл.

Изм.	Кол.уч.	Лист	N°док.	Подп.	Дата
Разраб.		Семенов			02.2025
Провер.		Пильгуй М.Н.			02.2025
Н. контр.		Пильгуй Н.М.			02.2025
Нач. ОПИС №1		Белоусова Д.П.			02.2025

2024-00375-01-0-ИОС1

Капитальный ремонт здания Государственного бюджетного общеобразовательного учреждения города Москвы «Школа № 1574» по адресу: г. Москва, Старопименовский пер., д. №5

Система электроснабжения

Стадия	Лист	Листов
П	29	

Щит ЩР-126. Схема электрическая принципиальная

МОСЖИЛ НИИПРОЕКТ

Формат А4 х 3

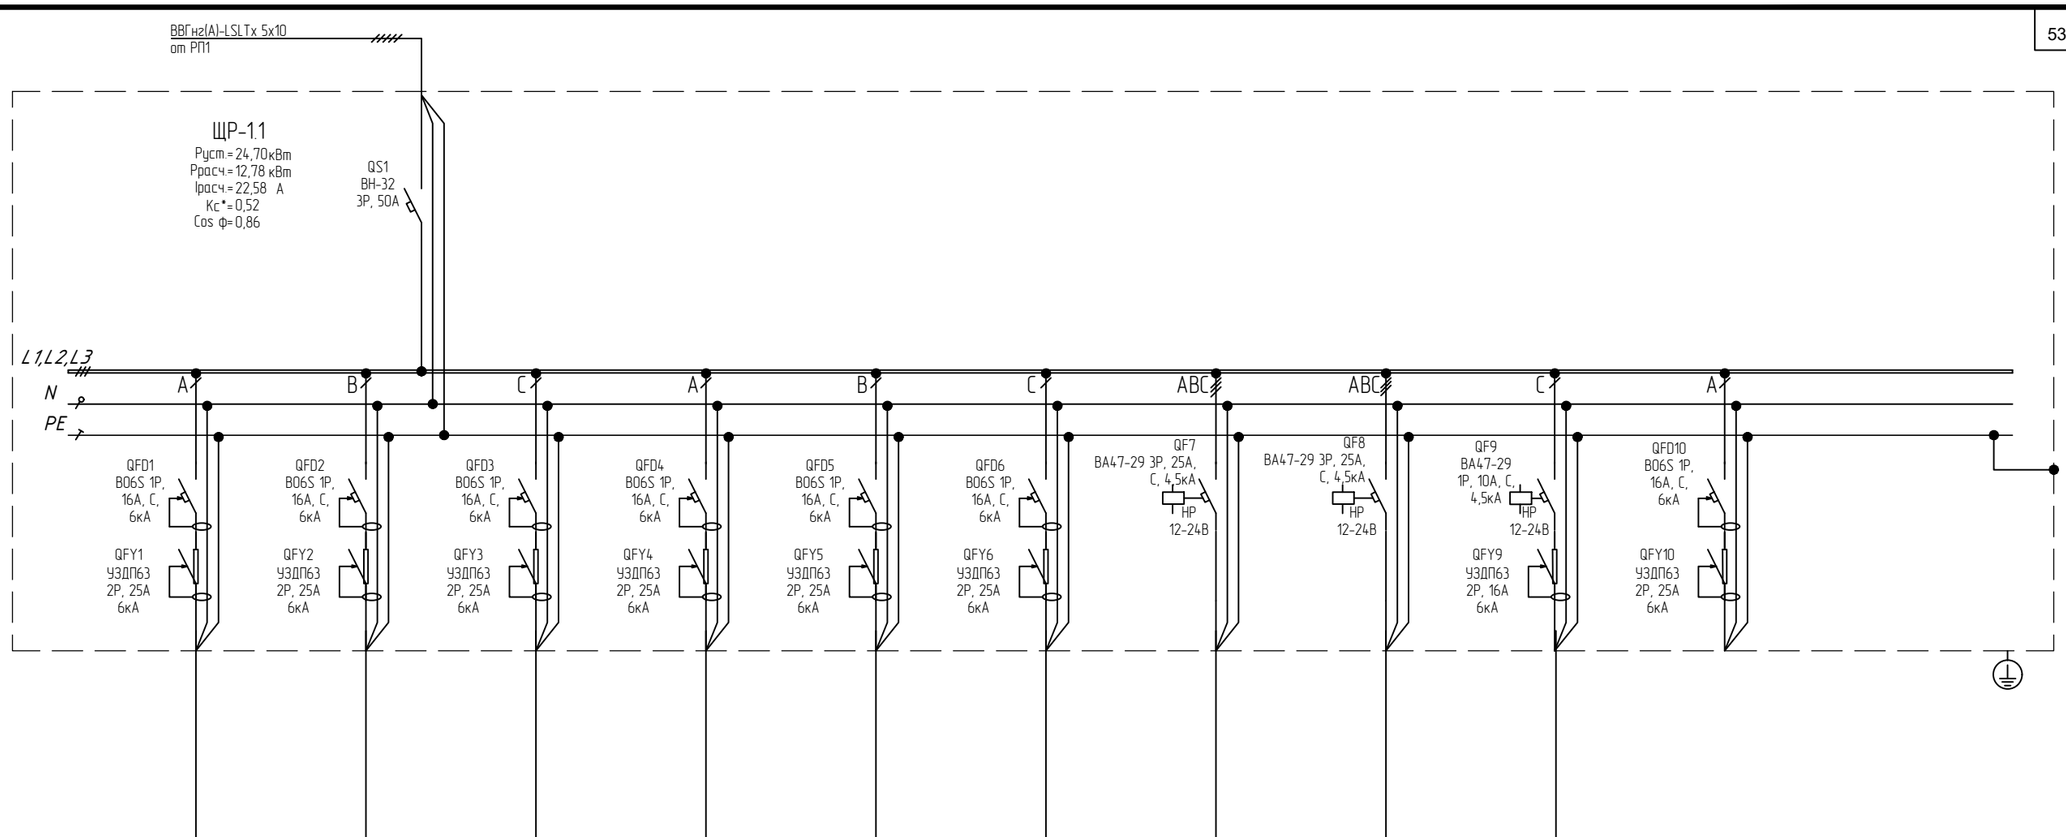

Питающая сеть, марка, сечение кабеля			ВВГнг(А)-LSLTx 3х2,5	ВВГнг(А)-LSLTx 3х2,5	ВВГнг(А)-LSLTx 3х2,5	ВВГнг(А)-LSLTx 3х2,5	ВВГнг(А)-LSLTx 3х2,5	ВВГнг(А)-LSLTx 3х2,5	ВВГнг(А)-LSLTx 5х4	ВВГнг(А)-LSLTx 5х4	ВВГнг(А)-LSLTx 3х1,5	
Щит распределительный	Аппараты ввода	Тип Iном. (А) Iу. (мА)										
	Аппараты отходящих линий	Тип Iном. (А) Iу. (мА)										
Марка и сечения кабелей			L= 58м	L= 38м	L= 39м	L= 43м	L= 47м	L= 44м	L= 38м	L= 37м	L= 48м	
Длина участка сети												
Электроприёмники	номер группы		P-1.1.1	P-1.1.2	P-1.1.3	P-1.1.4	P-1.1.5	P-1.1.6	P-1.1.7	P-1.1.8	P-1.1.9	
	Руст. (кВт)		0,80	2,50	1,50	2,50	2,70	2,70	6,00	6,00	0,04	
	Ip. (А)		3,66	11,44	6,86	11,44	12,36	12,36	9,60	9,60	0,23	
	Наименование		Бытовые розетки, бактерицидный облучатель, Весы, АРМ-1шт	Водонагреватель	Рукосушитель	Водонагреватель	Водонагреватель; Бытовые розетки	Рукосушитель, розетки коридора	Тепловая завеса	Тепловая завеса	Внутренние блоки К1	Резерв
	Помещения		109	109	108	108	107	119	101	105	107, 109	

* — Расчёт нагрузок выполнен согласно СП 256.1325800.2016:
- бытовые розетки — табл. 7.7;
- АРМ и электросушители — табл. 7.8.
- водонагреватели - табл.7.5.

Согласовано

Взам. инв.N

Подпись и дата

Инв.N подл.

Изм.	Кол.уч.	Лист	N°док.	Подп.	Дата
Разраб.		Семенов			02.2025
Провер.		Пильгуй М.Н.			02.2025
Н. контр.		Пильгуй Н.М			02.2025
Нач. ОПИС N°1		Белоусова Д.П.			02.2025

2024-00375-01-0-ИОС1

Капитальный ремонт здания Государственного бюджетного общеобразовательного учреждения города Москвы «Школа № 1574» по адресу: г. Москва, Старопименовский пер., д. №5

Система электроснабжения

Стадия	Лист	Листов
П	30	

Щит ЩР-1.1. Схема электрическая принципиальная

МОСЖИЛ НИИПРОЕКТ

Формат А3 х 1

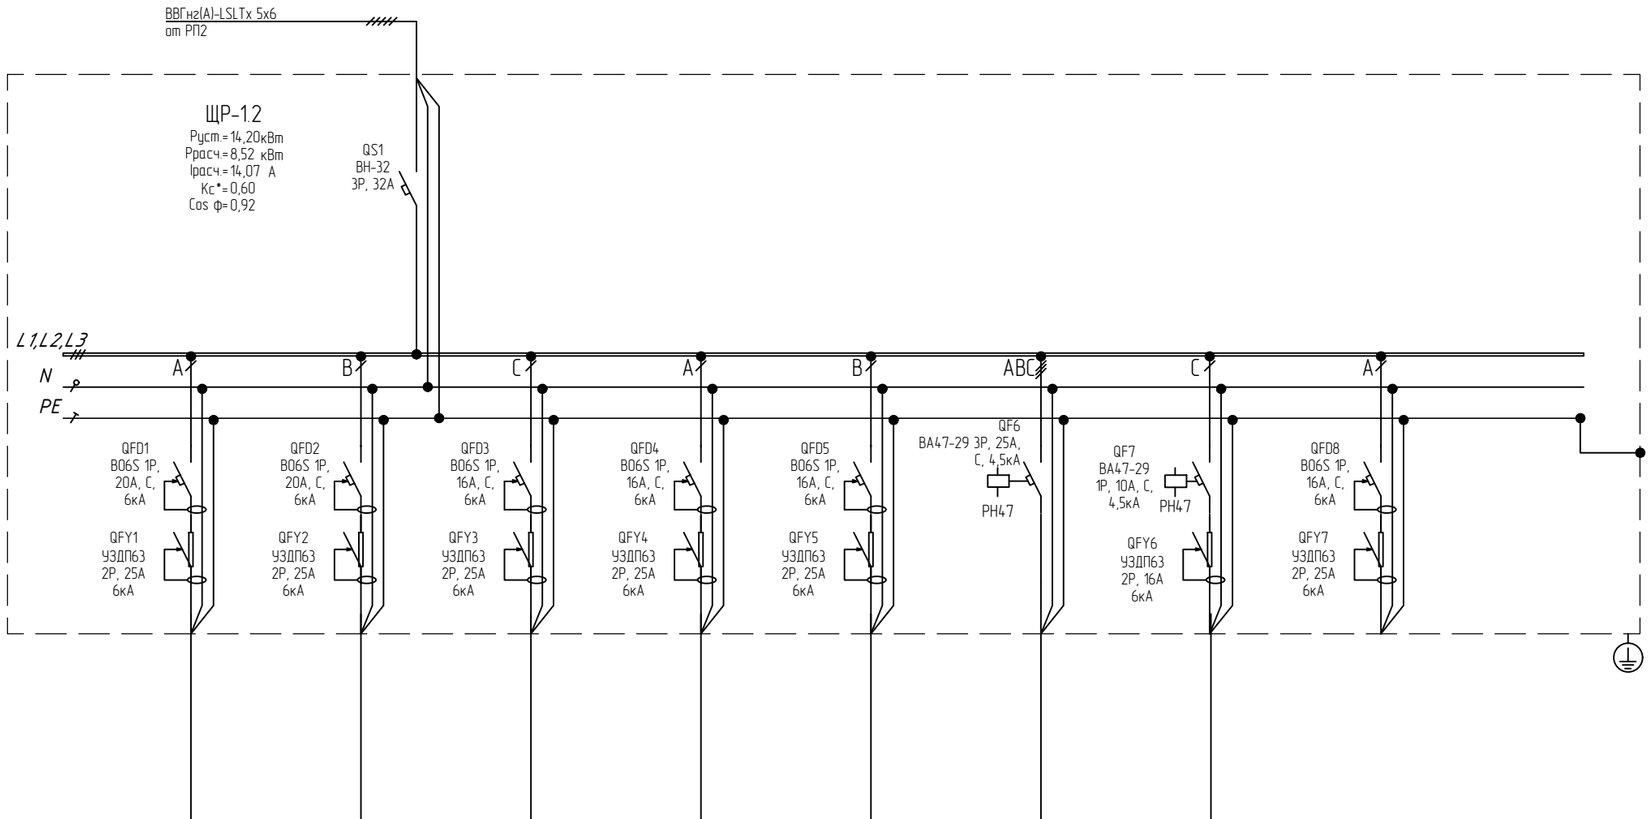

Щит распределительный			ВВГнг(А)-LSLTх 3х4	ВВГнг(А)-LSLTх 3х2,5	ВВГнг(А)-LSLTх 3х2,5	ВВГнг(А)-LSLTх 3х2,5	ВВГнг(А)-LSLTх 3х2,5	ВВГнг(А)-LSLTх 5х4	ВВГнг(А)-LSLTх 3х1,5	
	Аппараты ввода	Тип Iном. (А) Iу. (мА)								
	Аппараты отходящих линий	Тип Iном. (А) Iу. (мА)								
	Марка и сечения кабелей		L= 44м	L= 43м	L= 18м	L= 12м	L= 51м	L= 26м	L= 27м	
	Длина участка сети									
Электроприёмники	номер группы		P-1.2.1	P-1.2.2	P-1.2.3	P-1.2.4	P-1.2.5	P-1.2.6	P-1.2.7	
	Руст. (кВт)		4,00	0,60	1,50	1,50	1,00	6,00	0,02	14,62
	Ip. (А)		18,31	2,75	6,86	6,86	4,58	9,60	0,11	
	Наименование		Бытовые розетки (чайник, холодильник, микроволновая печь)	Бытовые розетки	Рукосушитель	Рукосушитель	Розетки коридора	Тепловая завеса	Внутренние блоки К2	Резерв
	Помещения		122	124	112	120	107	127	124	

* — Расчёт нагрузок выполнен согласно СП 256.1325800.2016:
- бытовые розетки — табл. 7.7;
- АРМ и электросушители — табл. 7.8.

Согласовано

Взам. инв.N

Подпись и дата

Инв.N подл.

Изм.	Кол.уч.	Лист	N°док.	Подп.	Дата
Разраб.		Семенов			02.2025
Провер.		Пильгуй М.Н.			02.2025
Н. контр.		Пильгуй Н.М			02.2025
Нач. ОПИС №1		Белоусова Д.П.			02.2025

2024-00375-01-0-ИОС1

Капитальный ремонт здания Государственного бюджетного общеобразовательного учреждения города Москвы «Школа № 1574» по адресу: г. Москва, Старопименовский пер., д. №5

Система электроснабжения

Стадия	Лист	Листов
П	31	

Щит ЩР-1.2. Схема электрическая принципиальная

МОСЖИЛ НИИПРОЕКТ

Формат А3 х 1

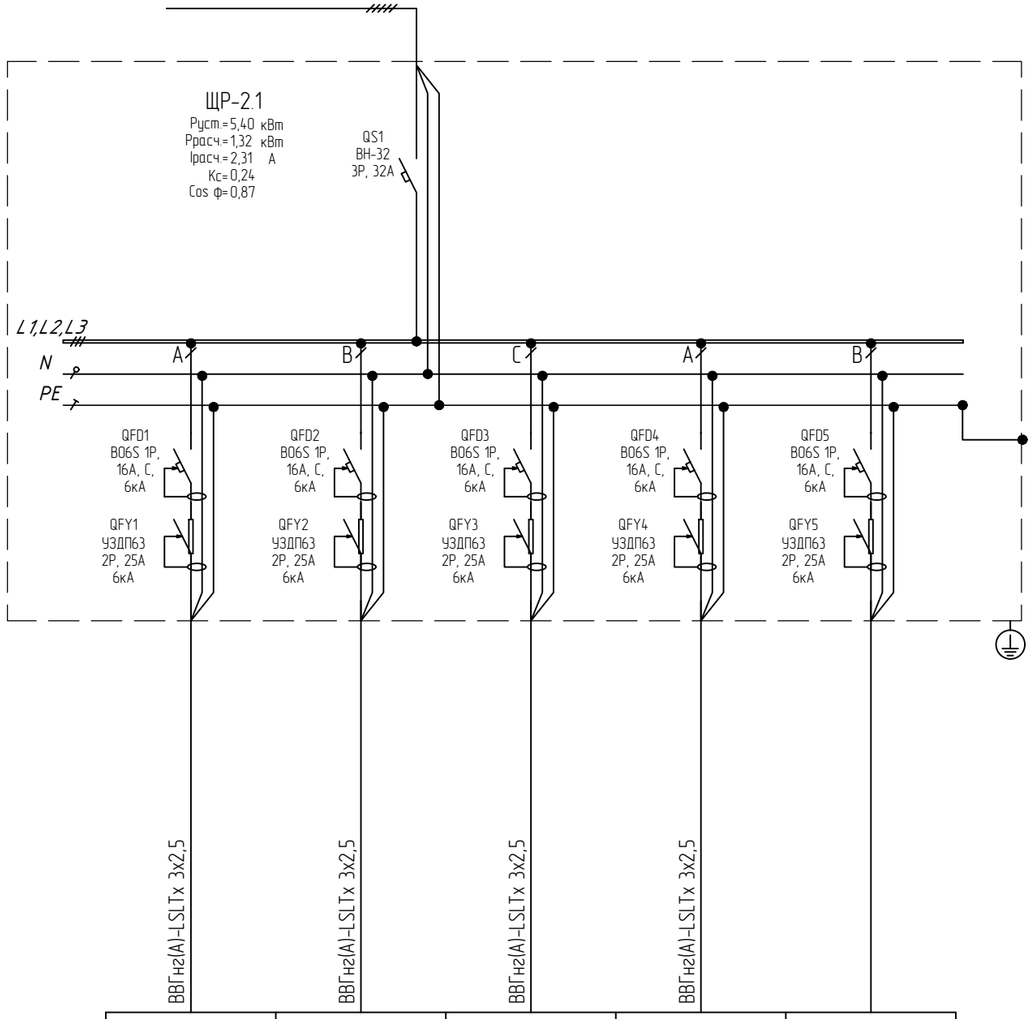

Щит распределительный	Аппараты ввода	Тип Iном. (А) Iу. (мА)	Питающая сеть, марка, сечение кабеля		
	Аппараты отходящих линий	Тип Iном. (А) Iу. (мА)			
	Марка и сечения кабелей		ВВГнг(А)-LSLTx 3х2,5	ВВГнг(А)-LSLTx 3х2,5	ВВГнг(А)-LSLTx 3х2,5	ВВГнг(А)-LSLTx 3х2,5	
	Длина участка сети						
Электроприёмники	номер группы		Р-2.1.1	Р-2.1.2	Р-2.1.3	Р-2.1.4	
	Руст. (кВт)		0,80	0,80	0,80	1,50	
	Ip. (А)		3,66	3,66	3,66	6,86	
	Наименование		Бытовые розетки, АРМ - 1шт	Бытовые розетки, АРМ - 1шт	Бытовые розетки, АРМ - 1шт	Рукосушитель	Резерв
	Помещения		211	208	207	213	

Согласовано

Взам. инв.N

Подпись и дата

Инв.N подл.

Изм.	Кол.уч.	Лист	N°док.	Подп.	Дата
Разраб.		Семенов			02.2025
Провер.		Пильгуй М.Н.			02.2025
Н. контр.		Пильгуй Н.М			02.2025
Нач. ОПИС №1		Белоусова Д.П.			02.2025

2024-00375-01-0-ИОС1

Капитальный ремонт здания Государственного бюджетного общеобразовательного учреждения города Москвы «Школа № 1574» по адресу: г. Москва, Старопименовский пер., д. №5

Система электроснабжения

Стадия	Лист	Листов
П	32	

Щит ЩР-2.1. Схема электрическая принципиальная

МОСЖИЛ НИИПРОЕКТ

Формат А3 х 1

Питающая сеть, марка, сечение кабеля

Щит распределительный

Аппараты ввода: Тип Iном. (А) Iу. (мА)

Аппараты отходящих линий: Тип Iном. (А) Iу. (мА)

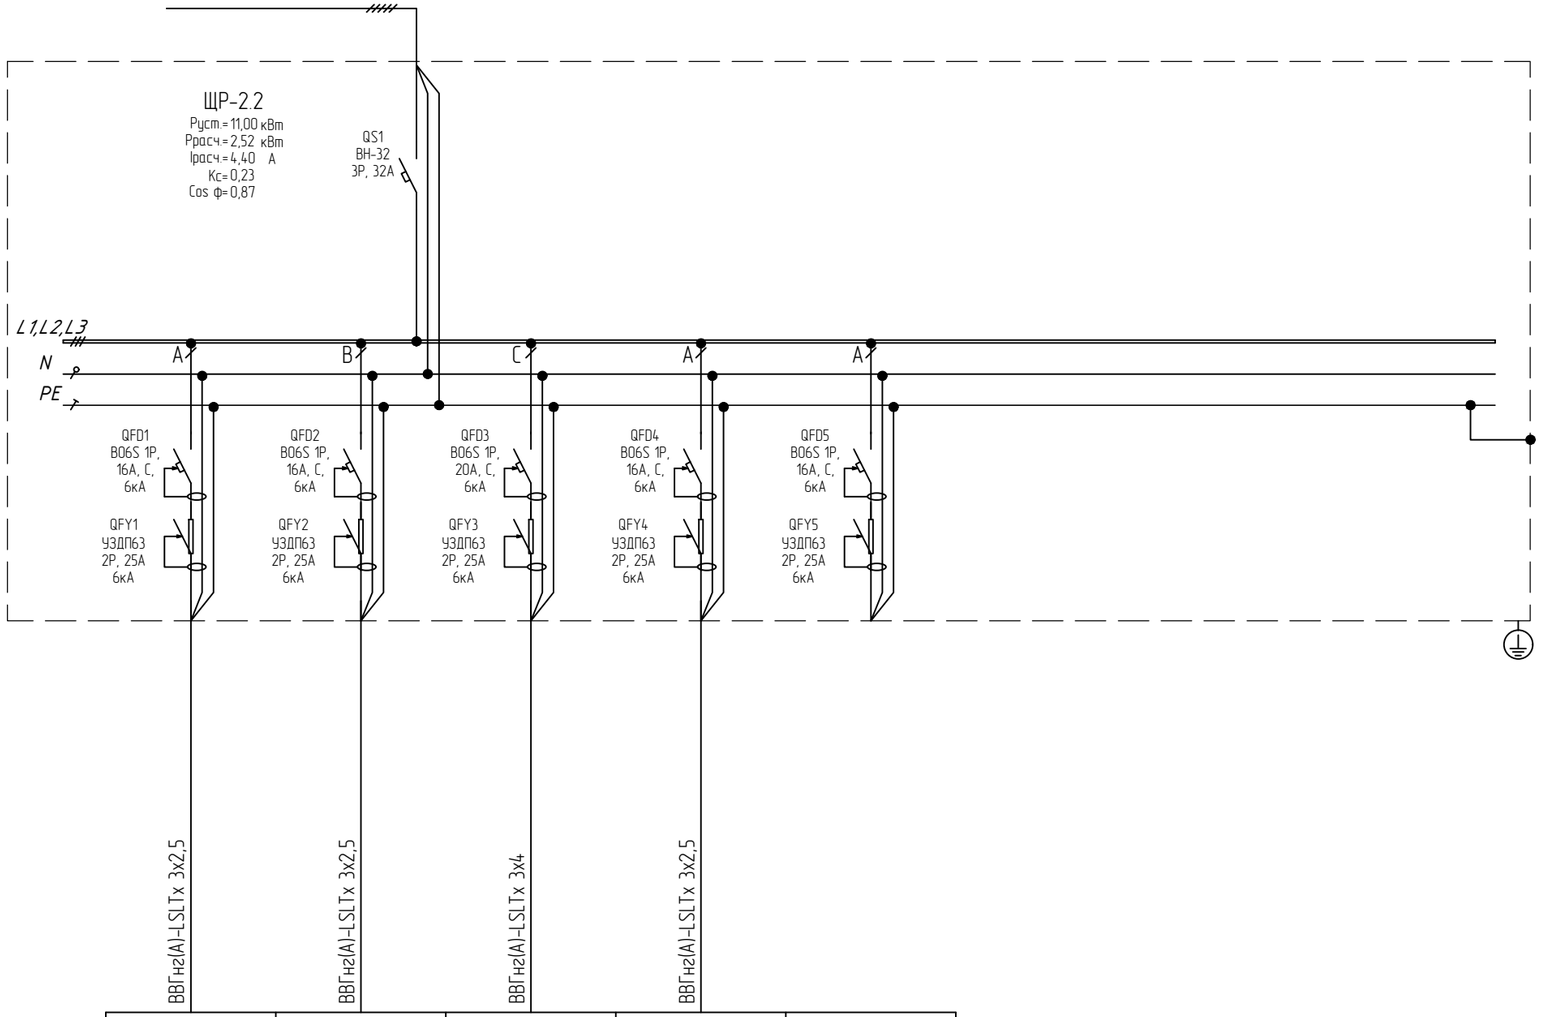

Марка и сечения кабелей

Длина участка сети

	ВВГнг(А)-LSLTx 3х2,5	ВВГнг(А)-LSLTx 3х2,5	ВВГнг(А)-LSLTx 3х4	ВВГнг(А)-LSLTx 3х2,5	
Электроприёмники: номер группы	Р-2.2.1	Р-2.2.2	Р-2.2.3	Р-2.2.4	
Руст. (кВт)	1,80	1,60	4,00	3,00	
Ip. (А)	8,24	7,32	18,31	13,73	
Наименование	Бытовые розетки, АРМ - 2шт	АРМ - 4шт	Бытовые розетки (чайник, холодильник, микроволновая печь)	Бытовые розетки (чайник, холодильник, микроволновая печь)	Рукосушитель, 2шт
Помещения	202	203	212		

Согласовано

Взам. инв.N

Подпись и дата

Инв.N подл.

Изм.	Кол.уч.	Лист	N°док.	Подп.	Дата
Разраб.		Семенов			02.2025
Провер.		Пильгуй М.Н.			02.2025
Н. контр.		Пильгуй Н.М			02.2025
Нач. ОПИС №1		Белоусова Д.П.			02.2025

2024-00375-01-0-ИОС1

Капитальный ремонт здания Государственного бюджетного общеобразовательного учреждения города Москвы «Школа № 1574» по адресу: г. Москва, Старопименовский пер., д. №5

Система электроснабжения

Стадия	Лист	Листов
П	33	

Щит ЩР-2.2. Схема электрическая принципиальная

МОСЖИЛ НИИПРОЕКТ

Формат А3 х 1

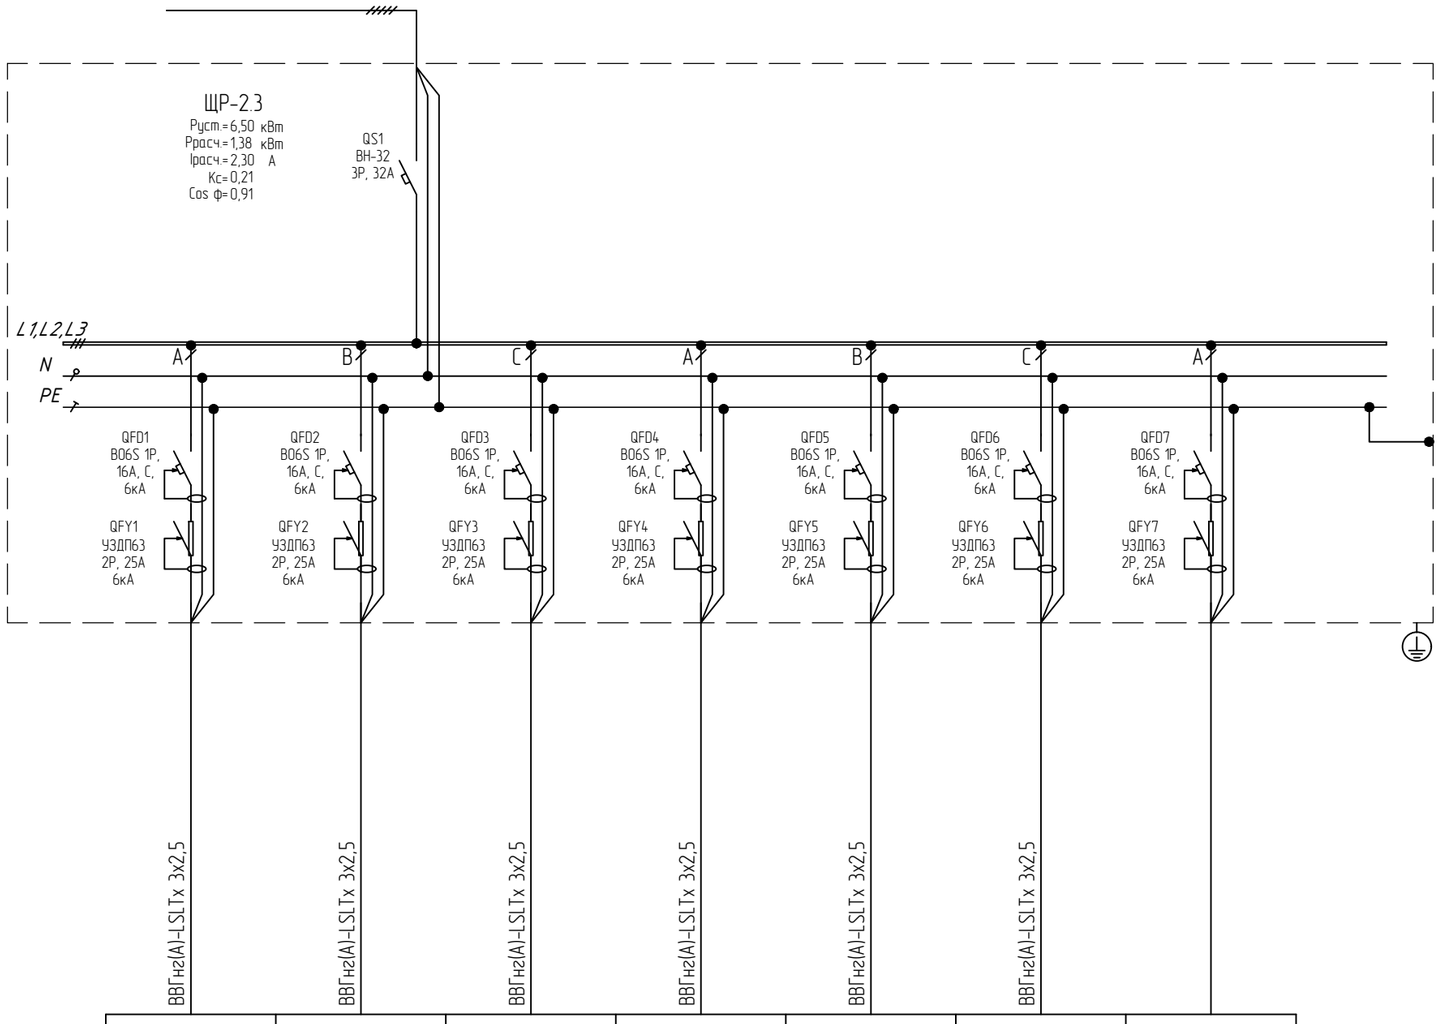

Питающая сеть, марка, сечение кабеля

Щит распределительный

Аппараты ввода: Тип, Iном. (А), Iу. (мА)

Аппараты отходящих линий: Тип, Iном. (А), Iу. (мА)

Марка и сечения кабелей

Длина участка сети

	ВВГнг(А)-LSLTx 3х2,5	ВВГнг(А)-LSLTx 3х2,5	ВВГнг(А)-LSLTx 3х2,5	ВВГнг(А)-LSLTx 3х2,5	ВВГнг(А)-LSLTx 3х2,5	ВВГнг(А)-LSLTx 3х2,5	
Электроприёмники: номер группы	P-2.3.1	P-2.3.2	P-2.3.3	P-2.3.4	P-2.3.5	P-2.3.6	
Руст. (кВт)	2,00	2,00	1,50	0,80	2,00	0,20	
Ip. (А)	9,15	9,15	6,86	3,66	9,15	0,92	
Наименование	Бытовые розетки, рукосушитель	Бытовые розетки, рукосушитель	Рукосушитель	Бытовые розетки АРМ - 1шт	Бытовые розетки спортивного зала, Электронное табло	Бытовые розетки	Резерв
Помещения	228, 229	224, 225	222	222, 221	220	320	

Согласовано

Взам. инв.N

Подпись и дата

Инв.N подл.

Изм.	Кол.уч.	Лист	N°док.	Подп.	Дата
Разраб.		Семенов			02.2025
Провер.		Пильгуй М.Н.			02.2025
Н. контр.		Пильгуй Н.М			02.2025
Нач. ОПИС №1		Белоусова Д.П.			02.2025

2024-00375-01-0-ИОС1

Капитальный ремонт здания Государственного бюджетного общеобразовательного учреждения города Москвы «Школа № 1574» по адресу: г. Москва, Старопименовский пер., д. №5

Система электроснабжения

Стадия	Лист	Листов
П	34	

Щит ЩР-2.3. Схема электрическая принципиальная

МОСЖИЛ НИИПРОЕКТ

Формат А3 х 1

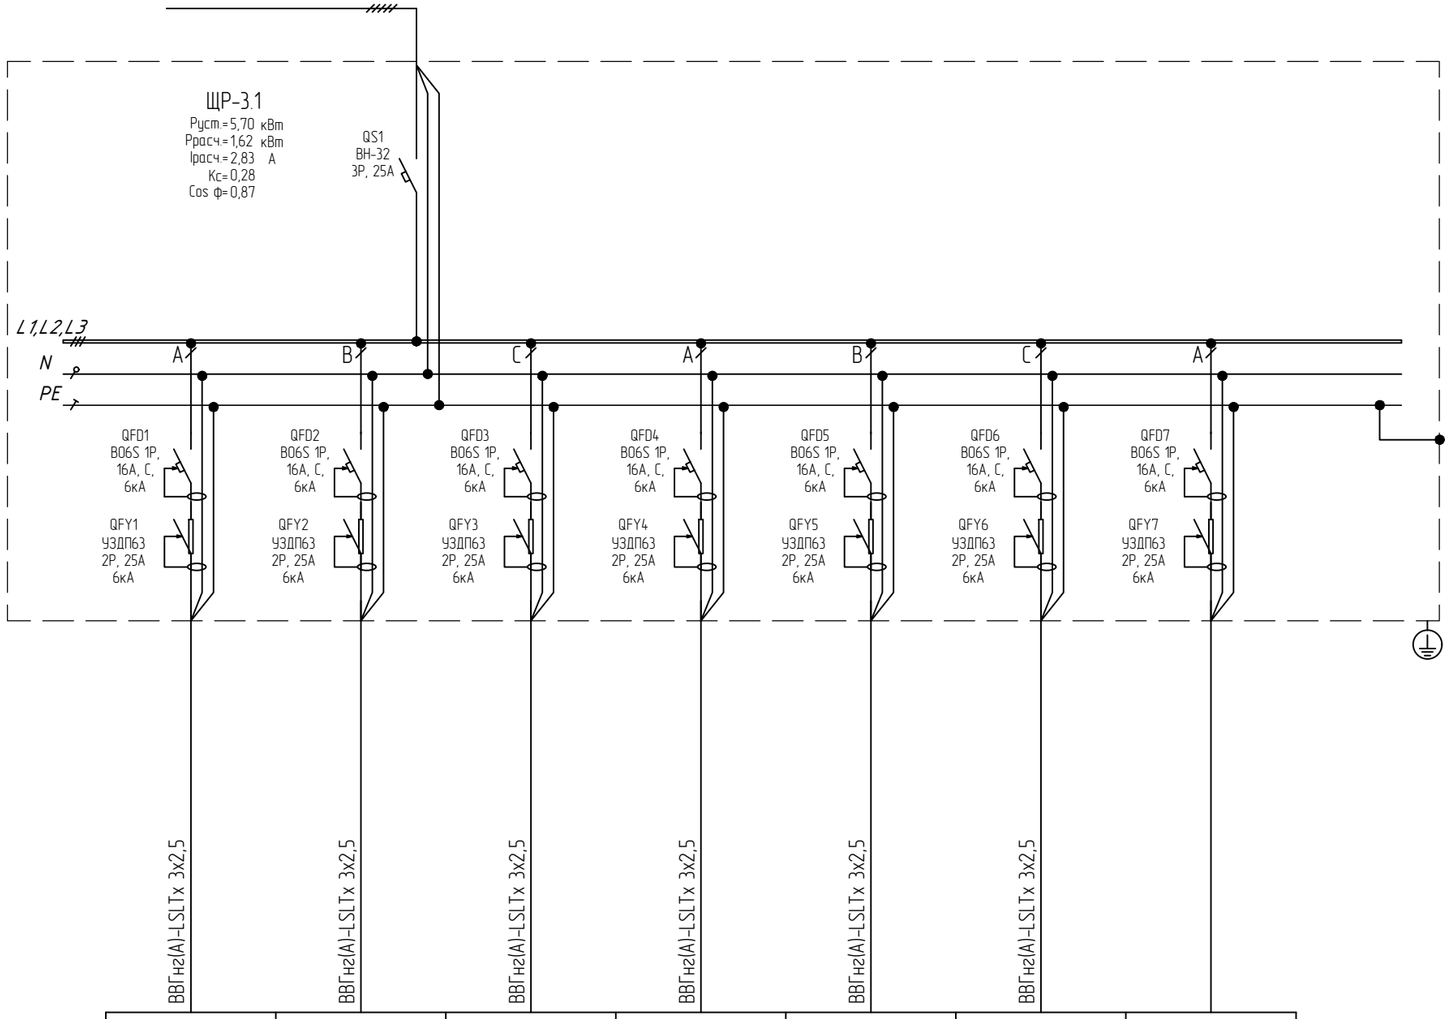

Щит распределительный		Питающая сеть, марка, сечение кабеля						
	Аппараты ввода	Тип Iном. (А) Iу. (мА)						
	Аппараты отходящих линий	Тип Iном. (А) Iу. (мА)						
	Марка и сечения кабелей		ВВГнг(А)-LSLTx 3х2,5	ВВГнг(А)-LSLTx 3х2,5	ВВГнг(А)-LSLTx 3х2,5	ВВГнг(А)-LSLTx 3х2,5	ВВГнг(А)-LSLTx 3х2,5	ВВГнг(А)-LSLTx 3х2,5	
	Длина участка сети								
Электроприёмники	номер группы		Р-3.1.1	Р-3.1.2	Р-3.1.3	Р-3.1.4	Р-3.1.5	Р-3.1.6	
	Руст. (кВт)		1,40	0,60	0,80	0,80	0,80	1,50	
	Ip. (А)		6,41	2,75	3,66	3,66	3,66	6,86	
	Наименование		Бытовые розетки, АРМ - 3шт	Бытовые розетки, АРМ - 1шт	Бытовые розетки, АРМ - 1шт	Бытовые розетки, АРМ - 1шт	Бытовые розетки	Рукосушитель	Резерв
	Помещения		312	313	309	308	306	314	

Согласовано

Взам. инв.N

Подпись и дата

Инв.N подл.

Изм.	Кол.уч.	Лист	N°док.	Подп.	Дата
Разраб.		Семенов			02.2025
Провер.		Пильгуй М.Н.			02.2025
Н. контр.		Пильгуй Н.М			02.2025
Нач. ОПИС N°1		Белоусова Д.П.			02.2025

2024-00375-01-0-ИОС1

Капитальный ремонт здания Государственного бюджетного общеобразовательного учреждения города Москвы «Школа № 1574» по адресу: г. Москва, Старопименовский пер., д. №5

Система электроснабжения

Стадия	Лист	Листов
П	35	

Щит ЩР-3.1. Схема электрическая принципиальная

МОСЖИЛ НИИПРОЕКТ

Формат А3 х 1

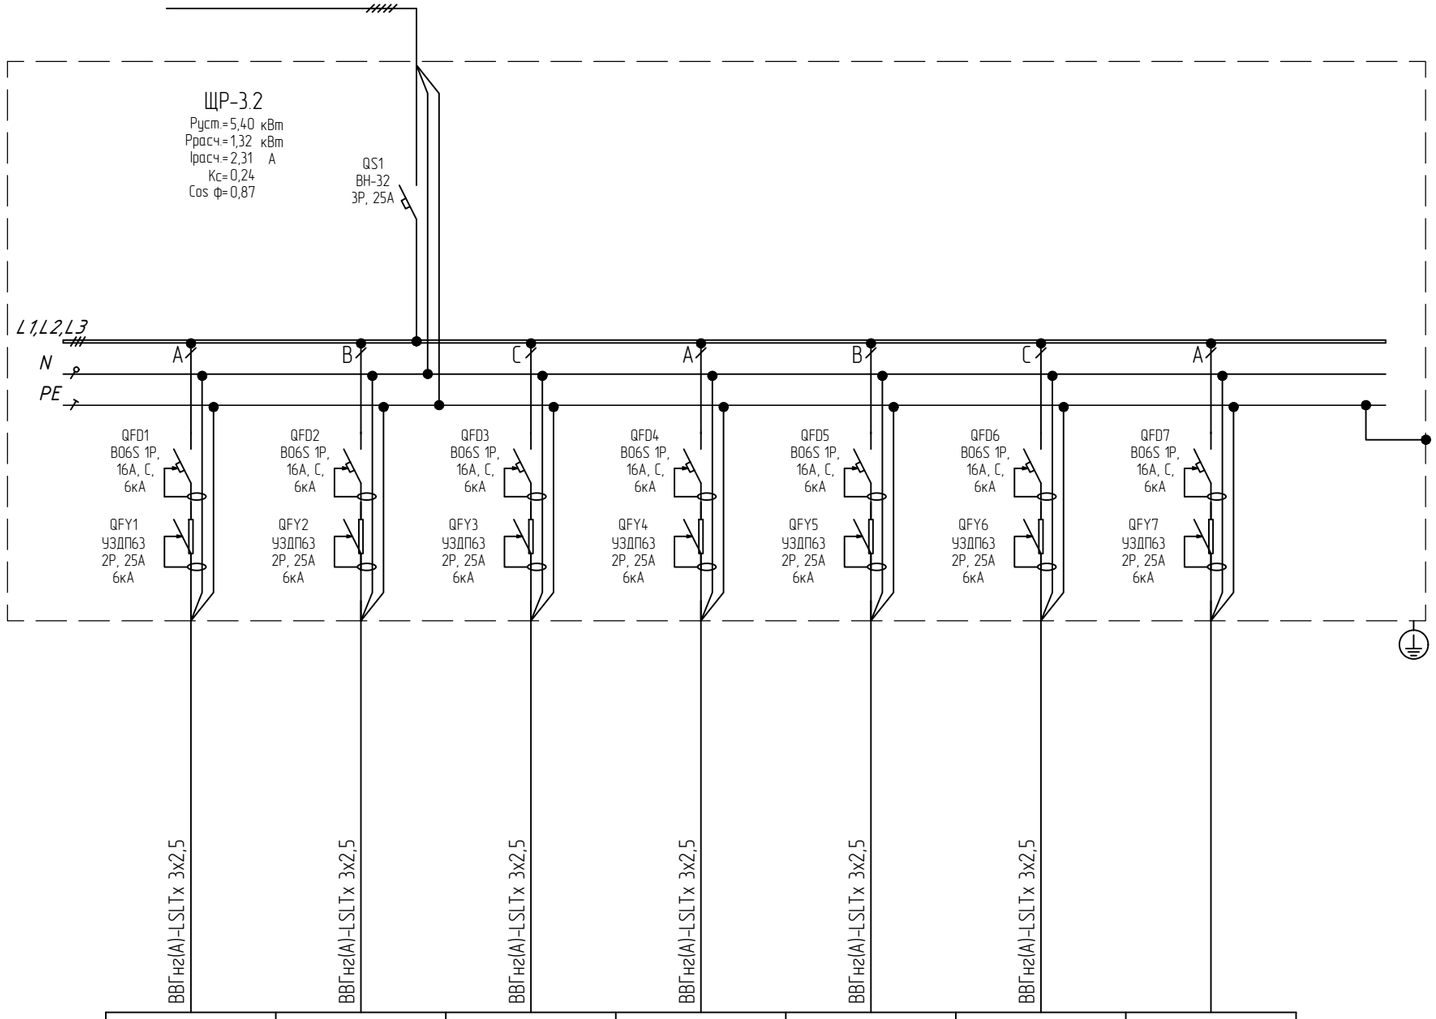

Питающая сеть, марка, сечение кабеля

Щит распределительный

Аппараты ввода: Тип, Iном. (А), Iу. (мА)

Аппараты отходящих линий: Тип, Iном. (А), Iу. (мА)

Марка и сечения кабелей

Длина участка сети

	ВВГнг(А)-LSLTx 3х2,5	ВВГнг(А)-LSLTx 3х2,5	ВВГнг(А)-LSLTx 3х2,5	ВВГнг(А)-LSLTx 3х2,5	ВВГнг(А)-LSLTx 3х2,5	ВВГнг(А)-LSLTx 3х2,5	
Электроприёмники: номер группы	P-3.2.1	P-3.2.2	P-3.2.3	P-3.2.4	P-3.2.5	P-3.2.6	
Руст. (кВт)	0,80	0,80	0,80	1,50	1,50	0,80	
Ip. (А)	3,66	3,66	3,66	6,86	6,86	3,66	
Наименование	Бытовые розетки, АРМ - 1шт	Бытовые розетки, АРМ - 1шт	Бытовые розетки, АРМ - 1шт	Рукосушитель	Рукосушитель	Бытовые розетки, АРМ - 1шт	Резерв
Помещения	302	303	305	318	319	317	

Согласовано

Взам. инв.N

Подпись и дата

Инв.N подл.

Изм.	Кол.уч.	Лист	N°док.	Подп.	Дата
Разраб.		Семенов			02.2025
Провер.		Пильгуй М.Н.			02.2025
Н. контр.		Пильгуй Н.М			02.2025
Нач. ОПИС №1		Белоусова Д.П.			02.2025

2024-00375-01-0-ИОС1

Капитальный ремонт здания Государственного бюджетного общеобразовательного учреждения города Москвы «Школа № 1574» по адресу: г. Москва, Старопименовский пер., д. №5

Система электроснабжения

Стадия	Лист	Листов
П	36	

Щит ЩР-3.2. Схема электрическая принципиальная

МОСЖИЛ НИИПРОЕКТ

Формат А3 х 1

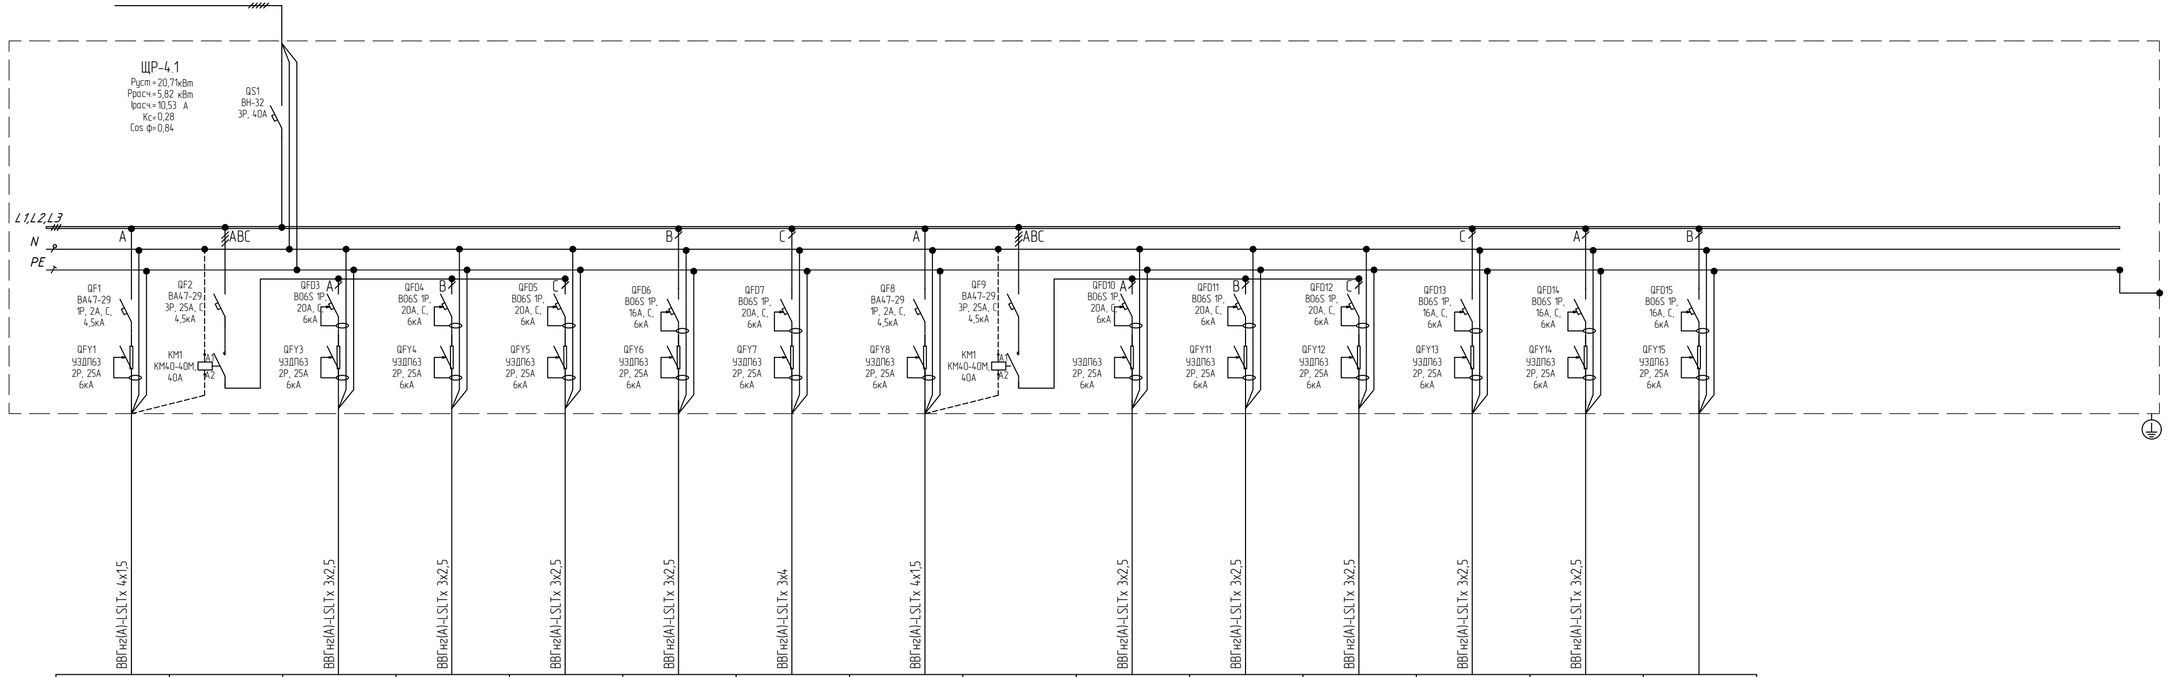

Питающая сеть, марка, сечение кабеля

Щит распределительный

Аппараты ввода: Тип, Iном. (А), Iу. (мА)

Аппараты отходящих линий: Тип, Iном. (А), Iу. (мА)

Марка и сечения кабелей

Длина участка сети

Электроприёмники	P-4.1.1		P-4.1.2	P-4.1.3	P-4.1.4	P-4.1.5	P-4.1.6	P-4.1.7		P-4.1.8	P-4.1.9	P-4.1.10	P-4.1.11	P-4.1.12	
номер группы															
Руст. (кВт)	0,01		3,00	3,00	3,00	1,10	1,10	0,01		1,20	2,40	2,40	1,60	1,50	
Ip. (А)	0,02		13,73	13,73	13,73	5,03	5,03	0,02		5,49	10,98	10,98	7,32	6,86	
Наименование	Управление питанием со стола препод.		Лючки в полу учеников	Лючки в полу учеников	Лючки в полу учеников	Бытовые розетки, АРМ - 1шт	Бытовые розетки, АРМ - 1шт	Управление питанием со стола препод.		Лючки в полу учеников	Лючки в полу учеников	Лючки в полу учеников	Бытовые розетки, АРМ - 1шт	Рукосушитель	Резерв
Помещения	410		410	410	410	409, 410	407	407		407	407	407	405, 406	411	

Согласовано

Взам. инв.N

Подпись и дата

Инв.N подл.

Изм.	Кол.уч.	Лист	N°док.	Подп.	Дата
Разраб.		Семенов			02.2025
Провер.		Пильгуй М.Н.			02.2025
Н. контр.		Пильгуй Н.М.			02.2025
Нач. ОПИС №1		Белоусова Д.П.			02.2025

2024-00375-01-0-ИОС1

Капитальный ремонт здания Государственного бюджетного общеобразовательного учреждения города Москвы «Школа № 1574» по адресу: г. Москва, Старопименовский пер., д. №5

Система электроснабжения

Стадия	Лист	Листов
П	37	

Щит ЩР-4.1. Схема электрическая принципиальная

МОСЖИЛ НИИПРОЕКТ

Формат А4 x 3

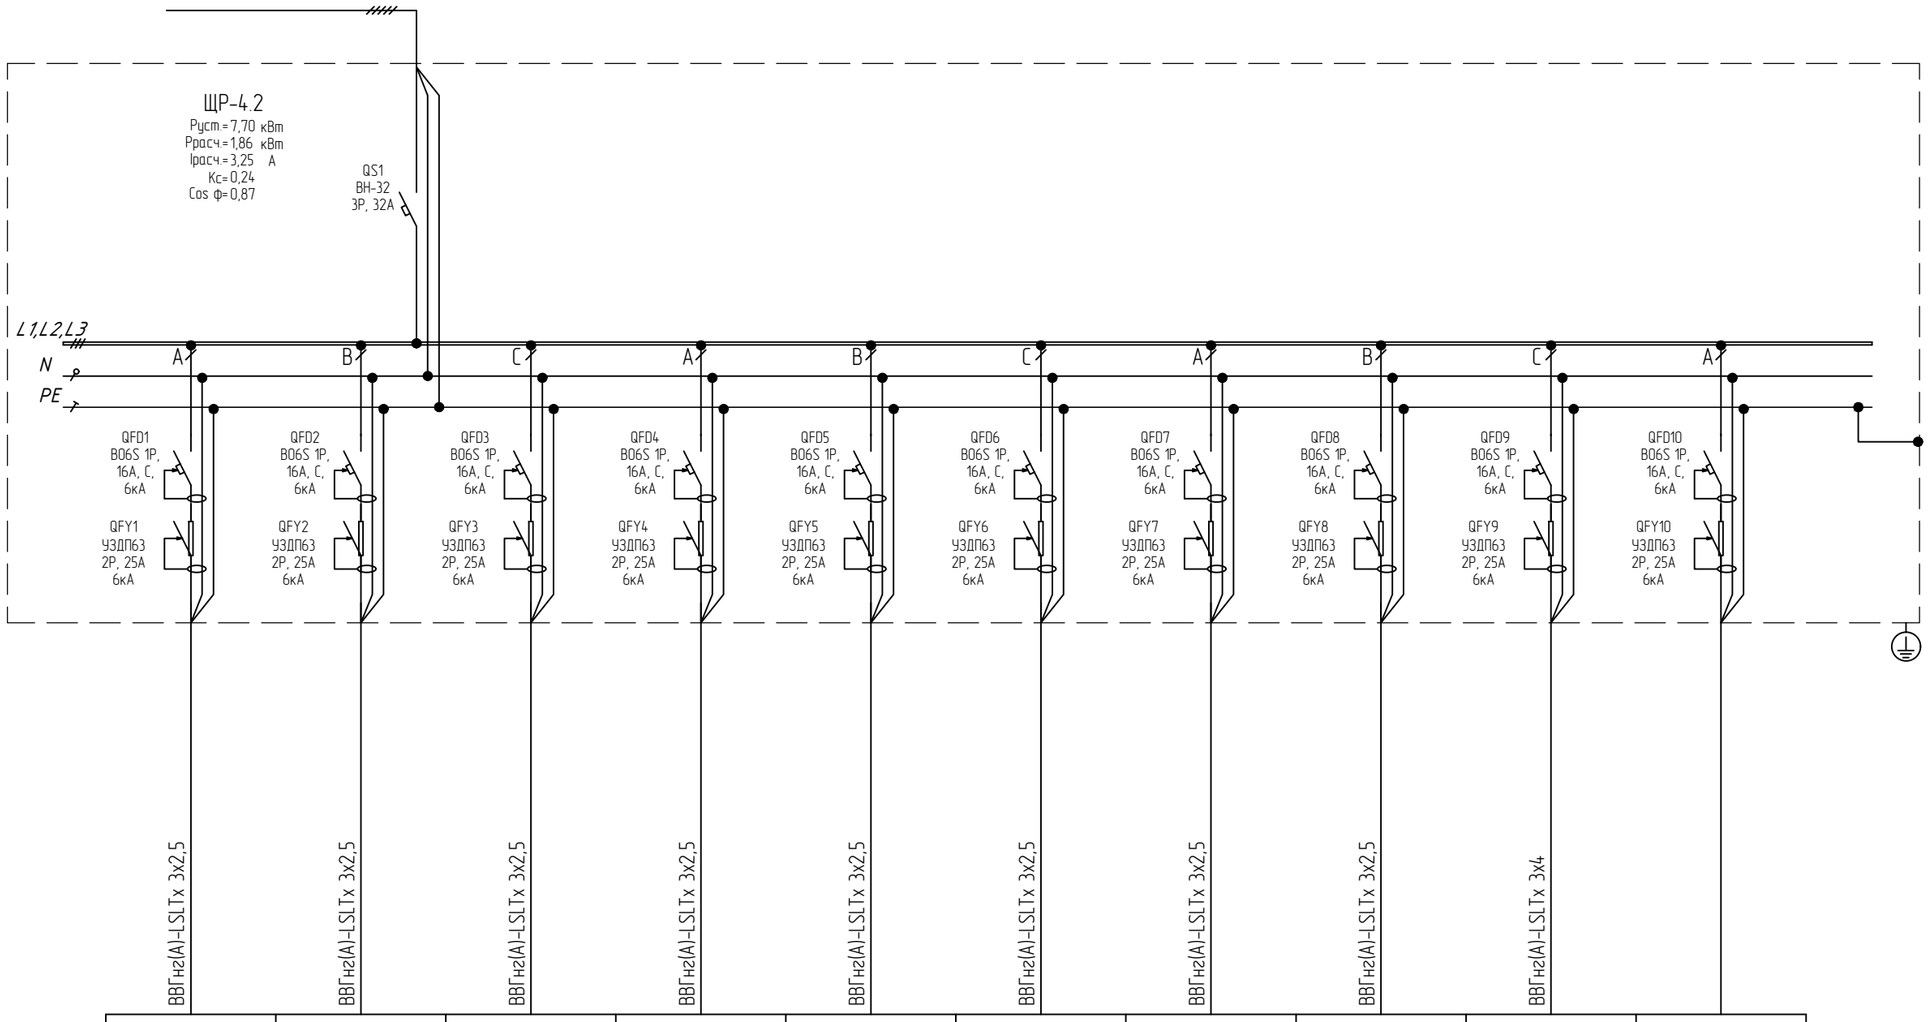

Щит распределительный		
	Аппараты ввода	Тип Iном. (А) Iу. (мА)
	Аппараты отходящих линий	Тип Iном. (А) Iу. (мА)
Марка и сечения кабелей		ВВГнг(А)-LSLTx 3х2,5	ВВГнг(А)-LSLTx 3х2,5	ВВГнг(А)-LSLTx 3х2,5	ВВГнг(А)-LSLTx 3х2,5	ВВГнг(А)-LSLTx 3х2,5	ВВГнг(А)-LSLTx 3х2,5	ВВГнг(А)-LSLTx 3х2,5	ВВГнг(А)-LSLTx 3х2,5	ВВГнг(А)-LSLTx 3х4	
Длина участка сети											
Электроприёмники	номер группы	Р-4.2.1	Р-4.2.2	Р-4.2.3	Р-4.2.4	Р-4.2.5	Р-4.2.6	Р-4.2.7	Р-4.2.8	Р-4.2.9	
	Руст. (кВт)	0,80	0,80	0,80	0,80	1,50	1,50	1,50	1,80	4,00	
	Ip. (А)	3,66	3,66	3,66	3,66	6,86	6,86	6,86	8,24	18,31	
	Наименование	Бытовые розетки, АРМ - 1шт	Бытовые розетки, АРМ - 1шт	Бытовые розетки, АРМ - 1шт	Бытовые розетки, АРМ - 1шт	Рукосушитель	Рукосушитель	Рукосушитель	Бытовые розетки, АРМ - 4шт	Бытовые розетки (чайник, холодильник, микроволновая печь)	Резерв
	Помещения	402	403	404	414	416	416	417	413	413	

Согласовано

Взам. инв.N

Подпись и дата

Инв.N подл.

Изм.	Кол.уч.	Лист	№док.	Подп.	Дата
Разраб.		Семенов			02.2025
Провер.		Пильгуй М.Н.			02.2025
Н. контр.		Пильгуй Н.М			02.2025
Нач. ОПИС №1		Белоусова Д.П.			02.2025

2024-00375-01-0-ИОС1

Капитальный ремонт здания Государственного бюджетного общеобразовательного учреждения города Москвы «Школа № 1574» по адресу: г. Москва, Старопименовский пер., д. №5

Система электроснабжения

Стадия	Лист	Листов
П	38	

Щит ЩР-4.2. Схема электрическая принципиальная

МОСЖИЛ НИИПРОЕКТ

Формат А3 х 1

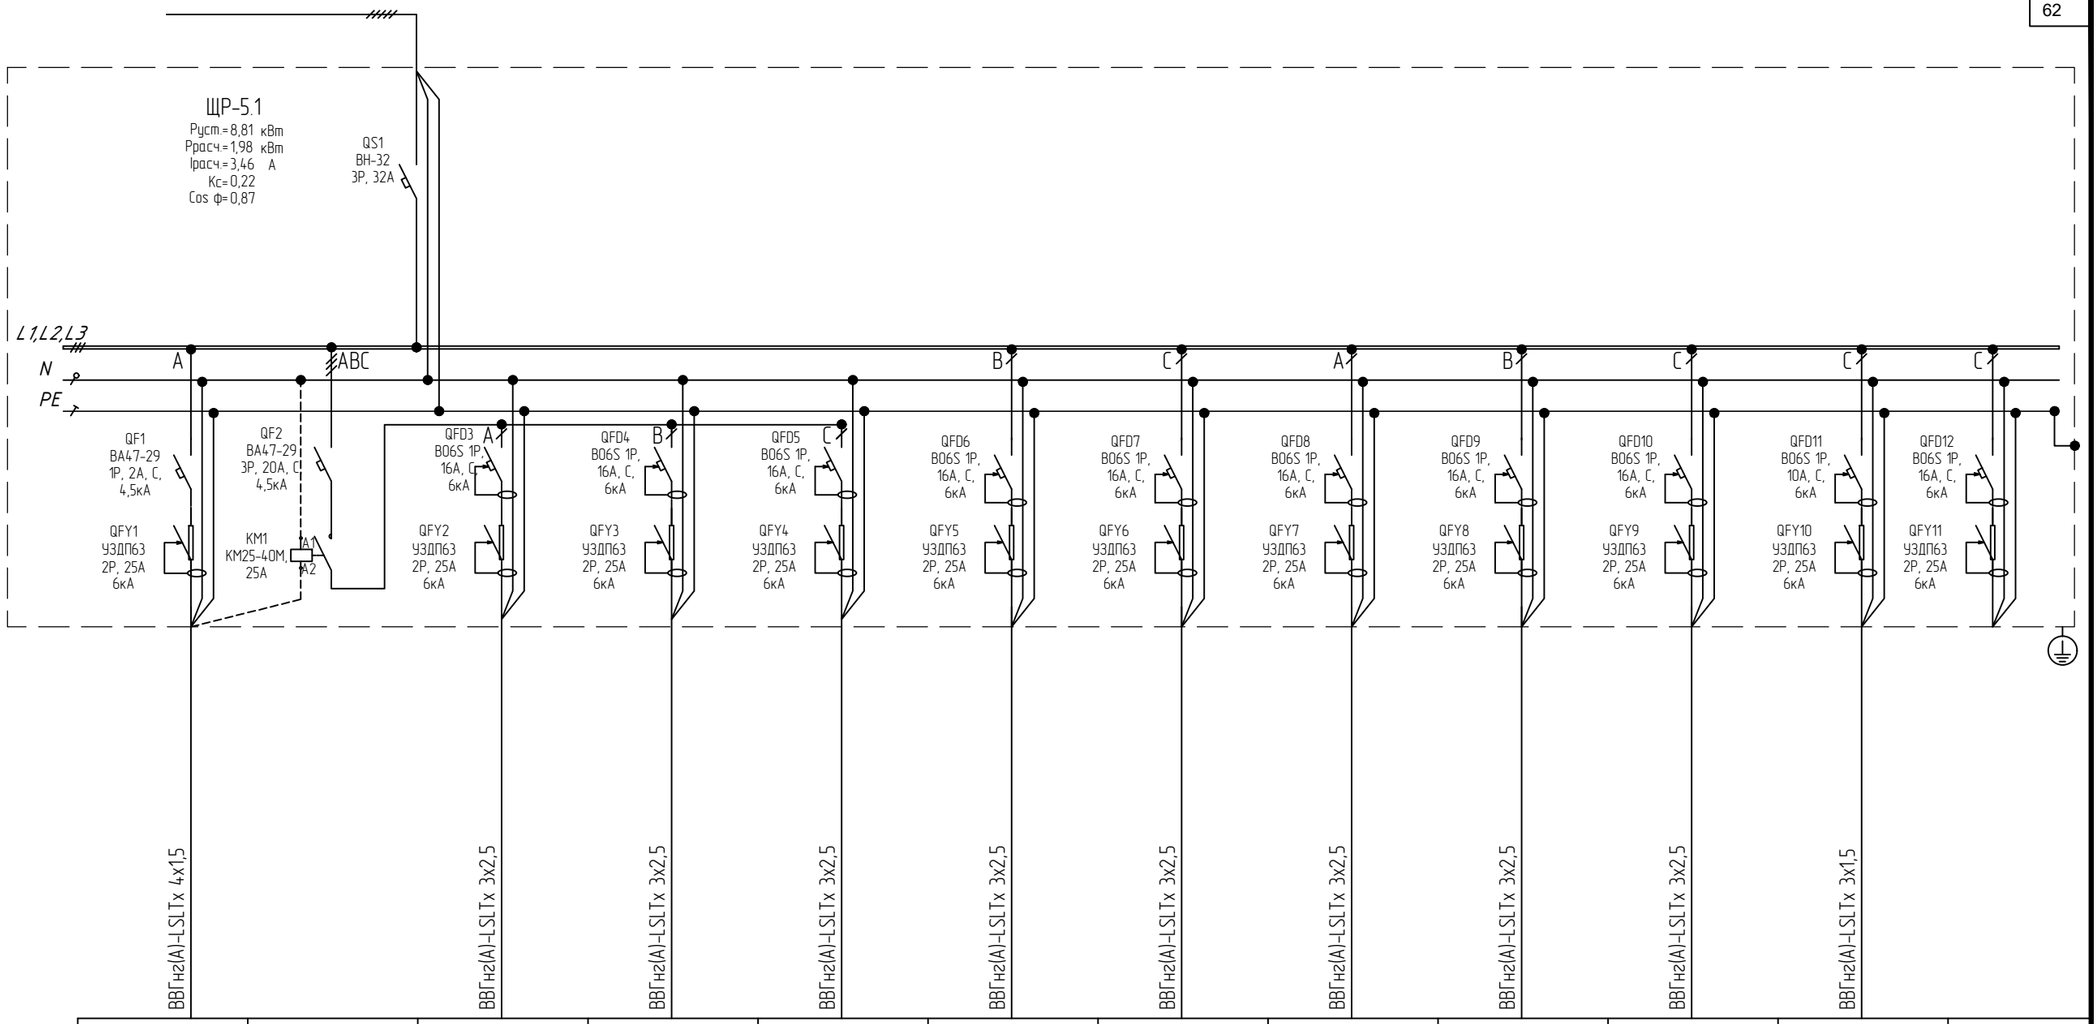

Щит распределительный	Аппараты ввода	Тип Iном. (А) Iу. (мА)		ВВГнг(А)-LSLTx 4х1,5		ВВГнг(А)-LSLTx 3х2,5	ВВГнг(А)-LSLTx 3х2,5	ВВГнг(А)-LSLTx 3х2,5	ВВГнг(А)-LSLTx 3х2,5	ВВГнг(А)-LSLTx 3х2,5	ВВГнг(А)-LSLTx 3х2,5	ВВГнг(А)-LSLTx 3х2,5	ВВГнг(А)-LSLTx 3х2,5	ВВГнг(А)-LSLTx 3х1,5	
	Аппараты отходящих линий	Тип Iном. (А) Iу. (мА)													
	Марка и сечения кабелей														
	Длина участка сети														
Электроприёмники	номер группы			P-5.1.1		P-5.1.2	P-5.1.3	P-5.1.4	P-5.1.5	P-5.1.6	P-5.1.7	P-5.1.8	P-5.1.9	P-5.1.10	
	Руст. (кВт)			0,01		1,50	1,50	1,50	1,10	0,80	0,80	1,50	0,80	0,03	
	Ip. (А)			0,02		6,86	6,86	6,86	5,03	3,66	3,66	6,86	3,66	0,12	
	Наименование			Кнопка с подсветкой для стола преподавателя		Лючки в полу учеников	Лючки в полу учеников	Лючки в полу учеников	Бытовые розетки АРМ - 1шт	Бытовые розетки АРМ - 1шт	Бытовые розетки АРМ - 1шт	Рукосушитель	Бытовые розетки, АРМ - 1шт	Станция СКТ	
	Помещения			511		511	511	511	511, 510	508	507	513	514	505	

Согласовано

Взам. инв.N

Подпись и дата

Инв.N подл.

Изм.	Кол.уч.	Лист	N°док.	Подп.	Дата
Разраб.		Семенов			02.2025
Провер.		Пильгуй М.Н.			02.2025
Н. контр.		Пильгуй Н.М			02.2025
Нач. ОПИС №1		Белоусова Д.П.			02.2025

2024-00375-01-0-ИОС1

Капитальный ремонт здания Государственного бюджетного общеобразовательного учреждения города Москвы «Школа № 1574» по адресу: г. Москва, Старопименовский пер., д. №5

Система электроснабжения

Стадия	Лист	Листов
П	39	

Щит ЩР-5.1. Схема электрическая принципиальная

МОСЖИЛ НИИПРОЕКТ

Формат А3 х 1

Питающая сеть, марка, сечение кабеля

Щит распределительный

Аппараты ввода

Тип Iном. (А) Iу. (мА)

Аппараты отходящих линий

Тип Iном. (А) Iу. (мА)

Марка и сечения кабелей

Длина участка сети

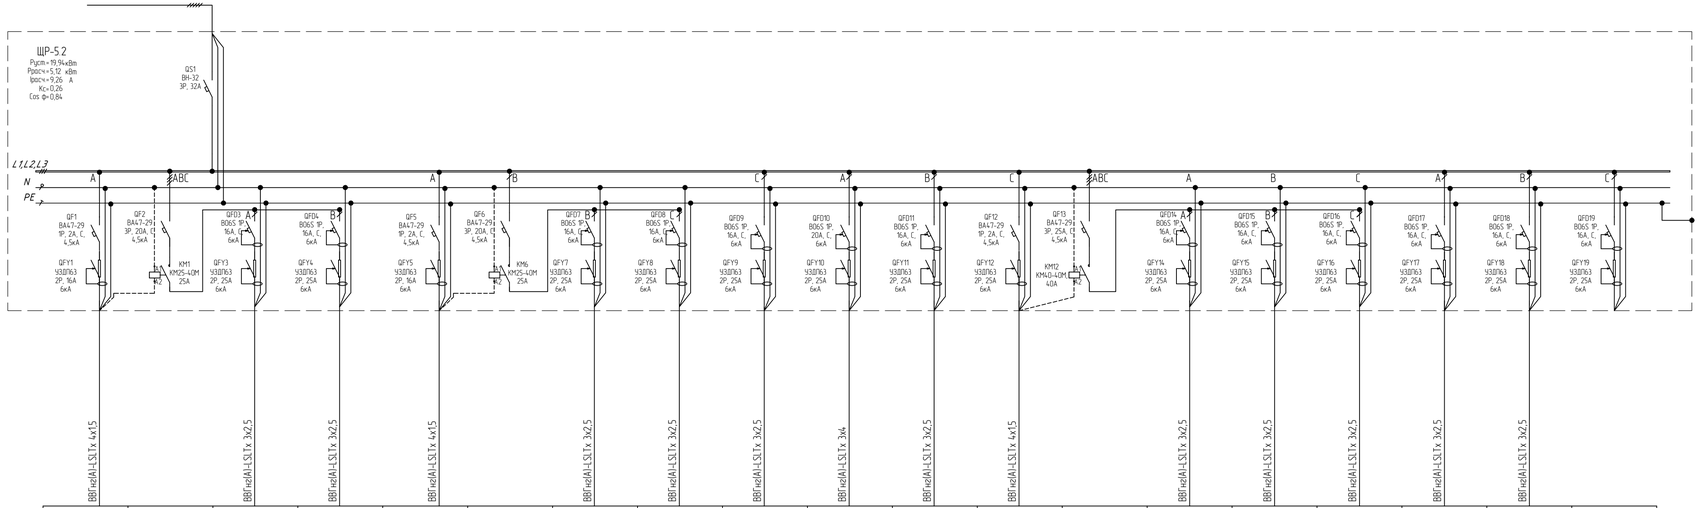

Электроприемники																		
номер группы	Р-5.2.1		Р-5.2.2	Р-5.2.3	Р-5.2.4		Р-5.2.5	Р-5.2.6	Р-5.2.7	Р-5.2.8	Р-5.2.9	Р-5.2.10		Р-5.2.11	Р-5.2.12	Р-5.2.13	Р-5.2.14	Р-5.2.15	
Руст. (кВт)	0,01		1,60	1,60	0,01		1,60	1,60	0,90	3,00	1,60	0,01		1,50	1,50	1,50	3,00	1,50	
Ip. (А)	0,02		7,32	7,32	0,02		7,32	7,32	4,12	13,73	7,32	0,02		6,86	6,86	6,86	13,73	6,86	
Наименование	Кнопка с подсветкой для стола преподавателя		АРМ учеников, 4шт	АРМ учеников, 4шт	Кнопка с подсветкой для стола преподавателя		АРМ учеников, 6шт	АРМ учеников, 6шт	Бытовые розетки, АРМ - 1шт	Бытовые розетки, Аквадистиллятор	Бытовые розетки, АРМ - 2шт	Кнопка с подсветкой для стола преподавателя		Лючки в полу учеников	Лючки в полу учеников	Лючки в полу учеников	Рукосушители, 2 шт	Рукосушитель	Резерв
Помещения	506		506	506	506		506	506	506	504	502, 503	506		503	503	503	516	517	

Согласовано

Взам. инв.N

Подпись и дата

Инв.N подл.

Изм.	Кол.уч.	Лист	№док.	Подп.	Дата
Разраб.		Семенов			02.2025
Провер.		Пильгуй М.Н.			02.2025
Н. контр.		Пильгуй Н.М.			02.2025
Нач. ОПИС №1		Белоусова Д.П.			02.2025

2024-00375-01-0-ИОС1

Капитальный ремонт здания Государственного бюджетного общеобразовательного учреждения города Москвы «Школа № 1574» по адресу: г. Москва, Старопименовский пер., д. №5

Система электроснабжения

Стадия	Лист	Листов
П	40	

Щит ЩР-5.2. Схема электрическая принципиальная

МОСЖИЛ НИИПРОЕКТ

Формат А4 x 4

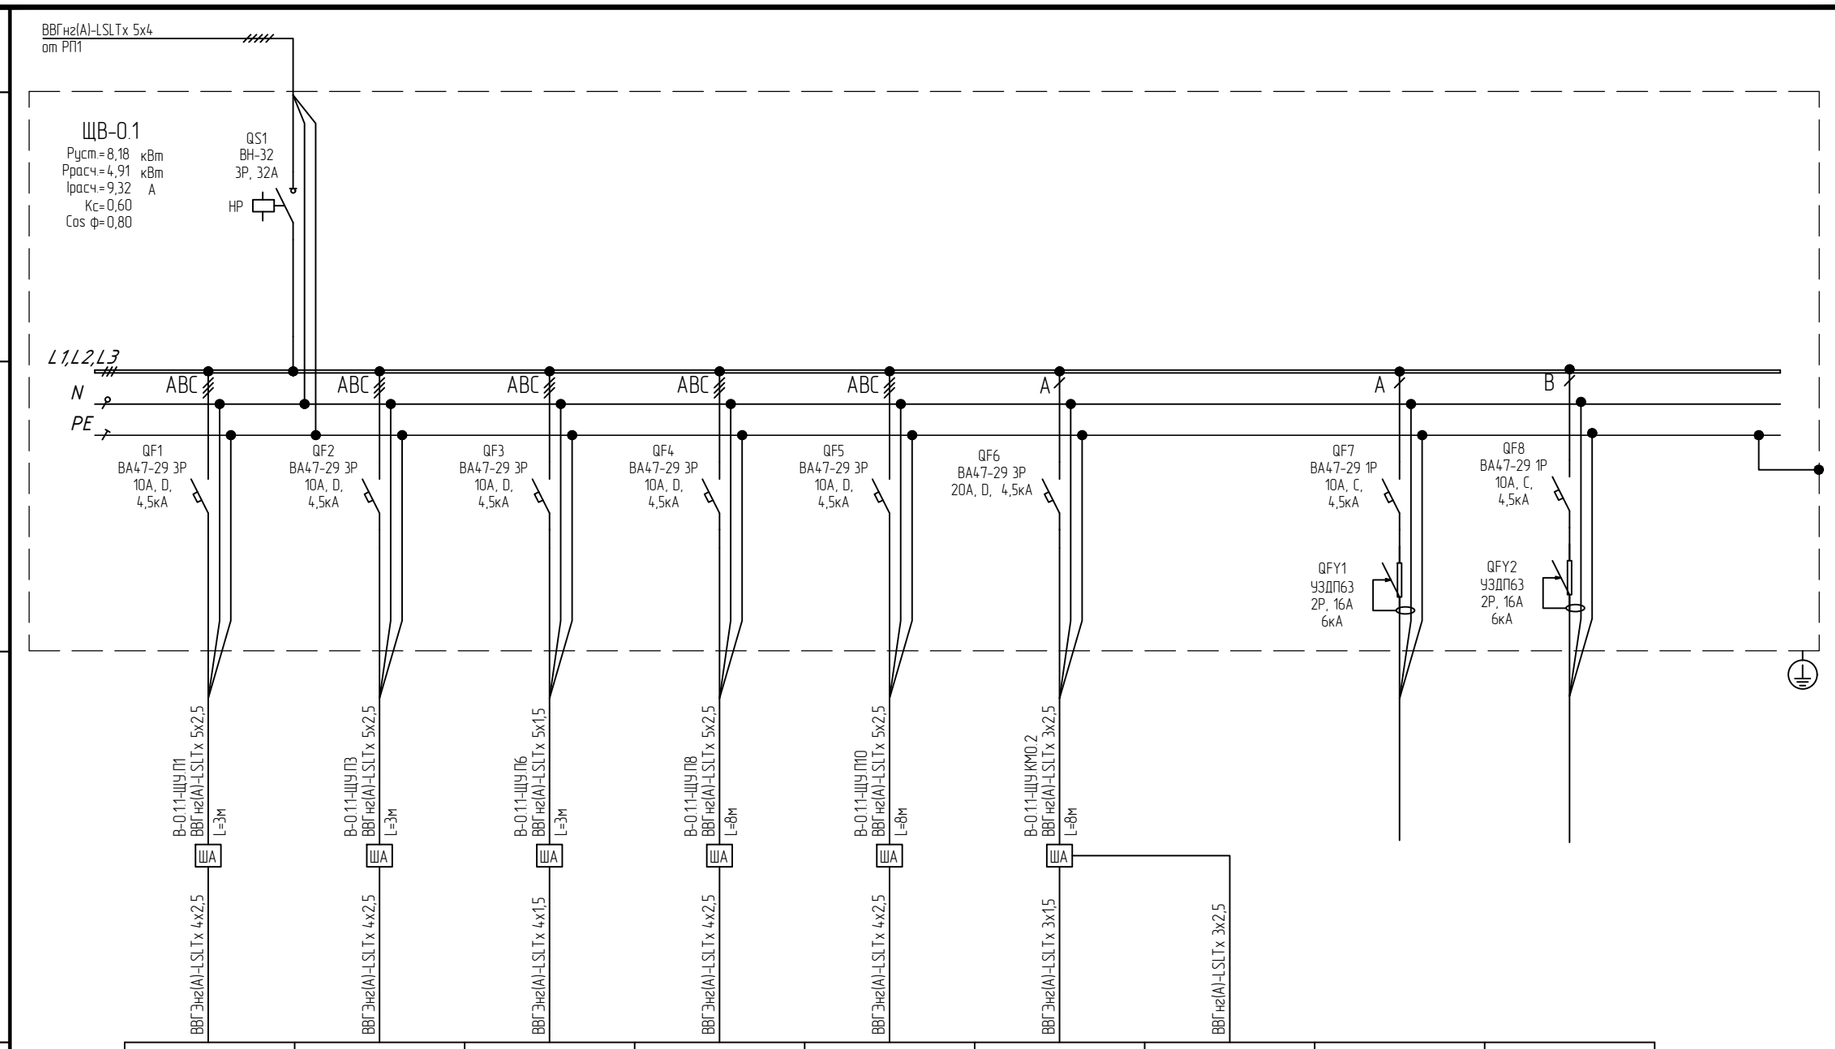

Щит распределительный

Аппараты ввода: Тип, Iном. (А), Iу. (мА)

Аппараты отходящих линий: Тип, Iном. (А), Iу. (мА)

Марка и сечение кабелей

Длина участка сети

Электроприёмники									
номер группы	В-0.1.1	В-0.1.2	В-0.1.3	В-0.1.4	В-0.1.5	В-0.1.6	В-0.1.6н		
Руст. (кВт)	1,10	0,55	0,37	0,80	2,20	0,16	3,00		
Iр. (А)	2,09	1,04	0,70	1,52	4,18	0,87	13,31		
Наименование	П1	П3	П6	П8	П10	КМО.2	КМО.2 (электронагревательный)	Резерв	Резерв
Помещения	004	004	004	004	004	004	004		

Согласовано

Взам. инв.N

Подпись и дата

Инв.N подл.

Изм.	Кол.уч.	Лист	N°док.	Подп.	Дата
Разраб.		Семенов			02.2025
Провер.		Пильгуй М.Н.			02.2025
Н. контр.		Пильгуй Н.М			02.2025
Нач. ОПИС №1		Белоусова Д.П			02.2025

2024-00375-01-0-ИОС1

Капитальный ремонт здания Государственного бюджетного общеобразовательного учреждения города Москвы «Школа № 1574» по адресу: г. Москва, Старопименовский пер., д. №5

Система электроснабжения

Стадия	Лист	Листов
П	41	

Щит ЩВ-0.1. Схема электрическая принципиальная

МОСЖИЛ НИИПРОЕКТ

Формат А3 х 1

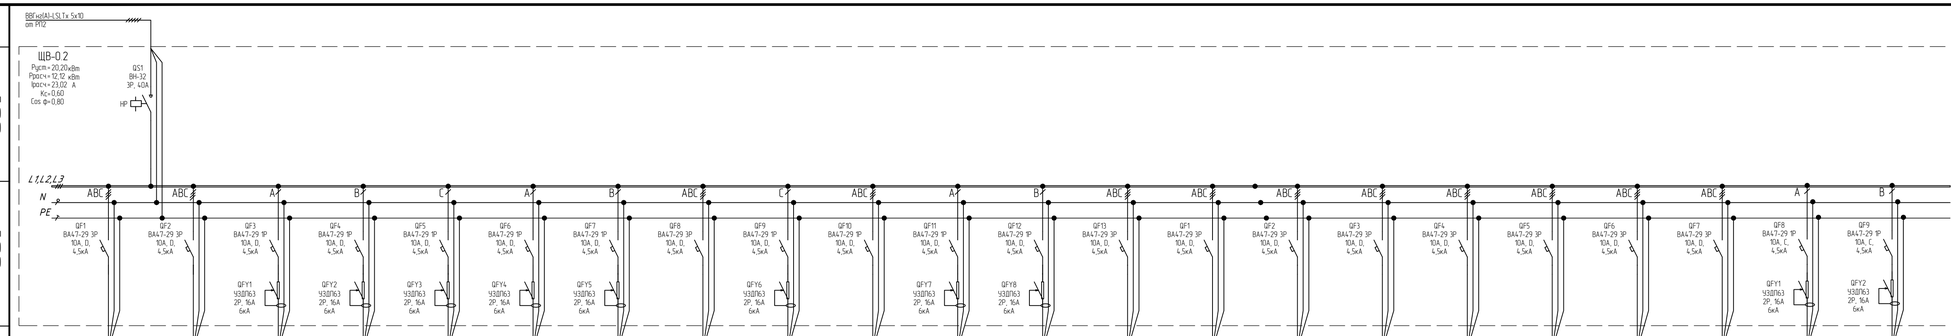

Электроприемники																							
номер группы	В-0.2.1	В-0.2.2	В-0.2.3	В-0.2.4	В-0.2.5	В-0.2.6	В-0.2.7	В-0.2.8	В-0.2.9	В-0.2.10	В-0.2.11	В-0.2.12	В-0.2.13	В-0.2.14	В-0.2.15	В-0.2.16	В-0.2.17	В-0.2.18	В-0.2.19	В-0.2.20		
Руст. (кВт)	2,20	0,40	0,10	0,10	0,10	0,10	0,10	0,90	0,10	0,10	0,10	2,20	0,75	2,20	2,20	4,00	1,10	2,20	1,10	0,75		
Ip. (А)	4,18	0,76	0,54	0,54	0,54	0,54	0,54	1,71	0,54	0,54	0,54	4,18	1,42	4,18	4,18	7,60	2,09	4,18	2,09	1,42		
Наименование	В4	В5	В11	В12	В14	В15	В19	В20	В21	В24	В25	М0-3	М0-4	П2	П4	П5	П9	П11	П13	КМ0.1	Резерв	Резерв
Помещения	Кровля 3 этажа	Кровля 3 этажа	Кровля 3 этажа	Кровля 3 этажа	Кровля 3 этажа	Кровля 2 этажа	Кровля 3 этажа	Кровля 3 этажа	Кровля 2 этажа	Кровля 2 этажа	Кровля 2 этажа	Кровля 2 этажа	Кровля 3 этажа	О24.А	О21	О21	О21	О24.А	О24.А	О24.А		

Согласовано

Взам. инв.N

Подпись и дата

Инв.N подл.

							2024-00375-01-0-ИОС1
							Капитальный ремонт здания Государственного бюджетного общеобразовательного учреждения города Москвы «Школа № 1574» по адресу: г. Москва, Старопименовский пер., д. №5
Изм.	Кол.уч.	Лист	№док.	Подп.	Дата		
Разраб.		Семенов			02.2025	Система электроснабжения	Стадия: П; Лист: 42; Листов:
Провер.		Пильгуй М.Н.			02.2025		
Н. контр.		Пильгуй Н.М.			02.2025	Щит ЩВ-0.2. Схема электрическая принципиальная	МОСЖИЛ НИИПРОЕКТ
Нач. ОПИС №1		Белоусова Д.П.			02.2025		

Формат А4 х 4

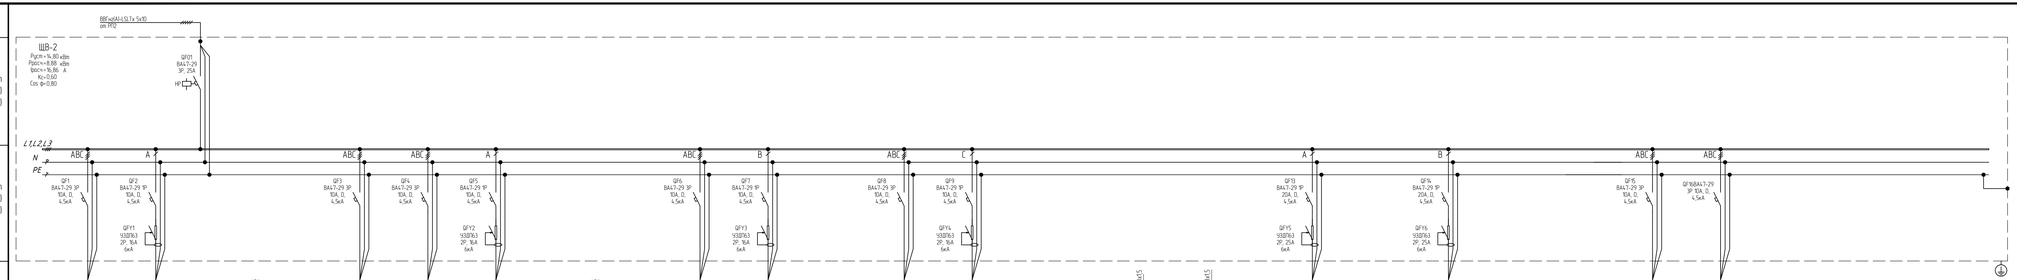

Питающая сеть, марка, сечение кабеля																										
Щит распределительный	Аппараты ввода	Тип Iном. (А) Iу. (мА)																								
	Аппараты отходящих линий	Тип Iном. (А) Iу. (мА)																								
Марка и сечение кабелей		Длина участка сети																								
Электроприемники	номер группы		В-2.1	В-2.2	В-2.3	В-2.4	В-2.5	В-2.6	В-2.7	В-2.8	В-2.9	В-2.10	В-2.11	В-2.12	В-2.13	В-2.14	В-2.15	В-2.16	В-2.17	В-2.18	В-2.19	В-2.19н	В-2.20	В-2.20н		В-2.21	В-2.22	
	Руст. (кВт)		1,10	0,10	0,10	0,10	0,40	0,40	0,10	0,30	0,16	1,70	0,16	0,16	0,40	0,30	0,23	0,10	0,10	0,10	0,16	3,00	0,16	3,00		2,20	0,37	14,90
	Ip. (А)		2,09	0,54	0,54	0,54	0,76	0,76	0,54	1,63	0,87	3,23	0,87	0,87	0,76	1,63	1,25	0,54	0,54	0,54	0,87	13,18	0,87	13,18		4,18	0,70	
	Наименование		В2	В17	В22	В7	В9	М0.1	М0.5	М0.6	В16	В1	М0.2	В23	В8	В3	В6	В10	В13	В18	П7	Электронагреватель (П7)	КМ0.3	Электронагреватель (КМ0.3)	Резерв	П12	КМ0.4	
	Помещения		6 эпох	6 эпох	6 эпох	6 эпох	6 эпох	6 эпох	6 эпох	6 эпох	6 эпох	6 эпох	6 эпох	6 эпох	6 эпох	6 эпох	6 эпох	6 эпох	6 эпох	6 эпох	6 эпох	6 эпох	6 эпох	6 эпох		6 эпох	6 эпох	

Инв.№ подл. | Подпись и дата | Взам. инв.№ | Изм. | Кол.уч. | Лист | №док. | Подп. | Дата

						2024-00375-01-0-ИОС1
						Капитальный ремонт здания Государственного бюджетного общеобразовательного учреждения города Москвы «Школа № 1574» по адресу: г. Москва, Старопименовский пер., д. №5
Разраб.	Семенов			02.2025		Система электроснабжения
Провер.	Пильщик М.Н.			02.2025		
Н. контр.	Пильщик М.М.			02.2025		Щит ЩВ-2. Схема электрическая принципиальная
Нач. ОПИС №1	Белошапка Д.И.			02.2025		

Стадия	Лист	Листов
П	43	

МОСЖИЛ НИИПРОЕКТ

Формат А4 х 5

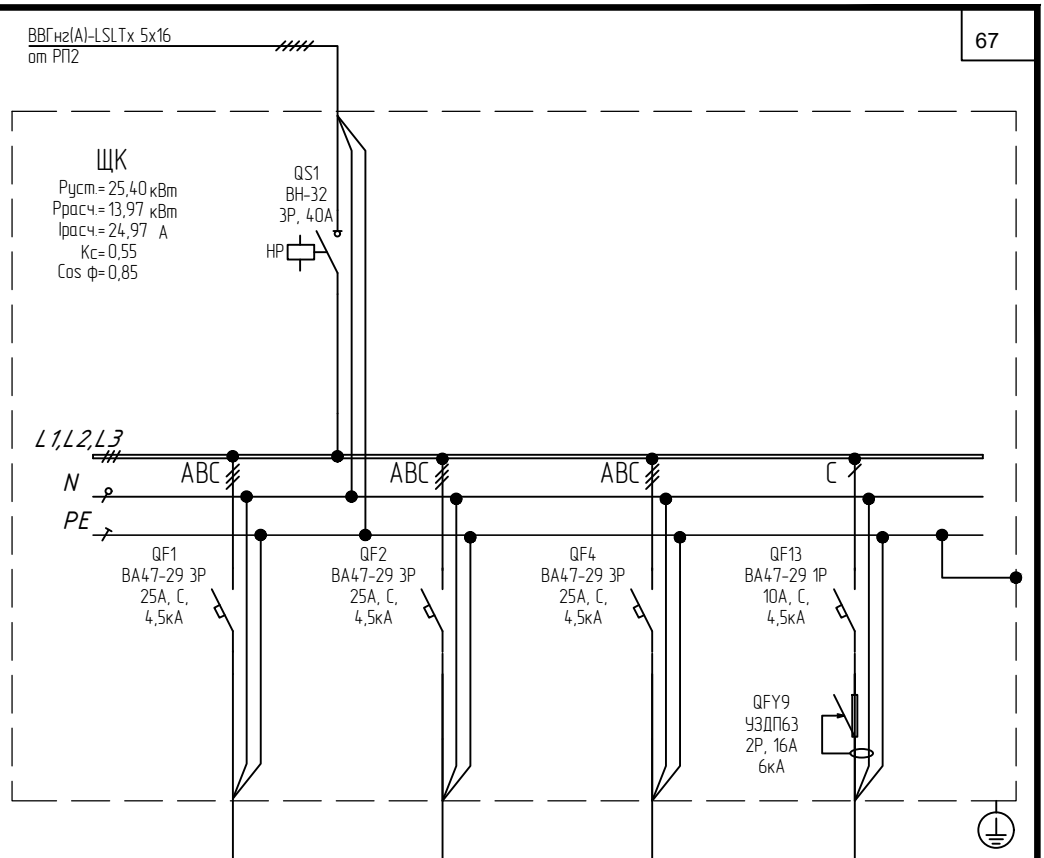

Щит распределительный	Аппараты ввода	Тип Iном. (А) Iу. (мА)
	Аппараты отходящих линий	Тип Iном. (А) Iу. (мА)
Марка и сечения кабелей		ВВГнг(А)-LSLTx 5х6
Длина участка сети		L= 12м
		ВВГнг(А)-LSLTx 5х6
		L= 12м
		ВВГнг(А)-LSLTx 5х6
		L= 13м

Электроприёмники	К-гр.1	К-гр.2	К-гр.3	
номер группы				
Руст. (кВт)	8,30	8,80	8,30	
Iр. (А)	14,84	15,73	14,84	
Наименование	К1	К2	К4	Резерв
Помещения	Кровля	Кровля	Кровля	

Согласовано

Взам. инв.N

Подпись и дата

Инв.N подл.

Изм.	Кол.уч.	Лист	N°док.	Подп.	Дата
Разраб.		Семенов			02.2025
Провер.		Пильгуй М.Н.			02.2025
Н. контр.		Пильгуй Н.М			02.2025
Нач. ОПИС №1		Белоусова Д.П			02.2025

2024-00375-01-0-ИОС1

Капитальный ремонт здания Государственного бюджетного общеобразовательного учреждения города Москвы «Школа № 1574» по адресу: г. Москва, Старопименовский пер., д. №5

Система электроснабжения

Стадия	Лист	Листов
П	44	

Щит ЩК. Схема электрическая принципиальная

МОСЖИЛ НИИПРОЕКТ

Формат А4 х 1

Питающая сеть, марка, сечение кабеля: ВВГнг(А)-LSLTx 5х6 от РП2

Щит распределительный

Аппараты ввода: Тип; Iном. (А); Iу. (мА)

Аппараты отходящих линий: Тип; Iном. (А); Iу. (мА)

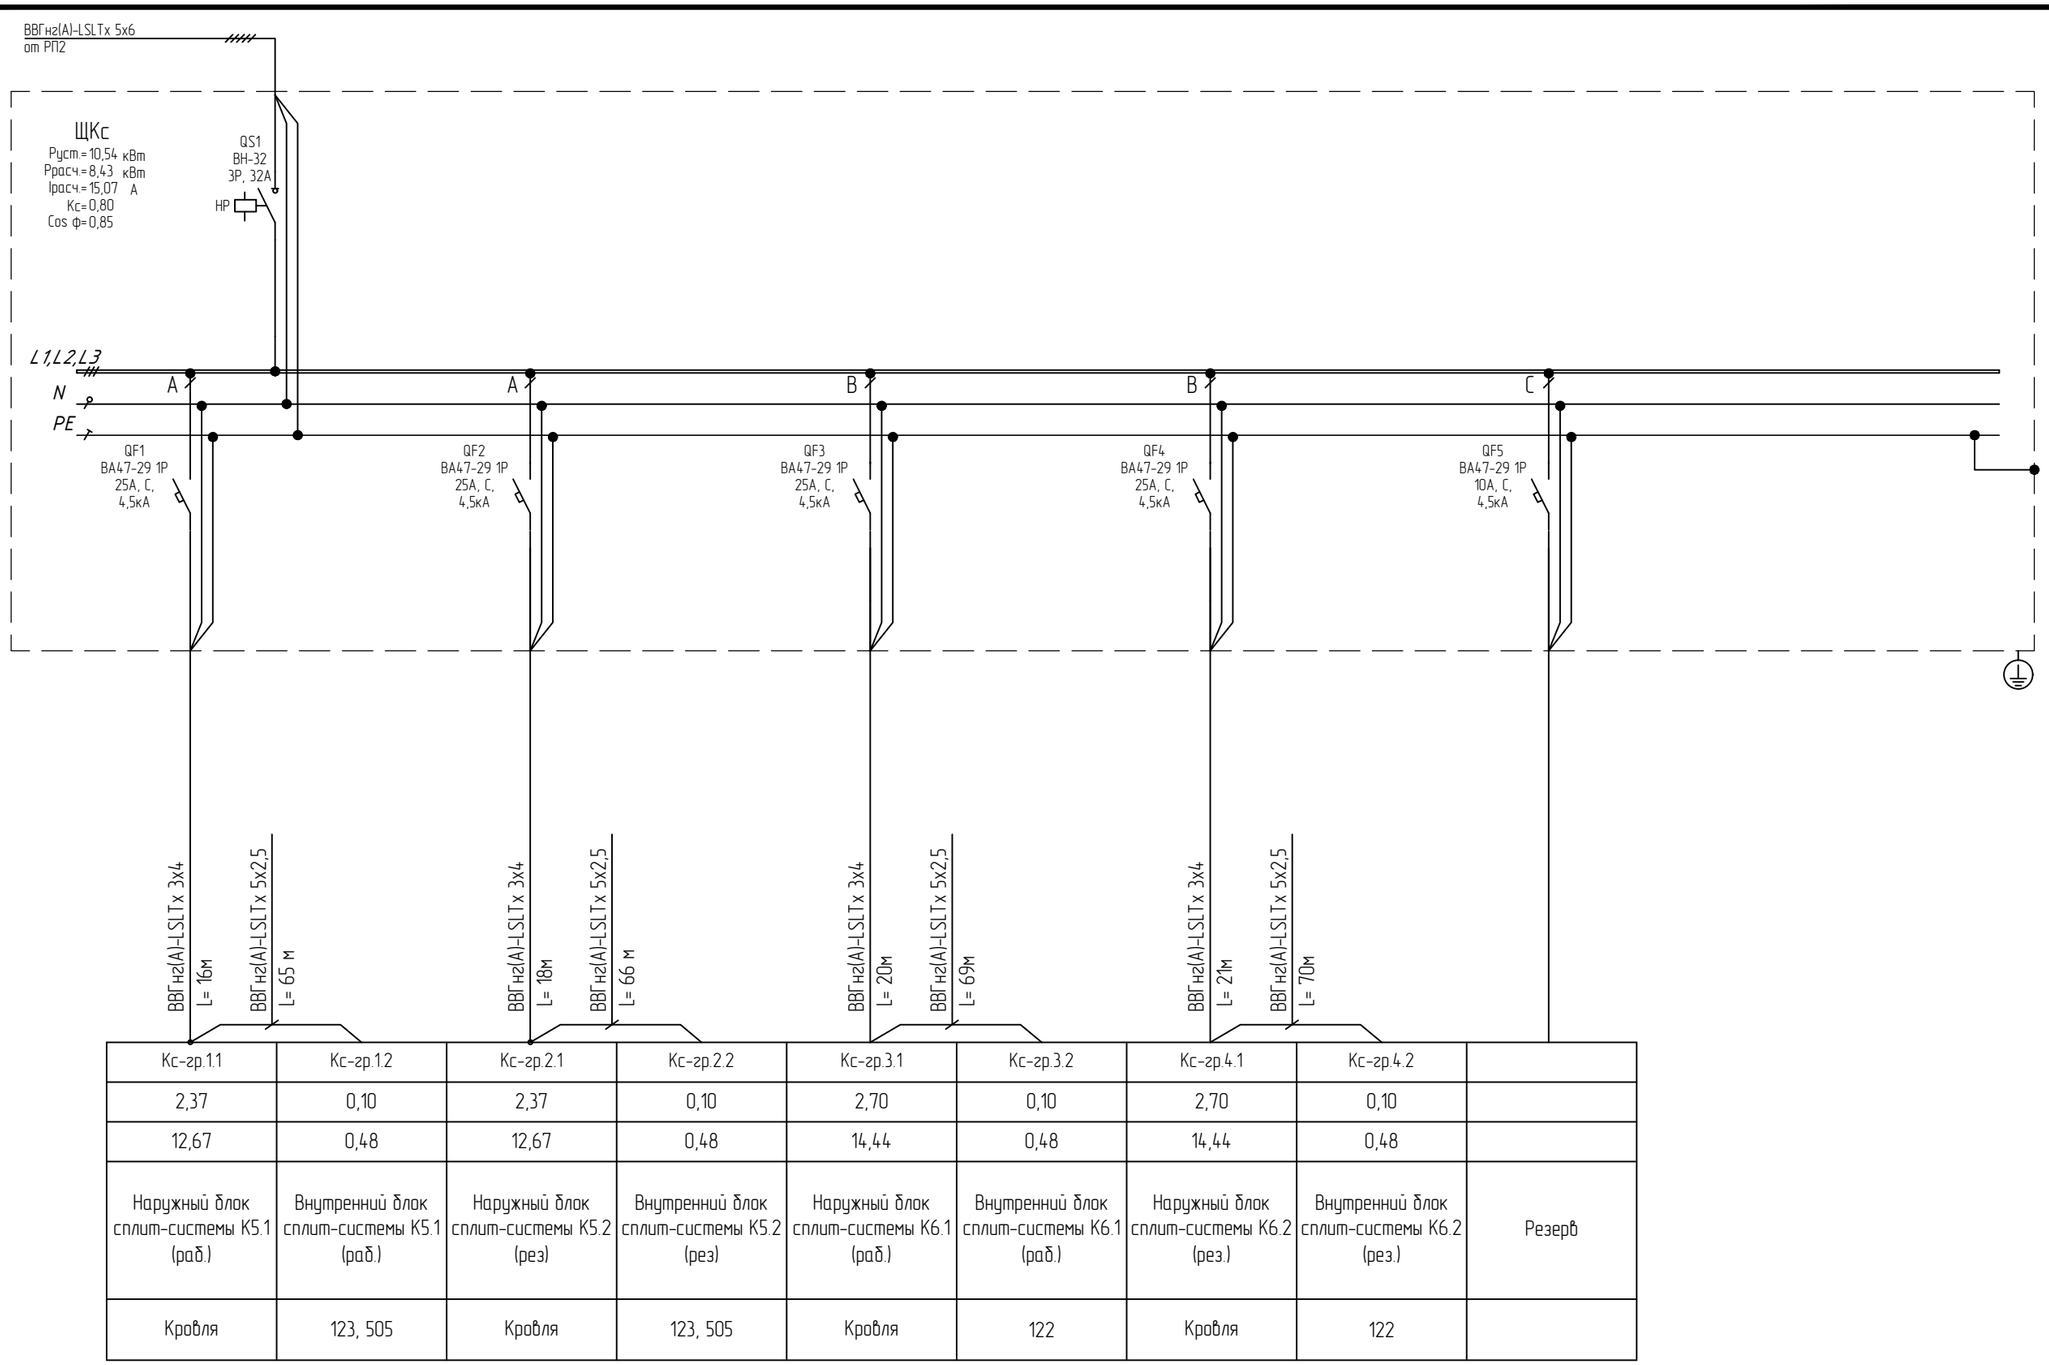

Марка и сечения кабелей / Длина участка сети

Электроприёмники									
	номер группы	Кс-гр.1.1	Кс-гр.1.2	Кс-гр.2.1	Кс-гр.2.2	Кс-гр.3.1	Кс-гр.3.2	Кс-гр.4.1	Кс-гр.4.2	
	Руст. (кВт)	2,37	0,10	2,37	0,10	2,70	0,10	2,70	0,10	
	Ip. (А)	12,67	0,48	12,67	0,48	14,44	0,48	14,44	0,48	
	Наименование	Наружный блок сплит-системы К5.1 (раб.)	Внутренний блок сплит-системы К5.1 (раб.)	Наружный блок сплит-системы К5.2 (рез)	Внутренний блок сплит-системы К5.2 (рез)	Наружный блок сплит-системы К6.1 (раб.)	Внутренний блок сплит-системы К6.1 (раб.)	Наружный блок сплит-системы К6.2 (рез.)	Внутренний блок сплит-системы К6.2 (рез.)	Резерв
	Помещения	Кровля	123, 505	Кровля	123, 505	Кровля	122	Кровля	122	

ВВГнг(А)-LSLTx 3х4 L= 16м; ВВГнг(А)-LSLTx 5х2,5 L= 65 м

ВВГнг(А)-LSLTx 3х4 L= 18м; ВВГнг(А)-LSLTx 5х2,5 L= 66 м

ВВГнг(А)-LSLTx 3х4 L= 20м; ВВГнг(А)-LSLTx 5х2,5 L= 69м

ВВГнг(А)-LSLTx 3х4 L= 21м; ВВГнг(А)-LSLTx 5х2,5 L= 70м

Согласовано

Взам. инв.N

Подпись и дата

Инв.N подл.

Изм.	Кол.уч.	Лист	N°док.	Подп.	Дата
Разраб.		Семенов			02.2025
Провер.		Пильгуй М.Н.			02.2025
Н. контр.		Пильгуй Н.М			02.2025
Нач. ОПИС №1		Белоусова Д.П.			02.2025

2024-00375-01-0-ИОС1

Капитальный ремонт здания Государственного бюджетного общеобразовательного учреждения города Москвы «Школа № 1574» по адресу: г. Москва, Старопименовский пер., д. №5

Система электроснабжения

Стадия	Лист	Листов
П	45	

Щит ЩКс. Схема электрическая принципиальная

МОСЖИЛ НИИПРОЕКТ

Формат А3 х 1

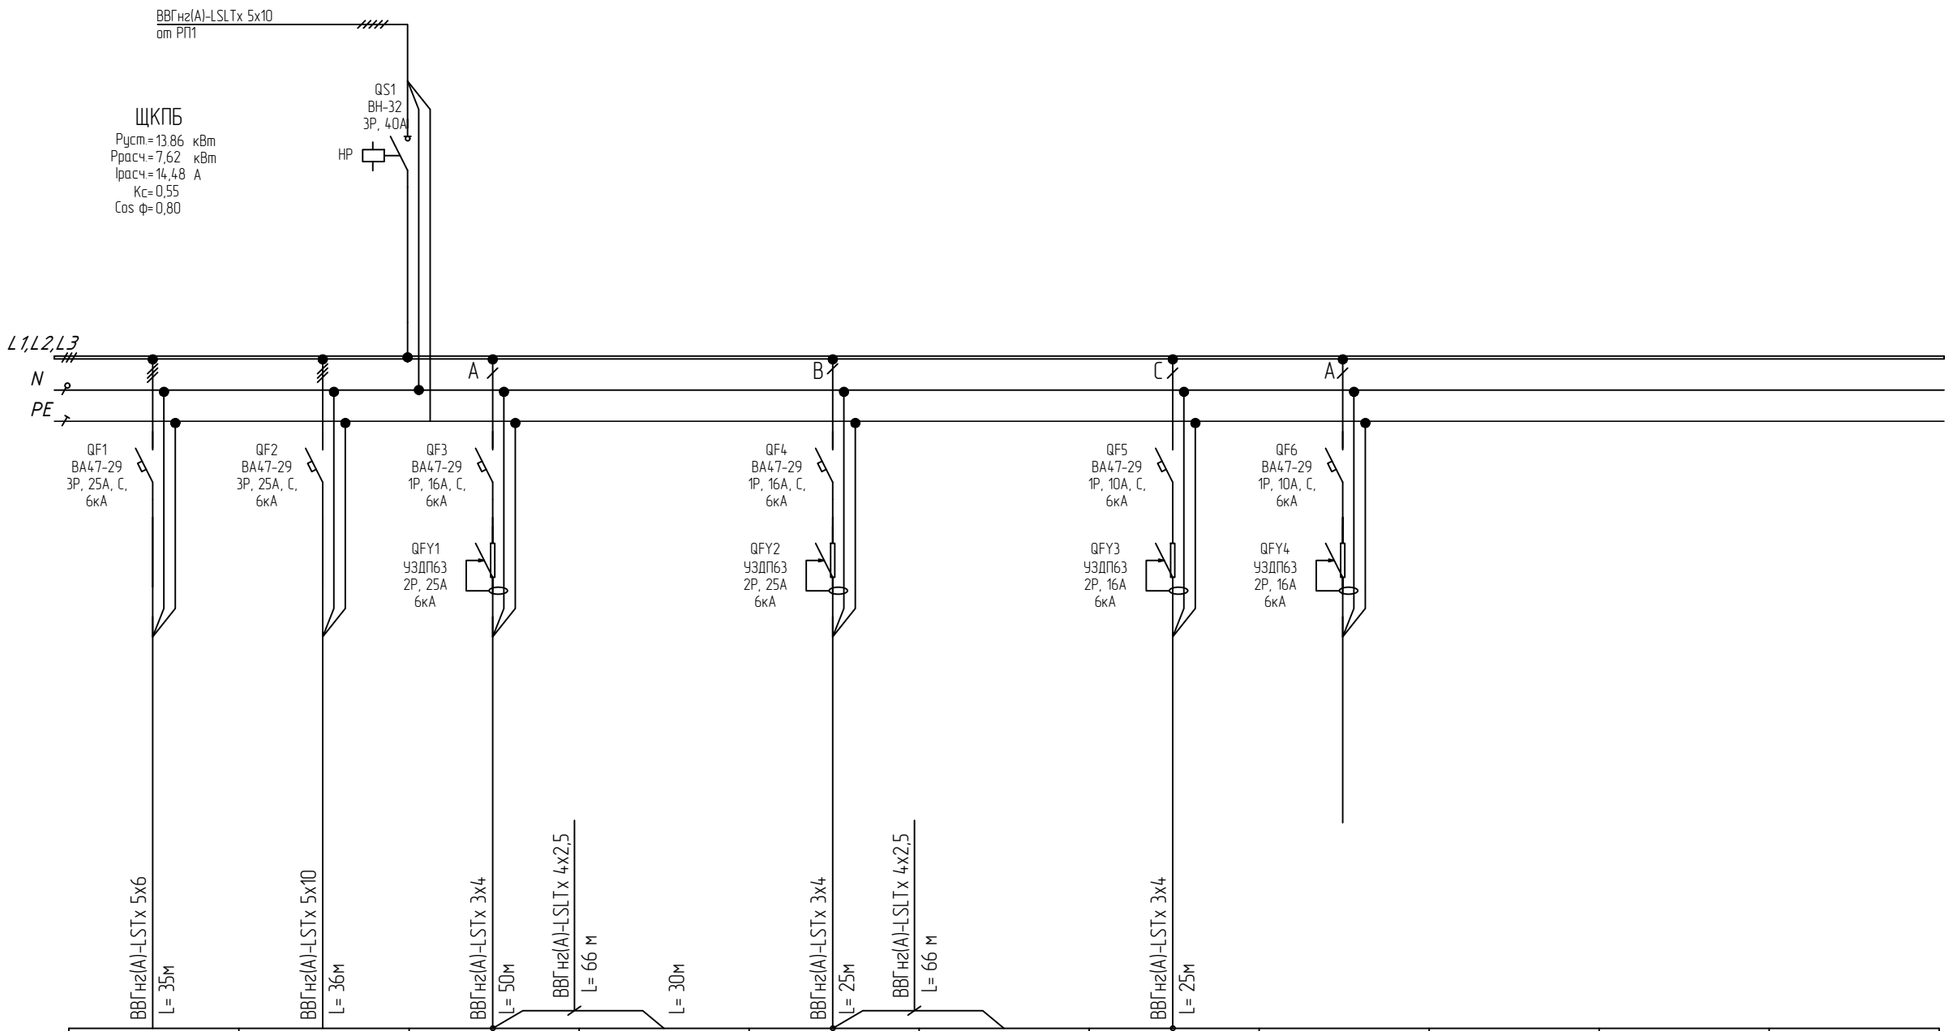

Щит распределительный	Аппараты ввода	Тип Iном. (А) Iу. (мА)
	Аппараты отходящих линий	Тип Iном. (А) Iу. (мА)
Марка и сечения кабелей		
Длина участка сети		

Электроприёмники											
	номер группы	КПБ-.1	КПБ-.2	КПБ-.3	КПБ-.4	КПБ-.5	КПБ-.6	КПБ-.7				
	Руст. (кВт)	6,00	8,30	2,70	0,10	2,70	0,10	0,30				
	Ip. (А)	9,61	13,29	12,36	0,46	12,36	0,46	1,37				
	Наименование	Тепловая завеса	К3	Наружный блок К7.1	Внутренний блок К7.1	Наружный блок К7.2	Внутренний блок К7.2	Внутренние блоки К3	Резерв			
	Помещения	144	Кровля 3 этажа	Кровля 3 этажа	140	Кровля 3 этажа	140	131, 133				

Согласовано

Взам. инв.N

Подпись и дата

Инв.N подл.

Изм.	Кол.уч.	Лист	N°док.	Подп.	Дата
Разраб.		Семенов			02.2025
Провер.		Пильгуй М.Н.			02.2025
Н. контр.		Пильгуй Н.М			02.2025
Нач. ОПИС №1		Белоусова Д.П.			02.2025

2024-00375-01-0-ИОС1

Капитальный ремонт здания Государственного бюджетного общеобразовательного учреждения города Москвы «Школа № 1574» по адресу: г. Москва, Старопименовский пер., д. №5

Система электроснабжения

Стадия	Лист	Листов
П	46	

Щит ЩКПБ. Схема электрическая принципиальная

МОСЖИЛ НИИПРОЕКТ

Формат А3 х 1

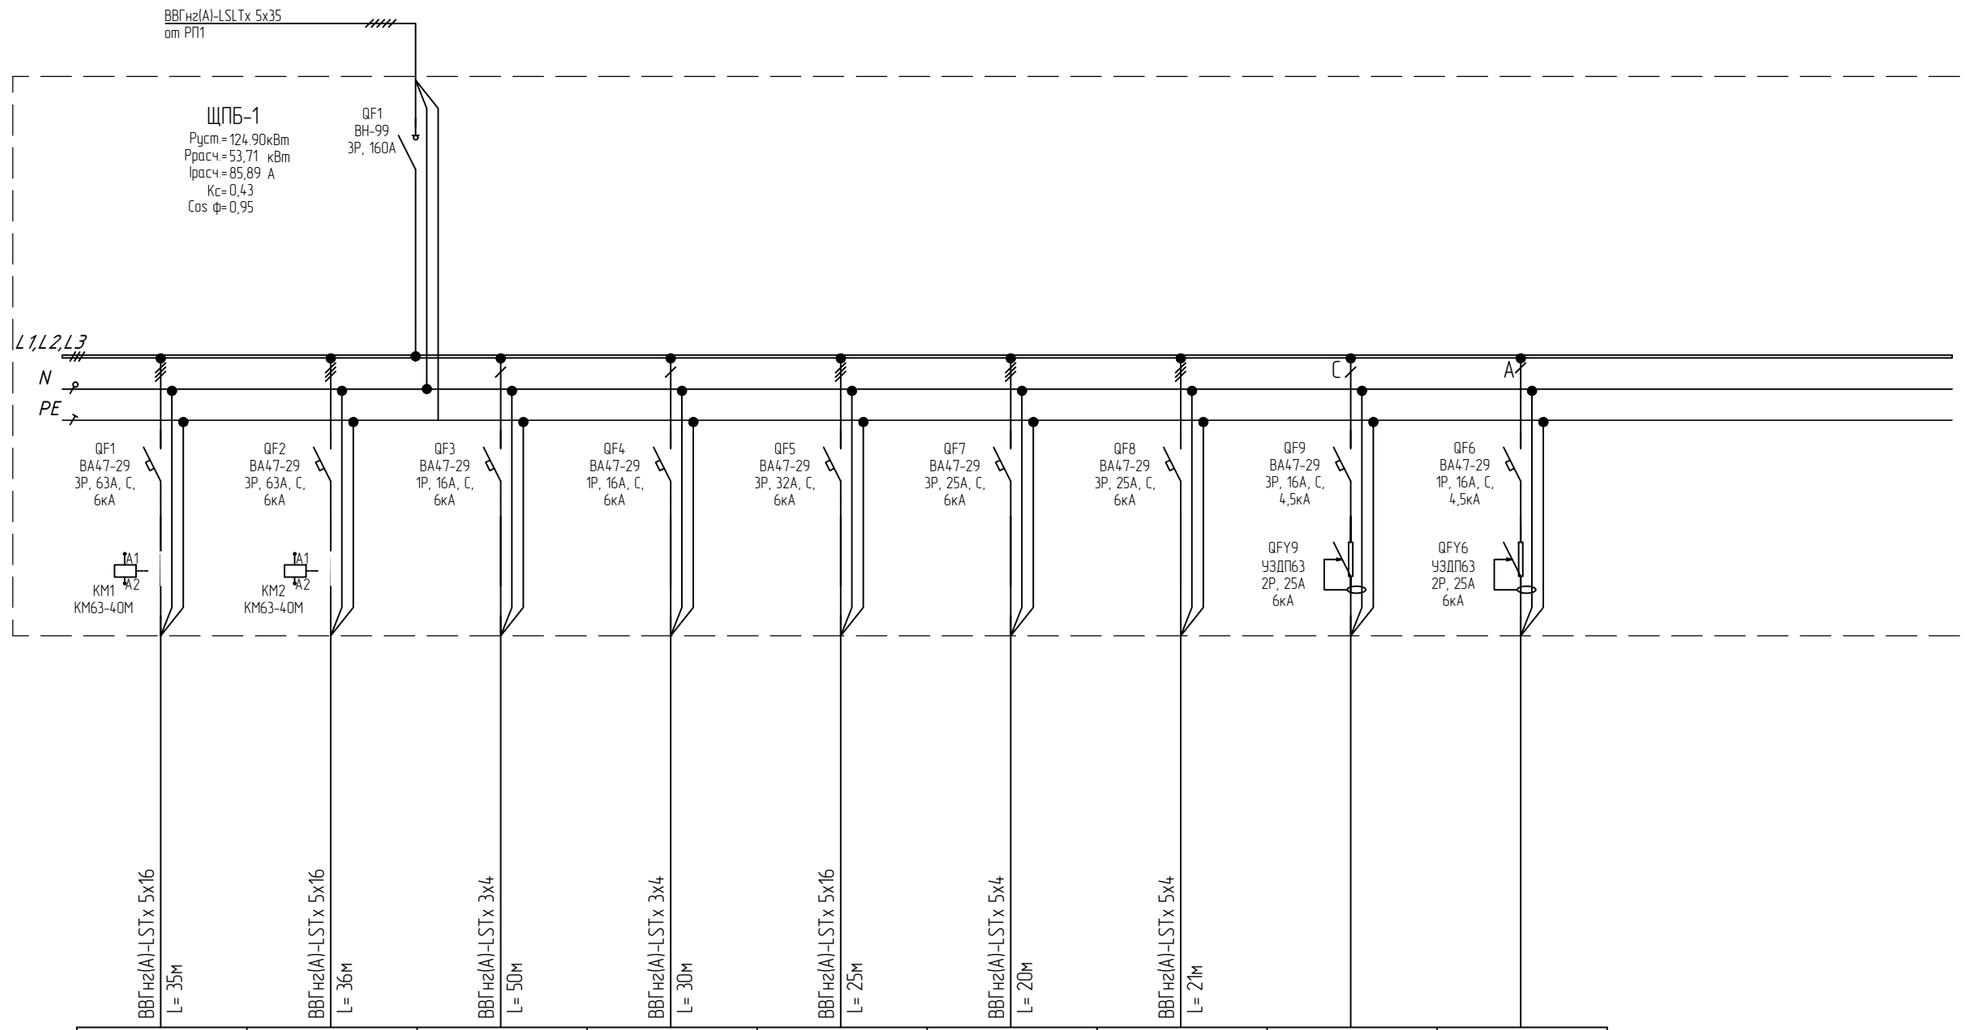

Щит распределительный			ВВГнг(А)-LSLTх 5х16 L= 35м	ВВГнг(А)-LSLTх 5х16 L= 36м	ВВГнг(А)-LSLTх 3х4 L= 50м	ВВГнг(А)-LSLTх 3х4 L= 30м	ВВГнг(А)-LSLTх 5х16 L= 25м	ВВГнг(А)-LSLTх 5х4 L= 20м	ВВГнг(А)-LSLTх 5х4 L= 21м		
	Аппараты ввода	Тип Iном. (А) Iу. (мА)									
	Аппараты отходящих линий	Тип Iном. (А) Iу. (мА)									
	Марка и сечения кабелей										
	Длина участка сети										
Электроприёмники	номер группы		ПБ-1.1	ПБ-1.2	ПБ-1.3	ПБ-1.4	ПБ-1.5	ПБ-1.6	ПБ-1.7		
	Руст. (кВт)		35,00	32,00	3,56	3,64	26,70	12,00	12,00		
	Ip. (А)		56,04	51,24	16,29	16,66	42,75	19,21	19,21		
	Наименование		Оборудование кухни	Оборудование кухни	Оборудование кухни	Оборудование кухни	Оборудование кухни	Водонагреватель проточный	Водонагреватель проточный	Резерв	Резерв
	Помещения		133	133	136	131	134	145	131		

Согласовано

Взам. инв.N

Подпись и дата

Инв.N подл.

Изм.	Кол.уч.	Лист	N°док.	Подп.	Дата
Разраб.		Семенов			02.2025
Провер.		Пильгуй М.Н.			02.2025
Н. контр.		Пильгуй Н.М.			02.2025
Нач. ОПИС №1		Белоусова Д.П.			02.2025

2024-00375-01-0-ИОС1

Капитальный ремонт здания Государственного бюджетного общеобразовательного учреждения города Москвы «Школа № 1574» по адресу: г. Москва, Старопименовский пер., д. №5

Система электроснабжения

Стадия	Лист	Листов
П	47	

Щит ЩПБ1. Схема электрическая принципиальная

МОСЖИЛ НИИПРОЕКТ

Формат А3 х 1

Согласовано

Взам. инв.N

Подпись и дата

Инв.N подл.

Питающая сеть, марка, сечение кабеля

Щит распределительный

Аппараты ввода

Тип Iном. (А) Iу. (мА)

Аппараты отходящих линий

Тип Iном. (А) Iу. (мА)

Марка и сечения кабелей

Длина участка сети

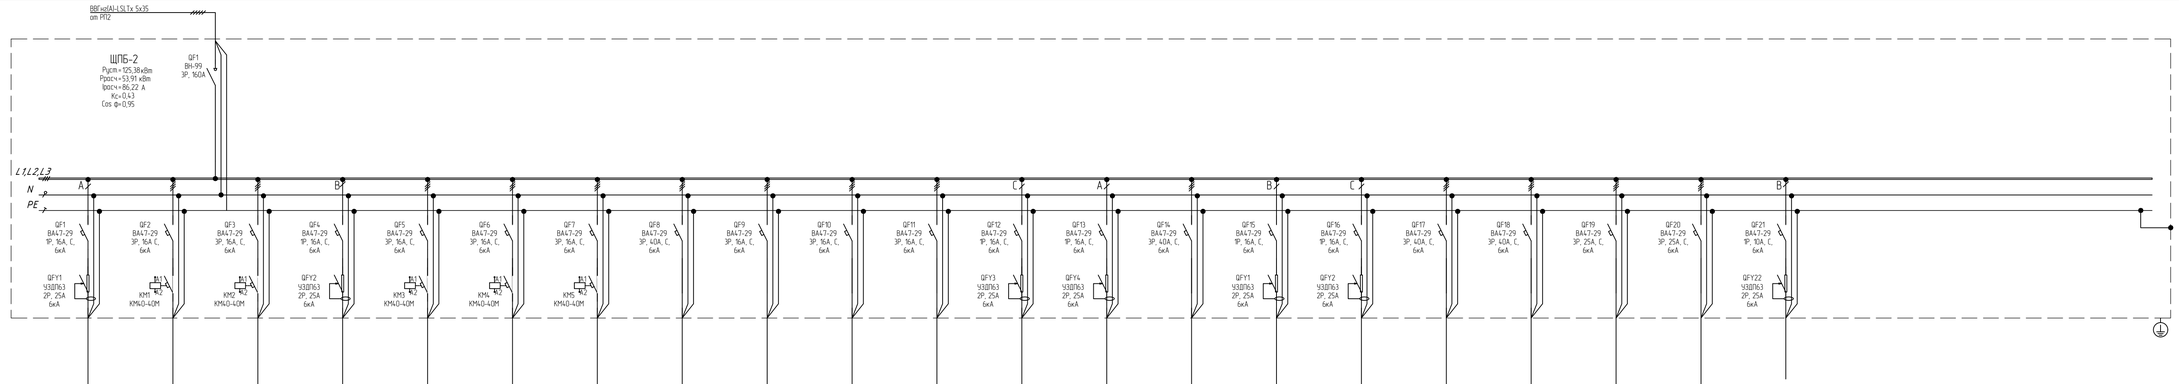

Электроприемники

номер группы	ПБ-2.1	ПБ-2.2	ПБ-2.3	ПБ-2.4	ПБ-2.5	ПБ-2.6	ПБ-2.7	ПБ-2.8	ПБ-2.9	ПБ-2.10	ПБ-2.11	ПБ-2.12	ПБ-2.13	ПБ-2.14	ПБ-2.15	ПБ-2.16	ПБ-2.17	ПБ-2.18	ПБ-2.19	ПБ-2.20	
Руст. (кВт)	0,81	1,00	1,00	0,95	2,71	2,71	1,00	22,80	1,13	1,13	1,13	0,92	1,92	22,80	3,00	0,38	18,00	18,00	12,00	12,00	
Ip. (А)	3,71	1,60	1,60	4,35	4,34	4,34	1,60	36,51	1,80	1,80	1,80	4,21	8,79	36,51	13,73	1,74	28,82	28,82	19,21	19,21	
Наименование	Оборудование кухни	Оборудование кухни	Оборудование кухни	Оборудование кухни	Оборудование кухни	Оборудование кухни	Оборудование кухни	Оборудование кухни	Оборудование кухни	Оборудование кухни	Оборудование кухни	Оборудование кухни	Оборудование кухни	Оборудование кухни	Оборудование кухни	Оборудование кухни	Оборудование кухни	Оборудование кухни	Водонагреватель проточный	Водонагреватель проточный	Резерв
Помещения	132	132	133	133	136	136	136	133	140	140	140	131,144	131	133	131	136	133	133	135	133	

Изм.	Кол.уч.	Лист	№док.	Подп.	Дата
Разраб.		Семенов			02.2025
Провер.		Пильгуй М.Н.			02.2025
Н. контр.		Пильгуй Н.М.			02.2025
Нач. ОПИС №1		Белоусова Д.П.			02.2025

2024-00375-01-0-ИОС1

Капитальный ремонт здания Государственного бюджетного общеобразовательного учреждения города Москвы «Школа № 1574» по адресу: г. Москва, Старопименовский пер., д. №5

Система электроснабжения

Стадия	Лист	Листов
П	48	

Щит ЩПБ2. Схема электрическая принципиальная

МОСЖИЛ НИИПРОЕКТ

Формат А4 х 4

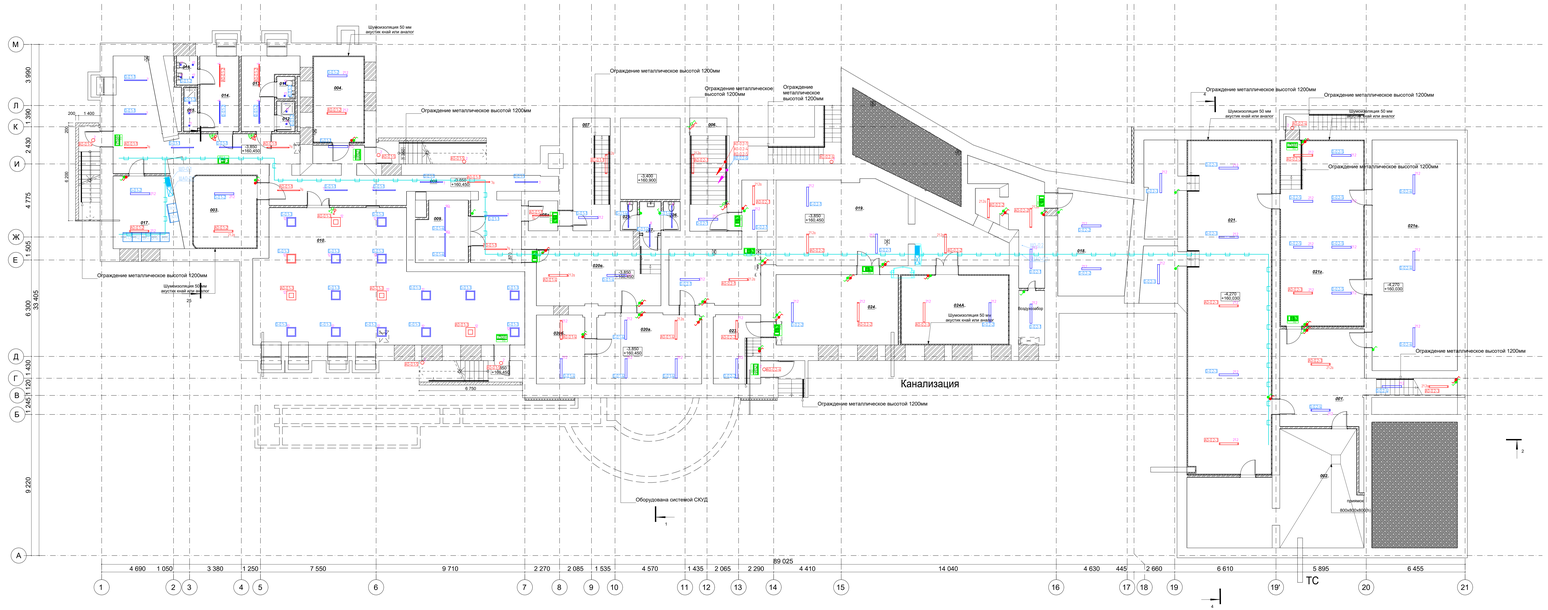

Перечень светильников Подвал

Индекс	Производитель	Наименование артикула	Светоотд. поток	Потребляемая мощность	Число
212	RVE	RVE-PRPE-SLIM-SC-38	4808 lm	38 W	53
12	RVE	RVE-PRPE-GRIL-SC-595 38W 4200K	3706 lm	38 W	18
7	RVE	RVE-PLI5070-GEARLINE-SC-940-P (50%)	1823 lm	20 W	9
17	RVE	RVE-LBX-CONTRO-SC-1005-1-GR IP54	801 lm	9 W	11
212a	RVE	RVE-PRPE-SLIM-SC-AP-38	4808 lm	38 W	12
2	RVE	RVE-CEILAIR-AP IP54 25W	3005 lm	25 W	6
9GL	RVE	RVE-PLI5777-GEARLINE-SC-930-P-IP54	2524 lm	28 W	2
8	RVE	RVE-PLI5070-GEARLINE-SC-IP54-940-P (50%)	1823 lm	20 W	3
10 11	RVE	RVE-PLI5070-GEARLINE-SC-IP54-980-P	2170 lm	24 W	2
6	RVE	RVE-PLI5070-GEARLINE-SC-940-P	3515 lm	39 W	4
7a	RVE	RVE-PLI5070-GEARLINE-SC-AP-940-P (50%)	1823 lm	20 W	6

Перечень оборудования щитового Подвал

Условное обозначение	Производитель	Наименование	Артикул	Цвет корпуса	Габариты, мм	Мощность, Вт	Степень защиты, IP	Кол-во, шт
PM01	ООО "Системы Освещения" (СО) ™	Светодиод. указатель постоянного действия FLAT S 2х3х10 30m 20 (M) IP54 with - EXIT	H600-000-05090	Белый	240х100х41	3	20	2
PM	ООО "Системы Освещения" (СО) ™	Светодиод. указатель постоянного действия FLAT S 2х3х10 30m 20 (M) IP54 with - EXIT right	H600-000-05092	Белый	240х100х41	3	20	1
PM	ООО "Системы Освещения" (СО) ™	Светодиод. указатель постоянного действия FLAT S 2х3х10 30m 20 (M) IP54 with - EXIT straight	H600-000-05093	Белый	240х100х41	3	20	1
PM01	ООО "Системы Освещения" (СО) ™	Светодиод. указатель постоянного действия INDEX S 250х130 30m 65 (M) IP54 with - EXIT	H600-000-05094	Белый	250х130х41	3	65	3
PM	ООО "Системы Освещения" (СО) ™	Светодиод. указатель постоянного действия INDEX S 250х130 30m 65 (M) IP54 with - EXIT straight	H600-000-05097	Белый	250х130х60	3	65	1

Экспликация помещений подвального этажа

Номер пом.	Наименование	Площадь, м2	Кат. пом.
001	Лестничная клетка	43.10	
002	ИТП	68.77	В4
003	Венткамера	20.99	В4
004	Венткамера	19.20	В4
005	Лестничная клетка тип 01	18.75	
007	Технологическая лестница	17.98	
008	Коридор	94.09	
008а	Тамбур-шлюз	3.78	
009	Снарядная	13.11	В3
010	Зал ЛФК	124.39	
011	Санузел	1.75	
012	Душевая	2.38	
013	Раздевальная (на более 5 чел)	10.72	
014	Раздевальная (на более 5 чел)	12.60	
015	Душевая	2.64	
016	Санузел	2.62	
017	Электрощитовая	19.98	В3
018	Подсобное помещение	31.35	В3
019	Коридор	127.62	
020а	Коридор	22.25	
020б	Помещение для прокладки коммуникаций	14.72	В4
020в	Коридор	30.83	
021	Венткамера	151.46	В4
021а	Помещение для прокладки коммуникаций	85.12	В4
021г	Венткамера	58.40	В3
023	Узел ввода	13.90	Д
024	Насосная	38.23	Д
024А	Венткамера	20.30	В4
025	Санузел	2.09	
026	Санузел	2.09	
027	Умывальная	2.64	
		1 112.65 м²	

Условные обозначения

- Переключатель 3кл IP54
- Выключатель 3кл IP54
- Выключатель 3кл IP20
- Выключатель 2кл IP20
- Выключатель 3кл IP20

								2024-00375-01-0-ИОС1	
								Капитальный ремонт объекта "Государственного бюджетного общеобразовательного учреждения города Москвы «Школа № 1574» по адресу: г. Москва, Северо-Западный пер., д. 8"	
Изм.	Кол.уч.	Лист	№ док.	Подп.	Дата				
Гип	Семенов				01.2025	Стадия	Лист	Листов	
ГАПвс	Тельцова М.С.				01.2025	П	49		
Н. контр.	Тельцова М.С.				01.2025	Система электроснабжения			
Нач. ПЭМ, ИОС	Кочнева Ю.В.				01.2025	План подвала		МОСЖИЛНИИПРОЕКТ	

Инв.№ подл. | Подпись и дата | Взам.инв.№

Копировал

Формат А2 x 1

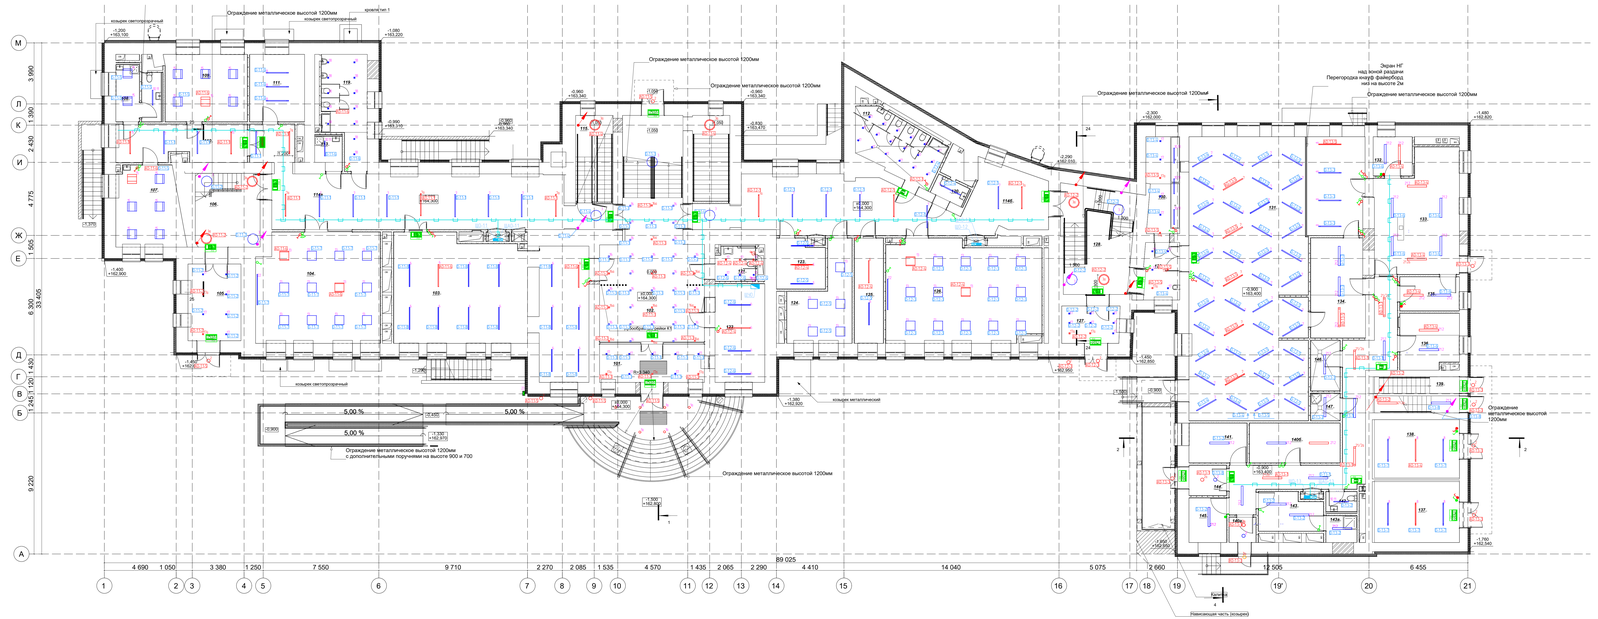

Перечень светильников Этаж 1

Файл	Производитель	Наименование артикул	Световой поток	Потребляемая мощность	Число
13	RVE	RVE-PRIME-SL-595 38W 4000K	3706 lm	38 W	30
15	RVE	RVE-PRIME-O-SL-595 CLIP IN IP54 38W 4000K	3706 lm	38 W	14
7	RVE	RVE-PI.55070-GEARLINE-SC-9660-P 150762	9823 lm	20 W	60
6	RVE	RVE-PI.55070-GEARLINE-SC-9660-P	3935 lm	39 W	20
8	RVE	RVE-PI.55070-GEARLINE-SC-IP54-9660-P 150762	9823 lm	20 W	10
10 11	RVE	RVE-PI.55070-GEARLINE-SC-IP54-980-P	2370 lm	26 W	6
16	RVE	RVE-LBX-CONTRO-SC-10205-1-GR	807 lm	9 W	28
17	RVE	RVE-LBX-CONTRO-SC-10205-1-GR IP54	807 lm	9 W	52
18	RVE	RVE-LBX-CONTRO-SC-10205-1-GR-Black IP54	807 lm	9 W	12
212	RVE	RVE-PRIME-SLIM-SC-38	4808 lm	38 W	29
14	RVE	RVE-DOT IP54 20W	1903 lm	20 W	6
3	RVE	RVE-LBX-RING-PRIME-SC-700 N	7452 lm	62 W	7
3a	RVE	RVE-LBX-RING-PRIME-SC-IP-700 N	7452 lm	62 W	6
7a	RVE	RVE-PI.55070-GEARLINE-SC-IP-9660-P 150762	9823 lm	20 W	7
5	RVE	RVE-PI.55070-GEARLINE-SC-9660-P-IP54 (N/Ex)	5935 lm	56 W	3
9a	RVE	RVE-LBX-CONTRO-SC-IP-10205-1-GR	807 lm	9 W	11
10a	RVE	RVE-LBX-CONTRO-SC-IP-10205-1-GR IP54	807 lm	9 W	11
21/2a	RVE	RVE-PRIME-SLIM-SC-IP-38	4808 lm	38 W	5
2a	RVE	RVE-CELLAR-BP IP54 25W	3005 lm	25 W	2
2	RVE	RVE-CELLAR IP54 25W	3005 lm	25 W	14
22	RVE	RVE-PI.53535-PRIMELINE-SC-2000-A	4375 lm	48 W	2
23	RVE	Prolar S 285x150x110 50Bm 65 4000 K15 WH 9600-000-05100	6250 lm	50 W	1

Перечень Извещателей (расположение) Этаж 1

Условное обозначение	Производитель	Наименование	Артикул	Цвет корпуса	Габариты, мм	Мощность, Вт	Степень защиты, IP	Кол-во, шт
ДИП1	ООО "Системы Оповещения" НТЦ ™	Светодиод указатель постоянного действия FLAT S 2х24/50 30m 20 (M) WH - EXIT	9600-000-05090	Белый	240х100х41	3	20	4
ДИП2	ООО "Системы Оповещения" НТЦ ™	Светодиод указатель постоянного действия FLAT S 2х24/50 30m 20 (M) wh - EXIT right	9600-000-05092	Белый	240х100х41	3	20	1
ДИП3	ООО "Системы Оповещения" НТЦ ™	Светодиод указатель постоянного действия FLAT S 2х24/50 30m 20 (M) WH - EXIT straight	9600-000-05093	Белый	240х100х41	3	20	12
ДИП4	ООО "Системы Оповещения" НТЦ ™	Светодиод указатель постоянного действия INDEX S 250х100 30m 65 (M) WH - EXIT	9600-000-05094	Белый	250х100х41	3	65	5
ДИП5	ООО "Системы Оповещения" НТЦ ™	Светодиод указатель постоянного действия INDEX S 250х100 30m 65 (M) wh - EXIT right	9600-000-05096	Белый	250х100х60	3	65	2
ДИП6	EX.GROUP	Светодиод указатель постоянного действия (EX.ISIS) на светильнике 30m 1.5ч + элементы схемы 3.32х3.42мм Multiscan	(EX.ISIS-1005-003-M2) (PCS-5-35-15-MEP/RAW)	Белый	363х152х23	3	20	1

Эксплуатация помещений 1 этажа

Номер поэт.	Наименование	Площадь, м2	Кат. пом.
101	Тамбур	16,08	
102	Вестибюль	72,40	
103	Гардеробная для обучающихся	94,68	
104	Учебный кабинет	57,67	
105	Тамбур	18,37	
106	Лестничная клетка тип Н2	22,57	
107	Процедурный (перевязочный) кабинет	22,14	
108	Место для приготовления дезинфицирующих растворов и хранения уборочного инвентаря	10,35	В4
109	Кабинет врача	23,64	
110	Зона ожидания посетителей	20,58	
111	Кладовая	10,75	В3
112	Санузел для девочек с комнатой личной гигиены	7,99	
113	ПУИ	3,70	В4
114а	Коридор	83,40	
114б	Коридор	75,18	
115	Технологическая лестница	13,98	
119	Санузел для мальчиков	5,69	
120	Санузел для персонала	3,40	
121	Санузел для МГН	6,40	
122	Комната охраны	20,95	
123	Кроссовая	9,82	В4
124	Административный кабинет тип 1	19,95	
125	Гардеробная комната для учителей	13,02	
126	Учебный кабинет	65,15	
127	Тамбур	10,38	
128	Лестничная клетка тип Л1	33,83	
129	Коридор	10,06	
130	Умывальная	13,97	
131	Обеденный зал	169,16	
132	Холодный цех	6,07	В4
133	Горячий цех	41,96	В3
134	Моечная столовой посуды	23,00	В4
135	Моечная кухонной посуды	8,66	В4
136	Доготовочный цех	13,73	В3
137	Техническое помещение (электрощитовая)	23,30	В3
138	Техническое помещение (электрощитовая)	21,83	В3
139	Лестничная клетка тип Л1	15,32	
140	Коридор	40,06	
140а	Тамбур	3,45	
140б	Помещение холодильного оборудования	15,31	В3
141	Кладовая сухих продуктов	9,82	В4
142	Санузел	2,68	
143	Помещение для персонала	6,91	
143а	Душ	3,52	
144	Загрузочный цех	5,78	В4
145	Кладовая и моечная оборотной тары	7,17	В4
146	Помещение для временного хранения пищевых отходов	6,16	В4
147	ПУИ	3,46	В4
		1 058,91 м²	

Условные обозначения

- Переключатель 1кл IP54
- Переключатель 1кл IP20
- Выключатель 1кл IP54
- Выключатель 1кл IP20
- Выключатель 2кл IP20
- Выключатель 3кл IP20

								2024-00375-01-0-ИОС1	
								Капитальный ремонт общеобразовательного учреждения города Москвы «Школа № 1534» по адресу: г. Москва, Северное Измайлово, вед. 3 ФП	
Изм.	Кол.уч.	Лист	№док.	Подп.	Дата				
Гип	Семенов				01.2025	Система электроснабжения		Стадия	Лист	Листов
ГлИнж	Кальцер М.Н.				01.2025			П	50	
Н. контр.	Кальцер М.Н.				01.2025	План этажа Этаж 1		МОСЖИЛНИИПРОЕКТ	
Нач. ОПИ, ИТ	Кальцер М.Н.				01.2025				

Формат А2 ×1

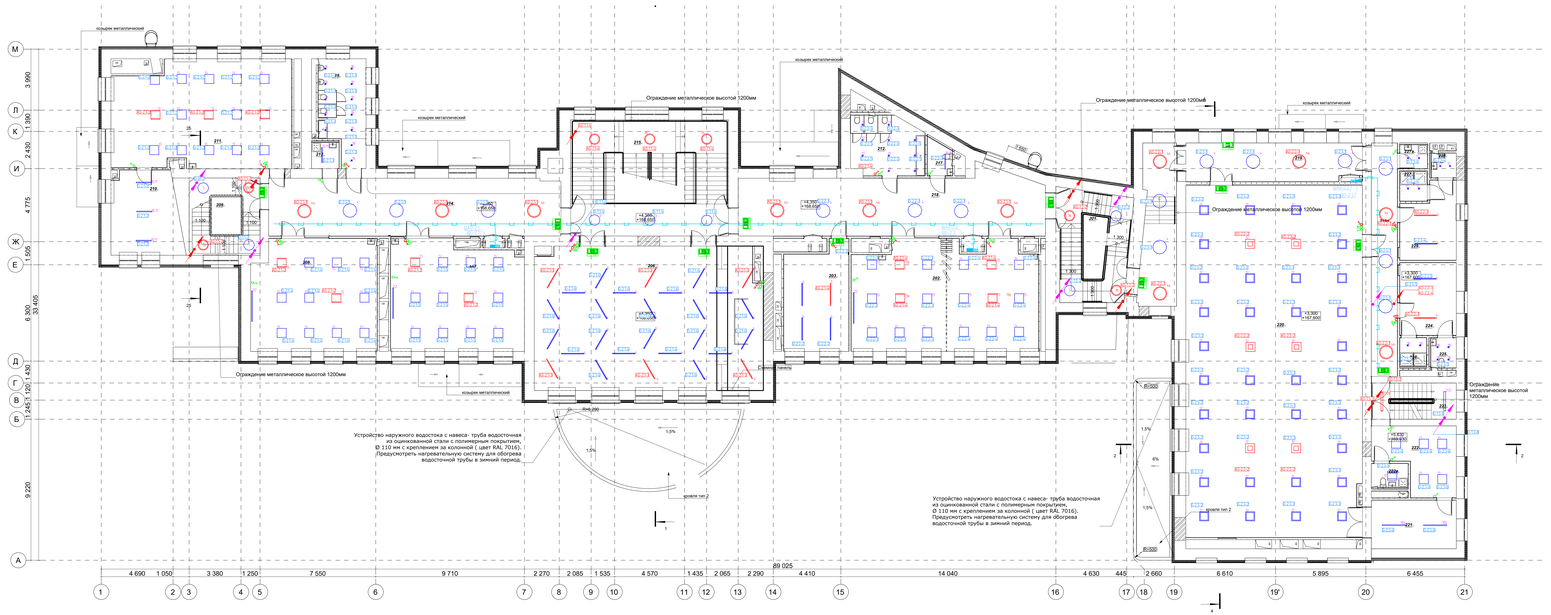

Перечень светильников (Этаж 2)

Индекс	Производитель	Наименование артикула	Световой поток	Потребляемая мощность	Число
3	RVE	RVE-LBX-RNG-PRME-SC-700 N	7452 lm	62 W	7
3a	RVE	RVE-LBX-RNG-PRME-SC-BP-700 N	7452 lm	62 W	7
13	RVE	RVE-PRME-SC-595 38W 4200K	3706 lm	38 W	62
12	RVE	RVE-PRME-GRL-SC-595 38W 4200K	3706 lm	38 W	40
6	RVE	RVE-PLS5070-GEARLINE-SC-9660-P	7055 lm	39 W	36
18	RVE	RVE-LBX-CONTRO-SC-9205-1-GR-Black IP54	801 lm	9 W	16
17	RVE	RVE-LBX-CONTRO-SC-9305-1-GR IP54	801 lm	9 W	16
4	RVE	RVE-LBX-RNG-PRME-SC-900-P (5276)	6371 lm	53 W	14
4a	RVE	RVE-LBX-RNG-PRME-SC-BP-900-P (5276)	6371 lm	53 W	11
15	RVE	RVE-PRME-D-SC-595 CLP IN IP54 38W 4200K	3706 lm	38 W	3
10 11	RVE	RVE-PLS5070-GEARLINE-SC-IP54-980-P	2370 lm	26 W	5
22	RVE	RVE-PLS35/5-PRMELINE-SC-2000-4	4375 lm	48 W	3
21.2	RVE	RVE-PRME-SLM-SC-38	4808 lm	38 W	1
21.2a	RVE	RVE-PRME-SLM-SC-BP-38	4808 lm	38 W	1
9SL	RVE	RVE-PLS3775-GEARLINE-SC-7500-P-IP54	2524 lm	28 W	2
15	RVE	RVE-PRME-D-SC-595 CLP IN IP54 38W 4200K	3706 lm	38 W	3

Перечень обозначения указателей
Этаж 2

Условное обозначение	Производитель	Наименование	Артикул	Цвет корпуса	Габариты, мм	Мощность, Вт	Степень защиты, IP	Кол-во, шт
2a	ООО "Системы Освещения" (с) ™	Светодиод указатель постоянного действия FLAT S 240x130 38w 20 EM1 WH - EXIT left	H600-000-05091	Белый	240x130x41	3	20	1
2b	ООО "Системы Освещения" (с) ™	Светодиод указатель постоянного действия FLAT S 240x130 38w 20 EM1 WH - EXIT straight	H600-000-05093	Белый	240x130x41	3	20	72

Экспликация помещений 2 этажа

Номер пом.	Наименование	Площадь, м²	Кат. пом.
201	Лестничная клетка тип Л1	53.37	
202	Кабинет иностранного языка	84.57	
203	Рабочее пространство для учителей тип 2	28.30	
205	Актовый зал	139.32	
207	Учебный кабинет	60.84	
208	Учебный кабинет	59.26	
209	Лестничная клетка Л1	23.31	
210	Кладовая инвентарь творческой мастерской	24.19	Б3
211	Кабинет ИЗО	79.82	
212	Санузел для девочек	6.89	
213	ПУИ	3.61	Б4
214	Коридор	61.13	
215	Вестибюль	76.16	
216	Санузел для мальчиков	5.90	
217	Санузел для персонала	3.48	
218	Коридор	78.84	
219	Коридор	53.72	
219а	Коридор	26.29	
220	Спортивный зал	265.70	
221	Снарядная	14.52	Б3
222	Комната инструктора	20.28	
222а	Душ с санузлом	3.77	
223	Лестничная клетка тип Л1	13.13	
224	Раздевальная	17.52	
225	Санузел	3.31	
226	Душевая	3.31	
227	Душевая	3.57	
227а	ПУИ	2.84	Б4
228	Санузел	2.96	
229	Раздевальная	16.33	
		1 222.94 м²	

Условные обозначения

- Переключатель 2кл. IP20
- Выключатель 1кл. IP20
- Выключатель 2кл. IP20
- Выключатель 3кл. IP20
- Выключатель 3кл. IP20

								2024-00375-01-0-ИОС1	
								Капитальный ремонт общеобразовательного учреждения города Москвы «Школа № 1234» по адресу: г. Москва, Северо-Западный пер., д. 8 стр.	
Изм.	Кол.уч.	Лист	№док.	Подп.	Дата				
Гип	Семенов				07.2025	Система электроснабжения		Стадия	Лист	Листов
Разраб.	Кальсина Н.Н.				07.2025			П	51	
Н. контр.	Кальсина Н.Н.				07.2025	План освещения 2 этажа		МОСКИЛ НИИПРОЕКТ		
Нач. ОПИС	Кальсина Н.Н.				07.2025					

Инв.№ подл. | Подпись и дата | Взам.инв.№ | Инв.№ дубл. | Подпись и дата

Формат А2 ×1

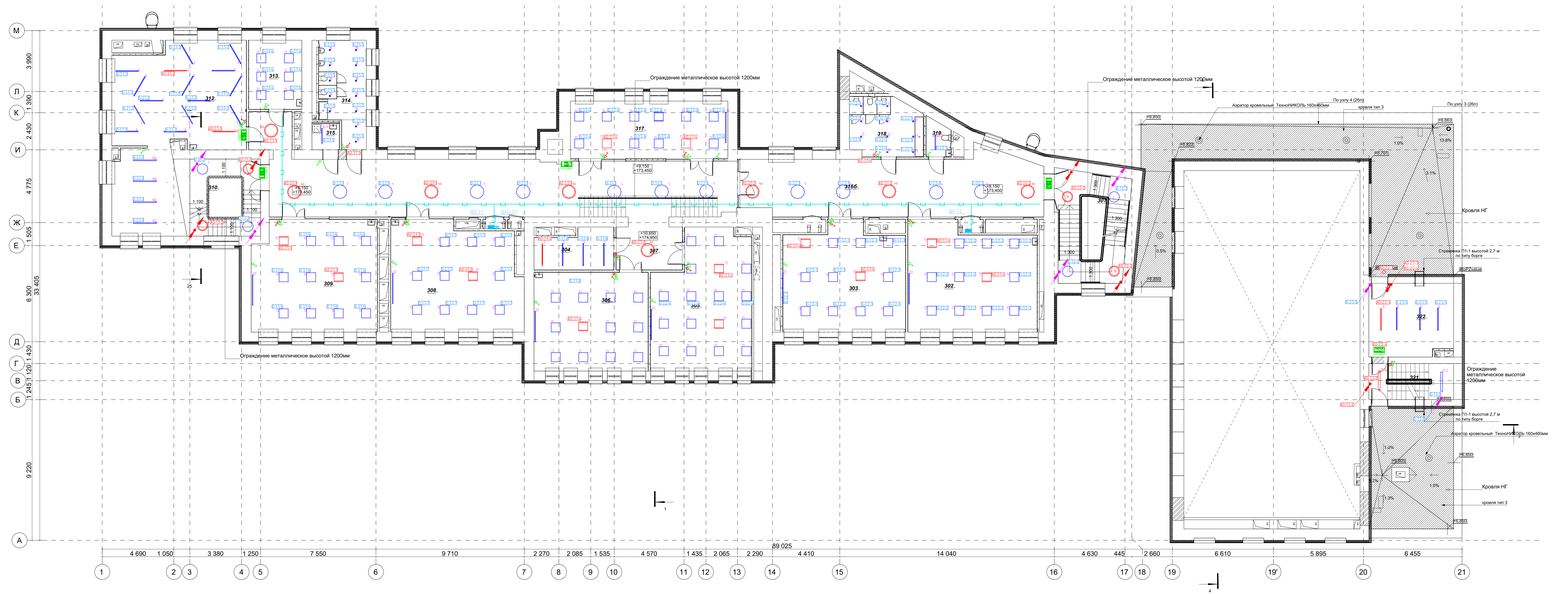

Перечень светильников (Этаж 3)

Индекс	Производитель	Название артикула	Световой поток	Потребляемая мощность	Число
90L	RVE	RVE-PI.55771-GEARLINE-SC-9.0.0-P-IP54	2524 lm	28 W	4
13	RVE	RVE-PRIME-SC-595 36W 4000K	3706 lm	38 W	95
18	RVE	RVE-LBX-CONTRO-SC-9.0.05-1-GR-Black IP54	801 lm	9 W	12
17	RVE	RVE-LBX-CONTRO-SC-9.0.05-1-GR IP54	801 lm	9 W	10
6	RVE	RVE-PI.55070-GEARLINE-SC-9.60-P	3555 lm	39 W	20
3	RVE	RVE-LBX-RING-PRIME-SC-700 N	7452 lm	62 W	4
3a	RVE	RVE-LBX-RING-PRIME-SC-BP-700 N	7452 lm	62 W	4
4	RVE	RVE-LBX-RING-PRIME-SC-900-P-152NJ	6371 lm	53 W	11
4a	RVE	RVE-LBX-RING-PRIME-SC-BP-900-P-152NJ	6371 lm	53 W	8
5	RVE	RVE-PI.55070-GEARLINE-SC-9.60-P-IP54 (14.75)	5705 lm	56 W	4
21.2	RVE	RVE-PRIME-SLIM-SC-38	4808 lm	38 W	1
21.2a	RVE	RVE-PRIME-SLIM-SC-BP-38	4808 lm	38 W	1
2	RVE	RVE-COLLAR IP54 25W	3005 lm	25 W	1
10.11	RVE	RVE-PI.55070-GEARLINE-SC-IP54-980-P	2370 lm	26 W	2
22	RVE	RVE-PI.55515-PRIMELINE-SC-2000-4	4375 lm	48 W	1

Перечень обращенных указателей Этаж 3

Условное обозначение	Производитель	Наименование	Артикул	Цвет корпуса	Габариты, мм	Мощность, Вт	Степень защиты, IP	Кол-во, шт
Выход	ООО "Системы Освещения" (СО) ™	Светодиод указатель постоянного действия FLAT S 240x130 3Вт 2D (90) мін - EXIT	H600-000-05090	белый	240x130x41	3	20	1
3L1	ООО "Системы Освещения" (СО) ™	Светодиод указатель постоянного действия FLAT S 240x130 3Вт 2D (90) мін - EXIT left	H600-000-05091	белый	240x130x41	3	20	1
3R1	ООО "Системы Освещения" (СО) ™	Светодиод указатель постоянного действия FLAT S 240x130 3Вт 2D (90) мін - EXIT straight	H600-000-05093	белый	240x130x41	3	20	3

Экспликация помещений 3 этажа

Номер пом.	Наименование	Площадь, м2	Кат. пом.
301	Лестничная клетка тип Л1	33,37	
302	Учебный кабинет	57,24	
303	Учебный кабинет	63,44	
304	Серверная	12,66	Б3
305	Учебный кабинет	66,09	
306	Учебный кабинет	48,33	
307	Коридор	137,41	
308	Учебный кабинет	59,17	
309	Учебный кабинет	59,25	
310	Лестничная клетка тип Н2	23,38	
312	Библиотека	69,66	Б3
313	Кабинет для индивидуальных занятий в т+с с учителем-логопедом	15,77	
314	Санузел для маломоров	19,83	
315	ПУИ	3,56	В4
3166	Коридор	76,16	
317	Кабинет иностранного языка	39,23	
318	Санузел для девочек	17,74	
319	Санузел для персонала	3,69	
321	Лестничная клетка тип Л1	13,13	
322	Техническое помещение	26,05	Б3
		837,57 м²	

Условные обозначения

- Выключатель 3кл IP20
- Выключатель 2кл IP20
- Выключатель 2кл IP20
- Выключатель 3кл IP20

										2024-00375-01-0-ИОС1	
										Капитальный ремонт общеобразовательного бюджетного общеобразовательного учреждения города Москвы «Школа № 1574» по адресу: г. Москва, Северо-Западный окр., р. р-н	
Изм.	Кол.уч.	Лист	№ док.	Подп.	Дата						
Гип	Семенов				01.2025					Система электроснабжения	Стадия: П; Лист: 52; Листов:
Разраб.	Тельцер М.Н.				01.2025						
										План освещения 3 этажа	МОСКИЛ НИИПРОЕКТ
Н. контр.	Тельцер М.Н.				01.2025						
Нач. ОПИС МГП	Кочубей Ю.В.				01.2025						

Инв.№ подл. | Подпись и дата | Взам.инв.№ | Инв.№ дубл. | Подпись и дата

Формат А2 x 1

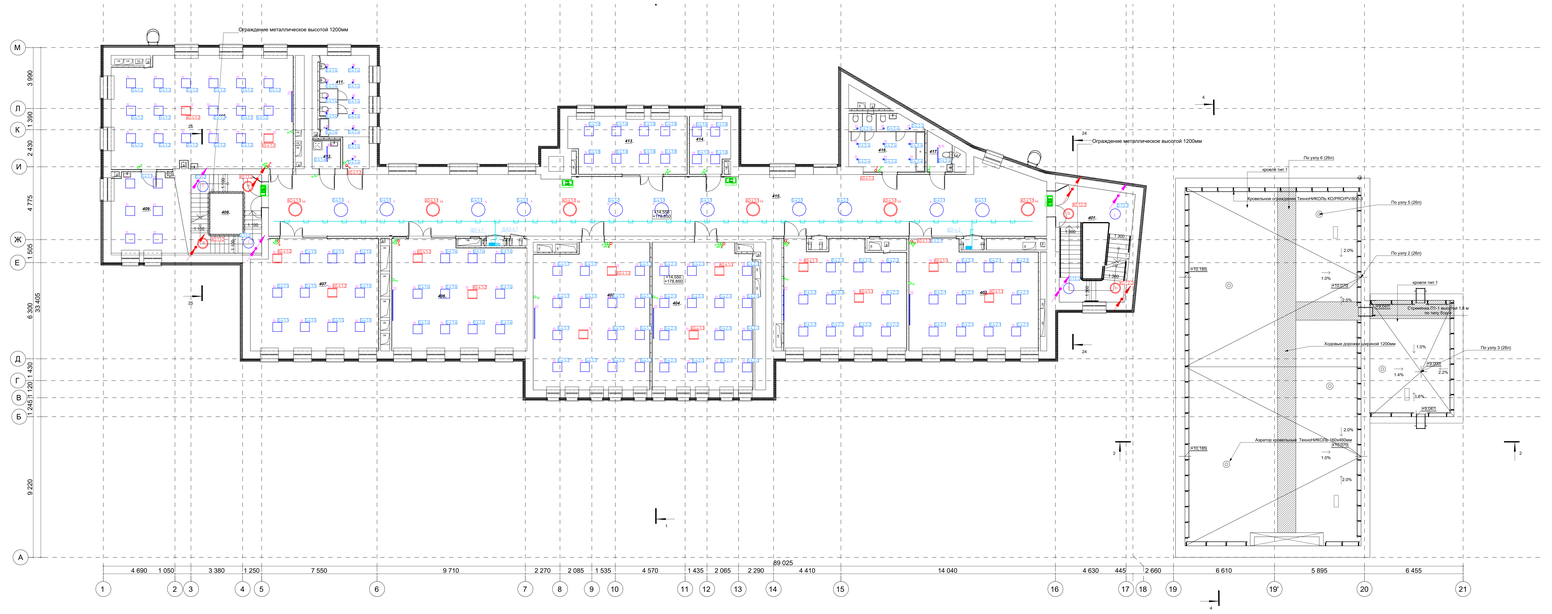

Перечень светильников Опись 42

Индекс	Производитель	Условное артикулу	Световой поток	Потребляемая мощность	Число
13	RVE	RVE-PRPE-SC-595 38W 4000K	3706 lm	38 W	196
4	RVE	RVE-LBX-RNG-PRPE-SC-900-P-150742	6371 lm	53 W	77
18	RVE	RVE-LBX-CONTRO-SC-1005-1-GR-Black IP54	801 lm	9 W	52
17	RVE	RVE-LBX-CONTRO-SC-BP-1005-1-GR IP54	801 lm	9 W	9
22	RVE	RVE-PLI5570-PRMLINE-SC-2000-K	4375 lm	48 W	6
3	RVE	RVE-LBX-RNG-PRPE-SC-700 N	7452 lm	62 W	4
36	RVE	RVE-LBX-RNG-PRPE-SC-BP-700 N	7452 lm	62 W	4
40	RVE	RVE-LBX-RNG-PRPE-SC-BP-900-P-150742	6371 lm	53 W	6
10 11	RVE	RVE-PLI5570-GEARLINE-SC-IP54-980-P	2370 lm	26 W	2

Перечень обозначений указателей
Лист 4

Условное обозначение	Производитель	Наименование	Артикул	Тип корпуса	Габариты, мм	Мощность, Вт	Световой поток, lm	Кол-во, шт
	ООО "Системы Освещения" (с) ™	Светодиод указатель постоянного действия FLAT S 240x130 3Вт 2D EMS left - EXIT left	H600-000-05091	Белый	240x130x41	3	20	1
	ООО "Системы Освещения" (с) ™	Светодиод указатель постоянного действия FLAT S 240x130 3Вт 2D EMS left - EXIT right	H600-000-05092	Белый	240x130x41	3	20	1
	ООО "Системы Освещения" (с) ™	Светодиод указатель постоянного действия FLAT S 240x130 3Вт 2D EMS left - EXIT straight	H600-000-05093	Белый	240x130x41	3	20	2

Экспликация помещений 4 этажа

Номер пом.	Наименование	Площадь, м2	Кат. пом.
401	Лестничная клетка тип Л1	35,72	
402	Кабинет русского языка и литературы	67,81	
403	Кабинет русского языка и литературы	58,37	
404	Кабинет истории тип 1	63,17	
405	Кабинет математики	71,92	
406	Кабинет математики	62,41	
407	ОБЗР	60,29	
408	Лестничная клетка тип Н2	24,40	
409	Лаборантская кабинета биологии	24,33	Б3
410	Учебные кабинеты для изучения естествознания: биология/ПЗРК	88,85	
411	Санузел для мальчиков	21,05	
412	ПУИ	3,67	Б4
413	Административный кабинет тип 1	28,57	
414	Кабинет для индивидуальных занятий в т.ч. педагогов-психологов	9,72	
415	Коридор	206,03	
416	Санузел для девочек с комнатой личной гигиены	17,93	
417	Санузел для персонала	3,72	
		832,76 м²	

Условные обозначения

- Выключатель 1кл. IP20
- Выключатель 2кл. IP20
- Выключатель 3кл. IP20
- Выключатель 3кл. IP20

Изм.	Кол.уч.	Лист	№док.	Подп.	Дата		
Гип		Синицкий				2024-00375-01-0-ИОС1	
ГИП		Тельцер М.Н.				Капитальный ремонт общеобразовательного учреждения города Москвы «Школа № 1574» по адресу: г. Москва, Северное Медведково пер. 3 №1	
Н. контр.		Тельцер М.Н.				Система электроснабжения	Стадия: П; Лист: 53; Листов:
Нач. ОПИС №1		Кочергина Л.В.				План 1(Опись 4 эпизод)	МОСКИЛ НИИПРОЕКТ

Инв.№ подл. | Подпись и дата | Взам.инв.№

Формат А2 ч

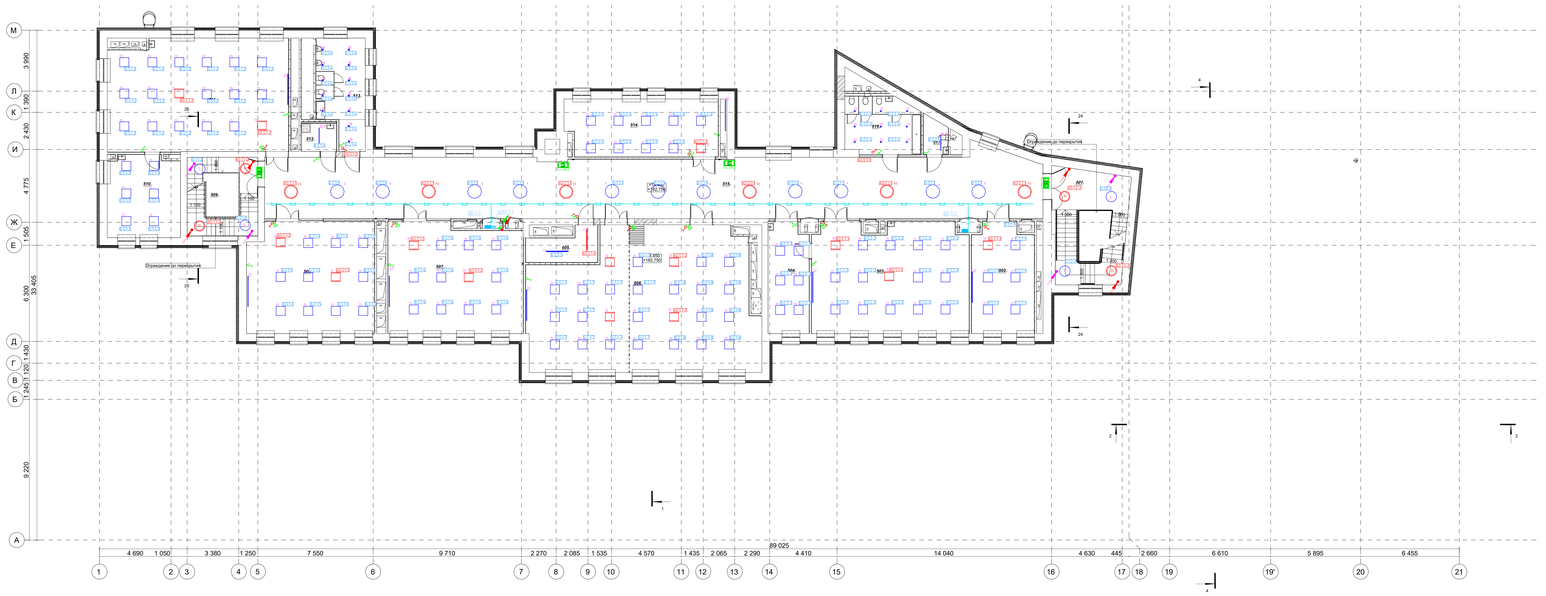

Перечень светильников Список 12

Индекс	Производитель	Название артикула	Световой поток	Потребляемая мощность	Число шт
13	RVE	RVE-PRIME-SC-595 30W 4200K	3706 lm	38 W	111
4	RVE	RVE-LBX-RING-PRIME-SC-900-P (52%)	6371 lm	53 W	11
18	RVE	RVE-LBX-CONTRO-SC-10075-1-GR-Black IP54	807 lm	9 W	12
17	RVE	RVE-LBX-CONTRO-SC-10075-1-GR IP54	801 lm	9 W	9
3	RVE	RVE-LBX-RING-PRIME-SC-700 N	7452 lm	62 W	4
36	RVE	RVE-LBX-RING-PRIME-SC-BP-700 N	7452 lm	62 W	4
46	RVE	RVE-LBX-RING-PRIME-SC-BP-900-P (52%)	6371 lm	53 W	6
22	RVE	RVE-PLY3575-PRIME-SC-2000-K	4375 lm	48 W	6
5	RVE	RVE-PLY3070-GEARLINE-SC-540-P-IP54 (47%)	1705 lm	16 W	2
1011	RVE	RVE-PLY3070-GEARLINE-SC-IP54-980-P	2370 lm	26 W	2

Перечень оборудования указателей
Лист 5

Условное обозначение	Производитель	Наименование	Артикул	Цвет корпуса	Габариты, мм	Мощность, Вт	Степень защиты, IP	Кол-во, шт
3	ООО "Галочка Дубровицы" ул. ∞	Светодиод указатель постоянного действия EVAC 3.2x2x0.5V 3Вт 2D EMS мин - EXIT left	4600-000-05091	Белый	340x150x41	3	20	1
4	ООО "Галочка Дубровицы" ул. ∞	Светодиод указатель постоянного действия EVAC 3.2x2x0.5V 3Вт 2D EMS мин - EXIT right	4600-000-05092	Белый	340x150x41	3	20	1
1	ООО "Галочка Дубровицы" ул. ∞	Светодиод указатель постоянного действия EVAC 3.2x2x0.5V 3Вт 2D EMS мин - EXIT straight	4600-000-05093	Белый	340x150x41	3	20	2

Экспликация помещений 5 этажа

Номер поэт.	Наименование	Площадь, м2	Кат. поэт.
501	Лестничная клетка тип Л1	38,72	
502	Кабинет иностранного языка для подгруппы	28,66	
503	Учебный кабинет для изучения естествознания (химии)	79,11	
504	Лаборантская кабинета химии	19,17	В3
505	Серверная	8,77	В4
506	Кабинет информационных технологий	131,15	
507	Кабинет географии	62,36	
508	Кабинет русского и литературы	66,13	
509	Лестничная клетка тип Л2	23,94	
510	Лабораторная кабинета физики	85,30	В3
511	Учебные кабинеты для изучения естественных физика	86,65	
512	Холл	4,90	В4
513	Санузел для мальчиков	20,87	
514	Кабинет иностранного языка для подгруппы	37,15	
515	Коридор	205,54	
516	Санузел для девочек с комнатой личной гигиены	17,88	
517	Санузел для персонала	3,67	
		844,57 м²	

Условные обозначения

- Выключатель 1кл IP20
- Выключатель 2кл IP20
- Выключатель 2кл IP20
- Выключатель 3кл IP20

Изм.	Кол.уч.	Лист	№док.	Подп.	Дата	2024-00375-01-0-ИОС1			
Гип	Тельцер				07.2024	Капитальный ремонт общеобразовательного бюджетного учреждения города Москвы «Школа № 1234» по адресу: г. Москва, Северянинский пер., д. 8			
Нач.отд.	Семенов				07.2024		Стадия	Лист	Листов
Разраб.	Тельцер				07.2024	Система электроснабжения	П	54	
Н. контр.	Тельцер				07.2024	План этажа 5 этажа	МОСКИЛ НИИПРОЕКТ		
Нач. ОПИК	Капустин				07.2024				

Формат А2 x

Инв.№ подл. | Подпись и дата | Взам.инв.№

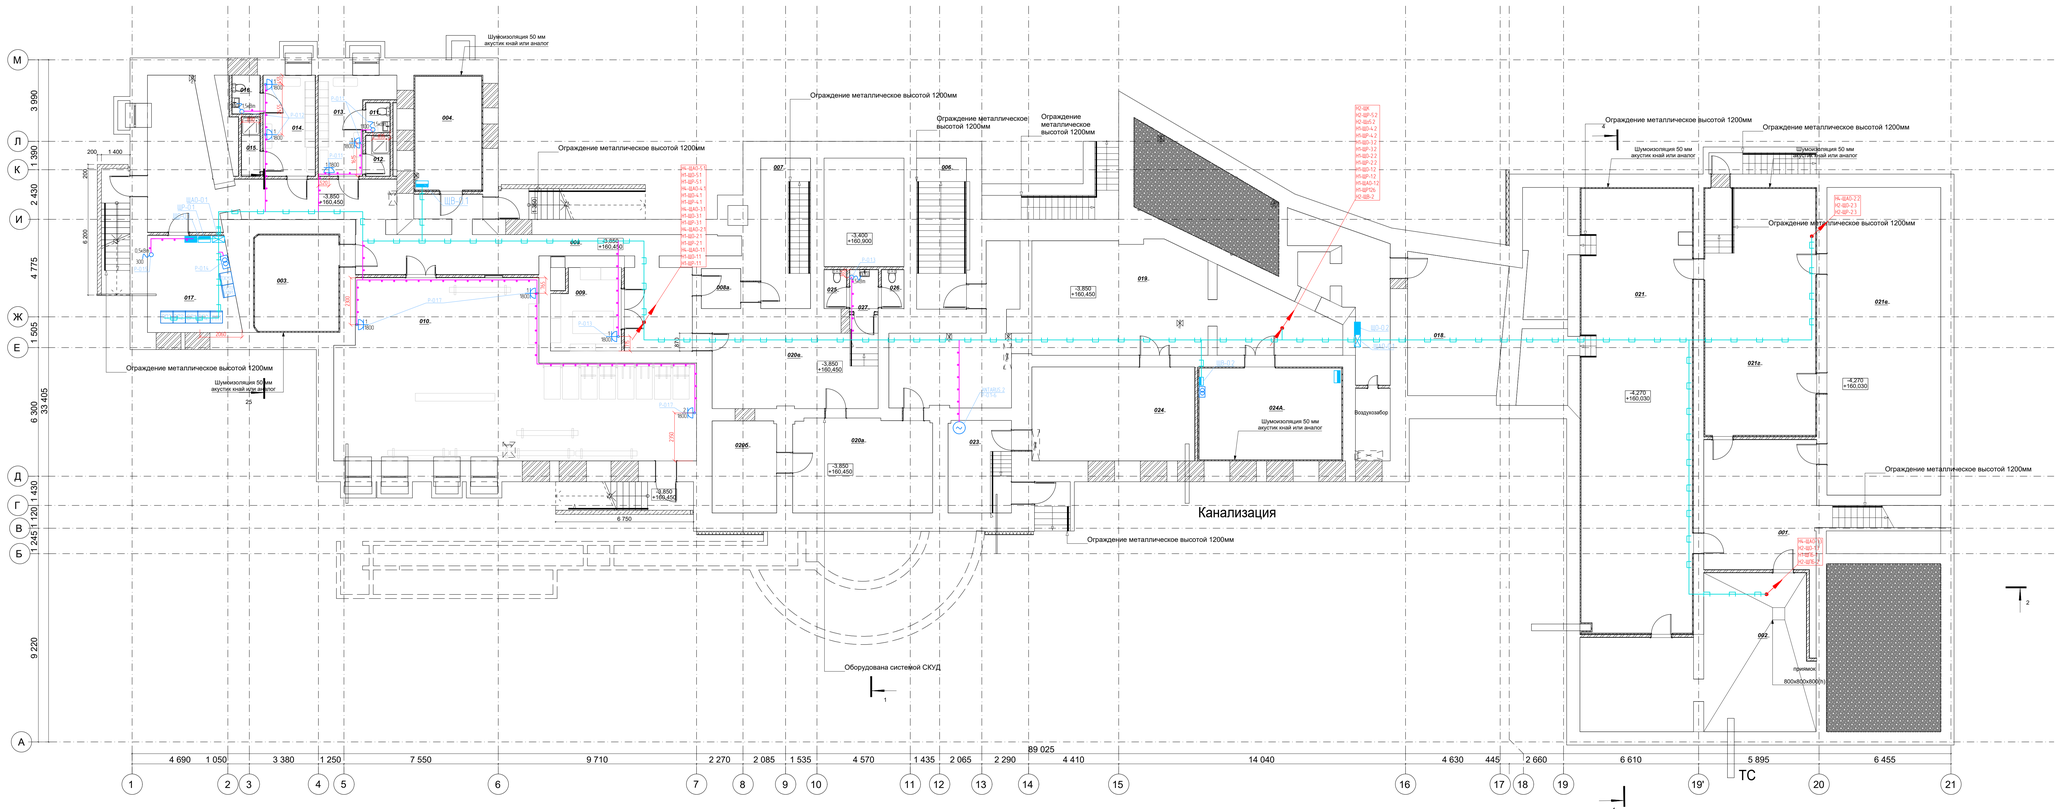
Ограждение металлическое высотой 1200мм
Шумоизоляция 50 мм акустик кний или аналог
Канализация
Оборудована системой СКУД
Воздухозабор
ТС
приямок 800х800х800(h)
-3.850 +160.450
-3.400 +160.900
-4.270 +160.030
-2.850 +161.450
А1-ШО-1
А2-ШО-1
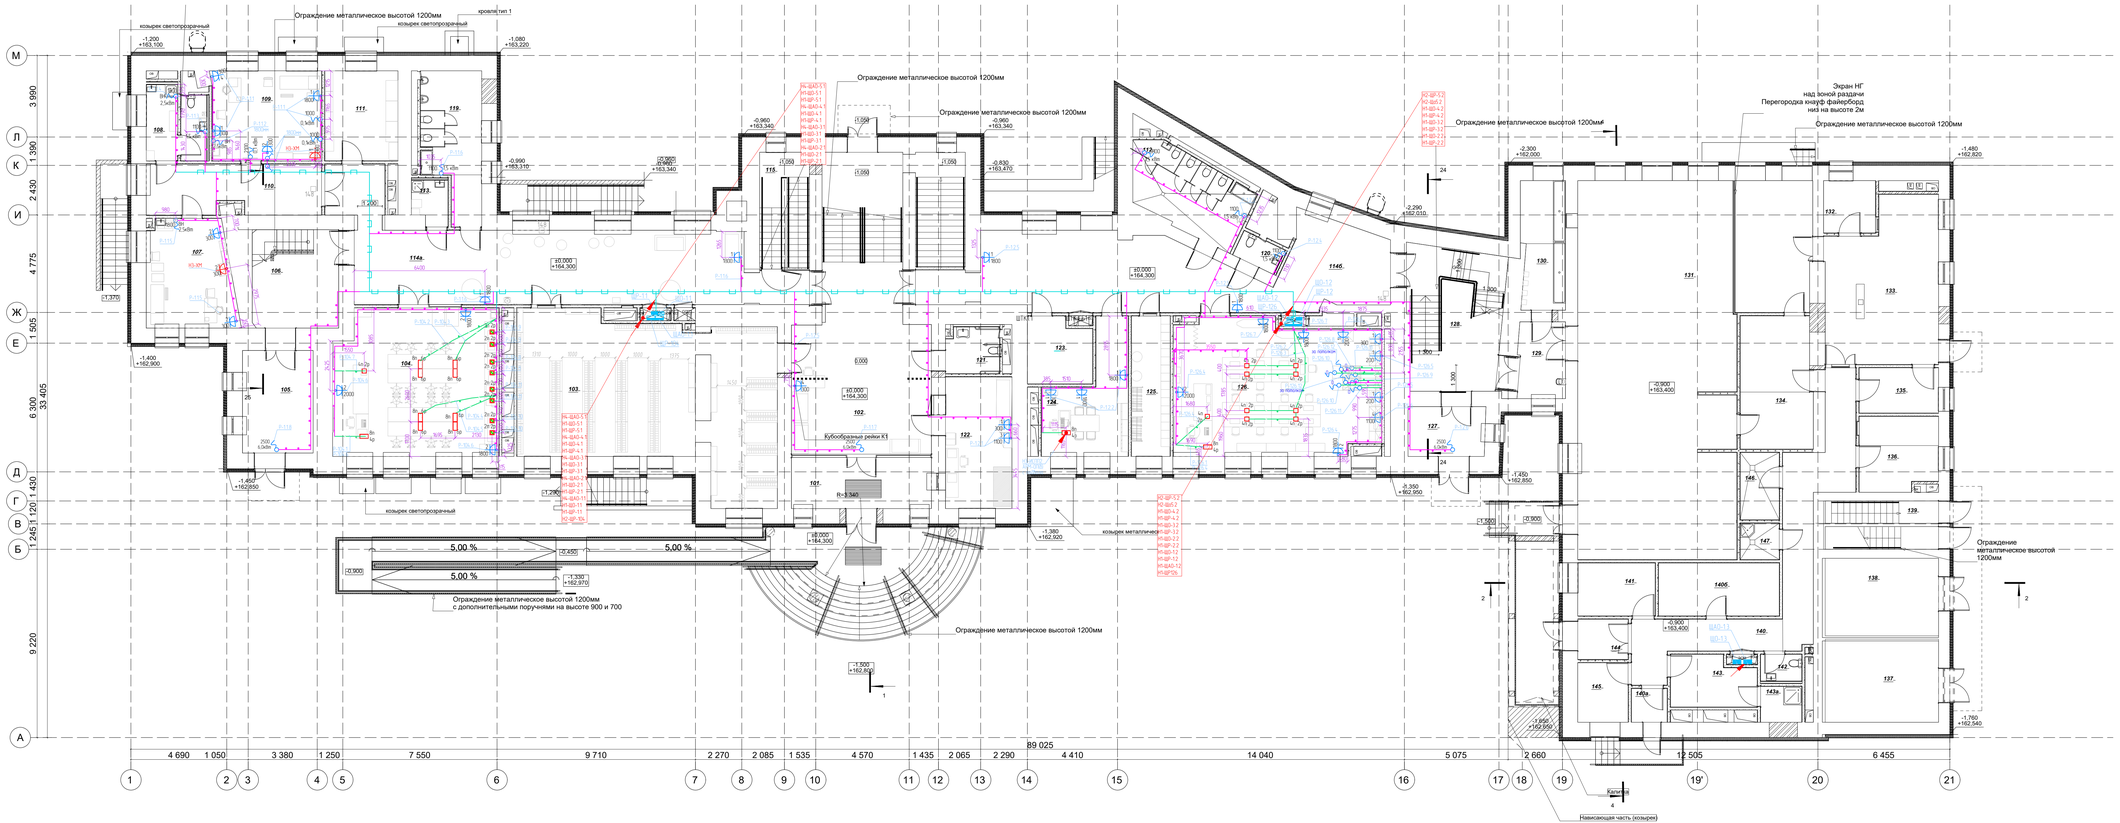

Экспликация помещений 1 этажа

Номер пом.	Наименование	Площадь, м2	Кат. пом.
101	Тамбур	18,09	
102	Вестибюль	79,49	
103	Гардеробная для обучающихся	94,58	
104	Учебный кабинет	57,67	
105	Тамбур	18,37	
106	Лестничная клетка тип Н2	22,57	
107	Процедурный (прививочный) кабинет	22,14	
108	Место для приготовления дезинфицирующих растворов и хранения уборочного инвентаря	10,35	В4
109	Кабинет врача	23,64	
110	Зона ожидания посетителей	20,55	
111	Кладовая	15,75	В3
112	Санузел для девочек с комнатой личной гигиены	7,99	
113	ПУИ	3,70	В4
114а	Коридор	83,40	
114б	Коридор	75,18	
115	Технологическая лестница	13,98	
119	Санузел для мальчиков	5,69	
120	Санузел для персонала	3,40	
121	Санузел для МГН	6,40	
122	Комната охраны	20,95	
123	Кроссовая	9,82	В4
124	Административный кабинет тип 1	19,95	
125	Гардеробная комната для учителей	13,02	
126	Учебный кабинет	65,15	
127	Тамбур	10,38	
128	Лестничная клетка тип Л1	33,63	
129	Коридор	10,06	
130	Умывальная	13,97	
131	Обеденный зал	169,16	
132	Холодный цех	6,57	В4
133	Горячий цех	41,96	В3
134	Моечная столовой посуды	23,00	В4
135	Моечная кухонной посуды	8,66	В4
136	Доготовочный цех	13,73	В3
137	Техническое помещение (электрощитовая)	23,30	В3
138	Техническое помещение (электрощитовая)	21,83	В3
139	Лестничная клетка лип Л1	13,32	
140	Коридор	40,06	
140а	Тамбур	3,45	
1406	помещение холодильного оборудования	15,31	В3
141	Кладовая сухих продуктов	9,82	В4
142	Санузел	2,68	
143	Помещение для персонала	9,91	
143а	Душ	3,52	
144	Загрузочный цех	5,78	В4
145	Кладовая и моечная оборотной тары	7,17	В4
146	Помещение для временного хранения пищевых отходов	6,35	В4
147	ПУИ	3,46	В4
		1 208,91 м²	

Условные обозначения

- Вывод кабеля 220В
- Ящик IP44 В полу с розетками орм. SPL 3000** WP с розетками SPL орм.200013
- Розетка IP20
- Прокладка кабеля в металлическом лотке под потолком
- Прокладка кабеля в пластиковой трубе в полу к лоткам
- Прокладка кабеля в гофрированной трубе

кол. постов в лотке
кол. розеток 3ОМ в лотке
8n 4p
кол-во розеток
высота спецобор.
2,2000

						2024-00375-01-0-ИОС1	
						Капитальный ремонт здания Государственного бюджетного общеобразовательного учреждения города Москвы «Школа № 1574» по адресу: г. Москва, Спортивный пер. д. №5	
Изм.	Кол.уч.	Лист	№док.	Подп.	Дата		
Разраб.		Семёнов			07.2025	Стадия	Лист	Листов
Провер.		Ульянцев М.Н.			07.2025	Система электроснабжения	П	56
Н. контр.		Ульянцев М.Н.			07.2025			
Нач. ОПИС №1		Белошапка В.П.			07.2025	Силовое электрооборудование. План 1 этажа	МОСЖИЛ НИИПРОЕКТ	

Инв.№ подл. | Подпись и дата | Взам. инв.№ | Инв.№ дубл. | Подпись и дата

Формат А2 х 3

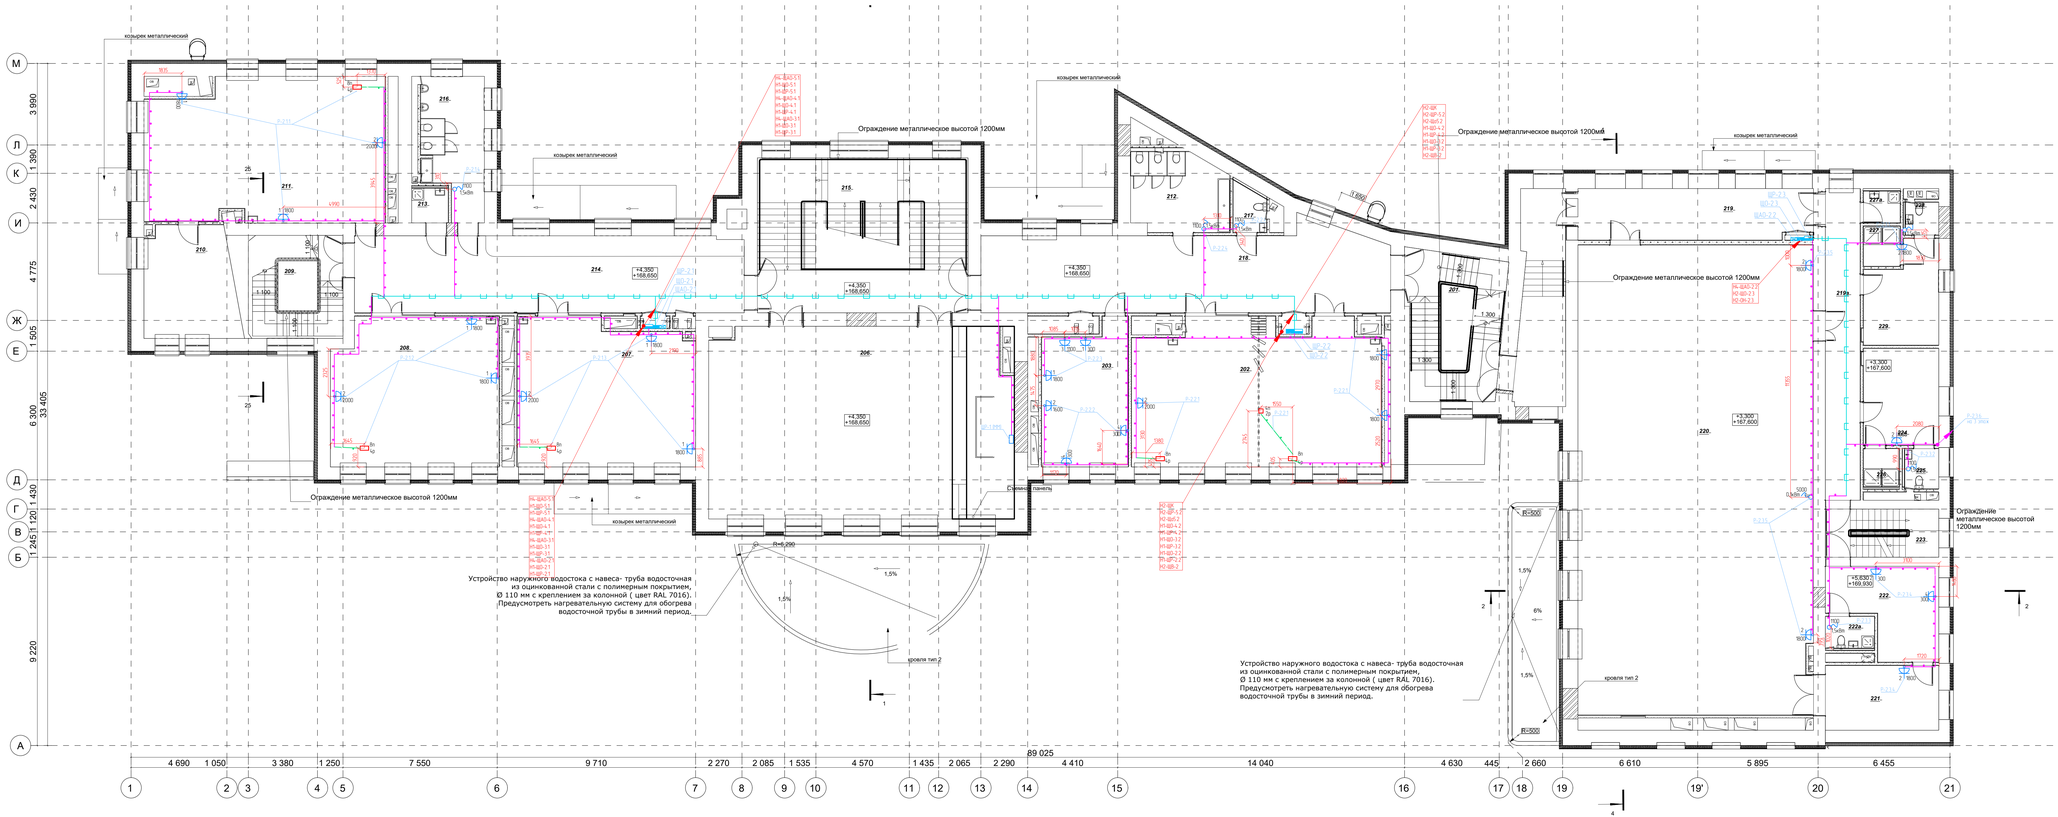

Экспликация помещений 2 этажа

Номер пом.	Наименование	Площадь, м2	Кат. пом.
201	Лестничная клетка тип Л1	33,37	
202	Кабинет иностранного языка	84,57	
203	Рабочее пространство для учителей тип 2	28,30	
206	Актовый зал	139,32	
207	Учебный кабинет	60,84	
208	Учебный кабинет	59,26	
209	Лестничная клетка Л1	23,31	
210	Кладовая инвентаря творческой мастерской	24,19	В3
211	Кабинет ИЗО	79,82	
212	Санузел для девочек	6,89	
213	ПУИ	3,61	В4
214	Коридор	61,13	
215	Вестибюль	79,16	
216	Санузел для мальчиков	5,90	
217	Санузел для персонала	3,48	
218	Коридор	78,84	
219	Коридор	53,72	
219а	Коридор	26,29	
220	Спортивный зал	265,70	
221	Снарядная	18,52	В3
222	Комната инструктора	20,28	
222а	Душ с санузлом	3,77	
223	Лестничная клетка тип Л1	13,13	
224	Раздевальная	17,52	
225	Санузел	3,31	
226	Душевая	3,31	
227	Душевая	3,57	
227а	ПУИ	2,84	В4
228	Санузел	2,66	
229	Раздевальная	16,33	
		1 222,94 м²	

Условные обозначения

- Вывод кабеля 220В
- 8n Ln — Люк IP44 в полу с розетками орп. SPL 3000** WP с розетками SPL орп.200013
- Розетка IP20
- Прокладка кабеля в металлическом лотке под полом
- Прокладка кабеля в пластиковой трубе в полу к лючкам
- Прокладка кабеля в гофрированной трубе

								2024-00375-01-0-ИОС1	
								Капитальный ремонт здания Государственного бюджетного общеобразовательного учреждения города Москвы «Школа № 1574» по адресу: г. Москва, Старопетровский пер. д. №5	
Изм.	Кол.уч.	Лист	№док.	Подп.	Дата				
Разраб.		Семёнов			02.2025	Стадия	Лист	Листов	
Гл.спец.		Ульянцев М.Н.			02.2025				
Н. контр.		Ульянцев М.Н.			02.2025	Система электроснабжения	П	57	
Рук. ГИП		Белошапка В.П.			02.2025	Силовое электрооборудование. План 2 этажа	МОСЖИЛ НИИПРОЕКТ		

Инв.№ подл. | Подпись и дата | Взам.инв.№ | Дубл.инв.№

Формат А2 х 3

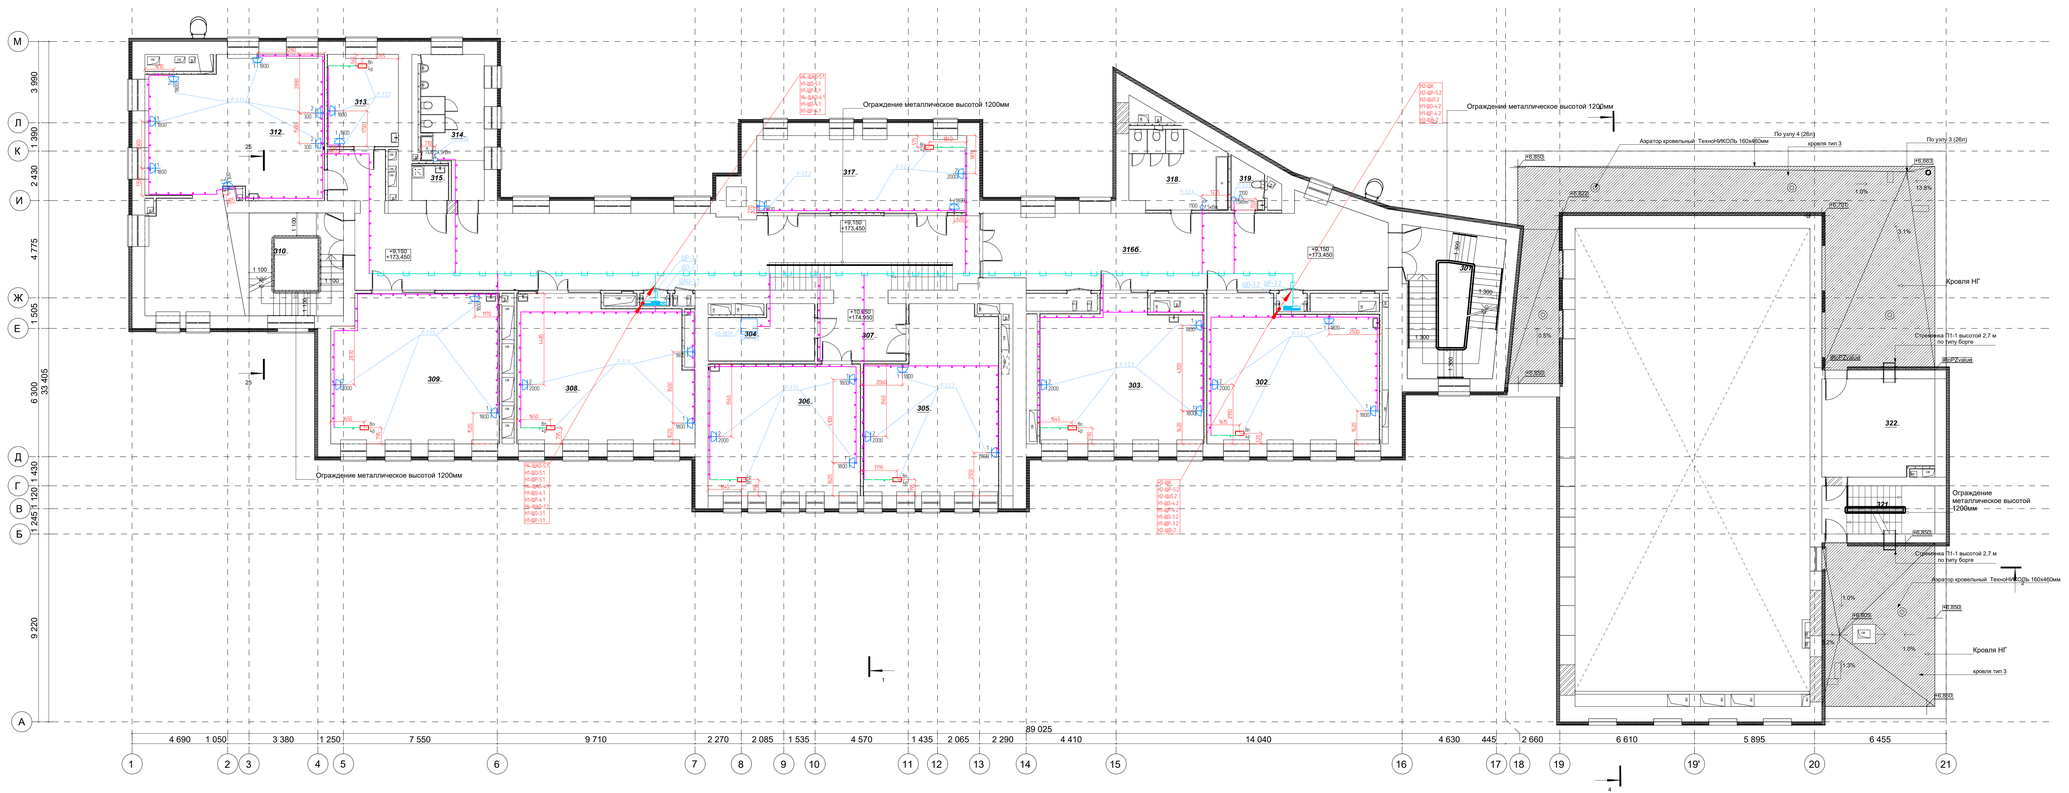

Экспликация помещений 3 этажа

Номер пом.	Наименование	Площадь, м2	Кат. пом.
301	Лестничная клетка тип Л1	33,37	
302	Учебный кабинет	57,24	
303	Учебный кабинет	53,44	
304	Серверная	12,66	В3
305	Учебный кабинет	55,09	
306	Учебный кабинет	48,33	
307	Коридор	137,41	
308	Учебный кабинет	59,17	
309	Учебный кабинет	59,25	
310	Лестничная клетка тип Н2	23,38	
312	Библиотека	83,05	В3
313	Кабинет для индивидуальных занятий в т-ч с учителем -логопедом	15,77	
314	Санузел для мальчиков	19,83	
315	ПУИ	3,58	В4
3166	Коридор	76,16	
317	Кабинет иностранного языка	39,23	
318	Санузел для девочек	17,74	
319	Санузел для персонала	3,69	
321	Лестничная клетка тип Л1	13,13	
322	Техническое помещение	26,05	В3
		837,57 м²	

Условные обозначения

- Выход кабеля 220В
- 8п 4ф — Люк IP44 в полу с розетками орп. SPL 3000** WP с розетками SPL орп.200013
- Розетка IP20
- Прокладка кабеля в металлическом лотке под потолком
- Прокладка кабеля в пластиковой трубе в полу к лючкам
- Прокладка кабеля в гофрированной трубе

кол. постов 8 лючке; кол. розеток 3ОМ 5 лючке; 8п 4ф; кол.п розеток; высота спецработ; 2,2000

Изм.	Кол.уч.	Лист	№док.	Подп.	Дата
ГИП		Сенько			07.2025
Разраб.		Пальцун М.Н.			07.2025
Н. контр.		Пальцун М.Н.			07.2025
Рук. ГПИС №1		Белошапка В.П.			07.2025

2024-00375-01-0-ИОС1

Капитальный ремонт здания Государственного бюджетного общеобразовательного учреждения города Москвы «Школа № 1574» по адресу: г. Москва, Старопетровский пер., д. №5

Система электроснабжения

Стадия	Лист	Листов
П	58	

Силовое электрооборудование. План 3 этажа

МОСЖИЛ НИИПРОЕКТ

Формат А2 х 3

Инв.№ подл. | Подпись и дата | Взам.инв.№ | Согласовано

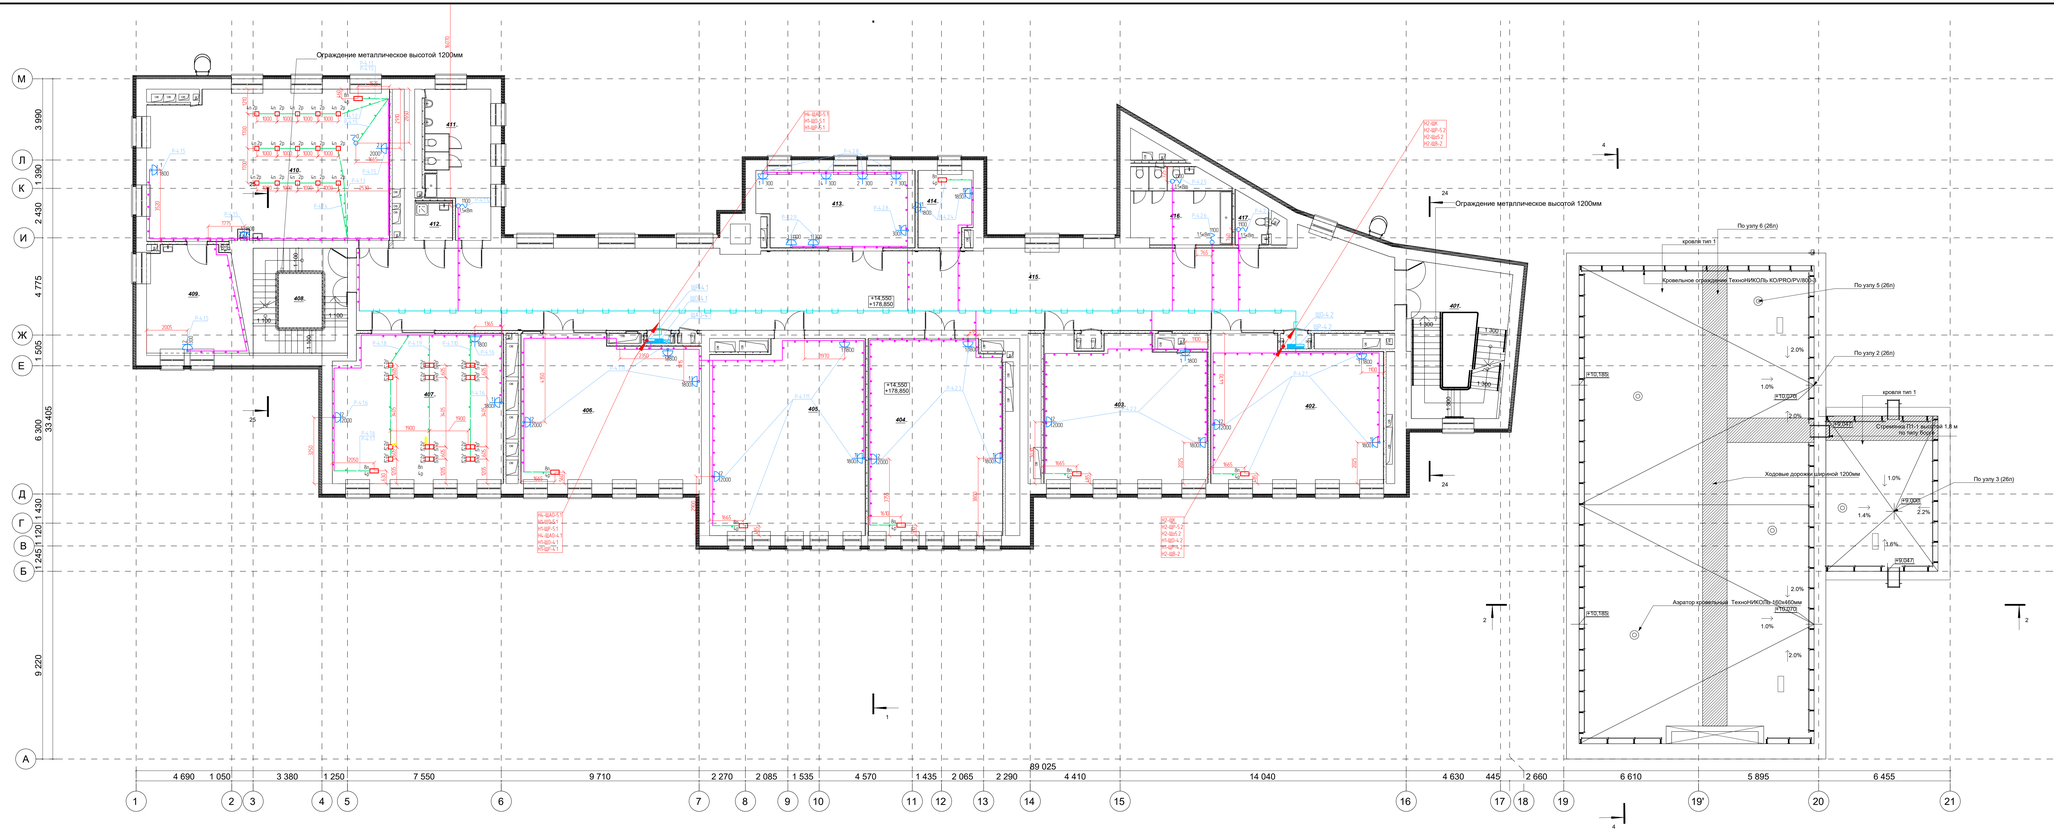

Экспликация помещений 4 этажа			
Номер пом.	Наименование	Площадь, м2	Кат. пом.
401	Лестничная клетка тип Л1	35,72	
402	Кабинет русского языка и литературы	57,81	
403	Кабинет русского языка и литературы	55,37	
404	Кабинет истории тип 1	63,17	
405	Кабинет математики	71,92	
406	Кабинет математики	62,41	
407	ОБЗР	60,29	
408	Лестничная клетка тип Н2	24,40	
409	Лаборантская кабинета биологии	24,33	В3
410	Учебные кабинеты для изучения естествознания: биологии/ПИК	86,65	
411	Санузел для мальчиков	21,05	
412	ПУИ	3,67	В4
413	Административный кабинет тип 1	28,57	
414	Кабинет для индивидуальных занятий в тч с педагогом-психологом	9,72	
415	Коридор	206,03	
416	Санузел для девочек с комнатой личной гигиены	17,93	
417	Санузел для персонала	3,72	
		832,76 м²	

Условные обозначения

- Выход кабеля 220В
- Ящик IP44 в полу с розетками орт. SPL 3000** WP с розетками SPL орт.200013
- Розетка IP20
- Прокладка кабеля в металлическом лотке под потолком
- Прокладка кабеля в пластиковой трубе в полу к лючкам
- Прокладка кабеля в гофрированной трубе

					2024-00375-01-0-ИОС1
Изм.	Кол.уч.	Лист	№док.	Подп.	Дата
Разраб.		Синяев			12.2025
Пров.		Пальцун М.Н.			12.2025
Н. контр.		Пальцун М.Н.			12.2025
Нач. ОПИС №1		Белошова В.П.			12.2025

Капитальный ремонт здания Государственного бюджетного общеобразовательного учреждения города Москвы «Школа № 1574» по адресу: г. Москва, Спиридоньевский пер., д. №5

Стадия	Лист	Листов
П	59	

Система электроснабжения

Силовое электрооборудование. План 4 этажа

МОСЖИЛ НИИПРОЕКТ

Формат А2 х 3

Инв.№ подл. | Подпись и дата | Взам. инв.№ | Подпись и дата

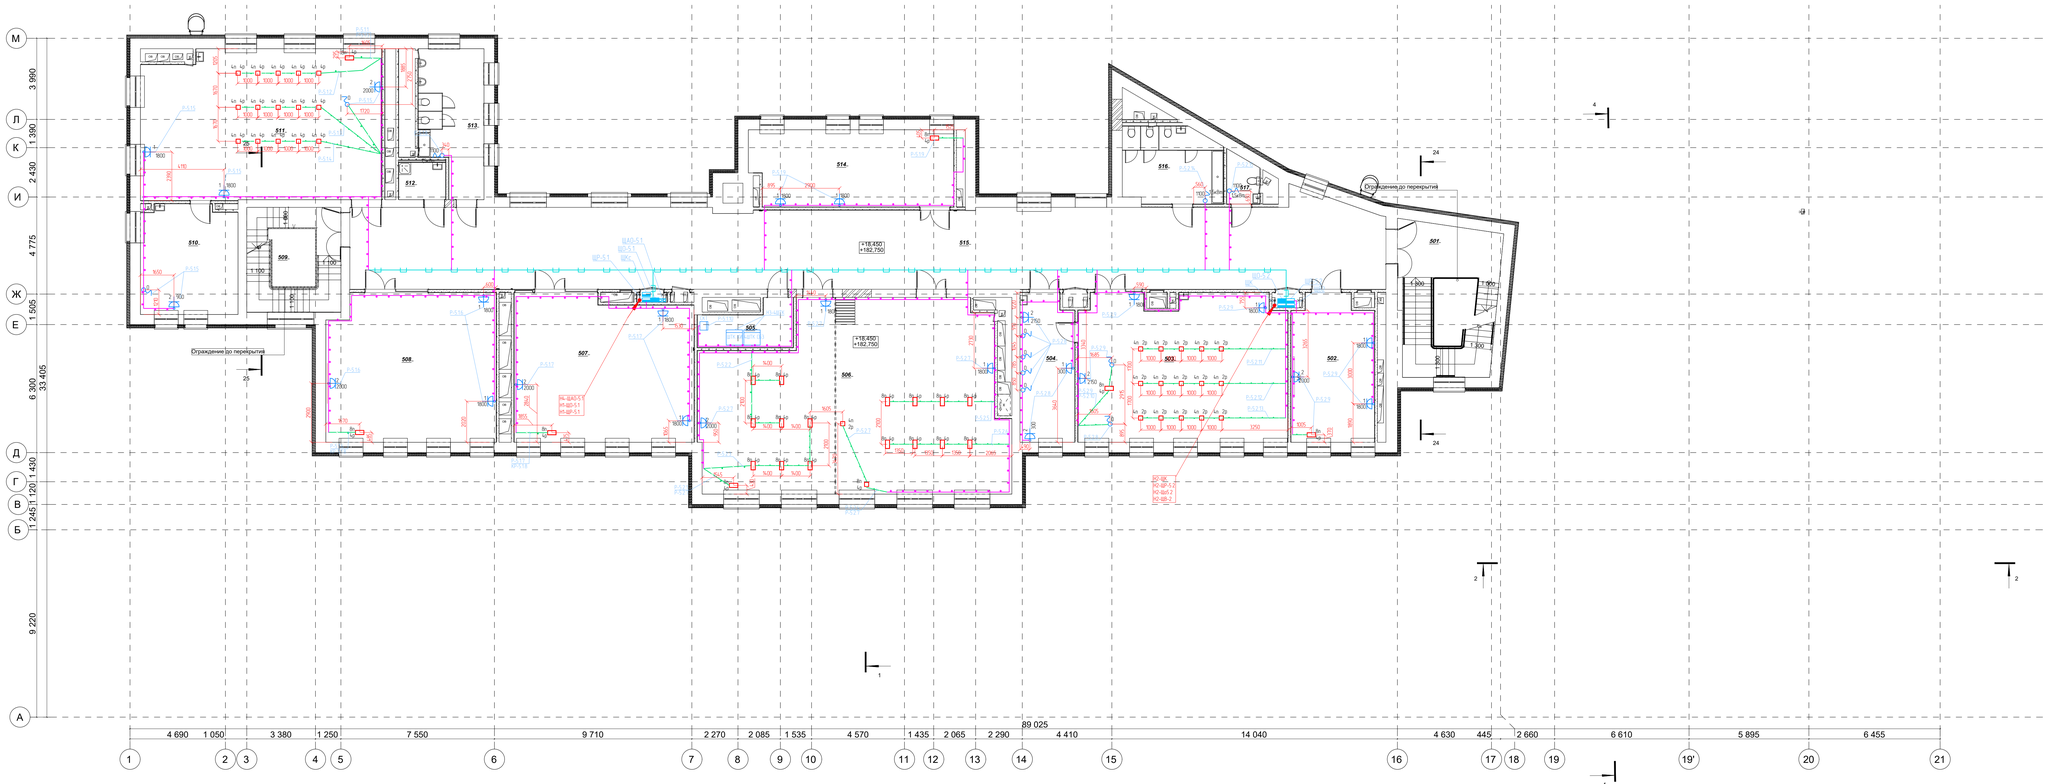

Экспликация помещений 5 этажа

Номер пом.	Наименование	Площадь, м2	Кат. пом.
501	Лестничная клетка тип Л1	35,72	
502	Кабинет иностранного языка для подгруппы	28,66	
503	Учебный кабинет для изучения естествознания (химия)	73,11	
504	Лаборантская кабинета химии	19,17	В3
505	Серверная	8,77	В4
506	Кабинет информационных технологий	131,15	
507	Кабинет географии	62,36	
508	Кабинет русского и литературы	60,13	
509	Лестничная клетка тип Н2	23,94	
510	Лаборантская кабинета физики	25,30	В3
511	Учебные кабинеты для изучения естествознания: физика	86,65	
512	ПУИ	4,50	В4
513	Санузел для мальчиков	20,87	
514	Кабинет иностранного языка для подгруппы	37,15	
515	Коридор	205,54	
516	Санузел для девочек с комнатой личной гигиены	17,88	
517	Санузел для персонала	3,67	
		844,57 м²	

Условные обозначения

- Выход кабеля 220В
- 8n Lp — Люкс IP44 8 полу с розетками орп. SPL 3000** WP с розетками SPL орп.200013
- Розетка IP20
- Прокладка кабеля в металлическом лотке под потолком
- Прокладка кабеля в пластиковой трубе в полу к люкам
- Прокладка кабеля в гофрированной трубе
- кол. постов 8 лючке
- кол. розеток 30M 8 лючке
- 8n 4p
- кол-во розеток
- высота спецработ
- 2,2000

					2024-00375-01-0-ИОС1
Изм.	Кол.уч.	Лист	№док.	Подп.	Дата
Разраб.		Семенов			12.2025
Гл.спец.		Ульянцев М.Н.			12.2025
Н. контр.		Ульянцев М.Н.			12.2025
Рук. ГИП		Белошапка В.П.			12.2025

Капитальный ремонт здания Государственного бюджетного общеобразовательного учреждения города Москвы «Школа № 1574» по адресу: г. Москва, Спортивно-техническая пер. д. №5

Система электроснабжения

Стадия	Лист	Листов
П	60	

Силовое электрооборудование. План 5 этажа

МОСЖИЛ НИИПРОЕКТ

Формат А2 х 3

Инв. № подл. | Подпись и дата | Взам. инв.№ | Подпись и дата

Экспликация помещений 1 этажа			
Номер		Площадь,	Кат.
131	Обеденный зал	169,16	
132	Холодный цех	6,57	В4
133	Горячий цех	41,96	В3
134	Моечная столовой посуды	23,00	В4
135	Моечная кухонной посуды	8,66	В4
136	Доготовочный цех	13,73	В3
137	Техническое помещение (электрощитовая)	23,30	В3
138	Техническое помещение (электрощитовая)	21,83	В3
139	Лестничная клетка лип Л1	13,32	
140	Коридор	40,06	
140а	Тамбур	3,45	
140б	помещение холодильного оборудования	15,31	В3
141	Кладовая сухих продуктов	9,82	В4
142	Санузел	2,68	
143	Помещение для персонала	9,91	
143а	Душ	3,52	
144	Загрузочный цех	5,78	В4
145	Кладовая и моечная оборотной тары	7,17	В4
146	Помещение для временного хранения пищевых отходов	6,35	В4
147	ПУИ	3,46	В4
		1 208,91 м²	

Условные обозначения

- Выход кабеля
- Розетка IP54
- Прокладка кабеля в металлическом лотке под потолком
- Прокладка кабеля в металлической трубе в полу
- Прокладка кабеля в гофрированной трубе

Согласовано

Взам. инв.N

Подпись и дата

Инв.N подл.

						2024-00375-01-0-ИОС1	
						Капитальный ремонт здания Государственного бюджетного общеобразовательного учреждения города Москвы «Школа № 1574» по адресу: г. Москва, Старопименовский пер., д. №5	
Изм.	Кол.уч.	Лист	№док.	Подп.	Дата		
Разраб.		Семенов			02.2025	Система электроснабжения	Стадия: П; Лист: 61; Листов:
Провер.		Пильгуй М.Н.			02.2025		
Н. контр.		Пильгуй Н.М.			02.2025	Силовое электрооборудование. План пищеблока	МОСЖИЛ НИИПРОЕКТ
Нач. ОПИС №1		Белоусова Д.П.			02.2025		

Формат А1 x 1

ПЛАН КРОВЛИ

М1:100

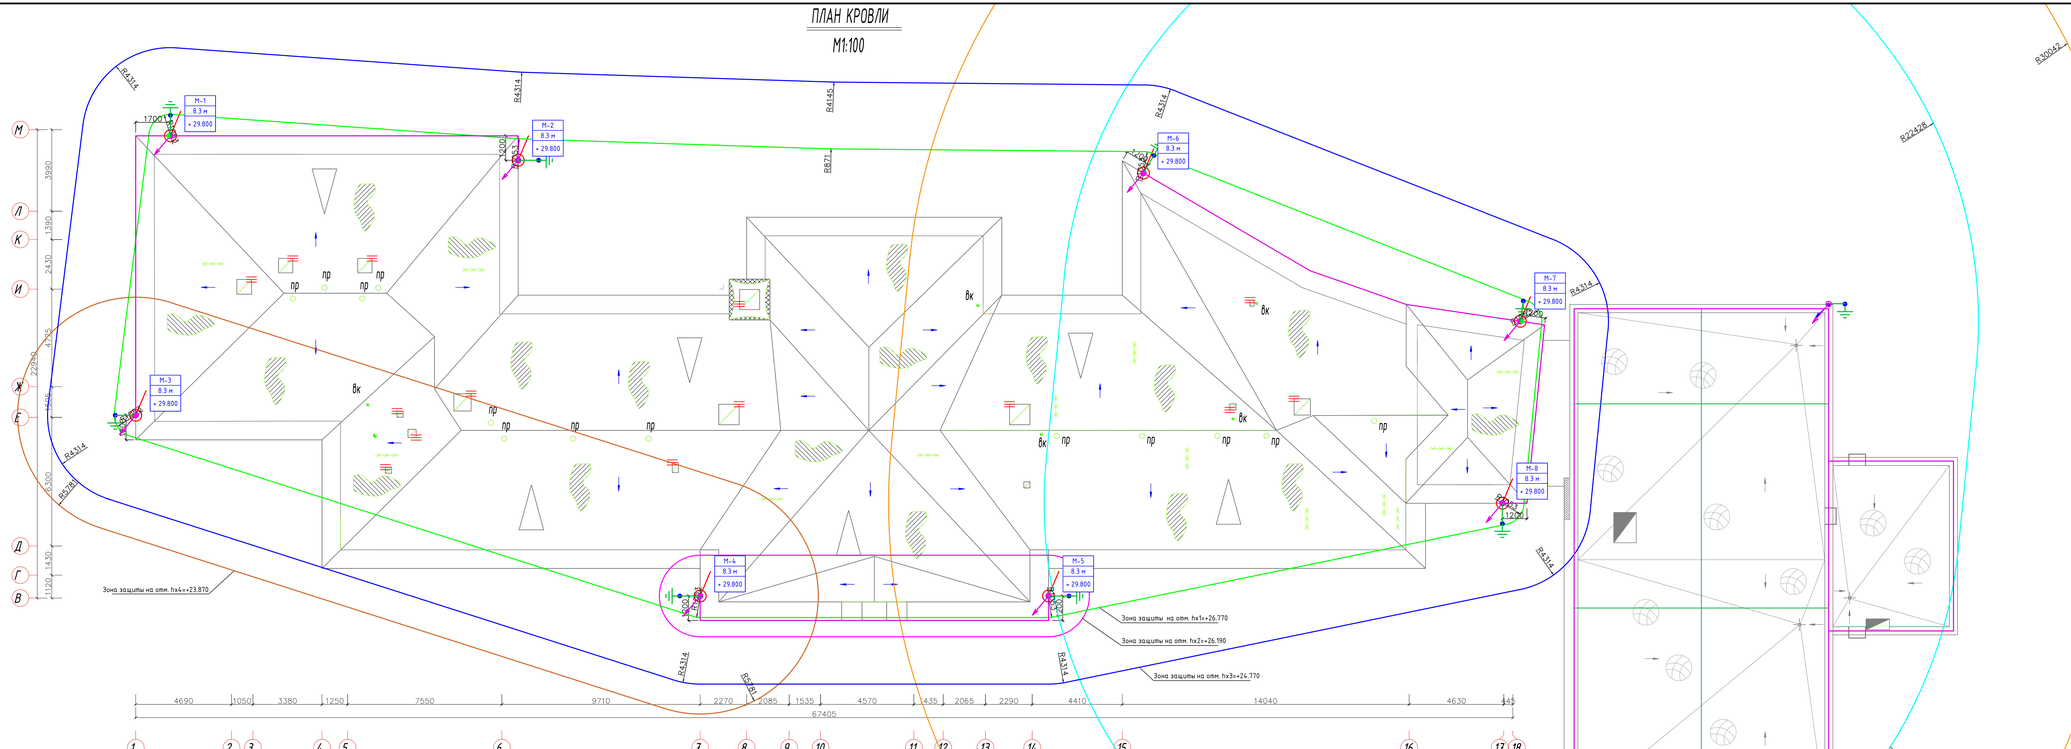

Узлы крепления ZANDZ

Крепление молниеприемника на стене

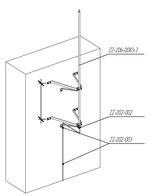

Соединение проводника в узле пересечения токоотводов

Организация крепления проводника на стене

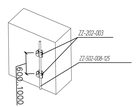

Спуск токоотвода к заземляющему устройству

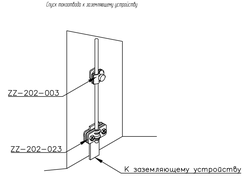

Условные обозначения:

- стержневой молниеприемник;
- Присоединение к существующему контуру заземления;
- пруток по кровле на держателях ZZ-202-005;
- токоотвод по стене на зажимах ZZ-202-003;
- зажим для подключения проводника (ZZ-202-022);
- зажим контрольный (проволока+полоса) (ZZ-202-023);
- зажим для соединения токоотводов (ZZ-202-021);
- спуск токоотвода по стене на зажимах ZZ-202-003

Мероприятия выполнены в соответствии с ПУЭ 7-е изд. Глава 1.7, СО 153-34.21.122-2003 «Инструкция по устройству молниезащиты зданий, сооружений и промышленных коммуникаций» (далее СО) и РД 34.21.122-87 «Инструкция по устройству молниезащиты зданий и сооружений» (далее РД).
Защищаемое сооружение относится к III категории молниезащиты в соответствии с СО. Защита зданий от разрядов молнии осуществляется с помощью молниеотводов.
Комплекс мероприятий по обеспечению необходимых требований к системе молниезащиты представлен следующими решениями:
- установка 8 стержневых молниеприемников высотой 8,3 м на стене. Учтено, что 1,5 м длины стержня уходит на крепление;
- молниеприемники соединяются между собой для организации двух токоотводов с применением оцинкованной проволоки Ø=8 мм от каждого молниеприемника;
- крепление токоотводов производится через установки 0,6-1 м): на стене с помощью зажимов ZZ-202-003;
- соединение и разветвление токоотводов производится с использованием зажимов ZZ-202-021.
Подключение токоотводов осуществляется к существующему контуру заземления. Соединение токоотводов с полосой существующего контура заземления осуществляется с помощью зажимов ZZ-202-023.
Расчет зон защиты стержневых молниеприемников представлен на листе 60

						2024-00375-01-0-ИОС1	
						Капитальный ремонт здания Государственного бюджетного общеобразовательного учреждения города Москвы «Школа № 1574» по адресу: г. Москва, Спортивный пер. д. №5	
Изм.	Кол.уч.	Лист	№док.	Подп.	Дата		
Разраб.		Семёнов			12.2024	Стадия	Лист	Листов
Провер.		Ульянцев М.Н.			12.2024	Система электроснабжения	П	62
Н. контр.		Ульянцев М.Н.			12.2024	План молниезащиты и заземления	МОСЖИЛ НИИПРОЕКТ	
Нач. ГИП (МИС №1)		Безносиков В.П.			12.2024			

Инв.№ подл. | Подпись и дата | Взам. инв.№ | Инв.№ дубл. | Подпись и дата

Формат А2 х 3

Расчет зон защиты стержневых молниеотводов

hx1=+26,770	
Двойной стержневой молниеотвод	M1-M2
Высота молниеприемника от земли до вершины h, м	29.8
Расстояние между молниеприемниками L, м	17.062
Высота защищаемого объекта hx, м	26.77
Высота конуса зоны защиты, h0=0,92h, м	27.416
Радиус конуса зоны защиты, r0=1,5h, м	44.7
rx =1,5(h-hx/0,92), м	1.053
hc=h0, м	27.416
rc=r0, м	44.7
Радиус зоны посередине между молниеприемниками rcx=rx	1.053
Двойной стержневой молниеотвод	M1-M3
Высота молниеприемника от земли до вершины h, м	29.8
Расстояние между молниеприемниками L, м	13.795
Высота защищаемого объекта hx, м	26.77
Высота конуса зоны защиты, h0=0,92h, м	27.416
Радиус конуса зоны защиты, r0=1,5h, м	44.7
rx =1,5(h-hx/0,92), м	1.053
hc=h0, м	27.416
rc=r0, м	44.7
Радиус зоны посередине между молниеприемниками rcx=rx	1.053
Двойной стержневой молниеотвод	M2-M6
Высота молниеприемника от земли до вершины h, м	29.8
Расстояние между молниеприемниками L, м	30.612
Высота защищаемого объекта hx, м	26.77
Высота конуса зоны защиты, h0=0,92h, м	27.416
Радиус конуса зоны защиты, r0=1,5h, м	44.7
rx =1,5(h-hx/0,92), м	1.053
hc=h0-0,14(L-h), м	27.30232
rc=r0, м	44.7
Радиус зоны посередине между молниеприемникамигсх=r0	0.872
Двойной стержневой молниеотвод	M3-M4
Высота молниеприемника от земли до вершины h, м	29.8
Расстояние между молниеприемниками L, м	29.013
Высота защищаемого объекта hx, м	26.77
Высота конуса зоны защиты, h0=0,92h, м	27.416
Радиус конуса зоны защиты, r0=1,5h, м	44.7
Радиус горизонтального сечения вокруг молнеприемника r	1.053
hc=h0, м	27.416
rc=r0, м	44.7
Радиус зоны посередине между молниеприемниками rcx=rx	1.053
Двойной стержневой молниеотвод	M4-M5
Высота молниеприемника от земли до вершины h, м	29.8
Расстояние между молниеприемниками L, м	17.05
Высота защищаемого объекта hx, м	26.77
Высота конуса зоны защиты, h0=0,92h, м	27.416
Радиус конуса зоны защиты, r0=1,5h, м	44.7
rx =1,5(h-hx/0,92), м	1.053
hc=h0, м	27.416
rc=r0, м	44.7
Радиус зоны посередине между молниеприемниками rcx=rx	1.053

Двойной стержневой молниеотвод	M5-M8
Высота молниеприемника от земли до вершины h, м	29.8
Расстояние между молниеприемниками L, м	22.674
Высота защищаемого объекта hx, м	26.77
Высота конуса зоны защиты, h0=0,92h, м	27.416
Радиус конуса зоны защиты, r0=1,5h, м	44.7
=1,5(h-hx/0,92), м	1.053
hc=h0, м	27.416
rc=r0, м	44.7
rcx=rx, м	**1.0532609**
Двойной стержневой молниеотвод	M6-M7
Высота молниеприемника от земли до вершины h, м	29.8
Расстояние между молниеприемниками L, м	19.821
Высота защищаемого объекта hx, м	26.77
Высота конуса зоны защиты, h0=0,92h, м	27.416
Радиус конуса зоны защиты, r0=1,5h, м	44.7
=1,5(h-hx/0,92), м	1.053
hc=h0, м	27.416
rc=r0, м	44.7
rcx=rx, м	1.053
Двойной стержневой молниеотвод	M7-M8
Высота молниеприемника от земли до вершины h, м	29.8
Расстояние между молниеприемниками L, м	8.954
Высота защищаемого объекта hx, м	26.77
Высота конуса зоны защиты, h0=0,92h, м	27.416
Радиус конуса зоны защиты, r0=1,5h, м	44.7
=1,5(h-hx/0,92), м	1.053
hc=h0, м	27.416
rc=r0, м	44.7
rcx=rx, м	1.053
hx2=+26,190	
Двойной стержневой молниеотвод	M4-M5
Высота молниеприемника от земли до вершины h, м	29.8
Расстояние между молниеприемниками L, м	17.05
Высота защищаемого объекта hx, м	26.19
Высота конуса зоны защиты, h0=0,92h, м	27.416
Радиус конуса зоны защиты, r0=1,5h, м	44.7
=1,5(h-hx/0,92), м	1.999
hc=h0, м	27.416
rc=r0, м	44.7
rcx=rx, м	1.999
hx3=+24,770	
Двойной стержневой молниеотвод	M1-M2
Высота молниеприемника от земли до вершины h, м	29.8
Расстояние между молниеприемниками L, м	17.062
Высота защищаемого объекта hx, м	24.77
Высота конуса зоны защиты, h0=0,92h, м	27.416
Радиус конуса зоны защиты, r0=1,5h, м	44.7
=1,5(h-hx/0,92), м	4.314
hc=h0, м	27.416
rc=r0, м	44.7
rcx=rx, м	4.314

Двойной стержневой молниеотвод	M1-M3
Высота молниеприемника от земли до вершины h, м	29.8
Расстояние между молниеприемниками L, м	13.795
Высота защищаемого объекта hx, м	24.77
Высота конуса зоны защиты, h0=0,92h, м	27.416
Радиус конуса зоны защиты, r0=1,5h, м	44.7
Радиус горизонтального сечения вокруг молнеприемника rx =1,5(h-hx/0,92	4.314
hc=h0, м	27.416
rc=r0, м	44.7
rcx=rx, м	4.314
Двойной стержневой молниеотвод	M2-M6
Высота молниеприемника от земли до вершины h, м	29.8
Расстояние между молниеприемниками L, м	30.612
Высота защищаемого объекта hx, м	24.77
Высота конуса зоны защиты, h0=0,92h, м	27.416
Радиус конуса зоны защиты, r0=1,5h, м	44.7
Радиус горизонтального сечения вокруг молнеприемника rx =1,5(h-hx/0,92	4.314
hc=h0-0,14(L-h), м	27.302
rc=r0, м	44.7
rcx=r0(hc-hx)/hc, м	4.146
Двойной стержневой молниеотвод	M3-M4
Высота молниеприемника от земли до вершины h, м	29.8
Расстояние между молниеприемниками L, м	29.013
Высота защищаемого объекта hx, м	24.77
Высота конуса зоны защиты, h0=0,92h, м	27.416
Радиус конуса зоны защиты, r0=1,5h, м	44.7
Радиус горизонтального сечения вокруг молнеприемника rx =1,5(h-hx/0,92	4.314
hc=h0, м	27.416
rc=r0, м	44.7
rcx=rx, м	4.314
Двойной стержневой молниеотвод	M4-M5
Высота молниеприемника от земли до вершины h, м	29.8
Расстояние между молниеприемниками L, м	17.05
Высота защищаемого объекта hx, м	24.77
Высота конуса зоны защиты, h0=0,92h, м	27.416
Радиус конуса зоны защиты, r0=1,5h, м	44.7
Радиус горизонтального сечения вокруг молнеприемника rx =1,5(h-hx/0,92	4.314
hc=h0, м	27.416
rc=r0, м	44.7
rcx=rx, м	4.314
Двойной стержневой молниеотвод	M5-M8
Высота молниеприемника от земли до вершины h, м	29.8
Расстояние между молниеприемниками L, м	22.674
Высота защищаемого объекта hx, м	24.77
Высота конуса зоны защиты, h0=0,92h, м	27.416
Радиус конуса зоны защиты, r0=1,5h, м	44.7
Радиус горизонтального сечения вокруг молнеприемника rx =1,5(h-hx/0,92	4.314
hc=h0, м	27.416
rc=r0, м	44.7
rcx=rx, м	4.314

Двойной стержневой молниеотвод	M6-M7
Высота молниеприемника от земли до вершины h, м	29.8
Расстояние между молниеприемниками L, м	19.821
Высота защищаемого объекта hx, м	24.77
Высота конуса зоны защиты, h0=0,92h, м	27.416
Радиус конуса зоны защиты, r0=1,5h, м	44.7
rx =1,5(h-hx/0,92), м	4.314
hc=h0, м	27.416
rc=r0, м	44.7
rcx=rx, м	4.314
Двойной стержневой молниеотвод	M7-M8
Высота молниеприемника от земли до вершины h, м	29.8
Расстояние между молниеприемниками L, м	8.954
Высота защищаемого объекта hx, м	24.77
Высота конуса зоны защиты, h0=0,92h, м	27.416
Радиус конуса зоны защиты, r0=1,5h, м	44.7
rx =1,5(h-hx/0,92), м	4.314
hc=h0, м	27.416
rc=r0, м	44.7
rcx=rx, м	4.314
hx4=+23,870	
Двойной стержневой молниеотвод	M3-M4
Высота молниеприемника от земли до вершины h, м	29.8
Расстояние между молниеприемниками L, м	29.013
Высота защищаемого объекта hx, м	23.87
Высота конуса зоны защиты, h0=0,92h, м	27.416
Радиус конуса зоны защиты, r0=1,5h, м	44.7
rx =1,5(h-hx/0,92), м	**5.782**
hc=h0, м	27.416
rc=r0, м	44.7
rcx=rx, м	**5.782**
hx5=+13,660	
Двойной стержневой молниеотвод	M7-M8
Высота молниеприемника от земли до вершины h, м	29.8
Расстояние между молниеприемниками L, м	8.954
Высота защищаемого объекта hx, м	13.66
Высота конуса зоны защиты, h0=0,92h, м	27.416
Радиус конуса зоны защиты, r0=1,5h, м	44.7
rx =1,5(h-hx/0,92), м	22.428
hc=h0, м	27.416
rc=r0, м	44.7
rcx=rx, м	22.428
hx6=+8,990	
Двойной стержневой молниеотвод	M7-M8
Высота молниеприемника от земли до вершины h, м	29.8
Расстояние между молниеприемниками L, м	8.954
Высота защищаемого объекта hx, м	8.99
Высота конуса зоны защиты, h0=0,92h, м	27.416
Радиус конуса зоны защиты, r0=1,5h, м	44.7
rx =1,5(h-hx/0,92), м	30.042
hc=h0, м	27.416
rc=r0, м	44.7
rcx=rx, м	30.042

Гор.гл.сборочн.

Взам. инв.N

Подпись и дата

Инв.N подл.

Изм.	Кол.уч.	Лист	№док.	Подп.	Дата
Разраб.		Семенов			02.2025
Провер.		Пильгуй М.Н.			02.2025
Н. контр.		Пильгуй Н.М.			02.2025
Нач. ОПИС №1		Белоусова Д.П.			02.2025

2024-00375-01-0-ИОС1

Капитальный ремонт здания Государственного бюджетного общеобразовательного учреждения города Москвы «Школа № 1574» по адресу: г. Москва, Старопименовский пер., д №5

Система электроснабжения

Стадия	Лист	Листов
П	63	

Расчет зон защиты стержневых молниеотводов

МОСЖИЛ НИИПРОЕКТ

Формат А3 х 3

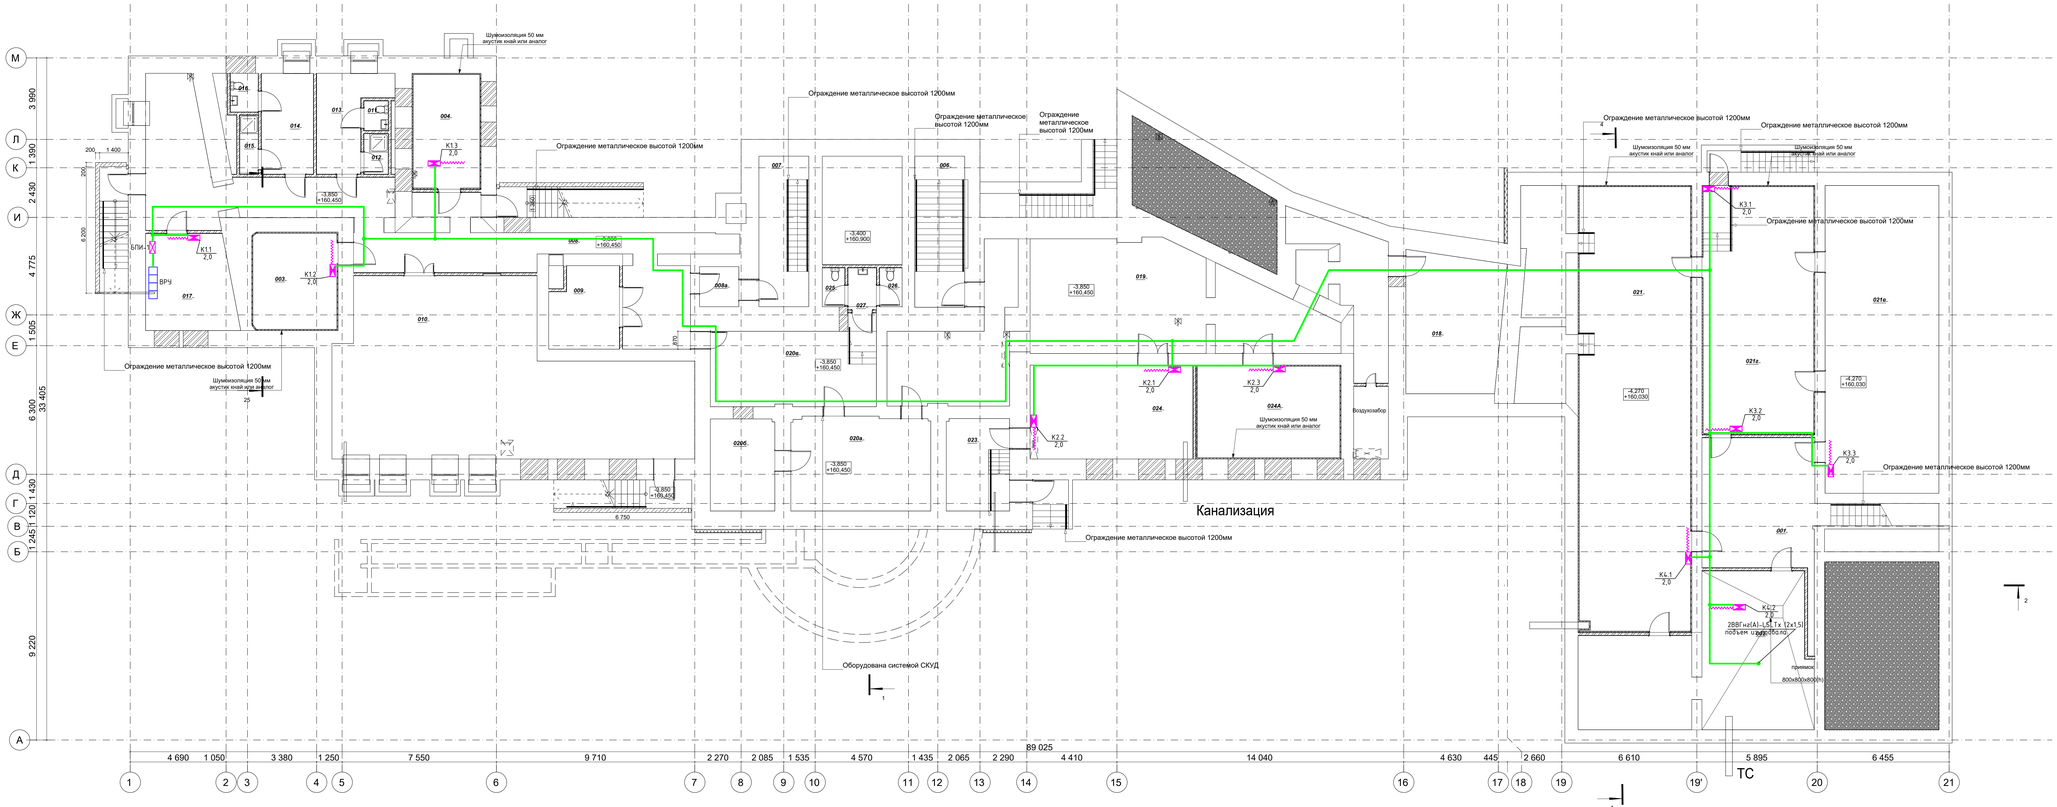

Экспликация помещений подвального этажа

Номер пом.	Наименование	Площадь, м2	Кат. пом.
001	Лестничная клетка	43,10	
002	ИТП	68,77	В4
003	Венткамера	20,99	В4
004	Венткамера	19,20	В4
006	Лестничная клетка тип Л1	18,75	
007	Технологическая лестница	17,98	
008	Коридор	94,09	
008а	Тамбур-шлюз	3,76	
009	Снарядная	13,11	В3
010	Зал ЛФК	124,39	
011	Санузел	1,75	
012	Душевая	2,38	
013	Раздевальная (не более 5 чел)	12,72	
014	Раздевальная (не более 5 чел)	12,60	
015	Душевая	2,64	
016	Санузел	2,62	
017	Электрощитовая	19,98	В3
018	Подсобное помещение	31,35	В3
019	Коридор	127,62	
020а	Коридор	32,25	
020б	Помещение для прокладки коммуникаций	14,72	В4
020в	Коридор	30,63	
021	Венткамера	151,46	В4
021а	Помещение для прокладки коммуникаций	85,12	В4
021г	Венткамера	68,40	В3
023	Узел ввода	13,90	Д
024	Насосная	38,23	Д
024А	Венткамера	33,30	В4
025	Санузел	2,09	
026	Санузел	2,09	
027	Умывальная	2,64	
		1 112,65 м²	

Изм.	Кол.уч.	Лист	№док.	Подп.	Дата
Разраб.		Семёнов			12.2025
Пров.		Ульянцев М.Н.			12.2025
Н. контр.		Ульянцев М.Н.			12.2025
Нач. ОПИС №1		Безрукова В.П.			12.2025

2024-00375-01-0-ИОС1

Капитальный ремонт здания Государственного бюджетного общеобразовательного учреждения города Москвы «Школа № 1574» по адресу: г. Москва, Спартаковский пер. д. №5

Стадия	Лист	Листов
П	64	

Система электроснабжения

План подвала с трубными проводками 038С

МОСЖИЛ НИИПРОЕКТ

Формат А2 х 3

Инв. № подл. | Подпись и дата | Взам. инв.№ | Подпись и дата

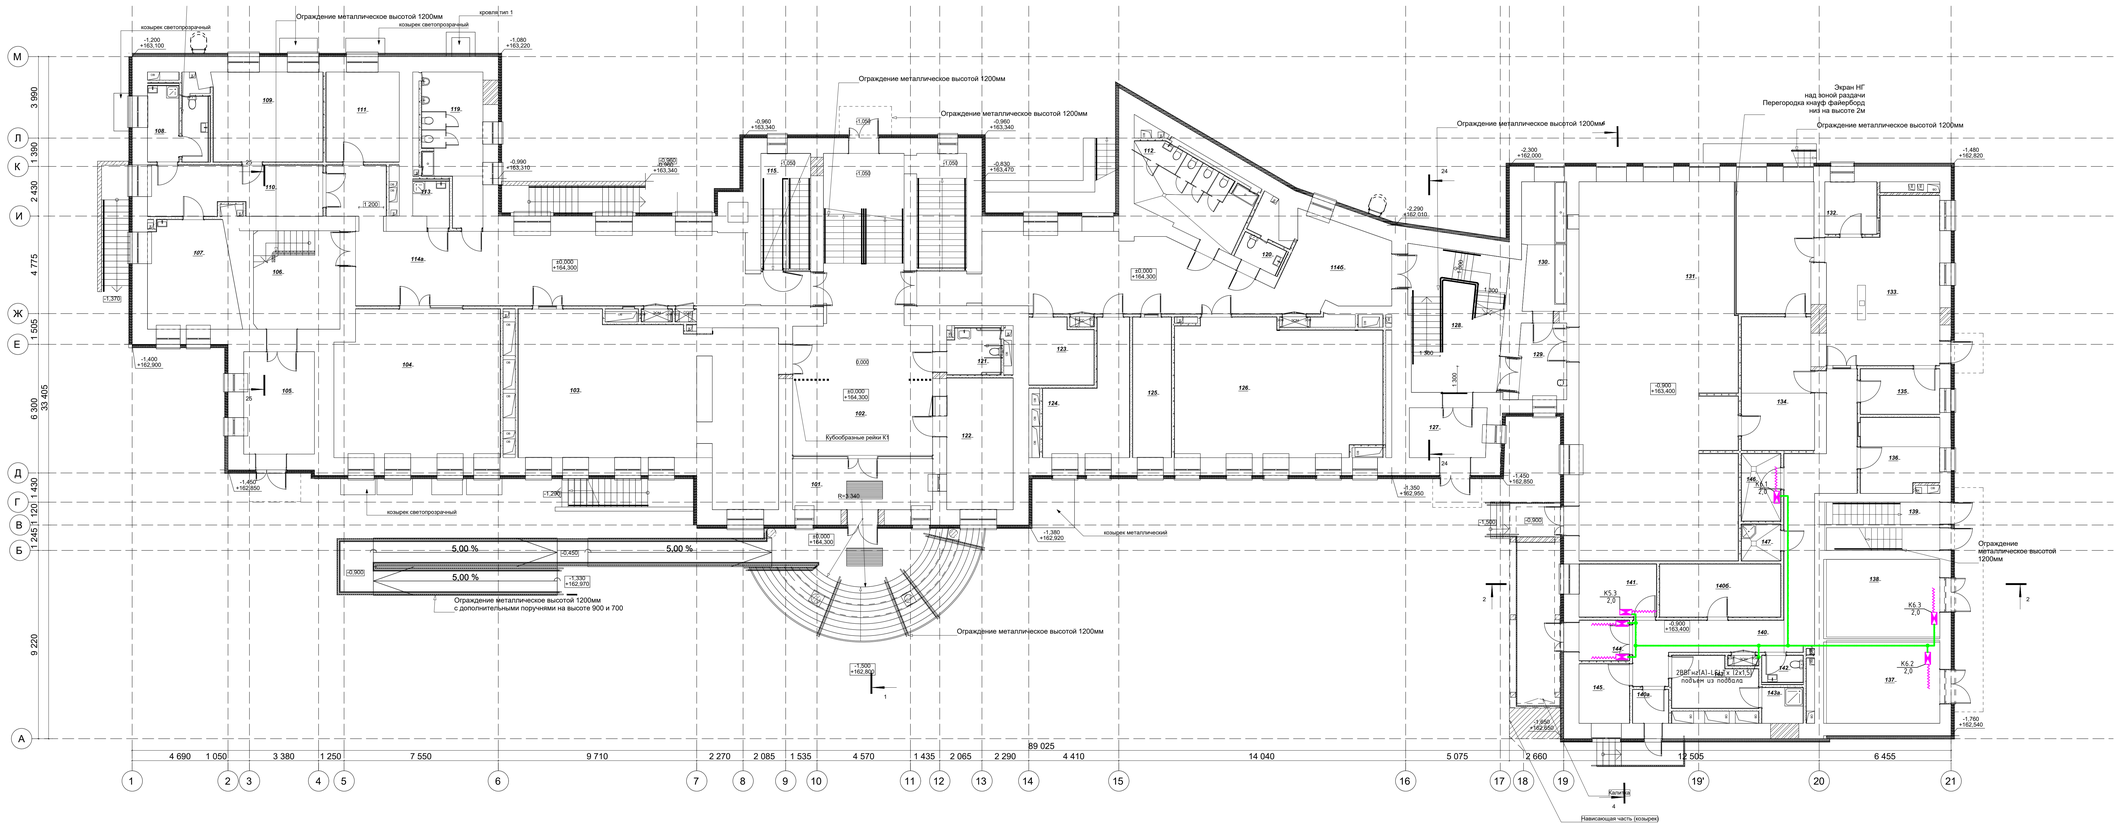

Экспликация помещений 1 этажа

Номер пом.	Наименование	Площадь, м2	Кат. пом.
101	Тамбур	18,09	
102	Вестибюль	79,49	
103	Гардеробная для обучающихся	94,58	
104	Учебный кабинет	57,67	
105	Тамбур	18,37	
106	Лестничная клетка тип Н2	22,57	
107	Процедурный (прививочный) кабинет	22,14	
108	Место для приготовления дезинфицирующих растворов и хранения уборочного инвентаря	10,35	В4
109	Кабинет врача	23,64	
110	Зона ожидания посетителей	20,55	
111	Кладовая	15,75	В3
112	Санузел для девочек с комнатой личной гигиены	7,99	
113	ПУИ	3,70	В4
114а	Коридор	83,40	
114б	Коридор	75,18	
115	Технологическая лестница	13,98	
119	Санузел для мальчиков	5,69	
120	Санузел для персонала	3,40	
121	Санузел для МГН	6,40	
122	Комната охраны	20,95	
123	Кроссовая	9,82	В4
124	Административный кабинет тип 1	19,95	
125	Гардеробная комната для учителей	13,02	
126	Учебный кабинет	65,15	
127	Тамбур	10,38	
128	Лестничная клетка тип Л1	33,63	
129	Коридор	10,06	
130	Умывальная	13,97	
131	Обеденный зал	169,16	
132	Холодный цех	6,57	В4
133	Горячий цех	41,96	В3
134	Моечная столовой посуды	23,00	В4
135	Моечная кухонной посуды	8,66	В4
136	Доготовочный цех	13,73	В3
137	Техническое помещение (электрощитовая)	23,30	В3
138	Техническое помещение (электрощитовая)	21,83	В3
139	Лестничная клетка лип Л1	13,32	
140	Коридор	40,06	
140а	Тамбур	3,45	
1406	помещение холодильного оборудования	15,31	В3
141	Кладовая сухих продуктов	9,82	В4
142	Санузел	2,68	
143	Помещение для персонала	9,91	
143а	Душ	3,52	
144	Загрузочный цех	5,78	В4
145	Кладовая и моечная оборотной тары	7,17	В4
146	Помещение для временного хранения пищевых отходов	6,35	В4
147	ПУИ	3,46	В4
		1 208,91 м²	

Инв. № подл. | Подпись и дата | Взам. инв.№ | Инв.№ дубл. | Подпись и дата

Изм.	Кол.уч.	Лист	№док.	Подп.	Дата
Разраб.		Семёнов			12.2025
Пров.		Ильяш М.Н.			12.2025
Н. контр.		Ильяш М.Н.			12.2025
ГИП (ГИС №1)		Белошова В.П.			12.2025

2024-00375-01-0-ИОС1

Капитальный ремонт здания Государственного бюджетного общеобразовательного учреждения города Москвы «Школа № 1574» по адресу: г. Москва, Спортивный пер. д. №5

Система электроснабжения

Стадия	Лист	Листов
П	65	

План 1 этажа с групповыми проводками ОЗОС

МОСЖИЛ НИИПРОЕКТ

Формат А2 х 3

1. Для уравнивания потенциалов и защиты от статического электричества выполняется система уравнивания потенциалов, которая соединяет между собой:
- PEN-проводник питающих кабелей;
- металлическую броню питающих кабелей;
- металлические части каркаса здания;
- трубы инженерных коммуникаций, входящих в здание;
- металлическую кровлю здания;
- металлические корпуса щитов управления;
- ГЗШ здания.

2. Соединение с металлическими частями здания выполнить сваркой, с ГЗШ – болтовыми зажимами, с трубами – проводом марки ПуГВ и ленточными хомутами заземления.

3. Заземляющие проводники в местах их присоединения обозначить желто-зелеными полосами, выполненными краской или двухцветной липкой лентой.

4. Молниезащита здания выполняется путем присоединения металлической кровли здания к наружному контуру заземления.

Условные обозначения:

- С1 – трубопроводы коммуникаций на вводе в здание;
- С2 – броня питающих кабелей;

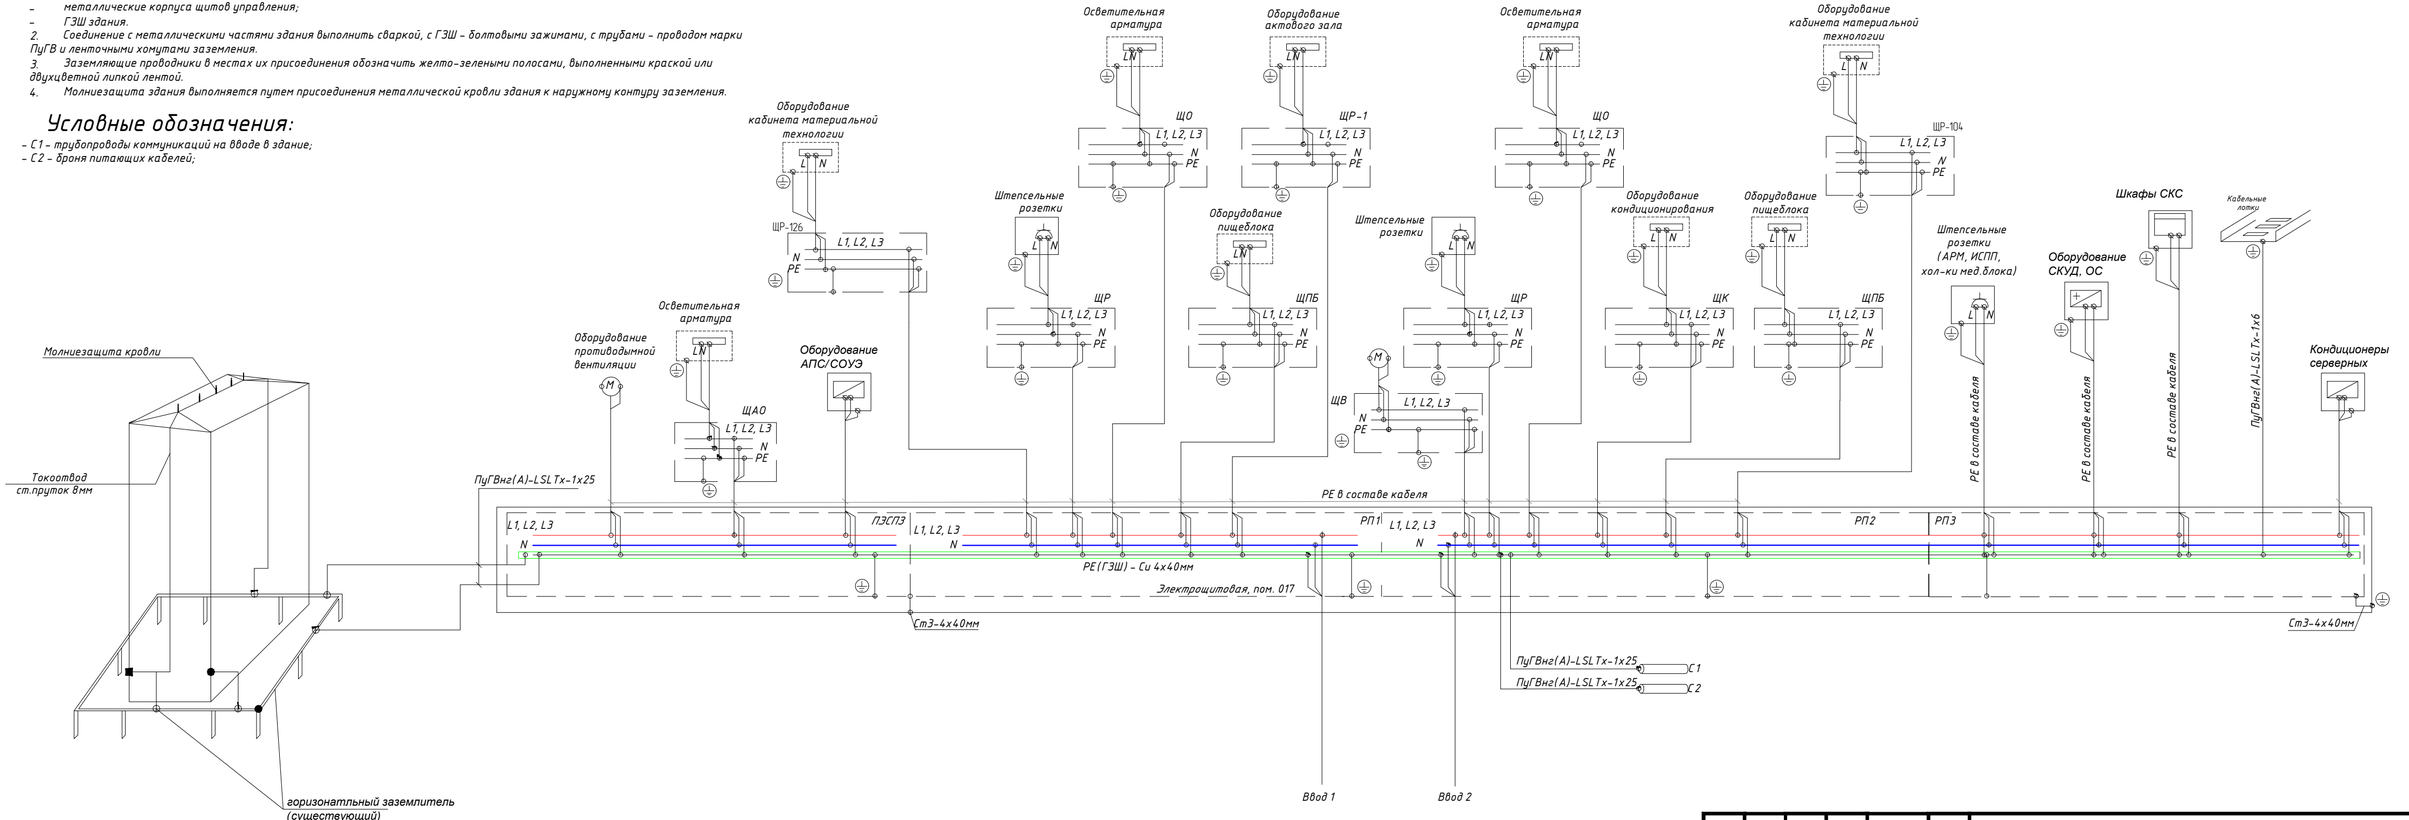

Согласовано

Взам. инв.№

Подпись и дата

Инв.№ подл.

						2024-00375-01-0-ИОС1	
						Капитальный ремонт здания Государственного бюджетного общеобразовательного учреждения города Москвы «Школа № 1574» по адресу: г. Москва, Старопименовский пер., д. №5	
Изм.	Кол.уч.	Лист	№док.	Подп.	Дата		
Разраб.		Семенов			02.2025	Система электроснабжения	Стадия: П; Лист: 66; Листов:
Провер.		Пильгуй М.Н.			02.2025		
Н. контр.		Пильгуй Н.М.			02.2025	Схема уравнивания потенциалов	МОСЖИЛ НИИПРОЕКТ
Нач. ОПИС №1		Белоусова Д.П.			02.2025		

Формат А4 х 3

	Наименование и техническая характеристика	Тип, марка, обозначение документа, опросного листа	Код продукции	Поставщик	Ед. измерения	Кол.		Примечания
	1. Низковольтное оборудование							
ВП1, ВП2	***Вводные панели №1, №2 индивидуального исполнения, напольные***		Лист 1 2024-00375-01-0-ИОС1		кмпл.	1		
РП1, РП2, РП3	***Распределительные панели №1, №2, №3 индивидуального исполнения, напольные***		Лист 1 2024-00375-01-0-ИОС1		кмпл.	1		
ПЭСПЗ	***Панель питания электрооборудования систем противопожарной защиты, индивидуального исполнения, напольная***		Лист 2 2024-00375-01-0-ИОС1		кмпл.	1		
	ЩО-0.1							
	Корпус метал. распределительный, навесной на 24 модулей ЩРн-24з-1 36 УХЛ3 IP31, 395х310х120 мм		MKM11-N-24-31-Z	IEK	шт	1		
	Выключатель нагрузки ВН-32 3Р 25А		MNV10-3-032	IEK	шт	1		
	Выключатель автоматический ВА47-29 1Р 10А тип В		MVA20-1-010-B	IEK	шт	5		
	Контактор модульный 20А		MKK11-20-20	IEK	шт	1		
	Устройство защиты от дугового пробоя IEK УЗДП63-1 16А		MDP10-16	IEK	шт	5		
	Шина N "ноль" на DIN-изоляторе ШНИ-6х9-6-Д-С		YNN10-69-6D-K07	IEK	шт	1		
	Шина PEN "земля-ноль" 6х9мм 10/2 (10групп/крепеж по краям)		YNN11-10-100	IEK	шт	1		
	ЩО-0.2							
	Корпус метал. распределительный, навесной на 24 модулей ЩРн-24з-1 36 УХЛ3 IP31, 395х310х120 мм		MKM11-N-24-31-Z	IEK	шт	1		

Согласовано

Взам. инв.№

Подп. и дата

Инв.№ подл.

Таблица регистрации изменений								
Изм.	Номера листов (страниц)				Всего листов (страниц) в док.	Номер док.	Подп.	Дата
	Изменённых	Заменённых	Новых	Аннулированных				

Изм.	Кол.уч.	Лист	№ док.	Подпись	Дата
Разраб.		Семенов Д.Ф			02.2025
Проверил		Пильгуй Н.М			02.2025
Н.контр.		Пильгуй Н.М			02.2025
Нач.отдела		Белоусова Д.Г			02.2025

2024-00375-01-0-ИОС1.СО

Капитальный ремонт здания Государственного бюджетного общеобразовательного учреждения города Москвы «Школа № 1574» по адресу: г. Москва, Старопименовский пер., д. №5

Система электроснабжения

Стадия	Лист	Листов
Р	1	37

Спецификация оборудования, изделий и материалов

МОСЖИЛ НИИПРОЕКТ

	Наименование и техническая характеристика	Тип, марка, обозначение документа, опросного листа	Код продукции	Поставщик	Ед. изме-рения	Кол.		Примечания
	Выключатель нагрузки ВН-32 3Р 25А		MNV10-3-032	IEK	шт	1		
	Выключатель автоматический ВА47-29 1Р 10А тип В		MVA20-1-010-B	IEK	шт	7		
	Устройство защиты от дугового пробоя IEK УЗДП63-1 16А		MDP10-16	IEK	шт	7		
	Шина N "ноль" на DIN-изоляторе ШНИ-6х9-6-Д-С		YNN10-69-6D-K07	IEK	шт	1		
	Шина PEN "земля-ноль" 6х9мм 10/2 (10групп/крепеж по краям)		YNN11-10-100	IEK	шт	1		
	ЩО-1.1							
	Корпус метал. распределительный, навесной на 36 модулей ЩРн-36з-1 36 УХЛ3 IP31, 540х310х120 мм		MKM14-N-36-31-Z	IEK	шт	1		
	Выключатель нагрузки ВН-32 3Р 25А		MNV10-3-032	IEK	шт	1		
	Выключатель автоматический ВА47-29 1Р 10А тип В		MVA20-1-010-B	IEK	шт	9		
	Устройство защиты от дугового пробоя IEK УЗДП63-1 16А		MDP10-16	IEK	шт	9		
	Контактор модульный КМ20-20М АС		MKK11-20-20	IEK	шт	5		
	Шина N "ноль" на DIN-изоляторе ШНИ-6х9-6-Д-С		YNN10-69-6D-K07	IEK	шт	1		
	Шина PEN "земля-ноль" 6х9мм 10/2 (10групп/крепеж по краям)		YNN11-10-100	IEK	шт	1		
	ЩО-1.2							
	Корпус метал. распределительный, навесной на 24 модулей ЩРн-24з-1 36 УХЛ3 IP31, 395х310х120 мм		MKM14-N-24-31-Z	IEK	шт	1		
	Выключатель нагрузки ВН-32 3Р 25А		MNV10-3-032	IEK	шт	1		
	Выключатель автоматический ВА47-29 1Р 10А тип В		MVA20-1-010-B	IEK	шт	6		
	Устройство защиты от дугового пробоя IEK УЗДП63-1 16А		MDP10-16	IEK	шт	6		
	Контактор модульный КМ20-20М АС		MKK11-20-20	IEK	шт	2		

	Наименование и техническая характеристика	Тип, марка, обозначение документа, опросного листа	Код продукции	Поставщик	Ед. изме-рения	Кол.		Примечания
	Шина N "ноль" на DIN-изоляторе ШНИ-6х9-6-Д-С		YNN10-69-6D-K07	IEK	шт	1		
	Шина PEN "земля-ноль" 6х9мм 10/2 (10групп/крепеж по краям)		YNN11-10-100	IEK	шт	1		
	ЩО-1.3							
	Корпус метал. распределительный, навесной на 36 модулей ЩРн-36з-1 36 УХЛ3 IP31, 540х310х120 мм		MKM14-N-36-31-Z	IEK	шт	1		
	Выключатель нагрузки ВН-32 3Р 25А		MNV10-3-032	IEK	шт	1		
	Выключатель автоматический ВА47-29 1Р 10А тип В		MVA20-1-010-B	IEK	шт	8		
	Устройство защиты от дугового пробоя IEK УЗДП63-1 16А		MDP10-16	IEK	шт	8		
	Контактор модульный КМ20-20М АС		MKK11-20-20	IEK	шт	2		
	Шина N "ноль" на DIN-изоляторе ШНИ-6х9-6-Д-С		YNN10-69-6D-K07	IEK	шт	1		
	Шина PEN "земля-ноль" 6х9мм 10/2 (10групп/крепеж по краям)		YNN11-10-100	IEK	шт	1		
	ЩО-2.1							
	Корпус метал. распределительный, навесной на 36 модулей ЩРн-36з-1 36 УХЛ3 IP31, 540х310х120 мм		MKM14-N-36-31-Z	IEK	шт	1		
	Выключатель нагрузки ВН-32 3Р 25А		MNV10-3-032	IEK	шт	1		
	Выключатель автоматический ВА47-29 1Р 10А тип В		MVA20-1-010-B	IEK	шт	7		
	Устройство защиты от дугового пробоя IEK УЗДП63-1 16А		MDP10-16	IEK	шт	7		
	Контактор модульный КМ20-20М АС		MKK11-20-20	IEK	шт	1		
	Шина N "ноль" на DIN-изоляторе ШНИ-6х9-6-Д-С		YNN10-69-6D-K07	IEK	шт	1		
	Шина PEN "земля-ноль" 6х9мм 10/2 (10групп/крепеж по краям)		YNN11-10-100	IEK	шт	1		

	Наименование и техническая характеристика	Тип, марка, обозначение документа, опросного листа	Код продукции	Поставщик	Ед. изме-рения	Кол.		Примечания
	ЩО-2.2							
	Корпус метал. распределительный, навесной на 36 модулей ЩРн-36з-1 36 УХЛ3 IP31, 540х310х120 мм		MKM14-N-36-31-Z	IEK	шт	1		
	Выключатель нагрузки ВН-32 3Р 25А		MNV10-3-032	IEK	шт	1		
	Выключатель автоматический ВА47-29 1Р 10А тип В		MVA20-1-010-B	IEK	шт	6		
	Устройство защиты от дугового пробоя IEK УЗДП63-1 16А		MDP10-16	IEK	шт	6		
	Контактор модульный КМ20-20М АС		MKK11-20-20	IEK	шт	1		
	Шина N "ноль" на DIN-изоляторе ШНИ-6х9-6-Д-С		YNN10-69-6D-K07	IEK	шт	1		
	Шина PEN "земля-ноль" 6х9мм 10/2 (10групп/крепеж по краям)		YNN11-10-100	IEK	шт	1		
	ЩО-2.3							
	Корпус метал. распределительный, навесной на 36 модулей ЩРн-36з-1 36 УХЛ3 IP31, 540х310х120 мм		MKM14-N-36-31-Z	IEK	шт	1		
	Выключатель нагрузки ВН-32 3Р 25А		MNV10-3-032	IEK	шт	1		
	Выключатель автоматический ВА47-29 1Р 10А тип В		MVA20-1-010-B	IEK	шт	7		
	Устройство защиты от дугового пробоя IEK УЗДП63-1 16А		MDP10-16	IEK	шт	7		
	Контактор модульный КМ20-20М АС		MKK11-20-20	IEK	шт	1		
	Шина N "ноль" на DIN-изоляторе ШНИ-6х9-6-Д-С		YNN10-69-6D-K07	IEK	шт	1		
	Шина PEN "земля-ноль" 6х9мм 10/2 (10групп/крепеж по краям)		YNN11-10-100	IEK	шт	1		
	ЩО-3.1							
	Корпус метал. распределительный, навесной на 36 модулей ЩРн-36з-1 36 УХЛ3 IP31, 540х310х120 мм		MKM14-N-36-31-Z	IEK	шт	1		
	Выключатель нагрузки ВН-32 3Р 25А		MNV10-3-032	IEK	шт	1		

	Наименование и техническая характеристика	Тип, марка, обозначение документа, опросного листа	Код продукции	Поставщик	Ед. изме-рения	Кол.		Примечания
	Выключатель автоматический ВА47-29 1Р 10А тип В		MVA20-1-010-B	IEK	шт	9		
	Устройство защиты от дугового пробоя IEK УЗДП63-1 16А		MDP10-16	IEK	шт	9		
	Контактор модульный КМ20-20М АС		MKK11-20-20	IEK	шт	1		
	Шина N "ноль" на DIN-изоляторе ШНИ-6х9-6-Д-С		YNN10-69-6D-K07	IEK	шт	1		
	Шина PEN "земля-ноль" 6х9мм 10/2 (10групп/крепеж по краям)		YNN11-10-100	IEK	шт	1		
	ЩО-3.2							
	Корпус метал. распределительный, навесной на 36 модулей ЩРн-36з-1 36 УХЛ3 IP31, 540х310х120 мм		MKM14-N-36-31-Z	IEK	шт	1		
	Выключатель нагрузки ВН-32 3Р 25А		MNV10-3-032	IEK	шт	1		
	Выключатель автоматический ВА47-29 1Р 10А тип В		MVA20-1-010-B	IEK	шт	7		
	Устройство защиты от дугового пробоя IEK УЗДП63-1 16А		MDP10-16	IEK	шт	7		
	Контактор модульный КМ20-20М АС		MKK11-20-20	IEK	шт	1		
	Шина N "ноль" на DIN-изоляторе ШНИ-6х9-6-Д-С		YNN10-69-6D-K07	IEK	шт	1		
	Шина PEN "земля-ноль" 6х9мм 10/2 (10групп/крепеж по краям)		YNN11-10-100	IEK	шт	1		
	ЩО-4.1							
	Корпус метал. распределительный, навесной на 36 модулей ЩРн-36з-1 36 УХЛ3 IP31, 540х310х120 мм		MKM14-N-36-31-Z	IEK	шт	1		
	Выключатель нагрузки ВН-32 3Р 25А		MNV10-3-032	IEK	шт	1		
	Выключатель автоматический ВА47-29 1Р 10А тип В		MVA20-1-010-B	IEK	шт	9		
	Устройство защиты от дугового пробоя IEK УЗДП63-1 16А		MDP10-16	IEK	шт	9		
	Контактор модульный КМ20-20М АС		MKK11-20-20	IEK	шт	1		

	Наименование и техническая характеристика	Тип, марка, обозначение документа, опросного листа	Код продукции	Поставщик	Ед. изме-рения	Кол.		Примечания
	Шина N "ноль" на DIN-изоляторе ШНИ-6х9-6-Д-С		YNN10-69-6D-K07	IEK	шт	1		
	Шина PEN "земля-ноль" 6х9мм 10/2 (10групп/крепеж по краям)		YNN11-10-100	IEK	шт	1		
	ЩО-4.2							
	Корпус метал. распределительный, навесной на 24 модулей ЩРн-24з-1 36 УХЛ3 IP31, 395х310х120 мм		MKM14-N-24-31-Z	IEK	шт	1		
	Выключатель нагрузки ВН-32 3Р 25А		MNV10-3-032	IEK	шт	1		
	Выключатель автоматический ВА47-29 1Р 10А тип В		MVA20-1-010-B	IEK	шт	5		
	Устройство защиты от дугового пробоя IEK УЗДП63-1 16А		MDP10-16	IEK	шт	5		
	Шина N "ноль" на DIN-изоляторе ШНИ-6х9-6-Д-С		YNN10-69-6D-K07	IEK	шт	1		
	Шина PEN "земля-ноль" 6х9мм 10/2 (10групп/крепеж по краям)		YNN11-10-100	IEK	шт	1		
	ЩО-5.1							
	Корпус метал. распределительный, навесной на 36 модулей ЩРн-36з-1 36 УХЛ3 IP31, 540х310х120 мм		MKM14-N-36-31-Z	IEK	шт	1		
	Выключатель нагрузки ВН-32 3Р 25А		MNV10-3-032	IEK	шт	1		
	Выключатель автоматический ВА47-29 1Р 10А тип В		MVA20-1-010-B	IEK	шт	9		
	Устройство защиты от дугового пробоя IEK УЗДП63-1 16А		MDP10-16	IEK	шт	9		
	Контактор модульный КМ20-20М АС		MKK11-20-20	IEK	шт	1		
	Шина N "ноль" на DIN-изоляторе ШНИ-6х9-6-Д-С		YNN10-69-6D-K07	IEK	шт	1		
	Шина PEN "земля-ноль" 6х9мм 10/2 (10групп/крепеж по краям)		YNN11-10-100	IEK	шт	1		
	ЩО-5.2							

	Наименование и техническая характеристика	Тип, марка, обозначение документа, опросного листа	Код продукции	Поставщик	Ед. измерения	Кол.		Примечания
	Корпус метал. распределительный, навесной на 24 модулей ЩРн-24з-1 36 УХЛ3 IP31, 395х310х120 мм		MKM14-N-24-31-Z	IEK	шт	1		
	Выключатель нагрузки ВН-32 3Р 25А		MNV10-3-032	IEK	шт	1		
	Выключатель автоматический ВА47-29 1Р 10А тип В		MVA20-1-010-B	IEK	шт	6		
	Устройство защиты от дугового пробоя IEK УЗДП63-1 16А		MDP10-16	IEK	шт	6		
	Шина N "ноль" на DIN-изоляторе ШНИ-6х9-6-Д-С		YNN10-69-6D-K07	IEK	шт	1		
	Шина PEN "земля-ноль" 6х9мм 10/2 (10групп/крепеж по краям)		YNN11-10-100	IEK	шт	1		
	ЩАО-0.1							
	Корпус метал. распределительный, навесной на 12 модулей ЩРн-12з-1 36 УХЛ3 IP31, 265х310х120 мм		MKM14-N-12-31-Z	IEK	шт	1		
	Выключатель нагрузки ВН-32 3Р 25А		MNV10-3-032	IEK	шт	1		
	Выключатель автоматический ВА47-29 1Р 10А тип В		MVA20-1-010-B	IEK	шт	7		
	Шина N "ноль" на DIN-изоляторе ШНИ-6х9-6-Д-С		YNN10-69-6D-K07	IEK	шт	1		
	Шина PEN "земля-ноль" 6х9мм 10/2 (10групп/крепеж по краям)		YNN11-10-100	IEK	шт	1		
	ЩАО-0.2							
	Корпус метал. распределительный, навесной на 12 модулей ЩРн-12з-1 36 У2 IP54, 265х310х120 мм		MKM11-N-12-54-Z	IEK	шт	1		
	Выключатель нагрузки ВН-32 3Р 25А		MNV10-3-032	IEK	шт	1		
	Выключатель автоматический ВА47-29 1Р 10А тип В		MVA20-1-010-B	IEK	шт	6		
	Шина N "ноль" на DIN-изоляторе ШНИ-6х9-6-Д-С		YNN10-69-6D-K07	IEK	шт	1		
	Шина PEN "земля-ноль" 6х9мм 10/2 (10групп/крепеж по краям)		YNN11-10-100	IEK	шт	1		

	Наименование и техническая характеристика	Тип, марка, обозначение документа, опросного листа	Код продукции	Поставщик	Ед. изме-рения	Кол.		Примечания
	ЩАО-1.1							
	Корпус метал. распределительный, навесной на 24 модулей ЩРн-24з-1 36 УХЛ3 IP31, 395х310х120 мм		MKM14-N-24-31-Z	IEK	шт	1		
	Выключатель нагрузки ВН-32 3Р 25А		MNV10-3-032	IEK	шт	1		
	Выключатель автоматический ВА47-29 1Р 10А тип В		MVA20-1-010-B	IEK	шт	8		
	Контактор модульный КМ20-20М АС		MKK11-20-20	IEK	шт	5		
	Шина N "ноль" на DIN-изоляторе ШНИ-6х9-6-Д-С		YNN10-69-6D-K07	IEK	шт	1		
	Шина PEN "земля-ноль" 6х9мм 10/2 (10групп/крепеж по краям)		YNN11-10-100	IEK	шт	1		
	ЩАО-1.2							
	Корпус метал. распределительный, навесной на 24 модулей ЩРн-24з-1 36 УХЛ3 IP31, 395х310х120 мм		MKM14-N-24-31-Z	IEK	шт	1		
	Выключатель нагрузки ВН-32 3Р 25А		MNV10-3-032	IEK	шт	1		
	Выключатель автоматический ВА47-29 1Р 10А тип В		MVA20-1-010-B	IEK	шт	6		
	Контактор модульный КМ20-20М АС		MKK11-20-20	IEK	шт	3		
	Шина N "ноль" на DIN-изоляторе ШНИ-6х9-6-Д-С		YNN10-69-6D-K07	IEK	шт	1		
	Шина PEN "земля-ноль" 6х9мм 10/2 (10групп/крепеж по краям)		YNN11-10-100	IEK	шт	1		
	ЩАО-1.3							
	Корпус метал. распределительный, навесной на 24 модулей ЩРн-24з-1 36 УХЛ3 IP31, 395х310х120 мм		MKM14-N-24-31-Z	IEK	шт	1		
	Выключатель нагрузки ВН-32 3Р 25А		MNV10-3-032	IEK	шт	1		
	Выключатель автоматический ВА47-29 1Р 10А тип В		MVA20-1-010-B	IEK	шт	7		
	Контактор модульный КМ20-20М АС		MKK11-20-20	IEK	шт	2		

	Наименование и техническая характеристика	Тип, марка, обозначение документа, опросного листа	Код продукции	Поставщик	Ед. изме-рения	Кол.		Примечания
	Шина N "ноль" на DIN-изоляторе ШНИ-6х9-6-Д-С		YNN10-69-6D-K07	IEK	шт	1		
	Шина PEN "земля-ноль" 6х9мм 10/2 (10групп/крепеж по краям)		YNN11-10-100	IEK	шт	1		
	ЩАО-2.1							
	Корпус метал. распределительный, навесной на 12 модулей ЩРн-12з-1 36 УХЛ3 IP31, 265х310х120 мм		MKM14-N-12-31-Z	IEK	шт	1		
	Выключатель нагрузки ВН-32 3Р 25А		MNV10-3-032	IEK	шт	1		
	Выключатель автоматический ВА47-29 1Р 10А тип В		MVA20-1-010-B	IEK	шт	5		
	Контактор модульный КМ20-20М АС		MKK11-20-20	IEK	шт	1		
	Шина N "ноль" на DIN-изоляторе ШНИ-6х9-6-Д-С		YNN10-69-6D-K07	IEK	шт	1		
	Шина PEN "земля-ноль" 6х9мм 10/2 (10групп/крепеж по краям)		YNN11-10-100	IEK	шт	1		
	ЩАО-2.2							
	Корпус метал. распределительный, навесной на 12 модулей ЩРн-12з-1 36 УХЛ3 IP31, 265х310х120 мм		MKM14-N-12-31-Z	IEK	шт	1		
	Выключатель нагрузки ВН-32 3Р 25А		MNV10-3-032	IEK	шт	1		
	Выключатель автоматический ВА47-29 1Р 10А тип В		MVA20-1-010-B	IEK	шт	6		
	Контактор модульный КМ20-20М АС		MKK11-20-20	IEK	шт	1		
	Шина N "ноль" на DIN-изоляторе ШНИ-6х9-6-Д-С		YNN10-69-6D-K07	IEK	шт	1		
	Шина PEN "земля-ноль" 6х9мм 10/2 (10групп/крепеж по краям)		YNN11-10-100	IEK	шт	1		
	ЩАО-3.1							
	Корпус метал. распределительный, навесной на 12 модулей ЩРн-12з-1 36 УХЛ3 IP31, 265х310х120 мм		MKM14-N-12-31-Z	IEK	шт	1		

	Наименование и техническая характеристика	Тип, марка, обозначение документа, опросного листа	Код продукции	Поставщик	Ед. изме-рения	Кол.		Примечания
	Выключатель нагрузки ВН-32 3Р 25А		MNV10-3-032	IEK	шт	1		
	Выключатель автоматический ВА47-29 1Р 10А тип В		MVA20-1-010-B	IEK	шт	6		
	Контактор модульный КМ20-20М АС		MKK11-20-20	IEK	шт	1		
	Шина N "ноль" на DIN-изоляторе ШНИ-6х9-6-Д-С		YNN10-69-6D-K07	IEK	шт	1		
	Шина PEN "земля-ноль" 6х9мм 10/2 (10групп/крепеж по краям)		YNN11-10-100	IEK	шт	1		
	ЩАО-4.1							
	Корпус метал. распределительный, навесной на 12 модулей ЩРн-12з-1 36 УХЛ3 IP31, 265х310х120 мм		MKM14-N-12-31-Z	IEK	шт	1		
	Выключатель нагрузки ВН-32 3Р 25А		MNV10-3-032	IEK	шт	1		
	Выключатель автоматический ВА47-29 1Р 10А тип В		MVA20-1-010-B	IEK	шт	5		
	Контактор модульный КМ20-20М АС		MKK11-20-20	IEK	шт	1		
	Шина N "ноль" на DIN-изоляторе ШНИ-6х9-6-Д-С		YNN10-69-6D-K07	IEK	шт	1		
	Шина PEN "земля-ноль" 6х9мм 10/2 (10групп/крепеж по краям)		YNN11-10-100	IEK	шт	1		
	ЩАО-5.1							
	Корпус метал. распределительный, навесной на 12 модулей ЩРн-12з-1 36 УХЛ3 IP31, 265х310х120 мм		MKM14-N-12-31-Z	IEK	шт	1		
	Выключатель нагрузки ВН-32 3Р 25А		MNV10-3-032	IEK	шт	1		
	Выключатель автоматический ВА47-29 1Р 10А тип В		MVA20-1-010-B	IEK	шт	6		
	Контактор модульный КМ20-20М АС		MKK11-20-20	IEK	шт	1		
	Шина N "ноль" на DIN-изоляторе ШНИ-6х9-6-Д-С		YNN10-69-6D-K07	IEK	шт	1		
	Шина PEN "земля-ноль" 6х9мм 10/2 (10групп/крепеж по краям)		YNN11-10-100	IEK	шт	1		

	Наименование и техническая характеристика	Тип, марка, обозначение документа, опросного листа	Код продукции	Поставщик	Ед. изме-рения	Кол.		Примечания
	ЩУО							
	Корпус металлический ЩМП-4-0 36 УХЛ3 IP31 800х650х250	ЩМП-4-0 36 УХЛ3 IP31	YKM40-04-31	IEK	шт.	1		
	LAY5-BD33 3 фикс. положения «I-0-II» стандарт. ручка		BSW60-BD-3-K02	IEK	шт.	33		
	Лампа AL-22 сигнальная d22мм зеленый неон/240В цилиндр ИЭК		BLS20-AL-K06	IEK	шт.	33		
	Выключатель автоматический ВА47-29 1Р 6А тип В		MVA20-1-010-B	IEK	шт	1		
	Выключатель сумеречный, ФР-16а			НТК «Электроника»	шт	1		
	DIN-рейка (30 см) оцинкованная		YDN10-0030	IEK	шт	1		
	ЩР-0.1							
	Корпус метал. распределительный, навесной на 36 модулей ЩРн-36з-1 36 УХЛ3 IP31, 540х310х120 мм		MKM14-N-36-31-Z	IEK	шт	1		
	Выключатель нагрузки ВН-32 3Р 32А		MNV10-3-032	IEK	шт	1		
	Выключатель автоматический ВА47-29 3Р 10А тип С		MVA20-3-010-C	IEK	шт	1		
	Выключатель автоматический дифференциальный B06S 1P+NP C16 30мА тип АС		AR-B06S-1N-C16C030	IEK	шт	7		
	Устройство защиты от дугового пробоя УЗДП63-1 25А		MDP10-25	IEK	шт	7		
	Шина N "ноль" на DIN-изоляторе ШНИ-6х9-6-Д-С		YNN10-69-6D-K07	IEK	шт	1		
	Шина PEN "земля-ноль" 6х9мм 10/2 (10групп/крепеж по краям)		YNN11-10-100	IEK	шт	1		
	ЩР-104							
	Корпус метал. распределительный, навесной на 48 модулей ЩРн-48з-1 36 УХЛ3 IP31, 620х310х120 мм		MKM14-N-48-31-Z	IEK	шт	1		
	Выключатель нагрузки ВН-32 3Р 63А		MNV10-3-063	IEK	шт	1		

	Наименование и техническая характеристика	Тип, марка, обозначение документа, опросного листа	Код продукции	Поставщик	Ед. измерения	Кол.		Примечания
	Выключатель автоматический дифференциальный B06S 1P+NP C16 30мА тип AC		AR-B06S-1N-C16C030	IEK	шт	6		
	Выключатель автоматический дифференциальный B06S 1P+NP C20 30мА тип AC		AR-B06S-1N-C20C030	IEK	шт	5		
	Выключатель автоматический ВА47-29 1Р 2А тип С		MVA20-1-002-C	IEK	шт	1		
	Выключатель автоматический ВА47-29 3Р 32А тип С		MVA20-3-032-C	IEK	шт	1		
	Устройство защиты от дугового пробоя УЗДП63-1 63А		MDP16-63	IEK	шт	1		
	Устройство защиты от дугового пробоя УЗДП63-1 63А		MDP25-63	IEK	шт	11		
	Контактор модульный КМ25-40М AC		MKK21-25-40	IEK	шт	1		
	Шина N "ноль" на DIN-изоляторе ШНИ-6х9-6-Д-С		YNN10-69-6D-K07	IEK	шт	1		
	Шина PEN "земля-ноль" 6х9мм 10/2 (10групп/крепеж по краям)		YNN11-10-100	IEK	шт	1		
	ЩР-126							
	Корпус метал. распределительный, навесной на 54 модулей ЩРн-54з-1 36 УХЛ3 IP31, 540х440х120 мм		MKM14-N-54-31-Z	IEK	шт	1		
	Выключатель нагрузки ВН-32 3Р 63А		MNV10-3-063	IEK	шт	1		
	Выключатель автоматический дифференциальный B06S 1P+NP C16 30мА тип AC		AR-B06S-1N-C16C030	IEK	шт	3		
	Выключатель автоматический дифференциальный B06S 1P+NP C20 30мА тип AC		AR-B06S-1N-C20C030	IEK	шт	5		
	Выключатель автоматический дифференциальный B06S 1P+NP C25 30мА тип AC		AR-B06S-1N-C25C030	IEK	шт	4		
	Выключатель автоматический ВА47-29 1Р 2А тип С		MVA20-1-002-C	IEK	шт	1		
	Выключатель автоматический ВА47-29 3Р 32А тип С		MVA20-3-032-C	IEK	шт	1		
	Устройство защиты от дугового пробоя УЗДП63-1 16А		MDP16-63	IEK	шт	1		
	Устройство защиты от дугового пробоя УЗДП63-1 25А		MDP25-63	IEK	шт	8		
	Устройство защиты от дугового пробоя УЗДП63-1 32А		MDP32-63	IEK	шт	4		

	Наименование и техническая характеристика	Тип, марка, обозначение документа, опросного листа	Код продукции	Поставщик	Ед. изме-рения	Кол.		Примечания
	Контактор модульный КМ25-40М АС		MKK21-25-40	IEK	шт	1		
	Шина N "ноль" на DIN-изоляторе ШНИ-6х9-6-Д-С		YNN10-69-6D-K07	IEK	шт	1		
	Шина PEN "земля-ноль" 6х9мм 10/2 (10групп/крепеж по краям)		YNN11-10-100	IEK	шт	1		
	ЩР-1.1							
	Корпус метал. распределительный, навесной на 36 модулей ЩРн-36з-1 36 УХЛ3 IP31, 540х310х120 мм		MKM14-N-36-31-Z	IEK	шт	1		
	Выключатель нагрузки ВН-32 3Р 50А		MNV10-3-050	IEK	шт	1		
	Выключатель автоматический ВА47-29 3Р 25А тип С		MVA20-3-025-C	IEK	шт	2		
	Выключатель автоматический ВА47-29 1Р 10А тип С		MVA20-1-010-C	IEK	шт	1		
	Выключатель автоматический дифференциальный B06S 1P+NP C16 30мА тип АС		AR-B06S-1N-C16C030	IEK	шт	7		
	Независимый расцепитель AR-AUX-SR 12…24В		AR-AUX-SR-12-24	IEK	шт	3		
	Устройство защиты от дугового пробоя УЗДП63-1 25А		MDP10-25	IEK	шт	7		
	Устройство защиты от дугового пробоя УЗДП63-1 16А		MDP10-16	IEK	шт	1		
	Шина N "ноль" на DIN-изоляторе ШНИ-6х9-6-Д-С		YNN10-69-6D-K07	IEK	шт	1		
	Шина PEN "земля-ноль" 6х9мм 10/2 (10групп/крепеж по краям)		YNN11-10-100	IEK	шт	1		
	ЩР-1.2							
	Корпус метал. распределительный, навесной на 36 модулей ЩРн-36з-1 36 УХЛ3 IP31, 540х310х120 мм		MKM14-N-36-31-Z	IEK	шт	1		
	Выключатель нагрузки ВН-32 3Р 32А		MNV10-3-032	IEK	шт	1		
	Выключатель автоматический дифференциальный B06S 1P+NP C16 30мА тип АС		AR-B06S-1N-C16C030	IEK	шт	5		
	Выключатель автоматический дифференциальный B06S 1P+NP C20 30мА тип АС		AR-B06S-1N-C20C030	IEK	шт	1		

	Наименование и техническая характеристика	Тип, марка, обозначение документа, опросного листа	Код продукции	Поставщик	Ед. изме-рения	Кол.		Примечания
	Выключатель автоматический ВА47-29 3Р 25А тип С		MVA20-3-025-C	IEK	шт	1		
	Выключатель автоматический ВА47-29 1Р 10А тип С		MVA20-1-010-C	IEK	шт	1		
	Независимый расцепитель AR-AUX-SR 12…24В		AR-AUX-SR-12-24	IEK	шт	1		
	Устройство защиты от дугового пробоя УЗДП63-1 25А		MDP10-25	IEK	шт	6		
	Устройство защиты от дугового пробоя УЗДП63-1 16А		MDP10-16	IEK	шт	1		
	Шина N "ноль" на DIN-изоляторе ШНИ-6х9-6-Д-С		YNN10-69-6D-K07	IEK	шт	1		
	Шина PEN "земля-ноль" 6х9мм 10/2 (10групп/крепеж по краям)		YNN11-10-100	IEK	шт	1		
	ЩР-2.1							
	Корпус метал. распределительный, навесной на 36 модулей ЩРн-36з-1 36 УХЛ3 IP31, 540х310х120 мм		MKM14-N-36-31-Z	IEK	шт	1		
	Выключатель нагрузки ВН-32 3Р 32А		MNV10-3-032	IEK	шт	1		
	Выключатель автоматический ВА47-29 1Р 10А тип С		MVA20-1-010-C	IEK	шт	1		
	Независимый расцепитель AR-AUX-SR 12…24В		AR-AUX-SR-12-24	IEK	шт	1		
	Выключатель автоматический дифференциальный B06S 1P+NP C16 30мА тип АС		AR-B06S-1N-C16C030	IEK	шт	5		
	Устройство защиты от дугового пробоя УЗДП63-1 25А		MDP10-25	IEK	шт	5		
	Устройство защиты от дугового пробоя УЗДП63-1 16А		MDP10-16	IEK	шт	1		
	Шина N "ноль" на DIN-изоляторе ШНИ-6х9-6-Д-С		YNN10-69-6D-K07	IEK	шт	1		
	Шина PEN "земля-ноль" 6х9мм 10/2 (10групп/крепеж по краям)		YNN11-10-100	IEK	шт	1		
	ЩР-2.2							
	Корпус метал. распределительный, навесной на 24 модулей ЩРн-24з-1 36 УХЛ3 IP31, 395х310х120 мм		MKM14-N-24-31-Z	IEK	шт	1		

	Наименование и техническая характеристика	Тип, марка, обозначение документа, опросного листа	Код продукции	Поставщик	Ед. измерения	Кол.		Примечания
	Выключатель нагрузки ВН-32 3Р 32А		MNV10-3-032	IEK	шт	1		
	Выключатель автоматический дифференциальный B06S 1P+NP C16 30мА тип AC		AR-B06S-1N-C16C030	IEK	шт	4		
	Выключатель автоматический дифференциальный B06S 1P+NP C20 30мА тип AC		AR-B06S-1N-C20C030	IEK	шт	1		
	Устройство защиты от дугового пробоя УЗДП63-1 25А		MDP10-25	IEK	шт	5		
	Шина N "ноль" на DIN-изоляторе ШНИ-6х9-6-Д-С		YNN10-69-6D-K07	IEK	шт	1		
	Шина PEN "земля-ноль" 6х9мм 10/2 (10групп/крепеж по краям)		YNN11-10-100	IEK	шт	1		
	ЩР-2.3							
	Корпус метал. распределительный, навесной на 24 модулей ЩРн-24з-1 36 УХЛ3 IP31, 395х310х120 мм		MKM14-N-24-31-Z	IEK	шт	1		
	Выключатель нагрузки ВН-32 3Р 32А		MNV10-3-032	IEK	шт	1		
	Выключатель автоматический дифференциальный B06S 1P+NP C16 30мА тип AC		AR-B06S-1N-C16C030	IEK	шт	7		
	Устройство защиты от дугового пробоя УЗДП63-1 25А		MDP10-25	IEK	шт	7		
	Шина N "ноль" на DIN-изоляторе ШНИ-6х9-6-Д-С		YNN10-69-6D-K07	IEK	шт	1		
	Шина PEN "земля-ноль" 6х9мм 10/2 (10групп/крепеж по краям)		YNN11-10-100	IEK	шт	1		
	ЩР-3.1							
	Корпус метал. распределительный, навесной на 36 модулей ЩРн-36з-1 36 УХЛ3 IP31, 540х310х120 мм		MKM14-N-36-31-Z	IEK	шт	1		
	Выключатель нагрузки ВН-32 3Р 32А		MNV10-3-032	IEK	шт	1		
	Выключатель автоматический дифференциальный B06S 1P+NP C16 30мА тип AC		AR-B06S-1N-C16C030	IEK	шт	7		
	Выключатель автоматический ВА47-29 1Р 10А тип С		MVA20-1-010-C	IEK	шт	1		
	Независимый расцепитель AR-AUX-SR 12…24В		AR-AUX-SR-12-24	IEK	шт	1		

	Наименование и техническая характеристика	Тип, марка, обозначение документа, опросного листа	Код продукции	Поставщик	Ед. изме-рения	Кол.		Примечания
	Устройство защиты от дугового пробоя УЗДП63-1 16А		MDP10-16	IEK	шт	1		
	Устройство защиты от дугового пробоя УЗДП63-1 32А		MDP10-25	IEK	шт	7		
	Шина N "ноль" на DIN-изоляторе ШНИ-6х9-6-Д-С		YNN10-69-6D-K07	IEK	шт	1		
	Шина PEN "земля-ноль" 6х9мм 10/2 (10групп/крепеж по краям)		YNN11-10-100	IEK	шт	1		
	ЩР-3.2							
	Корпус метал. распределительный, навесной на 24 модулей ЩРн-24з-1 36 УХЛ3 IP31, 395х310х120 мм		MKM14-N-24-31-Z	IEK	шт	1		
	Выключатель нагрузки ВН-32 3Р 32А		MNV10-3-032	IEK	шт	1		
	Выключатель автоматический дифференциальный B06S 1P+NP C16 30мА тип АС		AR-B06S-1N-C16C030	IEK	шт	7		
	Устройство защиты от дугового пробоя УЗДП63-1 25А		MDP10-25	IEK	шт	7		
	Шина N "ноль" на DIN-изоляторе ШНИ-6х9-6-Д-С		YNN10-69-6D-K07	IEK	шт	1		
	Шина PEN "земля-ноль" 6х9мм 10/2 (10групп/крепеж по краям)		YNN11-10-100	IEK	шт	1		
	ЩР-4.1							
	Корпус метал. распределительный, навесной на 72 модулей ЩРн-72з-1 36 УХЛ3 IP31, 540х600х120 мм		MKM14-N-72-31-Z	IEK	шт	1		
	Выключатель нагрузки ВН-32 3Р 40А		MNV10-3-032	IEK	шт	1		
	Выключатель автоматический ВА47-29 1Р 2А тип С		MVA20-1-002-C	IEK	шт	2		
	Выключатель автоматический ВА47-29 3Р 25А тип С		MVA20-3-025-C	IEK	шт	2		
	Выключатель автоматический дифференциальный B06S 1P+NP C16 30мА тип АС		AR-B06S-1N-C16C030	IEK	шт	4		
	Выключатель автоматический дифференциальный B06S 1P+NP C20 30мА тип АС		AR-B06S-1N-C20C030	IEK	шт	7		
	Выключатель автоматический ВА47-29 1Р 10А тип С		MVA20-1-010-C	IEK	шт	1		

	Наименование и техническая характеристика	Тип, марка, обозначение документа, опросного листа	Код продукции	Поставщик	Ед. измерения	Кол.		Примечания
	Независимый расцепитель AR-AUX-SR 12…24В		AR-AUX-SR-12-24	IEK	шт	1		
	Устройство защиты от дугового пробоя УЗДП63-1 16А		MDP10-16	IEK	шт	1		
	Устройство защиты от дугового пробоя УЗДП63-1 25А		MDP10-25	IEK	шт	13		
	Контактор модульный КМ40-40М АС		MKK21-40-40	IEK	шт	2		
	Шина N "ноль" на DIN-изоляторе ШНИ-6х9-6-Д-С		YNN10-69-6D-K07	IEK	шт	1		
	Шина PEN "земля-ноль" 6х9мм 10/2 (10групп/крепеж по краям)		YNN11-10-100	IEK	шт	1		
	ЩР-4.2							
	Корпус метал. распределительный, навесной на 36 модулей ЩРн-36з-1 36 УХЛ3 IP31, 540х310х120 мм		MKM14-N-36-31-Z	IEK	шт	1		
	Выключатель нагрузки ВН-32 3Р 32А		MNV10-3-032	IEK	шт	1		
	Выключатель автоматический дифференциальный B06S 1P+NP C16 30мА тип АС		AR-B06S-1N-C16C030	IEK	шт	10		
	Устройство защиты от дугового пробоя УЗДП63-1 25А		MDP10-25	IEK	шт	10		
	Шина N "ноль" на DIN-изоляторе ШНИ-6х9-6-Д-С		YNN10-69-6D-K07	IEK	шт	1		
	Шина PEN "земля-ноль" 6х9мм 10/2 (10групп/крепеж по краям)		YNN11-10-100	IEK	шт	1		
	ЩР-5.1							
	Корпус метал. распределительный, навесной на 54 модулей ЩРн-54з-1 36 УХЛ3 IP31, 540х440х120 мм		MKM14-N-54-31-Z	IEK	шт	1		
	Выключатель нагрузки ВН-32 3Р 32А		MNV10-3-032	IEK	шт	1		
	Выключатель автоматический ВА47-29 1Р 2А тип С		MVA20-1-002-C	IEK	шт	1		
	Выключатель автоматический ВА47-29 1Р 10А тип С		MVA20-1-010-C	IEK	шт	1		
	Выключатель автоматический ВА47-29 3Р 20А тип С		MVA20-3-020-C	IEK	шт	1		

	Наименование и техническая характеристика	Тип, марка, обозначение документа, опросного листа	Код продукции	Поставщик	Ед. изме-рения	Кол.		Примечания
	Выключатель автоматический дифференциальный B06S 1P+NP C16 30мА тип AC		AR-B06S-1N-C16C030	IEK	шт	9		
	Выключатель автоматический ВА47-29 1Р 10А тип С		MVA20-1-010-C	IEK	шт	1		
	Независимый расцепитель AR-AUX-SR 12…24В		AR-AUX-SR-12-24	IEK	шт	1		
	Устройство защиты от дугового пробоя УЗДП63-1 16А		MDP10-16	IEK	шт	1		
	Устройство защиты от дугового пробоя УЗДП63-1 25А		MDP10-25	IEK	шт	11		
	Контактор модульный КМ25-40М АС		MKK21-25-40	IEK	шт	1		
	Шина N "ноль" на DIN-изоляторе ШНИ-6х9-6-Д-С		YNN10-69-6D-K07	IEK	шт	1		
	Шина PEN "земля-ноль" 6х9мм 10/2 (10групп/крепеж по краям)		YNN11-10-100	IEK	шт	1		
	ЩР-5.2							
	Корпус метал. распределительный, навесной на 72 модуля ЩРн-72з-1 36 УХЛ3 IP31, 540х600х120 мм		MKM14-N-72-31-Z	IEK	шт	1		
	Выключатель нагрузки ВН-32 3Р 32А		MNV10-3-032	IEK	шт	1		
	Выключатель автоматический ВА47-29 1Р 2А тип С		MVA20-1-002-C	IEK	шт	3		
	Выключатель автоматический ВА47-29 3Р 20А тип С		MVA20-3-020-C	IEK	шт	2		
	Выключатель автоматический ВА47-29 3Р 25А тип С		MVA20-3-025-C	IEK	шт	1		
	Выключатель автоматический дифференциальный B06S 1P+NP C16 30мА тип AC		AR-B06S-1N-C16C030	IEK	шт	12		
	Устройство защиты от дугового пробоя УЗДП63-1 25А		MDP10-25	IEK	шт	14		
	Устройство защиты от дугового пробоя УЗДП63-1 16А		MDP10-16	IEK	шт	3		
	Контактор модульный КМ25-20М АС		MKK21-25-20	IEK	шт	2		
	Контактор модульный КМ40-40М АС		MKK21-40-40	IEK	шт	1		
	Шина N "ноль" на DIN-изоляторе ШНИ-6х9-6-Д-С		YNN10-69-6D-K07	IEK	шт	1		

	Наименование и техническая характеристика	Тип, марка, обозначение документа, опросного листа	Код продукции	Поставщик	Ед. изме-рения	Кол.		Примечания
	Шина PEN "земля-ноль" 6х9мм 10/2 (10групп/крепеж по краям)		YNN11-10-100	IEK	шт	1		
	ЩК							
	Корпус метал. распределительный, навесной на 36 модуля ЩРн-36з-0 У2 IP54, 540х330х120 мм		MKM11-N-36-54-Z	IEK	шт	1		
	Выключатель нагрузки ВН-32 3Р 80А		MNV10-3-080	IEK	шт	1		
	Независимый расцепитель AR-AUX-SR 12…24В		AR-AUX-SR-12-24	IEK	шт	1		
	Выключатель автоматический ВА47-29 3Р 25А тип С		MVA20-3-025-C	IEK	шт	3		
	Выключатель автоматический ВА47-29 1Р 20А тип С		MVA20-1-020-C	IEK	шт	4		
	Устройство защиты от дугового пробоя УЗДП63-1 25А		MDP10-25	IEK	шт	4		
	Устройство защиты от дугового пробоя УЗДП63-1 16А		MDP10-16	IEK	шт	1		
	Шина N "ноль" на DIN-изоляторе ШНИ-6х9-6-Д-С		YNN10-69-6D-K07	IEK	шт	1		
	Шина PEN "земля-ноль" 6х9мм 10/2 (10групп/крепеж по краям)		YNN11-10-100	IEK	шт	1		
	ЩКПБ							
	Корпус метал. распределительный, навесной на 24 модулей ЩРн-24з-1 36 УХЛ3 IP31, 395х310х120 мм		MKM11-N-24-31-Z	IEK	шт	1		
	Выключатель нагрузки ВН-32 3Р 40А		MNV10-3-040	IEK	шт	1		
	Независимый расцепитель AR-AUX-SR 12…24В		AR-AUX-SR-12-24	IEK	шт	1		
	Выключатель автоматический ВА47-29 3Р 25А тип С		MVA20-3-025-C	IEK	шт	2		
	Выключатель автоматический ВА47-29 1Р 16А тип С		MVA20-1-016-C	IEK	шт	2		
	Выключатель автоматический ВА47-29 1Р 10А тип С		MVA20-1-010-C	IEK	шт	2		
	Устройство защиты от дугового пробоя УЗДП63-1 16А		MDP10-16	IEK	шт	2		

	Наименование и техническая характеристика	Тип, марка, обозначение документа, опросного листа	Код продукции	Поставщик	Ед. изме-рения	Кол.		Примечания
	Устройство защиты от дугового пробоя УЗДП63-1 25А		MDP10-25	IEK	шт	2		
	Шина N "ноль" на DIN-изоляторе ШНИ-6х9-6-Д-С		YNN10-69-6D-K07	IEK	шт	1		
	Шина PEN "земля-ноль" 6х9мм 10/2 (10групп/крепеж по краям)		YNN11-10-100	IEK	шт	1		
	ЩКс							
	Корпус метал. распределительный, навесной на 24 модулей ЩРн-24з-1 36 УХЛ3 IP54, 395х310х120 мм		MKM11-N-24-54-Z	IEK	шт	1		
	Выключатель нагрузки ВН-32 3Р 32А		MNV10-3-032	IEK	шт	1		
	Независимый расцепитель AR-AUX-SR 12…24В		AR-AUX-SR-12-24	IEK	шт	1		
	Выключатель автоматический ВА47-29 1Р 25А тип С		MVA20-1-025-C	IEK	шт	4		
	Выключатель автоматический ВА47-29 1Р 10А тип С		MVA20-1-010-C	IEK	шт	1		
	Шина N "ноль" на DIN-изоляторе ШНИ-6х9-6-Д-С		YNN10-69-6D-K07	IEK	шт	1		
	Шина PEN "земля-ноль" 6х9мм 10/2 (10групп/крепеж по краям)		YNN11-10-100	IEK	шт	1		
	ЩВ-2							
	Корпус металлический ЩМП-4-0 (800х650х250мм) У2 IP54		YKM40-04-54	IEK	шт	1		
	Выключатель автоматический ВА47-29 3Р 25А тип D		MVA20-3-025-D	IEK	шт	1		
	Выключатель автоматический ВА47-29 3Р 16А тип D		MVA20-3-016-D	IEK	шт	1		
	Независимый расцепитель AR-AUX-SR 12…24В		AR-AUX-SR-12-24	IEK	шт	1		
	Выключатель автоматический ВА47-29 3Р 10А тип D		MVA20-3-010-D	IEK	шт	7		
	Выключатель автоматический ВА47-29 1Р 20А тип D		MVA20-1-020-D	IEK	шт	2		
	Выключатель автоматический ВА47-29 1Р 10А тип D		MVA20-1-010-D	IEK	шт	4		

	Наименование и техническая характеристика	Тип, марка, обозначение документа, опросного листа	Код продукции	Поставщик	Ед. изме-рения	Кол.		Примечания
	Выключатель автоматический ВА47-29 1Р 10А тип С		MVA20-1-010-C	IEK	шт	1		
	Устройство защиты от дугового пробоя УЗДП63-1 25А		MDP10-25	IEK	шт	2		
	Устройство защиты от дугового пробоя УЗДП63-1 16А		MDP10-16	IEK	шт	5		
	Шина N "ноль" на DIN-изоляторе ШНИ-6х9-6-Д-С		YNN10-69-6D-K07	IEK	шт	1		
	Шина PEN "земля-ноль" 6х9мм 10/2 (10групп/крепеж по краям)		YNN11-10-100	IEK	шт	1		
	ЩВ-0.1							
	Корпус метал. распределительный, навесной на 36 модулей ЩРн-36з-0 У2 IP54, 540х330х120 мм		MKM11-N-36-54-Z	IEK	шт	1		
	Выключатель нагрузки ВН-32 3Р 32А		MNV10-3-032	IEK	шт	1		
	Выключатель автоматический ВА47-29 3Р 10А тип D		MVA20-3-010-D	IEK	шт	5		
	Выключатель автоматический ВА47-29 1Р 20А тип D		MVA20-1-020-D	IEK	шт	1		
	Независимый расцепитель AR-AUX-SR 12…24В		AR-AUX-SR-12-24	IEK	шт	1		
	Выключатель автоматический ВА47-29 1Р 10А тип С		MVA20-1-010-C	IEK	шт	3		
	Устройство защиты от дугового пробоя УЗДП63-1 16А		MDP10-16	IEK	шт	3		
	Шина N "ноль" на DIN-изоляторе ШНИ-6х9-6-Д-С		YNN10-69-6D-K07	IEK	шт	1		
	Шина PEN "земля-ноль" 6х9мм 10/2 (10групп/крепеж по краям)		YNN11-10-100	IEK	шт	1		
	ЩВ-0.2							
	Корпус метал. распределительный, навесной на 54 модуля ЩРн-54з-0 У2 IP54, 540х440х120 мм		MKM11-N-54-54-Z	IEK	шт	1		
	Выключатель нагрузки ВН-32 3Р 32А		MNV10-3-032	IEK	шт	1		
	Независимый расцепитель AR-AUX-SR 12…24В		AR-AUX-SR-12-24	IEK	шт	1		

	Наименование и техническая характеристика	Тип, марка, обозначение документа, опросного листа	Код продукции	Поставщик	Ед. измерения	Кол.		Примечания
	Выключатель автоматический ВА47-29 3Р 10А тип D		MVA20-3-010-D	IEK	шт	5		
	Выключатель автоматический ВА47-29 1Р 10А тип D		MVA20-1-010-D	IEK	шт	15		
	Выключатель автоматический ВА47-29 1Р 10А тип С		MVA20-1-010-C	IEK	шт	2		
	Устройство защиты от дугового пробоя УЗДП63-1 16А		MDP10-16	IEK	шт	10		
	Шина N "ноль" на DIN-изоляторе ШНИ-6х9-6-Д-С		YNN10-69-6D-K07	IEK	шт	1		
	Шина PEN "земля-ноль" 6х9мм 10/2 (10групп/крепеж по краям)		YNN11-10-100	IEK	шт	1		
	Ящик с понижающим трансформатором	ЯТП 0,25кВА 220/36В EKF Basic			шт	4		
	Светотехническое оборудование							
	Светильник светодиодный круглый. Способ монтажа встраиваемый. Габариты светильника 140×30мм. Мощность светильника 20W. Цветовая температура 4000К CRI90. Степень защиты IP54. Укомплектован БАП на 3ч.	RVE-DOT BP IP54 20W 4000K 220V/ Светильник LED встраиваемый с БАП на 3 часа		RVElektro	шт	6		1а
	Светильник светодиодный круглый. Способ монтажа накладной. Габариты светильника 220х50мм. Мощность светильника 25W. Цветовая температура 4000К CRI90. Степень защиты IP54.	RVE-COLLAR IP54 25W 4000K 220V/ Светильник LED накладной		RVElektro	шт	2		2
	Светильник светодиодный круглый. Способ монтажа накладной. Габариты светильника 220х50мм. Мощность светильника 25W. Цветовая температура 4000К CRI90. Степень защиты IP54. Укомплектован БАП на 3ч.	RVE-COLLAR BP IP54 25W 4000K 220V/ Светильник LED накладной с БАП на 3 часа		RVElektro	шт	21		2а
	Светодиодный светильник. Форма Круг. Борт ПВХ. Мощность 62Вт. Световой поток 7440лм. Цветовая температура 4000К CRI90. Габаритные размеры 700х700х100мм. Цвет корпуса Черный. Способ монтажа накладной. Блок питания встроенный. Крепеж Комплект магнитного крепления.	RVE-LBX-RING-PRIME-SC-700-N (Круг d700х100мм 62Вт Накладной 4000К Черный) светильник		RVElektro	шт	26		3
	Светодиодный светильник. Форма Круг. Борт ПВХ. Мощность 62Вт. Световой поток 7440лм. Цветовая температура 4000К CRI90. Габаритные размеры 700х700х100мм. Цвет корпуса Черный. Способ монтажа накладной. Укомплектован БАП на 3ч. Светильник в аварийном режиме светится частично. Блоки питания встроенные. Крепеж Комплект магнитного крепления.	RVE-LBX-RING-PRIME-SC-BP-700-N (Круг d700х100мм 62Вт Накладной 4000К черный БАП 3 часа) светильник		RVElektro	шт	25		3а

Взам. инв.№

Подп. и дата

Инв.№ подл.

	Наименование и техническая характеристика	Тип, марка, обозначение документа, опросного листа	Код продукции	Поставщик	Ед. измерения	Кол.		Примечания
	Светодиодный светильник. Форма Линейный. Мощность 56Вт. (141%) Световой поток 5096лм. Цветовая температура 4000К CRI90. Размеры 1460х50х70мм. Цвет корпуса Чёрный. Сечение профиля 50х70мм. Способ монтажа подвесной. Блок питания встроенный. Крепеж трос 2м. Степень пылевлагозащиты IP54.	RVE-PLS5070-GEARLINE-SC-1460-P-IP54 (Линейный 1460ммх50х70мм 56Вт (141%) Подвесной 4000К Черный) светильник		RVElektro	шт	6		5
	Светодиодный светильник. Форма Линейный. Мощность 56Вт. (141%) Световой поток 5096лм. Цветовая температура 4000К CRI90. Размеры 1460х50х70мм. Цвет корпуса Чёрный. Сечение профиля 50х70мм. Способ монтажа подвесной. Укомплектован БАП на 3ч. Блок питания встроенный. Крепеж трос 2м. Степень пылевлагозащиты IP54. Светильник в аварийном режиме светится частично.	RVE-PLS5070-GEARLINE-SC-BP-1460-P-IP54 (Линейный 1460ммх50х70мм 56Вт (141%) Подвесной 4000К Черный БАП на 3 часа) светильник		RVElektro	шт	3		5а
	Светодиодный светильник. Форма Линейный. Мощность 39Вт. Световой поток 3549лм. Цветовая температура 4000К CRI90. Размеры 1460х50х70мм. Цвет корпуса черный. Сечение профиля 50х70мм. Способ монтажа подвесной. Блок питания встроенный. Крепеж трос 2м.	RVE-PLS5070-GEARLINE-SC-1460-P (Линейный 1460ммх50х70мм 39Вт Подвесной 4000К Черный) светильник		RVElektro	шт	62		6
	Светодиодный светильник. Форма Линейный. Мощность 39Вт. Световой поток 3549лм. Цветовая температура 4000К CRI90. Размеры 1460х50х70мм. Цвет корпуса Чёрный. Сечение профиля 50х70мм. Способ монтажа подвесной. Укомплектован БАП на 3ч. Светильник в аварийном режиме светится частично. Блок питания встроенный. Крепеж трос 2м.	RVE-PLS5070-GEARLINE-SC-BP-1460-P (Линейный 1460ммх50х70мм 39Вт Подвесной 4000К Черный БАП 3 часа) светильник		RVElektro	шт	17		6а
	Светодиодный светильник. Форма Линейный. Мощность 20Вт. (50%) Световой поток 1820лм. Цветовая температура 4000К CRI90. Размеры 1460х50х70мм. Цвет корпуса черный. Сечение профиля 50х70мм. Способ монтажа подвесной. Блок питания встроенный. Крепеж трос 2м.	RVE-PLS5070-GEARLINE-SC-1460-P (Линейный 1460ммх50х70мм 20Вт (50%) Подвесной 4000К Черный) светильник		RVElektro	шт	63		7
	Светодиодный светильник. Форма Линейный. Мощность 20Вт. (50%) Световой поток 1820лм. Цветовая температура 4000К CRI90. Размеры 1460х50х70мм. Цвет корпуса Чёрный. Сечение профиля 50х70мм. Способ монтажа подвесной. Укомплектован БАП на 3ч. Светильник в аварийном режиме светится частично. Блок питания встроенный. Крепеж трос 2м.	RVE-PLS5070-GEARLINE-SC-BP-1460-P (Линейный 1460ммх50х70мм 20Вт (50%) Подвесной 4000К Черный БАП 3 часа) светильник		RVElektro	шт	20		7а
	Светодиодный светильник. Форма Линейный. Мощность 20Вт. (50%) Световой поток 1820лм. Цветовая температура 4000К CRI90. Размеры 1460х50х70мм. Цвет корпуса черный. Сечение профиля 50х70мм. Способ монтажа подвесной. Степень пылевлагозащиты IP54. Блок питания встроенный. Крепеж трос 2м.	RVE-PLS5070-GEARLINE-SC-1460-P-IP54 (Линейный 1460ммх50х70мм 20Вт (50%) Подвесной 4000К Черный) светильник		RVElektro	шт	13		8

Взам. инв.№

Подп. и дата

Инв.№ подл.

Изм.	Кол.уч.	Лист	№ док.	Подпись	Дата

	Наименование и техническая характеристика	Тип, марка, обозначение документа, опросного листа	Код продукции	Поставщик	Ед. измерения	Кол.		Примечания
	Светодиодный светильник. Форма Линейный. Мощность 20Вт. (50%) Световой поток 1820лм. Цветовая температура 4000К CRI90. Размеры 1460х50х70мм. Цвет корпуса Чёрный. Сечение профиля 50х70мм. Способ монтажа подвесной. Укомплектован БАП на 3ч. Светильник в аварийном режиме светится частично. Блок питания встроенный. Степень пылевлагозащиты IP54. Крепеж трос 2м.	RVE-PLS5070-GEARLINE-SC-BP-1460-P-IP54 (Линейный 1460ммх50х70мм 20Вт (50%) Подвесной 4000К Черный БАП 3 часа) светильник		RVElektro	шт	3		8а
	Светодиодный светильник. Форма Линейный. Мощность 26Вт. Световой поток 2366лм. Цветовая температура 4000К CRI90. Размеры 980х50х70мм. Цвет корпуса черный. Сечение профиля 50х70мм. Способ монтажа подвесной. Степень пылевлагозащиты IP54. Блок питания встроенный. Крепеж трос 2м.	RVE-PLS5070-GEARLINE-SC-980-P-IP54 (Линейный 980ммх50х70мм 26Вт Подвесной 4000К Черный) светильник		RVElektro	шт	19		10,11
	Светодиодный светильник. Мощность 38Вт. Световой поток 3700лм. Цветовая температура 4000К CRI90. Широкая КСС. Размеры 595х595х40мм. Способ монтажа накладной с защитной решеткой.	RVE-PRIME-GRIL-SC-595 38W 4000K 220V/ Светильник LED 595x595mm (RVElektro) с защитной решеткой		RVElektro	шт	48		12
	Светодиодный светильник. Мощность 38Вт. Световой поток 3700лм. Цветовая температура 4000К CRI90. Широкая КСС. Размеры 595х595х40мм. Способ монтажа накладной с защитной решеткой. Укомплектован БАП на 3ч.	RVE-PRIME-GRIL-SC-BP-595 38W 4000K 220V/ Светильник LED 595x595mm (RVElektro) с защитной решеткой с БАП 3 часа		RVElektro	шт	10		12а
	Светодиодный светильник. Мощность 38Вт. Световой поток 3700лм. Цветовая температура 4000К CRI90. Размеры 595х595х40мм. Способ монтажа универсальный (встраиваемый в потолоки типа Армстронг, накладной).	RVE-PRIME-SC-595 38W 4000K 220V/ Светильник LED 595x595x40mm (RVElektro) стандартный (встраиваемый, накладной)		RVElektro	шт	360		13
	Светодиодный светильник. Мощность 38Вт. Световой поток 3700лм. Цветовая температура 4000К CRI90. Размеры 595х595х40мм. Способ монтажа универсальный (встраиваемый в потолоки типа Армстронг, накладной). Укомплектован БАП на 3ч.	RVE-PRIME-SC-595-BP 38W 4000K 220V/ Светильник LED 595x595x40mm (RVElektro) стандартный (встраиваемый, накладной с БАП 3 часа)		RVElektro	шт	56		13а
	Светодиодный светильник. Мощность 38Вт. Световой поток 3700лм. Цветовая температура 4000К CRI90. Размеры 600х600х48мм. Способ монтажа встраиваемый в потолоки типа Clip-in. Степень пылевлагозащиты IP54.	RVE-PRIME-CI-SC-595 CLIP-IN IP54 600x600x48 38Вт 4000К Опал		RVElektro	шт	15		15
	Светодиодный светильник. Мощность 38Вт. Световой поток 3700лм. Цветовая температура 4000К CRI90. Размеры 600х600х48мм. Способ монтажа встраиваемый в потолоки типа Clip-in. Степень пылевлагозащиты IP54. Укомплектован БАП на 3ч.	RVE-PRIME-CI-SC-BP-595 CLIP-IN IP54 600x600x48 45Вт 4000К Опал с БАП 3 часа		RVElektro	шт	2		15а

	Наименование и техническая характеристика	Тип, марка, обозначение документа, опросного листа	Код продукции	Поставщик	Ед. измерения	Кол.		Примечания
	Светодиодный светильник 1шт. Мощность 9Вт. Световой поток 800лм. Цветовая температура 4000К CRI90. Габаритные размеры 85х85х40мм. Цвет корпуса белый. Способ монтажа встраиваемый в потолок Грильято с ячейкой 100х100мм и шириной рейки 15мм.	RVE-LBX-CONTRO-SC-10015-1-GR (Квадрат Грильято 1шт 85х85х40мм 9Вт встраиваемый 4000К Белый) светильник		RVElektro	шт	28		16
	Светодиодный светильник 1шт. Мощность 9Вт. Световой поток 800лм. Цветовая температура 4000К CRI90. Габаритные размеры 85х85х40мм. Цвет корпуса белый. Способ монтажа встраиваемый в потолок Грильято с ячейкой 100х100мм и шириной рейки 15мм. Укомплектован БАП на 3ч.	RVE-LBX-CONTRO-SC-BP-10015-1-GR (Квадрат Грильято 1шт 85х85х40мм 9Вт встраиваемый 4000К Белый БАП на 3ч) светильник		RVElektro	шт	11		16а
	Светодиодный светильник 1шт. Мощность 9Вт. Световой поток 800лм. Цветовая температура 4000К CRI90. Габаритные размеры 85х85х40мм. Цвет корпуса белый. Способ монтажа встраиваемый в потолок Грильято с ячейкой 100х100мм и шириной рейки 15мм. Степень пылевлагозащиты IP54.	RVE-LBX-CONTRO-SC-10015-1-GR-IP54 (Квадрат Грильято 1шт 85х85х40мм 9Вт встраиваемый 4000К Белый) светильник		RVElektro	шт	100		17
	Светодиодный светильник 1шт. Мощность 9Вт. Световой поток 800лм. Цветовая температура 4000К CRI90. Габаритные размеры 85х85х40мм. Цвет корпуса белый. Способ монтажа встраиваемый в потолок Грильято с ячейкой 100х100мм и шириной рейки 15мм. Укомплектован БАП на 3ч. Степень пылевлагозащиты IP54	RVE-LBX-CONTRO-SC-BP-10015-1-GR-IP54 (Квадрат Грильято 1шт 85х85х40мм 9Вт встраиваемый 4000К Белый БАП на 3ч) светильник		RVElektro	шт	14		17а
	Светодиодный светильник 1шт. Мощность 9Вт. Световой поток 800лм. Цветовая температура 4000К CRI90. Габаритные размеры 85х85х40мм. Цвет корпуса черный. Способ монтажа встраиваемый в потолок Грильято с ячейкой 100х100мм и шириной рейки 15мм. Степень пылевлагозащиты IP54.	RVE-LBX-CONTRO-SC-10015-1-GR-IP54 (Квадрат Грильято 1шт 85х85х40мм 9Вт встраиваемый 4000К Черный) светильник		RVElektro	шт	64		18
	Светодиодный светильник. Монтаж накладной. Размер 1262х124х85мм. Мощность 38Вт. Световой поток 4800лм.	RVE-PRIME-SLIM-SC-38/(IP65, 4000K) 1262х124х85мм 38Вт		RVElektro	шт	82		21,2
	Светодиодный светильник. Монтаж накладной. Размер 1262х124х85мм. Мощность 38Вт. Световой поток 4800лм. Укомплектован БАП на 3ч.	RVE-PRIME-SLIM-SC-BP-38/(IP65, 4000K) 1262х124х85мм 38Вт с БАП 3 часа		RVElektro	шт	40		21,2а
	Светодиодный светильник. Форма линейнный на двух кронштейнах с поворотным механизмом. Угол свечения 120гр. Мощность 48Вт. Световой поток 4368Лм. Габаритные размеры светильника 2000х500х35мм. Размеры световой части 1930х35х35мм. Цветовая температура 4000К CRI90. Цвет светильника черный. Монтаж на поворотных кронштейнах. Размер кронштейна 500х35х35мм. Блок питания встраиваемый.	RVE-PLS3535-PRIMELINE-SC-2000-K (Линейный 2000х35х35мм 48Вт на кронштейне 500мм 4000К черный) светильник		RVElektro	шт	24		22

Взам. инв.№

Подп. и дата

Инв.№ подл.

Изм.	Кол.уч.	Лист	№ док.	Подпись	Дата

	Наименование и техническая характеристика	Тип, марка, обозначение документа, опросного листа	Код продукции	Поставщик	Ед. измерения	Кол.		Примечания
	Светодиодный светильник. Форма Круг. Борт ПВХ. Мощность 53Вт. (50%) Световой поток 6360лм. Цветовая температура 4000К CRI90. Габаритные размеры 900х900х100мм. Цвет корпуса Черный. Способ монтажа подвесной. Блок питания встроенный. Крепеж Трос 2м.	RVE-LBX-RING-PRIME-SC-900-P (Круг d900х100мм 53Вт (50%) Подвесной 4000К Черный) светильник		RVElektro	шт	47		4
	Светодиодный светильник. Форма Круг. Борт ПВХ. Мощность 53Вт. (50%) Световой поток 6360лм. Цветовая температура 4000К CRI90. Габаритные размеры 900х900х100мм. Цвет корпуса Черный. Способ монтажа подвесной. Укомплектован БАП на 3ч. Светильник в аварийном режиме светится частично. Блоки питания встроенные. Крепеж Трос 2м.	RVE-LBX-RING-PRIME-SC-BP-900-P (Круг d900х100мм 53Вт (50%) Подвесной 4000К черный БАП 3 часа) светильник		RVElektro	шт	31		4a
	Светодиодный светильник с силикатным стеклом. Форма Линейный. Мощность 28Вт. Световой поток 2520лм. Цветовая температура 4000К CRI90. Размеры 1500х57х71мм. Цвет корпуса черный. Сечение профиля 50х70мм. Способ монтажа подвесной. Блок питания встроенный. Крепеж трос 2м. Степень пылевлагозащиты IP54.	RVE-PLS5771-GEARLINE-SC-1500-P-IP54 (Линейный силикатное стекло 1500ммх57х71мм 28Вт Подвесной 4000К Черный) светильник		RVElektro	шт	8		9GL
	Световой указатель постоянного действия HTL FLAT, 240х130х41мм., 3Вт., IP20, БАП 3ч., белый с Пиктограммой "Выход"	FLAT S 240x130 3Вт 20 EM3 WH - EXIT	H600-000-05090	HTL	шт	7		
	Световой указатель постоянного действия HTL FLAT, 240х130х41мм., 3Вт., IP20, БАП 3ч., белый с Пиктограммой "Движение Налево"	FLAT S 240x130 3Вт 20 EM3 WH - EXIT left	H600-000-05091	HTL	шт	4		
	Световой указатель постоянного действия HTL FLAT, 240х130х41мм., 3Вт., IP20, БАП 3ч., белый с Пиктограммой "Движение Направо"	FLAT S 240x130 3Вт 20 EM3 WH - EXIT right	H600-000-05092	HTL	шт	4		
	Световой указатель постоянного действия HTL FLAT, 240х130х41мм., 3Вт., IP20, БАП 3ч., белый с Пиктограммой "Дверь Эвакуационного Выхода"	FLAT S 240x130 3Вт 20 EM3 WH - EXIT straight	H600-000-05093	HTL	шт	32		
	Световой указатель постоянного действия HTL INDEX, 250х130х60мм., 3Вт., IP65, БАП 3ч., белый с Пиктограммой "Выход"	INDEX S 250x130 3Вт 65 EM3 WH - EXIT	H600-000-05094	HTL	шт	11		
	Световой указатель постоянного действия HTL INDEX, 250х130х60мм., 3Вт., IP65, БАП 3ч., белый с Пиктограммой "Движение Направо"	INDEX S 250x130 3Вт 65 EM3 WH - EXIT right	H600-000-05096	HTL	шт	2		

	Наименование и техническая характеристика	Тип, марка, обозначение документа, опросного листа	Код продукции	Поставщик	Ед. измерения	Кол.		Примечания
	Световой указатель постоянного действия HTL INDEX, 250х130х60мм., 3Вт., IP65, БАП 3ч., белый с Пиктограммой "Дверь Эвакуационного Выхода"	INDEX S 250x130 3Вт 65 EM3 WH - EXIT straight	H600-000-05097	HTL	шт	8		
	Световой указатель постоянного действия CCA1005 на светодиодах 3Вт 1,5ч + этикетка самокл. 330х140мм Медпункт	LSSA0-1005-003-K03 LPC10-1-35-13-MEDPUNKT		IEK	шт	1		
	Электроустановочное оборудование							
	Выключатель одноклавишный скрытой установки, IP 20 белый		ERV10-021-10	EKF	шт.	131		
	Выключатель двухклавишный скрытой установки, IP 20 белый		ERV10-023-10	EKF	шт.	24		
	Выключатель трехклавишный скрытой установки, IP 20 белый		ERV10-024-10	EKF	шт.	22		
	Выключатель одноклавишный СП проходной, IP 20 белый		ERV10-025-10	EKF	шт.	8		
	Выключатель двухклавишный СП проходной, IP 20 белый		ERV10-027-10	EKF	шт.	6		
	Выключатель одноклавишный открытой установки, IP 54		EQR16-021-30-54	EKF	шт.	44		
	Выключатель одноклавишный проходной открытой установки, IP 54		EFV10-025-30-54	EKF	шт.	44		
	Лючки напольные/настольные на 2 поста IP44		300004	SPL Кабель- ные си-стемы	шт	8		
	Лючки стальные в уровень пола на 4 постов Вертикально IP44		300020 WP	SPL Кабель- ные си-стемы	шт	77		
	Лючки стальные в уровень пола на 8 постов Вертикально IP44		300026 WP	SPL Кабель- ные си-стемы	шт	56		
	Розетка 220В модульной установки, 1-мест. с защ.конт. цв. Белый для установки в Лючок	16A IP20	200013	SPL Кабель- ные си-стемы	шт	470		
	Розетка 220В скрытой установки, 1-мест. с защ.конт. с защ.штор. белый	16A IP20	ERR16-028-100	EKF	шт	223		
	Рамка 2-местная горизонтальная белая EKF Basic Минск		ERM-G-302-10		шт	89		
	Рамка 3-местная горизонтальная белая EKF Basic Минск		ERM-G-303-10		шт	9		
	Рамка 4-местная горизонтальная белая EKF Basic Минск		ERM-G-304-10		шт	4		
	Коробка установочная С3 блочная для твердых стен D=68х45мм		UKT10-068-045-000-A-S-UO	EKF	шт	402		

Взам. инв.№

Подп. и дата

Инв.№ подл.

	Наименование и техническая характеристика	Тип, марка, обозначение документа, опросного листа	Код продукции	Поставщик	Ед. изме-рения	Кол.		Примечания
	3-проводная клемма, d: 0,08-2,5 мм2, t-85 С, оранж. рычаг		222-413	WAGO	шт	2000		
	5-проводная клемма, d: 0,08-2,5 мм2, t-85 С, оранж. рычаг		222-415	WAGO	шт	1000		
	Коробка КМ41233 распаячная для о/п IP44 RAL7035 (6 вводов)		UKO11-100-100-050-K41-44	DKC	шт	1500		
	Коробка ответвительная FS 100х100х50мм 4р 450В 6А 4кв.мм с каб. вводами и клеммн. IP55 пластик.		FSB11404	DKC	шт	200		
	Кнопка S-Pro67 19 мм с фикс. с красной подсв. 230В EKF PROxima				шт.	8		
	Корпус КП101 для кнопок 1место белый IEK				шт.	8		
	Кабельные изделия							
	Силовой кабель, с медной жилой, изоляцией и оболочкой из ПВХ пониженной пожарной опасности, сечением:	ВВГнг(А)-LSLTх						
	1х95				м	25		
	5х35				м	333		
	5х16				м	255		
	5х10				м	607		
	5х6				м	573		
	5х4				м	1403		
	5х2,5				м	625		
	5х1,5				м	508		
	4х2,5				м	338		
	3х6				м	142		
	3х4				м	392		

	Наименование и техническая характеристика	Тип, марка, обозначение документа, опросного листа	Код продукции	Поставщик	Ед. изме-рения	Кол.		Примечания
	3х2,5				м	4660		
	3х1,5				м	7174		
	Силовой кабель, с медной жилой, изоляцией и оболочкой из ПВХ пониженной пожарной опасности,огнестойкий, сечением:	ВВГнг(А)-FRLSLTх						
	1х120				м	70		
	5х16				м	221		
	5х10				м	281		
	5х6				м	684		
	5х4				м	721		
	5х2,5				м	676		
	4х16				м	43		
	4х10				м	44		
	4х6				м	146		
	4х4				м	73		
	4х1,5				м	3088		
	3х4				м	115		
	3х2,5				м	1194		
	3х1,5				м	1138		
	Силовой кабель, с медной жилой, изоляцией и оболочкой из ПВХ пониженной пожарной опасности, экранированный сечением:	ВВГЭнг(А)- LSLTх						
	4х2,5				м	209		
	4х1,5				м	257		
	3х1,5				м	771		

	Наименование и техническая характеристика	Тип, марка, обозначение документа, опросного листа	Код продукции	Поставщик	Ед. измерения	Кол.		Примечания
	Контрольный кабель, с медной жилой, изоляцией и оболочкой из ПВХ пониженной пожарной опасности, сечением:	КВВГнг(А)-LSLTх						
	5х1				м	35		
	4х1				м	928		
	Силовой кабель, с медной жилой, изоляцией и оболочкой из ПВХ пониженной пожарной опасности,огнестойкий, сечением:	КВВГнг(А)-FRLSLTх						
	5х1				м	35		
	4х1				м	350		
	Материалы							
	Трубы стальные водогазопроводные DуØ32 мм		ГОСТ3262-75		м	300		
	Трубы стальные водогазопроводные DуØ40 мм		ГОСТ3262-75		м	250		
	Труба ПВХ гибкая легкая с протяжкой 25мм	Л ПВХ 25 СП ТУ2247-008-47022248-2002	91925	DKC	м	7500		
	Труба ПВХ гибкая легкая 20мм	Л ПВХ 20 БП ТУ2247-008-47022248-2002	90920	DKC	м	6500		
	Труба ПВХ жёсткая гладкая д.25мм, лёгкая, 3м, цвет серый	ЛЖ ПВХ 25х2000	63920	ДКС	м	300		
	Металлорукав Р3-ЦХ-32				м	50		
	Металлорукав Р3-ЦХ-25				м	115		
	Держатель с защелкой и дюбелем D25мм, полипропилен	25	51325	DKC	шт	15000		
	Держатель с защелкой и дюбелем D20мм, полипропилен	20	51320	DKC	шт	13000		
	Противопожарный терморасширяющийся акриловый герметик ОГНЕЗА ГТ, 3 кг	105039			шт	14		
	Проходка на кровлю Гусак ПГ1 100-1000 с опорной пластиной				шт	6		
	Проходка на кровлю Гусак ПГ1 40-1000 с опорной пластиной				шт	1		

	Наименование и техническая характеристика	Тип, марка, обозначение документа, опросного листа	Код продукции	Поставщик	Ед. измерения	Кол.		Примечания
	Проходка на кровлю Гусак ПГ1 32-1000 с опорной пластиной				шт	2		
	Наконечник медный луженый ТМЛ 6–4–4	ТМЛ 6–4–4	UNP41-006-03-04	IEK	шт	150		
	Наконечник медный луженый ТМЛ 10–5–5	ТМЛ 10–5–5	UNP41-010-05-05	IEK	шт	60		
	Наконечник медный луженый ТМЛ 16–6–6	ТМЛ 16–6–6	UNP41-016-06-06	IEK	шт	40		
	Наконечник медный луженый ТМЛ 35–8–10	ТМЛ 35–8–10	UNP41-035-08-10	IEK	шт	30		
	Наконечник медный луженый ТМЛ 95–10–15	ТМЛ 95–10–15	UNP41-095-10-15	IEK	шт	20		
	Наконечник медный луженый ТМЛ 120–12–17	ТМЛ 120–12–17	UNP41-120-12-17	IEK	шт	20		
	Лотки							
	лоток перфорированный 400х80 L3000		35306	АО ДКС	м	78		
	Винт с крестообразным шлицем М6х10		СМ010610	АО ДКС	шт	125		
	Гайка с насечкой, препятствующей откручиванию М6		СМ100600	АО ДКС	шт	125		
	П-образный профиль PSM, L500, толщ.2,5 мм		BPM2905	АО ДКС	шт	52		
	Шпилька М8х1000		СМ200801	АО ДКС	м	104		
	Шайба с узкими полями М8		СМ240800	АО ДКС	шт	208		
	Гайка с насечкой, препятствующей откручиванию М6		СМ100600	АО ДКС	шт	104		
	Гайка шестигранная М8		СМ110800	АО ДКС	шт	208		
	Шайба М6 кузовная DIN9021		СМ120600	АО ДКС	шт	104		
	Забивной анкер М8		СМ400830	АО ДКС	шт	104		
	Винт с гладкой головкой и квадратным подголовником М6х16		СМ010616	АО ДКС	шт	104		
	Ответвитель DPT Т-образный горизонтальный 400х80 в комплекте скрепежными элементами и соединительными пластинами, необходимыми длямонтажа		36146K	АО ДКС	уп	1		

	Наименование и техническая характеристика	Тип, марка, обозначение документа, опросного листа	Код продукции	Поставщик	Ед. измерения	Кол.		Примечания
	Угол СРО 90 горизонтальный 90° 400х80 в комплекте с крепежными элементами и соединительными пластинами, необходимыми для монтажа		36026K	АО ДКС	уп	9		
	лоток перфорированный 400х50 L3000		35266	АО ДКС	м	69		
	Винт с крестообразным шлицем М6х10		СМ010610	АО ДКС	шт	66		
	Гайка с насечкой, препятствующей откручиванию М6		СМ100600	АО ДКС	шт	66		
	П-образный профиль PSM, L500, толщ.2,5 мм		BPM2905	АО ДКС	шт	48		
	Шпилька М8х1000		СМ200801	АО ДКС	м	96		
	Шайба с узкими полями М8		СМ240800	АО ДКС	шт	192		
	Гайка с насечкой, препятствующей откручиванию М6		СМ100600	АО ДКС	шт	96		
	Гайка шестигранная М8		СМ110800	АО ДКС	шт	192		
	Шайба М6 кузовная DIN9021		СМ120600	АО ДКС	шт	96		
	Забивной анкер М8		СМ400830	АО ДКС	шт	96		
	Винт с гладкой головкой и квадратным подголовником М6х16		СМ010616	АО ДКС	шт	96		
	Ответвитель DPT Т-образный горизонтальный 400х50 в комплекте с крепежными элементами и соединительными пластинами, необходимыми для монтажа		36126K	АО ДКС	уп	3		
	Угол СРО 90 горизонтальный 90° 400х50 в комплекте с крепежными элементами и соединительными пластинами, необходимыми для монтажа		36006K	АО ДКС	уп	1		
	Переходник RRD правосторонний 400/300 H50 в комплекте с крепежными элементами и соединительными пластинами, необходимыми для монтажа		36339K	АО ДКС	уп	1		
	Переходник RRD правосторонний 400/200 H50 в комплекте с крепежными элементами и соединительными пластинами, необходимыми для монтажа		36338K	АО ДКС	уп	3		
	лоток перфорированный 300х50 L3000 толщ.1,0 мм		3526510	АО ДКС	м	55		
	Винт с крестообразным шлицем М6х10		СМ010610	АО ДКС	шт	54		
	Гайка с насечкой, препятствующей откручиванию М6		СМ100600	АО ДКС	шт	54		
	П-образный профиль PSM, L400, толщ.2,5 мм		BPM2904	АО ДКС	шт	30		
	Шпилька М8х1000		СМ200801	АО ДКС	м	60		

Взам. инв.№

Подп. и дата

Инв.№ подл.

	Наименование и техническая характеристика	Тип, марка, обозначение документа, опросного листа	Код продукции	Поставщик	Ед. измерения	Кол.		Примечания
	Шайба с узкими полями М8		СМ240800	АО ДКС	шт	120		
	Гайка с насечкой, препятствующей откручиванию М6		СМ100600	АО ДКС	шт	60		
	Гайка шестигранная М8		СМ110800	АО ДКС	шт	120		
	Шайба М6 кузовная DIN9021		СМ120600	АО ДКС	шт	60		
	Забивной анкер М8		СМ400830	АО ДКС	шт	60		
	Винт с гладкой головкой и квадратным подголовником М6х16		СМ010616	АО ДКС	шт	60		
	Ответвитель DPT Т-образный горизонтальный 300х50 в комплекте с крепежными элементами и соединительными пластинами, необходимыми для монтажа		36125K	АО ДКС	уп	1		
	Угол CPO 90 горизонтальный 90° 300х50 в комплекте с крепежными элементами и соединительными пластинами, необходимыми для монтажа		36005K	АО ДКС	уп	1		
	Переходник RRD правосторонний 300/200 H50 в комплекте с крепежными элементами и соединительными пластинами, необходимыми для монтажа		36337K	АО ДКС	уп	2		
	лоток перфорированный 200х50 L3000 толщ.1,0 мм		3526410	АО ДКС	м	447		
	Винт с крестообразным шлицем М6х10		СМ010610	АО ДКС	шт	444		
	Гайка с насечкой, препятствующей откручиванию М6		СМ100600	АО ДКС	шт	444		
	П-образный профиль PSM, L300, толщ.2,5 мм		BPM2903	АО ДКС	шт	300		
	Шпилька М8х1000		СМ200801	АО ДКС	м	600		
	Шайба с узкими полями М8		СМ240800	АО ДКС	шт	1200		
	Гайка с насечкой, препятствующей откручиванию М6		СМ100600	АО ДКС	шт	600		
	Гайка шестигранная М8		СМ110800	АО ДКС	шт	1200		
	Шайба М6 кузовная DIN9021		СМ120600	АО ДКС	шт	600		
	Забивной анкер М8		СМ400830	АО ДКС	шт	600		
	Винт с гладкой головкой и квадратным подголовником М6х16		СМ010616	АО ДКС	шт	600		

Взам. инв.№

Подп. и дата

Инв.№ подл.

	Наименование и техническая характеристика	Тип, марка, обозначение документа, опросного листа	Код продукции	Поставщик	Ед. измерения	Кол.		Примечания
	Ответвитель DPT Т-образный горизонтальный 200х50 в комплекте скрепежными элементами и соединит. пластинами, необходимыми для монтажа		36124K	АО ДКС	уп	15		
	Угол CPO 90 горизонтальный 90° 200х50 в комплекте с крепежными элементами и соединительными пластинами, необходимыми для монтажа		36004K	АО ДКС	уп	10		
	Угол CPO 45 горизонтальный 45° 200х50 в комплекте с крепежными элементами и соединительными пластинами, необходимыми для монтажа		36064K	АО ДКС	уп	2		
	Переходник RRD правосторонний 200/100 H50 в комплекте с крепежными элементами и соединительными пластинами, необходимыми для монтажа		36333K	АО ДКС	уп	6		
	лоток перфорированный 100х50 L3000 толщ.1,0 мм		3526210	АО ДКС	м	513		
	Винт с крестообразным шлицем М6х10		CM010610	АО ДКС	шт	510		
	Гайка с насечкой, препятствующей откручиванию М6		CM100600	АО ДКС	шт	510		
	Скоба SPC под лоток осн.100 мм		BMT1010	АО ДКС	шт	340		
	Шпилька М8х1000		CM200801	АО ДКС	м	340		
	Гайка с насечкой, препятствующей откручиванию М6		CM100600	АО ДКС	шт	680		
	Гайка с насечкой, препятствующей откручиванию М8		CM100800	АО ДКС	шт	1020		
	Винт с гладкой головкой и квадратным подголовником М6х16		CM010616	АО ДКС	шт	680		
	Анкер-шуруп для бетона с внутренней резьбой М8, 6х55 мм		CM57080655	АО ДКС	шт	340		
	Ответвитель DPT Т-образный горизонтальный 100х50 в комплекте скрепежными элементами и соединит. пластинами, необходимыми для монтажа		36122K	АО ДКС	уп	10		
	Угол CPO 90 горизонтальный 90° 100х50 в комплекте с крепежными элементами и соединительными пластинами, необходимыми для монтажа		36002K	АО ДКС	уп	23		
	Угол CPO 45 горизонтальный 45° 100х50 в комплекте с крепежными элементами и соединительными пластинами, необходимыми для монтажа		36062K	АО ДКС	уп	2		
	лоток перфорированный 100х50 L3000 толщ.1,0 мм (кровля 3 этажа)		3526210	АО ДКС	м	46		Крепление к стене
	Крышка с заземлением на лоток осн.100 L3000		35522	АО ДКС	м	46		
	Винт с крестообразным шлицем М6х10		CM010610	АО ДКС	шт	45		
	Гайка с насечкой, препятствующей откручиванию М6		CM100600	АО ДКС	шт	45		
	Гайка с насечкой, препятствующей откручиванию М6		CM100600	АО ДКС	шт	64		

	Наименование и техническая характеристика	Тип, марка, обозначение документа, опросного листа	Код продукции	Поставщик	Ед. измерения	Кол.		Примечания
	Консоль легкая осн.100 мм		BBL3010	АО ДКС	шт	32		
	Стандартный анкер с болтом М8		CM430850	АО ДКС	шт	64		
	Винт с гладкой головкой и квадратным подголовником М6х16		CM010616	АО ДКС	шт	64		
	Угол вертикальный внутренний 90 градусов 50х100, 1,5 мм, в комплекте с крепежными элементами и соединительными пластинами, необходимыми для монтажа		SIM510K	АО ДКС	уп	2		
	Угол вертикальный внешний 90 градусов 50х100, 1,5 мм, в комплекте с крепежными элементами и соединительными пластинами, необходимыми для монтажа		SOM510K	АО ДКС	уп	2		
	Лестничный лоток 50х400, L3000		LL5040	АО ДКС	м	99		
	Винт с крестообразным шлицем М6х10		CM010610	АО ДКС	шт	64		
	Гайка шестигранная М6		CM110600	АО ДКС	шт	64		
	Шайба стопорная М6		CM220600	АО ДКС	шт	64		
	Стеновое крепление лотка (кронштейн)		LP5000	АО ДКС	шт	198		
	Гайка с насечкой, препятствующей откручиванию М6		CM100600	АО ДКС	шт	792		
	Стандартный анкер с болтом М8		CM430850	АО ДКС	шт	396		
	Винт с гладкой головкой и квадратным подголовником М6х20		CM010620	АО ДКС	шт	792		
	Лестничный лоток 50х200, L3000		LL5020	АО ДКС	м	32		
	Винт с крестообразным шлицем М6х10		CM010610	АО ДКС	шт	6		
	Гайка шестигранная М6		CM110600	АО ДКС	шт	6		
	Шайба стопорная М6		CM220600	АО ДКС	шт	6		
	Стеновое крепление лотка (кронштейн)		LP5000	АО ДКС	шт	24		
	Гайка с насечкой, препятствующей откручиванию М6		CM100600	АО ДКС	шт	96		
	Стандартный анкер с болтом М8		CM430850	АО ДКС	шт	48		

Взам. инв.№

Подп. и дата

Инв.№ подл.

	Наименование и техническая характеристика	Тип, марка, обозначение документа, опросного листа	Код продукции	Поставщик	Ед. измерения	Кол.		Примечания
	Винт с гладкой головкой и квадратным подголовником М6х20		СМ010620	АО ДКС	шт	96		
	Молниезащита и заземление							
	Молниеприёмник-мачта ZANDZ модульный вертикальный 8,3 м с комплектом из 2х креплений к стене (нерж. сталь AISI 304; сечение > 200 мм2)		ZZ-206-0083-3		шт	8		
	ZANDZ Зажим к молниеприёмнику D42 мм для токоотводов (нержавеющая сталь)		ZZ-202-002		шт	8		
	Проволока ZANDZ стальная оцинкованная (D 8 мм / S 50 мм²; бухта 125 м)		ZZ-502-008-125		шт	5		
	Держатель для круглого проводника с возвышением 20 мм (D8-10; внутренняя резьба М6; толщина цинк. покрытия > 30 мкм)		ZZ-202-003		шт	550		
	Зажим ZANDZ для круглого проводника универсальный (D6-10 мм; оцинкованная сталь)		ZZ-202-021		шт	6		
	Зажим ZANDZ для круглого проводника и полосы (D6-10 мм; до 50х6; оцинкованная сталь)		ZZ-202-023		шт	11		
	Держатель с крестовой фиксацией круглого проводника на плоской кровле		ZZ-202-005		шт	50		
	<u>Система уравнивания потенциалов</u>							
	Коробка с шиной заземления (КУП)	КУП2603- И			шт	15		
	Провод ж/з цвета 4мм	ПуГВнг(А)- LSLTX			м	400		
	Провод ж/з цвета 6мм	ПуГВнг(А)- LSLTX			м	150		
	Провод ж/з цвета 25мм	ПуГВнг(А)- LSLTX			м	450		
	Полоса стальная оцинкованная 4х40мм							
	Наконечник кабельный медный луженый	ТМЛ 6–6–4	UNP41-006-06-04	IEK	шт	20		
	Наконечник кабельный медный луженый		UNP41-025-10-08	IEK	шт	20		

	Наименование и техническая характеристика	Тип, марка, обозначение документа, опросного листа	Код продукции	Поставщик	Ед. измерения	Кол.		Примечания
	ОЗДС							
	Оборудование							
	Блок преобразователя импульсный (БПИ)	ИССАН-ОХРА-Д-333 (БПИ УООГ.435144.002)		ООО "ИССАН"	компл.	1		
	Блок высоковольтного усилителя (БВУ)	ИССАН-ОХРА-Д-333 (БВУ УООГ.468741.001)		ООО "ИССАН"	шт	17		
	Барьер электризуемый (БЭ)	ИССАН-ОХРА-Д-333 (БЭП ТУ 16К76-165-2000)		ООО "ИССАН"	Шт/м	17/34		
	Провод высоковольтный ПВМТ-40 сечением 0,35мм	ТУ16.К76-036-90		ООО "ИССАН"	м	34		
	Изделия и материалы							
	Кабель силовой с медными жилами с низким дымо и газовыделением	ВВГнг(А)-LSLTx(2х1,5)		АО "Завод "Энергокабель"	м	935		
	Кабель силовой с медными жилами с низким дымо и газовыделением	ВВГнг(А)-LSLTx(3х1,5)		АО "Завод "Энергокабель"	м	10		
	Труба гофрированная с пониженной горючестью	ПНД НГ D=20мм		АО "Завод "Энергокабель"	м	620		
	Гильзы в стенах и перегородках из труб гладких ПВХ HF d-25			АО "Завод "Энергокабель"	м/шт	6/60		
	Крепеж-скоба (Двухлапковые скобы)	20 скоба двухлапковая		Компания "Промрукав"	шт	320		
	Стяжка нейлоновая неразмыкаемая, белая 100х2,5мм (100шт)	СК100-WT		Компания "Промрукав"	упак.	1		
	Стяжка нейлоновая неразмыкаемая, белая 250х4,0мм (100шт)	СК250-WT		Компания "Альфа-Сети"	упак.	1		
	Самоклеющиеся маркеры, книжка 10 листов, цифры 0-45	WMB-3		Компания "Альфа-Сети"	упак.	1		
	Электроустановочные материалы							
	Коробка ответвительная КРП-1	ТУ 400-28-98-75			шт	9		
	Колодка клеммная	ГОСТ 17557-88			шт	17		
	Штепсельная розетка с заземляющим контактом 16А о/п IP44 IEK	Р С620-3			шт	1		

Взам. инв.№

Подп. и дата

Инв.№ подл.