Департамент капитального ремонта города Москвы Государственное автономное учреждение города Москвы Московский научно-исследовательский и проектный институт жилищного хозяйства «МосжилНИИпроект» (ГАУ «МосжилНИИпроект»)

mgnp@mgnp.mos.ru +7 495 624 40 65 107078, г. Москва, ул. Каланчевская, д. 4/2, стр. 1

Арх. №

Капитальный ремонт здания Государственного бюджетного общеобразовательного учреждения города Москвы «Школа №1574», расположенного по адресу: г. Москва, пер. Старопимновский, д. 5

ПРОЕКТНАЯ ДОКУМЕНТАЦИЯ

Раздел 11. «Мероприятия по обеспечению доступа инвалидов к объекту капитального строительства»

2024-00377-01-0-ОДИ

Том 11

1 этап

2025

Департамент капитального ремонта города Москвы Государственное автономное учреждение города Москвы Московский научно-исследовательский и проектный институт жилищного хозяйства «МосжилНИИпроект» (ГАУ «МосжилНИИпроект»)

mgnp@mgnp.mos.ru +7 495 624 40 65 107078, г. Москва,ул.Каланчевская, д. 4/2, стр. 1

Капитальный ремонт здания Государственного бюджетного общеобразовательного учреждения города Москвы «Школа №1574», расположенного по адресу: г. Москва, пер. Старопимновский, д. 5

ПРОЕКТНАЯ ДОКУМЕНТАЦИЯ

Раздел 3. «Мероприятия по обеспечению доступа инвалидов к объекту капитального строительства»

2024-00377-01-0-ОДИ

Том 11

1 этап

Заместитель директора Н.Р. Нигматулин 11.12.24

Главный инженер проекта Н.М. Пильгуй 11.12.24

2025

Содержание пояснительной записки

Раздел 11

«Мероприятия по обеспечению доступа инвалидов к объекту капитального строительства»

№ п/п	Наименование	Стр.
	Содержание тома	1
	Пояснительная записка	2-9
	Схема планировочной организации земельного участка, с указанием путей перемещения инвалидов	10
	План 1-го этажа. Схема путей перемещения МГН. М 1:100.	11
	План 1-го этажа. Схема путей эвакуации МГН. М 1:100.	12

А) Перечень мероприятий по обеспечению доступа инвалидов к объекта предусмотрен в подпункте в пункта 3 части 7 статьи 51 градостроительного кодекса Российской Федерации

Проектная документация выполнена в соответствии с требованиями Постановления Правительства РФ от 16 февраля 2008 г. № 87 «О составе разделов проектной документации и требованиях к их содержании» на основании гражданско-правового договора, а также технического отчета по обследованию состояния строительных конструкций зданий и сооружений (шифр 626-2023-ТО). В соответствии с заданием капитальный ремонт общеобразовательного учреждения ГБОУ **«Школа № 1574» по адресу: г. Москва, пер. Старопименовский, д. 5**

В соответствии с заданием настоящими проектными решениями, проводимыми в рамках капитального ремонта, не предусмотрено изменение существующего функционального назначения здания и помещений, конструктивных и объемно-планировочных решений, в том числе параметров путей эвакуации и эвакуационных выходов, и иных решений здания, а также не предусмотрено изменение объемно-планировочных и технологических решений помещений (этажей) и техникоэкономических показателей. Проектные решения соответствуют существующему состоянию здания и ранее разработанной и утвержденной проектной документации и остаются без изменений.

В объеме капитального ремонта выполнено восстановление существующих отдельных элементов строительных конструкций и других элементов здания и (или) замена на аналогичные или иные, улучшающие показатели таких конструкций и элементов с учетом требований и параметров, установленных в действующих нормативных документах.

«Мероприятия по обеспечению доступа инвалидов» предусмотрены в рамках разумного приспособления с учетом 4.8 при невозможности обеспечить доступность всего здания в уровне входа сохранен доступ МГН по фактическому положению (п.8.1.2 СП 59.13330.2020).

Фактические архитектурно-планировочные решения объекта обеспечивают доступ в здание маломобильных групп населения (далее по тексту МГН) М1-М4 на первый этаж здания в помещения 102 -вестибюль, 121 – санузел МГН.

Вход в здание осуществляется через главный вход в осях 5-14/В, доступ для МГН М4 осуществляется по пандусу с уклоном 5%, длина наклонных частей которого не более 9м, с промежуточными площадками длиной 1,5м, суммарная длина пандуса 27м

В соответствии с заданием на проектирование в составе персонала сотрудники М1 - М4 не предусмотрены. Так же не предусмотрено обучение школьников категории М1-М4.

Проектная документация на капитальный капитальному ремонту разработана с учетом требований нормативных документов в объеме указанном в п. 14.2 статьи 1 ФЗ № 190:

- Федеральный закон от 30.12.2009г №384-ФЗ «Технический регламент о безопасности зданий и сооружений» (ред. От 02.07.2013г)
- Федеральный закон от 22 июля 2008г №123 ФЗ - «Технический регламент о требованиях пожарной безопасности» (ред.30.04.2021)
- Закона города Москвы от 17.01.2001г (с изменениями от 20 февраля 2019 г.) «Об обеспечении беспрепятственного доступа инвалидов к объектам социальной, транспортной и инженерной инфраструктур г. Москвы»

-СП 118.13330.2022 «Общественные здания и сооружения»

-СП 1.13130.2020 «Системы противопожарной защиты. Эвакуационные пути и выходы»

-СП 59.13330.2020 «Доступность зданий и сооружений для маломобильных групп населения»

-СП 136.13330.2012 «Здания и сооружения. Общие положения проектирования с учетом доступности для маломобильных групп населения (с Изменением 1)»

-ГОСТ Р 52875-2019 «Указатели тактильные наземные для инвалидов по зрению. Технические требования»

б Обоснование принятых конструктивных, объемно-планировочных и иных технических решений обеспечивающих безопасное перемещение инвалидов на объекта указанных в подпункте а настоящего пункта, а также и эвакуацию из указанных объектов в случае пожара или стихийного бедствия

1. Пути движения МГН на участке.

Проектные решения на капитальный ремонт разработаны на 1 этап строительства.

Разработка благоустройства и обеспечение машиноместами входит во 2 этап строительства. Препятствия для перемещения МГН по территории отсутствую**т.**

Входные группы

В соответствии с существующим положением доступ МГН на первый этаж сохранен через 1 доступный вход в осях 5-14/В.

В рамках проводимого капитального ремонта предусмотрена замена финишной отделки ступеней, маршей пандуса и площадок, замена ограждений и поручней на аналогичные, замена финишной отделки козырька, наружного водостока, кровли козырька.

Геометрические параметры входной площадки, лестницы пандуса сохранены по существующему положению без изменений.

Параметры наружной лестницы соответствуют требованиям п 5.1.12, 5.1.13 СП 59.13330.2020.

Ширина лестничного марша внешней лестницы не менее 1,35 м. Ширина проступей не менее 300мм, высота ступеней 150мм. Все ступени лестниц в пределах одного марша одинаковые по форме в плане, по размерам ширины проступи и высоты подъема ступеней. Поперечный уклон ступеней не более 20 ‰. Ступени с подступенками.

С двух сторон лестницы предусмотрена замена существующих непрерывных по всей их длине ограждений и поручней в соответствии с ГОСТ Р 51261.

Высота поручней составляет 1,2 м с устройством боковых поручней на высоте 0,5м и 0,9мот его верхней части до поверхности проступи ступеней. Края поручней со стороны пешеходных путей расположены в одной вертикальной плоскости с границами прохожей части внешней лестницы.

Перед нижним и верхним маршами внешней лестницы предусмотрены завершающие части поручней, которые горизонтальны и выступают за границы лестничных маршей на 0.3м. Форма завершающих частей поручней травмобезопасная с плавным завершением вниз, в сторону ограждения.

На входной площадке лестницы, площадке пандуса и в начале пандуса располагается кнопка вызова персонала.

Лестница оборудована козырьком с водоотводом и освещением.

Параметры наружного пандуса соответствуют требованиям 5.1.14-5.1.16 СП 59.13330.2020 длина марша пандуса не более 9 м при уклоне от 1:20. Ширина марша пандуса в чистоте между поручнями не менее 0,9 м до 1,0 м. Горизонтальные площадки перед началом и после завершения пандуса с размерами прохожей части, не менее 1,8 х1,8м, при каждом изменении направления пандуса не менее - 1,5 х1,5 м. На горизонтальных площадках пандуса для водоотведения предусмотрен продольный уклон в сторону спуска или поперечный уклон от 5 до 10‰. По продольным краям марша пандуса восстанавливаются бортики высотой не менее 0,05 м. Предусмотрена замена двухстороннего ограждения с поручнями на высоте0,9 и 0,7 м верхний и нижний поручни пандуса находиться в одной вертикальной плоскости с границами прохожей части пандуса (краем бортика). Размеры входной площадки с пандусом не менее 2, 2х2.2 , м (6.1.4 СП 59.13330.2020).

Дверные проемы, доступные для инвалидов на креслах-колясках имеют ширину в свету не менее 0,9 м. Двухстворчатые входные двери шириной одной створки не менее 0,9 м. Двери, обеспечивают задержку автоматического закрывания дверей продолжительность не менее 5 с. Входные двери оборудованы доводчиками по ГОСТ Р 6177. Усилие открывания двери не превышает 50 Нм. (6.1.5 СП 59.13330.2020).

Прозрачные полотна дверей на входе в здание, а также прозрачные перегородки выполнены из ударостойкого безопасного стекла СМ4. На прозрачных полотнах дверей и ограждениях (перегородках) предусмотрена яркая контрастная маркировка в форме круга диаметром от 0,1 до 0.2м Расположение контрастной маркировки предусматривается на двух уровнях: 0.9-1,0 м и 1,3- 1,4 м. (6.1.6 СП 59.13330.2020).

Глубина тамбуров при прямом движении и одностороннем открывании дверей не менее 2,45 м при ширине не менее 1,6 м (6.1.8 СП 59.13330.2020). Фактические размеры составляют 2,45х6,65.

В соответствии с п. 6.2.3 СП 59.13330.2020 в тамбурах тактильные напольные указатели не предусмотрены.

В помещении 102 в зоне турников дополнительно к турникетам располагаются существующие калитки для эвакуации. Калитки заменяются на аналогичные, две калитки шириной в чистоте 1460 мм и две калитки шириной в чистоте 1210 мм, таким образом при эвакуации более 50-ти человек ширина выходов через калитки не менее 1,2 м. Предусмотрена замена турникетов на аналогичные шириной прохода в свету не менее 0,95 м, приспособленные для пропуска инвалидов на креслах-колясках (6.1.9 СП 59.13330.2020).

В соответствии с требованиями п 6.2.3, п. 5.1.10 СП 59.13330.2020 на входной площадке главного входа перед входными дверями предусмотрено устройство предупреждающих тактильных напольных указателей по ГОСТ Р 52875 . Тактильный указатель глубиной 500 мм, шириной, равной ширине дверного проема, рифы типа усеченных конусов, усеченных куполов, цилиндров, расположенных в линейном порядке, на расстоянии ширины открывающегося полотна двери от положения двери в закрытом состоянии.

Края первой и последней ступеней по всей длине лестницы расположены противоскользящие полосы, имеющей контрастную окраску по отношению к основному цвету ступеней, ширина полосы 0,08-0,1 м. п. 6.2.8 СП 59.13330.2020.

3 Пути движения МГН в здании

Фактические архитектурно-планировочные решения объекта обеспечивают доступ в здание маломобильных групп населения (далее по тексту МГН) М1-М4 на первый этаж здания в помещения 101-тамбур, 102 -вестибюль, 121– санузел МГН.

Горизонтальные коммуникации.

Ширина путей движения (в коридорах) не менее 1,8 м

При движении по коридору инвалиду на кресле-коляске обеспечено минимальное пространство:

- для поворота на 90 - 1, 2х1,2 м
- разворота на 180 - диаметром 1,4 м.

В тупиковом коридоре сохранена возможность разворота кресла-коляски на 180 . Фактическая высота проходов по всей их длине и ширине в свету не менее 2,1 м.

Подходы к различному оборудованию и мебели по ширине не менее 0,9 м, а при необходимости поворота кресла-коляски на 90 - не менее 1,2 м. Диаметр зоны для самостоятельного разворота на 180 инвалида на кресле-коляске не менее 1,4 м.

Глубина пространства для маневрирования кресла-коляски перед дверь при открывании от себя должна не менее 1,2 м, а при открывании к себе - не менее 1,5 м при ширине не менее 1,5 м.

На участках пола на основных путях движения перед дверными проемами в помещения по ходу движения, открытыми входами на лестничные клетки, открытыми лестничными маршами не предусмотрены предупреждающие тактильные напольные указатели в соответствии с п. 6.2.3 СП 59.13330.2020.

Ширина дверных полотен и открытых проемов в стене, а также выходов из помещений и коридоров на лестничную клетку не менее 0,9 м.

Дверные проемы не имеют порогов и перепадов высот пола. Входные двери и двери тамбуров имеют пороги не более 0,014 м .

На первом этаже, где ожидаются посетители, предусмотрена зона отдыха на два-три места, в том числе для инвалидов на креслах-колясках.

Конструктивные элементы и устройства внутри здания, а также декоративные элементы, размещаемые в габаритах путей движения на стенах и других вертикальных поверхностях, кроме пожарного оборудования, выступающего из стены не более чем на 0,20 м, имеют закругленные края и не выступать более чем на 0,1 м на высоте от 0,7 до 0,1 м от уровня пола. Указатели на отдельно стоящей опоре не выступают более чем на 0,3 м

Ковровые покрытия на путях движения отсутствуют.

4 Пути эвакуации

Пути эвакуации в рамках капитального ремонта не затрагиваются и сохраняются по существующему положению.

Места обслуживания и постоянного нахождения МГН расположены по фактическому положению на минимально возможных расстояниях от эвакуационных выходов из помещений зданий наружу.

Минимальная ширина эвакуационных выходов (дверей) из помещений при замене дверных блоков принята не менее 0,9 м. Ширина горизонтальных участков путей не менее 1, 2м

Полотна дверей на путях эвакуации имеют цвет, который с учетом характера поверхности, освещенности при применении аварийного освещения и пр. обеспечивает контраст не менее 0,7 (70%) относительно цвета стены

На первом этаже МГН группы М4 эвакуируются за пределы здания через выход непосредственно наружу в осях 5-14/В.

Обеспечена освещенность не менее 100 лк на входной площадке главного входа, доступной для МГН, в санузле для МГН (1 пом.), на путях эвакуации. На путях эвакуации предусмотрено аварийное освещение в соответствии с требованиями СП 52.13330.

5 Санитарно-гигиенические помещения

В рамках капитального ремонта существующие планировочные решения сохранены. На первом этаже в зоне вестибюля расположен санузел для МГН- универсальная кабина с центральным расположением унитаза. Санузел предусмотрен для использования всеми категориями граждан. фактические размеры помещения -2,285х2,645

В санузле сбоку от унитаза предусмотрено пространство рядом с унитазом шириной не менее 0,8 м для размещения кресла-коляски, а также крючки для одежды, костылей и других принадлежностей. В санузле сохранено свободное пространство диаметром 1,4 м для разворота кресла-коляски. Двери открываться наружу.

В санузле предусмотрена установка стационарных и откидных опорных поручней, унитаза, имеющего опору для спины высотой 0,45-0.5 м (от уровня пола до поверхности сидения), длиной - 0,7 м. Раковина установлена на высоту до верхнего края не более 0,8 м и свободное пространство для ног не менее 0,75 , глубина 0,5 м.

У двери санузла предусмотрены со стороны ручки информационные таблички помещения (выполненные рельефно-графическим и рельефно-точечным способом), расположенные на высоте от 1,2 до 1,6 м от уровня пола и на расстоянии 0,1-0,5 м от края двери. Санузел оборудован системой двухсторонней громкоговорящей связи в соответствии с заданием на проектирование.

В санузле у раковины для инвалидов применен водопроводный сенсорный кран бесконтактного типа. Применение кранов с раздельным управлением горячей и холодной водой исключено. Унитаз с ручным кнопочным управлением.

В дверях предусмотрено запирающее устройство с открыванием снаружи в экстренных случаях для оказания помощи и знаком индикации занято/свободно.


Снаружи предусмотрена табличка доступный санузел с пиктограммой доступности, из белого акрила 3мм в цвет навигации здания, габаритами 150 х150 мм на высоте 1400 -1600 мм.

Кабины санузлов оборудуются системой связи с диспетчером (дежурным) - устройство вызова-сброса на высоте 1100 мм.

Откидные поручни для унитаза устанавливаются на высоте 0,85м от уровня пола.

Раковина для МГН выполнена на высоте 0,8 м от уровня пола и на расстоянии 0,2 м от боковой стены.

Поручень для раковины примыкает к раковине таким образом, чтобы представитель МГН (в том числе на инвалидной коляске) смог подтянуться к раковине и опереться на поручень, устанавливается на высоте 0,6 м от уровня пола.

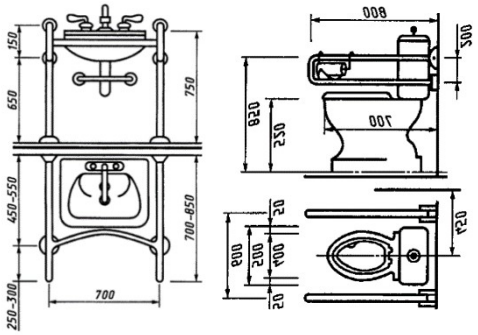


Смеситель для МГН сенсорного управления позволяет действовать без применения излишних усилий, а также крутых поворотов или изгибов руки в запястье. Диспансер для мыла сенсорного управления позволяет действовать без применения излишних усилий, а также препятствует скоплению бактерий. зеркало для МГН установлено на высоте 0,8 м от уровня пола до нижнего края ручки управления.

Электрическую сушилку для рук с сенсорным управлением на высоте 0,7 м от уровня пола до верха сушилки. Сенсорные сушилки для рук препятствуют скоплению бактерий и являются удобным вариантом для представителей МГН, в том числе для инвалидов-колясочников.

Крючки травмобезопасные для МГН предусмотрены рядом с унитазом и раковиной, чтобы легко повесить и снять костыли. Следует размещать крючки с закругленными окончаниями во избежание травмирования.

Поручни для инвалидов по периметру помещения выполнены на высоте 0.7- 0.9м, позволяющей пользоваться ими всем представителям МГН. Завершающие горизонтальные части поручня имеют травмобезопасное исполнение. Поручни округлого сечения диаметром 0,04 м.

Опорные устройства из нержавеющей стали сечением 40 мм в соответствии с ГОСТ Р 51261- 2017. Дверь кабины оборудовать автодоводчиком, а также накладной заверткой типа ЗФ1 по ГОСТ 5090 - 2016 с возможность открывания двери спец ключом снаружи. Открывается наружу. Выключатель света в санузел установлен на высоте 800 мм от пола.

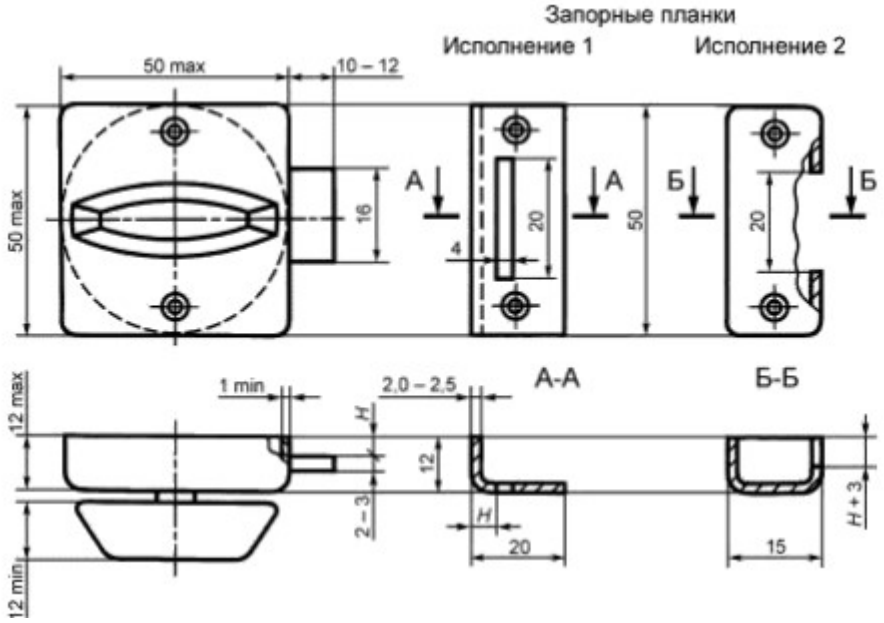

Проектом предусматривается двухсторонняя связь в санузел для МГН: кабина МГН

- пост дежурного. В кабине санузла для инвалидов установлена кнопка тревожного вызова и кнопка отмены вызова (см. раздел «ИОС ») - электронное устройство оповещения для инвалидов различных категорий.

Применяется в экстренных ситуациях нажатием клавиши для вызова обслуживающего персонала.

6. Внутреннее оборудование и устройство здания.

На путях движения маломобильных групп населения по зданию максимально уменьшено количество выступающих углов и острых кромок оборудования.

Скруглять внешние углы выступающих в сторону путей движения частей оборудования в местах ожидания и отдыха (радиус -не менее 5см).

Предусмотрены П-образные не травмирующие дверные ручки, а также механизмы, краны и другие устройства управления или регулирования, позволяющие действовать одной рукой без применения излишних усилий, крутых поворотов или изгибов в запястье.

Обеспечена устойчивость к сдвигу и опрокидыванию стационарного оборудования и мебели.

7. Технические средства информирования ориентирования и сигнализации.

Технические средства информирования, ориентирования и сигнализации, размещаемые в помещениях, предназначенных для пребывания различных категорий инвалидов и МГН, и на путях их движения, должны унифицированы и обеспечивают визуальную, звуковую , радио- и тактильную информацию , и сигнализацию , обеспечивают указание направления движения, идентификацию мест и возможность получения услуги

Технические средства информирования, ориентирования и сигнализации, размещаемые в помещениях, предназначенных для пребывания инвалидов различных категорий и МГН соответствуют требованиям ГОСТ Р 51671-2015 , ГОСТ Р 51885-2002 и ГОСТ Р 52131-2003.

Визуальная информация располагается на контрастном фоне с размерами знаков, соответствующими расстоянию распознавания, увязана с художественным решением интерьера и располагается на высоте не менее 1,5 м и не более 4,5 м от уровня пола.

Кроме визуальной информации предусмотрена звуковая сигнализация.

Предусмотрены световые оповещатели, эвакуационные знаки пожарной безопасности, указывающие направления движения, подключенные к системе оповещения и управления эвакуацией людей при пожаре.

В вестибюле установлены тактильносенсорный информационный терминал, индукционная система для слабослышащих, мнемосхема объекта, адаптивная система оповещения для восприятия передаваемой информации всеми посетителями заведения, включая даже такие категории инвалидов, как тотально незрячие и глухие. На прозрачных полотнах дверей предусмотрена яркая контрастная маркировка в форме круга. Замкнутое пространство здания (санузел для МГН), где инвалид может оказаться один, оборудовано системой связи с диспетчером или дежурным. Система связи снабжена звуковыми и визуальными аварийными сигнальными устройствами. В санузле для МГН предусмотрено аварийное освещение. В санузле для МГН тревожный сигнал или извещатель выводится в дежурную комнату (пост охраны). В коридоре на расстоянии 0,1-0,5 м от края двери санузла МГН и на высоте 1,2 -1,6м от уровня пола предусмотрена тактильная мнемосхема размещения санитарногигиенического оборудования санузла.

Перед входом установлено устройства для оповещения инвалидов категории С (незрячие лица) - звуковые маяки, и устройства для оповещения инвалидов категории Г (тотально глухие лица) -световые маяки, которые оповещают о месте нахождения входа в помещение.

в Описание проектных решений по обустройству рабочих мест инвалидов при необходимости

Рабочих мест для инвалидов не предусмотрено по заданию на проектирование.

ТЕРРИТОРИЯ ОБЪЕДИНЕННЫХ ОХРАННЫХ ЗОН ОКН

ТЕРРИТОРИЯ ОКН

1к.пр.

2тр.пр.

ГАЗОН

162.86

162.78

162.79

162.65

162.62

162.63

162.53

162.45

162.36

162.55

162.52

ФЛАГШТОК

КЛЕН

ТОПОЛЬ

АГИТ.

3тр.пр.

Нависающая часть (козырек)

СПОРТ ПЛ.

Н/Н

Ц

Л

А

СТАРОПИМЕНОВСКИЙ ПЕРЕУЛОК

- Асфальтобетонное покрытие
- Газон
- Здание капитального ремонта
- Вход в здание
- Эвакуационных выход

							2024-00375-00-0-ОДИ
Изм.	Кол.уч.	Лист	№док.	Подп.	Дата		Здания Государственного бюджетного общеобразовательного учреждения города Москвы "Школа № 1574", расположенного по адресу:г. Москва, пер. Старопименовский, д. 5
Разработал		Рахманова			10.25		
ГИП		Пильгуй			10.25	Капитальный ремонт	Стадия: П; Лист: 1; Листов:
Н.Контр.		Нигматулин			10.25	Схема планировочной организации земельного участка, с указанием путей перемещения инвалидов	МОСЖИЛ НИИПРОЕКТ

Согласовано

Взам. инв. №

Подп. и дата

Инв. №подл.

Экспликация помещений 1 этажа

Номер помещения	Наименование	Площадь, м2	Кат. помещения
101	Тамбур	18,09	
102	Вестибюль	79,49	
103	Гардеробная для обучающихся	94,58	
104	Учебный кабинет	57,67	
105	Тамбур	18,37	
106	Лестничная клетка тип Н2	22,57	
107	Процедурный (прививочный) кабинет	22,14	
108	Место для приготовления дезинфицирующих растворов и хранения уборочного инвентаря	10,35	В4
109	Кабинет врача	23,64	
110	Зона ожидания посетителей	20,55	
111	Кладовая	15,75	В3
112	Санузел для девочек с комнатой личной гигиены	7,99	
113	ПУИ	3,70	В4
114а	Коридор	83,40	
1146	Коридор	75,18	
115	Технологическая лестница	13,98	
119	Санузел для мальчиков	5,69	
120	Санузел для персонала	3,40	
121	Санузел для МГН	6,40	
122	Комната охраны	20,95	
123	Кроссовая	9,82	В4
124	Административный кабинет тип 1	19,95	
125	Гардеробная комната для учителей	13,02	
126	Учебный кабинет	65,15	
127	Тамбур	10,38	
128	Лестничная клетка тип Л1	33,63	
129	Коридор	10,06	
130	Умывальная	13,97	
131	Обеденный зал	169,16	
132	Холодный цех	6,57	В4
133	Горячий цех	41,96	В3
134	Моечная столовой посуды	23,00	В4
135	Моечная кухонной посуды	8,66	В4
136	Доготовочный цех	13,73	В3
137	Техническое помещение (электрощитовая)	23,30	В3
138	Техническое помещение (электрощитовая)	21,83	В3
139	Лестничная клетка лип Л1	13,32	
140	Коридор	40,06	
140а	Тамбур	3,45	
1406	помещение холодильного оборудования	15,31	В3
141	Кладовая сухих продуктов	9,82	В4
142	Санузел	2,68	
143	Помещение для персонала	9,91	
143а	Душ	3,52	
144	Загрузочный цех	5,78	В4
145	Кладовая и моечная оборотной тары	7,17	В4
146	Помещение для временного хранения пищевых отходов	6,35	В4
147	ПУИ	3,46	В4
		1 208,91 м²	

Путь передвижения М1-М3

Путь передвижения М4


Условные обозначения

- Существующие стены
- Восстановление кирпичной кладки
- Утеплитель минераловатный
- Заменяемые перегородки из глиняного полнотелого кирпича, толщиной 120мм
- Заменяемые перегородки из газобетона, толщиной 120мм, плотность D600
- Заменяемая обшивка из ГКЛВ
- Ж - Заменяемые внутренние витражи

120 / 89,0 м² - Номер помещения

0,000 - Отметка чистого пола

поз	Наименование	Кол-во
1	Унитаз для инвалидов соответствующий нормам DSTRANA	1
2	Поручень откидной без бумагодержателя по ГОСТ 900х150 мм h до верхнего края +770	1
3	Поручень для туалета напольный для инвалидов П-образный с бумагодержателем по ГОСТ 900х750 мм, универсальный	1
4	Чаша для санузла 15 л	1
5	Автоматический диспенсер для туалетной бумаги h=1000	1
6	Система вызова помощи в санузел с кнопкой со шнуром А310м h до центра=820	1
7	Сенсорный дозатор для людей с ограниченными возможностями 210х140х105 мм, 450мл h=1000	1
8	Поручень для раковины Икуполярный 600мм h до верхнего края=850	2
9	Сенсорный смеситель с термостатом для санузла для инвалидов (для раковин 4624, 6926)	1
10	Раковина для инвалидов DSTRANA 640х550х165мм h до верхнего края=800	1
11	Зеркало настенное поворотное h до нижнего края =1100	1
12	Сушилка для рук для МГН h=1100	1
13	Крючок-держатель для простей и других вещей h=900-1100	1
14	Тактильно-визуальный знак "Туалет для инвалидов" h=1200- 1600	1
15	Поручень прямой настенный 600мм	1
16	Поручень-опора регулируемая с подушкой для спины в санитарно-гигиенические комнаты 250-370х650 мм h=850	1
17	Универсальный противобезопасный держатель (крючок) из нержавеющей стали h до центра=1200	1
*	Плоский сифон для раковин арт. 4624, 6926	1

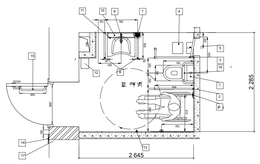


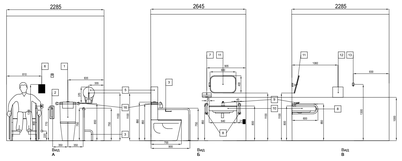


Схема установки поручня на дверь

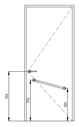

№1	ВЫХОД	- выход из помещения, фотолюминесцентный (размещается над дверями, ведущими к выходу. Устанавливаются над дверным проемом). См. раздел ИОС 5.4
№3.1		- выход для инвалидов на кресле-коляске, диапазон размещения от 1,7 до 2,2м)
№4		- направляющая стрелка,(диапазон размещения от 1,7 до 2,2м)
№5		- Место кратковременного отдыха или ожидания для инвалидов (размещается на высоте от 1,2 до 1,6 м)
№6		- Направление движения (размещается на высоте от 1,2 до 1,6 м)
№7	WC СЛУШАЙТЕ	- санузел для инвалидов (размещается на высоте от 1,2 до 1,6 м)
№8		- Указатель информации, мест расположения мнемосхем (размещается на высоте от 1,2 до 1,6 м)
1	НЕ ЗАБЫВАЙТЕ	- адаптивная система оповещения "Сурдоцентр"
1		- доступность объектов для инвалидов по зрению и по слуху, а также в креслах-колясках (размещается на высоте от 1,2 до 1,6 м)
2		-тактильная табличка Вход в помещение (размещается на высоте от 1,2 до 1,6 м)

3	WC	-тактильная табличка "туалет", с дублированием на шрифт Брайля (размещается рядом с дверью на высоте от 1,2 до 1,6 м со стороны дверной ручки)
4		-Мнемосхема тактильная для санузла (размещается на высоте от 1,2 до 1,6 м)
5		-Мнемосхема тактильная этажа, полноцветная на основе оргстекла (размещается на высоте от 1,2 до 1,6 м)
7		-тактильная табличка "Кнопка бызова экстренной помощи", с дублированием на шрифт Брайля (размещается над кнопкой бызова помощи)
1.1		- предупреждающий тактильный указатель выполняется тактильными конусами в линейном порядке. Ширина поля тактильных указателей - по ширине лестницы, двери, глубина поля – 50 или 60 см.п. 5.1.10 СП 59.13330.2020, ГОСТ Р 52875-2018
		- лента контрастная для маркировки ступеней, ширина 100мм, цвет - желтый
		-тактильные наклейки на поручни, ПВХ желтый/прозрачный 40х160 мм
		Контрастные круги диаметром от 0,1 до 0,2 м устанавливаются на уровнях 0,9–1,0 м и 1,3–1,4 м от поверхности, наносится с наружной и внутренней стороны дверного полотна.п. 6.1.6 СП 59.13330.2020

					2024-00375-00-0-ОДИ	
					Здания Государственного бюджетного общеобразовательного учреждения города Москвы "Школа № 1574", расположенного по адресу:г. Москва, пер. Старопименовский, д. 5	
Изм.	Кол.уч.	Лист	№док.	Подп.	Дата	
Разработал		Романова			10.25	Капитальный ремонт
ГИП		Пильуй			10.25	
Н.Контр		Нигматулин			10.25	План 1-го этажа. Схема путей перемещения МГН. М 1:100.

Стадия	Лист	Листов
П	2	


МОСЖИЛ НИИПРОЕКТ

Согласовано

Взам. инв. №

Подп. и дата

Инв. №подл.

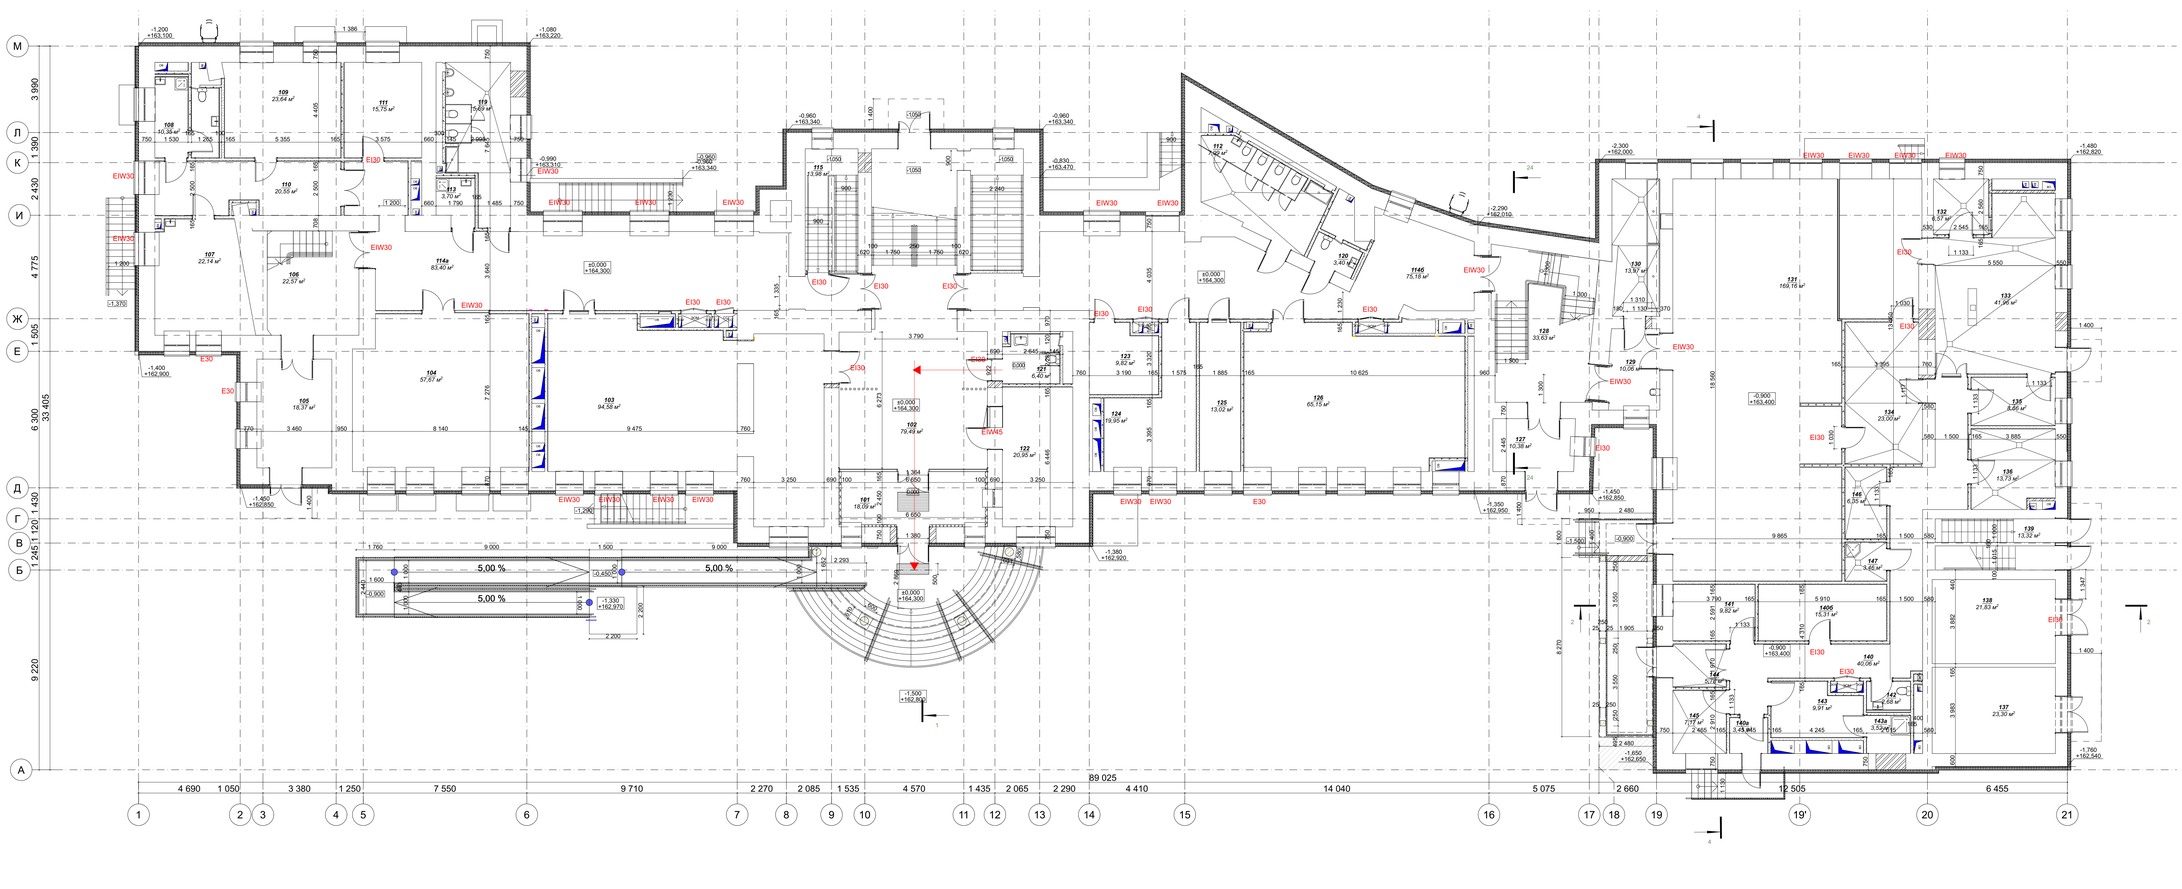

Экспликация помещений 1 этажа

Номер помещения	Наименование	Площадь, м2	Кат. помещения
101	Тамбур	18,09	
102	Вестибюль	79,49	
103	Гардеробная для обучающихся	94,58	
104	Учебный кабинет	57,67	
105	Тамбур	18,37	
106	Лестничная клетка тип Н2	22,57	
107	Процедурный (прививочный) кабинет	22,14	
108	Место для приготовления дезинфицирующих растворов и хранения уборочного инвентаря	10,35	В4
109	Кабинет врача	23,64	
110	Зона ожидания посетителей	20,55	
111	Кладовая	15,75	В3
112	Санузел для девочек с комнатой личной гигиены	7,99	
113	ПУИ	3,70	В4
114а	Коридор	83,40	
1146	Коридор	75,18	
115	Технологическая лестница	13,98	
119	Санузел для мальчиков	5,69	
120	Санузел для персонала	3,40	
121	Санузел для МГН	6,40	
122	Комната охраны	20,95	
123	Кроссовая	9,82	В4
124	Административный кабинет тип 1	19,95	
125	Гардеробная комната для учителей	13,02	
126	Учебный кабинет	65,15	
127	Тамбур	10,38	
128	Лестничная клетка тип Л1	33,63	
129	Коридор	10,06	
130	Умывальная	13,97	
131	Обеденный зал	169,16	
132	Холодный цех	6,57	В4
133	Горячий цех	41,96	В3
134	Моечная столовой посуды	23,00	В4
135	Моечная кухонной посуды	8,66	В4
136	Доготовочный цех	13,73	В3
137	Техническое помещение (электрощитовая)	23,30	В3
138	Техническое помещение (электрощитовая)	21,83	В3
139	Лестничная клетка лип Л1	13,32	
140	Коридор	40,06	
140а	Тамбур	3,45	
1406	помещение холодильного оборудования	15,31	В3
141	Кладовая сухих продуктов	9,82	В4
142	Санузел	2,68	
143	Помещение для персонала	9,91	
143а	Душ	3,52	
144	Загрузочный цех	5,78	В4
145	Кладовая и моечная оборотной тары	7,17	В4
146	Помещение для временного хранения пищевых отходов	6,35	В4
147	ПУИ	3,46	В4
		1 208,91 м²	

Путь эвакуации

Условные обозначения

- Существующие стены
- Восстановление кирпичной кладки
- Утеплитель минераловатный
- Заменяемые перегородки из глиняного полнотелого кирпича, толщиной 120мм
- Заменяемые перегородки из газобетона, толщиной 120мм, плотность D600
- Заменяемая облицовка из ГКЛВ
- Заменяемые внутренние витражи

120 / 89,0 м² - Номер помещения

0.000 - Отметка чистого пола

Согласовано

Взам. инв. №

Подп. и дата

Инв. №подл.

Изм.	Кол.уч.	Лист	№док.	Подп.	Дата
Разработал		Романова			10.25
ГИП		Пильуй			10.25
Н.Контр		Нигматулин			10.25

2024-00375-00-0-ОДИ

Здания Государственного бюджетного общеобразовательного учреждения города Москвы "Школа № 1574", расположенного по адресу:г. Москва, пер. Старопименовский, д. 5

Капитальный ремонт

Стадия	Лист	Листов
П	3	

План 1-го этажа. Схема путей эвакуации МГН. М 1:100.

МОСЖИЛ НИИПРОЕКТ