Департамент капитального ремонта города Москвы Государственное автономное учреждение города Москвы Московский научно-исследовательский и проектный институт жилищного хозяйства «МосжилНИИпроект» (ГАУ «МосжилНИИпроект»)

mgnp@mgnp.mos.ru +7 495 624 40 65 107078, г. Москва, ул. Каланчевская, д. 4/2, стр. 1

Арх. №

Капитальный ремонт здания государственного бюджетного общеобразовательного учреждения города Москвы "Школа № 1574", расположенное по адресу: г. Москва, пер. Старопименовский, д. 5

ПРОЕКТНАЯ ДОКУМЕНТАЦИЯ

Раздел 10. Требования к обеспечению безопасной эксплуатации объектов капитального строительства Подраздел 1. Мероприятия по противодействию террористическим актам.

Том 10.1

2024-00375-01-0-ПТА

2024 г.

Департамент капитального ремонта города Москвы Государственное автономное учреждение города Москвы Московский научно-исследовательский и проектный институт жилищного хозяйства «МосжилНИИпроект» (ГАУ «МосжилНИИпроект»)

mgnp@mgnp.mos.ru +7 495 624 40 65 107078, г. Москва,ул.Каланчевская, д. 4/2, стр. 1

Капитальный ремонт здания государственного бюджетного общеобразовательного учреждения города Москвы "Школа № 1574", расположенное по адресу: г. Москва, пер.Старопименовский, д. 5

ПРОЕКТНАЯ ДОКУМЕНТАЦИЯ

Раздел 10. Требования к обеспечению безопасной эксплуатации объектов капитального строительства Подраздел 1. Мероприятия по противодействию террористическим актам.

Том 10.1

2024-00375-01-0-ПТА

Заместитель директора 09.10.24 Н.Р. Нигматулин

Главный архитектор проекта 09.10.24 О.О. Ходос

2024 г.

СОСТАВ ПРОЕКТНОЙ ДОКУМЕНТАЦИИ

1 этап

См. том 1.1

Взам. инв. №

Подпись и дата

Инв. № подл.

Изм.	Кол.	Лист	№док	Подпись	Дата
Разработал		Фугельзанг Е.А.			
ГАП		Шведов В.В.			
Н.контроль		Фугельзанг Е.А.			
Нач.М-1		Чередниченко В.В.			

2024-00375-01-0-ПТА


Капитальный ремонт здания ГБОУ города Москвы "Школа № 1574", расположенное по адресу: г. Москва, пер.Старопименовский, д. 5

Стадия	Лист	Листов
П	2	43

МОСЖИЛ НИИПРОЕКТ

ТЕКСТОВАЯ ЧАСТЬ

1. СПИСОК РАЗРАБОТЧИКОВ РАЗДЕЛА

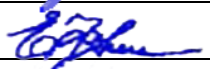Должность	*ФИО*	*Подпись*	*Дата*
Главный инженер проекта	Шведов В.В.		
Инженер-проектировщик	Фугельзанг Е.А.		

Взам. инв. №

Подпись и дата

Инв. № подл.

Изм.	Кол.	Лист	№док	Подпись	Дата

2024-00375-01-0-ПТА

Разработал	*Фугельзанг Е.А.*	
ГАП	*Шведов В.В.*	
Н.контроль	*Фугельзанг Е.А.*	
Нач.М-1	*Чередниченко В.В.*	

Капитальный ремонт здания ГБОУ города Москвы "Школа № 1574", расположенное по адресу: г. Москва, пер.Старопименовский, д. 5

Стадия	*Лист*	*Листов*
П	*3*	*43*

МОСЖИЛ НИИПРОЕКТ

2. ЗАВЕРЕНИЯ ПРОЕКТНОЙ ОРГАНИЗАЦИИ

Проектная документация разработана в соответствии с градостроительным планом земельного участка, заданием на проектирование, градостроительным регламентом, документами об использовании земельного участка для строительства, техническими регламентами, в том числе устанавливающими требования по обеспечению безопасной эксплуатации зданий, строений, сооружений и безопасного пользования эксплуатации зданий, строений, сооружений и безопасного пользования прилегающих к ним территорий, и с соблюдением технических условий.

Главный инженер проекта: В.В. Шведов

Взам. инв. №

Подпись и дата

Инв. № подл.

Изм.	Кол.	Лист	№док	Подпись	Дата

2024-00375-01-0-ПТА

Разработал	Фугельзанг Е.А.	
ГАП	Шведов В.В.	
Н.контроль	Фугельзанг Е.А.	
Нач.М-1	Чередниченко В.В.	

Капитальный ремонт здания ГБОУ города Москвы "Школа № 1574", расположенное по адресу: г. Москва, пер.Старопименовский, д. 5

Стадия	Лист	Листов
П	4	43

МОСЖИЛ НИИПРОЕКТ

3. ОБЩИЕ ПОЛОЖЕНИЯ

3.1 Данные об организации-разработчике проектной документации «Мероприятия по противодействию террористическим актам»

Мероприятия по противодействию террористическим актам (далее по тексту - «ПТА») разработан государственным автономное учреждение ГАУ «МосжилНИИпроект» (далее по тексту - ГАУ «МосжилНИИпроект»),

Юридический (фактический) адрес: Российская Федерация, 107078, г. Москва, Каланчевская ул. д.4/2, стр.1, телефон: (495) 624-40-65, сайт организации: mgnp.ru.

3.2 Сведения о наличии у организации-разработчика проектной документации «Мероприятия по антитеррористической защищенности» свидетельства, выданного саморегулируемой организацией

ГУП «МосжилНИИпроект» имеет допуск к виду или видам работ, которые оказывают влияние на безопасность объектов капитального строительства Выписка из реестра членов саморегулируемой организации № 622 от 21.12.2017 (приложение А).

3.3 Исходные данные, полученные для разработки мероприятия по антитеррористической защищенности

Для разработки ПТА получены проектные материалы и исходные данные от Заказчика (задание на проектирование, градостроительный план земельного участка и т. д.).

ПТА разработаны в соответствии с:

- Указом Президента Российской Федерации от 15.02.2006 № 116 «О мерах по противодействию терроризму»;

- Федеральным законом от 06.03.2006 № 35-ФЗ «О противодействии терроризму»;

- ПП РФ от 02.08.2019 № 1006 "Об утверждении требований к антитеррористической защищенности объектов (территорий) Министерства просвещения Российской Федерации и объектов (территорий), относящихся к сфере деятельности Министерства просвещения Российской Федерации, и формы паспорта безопасности этих объектов (территорий)".

- Градостроительным кодексом Российской Федерации (Федеральный закон от 29.12.2006 № 190-ФЗ);

- Федеральным законом от 21.12.1996 № 68-ФЗ «О защите населения и территорий от чрезвычайных ситуаций природного и техногенного характера»;

- Федеральным законом от 30.12.2009 № 384-ФЗ «Технический регламент о безопасности зданий и сооружений»;

- Постановлением Правительства Российской Федерации от 16.02.2008 № 87 «О составе разделов проектной документации и требованиях к их содержанию»;

- Сводом Правил СП 132.13330.2011 «Обеспечение антитеррористической защищенности зданий и сооружений. Общие требования проектирования».

Проектные решения по ПТА направлены на обеспечение защиты проектируемого объекта от угроз террористического характера и несанкционированного вторжения.

Реализация проектных решений, содержащихся в подразделе ПТА, осуществляется путём их учёта при разработке рабочей документации (на следующей стадии проектирования) и в процессе строительства.

3.4. Краткая характеристика проектируемого объекта

Здание, подлежащее капитальному ремонту, государственного бюджетного общеобразовательного учреждения города Москвы "Школа № 1574", расположенное по адресу: г. Москва, пер. Старопименовский, д. 5

Взам. инв. №

Подпись и дата

Инв. № подл.

Изм.	Кол.	Лист	№док	Подпись	Дата	**2024-00375-01-0-ПТА**			
Разработал		Фугельзанг Е.А.				Капитальный ремонт здания ГБОУ города Москвы "Школа № 1574", расположенное по адресу: г. Москва, пер.Старопименовский, д. 5	Стадия	Лист	Листов
ГАП		Шведов В.В.					П	5	43
Н.контроль		Фугельзанг Е.А.					МОСЖИЛ НИИПРОЕКТ		
Нач.М-1		Чередниченко В.В.							

Согласно Федерального закона от 30.12.2009 года №384-ФЗ (ред. от 02.07.2013) «Технический регламент о безопасности зданий и сооружений», здание относится к сооружениям «нормального» уровня ответственности.

Идентификационные сведения объекта защиты:

1. *Уровень ответственности – II нормальный (согласно ФЗ № 384 от 30.12.2009);*
2. *Степень огнестойкости – I (не ниже II);*
3. *Класс конструктивной пожарной опасности – С0;*

Класс функциональной пожарной опасности: Ф 4.1 здания общеобразовательных организаций, организаций дополнительного образования детей, профессиональных образовательных организаций.

Вместимость рассматриваемого здания составляет 400 учащихся и Административно управленческий персонал
Организационно-педагогическая структура школы:
Начальна школа (1-4 классы)- 8 классов (160 чел.),
Основная школа (5-9 классы) - 10 классов (200 чел.),
Старшая школа (10-11 классы) - 2 классов (40 чел.)
Наполняемость - 400 учащихся, (количество классов: 20).

Обучение происходит по государственным общеобразовательным программам, утвержденным Российской академией наук.
Проведение работ по капитальному ремонту здания школы предусматривает сохранение существующей функциональной схемы размещения помещений.

В соответствии с требованиями Федерального закона № 384-ФЗ «Технический регламент о безопасности зданий и сооружений» объект идентифицируется по следующим признакам:

1) Функциональное назначение здания:
***Вид** - объект общего образования.*
***Функциональное назначение**: Блок начальных классов и общеобразовательная организация.*
2) принадлежность к объектам транспортной инфраструктуры и др. функционально-технологические особенности, которые влияют на их безопасность - не принадлежит;
3) возможность опасных природных процессов, явлений и техногенных воздействий на территории строительства - отсутствуют;
4) принадлежность к опасным производственным объектам - не принадлежит;
5) пожарная и взрывопожарная опасность здания - ГО;
6) наличие помещений с постоянным пребыванием людей - предусмотрено (помещения 1-4-го этажей, кроме помещений подвала);
7) уровень ответственности - нормальный;
8) степень огнестойкости зданий и сооружений - II;
9) класс функциональной пожарной опасности:

- *Ф4.1 - школа;*

Взам. инв. №

Подпись и дата

Инв. № подл.

Изм.	Кол.	Лист	№док	Подпись	Дата	**2024-00375-01-0-ПТА**			
Разработал		Фугельзанг Е.А.				Капитальный ремонт здания ГБОУ города Москвы "Школа № 1574", расположенное по адресу: г. Москва, пер.Старопименовский, д. 5	Стадия	Лист	Листов
ГАП		Шведов В.В.					П	6	43
Н.контроль		Фугельзанг Е.А.					МОСЖИЛ НИИПРОЕКТ		
Нач.М-1		Чередниченко В.В.							

Проектная документация разработана в соответствии с заданием на проектирование, градостроительным регламентом, техническими регламентами, в том числе устанавливающими требованиями по обеспечению безопасной эксплуатации зданий, строений, сооружений и безопасного использования прилегающих к ним территориям, и с соблюдением технических условий

4. МЕРОПРИЯТИЯ И ПРОЕКТНЫЕ РЕШЕНИЯ, НАПРАВЛЕННЫЕ НА ОБЕСПЕЧЕНИЕ ЗАЩИТЫ ОБЪЕКТА ОТ УГРОЗ ТЕРРОРИСТИЧЕСКОГО ХАРАКТЕРА И НЕСАНКЦИОНИРОВАННОГО ВТОРЖЕНИЯ

Мероприятия по обеспечению антитеррористической защищенности данного объекта применены согласно Свода Правил СП 132.13330.2011 «Обеспечение антитеррористической защищенности зданий и сооружений. Общие требования проектирования», а также раздела III. «Мероприятия по обеспечению антитеррористической защищенности объектов (территорий)» ПП РФ от 2 августа 2019 г. № 1006 “Об утверждении требований к антитеррористической защищенности объектов (территорий) Министерства просвещения Российской Федерации и объектов (территорий), относящихся к сфере деятельности Министерства просвещения Российской Федерации, и формы паспорта безопасности этих объектов (территорий)”;

Согласно разд. VI Требований паспорт безопасности требует корректировки после реализации в рамках проведения капитального ремонта проектных решений направленных на обеспечение защиты объекта от угроз террористического характера и несанкционированного вторжения.

В соответствии с пунктом №17, на нашем объекте антитеррористическая защищенность объекта и территории, обеспечивается путем осуществления комплекса мер:

а) на воспрепятствование неправомерному проникновению на объект предусмотрено;

•Организация пропускного режима на объекте;
•На территории имеется ограждение с установленными калиткой и воротами. (сущ. положение)
•Контроль прохода и проезда на территорию по существующему положению;
•На объекте имеется круглосуточная охрана, которая делает обход объекта.
•На объекте имеется наружное видеонаблюдение.
•На объекте устанавливается сигнализация
•При въезде автотранспорт подлежит осмотру, без изменения сущ. положения
•Информационная безопасность данных, обеспечена за счет установки сигнализации в серверную. комнату и системы СКУД на входе.

б) на выявление нарушителей, установлен пропускного режимов:

•При входе на объект во время работы учреждения дежурит охранник.
•При входе в здание все проходят досмотр с помощью средств досмотра.
•При въезде автотранспорт досматривают по сущ. положению
•За счет того, что на объекте имеется круглосуточная охрана, на объекте исключено бесконтрольное пребывание на объекте посторонних лиц.
•На объекте установлено видеонаблюдение
•В комнате охраны имеется экстренная связь, что в свою очередь обеспечивает своевременное информирование правоохранительных органов в случае необходимости (РосГвардии).

Взам. инв. №

Подпись и дата

Инв. № подл.

Изм.	Кол.	Лист	№док	Подпись	Дата

2024-00375-01-0-ПТА

Разработал	Фугельзанг Е.А.	
ГАП	Шведов В.В.	
Н.контроль	Фугельзанг Е.А.	
Нач.М-1	Чередниченко В.В.	

Капитальный ремонт здания ГБОУ города Москвы "Школа № 1574", расположенное по адресу: г. Москва, пер.Старопименовский, д. 5

Стадия	Лист	Листов
П	7	43

МОСЖИЛ НИИПРОЕКТ

в) на пресечение попыток совершения террористических актов на объектах (территориях):

•Организация пропускного режима на объекте;
•На въезде организован досмотр въезжающего автотранспорта (по сущ. положению)
•Организация досмотра посетителей, персонала, учителей и учащихся в зоне досмотра, расположенной до турникетов;
•На объекте организована круглосуточная охрана
•На объекте организовано видеонаблюдение
•Помещениях с массовым пребыванием людей (вестибюль; поэтажные коридоры; рекреации; гардероб; столовая, спортзал; лаборатории; библиотека и трансформируемые пространства) оборудуются экстренной связью с помещением охраны, в том числе видеокамерами в помещения и направленные на входы в них
•В помещении охраны, при необходимости, имеются средства экстренной связи с РосГвардией.

г) на минимизацию возможных последствий совершения террористических актов на объектах (территориях) и ликвидацию угрозы их совершения:

•На объекте существует постоянный контроль, осуществляемый за счет обхода здания и подконтрольной территории;
•При необходимости производят огораживание территории происшествия;
•При необходимости активируется экстренная эвакуация;
•При необходимости вызываются специальные службы, в комнате охраны имеется экстренная связь с полицией;
•При необходимости используется локализатор взрыва

д) на обеспечение защиты служебной информации ограниченного распространения, содержащейся в паспорте безопасности и иных документах объектов (территорий), в том числе служебной информации ограниченного распространения о принимаемых мерах по антитеррористической защищенности объектов (территорий):
•Обеспечение надлежащего хранения и использования служебной информации
•На объекте организовано помещение хранения служебной информации;
•Устанавливается порядок работы со служебной информацией ограниченного распространения;
•Ограничен доступ к служебной информации, за счет установки системы СКУД на входе в помещение
•Помещение хранения информации оборудовано сигнализацией и видеонаблюдением.

е) на выявление и предотвращение несанкционированного проноса (провоза) и применения на объекте (территории) токсичных химикатов, отравляющих веществ и патогенных биологических агентов, в том числе при их получении посредством почтовых отправлений.

•Организован санкционированный допуск на объект и территорию посетителей и автотранспортных средств;
•Своевременное выявление фактов нарушения на объекте, обеспечивается за счет круглосуточной охраны, досмотра автотранспорта с помощью набора зеркал, досмотра всех посетителей в зоне досмотра с помощью досмотровых технических средств, которые выявляют возможные токсичные химикаты, отравляющие вещества и патогенные биологические агенты (в т.ч. полученные в почтовых отправлениях);
•Осуществляется контроль за состоянием помещений с массовым пребыванием людей (вестибюль; поэтажные коридоры, в т.ч используемые для отдыха; столовая, спортзал; актовый зал) оборудуются экстренной связью с помещением охраны, видеонаблюдением в т.ч. видеокамеры устанавливаются на против входа в эти помещения.

Здание находится на огороженной территории, но территория не входит в рамки капитального ремонта, территория с ограждением и необходимым наружным освещением остается по существующему положению.

Взам. инв. №

Подпись и дата

Инв. № подл.

Изм.	Кол.	Лист	№док	Подпись	Дата	**2024-00375-01-0-ПТА**		
Разработал		Фугельзанг Е.А.				Капитальный ремонт здания ГБОУ города Москвы "Школа № 1574", расположенное по адресу: г. Москва, пер.Старопименовский, д. 5	Стадия	Лист	Листов
ГАП		Шведов В.В.					П	8	43
Н.контроль		Фугельзанг Е.А.					МОСЖИЛ НИИПРОЕКТ		
Нач.М-1		Чередниченко В.В.							

В соответствии с разделом АР и ТХ, планируемое штатное расписание составляет 400 учащихся.

В соответствие с п.25 ПП РФ от 2 августа 2019 г. № 1006. В отношении объектов (территорий) третья категории опасности осуществляются следующие мероприятия:

- На объекте введен пропускной и внутриобъектовый режим и осуществлен контроль за их функционированием;
- Объект оснащен системой передачи тревожных сообщений в подразделения войск национальной гвардии Российской Федерации поддержание ее в исправном состоянии (см. том 5.5.9);
- Объект оборудован системами оповещения и управления эвакуацией работников, обучающихся и иных лиц, находящихся на объекте и территории, о потенциальной угрозе возникновения или о возникновении чрезвычайной ситуации (см. том 5.5.2);
- Обход периодический обход и осмотр объектов (территорий), их помещений, систем подземных коммуникаций, стоянок транспорта, а также периодическая проверка складских помещений;
- На объекте и территории исключается бесконтрольное пребывание посторонних лиц и нахождения транспортных средств, в том числе в непосредственной близости от здания и территории;
- На объекте осуществляются мероприятий по информационной безопасности, обеспечивающих защиту от несанкционированного доступа к информационным ресурсам объекта;
- Объект и территория оснащен системой наружного освещения (см. том 5.1);
- Организовано взаимодействие с территориальными органами безопасности и территориальными органами Федеральной службы войск национальной гвардии Российской Федерации (подразделениями вневедомственной охраны войск национальной гвардии Российской Федерации).
- Здание и прилегающая территория оснащена системами видеонаблюдения (см. том 5.5.7), охранной сигнализации (см. том 5.5.9);
- Охрана объекта обеспечивается сотрудниками организации, имеющей право на создание и ведение охраны;
- На 1-м этаже оборудовано помещение для охраны с установкой в нем систем видеонаблюдения, охранной сигнализации и средств передачи тревожных сообщений в подразделения войск национальной гвардии Российской Федерации см. приложение «План 1-го этажа»;
- На основном входе на объект оборудован стационарным постом охраны с зоной досмотра;
- Объект оснащен стационарными или ручными металлоискателями.

Взам. инв. №

Подпись и дата

Инв. № подл.

Изм.	Кол.	Лист	№док	Подпись	Дата

2024-00375-01-0-ПТА

Разработал	Фугельзанг Е.А.	
ГАП	Шведов В.В.	
Н.контроль	Фугельзанг Е.А.	
Нач.М-1	Чередниченко В.В.	

Капитальный ремонт здания ГБОУ города Москвы "Школа № 1574", расположенное по адресу: г. Москва, пер.Старопименовский, д. 5

Стадия	Лист	Листов
П	9	43

МОСЖИЛ НИИПРОЕКТ

4.1. Обоснование классификации объекта по значимости в зависимости от вида и размеров ущерба, который может быть нанесен объекту в случае реализации террористических угроз

В соответствии с СП 132.13330.2011 «Обеспечение антитеррористической защищенности зданий и сооружений. Общие требования проектирования» в зависимости от вида и размеров ущерба, который может быть нанесен объекту, находящимся на нем людям и имуществу в случае реализации террористических угроз, все объекты подразделяются, на следующие классы:

- *класс 1 (высокая значимость) - ущерб в результате реализации террористических угроз приобретет федеральный или межрегиональный масштаб;*
- *класс 2 (средняя значимость) - ущерб в результате реализации террористических*
- *класс 3 (низкая значимость) - ущерб в результате реализации террористических угроз приобретет муниципальный или локальный масштаб.*

В настоящем подразделе, для оценки класса значимости объекта в зависимости от вида и размеров ущерба, который может быть нанесен ему, находящимся на нем людям и имуществу в случае реализации террористических угроз, не предусмотрено применение методов многокритериальной оценки возможного ущерба, в связи с чем, класс значимости объекта, согласно пункта 6.3 СП 132.13330.2011, определен по усмотрению Заказчика.

Проектируемому объекту присвоен 3-й класс (низкая значимость) классификации объекта по значимости в зависимости от вида и размеров ущерба, который может быть нанесен объекту в случае реализации террористических угроз.

Согласно п. 13 подпункт в) ПП от 2 августа 2019 г. № 1006 “Об утверждении требований к антитеррористической защищенности объектов (территорий) Министерства просвещения Российской Федерации и объектов (территорий), относящихся к сфере деятельности Министерства просвещения Российской Федерации, и формы паспорта безопасности этих объектов (территорий)” с учетом оценки степени угрозы совершения террористического акта (на основании анализа значимости объекта (данный объект муниципального значения) и оценки объектов располагающихся вблизи или непосредственно граничащих с ним), а также оценки возможных последствий его совершения, проведенного согласно п.12 ПП от 2 августа 2019 г. № 1006 “Об утверждении требований к антитеррористической защищенности объектов (территорий) Министерства просвещения Российской Федерации и объектов (территорий), относящихся к сфере деятельности Министерства просвещения Российской Федерации, и формы паспорта безопасности этих объектов (территорий)” по определению критических элементов для данного объекта, в силу его специфики, как учебного заведения не выявлено зон, конструктивных и технологических элементов объекта, в том числе коммуникаций; элементов систем, узлов оборудования или устройств потенциально опасных установок на объекте; мест использования или хранения опасных веществ и материалов на объекте; других систем, элементов и коммуникаций объекта, которые могут быть определены как критические элементы. Критические точки: входы, вестибюль, стены (и другие конструктивные элементы объекта, повреждение или разрушение которых является жизненно-важным для объекта), периметр, коридоры, столовая, спортзал, актовый-зал.

4.2. Описание технических систем (средств) и обоснование проектных решений, направленных на обнаружение радиоактивных, взрывчатых, отравляющих веществ, оружия, боеприпасов, наркотических средств и других опасных предметов и веществ

Ремонтируемый объект предусматривает в своем составе помещения с единовременным нахождением более 50 человек (вестибюль; поэтажные коридоры, используемые для отдыха; столовая, спортзал; актовый зал).

Проектные решения в части состава систем безопасности, направленных на предотвращение криминальных проявлений и их последствий, способствующие минимизации возможного ущерба людям, зданию и имуществу при возникновении противоправных действий, разрабатываются в соответствии с нормами по обеспечению антитеррористической

Взам. инв. №

Подпись и дата

Инв. № подл.

Изм.	Кол.	Лист	№док	Подпись	Дата	2024-00375-01-0-ПТА		
Разработал		Фуэльзанг Е.А.				Капитальный ремонт здания ГБОУ города Москвы "Школа № 1574", расположенное по адресу: г. Москва, пер.Старопименовский, д. 5	Стадия	Лист	Листов
ГАП		Шведов В.В.					П	10	43
Н.контроль		Фуэльзанг Е.А.					МОСЖИЛ НИИПРОЕКТ		
Нач.М-1		Чередниченко В.В.							

защищенности зданий и сооружений п.6.24 СП 118.13330.2022 «Общественные здания и сооружения (актуализированная редакция СНиП 31-06-2009)». Эти мероприятия установлены в задании на проектирование и разрабатываются в соответствии с СП 132.13330.2011 «Обеспечение антитеррористической защищенности зданий и сооружений. Общие требования проектирования».

С учетом установления проектируемому объекту 3 класса значимости, в соответствии с таблицей 1 СП 132.13330.2011 предусмотрено его оснащение следующими системами защиты от угроз террористического характера:

- *охранного телевидения (далее по тексту - СОТ);*
- *охранного освещения (далее по тексту - СОО);*
- *охранно-тревожной сигнализации (далее по тексту - СОТС);*
- *экстренной связи (далее по тексту - СЭС).*

Согласно п.7.4 СП 132.13330.2011 «Обеспечение антитеррористической защищенности зданий и сооружений. Общие требования проектирования» Проектной документацией должна быть предусмотрена возможность оборудования и функционирования СОТ, СОО, СОТС, СЭС всех входов, а также мест пребывания людей численностью более 50 человек в помещениях (гардероб № 103; столовая № 131, спортзал № 010, 220; актовый зал № 206; библиот. и информ. центр №421 и коридоры, рекреации подвала: 1шт; 1-го этажа: № 114 (2шт); 2-го этажа: № 214, 218, 219; 3-его этажа: № 316; 4-го этажа: № 415; 5-го этажа: 515 и лестница № 215).

Дополнительно, проектом предусмотрено оснащение ремонтируемого объекта системой контроля и управления доступом (далее по тексту - СКУД).

Системы безопасности объекта

Проектные решения системы безопасности объекта принимаются на основании Свода Правил СП 132.13330.2011 Обеспечение антитеррористической защищенности зданий и сооружений. Общие требования проектирования». Проектируемый комплекс систем безопасности должен обеспечивать: обнаружение и фиксацию фактов несанкционированного проникновения человека («нарушителя») в здание и отдельные помещения;

- *оповещение службы охраны о срабатывании технических средств системы охранной сигнализации и контроля и управления доступом, а также о возникновении нештатных ситуаций;*
- *автоматическое ведение отчета и сохранение его в базе о посетителях и обслуживающем персонале находящихся на территории комплекса;*
- *контроль работоспособности систем безопасности;*
- *автоматическое регулирование ограничением входа/выхода в точках прохода, оборудованных системой контроля доступа.*

В соответствии с п. 25 Требований подпункт в) на проектируемом объекте на первом этаже организованно помещение охраны, которое оборудовано следующими средствами контроля безопасности:

- *Пульт управления*
- *Пост управления видеонаблюдением*
- *Ручной металлоискатель «Сфинкс ВМ-611 РД-2.0»;*
- *Газоанализаторами паров взрывчатых и наркотических веществ «Кербер-Т»;*
- *Прибор управления речевого оповещения*

Организованно круглосуточное дежурство на объекте. На центральном входе на объект организован стационарный пост охраны, с оборудованием для досмотра подозрительных лиц.

Остальные входы-выходы, находящиеся (на плане 1 этажа) используются по мере необходимости как служебные или запасные входы-выходы, которые контролируются СКУД и автоматически разблокируются для эвакуации людей при срабатывании пожарной сигнализации.

Система охранная телевизионная

Система телевизионного наблюдения является элементом системы охраны объекта и предназначена для обеспечения физической безопасности и защиты вышеуказанного объекта от криминальных действий, а так же повышения эффективности действий службы охраны при возникновении внештатных ситуаций. Разрабатываемая система видеонаблюдения обеспечивает решение следующих задач:

Взам. инв. №

Подпись и дата

Инв. № подл.

Изм.	Кол.	Лист	№док	Подпись	Дата	2024-00375-01-0-ПТА		
Разработал		Фугельзанг Е.А.				Капитальный ремонт здания ГБОУ города Москвы "Школа № 1574", расположенное по адресу: г. Москва, пер.Старопименовский, д. 5	Стадия	Лист	Листов
ГАП		Шведов В.В.					П	11	43
Н.контроль		Фугельзанг Е.А.					МОСЖИЛ НИИПРОЕКТ		
Нач.М-1		Чередниченко В.В.							

• получение видеоинформации с целью определения характера и места нарушения, направления движения нарушителя;

• контроль за действиями персонала охраны с возможностью последующего анализа;

• представление оператору необходимой и достаточной информации об обстановке на объекте;

• представление информации для оценки обстановки в случае выявления фактов совершения несанкционированных действий и видеоподтверждение фактов их совершения;

• непрерывный визуальный контроль со стороны сотрудников служб охраны всех подлежащих контролю участков объекта;

• просмотр оператором изображений от всех или определенных камер в полноэкранном режиме или вывод нескольких изображений одновременно на один экран монитора;

• включение передающих телекамер как вручную с пульта управления, так и автоматически при срабатывании средств обнаружения;

• мониторинг объекта защиты в реальном масштабе времени;

• передача видеоизображения на удаленные рабочие станции для осуществления удаленного мониторинга.

Система охранного телевидения (далее-СОТ) предназначена для обеспечения визуального контроля и регистрации обстановки средствами телевизионной техники на территории объекта с целью предотвращения противоправных действий и документирования происходящих событий.

В состав системы входят:

- телевизионные камеры;
- устройство коммутации;
- устройство записи на жесткие диски;
- устройства отображения;
- кабельная распределительная сеть;
- блоки резервного питания.

Средствами СОТ контролируются:

- периметр здания;
- все входы в здание;
- холлы;
- лестничные клетки;
- входы и помещения с возможностью одновременного пребывания более 50 человек (вестибюль; поэтажные коридоры, используемые для отдыха; столовая, спортзал; актовый зал, библиотека и гардеробы);

- входы в помещения, где установлено оборудование инженерных систем;
- входы на технический/цокольный/ полуподвальные этажи.

Глубина видеоархива составляет не менее 30 суток записи в режиме детектора движения.

Резервное электропитание осуществить резервными источниками питания, обеспечивающими резервное электропитание не менее 3 ч работы, при отключении основного.

Периметральная СОТ обеспечивает поддержку обнаружения и информирования о движениях/пересечениях ограждений.

Устройства записи (видеосерверы) установить в серверной. Видеоинформацию от телевизионных камер вывести на мониторы АРМ оператора системы СОТ в помещение охранно-пожарного поста, а также в серверную. Предусмотреть запас 20% по емкости кроссового, сетевого и серверного оборудования для дальнейшего расширения системы.

СОТ обеспечивает круглосуточное наблюдение в режиме реального времени с установленных видеокамер при разрешении не менее 1280x720 пикселей в режиме не менее 15 к/с, с инфракрасной подсветкой, подогревом в зимний период, а также защиту от внешних атмосферных воздействий (пыль, вода) в соответствии со стандартом IP66 и выше и эксплуатацией в условиях температур от минус 40°С до 50°С.

СОТ предназначена для визуального контроля обстановки в выделенных зонах, анализа нештатных ситуаций, проверки поступающих сигналов тревоги, оказания помощи в принятии оперативных решений, документирования данных видеонаблюдения.

СОТ создается в соответствии с ГОСТ Р 51558-2008 "Системы охранные телевизионные общие технические требования и методы испытаний", и с учетом требований РД 78.36.003-2002 "Инженерно-техническая укрепленность. Технические средства охраны. Требования и нормы проектирования по защите объектов от преступных посягательств" и Р78.36.002-99 "Выбор и

применение телевизионных схем видеоконтроля. Рекомендации", ГОСТ Р МЭК 60950-2002 "Безопасность оборудования информационных технологий", ГОСТ Р 51318.22-99 "Совместимость технических средств электромагнитная. Радиопомехи индустриальные от оборудования информационных технологий", ГОСТ Р 51318.24-99 "Совместимость технических средств электромагнитная. Устойчивость оборудования информационных технологий к электромагнитным помехам", ГОСТ Р 51317.3.2-99 "Совместимость технических средств электромагнитная. Устойчивость к электростатическим разрядам", ГОСТ Р 51317.3.3-99 "Совместимость технических средств электромагнитная. Колебания напряжения и фликер, вызываемые техническими средствами, подключаемыми к низковольтным системам электроснабжения".

Для защиты оборудования системы видеонаблюдения, расположенного в здании, необходимо оборудование присоединить к контуру заземления здания.

Оборудование и материалы, применяемые в проекте, соответствуют требованиям государственных стандартов и технических условий и имеют сертификаты соответствия и пожарной безопасности.

Более подробно проектные решения приведены в Части 7 «Система охранного телевидения» Подраздела 5 «Сети связи» Раздела 5 «Сведения об инженерном оборудовании, о сетях инженерно-технического обеспечения, перечень инженерно-технических мероприятий, содержание технологических решений».

Система охранного освещения

Согласно приложения Б (справочное) СП 132.13330.2011, СОО - совокупность средств освещения, позволяющих обеспечить видимость нарушителя и необходимый уровень освещенности для системы охранного телевидения в ночное время.

Функционирование СОО на проектируемом объекте обеспечивается за счет существующей системы внутреннего и наружного освещения территории реконструируемого объекта, управление которой осуществляется централизовано.

Видимость нарушителя и необходимый уровень освещенности для системы охранного телевидения в ночное время также обеспечены функцией ночного видения камер наблюдения.

Более подробно проектные решения по управлению наружным и внутренним освещением, включая дежурное освещение, приведены в Подразделе 1 «Система электроснабжения» Раздела 5 «Сведения об инженерном оборудовании, о сетях инженерно- технического обеспечения, перечень инженерно-технических мероприятий, содержание технологических решений».

Взам. инв. №

Подпись и дата

Инв. № подл.

Изм.	Кол.	Лист	№док	Подпись	Дата

2024-00375-01-0-ПТА

Разработал	Фугельзанг Е.А.	
ГАП	Шведов В.В.	
Н.контроль	Фугельзанг Е.А.	
Нач.М-1	Чередниченко В.В.	

Капитальный ремонт здания ГБОУ города Москвы "Школа № 1574", расположенное по адресу: г. Москва, пер.Старопименовский, д. 5

Стадия	Лист	Листов
П	13	43

МОСЖИЛ НИИПРОЕКТ

Система охранно-тревожной сигнализации

Система охранной сигнализации предназначена для своевременного обнаружения факта несанкционированного проникновения в охраняемые помещения (площадки, зоны) с точным определением места и документированием информации. Главной задачей подсистемы охранной сигнализации является оперативное и гарантированное извещение лиц, ответственных за охраняемые помещения, и/или правоохранительных служб о несанкционированном проникновении в охраняемые помещения. Система охранной сигнализации соответствует требованиям нормативной документации

Система тревожной сигнализации предназначена для автоматической или ручной передачи сигналов тревоги на пульт территориального подразделения ГУ МЧС России по г. Москве и дежурной части территориального отдела внутренних дел при возникновении на объекте чрезвычайной ситуации экологического, техногенного или криминального характера. В целях обеспечения экстренного реагирования нарядов полиции и пресечения противоправных действий данная система также подключается на пульты централизованного наблюдения (ПЦН) ФГКУ УВО Росгвардии по г. Москве.

Система тревожной сигнализации соответствует требованиям нормативной документации.

Информация от системы тревожной сигнализации выведена на пульт охраны учреждения и используется при повседневной эксплуатации.

Кнопка системы тревожной сигнализации установлена на посту охраны.

СОТС предназначена для:

- контроля от несанкционированного доступа в охраняемые помещения;
- обнаружения проникновения или попытки проникновения в охраняемые помещения;
- сбора, обработки, передачи и представления в заданном виде информации о проникновении (попытки проникновения) и другой служебной информации на автоматизированное рабочее место (далее по тексту - АРМ).

Здание оборудуется многорубежной системой охранной сигнализации. Первым рубежом на "открывание" блокируются входные двери, вторым рубежом на "проникновение" защищаются объемы помещений. Объект оборудуется следующими рубежами системы охранной сигнализации:

1. *Охранной сигнализации блокируются:*
   - *ограждение объекта, входные двери, погрузочно-разгрузочные люки, ворота, калитки - на проникновение, открывание, разрушение и пролом;*
   - *деревянные, стеклянные и остекленные конструкции - на открывание, разрушение и разбитие;*
   - *стены, перекрытия и перегородки, за которыми размещаются помещения других юридических и физических лиц, - на разрушение и пролом;*
   - *вентиляционные короба, дымоходы, места ввода/вывода коммуникаций сечением более 200 х 200 миллиметров - на разрушение и пролом.*
2. *Охранная сигнализация на объекте осуществляется путем установки объемных извещателей различного принципа действия в охраняемых помещениях.*

В целях формирования и передачи сообщений о противоправных действиях в отношении объекта на внутренний пост охраны или пункт централизованной охраны «ПЦО» охранной организации, осуществляющей охрану объекта, объект оборудуется системой тревожной сигнализации.

Требования, предъявляемые к подключению охранной (тревожной) сигнализации и передаче извещений о ее срабатывании реализуются с помощью:

Взам. инв. №

Подпись и дата

Инв. № подл.

Изм.	Кол.	Лист	№док	Подпись	Дата

2024-00375-01-0-ПТА

Разработал	Фугельзанг Е.А.	
ГАП	Шведов В.В.	
Н.контроль	Фугельзанг Е.А.	
Нач.М-1	Чередниченко В.В.	

Капитальный ремонт здания ГБОУ города Москвы "Школа № 1574", расположенное по адресу: г. Москва, пер.Старопименовский, д. 5

Стадия	Лист	Листов
П	14	43

МОСЖИЛ НИИПРОЕКТ

- *передачи извещений о срабатывании охранной и (или) тревожной сигнализации с объекта на ПЦО, которая осуществляется с помощью оконечных объектовых устройств, обеспечивающих запоминание тревожного состояния и его фиксацию на выносном световом (звуковом) оповещателе или индикаторе и входящих в состав системы передачи извещений, функционирующей на ПЦО, или совместимых с ней;*
- *организации на объекте поста охраны с пультом внутренней охраны с круглосуточным дежурством, обеспечивающем подключение всех рубежей охранной и (или) тревожной сигнализации помещений объекта.*

Система охранной сигнализации построена на базе современной системы охраны.

Система охранной сигнализации на объекте представляет собой сеть, состоящую из пульта управления, контроллеров 2-х проводной линии связи, контроллеров доступа, прибора приемно-контрольного, блоков реле и блоков индикации.

Обмен данными между элементами сети происходит по кабелю. Передача данных происходит по интерфейсу.

Основу аппаратной части составляет пульт управления; контроллеры доступа, контроллеры двухпроводной линии и с извещателями работают под управлением пульта управления.

Пульт контроля и управления, контроллеры 2-х проводной линии связи, часть реле и блоков индикации Система АУПС выписаны охраной раздел сигненализации предназначена для:

- *контроля от несанкционированного доступа в охраняемые помещения;*
- *обнаружения проникновения или попытки проникновения в охраняемые помещения;*
- *сбора, обработки, передачи и представления в заданном виде информации о проникновении*

(попытки проникновения) и другой служебной информации на Автоматизированное Рабочее Место.

Данным проектом выполняется охранная сигнализация помещений по списку Заказчика.

Дверные проемы с глухими дверями оборудуются магнито-контактными извещателями открытия/закрытия.

Для защиты оконных проемов проектом применяется извещатель охранный адресный оптико-электронный поверхностный

Так же помещения блокируются инфракрасными адресными объемными извещателями движения.

Адресные объемные извещатели установить в электрощитовую, в серверную, в архивы, в венткамеру, в узел учета тепла, в подсобные помещения. Места установки объемных извещателей определяется по месту при монтаже для наиболее точного обслуживания пространства помещения.

Постановка помещений на охрану и снятие с охраны осуществляется с пульта контроля и управления или с АРМ.

Более подробно проектные решения приведены в Части 9 «Система охранной сигнализации» Подраздела 5 «Сети связи» Раздела 5 «Сведения об инженерном оборудовании, о сетях инженерно-технического обеспечения, перечень инженерно-технических мероприятий, содержание технологических решений».

Система экстренной связи

Согласно приложения Б (справочное) СП 132.13330.2011, СЭС - система связи, предназначенная для организации экстренной связи людей с комнатой охраны. В комнате охраны имеется связь с экстренными службами. Например: службой спасения МЧС, полицией, скорой помощью и другими.

Комната охраны оборудуется тревожной кнопкой, сигнал от которой передается на пульт централизованного наблюдения ПЦН.

Взам. инв. №

Подпись и дата

Инв. № подл.

Изм.	Кол.	Лист	№док	Подпись	Дата	2024-00375-01-0-ПТА			
Разработал		Фугельзанг Е.А.				Капитальный ремонт здания ГБОУ города Москвы "Школа № 1574", расположенное по адресу: г. Москва, пер.Старопименовский, д. 5	Стадия	Лист	Листов
ГАП		Шведов В.В.					П	15	43
Н.контроль		Фугельзанг Е.А.					МОСЖИЛ НИИПРОЕКТ		
Нач.М-1		Чередниченко В.В.							

Для обеспечения экстренной связи помещений с предусмотренным единовременным нахождением более 50 человек с охраной объекта, используется тревожная система связи (переговорные устройства) в помещениях: гардероб № 103; столовая № 131, спортзал № 010, 220; актовый зал № 206; библиот. и информ. центр № 421 и коридоры, рекреации подвала: 1 шт; 1-го этажа: № 114 (2 шт); 2-го этажа: № 214, 218, 219; 3-его этажа: № 316; 4-го этажа: № 415; 5-го этажа: 515 и лестница № 215, а так же на улице перед главным входом в здание. Ответная часть тревожной системы, для приёма сигнала, находится на постах охраны и в комнатах охраны.

При обращении, охрана объекта фиксирует причину обращение и вызывает на объект соответствующую службу для ликвидации причины обращения по экстренной связи. Функционирование СЭС на проектируемом объекте обеспечивается предусмотренной системой связи (переговорными устройствами), сведения о которой представлены в Части 9 «Система охранной сигнализации» Подраздела 5 «Сети связи» Раздела 5 «Сведения об инженерном оборудовании, о сетях инженерно-технического обеспечения, перечень инженерно-технических мероприятий, содержание технологических решений». Экстренной связью с помещением охраны оборудуются вестибюль; поэтажные коридоры, используемые для отдыха; столовая, спортзал; актовый зал.

Система контроля и управления доступом

Система контроля и управления доступом (СКУД) предназначена для:

- обеспечения санкционированного входа в здание и в зоны ограниченного доступа и выхода из них путем идентификации личности по комбинации различных признаков: вещественный код (вигандкарточки, ключи touch-memory и другие устройства), запоминаемый код (клавиатуры, кодонаборные панели и другие устройства), биометрические признаки (отпечатки пальцев, сетчатка глаз и другие признаки);

- предотвращения несанкционированного прохода в помещения и зоны ограниченного доступа.

Предусмотрена система контроля и управления доступом, с использованием программного комплекса.

Предусмотрен защищенный доступ в технические помещения здания, а также помещения по списку, утвержденному руководством учебного заведения.

Предусмотрено оборудование защищаемых помещений объекта дверными электромеханическими замками.

Обеспечено проникновение в защищаемое помещение путем поднесения бесконтактных карт доступа.

Обеспечена автоматическая разблокировка дверей в экстренных случаях по команде от АРМ, в помещении охранно-пожарного поста или по сигналу от автоматической установки пожарной сигнализации.

Обеспечен контроль событий (вход и выход), фиксируя в энергонезависимой памяти системы, с возможностью просмотра на автоматизированном рабочем месте (АРМ) в помещении охранно-пожарного поста.

Предусмотрено администрирование системы контроля и управления доступа с использованием программного обеспечения на рабочем месте в помещении охранно-пожарного поста.

Предусмотрена возможность управления открыванием/ закрыванием ворот и шлагбаумов на территории (при наличии).

Тип кабелей определяется в соответствии с требованиями технических регламентов. Прокладку кабельных трасс осуществить в коробах и гофрах не содержащих галогенов.

Резервное электропитание осуществляется резервными источниками питания, обеспечивающими резервное электропитание, при отключении основного.

СКУД соответствует требованиям ГОСТа. Классификация. Общие технические требования. Методы испытаний".

В соответствии «Требований» инженерно-техническая укрепленность обеспечивает противодействие несанкционированному проникновению на охраняемый объект, связанному с механическим воздействием на его конструктивные элементы, на период, необходимый для его выявления и пресечения.

СКУД принадлежит к техническим средствам высокого уровня и предназначена для решения задач контроля и управления посещением с помощью электронных идентификаторов.

Помимо управления доступом в здание, СКУД предназначена для контроля доступа в технические помещения, в подсобные помещения, в электрощитовую, в серверную, в архивы, в венткамеру, в узел учета тепла.

Более подробно проектные решения приведены в Части 8 «Система контроля управления доступом» Подраздела 5 «Сети связи» Раздела 5 «Сведения об инженерном оборудовании, о сетях инженерно-технического обеспечения, перечень инженерно-технических мероприятий, содержание технологических решений».

Мероприятия по обеспечению антитеррористической защищенности

К данному объекту, как объекту Министерства просвещения Российской Федерации - зданию общеобразовательной школы, в составе которого предусматриваются помещения предполагающие единовременное нахождение более 50 человек и эксплуатация которого не предусматривает установление специального пропускного режима (Постановление Правительства РФ от 16 февраля 2008 г. N 87 "О составе разделов проектной документации и требованиях к их содержанию" Пункт 22 п.2), в части обоснования проектных решений, направленных на обнаружение радиоактивных, взрывчатых, отравляющих веществ, оружия, боеприпасов, опасных средств и других опасных предметов и веществ согласно ПП РФ от 2 августа 2019 г. № 1006 “Об утверждении требований к антитеррористической защищенности объектов (территорий) Министерства просвещения Российской Федерации и объектов (территорий), относящихся к сфере деятельности Министерства просвещения Российской Федерации, и формы паспорта безопасности этих объектов (территорий)” предъявляются следующие требования:

1. *Технические средства досмотра применяются для обнаружения оружия и других предметов и веществ, предназначенных для осуществления криминальных действий, при проходе людей или въезде транспортных средств на охраняемый объект, а также для предотвращения криминальных действий, включающих хищения с охраняемых объектов и несанкционированный пронос на них запрещенных веществ и предметов. В перечень технических средств досмотра входят:*
   - *панельные и ручные металлоискатели;*
   - *газоанализаторы паров взрывчатых и наркотических веществ;*
   - *средства обнаружения химических, биологических и других опасных веществ, находящихся в жидком и твердом виде в закрытой упаковке;*
   - *набор досмотровых зеркал;*
   - *локализаторы взрыва.*
2. *Металлообнаружители (металлодетекторы) должны обеспечивать выполнение обнаружение холодного и огнестрельного оружия, металлосодержащих взрывных устройств (гранат), запрещенных к проносу различных видов металлосодержащей продукции производства и быть выполнены в виде стационарных устройств арочного или стоечного типа либо в виде портативных приборов.*

Взам. инв. №

Подпись и дата

Инв. № подл.

Изм.	Кол.	Лист	№док	Подпись	Дата	2024-00375-01-0-ПТА		
Разработал		Фугельзанг Е.А.				Капитальный ремонт здания ГБОУ города Москвы "Школа № 1574", расположенное по адресу: г. Москва, пер.Старопименовский, д. 5	Стадия	Лист	Листов
ГАП		Шведов В.В.					П	17	43
Н.контроль		Фугельзанг Е.А.					МОСЖИЛ НИИПРОЕКТ		
Нач.М-1		Чередниченко В.В.							

Стационарные металлообнаружители должны обеспечивать:

- *обнаружение объектов поиска;*
- *селективность по отношению к металлическим предметам, разрешенным к проносу на охраняемый объект;*
- *адаптацию к окружающей обстановке (в том числе металлосодержащей);*
- *помехозащищенность от внешних источников электромагнитных излучений;*
- *однородную чувствительность обнаружения во всем объеме контролируемого пространства;*
- *способность перенастройки на обнаружение различных масс металла;*
- *допустимым уровнем влияния на имплантируемые электрокардиостимуляторы и магнитные носители информации.*

Портативные (ручные) приборы должны обеспечивать:

- *обнаружение и, в случае необходимости, распознавание черных и цветных металлов и их сплавов;*
- *возможность перенастройки на обнаружение различных масс металла;*
- *возможность использования при совместной работе со стационарными металлообнаружителями.*

3. *Досмотровые эндоскопы и зеркала должны применяться для облегчения визуального осмотра труднодоступных мест и выявления в них взрывных устройств, огнестрельного и холодного оружия, средств негласного съема информации и других объектов. Технические эндоскопы и видеоскопы должны применяться для визуального осмотра различных полостей, каналов и других мест, доступ к которым возможен лишь через сравнительно небольшие отверстия. Они должны обеспечивать:*
   - *доступ на расстояния не менее 1,5 м с углом зрения не менее 40 градусов для гибких и полужестких конструкций и 90 градусов - для жестких;*
   - *возможность подсветки места осмотра, регулировки условий освещения;*
   - *видеодокументирование результатов досмотра.*
4. *Аппаратура для обнаружения взрывчатых и опасных химических веществ должна применяться для выявления наличия их или их следов путем проведения компонентного и структурного анализа подозрительных проб воздуха. Она должна обеспечивать:*
   - *идентификацию веществ, основанную на использовании современных физико-химических методов анализа;*
   - *чувствительность, позволяющую фиксировать наличие штатных взрывчатых веществ типа тротила, гексогена;*
   - *экспресс-выявление следов взрывчатых веществ на поверхности предметов (анализаторы следов взрывчатых веществ);*
5. *Аппаратура для обнаружения химических, биологических и других опасных веществ, находящихся в жидком и твердом виде в закрытой упаковке должна обеспечивать выявление токсичных химикатов, отравляющих веществ и патогенных биологических агентов, в том числе при их получении посредством почтовых отправлений. Она должна обеспечивать:*
   - *идентификацию веществ, основанную на использовании современных физических методов анализа;*
   - *чувствительность, позволяющую фиксировать наличие токсичных химикатов, отравляющих веществ и патогенных биологических агентов, опасных и взрывчатых веществ, находящихся в конденсированном состоянии – в жидком, твердом, в том числе, сыпучем виде;*

Номенклатура средств обнаружения взрывчатых, отравляющих веществ, оружия, боеприпасов и других опасных предметов и веществ в проектируемом объекте формируется в соответствии с подпунктом «е» п.17 Требований к антитеррористической защищенности объектов (территорий) Министерства просвещения Российской Федерации и объектов (территорий), относящихся к сфере деятельности Министерства просвещения Российской Федерации, утвержденных Постановлением Правительства РФ от 02.08.2019 г. № 1006 и соответствует вышеприведенным требованиям. В результате на данном объекте применены следующие технические средства и проектные решения, направленные на обнаружение взрывчатых, отравляющих веществ, оружия, боеприпасов и других опасных предметов и веществ.

Металлодетекторы

Панельного исполнения Паутина-Н2-1 устанавливаются при входах в здание, в соответствии с инструкциями организации. Стационарный стационарный металлодетектор с микропроцессорным управлением "Паутина-Н2-1" предназначен для обнаружения, как огнестрельное и травматическое оружие, боеприпасы, ножи, пр. А наличие и звуковой, и световой сигнализации гарантирует, что оператор не пропустит сигнал тревоги.

Количество ручных металлодетекторов, а также досмотровых зеркал устанавливается в соответствии с инструкциями организации, осуществляющей охрану объекта или отдельных помещений. При необходимости, организация, осуществляющая охрану объекта (или отдельных помещений), может использовать дополнительные оборудование.

Ручные металлодетекторы хранятся в помещениях охраны, в местах указанных на плане.

В качестве альтернативных вариантов МИ могут быть использованы сертифицированные металлоискатели типа «Сфинкс ВМ-611 РД-2.0» (см. приложение). Высокочувствительный вихретоковый микропроцессорный ручной металлоискатель «Сфинкс ВМ-611 РД-2.0» предназначен для поиска и обнаружения металлических предметов при проведении личного досмотра, контроля багажа и корреспонденции.

(Поставку, монтаж и выполнение пусконаладочных работ стационарных металлодетекторов выполнить силами подрядной организации в рамках проведения капитального ремонта)

Средства обнаружения паров взрывчатых и наркотических веществ

При срабатывании тревоги на входе панельного металлодетектора «Паутина-Н2-1» или газоанализатора паров взрывчатых веществ «Кербер-Т», производится визуальный досмотр подозрительных лиц сотрудниками охраны объекта, с помощью, ручного металлоискателя «Сфинкс ВМ-611 РД-2.0», на наличие взрывных устройств, оружия и боеприпасов.

Досмотр на наличие взрывчатых и наркотических веществ осуществляется с использованием газоанализатора паров взрывчатых веществ «Кербер-Т», который обеспечивает оперативное проведение работ по поиску источников всех основных видов взрывчатых и наркотических веществ. Конструкция прибора обеспечивает максимальную простоту проведения замеров и не требует специального образования оператора. Принцип действия основан на тушении фотолюминесценции сенсорного материала в присутствии паров взрывчатых веществ. Встроенный воздушный насос и конструкция прибора создают закрученный поток воздуха, обеспечивающий устойчивый забор воздуха на расстоянии до 200 мм от обследуемого объекта. Технология определения взрывчатых веществ заложенная в приборе позволяет производить замеры как в помещении, так и на открытом воздухе при соблюдении температурных режимов, указанных в технических характеристиках прибора. Так же устанавливается дополнительный модуль для определения наркотических веществ.

Взам. инв. №

Подпись и дата

Инв. № подл.

Изм.	Кол.	Лист	№док	Подпись	Дата	2024-00375-01-0-ПТА			
Разработал		Фугельзанг Е.А.				Капитальный ремонт здания ГБОУ города Москвы "Школа № 1574", расположенное по адресу: г. Москва, пер.Старопименовский, д. 5	Стадия	Лист	Листов
ГАП		Шведов В.В.					П	19	43
Н.контроль		Фугельзанг Е.А.					МОСЖИЛ НИИПРОЕКТ		
Нач.М-1		Чередниченко В.В.							

Локализаторы взрыва

Локализаторы взрыва представляют собой контейнеры различного размера и конфигурации и предназначены для изоляции взрывоопасного предмета и его транспортировки.

Применение специальных контейнеров при обнаружении опасных предметов позволяет в значительной степени снизить силу взрыва и минимизировать его последствия.

Локализаторы взрыва дают возможность обезопасить находящихся рядом людей, а также могут служить для транспортировки взрывоопасных или подозрительных предметов или для того, чтобы накрыть сверху такие предметы до прибытия профильных специалистов.

Устройство не создает помех в рентгеновском диапазоне, что удобно для обследовании взрывоопасного предмета. Быстрая блокировка опасной зоны с помощью 1-2 человек, и не нужна эвакуация людей и остановка работы учреждения.

В качестве альтернативных вариантов ЛВ могут быть использованы сертифицированные локализаторы взрыва типа «Фонтан-2» (приложение В).

При срабатывании тревоги на входе панельного металлодетектора «Паутина-Н2-1» производится визуальный досмотр подозрительных лиц сотрудниками охраны объекта, с помощью ручного металлоискателя «Сфинкс ВМ-611 РД-2.0» и газоанализатора паров взрывчатых и наркотических веществ «Кербер-Т» на наличие взрывных устройств, оружия и боеприпасов.

4.3 Описание технических систем (средств), направленных на оповещения находящихся в здании людей о ЧС.

Для оповещения находящихся в здании людей при возникновении ЧС, предусмотрены системы:

- *Система радиофикации*
- *Система оповещения и управления эвакуацией (далее по тексту - СОУЭ)*
- *Система коллективного приема телевидения (см. том 5.5.4)*

Система радиофикации

Система радиофикации предназначена для организации проводного вещания программ, передаваемых ФГУП РСВО (в том числе для информирования сотрудников охраны, располагающихся в помещении охраны в соответствии с необходимыми требованиями).

В состав системы радиофикации входят кабельные линии связи, подключенные к существующей сети проводного вещания через абонентский трансформатор, и радио-розетки , подключенные к сети радиофикации с помощью ограничительных коробок.

Более подробно проектные решения по радиофикации объекта, включая структурные схемы и места размещения оборудования, приведены в Части 3 « Радиотрансляционная сеть» Подраздела 5 «Сети связи» Раздела 5 «Сведения об инженерном оборудовании, о сетях инженерно-технического обеспечения, перечень инженерно-технических мероприятий, содержание технологических решений».

Система оповещения о пожаре и управления эвакуацией

Подсистема оповещения предназначена для своевременного предупреждения о возникновении пожара, угроз экологического и техногенного характера, противоправных действий, применения оружия массового поражения и др. В составе подсистемы необходимо предусматривать возможность голосового оповещения и оповещения с использованием других технических средств, которые должны обеспечивать возможность трансляции объявлений в режиме реального времени.

Подсистема позволяет сообщить всем, кто находится в здании или сооружении:

- информацию о наличии и о характере опасности;
- инструкции о дальнейших действиях;
- информацию о порядке эвакуации (если это необходимо).

Система оповещения и управления эвакуацией людей при пожаре (СОУЭ) предназначена для оповещения находящихся в здании людей о возникшем пожаре и организации их своевременной эвакуации, путем трансляции речевой информации в помещениях, о необходимости эвакуации, путях эвакуации и других действиях, направленных на обеспечение безопасности.

Основные требования к СОУЭ изложены в нормативной документации «Система оповещения и управления эвакуацией людей при пожаре».

Звуковые сигналы СОУЭ должны обеспечивать общий уровень звука (уровень звука постоянного шума вместе со всеми сигналами, производимыми оповещателями) соответствующий нормам в любой точке защищаемого помещения. Речевые сигналы СОУЭ должны обеспечивать нормативный уровень звука. Не выше допустимого уровня звука постоянного шума в защищаемом помещении. Количество речевых пожарных оповещателей, их расстановка и мощность должны обеспечивать уровень звука во всех местах постоянного или временного пребывания людей в соответствии с нормами свода правил. Следует учитывать ослабление сигнала при прохождении через двери.

Для оповещения находящихся в здании людей о возникшем пожаре, принята система оповещения совмещенная с громкоговорящей связью.

Оборудование СОУЭ обеспечивает выполнение основных функций:
- подача звуковых (речевых) сигналов в помещения объекта оповещения с постоянным или временным пребыванием людей;
- трансляцию текстов (голосовое сообщение в микрофон) о необходимости эвакуации, путях эвакуации, направлении движения и других действиях, направленных на обеспечение безопасности людей и распределением сигналов оповещения по зонам;
- автоматической трансляцией специально разработанных текстов (речевое сообщение, записанное на магнитофон), направленных на предотвращение паники и других явлений, усложняющих эвакуацию с распределением сигналов оповещения по зонам в автоматическом режиме;
- автоматическое распределение сигналов в группе зон оповещения по зонам, в соответствии с очередностью оповещения (установленным алгоритмом);
- сопряжение с системой оповещения ГО;

Для оповещения МГН дополнительно устанавливаются свето-звуковые оповещатели. Настенные звуковые оповещатели, должны крепиться на высоте в соответствии с нормами
- включение от командного импульса, формируемого автоматической установкой пожарной сигнализацией или пожаротушения;

Взам. инв. №

Подпись и дата

Инв. № подл.

Изм.	Кол.	Лист	№док	Подпись	Дата	2024-00375-01-0-ПТА		
Разработал		Фуэльзанг Е.А.				Капитальный ремонт здания ГБОУ города Москвы "Школа № 1574", расположенное по адресу: г. Москва, пер.Старопименовский, д. 5	Стадия	Лист	Листов
ГАП		Шведов В.В.					П	21	43
Н.контроль		Фуэльзанг Е.А.					МОСЖИЛ НИИПРОЕКТ		
Нач.М-1		Чередниченко В.В.							

- возможность совмещения СОУЭ с сетью ГО и ЧС здания с приоритетом оповещения.

Система речевого оповещения принята в составе:

Прибор управления предназначен для приема командных импульсов, формируемых автоматической установкой пожарной сигнализации, и выдачи, в соответствии с алгоритмом работы, команд и электрических сигналов в систему звукового оповещения, подачу основного или резервного питания на усилитель мощности.

Основное питание прибора управления осуществляется от сети переменного тока.

Резервное питание обеспечивает аккумулятор, установленный внутри прибора.

- Усилитель мощности трансляционный предназначен для приема электрических сигналов от прибора управления (звук, голосовое сообщение оператора, речевая информация фонограммы), усиления этих сигналов до необходимой мощности и выдачу усиленных сигналов через коммутационную группу прибора управления в трансляционные линии звукового оповещения.

Основное питание усилителя осуществляется от сети переменного тока. Резервное питание обеспечивается от внешнего блока резервного питания.

- Блок резервного питания предназначен для обеспечения резервным питанием усилителя мощности, входящего в состав системы звукового оповещения, питания световых оповещателей.

- Речевые пожарные извещатели и настенный, навесной предназначены для воспроизведения голосовых сообщений, специальных сигналов в системах пожарного оповещения, речевой информации и фоновой музыки в системах: громкоговорящей связи, звукоусиления и трансляции. Установить извещатели на этаже, согласно рабочим чертежам.

Система аварийного и эвакуационного освещения предназначена для обеспечения нормальной жизнедеятельности при аварийном отключении рабочего освещения и для обеспечения эвакуации людей в чрезвычайных ситуациях. Она должна соответствовать всем необходимым требованиям

Более подробно проектные решения по системе коллективного приема телевидения объекта, включая структурные схемы и места размещения оборудования, приведены В Части 2 «Система оповещения управления эвакуацией» Подраздела 5 «Сети связи» Раздела 5 «Сведения об инженерном оборудовании, о сетях инженерно-технического обеспечения, перечень инженерно-технических мероприятий, содержание технологических решений».

Система эвакуационного освещения принята в составе:

- световой оповещатель предназначен для указания мест и маршрута эвакуации с помощью световой индикации. Световые оповещатели установить согласно рабочим чертежам. Режим работы эвакуационных знаков безопасности предполагает непрерывную работу:

- при наличии основного питания;

- при отсутствии основного питания от аккумуляторных батарей

Головное оборудование СОУЭ устанавливается в стойку, располагаемую в помещении охраны. Стойка комплектуется блоком розеток.

В целях снижения потерь тока в линиях связи СОУЭ, и увеличения величины звукового давления оповещателей, и, как следствие, уменьшение количества оповещателей, выбирается напряжение в линиях связи.

Система коллективного приема телевидения

Телефикация объекта выполняется с подключением в серверной кроссовой. С возможностью управления из комнаты охраны.

Система кабельного телевидения предназначена для организации телевизионного вещания в здании.

Уровень сигнала на абонентских розетках соответствует нормам

В состав системы входит:

- *головная станция;*
- *переменный эквалайзер;*
- *делители на U ;*
- *телевизионные розетки*

Взам. инв. №

Подпись и дата

Инв. № подл.

Изм.	Кол.	Лист	№док	Подпись	Дата

2024-00375-01-0-ПТА

Разработал	Фугельзанг Е.А.	
ГАП	Шведов В.В.	
Н.контроль	Фугельзанг Е.А.	
Нач.М-1	Чередниченко В.В.	

Капитальный ремонт здания ГБОУ города Москвы "Школа № 1574", расположенное по адресу: г. Москва, пер.Старопименовский, д. 5

Стадия	Лист	Листов
П	22	43

МОСЖИЛ НИИПРОЕКТ

Более подробно проектные решения по системе коллективного приема телевидения объекта, включая структурные схемы и места размещения оборудования, приведены В Части 4 «Система кабельного телевидения» Подраздела 5 «Сети связи» Раздела 5 «Сведения об инженерном оборудовании, о сетях инженерно-технического обеспечения, перечень инженерно-технических мероприятий, содержание технологических решений».

Организация обеспечения информационной безопасности, разработка и реализация мер, исключающих несанкционированный доступ к информационным ресурсам объекта

В целях обеспечения необходимой степени антитеррористической защищенности объекта в соответствии с п. 17 ПП РФ от 2 августа 2019 г. № 1006 "Об утверждении требований к антитеррористической защищенности объектов (территорий) Министерства просвещения Российской Федерации и объектов (территорий), относящихся к сфере деятельности Министерства просвещения Российской Федерации, и формы паспорта безопасности этих объектов (территорий)" в части обеспечения защиты служебной информации ограниченного распространения необходимо:

- согласно п.17 подпункт д) обеспечение защиты служебной информации ограниченного распространения, содержащейся в паспорте безопасности и иных документах объектов (территорий), в том числе служебной информации ограниченного распространения о принимаемых мерах по антитеррористической защищенности объектов (территорий);

- согласно п.18 подпункт е) организация обеспечения информационной безопасности, разработки и реализации мер, исключающих несанкционированный доступ к информационным ресурсам объектов (территорий);

- согласно п.22 обеспечение защиты служебной информации ограниченного распространения, содержащейся в паспорте безопасности и иных документах объектов (территорий), в том числе служебной информации ограниченного распространения о принимаемых мерах по антитеррористической защищенности объектов (территорий), достигается посредством:

- определения должностных лиц, имеющих право доступа к служебной информации ограниченного распространения, содержащейся в паспорте безопасности объекта (территории) и иных документах объекта (территории), в том числе служебной информации ограниченного распространения о принимаемых мерах по его антитеррористической защищенности;

- выбор надежного оборудования.

- *необходимо использовать отказоустойчивые компьютеры, т. е. такие, выход из строя отдельного компонента которых не приводит к отказу машины.*
- *нельзя использовать устройства, собранные из комплектующих низкого качества, и нелицензионное ПО.*

- выбор источников бесперебойного питания и дублирование электропитания.

Порядок работы со служебной информацией ограниченного распространения

(персональные данные; данные, содержащиеся в паспорте безопасности объекта; д) определен с учетом положений Федерального закона от 27 июля 2006 г. N 149-ФЗ "Об информации, информационных технологиях и о защите информации" и включает следующие меры по защите служебной информации ограниченного распространения, обрабатываемой с использованием средств вычислительной техники.

Не требуются в связи с тем что вся служебная информация хранится на сервере в Департаменте образования г. Москвы

Взам. инв. №

Подпись и дата

Инв. № подл.

Изм.	Кол.	Лист	№док	Подпись	Дата	2024-00375-01-0-ПТА		
Разработал		Фугельзанг Е.А.				Капитальный ремонт здания ГБОУ города Москвы "Школа № 1574", расположенное по адресу: г. Москва, пер.Старопименовский, д. 5	Стадия	Лист	Листов
ГАП		Шведов В.В.					П	23	43
Н.контроль		Фугельзанг Е.А.					МОСЖИЛ НИИПРОЕКТ		
Нач.М-1		Чередниченко В.В.							

Средства инженерной укрепленности специальных помещений для хранения и работы со служебной информацией ограниченного доступа

Не требуются в связи с тем что вся служебная информация хранится на сервере в Департаменте образования г. Москвы

4.4. Мероприятия по обеспечению антитеррористической защиты объекта

Основной задачей мероприятий по обеспечению антитеррористической защиты является, оперативное реагирования охраны на входящие сигналы об опасности от средств контроля безопасности, а также персонала и посетителей проектируемого объекта.

С учетом специфики данного объекта согласно п.17 ПП РФ от 2 августа 2019 г. № 1006 "Об утверждении требований к антитеррористической защищенности объектов (территорий) Министерства просвещения Российской Федерации и объектов (территорий), относящихся к сфере деятельности Министерства просвещения Российской Федерации, и формы паспорта безопасности этих объектов (территорий)" в целях обеспечения необходимой степени антитеррористической защищенности объекта осуществляется комплекс мер, направленных:

а) на воспрепятствование неправомерному проникновению на объект;
б) на выявление нарушителей установленных на объекте пропускного и внутриобъектового режимов и (или) признаков подготовки или совершения террористического акта;
в) на пресечение попыток совершения террористических актов на объекте;
г) на минимизацию возможных последствий совершения террористических актов на объекте и ликвидацию угрозы их совершения;
д) на обеспечение защиты служебной информации ограниченного распространения, содержащейся в паспорте безопасности и иных документах объекта, в том числе служебной информации ограниченного распространения о принимаемых мерах по антитеррористической защищенности объекта;
е) на выявление и предотвращение несанкционированного проноса (провоза) и применения на объекте токсичных химикатов, отравляющих веществ и патогенных биологических агентов, в том числе при их получении посредством почтовых отправлений.

На проектируемом объекте организованно помещение охраны на первом этаже (пом.103), в котором находится охранник круглосуточно для оперативного реагирования на срабатывания средств контроля, оборудовано средствами контроля безопасности.

Организованно круглосуточное дежурство, с по часовым обходом объекта резервным охранником, оснащенным для обследования и первичной диагностики бесхозных и иных предметов, а также закладок, ручным металлоискателем «Сфинкс ВМ-611 РД-2.0», газоанализатором паров взрывчатых и наркотических веществ «Кербер-Т», набор досмотровых зеркал.

На главном входе в объект организован стационарный пост. Пост оборудован средствами для досмотра подозрительных лиц и обслуживаются охранниками, осуществляющими досмотр. Запасные входы открываются по мере необходимости и при них оборудуются временный пост, обслуживаемый резервным охранником.

Досмотр осуществляется на стационарном или временном посту, размещенном в помещении в котором поддерживаются климатические условия, необходимые для штатной эксплуатации досмотрового оборудования (температура от 0 до плюс 40 °С; относительная влажность не более 85 % при температуре плюс 25 ± 1 °С).

При срабатывании тревоги на входе панельного металлодетектора «Паутина-Н2-1» (размещенного максимально близко к входным дверям), производится визуальный досмотр подозрительных лиц охранником на наличие взрывных устройств, оружия и боеприпасов с помощью ручного металлоискателя «Сфинкс ВМ-611 РД-2.0» и газоанализатора паров взрывчатых и наркотических веществ «Кербер-Т».

Досмотр посетителей на временном посту осуществляется резервным охранником с использованием переносных средств: газоанализатора паров взрывчатых и наркотических веществ «Кербер-Т», ручного металлоискателя «Сфинкс ВМ-611 РД-2.0», на наличие взрывных устройств, оружия и боеприпасов.

Резервный охранник с использованием этих же средств также по мере необходимости осуществляет досмотр почтовых отправлений и автотранспорта, въезжающего на территорию объекта.

Минимальное кол-во охранников в рабочий день не менее 3-х человек (1 в комнате охраны: 1 на посту охраны при входе и 1 дополнительный, для обхода здания и территории и на случай необходимости досмотра транспортного средства на въезде на территорию). На ночь остается 1 человек.

Количество средств обнаружения взрывчатых, отравляющих веществ, оружия, боеприпасов, наркотических средств и других опасных предметов и веществ на объекте принимается из расчета: стационарный металлодетектор «Паутина-Н2-1» - 1 единицы на 1 стационарный пост и локализатор взрыва типа «Фонтан-2» - 1 единицы на 1 стационарный пост (см. план 1-го этажа и спецификацию); ручной металлоискатель «Сфинкс ВМ-611 РД-2.0», газоанализатор паров взрывчатых веществ «Кербер-Т», на 1 охранника стационарного поста и набор досмотровых зеркал и 1 ручной металлодетектор на резервного охранника.

Во время работы учреждения, при обращении, с помощью тревожной системы связи, охрана объекта фиксирует причину обращение и оперативно реагирует для устранения этой причины, в случае невозможности самостоятельно ликвидировать причину, вызывают на объект соответствующую службу для ликвидации причины обращения по экстренной связи. При срабатывании пожарной сигнализации, самостоятельные действия могут осуществляться подручными средствами в случае, если нет прямой угрозы жизни и здоровью сотруднику охраны. Своевременные и правильные действия сотрудников охраны при срабатывании пожарной сигнализации, должны предотвратить гибель людей и самого объекта.

При обнаружении взрывного устройства или источников ионизирующих излучений, немедленно сообщить по экстренной связи в соответствующую службу и организовывать работу по выводу людей из опасной зоны.

Взам. инв. №

Подпись и дата

Инв. № подл.

Изм.	Кол.	Лист	№док	Подпись	Дата	2024-00375-01-0-ПТА		
Разработал		Фугельзанг Е.А.				Капитальный ремонт здания ГБОУ города Москвы "Школа № 1574", расположенное по адресу: г. Москва, пер.Старопименовский, д. 5	Стадия	Лист	Листов
ГАП		Шведов В.В.					П	25	43
Н.контроль		Фугельзанг Е.А.					МОСЖИЛ НИИПРОЕКТ		
Нач.М-1		Чередниченко В.В.							

Общие требования к организации эксплуатации комплексной системе безопасности (по ГОСТу Р 53704-2009) *Общие требования включают следующие мероприятия:*

- организацию и проведение планового технического обслуживания (регламентные работы) (далее по тексту ТО) проводят в сроки, установленные в нормативных документах, утвержденных в установленном порядке;
- проведение планово-предупредительного ремонта на местах установки технических средств проводят согласованному графику;
- внеплановое ТО (проводят при необходимости);
- техническое освидетельствование (переосвидетельствование) объекта после ЧС, в случае временной приостановки действия (целевого применения) технических средств с их возможной последующей регламентируемой консервацией (например, для подсистем сигнализации, теле/видеонаблюдения, досмотра и поиска, связи, пожарной автоматики);
- проведение текущих ремонтов, включая использование обменного фонда (если это установлено в нормативных документах и предусмотрено договором на обслуживание объекта);
- своевременную отправку отказавших технических средств в ремонтные предприятия и получение их из ремонта производит технический персонал;
- содержание обменного фонда в объемах, необходимых для проведения восстановительных работ на объекте производится за минимальное время;
- на объекте имеется помещение для хранения приборов, оборудования, материалов и инструментов, необходимых для проведения восстановительных работ в технических подсистемах КСБ;
- организацию и содержание рабочих мест для проведения ремонтов силами технической службы объекта обязанность;
- проведение постоянного технического надзора за состоянием технических подсистем;
- проведение периодических технических осмотров контрольных зон с установленными техническими средствами подсистем;
- техническое освидетельствование/переосвидетельствование подсистем по результатам эксплуатации;
- производится списание и утилизацию пришедших в негодность и выработавших установленные сроки службы или достигших предельного состояния по износу технических средств подсистем;
- производится ведение эксплуатационной документации (паспортов, журналов по эксплуатации);
- производится проведение статистического анализа по результатам эксплуатации технических средств подсистем.

Периодичность осмотров:

- ежедневные – производятся ежедневно при сдаче и приеме смены;
- сезонные – производятся 2 раза в год (перед летним и перед зимним сезонами). ТО и ремонт технических средств проводят по официально утвержденным действующим методикам, инструкциям, руководствам, описаниям и нормативам. Списание восстанавливаемых технических средств проводят в установленном порядке по истечении сроков службы и на основании критериев предельного состояния, устанавливаемых в нормативных документах на конкретные изделия. Списание и утилизацию не подлежащих восстановлению технических средств проводят на основании экспертных заключений по ГОСТ Р 51769, ГОСТ Р 52106, ГОСТ Р 52108. Эксплуатационная документация технических средств должна соответствовать ГОСТ 2.601.В делопроизводстве и отчетности при эксплуатации применяют документы по ГОСТ Р 6.30 или нестандартизованные текстовые документы в вербальной форме: указания, предписания, представления, планы, планы-графики, акты, справки, служебные записки, уведомления, заключения, протоколы, перечни.

Взам. инв. №

Подпись и дата

Инв. № подл.

Изм.	Кол.	Лист	№док	Подпись	Дата	**2024-00375-01-0-ПТА**		
Разработал		Фугельзанг Е.А.				Капитальный ремонт здания ГБОУ города Москвы "Школа № 1574", расположенное по адресу: г. Москва, пер.Старопименовский, д. 5	Стадия	Лист	Листов
ГАП		Шведов В.В.					П	26	43
Н.контроль		Фугельзанг Е.А.					МОСЖИЛ НИИПРОЕКТ		
Нач.М-1		Чередниченко В.В.							

5. ПЕРЕЧЕНЬ ИСПОЛЬЗУЕМЫХ СОКРАЩЕНИЙ И ОБОЗНАЧЕНИЙ

Сокращенное наименование	Полное наименование
АРМ	*Автоматизированное рабочее место*
ЛВ	*Локализация взрыва*
МГН	*Маломобильные группы населения*
МИ	*Ручной металлоискатель*
ПТА	*Мероприятие по противодействию террористическим актам*
РАСЦО	*Региональная автоматизированная система централизованного оповещения населения*
СКТВ	*Система кабельного телевидения*
СКС	*Структурированная кабельная система*
СКУД	*Система контроля и управления доступом*
СОТС	*Система охранно-тревожной сигнализации*
СОО	*Система охранного освещения*
СОТ	*Система охранная телевизионная*
СОУЭ	*Система оповещения и управления эвакуацией*
СЭС	*Система экстренной связи*
ТО	*Техническое обслуживание*
ТУ	*Технические условия*
ЧС	*Чрезвычайная ситуация*

6. ПЕРЕЧЕНЬ ФЕДЕРАЛЬНЫХ ЗАКОНОВ, НОРМАТИВНЫХ ПРАВОВЫХ АКТОВ РОССИЙСКОЙ ФЕДЕРАЦИИ И СООТВЕТСТВУЮЩЕГО СУБЪЕКТА РОССИЙСКОЙ ФЕДЕРАЦИИ, НОРМАТИВНЫХ ДОКУМЕНТОВ, ДОКУМЕНТОВ В ОБЛАСТИ СТАНДАРТИЗАЦИИ И ИНЫХ ДОКУМЕНТОВ, ИСПОЛЬЗОВАННЫХ ПРИ РАЗРАБОТКЕ ПЕРЕЧНЯ МЕРОПРИЯТИЙ ПО ПРОТИВОДЕЙСТВИЮ ТЕРРОРИЗМУ

Дата и номер документа	Наименование документа
Указы президента Российской Федерации	
Указ президента Российской Федерации от 15.02.2006 № 116	О мерах по противодействию терроризму
Федеральные законы	
Федеральный закон от 06.03.2006 № 35-ФЗ	О противодействии терроризму
Федеральный закон от 28.11.2011 № 337-ФЗ	О внесении изменений в градостроительный кодекс Российской Федерации и отдельные законодательные акты Российской Федерации
Федеральный закон от 29.09.2004 № 190-ФЗ	Градостроительный кодекс Российской Федерации
Федеральный закон от 12.02.1998 № 28-ФЗ	О гражданской обороне (в ред. от 22.08.2004 г.)
Федеральный закон от 21.12.1994 № 68-ФЗ	О защите населения и территорий от чрезвычайных ситуаций природного и техногенного характера (в ред. от 22.08.2004 г.)
Федеральный закон от 30.12.2009 № 384-ФЗ	Технический регламент о безопасности зданий и сооружений
Федеральный закон от 21.07.1997 № 116-ФЗ	О промышленной безопасности опасных производственных объектов
Постановления (распоряжения) Правительства	
Постановление Правительства от 16.02.2008 № 87	О составе разделов проектной документации и требованиях к их содержанию
Постановление Правительства от 28.05.2021г. № 815	"Об утверждении перечня национальных стандартов и сводов правил (частей таких стандартов и сводов правил), в результате применения которых на обязательной основе обеспечивается соблюдение требований Федерального закона "Технический регламент о безопасности зданий и сооружений", и о признании утратившим силу постановления Правительства Российской Федерации от 4 июля 2020 г. N 985"
Постановление Правительства РФ от 2 августа 2019 г. № 1006	“Об утверждении требований к антитеррористической защищенности объектов (территорий) Министерства просвещения Российской Федерации и объектов (территорий), относящихся к сфере деятельности Министерства просвещения Российской Федерации, и формы паспорта безопасности этих объектов (территорий)”
Нормативно-технические документы	
Свод Правил СП 132.13330.2011	Обеспечение антитеррористической защищенности зданий и сооружений. Общие требования проектирования (утвержден и введен в действие приказом Министерства регионального развития РФ от 05.07.2011 г. № 320)

Взам. инв. №

Подпись и дата

Инв. № подл.

Изм.	Кол.	Лист	№док	Подпись	Дата

2024-00375-01-0-ПТА

Разработал	Фугельзанг Е.А.	
ГАП	Шведов В.В.	
Н.контроль	Фугельзанг Е.А.	
Нач.М-1	Чередниченко В.В.	

Капитальный ремонт здания ГБОУ города Москвы "Школа № 1574", расположенное по адресу: г. Москва, пер.Старопименовский, д. 5

Стадия	Лист	Листов
П	28	43

МОСЖИЛ НИИПРОЕКТ

ПРИЛОЖЕНИЯ

Взам. инв. №

Подпись и дата

Инв. № подл.

Изм.	Кол.	Лист	№док	Подпись	Дата	**2024-00375-01-0-ПТА**		
Разработал		Фугельзанг Е.А.				Капитальный ремонт здания ГБОУ города Москвы "Школа № 1574", расположенное по адресу: г. Москва, пер.Старопименовский, д. 5	Стадия	Лист	Листов
ГАП		Шведов В.В.					П	29	43
Н.контроль		Фугельзанг Е.А.					МОСЖИЛ НИИПРОЕКТ		
Нач.М-1		Чередниченко В.В.							

МЕТАЛЛОДЕТЕКТОР ПАНЕЛЬНЫЙ ПАУТИНА-Н2-1





Металлодетектор выполнен в виде двух панелей без соединительной перекладины. Рекомендован к использованию в местах, где требуется обеспечить досмотр с целью обнаружения оружия и иных запрещенных предметов, сохранив высокую пропускную способность за счет широкого прохода до 1,4 метров. При выборе модели просим обращать внимание на допустимую ширину контрольной зоны, поскольку модификация "Паутин-Н2-1" не имеет возможность расширения прохода до 2 м, также как и аналогичная модификация "Паутина-Н2-2" не может использоваться с шириной прохода меньше 1,6 м. При необходимости организации прохода с пограничным расстоянием рекомендуем обратиться к менеджерам компании.

Корпус может быть изготовлен из различных материалов и различных цветов, что позволяет применять модели для реализации любых дизайнерских решений.

Металлодетектор может быть выполнен в конфигурации со сдвоенным проходом для разграничения потоков посетителей или для увеличения ширины зоны досмотра до 3 метров. В такой конфигурации металлодетектор будет состоять из трех панелей, и будет обеспечиваться раздельная индикация тревоги для каждого контрольного прохода.

Металлодетектор включен в Единый реестр радиоэлектронной продукции ПП 878.

В данном разделе представлены базовые стандартные характеристики. По заказу может быть изготовлен металлодетектор с индивидуальными характеристиками, не указанными в описании, или с изменением текущих параметров.

Корпус металлодетектора	пластик АБС
Цвет корпуса (на выбор)	серый или черный
Контрольная зона	800-1400 мм
Количество зон обнаружения	1
Защита настроек системой паролей	есть
Заводские программы обнаружения	50
Возможность создания пользовательских программ	есть
Возможность сохранить все сохраненные пользователем параметры в пользовательскую конфигурацию (позволяет сохранить рабочие параметры для различных условий эксплуатации)	есть
Управление настройками при помощи ПДУ	есть
Энергонезависимая память для сохранения установок	есть
Тестовый режим самодиагностики	есть
Счетчик проходов с функцией маскировки ложных сигналов: активация режима обнаружения при прохождении через контрольную зону металлодетектора	есть
Режимы счетчика проходов	отключение показателя на дисплее, инверсия счетчика проходов, выбор отображения посетителей – сумма или разница показателей
Световая и звуковая сигнализация	есть
Функция "искусственный сигнал тревоги"	есть
Возможность синхронизации нескольких устройств	есть
Минимальное расстояние между металлодетекторами в режиме синхронизации	800 мм

Взам. инв. №

Подпись и дата

Инв. № подл.

Изм.	Кол.	Лист	№док	Подпись	Дата

2024-00375-01-0-ПТА

Разработал	Фугельзанг Е.А.	
ГИП	Шведов В.В.	
Н.контроль	Фугельзанг Е.А.	
Нач. отдела	Чередниченко В.В.	

Капитальный ремонт здания ГБОУ города Москвы "Школа № 1574", расположенное по адресу: г. Москва, пер.Старопименовский, д. 5

Стадия	Лист	Листов
П	30	43

МОСЖИЛ НИИПРОЕКТ

ДОБРОВОЛЬНАЯ СЕРТИФИКАЦИЯ ПРОДУКЦИИ

Система добровольной сертификации в области промышленной и экологической безопасности "Промышленный эксперт"
Зарегистрирована Федеральным агентством по техническому регулированию и метрологии 11.04.2016 г.,
регистрационный №РОСС RU.31485.04ИДЮ0

СЕРТИФИКАТ СООТВЕТСТВИЯ

№ 04ИДЮ101.RU.C04904

Срок действия **с** 22.12.2022 **по** 21.12.2025

№ 1306639

ОРГАН ПО СЕРТИФИКАЦИИ Общества с ограниченной ответственностью «СамараТест». Место нахождения (адрес юридического лица): 443030, РОССИЯ, Самарская область, город Самара, улица Урицкого, дом 19. Адрес места осуществления деятельности: 443030, РОССИЯ, Самарская обл, г Самара, Железнодорожный район, ул. Урицкого, д. 19, комн. 46, 48, 49. Телефон: +7(846)206-03-79. Адрес электронной почты: info@samarasert.ru. Свидетельство о признании компетентности органа по сертификации № РОСС RU.31485.04ИДЮ0.101 от 20.05.2021 года.

ПРОДУКЦИЯ Металлодетекторы, серия «Паутина»
ТУ 4372-001-60773961-2011
Серийный выпуск

код ОК
034-2014 (КПЕС 2008)
27.90.40.190

СООТВЕТСТВУЕТ ТРЕБОВАНИЯМ НОРМАТИВНЫХ ДОКУМЕНТОВ
ГОСТ Р 53705-2009 (Пп. 5.2, 5.8, 5.9.1, 5.9.2 (разд. 6)), ГОСТ Р 50009-2000, ГОСТ 30804.3.2-2013, ГОСТ 30804.3.3-2013, ГОСТ Р 51318.22-99, ГОСТ CISPR 24-2013

код ТН ВЭД
8543709000

ИЗГОТОВИТЕЛЬ ООО «Локаторная техника»
Юридический адрес: 620049, г. Екатеринбург, пер. Автоматики дом 1, офис 27
ИНН: 6670243472

СЕРТИФИКАТ ВЫДАН ООО «Локаторная техника»
Юридический адрес: 620049, г. Екатеринбург, пер. Автоматики дом 1, офис 27
Телефон: 8 (343)345-03-51. E-mail: manager@mdpautina.ru
ИНН: 6670243472

НА ОСНОВАНИИ Протокола испытаний № 330-12-22-ВТ от 21.12.2022 года, выданного Испытательной лабораторией "Вольтекс" Общества с ограниченной ответственностью "ПрофНадзор" (Свидетельство о признании компетентности РОСС RU.31485.04ИДЮ0.121)

ДОПОЛНИТЕЛЬНАЯ ИНФОРМАЦИЯ Схема сертификации: 3с

М.П.

Руководитель органа Подпись **А.М. Кузнецов** (инициалы, фамилия)

Эксперт Подпись **Ф.Ю. Зубков** (инициалы, фамилия)

Взам. инв. №

Подпись и дата

Инв. № подл.

Изм.	Кол.	Лист	№док	Подпись	Дата

2024-00375-01-0-ПТА

Разработал	Фугельзанг Е.А.	
ГИП	Шведов В.В.	
Н.контроль	Фугельзанг Е.А.	
Нач. отдела	Чередниченко В.В.	

Капитальный ремонт здания ГБОУ города Москвы "Школа № 1574", расположенное по адресу: г. Москва, пер.Старопименовский, д. 5

Стадия	Лист	Листов
П	31	43

МОСЖИЛ НИИПРОЕКТ



ФОНТАН-2 модель 10У

Технические характеристики:

Для локализации взрывоопасного предмета, не требующей его перемещения, включает в себя противоосколочный экран. Устройство "Фонтан" позволяет локализовать взрыв и обезопасить людей и здания от его действия. Рекомендуется использовать в административных зданиях, кредитно-финансовых учреждениях, на вокзалах, в аэропортах, метрополитене, музеях, гостиницах и в др. местах большого скопления людей и повышенной опасности террористических актов.

Возможности:

Снижает до минимума разрушения и человеческие жертвы.
Эффективно подавляет фугасное, осколочное, термическое, термобарическое и другие разрушительные последствия взрыва на открытой местности, в замкнутых и полузамкнутых пространствах.
Многократно снижает амплитуду давления на фронте ударной волны.
Размывает и выполаживает фронт ударной волны.
Предотвращает возгорания, термические и термобарические поражения за счет полного подавления огненного шара.
Уменьшает осколочный поток и снижает вероятность поражения.
Блокировка опасной зоны без эвакуации людей и остановки работы (больницы, магазины, стадионы).

Применение:

Обнаруженный взрывоопасный предмет накрывают локализатором взрыва "ФОНТАН-2" до прибытия взрывотехников.
Не требуется перемещать предмет или касаться его, что значительно снижает риск срабатывания взрывоопасного устройства.
При обследовании взрывоопасного предмета, устройство не создает помех в рентгеновском диапазоне.
Быстрая блокировка опасной зоны силами 1-2 человек.

Взам. инв. №

Подпись и дата

Инв. № подл.

Изм.	Кол.	Лист	№док	Подпись	Дата

2024-00375-01-0-ПТА

Разработал	Фугельзанг Е.А.	
ГИП	Шведов В.В.	
Н.контроль	Фугельзанг Е.А.	
Нач. отдела	Чередниченко В.В.	

Капитальный ремонт здания ГБОУ города Москвы "Школа № 1574", расположенное по адресу: г. Москва, пер.Старопименовский, д. 5

Стадия	Лист	Листов
П	32	43

МОСЖИЛ НИИПРОЕКТ

ДОБРОВОЛЬНАЯ СЕРТИФИКАЦИЯ ПРОДУКЦИИ

СЕРТИФИКАТ СООТВЕТСТВИЯ

№ ЦОТК.RU.ПР009.Н.00042

Срок действия с 31.05.2022 по 30.05.2025

№ 0022886

ОРГАН ПО СЕРТИФИКАЦИИ

Орган по сертификации Общество с ограниченной ответственностью "Лаборатория Стандартов" (ОС ООО "Лаборатория Стандартов"), 109443, г. Москва, Волгоградский пр-кт, д.135, к.3, пом. 3 комната 13А, тел. (495)-150-95-38, факс (495)-150-95-38, ОГРН 1187746994984,
Свидетельство № ЦОТК ИДВ0.RU.ОС.ПР009 от 24.06.2019 г.

ПРОДУКЦИЯ

Устройство для защиты от взрыва «Фонтан-2»
ТУ 0989-047-31041642-05
Модельный ряд - см. Приложение (бланк № 0008973)
Серийный выпуск

код ОК
28.99.39.190

СООТВЕТСТВУЕТ ТРЕБОВАНИЯМ НОРМАТИВНЫХ ДОКУМЕНТОВ

код ТН ВЭД

ТУ 0989-047-31041642-05 (п.п. 1.2.3, 1.2.5, 1.2.6) и обеспечивает снижение избыточного давления во фронте воздушной ударной волны до уровня не более 50 кПа с погрешностью измерений не более 10 кПа, расстояние от края изделия при подрыве взрывного устройства и масса ТНТ согласно Приложению

ИЗГОТОВИТЕЛЬ

Акционерное общество «Научно-производственное объединение специальных материалов»
194044, г. Санкт-Петербург, Большой Сампсониевский проспект, д. 28а,
тел.: +7(812) 294-58-97, электронная почта: nii@npo-sm.ru

СЕРТИФИКАТ ВЫДАН

Акционерное общество «Научно-производственное объединение специальных материалов»
194044, г. Санкт-Петербург, Большой Сампсониевский проспект, д. 28а,
тел.: +7(812) 294-58-97, электронная почта: nii@npo-sm.ru

НА ОСНОВАНИИ

Протоколов испытаний № Ц006С-22 от 12.05.2022 г., № Ц007С-22 от 12.05.2022 г., № Ц008С-22 от 12.05.2022 г., № Ц010С-22 от 25.05.2022 г., выданных ИЦ СМИ АО «НПО Спецматериалов», № 206С-16 от 04.07.16 г., № 411С-17 от 25.09.17 г., выданных ИЦ СМИ ЗАО «НПО СМ», свидетельство № ЦОТК ИДВО.RU.ИЛ.ПР010
Сертификата ISO 9001:2015 № RU003529 АО «Бюро Веритас Сертификейшн Русь»

ДОПОЛНИТЕЛЬНАЯ ИНФОРМАЦИЯ

Орган по сертификации ООО "Лаборатория Стандартов" ЦОТК ИДВ0.RU.ОС.ПР009 ЦОТК М.П.

Руководитель органа _____ Солодских Алексей Сергеевич
подпись — инициалы, фамилия

Эксперт _____ Зуева Юлия Алексеевна
подпись — инициалы, фамилия

Сертификат не применяется при обязательной сертификации

АО «Опцион», Москва, 2018, «В»

Взам. инв. №

Подпись и дата

Инв. № подл.

Изм.	Кол.	Лист	№док	Подпись	Дата

2024-00375-01-0-ПТА

Разработал	Фугельзанг Е.А.	
ГИП	Шведов В.В.	
Н.контроль	Фугельзанг Е.А.	
Нач. отдела	Чередниченко В.В.	

Капитальный ремонт здания ГБОУ города Москвы "Школа № 1574", расположенное по адресу: г. Москва, пер.Старопименовский, д. 5

Стадия	Лист	Листов
П	33	43

МОСЖИЛ НИИПРОЕКТ

Металлоискатель СФИНКС ВМ-611 РД-2.0



Назначение и применение

Досмотровый детектор радиоактивных и металлических объектов "СФИНКС" ВМ-611РД-2.0 предназначен для одновременного обнаружения радиоактивных и ядерных материалов по их гамма-излучению, а так же объектов из цветных и черных металлов, при проведении личного досмотра, контроле багажа и корреспонденции на проходных и контрольно-пропускных пунктах любых гражданских и военных объектов.

Прибор «СФИНКС» ВМ-611РД-2.0 выявляет проносимые людьми источники радиоактивного излучения и металлические предметы, такие как оружие, контейнеры для радиоактивных материалов.

Модель «СФИНКС» ВМ-611РД-2.0 призвана обеспечить решение актуальных задач, связанных с противодействием несанкционированному перемещению радиоактивных и ядерных материалов.

Прибор может использоваться предприятиями ядерно-промышленного комплекса, службами таможенного контроля и досмотра, специальными подразделениями МВД и ФСБ, охранными предприятиями и прочими службами в качестве портативного средства обнаружения радиоактивных материалов из черных и цветных металлов.

Технические характеристики

Рабочая частота металлоискателя:	50 кГц;
Вероятность обнаружения:	0,98;
Чувствительность - пистолет ПМ:	160 мм.;
Питание:	9В;
Время непрерывной работы:	около 120 ч. (при использовании U9VL-J 9V);
Ток потребления:	10 мА;
Порог срабатывания индикации разряда батареи:	6,5 В;
Вес:	0,38 кг.;
Габариты:	420 х 80 х 30 мм.;
Диапазон рабочих температур:	-15...+50 С°

Детектор гамма-излучений (сцинтиллятор) имеет следующий характеристики:

- Диапазон энергий регистрируемого гамма излучения от 0,03 до 3 МэВ;
- Импульсная чувствительность детектора (по Cs137) - 200 (имп/с)/ (мкЗв/ч);
- Пределы допускаемой основной относительной погрешности измерения (по линии Cs137) не более + 30%;
- Порог срабатывания по МЭД - 0,3 мкЗв/ч*;
- Частота ложных срабатываний в режиме поиска У-излучения не более одного срабатывания при уровне У-фона 0,1-0,2 мкЗв/ч за 10 минут;

* может быть изменен по требованию заказчика;

Взам. инв. №

Подпись и дата

Инв. № подл.

Изм.	Кол.	Лист	№док	Подпись	Дата

2024-00375-01-0-ПТА

Разработал	Фугельзанг Е.А.	
ГИП	Шведов В.В.	
Н.контроль	Фугельзанг Е.А.	
Нач. отдела	Чередниченко В.В.	

Капитальный ремонт здания ГБОУ города Москвы "Школа № 1574", расположенное по адресу: г. Москва, пер.Старопименовский, д. 5

Стадия	Лист	Листов
П	34	43

МОСЖИЛ НИИПРОЕКТ

СИСТЕМА СЕРТИФИКАЦИИ ГОСТ Р

ФЕДЕРАЛЬНОЕ АГЕНТСТВО ПО ТЕХНИЧЕСКОМУ РЕГУЛИРОВАНИЮ И МЕТРОЛОГИИ

Добровольная сертификация

СЕРТИФИКАТ СООТВЕТСТВИЯ

№ РОСС RU.AM05.Н13293

Срок действия с 12.05.2022 по 11.05.2025

№ 0632365

ОРГАН ПО СЕРТИФИКАЦИИ RA.RU.11AM05

Орган по сертификации продукции ООО "Центр сертификации и экспертизы "Тверьэкс". Адрес: 390013, РОССИЯ, Рязанская обл, Рязань г, Ситниковская ул, дом 69а, 38. Телефон 8-916-423-9885, адрес электронной почты: os-tverex@yandex.ru

ПРОДУКЦИЯ Металлоискатели портативные электромагнитные модели ВМ-611Х, ВМ-611Х ПРО, ВМ-611 ВИХРЬ, ВМ-611 ВИХРЬ ПРО, ВМ-611 ВИХРЬ Т, изготовлены в соответствии с ТУ-4276-001-11641506-22, торговая марка «Сфинкс» ("SPHINX"). Серийный выпуск.

код ОК 26.51.66.120

СООТВЕТСТВУЕТ ТРЕБОВАНИЯМ НОРМАТИВНЫХ ДОКУМЕНТОВ

ТУ-4276-001-11641506-22 «МЕТАЛЛОИСКАТЕЛИ ПОРТАТИВНЫЕ ЭЛЕКТРОМАГНИТНЫЕ серии ВМ-611».

код ТН ВЭД 9031803800

ИЗГОТОВИТЕЛЬ Закрытое акционерное общество "СФИНКС". ОГРН: 1027739827444. Адрес: 125413, РОССИЯ, Москва, улица Онежская, дом 24, строение 1, комната 29, телефон: +74951500906, адрес электронной почты: info@sphinx-md.ru.

СЕРТИФИКАТ ВЫДАН Закрытое акционерное общество "СФИНКС". ОГРН: 1027739827444. Адрес: 125413, РОССИЯ, Москва, улица Онежская, дом 24, строение 1, комната 29, телефон: +74951500906, адрес электронной почты: info@sphinx-md.ru.

НА ОСНОВАНИИ

Протокол испытаний № 004/Е-12/05/22 от 12.05.2022 года, выданный Испытательной лабораторией "Вега-тест" (аттестат РОСС RU.31578.04ОЛН0.ИЛ23)

ДОПОЛНИТЕЛЬНАЯ ИНФОРМАЦИЯ

Схема сертификации: 1с

Для сертификатов М.П.

Руководитель органа _____ (подпись) М.А. Шуршова (инициалы, фамилия)

Эксперт _____ (подпись) А.А. Белянин (инициалы, фамилия)

Сертификат не применяется при обязательной сертификации

АО «ОПЦИОН», Москва, 2019, «Б» лицензия № 05-05-09/003 ФНС РФ, тел. (495) 726 4742, www.opcion.ru

Взам. инв. №

Подпись и дата

Инв. № подл.

Изм.	Кол.	Лист	№док	Подпись	Дата

2024-00375-01-0-ПТА

Разработал	Фугельзанг Е.А.	
ГИП	Шведов В.В.	
Н.контроль	Фугельзанг Е.А.	
Нач. отдела	Чередниченко В.В.	

Капитальный ремонт здания ГБОУ города Москвы "Школа № 1574", расположенное по адресу: г. Москва, пер.Старопименовский, д. 5

Стадия	Лист	Листов
П	35	43

МОСЖИЛ НИИПРОЕКТ

Устройство для контроля и идентификации взрывчатых и наркотических веществ **«ИДД Кербер-Т»**



Описание:

ИДД «Кербер-Т» соответствует требованиям, предъявляемым к техническим средствам обеспечения защищенности объектов транспортной инфраструктуры, регламентированным документами: №16/УНТР/1-2258от 03.07.2013, №16/УНТР/1-3827 от 15.12.2010 с дополнением №16/УНТР/1-758 от 24.02.2014, для категории технических средств – портативные обнаружители паров и следов ВВ. (Заключение ФГКУ «В/ч 35533» №16/16/С6/2/2331).

ИДД «Кербер-Т» как техническое средство обнаружения и идентификации взрывчатых веществ обладает чувствительностью, позволяющей определять наличие следующих взрывчатых веществ и их компонентов: нитроамины (гексоген, октоген, тетрил), нитроэфиры (нитроглицерин, этиленгликольдинитрат, ТЭН), нитроароматические соединения (тротил, динитротолуол), органические перекисные соединения (перекись ацетона, ГМТД), неорганические нитраты (аммиачная, калийная и натриевая селитры), а также смесевые взрывчатые вещества на их основе.

Технические характеристики:

Принцип детектирования	Биполярная спектрометрия ионной подвижности
Способ ионизации	Импульсный коронный разряд (без радиоактивного источника)
Габаритные размеры детектора (Д×Ш×В)	410×110×170 мм
Масса	3,7 кг
Обнаруживаемые взрывчатые вещества	Бризантные и инициирующие; промышленные и самодельные. В т.ч.: ТНТ, гексоген, ТЭН, ДНТ, нитроглицерин, ЭГДН, октоген, тетрил, тринитрофенол, аммиачная селитра/АСДТ, динитронафталин, триперекись ацетона, ГМТД, а также смесевые ВВ на их основе (пластиты, динамиты, пороха и пр.)
Обнаруживаемые наркотические средства и психотропные вещества	Каннабиоиды (гашиш, марихуана), опиаты (морфин, героин,кодеин, фентанил и др.), амфетамины (амфетамин, метамфетамин, МДМА и др.), кокаин и др.
Обнаруживаемые опасные химические агенты	Аварийно химически опасные вещества: Сероводород, хлористый водород (соляная кислота), фтористый водород (плавиковая кислота), сернистый газ (сернистый ангидрид), хлор, аммиак, азотная кислота. Боевые отравляющие вещества: Зарин, зоман, Ви-Экс (VX), горчичный газ (иприт), фосген/дифосген, синильная (цианистоводородная) кислота/цианиды.
Диапазон детектирования малолетучих веществ по 2,4,6-тринитротолуолу (ТНТ), г,	от 1,0·10-11 до 2,0·10-7
Предел обнаружения малолетучих веществ по 2,4,6-тринитротолуолу (ТНТ), — по твердым частицам, г, не более	1,0·10-11
— по парам, г/см3, не более	1,0·10-14
Время установления рабочего режима, мин, не более	15
Время обнаружения и идентификации для всех обнаруживаемых веществ, сек, не более	5
Время переключения между режимами детектирования паров и частиц, сек, не более	1
Переключение между режимами детектирования паров и частиц	Без присоединения дополнительных приспособлений
Время смены типа анализируемых ионов (автоматическая циклическая смена полярности), сек, не более	0,2
Вероятность ложного срабатывания, %, не более	1
Время непрерывной автономной работы со штатным блоком аккумуляторных батарей, час, не менее	4
Время очистки детектора при нормальных условиях эксплуатации, мин, не более	3

Взам. инв. №

Подпись и дата

Инв. № подл.

Изм.	Кол.	Лист	№док	Подпись	Дата

2024-00375-01-0-ПТА

Разработал	Фугельзанг Е.А.	
ГИП	Шведов В.В.	
Н.контроль	Фугельзанг Е.А.	
Нач. отдела	Чередниченко В.В.	

Капитальный ремонт здания ГБОУ города Москвы "Школа № 1574", расположенное по адресу: г. Москва, пер.Старопименовский, д. 5

Стадия	Лист	Листов
П	36	43

МОСЖИЛ НИИПРОЕКТ

RUSSIAN FEDERATION

№ 0153548

СИСТЕМА ДОБРОВОЛЬНОЙ СЕРТИФИКАЦИИ
«ПРОМТЕХСТАНДАРТ»

№РОСС RU.32001.04ИБФ1 в едином реестре зарегистрированных систем добровольной сертификации
ФЕДЕРАЛЬНОЕ АГЕНТСТВО ПО ТЕХНИЧЕСКОМУ РЕГУЛИРОВАНИЮ И МЕТРОЛОГИИ

СЕРТИФИКАТ СООТВЕТСТВИЯ

Регистрационный номер РОСС RU.32001.04ИБФ1.ОСП18.26599

Срок действия с 29.11.2022 по 28.11.2025

ОРГАН ПО СЕРТИФИКАЦИИ № РОСС RU.32001.04ИБФ1.ОСП18, Общество с ограниченной ответственностью «ВНИИЦИ», 107076, г. Москва, вн.тер.г. Муниципальный Округ Преображенское, ул. Потешная, д. 6, этаж/помещ. 2/II, ком./офис 9/1, ИНН: 9718166591, ОГРН: 1207700477665, email: vniici@yandex.ru

ПРОДУКЦИЯ Спектрометр ионной подвижности «ИДД КЕРБЕР–Т».
Серийный выпуск.

код ОК 26.51.53

код ТН ВЭД 9027 80 170 0

СООТВЕТСТВУЕТ ТРЕБОВАНИЯМ НОРМАТИВНЫХ ДОКУМЕНТОВ
ТУ 4215-002-38343004-12

ИЗГОТОВИТЕЛЬ Общество с ограниченной ответственностью «Модус»
Адрес: Россия, г. Москва, Варшавское шоссе, дом 56, стр. 2, эт. 4, пом. IV, ком. 9,
ИНН: 7726691417, ОГРН: 1127746097841, телефон: 8 (499) 723-11-49, 723-11-28,
электронная почта: sales@modus-ltd.ru

СЕРТИФИКАТ ВЫДАН Общество с ограниченной ответственностью «Модус»
Адрес: Россия, г. Москва, Варшавское шоссе, дом 56, стр. 2, эт. 4, пом. IV, ком. 9,
ИНН: 7726691417, ОГРН: 1127746097841, телефон: 8 (499) 723-11-49, 723-11-28,
электронная почта: sales@modus-ltd.ru

НА ОСНОВАНИИ Протокол испытаний №23749-ВНИ/22 от 28.11.2022, Испытательная лаборатория ООО «ВНИИЦИ» аттестат аккредитации №РОСС RU.32001.04ИБФ1.ИЛ30 от 2021-03-29

ДОПОЛНИТЕЛЬНАЯ ИНФОРМАЦИЯ Схема сертификации: 1с (ГОСТ Р 53603-2009. Оценка соответствия. Схемы сертификации продукции в Российской Федерации).

Проверка подлинности сертификата соответствия

ООО «ВНИИЦИ»

Руководитель органа подпись И.М. Тимохина (инициалы, фамилия)

Эксперт подпись Д.И. Султанов (инициалы, фамилия)

Настоящий сертификат соответствия обязывает организацию поддерживать выпуск (реализацию) продукции в соответствие с вышеуказанным стандартом, что будет находиться под контролем органа по сертификации системы добровольной сертификации «ПромТехСтандарт» и подтверждаться при прохождении ежегодного инспекционного контроля

АО «ОПЦИОН», Москва, 2022 г., «В», ТЗ № 621.

Взам. инв. №

Подпись и дата

Инв. № подл.

Изм.	Кол.	Лист	№док	Подпись	Дата

2024-00375-01-0-ПТА

Разработал	Фугельзанг Е.А.	
ГИП	Шведов В.В.	
Н.контроль	Фугельзанг Е.А.	
Нач. отдела	Чередниченко В.В.	

Капитальный ремонт здания ГБОУ города Москвы "Школа № 1574", расположенное по адресу: г. Москва, пер.Старопименовский, д. 5

Стадия	Лист	Листов
П	37	43

МОСЖИЛ НИИПРОЕКТ

СФИНКС
Набор досмотровых зеркал ДУ-104



Описание

Изделие представляет собой инспекционное зеркало на телескопической (раздвижной) штанге, оснащенное встроенным осветителем. Предназначено для визуального контроля труднодоступных мест, скрытых полостей и предметов, непосредственный осмотр которых затруднен или не возможен в силу их расположения: вблизи земли, между стационарными конструкциями или выше роста человека.

Предназначено для применения:

-сотрудниками силовых структур и сотрудниками ЧОП для осуществления мероприятий по обеспечению установленного порядка досмотра и пропуска транспортных средств и грузов на объекты подлежащие охране, в том числе относящиеся к объектам подгруппы AI (объекты особо важные, повышенной опасности и жизнеобеспечения, включенные в Перечень объектов, подлежащих государственной охране, согласно Постановлению Правительства Российской Федерации от 14 августа 1992 года N587).

-сотрудниками коммунальных служб и технического обслуживающего персонала, при обследовании состояния защитных покрытий, узлов и агрегатов, а также поиска технических неисправностей.

Использование досмотрового устройства не требует специальной подготовки персонала. Досмотр осуществляется при помощи зеркала, закрепленного на телескопической штанге. Подсветка зоны контроля осуществляется светодиодным фонарем, закрепляемым на штанге. Устройство может применяться как на постоянных, так и временных постах контроля, а также мобильными нарядами.

Технические характеристики

Телескопическое зеркало:

Длинна изделия	- от 700 до 2000 мм;
Зеркало (ДУ-104 - 100х60, диаметр 100, 160 и 220 мм);	- 160 мм
Угол поворота зеркала	- 180 град;
Температурный диапазон	- - 20 +60 С°
Вес	- 1 кг.

Фонарь:

Яркость	- 100 лм;
Количество светодиодов	- 9;
Угол поворота на кронштейне	- 45 град;
Питание	- 3 ААА (4,5 В)

Взам. инв. №

Подпись и дата

Инв. № подл.

Изм.	Кол.	Лист	№док	Подпись	Дата	2024-00375-01-0-ПТА		
Разработал		Фугельзанг Е.А.				Капитальный ремонт здания ГБОУ города Москвы "Школа № 1574", расположенное по адресу: г. Москва, пер.Старопименовский, д. 5	Стадия	Лист	Листов
ГИП		Шведов В.В.					П	38	43
Н.контроль		Фугельзанг Е.А.					МОСЖИЛ НИИПРОЕКТ		
Нач. отдела		Чередниченко В.В.							

ДОБРОВОЛЬНАЯ СЕРТИФИКАЦИЯ ПРОДУКЦИИ

СЕРТИФИКАТ СООТВЕТСТВИЯ

№ РОСС.RU.04ССН0.04610

Срок действия с 15.06.2023 по 14.06.2026

№ 05648

ОРГАН ПО СЕРТИФИКАЦИИ

Общества с ограниченной ответственностью "Международный стандарт", 127030, РОССИЯ, город Москва, улица Новослободская, дом 20, этаж 2, помещение I, комната 15, офис 88к, Телефон: +79055740063, Адрес электронной почты: gost-st@mail.ru
Регистрационный номер аттестата аккредитации: РОСС RU.32509.04ССН0.ОС01

ПРОДУКЦИЯ

Досмотровое устройство ДУ-101 (ДУ-104, ДУ-203, ДУ-401). Торговая марка: SPHINX
Серийный выпуск

код ОК
26.51.66.120

СООТВЕТСТВУЕТ ТРЕБОВАНИЯМ НОРМАТИВНЫХ ДОКУМЕНТОВ

ТУ -4276-001-11641506-14

код ТН ВЭД
9031803800

ИЗГОТОВИТЕЛЬ

ЗАКРЫТОЕ АКЦИОНЕРНОЕ ОБЩЕСТВО "СФИНКС". Место нахождения: 125413, Россия, г. Москва, ул. Онежская д.24, стр.1, комн.29, ИНН 7722094018, ОГРН 1027739827444. Адрес места осуществления деятельности по изготовлению продукции: 125413, Россия, г. Москва, ул. Онежская д.24, стр.1, комн.29

СЕРТИФИКАТ ВЫДАН

ЗАКРЫТОЕ АКЦИОНЕРНОЕ ОБЩЕСТВО "СФИНКС". Место нахождения: 125413, Россия, г. Москва, ул. Онежская д.24, стр.1, комн.29, ИНН 7722094018, ОГРН 1027739827444.
Телефон: +74951500906. Адрес электронной почты:info@sphinx-md.ru

НА ОСНОВАНИИ

Протокола испытаний № 22254-МС-2023 от 15.06.2023 года, выданного Испытательной лабораторией «Международный стандарт» Общества с ограниченной ответственностью «Международный стандарт» (регистрационный номер аттестата аккредитации РОСС RU.32509.04ССН0.ИЛ01)

ДОПОЛНИТЕЛЬНАЯ ИНФОРМАЦИЯ

Схема сертификации: 3с.

«МЕЖДУНАРОДНЫЙ СТАНДАРТ» М.П. для сертификатов

Руководитель органа _____ Е.Н. Ситников
подпись — инициалы, фамилия

Эксперт _____ А.Л. Чернышевский
подпись — инициалы, фамилия

Сертификат не применяется при обязательной сертификации

АО «ОПЦИОН», Москва, 2023 г., «В», ТЗ № 483.

Взам. инв. №

Подпись и дата

Инв. № подл.

Изм.	Кол.	Лист	№док	Подпись	Дата

2024-00375-01-0-ПТА




Разработал	Фугельзанг Е.А.	
ГИП	Шведов В.В.	
Н.контроль	Фугельзанг Е.А.	
Нач. отдела	Чередниченко В.В.	

Капитальный ремонт здания ГБОУ города Москвы "Школа № 1574", расположенное по адресу: г. Москва, пер.Старопименовский, д. 5

Стадия	Лист	Листов
П	39	43

МОСЖИЛ НИИПРОЕКТ

Состав оборудования

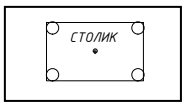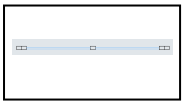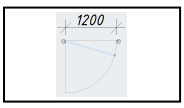Обозначение	Наименование	Кол-во, шт.
1	2	3
МД*	Металлодетектор стационарный «Паутина-Н2-1»	1
РМД	Ручной металлодетектор «ВМ-611 Сфинкс РД-2.0»	2
ГАПВВ	Газоанализатор паров взрывчатых веществ «Кербер-Т»	1
ЛВ	Локализатор взрыва «Фонтан-2» мод. 10У	1
Д	Набор досмотровых зеркал	1
	Стол досмотровый СД-950 (500х400х900)	1
	Ограждение полуростовое	2** п.м.
	Калитка одностворчатая	1

* Поставку, монтаж и выполнение пусконаладочных работ стационарных металлодетекторов выполнить силами подрядной организации в рамках проведения капитального ремонта

** Точный метраж измеряется после установки и настройки оборудования

Оборудование может быть заменено на аналог с такими же техническими характеристиками

Взам. инв. №

Подпись и дата

Инв. № подл.

Изм.	Кол.	Лист	№док	Подпись	Дата

2024-00375-01-0-ПТА

Разработал	Фугельзанг Е.А.	
ГИП	Шведов В.В.	
Н.контроль	Фугельзанг Е.А.	
Нач. отдела	Чередниченко В.В.	

Капитальный ремонт здания ГБОУ города Москвы "Школа № 1574", расположенное по адресу: г. Москва, пер.Старопименовский, д. 5


Стадия	Лист	Листов
П	40	43

МОСЖИЛ НИИПРОЕКТ

Здание Государственного бюджетного общеобразовательного учреждения города Москвы "Школа № 1574", расположенное по адресу: г. Москва, пер.Старопименовский, д. 5

План подвала

Масштаб 1:200

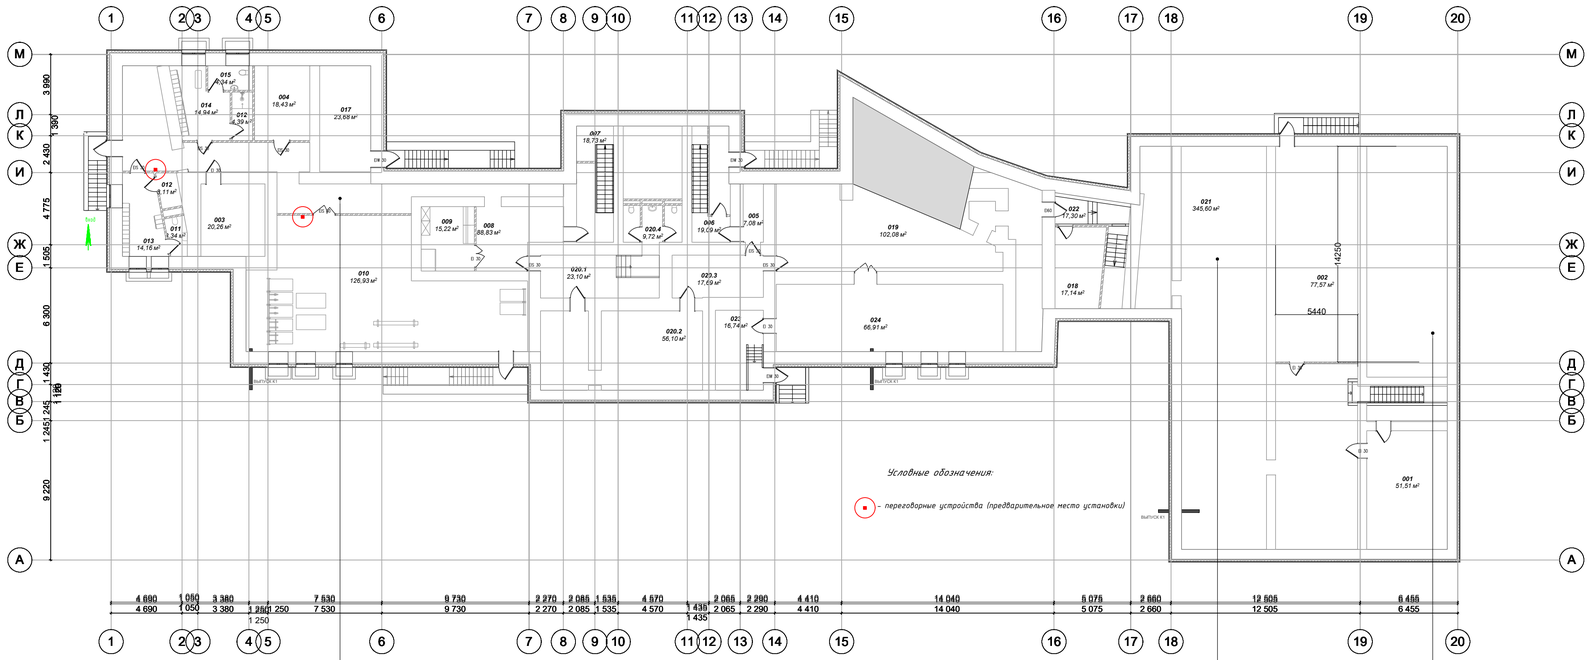

Обеспыливание путей эвакуации ко всем техническим помещениям

Обеспыливание путей эвакуации ко всем техническим помещениям

Обеспыливание путей эвакуации ко всем техническим помещениям

Экспликация помещений подвала

№	Наименование	Площадь	Кат.пом
001	Венткамера	51,51	Д
002	ИТП	77,57	В4
003	Техподполье	20,26	
004	Техподполье	18,43	
005	Коридор	7,08	
006	Лестничная клетка (Тип Л1)	19,09	
007	Лестничная клетка (Тип Л1)	18,73	
008	Коридор	88,83	
009	Снарядная	15,22	В3
010	Зал ЛФК	126,93	
011	Санузел	3,34	
012	Душевая	4,39	
012	Душевая	3,11	
013	Раздевальная	14,16	
014	Раздевальная	14,94	
015	Санузел	4,34	
017	Электрощитовая	23,68	В4
018	Подсобное помещение	17,14	В4
019	Коридор	102,08	
020.1	Помещение укрытия	23,10	
020.2	Помещение укрытия	56,10	
020.3	Помещение укрытия	17,69	
020.4	Техподполье	9,72	
021	Техподполье	345,60	
022	Лестничная клетка (Тип Н2)	17,30	

Площадь здания мменее 1300 кв метра разделение на пожарные зоны не требуются

ПРИМЕЧАНИЯ:

1. Возможность устройства проемов в несущих стенах будет уточняться в проекте;

2. Размер и расположение вентиляционных шахт будет уточнен в проекте;

3. Шахты,предназначенные для прокладки инженерных коммуникаций и стояков (ВК СС ЭОМ) оборудуются лючками для обслуживания;

4. Доступ маломобильных групп населения М1-М4 предусмотреть только на 1 этаж в помещения: коридор с зоной ожидания, санузел для МГН,помещение охраны,административные кабинеты.

5. Конструкция входных групп,в т.ч. количество ступеней и конфигурация пандуса уточняется разделом "Фасады"

*категорирование по взрывопожарной и пожарной опасности данных помещений выполнить на этапе проектирования

Условные обозначения:

- Музей
- Техподполье
- Технические помещения
- Помещение общего пользования
- Спортивные помещения
- Защитное сооружение гражданской обороны

Разработано:

Первый заместитель директора-
главный инженер
ГАУ "МосжилНИИпроект"

Img_8BCFBE4D_8BCFBE4D.bmp

К.Н. Сухов

*Площади помещений, открывание и габариты дверей уточняются проектом

Согласовано

Взамен инв. №

Подпись и дата

Инв. № подл

Копировал


Формат А1

Здание Государственного бюджетного общеобразовательного учреждения города Москвы "Школа № 1574", расположенное по адресу: г. Москва, пер.Старопименовский, д. 5

План 1 этажа

Масштаб 1:200

Начальна школа (1-4 классы)- 8 классов (160 чел.),
Основная школа (5-9 классы) - 10 классов (200 чел.),
Старшая школа (10-11 классы) - 2 классов (40 чел.)
Наполняемость - 400 учащихся, (количество классов: 20)

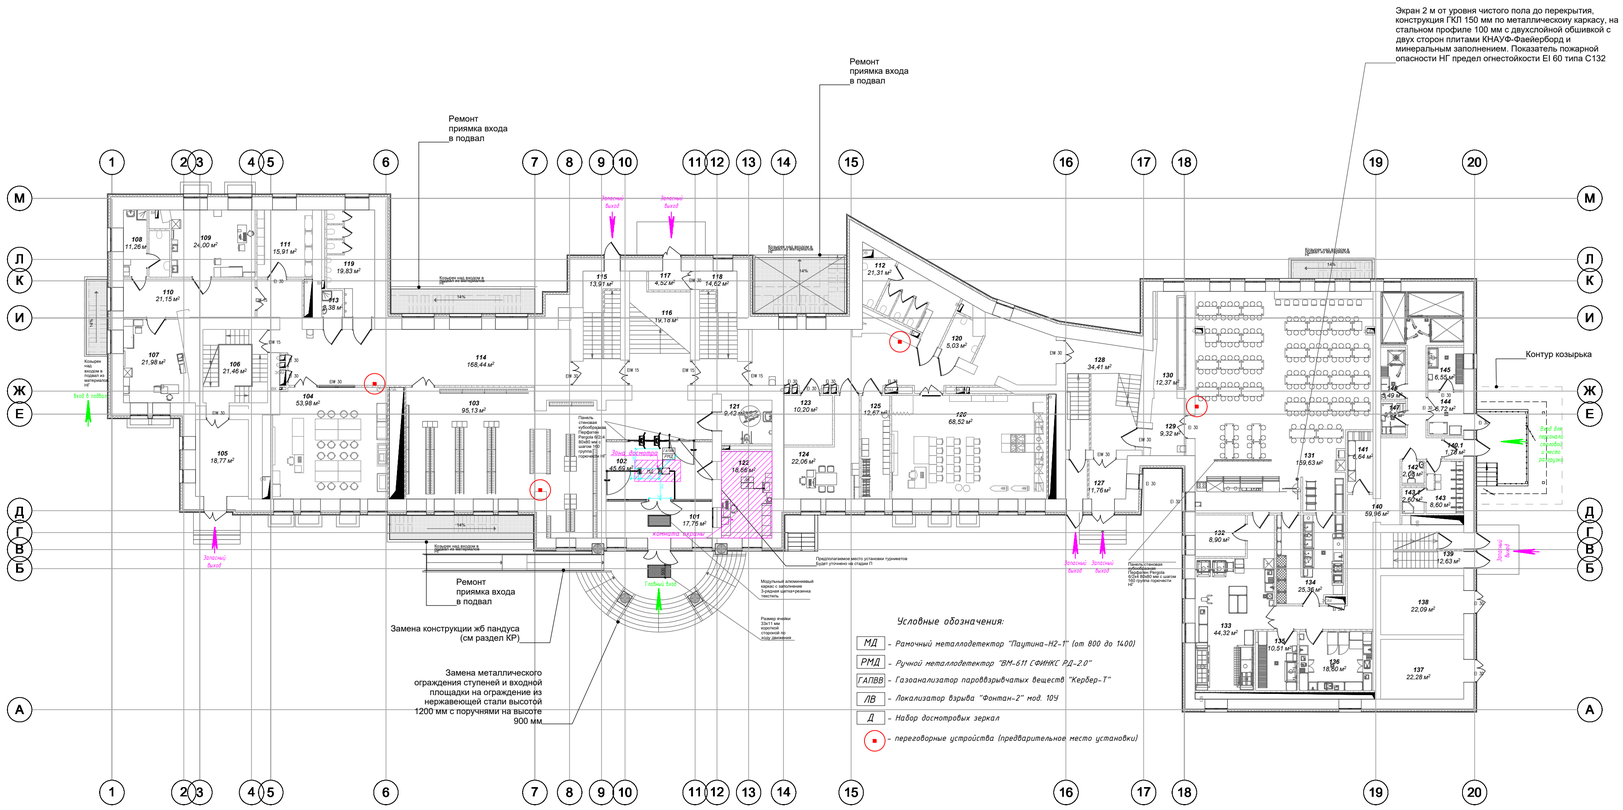

Экспликация помещений 1-го этажа			
№	Наименование	Площадь	Кат.пом
101	Тамбур	17,76	
102	Зона ожидания	45,69	
103	Гардеробная для обучающихся(начальная,основная и старшая школы)	95,13	
104	Кабинет материальной технологии тип2	53,98	
105	Тамбур	18,77	
106	Лестничная клетка(тип Н2)	21,46	
107	Процедурный(прививочный)кабинет	21,98	
108	Туалет медблока с местом для приготовления дезинфицирующих растворов и хрпанения уборочного инвентаря,предназначенных для помещений медицинского назначения	11,26	
109	Кабинет врача	24,00	
110	Коридор	21,15	
111	Кладовая кабинета материальной технологии	15,91	В3
112	Санузел для девочек с комнатой личной гигиены	21,31	
113	ПУИ	2,38	В4
114	Коридор	168,44	
115	Лестничная клетка(тип Л1)	13,91	
116	Лестничная клетка(тип Л1)	19,18	
117	Тамбур	4,52	
118	Лестничная клетка(тип Л1)	14,62	
119	Санузел для мальчиков	19,83	
120	Санузел для персонала	5,03	
121	Санузел для МГН	9,42	
122	Комната охраны	18,66	
123	Кроссовая	10,20	В3
124	Административный кабинет тип 1	22,06	
125	Гардеробная комната (для учителей)	12,67	
126	Кабинет материальной технологии тип1	68,52	
127	Тамбур	11,76	
128	Лестничная клетка(тип Н2)	34,41	
129	Коридор	9,32	
130	Умывальные	12,37	
131	Обеденный зал	159,63	
132	Холодный цех	8,90	*
133	Горячий цех	44,32	*
134	Моечная столовой посуды	25,36	*
135	Моечная кухонной посуды	10,51	*
136	Доготовочный цех	18,60	*
137	Техническое помещение	22,28	В3
138	Техническое помещение	22,09	В3
139	Лестничная клетка(тип Л1)	12,63	
140	Коридор с местом установки холодильного оборудования	59,96	*
140.1	Тамбур	1,78	
141	Кладовая сухих продуктов	6,64	*
142	Санузел	2,08	
143	Помещения для персонала	8,60	
143.1	Душ	2,60	
144	Загрузочный цех	6,72	*
145	Кладовая и моечная оборотной тары	6,55	*
146	Помещения для временного хранения пищевых отходов	5,49	*
147	ПУИ	3,99	*
		1 254,43 м^2	

Условные обозначения:

- Помещения общего пользования
- Административные и служебно-бытовые помещения
- Сантехнические помещения
- Специализированные кабинеты
- Гардеробные
- Спортивные помещения
- Технические помещения
- Медицинские помещения
- Пищеблок

Площадь здания мменее 1300 кв метра разделение на пожарные зоны не требуются

ПРИМЕЧАНИЯ:

1. Возможность устройства проемов в несущих стенах будет уточняться в проекте;

2. Размер и расположение вентиляционных шахт будет уточнен в проекте;

3. Шахты,предназначенные для прокладки инженерных коммуникаций и стояков (ВК СС ЭОМ) оборудуются лючками для обслуживания;

4. Доступ маломобильных групп населения М1-М4 предусмотреть только на 1 этаж в помещения: коридор с зоной ожидания, санузел для МГН,помещение охраны,административные кабинеты.

5. Конструкция входных групп,в т.ч. количество ступеней и конфигурация пандуса уточняется разделом "Фасады"

*категорирование по взрывопожарной и пожарной опасности данных помещений выполнить на этапе проектирования

*Площади помещений, открывание и габариты дверей уточняются проектом

Согласовано

Взамен инв. N°

Подпись и дата

Инв. N° подл


Копировал

Формат А1

Здание Государственного бюджетного общеобразовательного учреждения города Москвы "Школа № 1574", расположенное по адресу: г. Москва, пер.Старопименовский, д. 5

План 2 этажа

Масштаб 1:200

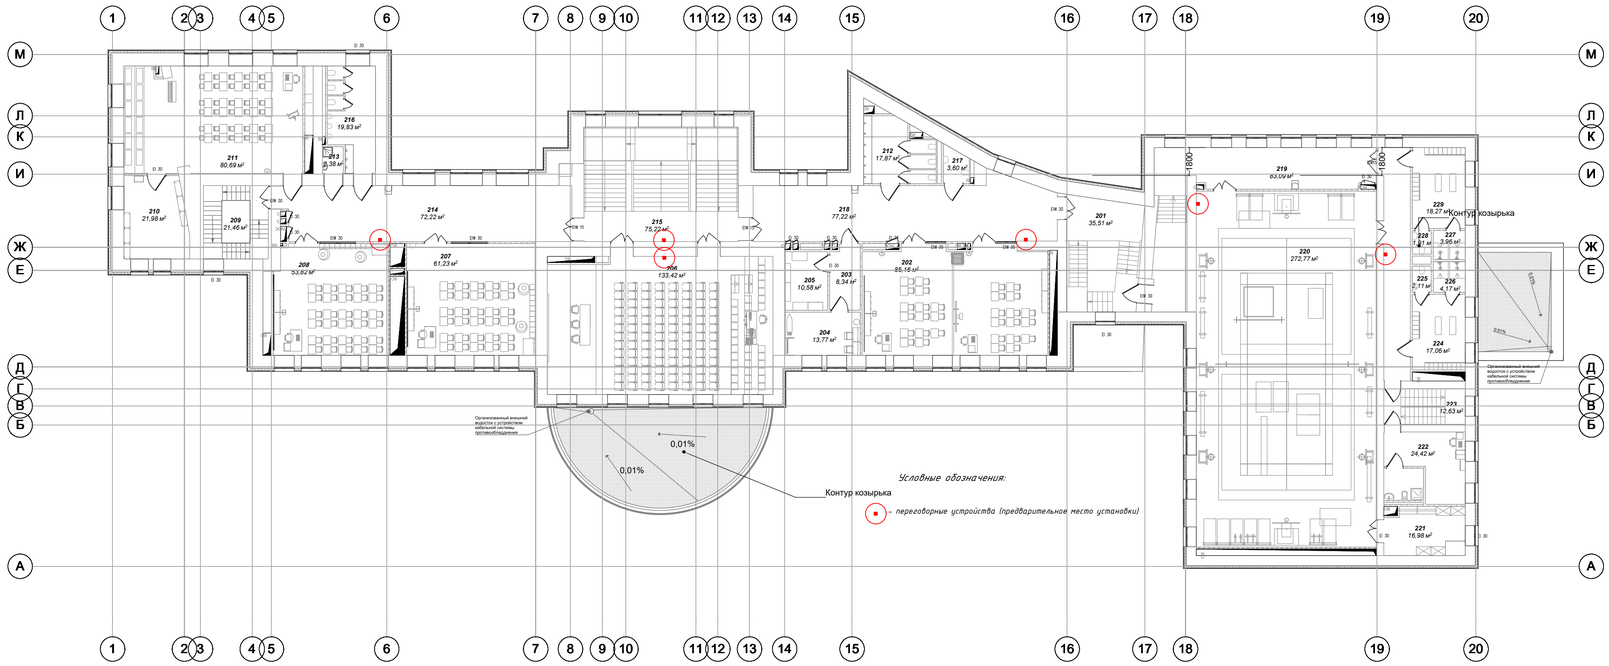

Экспликация помещений 2-го этажа			
№	Наименование	Площадь	Кат.пом
201	Лестничная клетка(Тип Н2)	35,51	
202	Кабинет иностранного языка с возможностью деления трансформируемой перегорододкой на два помещения(начальная школа)	85,16	
203	Коридор	8,34	
204	Артистическая	13,77	
205	Кладовая инвентаря	10,58	В3
206	Актовый зал с эстрадой в уровне пола	133,42	
207	Учебные кабинеты(1-ый класс)	61,23	
208	Учебные кабинеты(1-ый класс)	53,82	
209	Лестничная клетка(Тип Н2)	21,46	
210	Кладовая инвентаря творческой мастерской	21,98	В3
211	Творческая мастерская	80,69	
212	Санузел для девочек	17,87	
213	ПУИ	2,38	В4
214	Коридор	72,22	
215	Лестничная клетка(Тип Л1)	75,22	
216	Санузел для мальчиков	19,83	
217	Санузел для персонала	3,60	
218	Коридор	77,22	
219	Коридор	83,09	
220	Спортивный зал	272,77	
221	Снарядная	16,98	В3
222	Комната инструктора (с душем и санузлом)	24,42	
223	Лестничная клетка(Тип Л1)	12,63	
224	Раздевальная	17,06	
225	Санузел	2,11	
226	Душевая	4,17	
227	Душевая	3,96	
228	Санузел	1,91	
229	Раздевальная	18,27	
		1 251,67 м²	

Площадь здания мменее 1300 кв метра разделение на пожарные зоны не требуются

ПРИМЕЧАНИЯ:

1. Возможность устройства проемов в несущих стенах будет уточняться в проекте;

2. Размер и расположение вентиляционных шахт будет уточнен в проекте;

3. Шахты,предназначенные для прокладки инженерных коммуникаций и стояков (ВК СС ЭОМ) оборудуются лючками для обслуживания;

4. Доступ маломобильных групп населения М1-М4 предусмотреть только на 1 этаж в помещения: коридор с зоной ожидания, санузел для МГН,помещение охраны,административные кабинеты.

5. Конструкция входных групп,в т.ч. количество ступеней и конфигурация пандуса уточняется разделом "Фасады"

*категорирование по взрывопожарной и пожарной опасности данных помещений выполнить на этапе проектирования

Условные обозначения:

- Помещения общего пользования
- Сантехнические помещения
- Универсальные студии
- Спортивные помещения
- Учебные кабинеты начальной школы
- Группа зрительного зала

Разработано:

Первый заместитель директора-
главный инженер
ГАУ "МосжилНИИпроект"

Img_8BCFBE4D_8BCFBE4D.bmp

К.Н. Сухов

*Площади помещений, открывание и габариты дверей уточняются проектом

Согласовано

Взамен инв. №

Подпись и дата

Инв. № подл.


Копировал

Формат А1

Здание Государственного бюджетного общеобразовательного учреждения города Москвы "Школа № 1574", расположенное по адресу: г. Москва, пер.Старопименовский, д. 5

План 3 этажа

Масштаб 1:200

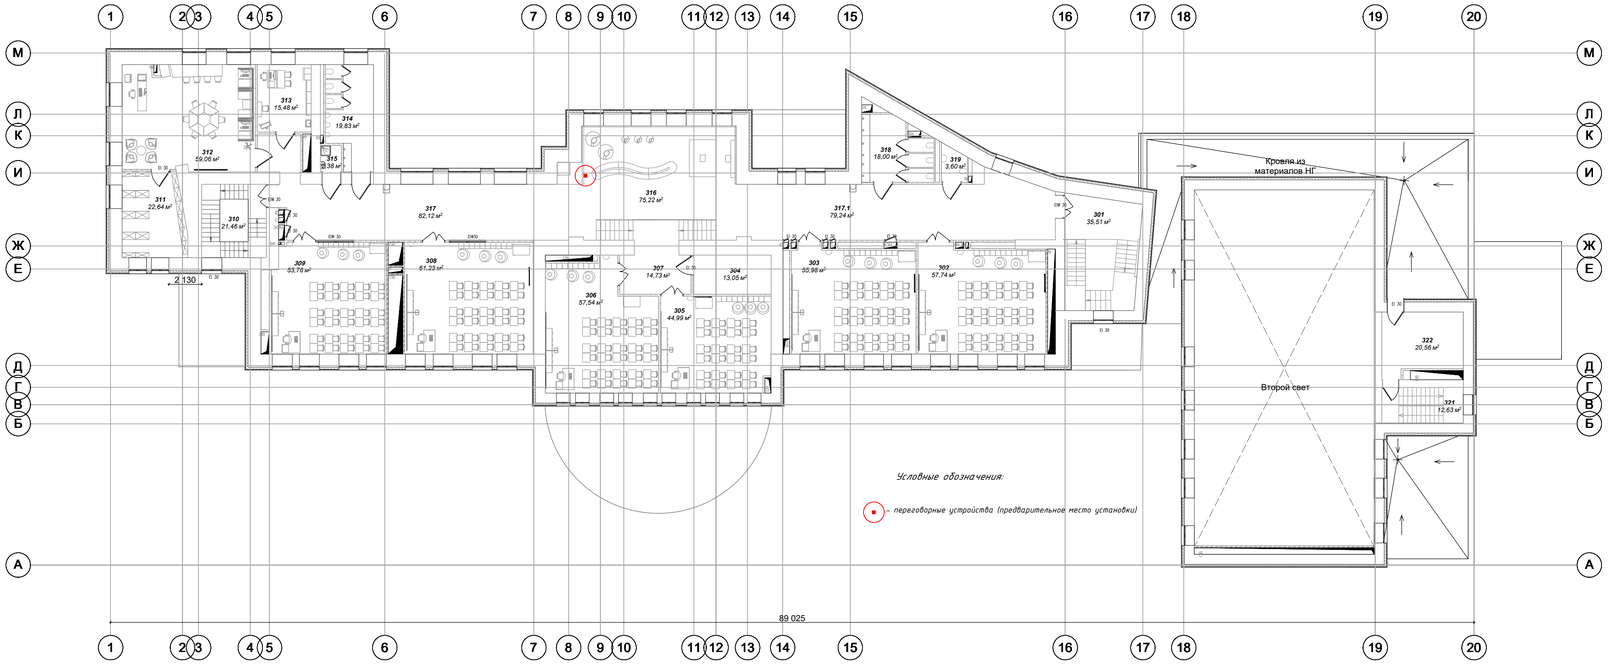

Экспликация помещений 3-го этажа

№	Наименование	Площадь	Кат.пом
301	Лестничная клетка(Тип Н2)	35,51	
302	Учебные кабинеты (2-4 классы)	57,74	
303	Учебные кабинеты (2-4 классы)	55,98	
304	Серверная	13,05	В4
305	Учебные кабинеты (2-4 классы)	44,99	
306	Учебные кабинеты (2-4 классы)	57,54	
307	Коридор	14,73	
308	Учебные кабинеты(2-4-ые классы)	61,23	
309	Учебные кабинеты(2-4 -ый класс)	53,76	
310	Лестничная клетка(Тип Н2)	21,46	
311	Информационный библиотечный центр(хранение и выдача книг)	22,64	В3
312	Информационный библиотечный центр с зоной для индивидуальных занятий	59,06	
313	Кабинет для индивидуальных занятий,в тч с учителем-логопедом	15,48	
314	Санузел для мальчиков	19,83	
315	ПУИ	2,38	В4
316	Зона ожидания	75,22	
317	Коридор	82,12	
317.1	Коридор	79,24	
318	Санузел для девочек	18,00	
319	Санузел для персонала	3,60	
321	Лестничная клетка(Тип Л1)	12,63	
322	Спортивный зал	20,56	
		826,75 м²	

Площадь здания мменее 1300 кв метра разделение на пожарные зоны не требуются

ПРИМЕЧАНИЯ:

1. Возможность устройства проемов в несущих стенах будет уточняться в проекте;

2. Размер и расположение вентиляционных шахт будет уточнен в проекте;

3. Шахты,предназначенные для прокладки инженерных коммуникаций и стояков (ВК СС ЭОМ) оборудуются лючками для обслуживания;

4. Доступ маломобильных групп населения М1-М4 предусмотреть только на 1 этаж в помещения: коридор с зоной ожидания, санузел для МГН,помещение охраны,административные кабинеты.

5. Конструкция входных групп,в т.ч. количество ступеней и конфигурация пандуса уточняется разделом "Фасады"

*категорирование по взрывопожарной и пожарной опасности данных помещений выполнить на этапе проектирования

Условные обозначения:

- Помещения общего пользования
- Сантехнические помещения
- Рекреационно-коммуникационное пространство
- Административные и служебно-бытовые помещения
- Учебные кабинеты начальной школы
- Технические помещения

Разработано:

Первый заместитель директора-главный инженер
ГАУ "МосжилНИИпроект"

Img_8BCFBE4D_8BCFBE4D.bmp

К.Н. Сухов

*Площади помещений, открывание и габариты дверей уточняются проектом

Согласовано

Взамен инв. N°

Подпись и дата

Инв. N° подл.

Копировал


Формат А1

Здание Государственного бюджетного общеобразовательного учреждения города Москвы "Школа № 1574", расположенное по адресу: г. Москва, пер.Старопименовский, д. 5

План 4 этажа

Масштаб 1:200

Начальна школа (1-4 классы)- 8 классов (160 чел.),
Основная школа (5-9 классы) - 10 классов (200 чел.),
Старшая школа (10-11 классы) - 2 классов (40 чел.)
Наполняемость - 400 учащихся, (количество классов: 20)

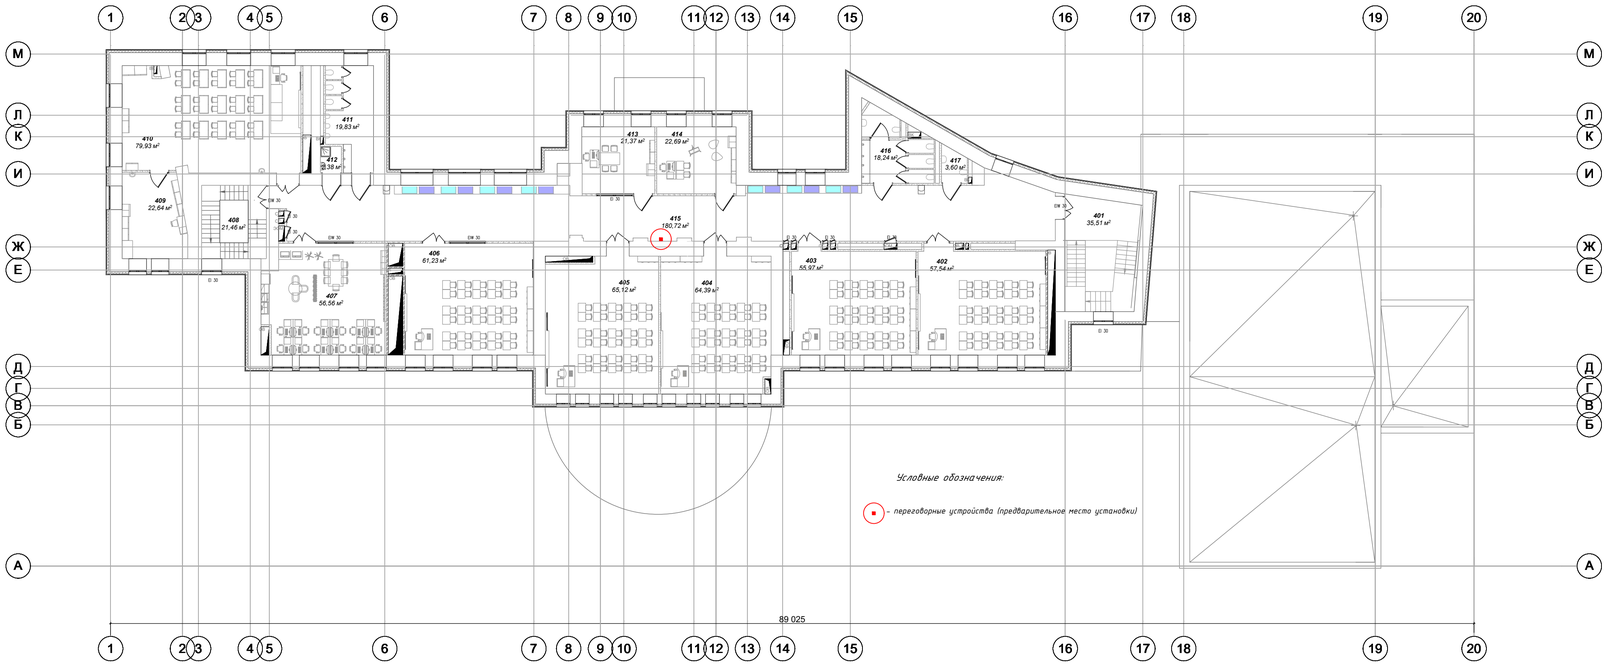

Экспликация помещений 4-го этажа			
№	Наименование	Площадь	Кат.пом
401	Лестничная клетка(Тип Н2)	35,51	
402	Кабинет русского языка и литературы	57,54	
403	Кабинет русского языка и литературы	55,97	
404	Кабинет истории Тип 1	64,39	
405	Кабинет математики	65,12	
406	Кабинет математики	61,23	
407	Кабинет с рабочим пространством для учителей тип 1	56,56	
408	Лестничная клетка(Тип Н2)	21,46	
409	Лаборантская кабинета физики	22,64	
410	Учебные кабинеты для изучения естествознания: физика	79,93	
411	Санузел для мальчиков	19,83	
412	ПУИ	2,38	В4
413	Административный кабинет тип1 (основная и старшая школы)	21,37	
414	Кабинет для индивидуальных занятий в тч педагогом-психологом	22,69	
415	Коридор	180,72	
416	Санузел для девочек с комнатой личной гигиены	18,24	
417	Санузел для персонала	3,60	
		789,18 м²	

Площадь здания мменее 1300 кв метра разделение на пожарные зоны не требуются

ПРИМЕЧАНИЯ:

1. Возможность устройства проемов в несущих стенах будет уточняться в проекте;

2. Размер и расположение вентиляционных шахт будет уточнен в проекте;

3. Шахты,предназначенные для прокладки инженерных коммуникаций и стояков (ВК СС ЭОМ) оборудуются лючками для обслуживания;

4. Доступ маломобильных групп населения М1-М4 предусмотреть только на 1 этаж в помещения: коридор с зоной ожидания, санузел для МГН,помещение охраны,административные кабинеты.

5. Конструкция входных групп,в т.ч. количество ступеней и конфигурация пандуса уточняется разделом "Фасады"

*категорирование по взрывопожарной и пожарной опасности данных помещений выполнить на этапе проектирования

Условные обозначения:

- Помещения общего пользования
- Сантехнические помещения
- Административные помещения
- Учебные кабинеты основной и старшей школы

Разработано:

Первый заместитель директора-
главный инженер
ГАУ "МосжилНИИпроект"

Img_8BCFBE4D_8BCFBE4D.bmp

К.Н. Сухов

*Площади помещений, открывание и габариты дверей уточняются проектом

Согласовано

Взамен инв. N°

Подпись и дата

Инв. N° подл.


Копировал

Формат А1

Здание Государственного бюджетного общеобразовательного учреждения города Москвы "Школа № 1574", расположенное по адресу: г. Москва, пер.Старопименовский, д. 5

План 5 этажа

Масштаб 1:200

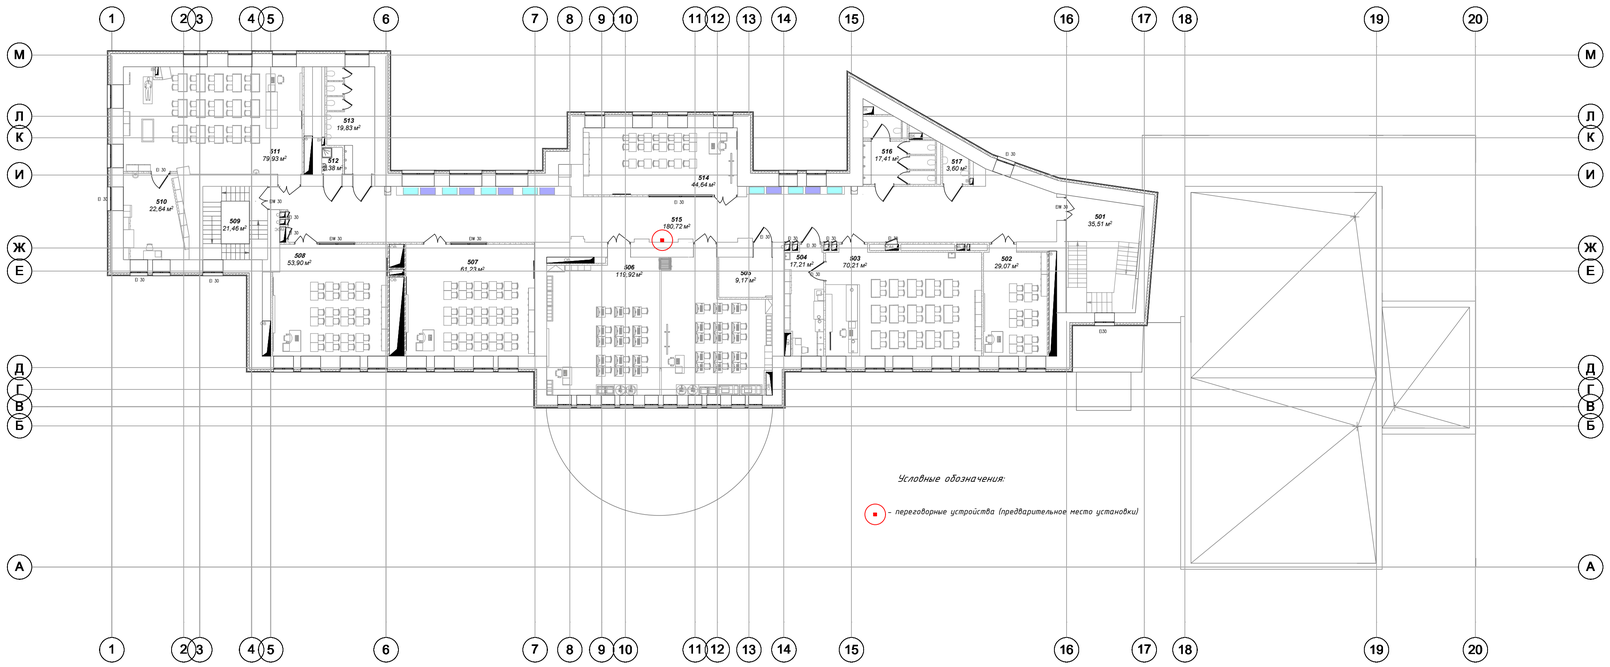

Экспликация помещений 5-го этажа			
№	Наименование	Площадь	Кат.пом
501	Лестничная клетка(Тип Н2)	35,51	
502	Кабинет иностранного языка для подгруппы(основная и старшая)	29,07	
503	Учебные кабинеты для изучения естествознания: химия	70,21	
504	Лаборантская кабинета химии	17,21	В4
505	Северная	9,17	В4
506	Кабинет информационных технологий с возможностью	119,92	
507	Кабинет географии	61,23	
508	Кабинет русского языка и литературы	53,90	
509	Лестничная клетка(Тип Н2)	21,46	
510	Лаборантская кабинета биологии	22,64	В4
511	Учебные кабинеты для изучения естествознания: биология+ОБЗР	79,93	
512	ПУИ	2,38	В4
513	Санузел для мальчиков	19,83	
514	Кабинет иностранного языка для подгруппы (основная и старшая школа)	44,64	
515	Коридор	180,72	
516	Санузел для девочек с комнатой личной гигиены	17,41	
517	Санузел для персонала	3,60	
		788,83 м²	

Площадь здания мменее 1300 кв метра разделение на пожарные зоны не требуются

ПРИМЕЧАНИЯ:

1. Возможность устройства проемов в несущих стенах будет уточняться в проекте;

2. Размер и расположение вентиляционных шахт будет уточнен в проекте;

3. Шахты,предназначенные для прокладки инженерных коммуникаций и стояков (ВК СС ЭОМ) оборудуются лючками для обслуживания;

4. Доступ маломобильных групп населения М1-М4 предусмотреть только на 1 этаж в помещения: коридор с зоной ожидания, санузел для МГН,помещение охраны,административные кабинеты.

5. Конструкция входных групп,в т.ч. количество ступеней и конфигурация пандуса уточняется разделом "Фасады"

*категорирование по взрывопожарной и пожарной опасности данных помещений выполнить на этапе проектирования

Условные обозначения:

- Помещения общего пользования
- Сантехнические помещения
- Учебные кабинеты основной и старшей школы
- Технические помещения

Разработано:

Первый заместитель директора-
главный инженер
ГАУ "МосжилНИИпроект"

Img_8BCFBE4D_8BCFBE4D.bmp

К.Н. Сухов

*Площади помещений, открывание и габариты дверей уточняются проектом

Согласовано

Взамен инв. №

Подпись и дата

Инв. № подл.

Копировал

Формат А1