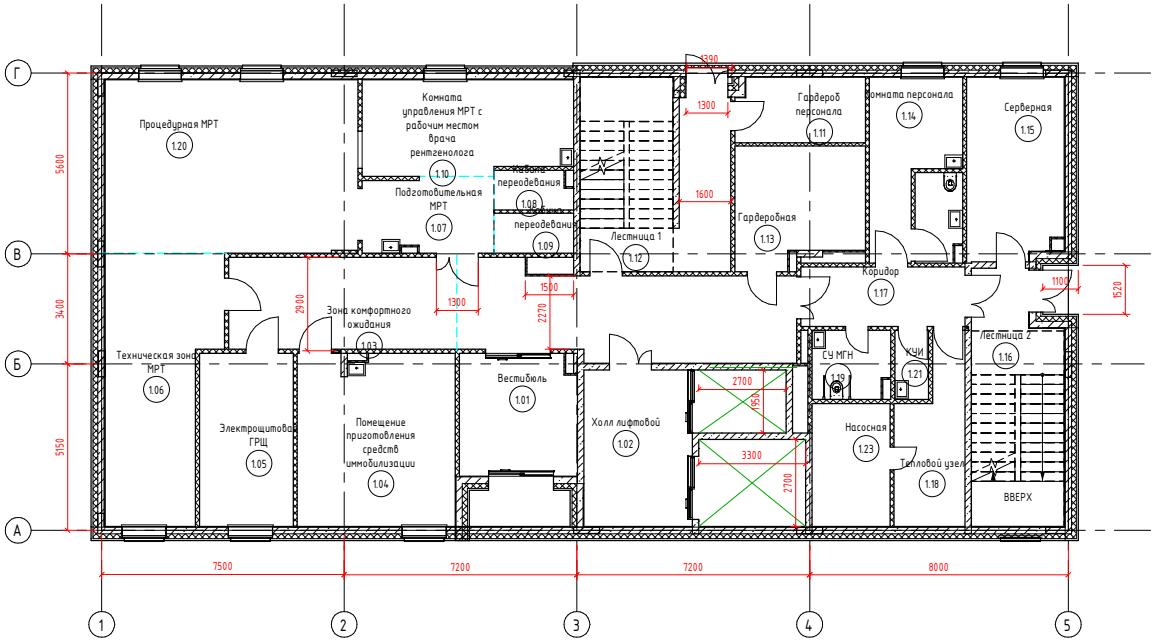


Экспликация помещений

Номер помещения	Наименование	Площадь, м²	Кат. помещения	Примечание
1.01	Вестибюль	13,6		
1.02	Холл лифтовой	16,3		9
1.03	Зона комфортного ожидания	20,1		18
1.04	Помещение приготовления средств иммобилизации	25,9		20
1.05	Электрощитовая ГРЩ	15,6	В3	12
1.06	Техническая зона МРТ	26,4		
1.07	Подготовительная МРТ	9,3		
1.08	Кабина переодевания	2,8		3
1.09	Кабина переодевания	3,1		3
1.10	Комната управления МРТ с рабочим местом врача рентгенолога	18,8		20
1.11	Гардероб персонала	8,0		
1.12	Лестница 1	26,2		
1.13	Гардеробная	14,1		15
1.14	Комната персонала	11,9		9
1.15	Серверная	16,7	В3	12
1.16	Лестница 2	21,0		
1.17	Коридор	9,3		
1.18	Тепловой узел	10,6	Д	12
1.19	СУ МГН	5,0		5
1.20	Процедурная МРТ	42,0		35
1.21	КУИ	2,2	В4	
1.23	Насосная	9,2	Д	

Согласовано

Согласовано

Взам. инв. №

Подп. и дата

Инв. № подл.

Изм.	Кол.уч.	Лист	№док.	Подп.	Дата

1525 –

Адрес проекта


Стадия	Лист	Листов
П	013	

Эскизный план 1го этажа

Название / логотип

Формат А2А

- 0_АР_Ф_Южный

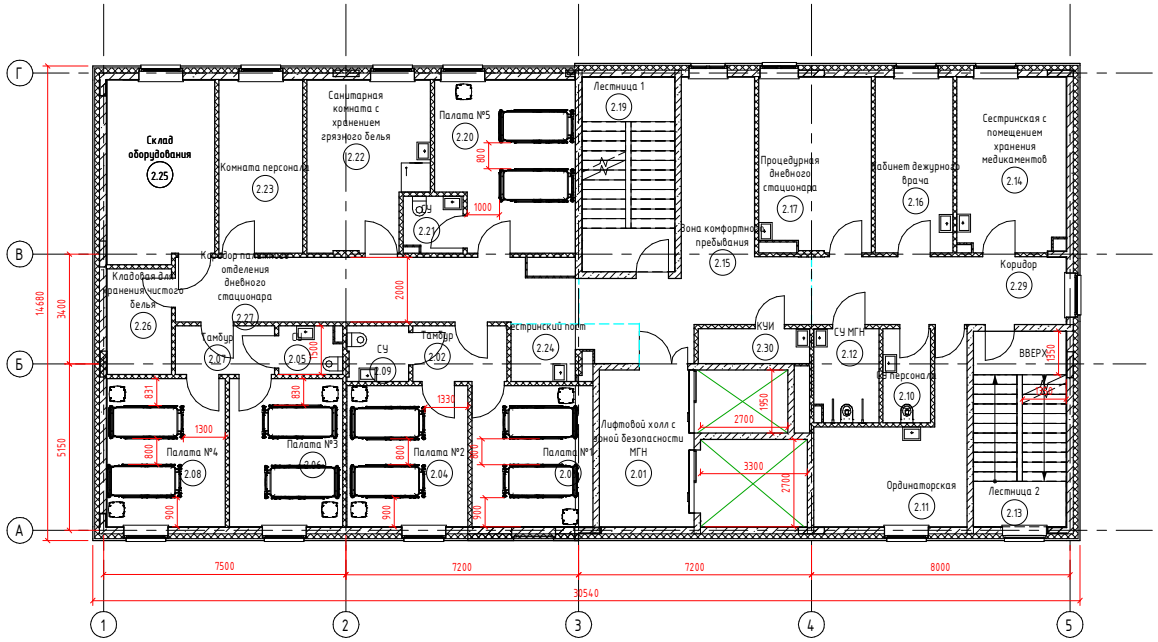

Экспликация помещений

Номер помещения	Наименование	Площадь, м²	Кат. помещения	Примечание
2.01	Лифтовой холл с зоной безопасности МГН	14,2		
2.02	Тамбур	5,0		
2.03	Палата №1	16,3		16
2.04	Палата №2	16,4		16
2.05	СУ	2,8		
2.06	Палата №3	16,1		16
2.07	Тамбур	4,6		
2.08	Палата №4	16,8		16
2.09	СУ	3,3		
2.10	СУ персонала	4,3		4
2.11	Ординаторская	17,7		18
2.12	СУ МГН	5,7		5
2.13	Лестница 2	17,4		
2.14	Сестринская с помещением хранения медикаментов	18,0		18
2.15	Зона комфортного пребывания	27,6		18
2.16	Кабинет дежурного врача	13,0		10
2.17	Процедурная дневного стационара	18,4		18
2.19	Лестница 1	17,3		
2.20	Палата №5	21,5		16
2.21	СУ	3,1		
2.22	Санитарная комната с хранением грязного белья	18,7		12+6
2.23	Комната персонала	13,9		9
2.24	Сестринский пост	5,7		
2.25	Склад оборудования	18,6	В3	18
2.26	Кладовая для хранения чистого белья	6,5	В4	6
2.27	Коридор палатного отделения дневного стационара	24,0		
2.29	Коридор	16,5		
2.30	КУИ	3,7	В4	

Согласовано

Согласовано

Взам. инв. №

Подп. и дата

Инв. № подл.

Изм.	Кол.уч.	Лист	№док.	Подп.	Дата

1525 –

Адрес проекта


Стадия	Лист	Листов
П	005	

Эскизный план 2го этажа

Название / логотип

Формат А2А

– В_АР_Ф_Южный

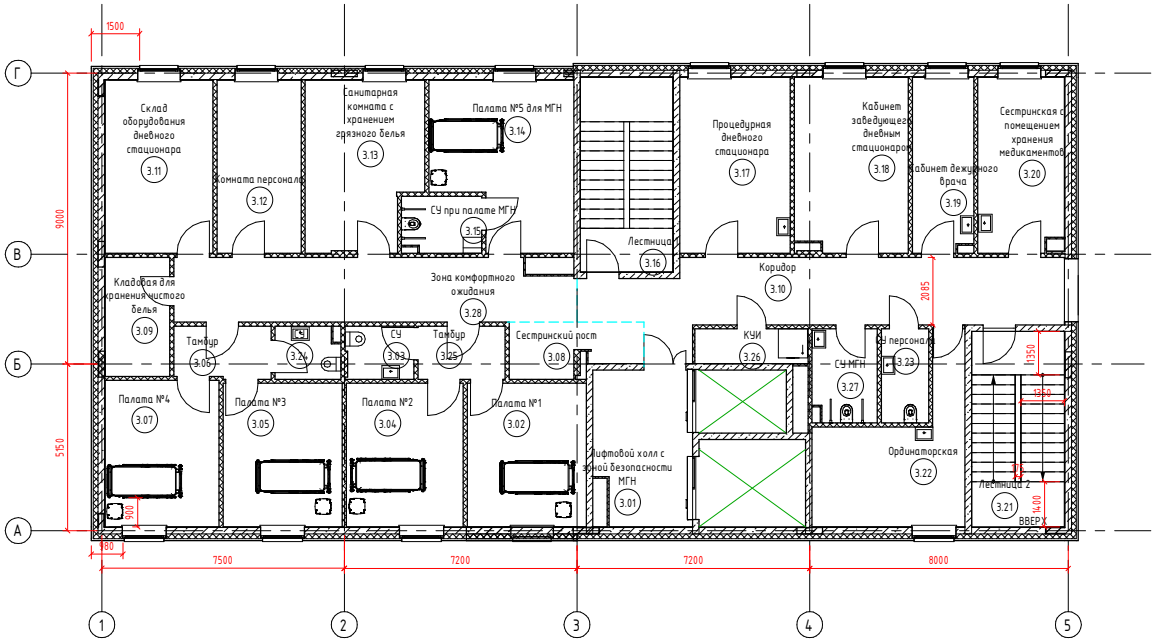

Экспликация помещений

Номер помещения	Наименование	Площадь, м²	Кат. помещения	Комментарии
3.01	Лифтовой холл с зоной безопасности МГН	14,2		
3.02	Палата №1	16,4		16
3.03	СУ	3,5		
3.04	Палата №2	16,1		16
3.05	Палата №3	16,4		16
3.06	Тамбур	4,8		
3.07	Палата №4	16,0		16
3.08	Сестринский пост	6,1		6
3.09	Кладовая для хранения чистого белья	7,4	В4	6
3.10	Коридор	31,0		18
3.11	Склад оборудования дневного стационара	17,9	В3	18
3.12	Комната персонала	13,9		9
3.13	Санитарная комната с хранением грязного белья	18,2	В3	12
3.14	Палата №5 для МГН	20,7		16
3.15	СУ при палате МГН	4,3		
3.16	Лестница 1	17,3		
3.17	Процедурная дневного стационара	18,6		18
3.18	Кабинет заведующего дневным стационаром	18,9		18
3.19	Кабинет дежурного врача	10,2		10
3.20	Сестринская с помещением хранения медикаментов	14,3		14
3.21	Лестница 2	17,4		
3.22	Ординаторская	17,7		18
3.23	СУ персонала	4,3		4
3.24	СУ	3,2		
3.25	Тамбур	4,4		
3.26	КУИ	3,8	В4	
3.27	СУ МГН	5,7		
3.28	Зона комфортного ожидания	24,0		

Согласовано

Согласовано

Взам. инв. №

Подп. и дата

Инв. № подл.

Изм.	Кол.уч.	Лист	№док.	Подп.	Дата

1525 –

Адрес проекта

Стадия	Лист	Листов
П	009	

Эскизный план 3го этажа

Название / логотип


Формат А2А

– В_АР_Ф_Южный

–

Экспликация помещений

Номер помещения	Наименование	Площадь, м²	Кат. помещения	Комментарии
4.01	Лестница 2	111,2		
4.02	Лестница Л1	16,7		

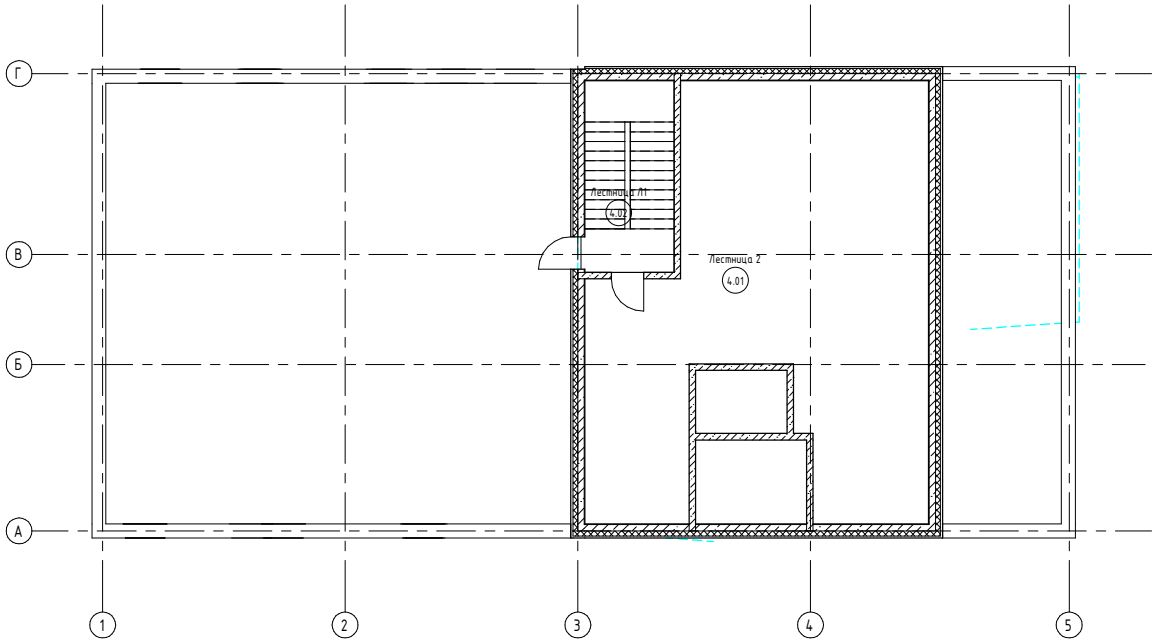

Согласовано

Согласовано

Взам. инв. №

Подп. и дата

Инв. № подл.

Изм.	Кол.уч.	Лист	№док.	Подп.	Дата

1525 –

Эскизный план технического этажа

Стадия	Лист	Листов
П	016	

Название / логотип

Формат А2А

– В_АР_Ф_Южный