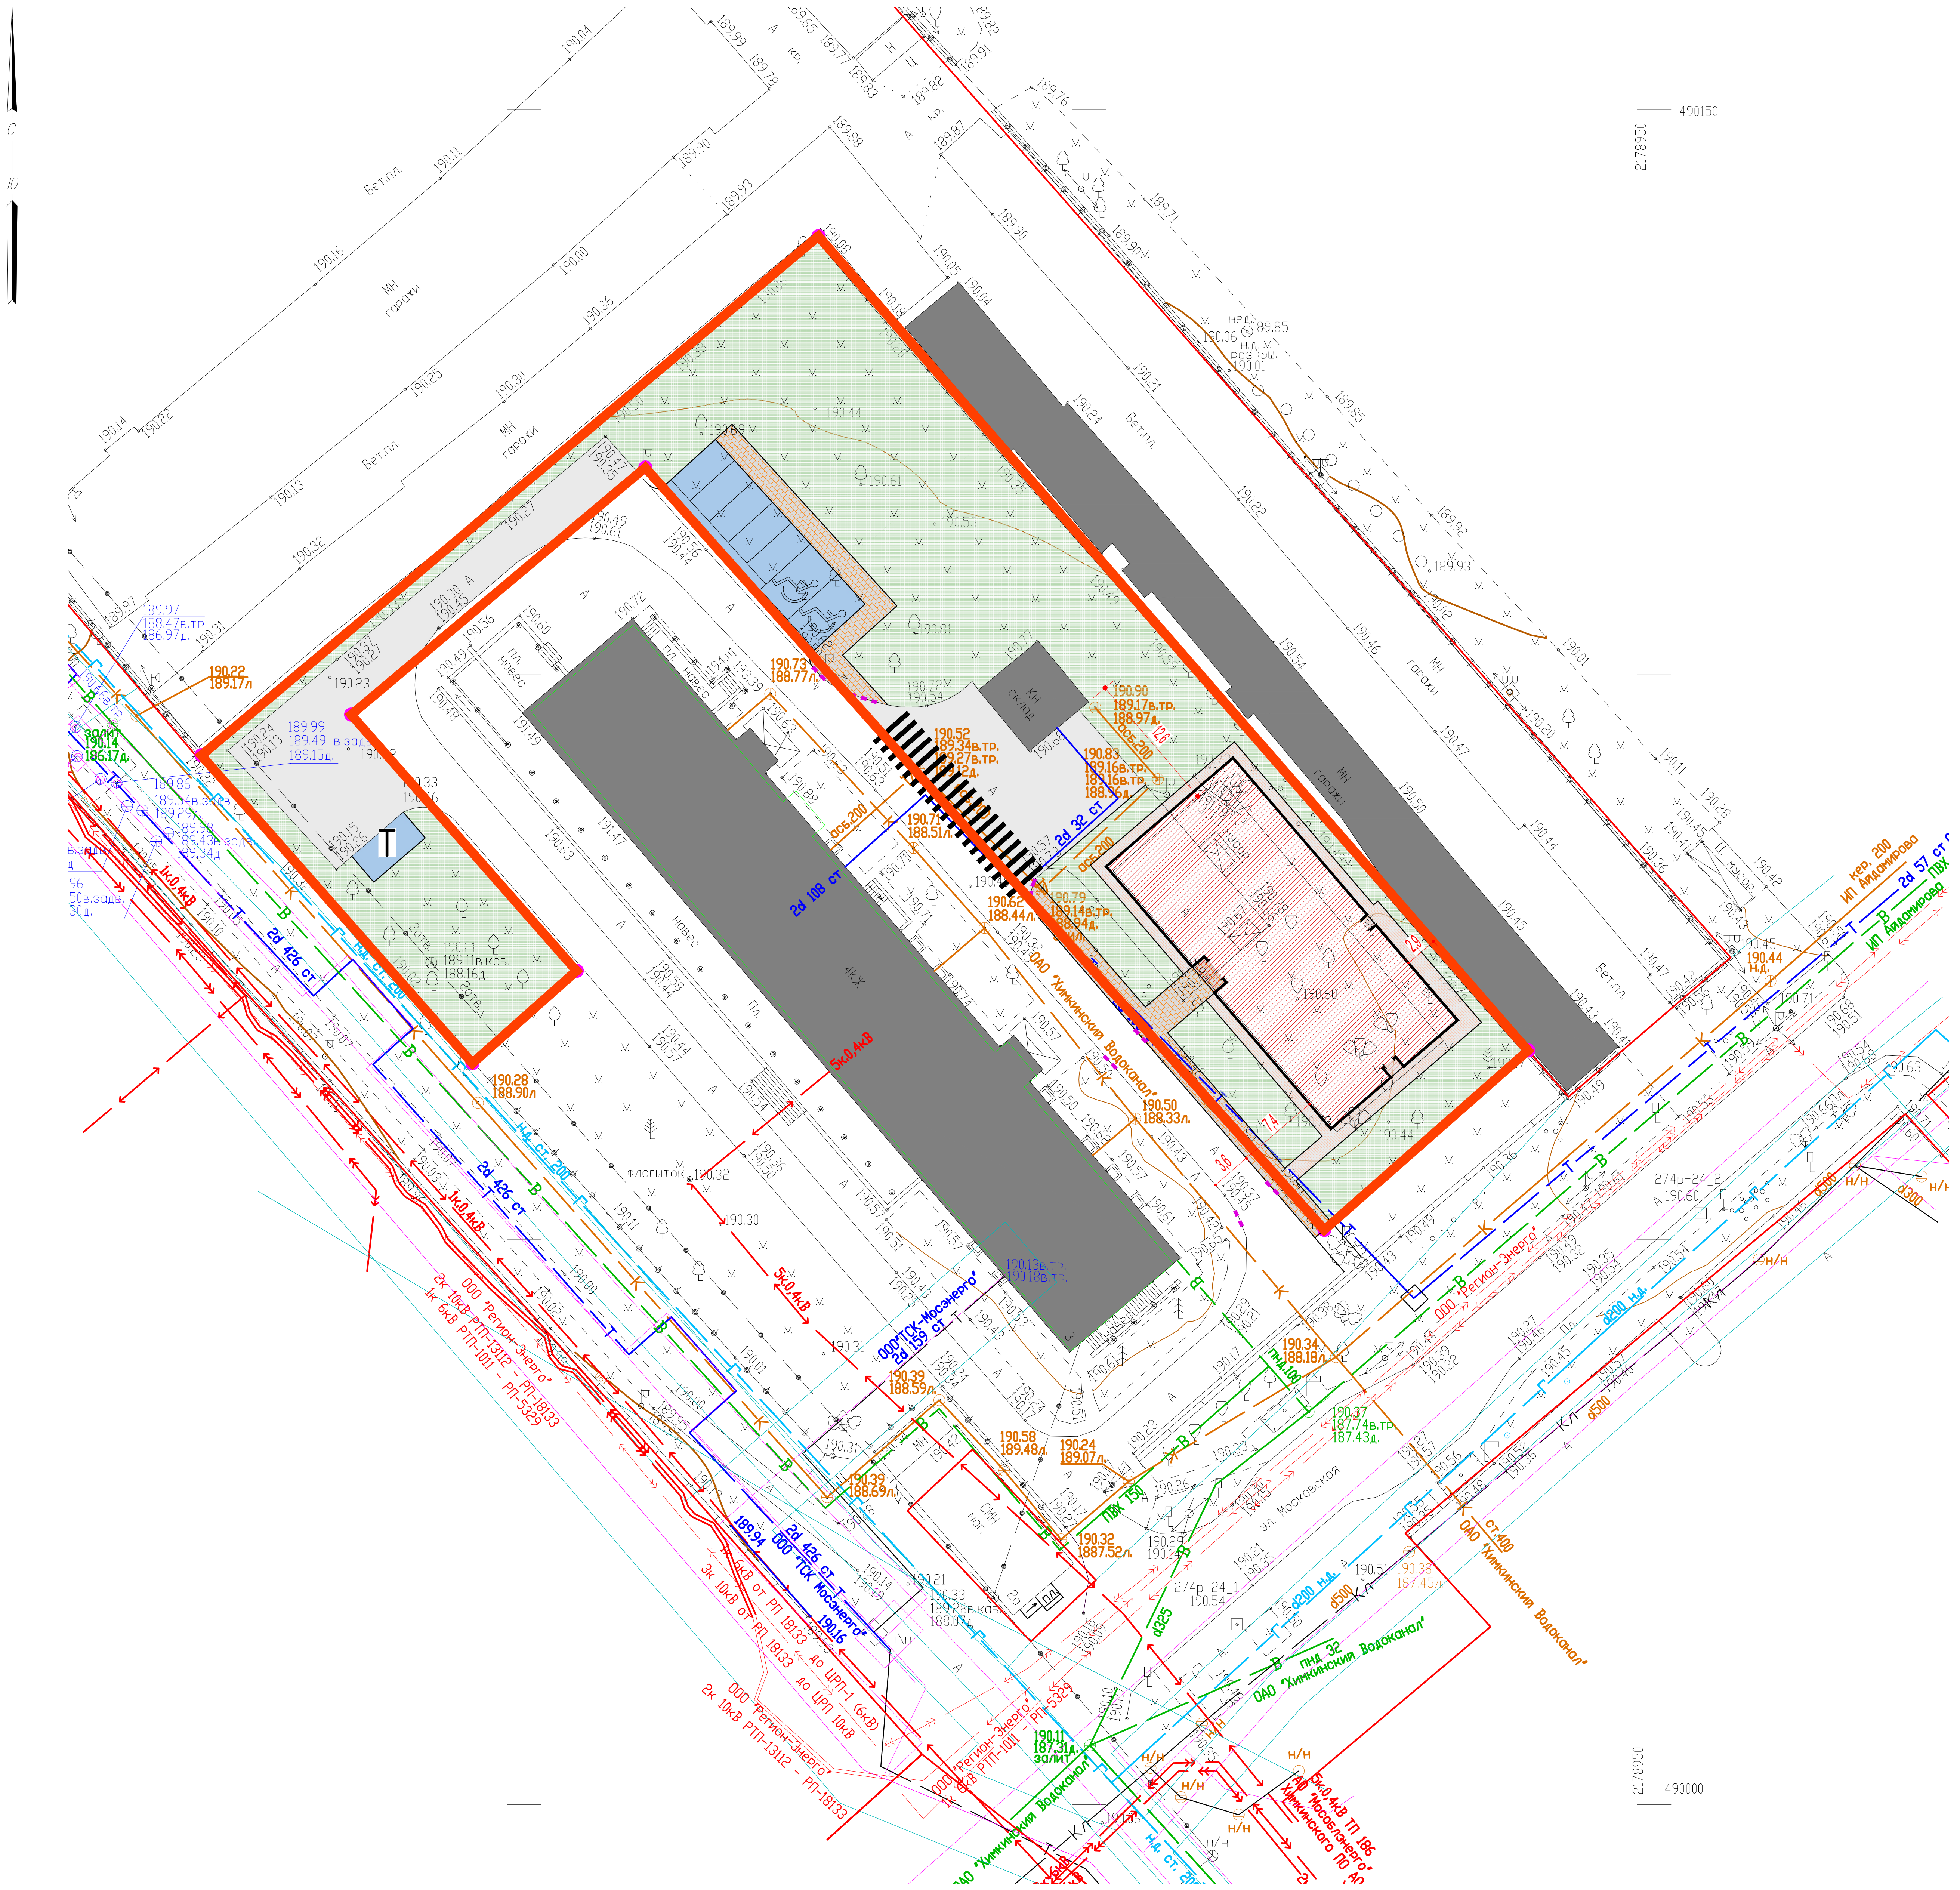

Условные обозначения

🟥	Границы земельных участков
🟩	Границы смежных земельных участков
🟧	Территория дополнительного благоустройства (
▬	Красные линии (показано в информационных целях)
▨	Проектируемые здания и сооружения с нависающими частями здания
⬛	Существующая застройка
🟥	Парковочные места 2.5 х 5.3 м приобъектного хранения (2.5 х 6.8 м при продольном расположении)
🟪	Парковочные места 2.5 х 5.3 м временного хранения (2.5 х 6.8 м при продольном расположении)
P5	Парковочные места 2.5 х 5.3 м постоянного хранения
♿	Парковочные места 3.6 х 6.0 м для МГН категории М4 (3.6 х 6.8 м при продольном расположении)
♿	Парковочные места 2.5 х 5.3 м для МГН
⚡	Парковочные места для электромобилей 3.0 х 6.0м
▮▮▮▮▮	Пешеходный переход
- - -	Понижение борта
⬜	Существующие проезды (асфальтобетон) (твёрдое покрытие)
🟦	Проектируемые проезды (асфальтобетон) (твёрдое покрытие)
▭	Проектируемые тротуары (бетонная плитка) (твёрдое покрытие)
▒	Проектируемые тротуары (бетонная плитка) (твёрдое покрытие)
Т	Контейнерные площадки ТКО, КГО ,СО
🟩	Проектируемый натуральный газон

Согласовано

Взамен инв. N

Подпись и дата

Инв. N подп.

						-ПЗУ
						г. Химки, мкр. Подрезково, ул. Школьная, д.3
Изм.	Кол.уч	Лист	№док.	Подп.	Дата	
Разработал		Иванов				Отдельно стоящее здание с размещением в нем тяжелого диагностического оборудования - магнитно-резонансного томографа
Проверил						
Н. контр.						Схема планировочной организации земельного участка М 1:500
ГИП						

Стадия	Лист	Листов
П	2	

Копировал

A2