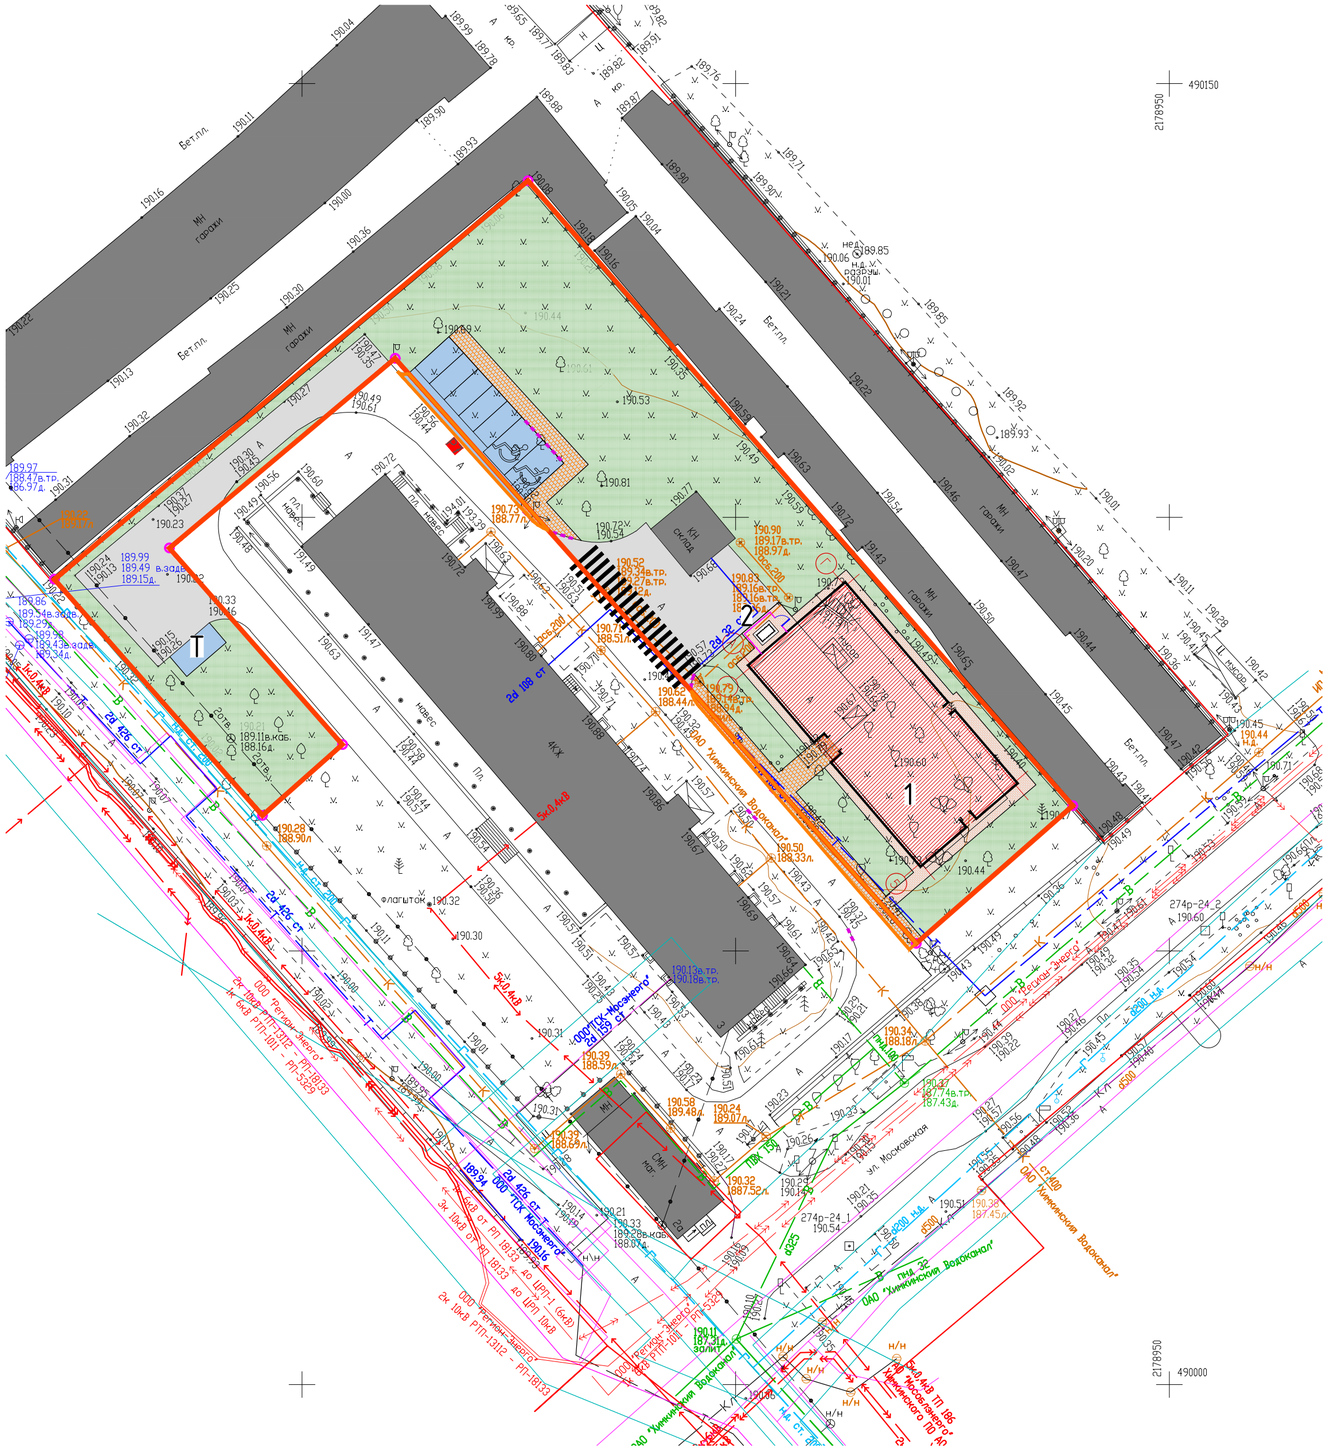


Экспликация зданий и сооружений

№	Наименование	Примечание
1	Проектируемое здание	
2	Площадка чиллеров	
3	Существующее здание	

Экспликация площадок различного назначения

№	Наименование		Площадь, кв.м	Примечание
Т	Контейнерные площадки**		18,0	
	Т1	Площадка ТКО	18,0	Твёрдое (асфальтобетон)

ВЕДОМОСТЬ ЭЛЕМЕНТОВ ОЗЕЛЕНЕНИЯ

Поз.	Обозначение	Наименование породы или вида насаждения	Возраст, лет	Кол.	Примечание
		Газоны			
9		Газон	-	864,90 кв.м.	Норма посева - 35 г/м^2

Технико-экономические показатели

№	Наименование	Ед. изм.	В границах ЗУ	В границах дополнительного благоустройства
1	Площадь участка в границах проектирования	кв.м	2994,00	
2	Площадь благоустройства вне границ ЗУ			47,00
3	Площадь застройки, в т.ч.:	кв.м	478,7	
	проектируемой		451,0	
	существующей		27,70	
4	Площадь твёрдых покрытий, в т.ч.:	кв.м	928,3	
	- асфальтобетонных проездов (проектируемых)		144,00	14,60
	- асфальтобетонных проездов (существующих)		496,90	
	- тротуары из бетонной плитки		287,4	32,40
6	Площадь озеленения, в т.ч.	кв.м	1587,00	
	- площадь газонов		1587,00	
16	Количество посещений	чел.	50	
17	Количество работников	чел.	16	
20	Количество машиномест приобъектных	шт.	7	

Условные обозначения

- Границы земельных участков
- Границы смежных земельных участков
- Красные линии (показано в информационных целях)
- Проектируемые здания и сооружения с нависающими частями здания
- Существующая застройка
- Парковочные места 2.5 х 5.3 м приобъектного хранения (2.5 х 6.8 м при продольном расположении)
- Парковочные места 3.6 х 6.0 м для МГН категории М4 (3.6 х 6.8 м при продольном расположении)
- Пешеходный переход
- Понижение борта
- Существующие проезды (асфальтобетон) (твёрдое покрытие)
- Проектируемые проезды (асфальтобетон) (твёрдое покрытие)
- Проектируемые тротуары (бетонная плитка) (твёрдое покрытие)
- Проектируемые тротуары (бетонная плитка) (твёрдое покрытие)
- Т — Контейнерные площадки ТКО, КГО ,СО
- Существующее озеленение
- Проектируемое ограждение площадки чиллеров с калиткой

Схема планировочной организации земельного участка (1:500)

Согласовано

Взамен инв. N

Подпись и дата

Инв. N подл.