Содержание альбома

Лист	Наименование	Примечание
	Обложка	
01	Титульный лист	
02	Содержание альбома	
03	Аксонометрия	
04	Визуализация	
05	Фасад в осях 1-5. М1:100	
06	Фасады в осях А-Г и Г-А. М1:100	
07	Фасад в осях 5-1. М1:100	
08	Фрагмент фасада	
09	План 1 этажа. М1:100	
10	План 2 этажа. М1:100	
11	План 3 этажа. М1:100	
12	План технического этажа. М1:100	
13	Разрезы 1-1 и 2-2. М1:100	
14	Пояснительная записка	
15	Архитектурно - художественные решения	
16	Технико-экономические показатели	

						#Пр№-АР		
						#Полный Адрес Участка		
Изм.	Кол.уч.	Лист	№Док.	Подп.	Дата			
						#Наименование Проекта	Стадия	Лист	Листов
							#Стадия Проекта	02	
						Содержание альбома	#Название Организации		

Аксонометрия



						#Пр№-АР	
						#Полный Адрес Участка	
Изм.	Кол.уч.	Лист	№Док.	Подп.	Дата		
						#Наименование Проекта	Стадия: #Стадия Проекта; Лист: 03; Листов:
						Аксонометрия	#Название Организации

Визуализация



						#Пр№-АР	
						#Полный Адрес Участка	
Изм.	Кол.уч.	Лист	№Док.	Подп.	Дата		
						#Наименование Проекта	Стадия: #Стадия Проекта; Лист: 04; Листов:
						Визуализация	#Название Организации


Фасад в осях 1-5. М1:100




№ поз.	Наименование элемента фасада	Наименование материала отделки	Эталон цвета (образец колера)	Наименование и номер эталона цвета
1.	Наружные стены	Композитные панели		RAL9002
2.				RAL7044
3.				RAL7016
4.		Металлосайдинг текстура дерево		Кедр/ Дуб
5.	Откосы	Композитные панели		RAL7016
6.	Окна			RAL7016
7.	Двери			RAL7016
8.	Вывеска			
9.	Адресные таблички			

						#ПрN-АР	
						#Полный Адрес Участка	
Изм.	Кол.уч.	Лист	№Док.	Подп.	Дата		
						#Наименование Проекта	Стадия: #Стадия Проекта; Лист: 05; Листов:
						Фасад в осях 1-5. М1:100	#Название Организации

Фасады в осях А-Г и Г-А. М1:100

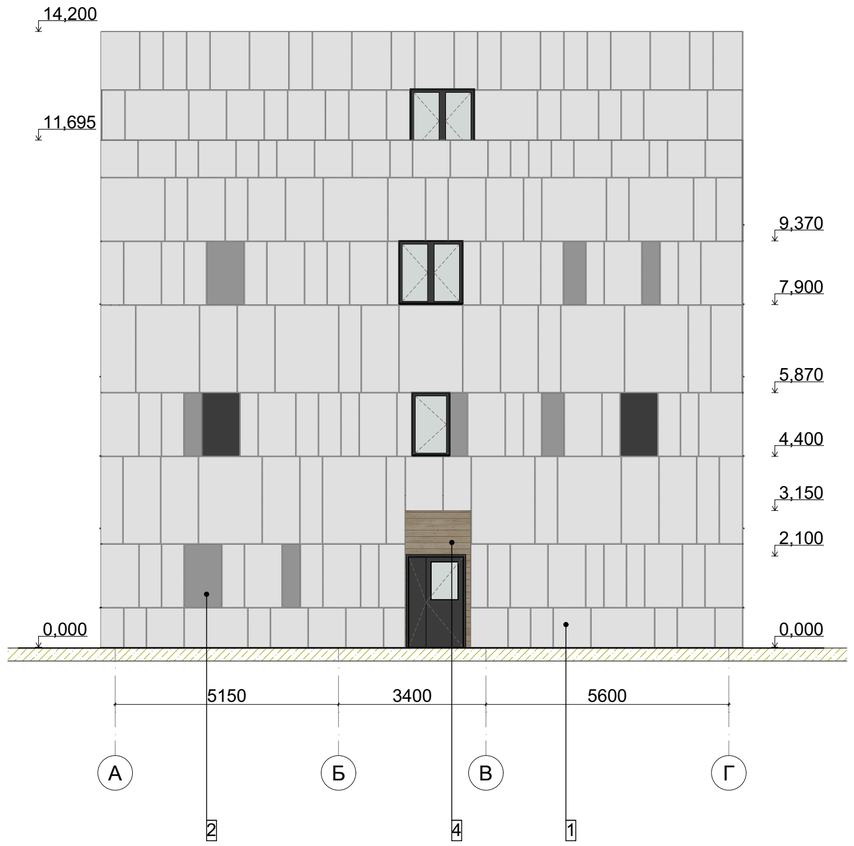

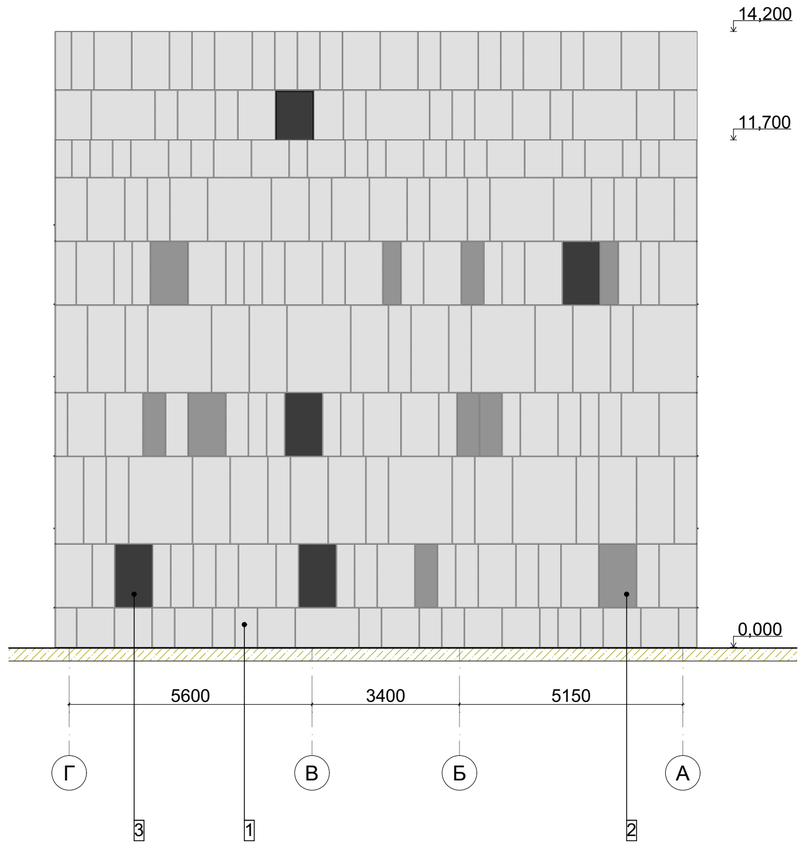

№ поз.	Наименование элемента фасада	Наименование материала отделки	Эталон цвета (образец колера)	Наименование и номер эталона цвета
1.	Наружные стены	Композитные панели		RAL9002
2.				RAL7044
3.				RAL7016
4.		Металлосайдинг текстура дерево		Кедр/ дуб
5.	Откосы	Композитные панели		RAL7016
6.	Окна			RAL7016
7.	Двери			RAL7016
8.	Вывеска			
9.	Адресные таблички			

							#ПрN-АР
							#Полный Адрес Участка
Изм.	Кол.уч.	Лист	№Док.	Подп.	Дата		
						#Наименование Проекта	Стадия: #Стадия Проекта; Лист: 06; Листов:
						Фасады в осях А-Г и Г-А. М1:100	#Название Организации

Фасад в осях 5-1. М1:100



№ поз.	Наименование элемента фасада	Наименование материала отделки	Эталон цвета (образец колера)	Наименование и номер эталона цвета
1.	Наружные стены	Композитные панели		RAL9002
2.				RAL7044
3.				RAL7016
4.		Металлосайдинг текстура дерево		Кедр/ Дуб
5.	Откосы	Композитные панели		RAL7016
6.	Окна			RAL7016
7.	Двери			RAL7016
8.	Вывеска			
9.	Адресные таблички			

							#Пр№-АР
							#Полный Адрес Участка
Изм.	Кол.уч.	Лист	№Док.	Подп.	Дата		
						#Наименование Проекта	Стадия: #Стадия Проекта; Лист: 07; Листов:
						Фасад в осях 5-1. М1:100	#Название Организации

Фрагмент фасада



Композитные панели RAL9002

Композитные панели RAL7016

Оконные откосы:
композитные панели RAL7016

Оконный профиль RAL7016


Металлосайдинг текстура дерево

Дверной откос
металлосайдинг текстура дерево

Дверной профиль RAL7016

						#ПрN-АР		
						#Полный Адрес Участка		
Изм.	Кол.уч.	Лист	№Док.	Подп.	Дата			
						#Наименование Проекта	Стадия	Лист	Листов
							#Стадия Проекта	08	
						Фрагмент фасада	#Название Организации		

План 1 этажа. М1:100

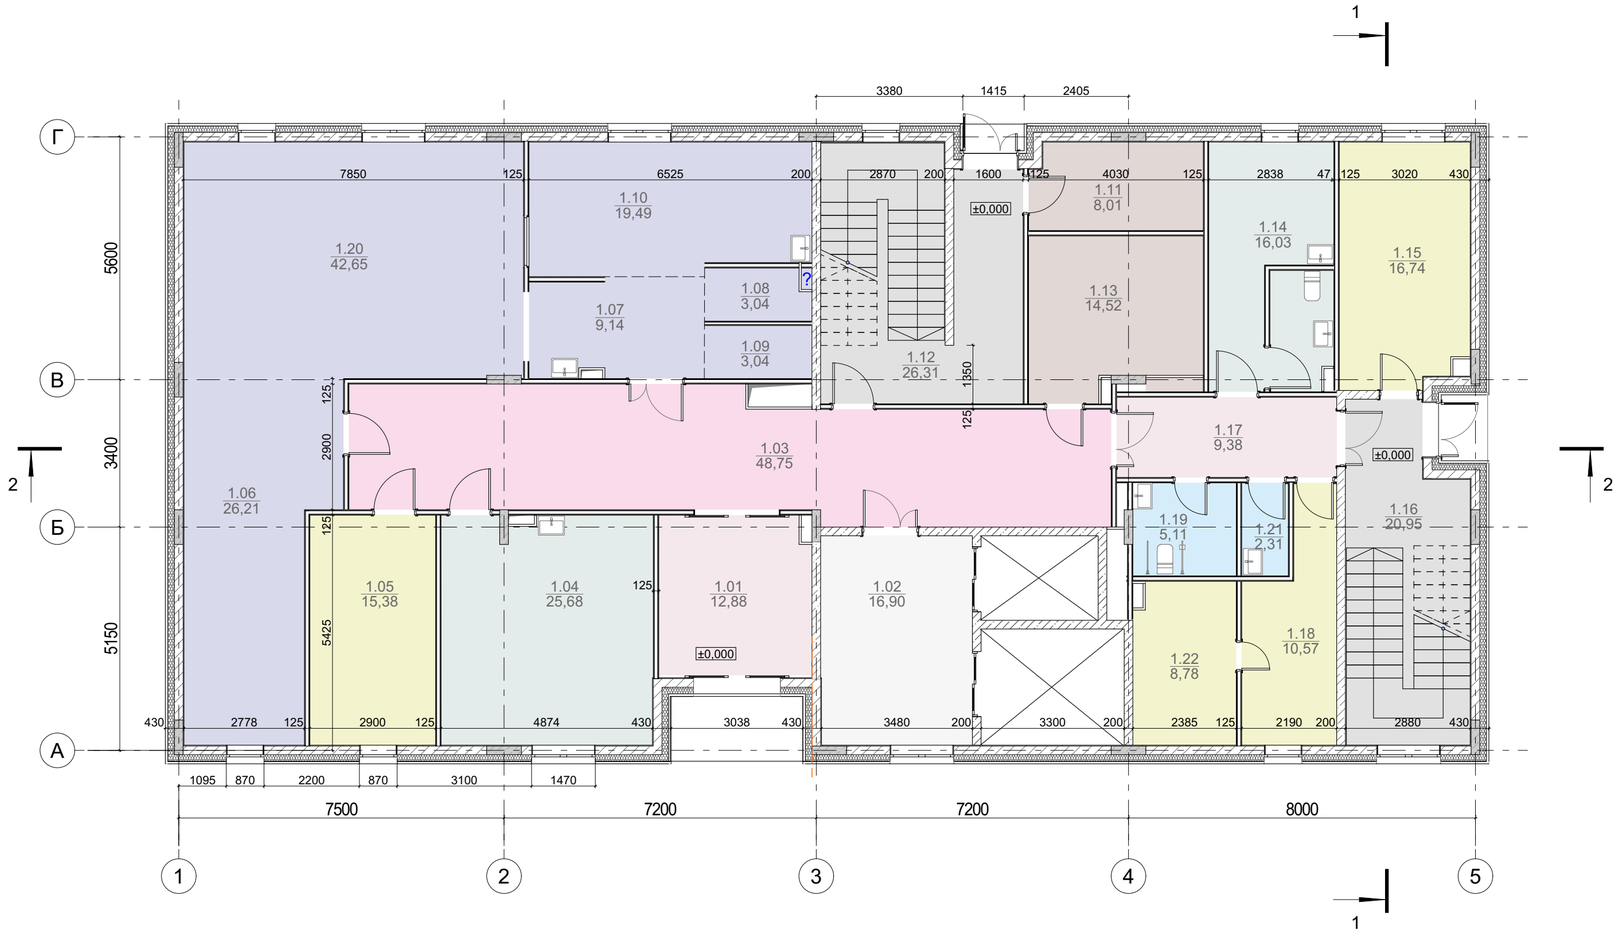

Условные обозначения

- зона МРТ
- рекреационная зона
- зона комфортного ожидания
- административная зона
- зона хранения
- санузлы
- техническая зона
- лифтовой холл
- лестницы

Экспликация помещений 1 этажа

№ помещения	Наименование	Площадь	Кат. помещения	Примечание
1.01	Вестибюль	12,9		
1.02	Лифтовой холл	16,9		
1.03	Зона комфортного ожидания	48,7		
1.04	Помещение приготовления средств иммобилизации	25,7		
1.05	Электрощитовая	15,4		
1.06	Техническая зона МРТ	26,2		
1.07	Подготовительная МРТ	9,1		
1.08	Зона переодевания	3,0		
1.09	Зона переодевания	3,0		
1.10	Комната управления МРТ с рабочим местом врача рентгенолога	19,5		
1.11	Гардероб персонала	8,0		
1.12	Лестница 1	26,3		
1.13	Гардеробная	14,5		
1.14	Комната персонала	16,0		
1.15	Серверная	16,7		
1.16	Лестница 2	20,9		
1.17	Коридор	9,4		
1.18	Тепловойм узел	10,6		
1.19	Санузел МГН	5,1		
1.20	Процедурная МРТ	42,6		
1.21	КУИ	2,3		
1.22	Насосная	8,8		
		361,6 м²		

						#Пр№-АР
						#Полный Адрес Участка
Изм.	Кол.уч.	Лист	№Док.	Подп.	Дата	
						#Наименование Проекта
						План 1 этажа. М1:100

Стадия	Лист	Листов
#Стадия Проекта	09	

#Название Организации

План 2 этажа. М1:100



Условные обозначения

- палаты
- рекреационная зона
- зона комфортного ожидания
- административная зона
- зона хранения
- санузлы
- процедурная
- лифтовой холл
- лестницы

Экспликация помещений 2 этажа

№ помещения	Наименование	Площадь	Кат. помещения	Примечание
2.01	Лифтовой холл с зоной безопасности МГН	14,5		
2.02	Тамбур	5,1		
2.03	Палата 1	16,6		
2.04	Палата 2	16,1		
2.05	Санузел	3,0		
2.06	Палата 3	16,2		
2.07	Тамбур	4,6		
2.08	Палата 4	16,8		
2.09	Санузел	3,2		
2.10	Санузел персонала	4,3		
2.11	Ординаторская	17,6		
2.12	Санузел МГН	5,6		
2.13	Лестница 2	17,4		
2.14	Сестринская с помещением хранения медикаментов	18,1		
2.15	Зона комфортного пребывания	27,6		
2.16	Кабинет дежурного врача	13,3		
2.17	Процедурная дневного стационара	18,6		
2.19	Лестница 1	17,2		
2.20	Палата 5	21,9		
2.21	Санузел	3,1		
2.22	Санитарная комната с хранением грязного белья	19,1		
2.23	Комната персонала	14,2		
2.24	Сестринский пост	6,1		
2.25	Склад оборудования	18,9		
2.26	Кладовая для хранения чистого белья	6,5		
2.27	Коридор палатного отделения дневного стационара	23,9		
2.29	Коридор	16,5		
2.30	КУИ	3,7		
		369,7 м²		

						#ПрN-АР	
						#Полный Адрес Участка	
Изм.	Кол.уч.	Лист	№Док.	Подп.	Дата		
						#Наименование Проекта	Стадия: #Стадия Проекта; Лист: 10; Листов:
						План 2 этажа. М1:100	#Название Организации

План 3 этажа. М1:100



Условные обозначения

- палаты
- рекреационная зона
- зона комфортного ожидания
- административная зона
- зона хранения
- процедурная
- санузлы
- лифтовой холл
- лестницы

Экспликация помещений 3 этажа


№ помещения	Наименование	Площадь	Кат. помещения	Примечание
3.01	Лифтовой холл	15,0		
3.02	Палата 1	16,8		
3.03	Санузел	3,4		
3.04	Палата 2	16,1		
3.05	Палата 3	16,1		
3.06	Тамбур	4,8		
3.07	Палата 4	16,0		
3.08	Сестринский пост	6,2		
3.09	Кладовая для хранения чистого белья	7,4		
3.10	Коридор	31,4		
3.11	Склад оборудования дневного стационара	18,2		
3.12	Комната персонала	14,3		
3.13	Санитарная комната с хранением грязного белья	18,4		
3.14	Палата 5 для МГН	21,1		
3.15	Санузел при палате МГН	4,4		
3.16	Лестница 1	17,3		
3.17	Процедурная дневного стационара	19,1		
3.18	Кабинет заведующего дневным стационаром	18,5		
3.19	Кабинет дежурного врача	10,1		
3.20	Сестринская с помещением хранением медикаментов	14,3		
3.21	Лестница 2	17,2		
3.22	Ординаторская	17,6		
3.23	Санузел персонала	4,3		
3.24	Санузел	3,4		
3.25	Тамбур	4,3		
3.26	КУИ	3,6		
3.27	Санузел МГН	5,7		
3.28	Зона комфортного ожидания	23,9		
		368,9 м²		

						#ПрN-АР
						#Полный Адрес Участка
Изм.	Кол.уч.	Лист	№Док.	Подп.	Дата	
						#Наименование Проекта
						План 3 этажа. М1:100

Стадия	Лист	Листов
#Стадия Проекта	11	

#Название Организации

План технического этажа. М1:100

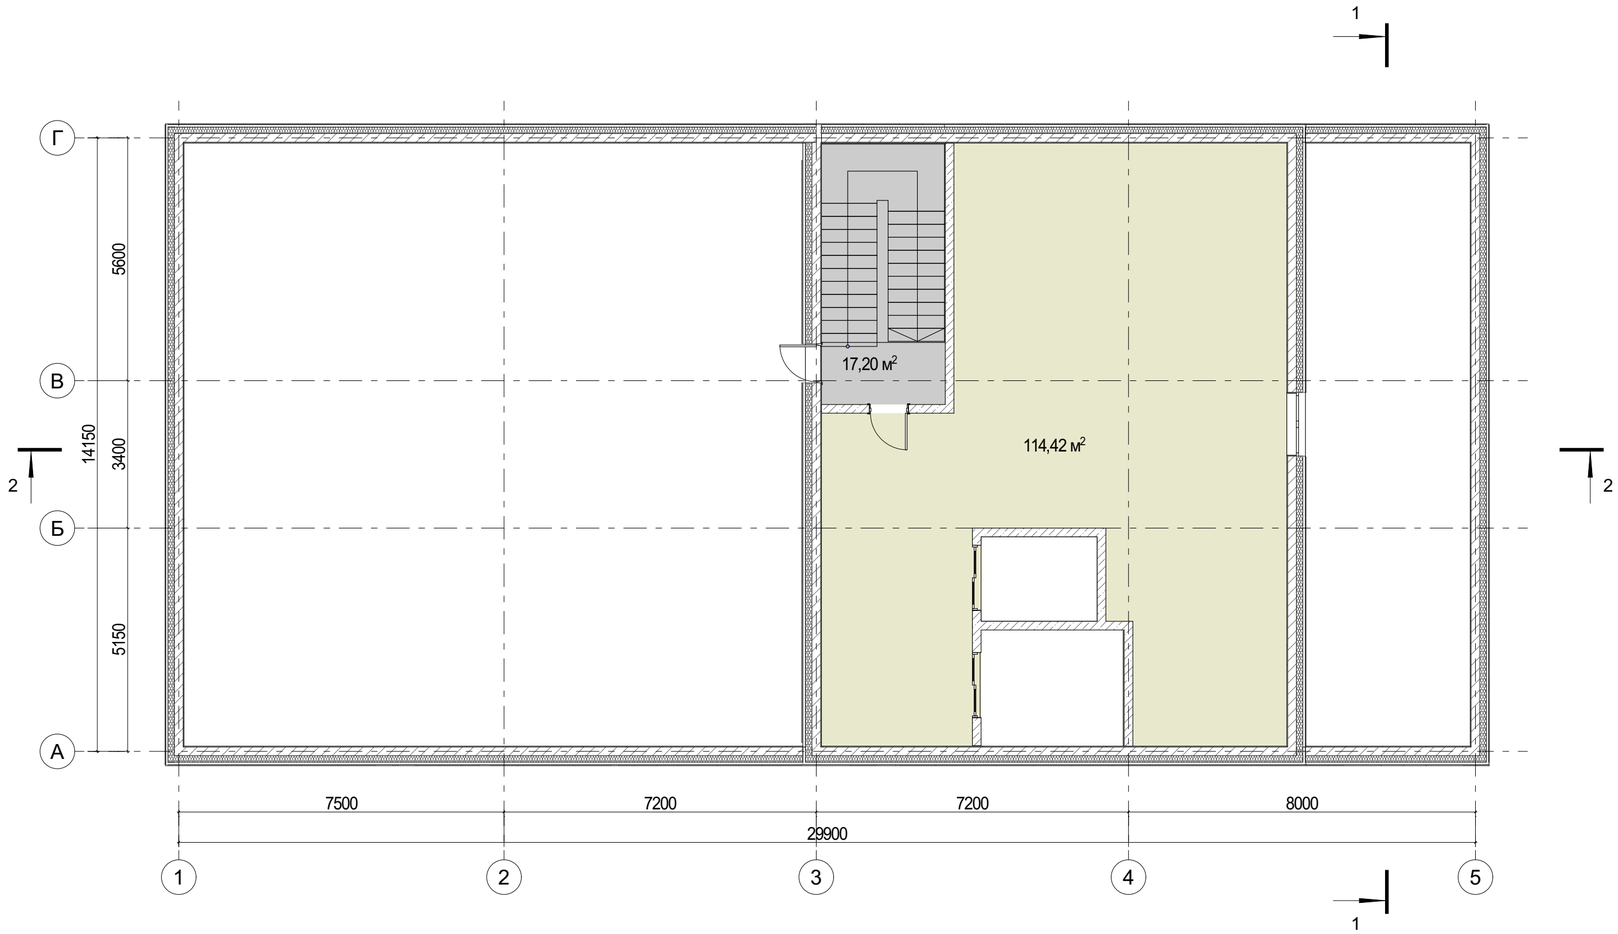


Условные обозначения

техническая зона

лестницы

						#ПрN-АР	
						#Полный Адрес Участка	
Изм.	Кол.уч.	Лист	№Док.	Подп.	Дата		
						#Наименование Проекта	Стадия: #Стадия Проекта; Лист: 12; Листов:
						План технического этажа. М1:100	#Название Организации

Разрезы 1-1 и 2-2. М1:100

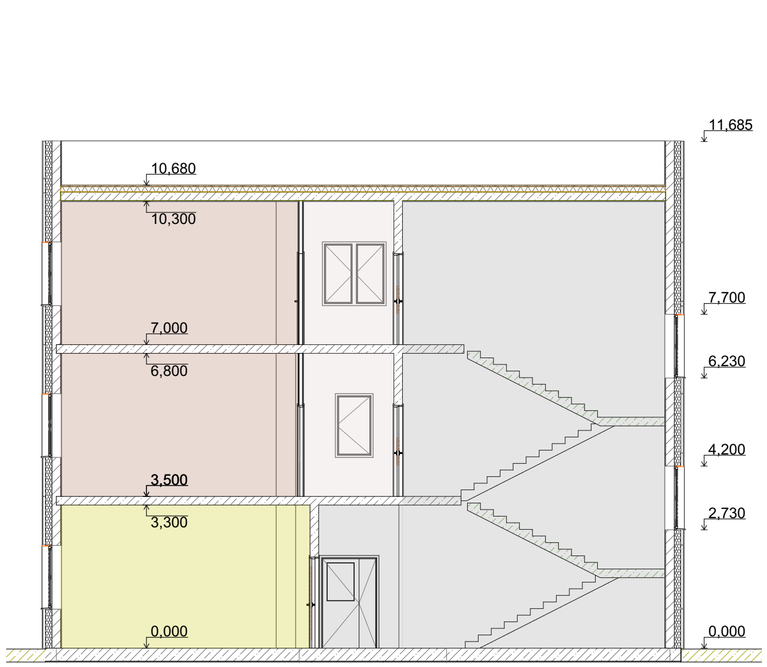



Условные обозначения

- зона МРТ
- рекреационная зона
- зона комфортного ожидания
- административная зона
- зона хранения
- санузлы
- техническая зона
- лифтовой холл
- лестницы

						#ПрN-АР		
						#Полный Адрес Участка		
Изм.	Кол.уч.	Лист	№Док.	Подп.	Дата			
						#Наименование Проекта	Стадия	Лист	Листов
							#Стадия Проекта	13	
						Разрезы 1-1 и 2-2. М1:100	#Название Организации		

Пояснительная записка

Общие сведения

Объект проектирования: отдельно стоящее здание с размещением магнитно-резонансного томографа по адресу: г. Химки, мкр. Подрезково, ул. Школьная, д.3. Кадастровый номер 50:10:0040207:3150

Основание проектирования: решение застройщика, договор на проектирование, дополнительное соглашение №1 к договору о комплексном развитии территории городского округа Химки.

Нормативная база

Проект разработан в соответствии с:

- Постановлением Правительства МО №671-ПП от 25.08.2023
- СП 118.13330.20 Общественные здания и сооружения
- СП 158.13330.2014 Здания и помещения медицинских организаций
- СП 1.13130.2020 Система противопожарной защиты
- ГОСТ 5746-2015
- СП 1313330.2020 СНиП 31-06-2009

Основные характеристики объекта

Функциональное зонирование:

Функционально помещения разделены на следующие зоны:

Рекреационная зона, административная зона, зоны хранения, техническая, зона палат, зона санузлов, зона комфортного ожидания, зона процедурных, зона МРТ, зона лифтов, зона лестниц.

Особенности планировки:

Планировки разработаны с учетом особенности земельного участка, с функциональным использованием площади. Здание представляет собой прямоугольник в плане, разделенный коридорами на функциональные зоны. Связи между функциональными зонами обеспечиваются в пределах этажей через коридоры и зоны ожидания, между этажами - через лифты и лестницы.

Вертикальная связь обеспечина лестницами и лифтами. Лестницы имеют ширину марша в свету 1350 мм. Лестница 1 - эвакуационная, сообщает 1 и технический этажи, Лестница 2 - эвакуационная, сообщает 1 и 3 этажи.

Технический этаж имеет выход на кровлю.

2 лифта категории А по ГОСТ 5746-2015, с габаритами кабин 1800х2700 мм грузоподъемностью 2500 кг и 1400х2200мм грузоподъемностью 1000 кг.

Входная группа с лифтами и лестницей находится в центре прямоугольника, что обеспечивает наилучшую доступность. Дополнительная лестница - с правой стороны, которая функционально отведена под административно-бытовые помещения.

На 1-м этаже находится входная группа, лифтовой холл, гардероб, диагностическое отделение с МРТ и зоной комфортного пребывания пациентов.

Второй и третий этажи функционально и планировочно повторяют друг друга, слева от лифтового холла расположены палатные отделения дневного стационара, права - диагностические и административно-бытовые помещения.

Технический этаж предназначен для расположения оборудования, доступ на него осуществляется через эвакуационную лестницу. Отвод ливневых и талых вод с кровли выполнен через организованную систему внутренних водостоков.

Беспрепятственный доступ маломобильных групп населения обеспечивается комфортными холлами, достаточными габаритами дверных проемов, разворотных площадок и путей движения МГН, лифтов.

На каждом этаже предусмотрен санузел для МГН.

Для маломобильных групп граждан предусмотрена палата в блоке дневного стационара.

						#Пр№-АР		
						#Полный Адрес Участка		
Изм.	Кол.уч.	Лист	№Док.	Подп.	Дата			
						#Наименование Проекта	Стадия	Лист	Листов
							#Стадия Проекта	14	
						Пояснительная записка	#Название Организации		

Фасадные решения:
Вход в помещения с улицы выполняется на одном уровне с тротуаром, что обеспечивает максимальную доступность для всех категорий населения. Защита от осадков входнов и обеспечена нишами. Входы запроектированы: главный - со стороны проезда, 2 эвакуационных. Выход в осях 5-В-Б и выход в осях Г-3-4.
Отделка фасадов навесными панелями обеспечивают необходимый уровень энергоэффективности, звуконепроницаемости и пожарной безопасности здания.
Наружная отделка фасада фасадными панелями осуществляется с соблюдением требований общей и пожарной безопасности к вентилируемым фасадам.
В отделке фасадов используются:
Стены - навесной вентилируемый фасад
Окна - ПВХ, двухкамерные стеклопакеты
Двери -металлические из оцинкованной стали с полимерным покрытием
Входная группа - металлические ламели под дерево.
Цветовое решение фасадал по каталогу RAL: 7016 (черный) - оконные рамы и темный фасад, 7044 -серый фасад, 9002-светлый фасад

5. Транспортная и пешеходная доступность, элементы благоустройства:
Размещение объекта капитального строительства в границах земельного участка произведено с учетом реализации требований нормативов градостроительного проектирования Московской области, утвержденных Постановлением Правительства Московской области от 17.08.2015 N 713/30 «Об утверждении нормативов градостроительного проектирования Московской области), стандартов качества, утвержденных Постановлением Правительства Московской области от 01.06.2021 № 435/18 «Об утверждении стандартов жилого помещения и комфортности проживания на территории Московской области», правил благоустройства территории муниципального образования Московской области.
Реализация и благоустройство транспортной и пешеходной сети, элементов благоустройства и мест хранения автотранспорта (с учетом МГН) будет производиться одновременно с объектом в соответствии со схемой планировочной организации земельного участка.
Расчет мест хранения автотранспортных средств
Расчет требуемого количества машиномест для организованного хранения принят в соответствии с п 11.31 СП 42.13330.2016 «Градостроительство. Планировка и застройка городских и сельских поселений», а так же в соответствии с п. 5.12 ПП МО №713/30 «Об утверждении нормативов градостроительного проектирования Московской области».

Расчет необходимого количества машино-мест на приобъектных стоянках:
Для 16 сотрудников амбулаторного заведения:
16/100 х 10 = 2 м/м. В том числе 1 м/м для МГН группы М4
На 50 посещений амбулаторного заведения:
50/100 х 4 = 2 м/м. В том числе 1 м/м для МГН группы М4
Всего на приобъектных стоянках необходимо разместить 4 м/м, в т.ч. 2 м/м для МГН группы М4.
Проектом предусматривается устройство автостоянки общим количеством 7 м/м, в т.ч. 2 м/м для МГН группы М4

Минимальная ширина пешеходного пути (тротуаров) с учетом встречного движения инвалидов на креслахколясках предусмотрена не менее 2,0 м. На пересечении тротуара с проезжей частью на путях передвижения пешеходов, организовано устройство пандуса с понижением бортового камня, для беспрепятственного передвижения МГН.
Места для личного транспорта инвалидов размещаются вблизи входа, доступного для инвалидов.
Машиноместа для МГН расположены на расстоянии не более 50 м от входов в помещения общественных назначений.
Тротуары и проходы предусмотрены шириной не менее 2,0 м.

						#ПрN-АР		
						#Полный Адрес Участка		
Изм.	Кол.уч.	Лист	№Док.	Подп.	Дата			
						#Наименование Проекта	Стадия	Лист	Листов
							#Стадия Проекта	15	
						Архитектурно - художественные решения	#Название Организации		

Технико-экономические показатели

№ п/п	Наименование показателя	Ед. изм.	Числовое значение
1.	Площадь здания по СП 54.13330.2016 (сумма площадей этажей здания, измеренных в пределах внутренних поверхностей наружных стен)	м2	1230.5
1.1.	Надземная	м2	448.3
1.2.	Подземная	м2	-
2.	Строительный объем здания в т.ч.	м2	17.5
3.	Общая площадь здания (сумма площадей помещений) в т.ч.	м2	1,384.4
3.1.	Лечебно-диагностические помещения	м2	315.1
3.2.	Административно-бытовые помещения	м2	221.7
3.3.	Помещения для хранения (кладовые)	м2	153.5
3.4.	Площадь помещений МОП	м2	347.5
3.5.	Площадь помещений технического и инженерного назначения	м2	165.9
4.	Количество машиномест*	шт.	7
5.	Количество этажей: включая подземный, подвальный, цокольный, тех. этаж и т.п.	шт.	4
6.	Этажность	шт.	4
7.	Максимальная отметка здания	м	14.2
8.	Минимальная отметка здания	м	0.0
9.	Высота первого этажа	м	3.3
10.	Высота второго этажа	м	3.3
11.	Высота третьего этажа	м	3.3
12.	Высота технического этажа	м	2.3
13.	Количество посещений в смену	шт.	50
14.	Количество работников	шт.	16
15.	Площадь застройки (всего), в т.ч.	м2	478.7
	существующей	м2	27.7
	проектируемой	м2	451.0

						#Пр№-АР			
						#Полный Адрес Участка			
Изм.	Кол.уч.	Лист	№Док.	Подп.	Дата				
						#Наименование Проекта	Стадия	Лист	Листов
							#Стадия Проекта	16	
						Технико-экономические показатели	#Название Организации		